




Front View



Terrace

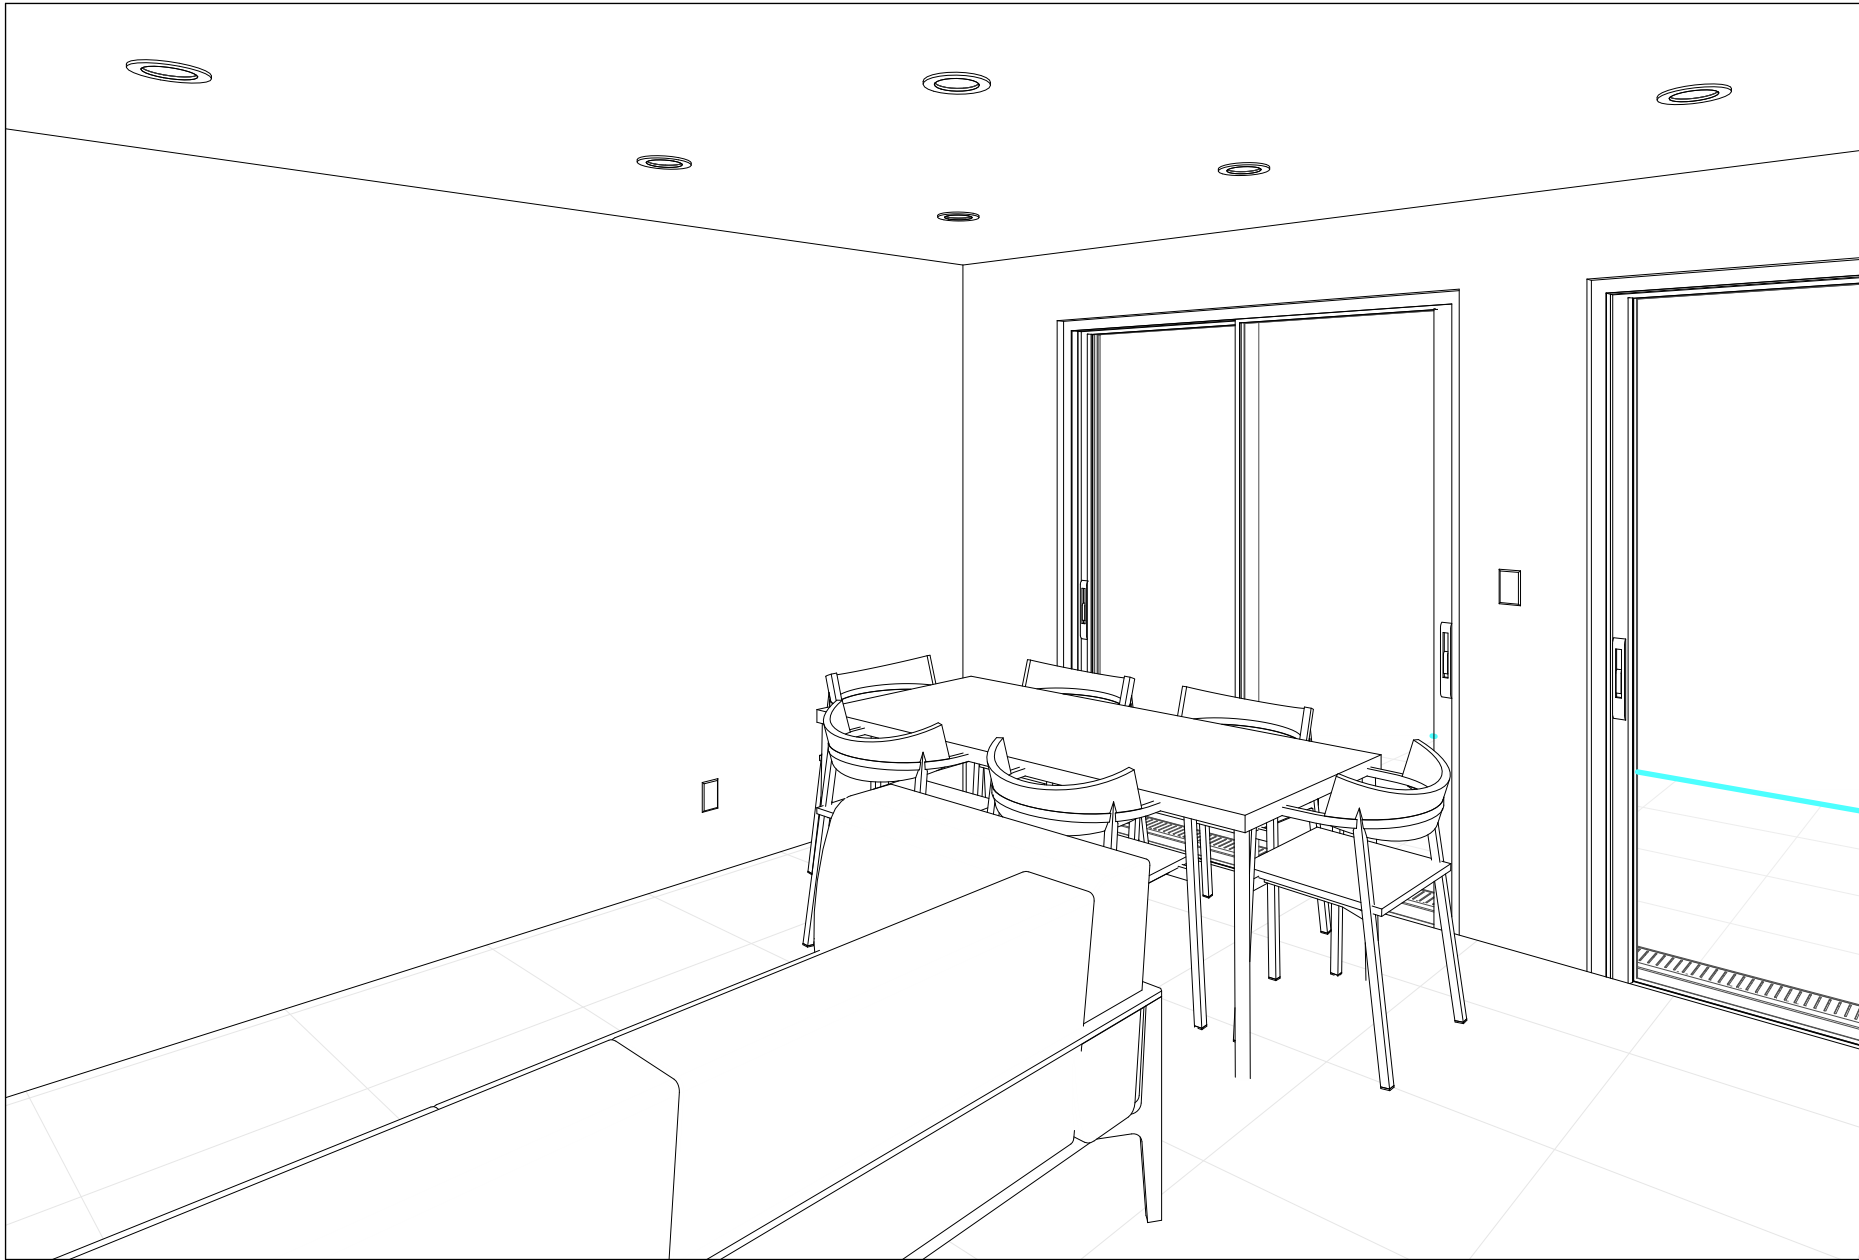

Living Area



Kitchen Area

1. THESE DRAWINGS MUST BE CHECKED BY THE CUSTOMER OR CONTRACTOR PRIOR TO APPROVAL. ANY ERRORS OR OMISSIONS MUST BE REPORTED IN WRITING TO BAUHU PRIOR TO COMMENCEMENT OF CONSTRUCTION.
2. ARCHITECTURAL DRAWINGS SHOULD BE READ IN CONJUNCTION WITH STRUCTURAL DETAILING AND FABRICATION GENERAL ASSEMBLY DRAWINGS.
3. FOR CONSTRUCTION PURPOSES, USE ONLY THE LATEST APPROVED DRAWINGS LABELED 'ISSUED FOR CONSTRUCTION'.
4. DO NOT SCALE FROM THIS DRAWING.
5. THE COMPANY OPERATES USING METRIC DIMENSIONS AS THE PRINCIPAL DENOMINATION.
6. ALL CONCRETE WORKS ARE OUTSIDE OF THE SCOPE OF THE COMPANY. INFORMATION REGARDING SLAB DESIGN AND CONNECTIONS IN THESE DRAWINGS ARE INTENDED FOR GUIDANCE ONLY. FOUNDATION AND SLAB WORKS SHOULD BE DESIGNED AND APPROVED BY A LOCAL STRUCTURAL ENGINEER.
7. THE COMPANY RETAINS FULL TITLE AND OWNERSHIP OF THESE PLANS AND DESIGNS. ANY UNAUTHORISED USE, REPRODUCTION, OR DISTRIBUTION OF THESE PLANS, WHETHER IN WHOLE OR PART, IS EXPRESSLY PROHIBITED WITHOUT PRIOR WRITTEN CONSENT.
8. THE HYBRID STEEL FRAME CONSTRUCTION SYSTEM AND METHODOLOGY (PATENT PENDING) DESCRIBED IN THESE PLANS HAS BEEN DEVELOPED BY THE COMPANY AND IS SUBJECT TO A PROVISIONAL PATENT APPLICATION & ASSIGNMENT - US APPLICATION No. 63/722,841.

No.	Revision	Date
01	Moved walls under roof joists	13.03

- ISSUED FOR:
- ☒ Issued for information
 - ☐ Issued for client approval
 - ☐ Issued for fabrication
 - ☐ Issued for construction

Bahama Beach


DRAWING TITLE: Views

DRAWN BY: Mladin Monica-Mihaela

SCALE:

DRAWING NO: A01

DATE: 17/03/2025

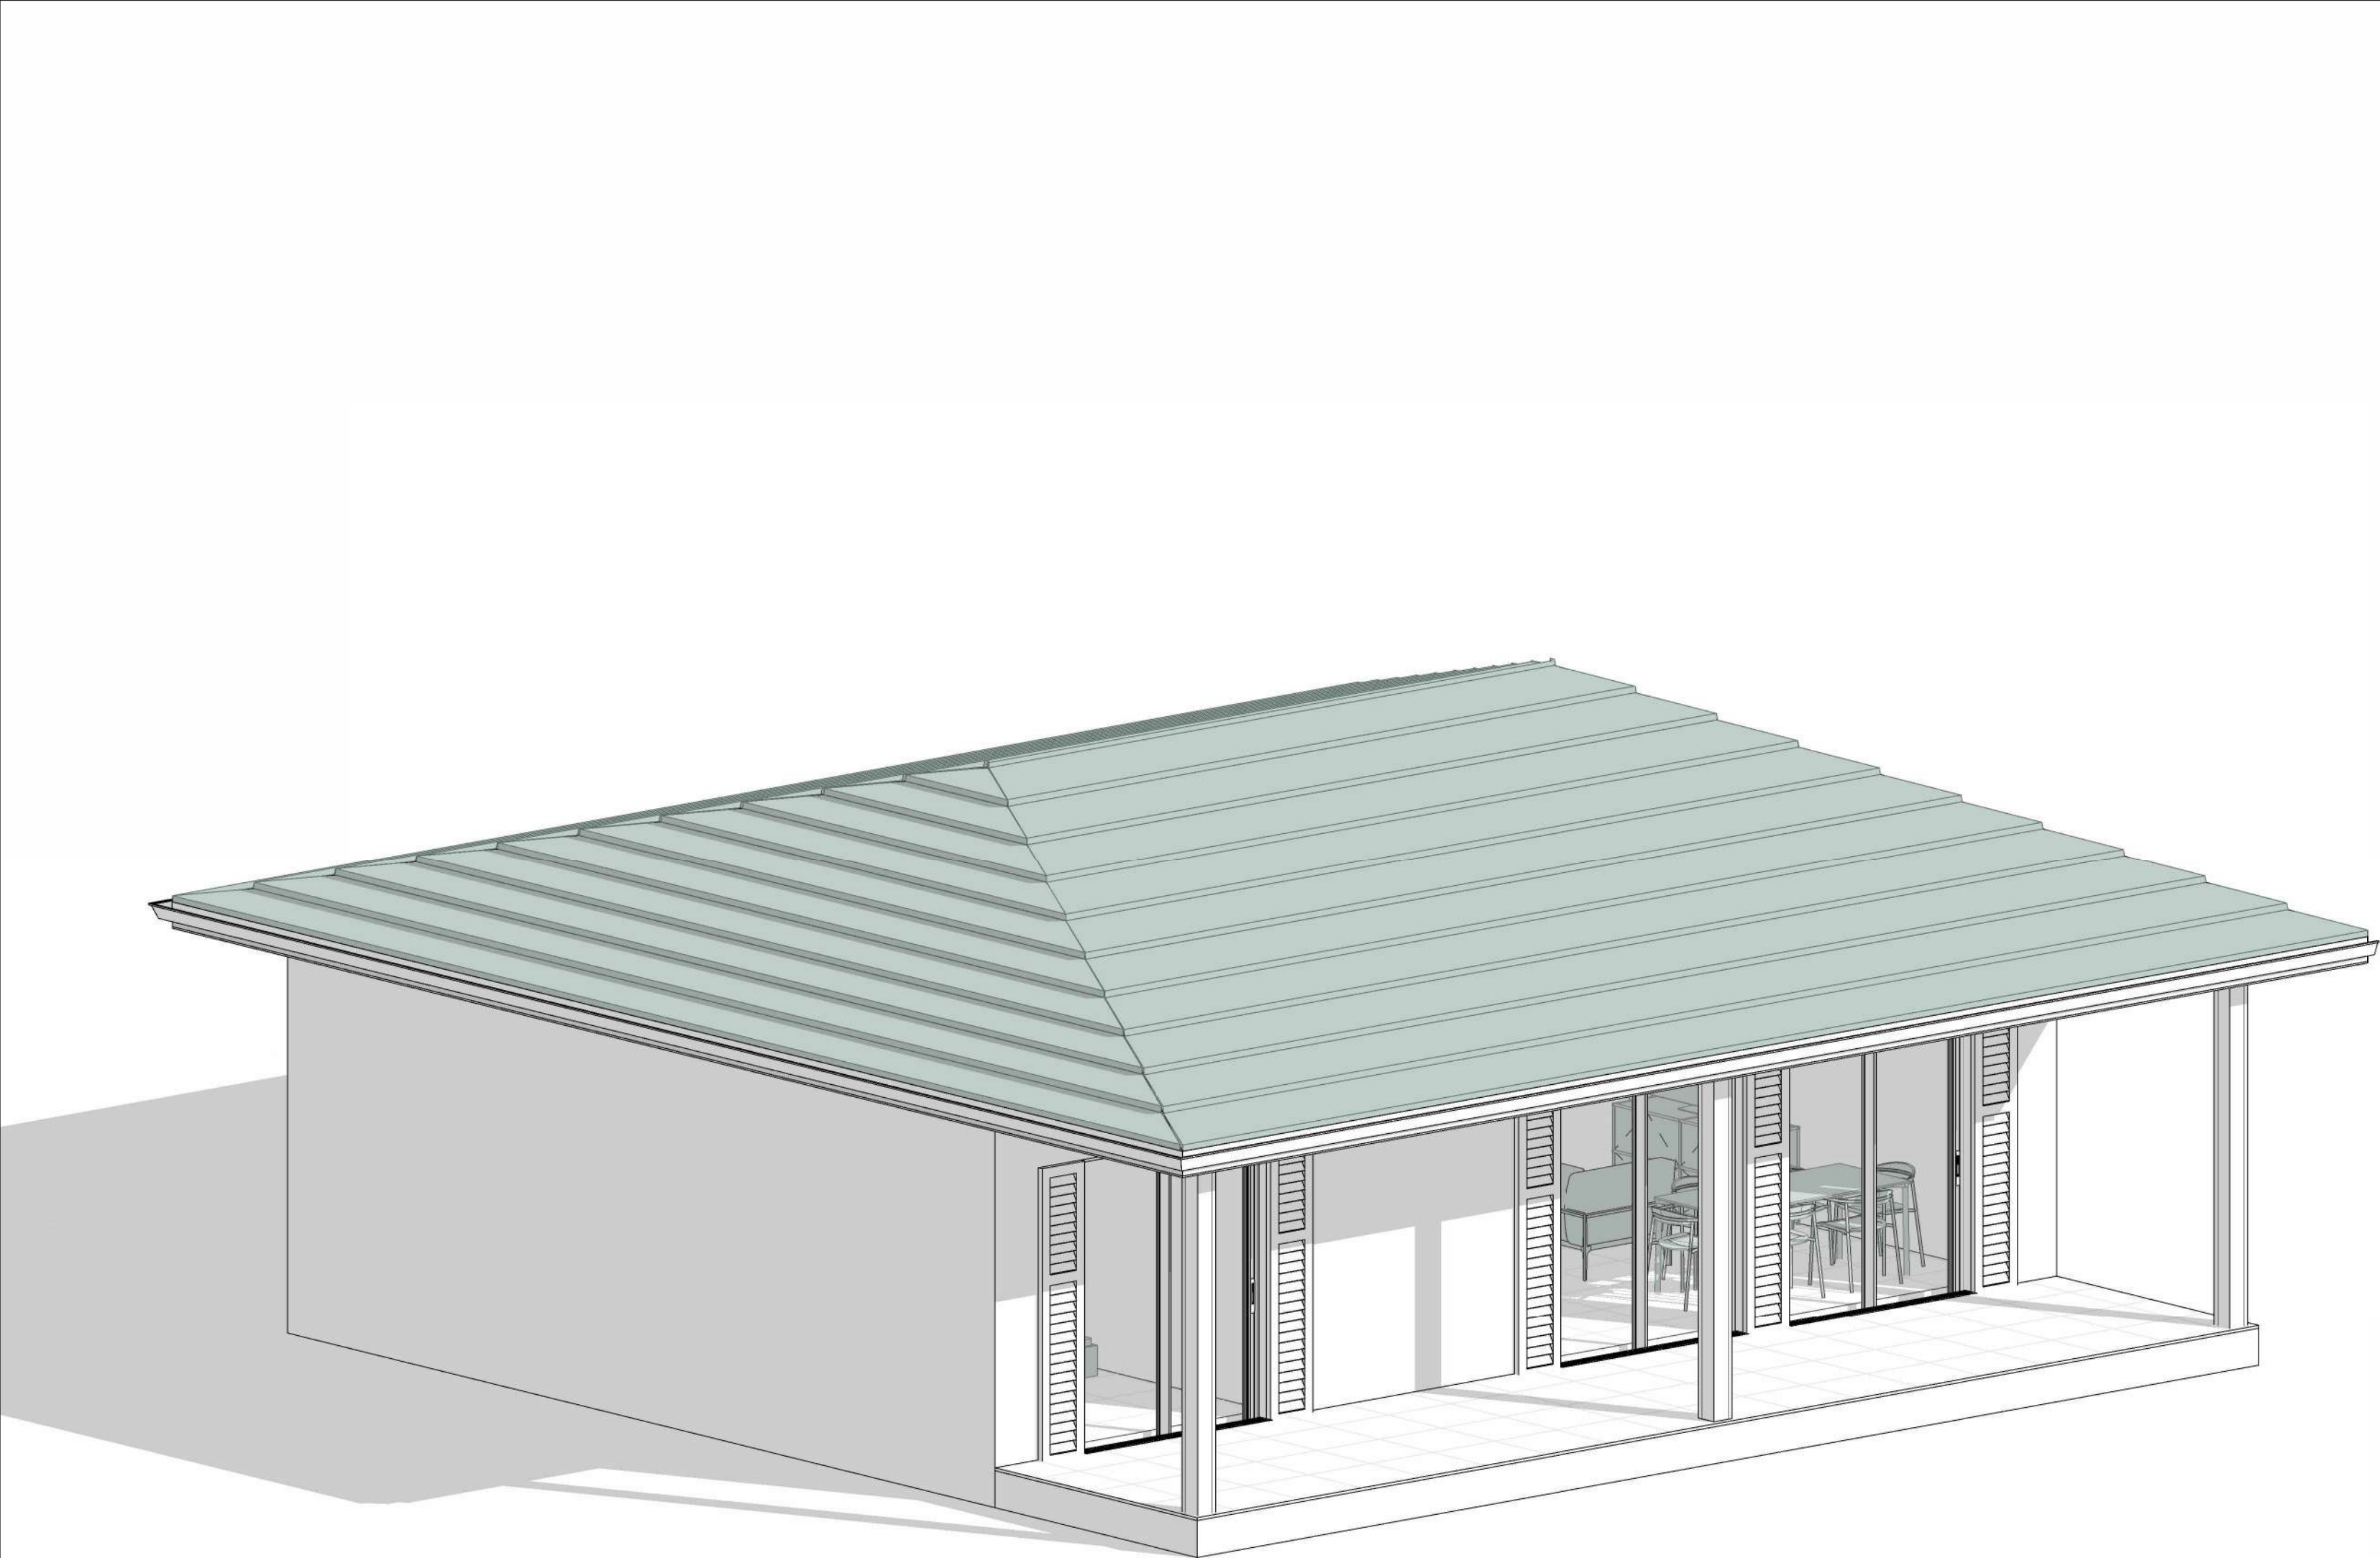

1. THESE DRAWINGS MUST BE CHECKED BY THE CUSTOMER OR CONTRACTOR PRIOR TO APPROVAL. ANY ERRORS OR OMISSIONS MUST BE REPORTED IN WRITING TO BAUHU PRIOR TO COMMENCEMENT OF CONSTRUCTION.
2. ARCHITECTURAL DRAWINGS SHOULD BE READ IN CONJUNCTION WITH STRUCTURAL DETAILING AND FABRICATION GENERAL ASSEMBLY DRAWINGS.
3. FOR CONSTRUCTION PURPOSES, USE ONLY THE LATEST APPROVED DRAWINGS LABELED 'ISSUED FOR CONSTRUCTION'.
4. DO NOT SCALE FROM THIS DRAWING.
5. THE COMPANY OPERATES USING METRIC DIMENSIONS AS THE PRINCIPAL DENOMINATION.
6. ALL CONCRETE WORKS ARE OUTSIDE OF THE SCOPE OF THE COMPANY. INFORMATION REGARDING SLAB DESIGN AND CONNECTIONS IN THESE DRAWINGS ARE INTENDED FOR GUIDENCE ONLY. FOUNDATION AND SLAB WORKS SHOULD BE DESIGNED AND APPROVED BY A LOCAL STRUCTURAL ENGINEER.
7. THE COMPANY RETAINS FULL TITLE AND OWNERSHIP OF THESE PLANS AND DESIGNS. ANY UNAUTHORISED USE, REPRODUCTION, OR DISTRIBUTION OF THESE PLANS, WHETHER IN WHOLE OR PART, IS EXPRESSLY PROHIBITED WITHOUT PRIOR WRITTEN CONSENT.
8. THE HYBRID STEEL FRAME CONSTRUCTION SYSTEM AND METHODOLOGY (PATENT PENDING) DESCRIBED IN THESE PLANS HAS BEEN DEVELOPED BY THE COMPANY AND IS SUBJECT TO A PROVISIONAL PATENT APPLICATION & ASSIGNMENT - US APPLICATION No. 63/722,841.

No.	Revision	Date
01	Moved walls under roof joists	13.03

- ISSUED FOR:
- Issued for information
- Issued for client approval
- Issued for fabrication
- Issued for construction

Bahama Beach


DRAWING TITLE: Front View

DRAWN BY: Mladin Monica-Mihaela

SCALE:

DRAWING NO: A02

DATE: 17/03/2025

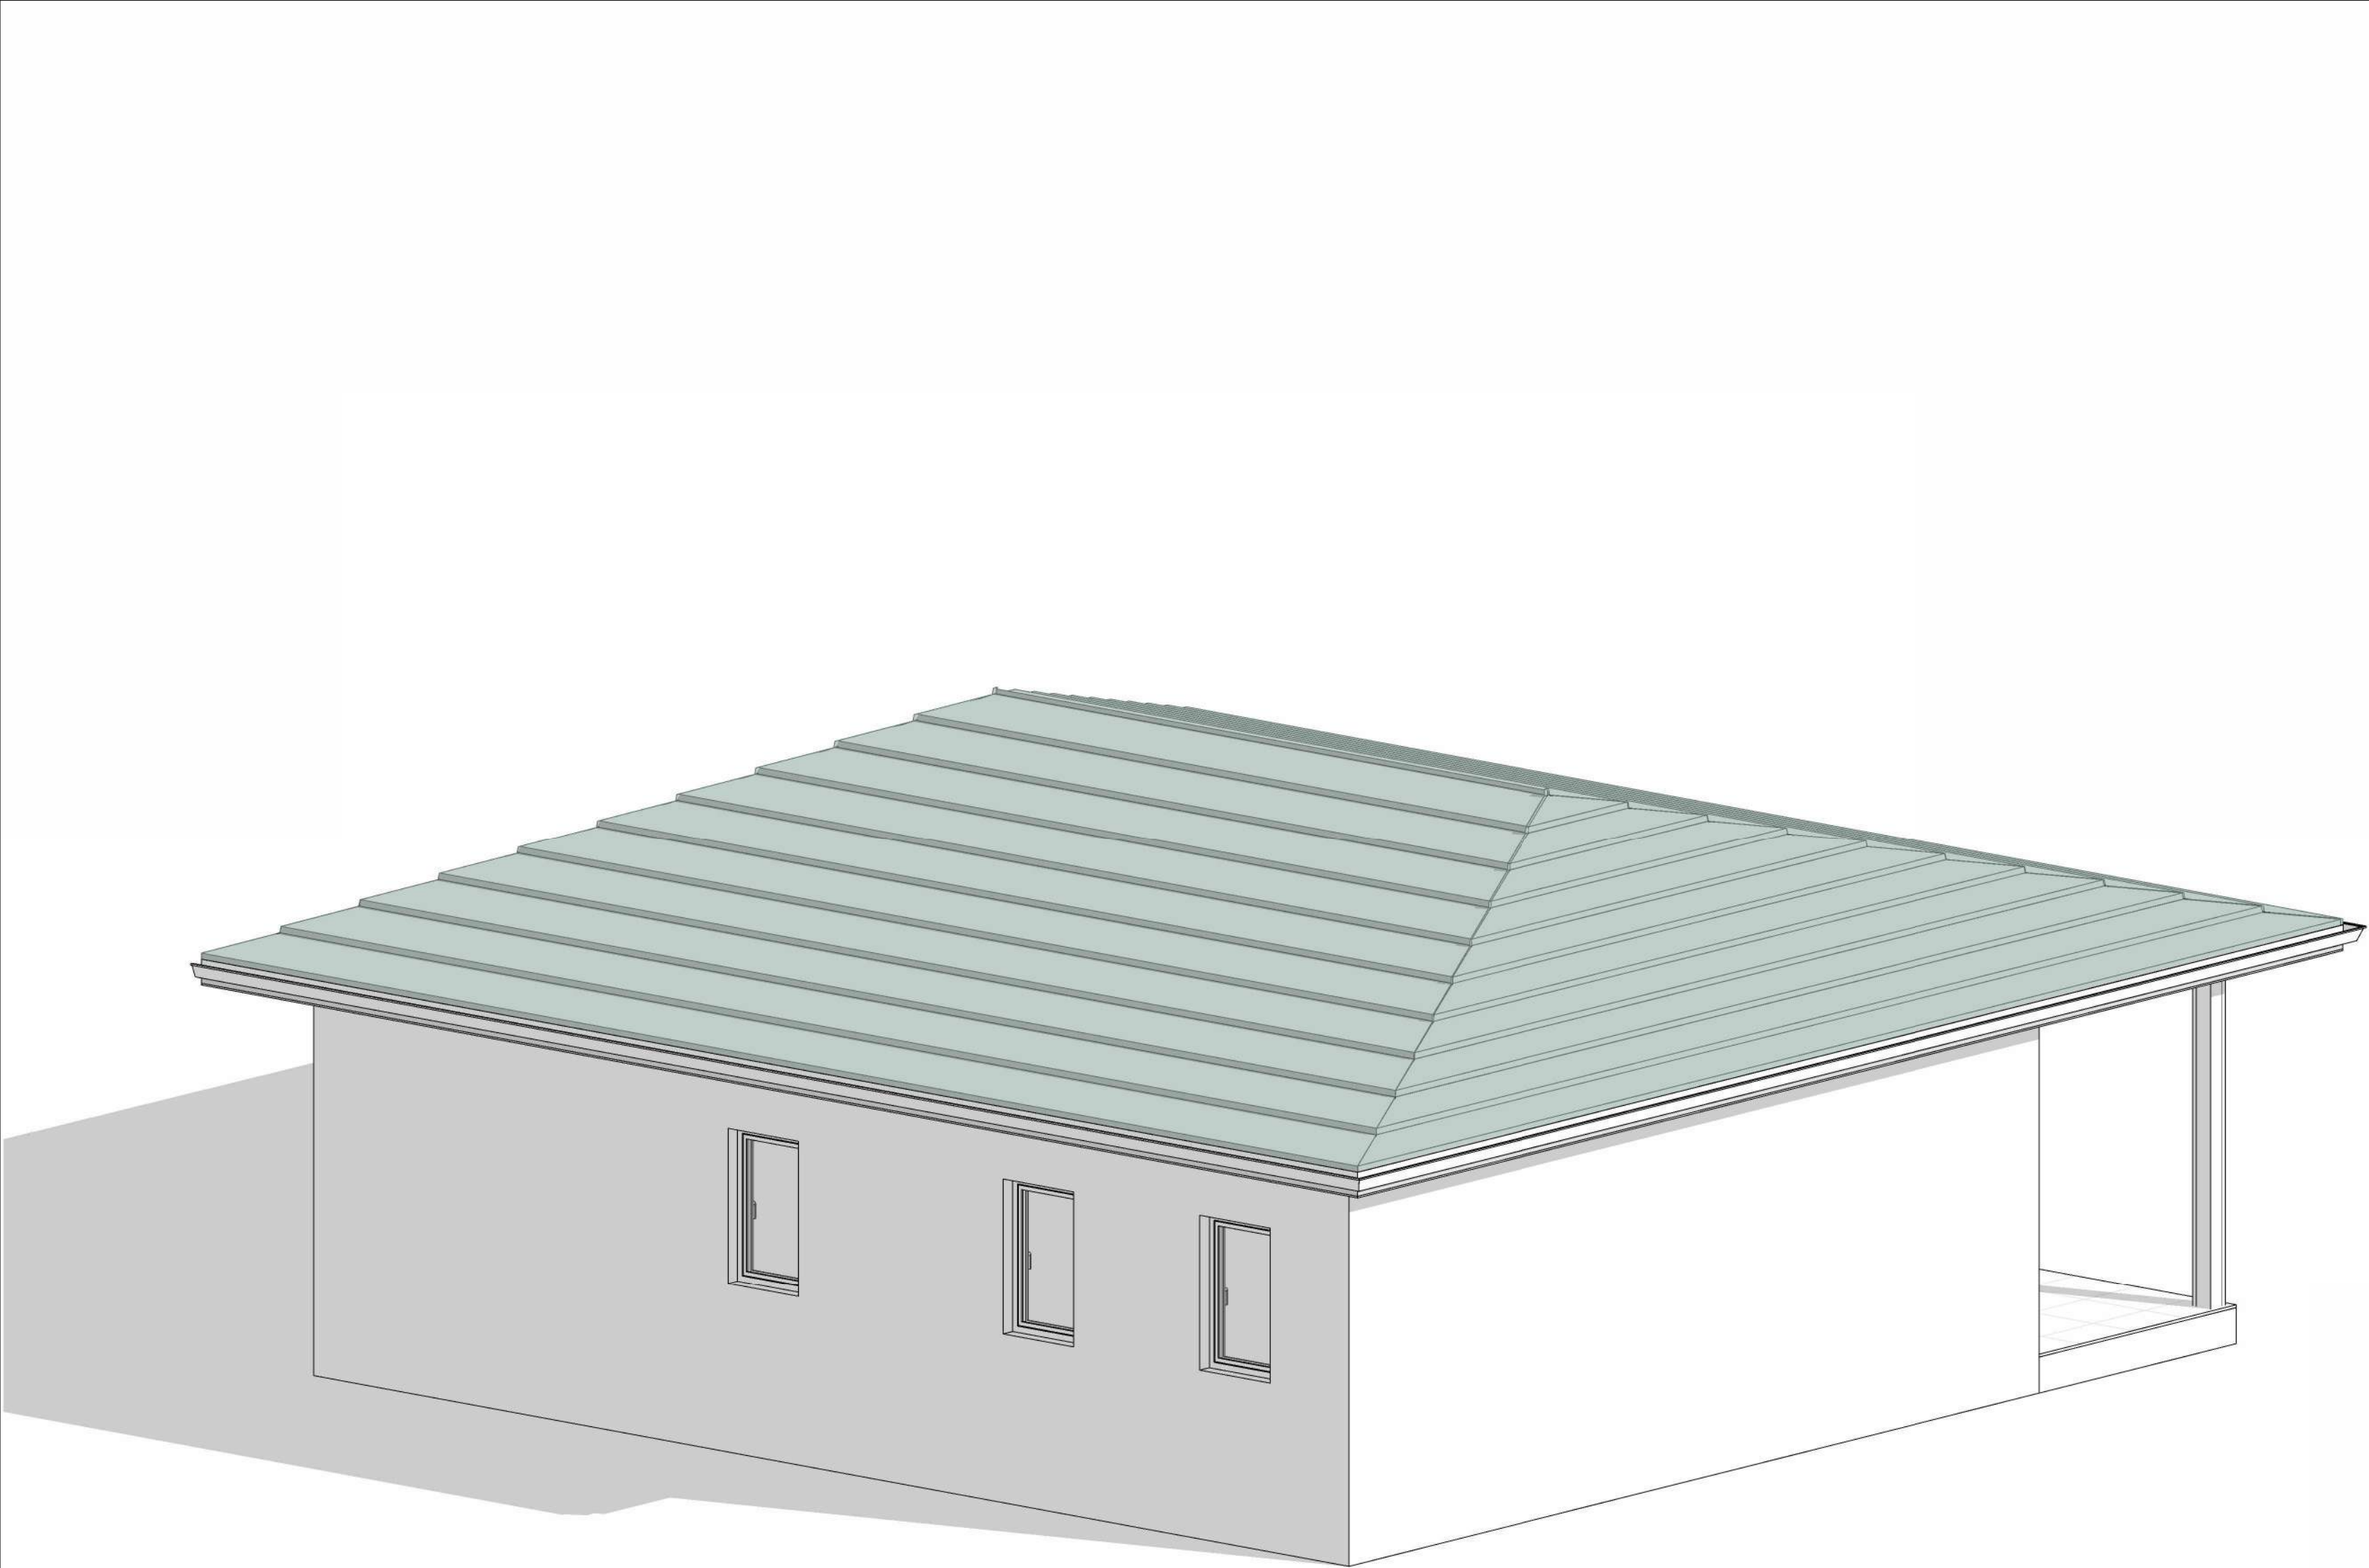

1. THESE DRAWINGS MUST BE CHECKED BY THE CUSTOMER OR CONTRACTOR PRIOR TO APPROVAL. ANY ERRORS OR OMISSIONS MUST BE REPORTED IN WRITING TO BAUHU PRIOR TO COMMENCEMENT OF CONSTRUCTION.
2. ARCHITECTURAL DRAWINGS SHOULD BE READ IN CONJUNCTION WITH STRUCTURAL DETAILING AND FABRICATION GENERAL ASSEMBLY DRAWINGS.
3. FOR CONSTRUCTION PURPOSES, USE ONLY THE LATEST APPROVED DRAWINGS LABELED 'ISSUED FOR CONSTRUCTION'.
4. DO NOT SCALE FROM THIS DRAWING.
5. THE COMPANY OPERATES USING METRIC DIMENSIONS AS THE PRINCIPAL DENOMINATION.
6. ALL CONCRETE WORKS ARE OUTSIDE OF THE SCOPE OF THE COMPANY. INFORMATION REGARDING SLAB DESIGN AND CONNECTIONS IN THESE DRAWINGS ARE INTENDED FOR GUIDENCE ONLY. FOUNDATION AND SLAB WORKS SHOULD BE DESIGNED AND APPROVED BY A LOCAL STRUCTURAL ENGINEER.
7. THE COMPANY RETAINS FULL TITLE AND OWNERSHIP OF THESE PLANS AND DESIGNS. ANY UNAUTHORISED USE, REPRODUCTION, OR DISTRIBUTION OF THESE PLANS, WHETHER IN WHOLE OR PART, IS EXPRESSLY PROHIBITED WITHOUT PRIOR WRITTEN CONSENT.
8. THE HYBRID STEEL FRAME CONSTRUCTION SYSTEM AND METHODOLOGY (PATENT PENDING) DESCRIBED IN THESE PLANS HAS BEEN DEVELOPED BY THE COMPANY AND IS SUBJECT TO A PROVISIONAL PATENT APPLICATION & ASSIGNMENT - US APPLICATION No. 63/722,841.

No.	Revision	Date
01	Moved walls under roof joists	13.03

ISSUED FOR:

Issued for information

Issued for client approval

Issued for fabrication

Issued for construction

Bahama Beach

DRAWING TITLE:

Rear View

DRAWN BY:

Mladin Monica-Mihaela


SCALE:

DRAWING NO:

A03

DATE:

17/03/2025

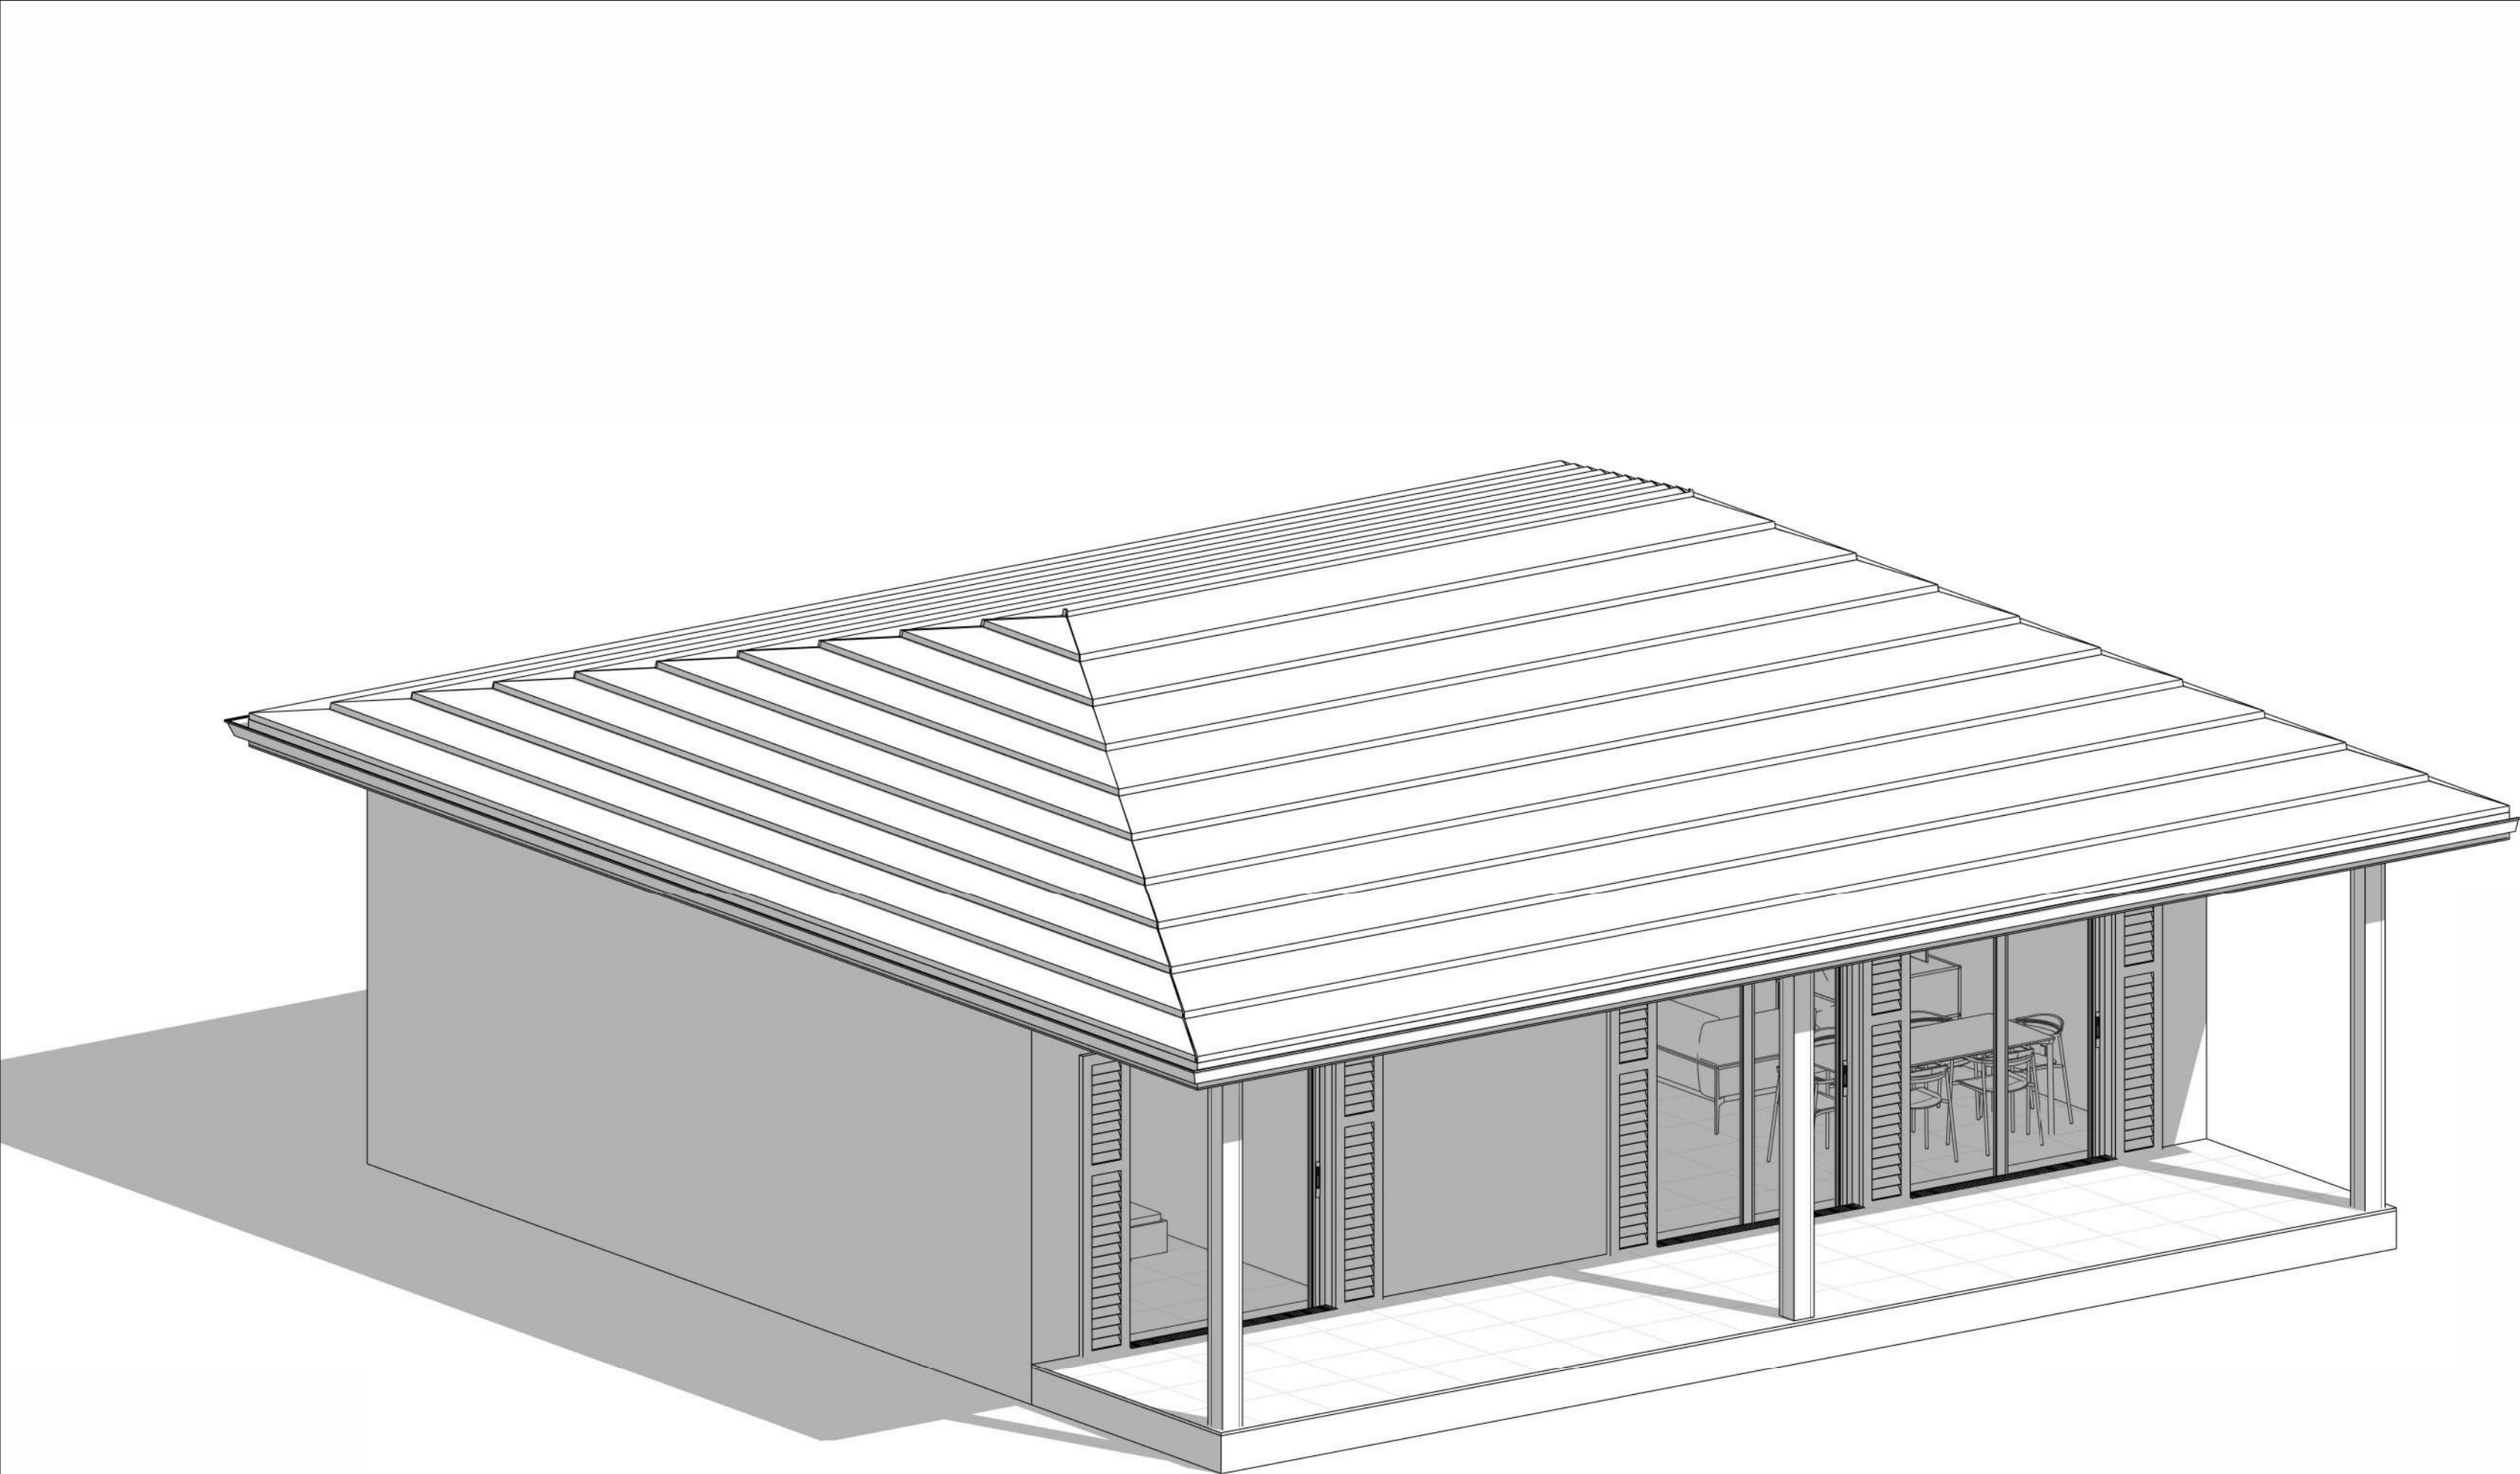

1. THESE DRAWINGS MUST BE CHECKED BY THE CUSTOMER OR CONTRACTOR PRIOR TO APPROVAL. ANY ERRORS OR OMISSIONS MUST BE REPORTED IN WRITING TO BAUHU PRIOR TO COMMENCEMENT OF CONSTRUCTION.
2. ARCHITECTURAL DRAWINGS SHOULD BE READ IN CONJUNCTION WITH STRUCTURAL DETAILING AND FABRICATION GENERAL ASSEMBLY DRAWINGS.
3. FOR CONSTRUCTION PURPOSES, USE ONLY THE LATEST APPROVED DRAWINGS LABELED 'ISSUED FOR CONSTRUCTION'.
4. DO NOT SCALE FROM THIS DRAWING.
5. THE COMPANY OPERATES USING METRIC DIMENSIONS AS THE PRINCIPAL DENOMINATION.
6. ALL CONCRETE WORKS ARE OUTSIDE OF THE SCOPE OF THE COMPANY. INFORMATION REGARDING SLAB DESIGN AND CONNECTIONS IN THESE DRAWINGS ARE INTENDED FOR GUIDENCE ONLY. FOUNDATION AND SLAB WORKS SHOULD BE DESIGNED AND APPROVED BY A LOCAL STRUCTURAL ENGINEER.
7. THE COMPANY RETAINS FULL TITLE AND OWNERSHIP OF THESE PLANS AND DESIGNS. ANY UNAUTHORISED USE, REPRODUCTION, OR DISTRIBUTION OF THESE PLANS, WHETHER IN WHOLE OR PART, IS EXPRESSLY PROHIBITED WITHOUT PRIOR WRITTEN CONSENT.
8. THE HYBRID STEEL FRAME CONSTRUCTION SYSTEM AND METHODOLOGY (PATENT PENDING) DESCRIBED IN THESE PLANS HAS BEEN DEVELOPED BY THE COMPANY AND IS SUBJECT TO A PROVISIONAL PATENT APPLICATION & ASSIGNMENT - US APPLICATION No. 63/722,841.

No.	Revision	Date
01	Moved walls under roof joists	13.03

ISSUED FOR:

Issued for information

Issued for client approval

Issued for fabrication

Issued for construction

Bahama Beach


DRAWING TITLE:
Building Axonometry

DRAWN BY:
Mladin Monica-Mihaela

SCALE:

DRAWING NO:
A04

DATE:
17/03/2025

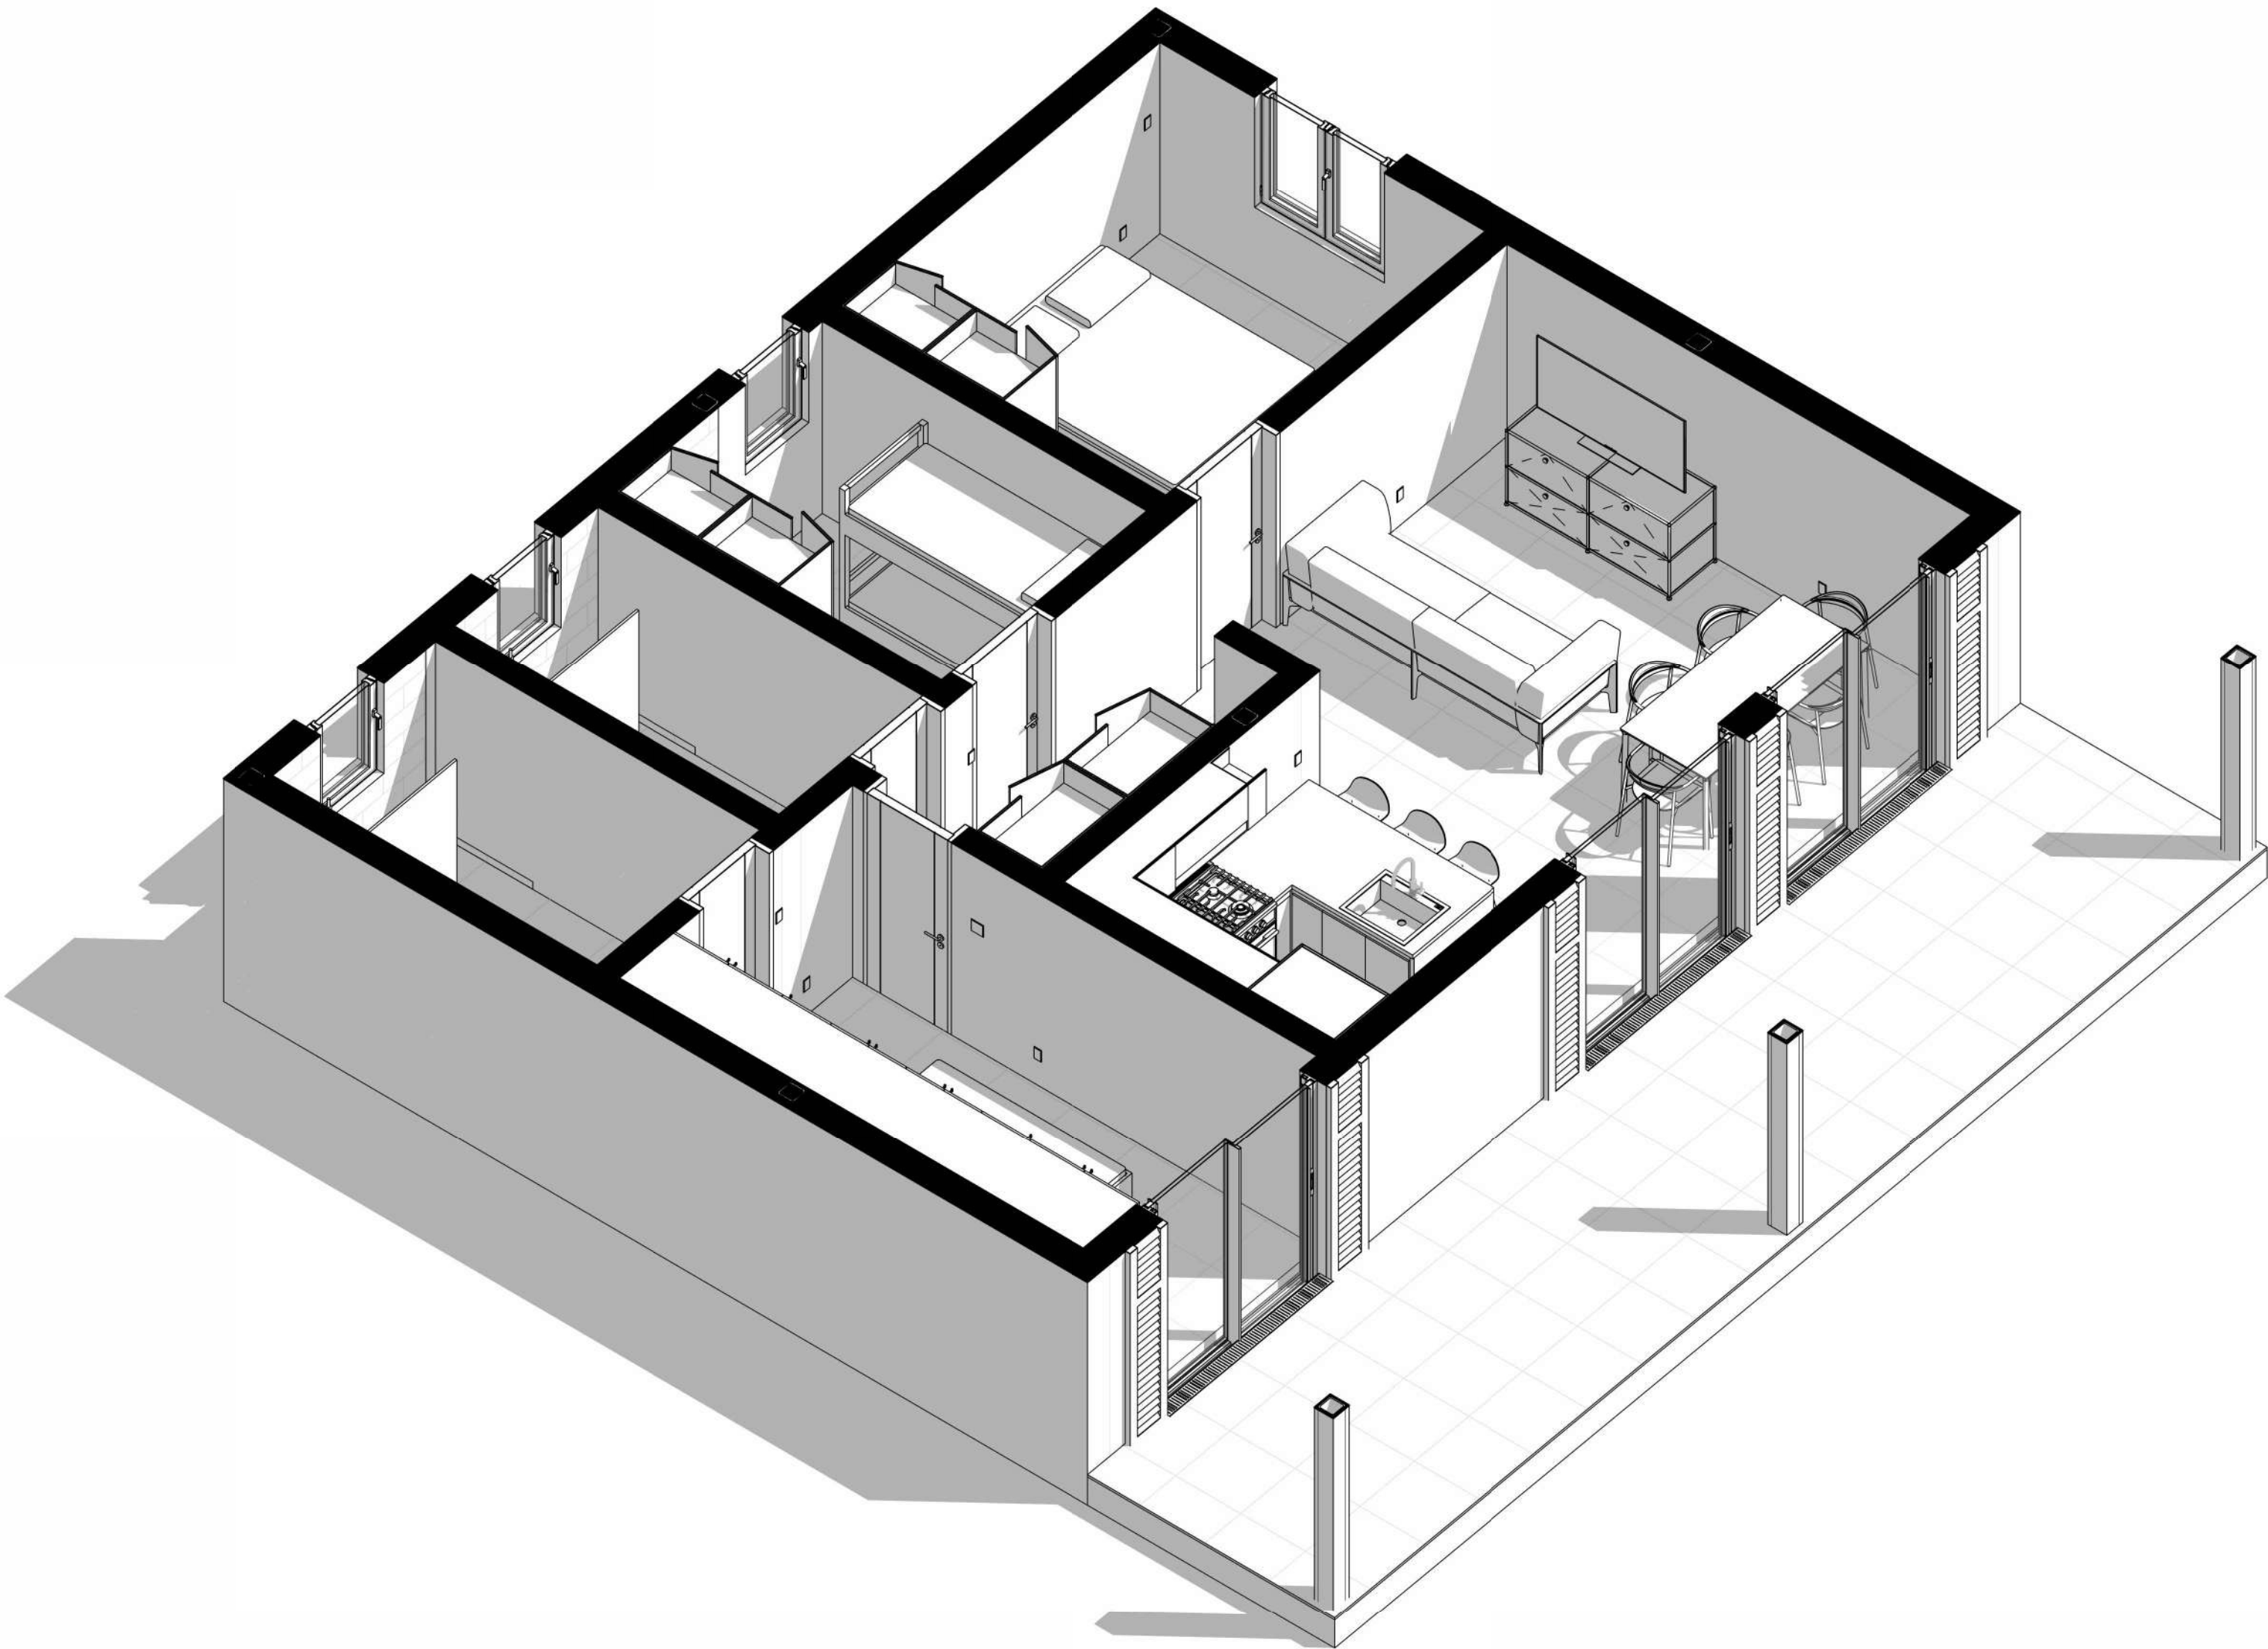

1. THESE DRAWINGS MUST BE CHECKED BY THE CUSTOMER OR CONTRACTOR PRIOR TO APPROVAL. ANY ERRORS OR OMISSIONS MUST BE REPORTED IN WRITING TO BAUHU PRIOR TO COMMENCEMENT OF CONSTRUCTION.
2. ARCHITECTURAL DRAWINGS SHOULD BE READ IN CONJUNCTION WITH STRUCTURAL DETAILING AND FABRICATION GENERAL ASSEMBLY DRAWINGS.
3. FOR CONSTRUCTION PURPOSES, USE ONLY THE LATEST APPROVED DRAWINGS LABELED 'ISSUED FOR CONSTRUCTION'.
4. DO NOT SCALE FROM THIS DRAWING.
5. THE COMPANY OPERATES USING METRIC DIMENSIONS AS THE PRINCIPAL DENOMINATION.
6. ALL CONCRETE WORKS ARE OUTSIDE OF THE SCOPE OF THE COMPANY. INFORMATION REGARDING SLAB DESIGN AND CONNECTIONS IN THESE DRAWINGS ARE INTENDED FOR GUIDENCE ONLY. FOUNDATION AND SLAB WORKS SHOULD BE DESIGNED AND APPROVED BY A LOCAL STRUCTURAL ENGINEER.
7. THE COMPANY RETAINS FULL TITLE AND OWNERSHIP OF THESE PLANS AND DESIGNS. ANY UNAUTHORISED USE, REPRODUCTION, OR DISTRIBUTION OF THESE PLANS, WHETHER IN WHOLE OR PART, IS EXPRESSLY PROHIBITED WITHOUT PRIOR WRITTEN CONSENT.
8. THE HYBRID STEEL FRAME CONSTRUCTION SYSTEM AND METHODOLOGY (PATENT PENDING) DESCRIBED IN THESE PLANS HAS BEEN DEVELOPED BY THE COMPANY AND IS SUBJECT TO A PROVISIONAL PATENT APPLICATION & ASSIGNMENT - US APPLICATION No. 63/722,841.

No.	Revision	Date
01	Moved walls under roof joists	13.03

ISSUED FOR:

Issued for information

Issued for client approval

Issued for fabrication

Issued for construction

Bahama Beach


DRAWING TITLE:
Floor Axonometry

DRAWN BY:
Mladin Monica-Mihaela

SCALE:

DRAWING NO:
A05

DATE:
17/03/2025

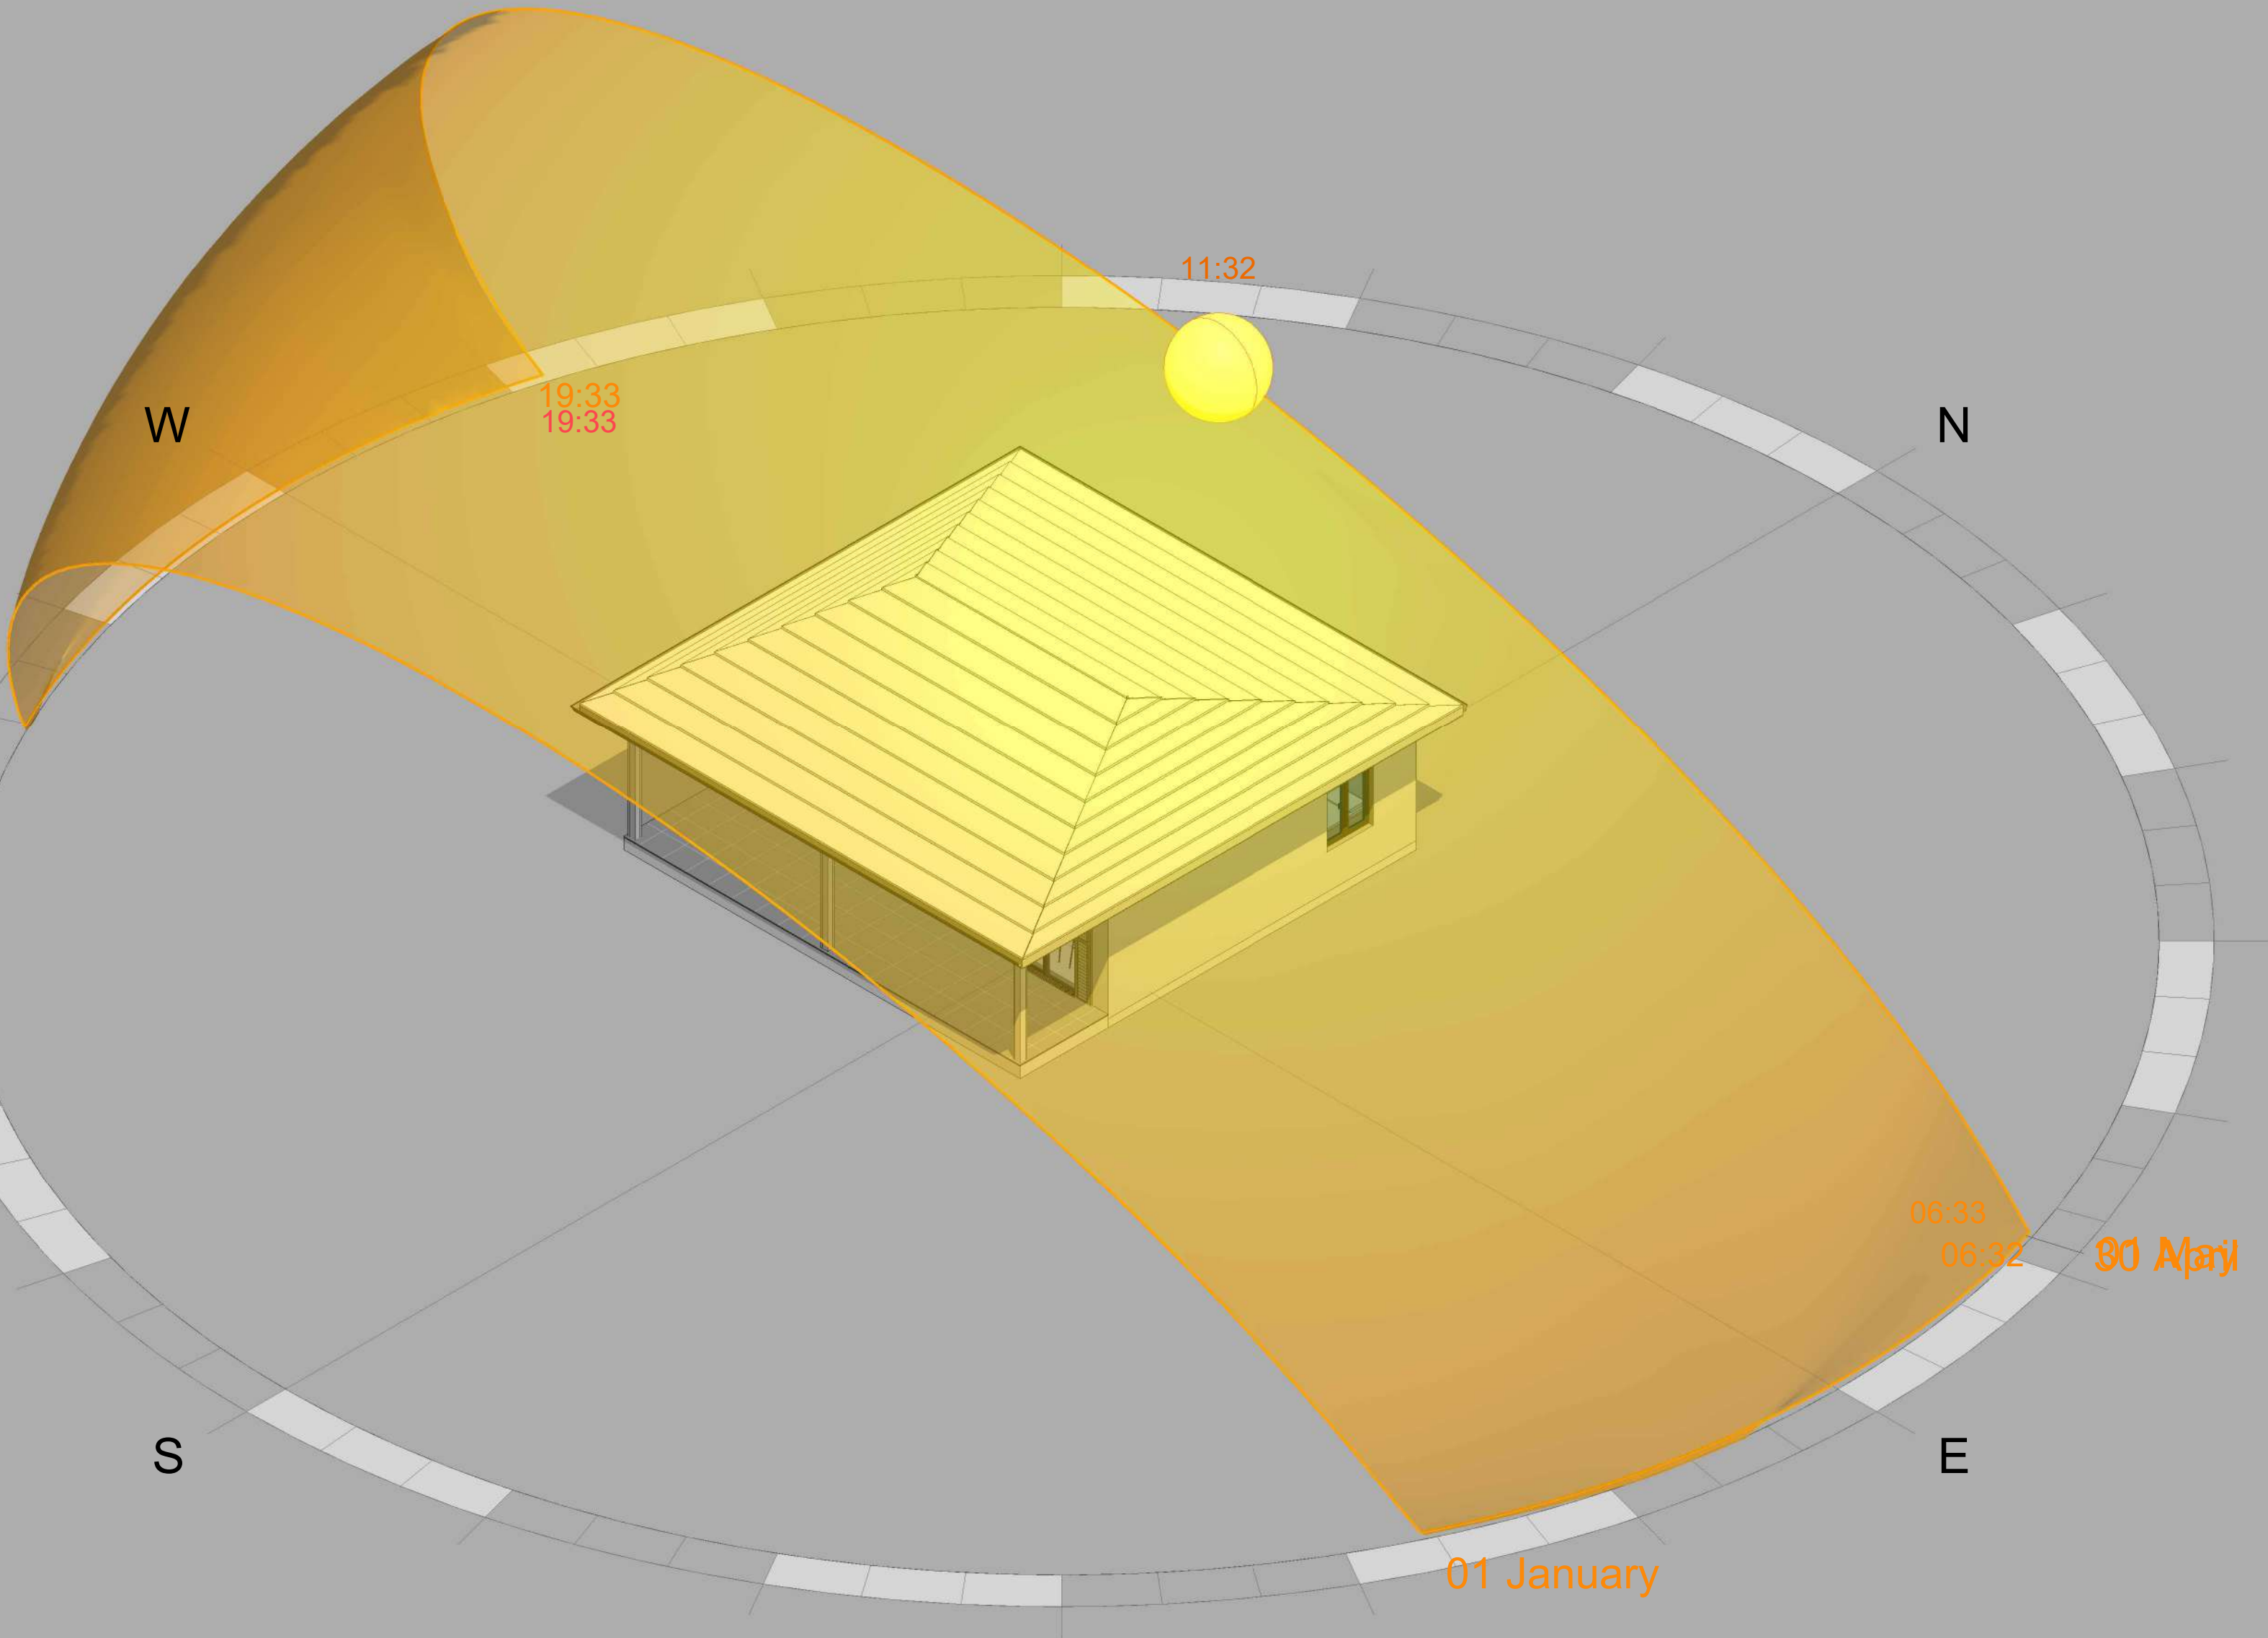

1. THESE DRAWINGS MUST BE CHECKED BY THE CUSTOMER OR CONTRACTOR PRIOR TO APPROVAL. ANY ERRORS OR OMISSIONS MUST BE REPORTED IN WRITING TO BAUHU PRIOR TO COMMENCEMENT OF CONSTRUCTION.
2. ARCHITECTURAL DRAWINGS SHOULD BE READ IN CONJUNCTION WITH STRUCTURAL DETAILING AND FABRICATION GENERAL ASSEMBLY DRAWINGS.
3. FOR CONSTRUCTION PURPOSES, USE ONLY THE LATEST APPROVED DRAWINGS LABELED 'ISSUED FOR CONSTRUCTION'.
4. DO NOT SCALE FROM THIS DRAWING.
5. THE COMPANY OPERATES USING METRIC DIMENSIONS AS THE PRINCIPAL DENOMINATION.
6. ALL CONCRETE WORKS ARE OUTSIDE OF THE SCOPE OF THE COMPANY. INFORMATION REGARDING SLAB DESIGN AND CONNECTIONS IN THESE DRAWINGS ARE INTENDED FOR GUIDENCE ONLY. FOUNDATION AND SLAB WORKS SHOULD BE DESIGNED AND APPROVED BY A LOCAL STRUCTURAL ENGINEER.
7. THE COMPANY RETAINS FULL TITLE AND OWNERSHIP OF THESE PLANS AND DESIGNS. ANY UNAUTHORISED USE, REPRODUCTION, OR DISTRIBUTION OF THESE PLANS, WHETHER IN WHOLE OR PART, IS EXPRESSLY PROHIBITED WITHOUT PRIOR WRITTEN CONSENT.
8. THE HYBRID STEEL FRAME CONSTRUCTION SYSTEM AND METHODOLOGY (PATENT PENDING) DESCRIBED IN THESE PLANS HAS BEEN DEVELOPED BY THE COMPANY AND IS SUBJECT TO A PROVISIONAL PATENT APPLICATION & ASSIGNMENT - US APPLICATION No. 63/722,841.

No.	Revision	Date
01	Moved walls under roof joists	13.03

- ISSUED FOR:
- ☒ Issued for information
 - ☐ Issued for client approval
 - ☐ Issued for fabrication
 - ☐ Issued for construction

Bahama Beach

DRAWING TITLE: Sun Analysis

DRAWN BY: Mladin Monica-Mihaela

SCALE:

DRAWING NO: A06

DATE: 17/03/2025

1. THESE DRAWINGS MUST BE CHECKED BY THE CUSTOMER OR CONTRACTOR PRIOR TO APPROVAL. ANY ERRORS OR OMISSIONS MUST BE REPORTED IN WRITING TO BAUHU PRIOR TO COMMENCEMENT OF CONSTRUCTION.
2. ARCHITECTURAL DRAWINGS SHOULD BE READ IN CONJUNCTION WITH STRUCTURAL DETAILING AND FABRICATION GENERAL ASSEMBLY DRAWINGS.
3. FOR CONSTRUCTION PURPOSES, USE ONLY THE LATEST APPROVED DRAWINGS LABELED 'ISSUED FOR CONSTRUCTION'.
4. DO NOT SCALE FROM THIS DRAWING.
5. THE COMPANY OPERATES USING METRIC DIMENSIONS AS THE PRINCIPAL DENOMINATION.
6. ALL CONCRETE WORKS ARE OUTSIDE OF THE SCOPE OF THE COMPANY. INFORMATION REGARDING SLAB DESIGN AND CONNECTIONS IN THESE DRAWINGS ARE INTENDED FOR GUIDENCE ONLY. FOUNDATION AND SLAB WORKS SHOULD BE DESIGNED AND APPROVED BY A LOCAL STRUCTURAL ENGINEER.
7. THE COMPANY RETAINS FULL TITLE AND OWNERSHIP OF THESE PLANS AND DESIGNS. ANY UNAUTHORISED USE, REPRODUCTION, OR DISTRIBUTION OF THESE PLANS, WHETHER IN WHOLE OR PART, IS EXPRESSLY PROHIBITED WITHOUT PRIOR WRITTEN CONSENT.
8. THE HYBRID STEEL FRAME CONSTRUCTION SYSTEM AND METHODOLOGY (PATENT PENDING) DESCRIBED IN THESE PLANS HAS BEEN DEVELOPED BY THE COMPANY AND IS SUBJECT TO A PROVISIONAL PATENT APPLICATION & ASSIGNMENT - US APPLICATION No. 63/722,841.

No.	Revision	Date
01	Moved walls under roof joists	13.03

ISSUED FOR:

Issued for information

Issued for client approval

Issued for fabrication

Issued for construction

Bahama Beach

DRAWING TITLE:

Site Plan

DRAWN BY:

Mladin Monica-Mihaela

SCALE:

1 : 50

DRAWING NO:

A07


DATE:

17/03/2025

Note:

- Foundation details, slab plans and layout are provided for information only. Refer to structural engineering plans for layout, connection details, stud embedment and edge distances. RC pier and footing to be designed by a local structural engineer according to site conditions.
- All groundworks, landscape and hardscape, fencing, footings, foundation and floor slab works, cisterns and sceptic tanks are the responsibility of the owner. Building components are provided on the assumption that the site is prepared and an adequate foundation approved by a competent local structural engineer, has been provided. All services and sub-slab conduits should be completed finishing in a perfectly square and level concrete platform to enable the building erection.

Room Schedule				
No.	Room Name	Sq. Meter	Sq. Feet	Perimeter
1	Living Room+Kitchen	29 m²	317.2 ft²	29468
2	Bedroom 1	11 m²	119.2 ft²	13752
3	En-Suite Bathroom	5 m²	58.4 ft²	9627
4	Main Bathroom	5 m²	51.5 ft²	9199
5	Bedroom 3	7 m²	73.6 ft²	10563
6	Bedroom 2	11 m²	114.1 ft²	13063
8	Terrace - Exterior	23 m²	251.4 ft²	25612
Grand total		92 m²	985.4 ft²	

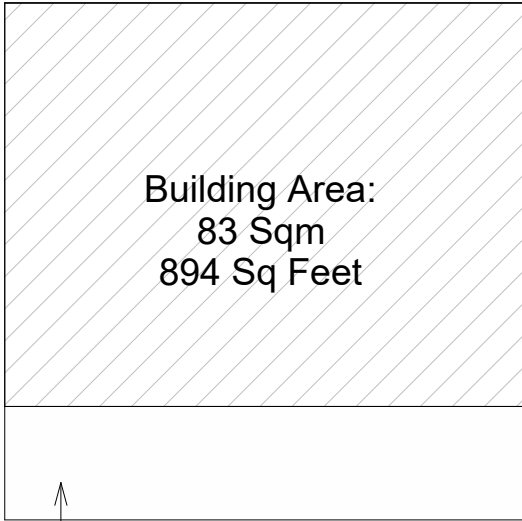


Terrace Area:
22 Sqm
240 Sq Feet

Acces

Note:

- Freestanding furniture and equipment are shown for illustrative purposes only. Renderings and reference images are for guidance only.
- Artisanal timber and carpentry requirements such as fretwork, architectural timber finishes, baseboards, decorative railings, deck and pergola structures, shade louvres, interior stairs and hand railing are to be provided by others.
- Railings and balustrades will be provided by others. Drawings are made for design purposes only. Refer to structural design drawings for post fixing dimensions.
- External HRS columns will be provided assuming a 50mm (2") height drop between interior concrete slab and exterior terrace concrete slab unless site conditions dictate otherwise.
- Final exterior slab height to be determined by the contractor. Internal floor screed and waterproofing membrane is to be supplied by the contractor.
- Contractors should ensure a correct fall is applied to external tiled terrace areas to facilitate rainwater drainage.
- Contractors should read these drawings in conjunction with structural engineering design drawings.
- Foundation details, slab plans and layout are provided for information only. Refer to structural engineering plans for layout, connection details, stud embedment and edge distances. RC pier and footing to be designed by a local structural engineer according to site conditions.
- All groundworks, landscape and hardscape, fencing, footings, foundation and floor slab works, cisterns and sceptic tanks are the responsibility of the owner. Building components are provided on the assumption that the site is prepared and an adequate foundation approved by a competent local structural engineer, has been provided. All services and sub-slab conduits should be completed finishing in a perfectly square and level concrete platform to enable the building erection.

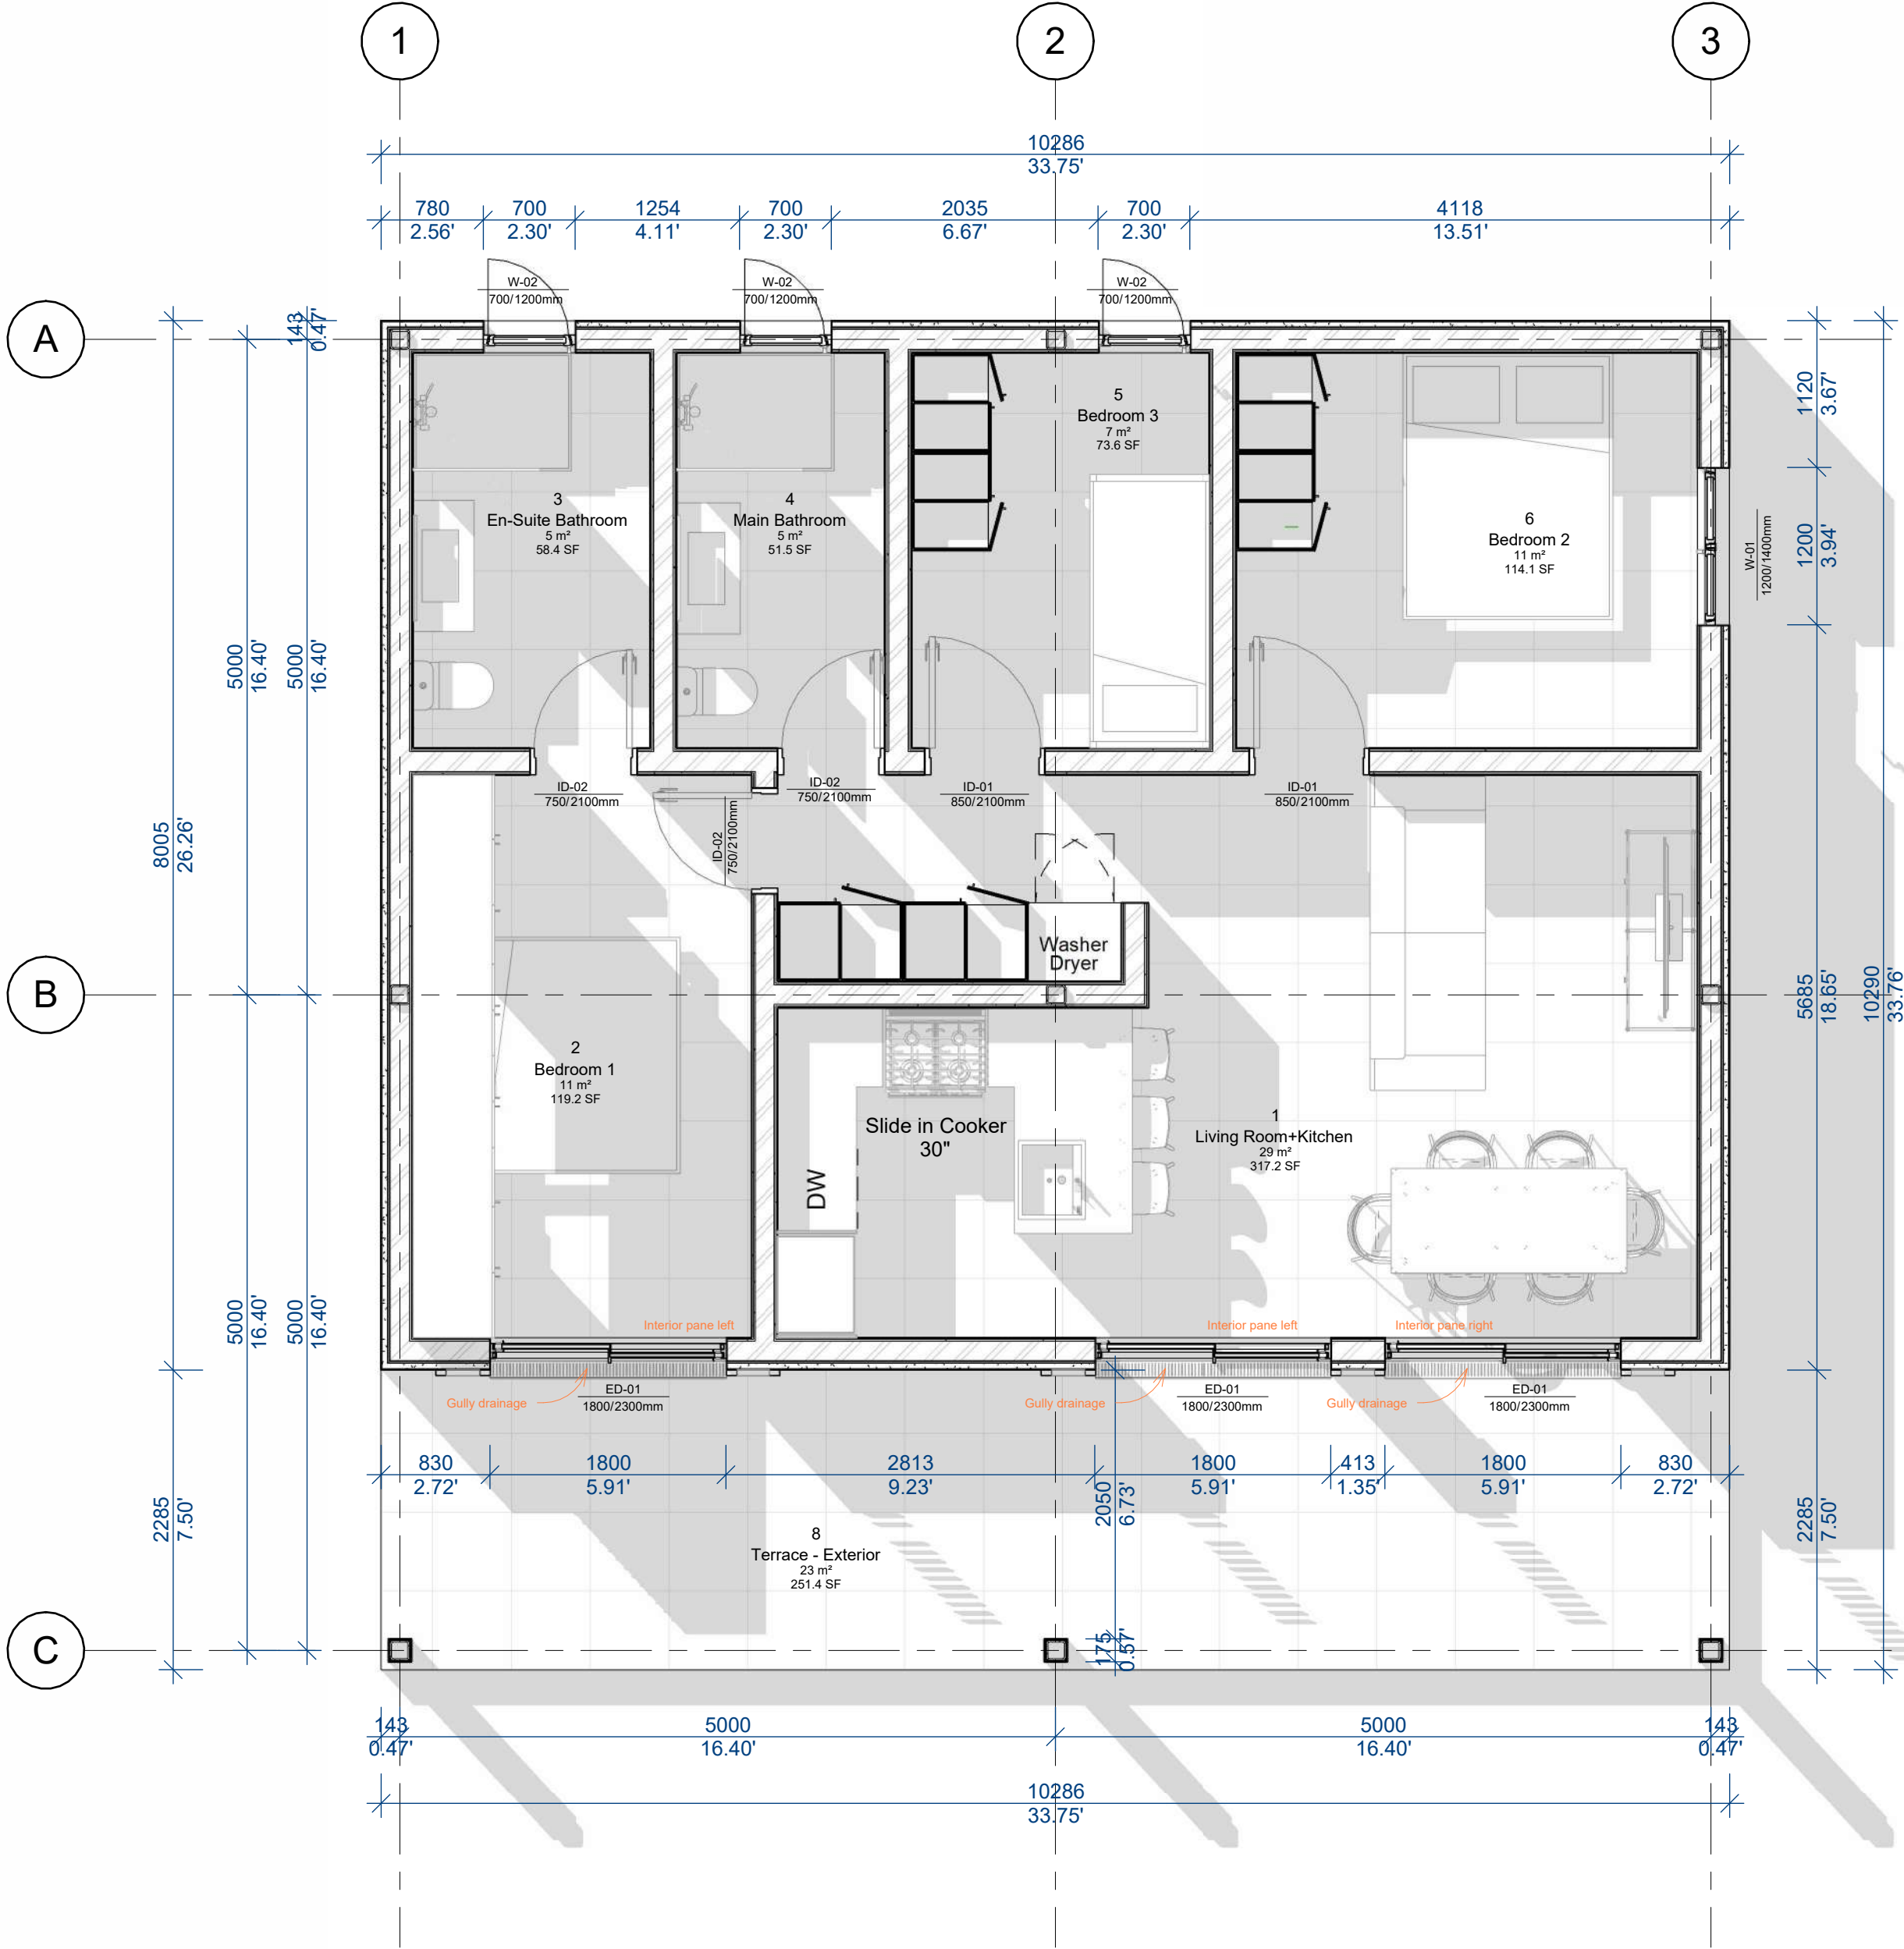

- THESE DRAWINGS MUST BE CHECKED BY THE CUSTOMER OR CONTRACTOR PRIOR TO APPROVAL. ANY ERRORS OR OMISSIONS MUST BE REPORTED IN WRITING TO BAUHU PRIOR TO COMMENCEMENT OF CONSTRUCTION.
- ARCHITECTURAL DRAWINGS SHOULD BE READ IN CONJUNCTION WITH STRUCTURAL DETAILING AND FABRICATION GENERAL ASSEMBLY DRAWINGS.
- FOR CONSTRUCTION PURPOSES, USE ONLY THE LATEST APPROVED DRAWINGS LABELED 'ISSUED FOR CONSTRUCTION'.
- DO NOT SCALE FROM THIS DRAWING.
- THE COMPANY OPERATES USING METRIC DIMENSIONS AS THE PRINCIPAL DENOMINATION.
- ALL CONCRETE WORKS ARE OUTSIDE OF THE SCOPE OF THE COMPANY. INFORMATION REGARDING SLAB DESIGN AND CONNECTIONS IN THESE DRAWINGS ARE INTENDED FOR GUIDANCE ONLY. FOUNDATION AND SLAB WORKS SHOULD BE DESIGNED AND APPROVED BY A LOCAL STRUCTURAL ENGINEER.
- THE COMPANY RETAINS FULL TITLE AND OWNERSHIP OF THESE PLANS AND DESIGNS. ANY UNAUTHORISED USE, REPRODUCTION, OR DISTRIBUTION OF THESE PLANS, WHETHER IN WHOLE OR PART, IS EXPRESSLY PROHIBITED WITHOUT PRIOR WRITTEN CONSENT.
- THE HYBRID STEEL FRAME CONSTRUCTION SYSTEM AND METHODOLOGY (PATENT PENDING) DESCRIBED IN THESE PLANS HAS BEEN DEVELOPED BY THE COMPANY AND IS SUBJECT TO A PROVISIONAL PATENT APPLICATION & ASSIGNMENT - US APPLICATION No. 63/722,841.

No.	Revision	Date
01	Moved walls under roof joists	13.03

ISSUED FOR:

Issued for information

Issued for client approval

Issued for fabrication

Issued for construction

Bahama Beach

DRAWING TITLE:
Ground Floor Plan

DRAWN BY:
Mladin Monica-Mihaela

SCALE:
As indicated

DRAWING NO:
A08

DATE:
17/03/2025

1. THESE DRAWINGS MUST BE CHECKED BY THE CUSTOMER OR CONTRACTOR PRIOR TO APPROVAL. ANY ERRORS OR OMISSIONS MUST BE REPORTED IN WRITING TO BAUHU PRIOR TO COMMENCEMENT OF CONSTRUCTION.
2. ARCHITECTURAL DRAWINGS SHOULD BE READ IN CONJUNCTION WITH STRUCTURAL DETAILING AND FABRICATION GENERAL ASSEMBLY DRAWINGS.
3. FOR CONSTRUCTION PURPOSES, USE ONLY THE LATEST APPROVED DRAWINGS LABELED 'ISSUED FOR CONSTRUCTION'.
4. DO NOT SCALE FROM THIS DRAWING.
5. THE COMPANY OPERATES USING METRIC DIMENSIONS AS THE PRINCIPAL DENOMINATION.
6. ALL CONCRETE WORKS ARE OUTSIDE OF THE SCOPE OF THE COMPANY. INFORMATION REGARDING SLAB DESIGN AND CONNECTIONS IN THESE DRAWINGS ARE INTENDED FOR GUIDENCE ONLY. FOUNDATION AND SLAB WORKS SHOULD BE DESIGNED AND APPROVED BY A LOCAL STRUCTURAL ENGINEER.
7. THE COMPANY RETAINS FULL TITLE AND OWNERSHIP OF THESE PLANS AND DESIGNS. ANY UNAUTHORISED USE, REPRODUCTION, OR DISTRIBUTION OF THESE PLANS, WHETHER IN WHOLE OR PART, IS EXPRESSLY PROHIBITED WITHOUT PRIOR WRITTEN CONSENT.
8. THE HYBRID STEEL FRAME CONSTRUCTION SYSTEM AND METHODOLOGY (PATENT PENDING) DESCRIBED IN THESE PLANS HAS BEEN DEVELOPED BY THE COMPANY AND IS SUBJECT TO A PROVISIONAL PATENT APPLICATION & ASSIGNMENT - US APPLICATION No. 63/722,841.

No.	Revision	Date
01	Moved walls under roof joists	13.03

ISSUED FOR:

Issued for information

Issued for client approval

Issued for fabrication

Issued for construction

Bahama Beach


DRAWING TITLE:
Front Elevation

DRAWN BY:
Mladin Monica-Mihaela

SCALE:
1 : 40

DRAWING NO:
A09

DATE:
17/03/2025

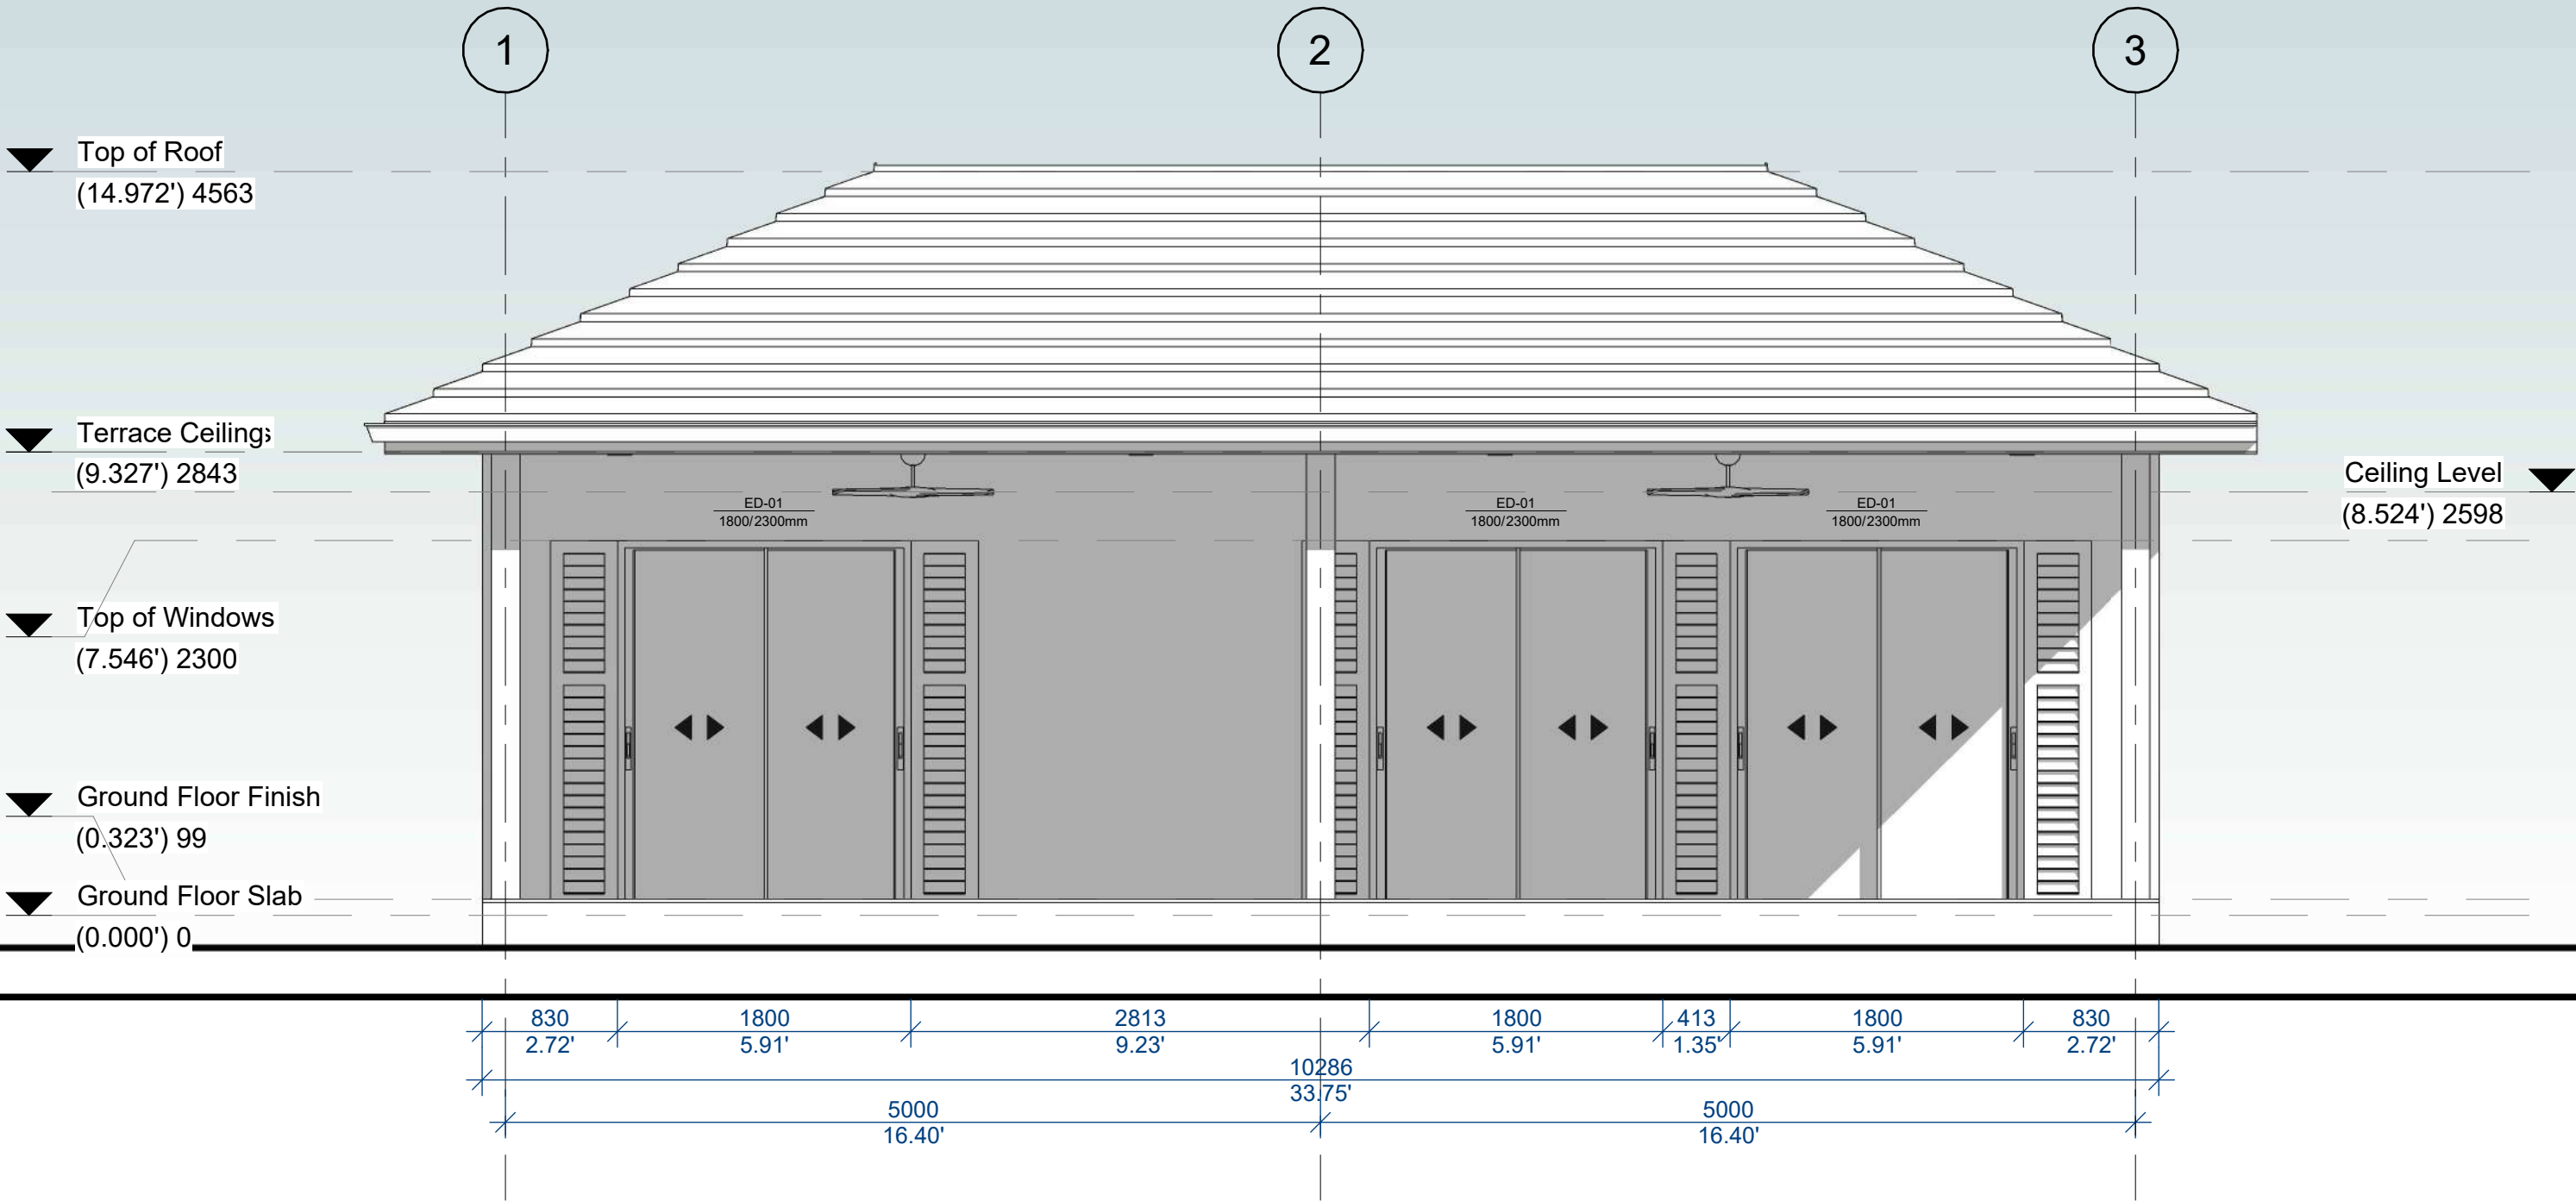

1. THESE DRAWINGS MUST BE CHECKED BY THE CUSTOMER OR CONTRACTOR PRIOR TO APPROVAL. ANY ERRORS OR OMISSIONS MUST BE REPORTED IN WRITING TO BAUHU PRIOR TO COMMENCEMENT OF CONSTRUCTION.
2. ARCHITECTURAL DRAWINGS SHOULD BE READ IN CONJUNCTION WITH STRUCTURAL DETAILING AND FABRICATION GENERAL ASSEMBLY DRAWINGS.
3. FOR CONSTRUCTION PURPOSES, USE ONLY THE LATEST APPROVED DRAWINGS LABELED 'ISSUED FOR CONSTRUCTION'.
4. DO NOT SCALE FROM THIS DRAWING.
5. THE COMPANY OPERATES USING METRIC DIMENSIONS AS THE PRINCIPAL DENOMINATION.
6. ALL CONCRETE WORKS ARE OUTSIDE OF THE SCOPE OF THE COMPANY. INFORMATION REGARDING SLAB DESIGN AND CONNECTIONS IN THESE DRAWINGS ARE INTENDED FOR GUIDENCE ONLY. FOUNDATION AND SLAB WORKS SHOULD BE DESIGNED AND APPROVED BY A LOCAL STRUCTURAL ENGINEER.
7. THE COMPANY RETAINS FULL TITLE AND OWNERSHIP OF THESE PLANS AND DESIGNS. ANY UNAUTHORISED USE, REPRODUCTION, OR DISTRIBUTION OF THESE PLANS, WHETHER IN WHOLE OR PART, IS EXPRESSLY PROHIBITED WITHOUT PRIOR WRITTEN CONSENT.
8. THE HYBRID STEEL FRAME CONSTRUCTION SYSTEM AND METHODOLOGY (PATENT PENDING) DESCRIBED IN THESE PLANS HAS BEEN DEVELOPED BY THE COMPANY AND IS SUBJECT TO A PROVISIONAL PATENT APPLICATION & ASSIGNMENT - US APPLICATION No. 63/722,841.

No.	Revision	Date
01	Moved walls under roof joists	13.03

ISSUED FOR:

Issued for information

Issued for client approval

Issued for fabrication

Issued for construction

Bahama Beach


DRAWING TITLE:
Rear Elevation

DRAWN BY:
Mladin Monica-Mihaela

SCALE:
1 : 40

DRAWING NO:
A10

DATE:
17/03/2025

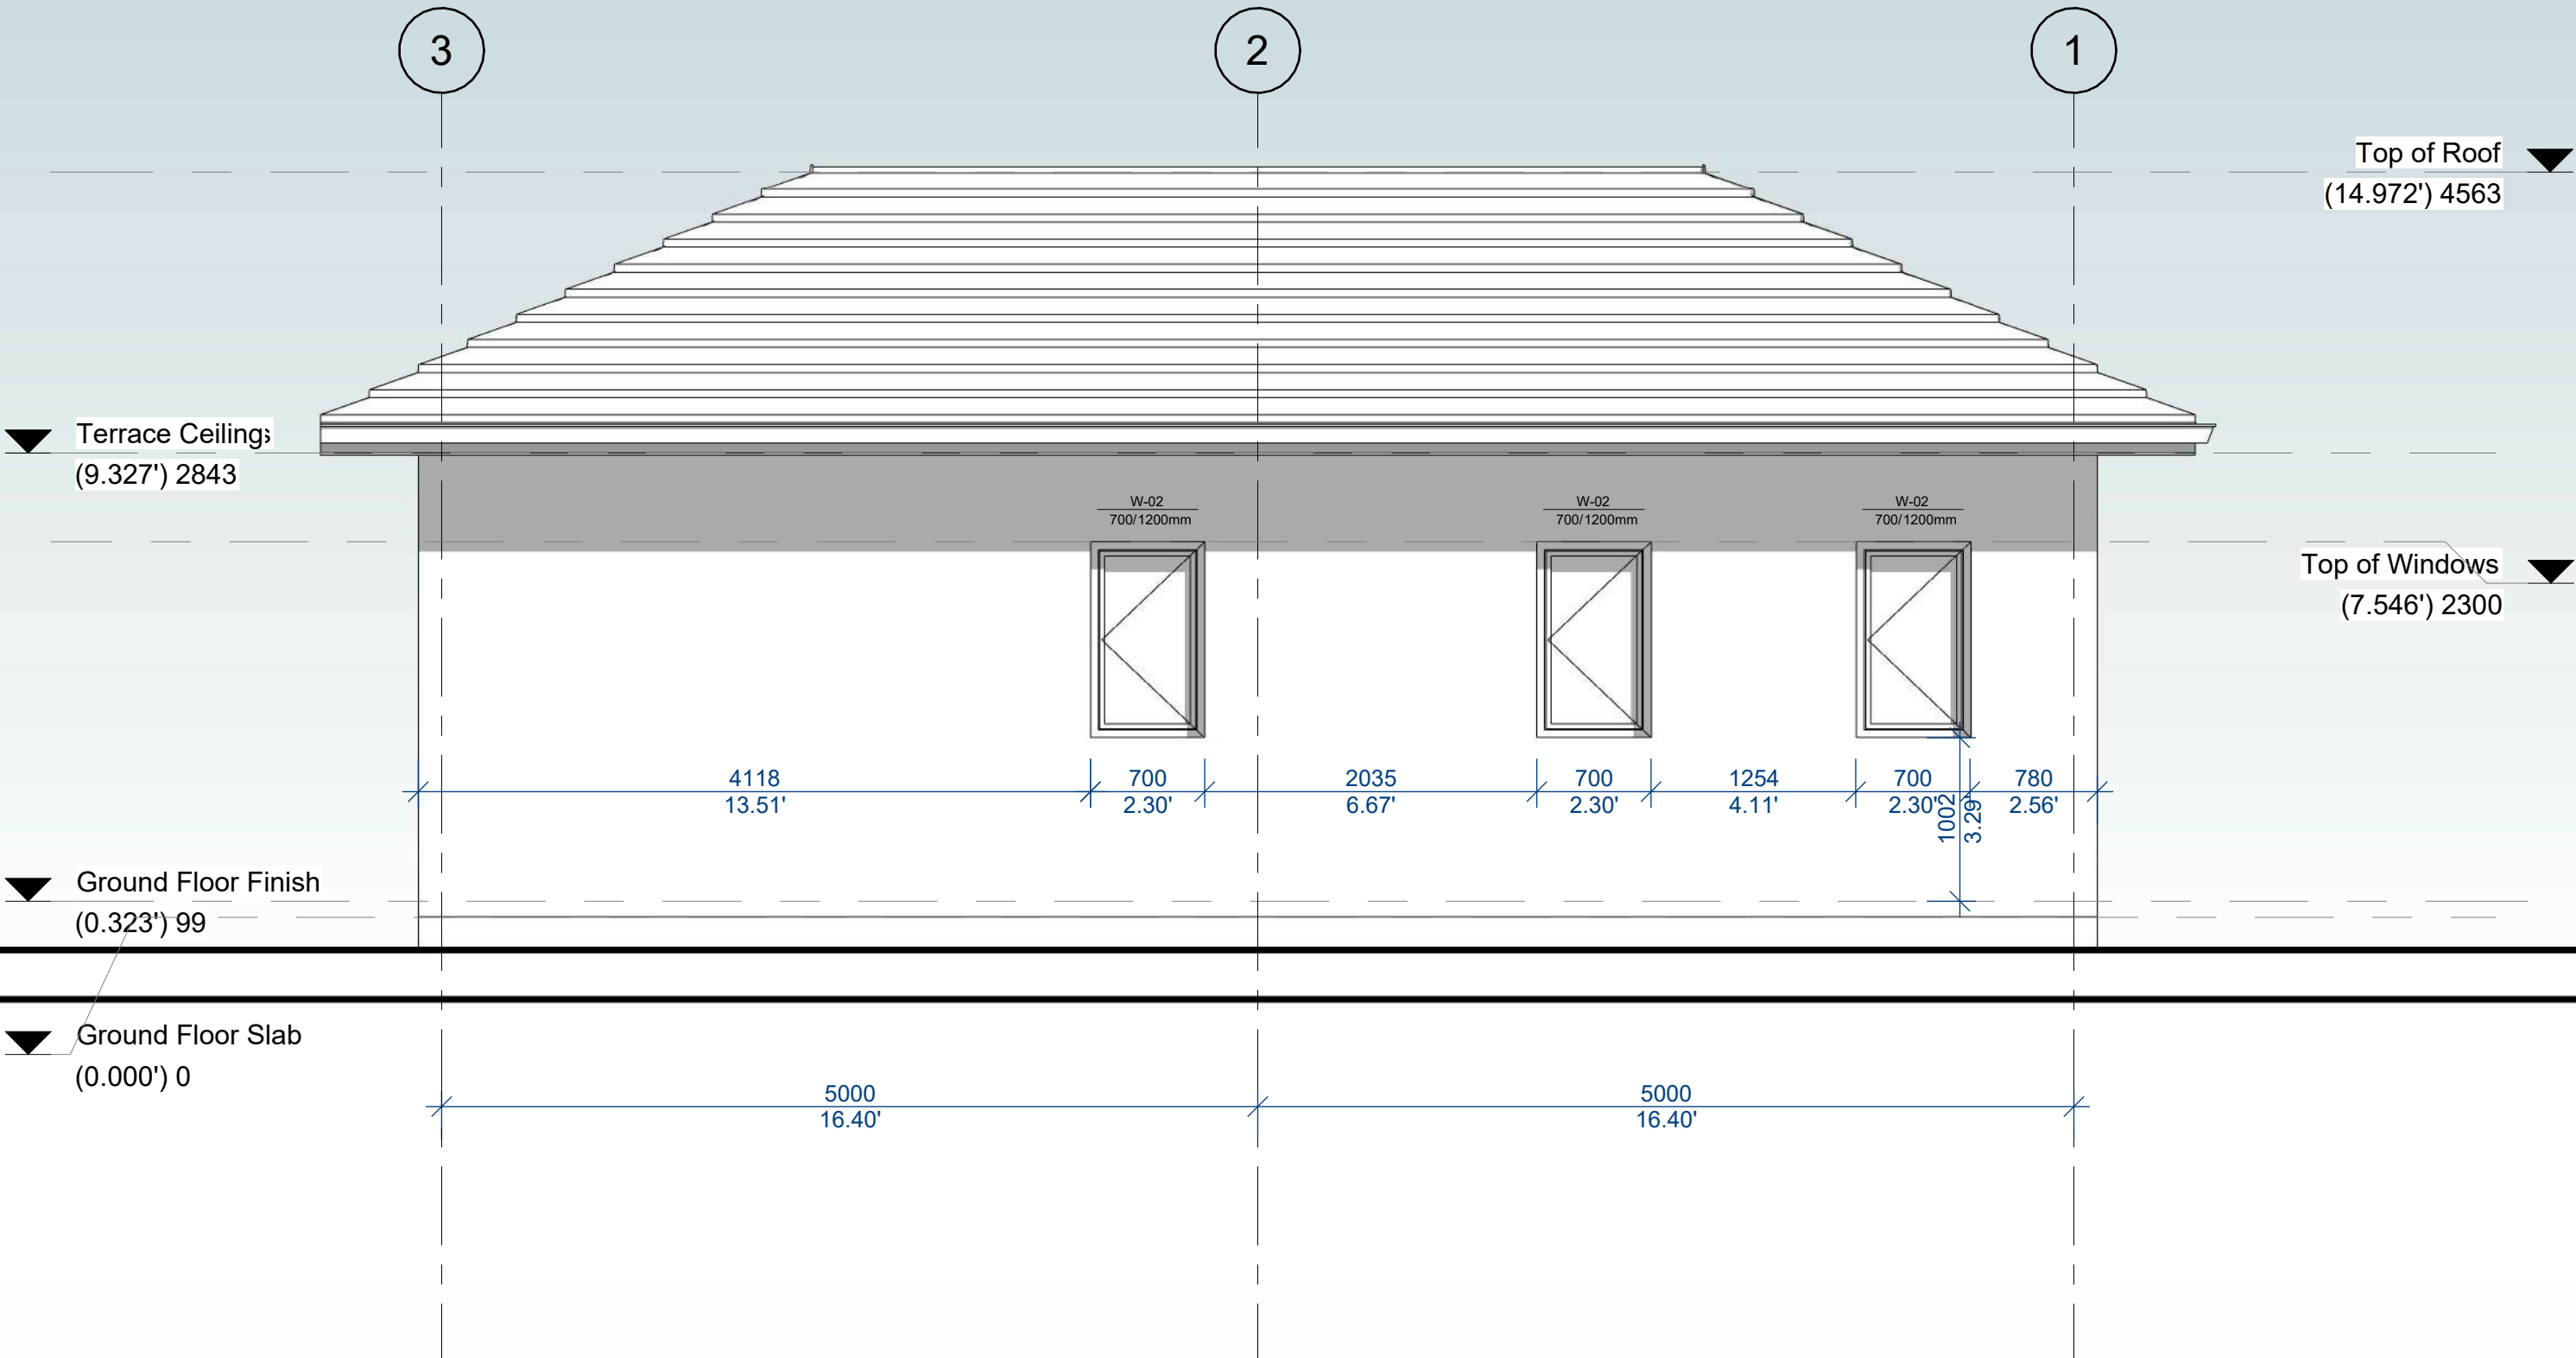

1. THESE DRAWINGS MUST BE CHECKED BY THE CUSTOMER OR CONTRACTOR PRIOR TO APPROVAL. ANY ERRORS OR OMISSIONS MUST BE REPORTED IN WRITING TO BAUHU PRIOR TO COMMENCEMENT OF CONSTRUCTION.
2. ARCHITECTURAL DRAWINGS SHOULD BE READ IN CONJUNCTION WITH STRUCTURAL DETAILING AND FABRICATION GENERAL ASSEMBLY DRAWINGS.
3. FOR CONSTRUCTION PURPOSES, USE ONLY THE LATEST APPROVED DRAWINGS LABELED 'ISSUED FOR CONSTRUCTION'.
4. DO NOT SCALE FROM THIS DRAWING.
5. THE COMPANY OPERATES USING METRIC DIMENSIONS AS THE PRINCIPAL DENOMINATION.
6. ALL CONCRETE WORKS ARE OUTSIDE OF THE SCOPE OF THE COMPANY. INFORMATION REGARDING SLAB DESIGN AND CONNECTIONS IN THESE DRAWINGS ARE INTENDED FOR GUIDENCE ONLY. FOUNDATION AND SLAB WORKS SHOULD BE DESIGNED AND APPROVED BY A LOCAL STRUCTURAL ENGINEER.
7. THE COMPANY RETAINS FULL TITLE AND OWNERSHIP OF THESE PLANS AND DESIGNS. ANY UNAUTHORISED USE, REPRODUCTION, OR DISTRIBUTION OF THESE PLANS, WHETHER IN WHOLE OR PART, IS EXPRESSLY PROHIBITED WITHOUT PRIOR WRITTEN CONSENT.
8. THE HYBRID STEEL FRAME CONSTRUCTION SYSTEM AND METHODOLOGY (PATENT PENDING) DESCRIBED IN THESE PLANS HAS BEEN DEVELOPED BY THE COMPANY AND IS SUBJECT TO A PROVISIONAL PATENT APPLICATION & ASSIGNMENT - US APPLICATION No. 63/722,841.

No.	Revision	Date
01	Moved walls under roof joists	13.03

ISSUED FOR:

Issued for information

Issued for client approval

Issued for fabrication

Issued for construction

Bahama Beach


DRAWING TITLE:
Left Elevation

DRAWN BY:
Mladin Monica-Mihaela

SCALE:
1 : 40

DRAWING NO:
A11

DATE:
17/03/2025

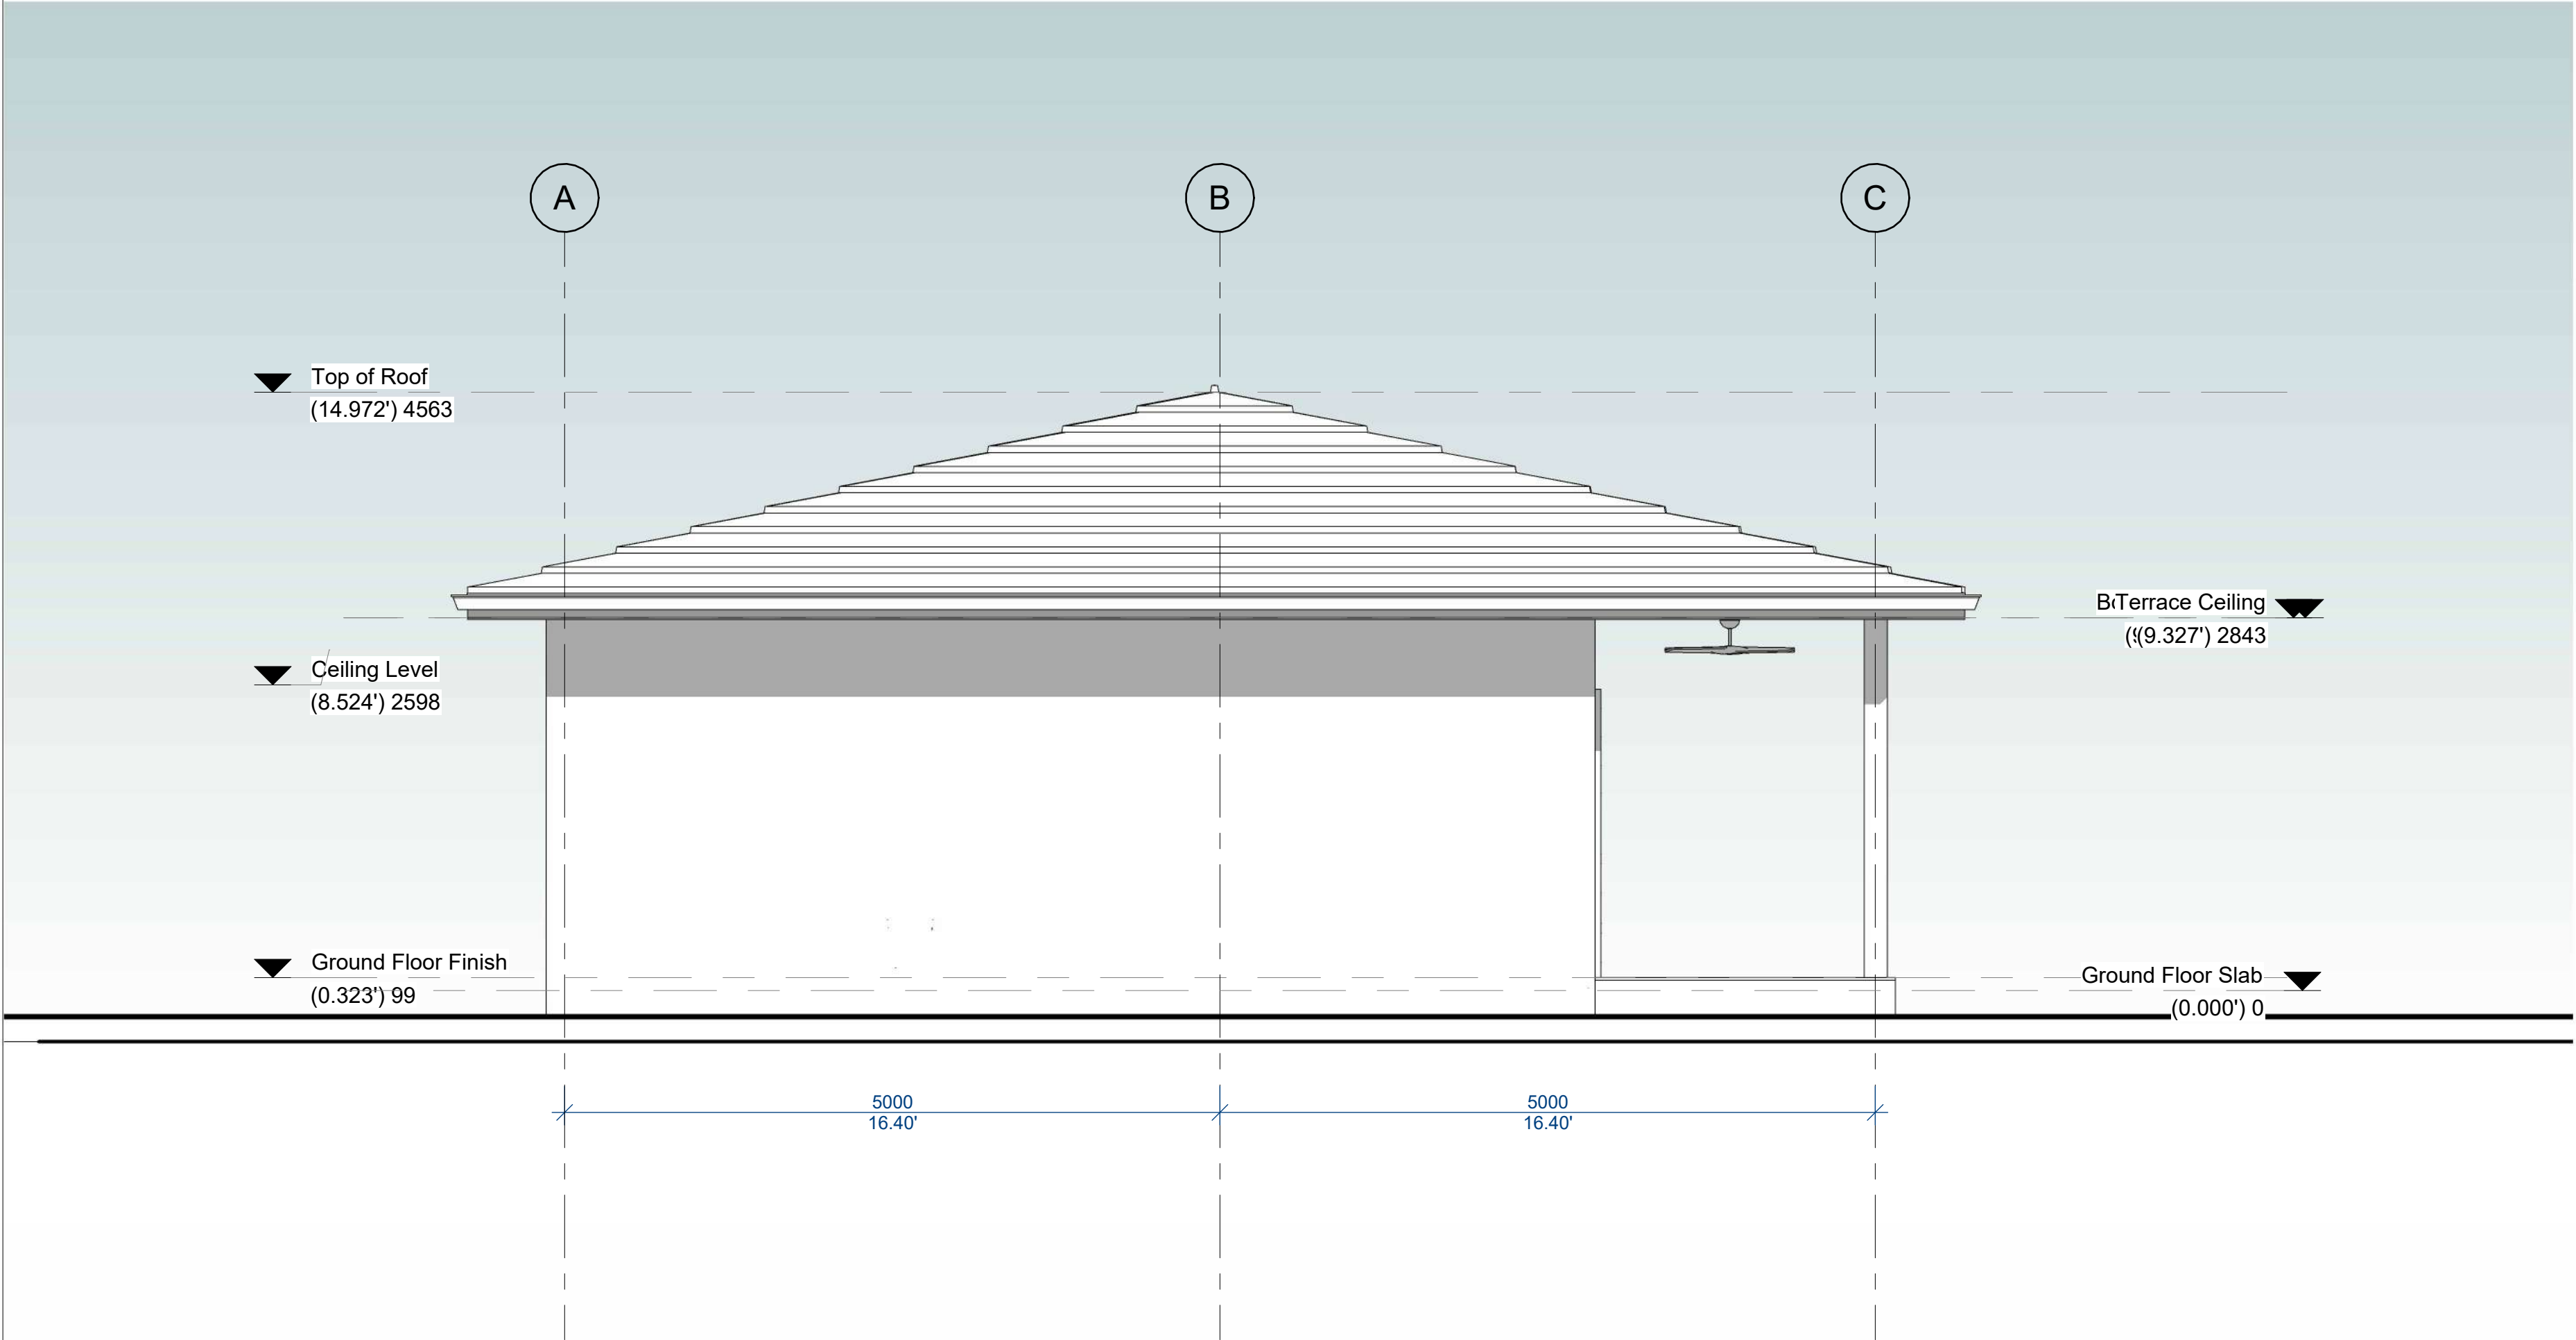

1. THESE DRAWINGS MUST BE CHECKED BY THE CUSTOMER OR CONTRACTOR PRIOR TO APPROVAL. ANY ERRORS OR OMISSIONS MUST BE REPORTED IN WRITING TO BAUHU PRIOR TO COMMENCEMENT OF CONSTRUCTION.
2. ARCHITECTURAL DRAWINGS SHOULD BE READ IN CONJUNCTION WITH STRUCTURAL DETAILING AND FABRICATION GENERAL ASSEMBLY DRAWINGS.
3. FOR CONSTRUCTION PURPOSES, USE ONLY THE LATEST APPROVED DRAWINGS LABELED 'ISSUED FOR CONSTRUCTION'.
4. DO NOT SCALE FROM THIS DRAWING.
5. THE COMPANY OPERATES USING METRIC DIMENSIONS AS THE PRINCIPAL DENOMINATION.
6. ALL CONCRETE WORKS ARE OUTSIDE OF THE SCOPE OF THE COMPANY. INFORMATION REGARDING SLAB DESIGN AND CONNECTIONS IN THESE DRAWINGS ARE INTENDED FOR GUIDENCE ONLY. FOUNDATION AND SLAB WORKS SHOULD BE DESIGNED AND APPROVED BY A LOCAL STRUCTURAL ENGINEER.
7. THE COMPANY RETAINS FULL TITLE AND OWNERSHIP OF THESE PLANS AND DESIGNS. ANY UNAUTHORISED USE, REPRODUCTION, OR DISTRIBUTION OF THESE PLANS, WHETHER IN WHOLE OR PART, IS EXPRESSLY PROHIBITED WITHOUT PRIOR WRITTEN CONSENT.
8. THE HYBRID STEEL FRAME CONSTRUCTION SYSTEM AND METHODOLOGY (PATENT PENDING) DESCRIBED IN THESE PLANS HAS BEEN DEVELOPED BY THE COMPANY AND IS SUBJECT TO A PROVISIONAL PATENT APPLICATION & ASSIGNMENT - US APPLICATION No. 63/722,841.

No.	Revision	Date
01	Moved walls under roof joists	13.03

ISSUED FOR:

Issued for information

Issued for client approval

Issued for fabrication

Issued for construction

Bahama Beach


DRAWING TITLE:
Right Elevation

DRAWN BY:
Mladin Monica-Mihaela

SCALE:
1 : 40

DRAWING NO:
A12

DATE:
17/03/2025

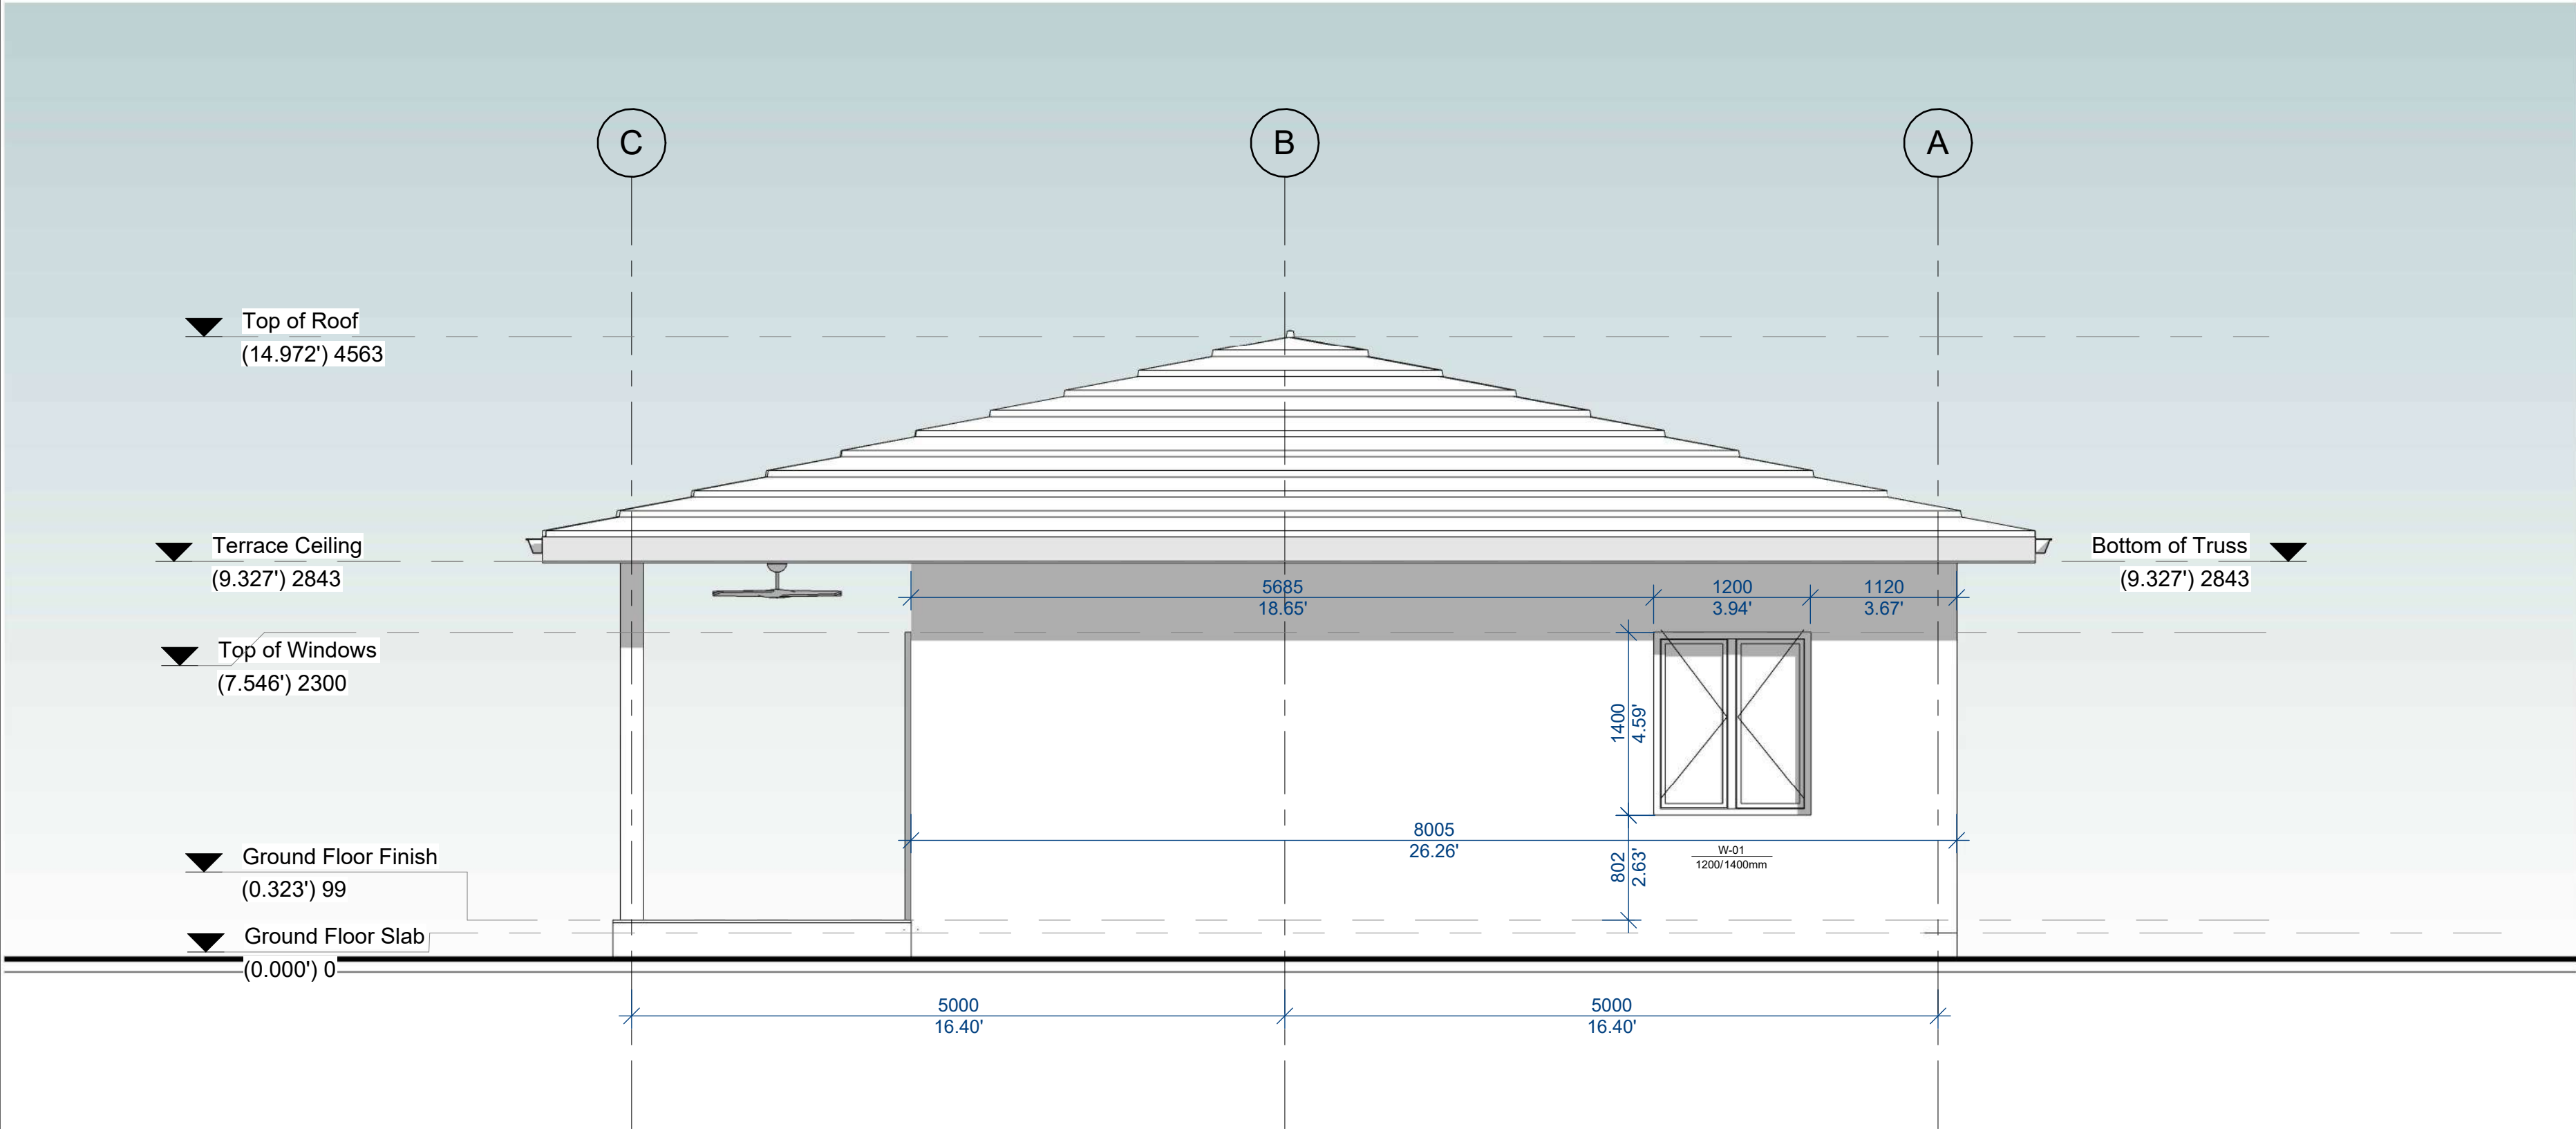

1. THESE DRAWINGS MUST BE CHECKED BY THE CUSTOMER OR CONTRACTOR PRIOR TO APPROVAL. ANY ERRORS OR OMISSIONS MUST BE REPORTED IN WRITING TO BAUHU PRIOR TO COMMENCEMENT OF CONSTRUCTION.
2. ARCHITECTURAL DRAWINGS SHOULD BE READ IN CONJUNCTION WITH STRUCTURAL DETAILING AND FABRICATION GENERAL ASSEMBLY DRAWINGS.
3. FOR CONSTRUCTION PURPOSES, USE ONLY THE LATEST APPROVED DRAWINGS LABELED 'ISSUED FOR CONSTRUCTION'.
4. DO NOT SCALE FROM THIS DRAWING.
5. THE COMPANY OPERATES USING METRIC DIMENSIONS AS THE PRINCIPAL DENOMINATION.
6. ALL CONCRETE WORKS ARE OUTSIDE OF THE SCOPE OF THE COMPANY. INFORMATION REGARDING SLAB DESIGN AND CONNECTIONS IN THESE DRAWINGS ARE INTENDED FOR GUIDENCE ONLY. FOUNDATION AND SLAB WORKS SHOULD BE DESIGNED AND APPROVED BY A LOCAL STRUCTURAL ENGINEER.
7. THE COMPANY RETAINS FULL TITLE AND OWNERSHIP OF THESE PLANS AND DESIGNS. ANY UNAUTHORISED USE, REPRODUCTION, OR DISTRIBUTION OF THESE PLANS, WHETHER IN WHOLE OR PART, IS EXPRESSLY PROHIBITED WITHOUT PRIOR WRITTEN CONSENT.
8. THE HYBRID STEEL FRAME CONSTRUCTION SYSTEM AND METHODOLOGY (PATENT PENDING) DESCRIBED IN THESE PLANS HAS BEEN DEVELOPED BY THE COMPANY AND IS SUBJECT TO A PROVISIONAL PATENT APPLICATION & ASSIGNMENT - US APPLICATION No. 63/722,841.

No.	Revision	Date
01	Moved walls under roof joists	13.03

ISSUED FOR:

Issued for information

Issued for client approval

Issued for fabrication

Issued for construction

Bahama Beach

DRAWING TITLE:

Section 1

DRAWN BY:

Mladin Monica-Mihaela

SCALE:


1 : 35

DRAWING NO:

A13

DATE:

17/03/2025

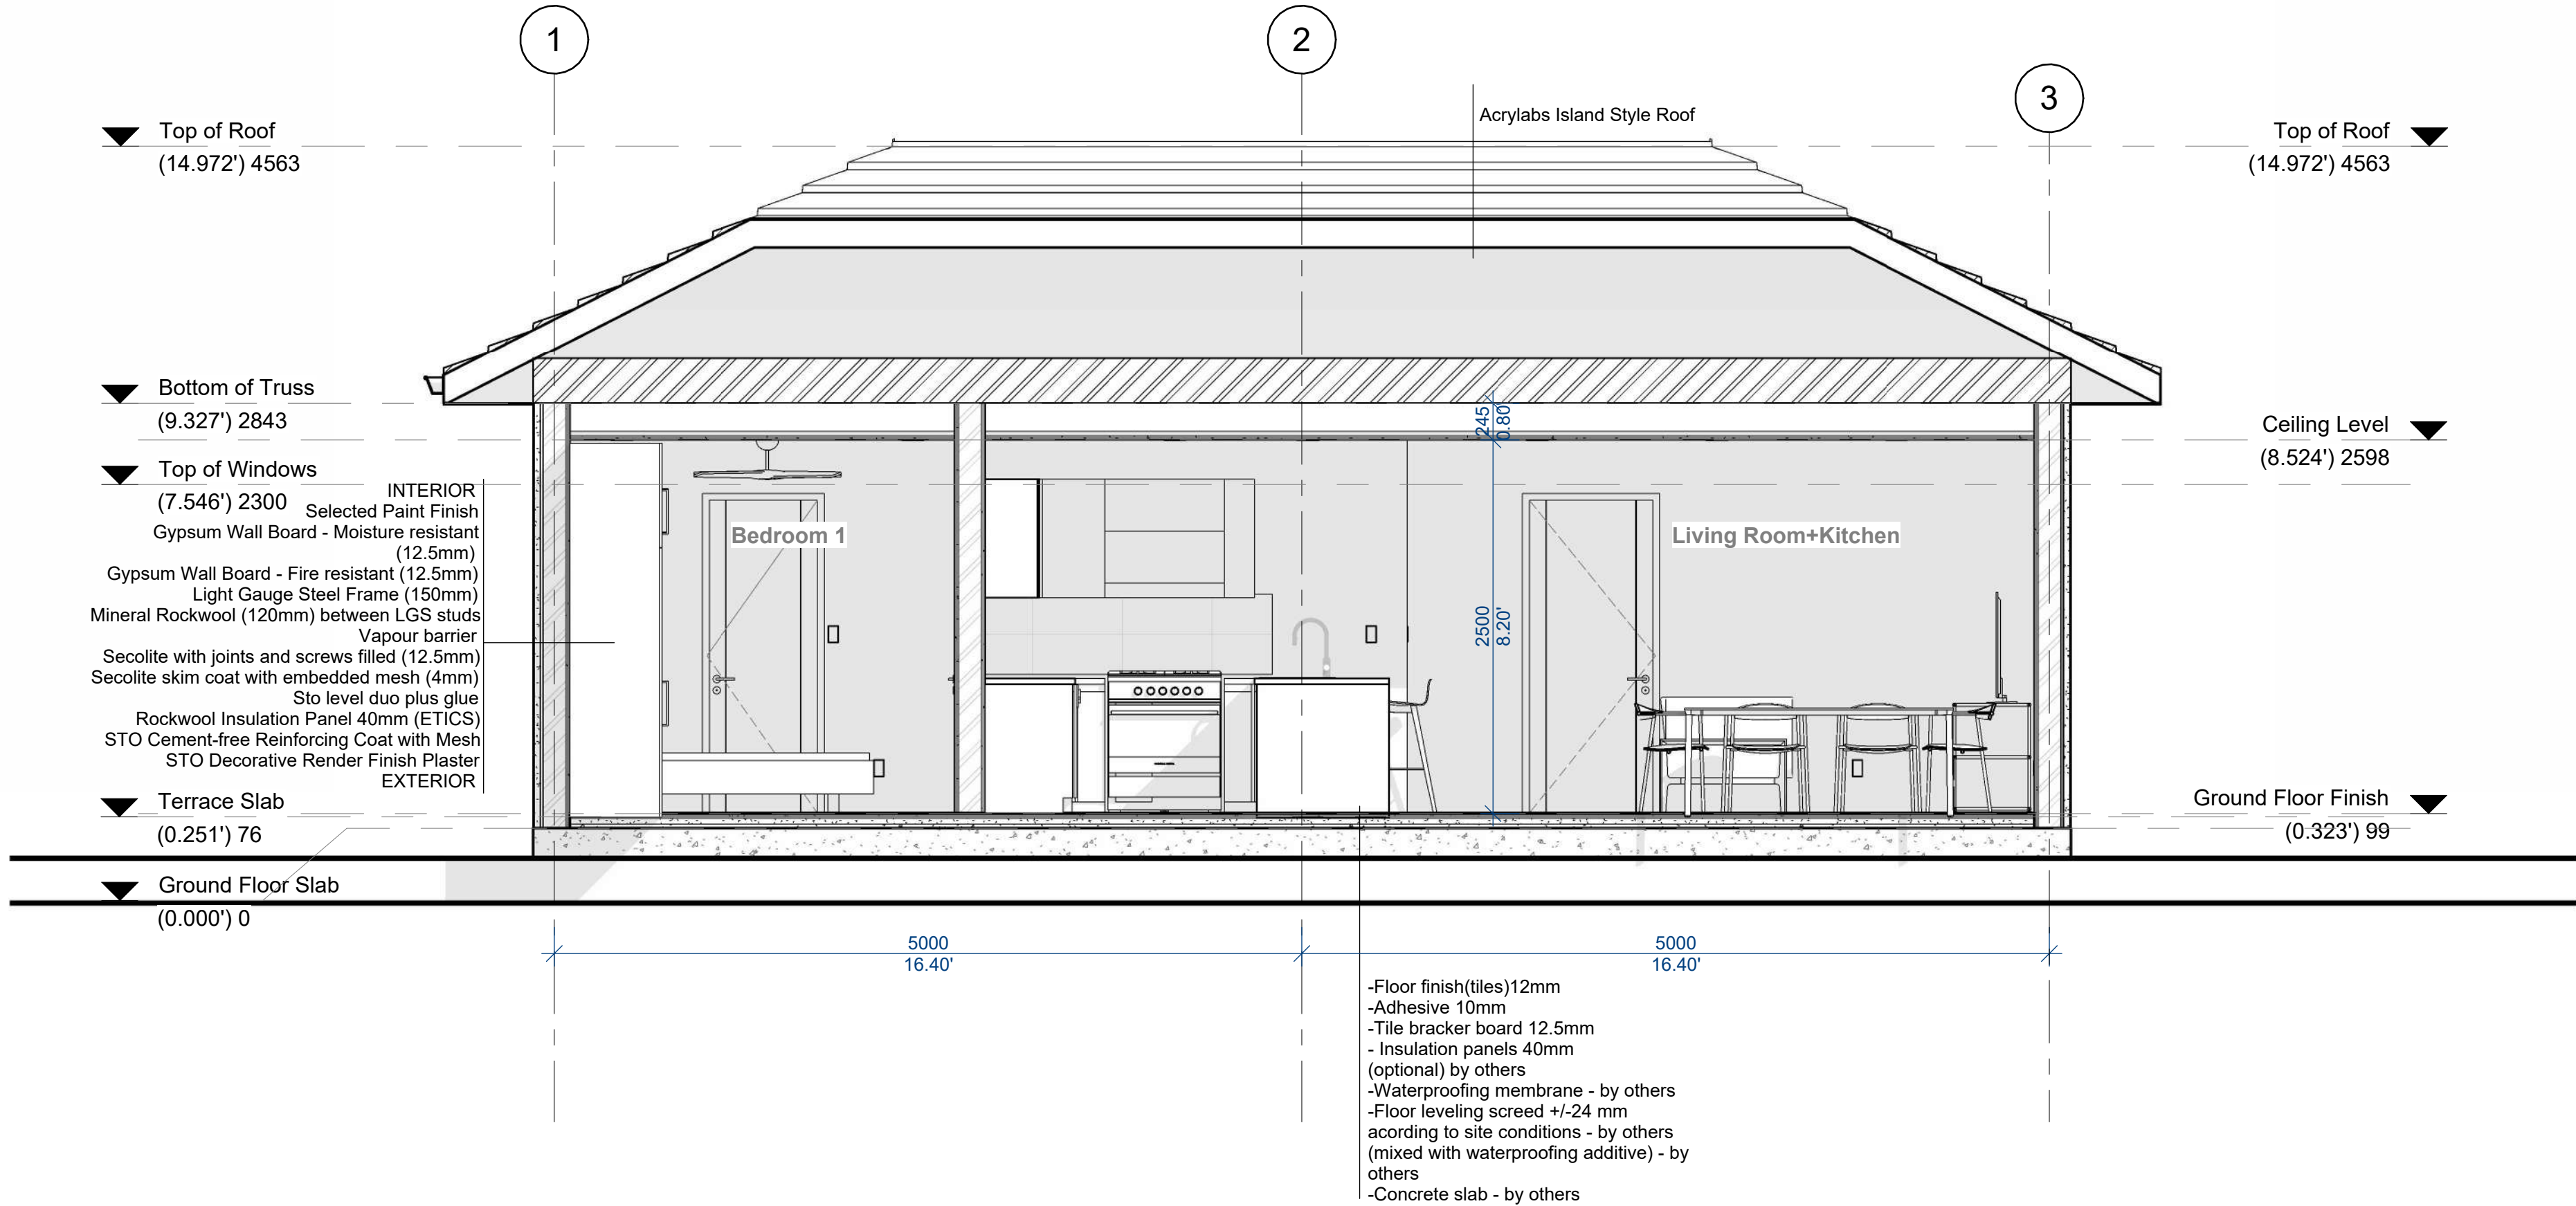

- THESE DRAWINGS MUST BE CHECKED BY THE CUSTOMER OR CONTRACTOR PRIOR TO APPROVAL. ANY ERRORS OR OMISSIONS MUST BE REPORTED IN WRITING TO BAUHU PRIOR TO COMMENCEMENT OF CONSTRUCTION.
- ARCHITECTURAL DRAWINGS SHOULD BE READ IN CONJUNCTION WITH STRUCTURAL DETAILING AND FABRICATION GENERAL ASSEMBLY DRAWINGS.
- FOR CONSTRUCTION PURPOSES, USE ONLY THE LATEST APPROVED DRAWINGS LABELED 'ISSUED FOR CONSTRUCTION'.
- DO NOT SCALE FROM THIS DRAWING.
- THE COMPANY OPERATES USING METRIC DIMENSIONS AS THE PRINCIPAL DENOMINATION.
- ALL CONCRETE WORKS ARE OUTSIDE OF THE SCOPE OF THE COMPANY. INFORMATION REGARDING SLAB DESIGN AND CONNECTIONS IN THESE DRAWINGS ARE INTENDED FOR GUIDENCE ONLY. FOUNDATION AND SLAB WORKS SHOULD BE DESIGNED AND APPROVED BY A LOCAL STRUCTURAL ENGINEER.
- THE COMPANY RETAINS FULL TITLE AND OWNERSHIP OF THESE PLANS AND DESIGNS. ANY UNAUTHORISED USE, REPRODUCTION, OR DISTRIBUTION OF THESE PLANS, WHETHER IN WHOLE OR PART, IS EXPRESSLY PROHIBITED WITHOUT PRIOR WRITTEN CONSENT.
- THE HYBRID STEEL FRAME CONSTRUCTION SYSTEM AND METHODOLOGY (PATENT PENDING) DESCRIBED IN THESE PLANS HAS BEEN DEVELOPED BY THE COMPANY AND IS SUBJECT TO A PROVISIONAL PATENT APPLICATION & ASSIGNMENT - US APPLICATION No. 63/722,841.

No.	Revision	Date
01	Moved walls under roof joists	13.03

ISSUED FOR:

Issued for information

Issued for client approval

Issued for fabrication

Issued for construction

Bahama Beach

DRAWING TITLE:

Section 2

DRAWN BY:

Mladin Monica-Mihaela

SCALE:


1 : 35

DRAWING NO:

A14

DATE:

17/03/2025

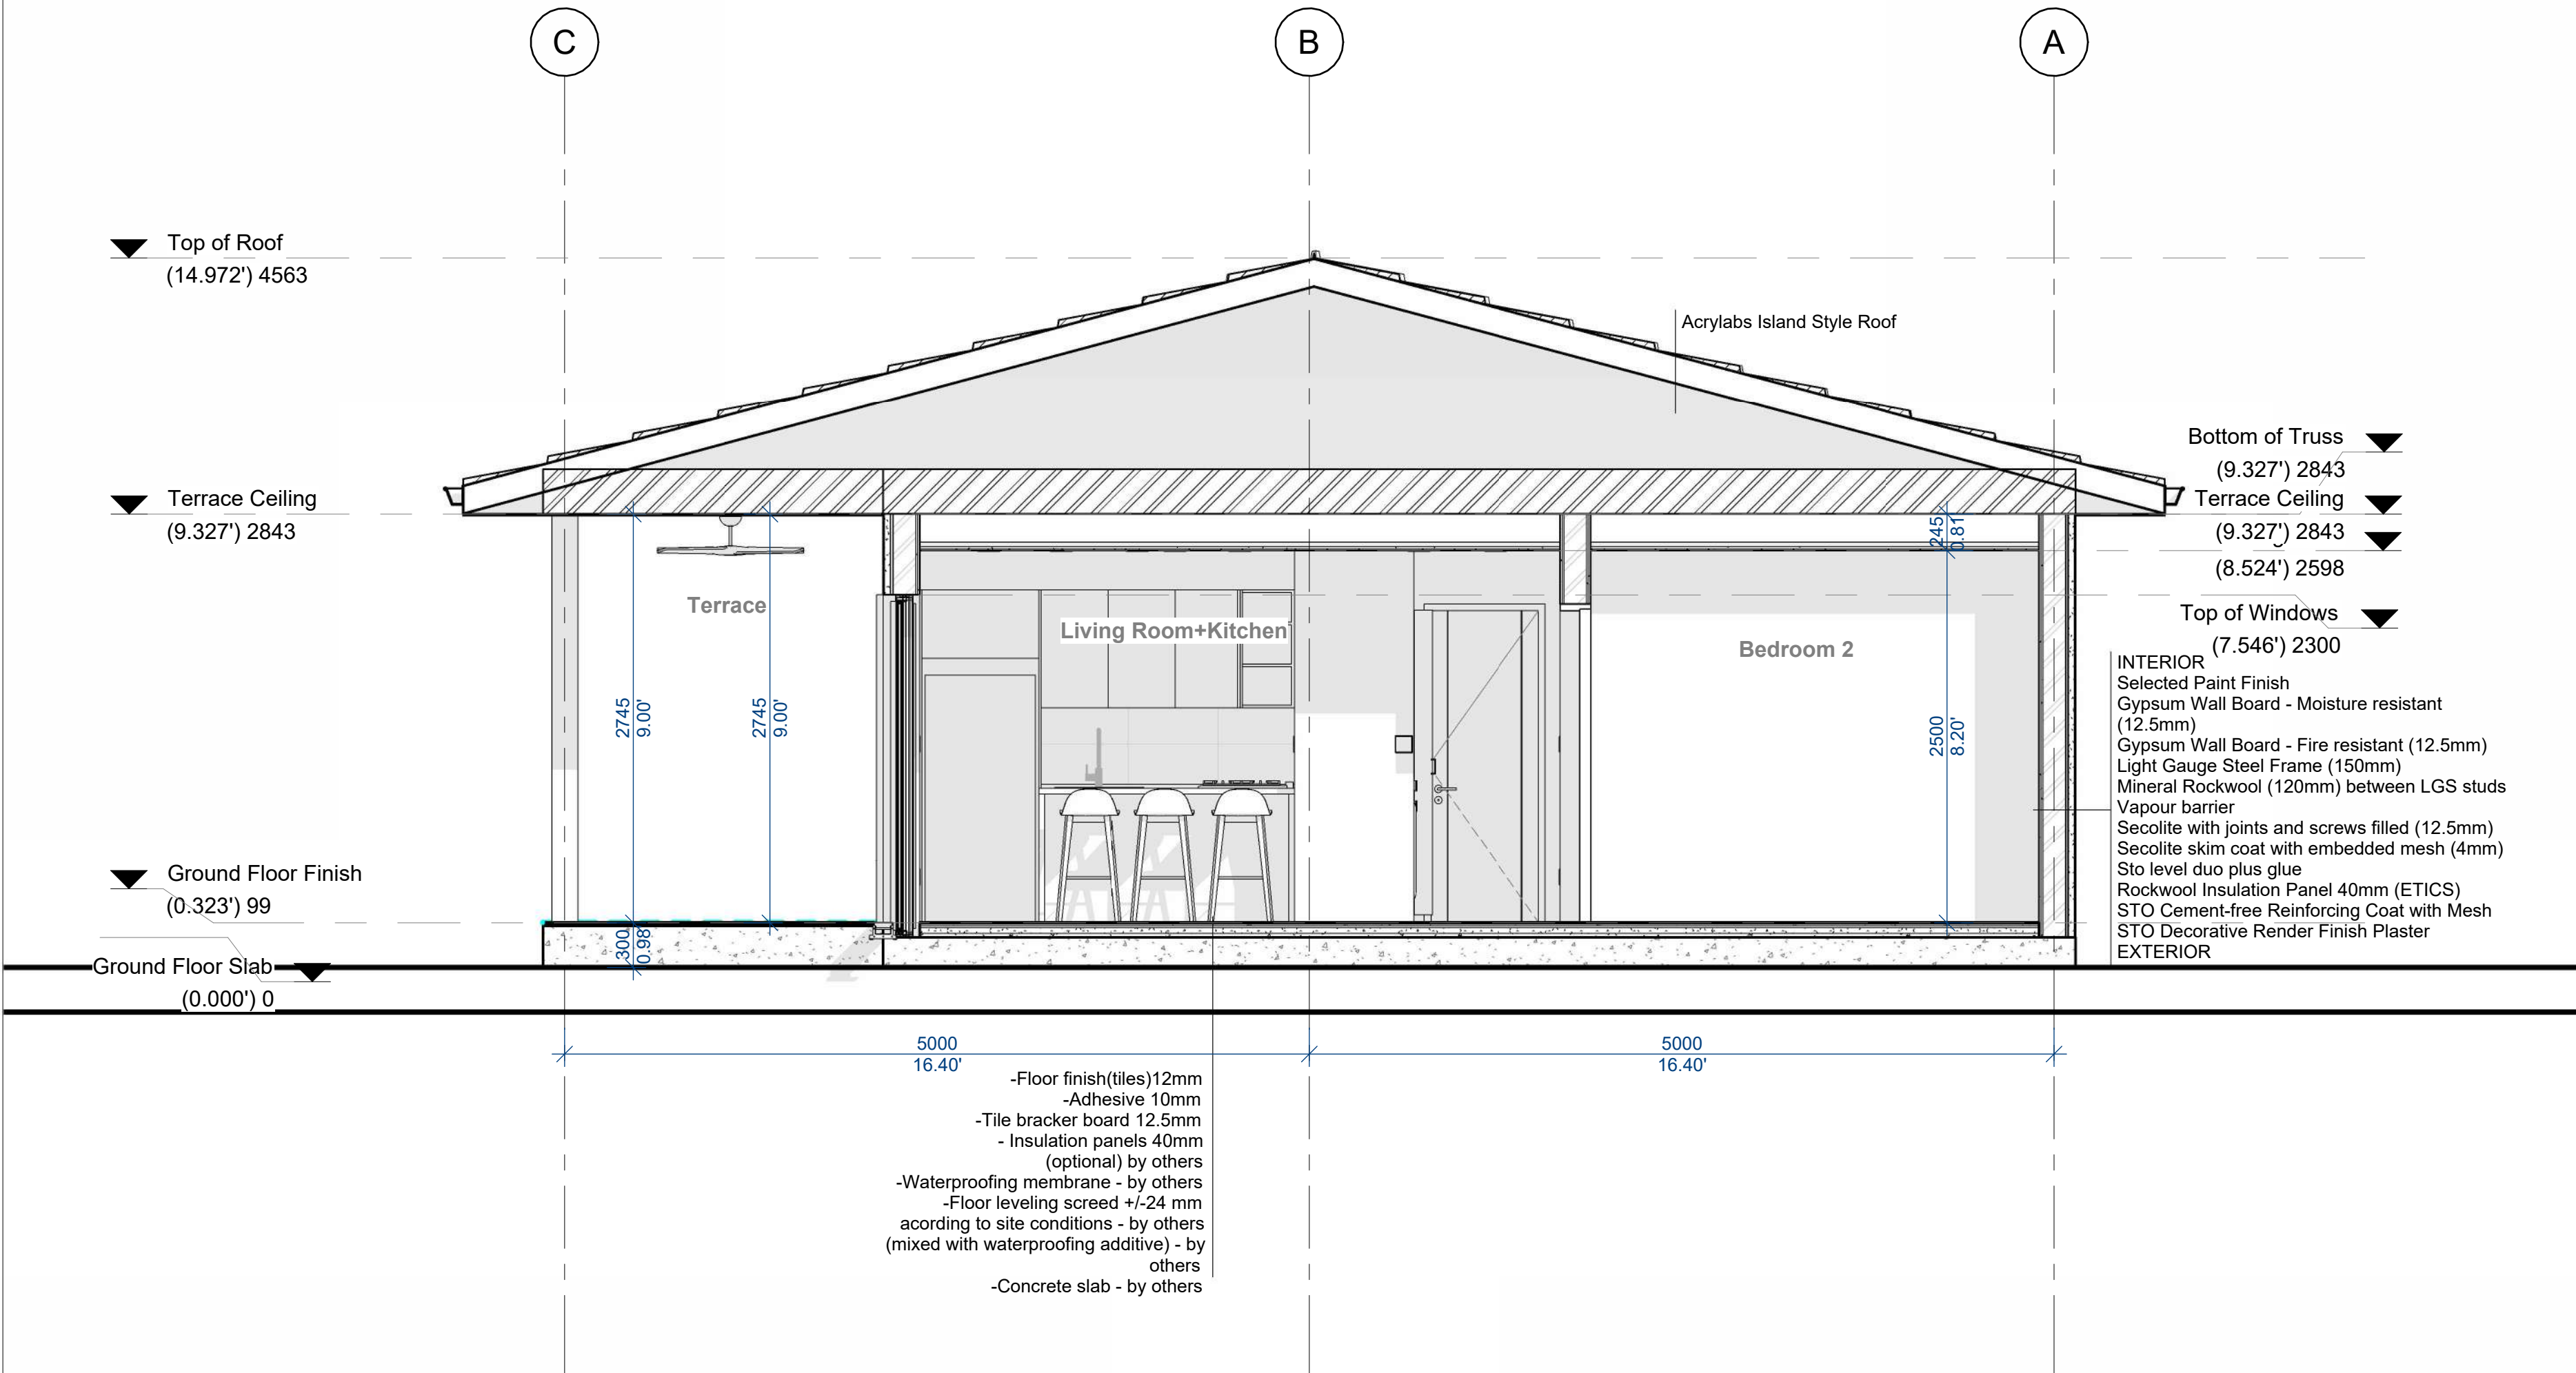

1. THESE DRAWINGS MUST BE CHECKED BY THE CUSTOMER OR CONTRACTOR PRIOR TO APPROVAL. ANY ERRORS OR OMISSIONS MUST BE REPORTED IN WRITING TO BAUHU PRIOR TO COMMENCEMENT OF CONSTRUCTION.
2. ARCHITECTURAL DRAWINGS SHOULD BE READ IN CONJUNCTION WITH STRUCTURAL DETAILING AND FABRICATION GENERAL ASSEMBLY DRAWINGS.
3. FOR CONSTRUCTION PURPOSES, USE ONLY THE LATEST APPROVED DRAWINGS LABELED 'ISSUED FOR CONSTRUCTION'.
4. DO NOT SCALE FROM THIS DRAWING.
5. THE COMPANY OPERATES USING METRIC DIMENSIONS AS THE PRINCIPAL DENOMINATION.
6. ALL CONCRETE WORKS ARE OUTSIDE OF THE SCOPE OF THE COMPANY. INFORMATION REGARDING SLAB DESIGN AND CONNECTIONS IN THESE DRAWINGS ARE INTENDED FOR GUIDENCE ONLY. FOUNDATION AND SLAB WORKS SHOULD BE DESIGNED AND APPROVED BY A LOCAL STRUCTURAL ENGINEER.
7. THE COMPANY RETAINS FULL TITLE AND OWNERSHIP OF THESE PLANS AND DESIGNS. ANY UNAUTHORISED USE, REPRODUCTION, OR DISTRIBUTION OF THESE PLANS, WHETHER IN WHOLE OR PART, IS EXPRESSLY PROHIBITED WITHOUT PRIOR WRITTEN CONSENT.
8. THE HYBRID STEEL FRAME CONSTRUCTION SYSTEM AND METHODOLOGY (PATENT PENDING) DESCRIBED IN THESE PLANS HAS BEEN DEVELOPED BY THE COMPANY AND IS SUBJECT TO A PROVISIONAL PATENT APPLICATION & ASSIGNMENT - US APPLICATION No. 63/722,841.

No.	Revision	Date
01	Moved walls under roof joists	13.03

ISSUED FOR:

Issued for information

Issued for client approval

Issued for fabrication

Issued for construction

Bahama Beach

DRAWING TITLE:

Section 3

DRAWN BY:

Mladin Monica-Mihaela

SCALE:


1 : 35

DRAWING NO:

A15

DATE:

17/03/2025

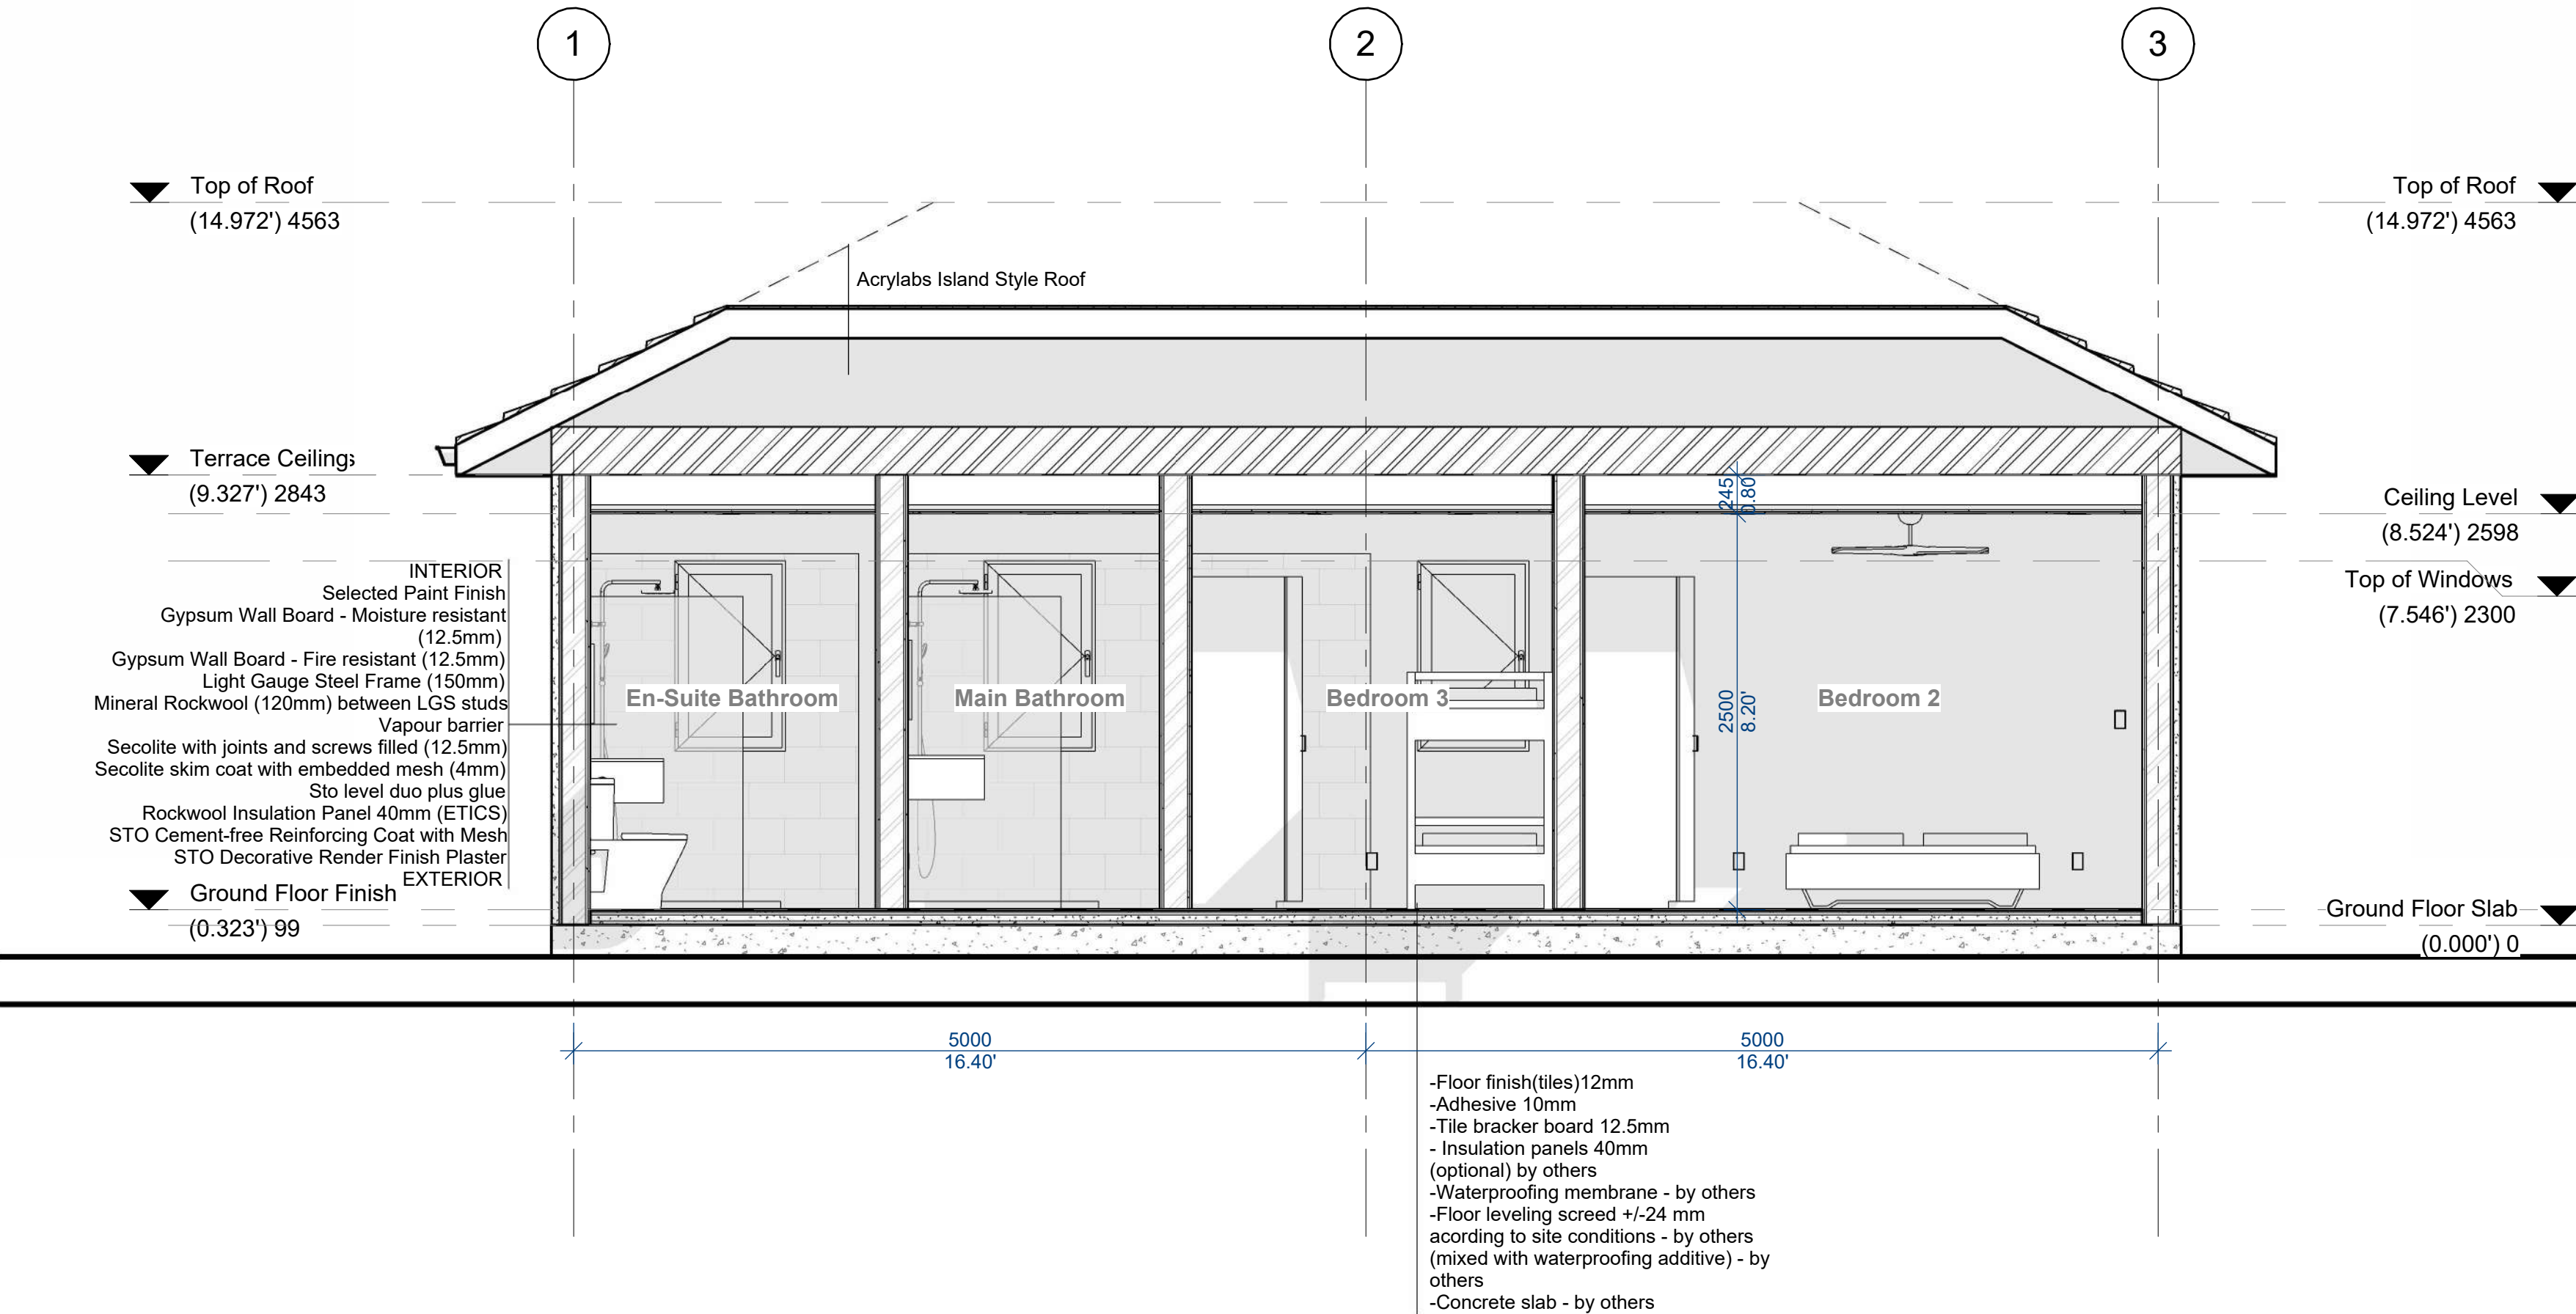

Door Schedule												
No	Type	Size		RO Size		Count	Opening Direction	Glass	Finishing	No of Leaves	Hinge Side	Lock
		Width	Height	RO Width	RO. Height							
ID-01	Interior Door	850 mm	2100 mm	915	2214	2	Casement		matt white	1	1L, 1R	Yes
ID-02	Interior Door 2	750 mm	2100 mm	815	2214	3	Casement		matt white	1	3R	Yes
Grand total						5						

Window Schedule																
No	Type	Size		RO Size		Count	Opening Direction	Interior pane	Frame Finish	No of Leaves	Hinge Side	Level	Lock	Insect screen	Reinforcing bar	Gully drain
		Width	Height	RO. Width	RO. Height											
ED-01	CORVISION Slider ED-01	1800 mm	2300	1834	2317	3	Sliding	2 left, 1 right	RAL 9010: Pure White RAL: 9010	2	Sliding	Ground Floor Slab	Yes	Yes	COR-4315	Yes
W-01	COR70 Casement W-01	1200 mm	1400	1234	1434	1	Casement double	x	RAL 9010: Pure White RAL: 9010	2	double	Ground Floor Finish	Yes	Yes	No	N/A
W-02	COR70 Casement W-02	700 mm	1200	734	1234	3	Casement	x	RAL 9010: Pure White RAL: 9010	1	3 right	Ground Floor Finish	Yes	Yes	No	N/A
Grand total						7										

Interior Doors

Compincar

Colour: Matt White Lac.

Model: Lisa

• R: Right hinge

• L: Left hinge

Handle

Model: 1003

LISA

Window/Door Frames

RAL 9010
Pure White

Colour: Pure White

RAL: 9010

Glass

https://www.guardianglass.com/gb/en/our-glass/glass-types/solar-control-glass

• 44.2+16argon we+6 SNX

- Note:
- Shutters, insect screens and screening will be provided by others-acquired locally according to dimensions of finished openings after finish application. Drawings are made for design purposes only.

• Garage type doors are excluded and should be sourced by the owner.

• All opening windows open outwards.

BAUHU

MODULAR • BUILDING • SOLUTIONS

1. THESE DRAWINGS MUST BE CHECKED BY THE CUSTOMER OR CONTRACTOR PRIOR TO APPROVAL. ANY ERRORS OR OMISSIONS MUST BE REPORTED IN WRITING TO BAUHU PRIOR TO COMMENCEMENT OF CONSTRUCTION.

2. ARCHITECTURAL DRAWINGS SHOULD BE READ IN CONJUNCTION WITH STRUCTURAL DETAILING AND FABRICATION GENERAL ASSEMBLY DRAWINGS.

3. FOR CONSTRUCTION PURPOSES, USE ONLY THE LATEST APPROVED DRAWINGS LABELED 'ISSUED FOR CONSTRUCTION'.

4. DO NOT SCALE FROM THIS DRAWING.

5. THE COMPANY OPERATES USING METRIC DIMENSIONS AS THE PRINCIPAL DENOMINATION.

6. ALL CONCRETE WORKS ARE OUTSIDE OF THE SCOPE OF THE COMPANY. INFORMATION REGARDING SLAB DESIGN AND CONNECTIONS IN THESE DRAWINGS ARE INTENDED FOR GUIDENCE ONLY. FOUNDATION AND SLAB WORKS SHOULD BE DESIGNED AND APPROVED BY A LOCAL STRUCTURAL ENGINEER.

7. THE COMPANY RETAINS FULL TITLE AND OWNERSHIP OF THESE PLANS AND DESIGNS. ANY UNAUTHORISED USE, REPRODUCTION, OR DISTRIBUTION OF THESE PLANS, WHETHER IN WHOLE OR PART, IS EXPRESSLY PROHIBITED WITHOUT PRIOR WRITTEN CONSENT.

8. THE HYBRID STEEL FRAME CONSTRUCTION SYSTEM AND METHODOLOGY (PATENT PENDING) DESCRIBED IN THESE PLANS HAS BEEN DEVELOPED BY THE COMPANY AND IS SUBJECT TO A PROVISIONAL PATENT APPLICATION & ASSIGNMENT - US APPLICATION No. 63/722,841.

No.	Revision	Date
01	Moved walls under roof joists	13.03

ISSUED FOR:

Issued for information

Issued for client approval

Issued for fabrication

Issued for construction

Bahama Beach

DRAWING TITLE:
Openings Schedule

DRAWN BY:
Mladin Monica-Mihaela

SCALE:

DRAWING NO:
A16

DATE:
17/03/2025

1. THESE DRAWINGS MUST BE CHECKED BY THE CUSTOMER OR CONTRACTOR PRIOR TO APPROVAL. ANY ERRORS OR OMISSIONS MUST BE REPORTED IN WRITING TO BAUHU PRIOR TO COMMENCEMENT OF CONSTRUCTION.
2. ARCHITECTURAL DRAWINGS SHOULD BE READ IN CONJUNCTION WITH STRUCTURAL DETAILING AND FABRICATION GENERAL ASSEMBLY DRAWINGS.
3. FOR CONSTRUCTION PURPOSES, USE ONLY THE LATEST APPROVED DRAWINGS LABELED 'ISSUED FOR CONSTRUCTION'.
4. DO NOT SCALE FROM THIS DRAWING.
5. THE COMPANY OPERATES USING METRIC DIMENSIONS AS THE PRINCIPAL DENOMINATION.
6. ALL CONCRETE WORKS ARE OUTSIDE OF THE SCOPE OF THE COMPANY. INFORMATION REGARDING SLAB DESIGN AND CONNECTIONS IN THESE DRAWINGS ARE INTENDED FOR GUIDENCE ONLY. FOUNDATION AND SLAB WORKS SHOULD BE DESIGNED AND APPROVED BY A LOCAL STRUCTURAL ENGINEER.
7. THE COMPANY RETAINS FULL TITLE AND OWNERSHIP OF THESE PLANS AND DESIGNS. ANY UNAUTHORISED USE, REPRODUCTION, OR DISTRIBUTION OF THESE PLANS, WHETHER IN WHOLE OR PART, IS EXPRESSLY PROHIBITED WITHOUT PRIOR WRITTEN CONSENT.
8. THE HYBRID STEEL FRAME CONSTRUCTION SYSTEM AND METHODOLOGY (PATENT PENDING) DESCRIBED IN THESE PLANS HAS BEEN DEVELOPED BY THE COMPANY AND IS SUBJECT TO A PROVISIONAL PATENT APPLICATION & ASSIGNMENT - US APPLICATION No. 63/722,841.

No.	Revision	Date
01	Moved walls under roof joists	13.03

ISSUED FOR:

Issued for information

Issued for client approval

Issued for fabrication

Issued for construction

Bahama Beach


DRAWING TITLE:
Window/DoorOpenings

DRAWN BY:
Mladin Monica-Mihaela

SCALE:
1 : 20



DRAWING NO:
A17

DATE:
17/03/2025

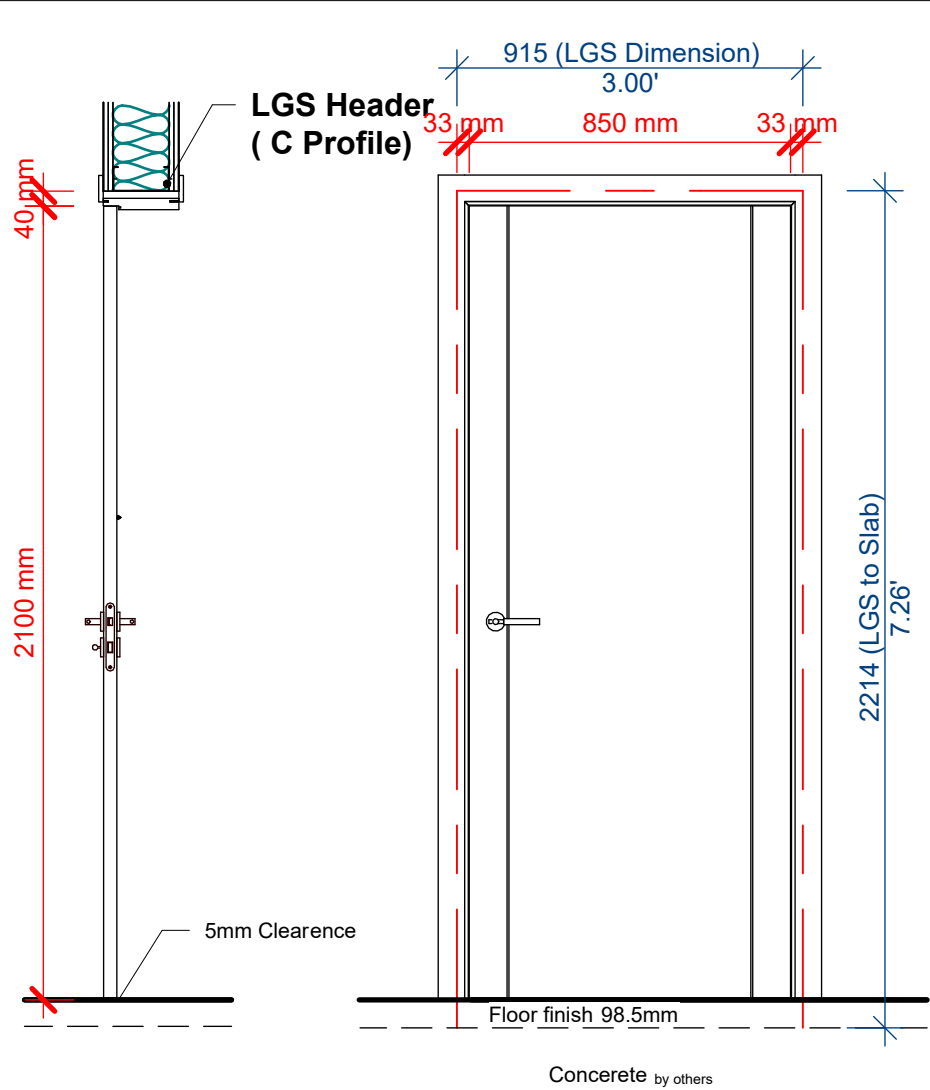



ID01

Type: Interior Casement
Size: 850x2100 mm
R.O. Size: 915x2214 mm
Colour: matt white
Number of Leaves: 1
Total Piece: 2
Hinge Side: 1 Right, 1 Left
Lock: Yes
Sill Height (from top of slab): 74

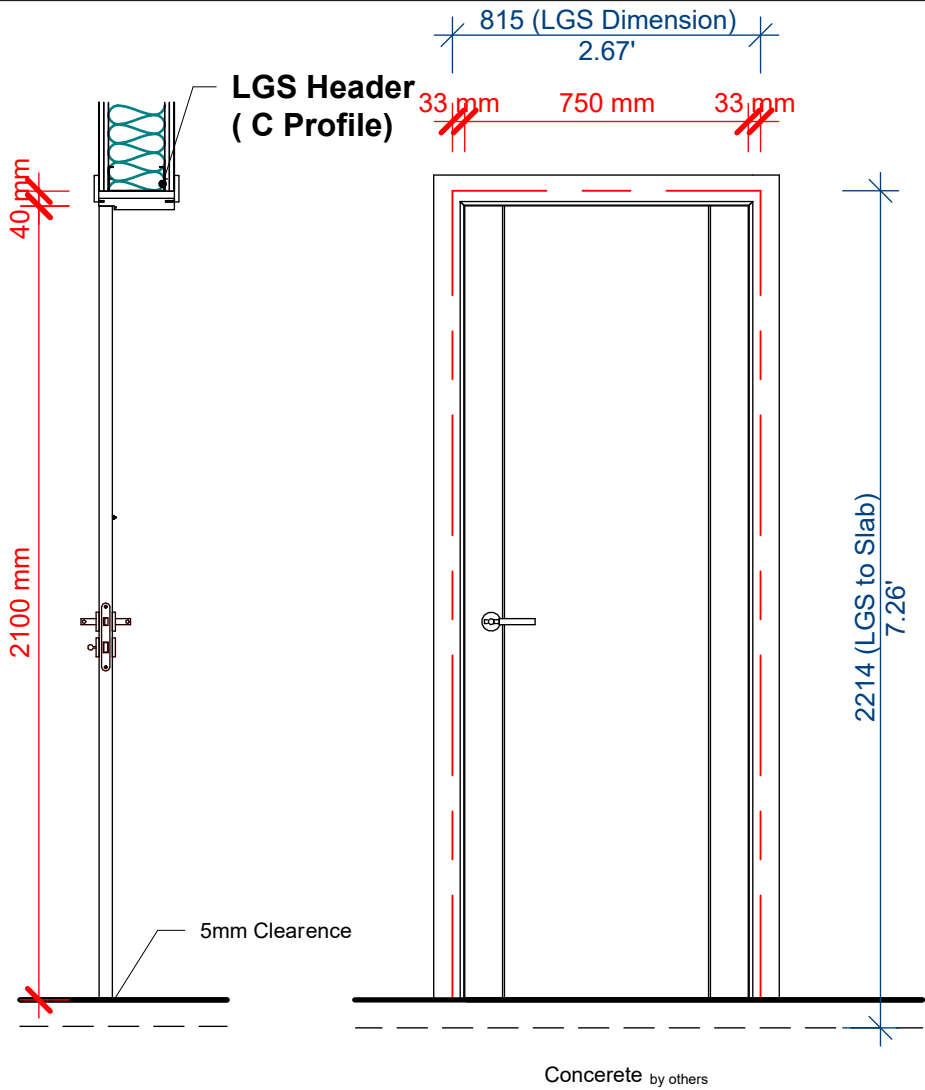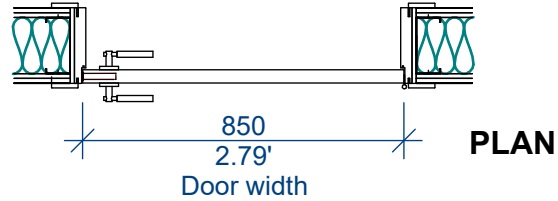


ID02

Type: Interior Casement
Size: 750x2100 mm
R.O. Size: 815x2214 mm
Colour: matt white
Number of Leaves: 1
Total Piece: 2
Hinge Side: 3 Right
Lock: Yes
Sill Height (from top of slab): 74

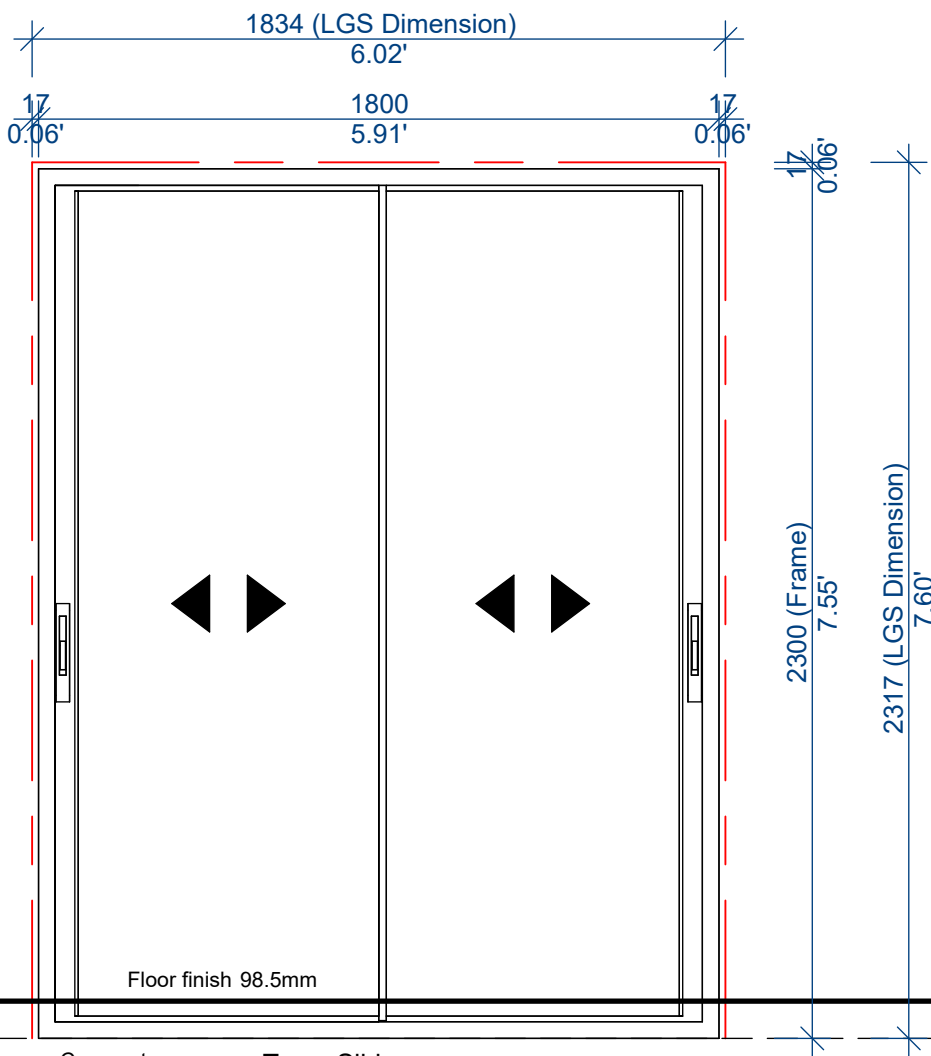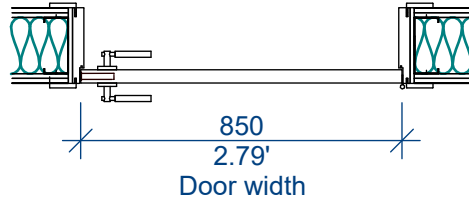


ED01

Type: Slider
Size: 1800x2300
R.O. Size: 1834x2317
Interior pane: 2 left, 1 right (seen from inside)
Colour: RAL 9010: Pure White
Number of Leaves: 2
Total Piece: 3
Hinge Side: -
Lock: Yes
Gully profile: Yes

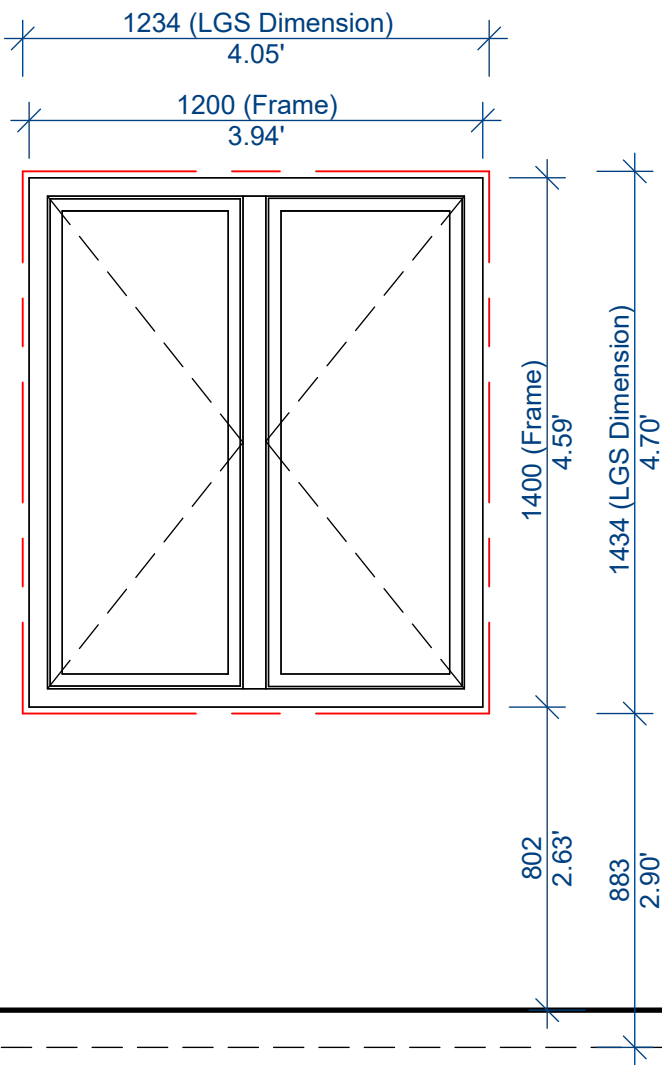


W01

Type: Casement
Size: 1200x1400
R.O. Size: 1234x1434
Colour: RAL 9010: Pure White
Number of Leaves: 2
Total Piece: 1
Hinge Side: double
Lock: Yes

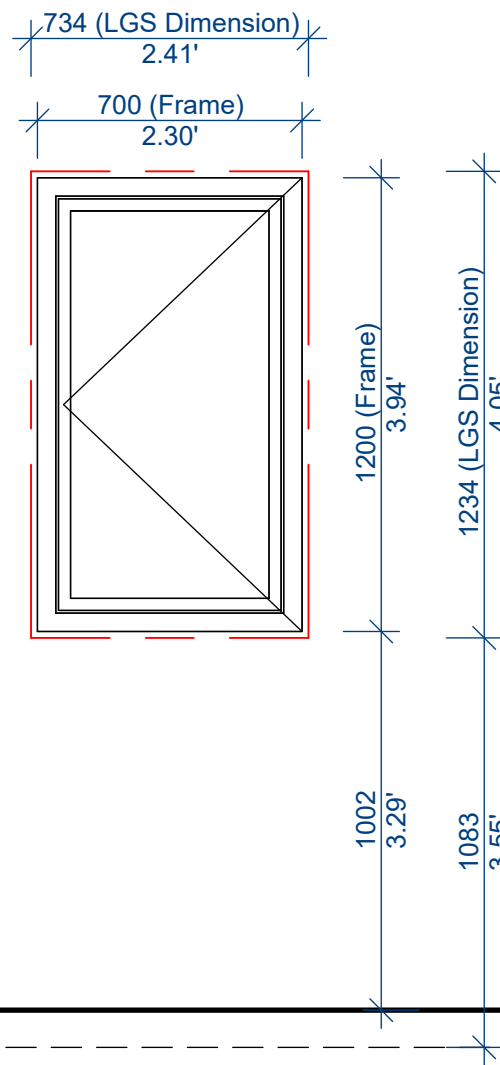

W02

Type: Casement
Size: 700x1200
R.O. Size: 734x1234
Colour: RAL 9010: Pure White
Number of Leaves: 1
Total Piece: 3
Hinge Side: 3 right
Lock: Yes

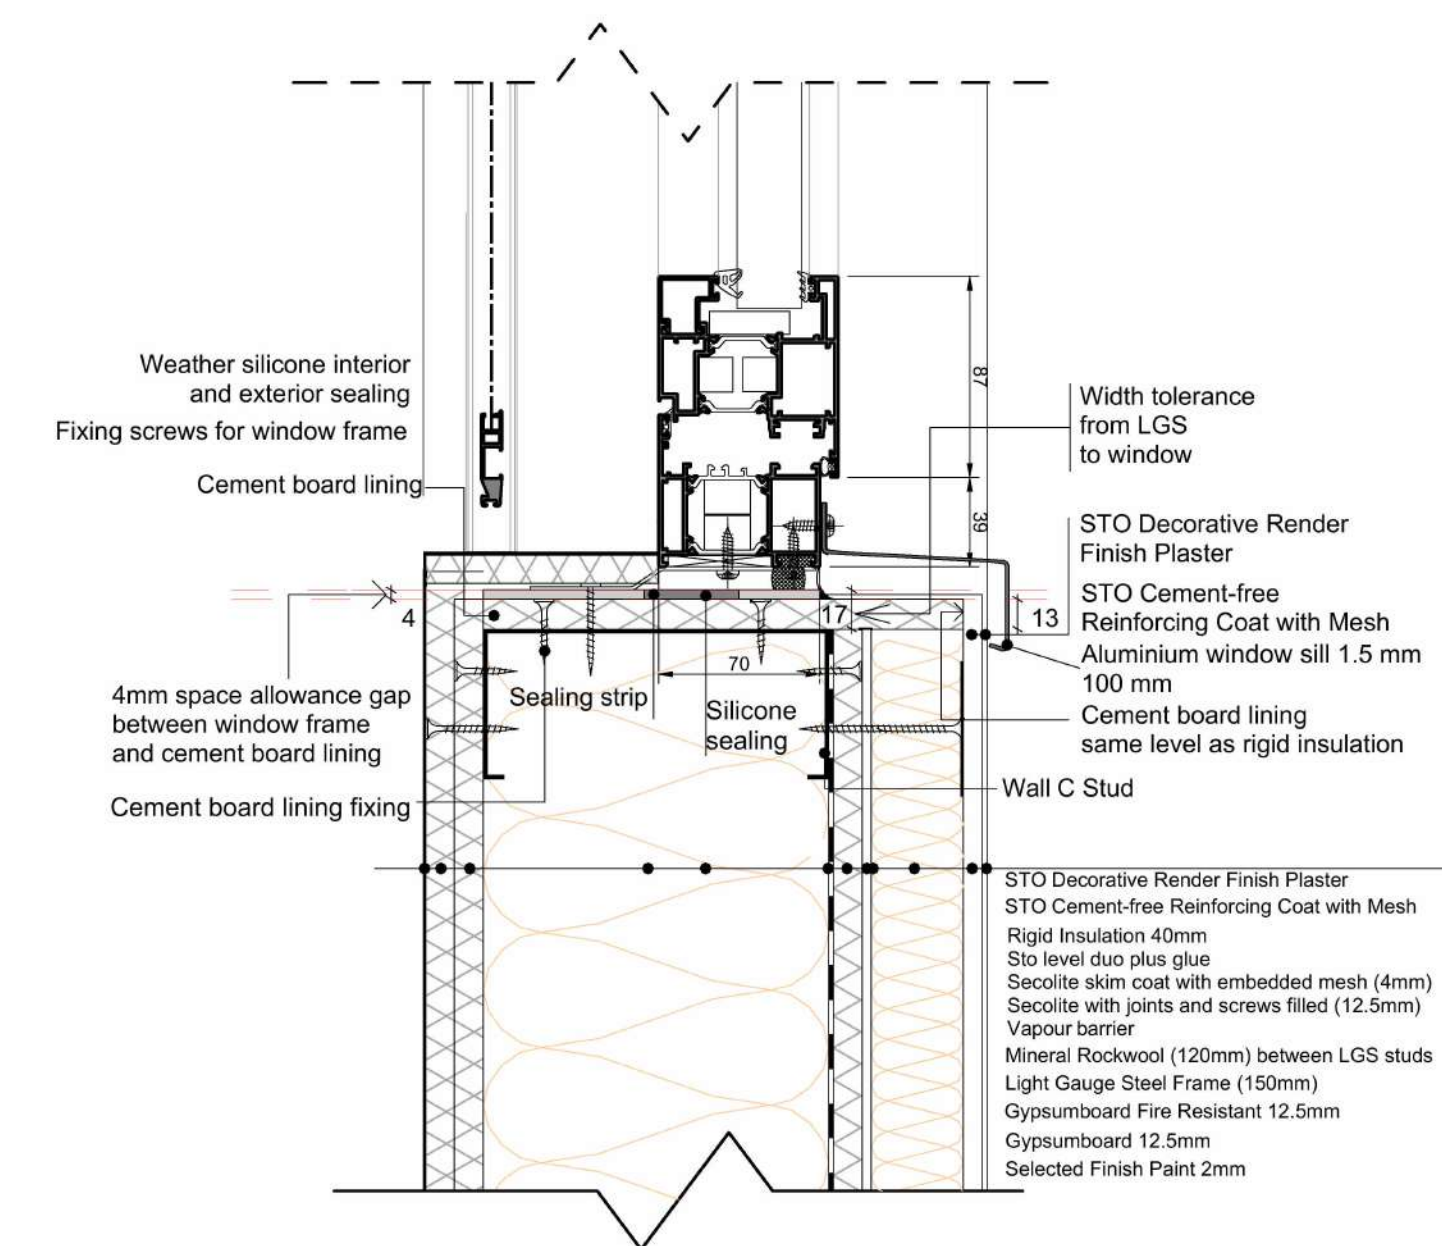

BAUHU

MODULAR • BUILDING • SOLUTIONS

1. THESE DRAWINGS MUST BE CHECKED BY THE CUSTOMER OR CONTRACTOR PRIOR TO APPROVAL. ANY ERRORS OR OMISSIONS MUST BE REPORTED IN WRITING TO BAUHU PRIOR TO COMMENCEMENT OF CONSTRUCTION.

2. ARCHITECTURAL DRAWINGS SHOULD BE READ IN CONJUNCTION WITH STRUCTURAL DETAILING AND FABRICATION GENERAL ASSEMBLY DRAWINGS.

3. FOR CONSTRUCTION PURPOSES, USE ONLY THE LATEST APPROVED DRAWINGS LABELED 'ISSUED FOR CONSTRUCTION'.

4. DO NOT SCALE FROM THIS DRAWING.

5. THE COMPANY OPERATES USING METRIC DIMENSIONS AS THE PRINCIPAL DENOMINATION.

6. ALL CONCRETE WORKS ARE OUTSIDE OF THE SCOPE OF THE COMPANY. INFORMATION REGARDING SLAB DESIGN AND CONNECTIONS IN THESE DRAWINGS ARE INTENDED FOR GUIDANCE ONLY. FOUNDATION AND SLAB WORKS SHOULD BE DESIGNED AND APPROVED BY A LOCAL STRUCTURAL ENGINEER.

7. THE COMPANY RETAINS FULL TITLE AND OWNERSHIP OF THESE PLANS AND DESIGNS. ANY UNAUTHORISED USE, REPRODUCTION, OR DISTRIBUTION OF THESE PLANS, WHETHER IN WHOLE OR PART, IS EXPRESSLY PROHIBITED WITHOUT PRIOR WRITTEN CONSENT.

8. THE HYBRID STEEL FRAME CONSTRUCTION SYSTEM AND METHODOLOGY (PATENT PENDING) DESCRIBED IN THESE PLANS HAS BEEN DEVELOPED BY THE COMPANY AND IS SUBJECT TO A PROVISIONAL PATENT APPLICATION & ASSIGNMENT - US APPLICATION No. 63/722,841.

No.	Revision	Date
01	Moved walls under roof joists	13.03

ISSUED FOR:

Issued for information

Issued for client approval

Issued for fabrication

Issued for construction

Bahama Beach

DRAWING TITLE:

Sliding/Casement Window
Section Details with insect

DRAWN BY:

screens

Mladin Monica-Mihaela

SCALE:


1 : 1

DRAWING NO:


A18

DATE:

17/03/2025

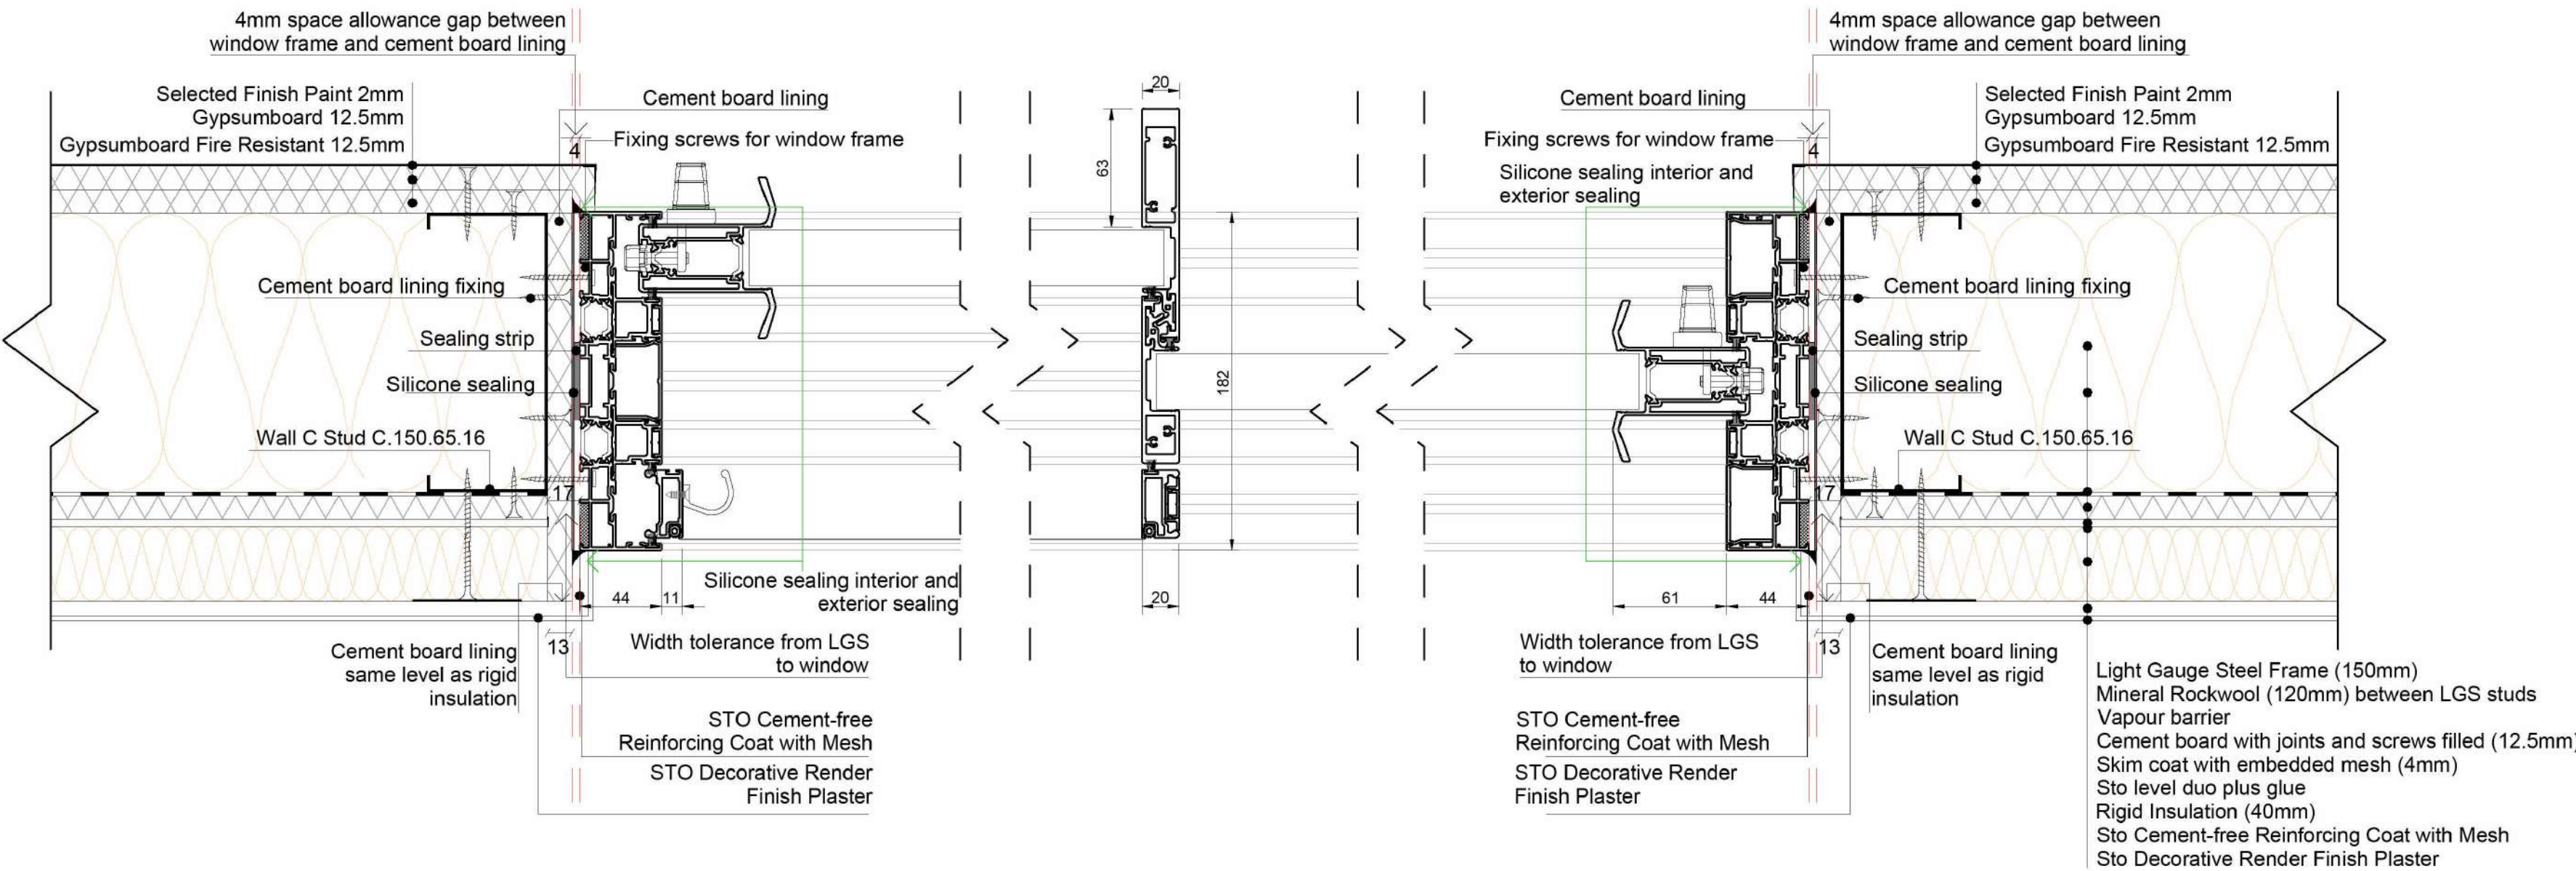

D.Sliding Door/Window Floor Plan with insect screens

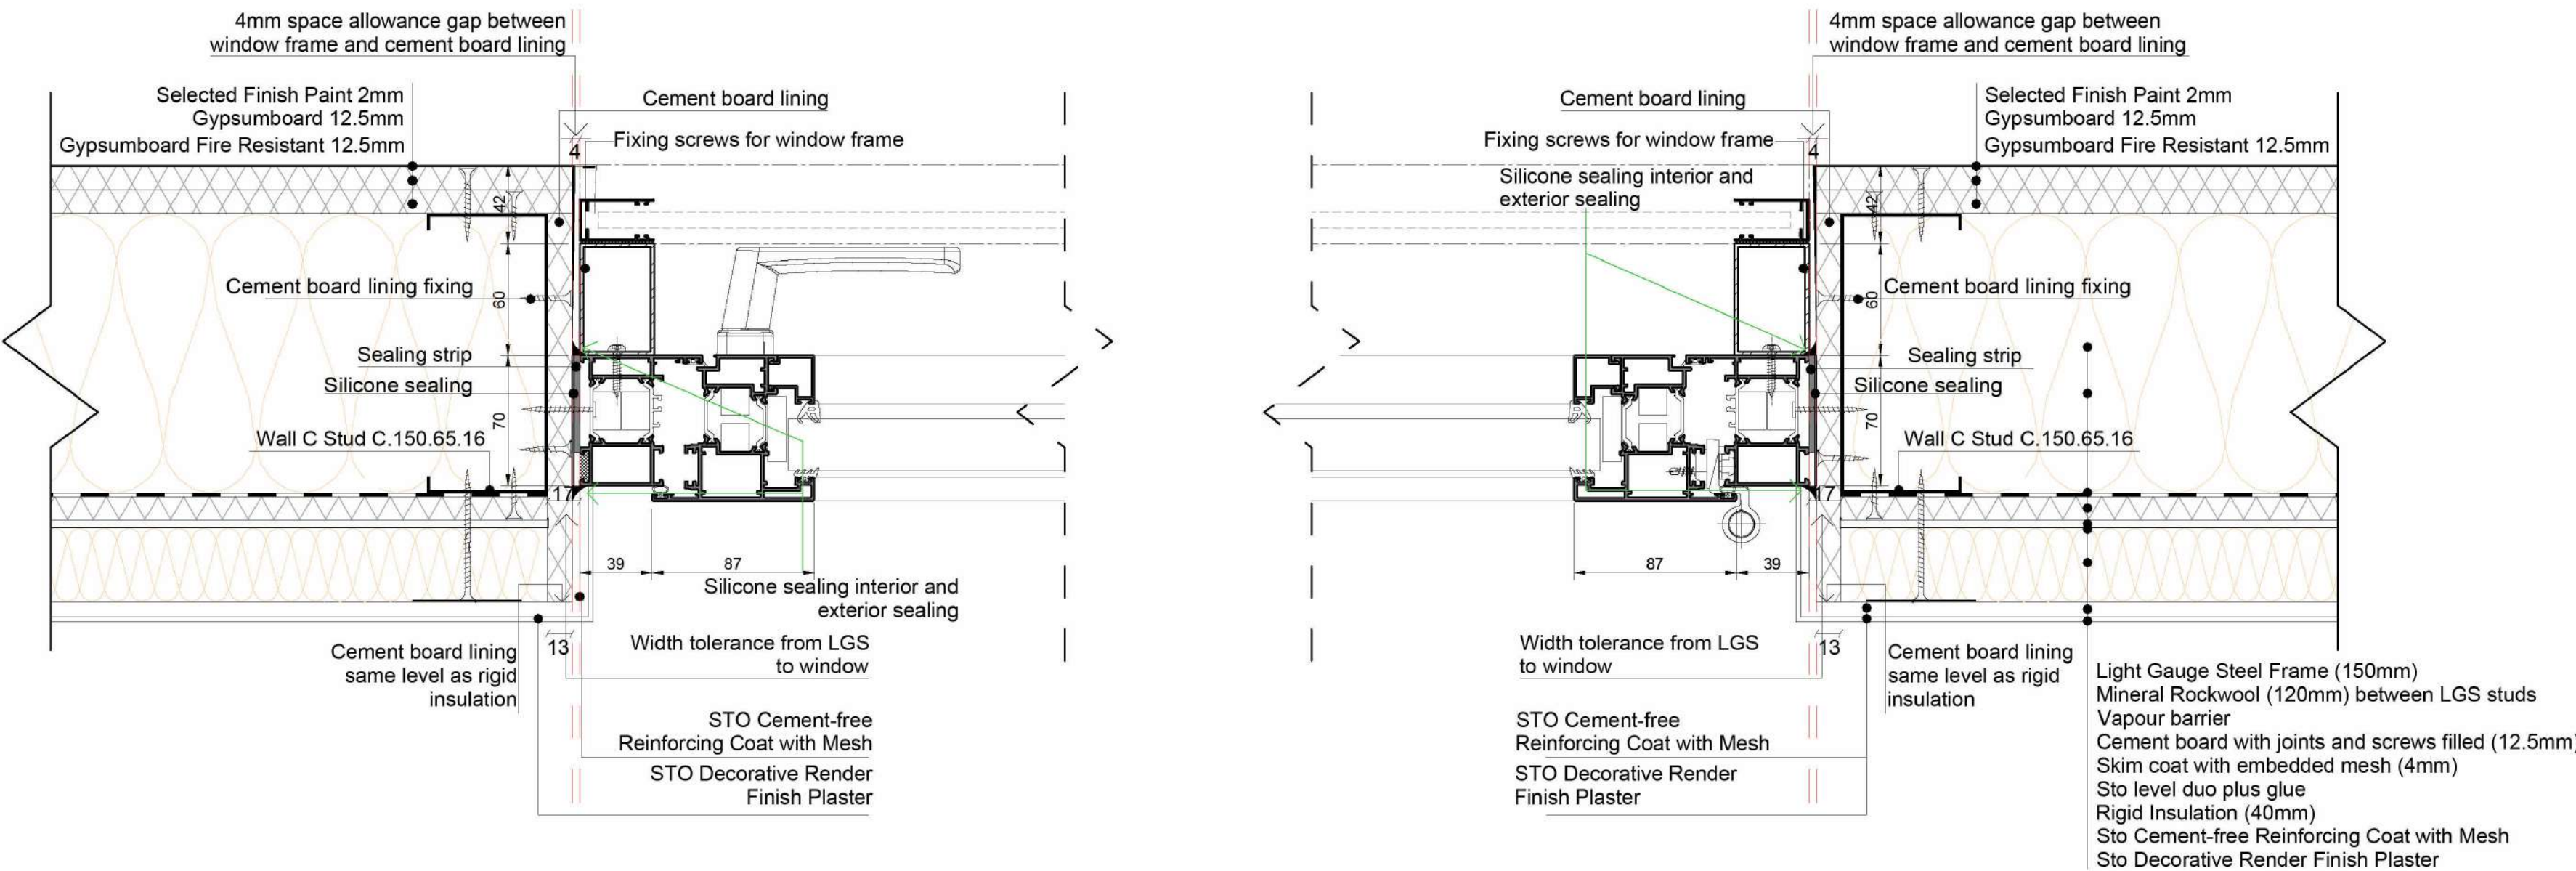

D.Casement Door/Window Floor Plan with insect screens

BAUHU

MODULAR • BUILDING • SOLUTIONS

1. THESE DRAWINGS MUST BE CHECKED BY THE CUSTOMER OR CONTRACTOR PRIOR TO APPROVAL. ANY ERRORS OR OMISSIONS MUST BE REPORTED IN WRITING TO BAUHU PRIOR TO COMMENCEMENT OF CONSTRUCTION.

2. ARCHITECTURAL DRAWINGS SHOULD BE READ IN CONJUNCTION WITH STRUCTURAL DETAILING AND FABRICATION GENERAL ASSEMBLY DRAWINGS.

3. FOR CONSTRUCTION PURPOSES, USE ONLY THE LATEST APPROVED DRAWINGS LABELED 'ISSUED FOR CONSTRUCTION'.

4. DO NOT SCALE FROM THIS DRAWING.

5. THE COMPANY OPERATES USING METRIC DIMENSIONS AS THE PRINCIPAL DENOMINATION.

6. ALL CONCRETE WORKS ARE OUTSIDE OF THE SCOPE OF THE COMPANY. INFORMATION REGARDING SLAB DESIGN AND CONNECTIONS IN THESE DRAWINGS ARE INTENDED FOR GUIDANCE ONLY. FOUNDATION AND SLAB WORKS SHOULD BE DESIGNED AND APPROVED BY A LOCAL STRUCTURAL ENGINEER.

7. THE COMPANY RETAINS FULL TITLE AND OWNERSHIP OF THESE PLANS AND DESIGNS. ANY UNAUTHORIZED USE, REPRODUCTION, OR DISTRIBUTION OF THESE PLANS, WHETHER IN WHOLE OR PART, IS EXPRESSLY PROHIBITED WITHOUT PRIOR WRITTEN CONSENT.

8. THE HYBRID STEEL FRAME CONSTRUCTION SYSTEM AND METHODOLOGY (PATENT PENDING) DESCRIBED IN THESE PLANS HAS BEEN DEVELOPED BY THE COMPANY AND IS SUBJECT TO A PROVISIONAL PATENT APPLICATION & ASSIGNMENT - US APPLICATION No. 63/722,841.

No.	Revision	Date
01	Moved walls under roof joists	13.03

ISSUED FOR:

Issued for information

Issued for client approval

Issued for fabrication

Issued for construction

Bahama Beach

DRAWING TITLE:

Sliding/Casement Window Plan Details

DRAWN BY:

Mladin Monica-Mihaela

SCALE:

DRAWING NO:

A19

DATE:

17/03/2025

Wall Details


Exterior Wall

- Interior side
- Selected Paint Finish
 - Gypsum Wall Board - Moisture resistant (12.5mm)
 - Gypsum Wall Board - Fire resistant (12.5mm)
 - Light Gauge Steel Frame (150mm)
 - Mineral Rockwool (120mm) between LGS studs
 - Vapour barrier
 - Secolite with joints and screws filled (12.5mm)
 - Secolite skim coat with embedded mesh (4mm)
 - Sto level duo plus glue
 - Rigid Insulation 40mm
 - STO Cement-free Reinforcing Coat with Mesh
 - STO Decorative Render Finish Plaster
- Exterior side


Interior Wall

- Interior side
- Selected Paint Finish
 - Gypsum Wall Board - Moisture resistant (12.5mm)
 - Gypsum Wall Board - Fire resistant (12.5mm)
 - Light Gauge Steel Frame (150mm)
 - Mineral Rockwool (120mm) between LGS studs
 - Gypsum Wall Board - Fire resistant (12.5mm)
 - Gypsum Wall Board - Moisture resistant (12.5mm)
 - Selected Paint Finish
- Interior side


D.Exterior - Interior Wall Connection Sc: 1/6

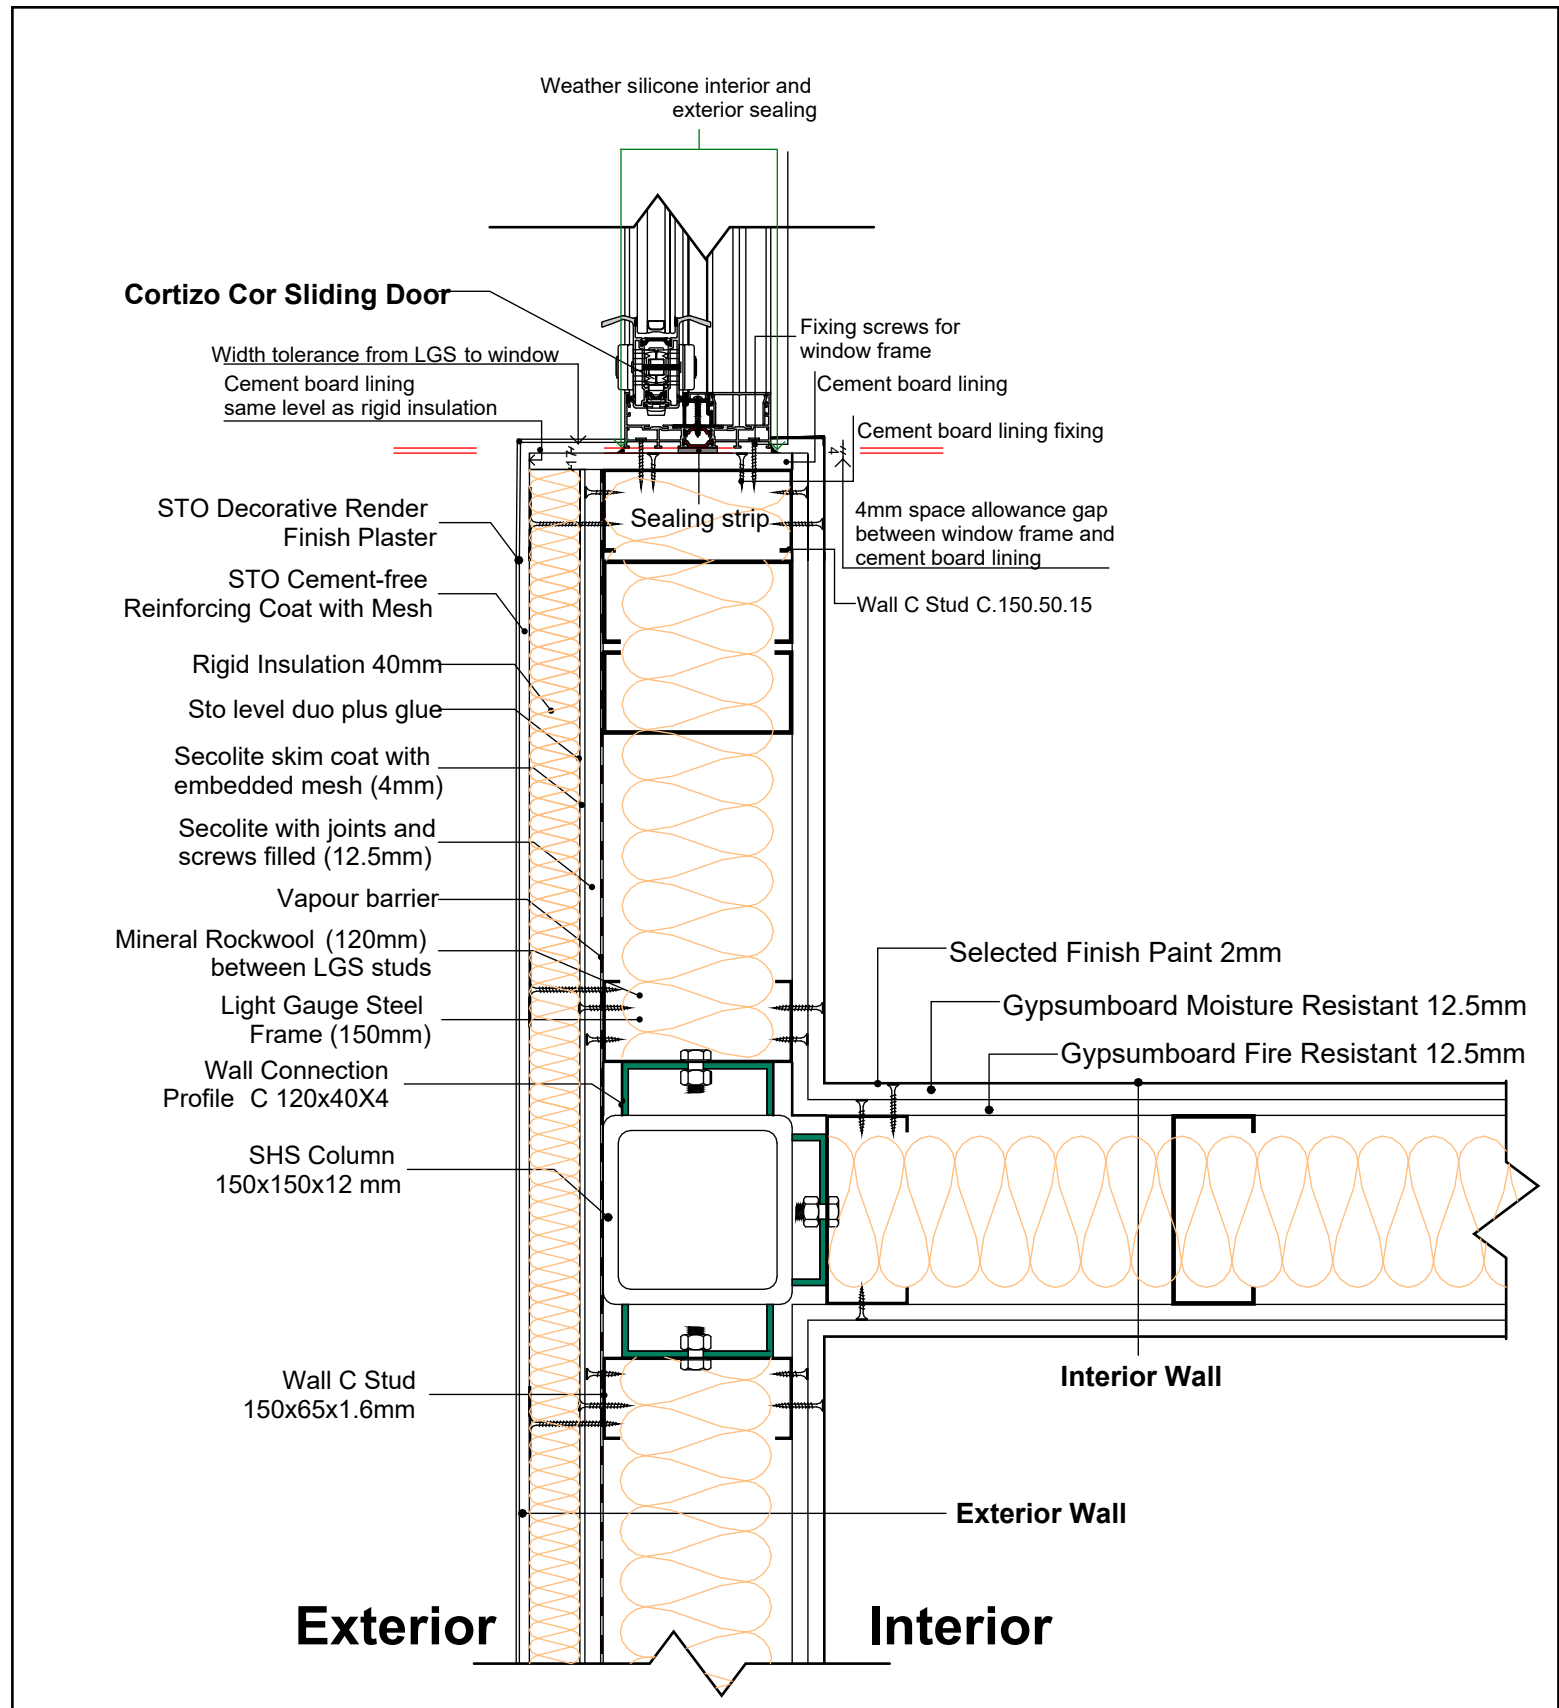

D.Exterior - Interior Wall Connection Sc: 1/6

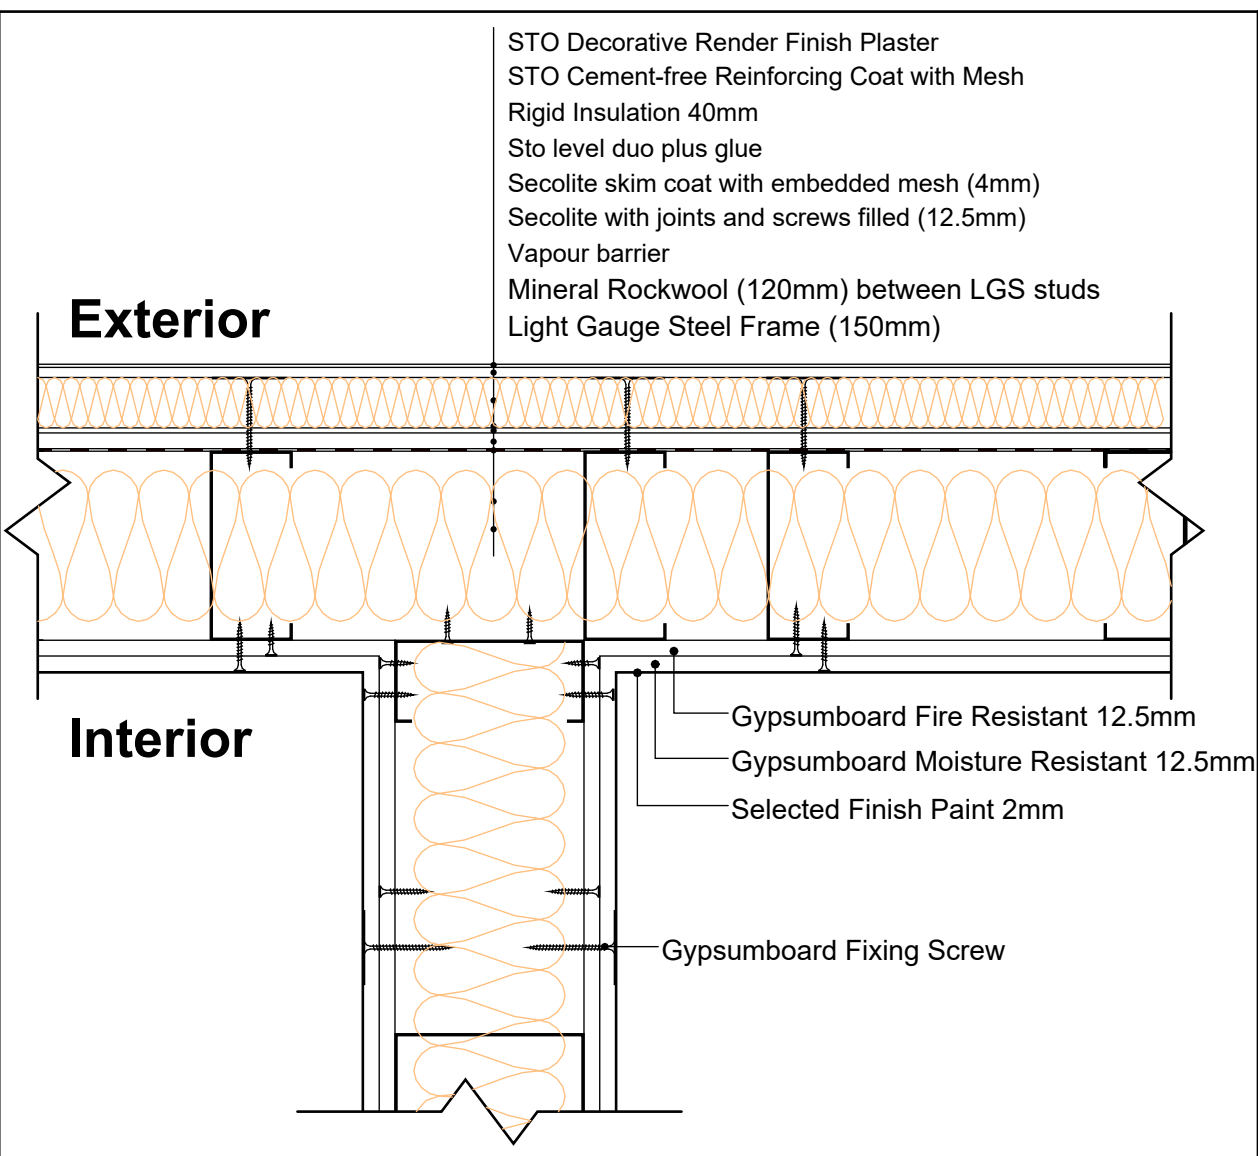

D.Exterior Corner Wall Sc: 1/6

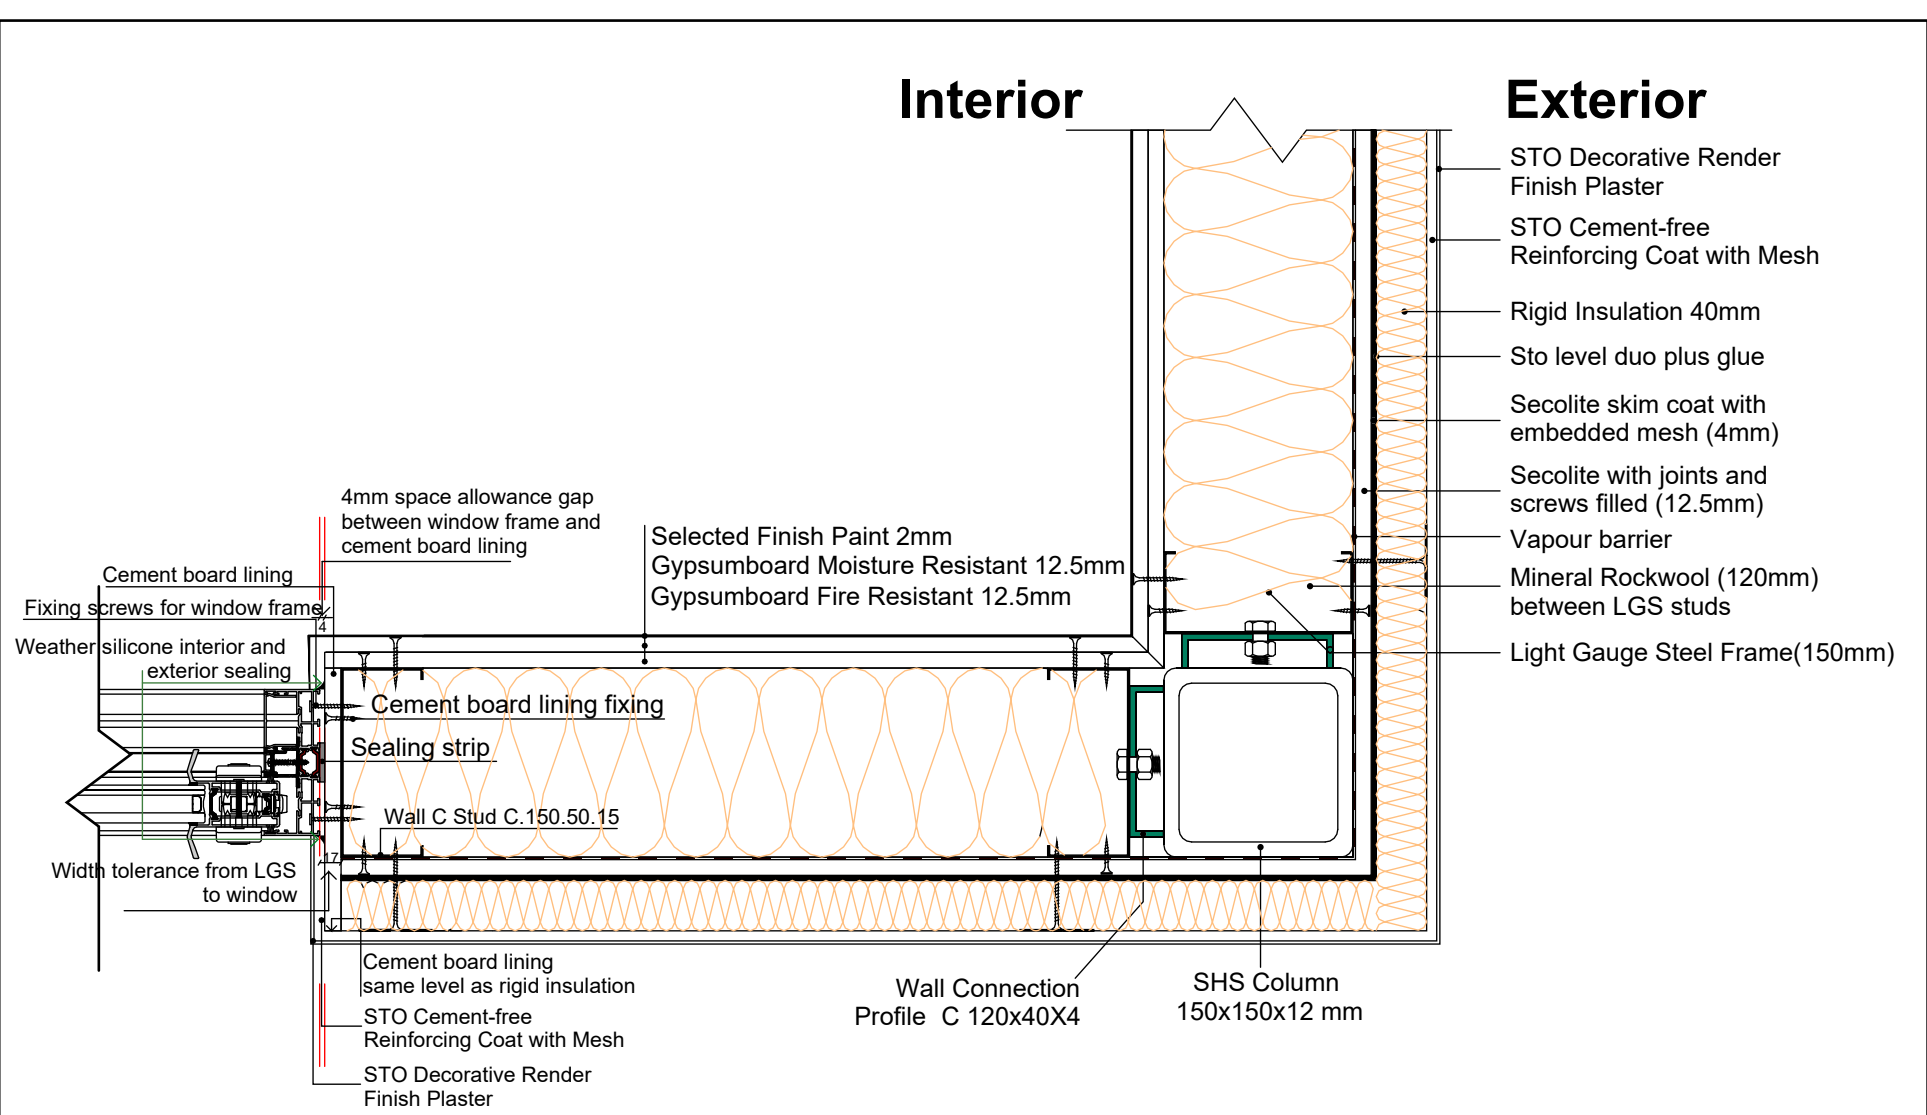

1. THESE DRAWINGS MUST BE CHECKED BY THE CUSTOMER OR CONTRACTOR PRIOR TO APPROVAL. ANY ERRORS OR OMISSIONS MUST BE REPORTED IN WRITING TO BAUHU PRIOR TO COMMENCEMENT OF CONSTRUCTION.
2. ARCHITECTURAL DRAWINGS SHOULD BE READ IN CONJUNCTION WITH STRUCTURAL DETAILING AND FABRICATION GENERAL ASSEMBLY DRAWINGS.
3. FOR CONSTRUCTION PURPOSES, USE ONLY THE LATEST APPROVED DRAWINGS LABELED 'ISSUED FOR CONSTRUCTION'.
4. DO NOT SCALE FROM THIS DRAWING.
5. THE COMPANY OPERATES USING METRIC DIMENSIONS AS THE PRINCIPAL DENOMINATION.
6. ALL CONCRETE WORKS ARE OUTSIDE OF THE SCOPE OF THE COMPANY. INFORMATION REGARDING SLAB DESIGN AND CONNECTIONS IN THESE DRAWINGS ARE INTENDED FOR GUIDENCE ONLY. FOUNDATION AND SLAB WORKS SHOULD BE DESIGNED AND APPROVED BY A LOCAL STRUCTURAL ENGINEER.
7. THE COMPANY RETAINS FULL TITLE AND OWNERSHIP OF THESE PLANS AND DESIGNS. ANY UNAUTHORISED USE, REPRODUCTION, OR DISTRIBUTION OF THESE PLANS, WHETHER IN WHOLE OR PART, IS EXPRESSLY PROHIBITED WITHOUT PRIOR WRITTEN CONSENT.
8. THE HYBRID STEEL FRAME CONSTRUCTION SYSTEM AND METHODOLOGY (PATENT PENDING) DESCRIBED IN THESE PLANS HAS BEEN DEVELOPED BY THE COMPANY AND IS SUBJECT TO A PROVISIONAL PATENT APPLICATION & ASSIGNMENT - US APPLICATION No. 63/722,841.

No.	Revision	Date
01	Moved walls under roof joists	13.03

- ISSUED FOR:
- ☐ Issued for information
 - ☐ Issued for client approval
 - ☐ Issued for fabrication
 - ☐ Issued for construction

Bahama Beach

DRAWING TITLE: Wall Details

DRAWN BY: Mladin Monica-Mihaela

SCALE:

DRAWING NO: A20

DATE: 17/03/2025

1. THESE DRAWINGS MUST BE CHECKED BY THE CUSTOMER OR CONTRACTOR PRIOR TO APPROVAL. ANY ERRORS OR OMISSIONS MUST BE REPORTED IN WRITING TO BAUHU PRIOR TO COMMENCEMENT OF CONSTRUCTION.
2. ARCHITECTURAL DRAWINGS SHOULD BE READ IN CONJUNCTION WITH STRUCTURAL DETAILING AND FABRICATION GENERAL ASSEMBLY DRAWINGS.
3. FOR CONSTRUCTION PURPOSES, USE ONLY THE LATEST APPROVED DRAWINGS LABELED 'ISSUED FOR CONSTRUCTION'.
4. DO NOT SCALE FROM THIS DRAWING.
5. THE COMPANY OPERATES USING METRIC DIMENSIONS AS THE PRINCIPAL DENOMINATION.
6. ALL CONCRETE WORKS ARE OUTSIDE OF THE SCOPE OF THE COMPANY. INFORMATION REGARDING SLAB DESIGN AND CONNECTIONS IN THESE DRAWINGS ARE INTENDED FOR GUIDANCE ONLY. FOUNDATION AND SLAB WORKS SHOULD BE DESIGNED AND APPROVED BY A LOCAL STRUCTURAL ENGINEER.
7. THE COMPANY RETAINS FULL TITLE AND OWNERSHIP OF THESE PLANS AND DESIGNS. ANY UNAUTHORISED USE, REPRODUCTION, OR DISTRIBUTION OF THESE PLANS, WHETHER IN WHOLE OR PART, IS EXPRESSLY PROHIBITED WITHOUT PRIOR WRITTEN CONSENT.
8. THE HYBRID STEEL FRAME CONSTRUCTION SYSTEM AND METHODOLOGY (PATENT PENDING) DESCRIBED IN THESE PLANS HAS BEEN DEVELOPED BY THE COMPANY AND IS SUBJECT TO A PROVISIONAL PATENT APPLICATION & ASSIGNMENT - US APPLICATION No. 63/722,841.

No.	Revision	Date
01	Moved walls under roof joists	13.03

ISSUED FOR:

Issued for information

Issued for client approval

Issued for fabrication

Issued for construction

Bahama Beach


DRAWING TITLE:
Island Style Roof Detail

DRAWN BY:
Mladin Monica-Mihaela

SCALE:

DRAWING NO:
A21

DATE:
17/03/2025

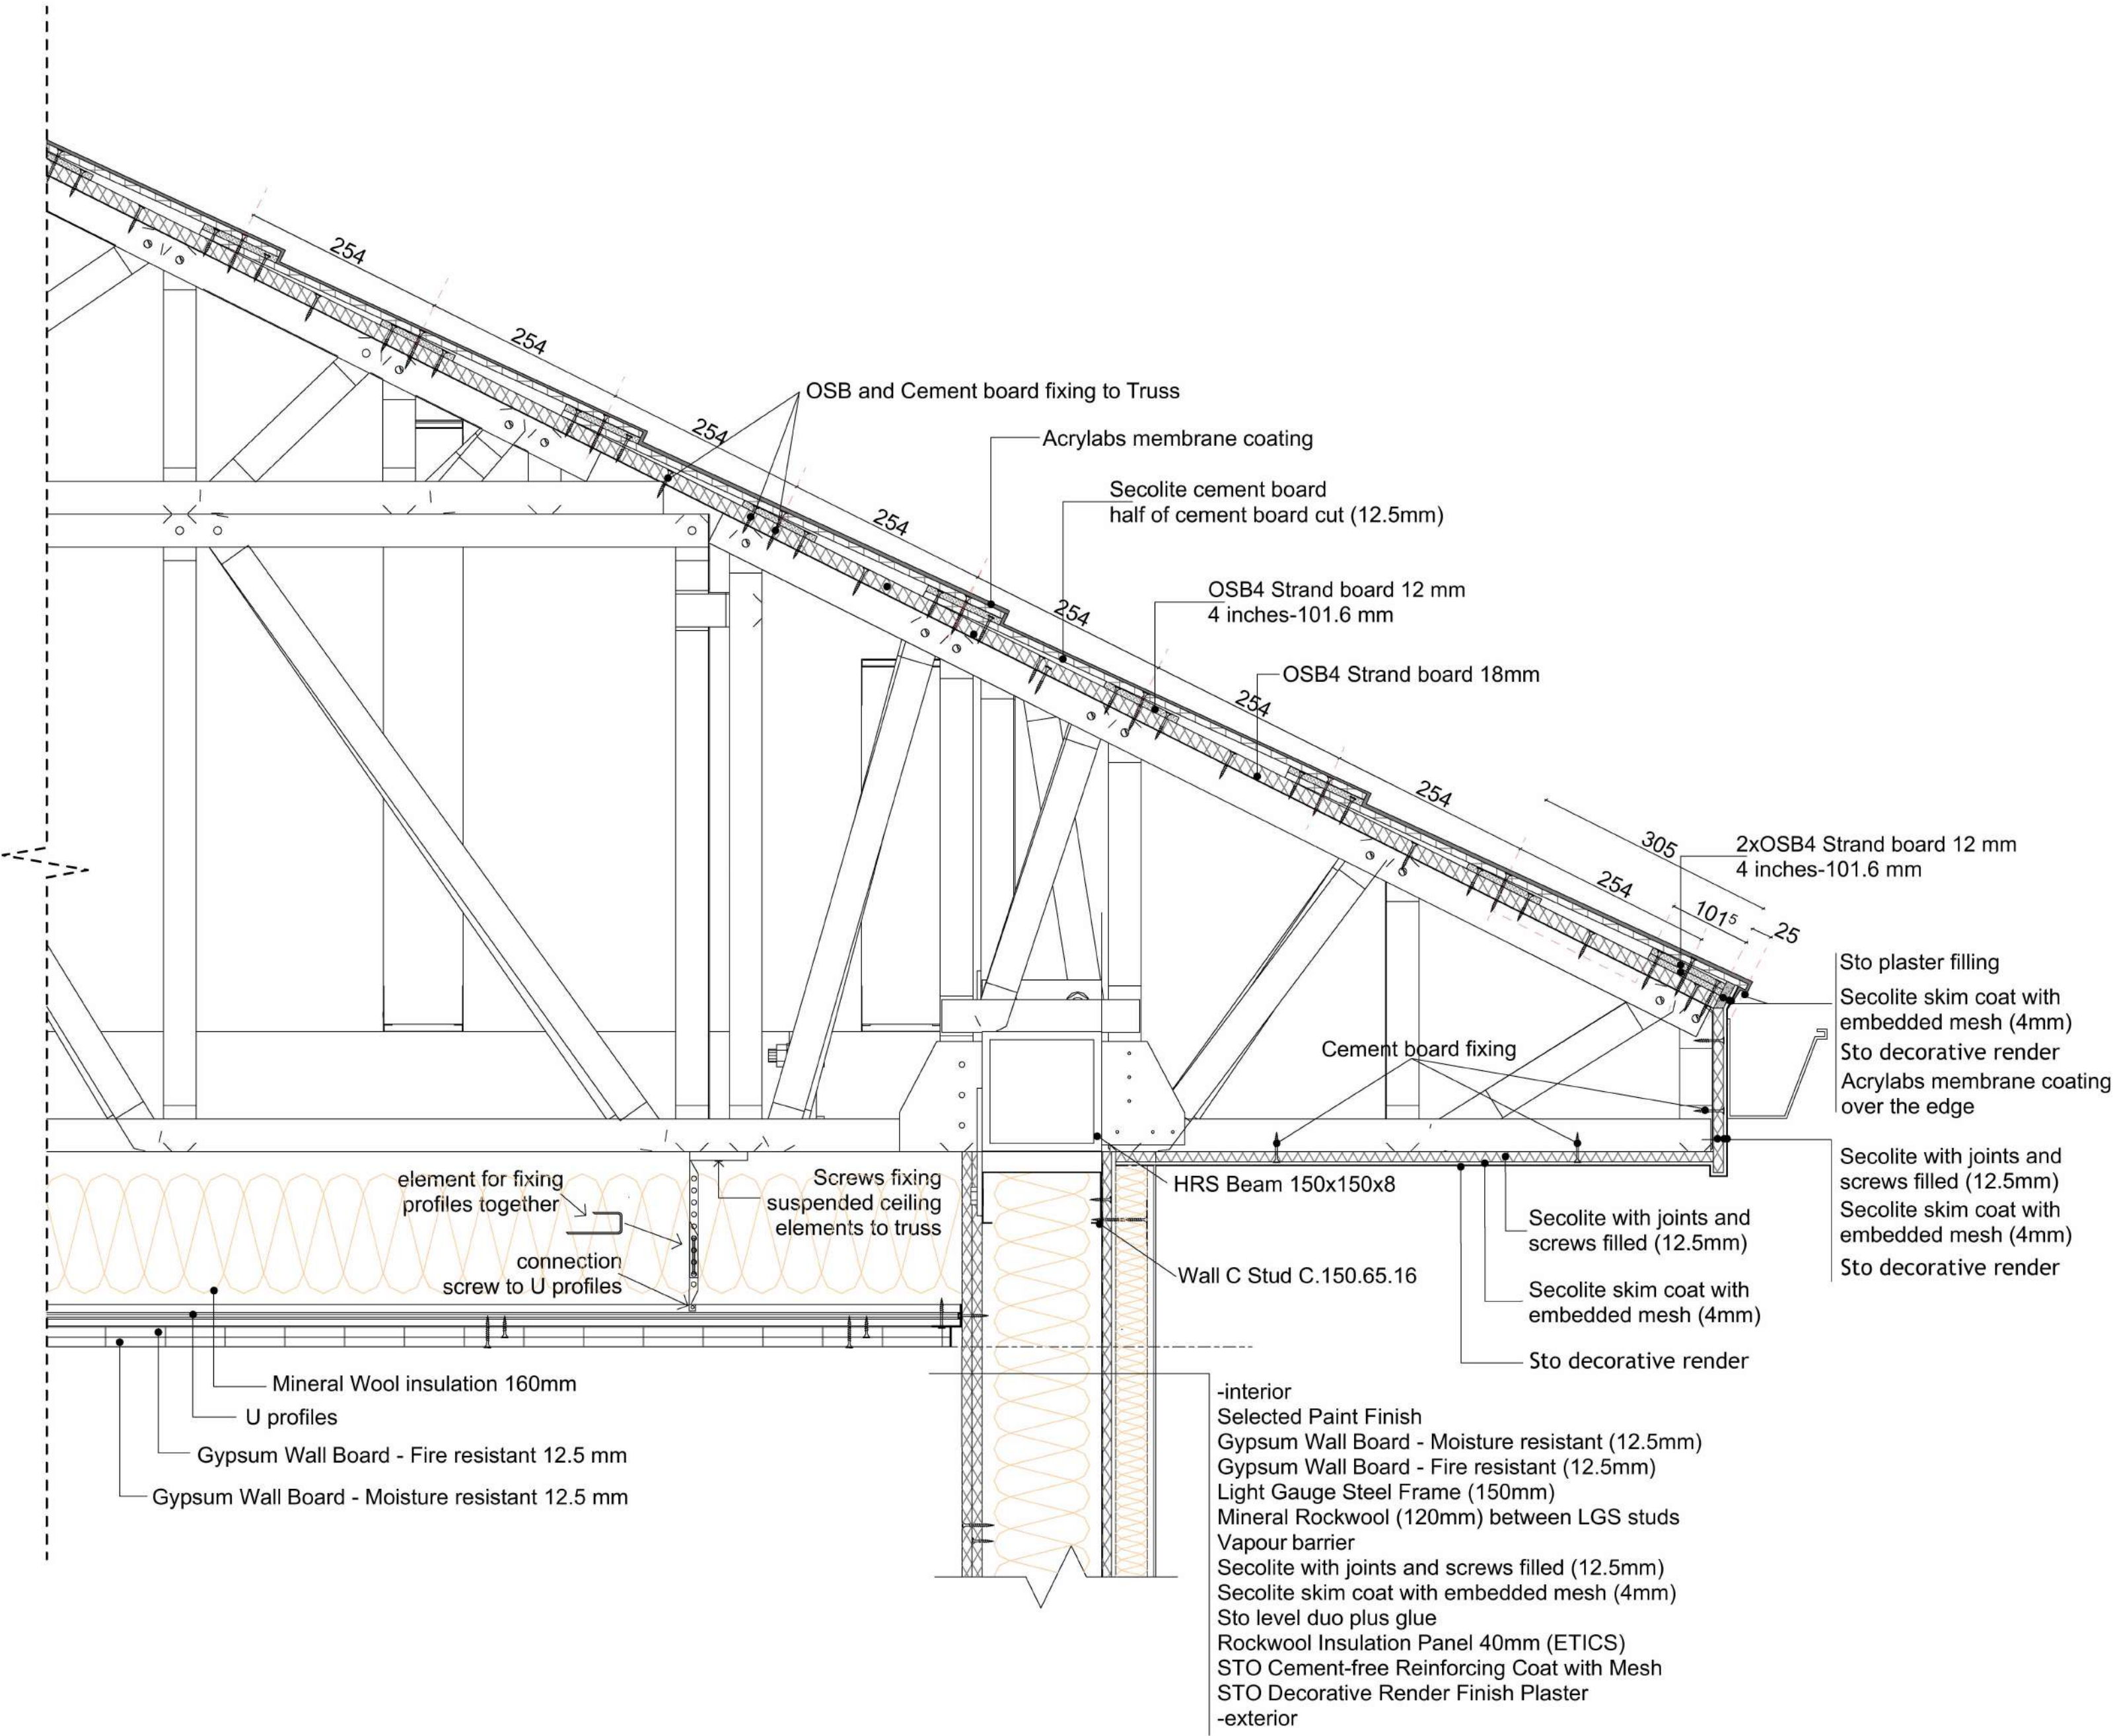

D.Island Style Roof Detail

1. THESE DRAWINGS MUST BE CHECKED BY THE CUSTOMER OR CONTRACTOR PRIOR TO APPROVAL. ANY ERRORS OR OMISSIONS MUST BE REPORTED IN WRITING TO BAUHU PRIOR TO COMMENCEMENT OF CONSTRUCTION.
2. ARCHITECTURAL DRAWINGS SHOULD BE READ IN CONJUNCTION WITH STRUCTURAL DETAILING AND FABRICATION GENERAL ASSEMBLY DRAWINGS.
3. FOR CONSTRUCTION PURPOSES, USE ONLY THE LATEST APPROVED DRAWINGS LABELED 'ISSUED FOR CONSTRUCTION'.
4. DO NOT SCALE FROM THIS DRAWING.
5. THE COMPANY OPERATES USING METRIC DIMENSIONS AS THE PRINCIPAL DENOMINATION.
6. ALL CONCRETE WORKS ARE OUTSIDE OF THE SCOPE OF THE COMPANY. INFORMATION REGARDING SLAB DESIGN AND CONNECTIONS IN THESE DRAWINGS ARE INTENDED FOR GUIDENCE ONLY. FOUNDATION AND SLAB WORKS SHOULD BE DESIGNED AND APPROVED BY A LOCAL STRUCTURAL ENGINEER.
7. THE COMPANY RETAINS FULL TITLE AND OWNERSHIP OF THESE PLANS AND DESIGNS. ANY UNAUTHORISED USE, REPRODUCTION, OR DISTRIBUTION OF THESE PLANS, WHETHER IN WHOLE OR PART, IS EXPRESSLY PROHIBITED WITHOUT PRIOR WRITTEN CONSENT.
8. THE HYBRID STEEL FRAME CONSTRUCTION SYSTEM AND METHODOLOGY (PATENT PENDING) DESCRIBED IN THESE PLANS HAS BEEN DEVELOPED BY THE COMPANY AND IS SUBJECT TO A PROVISIONAL PATENT APPLICATION & ASSIGNMENT - US APPLICATION No. 63/722,841.

No.	Revision	Date
01	Moved walls under roof joists	13.03

ISSUED FOR:

Issued for information

Issued for client approval

Issued for fabrication

Issued for construction

Bahama Beach


DRAWING TITLE:
Island Style Roof Detail

DRAWN BY:
Mladin Monica-Mihaela


SCALE:

DRAWING NO:
A22

DATE:
17/03/2025

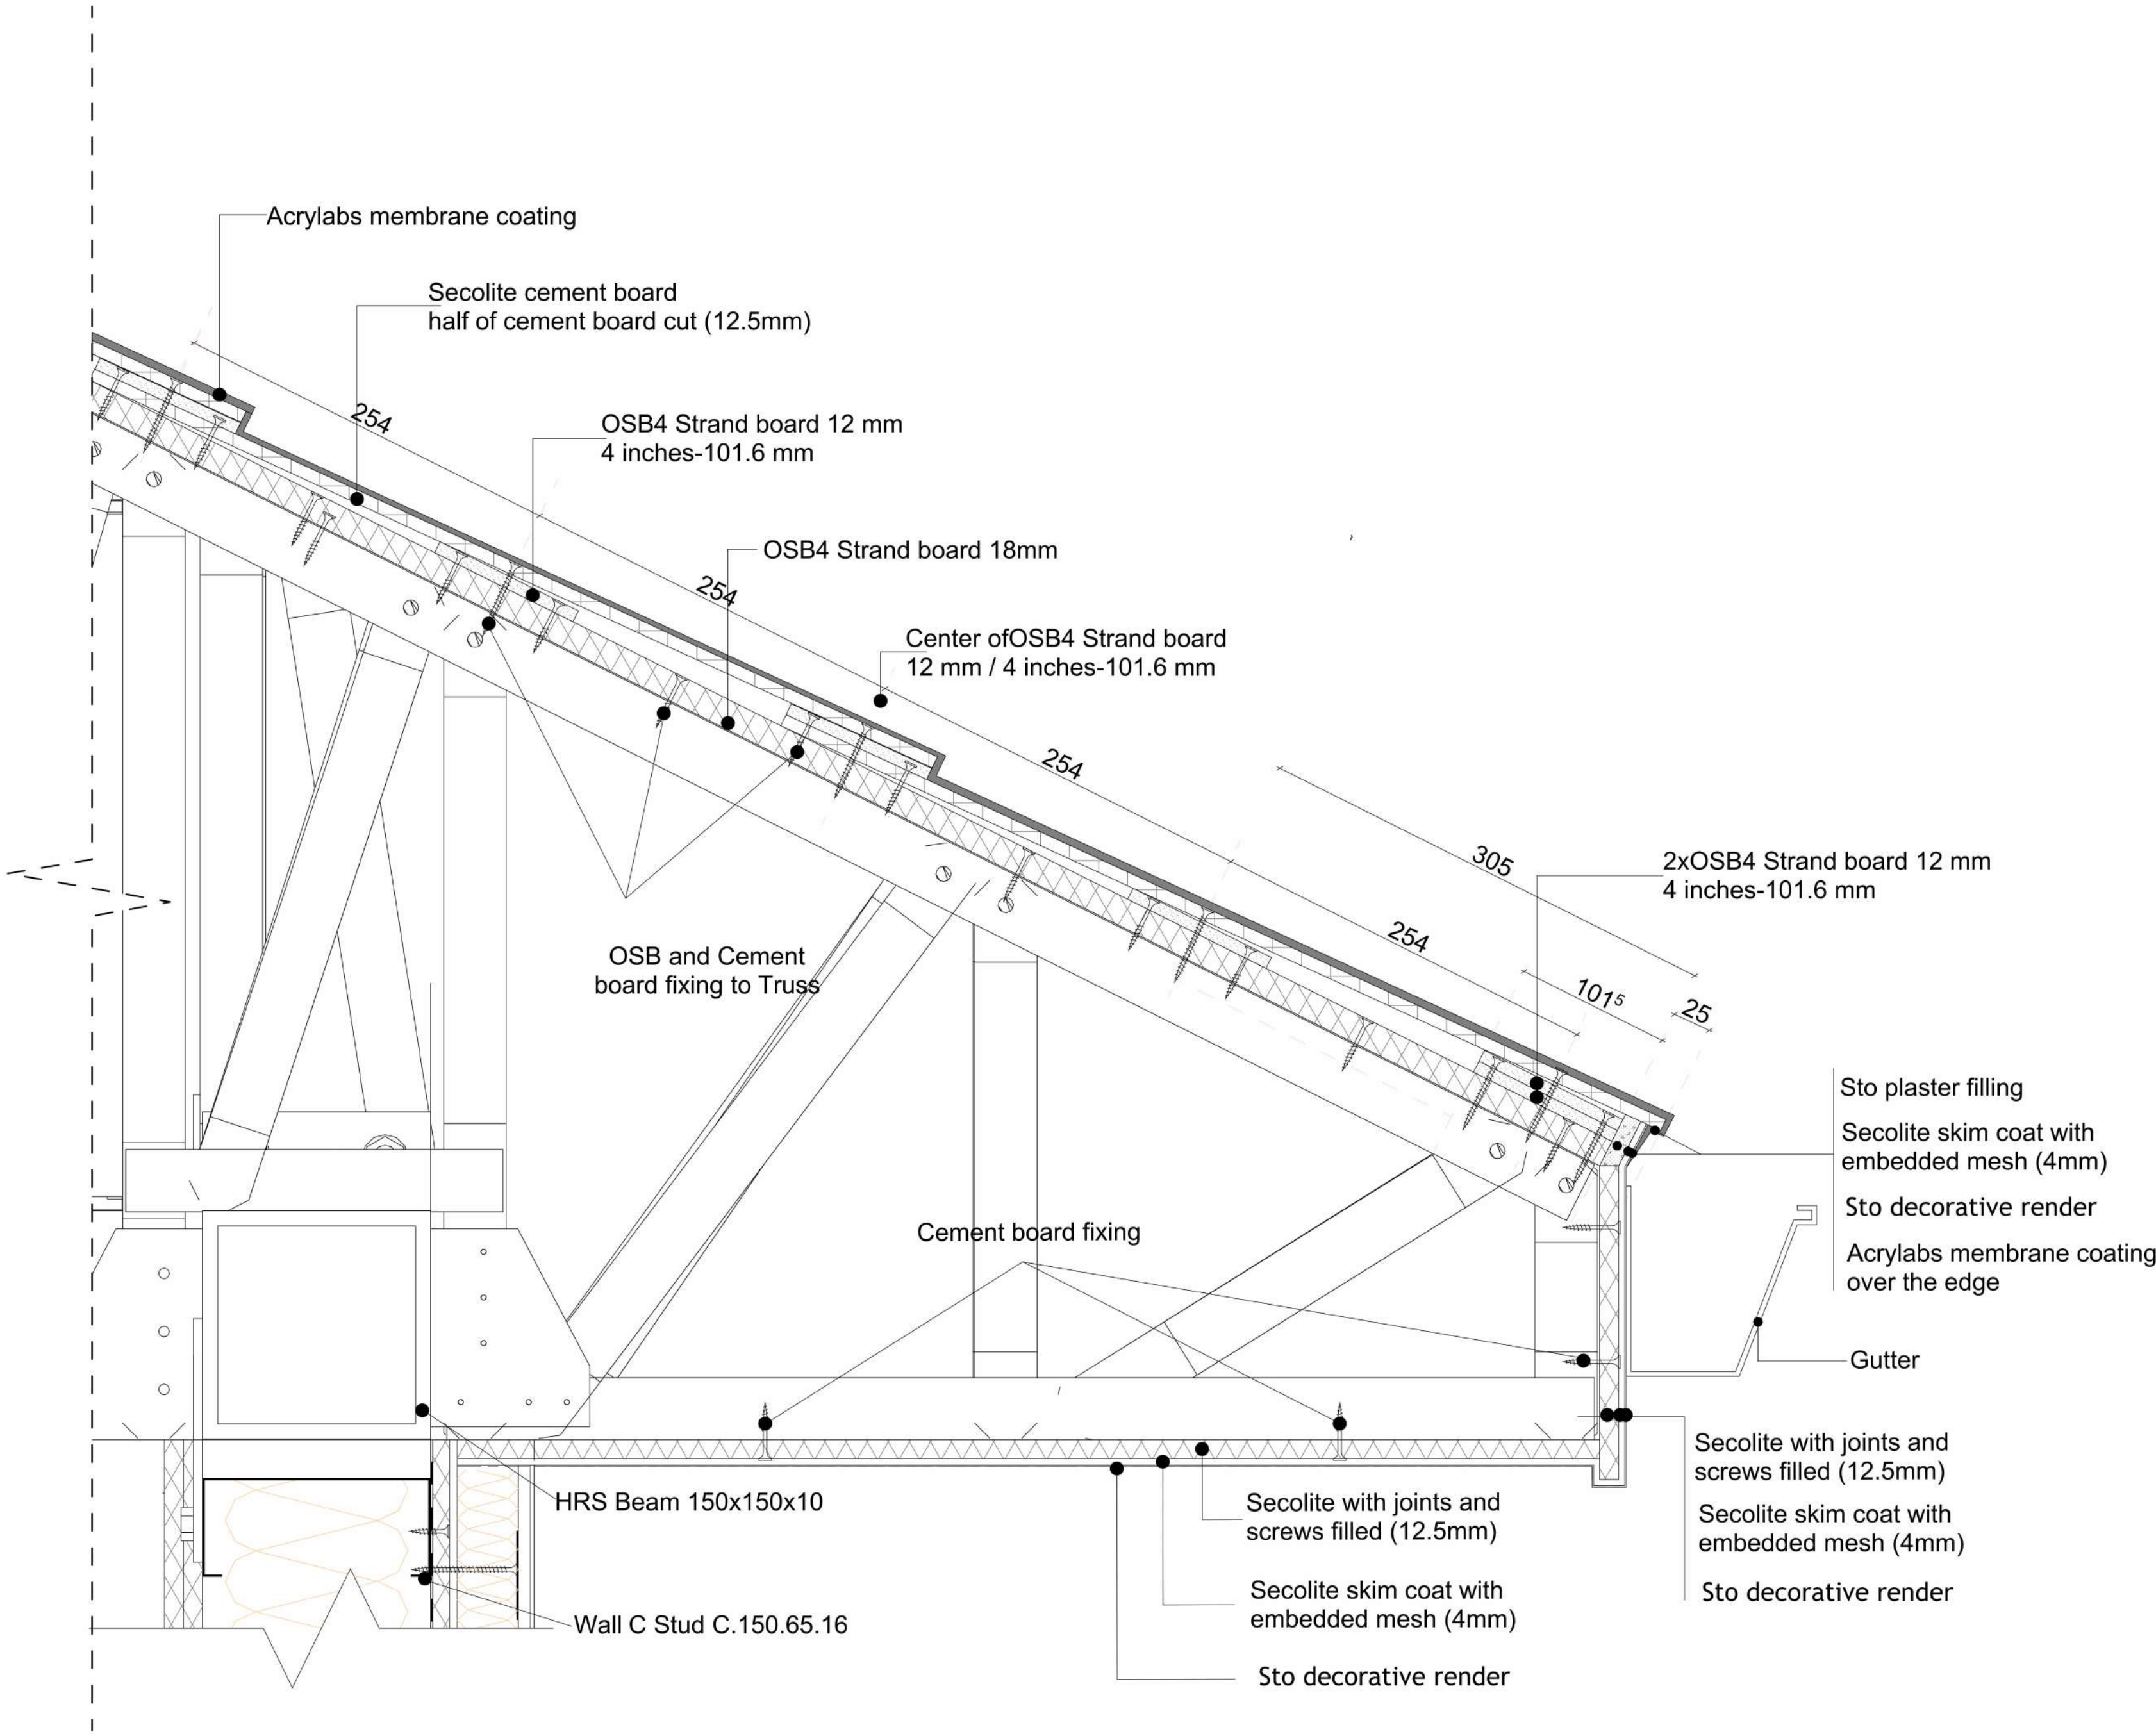

D.Island Style Roof Detail

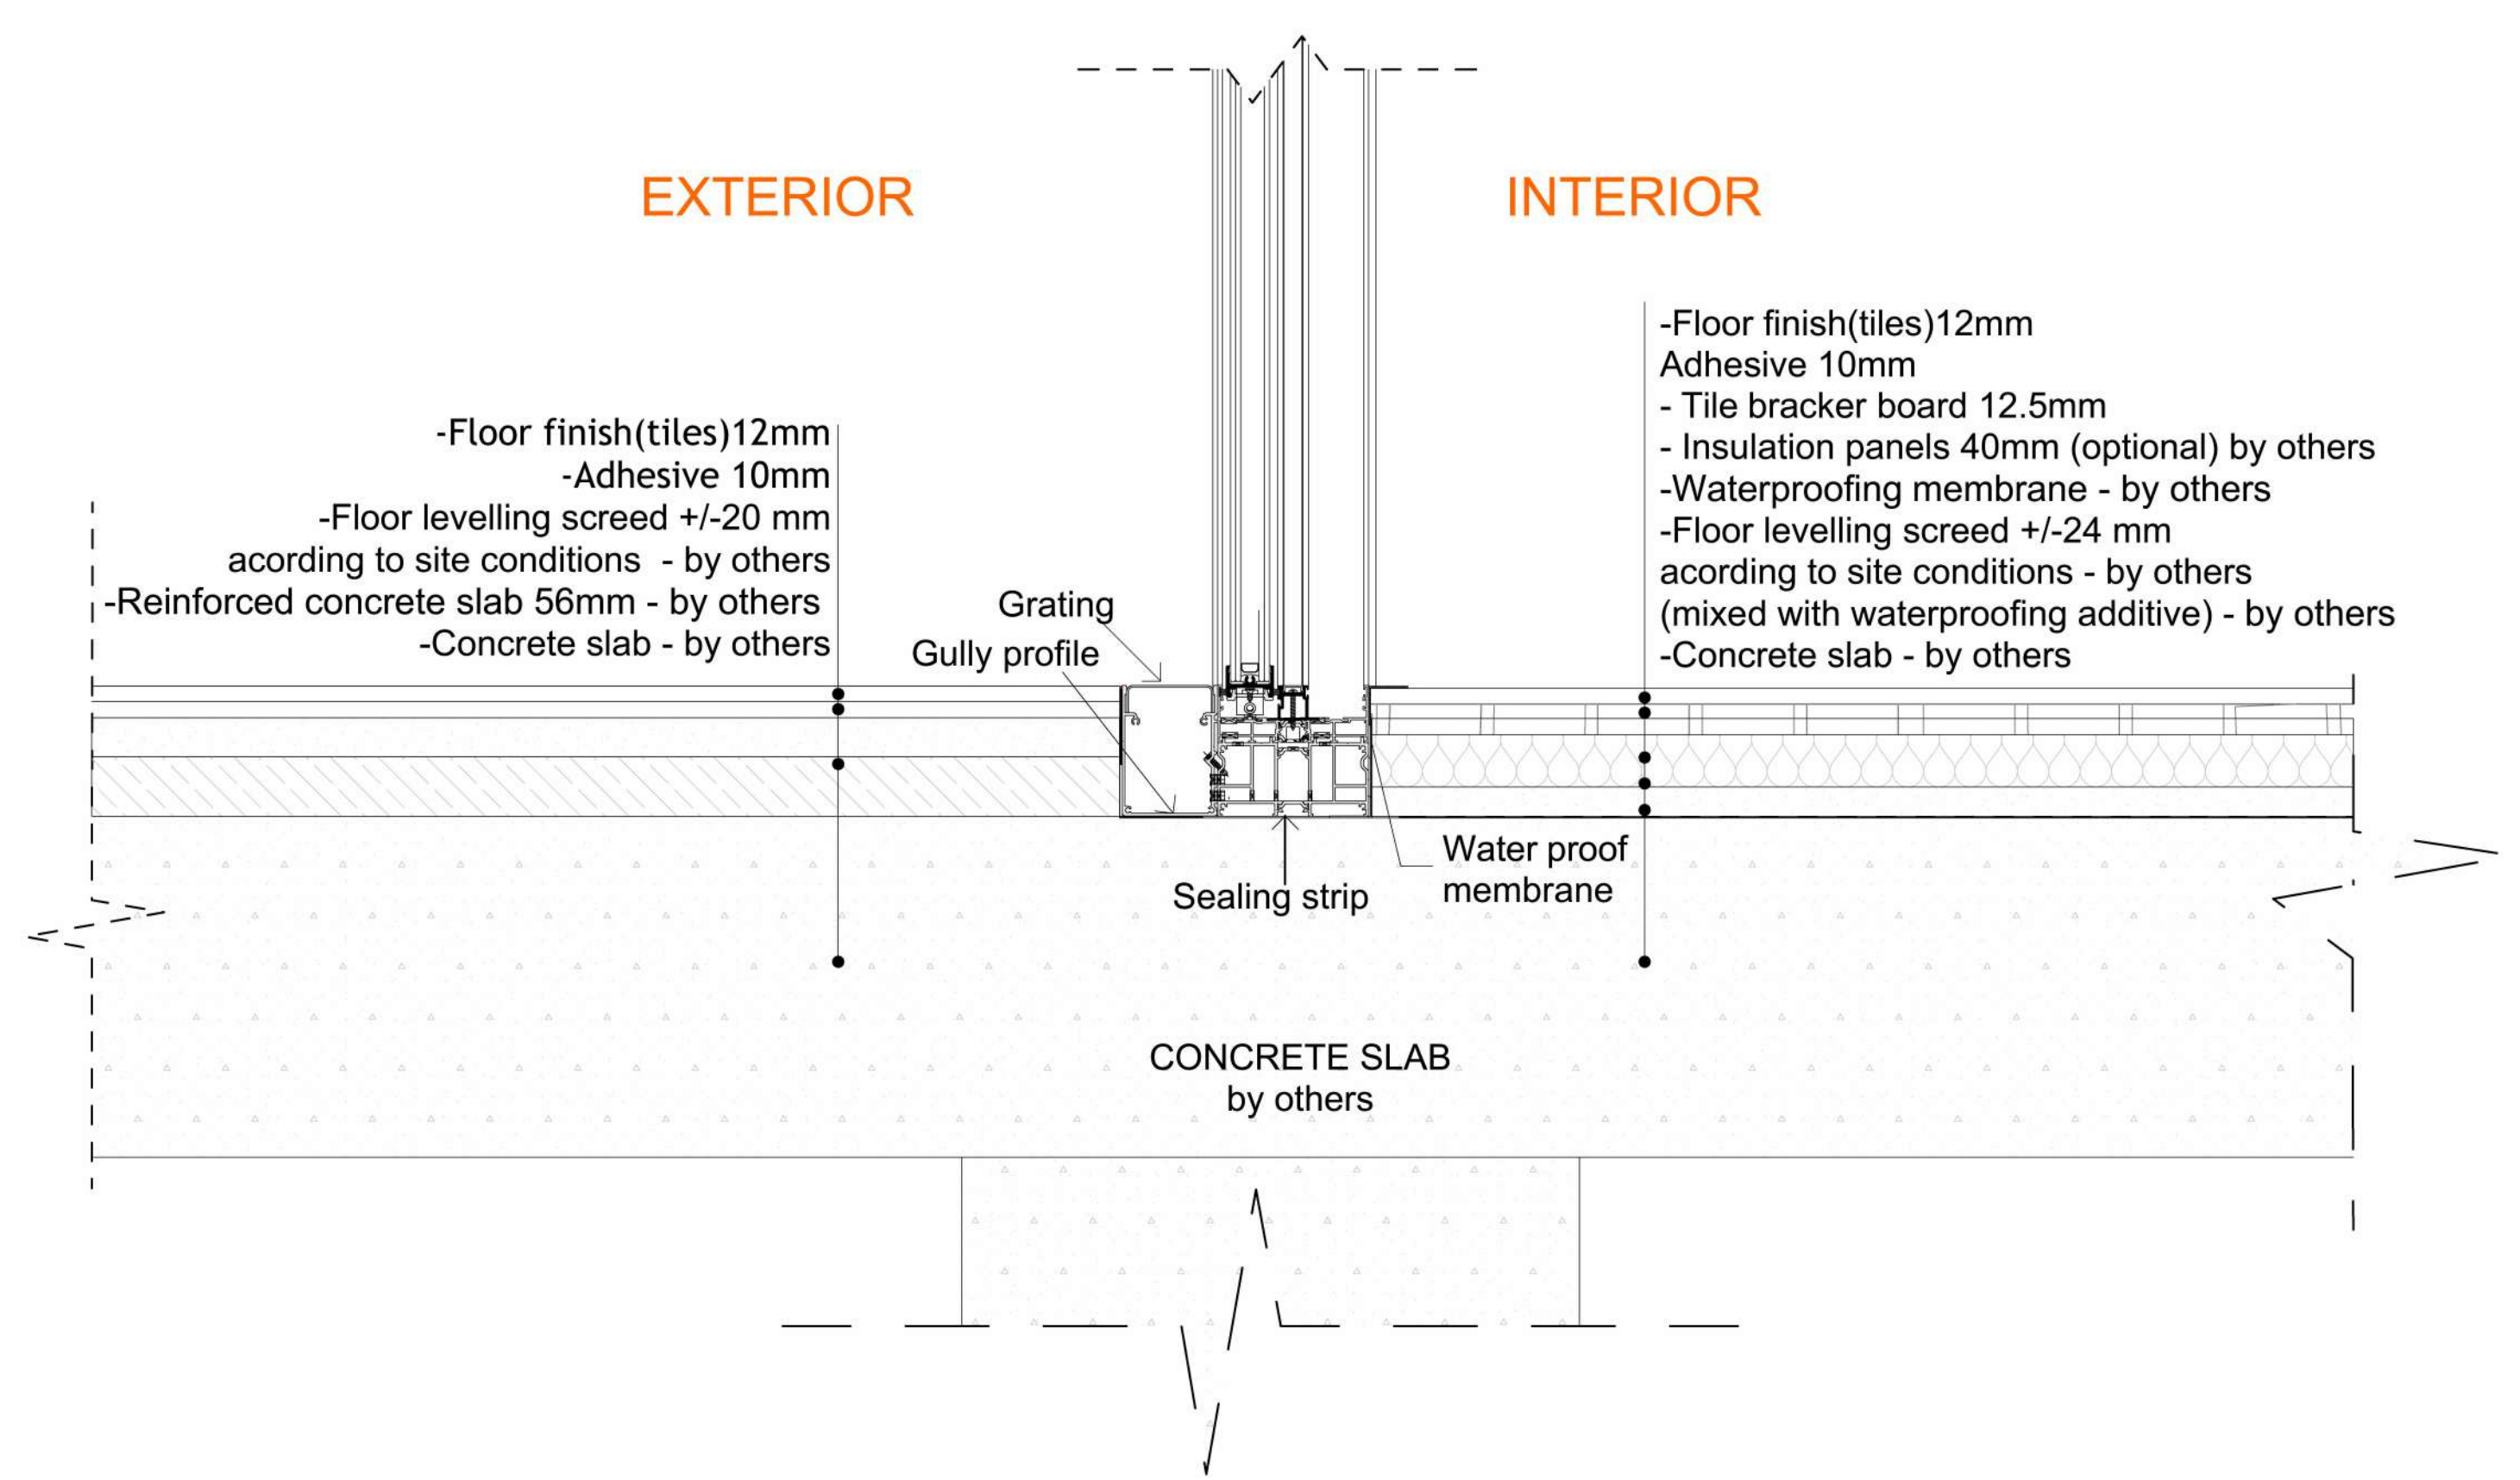

D5.Sliding Door/Window Section
Ground Floor

BAUHU

MODULAR • BUILDING • SOLUTIONS

1. THESE DRAWINGS MUST BE CHECKED BY THE CUSTOMER OR CONTRACTOR PRIOR TO APPROVAL. ANY ERRORS OR OMISSIONS MUST BE REPORTED IN WRITING TO BAUHU PRIOR TO COMMENCEMENT OF CONSTRUCTION.

2. ARCHITECTURAL DRAWINGS SHOULD BE READ IN CONJUNCTION WITH STRUCTURAL DETAILING AND FABRICATION GENERAL ASSEMBLY DRAWINGS.

3. FOR CONSTRUCTION PURPOSES, USE ONLY THE LATEST APPROVED DRAWINGS LABELED 'ISSUED FOR CONSTRUCTION'.

4. DO NOT SCALE FROM THIS DRAWING.

5. THE COMPANY OPERATES USING METRIC DIMENSIONS AS THE PRINCIPAL DENOMINATION.

6. ALL CONCRETE WORKS ARE OUTSIDE OF THE SCOPE OF THE COMPANY. INFORMATION REGARDING SLAB DESIGN AND CONNECTIONS IN THESE DRAWINGS ARE INTENDED FOR GUIDENCE ONLY. FOUNDATION AND SLAB WORKS SHOULD BE DESIGNED AND APPROVED BY A LOCAL STRUCTURAL ENGINEER.

7. THE COMPANY RETAINS FULL TITLE AND OWNERSHIP OF THESE PLANS AND DESIGNS. ANY UNAUTHORISED USE, REPRODUCTION, OR DISTRIBUTION OF THESE PLANS, WHETHER IN WHOLE OR PART, IS EXPRESSLY PROHIBITED WITHOUT PRIOR WRITTEN CONSENT.

8. THE HYBRID STEEL FRAME CONSTRUCTION SYSTEM AND METHODOLOGY (PATENT PENDING) DESCRIBED IN THESE PLANS HAS BEEN DEVELOPED BY THE COMPANY AND IS SUBJECT TO A PROVISIONAL PATENT APPLICATION & ASSIGNMENT - US APPLICATION No. 63/722,841.

No.	Revision	Date
01	Moved walls under roof joists	13.03

ISSUED FOR:

Issued for information

Issued for client approval

Issued for fabrication

Issued for construction

Bahama Beach

DRAWING TITLE:

Sliding Door Section Detail - base

DRAWN BY:

Mladin Monica-Mihaela


SCALE:

DRAWING NO:

A23

DATE:

17/03/2025

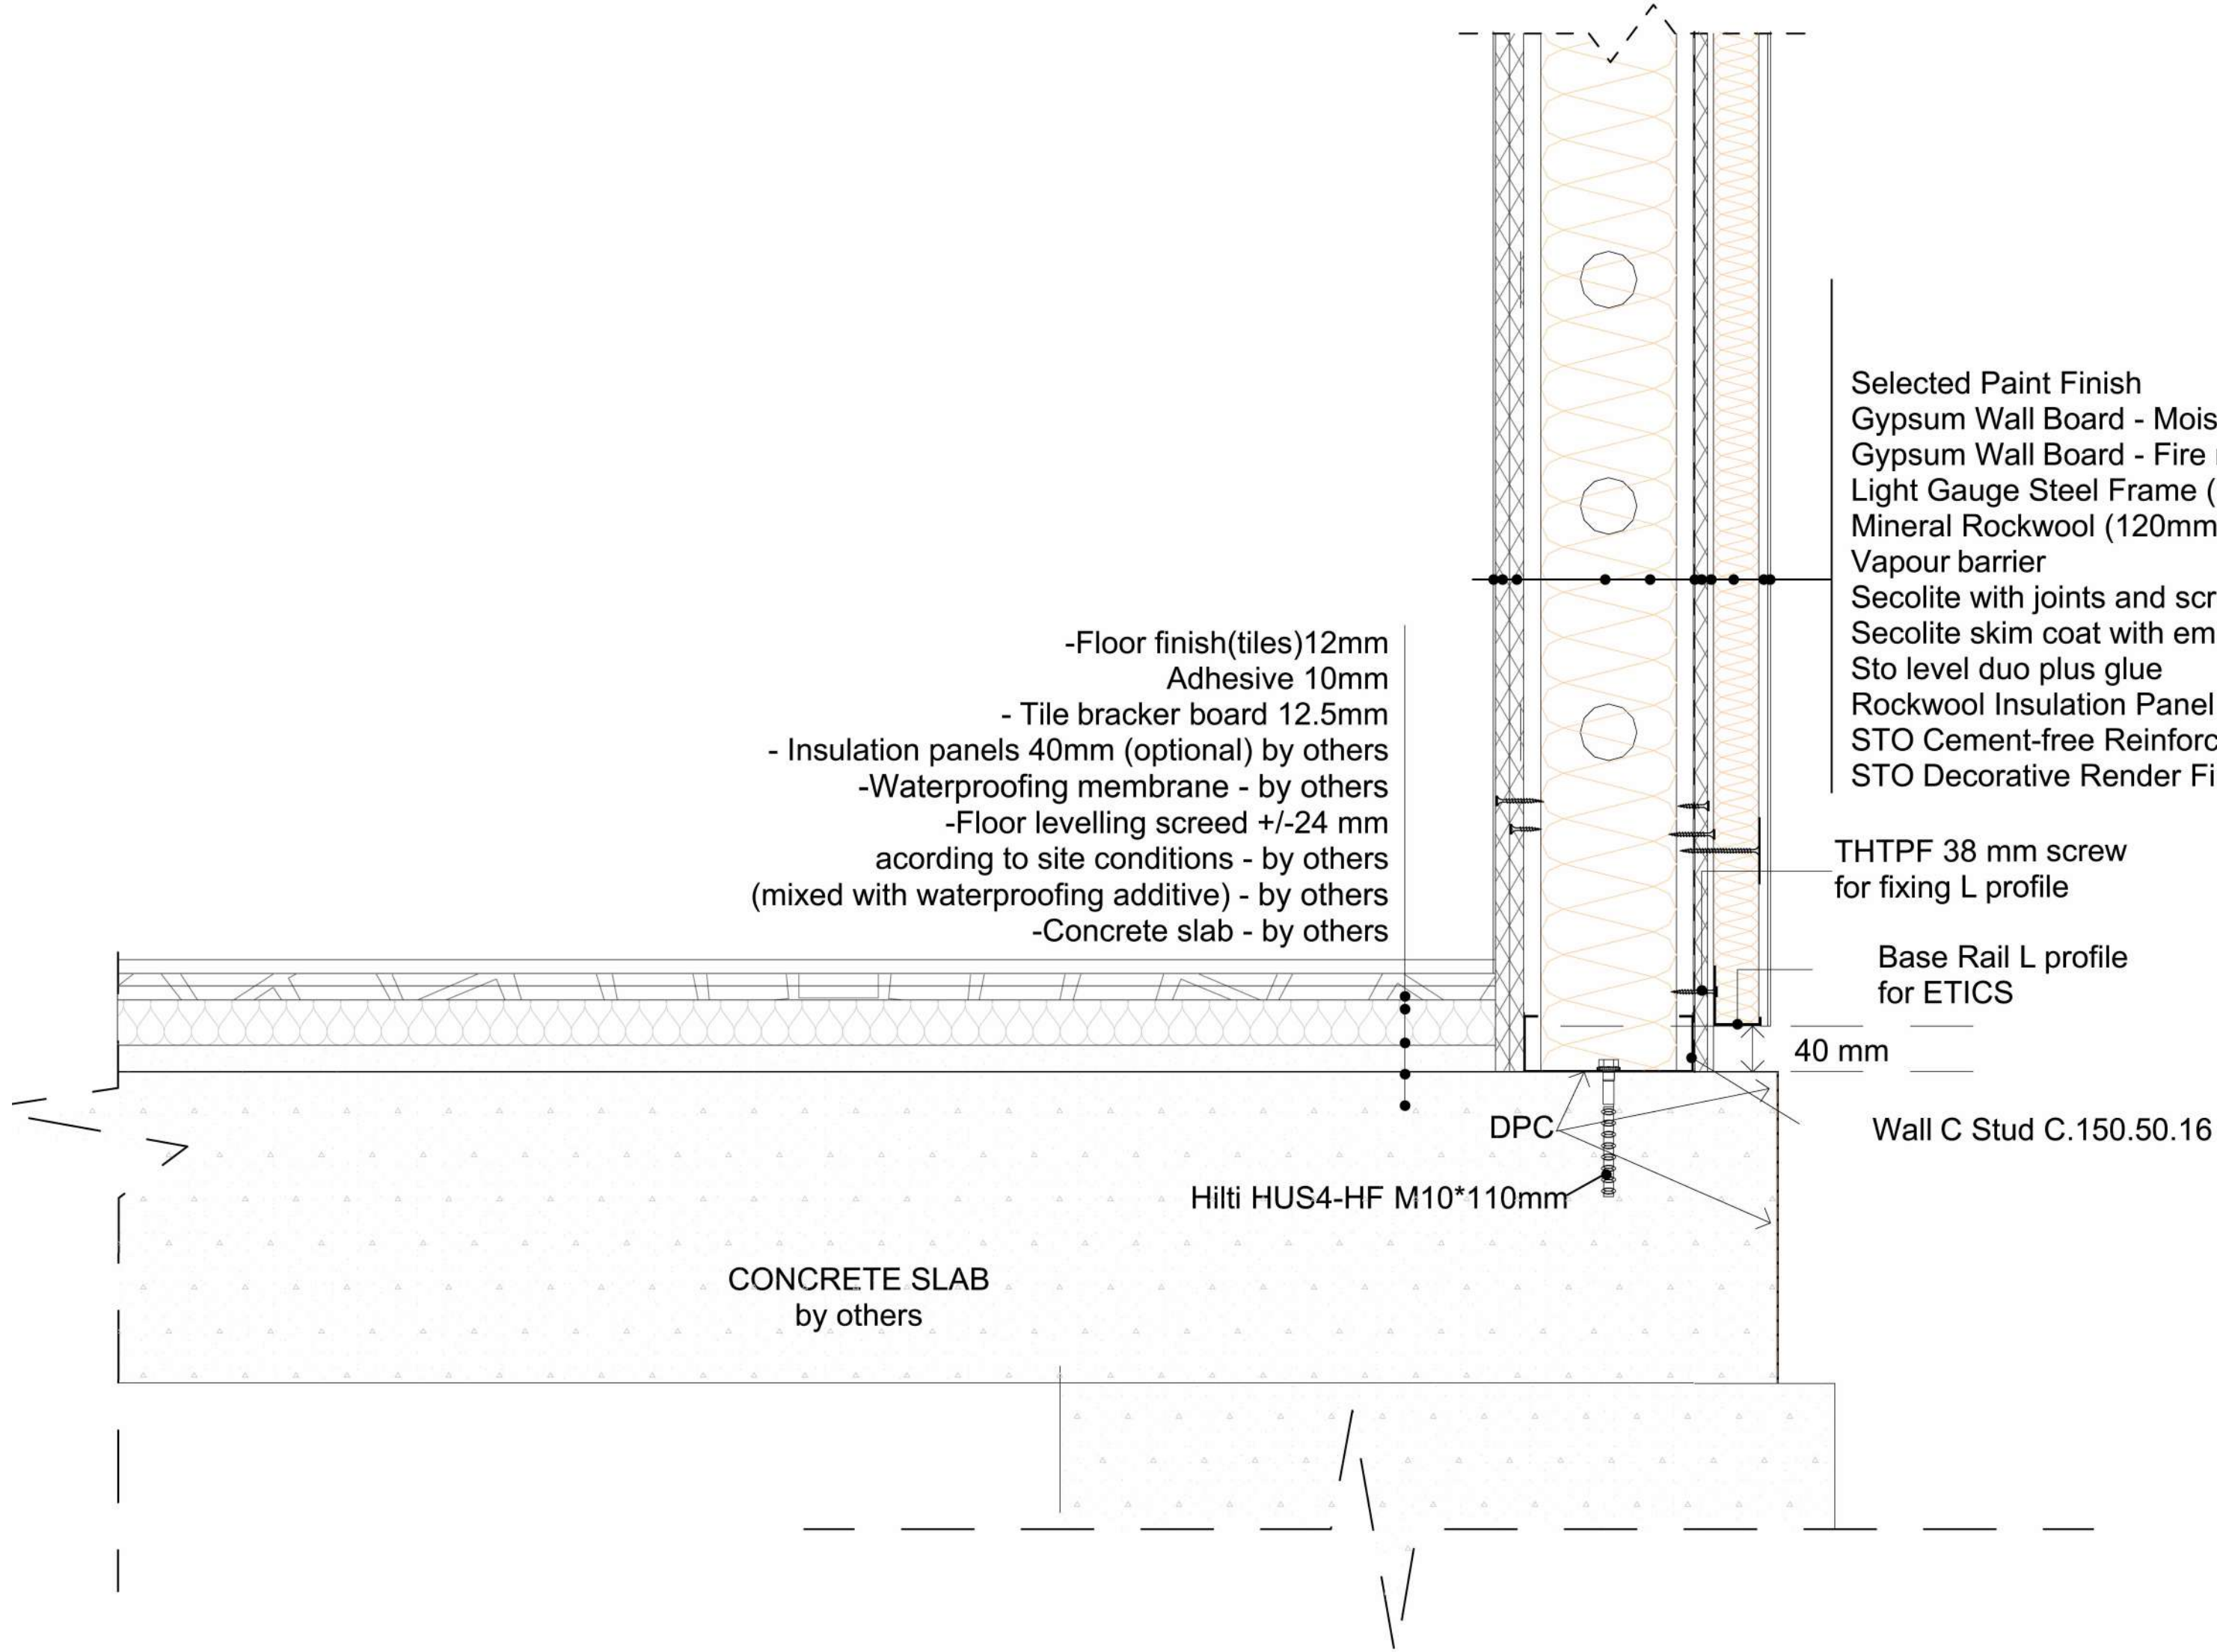

1. THESE DRAWINGS MUST BE CHECKED BY THE CUSTOMER OR CONTRACTOR PRIOR TO APPROVAL. ANY ERRORS OR OMISSIONS MUST BE REPORTED IN WRITING TO BAUHU PRIOR TO COMMENCEMENT OF CONSTRUCTION.
2. ARCHITECTURAL DRAWINGS SHOULD BE READ IN CONJUNCTION WITH STRUCTURAL DETAILING AND FABRICATION GENERAL ASSEMBLY DRAWINGS.
3. FOR CONSTRUCTION PURPOSES, USE ONLY THE LATEST APPROVED DRAWINGS LABELED 'ISSUED FOR CONSTRUCTION'.
4. DO NOT SCALE FROM THIS DRAWING.
5. THE COMPANY OPERATES USING METRIC DIMENSIONS AS THE PRINCIPAL DENOMINATION.
6. ALL CONCRETE WORKS ARE OUTSIDE OF THE SCOPE OF THE COMPANY. INFORMATION REGARDING SLAB DESIGN AND CONNECTIONS IN THESE DRAWINGS ARE INTENDED FOR GUIDENCE ONLY. FOUNDATION AND SLAB WORKS SHOULD BE DESIGNED AND APPROVED BY A LOCAL STRUCTURAL ENGINEER.
7. THE COMPANY RETAINS FULL TITLE AND OWNERSHIP OF THESE PLANS AND DESIGNS. ANY UNAUTHORISED USE, REPRODUCTION, OR DISTRIBUTION OF THESE PLANS, WHETHER IN WHOLE OR PART, IS EXPRESSLY PROHIBITED WITHOUT PRIOR WRITTEN CONSENT.
8. THE HYBRID STEEL FRAME CONSTRUCTION SYSTEM AND METHODOLOGY (PATENT PENDING) DESCRIBED IN THESE PLANS HAS BEEN DEVELOPED BY THE COMPANY AND IS SUBJECT TO A PROVISIONAL PATENT APPLICATION & ASSIGNMENT - US APPLICATION No. 63/722,841.

No.	Revision	Date
01	Moved walls under roof joists	13.03

- ISSUED FOR:
- Issued for information
 - Issued for client approval
 - Issued for fabrication
 - Issued for construction

Bahama Beach

DRAWING TITLE:
Exterior wall base Detail


DRAWN BY:
Mladin Monica-Mihaela

SCALE:

DRAWING NO:
A24

DATE:
17/03/2025

D10.Exterior wall base Detail

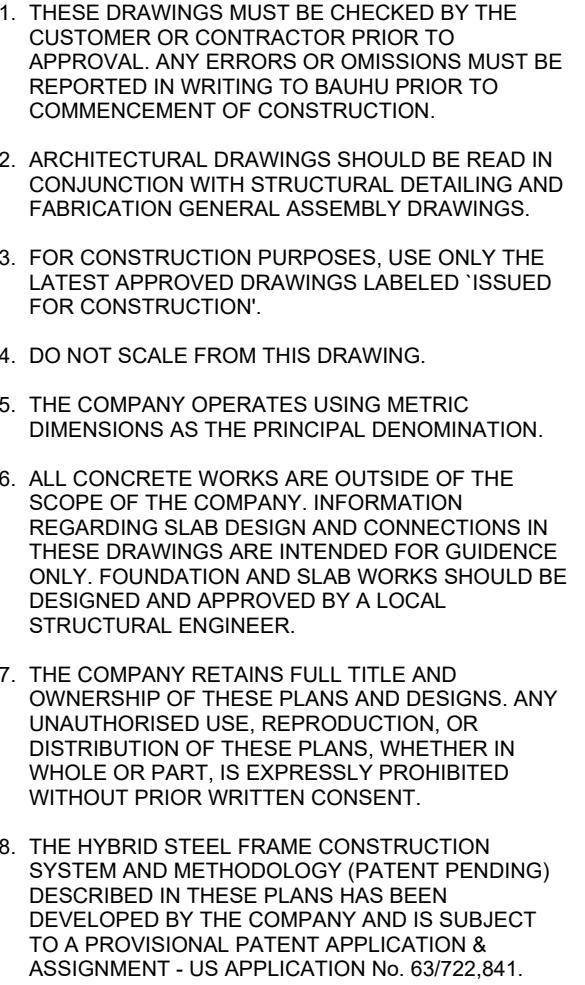[illegible]

Issued for information

Issued for client approval

Issued for fabrication

Issued for construction

DRAWING TITLE:
Exterior terrace base Detail


DRAWN BY:

Mladin Monica-Mihaela

SCALE:

DRAWING NO: A25

DATE: 17/03/2025

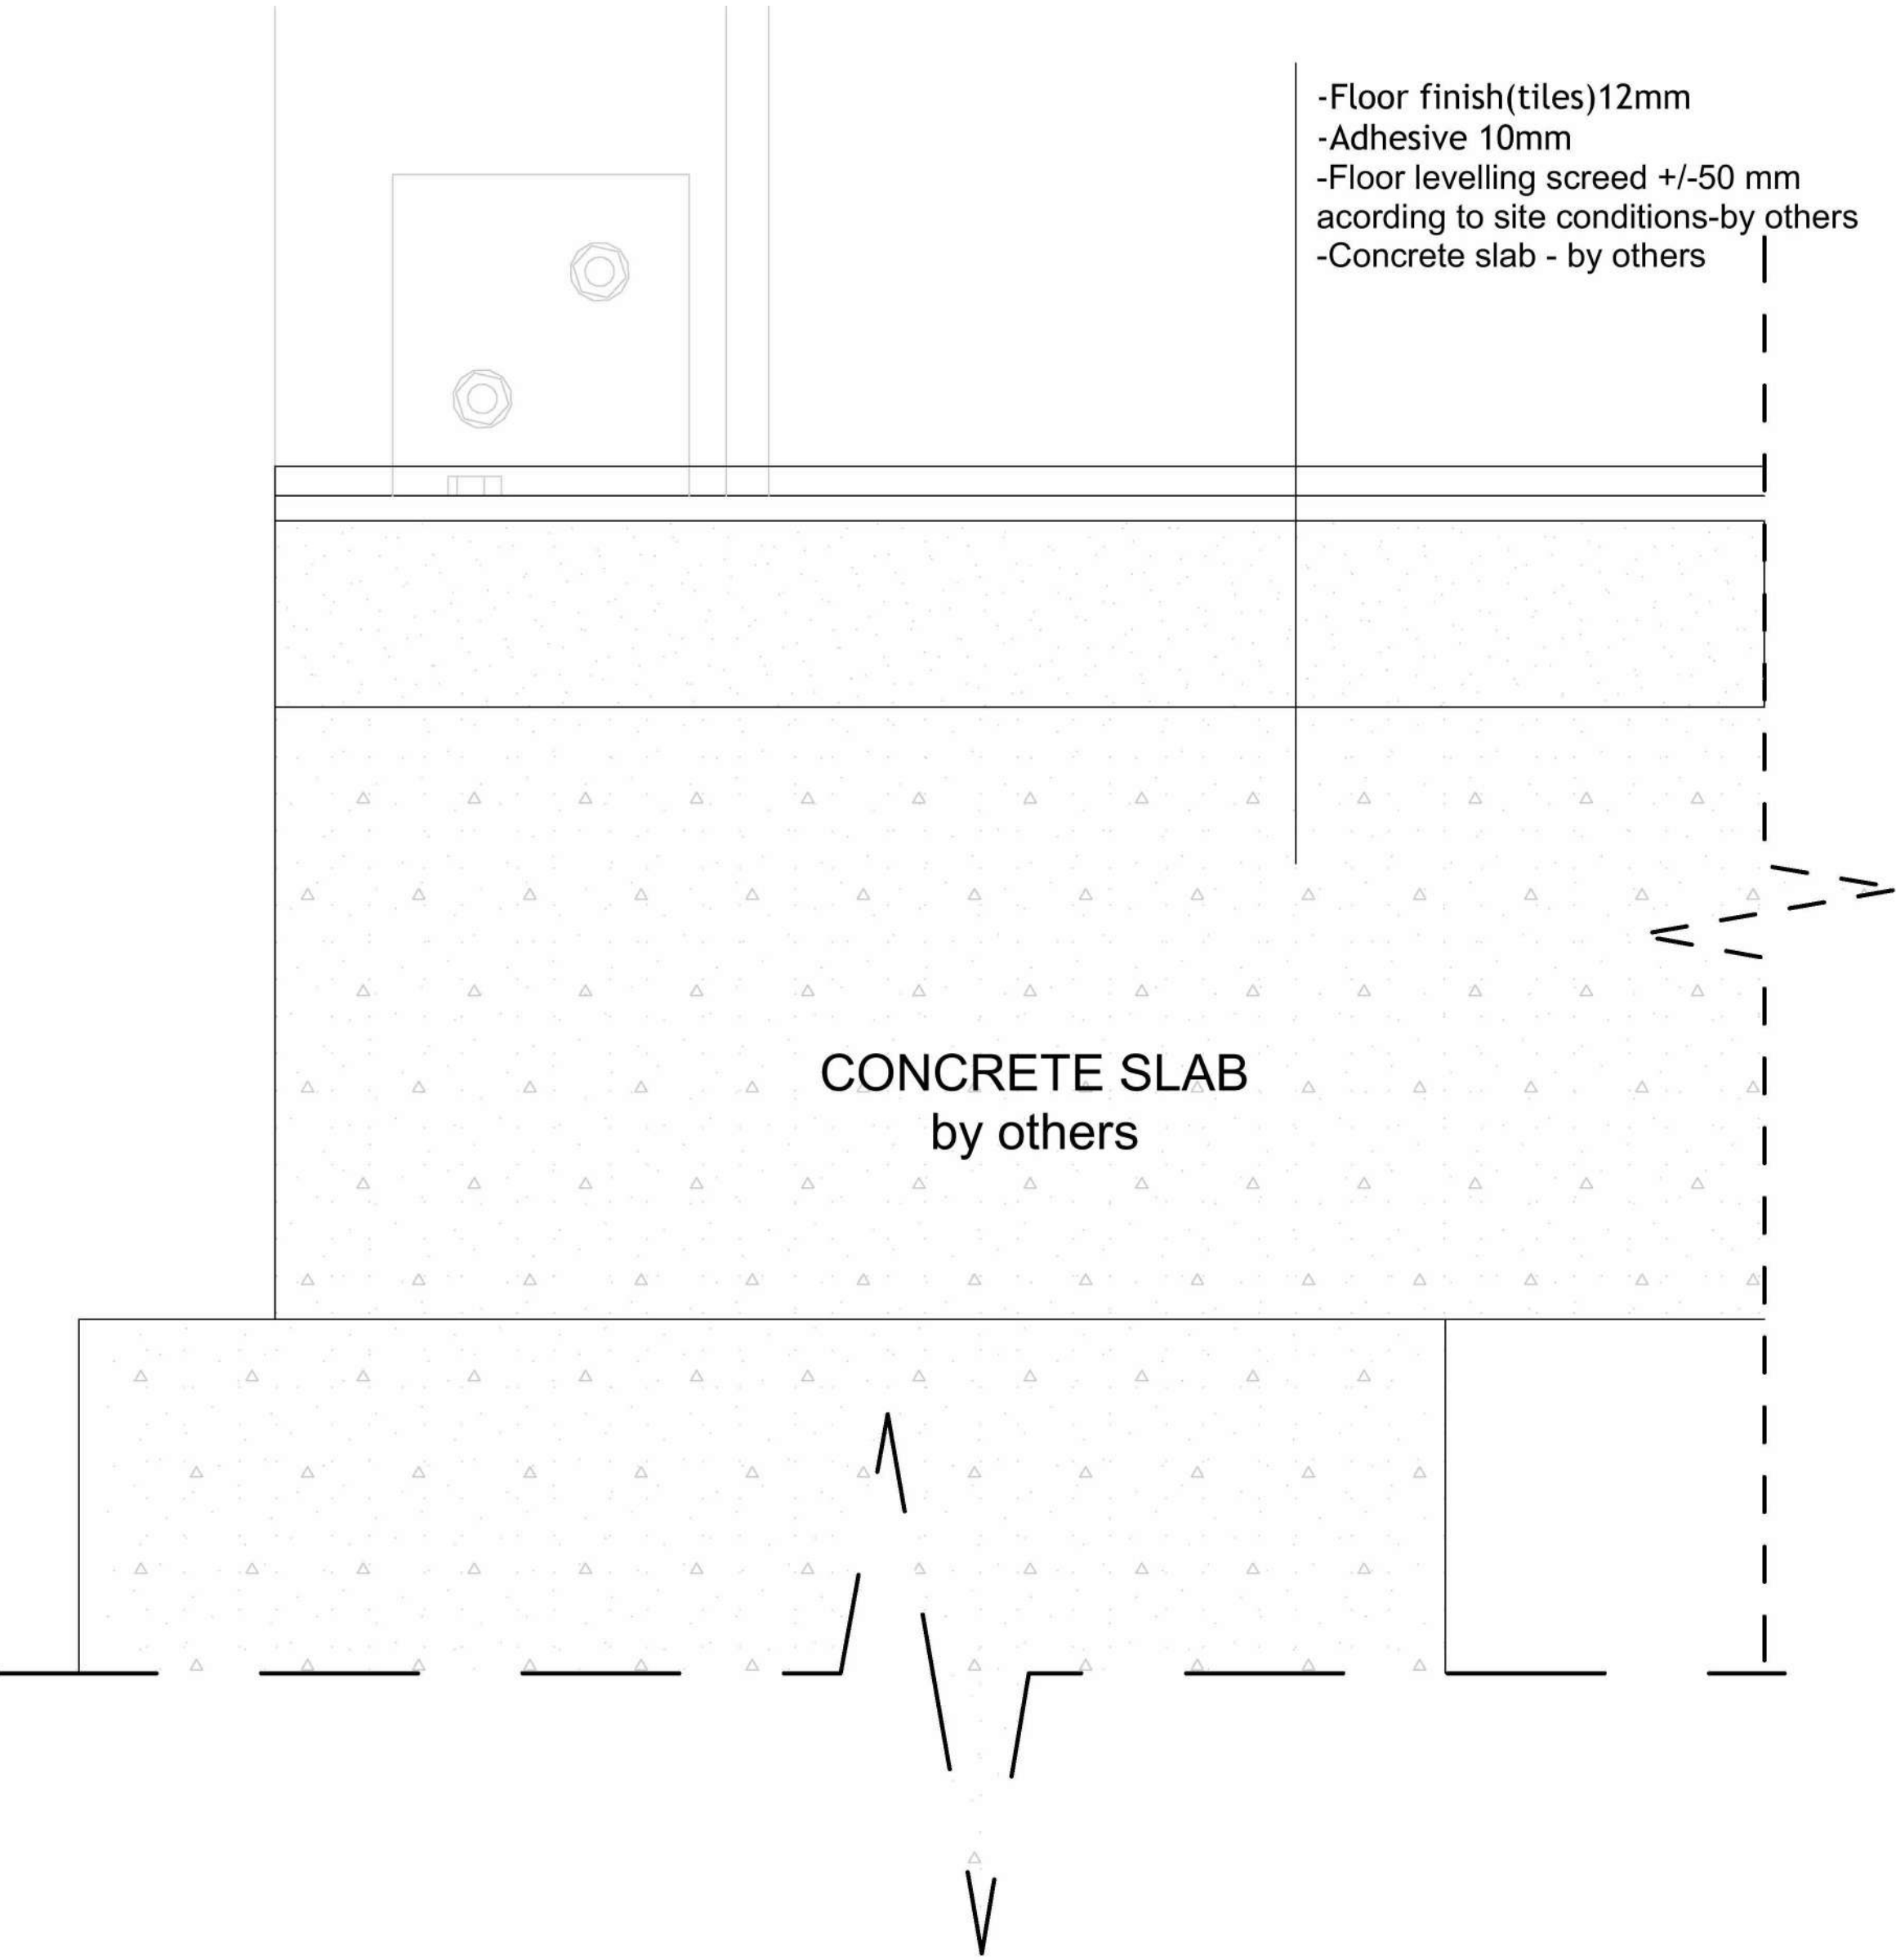

D11.Exterior terrace base Detail

- THESE DRAWINGS MUST BE CHECKED BY THE CUSTOMER OR CONTRACTOR PRIOR TO APPROVAL. ANY ERRORS OR OMISSIONS MUST BE REPORTED IN WRITING TO BAUHU PRIOR TO COMMENCEMENT OF CONSTRUCTION.
- ARCHITECTURAL DRAWINGS SHOULD BE READ IN CONJUNCTION WITH STRUCTURAL DETAILING AND FABRICATION GENERAL ASSEMBLY DRAWINGS.
- FOR CONSTRUCTION PURPOSES, USE ONLY THE LATEST APPROVED DRAWINGS LABELED 'ISSUED FOR CONSTRUCTION'.
- DO NOT SCALE FROM THIS DRAWING.
- THE COMPANY OPERATES USING METRIC DIMENSIONS AS THE PRINCIPAL DENOMINATION.
- ALL CONCRETE WORKS ARE OUTSIDE OF THE SCOPE OF THE COMPANY. INFORMATION REGARDING SLAB DESIGN AND CONNECTIONS IN THESE DRAWINGS ARE INTENDED FOR GUIDENCE ONLY. FOUNDATION AND SLAB WORKS SHOULD BE DESIGNED AND APPROVED BY A LOCAL STRUCTURAL ENGINEER.
- THE COMPANY RETAINS FULL TITLE AND OWNERSHIP OF THESE PLANS AND DESIGNS. ANY UNAUTHORISED USE, REPRODUCTION, OR DISTRIBUTION OF THESE PLANS, WHETHER IN WHOLE OR PART, IS EXPRESSLY PROHIBITED WITHOUT PRIOR WRITTEN CONSENT.
- THE HYBRID STEEL FRAME CONSTRUCTION SYSTEM AND METHODOLOGY (PATENT PENDING) DESCRIBED IN THESE PLANS HAS BEEN DEVELOPED BY THE COMPANY AND IS SUBJECT TO A PROVISIONAL PATENT APPLICATION & ASSIGNMENT - US APPLICATION No. 63/722,841.

No.	Revision	Date
01	Moved walls under roof joists	13.03

ISSUED FOR:

Issued for information

Issued for client approval

Issued for fabrication

Issued for construction

Bahama Beach

DRAWING TITLE:

Room Legend

DRAWN BY:

Mladin Monica-Mihaela

SCALE:

1 : 35

DRAWING NO:

A26

DATE:

17/03/2025

Room Legend

- Bedroom 1
- Bedroom 2
- Bedroom 3
- En-Suite Bathroom
- Living Room+Kitchen
- Main Bathroom
- Terrace - Exterior

Room Schedule II

No.	Room Name	Sq. Meter	Sq. Feet	Perimeter
1	Living Room+Kitchen	29 m²	317.2 ft²	29468
2	Bedroom 1	11 m²	119.2 ft²	13752
3	En-Suite Bathroom	5 m²	58.4 ft²	9627
4	Main Bathroom	5 m²	51.5 ft²	9199
5	Bedroom 3	7 m²	73.6 ft²	10563
6	Bedroom 2	11 m²	114.1 ft²	13063
8	Terrace - Exterior	23 m²	251.4 ft²	25612
Grand total		92 m²	985.4 ft²	

Finishes Schedule													
No.	Room Name	Floor Area		Room Perimeter	Floor Finish		Ceiling Finish		Wall Finish		Kitchen wall tiles	Wall Finish	
		Sq.Meter	Sq. Feet		Grout Colour	Tiles	Ceiling Colour	Ceiling Height	Wall Colour	Wall Tile		Shower Wall	Mirror wall
Ground Floor Finish													
1	Living Room+Kitchen	29 m²	317.2 ft²	29468	Jasmine 130	Garland Pearl RL05	White #0501	2500	Marble Beige #1390		Garland Pearl RL05		
2	Bedroom 1	11 m²	119.2 ft²	13752	Jasmine 130	Garland Pearl RL05	White #0501	2500	Marble Beige #1390				
3	En-Suite Bathroom	5 m²	58.4 ft²	9627	Jasmine 130	Garland Pearl RL05	White #0501	2500	Marble Beige #1390	Stella White SA05R/ Stella Blue SA53R		Stella Blue SA53R	Stella White
4	Main Bathroom	5 m²	51.5 ft²	9199	Jasmine 130	Garland Pearl RL05	White #0501	2500	Marble Beige #1390	Stella White SA05R/ Stella Blue SA53R		Stella Blue SA53R	Stella White
5	Bedroom 3	7 m²	73.6 ft²	10563	Jasmine 130	Garland Pearl RL05	White #0501	2500	Marble Beige #1390				
6	Bedroom 2	11 m²	114.1 ft²	13063	Jasmine 130	Garland Pearl RL05	White #0501	2703	Marble Beige #1390				
8	Terrace - Exterior	23 m²	251.4 ft²	25612									
Grand total		92 m²	985.4 ft²	111284									

Window/Door Exterior Schedule															
No	Type	Size		RO Size		Count	Opening Direction	Interior pane	Frame Finish	No of Leaves	Hinge Side	Lock	Insect screen	Reinforcing bar	Gully drain
		Width	Height	RO. Width	RO. Height										
ED-01	CORVISION Slider ED-01	1800 mm	2300	1834	2317	3	Sliding	2 left, 1 right	RAL 9010: Pure White RAL: 9010	2	Sliding	Yes	Yes	COR-4315	Yes
W-01	COR70 Casement W-01	1200 mm	1400	1234	1434	1	Casement double	x	RAL 9010: Pure White RAL: 9010	2	double	Yes	Yes	No	N/A
W-02	COR70 Casement W-02	700 mm	1200	734	1234	3	Casement	x	RAL 9010: Pure White RAL: 9010	1	3 right	Yes	Yes	No	N/A
Grand total						7									

Interior Door Schedule														
No	Type	Size		RO Size		Cou nt	Opening Direction	Glass	Finishing	No of Leaves	Hinge Side	Sill Height	Lock	
		Width	Height	RO Width	RO. Height									
ID-01	Interior Door	850 mm	2100 mm	915	2214	2	Casement			matt white	1	1L, 1R	0	Yes
ID-02	Interior Door 2	750 mm	2100 mm	815	2214	3	Casement			matt white	1	3R	0	Yes
Grand total						5								

Wall Schedule			
Type	Width	Length	Area
BAU Exterior Wall	245	35601	85 m²
BAU Interior Wall	204	27791	64 m²
Cement Boards Column	13	1950	5 m²
Grand total		65342	154 m²

Level Schedule		
Name	Elevation	Elevation (feet)
Top of Roof	4563	14.97'
Bottom of Truss	2843	9.33'
Terrace Ceiling	2843	9.33'
Ceiling Level	2598	8.52'
Top of Windows	2300	7.55'
Ground Floor Finish	99	0.32'
Terrace Slab	76	0.25'
Ground Floor Slab	0	0.00'

Wall Material Takeoff	
Room	Wall Area
Garland Pearl RL05	2 m²
Gypsum Wall Board	5 m²
Gypsum Wall Board - Fire resistant	212 m²
Gypsum Wall Board - Moisture resistant	212 m²
Light Gauge Steel frame	148 m²
Marble Beige #1390	174 m²
Paint(3)	85 m²
Rigid insulation	85 m²
Secolite skim coat with embedded mesh	85 m²
Secolite with joints and screws filled	85 m²

Ceiling Schedule				
Type	Area	Perimeter	Finish colour	Description
Ceiling Level				
Interior Ceiling	68 m²	85951	White #0501	Interior
Bottom of Truss				
Interior Ceiling 2	49 m²	82411	White #0501	Interior
Grand total	117 m²	168361		

Wall Material Takeoff	
Room	Wall Area
Selected Paint Finish	212 m²
Spray Foam by others	148 m²
Stella Brick Blue	18 m²
STO Cement-free reinforcing coat	85 m²
STO Decorative Render Finish Plaster	85 m²
Vapour Barrier	148 m²
White RAL 9010	18 m²
Grand total	1806 m²

- BAUHU

MODULAR • BUILDING • SOLUTIONS
1.

THESE DRAWINGS MUST BE CHECKED BY THE CUSTOMER OR CONTRACTOR PRIOR TO APPROVAL. ANY ERRORS OR OMISSIONS MUST BE REPORTED IN WRITING TO BAUHU PRIOR TO COMMENCEMENT OF CONSTRUCTION.
2.

ARCHITECTURAL DRAWINGS SHOULD BE READ IN CONJUNCTION WITH STRUCTURAL DETAILING AND FABRICATION GENERAL ASSEMBLY DRAWINGS.
3.

FOR CONSTRUCTION PURPOSES, USE ONLY THE LATEST APPROVED DRAWINGS LABELED 'ISSUED FOR CONSTRUCTION'.
4.

DO NOT SCALE FROM THIS DRAWING.
5.

THE COMPANY OPERATES USING METRIC DIMENSIONS AS THE PRINCIPAL DENOMINATION.
6.

ALL CONCRETE WORKS ARE OUTSIDE OF THE SCOPE OF THE COMPANY. INFORMATION REGARDING SLAB DESIGN AND CONNECTIONS IN THESE DRAWINGS ARE INTENDED FOR GUIDENCE ONLY. FOUNDATION AND SLAB WORKS SHOULD BE DESIGNED AND APPROVED BY A LOCAL STRUCTURAL ENGINEER.
7.

THE COMPANY RETAINS FULL TITLE AND OWNERSHIP OF THESE PLANS AND DESIGNS. ANY UNAUTHORISED USE, REPRODUCTION, OR DISTRIBUTION OF THESE PLANS, WHETHER IN WHOLE OR PART, IS EXPRESSLY PROHIBITED WITHOUT PRIOR WRITTEN CONSENT.
8.

THE HYBRID STEEL FRAME CONSTRUCTION SYSTEM AND METHODOLOGY (PATENT PENDING) DESCRIBED IN THESE PLANS HAS BEEN DEVELOPED BY THE COMPANY AND IS SUBJECT TO A PROVISIONAL PATENT APPLICATION & ASSIGNMENT - US APPLICATION No. 63/722,841.

No.	Revision	Date
01	Moved walls under roof joists	13.03

ISSUED FOR:

Issued for information

Issued for client approval

Issued for fabrication

Issued for construction

Bahama Beach

DRAWING TITLE:

Schedules

DRAWN BY:

Mladin Monica-Mihaela


SCALE:

DRAWING NO:

A27

DATE:

17/03/2025

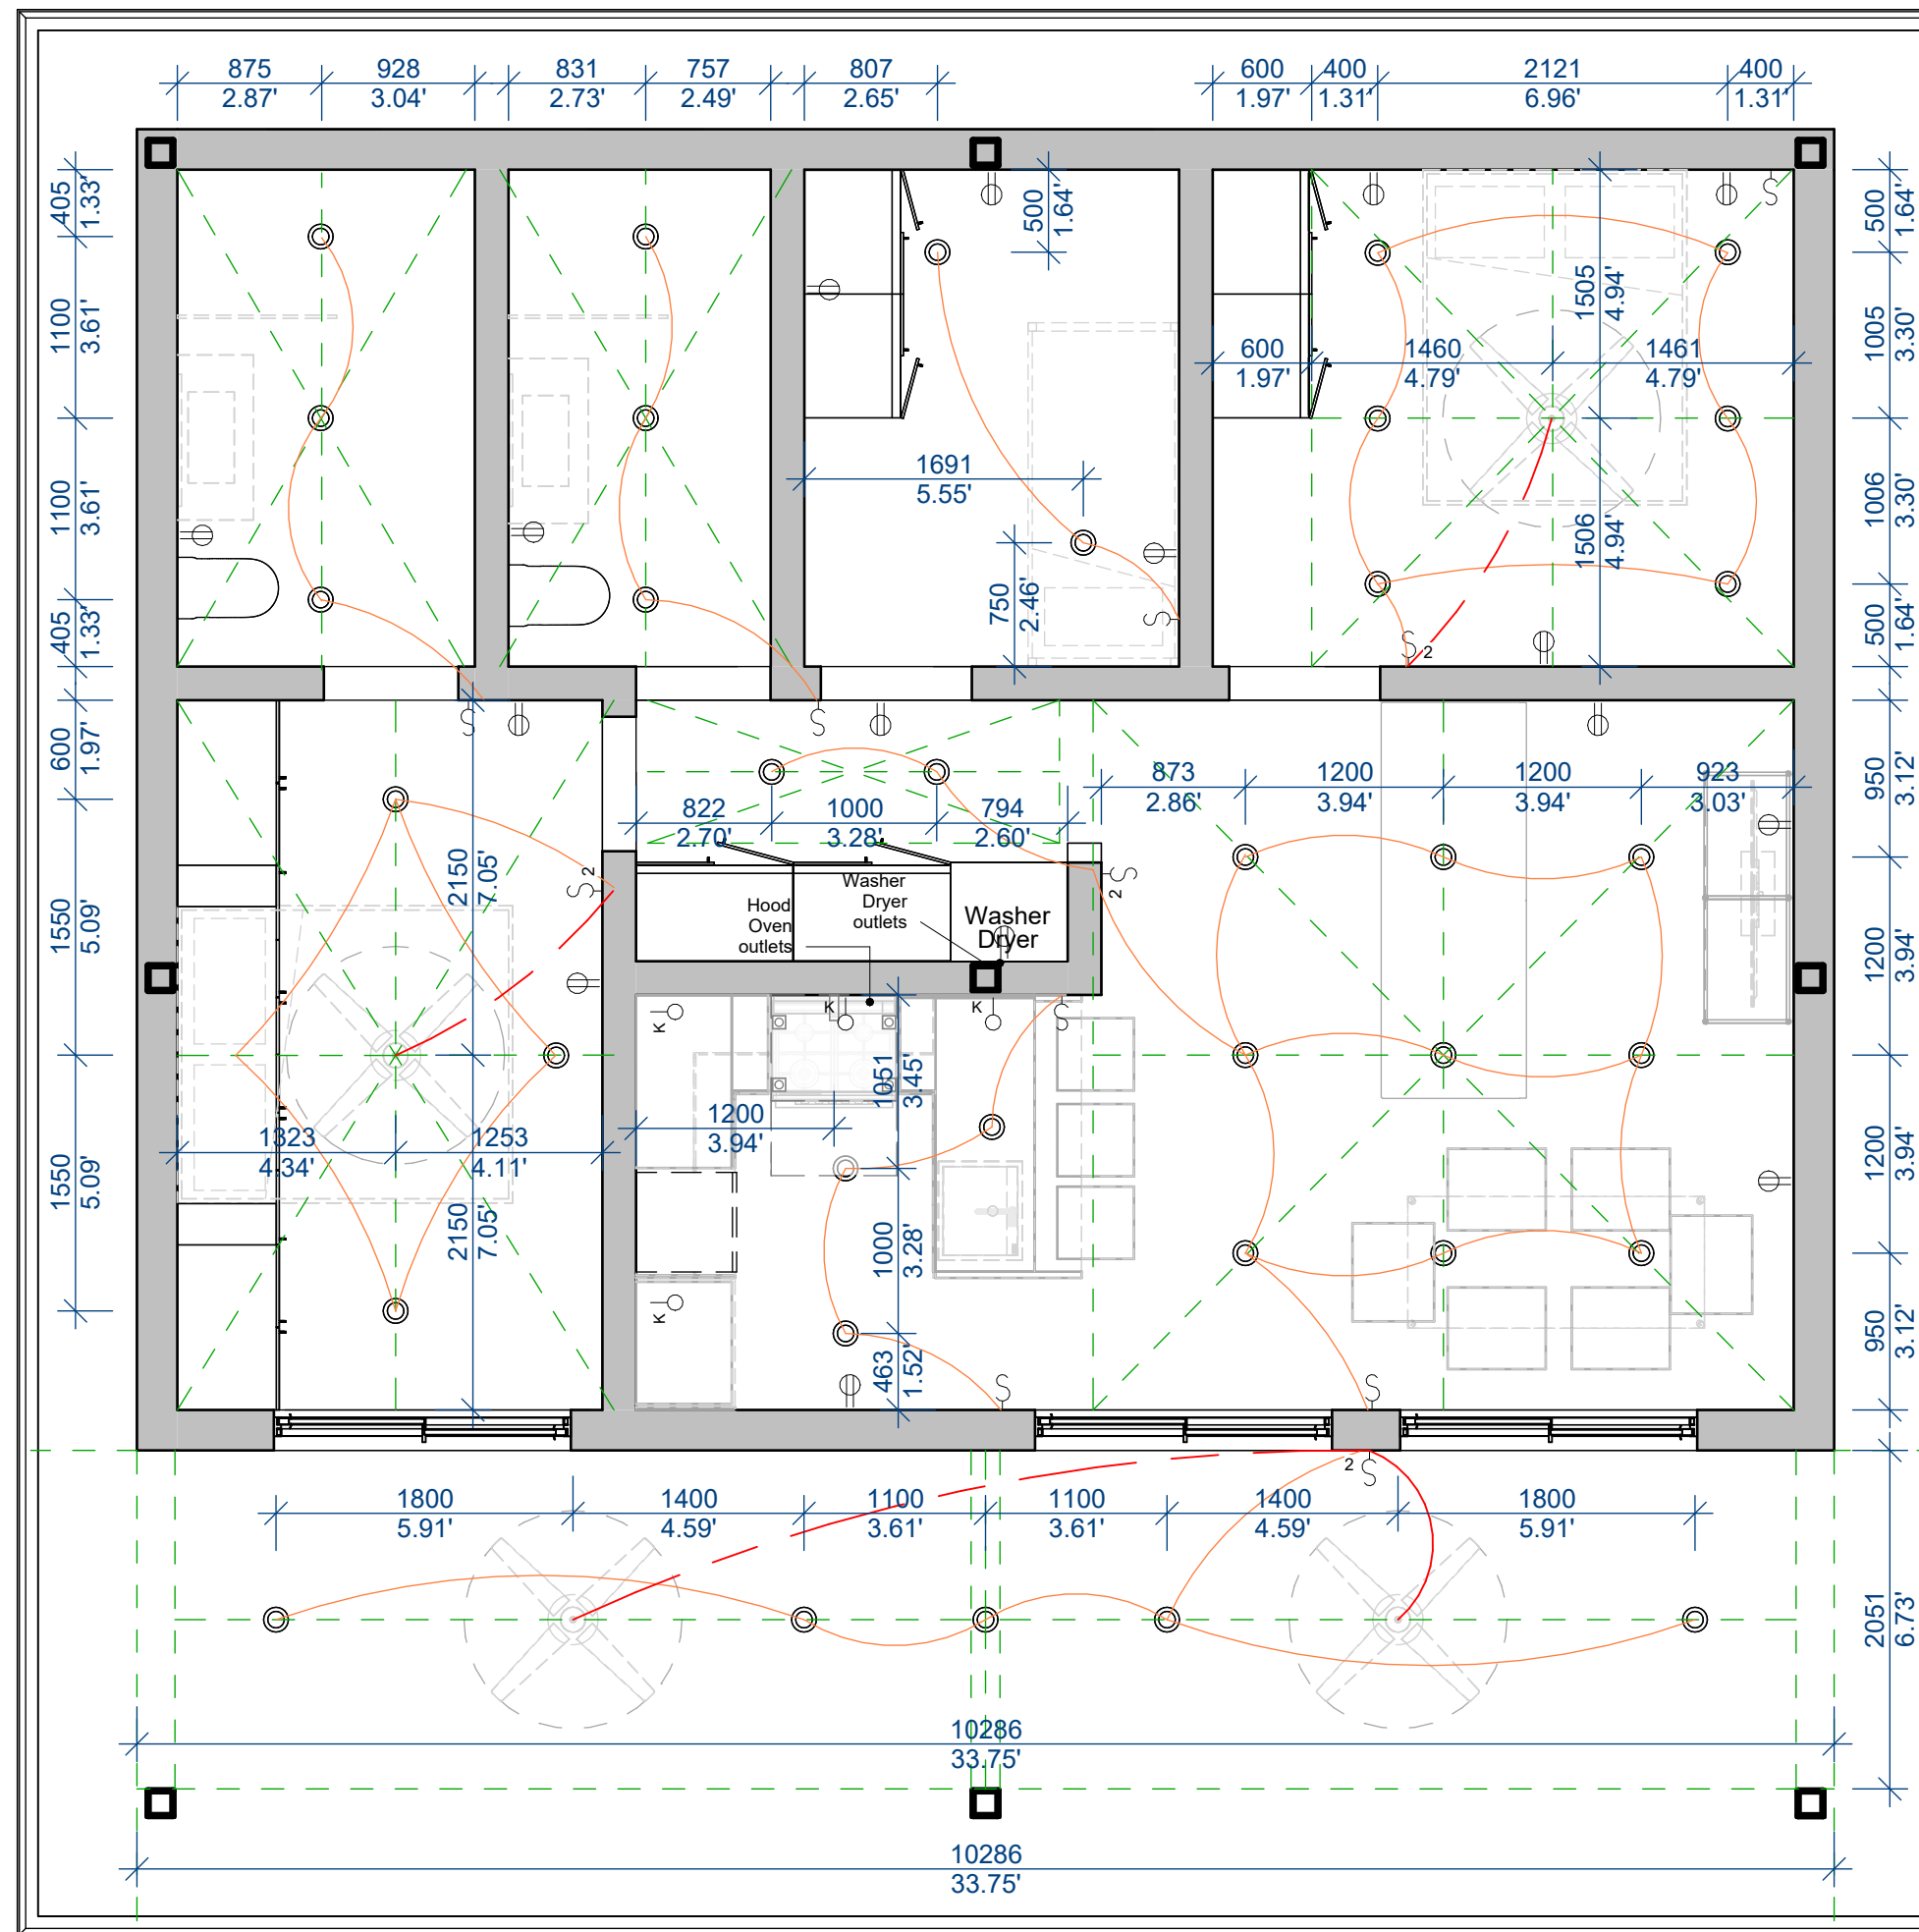

Symbols

- | | |
|---|--------------------------------|
|  | Bell |
|  | Television Outlet |
|  | Duplex Outlet |
|  | Single Switch |
|  | Double Switch |
|  | Three Way Switch |
|  | Outlet Fixed Kitchen Equipment |
|  | Fan Switch |


Note:

- The electrical and HVAC installation including cables, conduits, surface mounted switches, power outlets, light fittings, fans, extractors, water heating equipment, air conditioning equipment, kitchen appliances, solar appliances, data and communication equipment, other electrical fixtures and fittings, are not supplied. Electrical plans are provided as a guide for contractor information only. Electrical system design, supply and installation should be carried out by a competent electrician.
- Electrical engineer to provide adequate grounding to all steel members.
- Air conditioning and flood vents by others.

Typical Panel 120/240 1 60h 3W

CKT. NO.	IDENTIFICATION	CIRCUIT BREAKER		
		BKR.	WIRE	KW.
1	General Lightning and Receptacles	15 A.	# 14	
2	General Lightning and Receptacles	15 A.	# 14	
3	General Lightning and Receptacles	15 A.	# 14	
4	General Lightning and Receptacles	15 A.	# 14	
5	General Lightning and Receptacles	15 A.	# 14	
6	GFI Receptacles	20 A.	# 12	
7	General Lightning and Receptacles	15 A.	# 14	
8	Kitchen Small Appliance Receptacles	20 A.	# 12	
9	Kitchen Small Appliance Receptacles	20 A.	# 12	1.5
10	Garbage Disposer	20 A.	# 12	1.2
11	Outdoor Lightning and Receptacles	20 A.	# 12	1.5
12	Dishwasher	20 A.	# 12	1.2
13	Refrigerator	20 A.	# 12	1.2
14	Microwave	20 A.	# 12	
15 17	Range/Oven	50 A.	# 6	12
16 18	AC/MSCU #1 (Living Room)	30 A.	# 10	3.6
19 21	Water Heater #1	30 A.	# 10	4.5
20 22	AC/MSCU #2 (Dining/Kitchen)	30 A.	# 10	3.6
23 25	AC/MSU #3 (Master Bedroom)	30 A.	# 10	3.6
24 26	AC/MSU #4 (Bedroom 2)	30 A.	# 10	3.6
27	Spare			
28 30	AC/MSU #5 (Bedroom 3)	30 A.	# 10	3.6
29	Spare			

Service Riser

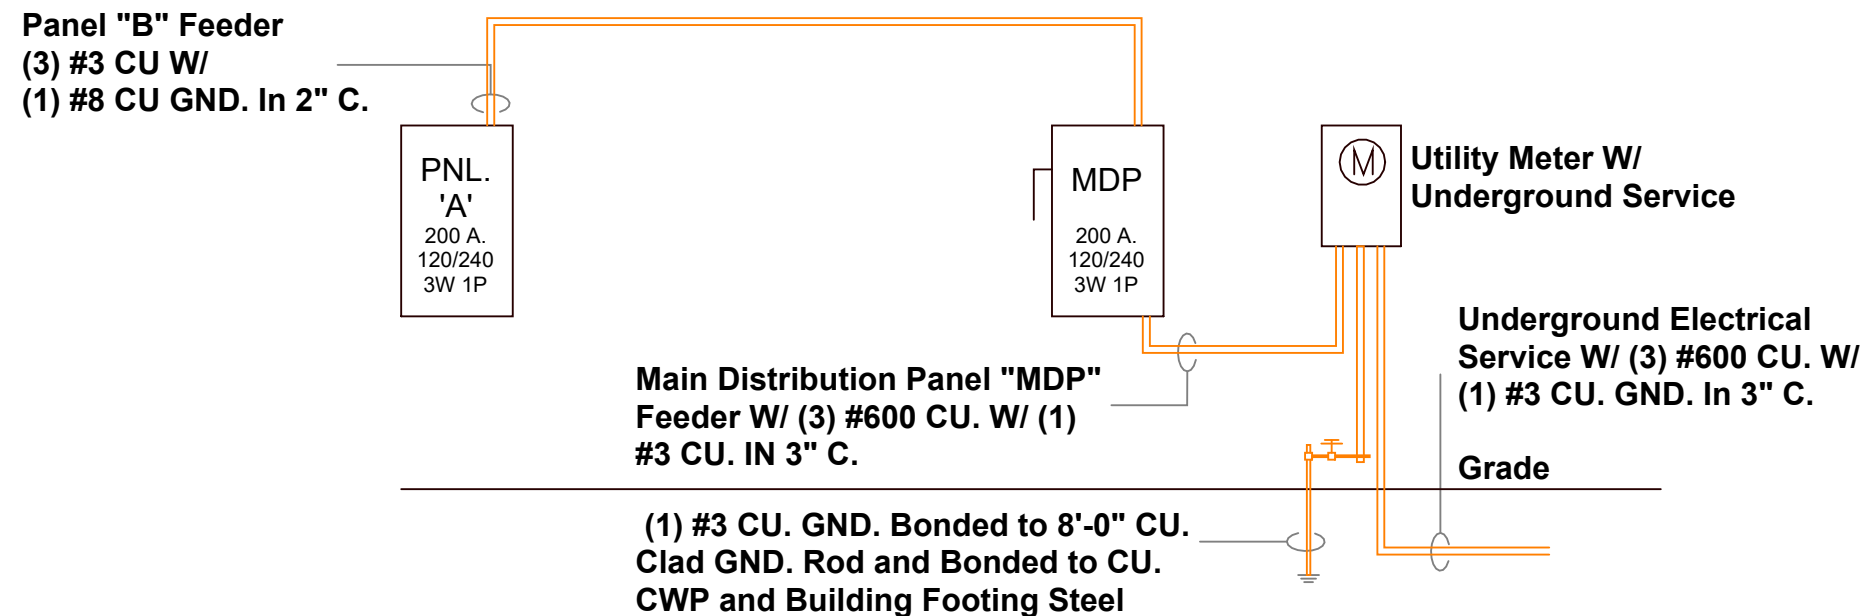

1. THESE DRAWINGS MUST BE CHECKED BY THE CUSTOMER OR CONTRACTOR PRIOR TO APPROVAL. ANY ERRORS OR OMISSIONS MUST BE REPORTED IN WRITING TO BAUHU PRIOR TO COMMENCEMENT OF CONSTRUCTION.
2. ARCHITECTURAL DRAWINGS SHOULD BE READ IN CONJUNCTION WITH STRUCTURAL DETAILING AND FABRICATION GENERAL ASSEMBLY DRAWINGS.
3. FOR CONSTRUCTION PURPOSES, USE ONLY THE LATEST APPROVED DRAWINGS LABELED 'ISSUED FOR CONSTRUCTION'.
4. DO NOT SCALE FROM THIS DRAWING.
5. THE COMPANY OPERATES USING METRIC DIMENSIONS AS THE PRINCIPAL DENOMINATION.
6. ALL CONCRETE WORKS ARE OUTSIDE OF THE SCOPE OF THE COMPANY. INFORMATION REGARDING SLAB DESIGN AND CONNECTIONS IN THESE DRAWINGS ARE INTENDED FOR GUIDANCE ONLY. FOUNDATION AND SLAB WORKS SHOULD BE DESIGNED AND APPROVED BY A LOCAL STRUCTURAL ENGINEER.
7. THE COMPANY RETAINS FULL TITLE AND OWNERSHIP OF THESE PLANS AND DESIGNS. ANY UNAUTHORISED USE, REPRODUCTION, OR DISTRIBUTION OF THESE PLANS, WHETHER IN WHOLE OR PART, IS EXPRESSLY PROHIBITED WITHOUT PRIOR WRITTEN CONSENT.
8. THE HYBRID STEEL FRAME CONSTRUCTION SYSTEM AND METHODOLOGY (PATENT PENDING) DESCRIBED IN THESE PLANS HAS BEEN DEVELOPED BY THE COMPANY AND IS SUBJECT TO A PROVISIONAL PATENT APPLICATION & ASSIGNMENT - US APPLICATION NO. 63/722,841.

[illegible]

ISSUED FOR:

- Issued for information
 Issued for client approval
 Issued for fabrication
 Issued for construction

Bahama Beach

DRAWING TITLE: Electrical Plan


DRAWN BY:
Mladin Monica-Mihaela

SCALE: As indicated

DRAWING NO: A28

DATE: 17/03/2025

Hot Water
Cold Water
Waste pipe

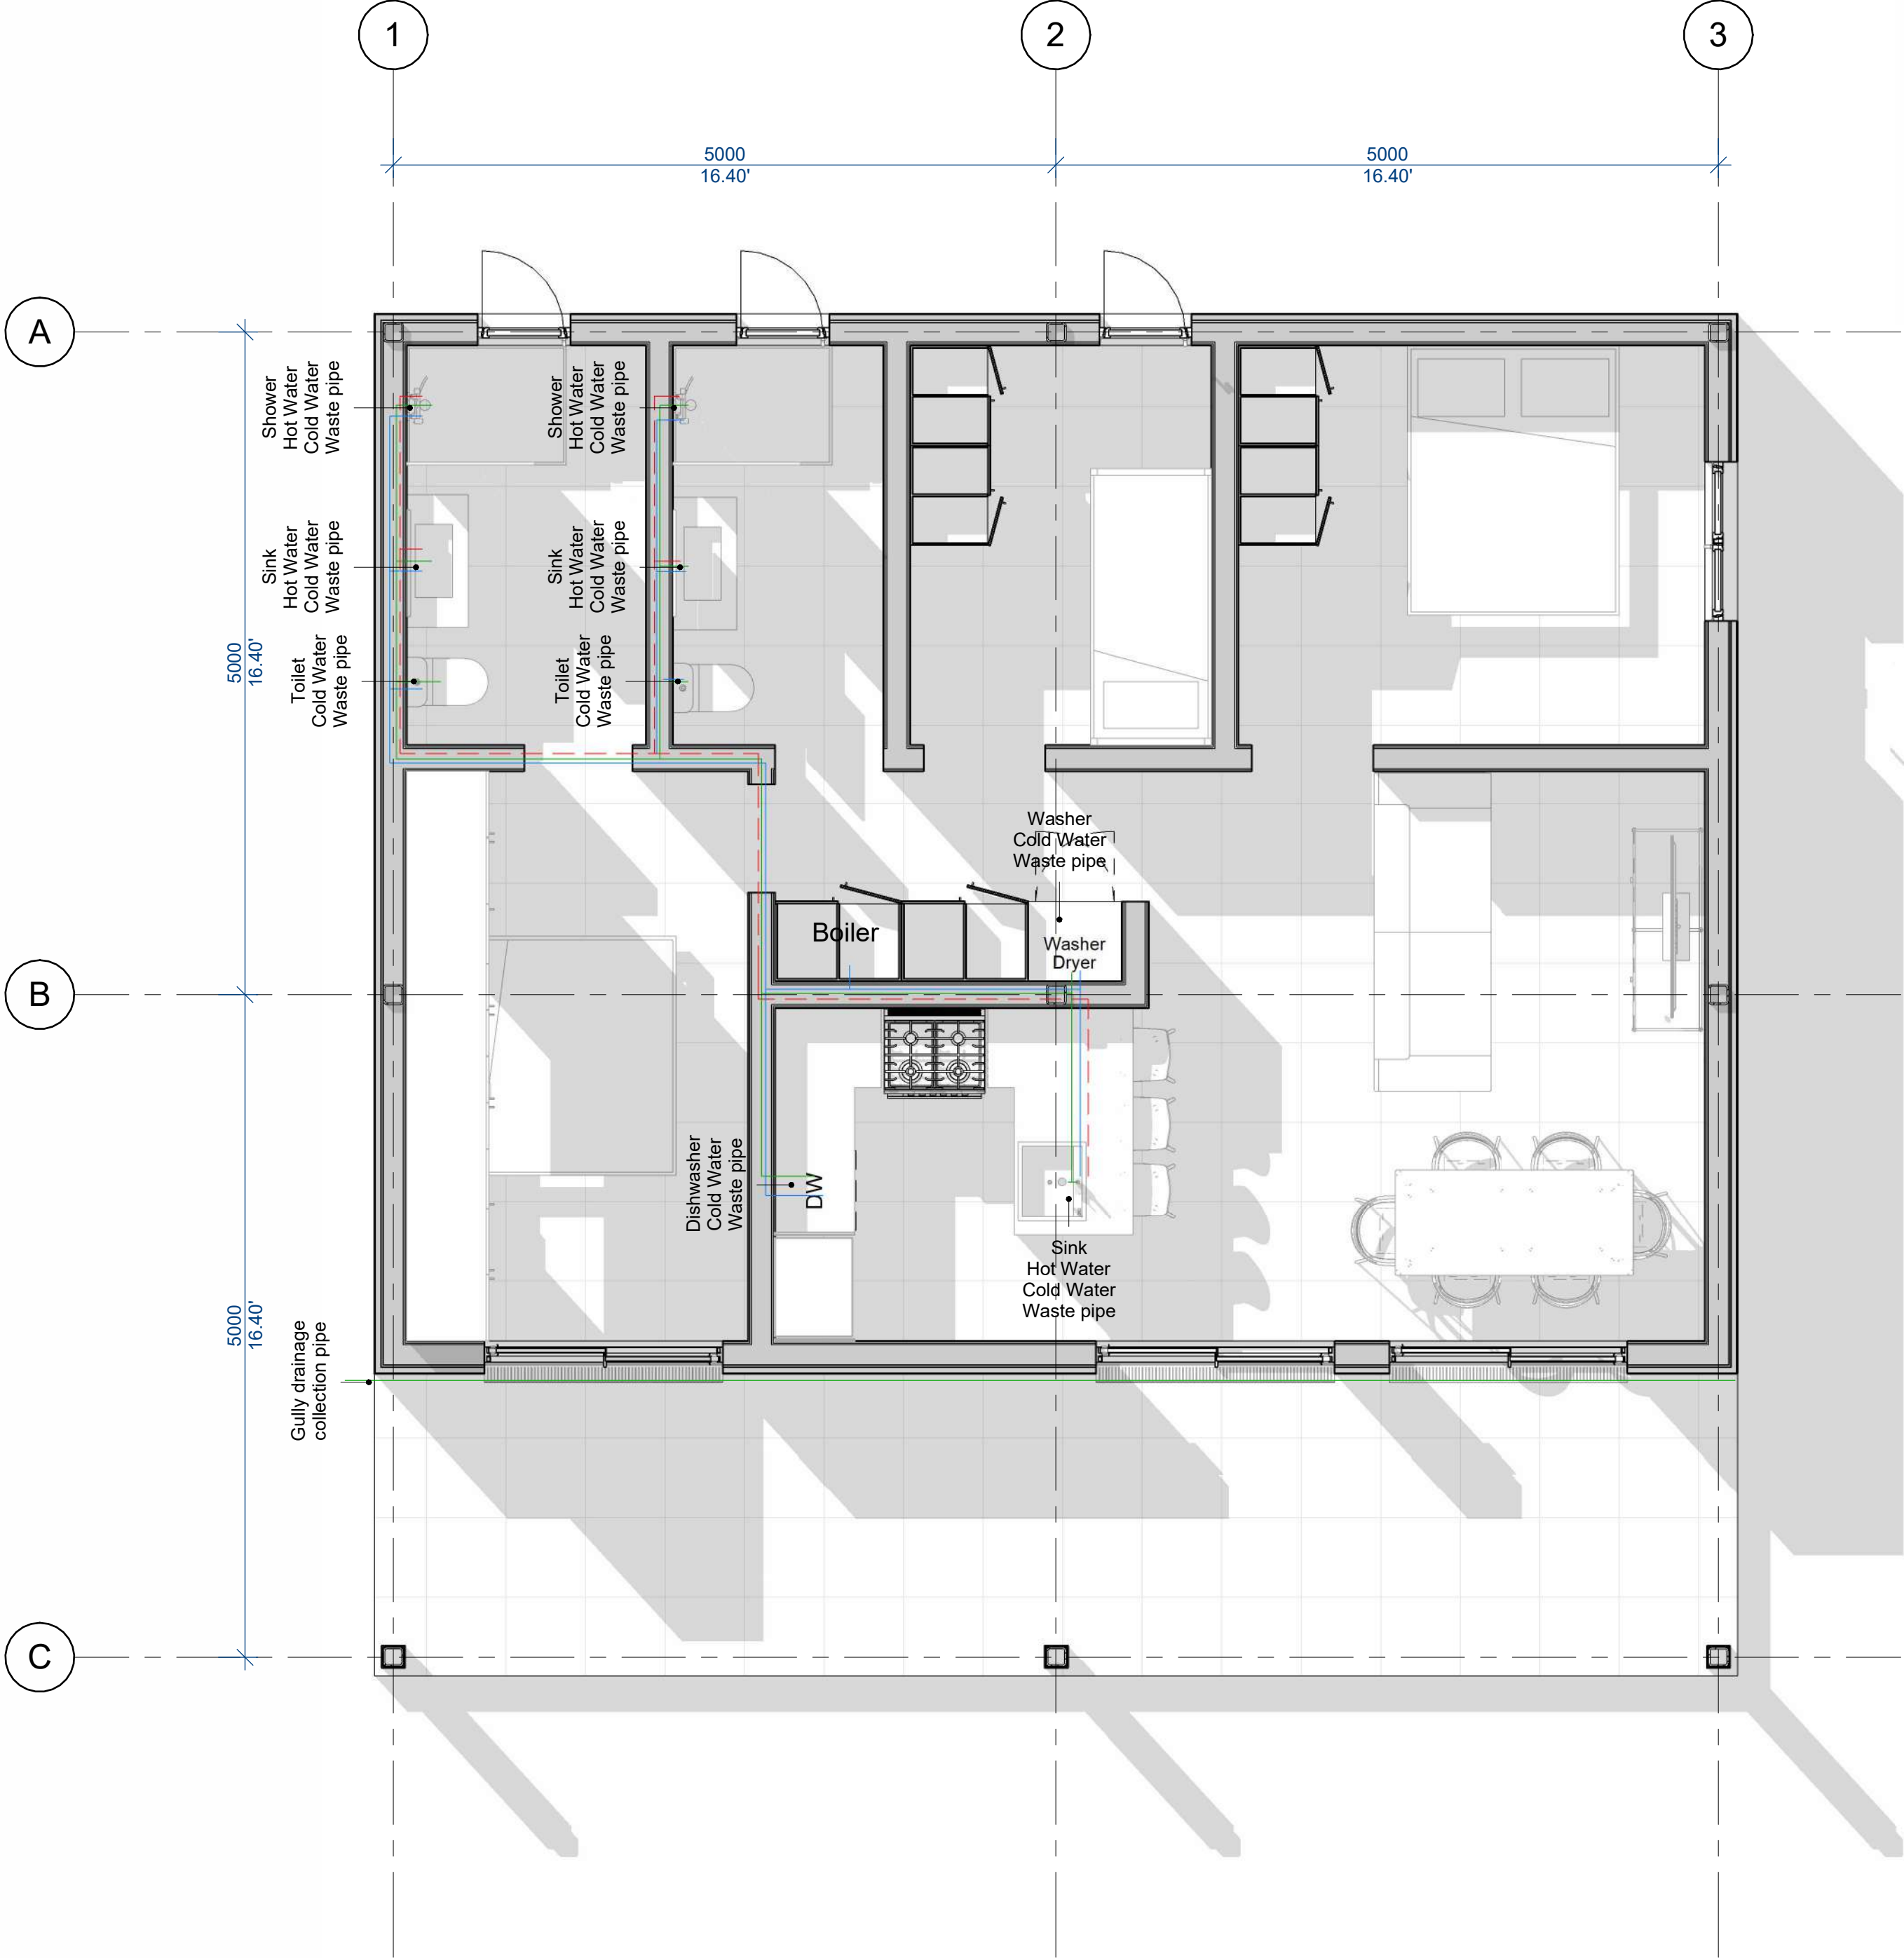

1. THESE DRAWINGS MUST BE CHECKED BY THE CUSTOMER OR CONTRACTOR PRIOR TO APPROVAL. ANY ERRORS OR OMISSIONS MUST BE REPORTED IN WRITING TO BAUHU PRIOR TO COMMENCEMENT OF CONSTRUCTION.
2. ARCHITECTURAL DRAWINGS SHOULD BE READ IN CONJUNCTION WITH STRUCTURAL DETAILING AND FABRICATION GENERAL ASSEMBLY DRAWINGS.
3. FOR CONSTRUCTION PURPOSES, USE ONLY THE LATEST APPROVED DRAWINGS LABELED 'ISSUED FOR CONSTRUCTION'.
4. DO NOT SCALE FROM THIS DRAWING.
5. THE COMPANY OPERATES USING METRIC DIMENSIONS AS THE PRINCIPAL DENOMINATION.
6. ALL CONCRETE WORKS ARE OUTSIDE OF THE SCOPE OF THE COMPANY. INFORMATION REGARDING SLAB DESIGN AND CONNECTIONS IN THESE DRAWINGS ARE INTENDED FOR GUIDENCE ONLY. FOUNDATION AND SLAB WORKS SHOULD BE DESIGNED AND APPROVED BY A LOCAL STRUCTURAL ENGINEER.
7. THE COMPANY RETAINS FULL TITLE AND OWNERSHIP OF THESE PLANS AND DESIGNS. ANY UNAUTHORISED USE, REPRODUCTION, OR DISTRIBUTION OF THESE PLANS, WHETHER IN WHOLE OR PART, IS EXPRESSLY PROHIBITED WITHOUT PRIOR WRITTEN CONSENT.
8. THE HYBRID STEEL FRAME CONSTRUCTION SYSTEM AND METHODOLOGY (PATENT PENDING) DESCRIBED IN THESE PLANS HAS BEEN DEVELOPED BY THE COMPANY AND IS SUBJECT TO A PROVISIONAL PATENT APPLICATION & ASSIGNMENT - US APPLICATION No. 63/722,841.

No.	Revision	Date
01	Moved walls under roof joists	13.03

ISSUED FOR:

Issued for information

Issued for client approval

Issued for fabrication

Issued for construction

Bahama Beach

DRAWING TITLE:
Plumbing Plan

DRAWN BY:
Mladin Monica-Mihaela

SCALE:
1 : 40

DRAWING NO:
A29

DATE:
17/03/2025


Note: Plumbing supply pipework, waste pipework, rainwater drain pipework, pipe connections and sub-slab roughing 's are excluded. Plumbing plans are provided as a guide for contractor information only.

Sanindusa
Model: Safira
Name: Safira shower panel
Reference: 8966002211
Finishes: 11-Chrome
Dimensions: 965Lx2000H mm
Count: 2



<https://sanindusa.com/en/product/telescopic-support-arm-for-cristal-shower-enclosure>

Bruma
Model: Nautic
Reference: 181 010 1CR
Finishes: Chrome
Count: 2
Room No: 3 / 7

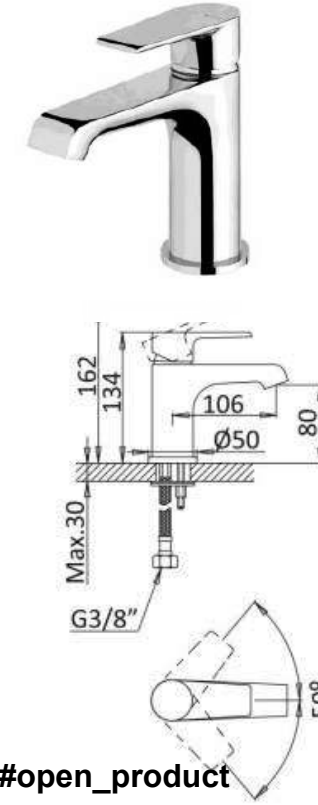

- # BAUHU
- MODULAR • BUILDING • SOLUTIONS
1. THESE DRAWINGS MUST BE CHECKED BY THE CUSTOMER OR CONTRACTOR PRIOR TO APPROVAL. ANY ERRORS OR OMISSIONS MUST BE REPORTED IN WRITING TO BAUHU PRIOR TO COMMENCEMENT OF CONSTRUCTION.
 2. ARCHITECTURAL DRAWINGS SHOULD BE READ IN CONJUNCTION WITH STRUCTURAL DETAILING AND FABRICATION GENERAL ASSEMBLY DRAWINGS.
 3. FOR CONSTRUCTION PURPOSES, USE ONLY THE LATEST APPROVED DRAWINGS LABELED 'ISSUED FOR CONSTRUCTION'.
 4. DO NOT SCALE FROM THIS DRAWING.
 5. THE COMPANY OPERATES USING METRIC DIMENSIONS AS THE PRINCIPAL DENOMINATION.
 6. ALL CONCRETE WORKS ARE OUTSIDE OF THE SCOPE OF THE COMPANY. INFORMATION REGARDING SLAB DESIGN AND CONNECTIONS IN THESE DRAWINGS ARE INTENDED FOR GUIDENCE ONLY. FOUNDATION AND SLAB WORKS SHOULD BE DESIGNED AND APPROVED BY A LOCAL STRUCTURAL ENGINEER.
 7. THE COMPANY RETAINS FULL TITLE AND OWNERSHIP OF THESE PLANS AND DESIGNS. ANY UNAUTHORISED USE, REPRODUCTION, OR DISTRIBUTION OF THESE PLANS, WHETHER IN WHOLE OR PART, IS EXPRESSLY PROHIBITED WITHOUT PRIOR WRITTEN CONSENT.
 8. THE HYBRID STEEL FRAME CONSTRUCTION SYSTEM AND METHODOLOGY (PATENT PENDING) DESCRIBED IN THESE PLANS HAS BEEN DEVELOPED BY THE COMPANY AND IS SUBJECT TO A PROVISIONAL PATENT APPLICATION & ASSIGNMENT - US APPLICATION No. 63/722,841.


[illegible]

Issued for construction

17/03/2025

Sanindusa
Model: Piano
Name: Piano anti-slip rectangular
shower tray
Reference: 8031500000
Finishes: white
Dimensions: 1203x903x75 mm
Count: 2
Room No: 3 / 7
Features: Ø90mm waste with built-in
trap not included


Shower System

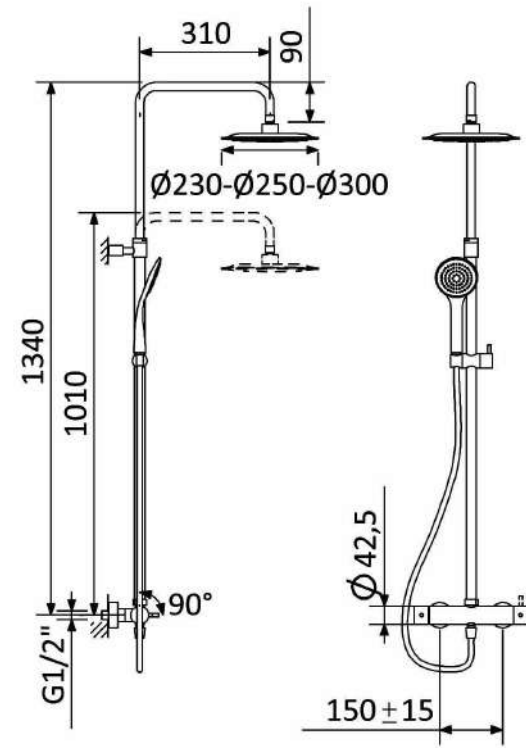


Note:

- Sanitary ware, faucets, kitchen and bathroom equipment are provided. Plumbing supply pipework, waste and sub-slab roughings are excluded. Plumbing plan is provided as a guide for contractor information only.
- Shower glass screens are fixed.

Kitbanho
Model:Alt 2, Top Ceramico, 100S
Finishes: light grey
Dimensions: 1000mm
Count: 2
Room No: 3 / 7

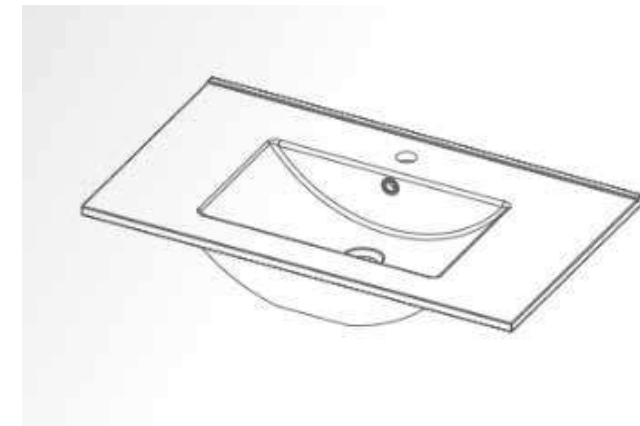


Kitbanho
Model: Odessa, Alt 26, Tipo 01, 100S
Finishes: Branco Brilho (glossy)
Dimensions: 1000 mm
Count: 2
Room No: 3 / 7

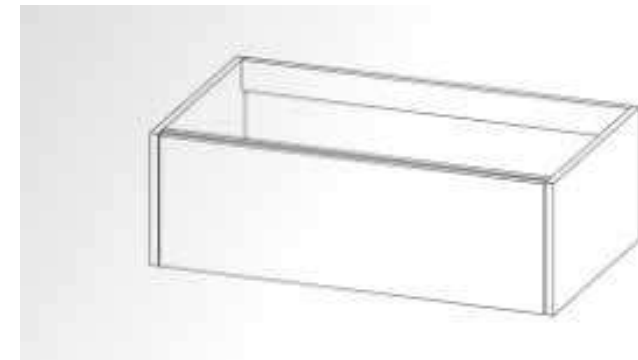

Sanindusa
Model: Winner Confort FJD close coupled toilet
Reference: 144021
Dimensions: L65xW37xH47
Finishes: Vitreous China 00-White
Count: 2
Room No: 3 / 7

Sanindusa
Model: Winner toilet seat with easyclip system
Reference: 24231
Finishes: Duroplast - 00-Chrome|White
Count: 2
Room No: 3 / 7

<https://www.tec.sanindusa.pt/winner-confort-fd-close-coupled-toilet>

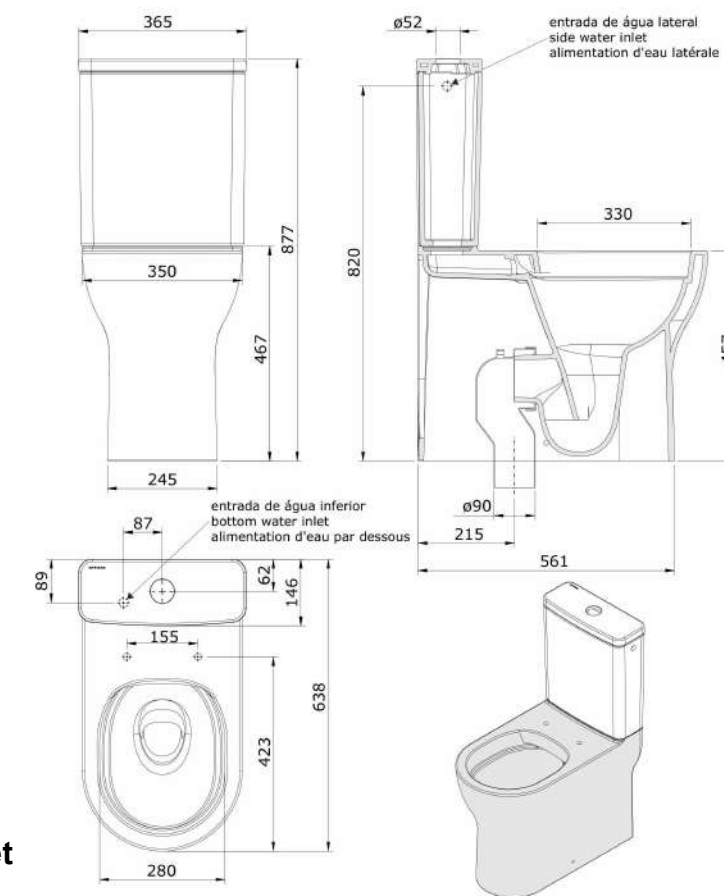

1. THESE DRAWINGS MUST BE CHECKED BY THE CUSTOMER OR CONTRACTOR PRIOR TO APPROVAL. ANY ERRORS OR OMISSIONS MUST BE REPORTED IN WRITING TO BAUHU PRIOR TO COMMENCEMENT OF CONSTRUCTION.
2. ARCHITECTURAL DRAWINGS SHOULD BE READ IN CONJUNCTION WITH STRUCTURAL DETAILING AND FABRICATION GENERAL ASSEMBLY DRAWINGS.
3. FOR CONSTRUCTION PURPOSES, USE ONLY THE LATEST APPROVED DRAWINGS LABELED 'ISSUED FOR CONSTRUCTION'.
4. DO NOT SCALE FROM THIS DRAWING.
5. THE COMPANY OPERATES USING METRIC DIMENSIONS AS THE PRINCIPAL DENOMINATION.
6. ALL CONCRETE WORKS ARE OUTSIDE OF THE SCOPE OF THE COMPANY. INFORMATION REGARDING SLAB DESIGN AND CONNECTIONS IN THESE DRAWINGS ARE INTENDED FOR GUIDENCE ONLY. FOUNDATION AND SLAB WORKS SHOULD BE DESIGNED AND APPROVED BY A LOCAL STRUCTURAL ENGINEER.
7. THE COMPANY RETAINS FULL TITLE AND OWNERSHIP OF THESE PLANS AND DESIGNS. ANY UNAUTHORISED USE, REPRODUCTION, OR DISTRIBUTION OF THESE PLANS, WHETHER IN WHOLE OR PART, IS EXPRESSLY PROHIBITED WITHOUT PRIOR WRITTEN CONSENT.
8. THE HYBRID STEEL FRAME CONSTRUCTION SYSTEM AND METHODOLOGY (PATENT PENDING) DESCRIBED IN THESE PLANS HAS BEEN DEVELOPED BY THE COMPANY AND IS SUBJECT TO A PROVISIONAL PATENT APPLICATION & ASSIGNMENT - US APPLICATION No. 63/722,841.

No.	Revision	Date
01	Moved walls under roof joists	13.03

ISSUED FOR:

☐ Issued for information

☐ Issued for client approval

☐ Issued for fabrication

☐ Issued for construction

Bahama Beach


DRAWING TITLE:
No 7 - Main Bathroom

DRAWN BY:
Mladin Monica-Mihaela


SCALE:
1 : 25

DRAWING NO:
A31







DATE:
17/03/2025

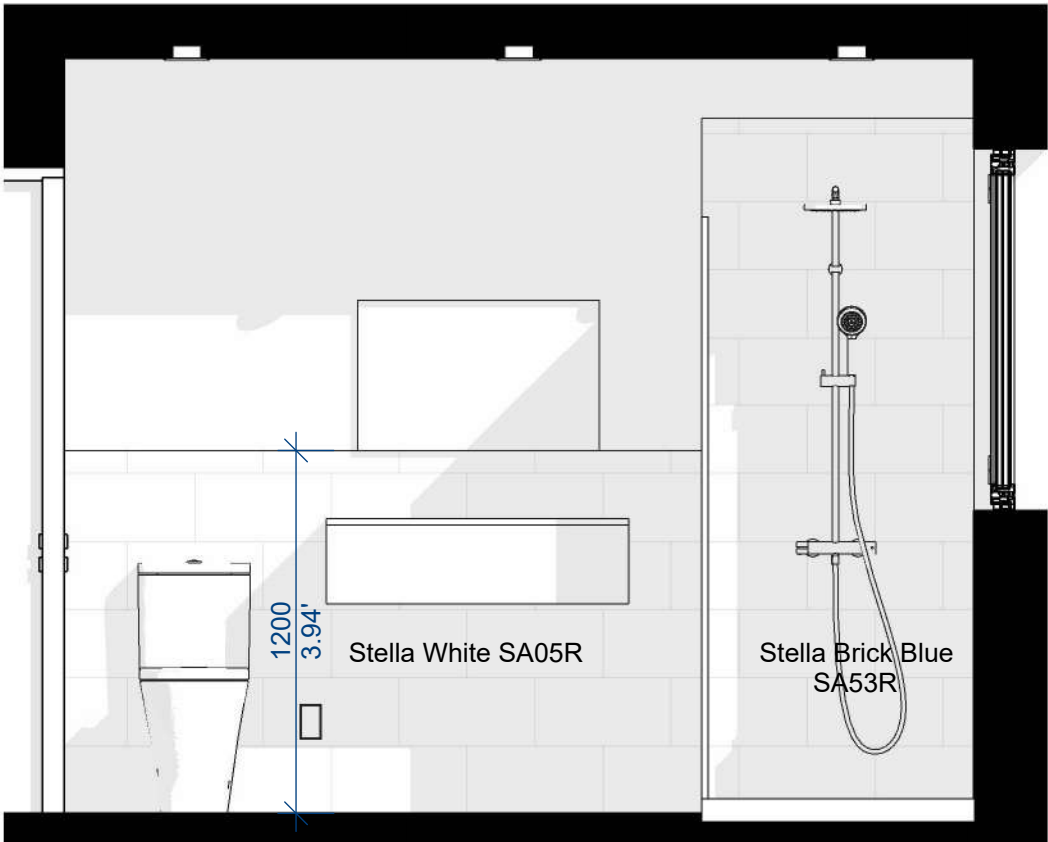

3 Section A
1 : 25

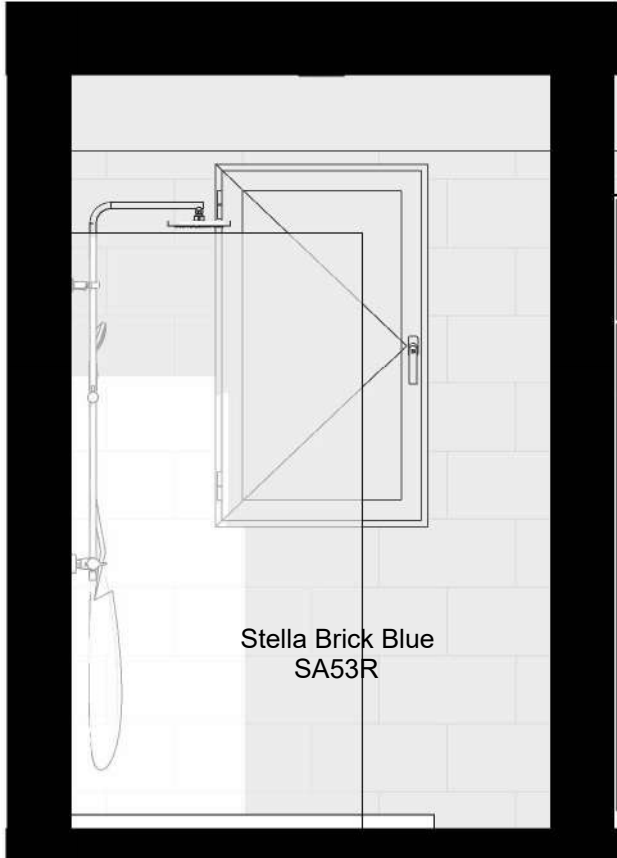

5 Section C
1 : 25

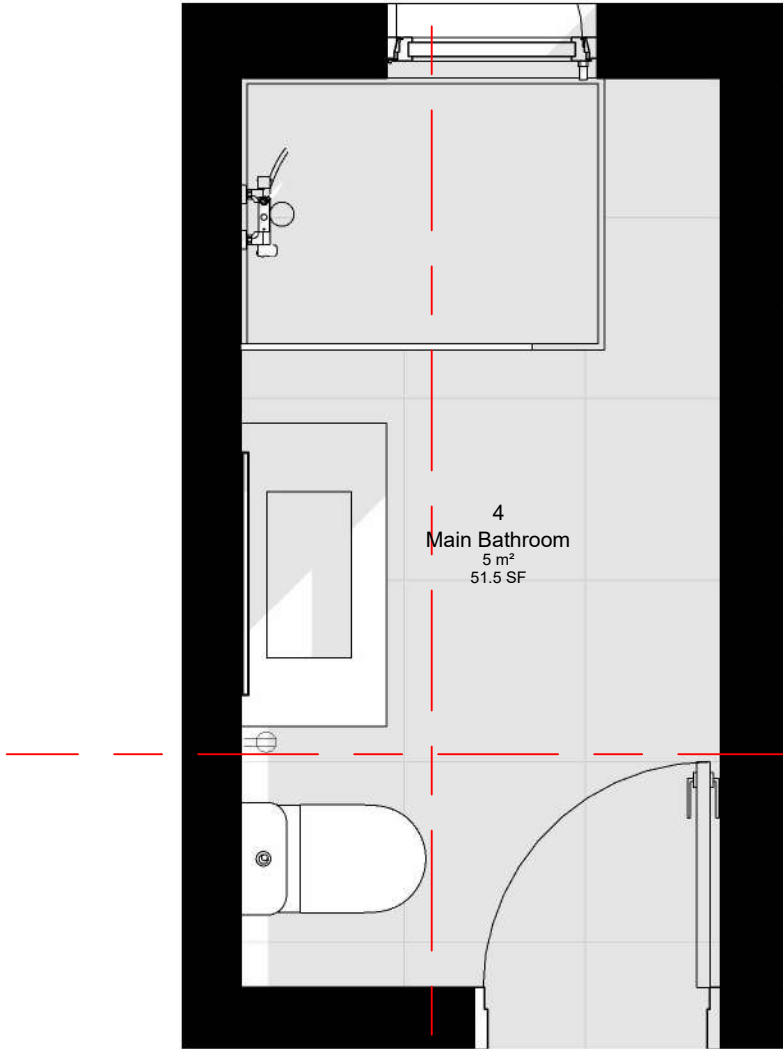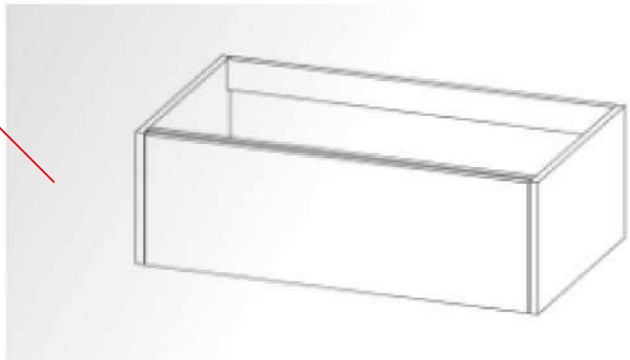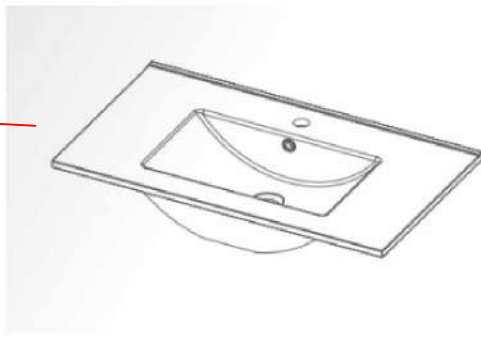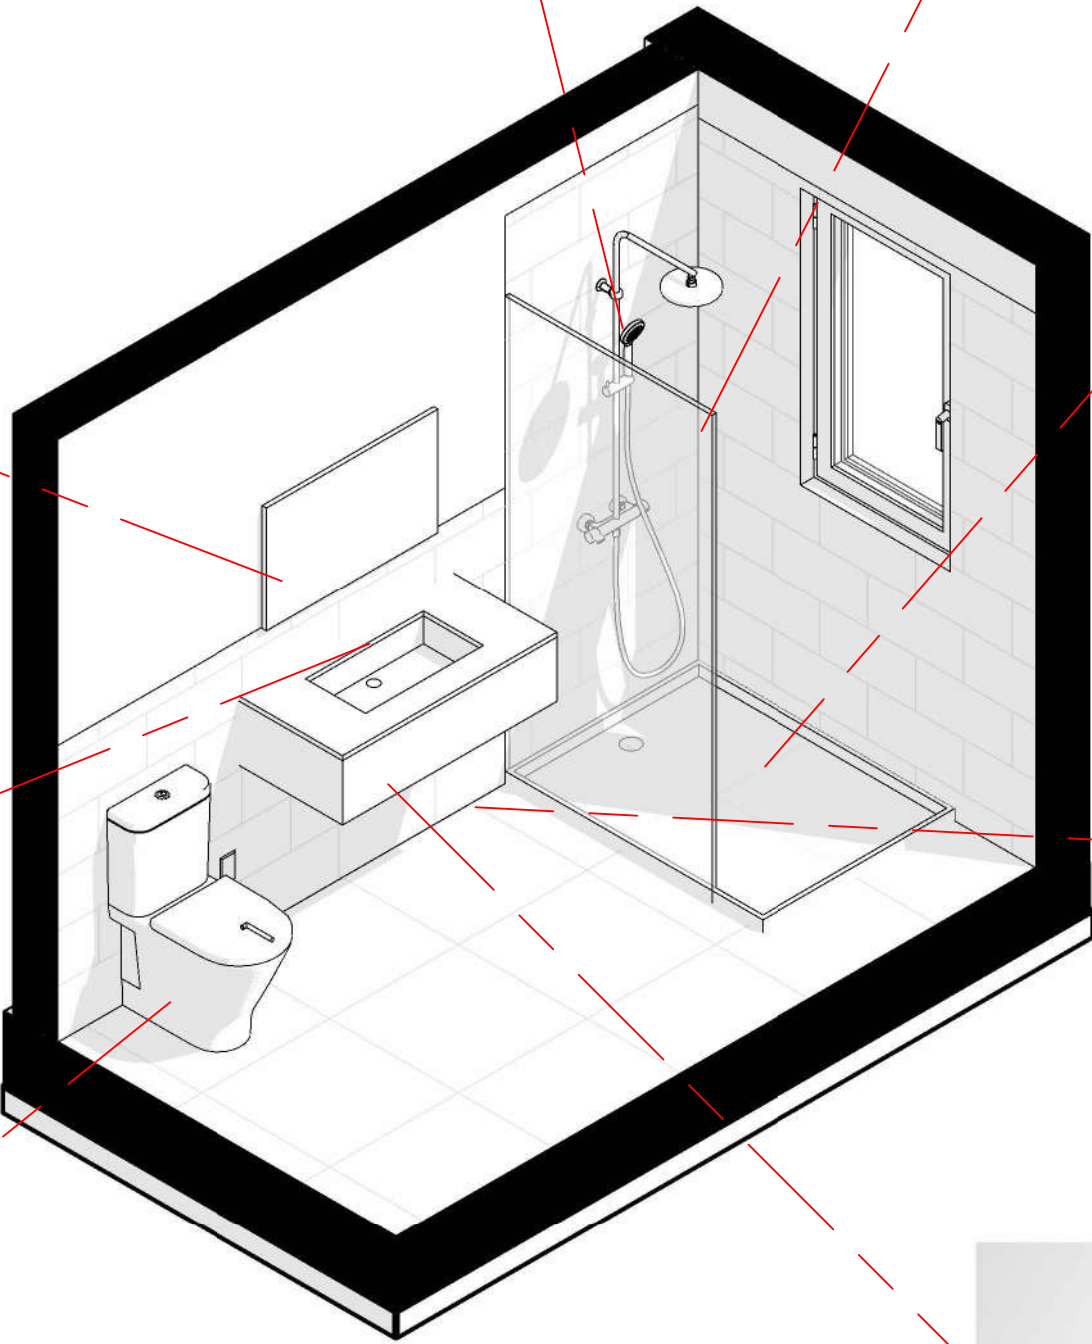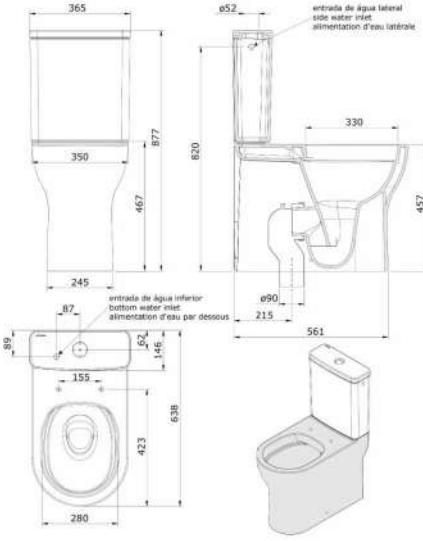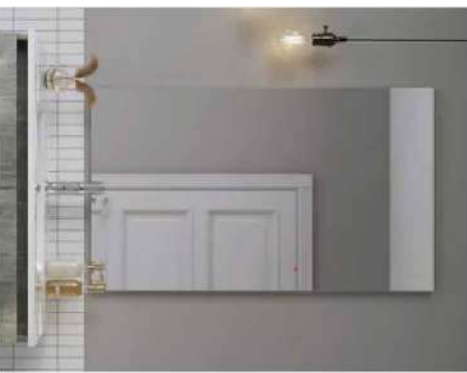

1 Bathroom 1 Plan
1 : 25

1. THESE DRAWINGS MUST BE CHECKED BY THE CUSTOMER OR CONTRACTOR PRIOR TO APPROVAL. ANY ERRORS OR OMISSIONS MUST BE REPORTED IN WRITING TO BAUHU PRIOR TO COMMENCEMENT OF CONSTRUCTION.
2. ARCHITECTURAL DRAWINGS SHOULD BE READ IN CONJUNCTION WITH STRUCTURAL DETAILING AND FABRICATION GENERAL ASSEMBLY DRAWINGS.
3. FOR CONSTRUCTION PURPOSES, USE ONLY THE LATEST APPROVED DRAWINGS LABELED 'ISSUED FOR CONSTRUCTION'.
4. DO NOT SCALE FROM THIS DRAWING.
5. THE COMPANY OPERATES USING METRIC DIMENSIONS AS THE PRINCIPAL DENOMINATION.
6. ALL CONCRETE WORKS ARE OUTSIDE OF THE SCOPE OF THE COMPANY. INFORMATION REGARDING SLAB DESIGN AND CONNECTIONS IN THESE DRAWINGS ARE INTENDED FOR GUIDANCE ONLY. FOUNDATION AND SLAB WORKS SHOULD BE DESIGNED AND APPROVED BY A LOCAL STRUCTURAL ENGINEER.
7. THE COMPANY RETAINS FULL TITLE AND OWNERSHIP OF THESE PLANS AND DESIGNS. ANY UNAUTHORISED USE, REPRODUCTION, OR DISTRIBUTION OF THESE PLANS, WHETHER IN WHOLE OR PART, IS EXPRESSLY PROHIBITED WITHOUT PRIOR WRITTEN CONSENT.
8. THE HYBRID STEEL FRAME CONSTRUCTION SYSTEM AND METHODOLOGY (PATENT PENDING) DESCRIBED IN THESE PLANS HAS BEEN DEVELOPED BY THE COMPANY AND IS SUBJECT TO A PROVISIONAL PATENT APPLICATION & ASSIGNMENT - US APPLICATION No. 63/722,841.

No.	Revision	Date
01	Moved walls under roof joists	13.03

ISSUED FOR:

Issued for information

Issued for client approval

Issued for fabrication

Issued for construction

Bahama Beach


DRAWING TITLE:
No 3 - En-Suite Bathroom

DRAWN BY:
Mladin Monica-Mihaela


SCALE:
As indicated

DRAWING NO:
A32






DATE:
17/03/2025

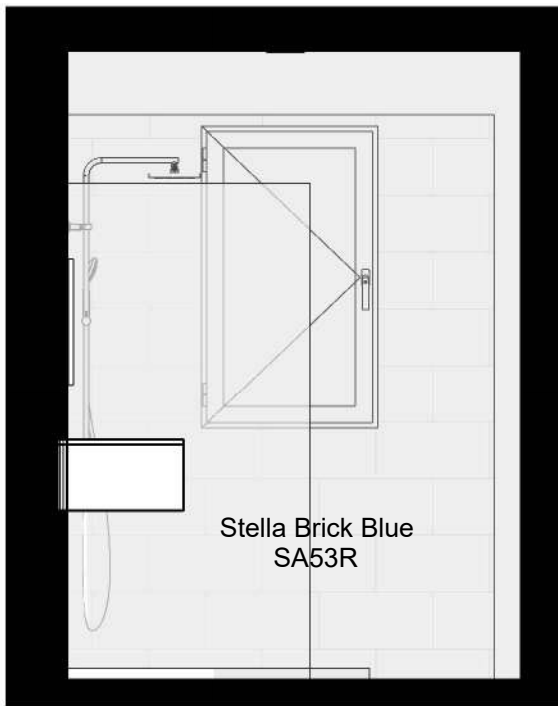

2 Section A'
1 : 30





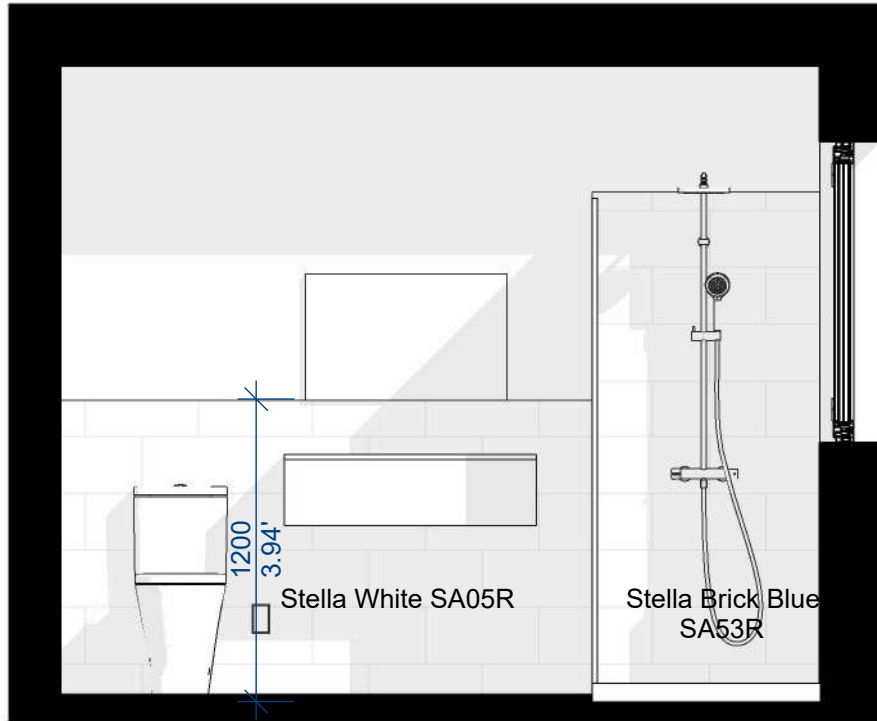


3 Section B'
1 : 30

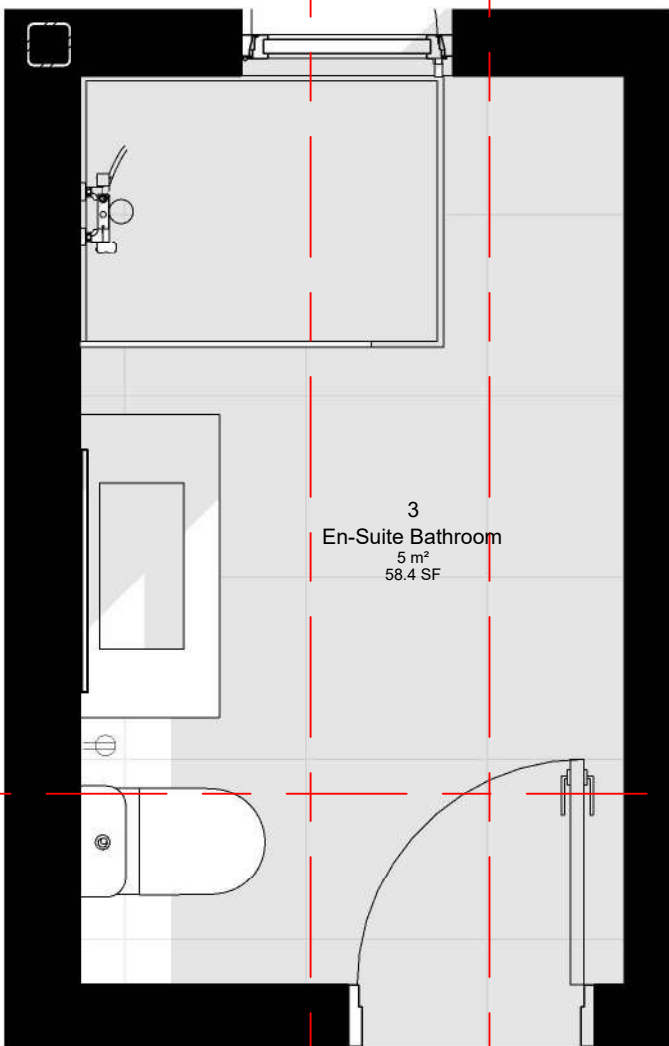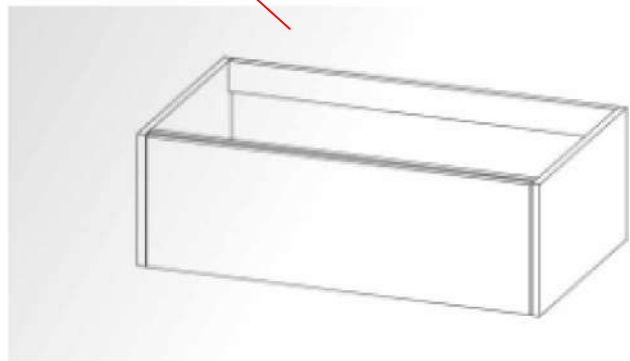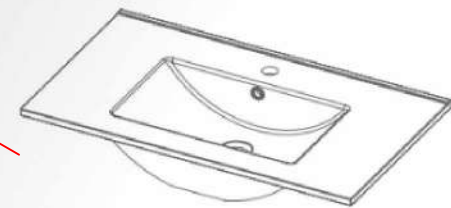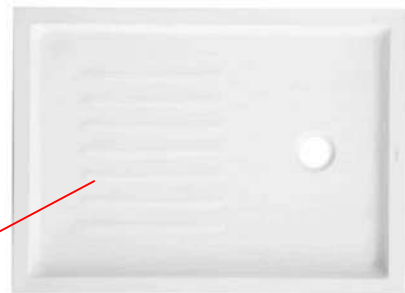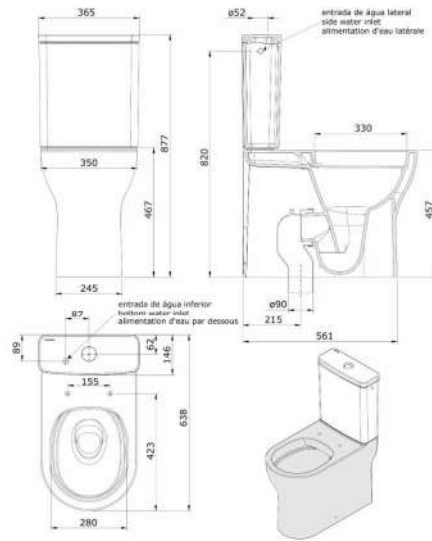

4 Bathroom 2 Plan
1 : 25

Interior Kitchen Nobilia

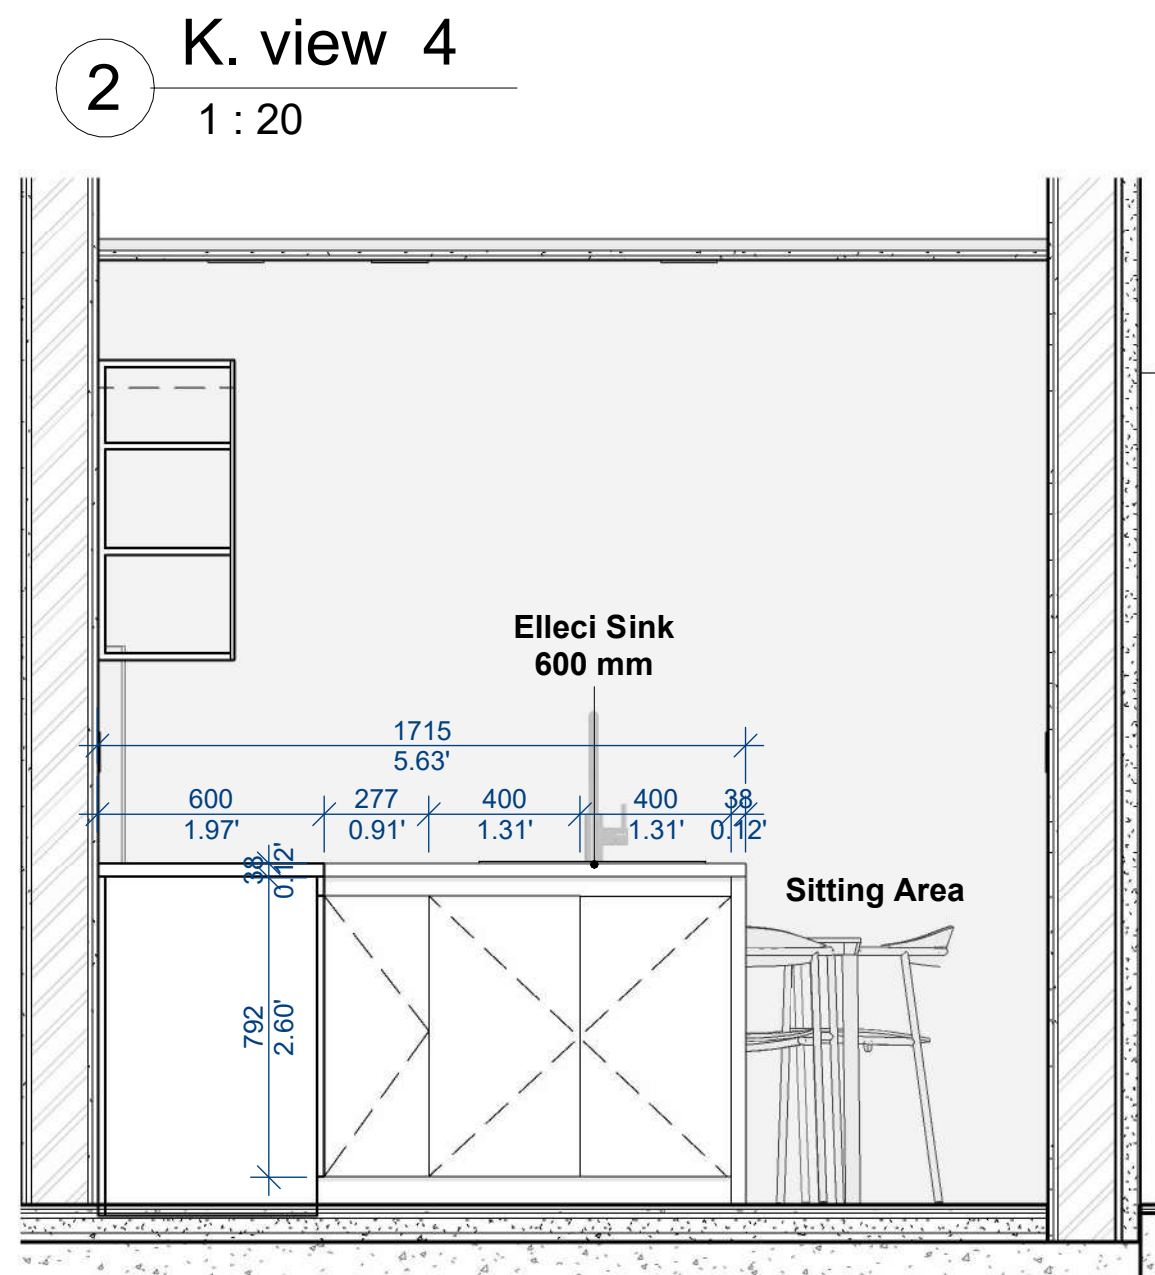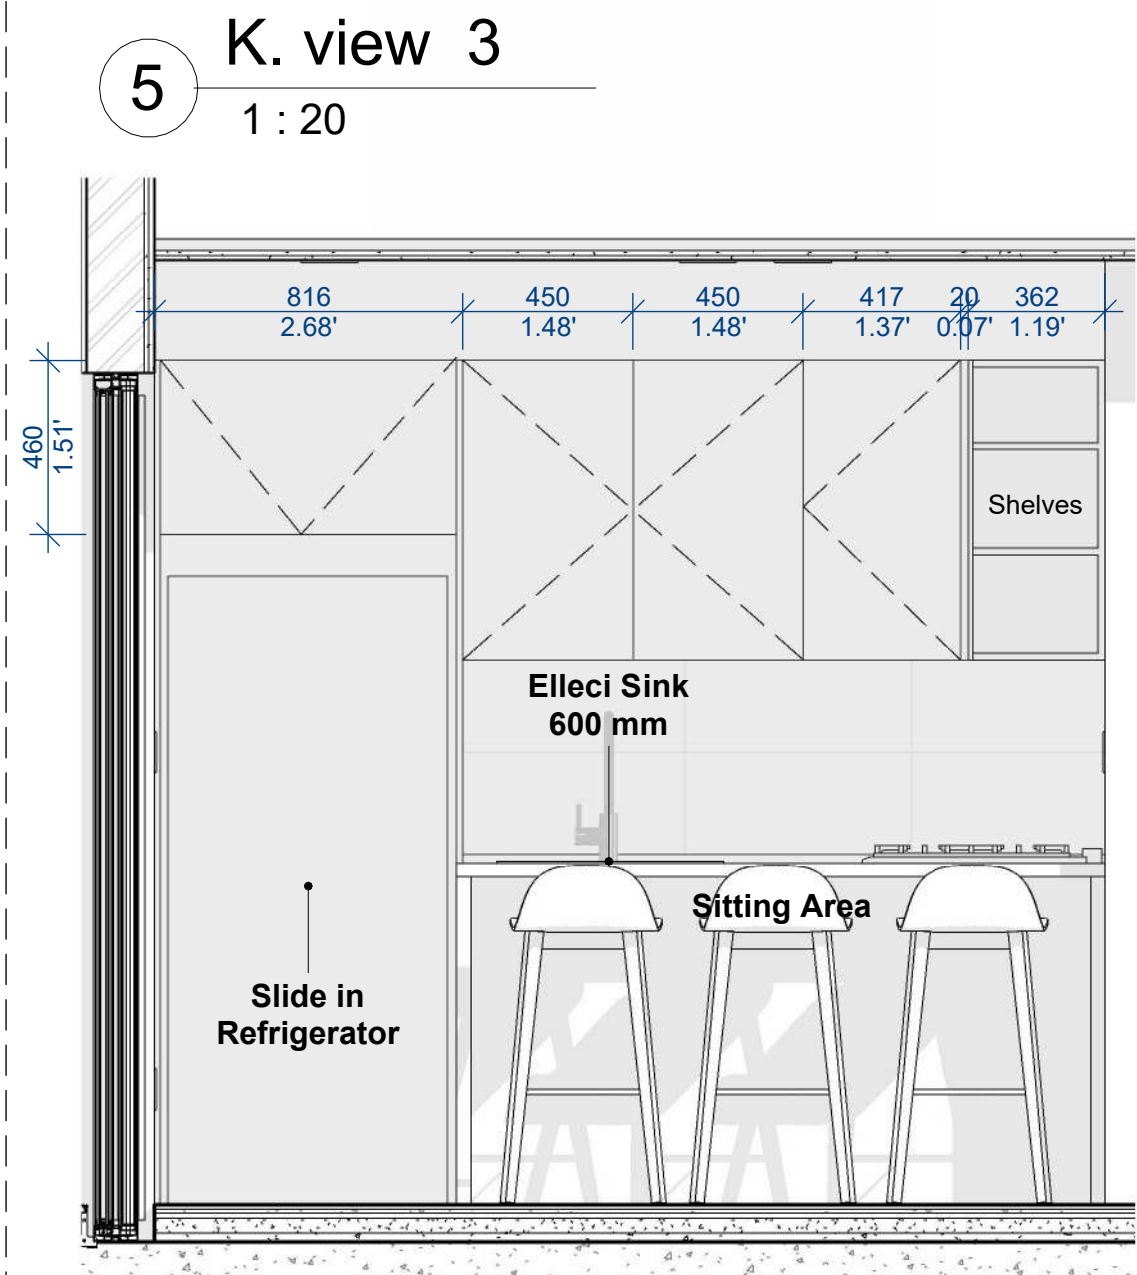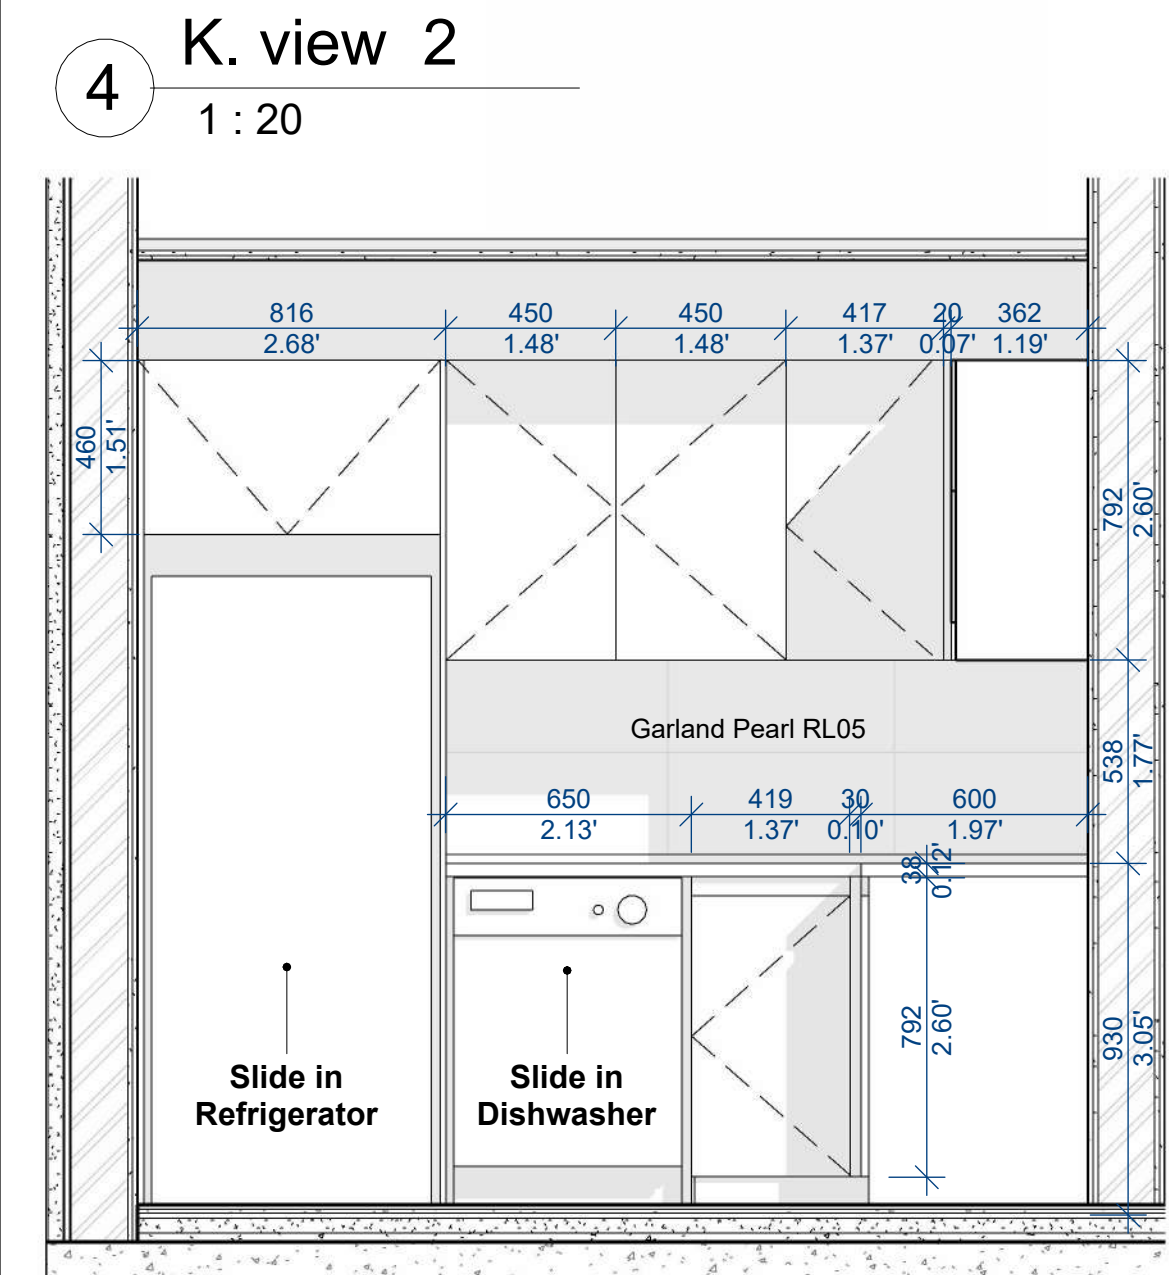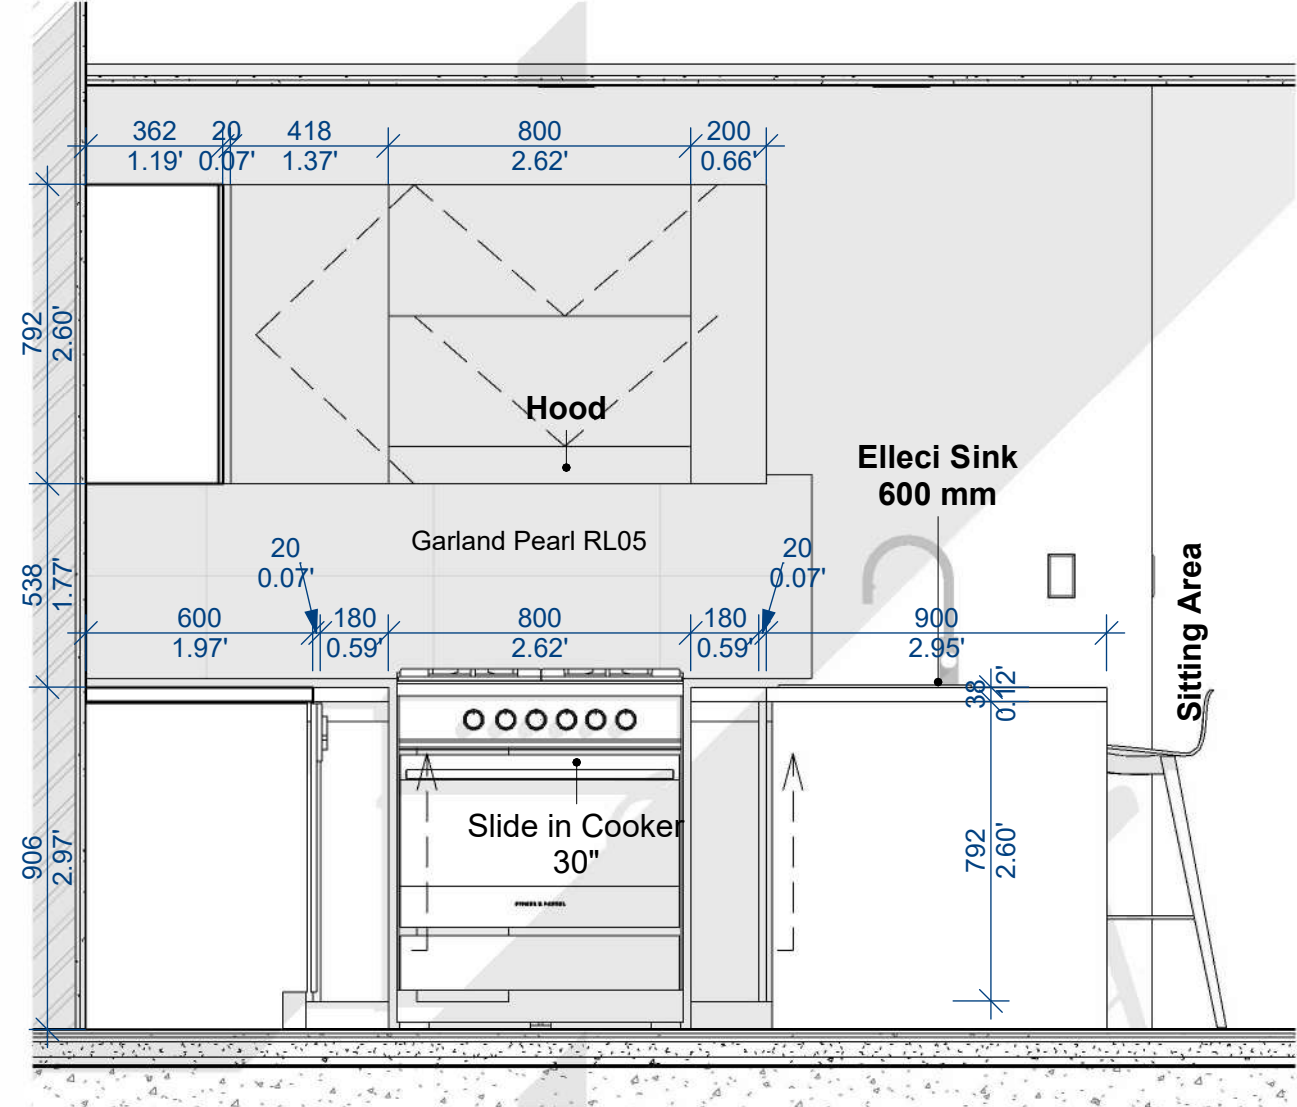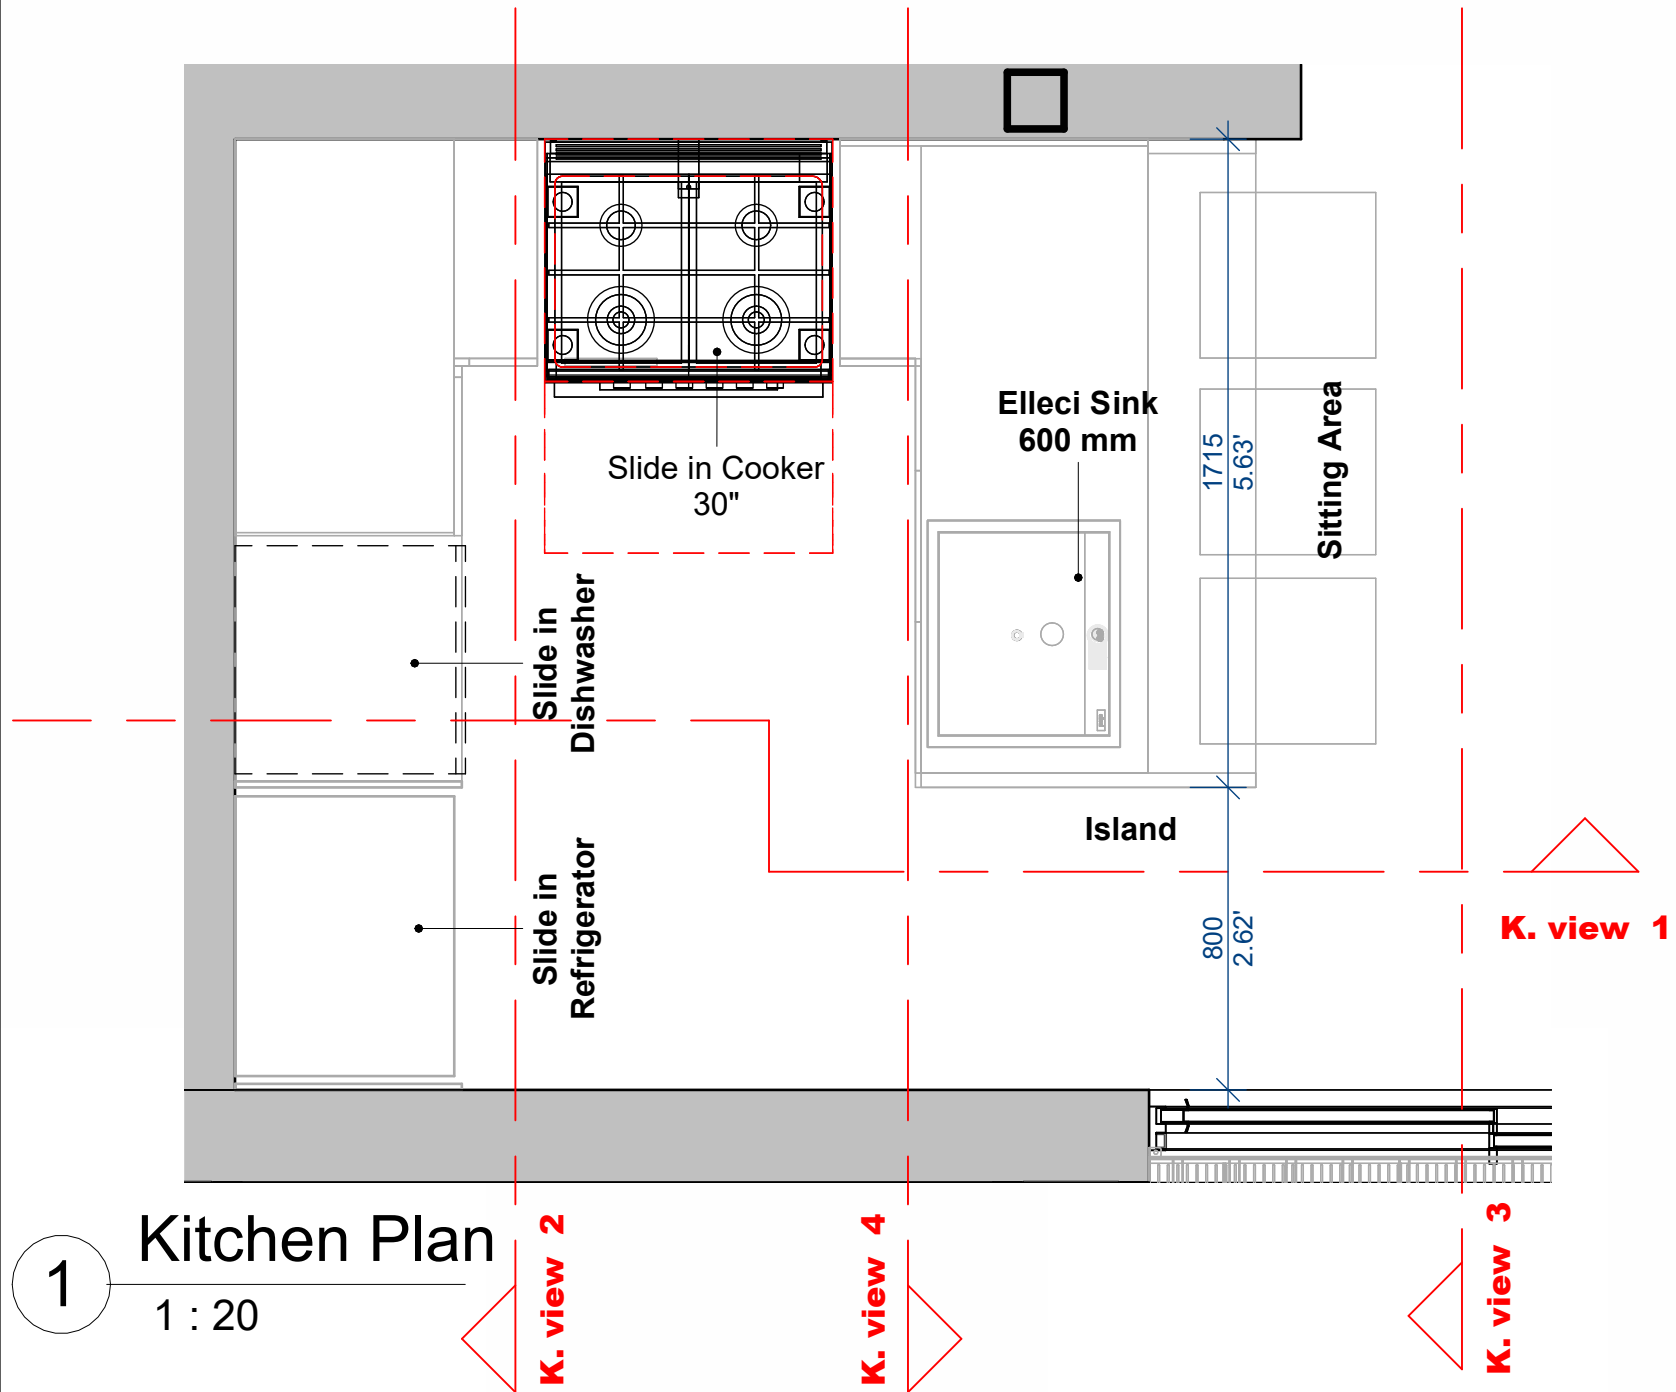

Kitchen appliances are shown for cabinet design purposes only and are not supplied.

1. THESE DRAWINGS MUST BE CHECKED BY THE CUSTOMER OR CONTRACTOR PRIOR TO APPROVAL. ANY ERRORS OR OMISSIONS MUST BE REPORTED IN WRITING TO BAUHU PRIOR TO COMMENCEMENT OF CONSTRUCTION.
2. ARCHITECTURAL DRAWINGS SHOULD BE READ IN CONJUNCTION WITH STRUCTURAL DETAILING AND FABRICATION GENERAL ASSEMBLY DRAWINGS.
3. FOR CONSTRUCTION PURPOSES, USE ONLY THE LATEST APPROVED DRAWINGS LABELED 'ISSUED FOR CONSTRUCTION'.
4. DO NOT SCALE FROM THIS DRAWING.
5. THE COMPANY OPERATES USING METRIC DIMENSIONS AS THE PRINCIPAL DENOMINATION.
6. ALL CONCRETE WORKS ARE OUTSIDE OF THE SCOPE OF THE COMPANY. INFORMATION REGARDING SLAB DESIGN AND CONNECTIONS IN THESE DRAWINGS ARE INTENDED FOR GUIDENCE ONLY. FOUNDATION AND SLAB WORKS SHOULD BE DESIGNED AND APPROVED BY A LOCAL STRUCTURAL ENGINEER.
7. THE COMPANY RETAINS FULL TITLE AND OWNERSHIP OF THESE PLANS AND DESIGNS. ANY UNAUTHORISED USE, REPRODUCTION, OR DISTRIBUTION OF THESE PLANS, WHETHER IN WHOLE OR PART, IS EXPRESSLY PROHIBITED WITHOUT PRIOR WRITTEN CONSENT.
8. THE HYBRID STEEL FRAME CONSTRUCTION SYSTEM AND METHODOLOGY (PATENT PENDING) DESCRIBED IN THESE PLANS HAS BEEN DEVELOPED BY THE COMPANY AND IS SUBJECT TO A PROVISIONAL PATENT APPLICATION & ASSIGNMENT - US APPLICATION No. 63/722,841.

No.	Revision	Date
01	Moved walls under roof joists	13.03

ISSUED FOR:

Issued for information

Issued for client approval

Issued for fabrication

Issued for construction

Bahama Beach


DRAWING TITLE:
Kitchen Plan&Sections

DRAWN BY:
Mladin Monica-Mihaela

SCALE:
1 : 20

DRAWING NO:
A33

DATE:
17/03/2025

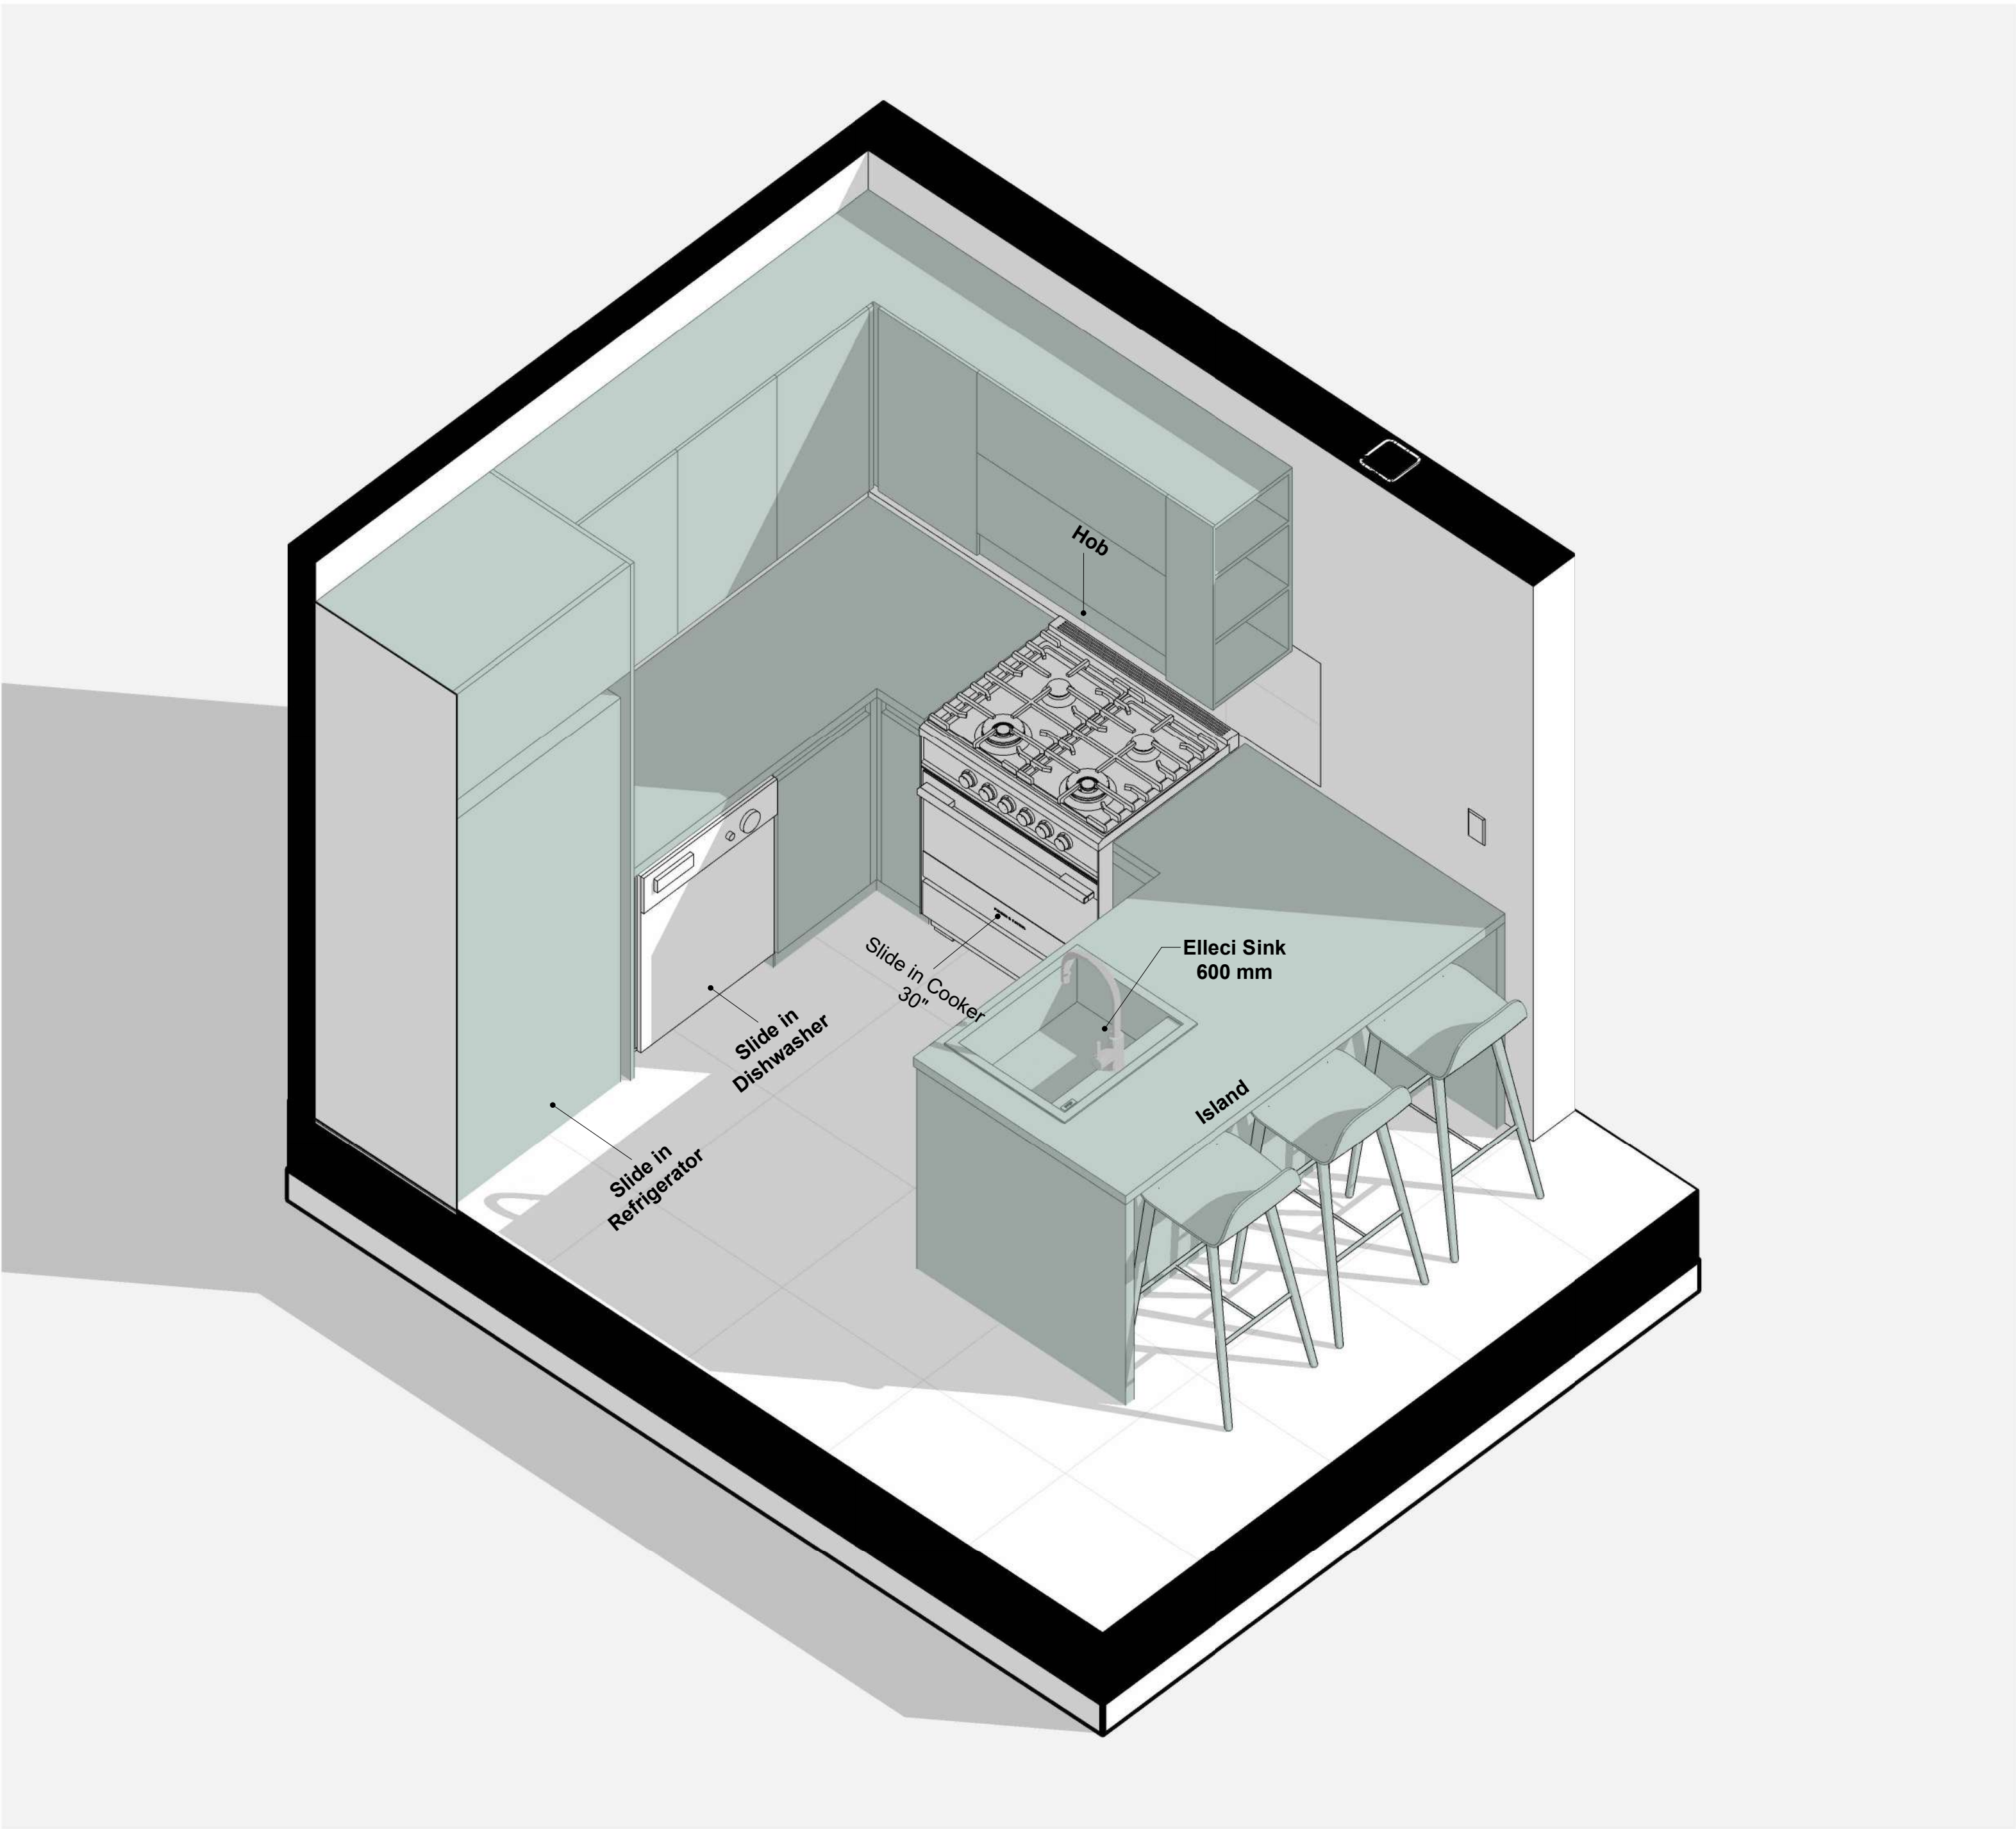

Kitchen appliances are shown for cabinet design purposes only and are not supplied.

1. THESE DRAWINGS MUST BE CHECKED BY THE CUSTOMER OR CONTRACTOR PRIOR TO APPROVAL. ANY ERRORS OR OMISSIONS MUST BE REPORTED IN WRITING TO BAUHU PRIOR TO COMMENCEMENT OF CONSTRUCTION.
2. ARCHITECTURAL DRAWINGS SHOULD BE READ IN CONJUNCTION WITH STRUCTURAL DETAILING AND FABRICATION GENERAL ASSEMBLY DRAWINGS.
3. FOR CONSTRUCTION PURPOSES, USE ONLY THE LATEST APPROVED DRAWINGS LABELED 'ISSUED FOR CONSTRUCTION'.
4. DO NOT SCALE FROM THIS DRAWING.
5. THE COMPANY OPERATES USING METRIC DIMENSIONS AS THE PRINCIPAL DENOMINATION.
6. ALL CONCRETE WORKS ARE OUTSIDE OF THE SCOPE OF THE COMPANY. INFORMATION REGARDING SLAB DESIGN AND CONNECTIONS IN THESE DRAWINGS ARE INTENDED FOR GUIDENCE ONLY. FOUNDATION AND SLAB WORKS SHOULD BE DESIGNED AND APPROVED BY A LOCAL STRUCTURAL ENGINEER.
7. THE COMPANY RETAINS FULL TITLE AND OWNERSHIP OF THESE PLANS AND DESIGNS. ANY UNAUTHORISED USE, REPRODUCTION, OR DISTRIBUTION OF THESE PLANS, WHETHER IN WHOLE OR PART, IS EXPRESSLY PROHIBITED WITHOUT PRIOR WRITTEN CONSENT.
8. THE HYBRID STEEL FRAME CONSTRUCTION SYSTEM AND METHODOLOGY (PATENT PENDING) DESCRIBED IN THESE PLANS HAS BEEN DEVELOPED BY THE COMPANY AND IS SUBJECT TO A PROVISIONAL PATENT APPLICATION & ASSIGNMENT - US APPLICATION No. 63/722,841.

No.	Revision	Date
01	Moved walls under roof joists	13.03

ISSUED FOR:

Issued for information

Issued for client approval

Issued for fabrication

Issued for construction

Bahama Beach

DRAWING TITLE:
Kitchen3D View

DRAWN BY:
Mladin Monica-Mihaela



SCALE:

DRAWING NO:
A34

DATE:
17/03/2025

Mixer

Bruma
Model: Kitchen Faucets
Name: Sink mixer with swivel spout and pull out aerator - Ginger
Reference: 107 054 2CR
Count: 1

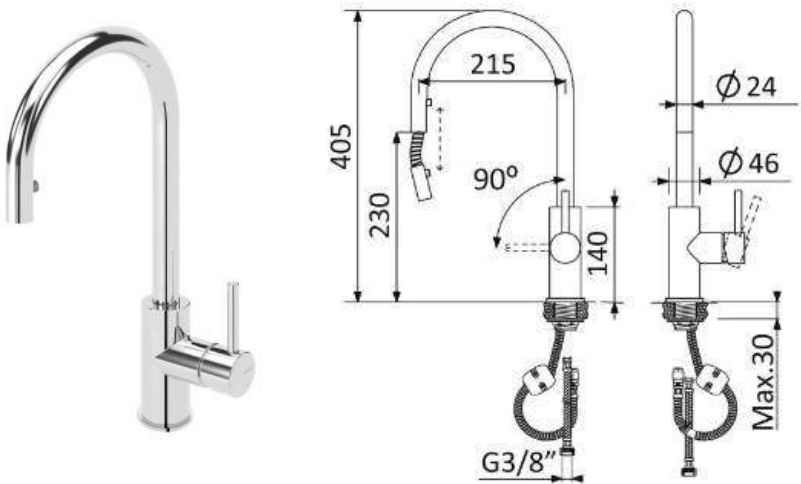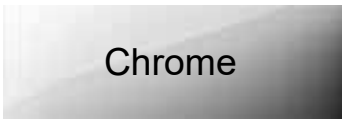

Nobilia Finishes

Worktop
Laminated 38 mm
376
Limestone reproduction




Kitchen - tiles

Garland Pearl RL05 - 45 x 45 cm . 18" x 18" / M15
45x45cm, Stone, Not Rectified
Glazed Porcelain Tiles, Mate

Kitchen Sink/Laundry sink

Sink Model: Elleci 1 bowl sink
Dimensions: 610x500
Reference: QUADRA 110
Colour: Dark Grey K99
Count: 1
<https://www.elleci.com/sinks/quadra-110/>

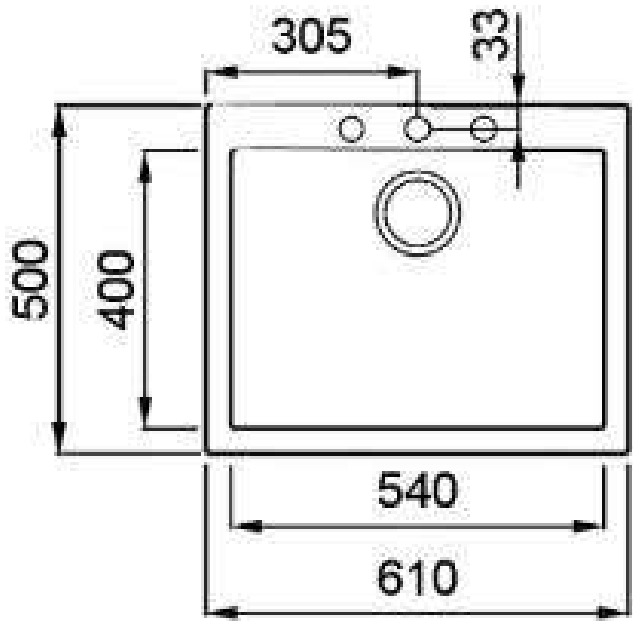

Nobilia Finishes

Handles - lower cabinets
012
Recessed Handle (LINE N),
Bronze metallic colour



Handles - suspended cabinets
cabinets
250
Bow handle, Black



Nobilia Finishes

Fronts suspended cabinets
415 - Sand

Carcase
122 - Sand





Carcase

Fronts

Nobilia Finishes

Fronts lower cabinets+ fridge cabinet + island
414 - Volcanic grey

Carcase
194 - Slate grey

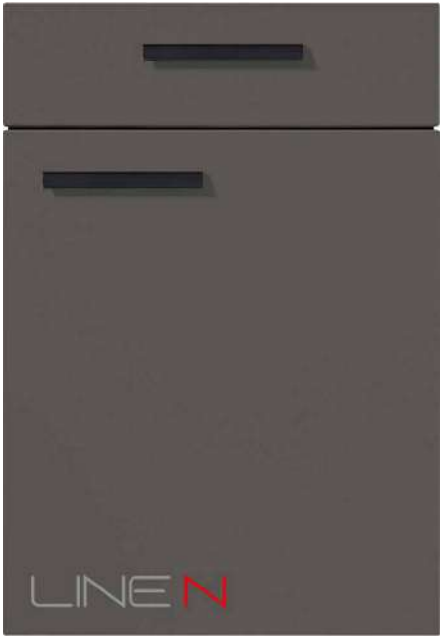 

Carcase

Fronts

BAUHU
MODULAR • BUILDING • SOLUTIONS

1. THESE DRAWINGS MUST BE CHECKED BY THE CUSTOMER OR CONTRACTOR PRIOR TO APPROVAL. ANY ERRORS OR OMISSIONS MUST BE REPORTED IN WRITING TO BAUHU PRIOR TO COMMENCEMENT OF CONSTRUCTION.
2. ARCHITECTURAL DRAWINGS SHOULD BE READ IN CONJUNCTION WITH STRUCTURAL DETAILING AND FABRICATION GENERAL ASSEMBLY DRAWINGS.
3. FOR CONSTRUCTION PURPOSES, USE ONLY THE LATEST APPROVED DRAWINGS LABELED 'ISSUED FOR CONSTRUCTION'.
4. DO NOT SCALE FROM THIS DRAWING.
5. THE COMPANY OPERATES USING METRIC DIMENSIONS AS THE PRINCIPAL DENOMINATION.
6. ALL CONCRETE WORKS ARE OUTSIDE OF THE SCOPE OF THE COMPANY. INFORMATION REGARDING SLAB DESIGN AND CONNECTIONS IN THESE DRAWINGS ARE INTENDED FOR GUIDENCE ONLY. FOUNDATION AND SLAB WORKS SHOULD BE DESIGNED AND APPROVED BY A LOCAL STRUCTURAL ENGINEER.
7. THE COMPANY RETAINS FULL TITLE AND OWNERSHIP OF THESE PLANS AND DESIGNS. ANY UNAUTHORISED USE, REPRODUCTION, OR DISTRIBUTION OF THESE PLANS, WHETHER IN WHOLE OR PART, IS EXPRESSLY PROHIBITED WITHOUT PRIOR WRITTEN CONSENT.
8. THE HYBRID STEEL FRAME CONSTRUCTION SYSTEM AND METHODOLOGY (PATENT PENDING) DESCRIBED IN THESE PLANS HAS BEEN DEVELOPED BY THE COMPANY AND IS SUBJECT TO A PROVISIONAL PATENT APPLICATION & ASSIGNMENT - US APPLICATION No. 63/722,841.

No.	Revision	Date
01	Moved walls under roof joists	13.03

ISSUED FOR:

Issued for information

Issued for client approval

Issued for fabrication

Issued for construction

Bahama Beach

DRAWING TITLE:
Kitchen Finishes

DRAWN BY:
Mladin Monica-Mihaela

SCALE:

DRAWING NO:
A35

DATE:
17/03/2025

Kitchen appliances are shown for cabinet design purposes only and are not supplied.

Refrigerator GTE18MSRRSS GE® ENERGY STAR® 18.3 Cu. Ft. Top-Freezer Refrigerator Dimensions: 66 3/4 H x 29 3/4 W x 32 7/8 D 1695.45 H x 755.65 W x 835.025 D (mm) 	Cook range GTE18MSRRSS DeLonghi Modern 70 DDC 707-DF Dimensions: width 70 cm 	BAUHU MODULAR • BUILDING • SOLUTIONS 1. THESE DRAWINGS MUST BE CHECKED BY THE CUSTOMER OR CONTRACTOR PRIOR TO APPROVAL. ANY ERRORS OR OMISSIONS MUST BE REPORTED IN WRITING TO BAUHU PRIOR TO COMMENCEMENT OF CONSTRUCTION. 2. ARCHITECTURAL DRAWINGS SHOULD BE READ IN CONJUNCTION WITH STRUCTURAL DETAILING AND FABRICATION GENERAL ASSEMBLY DRAWINGS. 3. FOR CONSTRUCTION PURPOSES, USE ONLY THE LATEST APPROVED DRAWINGS LABELED 'ISSUED FOR CONSTRUCTION'. 4. DO NOT SCALE FROM THIS DRAWING. 5. THE COMPANY OPERATES USING METRIC DIMENSIONS AS THE PRINCIPAL DENOMINATION. 6. ALL CONCRETE WORKS ARE OUTSIDE OF THE SCOPE OF THE COMPANY. INFORMATION REGARDING SLAB DESIGN AND CONNECTIONS IN THESE DRAWINGS ARE INTENDED FOR GUIDENCE ONLY. FOUNDATION AND SLAB WORKS SHOULD BE DESIGNED AND APPROVED BY A LOCAL STRUCTURAL ENGINEER. 7. THE COMPANY RETAINS FULL TITLE AND OWNERSHIP OF THESE PLANS AND DESIGNS. ANY UNAUTHORISED USE, REPRODUCTION, OR DISTRIBUTION OF THESE PLANS, WHETHER IN WHOLE OR PART, IS EXPRESSLY PROHIBITED WITHOUT PRIOR WRITTEN CONSENT. 8. THE HYBRID STEEL FRAME CONSTRUCTION SYSTEM AND METHODOLOGY (PATENT PENDING) DESCRIBED IN THESE PLANS HAS BEEN DEVELOPED BY THE COMPANY AND IS SUBJECT TO A PROVISIONAL PATENT APPLICATION & ASSIGNMENT - US APPLICATION No. 63/722,841. <table><tr><th>No.</th><th>Revision</th><th>Date</th></tr><tr><td>01</td><td>Moved walls under roof joists</td><td>13.03</td></tr><tr><td> </td><td> </td><td> </td></tr><tr><td> </td><td> </td><td> </td></tr><tr><td> </td><td> </td><td> </td></tr><tr><td> </td><td> </td><td> </td></tr><tr><td> </td><td> </td><td> </td></tr><tr><td> </td><td> </td><td> </td></tr><tr><td> </td><td> </td><td> </td></tr><tr><td> </td><td> </td><td> </td></tr><tr><td> </td><td> </td><td> </td></tr><tr><td> </td><td> </td><td> </td></tr></table> ISSUED FOR: Issued for information Issued for client approval Issued for fabrication Issued for construction Bahama Beach DRAWING TITLE: Kitchen Appliances DRAWN BY: Mladin Monica-Mihaela SCALE: DRAWING NO: A36 DATE: 17/03/2025	No.	Revision	Date	01	Moved walls under roof joists	13.03																														
No.	Revision	Date																																				
01	Moved walls under roof joists	13.03																																				
Built-in Dishwasher PDT795SYVFS GE Profile™ ENERGY STAR Smart UltraFresh System Dishwasher with Microban™ Antimicrobial Technology with Deep Clean Washing 3rd Rack, 39 dBA Dimensions: 34 H x 23 3/4 W x 24 D 863.6 H x 603.25 W x 609.6 D (mm) Color: Fingerprint Resistant Stainless 	Hood PVX7300SJSS GE Profile™ 30" Under The Cabinet Hood Dimensions: 5 1/2 H x 29 7/8 W x 20 D 139.7 H x 758.825 W x 508 D (mm) Color: Stainless Steel 																																					
Laundry Room - Washer GFW655SSVWW 5.0 cu. ft. Capacity Smart Front Load ENERGY STAR® Steam Washer with SmartDispense™ UltraFresh Vent System with OdorBlock™ and Sanitize + Allergen 	Laundry Room - Dryer GFD65GSSVWW 7.8 cu. ft. Capacity Smart Front Load Gas Dryer with Steam and Sanitize Cycle 																																					


Note:

- Kitchen appliances are shown for cabinet design purposes only and are not supplied.

Interior Finishes

Floor Tiles

Garland Pearl RL05 - 45 x 45 cm . 18" x 18" / M15
45x45cm, Stone, Not Rectified
Glazed Porcelain Tiles, Mate

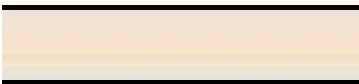


Grout Jasmine 130

Bathroom and kitchen tiles

Garland Pearl RL05 - 45 x 45 cm . 18" x 18" / M15
45x45cm, Stone, Not Rectified
Glazed Porcelain Tiles, Mate

Bathroom tiles

1.Stella White SA05R - 34 x 66,5 cm . 13,4" x 26,2" / R16
34x66,5cm, Cor, Não Rectificado
Revestimento Pasta Branca, Brilho
2.Stella Brick Blue SA53R - 34 x 66,5 cm . 13,4" x 26,2" / R17
Decorações 34x66,5cm, Cor, Não Rectificado
Revestimento Pasta Branca, Brilho

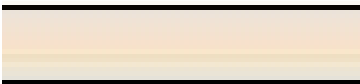

Grout Jasmine 130



Stella White SA05R



Stella Brick Blue SA53R

Ceiling Colour

CIN
• White #0501



Wall Colour

CIN
• Marble Beige #1390




Furniture type:

Compincar - model 1003

Interior Doors:

Compincar - Lisa

 

LISA

Exterior Finishes


Exterior Wall Finish

Exterior Wall Finish
Stolit K fine grain exterior plaster
Colour: RAL9003 Signal White
RGB: 236, 236, 232
HEX code: #ECECE8.




Exterior Floor Tiles

Garland Pearl RL05 - 45 x 45 cm . 18" x 18" / M15
45x45cm, Stone, Not Rectified
Glazed Porcelain Tiles, Mate

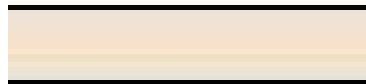

Cortizo Window/Door Frames

https://www.cortizo.com/paginas/carta_standard

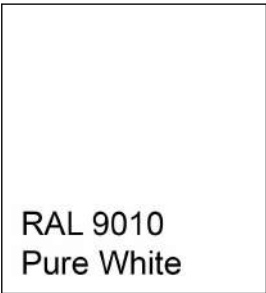

Colour: Pure White
RAL: 9010


Glass

<https://www.guardianglass.com/gb/en/our-glass/glass-types/solar-control-glass>

- 44.2+16argon we+6 SNX

Roof Finish

- Acrylabs elastomeric roofing membrane
- Colour: 'standard white'

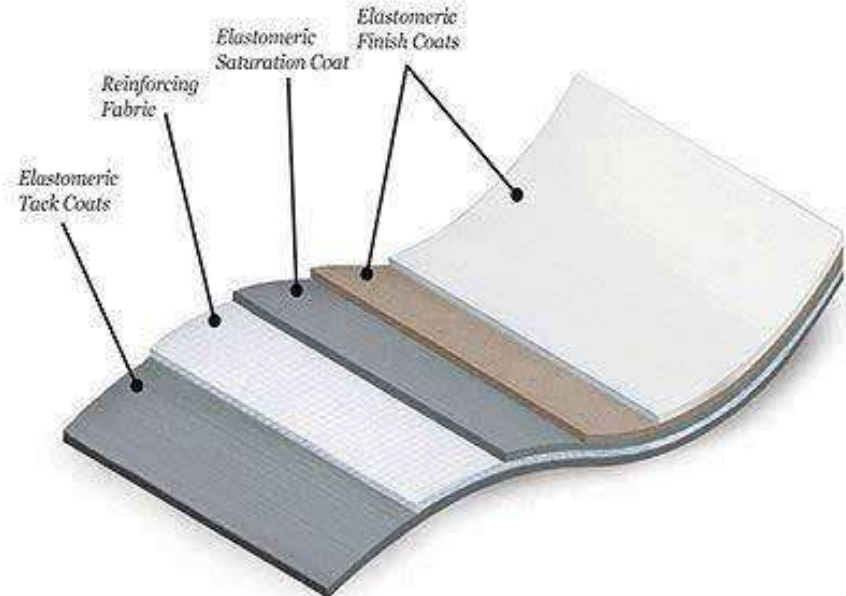

BAUHU
MODULAR • BUILDING • SOLUTIONS

1. THESE DRAWINGS MUST BE CHECKED BY THE CUSTOMER OR CONTRACTOR PRIOR TO APPROVAL. ANY ERRORS OR OMISSIONS MUST BE REPORTED IN WRITING TO BAUHU PRIOR TO COMMENCEMENT OF CONSTRUCTION.
2. ARCHITECTURAL DRAWINGS SHOULD BE READ IN CONJUNCTION WITH STRUCTURAL DETAILING AND FABRICATION GENERAL ASSEMBLY DRAWINGS.
3. FOR CONSTRUCTION PURPOSES, USE ONLY THE LATEST APPROVED DRAWINGS LABELED 'ISSUED FOR CONSTRUCTION'.
4. DO NOT SCALE FROM THIS DRAWING.
5. THE COMPANY OPERATES USING METRIC DIMENSIONS AS THE PRINCIPAL DENOMINATION.
6. ALL CONCRETE WORKS ARE OUTSIDE OF THE SCOPE OF THE COMPANY. INFORMATION REGARDING SLAB DESIGN AND CONNECTIONS IN THESE DRAWINGS ARE INTENDED FOR GUIDENCE ONLY. FOUNDATION AND SLAB WORKS SHOULD BE DESIGNED AND APPROVED BY A LOCAL STRUCTURAL ENGINEER.
7. THE COMPANY RETAINS FULL TITLE AND OWNERSHIP OF THESE PLANS AND DESIGNS. ANY UNAUTHORISED USE, REPRODUCTION, OR DISTRIBUTION OF THESE PLANS, WHETHER IN WHOLE OR PART, IS EXPRESSLY PROHIBITED WITHOUT PRIOR WRITTEN CONSENT.
8. THE HYBRID STEEL FRAME CONSTRUCTION SYSTEM AND METHODOLOGY (PATENT PENDING) DESCRIBED IN THESE PLANS HAS BEEN DEVELOPED BY THE COMPANY AND IS SUBJECT TO A PROVISIONAL PATENT APPLICATION & ASSIGNMENT - US APPLICATION No. 63/722,841.

No.	Revision	Date
01	Moved walls under roof joists	13.03

ISSUED FOR:

Issued for information

Issued for client approval

Issued for fabrication

Issued for construction

Bahama Beach

DRAWING TITLE:

Finishes

DRAWN BY:

Mladin Monica-Mihaela


SCALE:

DRAWING NO:

A37

DATE:

17/03/2025

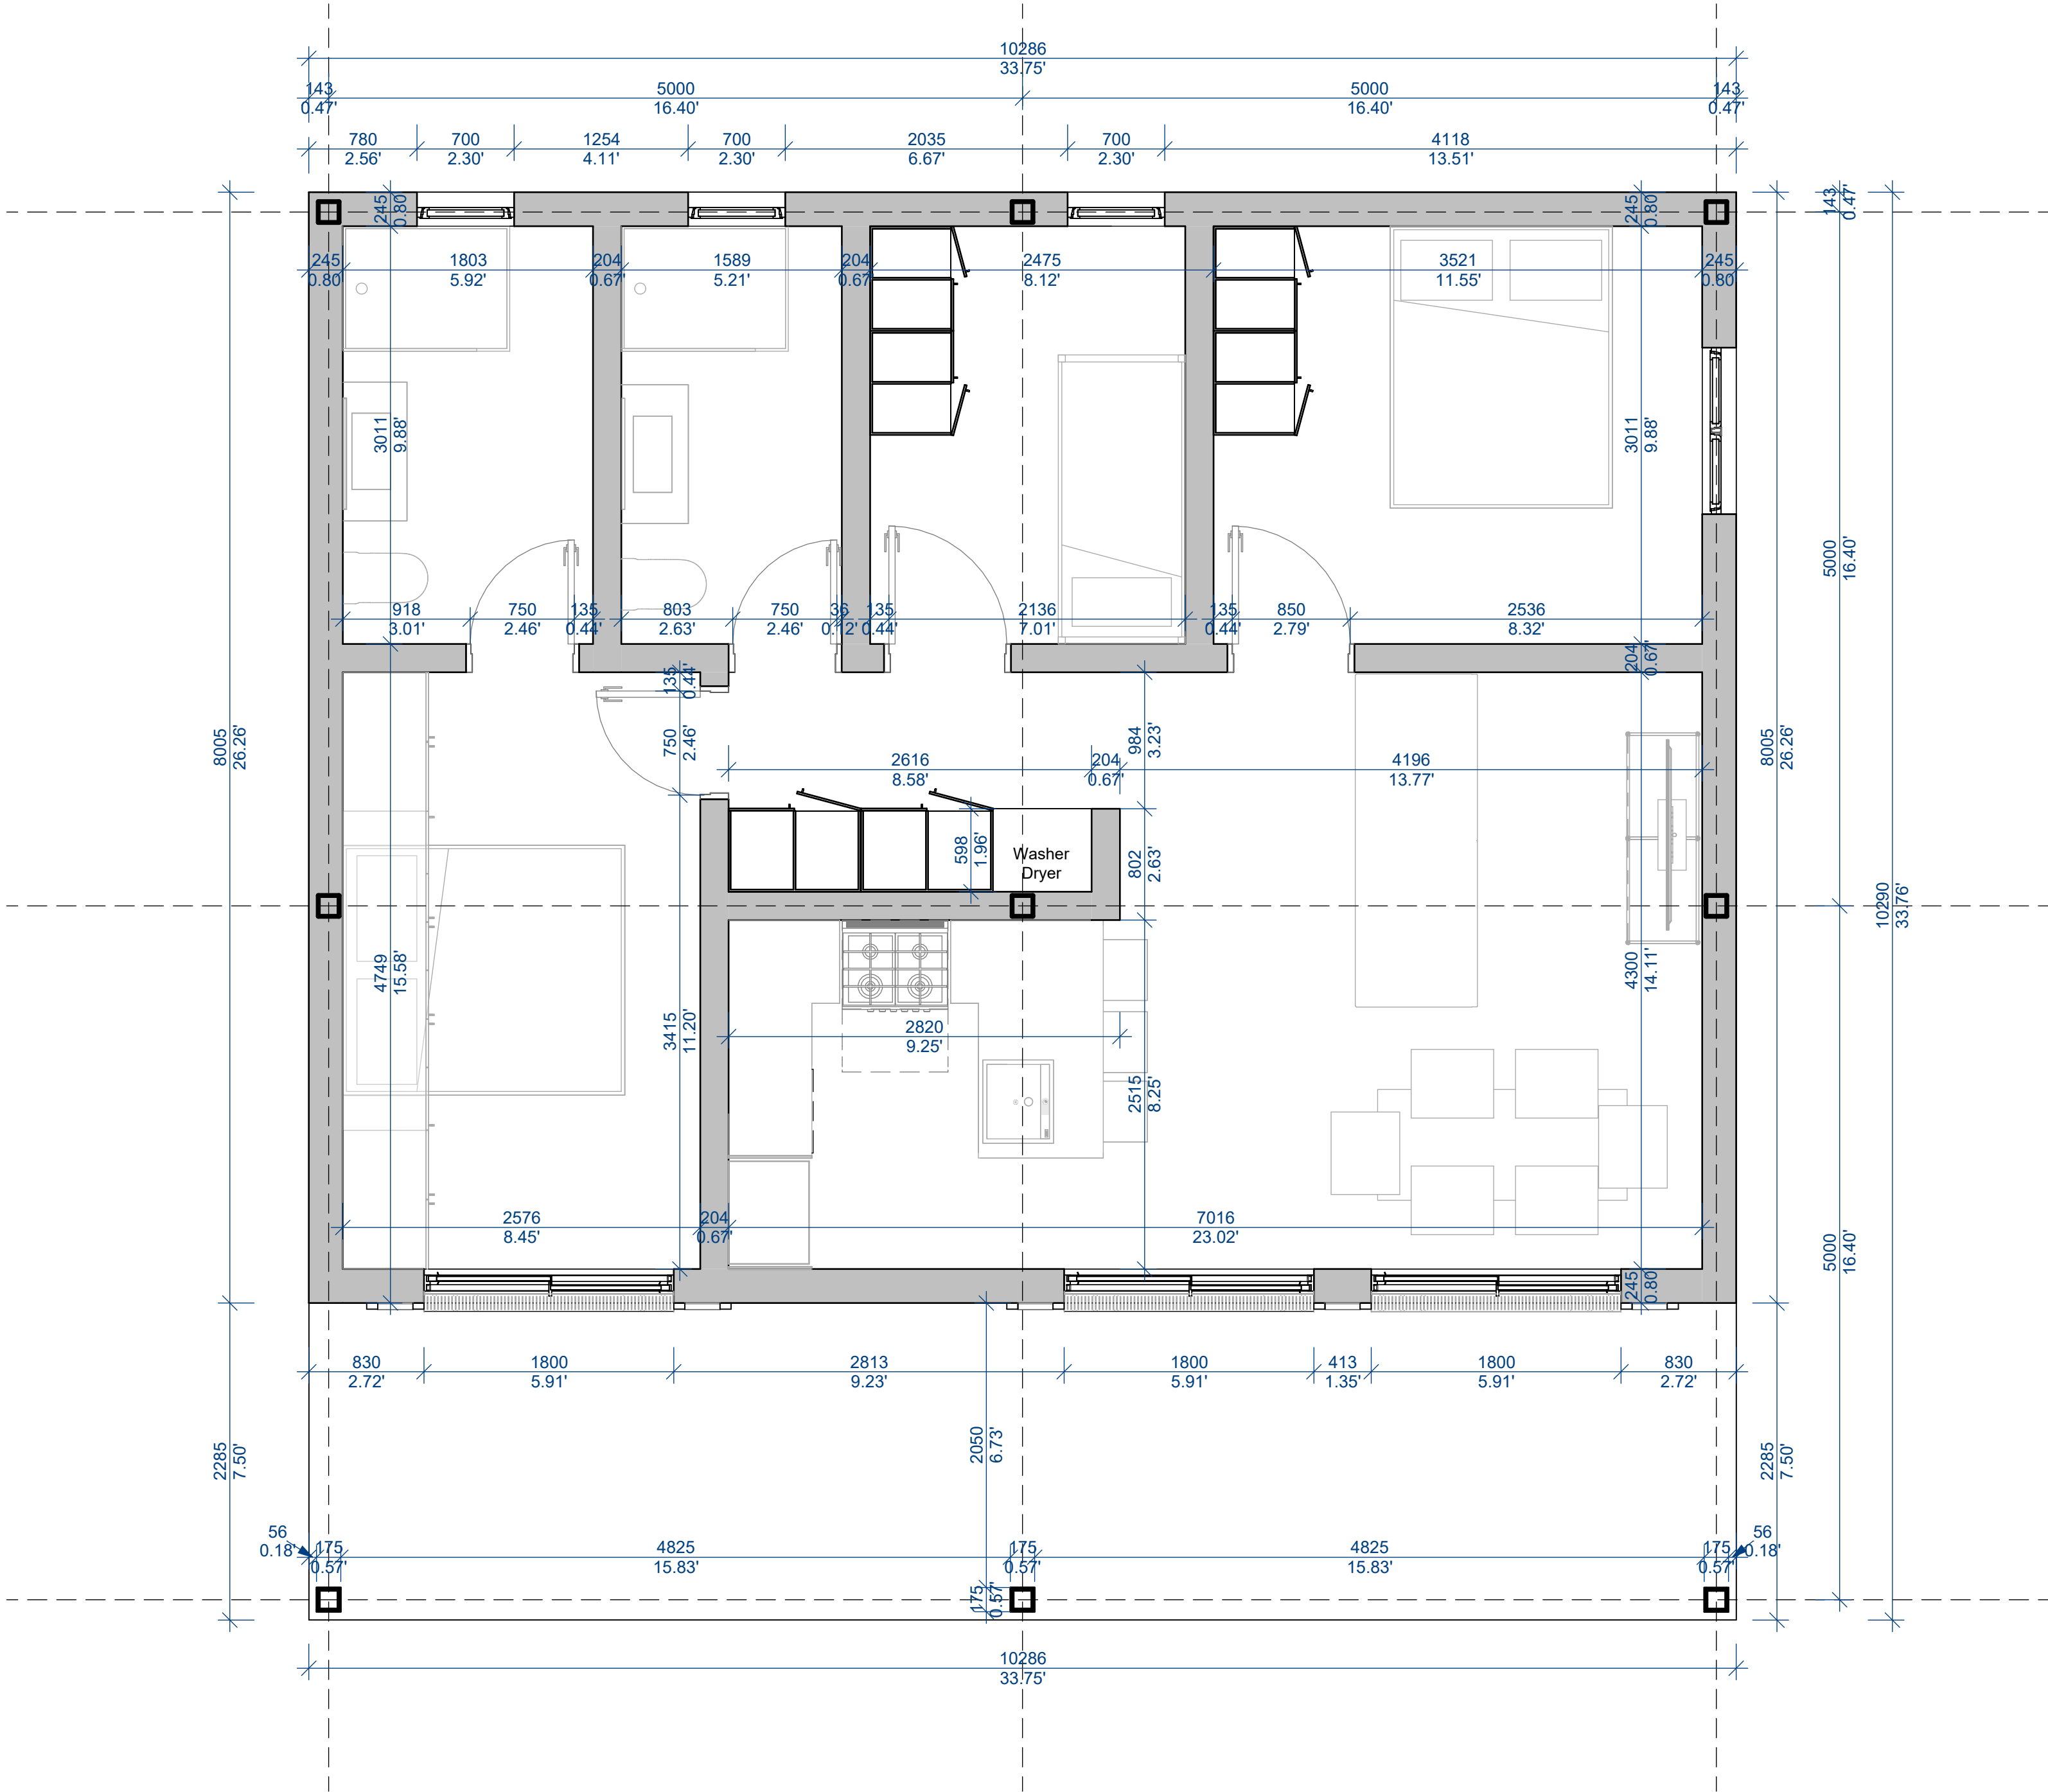

1. THESE DRAWINGS MUST BE CHECKED BY THE CUSTOMER OR CONTRACTOR PRIOR TO APPROVAL. ANY ERRORS OR OMISSIONS MUST BE REPORTED IN WRITING TO BAUHU PRIOR TO COMMENCEMENT OF CONSTRUCTION.
2. ARCHITECTURAL DRAWINGS SHOULD BE READ IN CONJUNCTION WITH STRUCTURAL DETAILING AND FABRICATION GENERAL ASSEMBLY DRAWINGS.
3. FOR CONSTRUCTION PURPOSES, USE ONLY THE LATEST APPROVED DRAWINGS LABELED 'ISSUED FOR CONSTRUCTION'.
4. DO NOT SCALE FROM THIS DRAWING.
5. THE COMPANY OPERATES USING METRIC DIMENSIONS AS THE PRINCIPAL DENOMINATION.
6. ALL CONCRETE WORKS ARE OUTSIDE OF THE SCOPE OF THE COMPANY. INFORMATION REGARDING SLAB DESIGN AND CONNECTIONS IN THESE DRAWINGS ARE INTENDED FOR GUIDENCE ONLY. FOUNDATION AND SLAB WORKS SHOULD BE DESIGNED AND APPROVED BY A LOCAL STRUCTURAL ENGINEER.
7. THE COMPANY RETAINS FULL TITLE AND OWNERSHIP OF THESE PLANS AND DESIGNS. ANY UNAUTHORISED USE, REPRODUCTION, OR DISTRIBUTION OF THESE PLANS, WHETHER IN WHOLE OR PART, IS EXPRESSLY PROHIBITED WITHOUT PRIOR WRITTEN CONSENT.
8. THE HYBRID STEEL FRAME CONSTRUCTION SYSTEM AND METHODOLOGY (PATENT PENDING) DESCRIBED IN THESE PLANS HAS BEEN DEVELOPED BY THE COMPANY AND IS SUBJECT TO A PROVISIONAL PATENT APPLICATION & ASSIGNMENT - US APPLICATION No. 63/722,841.

No.	Revision	Date
01	Moved walls under roof joists	13.03

- ISSUED FOR:
- ☒ Issued for information
 - ☐ Issued for client approval
 - ☐ Issued for fabrication
 - ☐ Issued for construction

Bahama Beach


DRAWING TITLE:
Floor Plan Dimensions

DRAWN BY:
Mladin Monica-Mihaela

SCALE:
1 : 35

DRAWING NO:
A38

DATE:
17/03/2025

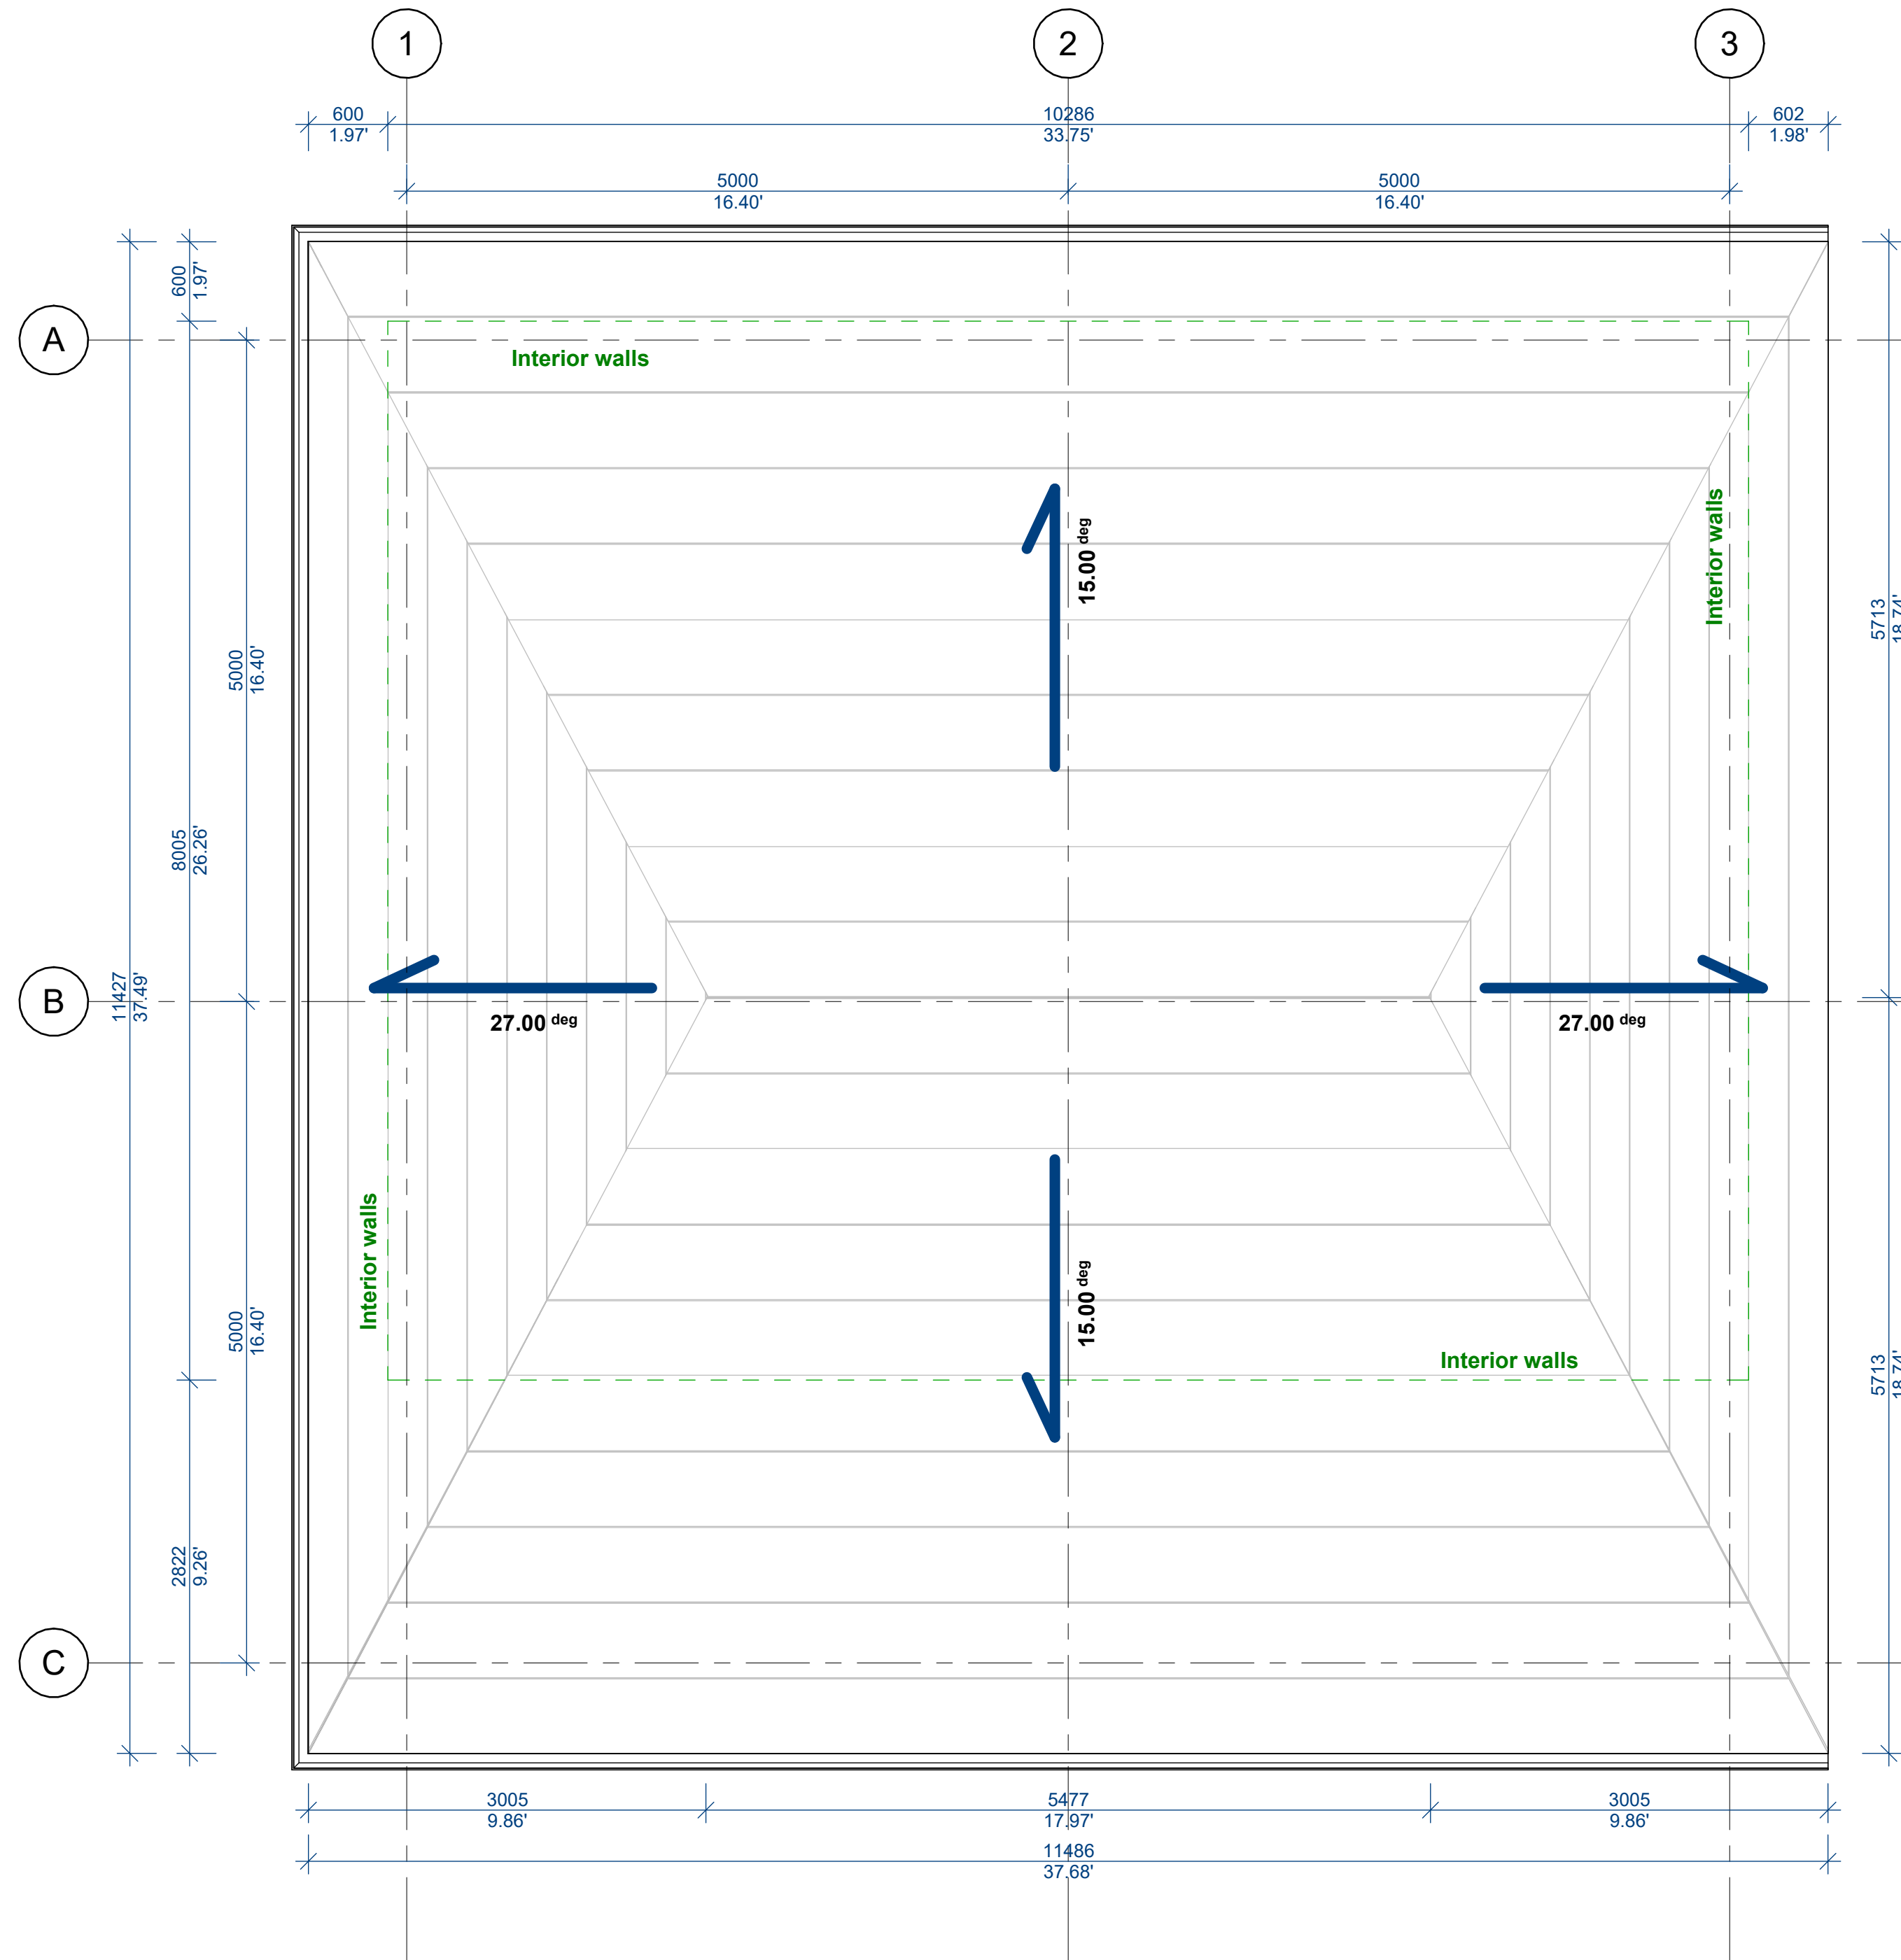

BAUHU
MODULAR • BUILDING • SOLUTIONS

1. THESE DRAWINGS MUST BE CHECKED BY THE CUSTOMER OR CONTRACTOR PRIOR TO APPROVAL. ANY ERRORS OR OMISSIONS MUST BE REPORTED IN WRITING TO BAUHU PRIOR TO COMMENCEMENT OF CONSTRUCTION.
2. ARCHITECTURAL DRAWINGS SHOULD BE READ IN CONJUNCTION WITH STRUCTURAL DETAILING AND FABRICATION GENERAL ASSEMBLY DRAWINGS.
3. FOR CONSTRUCTION PURPOSES, USE ONLY THE LATEST APPROVED DRAWINGS LABELED 'ISSUED FOR CONSTRUCTION'.
4. DO NOT SCALE FROM THIS DRAWING.
5. THE COMPANY OPERATES USING METRIC DIMENSIONS AS THE PRINCIPAL DENOMINATION.
6. ALL CONCRETE WORKS ARE OUTSIDE OF THE SCOPE OF THE COMPANY. INFORMATION REGARDING SLAB DESIGN AND CONNECTIONS IN THESE DRAWINGS ARE INTENDED FOR GUIDENCE ONLY. FOUNDATION AND SLAB WORKS SHOULD BE DESIGNED AND APPROVED BY A LOCAL STRUCTURAL ENGINEER.
7. THE COMPANY RETAINS FULL TITLE AND OWNERSHIP OF THESE PLANS AND DESIGNS. ANY UNAUTHORISED USE, REPRODUCTION, OR DISTRIBUTION OF THESE PLANS, WHETHER IN WHOLE OR PART, IS EXPRESSLY PROHIBITED WITHOUT PRIOR WRITTEN CONSENT.
8. THE HYBRID STEEL FRAME CONSTRUCTION SYSTEM AND METHODOLOGY (PATENT PENDING) DESCRIBED IN THESE PLANS HAS BEEN DEVELOPED BY THE COMPANY AND IS SUBJECT TO A PROVISIONAL PATENT APPLICATION & ASSIGNMENT - US APPLICATION No. 63/722.841.

[illegible]

ISSUED FOR:

Issued for information

Issued for client approval

Issued for fabrication

Issued for construction

Bahama Beach

DRAWING TITLE:
Roof Dimensions

DRAWN BY:

Mladin Monica-Mihaela


SCALE:

1 : 40

DRAWING NO:

A39

DATE: 17/03/2025

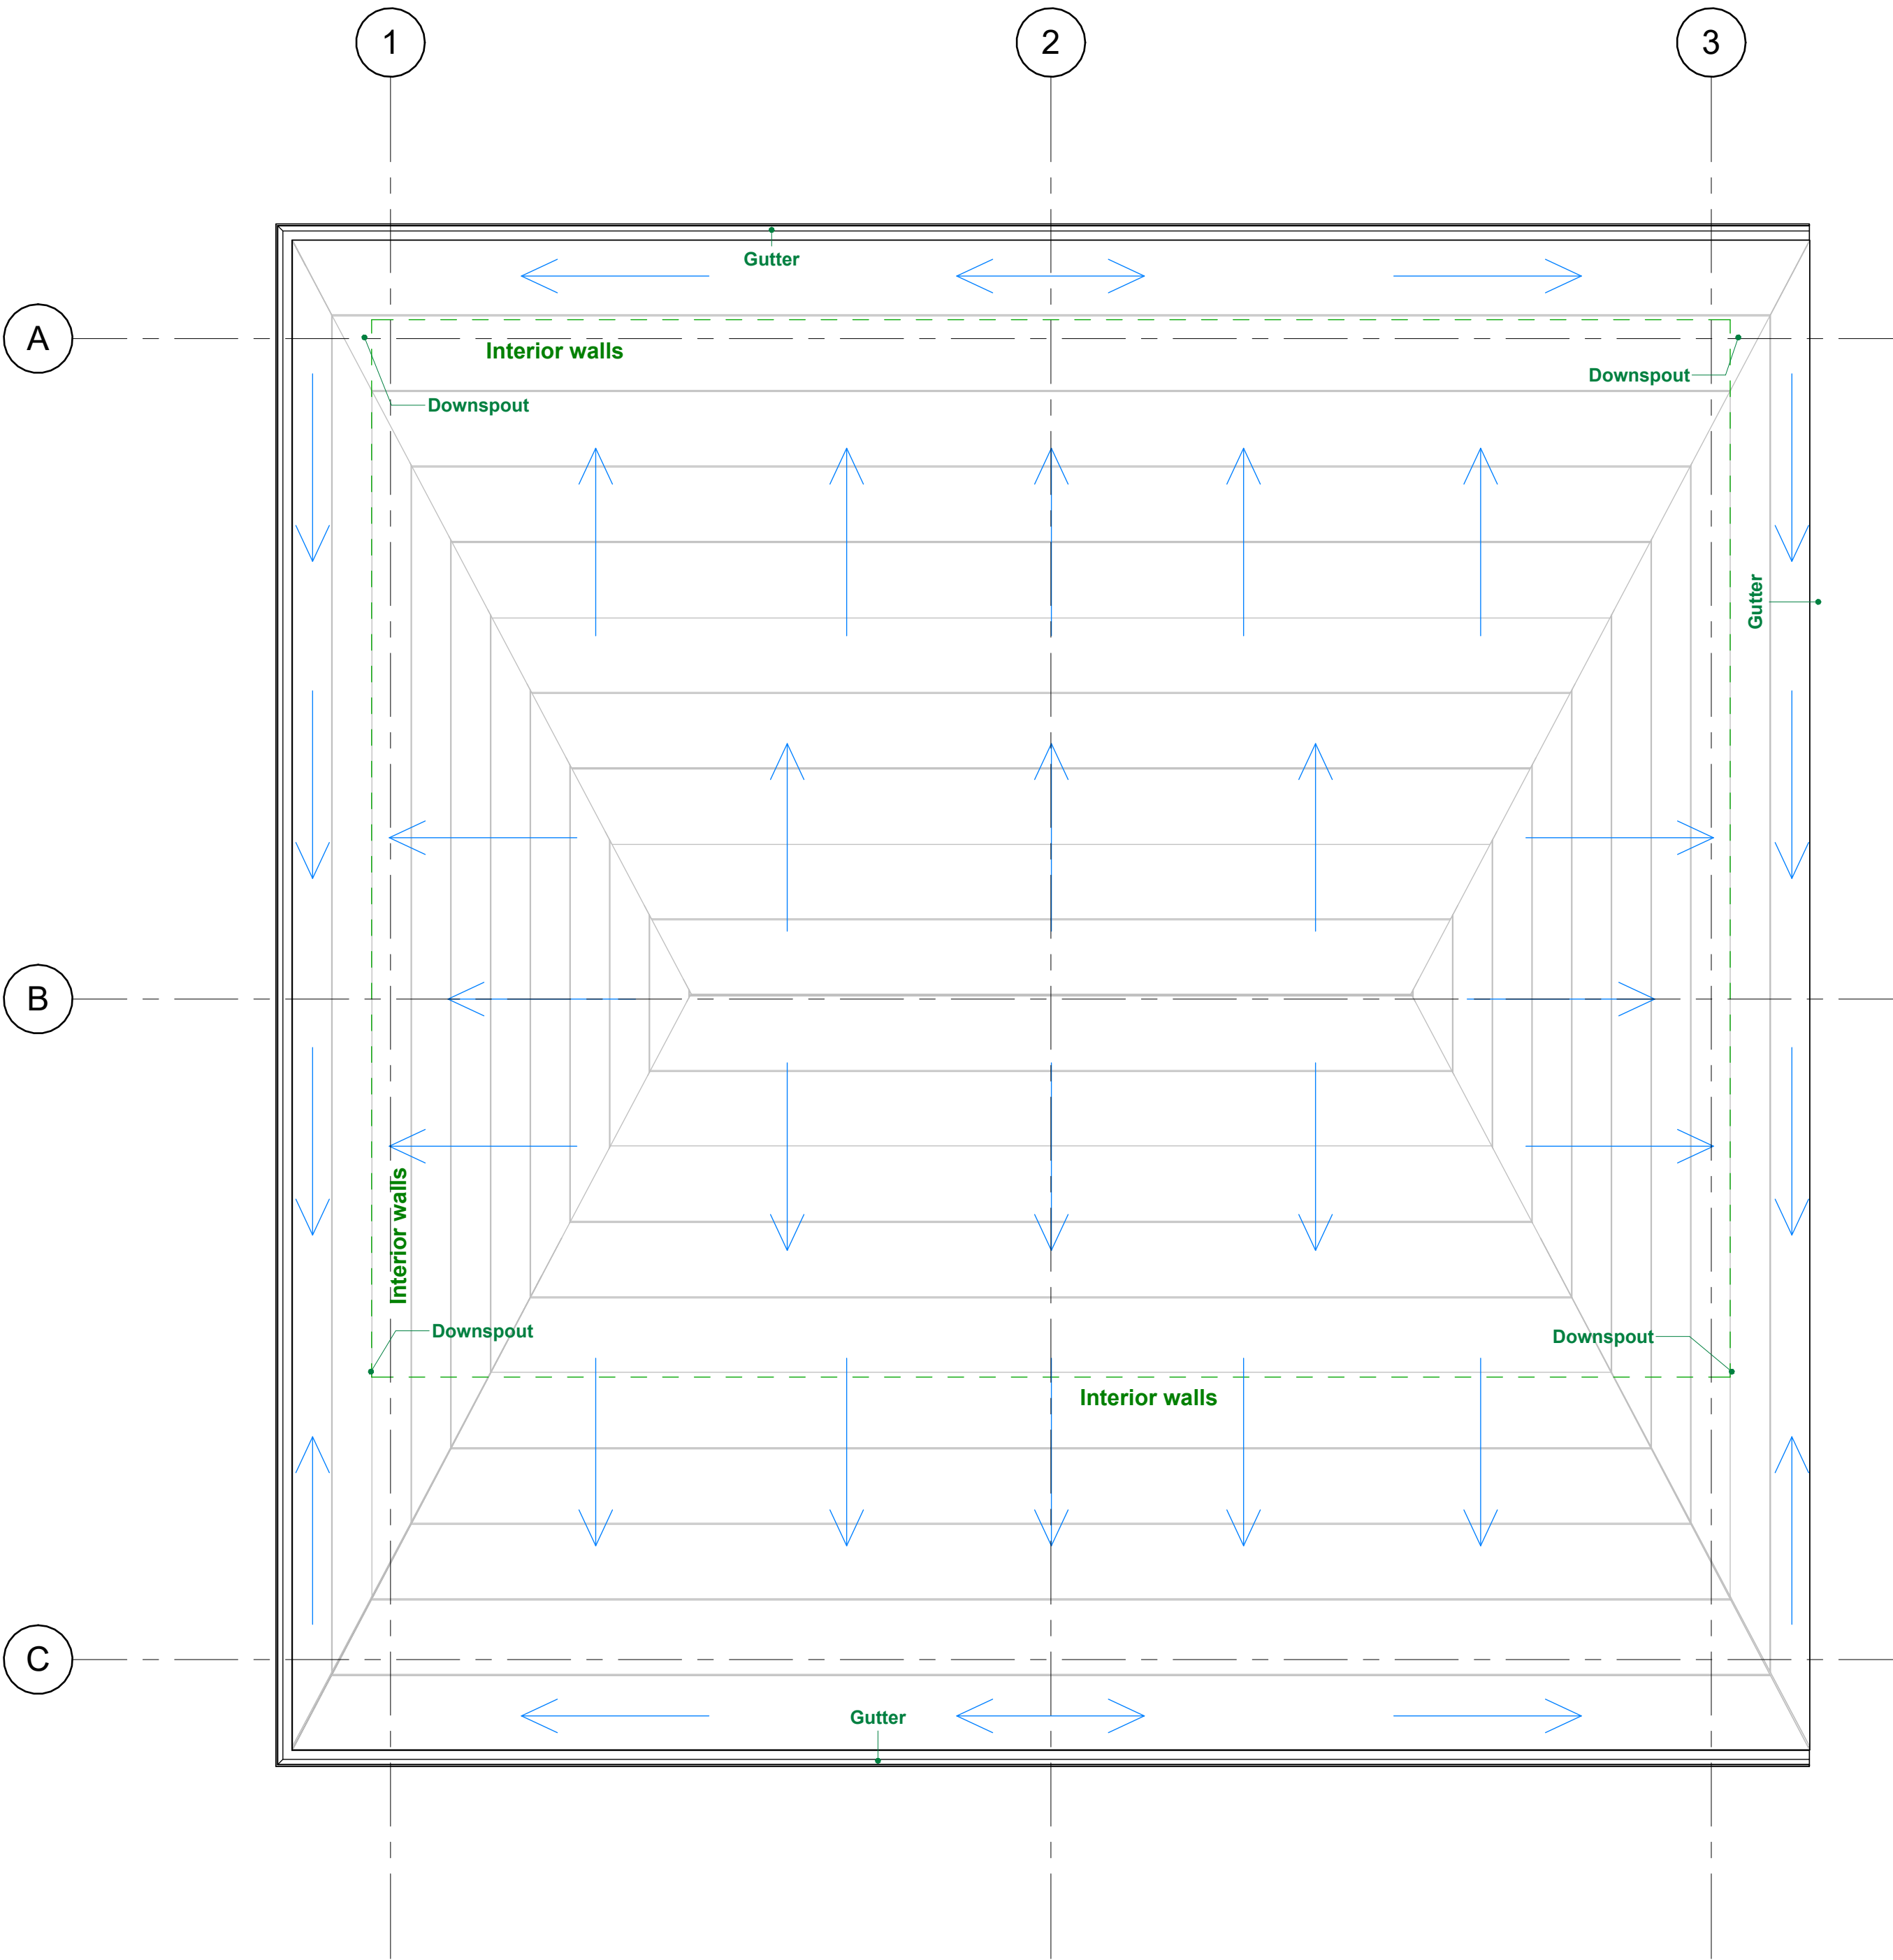

1. THESE DRAWINGS MUST BE CHECKED BY THE CUSTOMER OR CONTRACTOR PRIOR TO APPROVAL. ANY ERRORS OR OMISSIONS MUST BE REPORTED IN WRITING TO BAUHU PRIOR TO COMMENCEMENT OF CONSTRUCTION.
2. ARCHITECTURAL DRAWINGS SHOULD BE READ IN CONJUNCTION WITH STRUCTURAL DETAILING AND FABRICATION GENERAL ASSEMBLY DRAWINGS.
3. FOR CONSTRUCTION PURPOSES, USE ONLY THE LATEST APPROVED DRAWINGS LABELED 'ISSUED FOR CONSTRUCTION'.
4. DO NOT SCALE FROM THIS DRAWING.
5. THE COMPANY OPERATES USING METRIC DIMENSIONS AS THE PRINCIPAL DENOMINATION.
6. ALL CONCRETE WORKS ARE OUTSIDE OF THE SCOPE OF THE COMPANY. INFORMATION REGARDING SLAB DESIGN AND CONNECTIONS IN THESE DRAWINGS ARE INTENDED FOR GUIDENCE ONLY. FOUNDATION AND SLAB WORKS SHOULD BE DESIGNED AND APPROVED BY A LOCAL STRUCTURAL ENGINEER.
7. THE COMPANY RETAINS FULL TITLE AND OWNERSHIP OF THESE PLANS AND DESIGNS. ANY UNAUTHORISED USE, REPRODUCTION, OR DISTRIBUTION OF THESE PLANS, WHETHER IN WHOLE OR PART, IS EXPRESSLY PROHIBITED WITHOUT PRIOR WRITTEN CONSENT.
8. THE HYBRID STEEL FRAME CONSTRUCTION SYSTEM AND METHODOLOGY (PATENT PENDING) DESCRIBED IN THESE PLANS HAS BEEN DEVELOPED BY THE COMPANY AND IS SUBJECT TO A PROVISIONAL PATENT APPLICATION & ASSIGNMENT - US APPLICATION No. 63/722,841.

No.	Revision	Date
01	Moved walls under roof joists	13.03

ISSUED FOR:

Issued for information

Issued for client approval

Issued for fabrication

Issued for construction

Bahama Beach

DRAWING TITLE:
Rain water drainage plan


DRAWN BY:
Mladin Monica-Mihaela

SCALE:
1 : 40


DRAWING NO:
A40

DATE:
17/03/2025


LGS CONNECTIONS

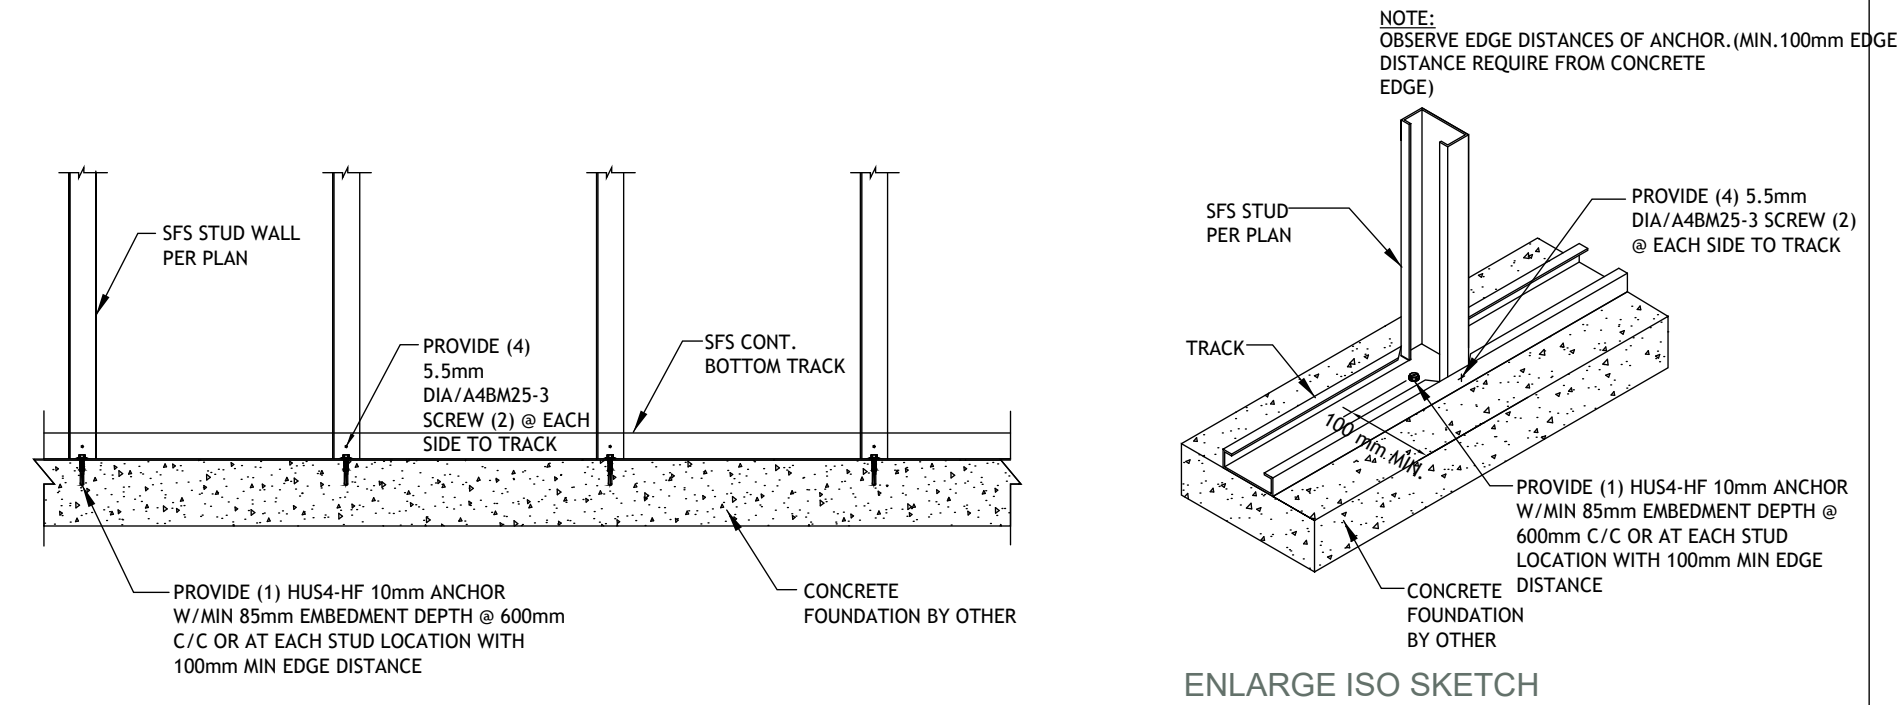


Typical Detail : SFS Bottom Track to Concrete Connection (External Wall)

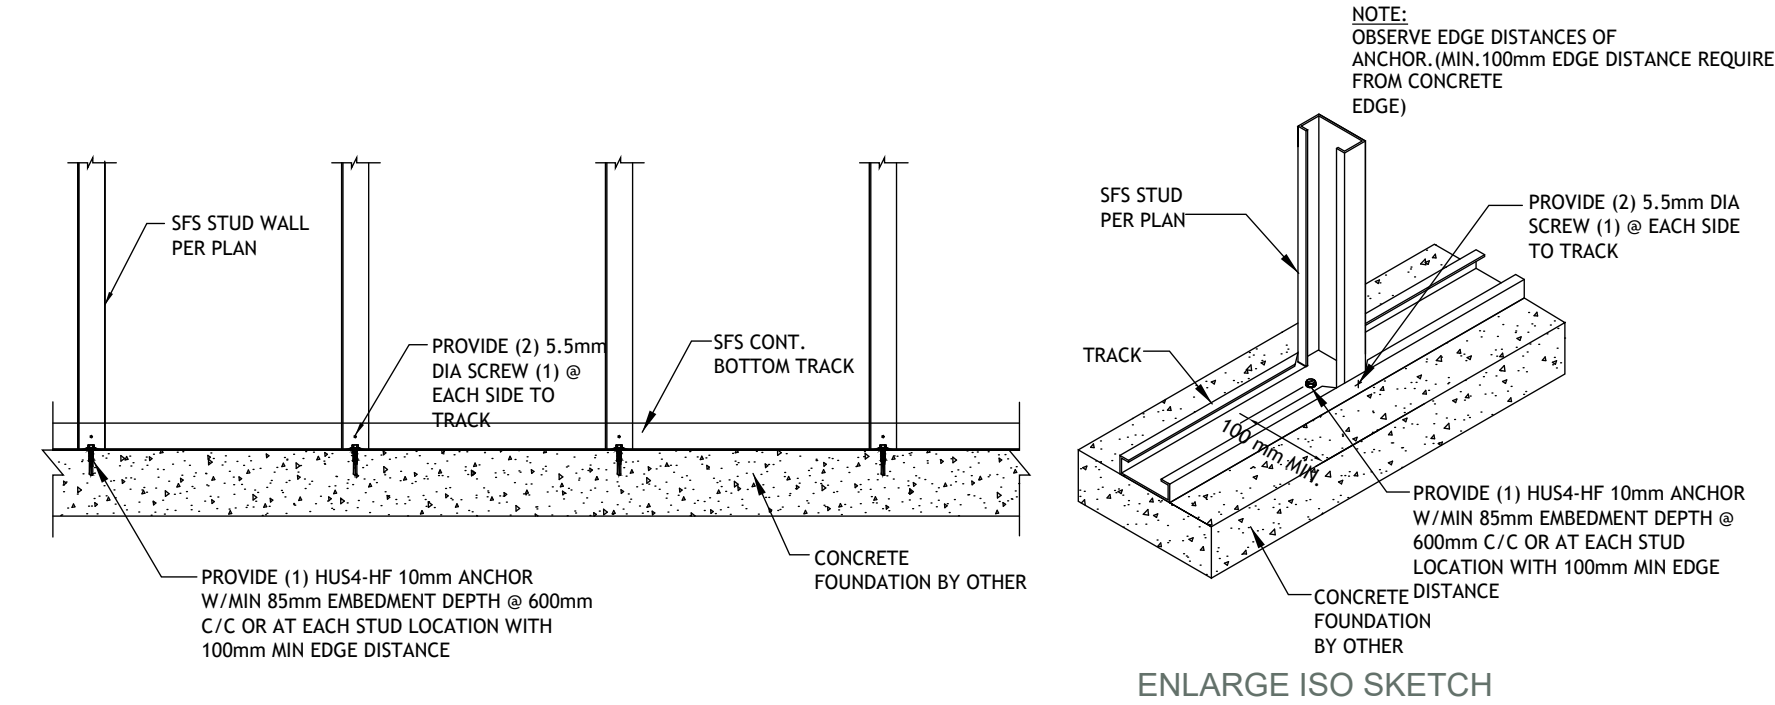


Typical Detail : Bottom Track to Concrete Connection (Internal Wall)

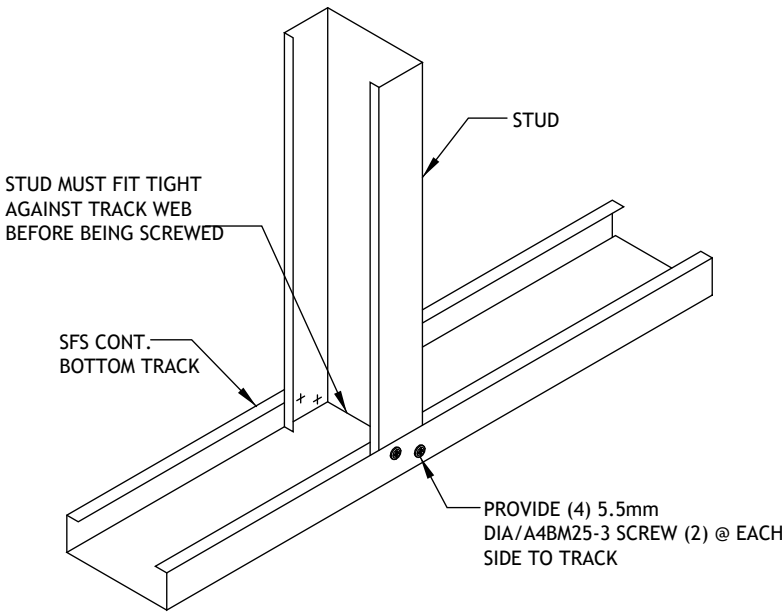


Stud to Bottom Track Connection (External Wall)

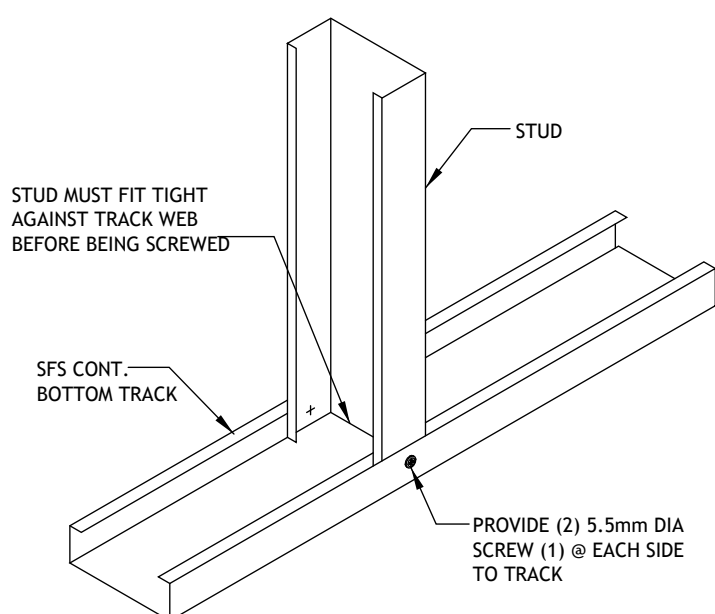


Stud to Bottom Track Connection (Internal Wall)

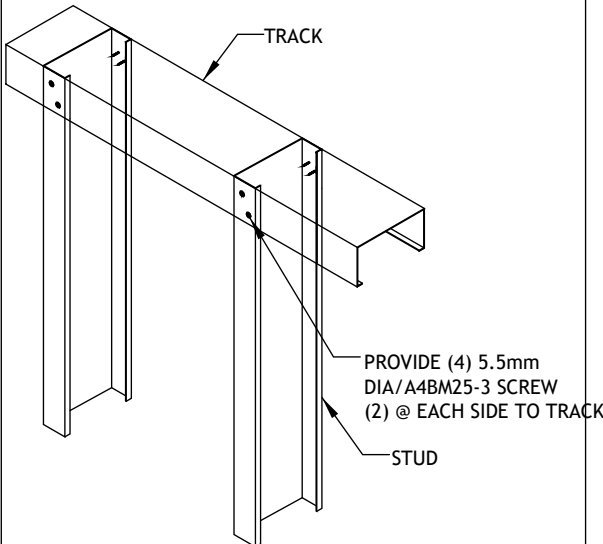


Stud to Top Track Connection (External Wall)

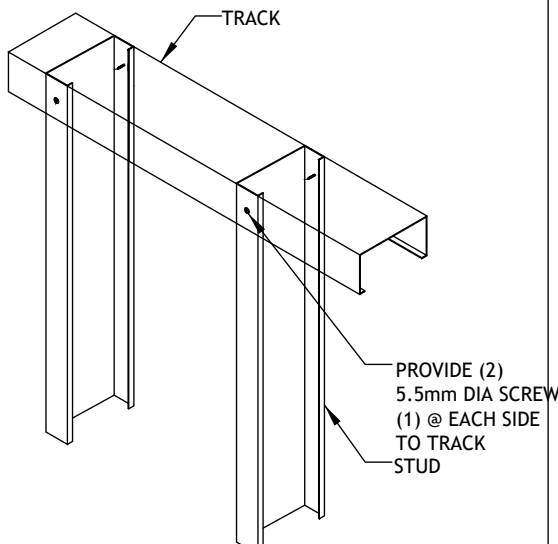


Stud to Top Track Connection (Internal Wall)

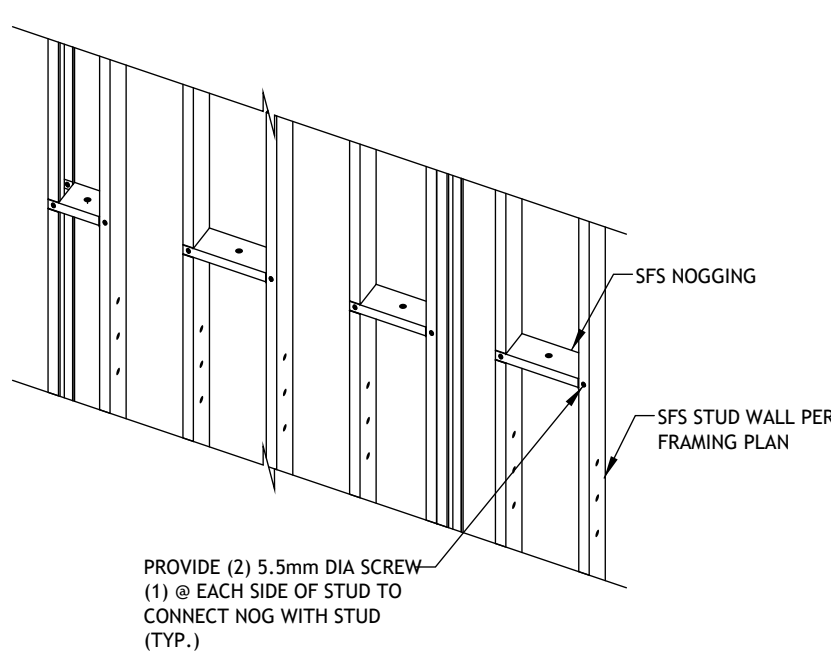


Hit and Miss Nogging to Stud Connection Detail

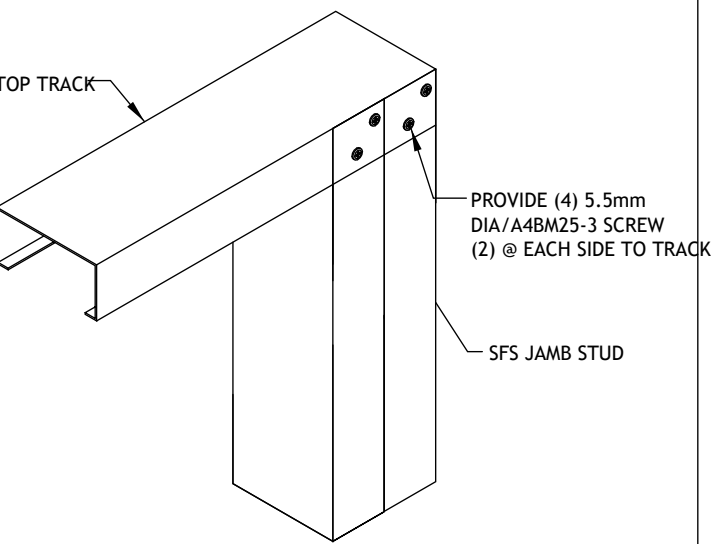


Box Jamb to Top Track Connection

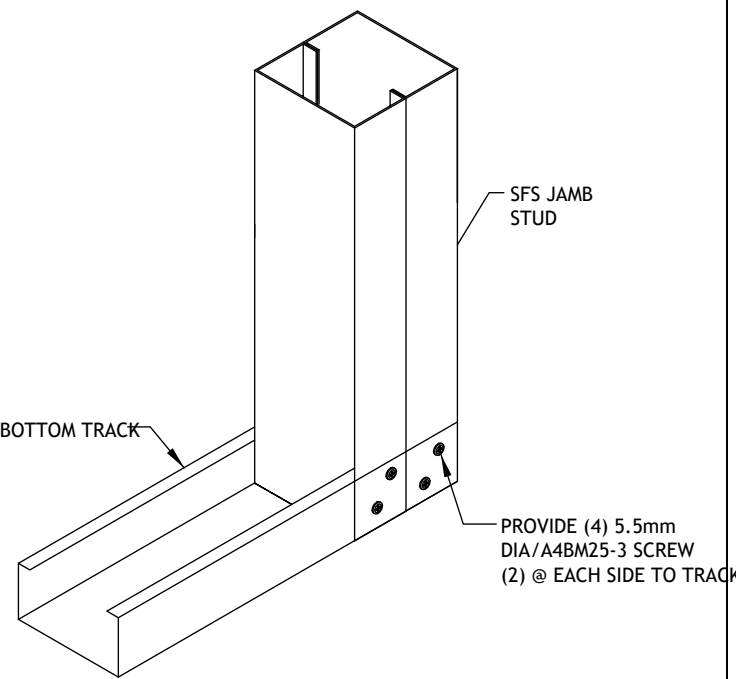


Box Jamb to Bottom Track Connection

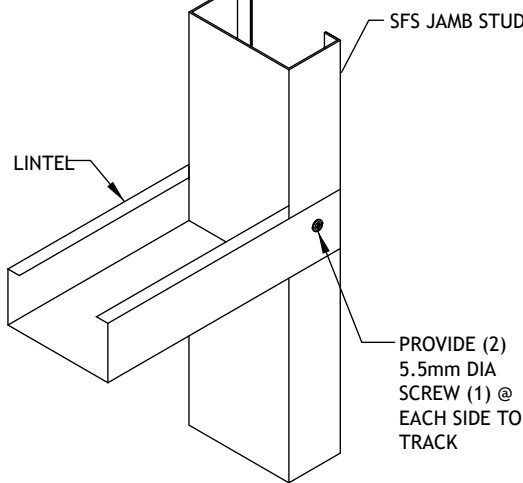


Lintel to Jamb Stud Connection

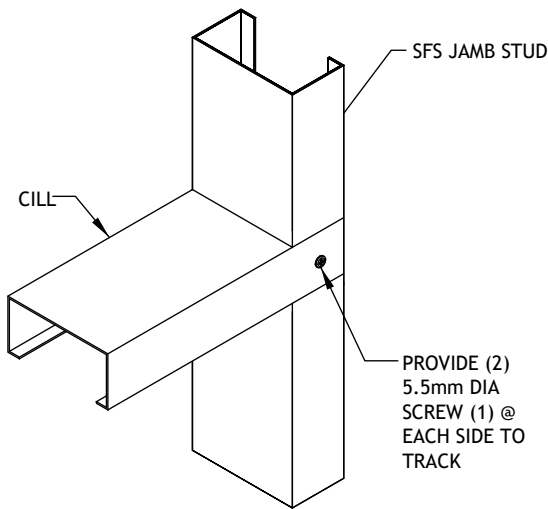

Typ. Cill to Jamb Stud Connection

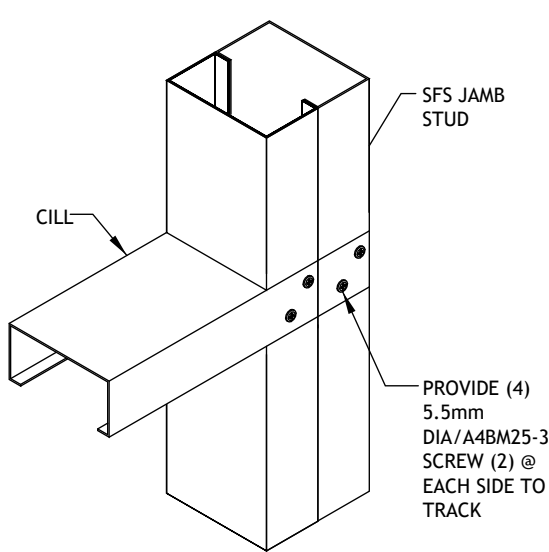

Typ. Cill to Jamb Stud Connection

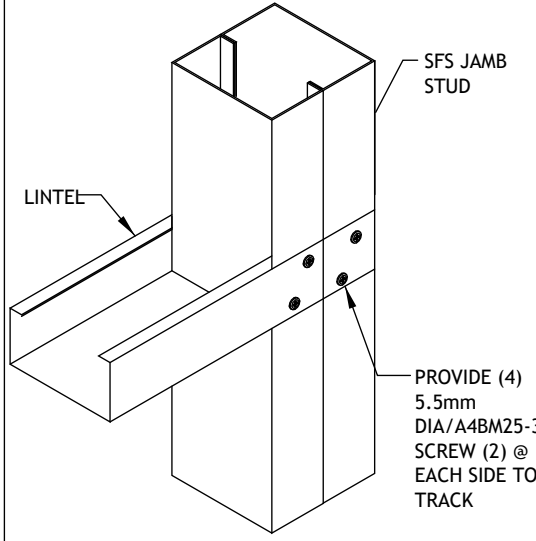

Lintel to Jamb Stud Connection

1. THESE DRAWINGS MUST BE CHECKED BY THE CUSTOMER OR CONTRACTOR PRIOR TO APPROVAL. ANY ERRORS OR OMISSIONS MUST BE REPORTED IN WRITING TO BAUHU PRIOR TO COMMENCEMENT OF CONSTRUCTION.
2. ARCHITECTURAL DRAWINGS SHOULD BE READ IN CONJUNCTION WITH STRUCTURAL DETAILING AND FABRICATION GENERAL ASSEMBLY DRAWINGS.
3. FOR CONSTRUCTION PURPOSES, USE ONLY THE LATEST APPROVED DRAWINGS LABELED 'ISSUED FOR CONSTRUCTION'.
4. DO NOT SCALE FROM THIS DRAWING.
5. THE COMPANY OPERATES USING METRIC DIMENSIONS AS THE PRINCIPAL DENOMINATION.
6. ALL CONCRETE WORKS ARE OUTSIDE OF THE SCOPE OF THE COMPANY. INFORMATION REGARDING SLAB DESIGN AND CONNECTIONS IN THESE DRAWINGS ARE INTENDED FOR GUIDENCE ONLY. FOUNDATION AND SLAB WORKS SHOULD BE DESIGNED AND APPROVED BY A LOCAL STRUCTURAL ENGINEER.
7. THE COMPANY RETAINS FULL TITLE AND OWNERSHIP OF THESE PLANS AND DESIGNS. ANY UNAUTHORISED USE, REPRODUCTION, OR DISTRIBUTION OF THESE PLANS, WHETHER IN WHOLE OR PART, IS EXPRESSLY PROHIBITED WITHOUT PRIOR WRITTEN CONSENT.
8. THE HYBRID STEEL FRAME CONSTRUCTION SYSTEM AND METHODOLOGY (PATENT PENDING) DESCRIBED IN THESE PLANS HAS BEEN DEVELOPED BY THE COMPANY AND IS SUBJECT TO A PROVISIONAL PATENT APPLICATION & ASSIGNMENT - US APPLICATION No. 63/722,841.

No.	Revision	Date
01	Moved walls under roof joists	13.03

ISSUED FOR:

Issued for information

Issued for client approval
Issued for fabrication
Issued for construction

Bahama Beach

DRAWING TITLE:
LGS Connections 3D


DRAWN BY:
Mladin Monica-Mihaela

SCALE:


DRAWING NO:
A41

DATE:
17/03/2025


Typical Frame Connections 1

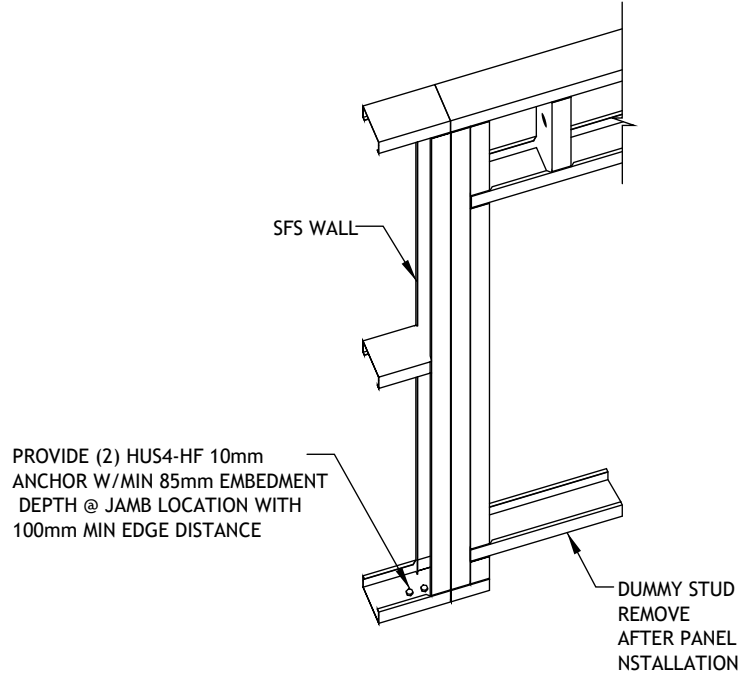


Typical Detail for Two Anchor at Jamb Location

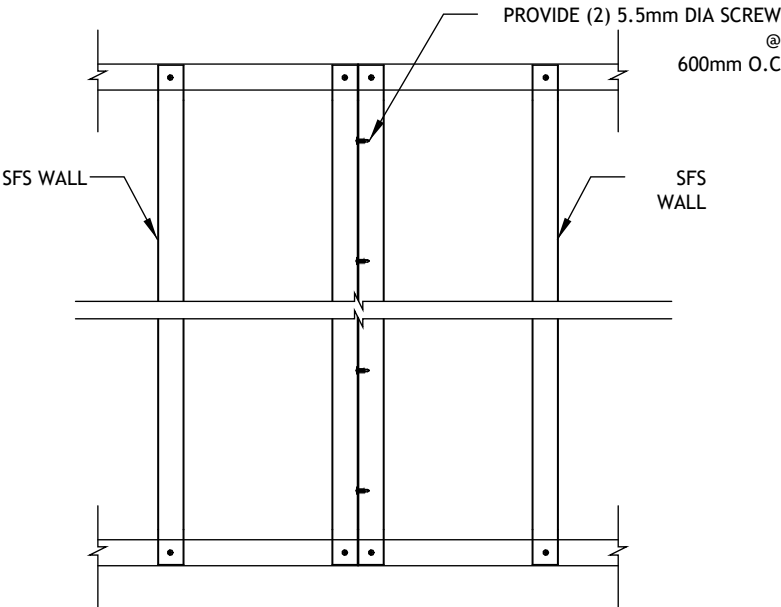


Typical Wall to SFS Wall Connection

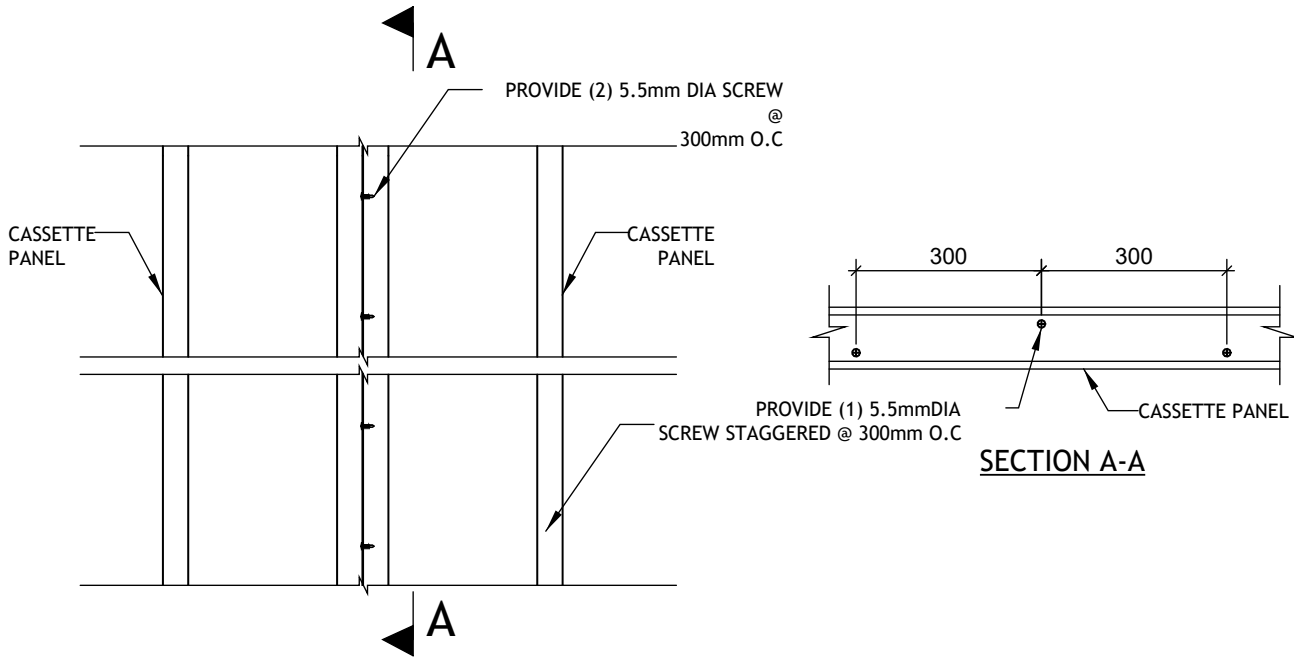


Cassette to Cassette Connection

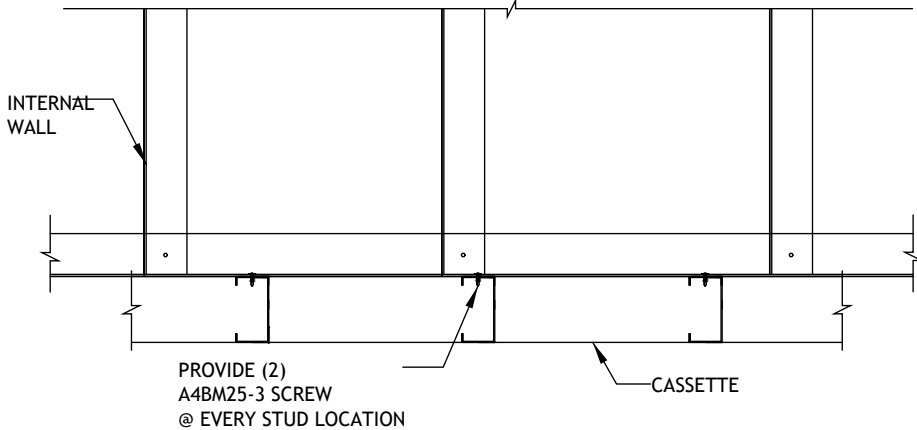


Internal Wall to Cassette Connection at Base

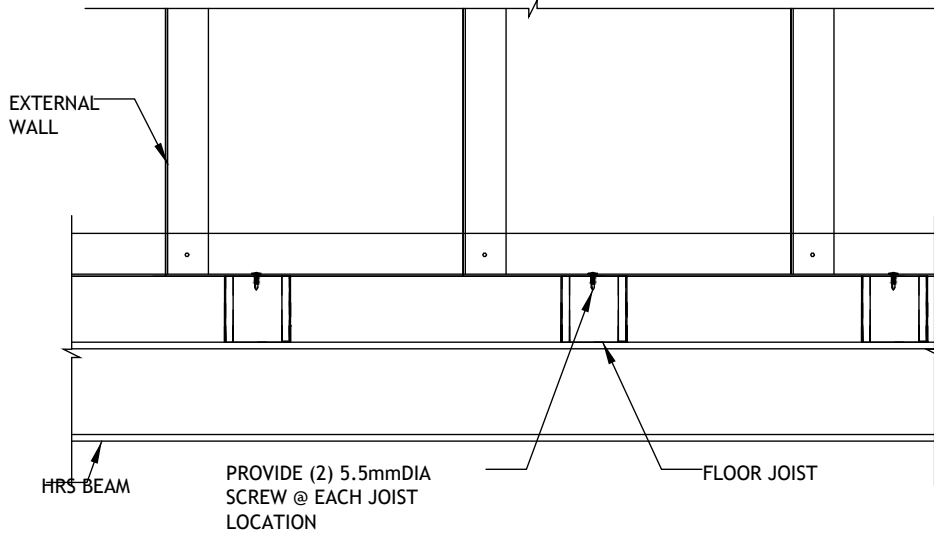


External Wall to Joist Connection at Base

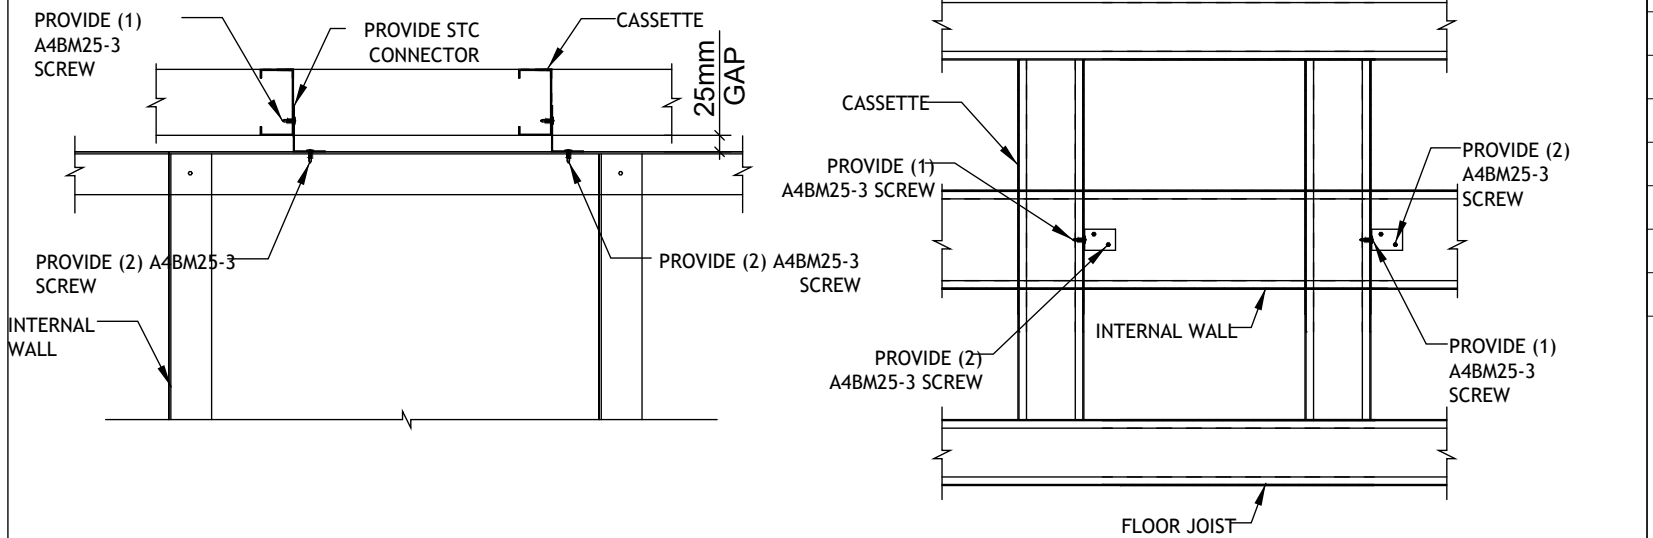


Typ. Internal Wall Connection at Roof Truss at Cassette Location

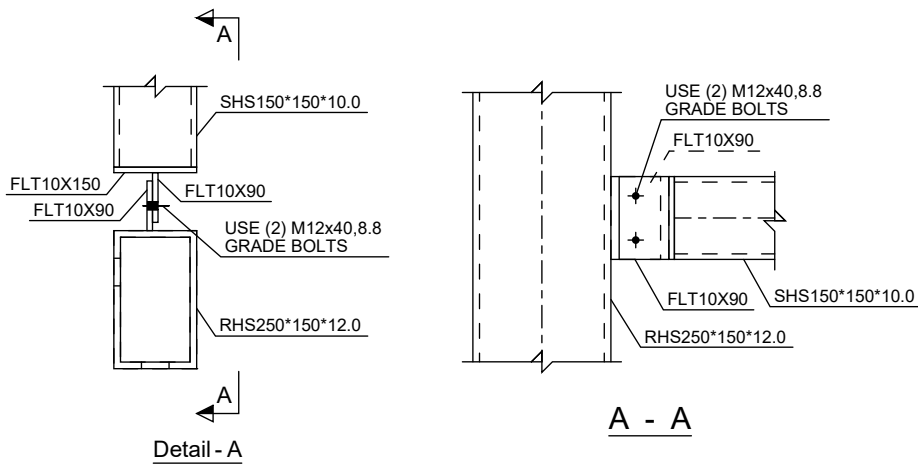

Typ. Fin Plate Connection Detail

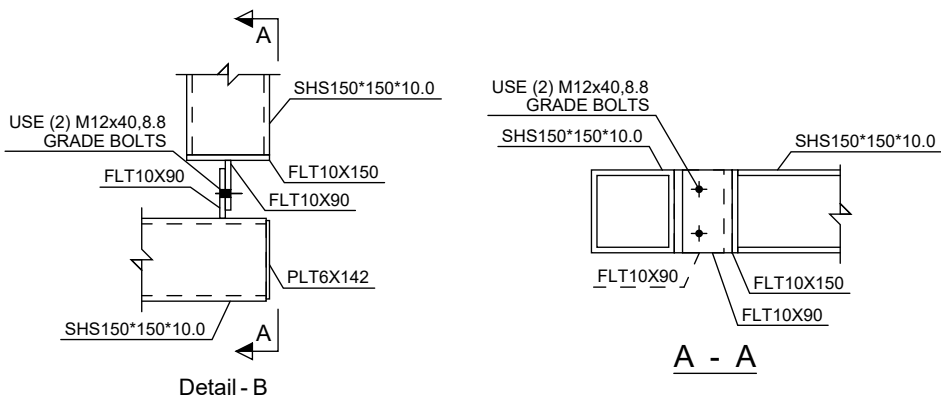

Typ. Fin Plate Connection Detail

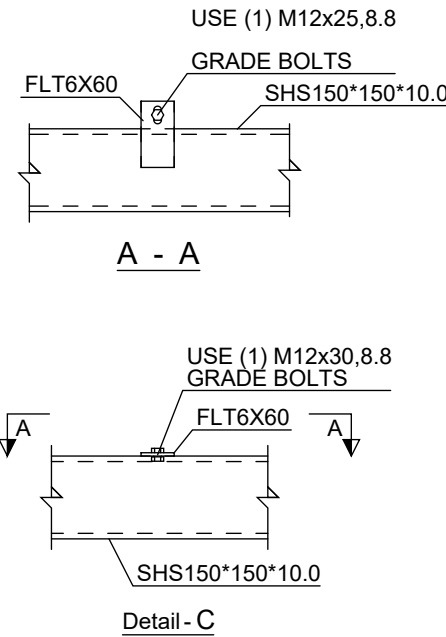

SFS Wall to HRS Beam Connection

1. THESE DRAWINGS MUST BE CHECKED BY THE CUSTOMER OR CONTRACTOR PRIOR TO APPROVAL. ANY ERRORS OR OMISSIONS MUST BE REPORTED IN WRITING TO BAUHU PRIOR TO COMMENCEMENT OF CONSTRUCTION.
2. ARCHITECTURAL DRAWINGS SHOULD BE READ IN CONJUNCTION WITH STRUCTURAL DETAILING AND FABRICATION GENERAL ASSEMBLY DRAWINGS.
3. FOR CONSTRUCTION PURPOSES, USE ONLY THE LATEST APPROVED DRAWINGS LABELED 'ISSUED FOR CONSTRUCTION'.
4. DO NOT SCALE FROM THIS DRAWING.
5. THE COMPANY OPERATES USING METRIC DIMENSIONS AS THE PRINCIPAL DENOMINATION.
6. ALL CONCRETE WORKS ARE OUTSIDE OF THE SCOPE OF THE COMPANY. INFORMATION REGARDING SLAB DESIGN AND CONNECTIONS IN THESE DRAWINGS ARE INTENDED FOR GUIDENCE ONLY. FOUNDATION AND SLAB WORKS SHOULD BE DESIGNED AND APPROVED BY A LOCAL STRUCTURAL ENGINEER.
7. THE COMPANY RETAINS FULL TITLE AND OWNERSHIP OF THESE PLANS AND DESIGNS. ANY UNAUTHORISED USE, REPRODUCTION, OR DISTRIBUTION OF THESE PLANS, WHETHER IN WHOLE OR PART, IS EXPRESSLY PROHIBITED WITHOUT PRIOR WRITTEN CONSENT.
8. THE HYBRID STEEL FRAME CONSTRUCTION SYSTEM AND METHODOLOGY (PATENT PENDING) DESCRIBED IN THESE PLANS HAS BEEN DEVELOPED BY THE COMPANY AND IS SUBJECT TO A PROVISIONAL PATENT APPLICATION & ASSIGNMENT - US APPLICATION No. 63/722,841.

No.	Revision	Date
01	Moved walls under roof joists	13.03

ISSUED FOR:

Issued for information

Issued for client approval

Issued for fabrication

Issued for construction

Bahama Beach

DRAWING TITLE:
Typical Frame Connections

DRAWN BY:
Mladin Monica-Mihaela



SCALE:

DRAWING NO:
A42

DATE:
17/03/2025


Typical Frame Connections 2

1. THESE DRAWINGS MUST BE CHECKED BY THE CUSTOMER OR CONTRACTOR PRIOR TO APPROVAL. ANY ERRORS OR OMISSIONS MUST BE REPORTED IN WRITING TO BAUHU PRIOR TO COMMENCEMENT OF CONSTRUCTION.
2. ARCHITECTURAL DRAWINGS SHOULD BE READ IN CONJUNCTION WITH STRUCTURAL DETAILING AND FABRICATION GENERAL ASSEMBLY DRAWINGS.
3. FOR CONSTRUCTION PURPOSES, USE ONLY THE LATEST APPROVED DRAWINGS LABELED 'ISSUED FOR CONSTRUCTION'.
4. DO NOT SCALE FROM THIS DRAWING.
5. THE COMPANY OPERATES USING METRIC DIMENSIONS AS THE PRINCIPAL DENOMINATION.
6. ALL CONCRETE WORKS ARE OUTSIDE OF THE SCOPE OF THE COMPANY. INFORMATION REGARDING SLAB DESIGN AND CONNECTIONS IN THESE DRAWINGS ARE INTENDED FOR GUIDANCE ONLY. FOUNDATION AND SLAB WORKS SHOULD BE DESIGNED AND APPROVED BY A LOCAL STRUCTURAL ENGINEER.
7. THE COMPANY RETAINS FULL TITLE AND OWNERSHIP OF THESE PLANS AND DESIGNS. ANY UNAUTHORISED USE, REPRODUCTION, OR DISTRIBUTION OF THESE PLANS, WHETHER IN WHOLE OR PART, IS EXPRESSLY PROHIBITED WITHOUT PRIOR WRITTEN CONSENT.
8. THE HYBRID STEEL FRAME CONSTRUCTION SYSTEM AND METHODOLOGY (PATENT PENDING) DESCRIBED IN THESE PLANS HAS BEEN DEVELOPED BY THE COMPANY AND IS SUBJECT TO A PROVISIONAL PATENT APPLICATION & ASSIGNMENT - US APPLICATION No. 63/722,841.

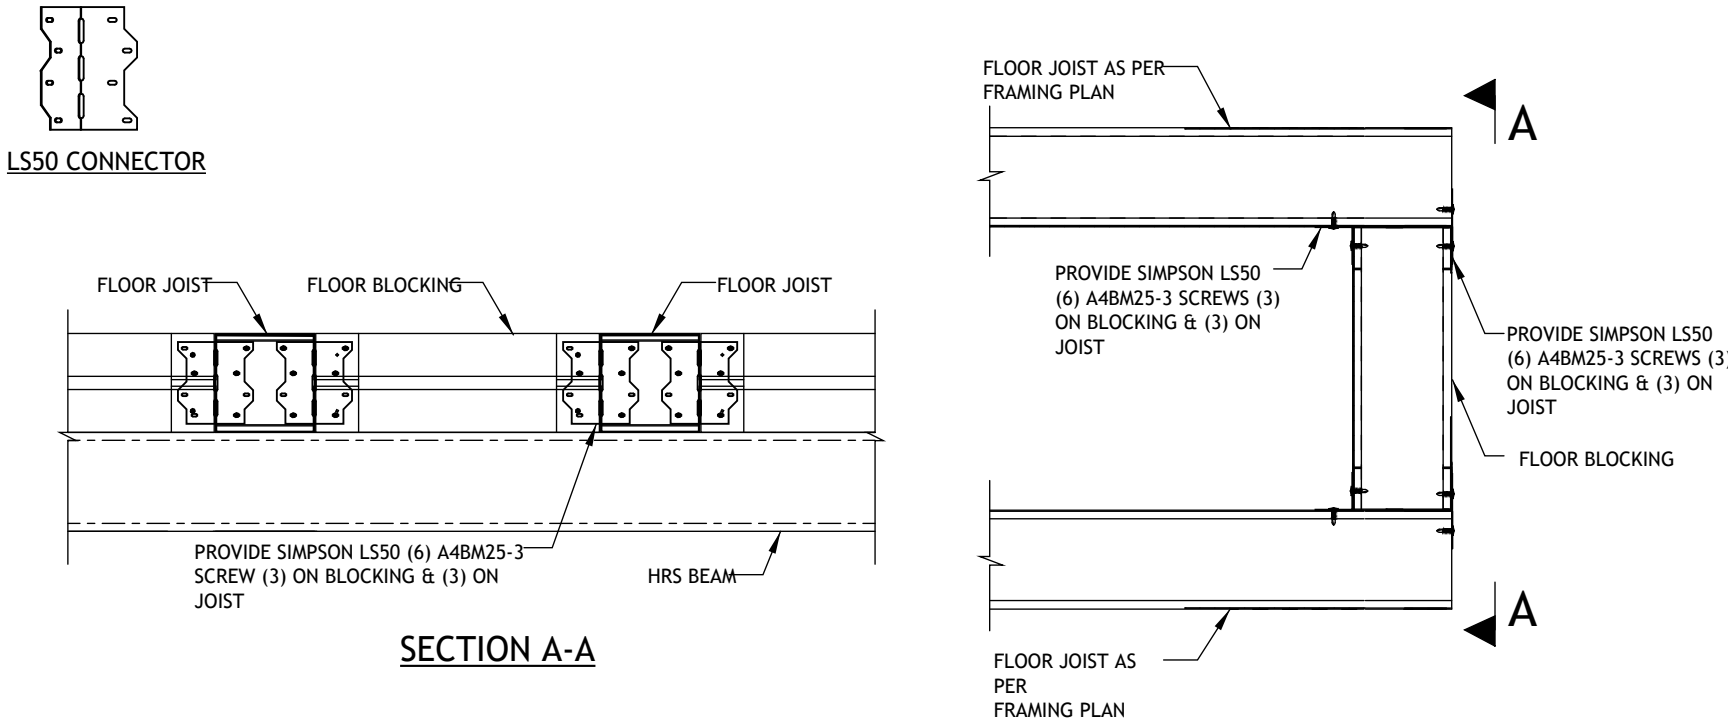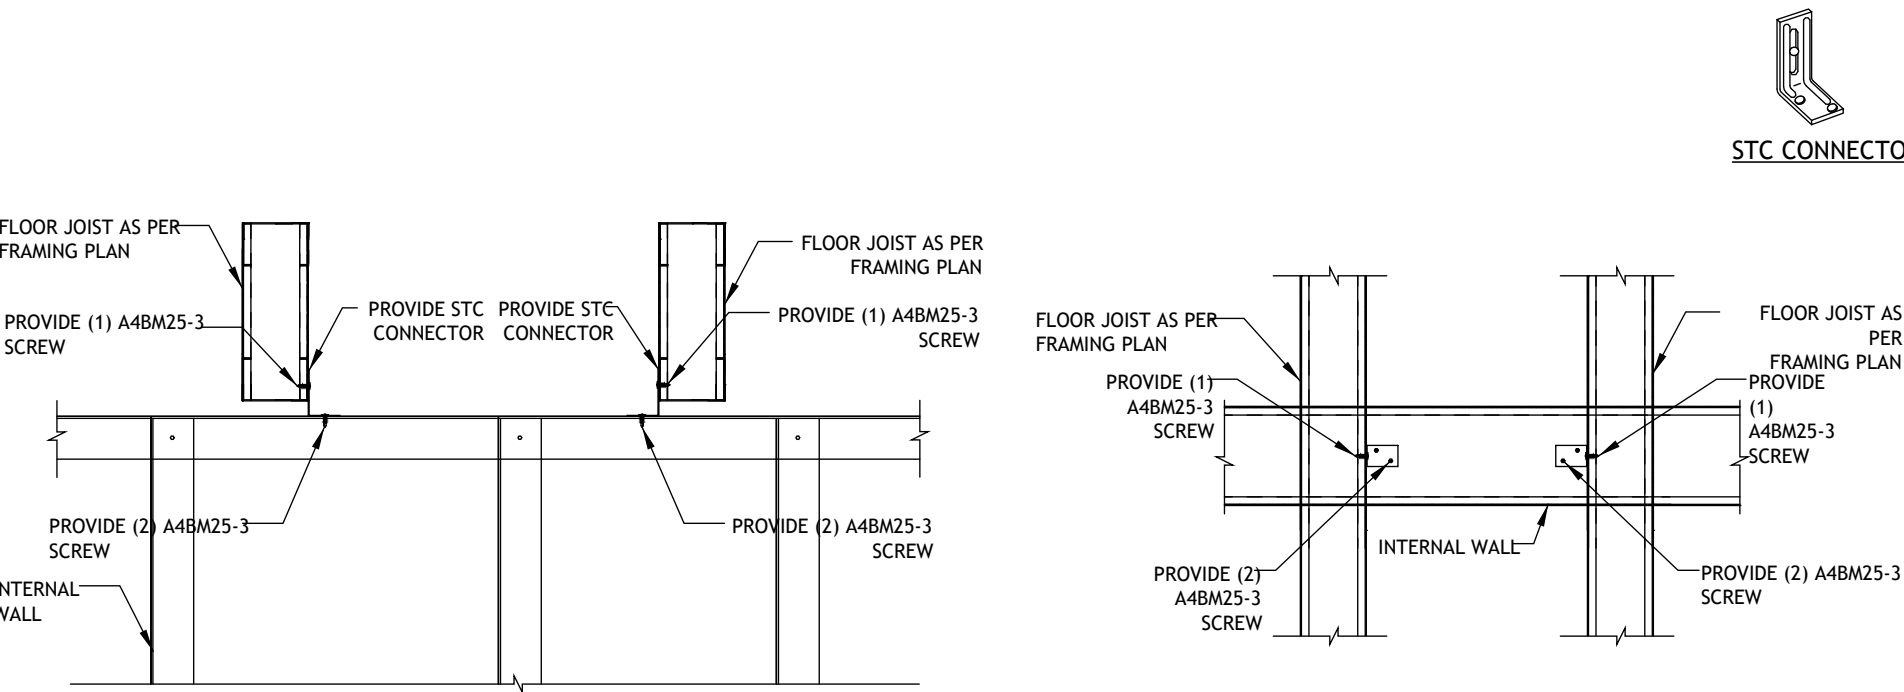


Typical Internal Wall Connection Floor Joist


Floor Blocking to Floor Joist Connection

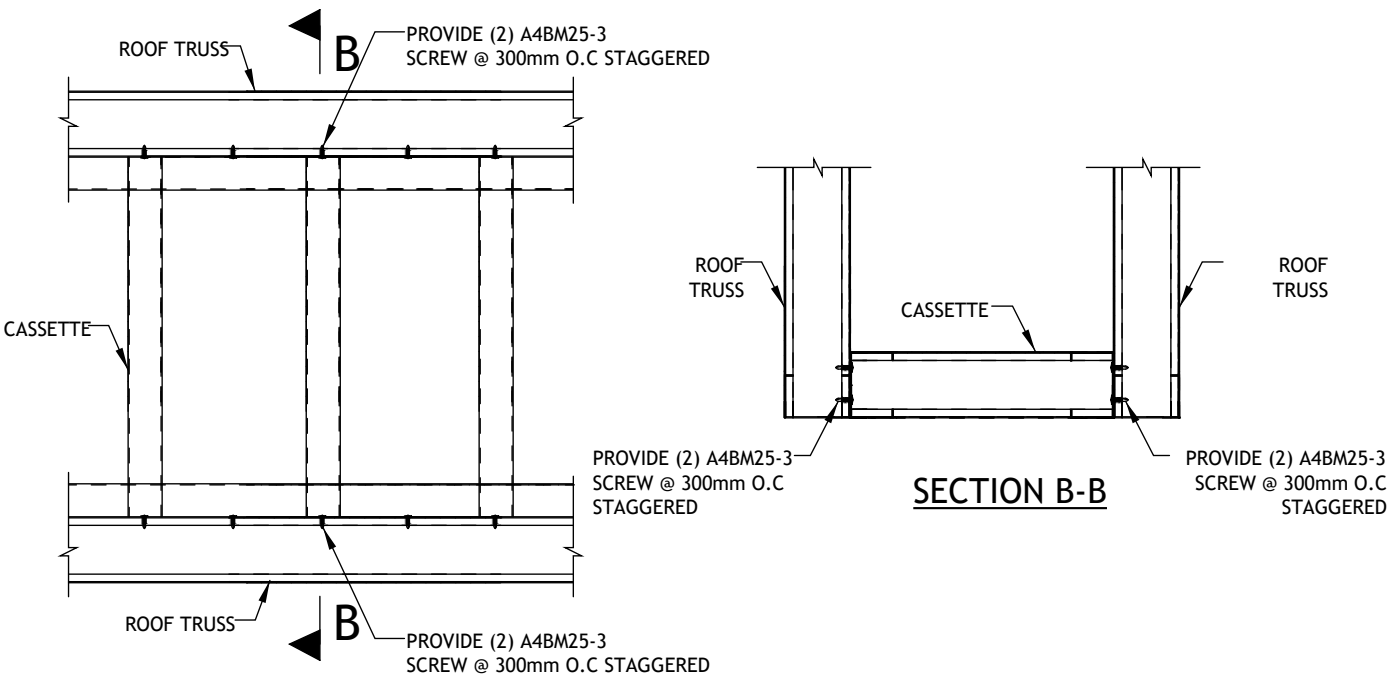


Cassette to Roof Truss Connection

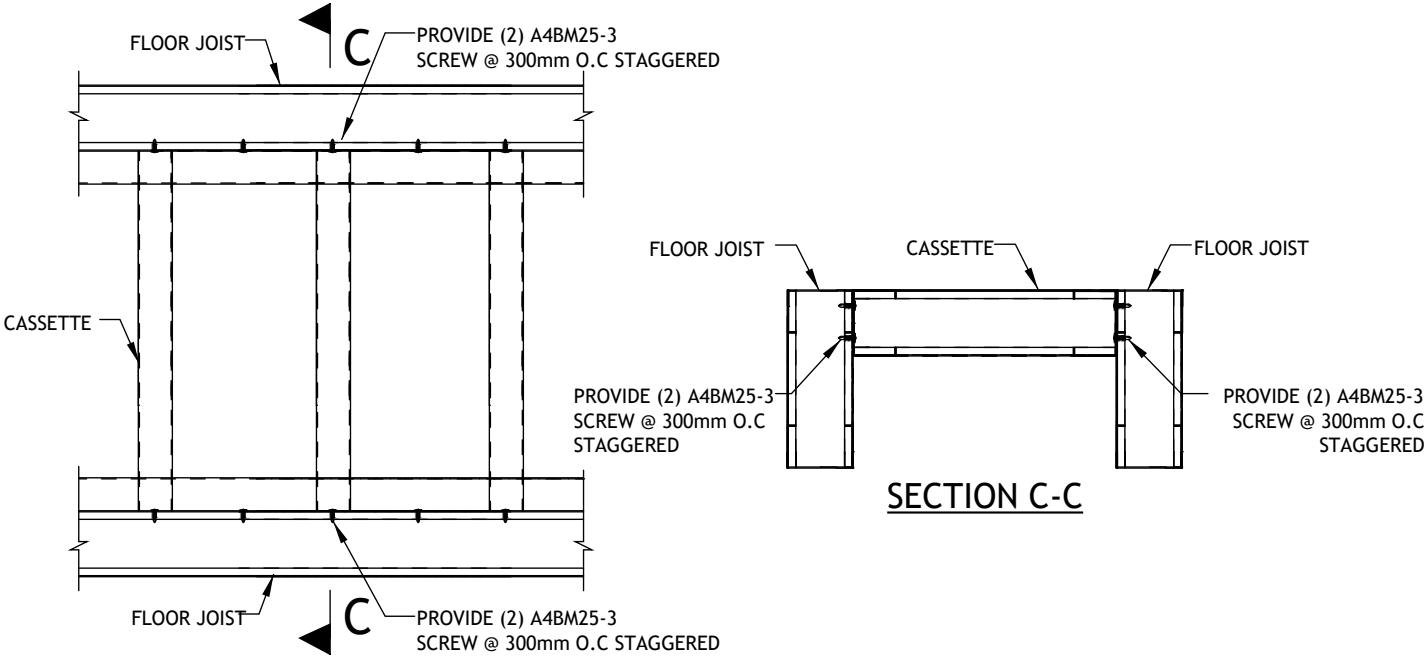

Cassette to Floor Joist Connection

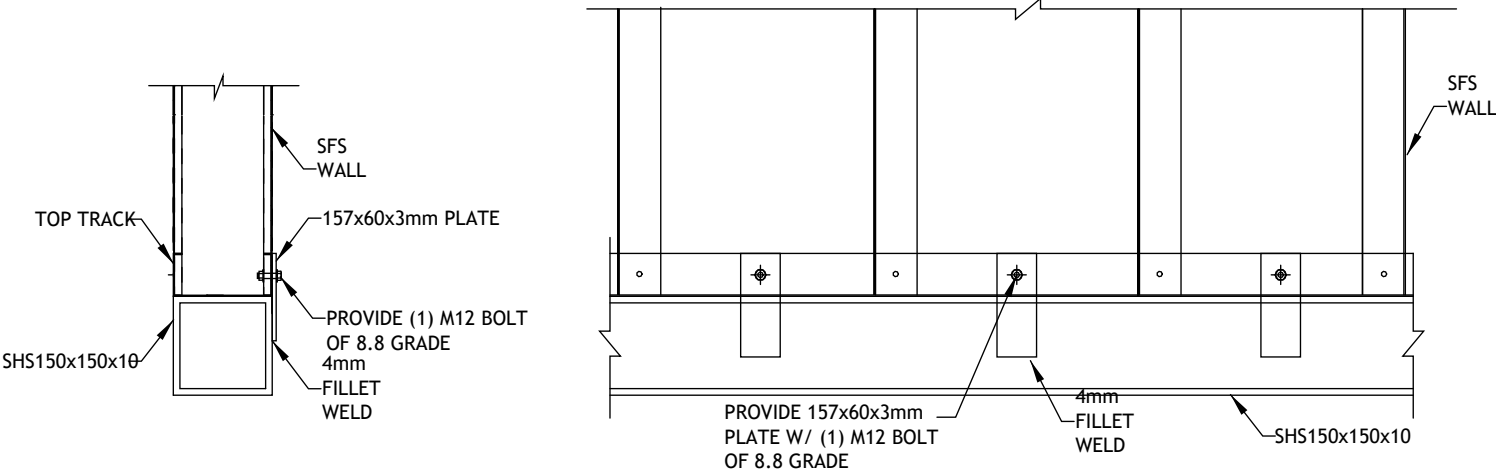

Typical Detail at SFS Bottom Track to HRS Beam Connection (External & Internal Wall)

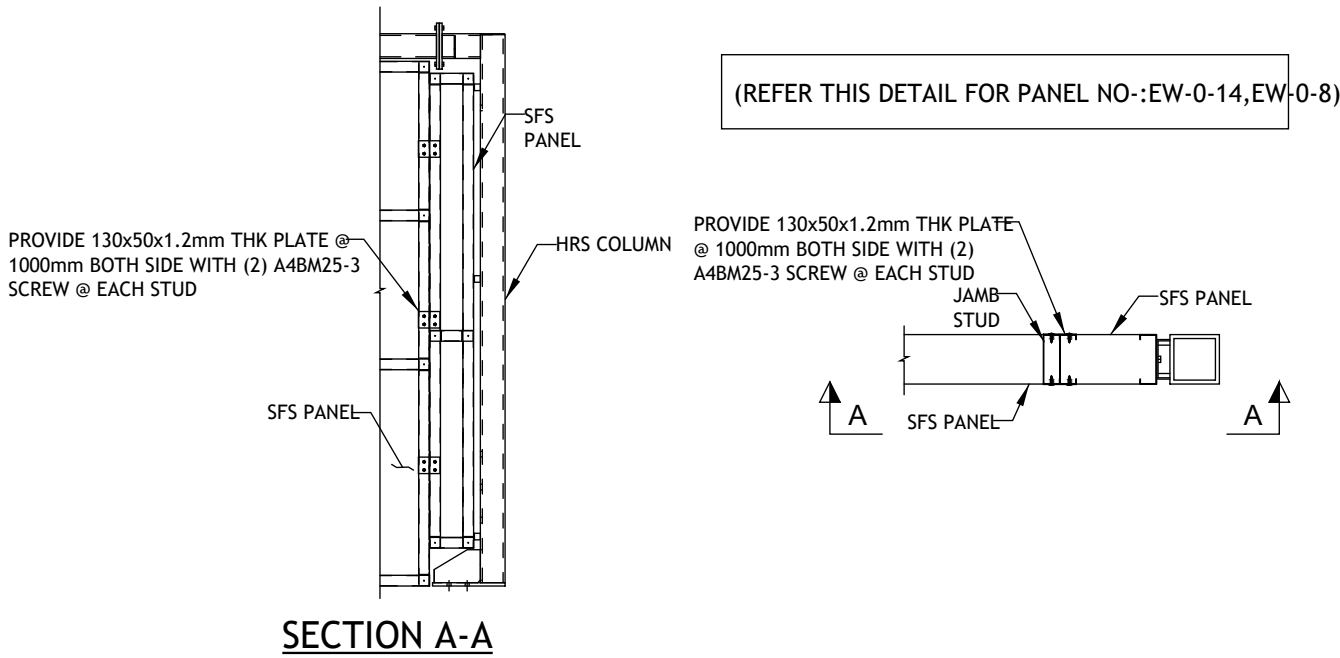

SFS Panel Connection Detail

No.	Revision	Date
01	Moved walls under roof joists	13.03

ISSUED FOR:

Issued for information

Issued for client approval

Issued for fabrication


Issued for construction

Bahama Beach


DRAWING TITLE:	Typical Frame Connections 2
DRAWN BY:	Mladin Monica-Mihaela
SCALE:	
DRAWING NO:	A43
DATE:	17/03/2025

Typical Frame Connections 3


NOTES:
ALL WELDS FOR CONNECTION OF ASSEMBLY TO BE NOTE FROM FABRICATION DRAWING

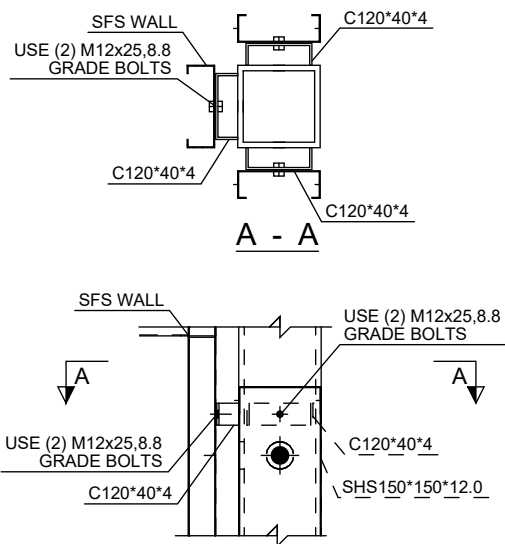


HRS Bracket Detail for Wall Connection

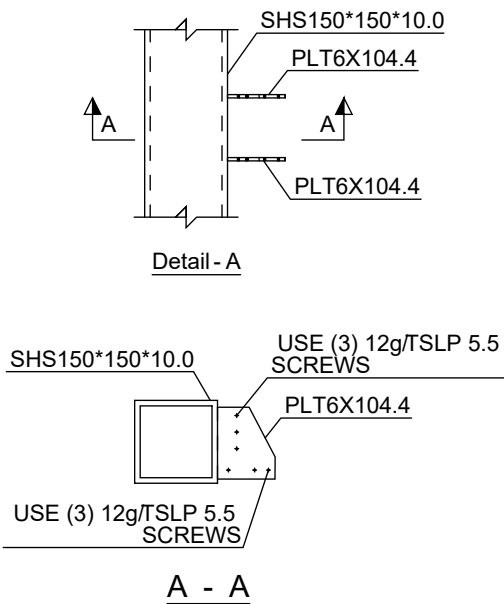


Typ. Truss Outside Plate Connection

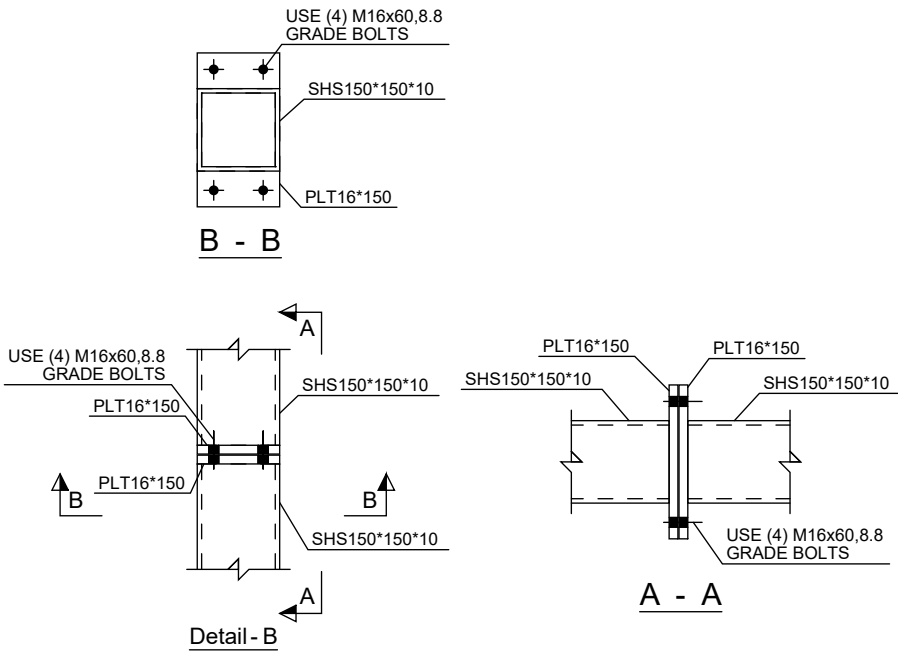


Typ. Vertical Splice Connection

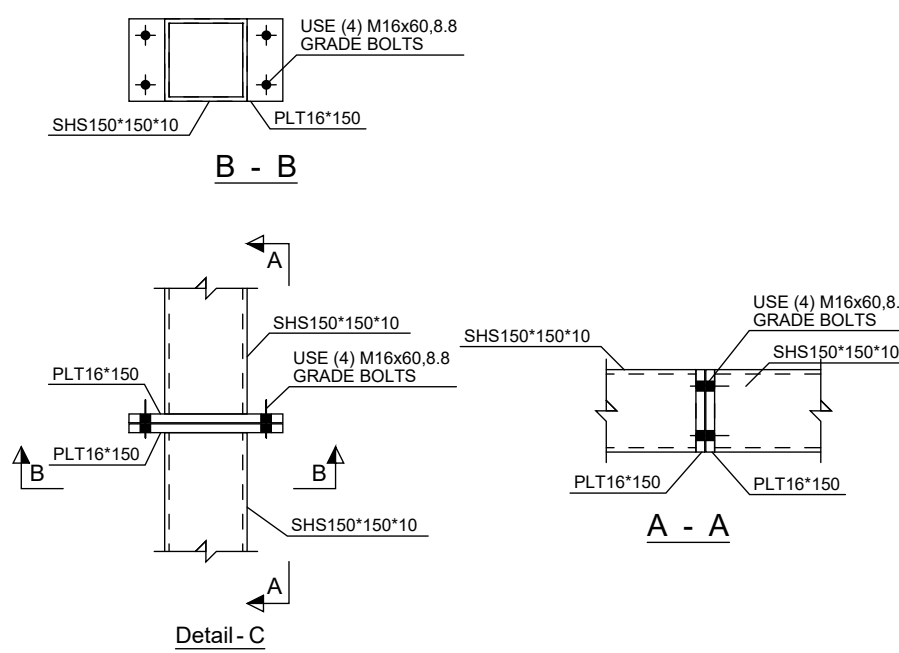


Typ. Horizontal Splice Connection

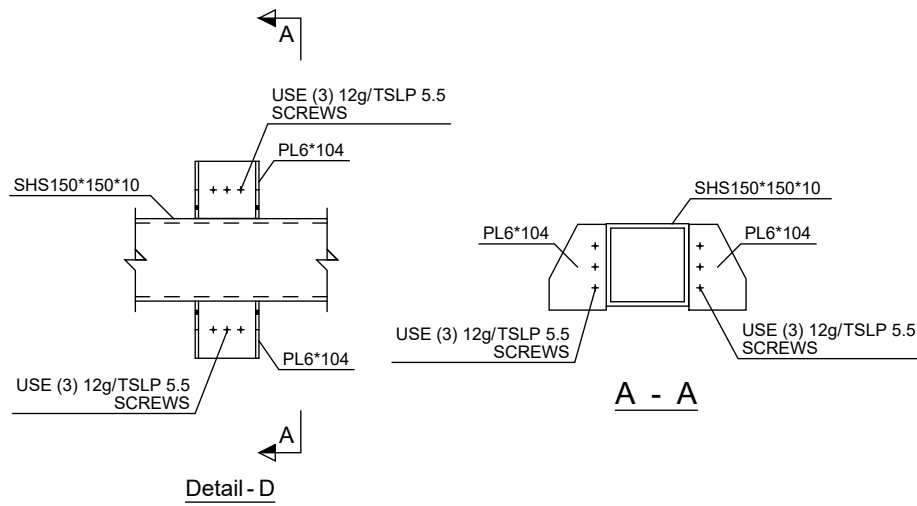


Typ. Truss Bracket Connection

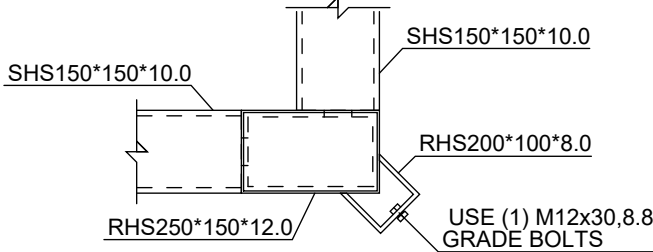


Typ. Corner Truss Connection

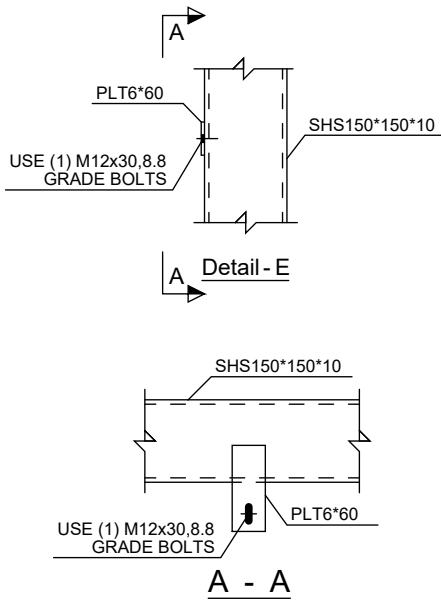


Typ. Wall to Beam Top Plate Connection

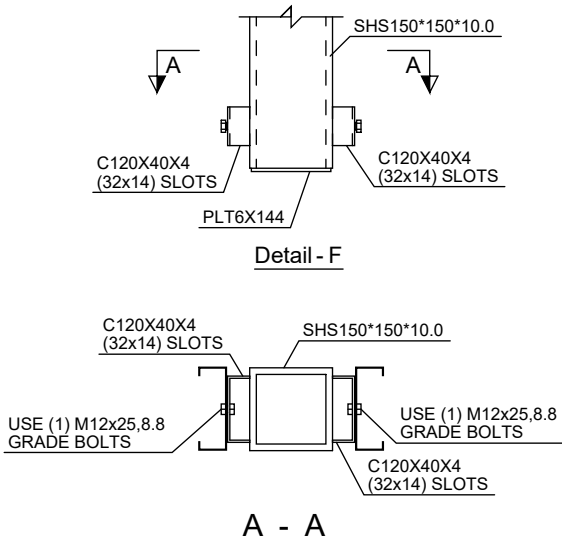


Typ. Lintel to Wind Post Connection

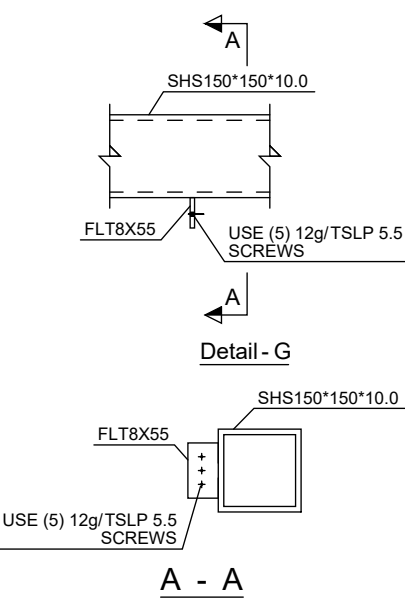


Cassette to Beam Connection

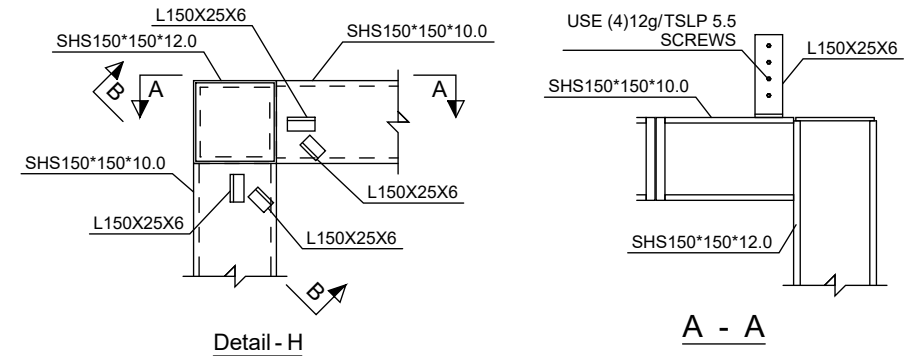

Typ. Beam to Column Connection Using C Bracket

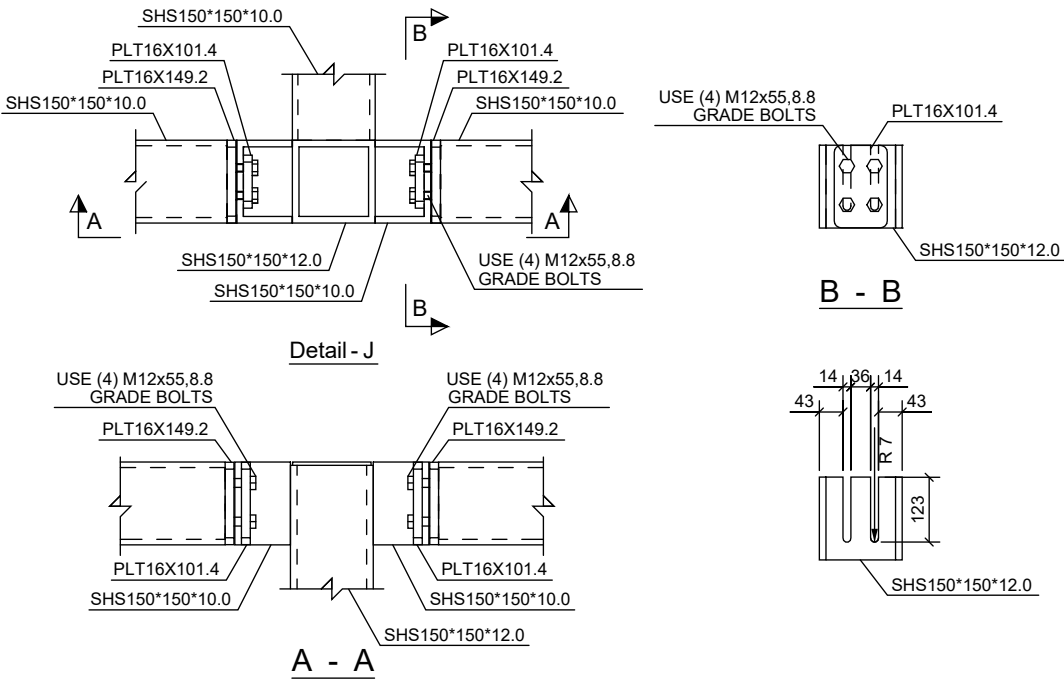

Typ. Beam to Column Connection Using C Bracket

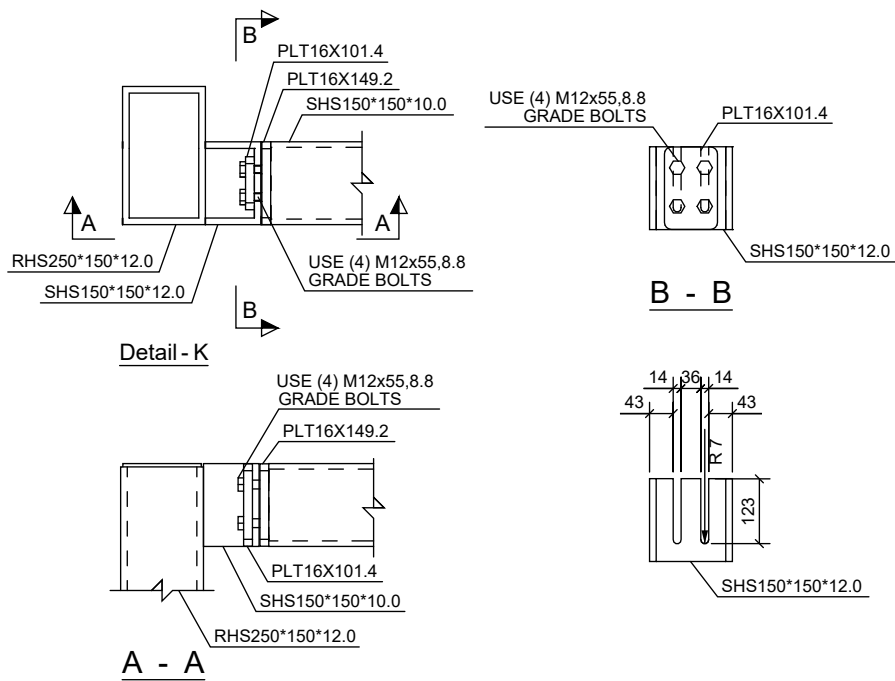

Typ. Beam to Column Connection Using C Bracket

1. THESE DRAWINGS MUST BE CHECKED BY THE CUSTOMER OR CONTRACTOR PRIOR TO APPROVAL. ANY ERRORS OR OMISSIONS MUST BE REPORTED IN WRITING TO BAUHU PRIOR TO COMMENCEMENT OF CONSTRUCTION.
2. ARCHITECTURAL DRAWINGS SHOULD BE READ IN CONJUNCTION WITH STRUCTURAL DETAILING AND FABRICATION GENERAL ASSEMBLY DRAWINGS.
3. FOR CONSTRUCTION PURPOSES, USE ONLY THE LATEST APPROVED DRAWINGS LABELED 'ISSUED FOR CONSTRUCTION'.
4. DO NOT SCALE FROM THIS DRAWING.
5. THE COMPANY OPERATES USING METRIC DIMENSIONS AS THE PRINCIPAL DENOMINATION.
6. ALL CONCRETE WORKS ARE OUTSIDE OF THE SCOPE OF THE COMPANY. INFORMATION REGARDING SLAB DESIGN AND CONNECTIONS IN THESE DRAWINGS ARE INTENDED FOR GUIDANCE ONLY. FOUNDATION AND SLAB WORKS SHOULD BE DESIGNED AND APPROVED BY A LOCAL STRUCTURAL ENGINEER.
7. THE COMPANY RETAINS FULL TITLE AND OWNERSHIP OF THESE PLANS AND DESIGNS. ANY UNAUTHORISED USE, REPRODUCTION, OR DISTRIBUTION OF THESE PLANS, WHETHER IN WHOLE OR PART, IS EXPRESSLY PROHIBITED WITHOUT PRIOR WRITTEN CONSENT.
8. THE HYBRID STEEL FRAME CONSTRUCTION SYSTEM AND METHODOLOGY (PATENT PENDING) DESCRIBED IN THESE PLANS HAS BEEN DEVELOPED BY THE COMPANY AND IS SUBJECT TO A PROVISIONAL PATENT APPLICATION & ASSIGNMENT - US APPLICATION No. 63/722,841.

No.	Revision	Date
01	Moved walls under roof joists	13.03

ISSUED FOR:

Issued for information

Issued for client approval

Issued for fabrication

Issued for construction

Bahama Beach

DRAWING TITLE:
Typical Frame Connections 3

DRAWN BY:
Mladin Monica-Mihaela


SCALE:

DRAWING NO:
A44

DATE:
17/03/2025


Typical Frame Connections 4

Hold Down Detail

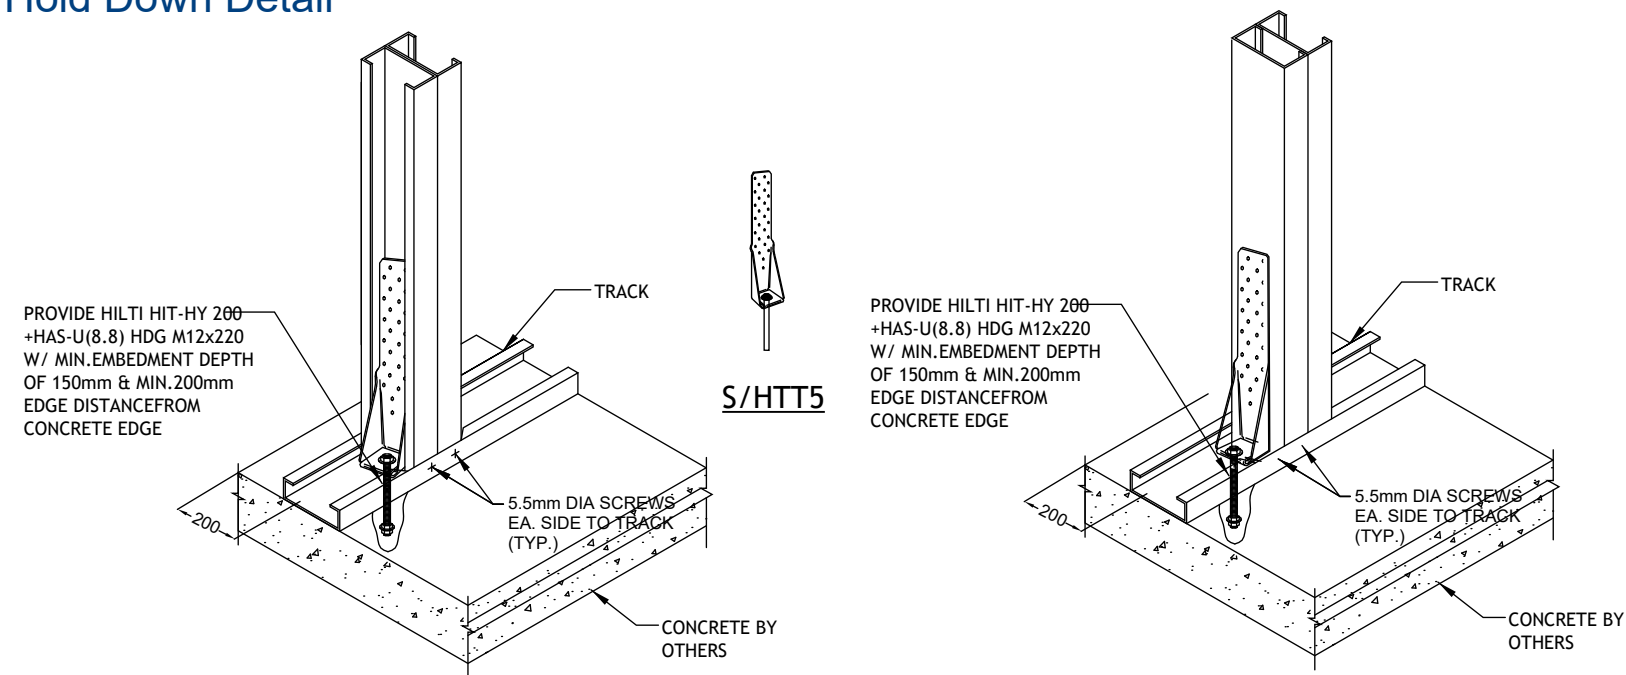

- NOTE -
- 1. ANCHOR & SCREWS SPECIFICATION AS PER SPECIFIED ON STRUCTURAL PLAN
 - 2. FIXING SPECIFICATION SUBJECT TO CHANGE AS PER DESIGN.


Casette to Floor/Roof Joist Connection

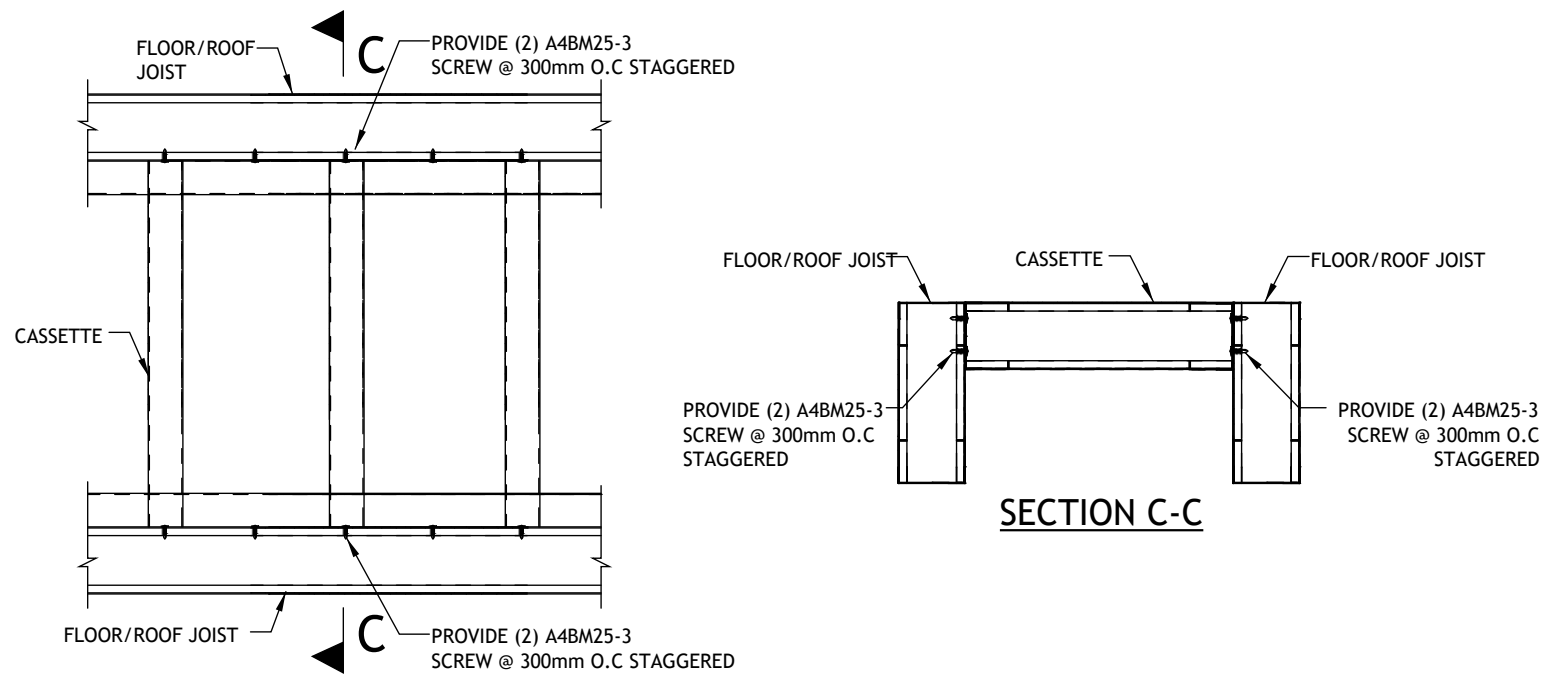

NOTE -FIXING SPECIFICATION SUBJECT TO CHANGE AS PER DESIGN.





Typ. Internal Wall Connection Floor/Roof Joist

(Perpendicular Condition)

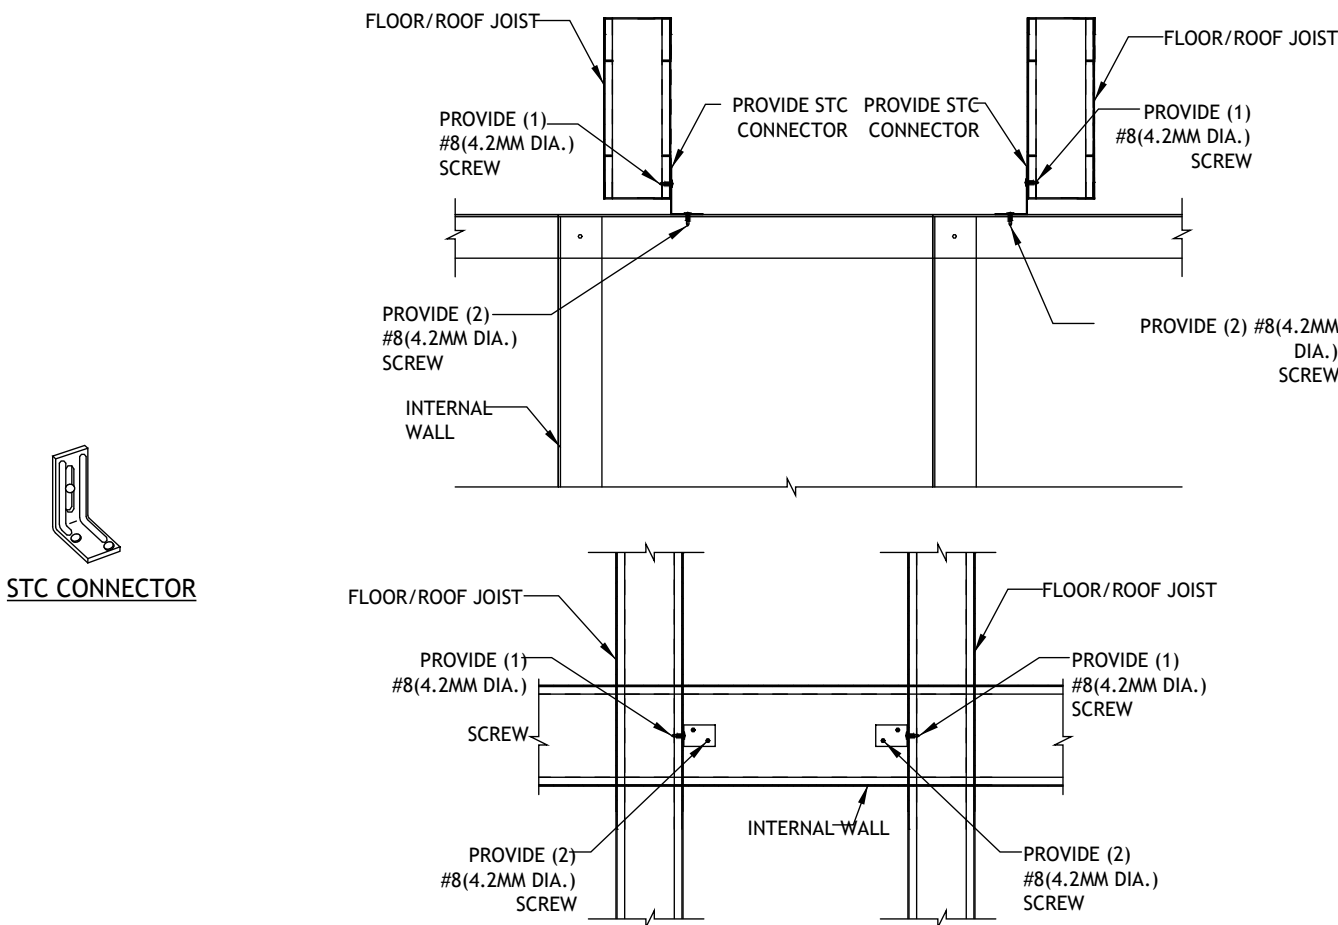


NOTE -FIXING SPECIFICATION SUBJECT TO CHANGE AS PER DESIGN.



Typ. Brace Wall Panel Connection with Treaded Rod

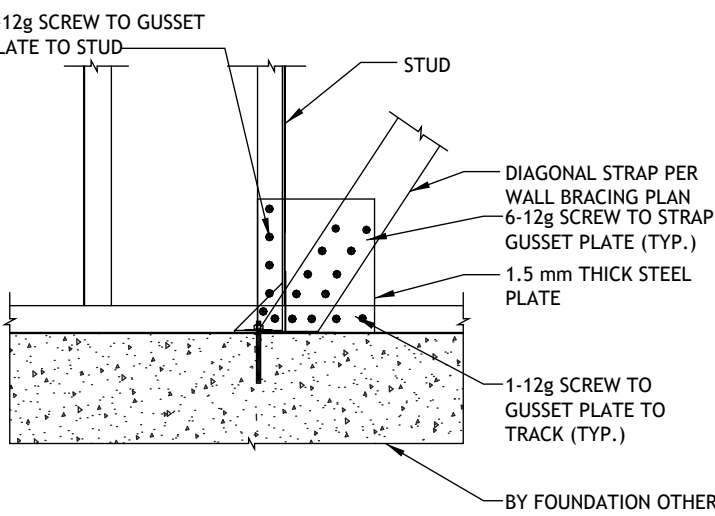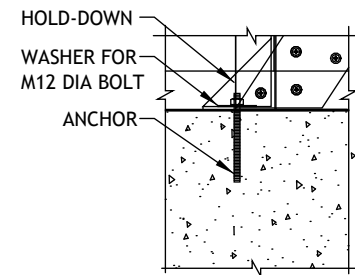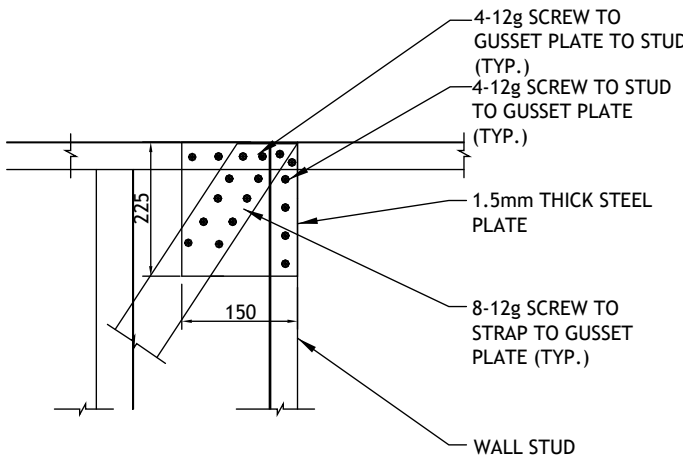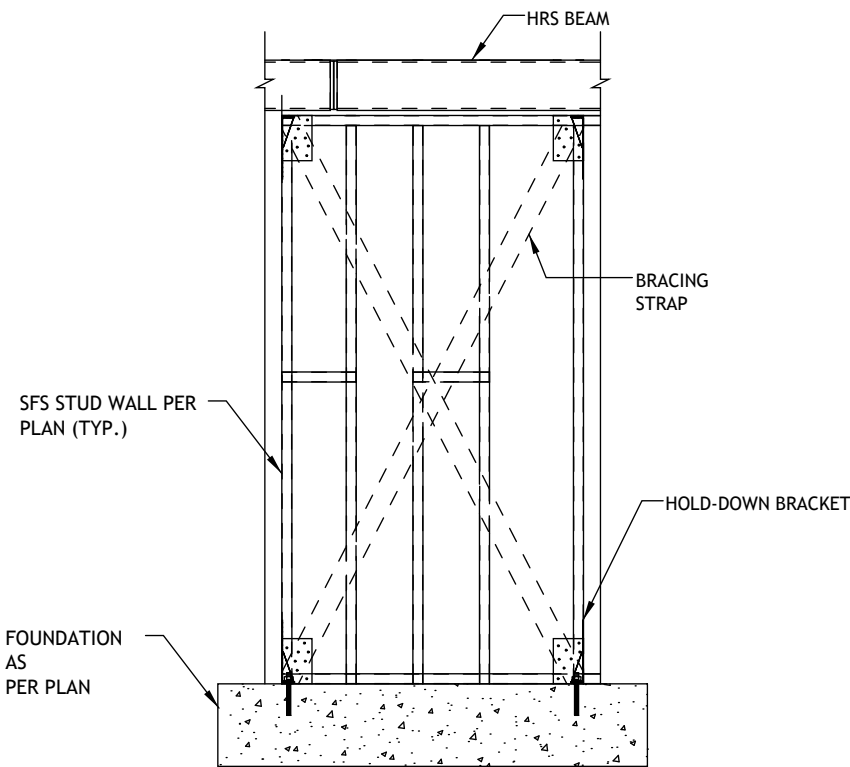

- NOTE -
- 1. ANCHOR & SCREWS SPECIFICATION AS PER SPECIFIED ON STRUCTURAL PLAN
 - 2. FIXING SPECIFICATION SUBJECT TO CHANGE AS PER DESIGN.

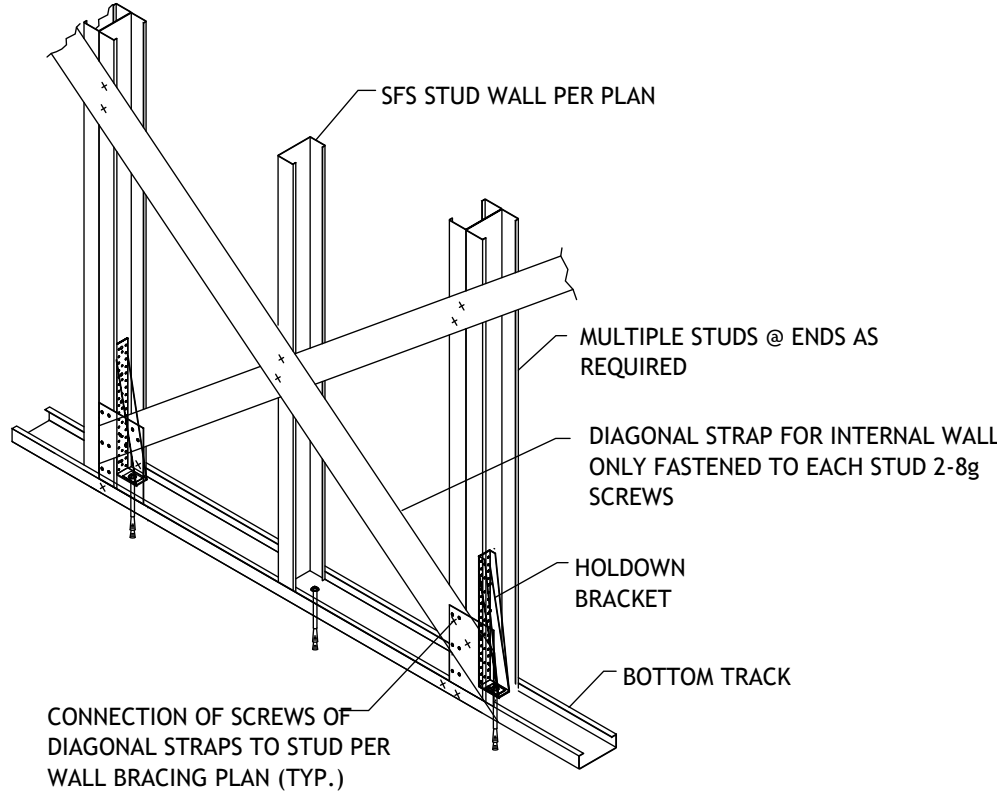

STRAP TO TRACK CONNECTION

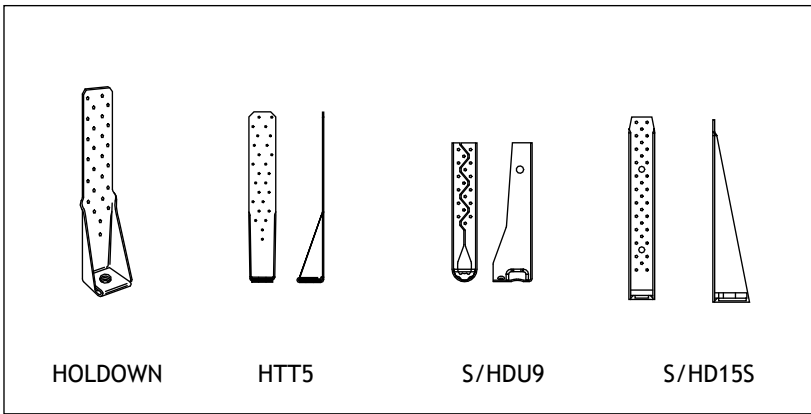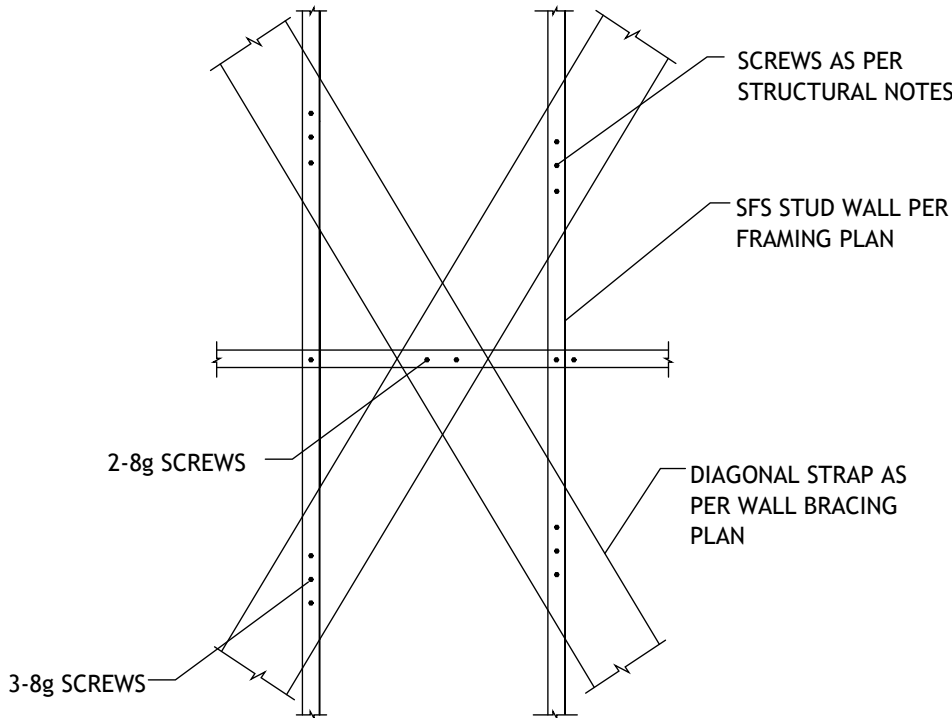

1. THESE DRAWINGS MUST BE CHECKED BY THE CUSTOMER OR CONTRACTOR PRIOR TO APPROVAL. ANY ERRORS OR OMISSIONS MUST BE REPORTED IN WRITING TO BAUHU PRIOR TO COMMENCEMENT OF CONSTRUCTION.
2. ARCHITECTURAL DRAWINGS SHOULD BE READ IN CONJUNCTION WITH STRUCTURAL DETAILING AND FABRICATION GENERAL ASSEMBLY DRAWINGS.
3. FOR CONSTRUCTION PURPOSES, USE ONLY THE LATEST APPROVED DRAWINGS LABELED 'ISSUED FOR CONSTRUCTION'.
4. DO NOT SCALE FROM THIS DRAWING.
5. THE COMPANY OPERATES USING METRIC DIMENSIONS AS THE PRINCIPAL DENOMINATION.
6. ALL CONCRETE WORKS ARE OUTSIDE OF THE SCOPE OF THE COMPANY. INFORMATION REGARDING SLAB DESIGN AND CONNECTIONS IN THESE DRAWINGS ARE INTENDED FOR GUIDANCE ONLY. FOUNDATION AND SLAB WORKS SHOULD BE DESIGNED AND APPROVED BY A LOCAL STRUCTURAL ENGINEER.
7. THE COMPANY RETAINS FULL TITLE AND OWNERSHIP OF THESE PLANS AND DESIGNS. ANY UNAUTHORISED USE, REPRODUCTION, OR DISTRIBUTION OF THESE PLANS, WHETHER IN WHOLE OR PART, IS EXPRESSLY PROHIBITED WITHOUT PRIOR WRITTEN CONSENT.
8. THE HYBRID STEEL FRAME CONSTRUCTION SYSTEM AND METHODOLOGY (PATENT PENDING) DESCRIBED IN THESE PLANS HAS BEEN DEVELOPED BY THE COMPANY AND IS SUBJECT TO A PROVISIONAL PATENT APPLICATION & ASSIGNMENT - US APPLICATION No. 63/722,841.

No.	Revision	Date
01	Moved walls under roof joists	13.03

ISSUED FOR:

Issued for information

Issued for client approval

Issued for fabrication

Issued for construction

Bahama Beach

DRAWING TITLE:
Typical Frame Connections 4

DRAWN BY:
Mladin Monica-Mihaela

SCALE:

DRAWING NO:
A45

DATE:
17/03/2025

General Construction notes

STANDARDS AND CODES OF PRACTICE

- International Building Code (IBC) 2015
- ASCE 7-16- American Society of civil Engineers (Minimum Design loads for buildings & other structures)
- AISC 360-10 - American Institute of steel construction (Specification for structural steel buildings)
- AISI -100-16 - American Iron and Steel Institute (Design of Cold Formed steel & structural members)
- ASTM - American Society for Testing and materials.
- All CFS frame will be designed to AISI LRFD CFS design standard

COLD FORMED STEEL (LGS)

Walls panels and trusses are made up by roll-formed cold rolled, galvanised steel sections fabricated and assembled into frames. Section properties in accordance with BS EN 1993-1-3:2006.
Steel grade S450GD + Z275.
C 70 -50/70- 1.2/1.5/2
C 100 -50/70- 1.2/1.5/2
C 150 -50/70- 1.2/1.5/2
LGS frames are fixed to each other and to the HRS members with specified mechanical fixings.

HOT ROLLED STEEL (HRS)

Material Availability of Hot Rolled Steel Sections is as per European/British sections with grade of S275.
Plate thickness 6, 8, 10,12mm grade S275, S355.
HRS members are hot dip galvanised and fixed to each other with specified mechanical fixings to form a portal frame.

SLAB FIXINGS

Concrete slab and foundation design is carried out by relevant local engineers and falls outside of the scope of Bauhu construction. HRS columns are supplied with pre-drilled column base plates for ground fixing with specified chemical anchor bolts.
LGS frame base rails are pre-punched for mechanical fixing to a concrete slab using the specified expanding bolts. A damp proof membrane is required.

CONSTRUCTIVE CLADDING

12.5mm lightweight, fire resistant, high density cement board is fixed to the entire exterior wall surface of the assembled building. Cement board is fixed at 300mm CTS to LGS studs and track profiles with AISI C1022 grade coated steel wing tip TEK-3 self-drilling and countersinking fixings 4.8mmx48mm.
Cement board spanning HRS members is adhered to the HRS outer surface.
Constructive cladding joints are sealed with mastic.

OPENING REVEALS CLADDING

12.5mm lightweight, fire resistant, high density cement board is fixed to opening reveals in the same manner. See assembly information and section drawings for dimension details.

CEILINGS

Ceilings are suspended from LGS roof or intermediate floor joists using Knauf C-Form suspended ceiling system mechanically fixed to joists. An insulation layer of 160mm mineral wool insulation is laid inside the ceiling void. Ceilings are finished in two layers of 12.5mm gypsumboard.
Knauf moisture panel + Knauf fire panel fixed at 300mm CTS to suspended ceiling profiles with AISI C1022 grade coated steel wing tip TEK-3 self drilling and countersinking fixings 4.8mmx48mm with joints taped and filled.
Internal low VOC acrylic paint finishes are applied per customer selection.

INTERMEDIATE FLOORS

Intermediate floor structures are supported by LGS lattice frame joists mechanically fixed to HRS beams typically at 500mm CTS according to project engineering.
18mm OSB4, termite treated, oriented strand board is fixed to the entire floor surface of the assembled building. OSB4 board is fixed at 300mm CTS to LGS joists with AISI C1022 grade coated steel wing tip TEK-3 self drilling and countersinking fixings 4.8mmx48mm.
6mm cement board floor backer sheets are mechanically fixed to the floor surface to accept client specified floor finishes.

EXTERIOR WALLS

Exterior walls are formed by pre-assembled 150mm x1.5mm profile LGS frames mechanically fixed to adjacent frames, floors and roof/floor joists. Section properties in accordance with BS EN 1993-1-3:2006. Steel grade S450GD + Z275. Frame profiles have pre-punched service holes for cable and pipe passage.
120mm mineral wool insulation is applied in the frame web.
The exterior wall surfaces are clad in a cement board constructive coating (see CONSTRUCTIVE COATING)
The interior wall surfaces are finished in two layers of 12.5mm gypsumboard Knauf moisture panel applied in horizontal format + Knauf fire panel applied in vertical format fixed at 300mm CTS to LGS profiles with AISI C1022 grade coated steel wing tip TEK-3 self drilling and countersinking fixings 4.8mmx48mm with joints taped and filled.
Internal low VOC acrylic paint finishes are applied per customer selection.

INTERIOR WALLS

Interior walls are formed by pre-assembled 150mm x1.5mm profile LGS frames mechanically fixed to adjacent walls, floors and roof/floor joists. Section properties in accordance with BS EN 1993-1-3:2006. Steel grade S450GD + Z275. Frame profiles have pre-punched service holes for cable and pipe passage.
120mm mineral wool insulation is applied in the frame web.
Internal walls are finished in two opposing layers of 12.5mm gypsumboard fixed at 300mm CTS to LGS profiles with AISI C1022 grade coated steel wing tip TEK-3 self drilling and countersinking fixings 4.8mmx48mm.
Knauf moisture panel applied in horizontal format + Knauf fire panel applied in vertical format with joints taped and filled.
Internal low VOC acrylic paint finishes are applied per customer selection.
EXTERIOR FACADE (ETICs)
The external facade is finished in an impact resistant, self colour, thermal and acoustic ETICs (External thermal insulation composite system) coating. An insulation layer of 40mm rigid Rockwool is applied to the cement board constructive coating with mechanical fixings. STO impact resistant plaster base coat is applied with fiberglass mesh and finished in STOLIT finish plaster coat.

FLAT ROOF STRUCTURE (EPDM)

Flat roof structures are supported by LGS lattice frame joists mechanically fixed to HRS beams typically at 500mm CTS according to project engineering.
18mm OSB4, termite treated, oriented strand board is fixed to the entire exterior roof surface of the assembled building. OSB4 is fixed at 300mm CTS to LGS joists with AISI C1022 grade coated steel wing tip TEK-3 self drilling and countersinking fixings 4.8mmx38mm.
A rigid 40mm PIR insulation board is mechanically fixed to the cement board constructive cladding.
Firestone 1.5mm heavy duty EPDM waterproofing membrane is fully bonded to the roof surface and parapet sides with rain water outlets and breather pipe boots at appropriate locations.
Leaf guards are installed in rain water outlets.

PARAPET DETAIL

LGS panels are mechanically fixed to HRS beams to form a parapet extension of exterior walls.
LGS parapet frames are clad in SECOLITE 12.5mm cement board on inner and top faces. A metal capping or acrylic render finishes parapet tops.

ACCESSIBLE ROOFS

Accessible roofs have the same properties as flat (EPDM) roofs. Final floor finishes of ceramic tile or composite decking should be laid over a supplementary geotextile membrane to protect the EPDM membrane. Refer to project files for specific details.

GREEN ROOFS

Green roofs have the same properties as flat (EPDM) roofs. Vegetation in specified containers is added over a textile membrane. Vegetation is NOT supplied.

SOLAR ROOFS

Projects requiring solar (PV) arrays to be roof mounted are subject to specialist analysis.



1. THESE DRAWINGS MUST BE CHECKED BY THE CUSTOMER OR CONTRACTOR PRIOR TO APPROVAL. ANY ERRORS OR OMISSIONS MUST BE REPORTED IN WRITING TO BAUHU PRIOR TO COMMENCEMENT OF CONSTRUCTION.
2. ARCHITECTURAL DRAWINGS SHOULD BE READ IN CONJUNCTION WITH STRUCTURAL DETAILING AND FABRICATION GENERAL ASSEMBLY DRAWINGS.
3. FOR CONSTRUCTION PURPOSES, USE ONLY THE LATEST APPROVED DRAWINGS LABELED 'ISSUED FOR CONSTRUCTION'.
4. DO NOT SCALE FROM THIS DRAWING.
5. THE COMPANY OPERATES USING METRIC DIMENSIONS AS THE PRINCIPAL DENOMINATION.
6. ALL CONCRETE WORKS ARE OUTSIDE OF THE SCOPE OF THE COMPANY. INFORMATION REGARDING SLAB DESIGN AND CONNECTIONS IN THESE DRAWINGS ARE INTENDED FOR GUIDENCE ONLY. FOUNDATION AND SLAB WORKS SHOULD BE DESIGNED AND APPROVED BY A LOCAL STRUCTURAL ENGINEER.
7. THE COMPANY RETAINS FULL TITLE AND OWNERSHIP OF THESE PLANS AND DESIGNS. ANY UNAUTHORISED USE, REPRODUCTION, OR DISTRIBUTION OF THESE PLANS, WHETHER IN WHOLE OR PART, IS EXPRESSLY PROHIBITED WITHOUT PRIOR WRITTEN CONSENT.
8. THE HYBRID STEEL FRAME CONSTRUCTION SYSTEM AND METHODOLOGY (PATENT PENDING) DESCRIBED IN THESE PLANS HAS BEEN DEVELOPED BY THE COMPANY AND IS SUBJECT TO A PROVISIONAL PATENT APPLICATION & ASSIGNMENT - US APPLICATION No. 63/722,841.

No.	Revision	Date
01	Moved walls under roof joists	13.03

ISSUED FOR:

Issued for information

Issued for client approval

Issued for fabrication

Issued for construction

Bahama Beach

DRAWING TITLE:

General Construction Notes

DRAWN BY:

Mladin Monica-Mihaela

SCALE:

DRAWING NO:

A46

DATE:

17/03/2025