




Rear View

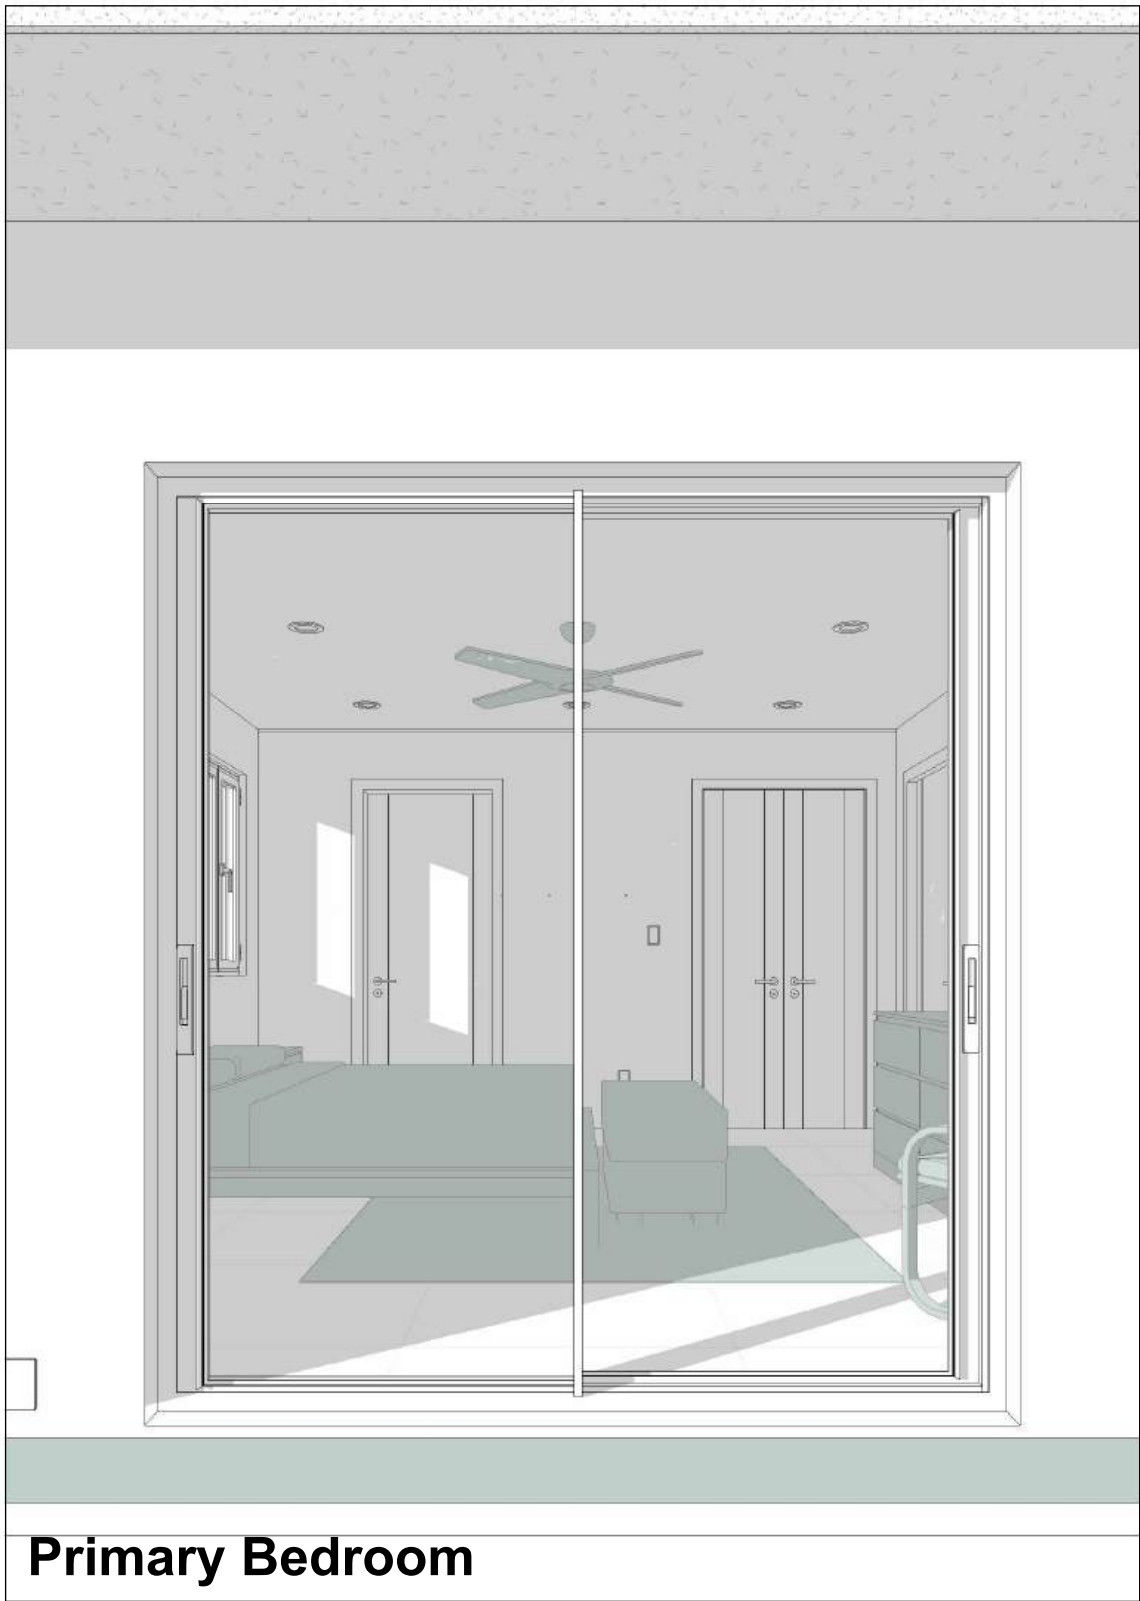

Primary Bedroom



Living Area



Living Area


1. THESE DRAWINGS MUST BE CHECKED BY THE CUSTOMER OR CONTRACTOR PRIOR TO APPROVAL. ANY ERRORS OR OMISSIONS MUST BE REPORTED IN WRITING TO BAUHU PRIOR TO COMMENCEMENT OF CONSTRUCTION.
2. ARCHITECTURAL DRAWINGS SHOULD BE READ IN CONJUNCTION WITH STRUCTURAL DETAILING AND FABRICATION GENERAL ASSEMBLY DRAWINGS.
3. FOR CONSTRUCTION PURPOSES, USE ONLY THE LATEST APPROVED DRAWINGS LABELED 'ISSUED FOR CONSTRUCTION'.
4. DO NOT SCALE FROM THIS DRAWING.
5. THE COMPANY OPERATES USING METRIC DIMENSIONS AS THE PRINCIPAL DENOMINATION.
6. ALL CONCRETE WORKS ARE OUTSIDE OF THE SCOPE OF THE COMPANY. INFORMATION REGARDING SLAB DESIGN AND CONNECTIONS IN THESE DRAWINGS ARE INTENDED FOR GUIDANCE ONLY. FOUNDATION AND SLAB WORKS SHOULD BE DESIGNED AND APPROVED BY A LOCAL STRUCTURAL ENGINEER.
7. THE COMPANY RETAINS FULL TITLE AND OWNERSHIP OF THESE PLANS AND DESIGNS. ANY UNAUTHORISED USE, REPRODUCTION, OR DISTRIBUTION OF THESE PLANS, WHETHER IN WHOLE OR PART, IS EXPRESSLY PROHIBITED WITHOUT PRIOR WRITTEN CONSENT.
8. THE HYBRID STEEL FRAME CONSTRUCTION SYSTEM AND METHODOLOGY (PATENT PENDING) DESCRIBED IN THESE PLANS HAS BEEN DEVELOPED BY THE COMPANY AND IS SUBJECT TO A PROVISIONAL PATENT APPLICATION & ASSIGNMENT - US APPLICATION NO. 63/722,841

No.	Revision	Date

- ISSUED FOR:
- ☒ Issued for information
 - ☐ Issued for client approval
 - ☐ Issued for fabrication
 - ☐ Issued for construction

Coconut Villa
3 Bed

DRAWING TITLE:	Views
DRAWN BY:	Y.A.Clark
SCALE:	
DRAWING NO:	A101
DATE:	16/02/2026

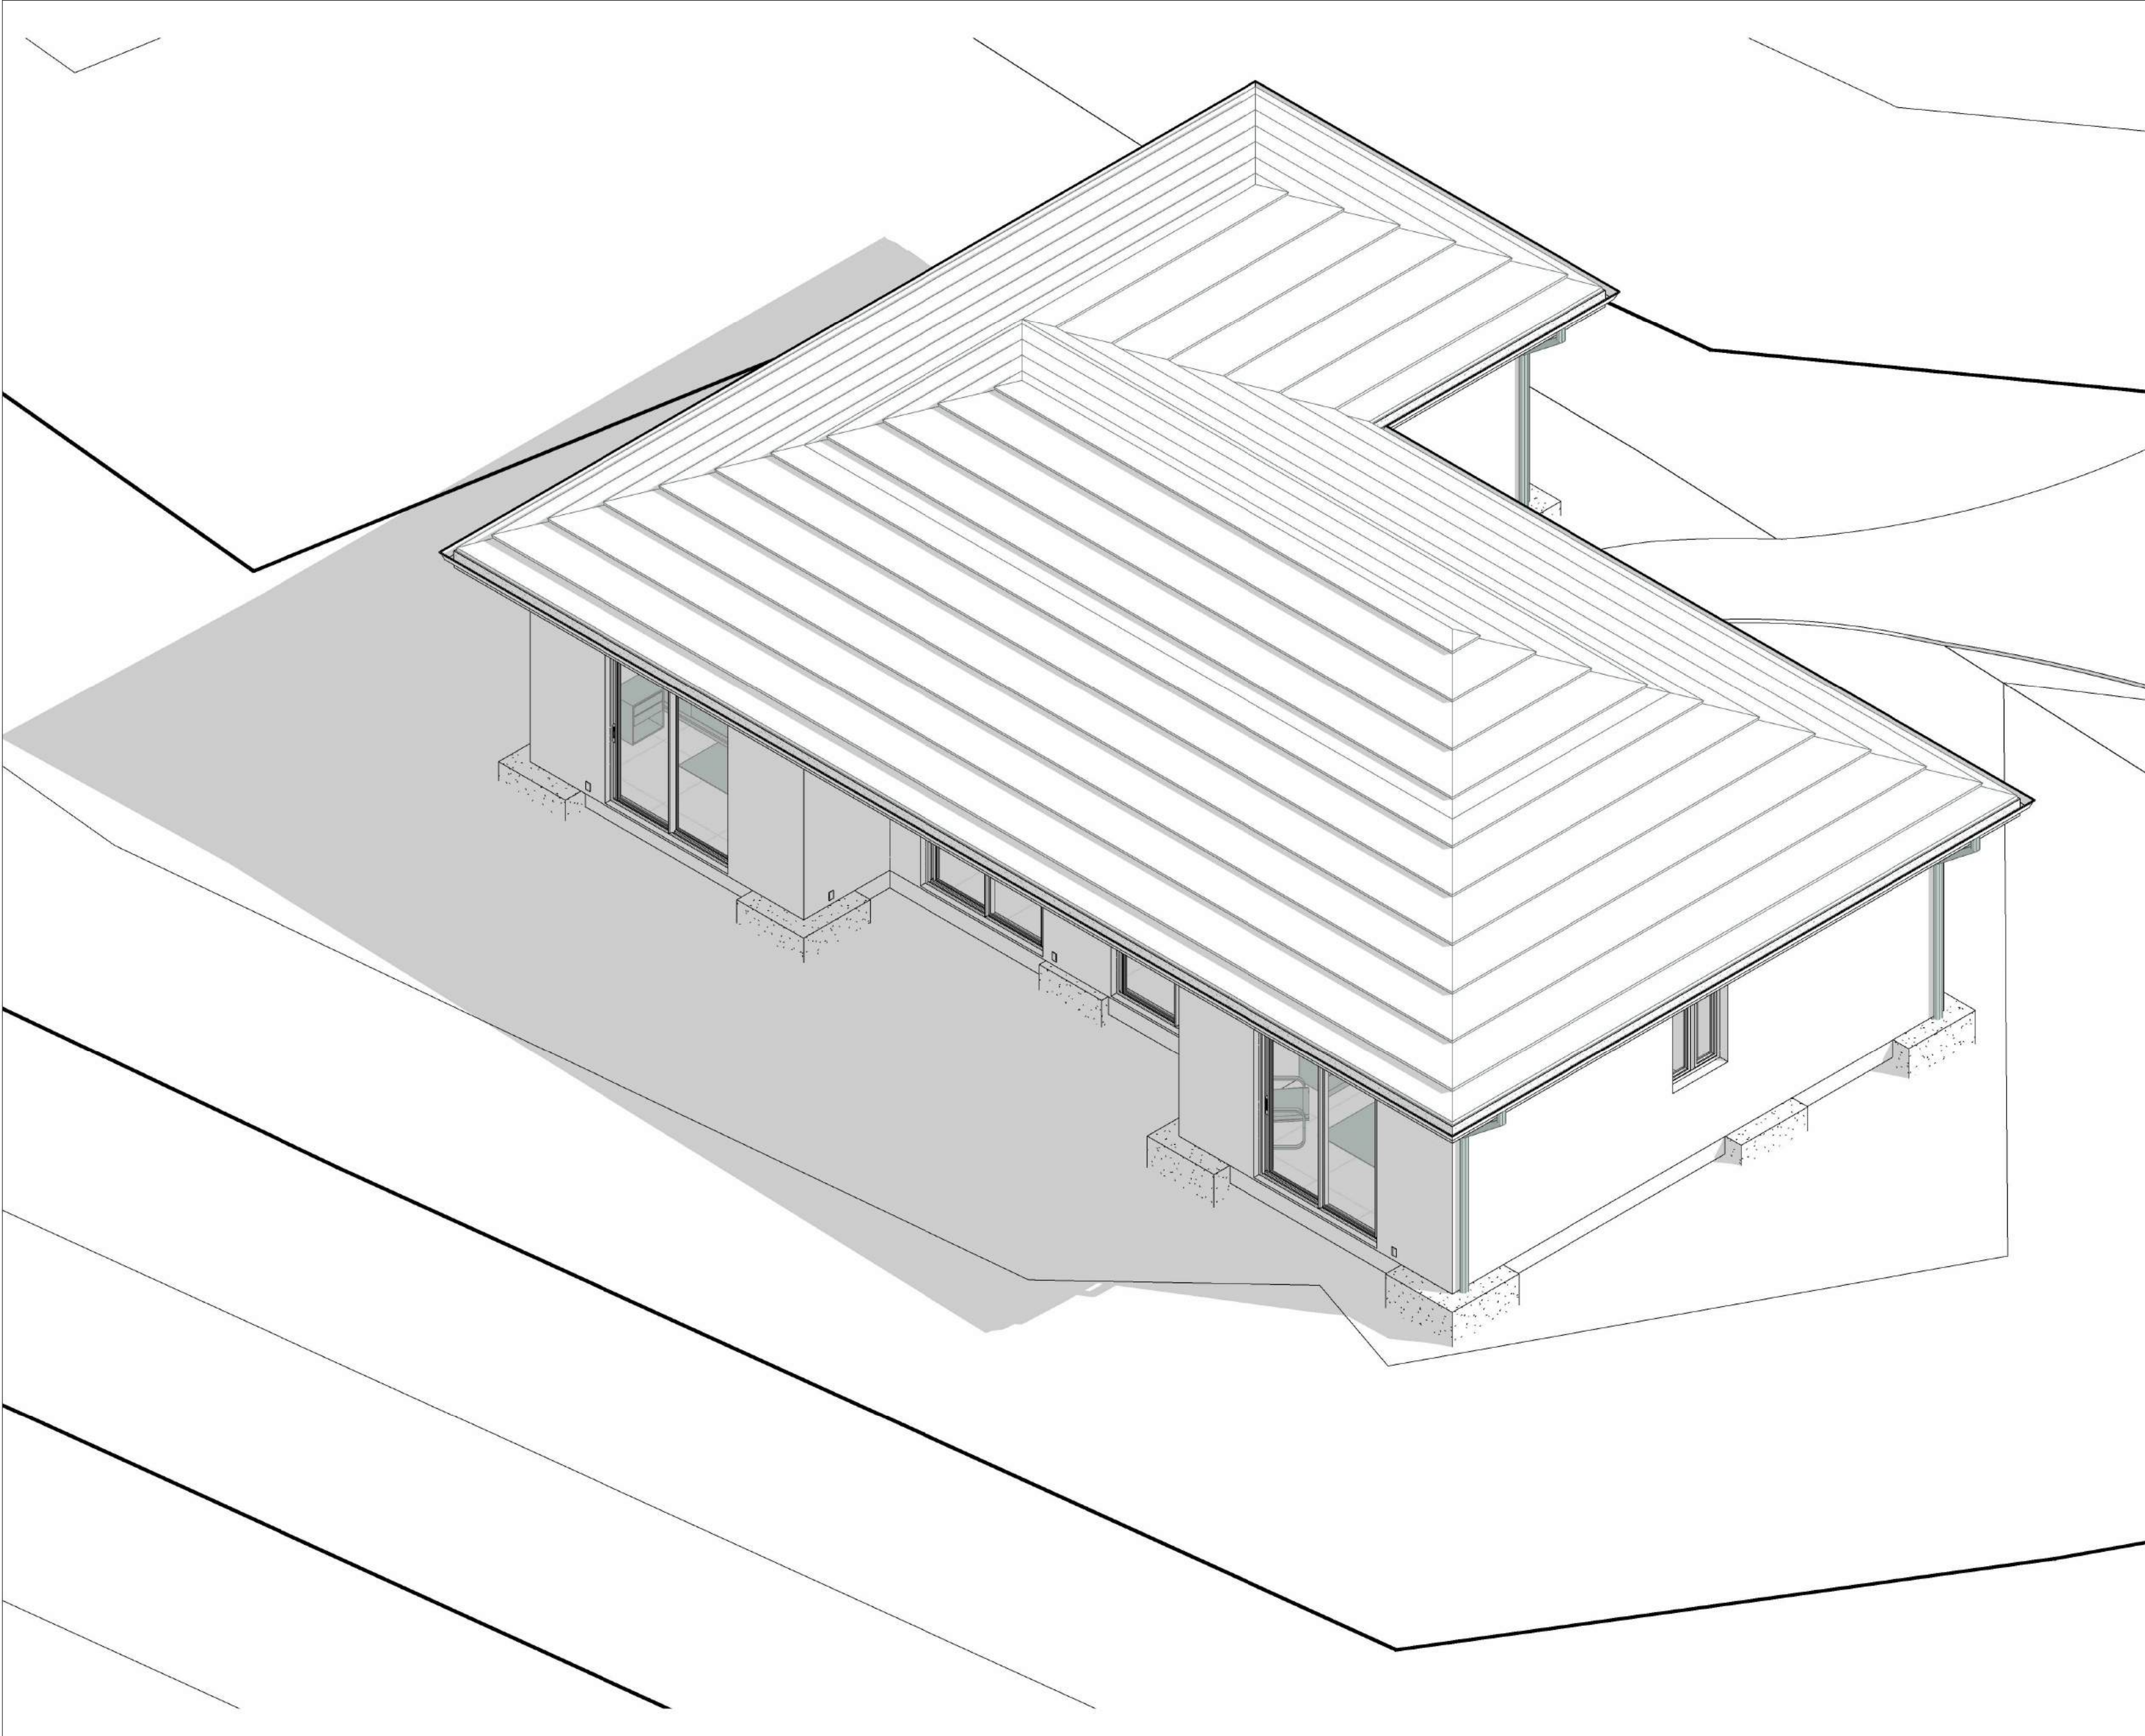

1. THESE DRAWINGS MUST BE CHECKED BY THE CUSTOMER OR CONTRACTOR PRIOR TO APPROVAL. ANY ERRORS OR OMISSIONS MUST BE REPORTED IN WRITING TO BAUHU PRIOR TO COMMENCEMENT OF CONSTRUCTION.
2. ARCHITECTURAL DRAWINGS SHOULD BE READ IN CONJUNCTION WITH STRUCTURAL DETAILING AND FABRICATION GENERAL ASSEMBLY DRAWINGS.
3. FOR CONSTRUCTION PURPOSES, USE ONLY THE LATEST APPROVED DRAWINGS LABELED 'ISSUED FOR CONSTRUCTION'.
4. DO NOT SCALE FROM THIS DRAWING.
5. THE COMPANY OPERATES USING METRIC DIMENSIONS AS THE PRINCIPAL DENOMINATION.
6. ALL CONCRETE WORKS ARE OUTSIDE OF THE SCOPE OF THE COMPANY. INFORMATION REGARDING SLAB DESIGN AND CONNECTIONS IN THESE DRAWINGS ARE INTENDED FOR GUIDENCE ONLY. FOUNDATION AND SLAB WORKS SHOULD BE DESIGNED AND APPROVED BY A LOCAL STRUCTURAL ENGINEER.
7. THE COMPANY RETAINS FULL TITLE AND OWNERSHIP OF THESE PLANS AND DESIGNS. ANY UNAUTHORISED USE, REPRODUCTION, OR DISTRIBUTION OF THESE PLANS, WHETHER IN WHOLE OR PART, IS EXPRESSLY PROHIBITED WITHOUT PRIOR WRITTEN CONSENT.
8. THE HYBRID STEEL FRAME CONSTRUCTION SYSTEM AND METHODOLOGY (PATENT PENDING) DESCRIBED IN THESE PLANS HAS BEEN DEVELOPED BY THE COMPANY AND IS SUBJECT TO A PROVISIONAL PATENT APPLICATION & ASSIGNMENT - US APPLICATION NO. 63/722,841

No.	Revision	Date

ISSUED FOR:

☒ Issued for information


☐ Issued for client approval

☐ Issued for fabrication

☐ Issued for construction

Coconut Villa
3 Bed

DRAWING TITLE:	Front View
DRAWN BY:	Y.A.Clark
SCALE:	
DRAWING NO:	A102
DATE:	16/02/2026

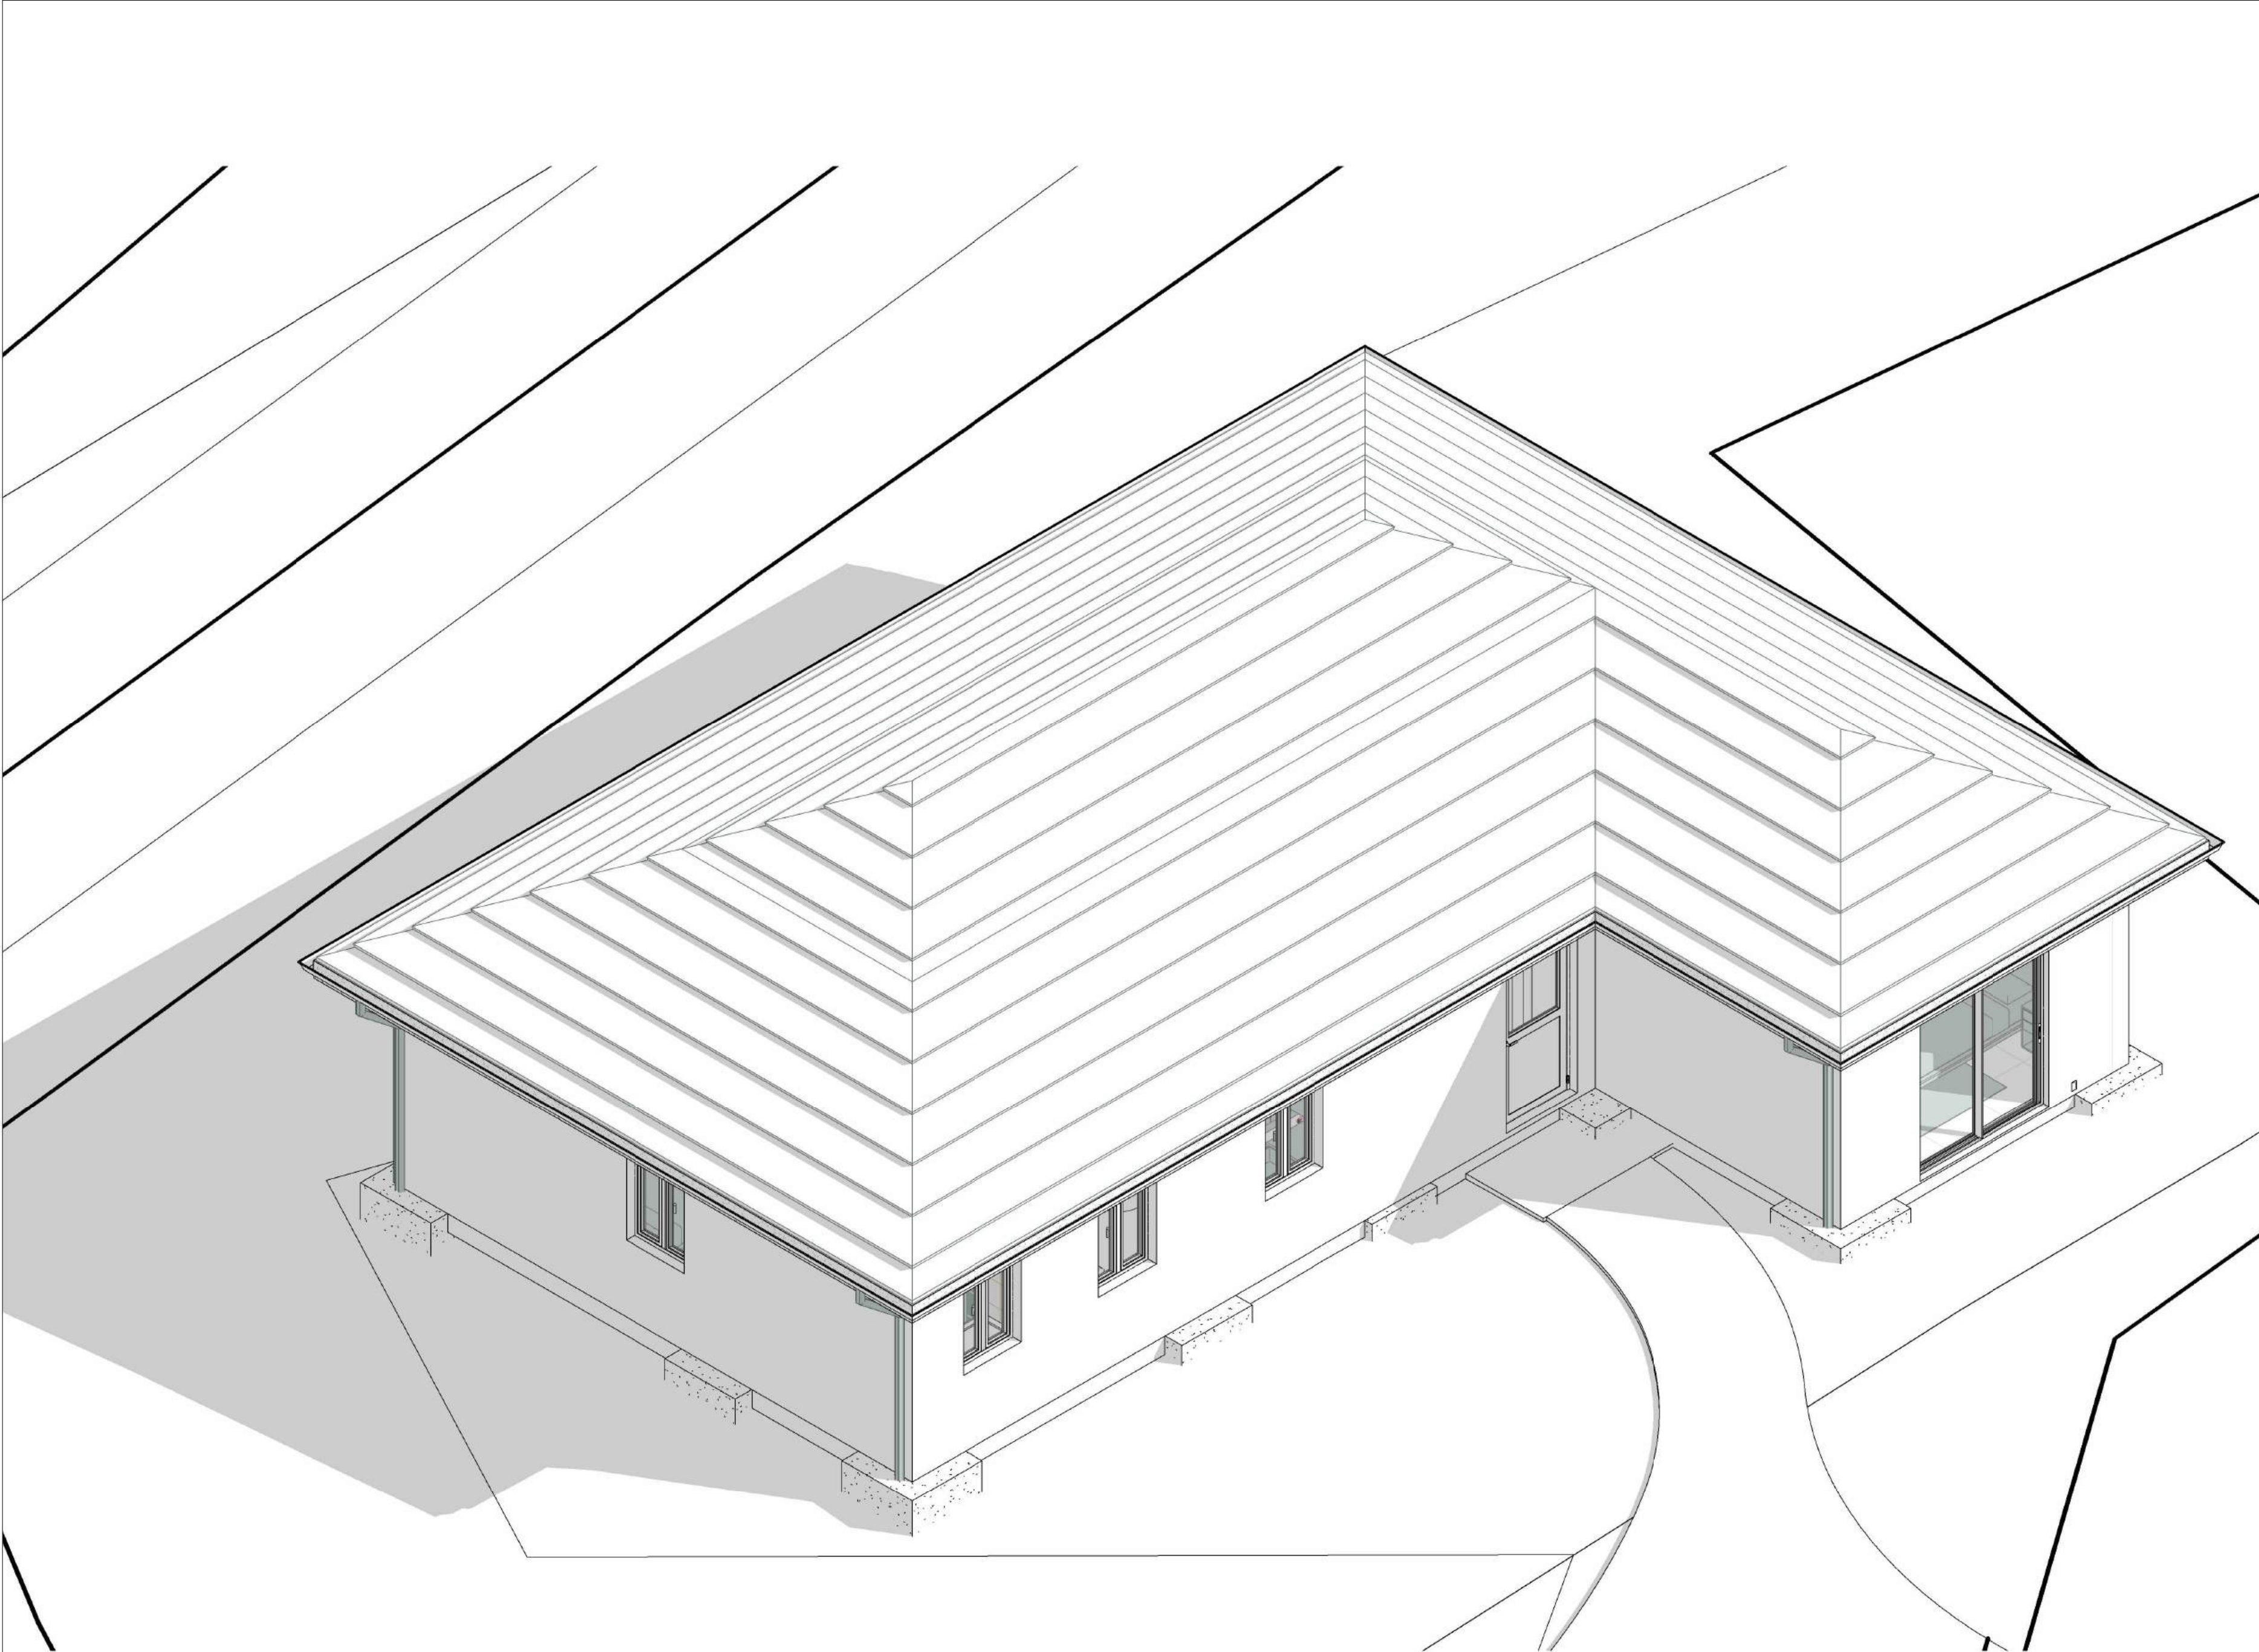

1. THESE DRAWINGS MUST BE CHECKED BY THE CUSTOMER OR CONTRACTOR PRIOR TO APPROVAL. ANY ERRORS OR OMISSIONS MUST BE REPORTED IN WRITING TO BAUHU PRIOR TO COMMENCEMENT OF CONSTRUCTION.
2. ARCHITECTURAL DRAWINGS SHOULD BE READ IN CONJUNCTION WITH STRUCTURAL DETAILING AND FABRICATION GENERAL ASSEMBLY DRAWINGS.
3. FOR CONSTRUCTION PURPOSES, USE ONLY THE LATEST APPROVED DRAWINGS LABELED 'ISSUED FOR CONSTRUCTION'.
4. DO NOT SCALE FROM THIS DRAWING.
5. THE COMPANY OPERATES USING METRIC DIMENSIONS AS THE PRINCIPAL DENOMINATION.
6. ALL CONCRETE WORKS ARE OUTSIDE OF THE SCOPE OF THE COMPANY. INFORMATION REGARDING SLAB DESIGN AND CONNECTIONS IN THESE DRAWINGS ARE INTENDED FOR GUIDENCE ONLY. FOUNDATION AND SLAB WORKS SHOULD BE DESIGNED AND APPROVED BY A LOCAL STRUCTURAL ENGINEER.
7. THE COMPANY RETAINS FULL TITLE AND OWNERSHIP OF THESE PLANS AND DESIGNS. ANY UNAUTHORISED USE, REPRODUCTION, OR DISTRIBUTION OF THESE PLANS, WHETHER IN WHOLE OR PART, IS EXPRESSLY PROHIBITED WITHOUT PRIOR WRITTEN CONSENT.
8. THE HYBRID STEEL FRAME CONSTRUCTION SYSTEM AND METHODOLOGY (PATENT PENDING) DESCRIBED IN THESE PLANS HAS BEEN DEVELOPED BY THE COMPANY AND IS SUBJECT TO A PROVISIONAL PATENT APPLICATION & ASSIGNMENT - US APPLICATION NO. 63/722,841

No.	Revision	Date

ISSUED FOR:

☒ Issued for information


☐ Issued for client approval

☐ Issued for fabrication

☐ Issued for construction

Coconut Villa
3 Bed

DRAWING TITLE:	Rear View
DRAWN BY:	Y.A.Clark
SCALE:	
DRAWING NO:	A103
DATE:	16/02/2026

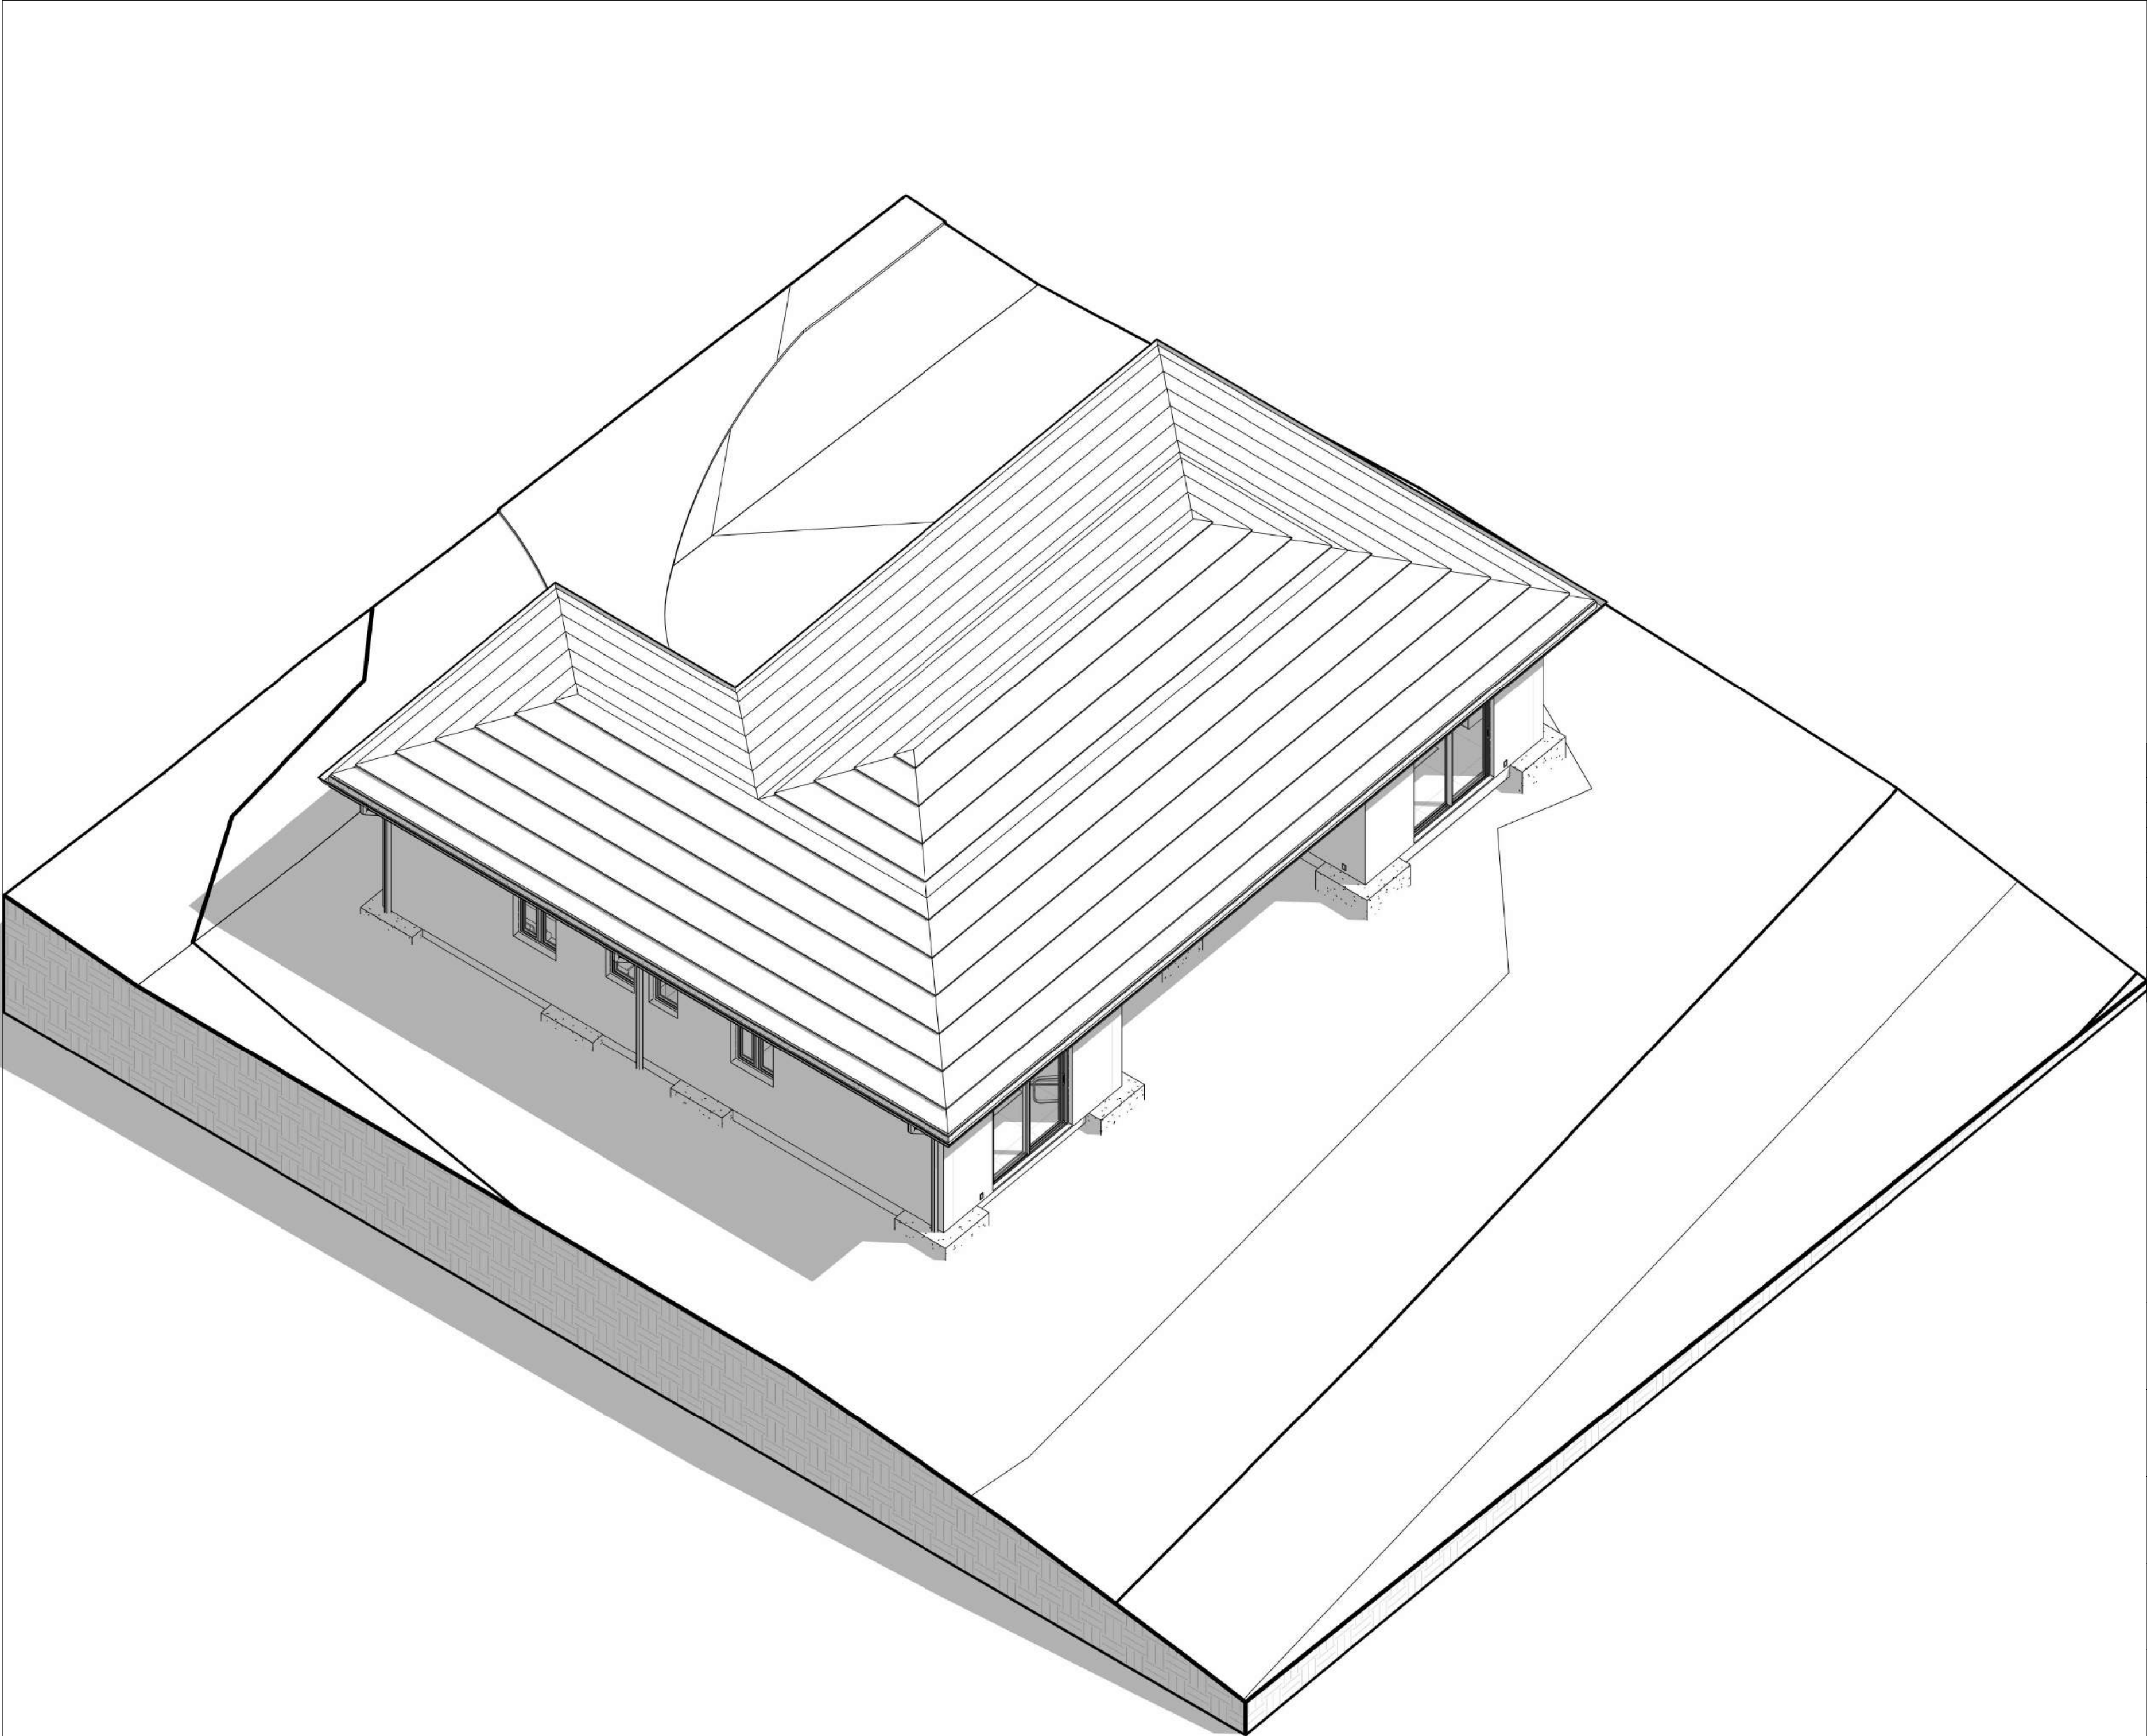

1. THESE DRAWINGS MUST BE CHECKED BY THE CUSTOMER OR CONTRACTOR PRIOR TO APPROVAL. ANY ERRORS OR OMISSIONS MUST BE REPORTED IN WRITING TO BAUHU PRIOR TO COMMENCEMENT OF CONSTRUCTION.
2. ARCHITECTURAL DRAWINGS SHOULD BE READ IN CONJUNCTION WITH STRUCTURAL DETAILING AND FABRICATION GENERAL ASSEMBLY DRAWINGS.
3. FOR CONSTRUCTION PURPOSES, USE ONLY THE LATEST APPROVED DRAWINGS LABELED 'ISSUED FOR CONSTRUCTION'.
4. DO NOT SCALE FROM THIS DRAWING.
5. THE COMPANY OPERATES USING METRIC DIMENSIONS AS THE PRINCIPAL DENOMINATION.
6. ALL CONCRETE WORKS ARE OUTSIDE OF THE SCOPE OF THE COMPANY. INFORMATION REGARDING SLAB DESIGN AND CONNECTIONS IN THESE DRAWINGS ARE INTENDED FOR GUIDENCE ONLY. FOUNDATION AND SLAB WORKS SHOULD BE DESIGNED AND APPROVED BY A LOCAL STRUCTURAL ENGINEER.
7. THE COMPANY RETAINS FULL TITLE AND OWNERSHIP OF THESE PLANS AND DESIGNS. ANY UNAUTHORISED USE, REPRODUCTION, OR DISTRIBUTION OF THESE PLANS, WHETHER IN WHOLE OR PART, IS EXPRESSLY PROHIBITED WITHOUT PRIOR WRITTEN CONSENT.
8. THE HYBRID STEEL FRAME CONSTRUCTION SYSTEM AND METHODOLOGY (PATENT PENDING) DESCRIBED IN THESE PLANS HAS BEEN DEVELOPED BY THE COMPANY AND IS SUBJECT TO A PROVISIONAL PATENT APPLICATION & ASSIGNMENT - US APPLICATION NO. 63/722,841

No.	Revision	Date

ISSUED FOR:

☒ Issued for information

☐ Issued for client approval

☐ Issued for fabrication

☐ Issued for construction

Coconut Villa
3 Bed


DRAWING TITLE:
Building Axonometry

DRAWN BY:
Y.A.Clark

SCALE:

DRAWING NO:
A104

DATE:
16/02/2026

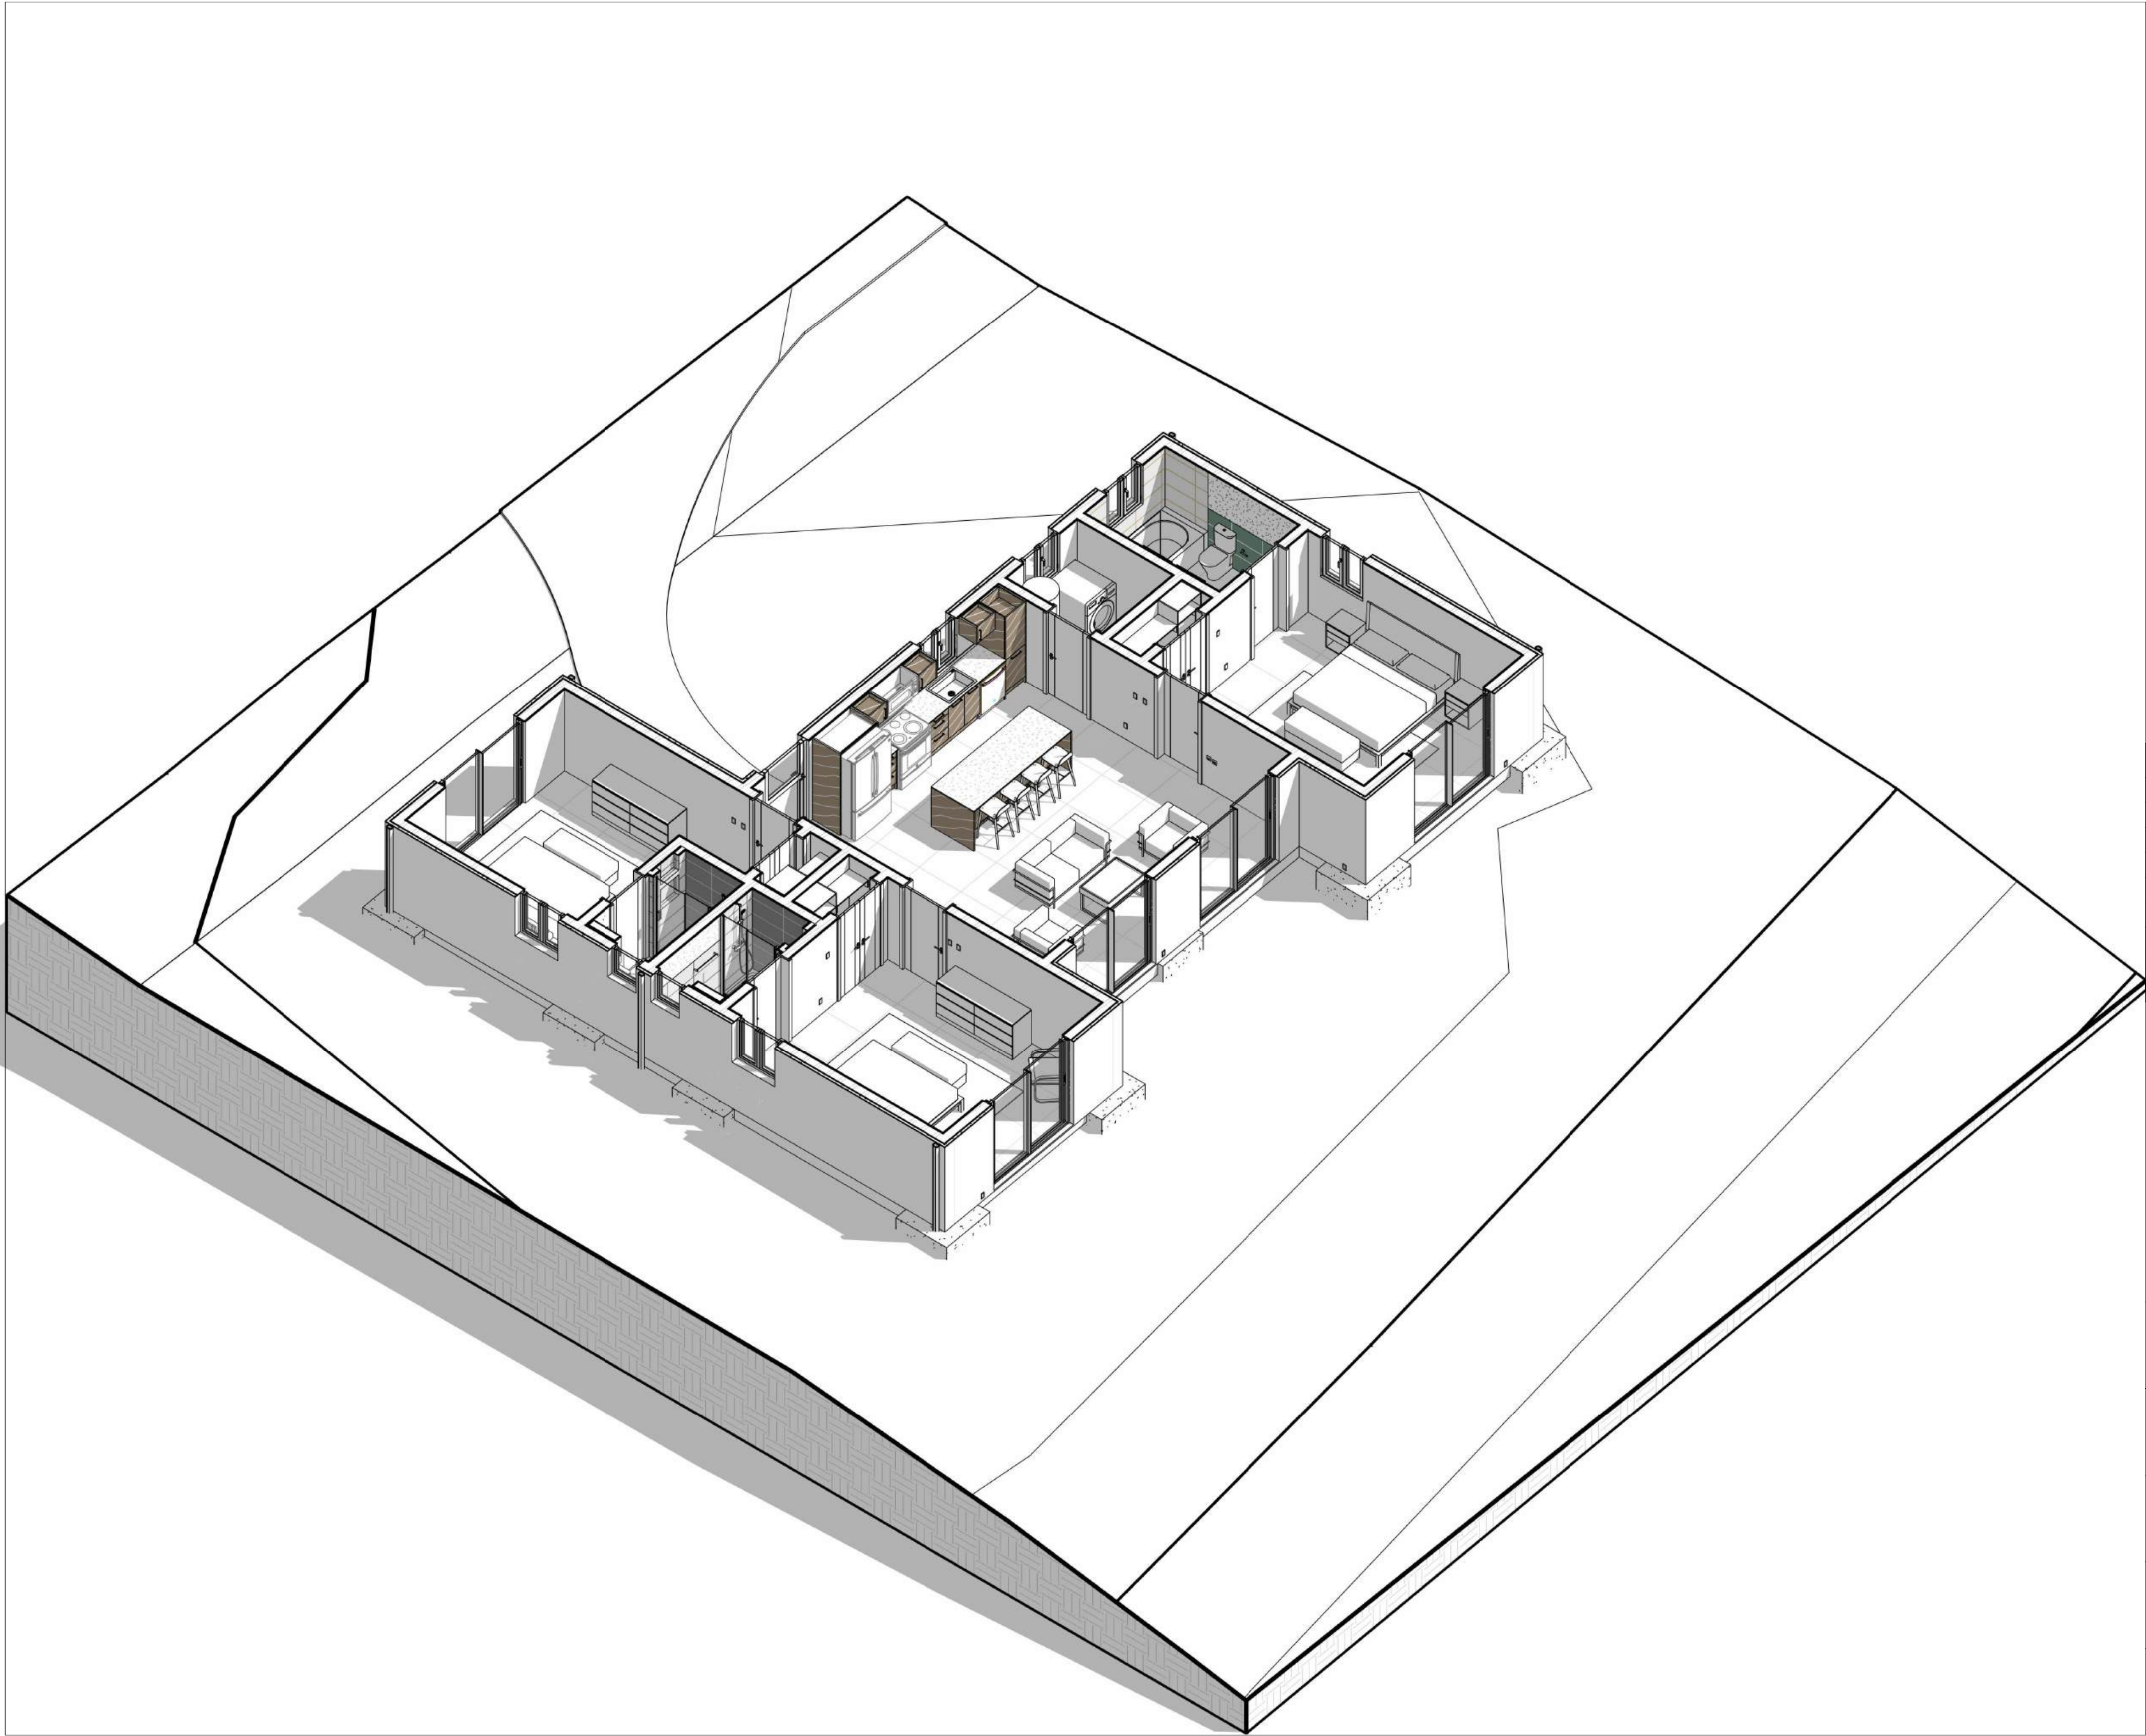

1. THESE DRAWINGS MUST BE CHECKED BY THE CUSTOMER OR CONTRACTOR PRIOR TO APPROVAL. ANY ERRORS OR OMISSIONS MUST BE REPORTED IN WRITING TO BAUHU PRIOR TO COMMENCEMENT OF CONSTRUCTION.
2. ARCHITECTURAL DRAWINGS SHOULD BE READ IN CONJUNCTION WITH STRUCTURAL DETAILING AND FABRICATION GENERAL ASSEMBLY DRAWINGS.
3. FOR CONSTRUCTION PURPOSES, USE ONLY THE LATEST APPROVED DRAWINGS LABELED 'ISSUED FOR CONSTRUCTION'.
4. DO NOT SCALE FROM THIS DRAWING.
5. THE COMPANY OPERATES USING METRIC DIMENSIONS AS THE PRINCIPAL DENOMINATION.
6. ALL CONCRETE WORKS ARE OUTSIDE OF THE SCOPE OF THE COMPANY. INFORMATION REGARDING SLAB DESIGN AND CONNECTIONS IN THESE DRAWINGS ARE INTENDED FOR GUIDENCE ONLY. FOUNDATION AND SLAB WORKS SHOULD BE DESIGNED AND APPROVED BY A LOCAL STRUCTURAL ENGINEER.
7. THE COMPANY RETAINS FULL TITLE AND OWNERSHIP OF THESE PLANS AND DESIGNS. ANY UNAUTHORISED USE, REPRODUCTION, OR DISTRIBUTION OF THESE PLANS, WHETHER IN WHOLE OR PART, IS EXPRESSLY PROHIBITED WITHOUT PRIOR WRITTEN CONSENT.
8. THE HYBRID STEEL FRAME CONSTRUCTION SYSTEM AND METHODOLOGY (PATENT PENDING) DESCRIBED IN THESE PLANS HAS BEEN DEVELOPED BY THE COMPANY AND IS SUBJECT TO A PROVISIONAL PATENT APPLICATION & ASSIGNMENT - US APPLICATION NO. 63/722,841

No.	Revision	Date

ISSUED FOR:

Issued for information


Issued for client approval

Issued for fabrication

Issued for construction

Coconut Villa
3 Bed

DRAWING TITLE:	Floor Plan Axonometry
DRAWN BY:	Y.A.Clark
SCALE:	
DRAWING NO:	A105
DATE:	16/02/2026

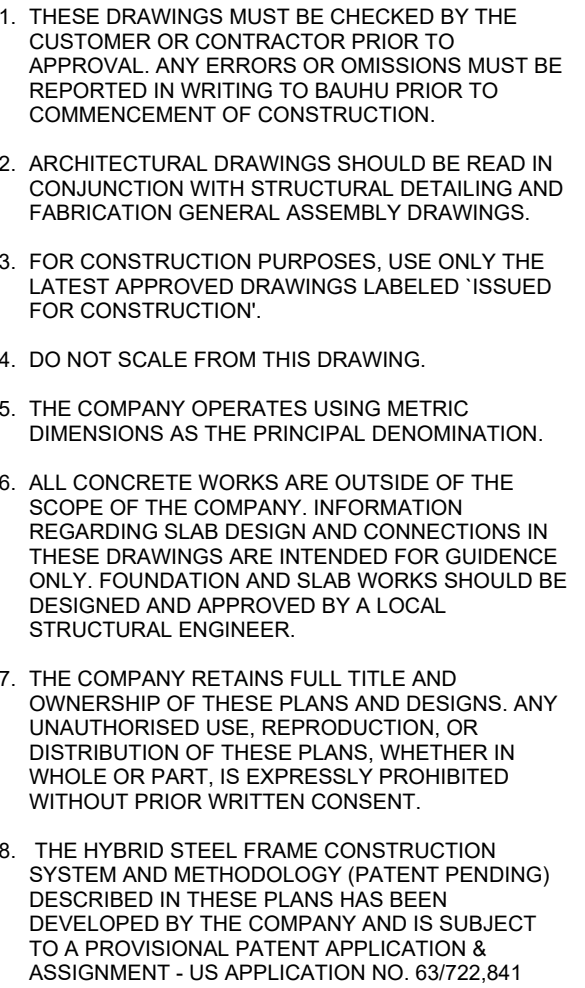[illegible]

Issued for construction

Coconut Villa

3 Bed


Roof Plan


Y.A.Clark

1 : 50

A107

16/02/2026

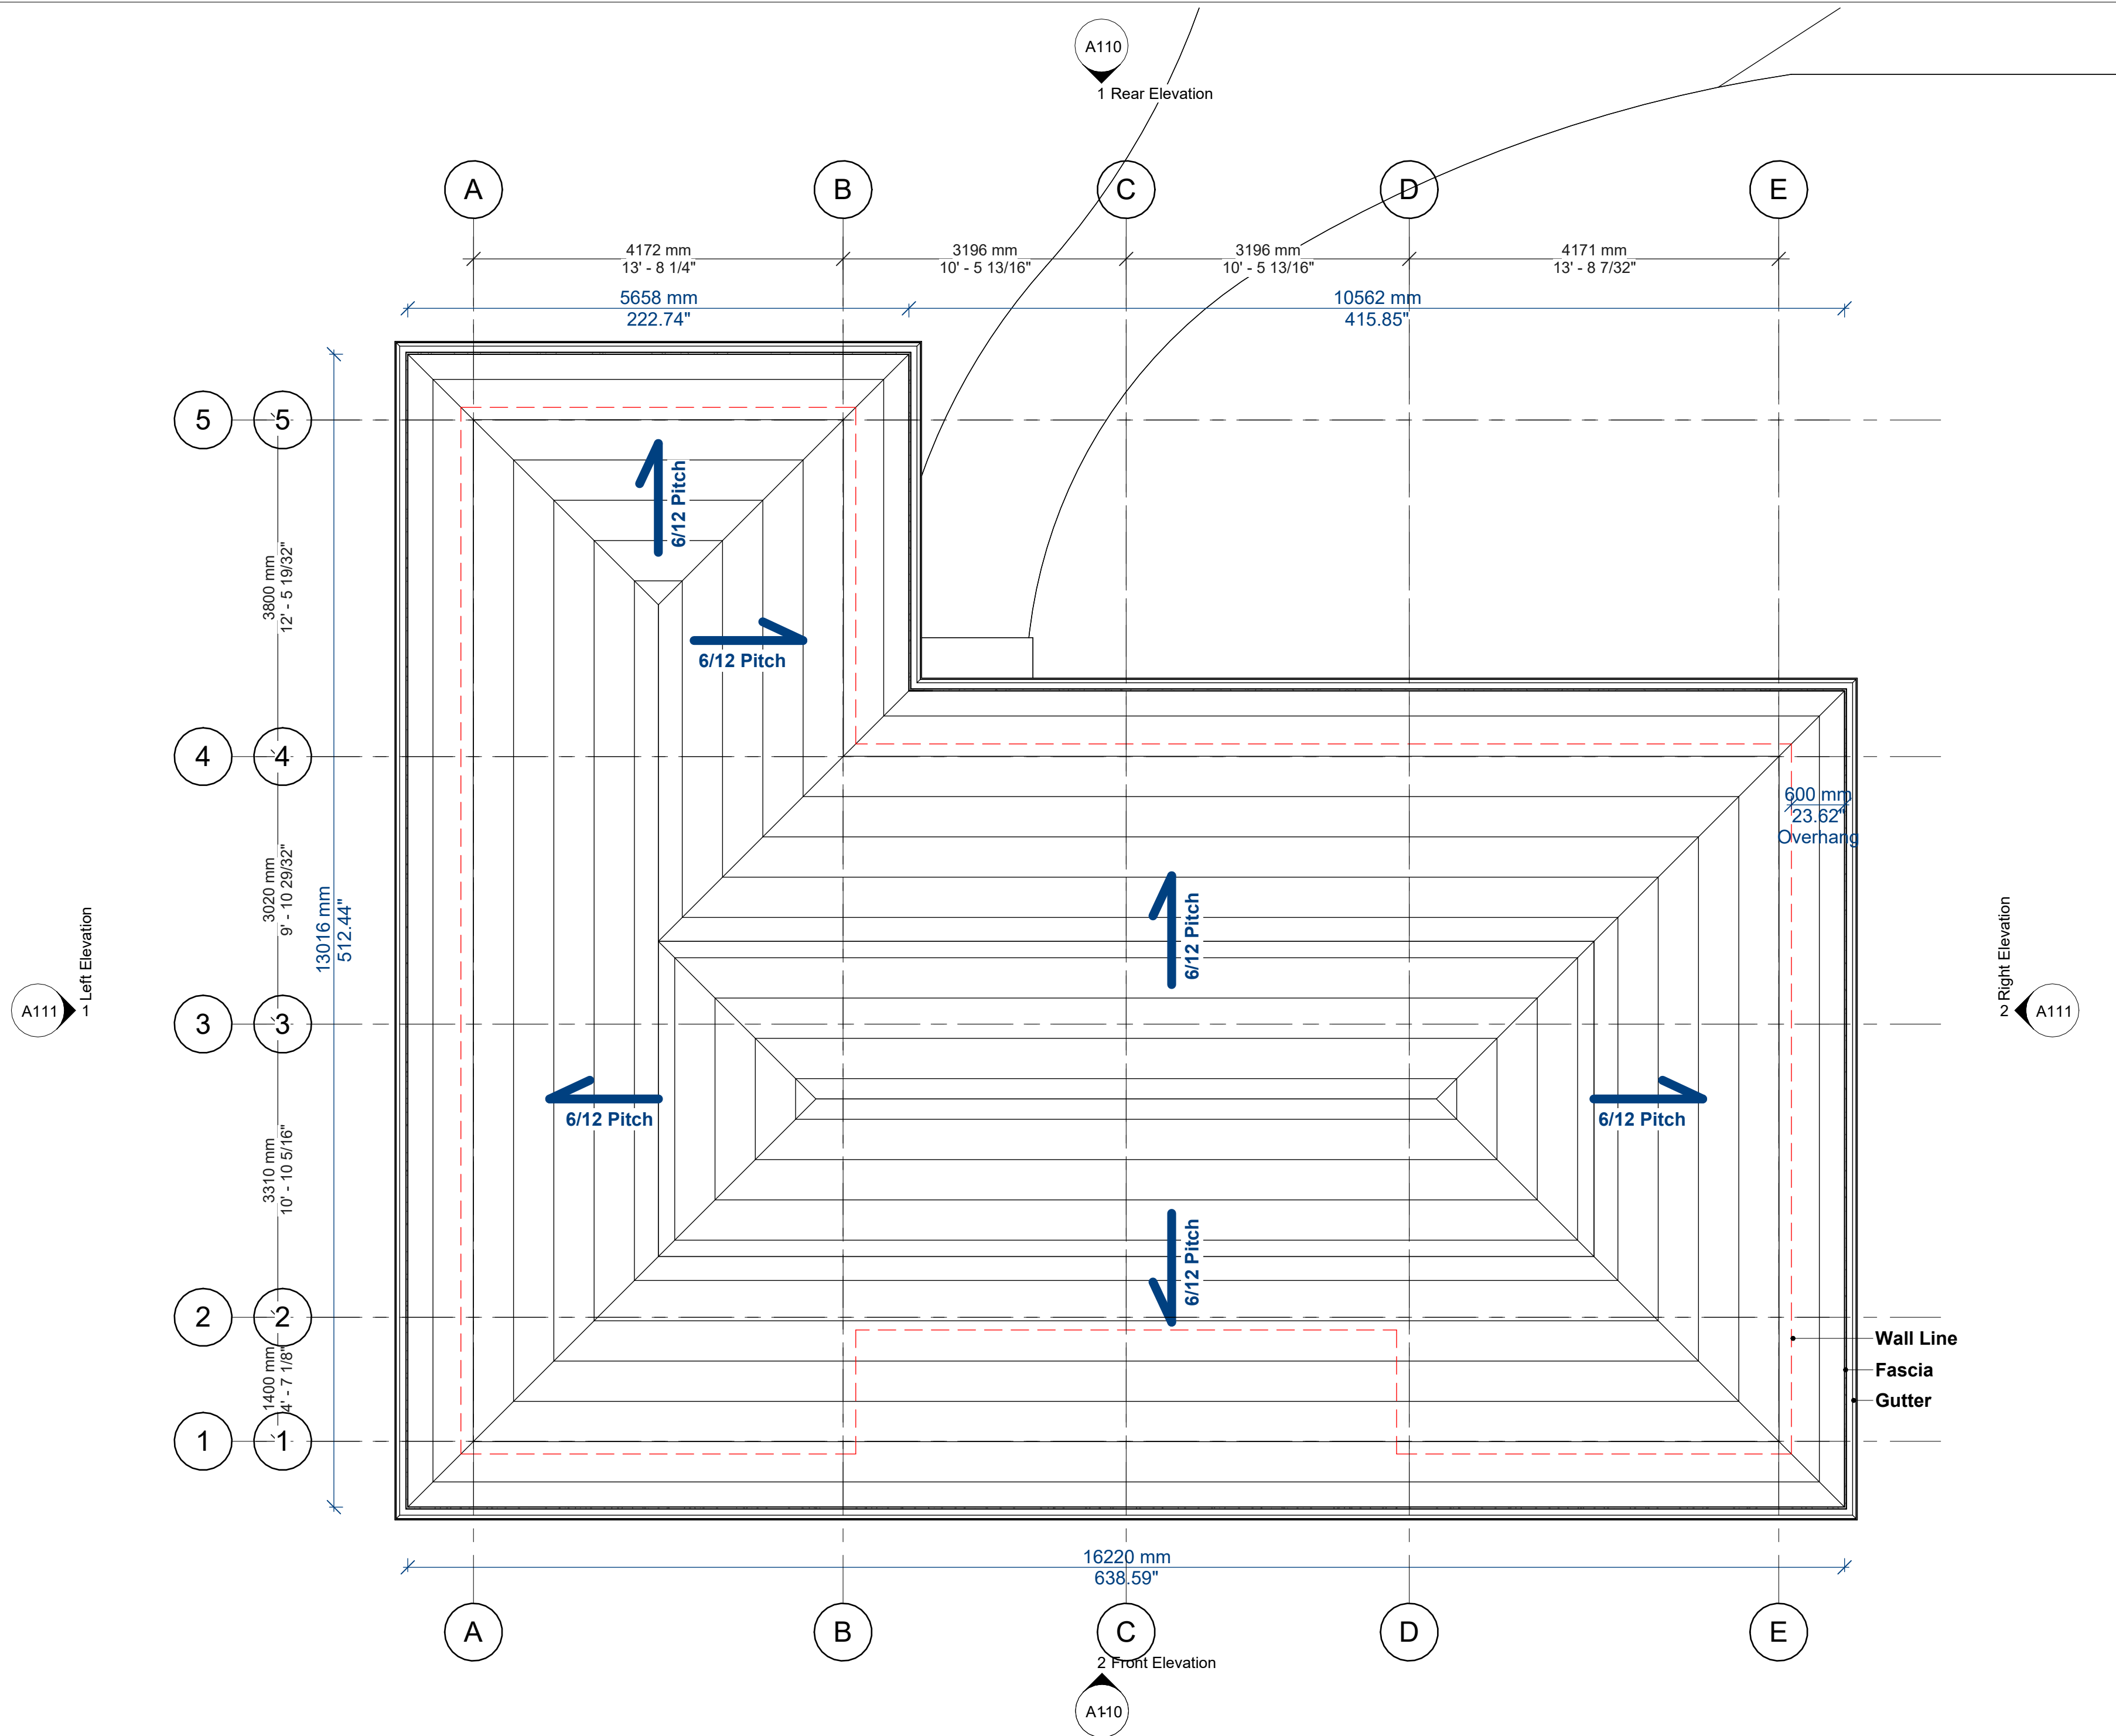

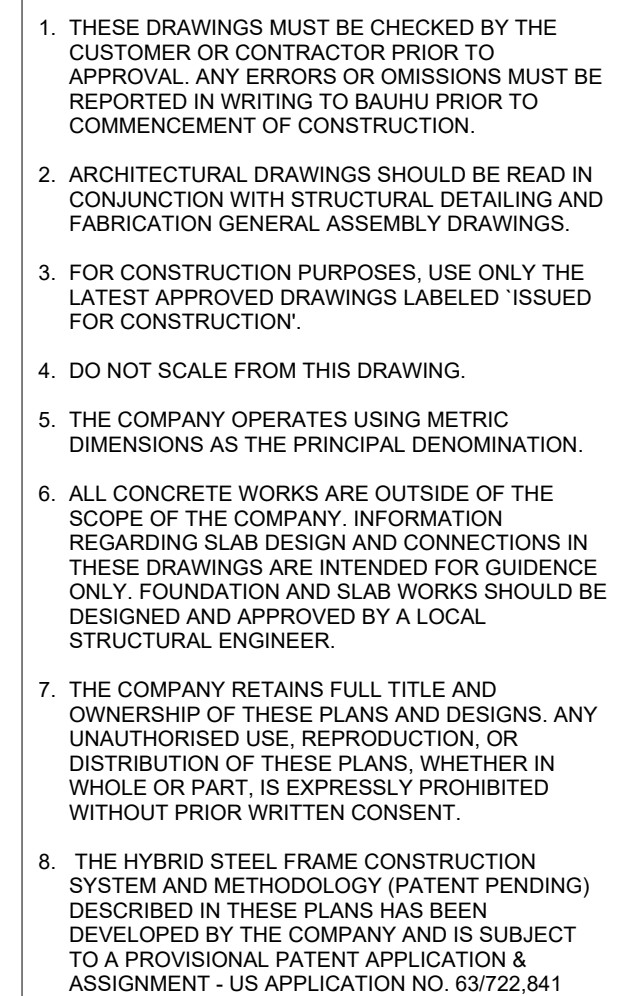[illegible]

Issued for information

Issued for client approval

Issued for fabrication

Issued for construction

Coconut Villa 3 Bed

DRAWING TITLE: Sun Analysis


DRAWN BY: Y.A.Clark


SCALE:

DRAWING NO:

A108

DATE: 16/02/2026

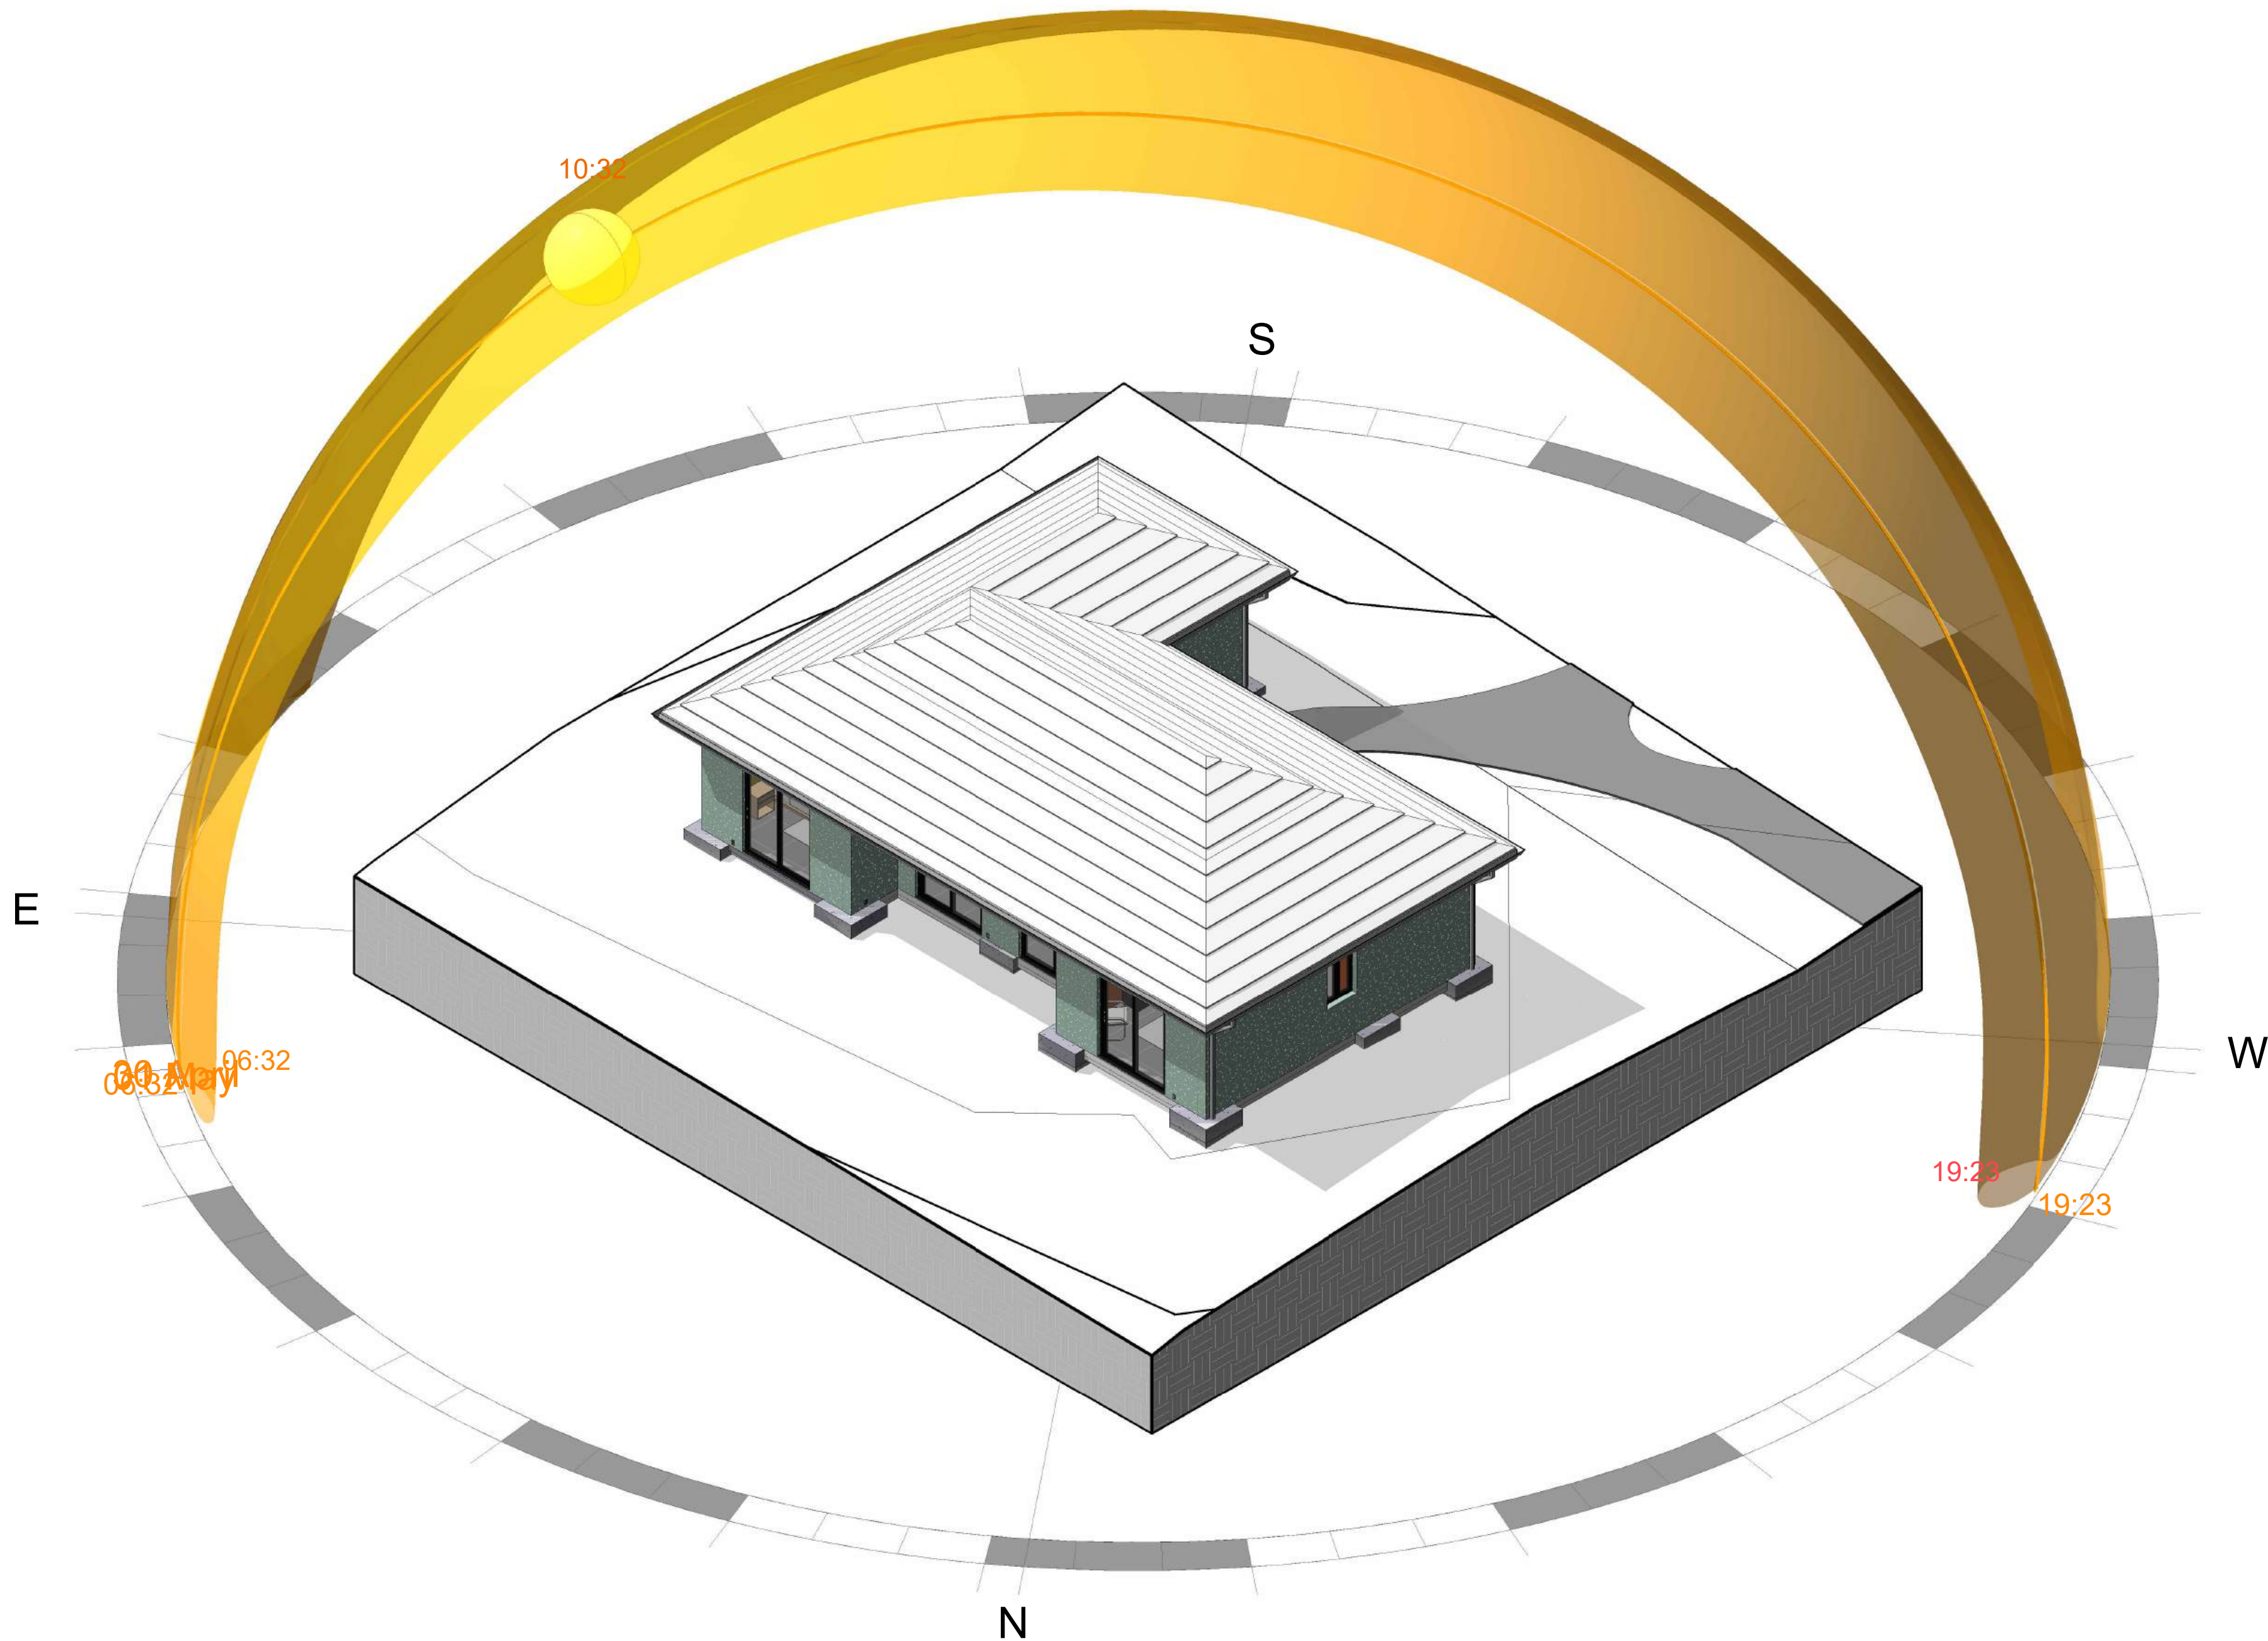

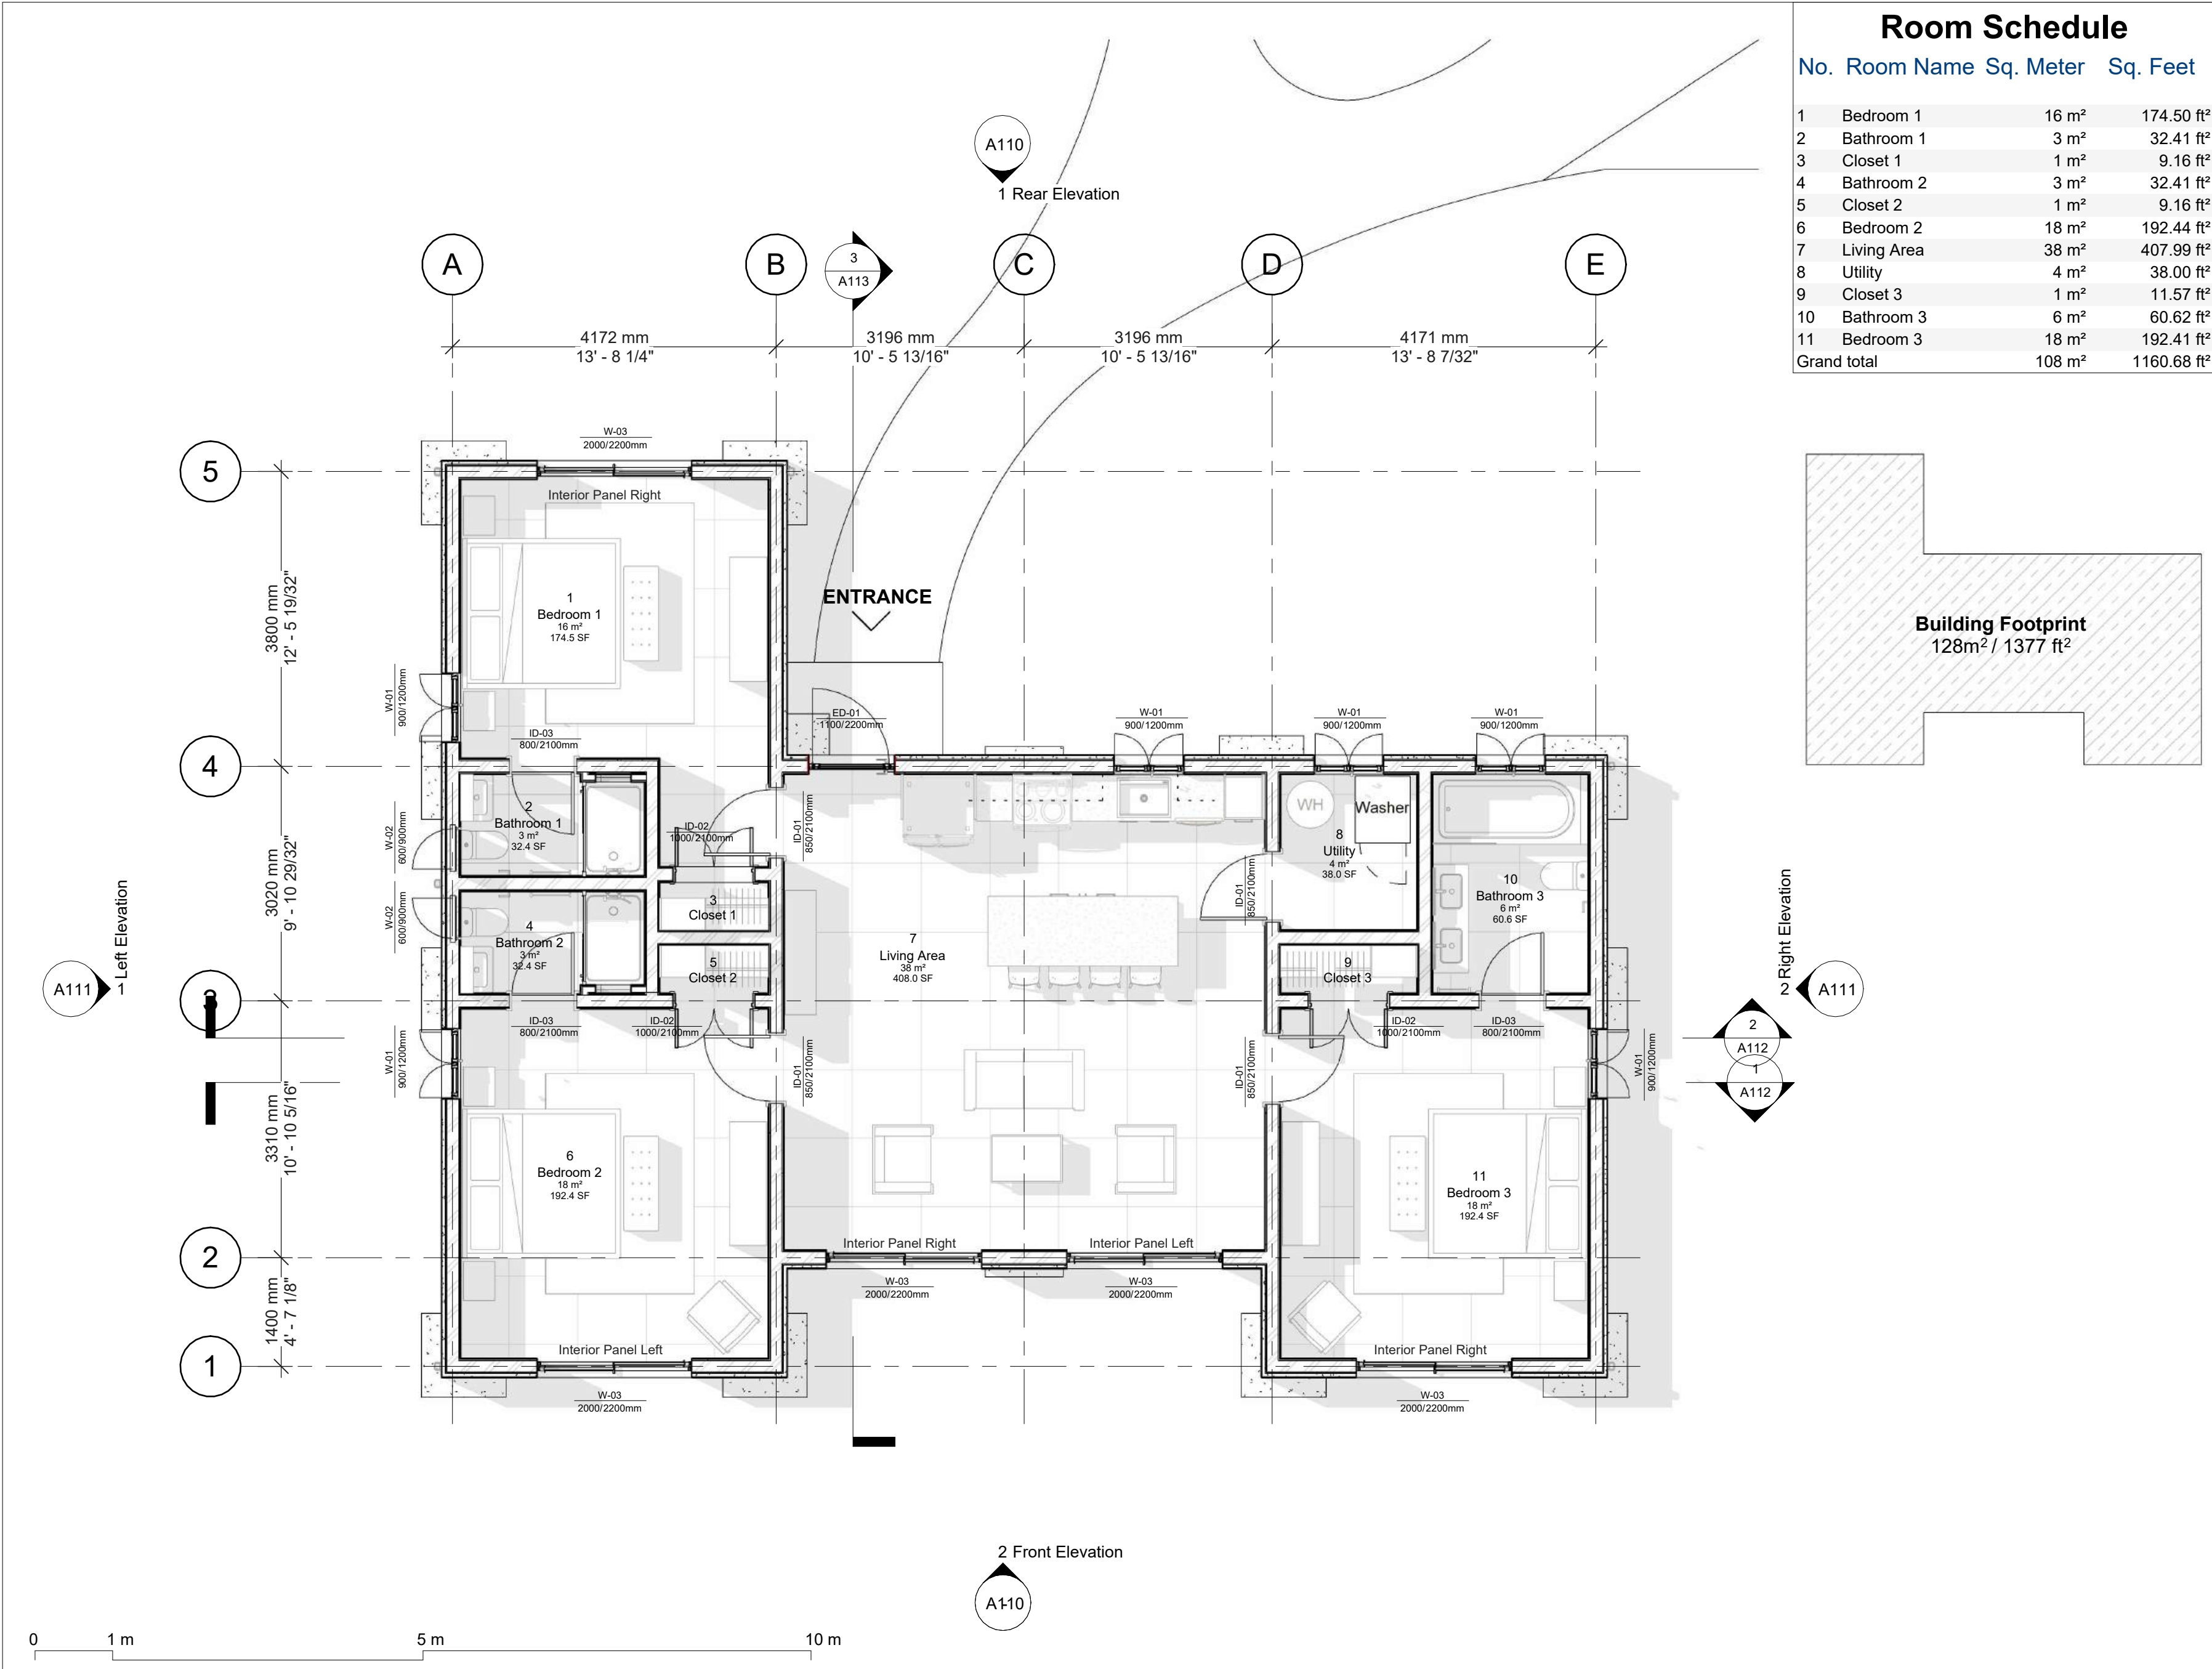

Room Schedule			
No.	Room Name	Sq. Meter	Sq. Feet
1	Bedroom 1	16 m ²	174.50 ft ²
2	Bathroom 1	3 m ²	32.41 ft ²
3	Closet 1	1 m ²	9.16 ft ²
4	Bathroom 2	3 m ²	32.41 ft ²
5	Closet 2	1 m ²	9.16 ft ²
6	Bedroom 2	18 m ²	192.44 ft ²
7	Living Area	38 m ²	407.99 ft ²
8	Utility	4 m ²	38.00 ft ²
9	Closet 3	1 m ²	11.57 ft ²
10	Bathroom 3	6 m ²	60.62 ft ²
11	Bedroom 3	18 m ²	192.41 ft ²
Grand total		108 m ²	1160.68 ft ²

- THESE DRAWINGS MUST BE CHECKED BY THE CUSTOMER OR CONTRACTOR PRIOR TO APPROVAL. ANY ERRORS OR OMISSIONS MUST BE REPORTED IN WRITING TO BAUHU PRIOR TO COMMENCEMENT OF CONSTRUCTION.
- ARCHITECTURAL DRAWINGS SHOULD BE READ IN CONJUNCTION WITH STRUCTURAL DETAILING AND FABRICATION GENERAL ASSEMBLY DRAWINGS.
- FOR CONSTRUCTION PURPOSES, USE ONLY THE LATEST APPROVED DRAWINGS LABELED 'ISSUED FOR CONSTRUCTION'.
- DO NOT SCALE FROM THIS DRAWING.
- THE COMPANY OPERATES USING METRIC DIMENSIONS AS THE PRINCIPAL DENOMINATION.
- ALL CONCRETE WORKS ARE OUTSIDE OF THE SCOPE OF THE COMPANY. INFORMATION REGARDING SLAB DESIGN AND CONNECTIONS IN THESE DRAWINGS ARE INTENDED FOR GUIDANCE ONLY. FOUNDATION AND SLAB WORKS SHOULD BE DESIGNED AND APPROVED BY A LOCAL STRUCTURAL ENGINEER.
- THE COMPANY RETAINS FULL TITLE AND OWNERSHIP OF THESE PLANS AND DESIGNS. ANY UNAUTHORISED USE, REPRODUCTION, OR DISTRIBUTION OF THESE PLANS, WHETHER IN WHOLE OR PART, IS EXPRESSLY PROHIBITED WITHOUT PRIOR WRITTEN CONSENT.
- THE HYBRID STEEL FRAME CONSTRUCTION SYSTEM AND METHODOLOGY (PATENT PENDING) DESCRIBED IN THESE PLANS HAS BEEN DEVELOPED BY THE COMPANY AND IS SUBJECT TO A PROVISIONAL PATENT APPLICATION & ASSIGNMENT - US APPLICATION NO. 63/722,841

No.	Revision	Date

ISSUED FOR:

☐ Issued for information

☐ Issued for client approval

☐ Issued for fabrication

☐ Issued for construction

Coconut Villa 3 Bed

DRAWING TITLE:

Ground Floor Plan

DRAWN BY:

Y.A.Clark

SCALE:

1 : 60

DRAWING NO:

A109

DATE:

16/02/2026

Note:

- Freestanding furniture and equipment are shown for illustrative purposes only. Renderings and reference images are for guidance only.
- Artisanal timber and carpentry requirements such as fretwork, architectural timber finishes, baseboards, decorative railings, deck and pergola structures, shade louvres, interior stairs and hand railing are to be provided by others.
- Railings and balustrades will be provided by others. Drawings are made for design purposes only. Refer to structural design drawings for post fixing dimensions.
- External HRS columns will be provided assuming a 50mm (2") height drop between interior concrete slab and exterior terrace concrete slab unless site conditions dictate otherwise.
- Final exterior slab height to be determined by the contractor. Internal floor screed and waterproofing membrane is to be supplied by the contractor.
- Contractors should ensure a correct fall is applied to external tiled terrace areas to facilitate rainwater drainage.
- Contractors should read these drawings in conjunction with structural engineering design drawings.

1. THESE DRAWINGS MUST BE CHECKED BY THE CUSTOMER OR CONTRACTOR PRIOR TO APPROVAL. ANY ERRORS OR OMISSIONS MUST BE REPORTED IN WRITING TO BAUHU PRIOR TO COMMENCEMENT OF CONSTRUCTION.
2. ARCHITECTURAL DRAWINGS SHOULD BE READ IN CONJUNCTION WITH STRUCTURAL DETAILING AND FABRICATION GENERAL ASSEMBLY DRAWINGS.
3. FOR CONSTRUCTION PURPOSES, USE ONLY THE LATEST APPROVED DRAWINGS LABELED 'ISSUED FOR CONSTRUCTION'.
4. DO NOT SCALE FROM THIS DRAWING.
5. THE COMPANY OPERATES USING METRIC DIMENSIONS AS THE PRINCIPAL DENOMINATION.
6. ALL CONCRETE WORKS ARE OUTSIDE OF THE SCOPE OF THE COMPANY. INFORMATION REGARDING SLAB DESIGN AND CONNECTIONS IN THESE DRAWINGS ARE INTENDED FOR GUIDANCE ONLY. FOUNDATION AND SLAB WORKS SHOULD BE DESIGNED AND APPROVED BY A LOCAL STRUCTURAL ENGINEER.
7. THE COMPANY RETAINS FULL TITLE AND OWNERSHIP OF THESE PLANS AND DESIGNS. ANY UNAUTHORISED USE, REPRODUCTION, OR DISTRIBUTION OF THESE PLANS, WHETHER IN WHOLE OR PART, IS EXPRESSLY PROHIBITED WITHOUT PRIOR WRITTEN CONSENT.
8. THE HYBRID STEEL FRAME CONSTRUCTION SYSTEM AND METHODOLOGY (PATENT PENDING) DESCRIBED IN THESE PLANS HAS BEEN DEVELOPED BY THE COMPANY AND IS SUBJECT TO A PROVISIONAL PATENT APPLICATION & ASSIGNMENT - US APPLICATION NO. 63/722,841

No.	Revision	Date

ISSUED FOR:

- ☒ Issued for information
☐ Issued for client approval
☐ Issued for fabrication
☐ Issued for construction

Coconut Villa
3 Bed

DRAWING TITLE:

Front&Rear Elevation

DRAWN BY:

Y.A.Clark

SCALE:


1 : 50

DRAWING NO:

A110


DATE:

16/02/2026

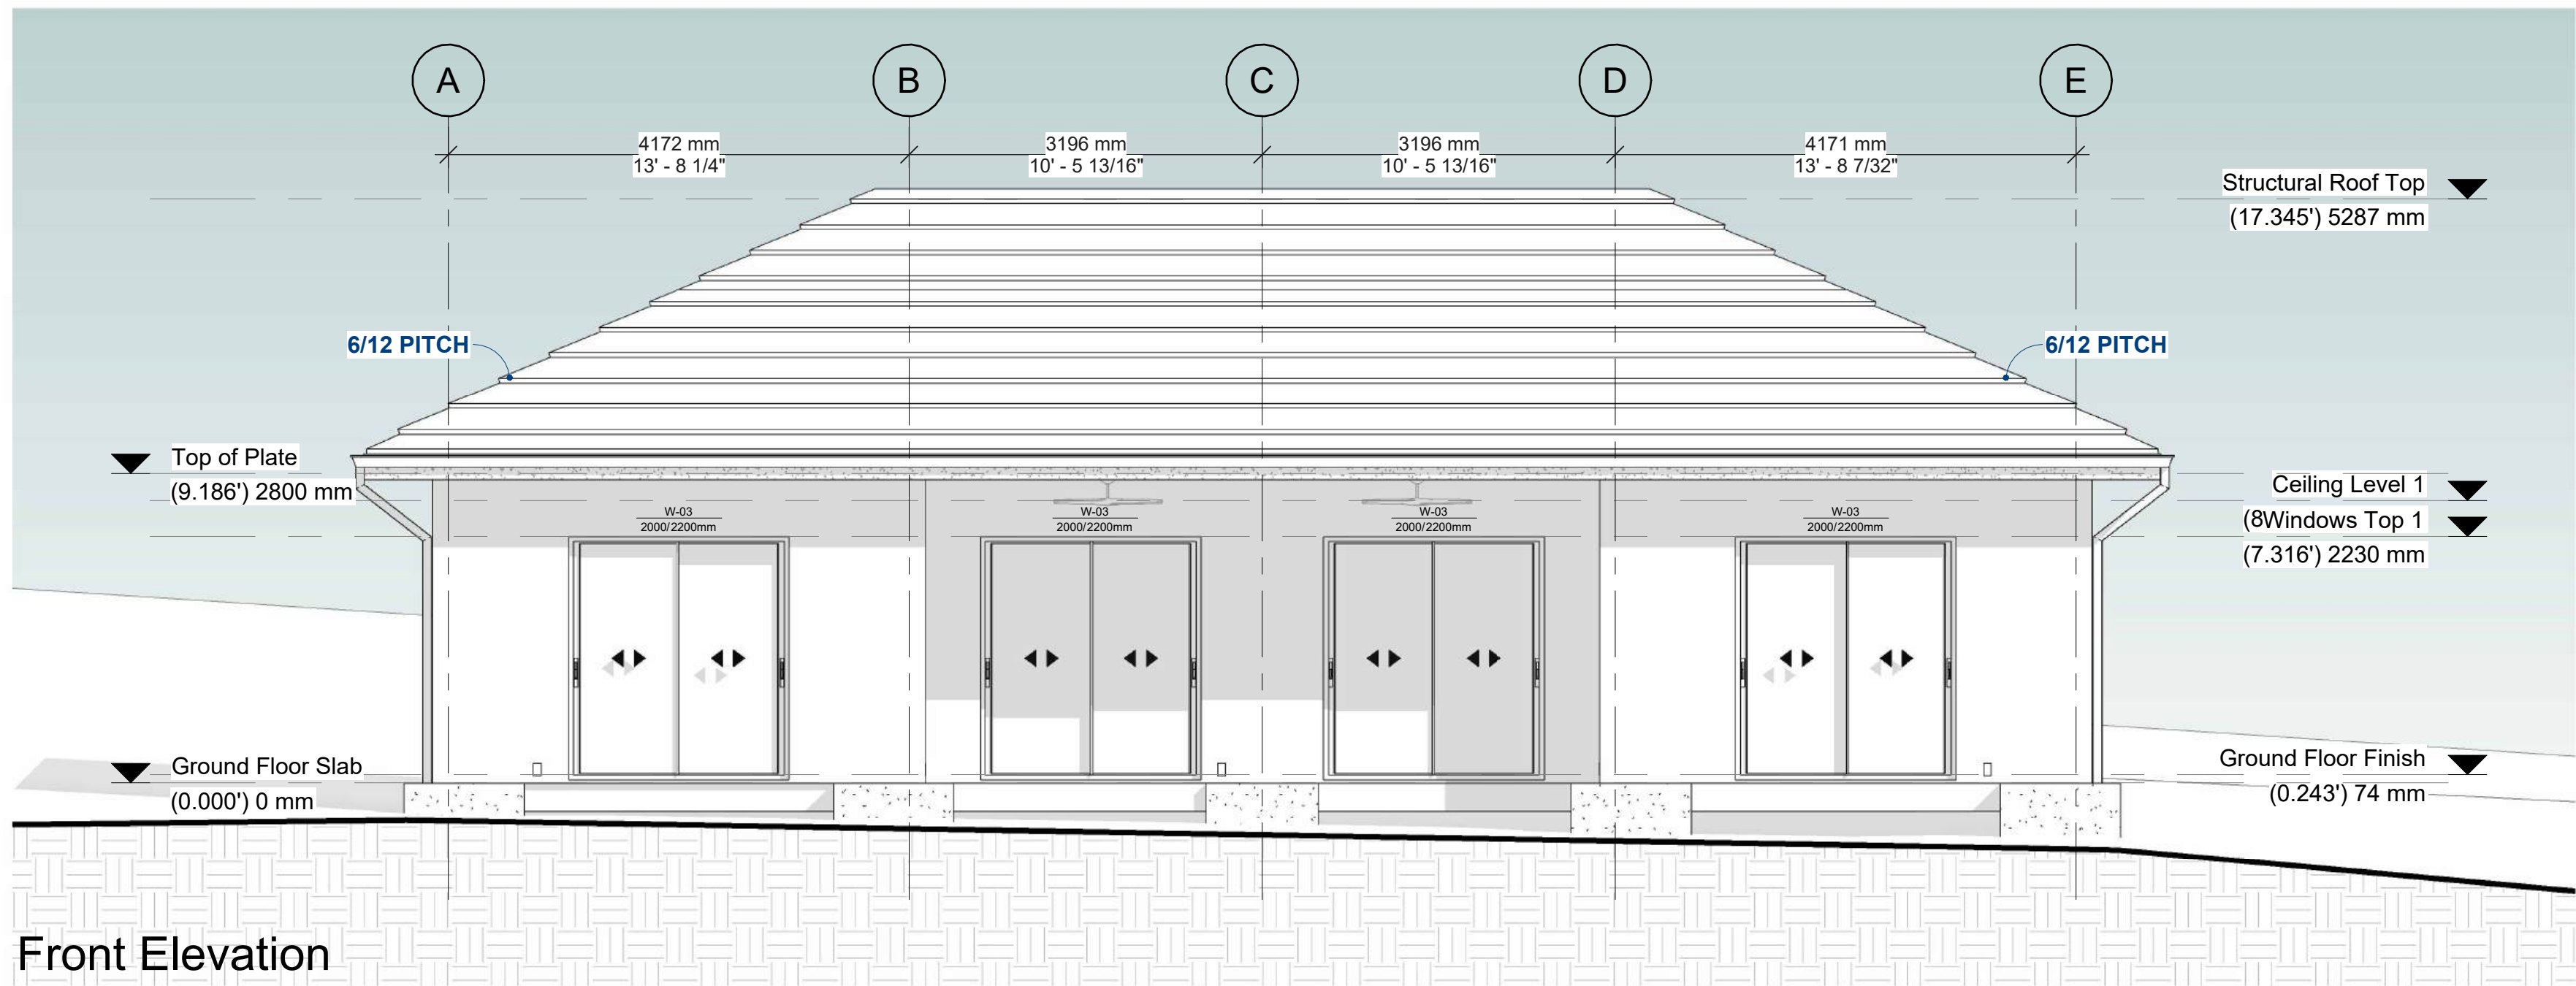

Front Elevation

1 : 50

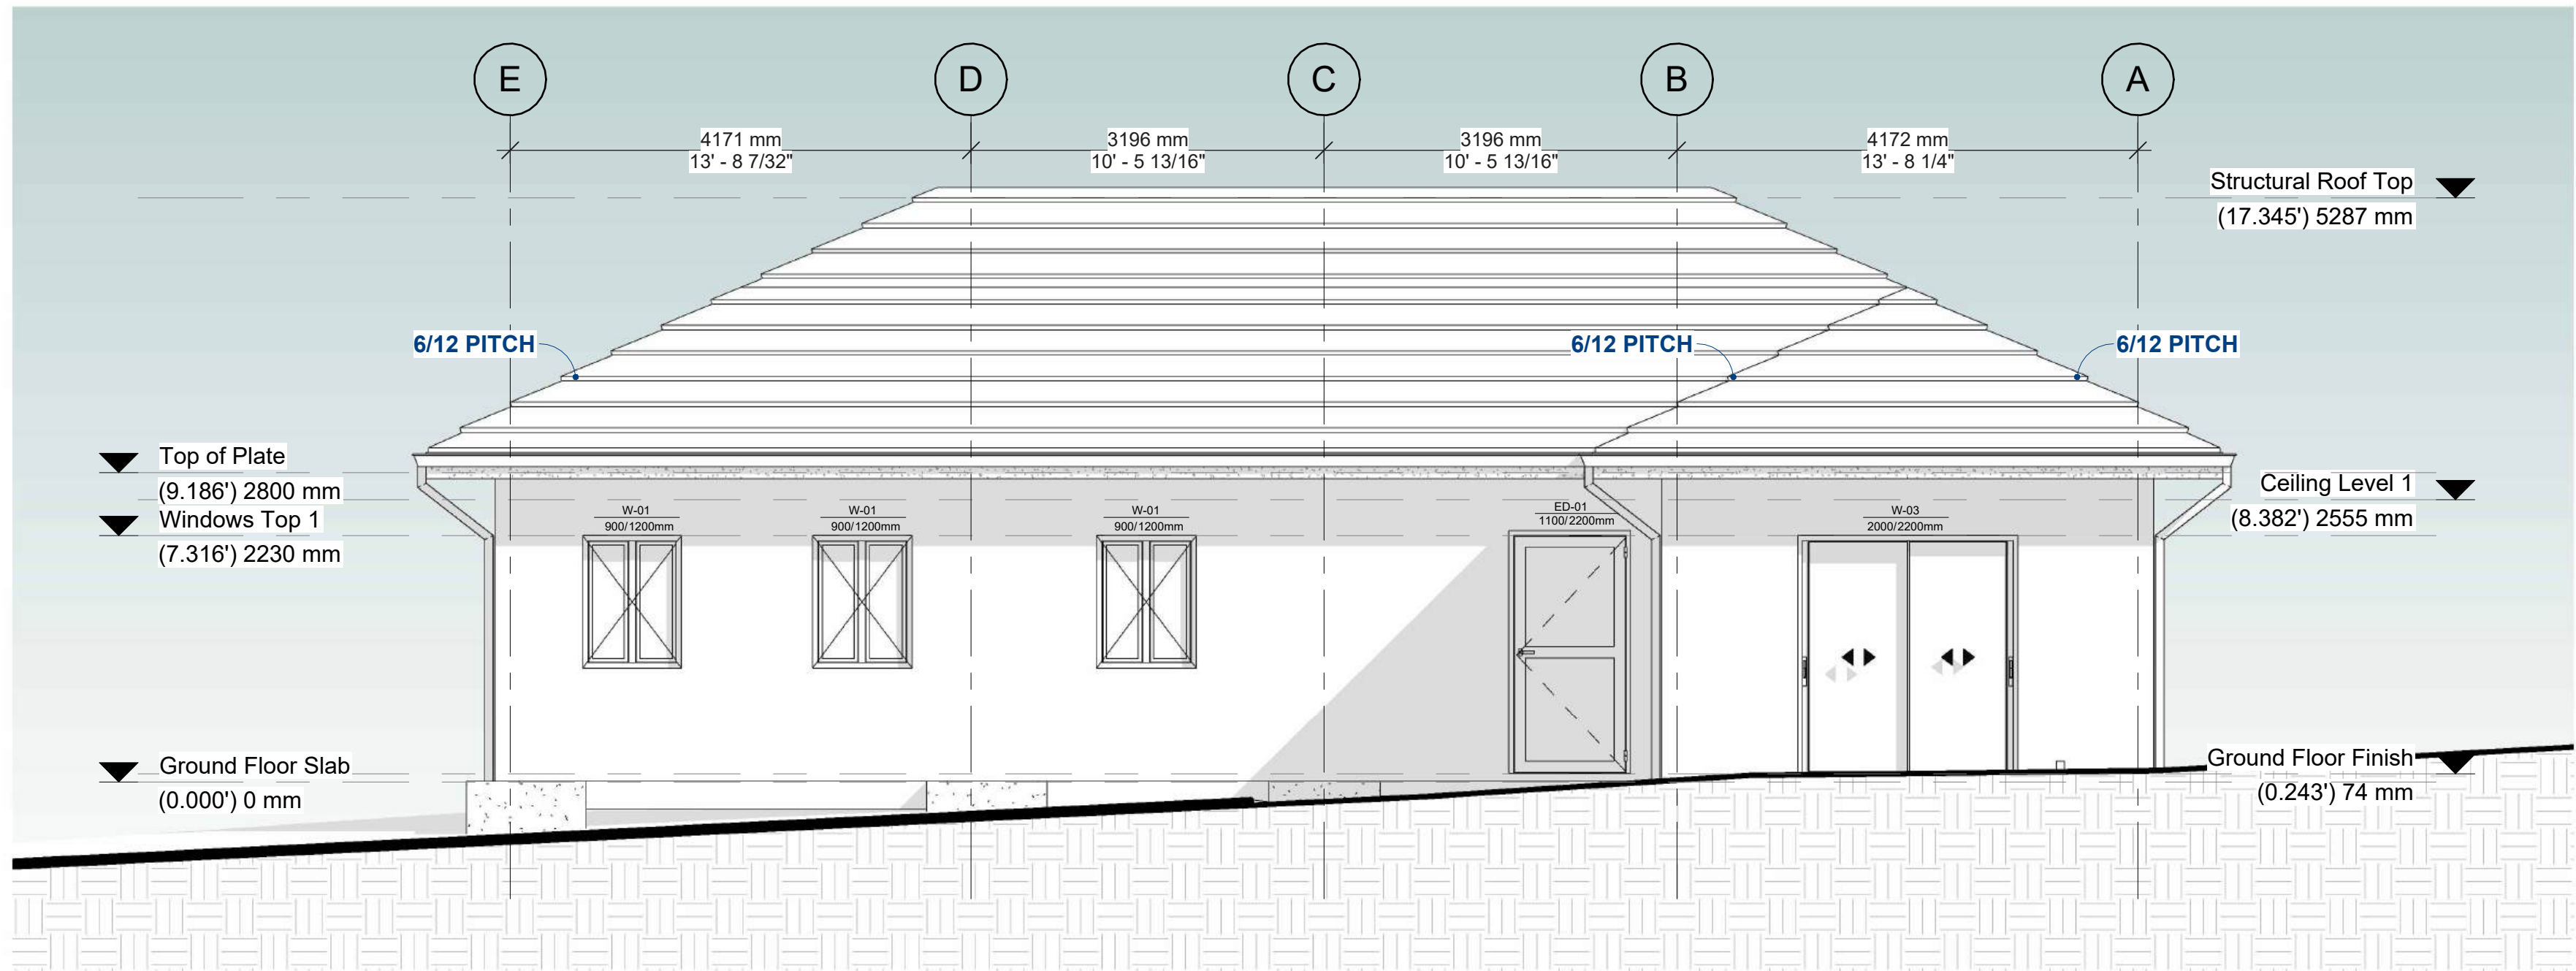

Rear Elevation

1 : 50

1. THESE DRAWINGS MUST BE CHECKED BY THE CUSTOMER OR CONTRACTOR PRIOR TO APPROVAL. ANY ERRORS OR OMISSIONS MUST BE REPORTED IN WRITING TO BAUHU PRIOR TO COMMENCEMENT OF CONSTRUCTION.
2. ARCHITECTURAL DRAWINGS SHOULD BE READ IN CONJUNCTION WITH STRUCTURAL DETAILING AND FABRICATION GENERAL ASSEMBLY DRAWINGS.
3. FOR CONSTRUCTION PURPOSES, USE ONLY THE LATEST APPROVED DRAWINGS LABELED 'ISSUED FOR CONSTRUCTION'.
4. DO NOT SCALE FROM THIS DRAWING.
5. THE COMPANY OPERATES USING METRIC DIMENSIONS AS THE PRINCIPAL DENOMINATION.
6. ALL CONCRETE WORKS ARE OUTSIDE OF THE SCOPE OF THE COMPANY. INFORMATION REGARDING SLAB DESIGN AND CONNECTIONS IN THESE DRAWINGS ARE INTENDED FOR GUIDANCE ONLY. FOUNDATION AND SLAB WORKS SHOULD BE DESIGNED AND APPROVED BY A LOCAL STRUCTURAL ENGINEER.
7. THE COMPANY RETAINS FULL TITLE AND OWNERSHIP OF THESE PLANS AND DESIGNS. ANY UNAUTHORISED USE, REPRODUCTION, OR DISTRIBUTION OF THESE PLANS, WHETHER IN WHOLE OR PART, IS EXPRESSLY PROHIBITED WITHOUT PRIOR WRITTEN CONSENT.
8. THE HYBRID STEEL FRAME CONSTRUCTION SYSTEM AND METHODOLOGY (PATENT PENDING) DESCRIBED IN THESE PLANS HAS BEEN DEVELOPED BY THE COMPANY AND IS SUBJECT TO A PROVISIONAL PATENT APPLICATION & ASSIGNMENT - US APPLICATION NO. 63/722,841

No.	Revision	Date

ISSUED FOR:

Issued for information

Issued for client approval

Issued for fabrication

Issued for construction

Coconut Villa
3 Bed

DRAWING TITLE:

Left&Right Elevation

DRAWN BY:

Y.A.Clark

SCALE:


1 : 50

DRAWING NO:


A111

DATE:

16/02/2026

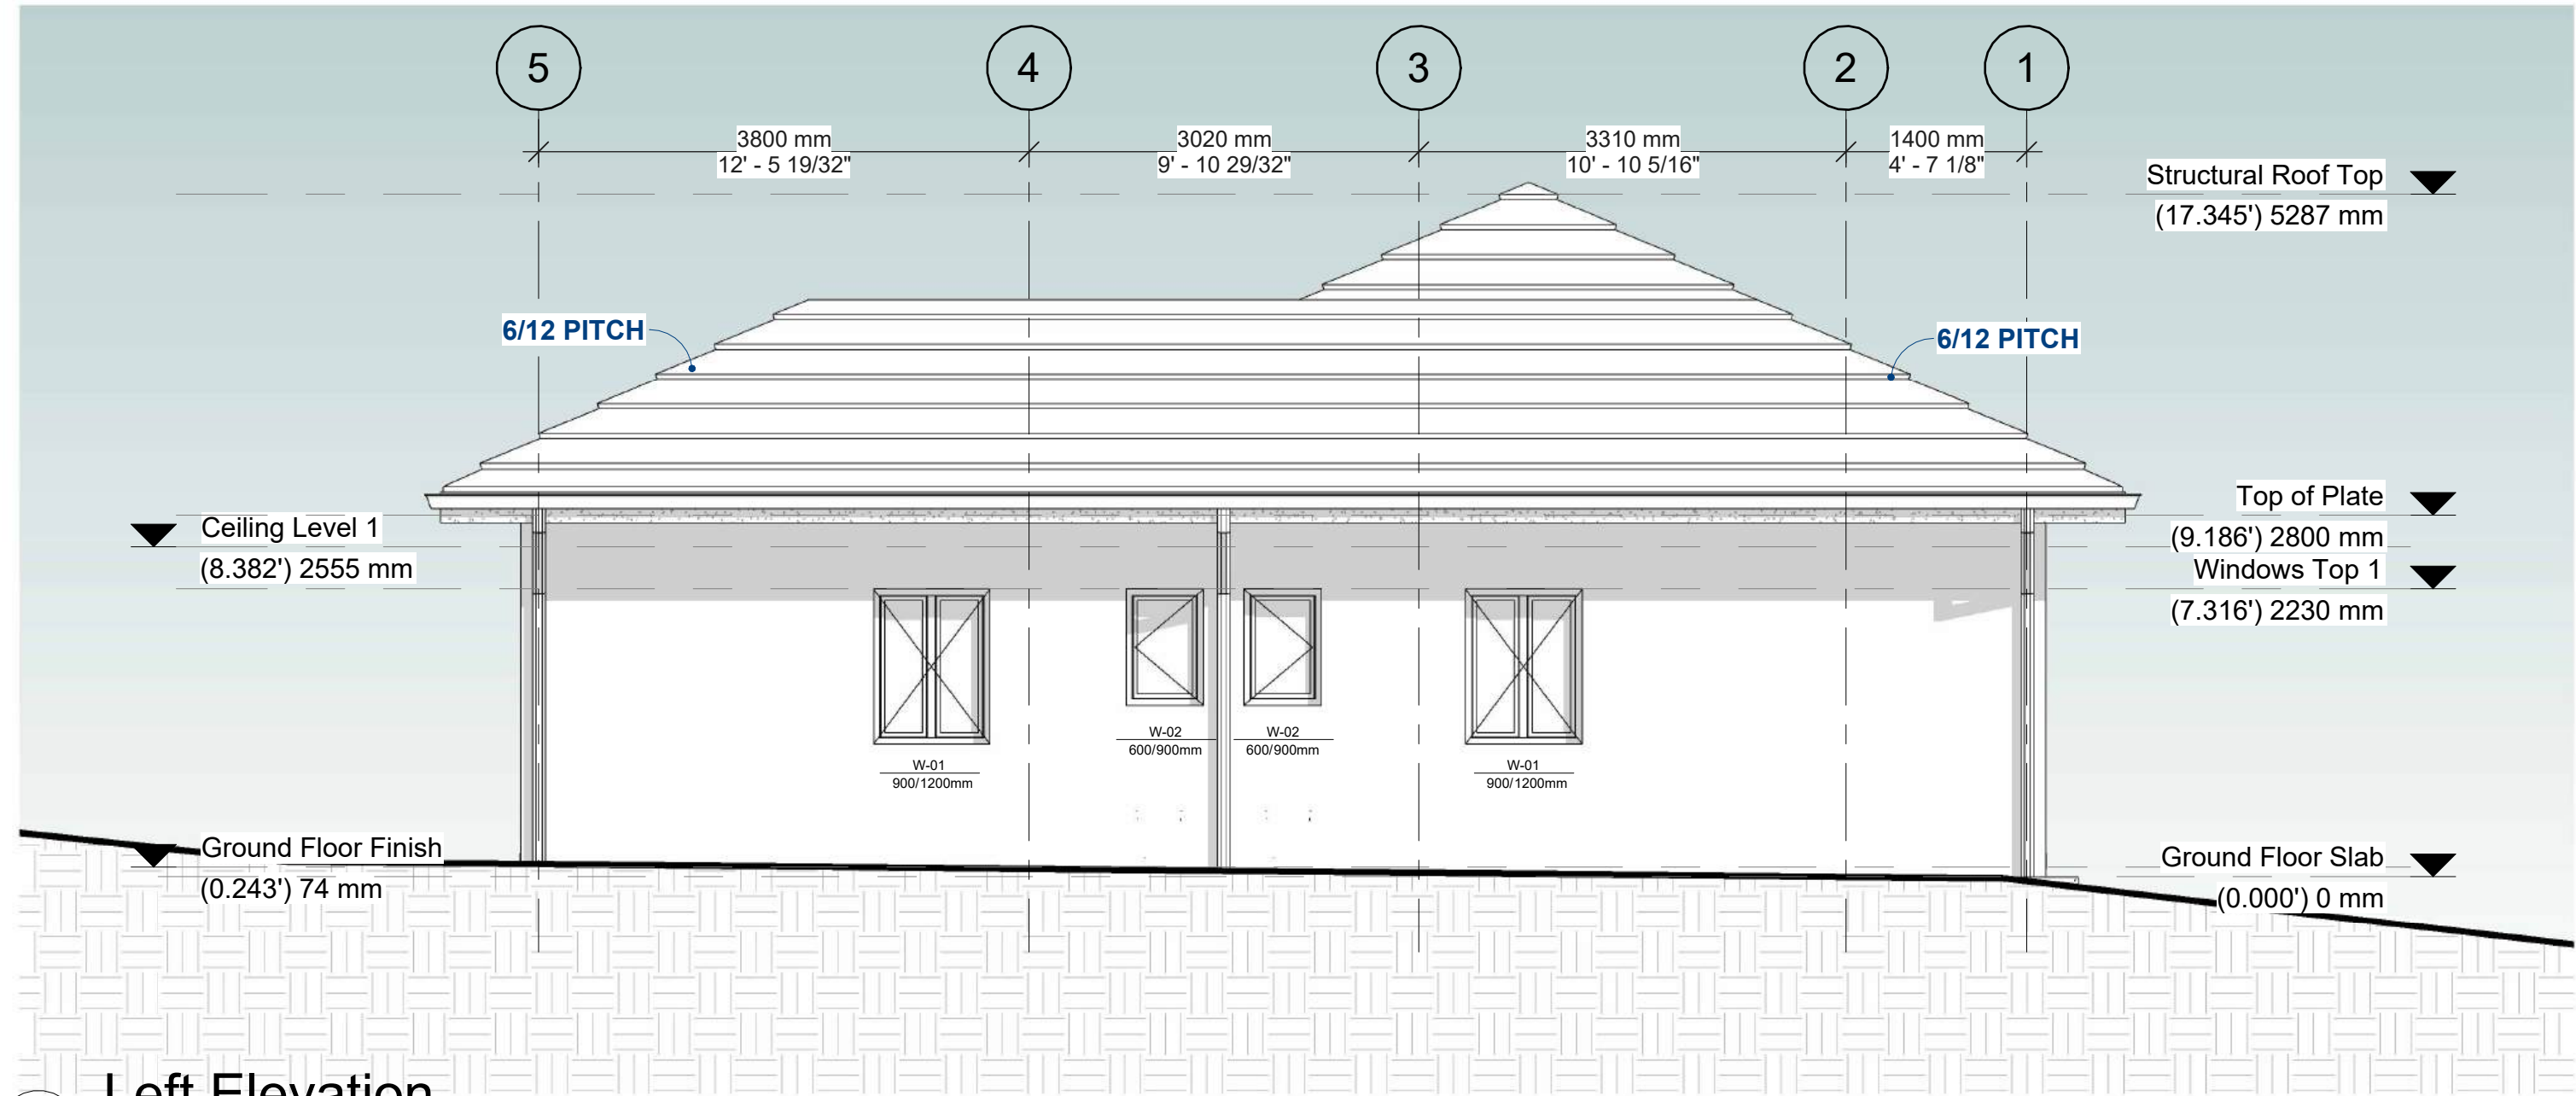

1 Left Elevation
1 : 50

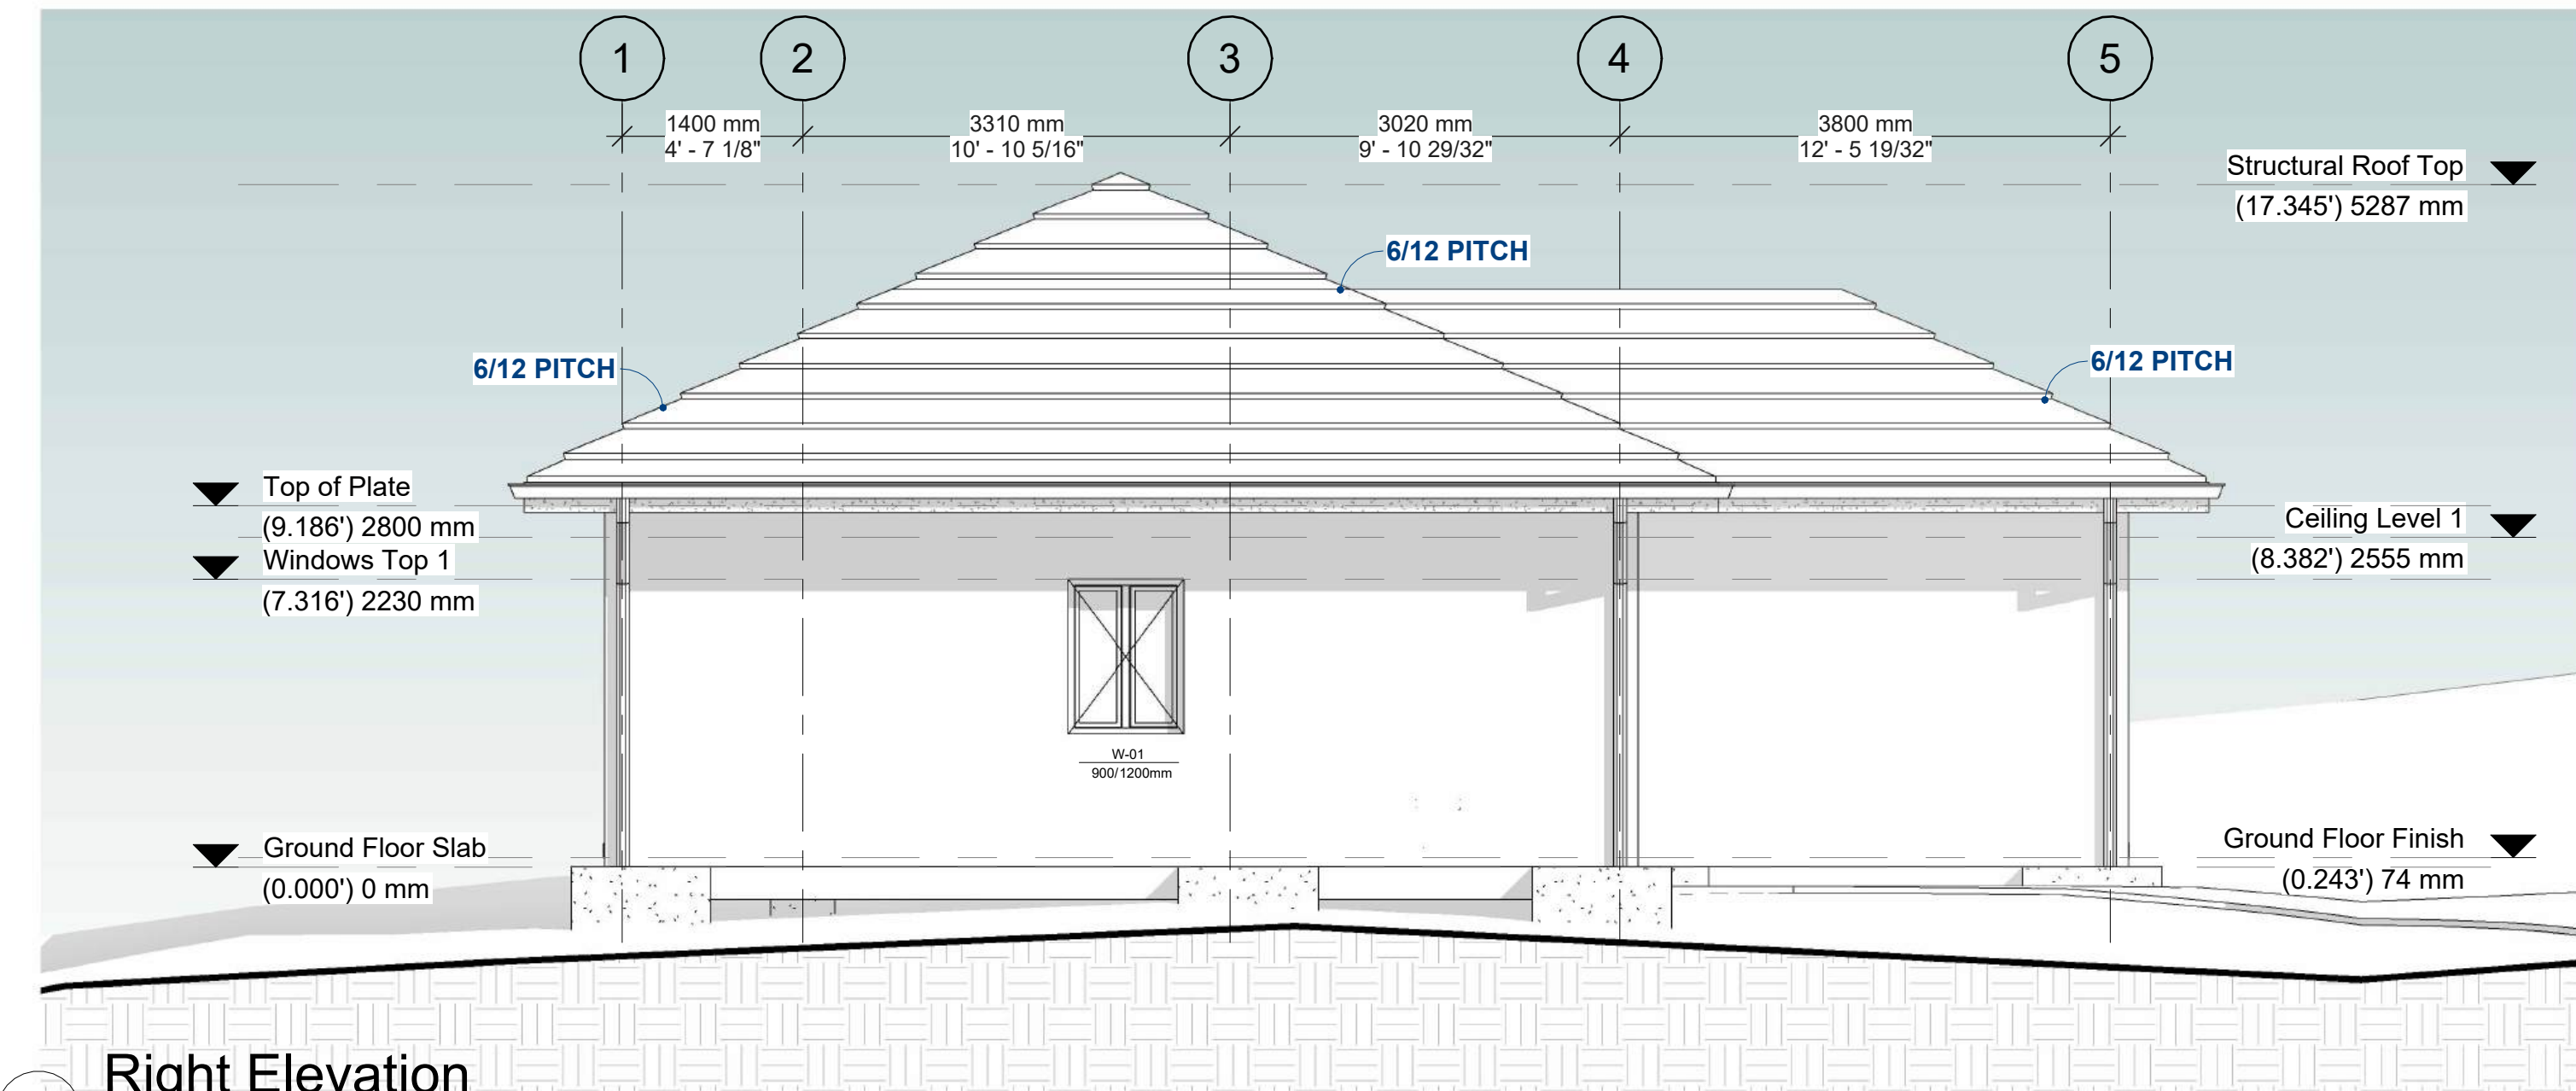

2 Right Elevation
1 : 50

1. THESE DRAWINGS MUST BE CHECKED BY THE CUSTOMER OR CONTRACTOR PRIOR TO APPROVAL. ANY ERRORS OR OMISSIONS MUST BE REPORTED IN WRITING TO BAUHU PRIOR TO COMMENCEMENT OF CONSTRUCTION.
2. ARCHITECTURAL DRAWINGS SHOULD BE READ IN CONJUNCTION WITH STRUCTURAL DETAILING AND FABRICATION GENERAL ASSEMBLY DRAWINGS.
3. FOR CONSTRUCTION PURPOSES, USE ONLY THE LATEST APPROVED DRAWINGS LABELED 'ISSUED FOR CONSTRUCTION'.
4. DO NOT SCALE FROM THIS DRAWING.
5. THE COMPANY OPERATES USING METRIC DIMENSIONS AS THE PRINCIPAL DENOMINATION.
6. ALL CONCRETE WORKS ARE OUTSIDE OF THE SCOPE OF THE COMPANY. INFORMATION REGARDING SLAB DESIGN AND CONNECTIONS IN THESE DRAWINGS ARE INTENDED FOR GUIDANCE ONLY. FOUNDATION AND SLAB WORKS SHOULD BE DESIGNED AND APPROVED BY A LOCAL STRUCTURAL ENGINEER.
7. THE COMPANY RETAINS FULL TITLE AND OWNERSHIP OF THESE PLANS AND DESIGNS. ANY UNAUTHORISED USE, REPRODUCTION, OR DISTRIBUTION OF THESE PLANS, WHETHER IN WHOLE OR PART, IS EXPRESSLY PROHIBITED WITHOUT PRIOR WRITTEN CONSENT.
8. THE HYBRID STEEL FRAME CONSTRUCTION SYSTEM AND METHODOLOGY (PATENT PENDING) DESCRIBED IN THESE PLANS HAS BEEN DEVELOPED BY THE COMPANY AND IS SUBJECT TO A PROVISIONAL PATENT APPLICATION & ASSIGNMENT - US APPLICATION NO. 63/722,841

No.	Revision	Date

ISSUED FOR:

- ☒ Issued for information
- ☐ Issued for client approval
- ☐ Issued for fabrication
- ☐ Issued for construction

Coconut Villa
3 Bed

DRAWING TITLE:

Section 1&2

DRAWN BY:

Y.A.Clark

SCALE:


1 : 50

DRAWING NO:

A112


DATE:

16/02/2026

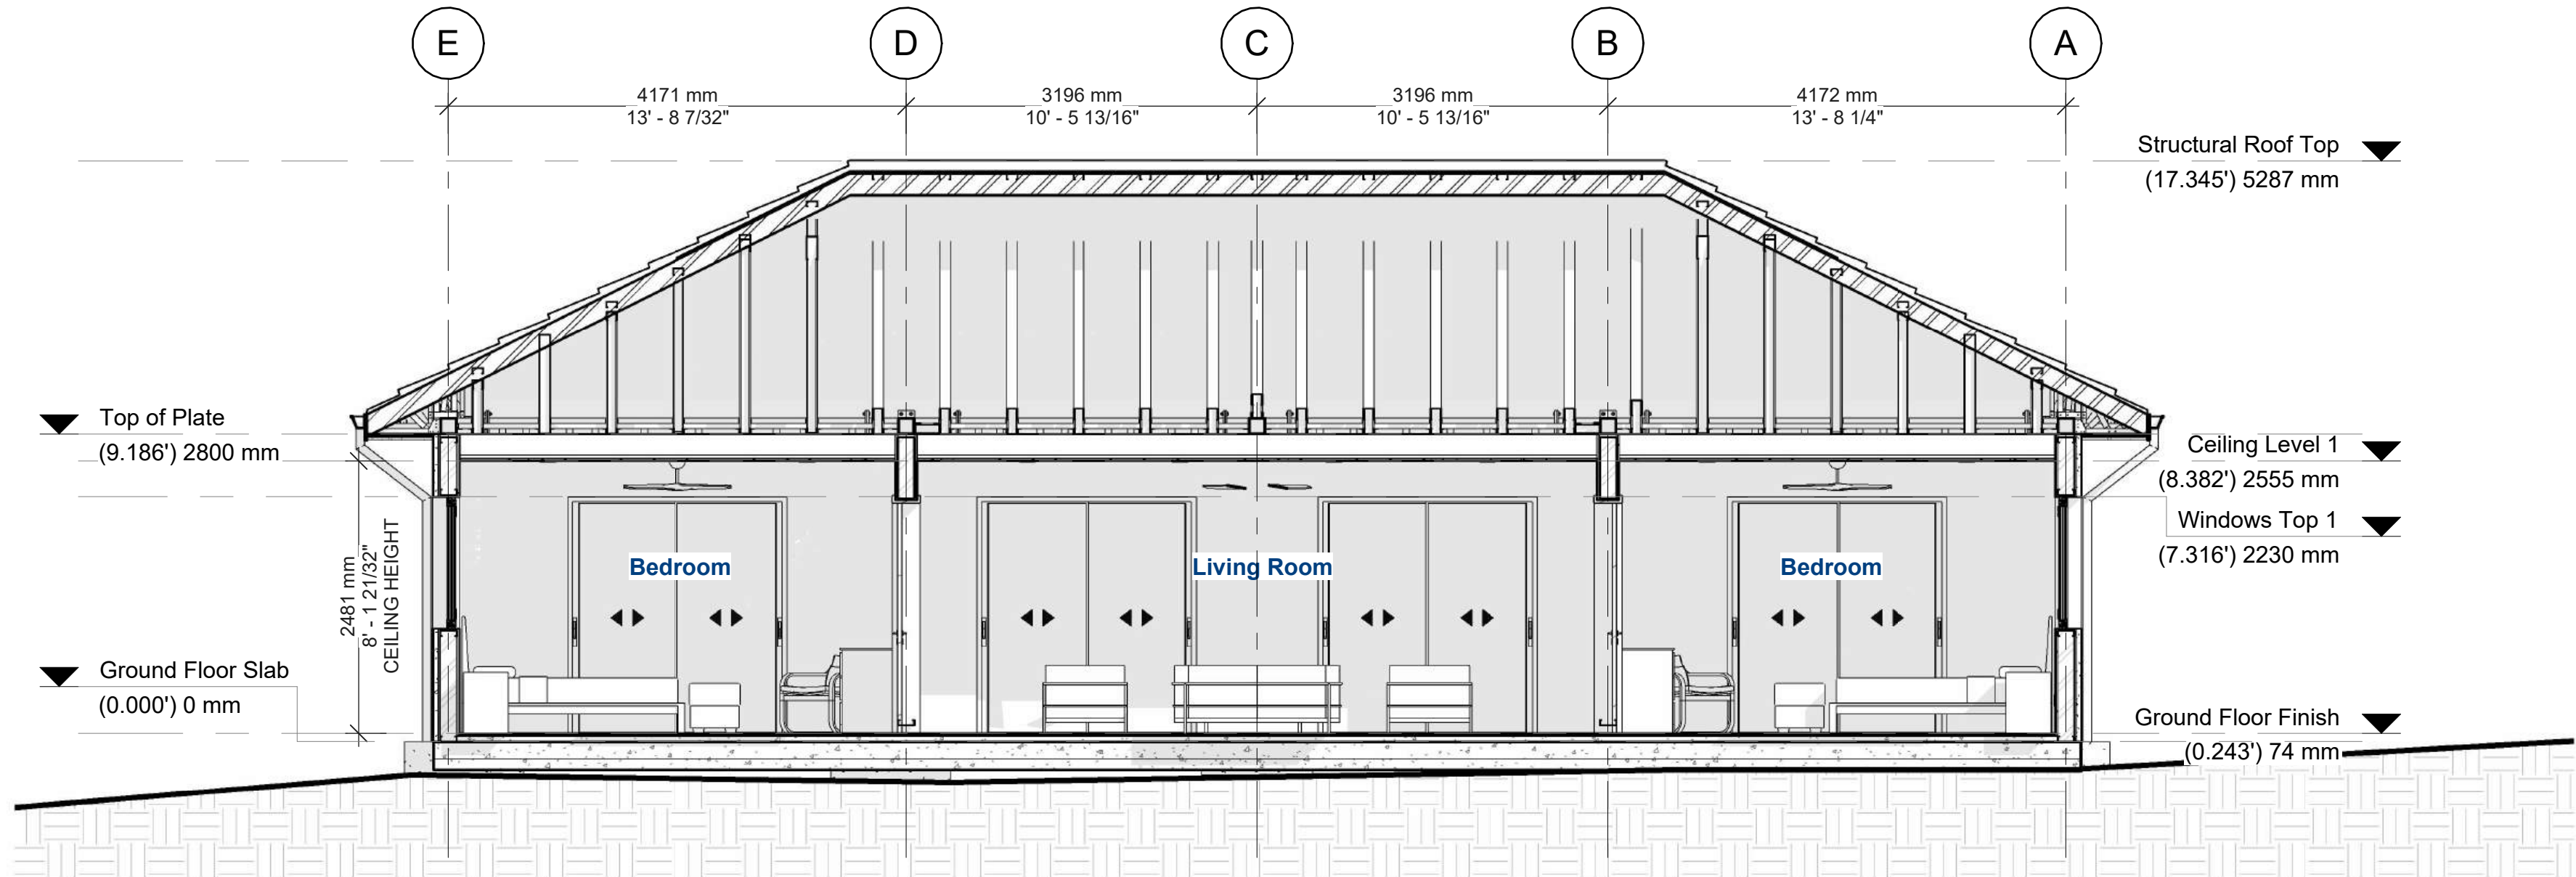

Section 1


1 : 50

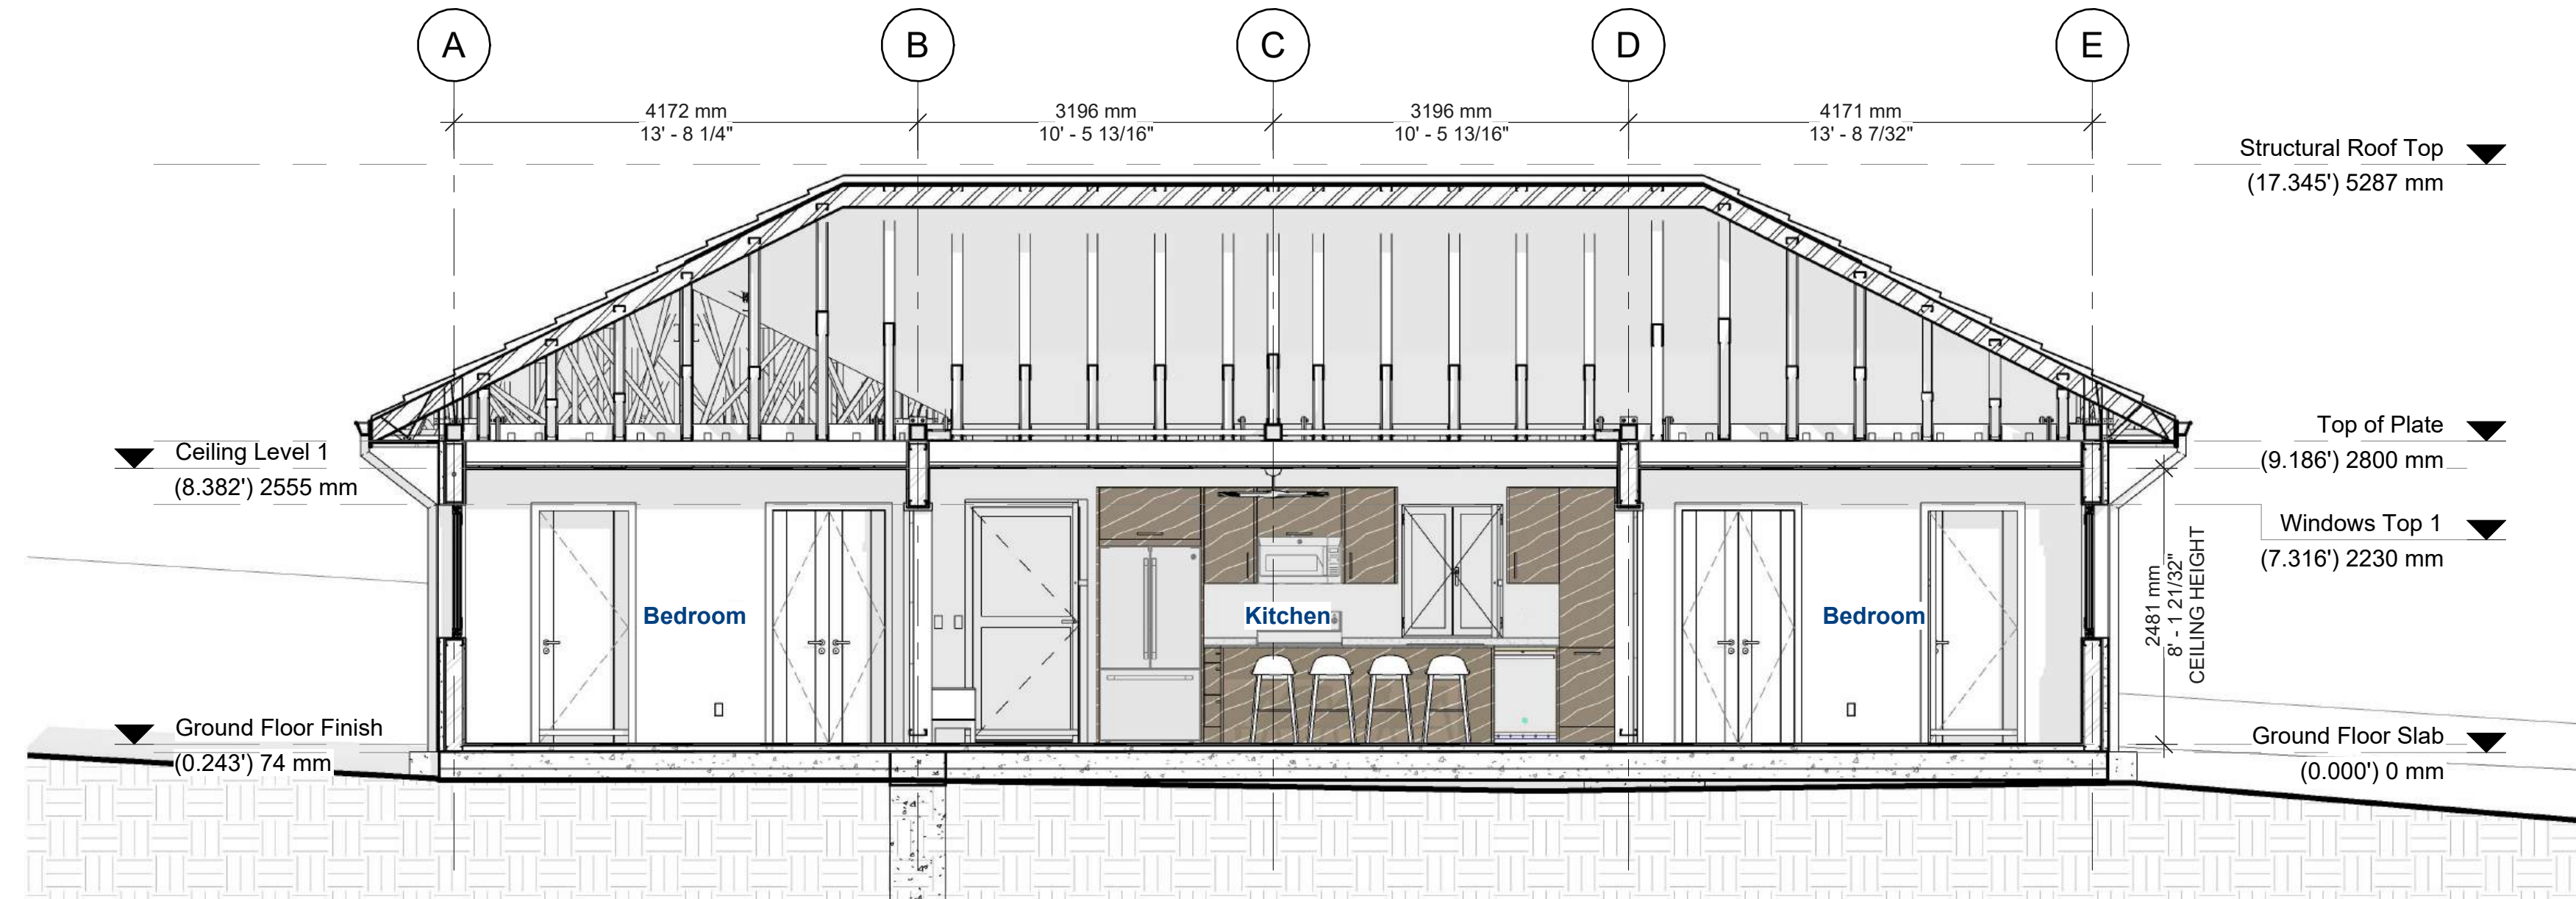


Section 2

1 : 50

1. THESE DRAWINGS MUST BE CHECKED BY THE CUSTOMER OR CONTRACTOR PRIOR TO APPROVAL. ANY ERRORS OR OMISSIONS MUST BE REPORTED IN WRITING TO BAUHU PRIOR TO COMMENCEMENT OF CONSTRUCTION.
2. ARCHITECTURAL DRAWINGS SHOULD BE READ IN CONJUNCTION WITH STRUCTURAL DETAILING AND FABRICATION GENERAL ASSEMBLY DRAWINGS.
3. FOR CONSTRUCTION PURPOSES, USE ONLY THE LATEST APPROVED DRAWINGS LABELED 'ISSUED FOR CONSTRUCTION'.
4. DO NOT SCALE FROM THIS DRAWING.
5. THE COMPANY OPERATES USING METRIC DIMENSIONS AS THE PRINCIPAL DENOMINATION.
6. ALL CONCRETE WORKS ARE OUTSIDE OF THE SCOPE OF THE COMPANY. INFORMATION REGARDING SLAB DESIGN AND CONNECTIONS IN THESE DRAWINGS ARE INTENDED FOR GUIDANCE ONLY. FOUNDATION AND SLAB WORKS SHOULD BE DESIGNED AND APPROVED BY A LOCAL STRUCTURAL ENGINEER.
7. THE COMPANY RETAINS FULL TITLE AND OWNERSHIP OF THESE PLANS AND DESIGNS. ANY UNAUTHORISED USE, REPRODUCTION, OR DISTRIBUTION OF THESE PLANS, WHETHER IN WHOLE OR PART, IS EXPRESSLY PROHIBITED WITHOUT PRIOR WRITTEN CONSENT.
8. THE HYBRID STEEL FRAME CONSTRUCTION SYSTEM AND METHODOLOGY (PATENT PENDING) DESCRIBED IN THESE PLANS HAS BEEN DEVELOPED BY THE COMPANY AND IS SUBJECT TO A PROVISIONAL PATENT APPLICATION & ASSIGNMENT - US APPLICATION NO. 63/722,841

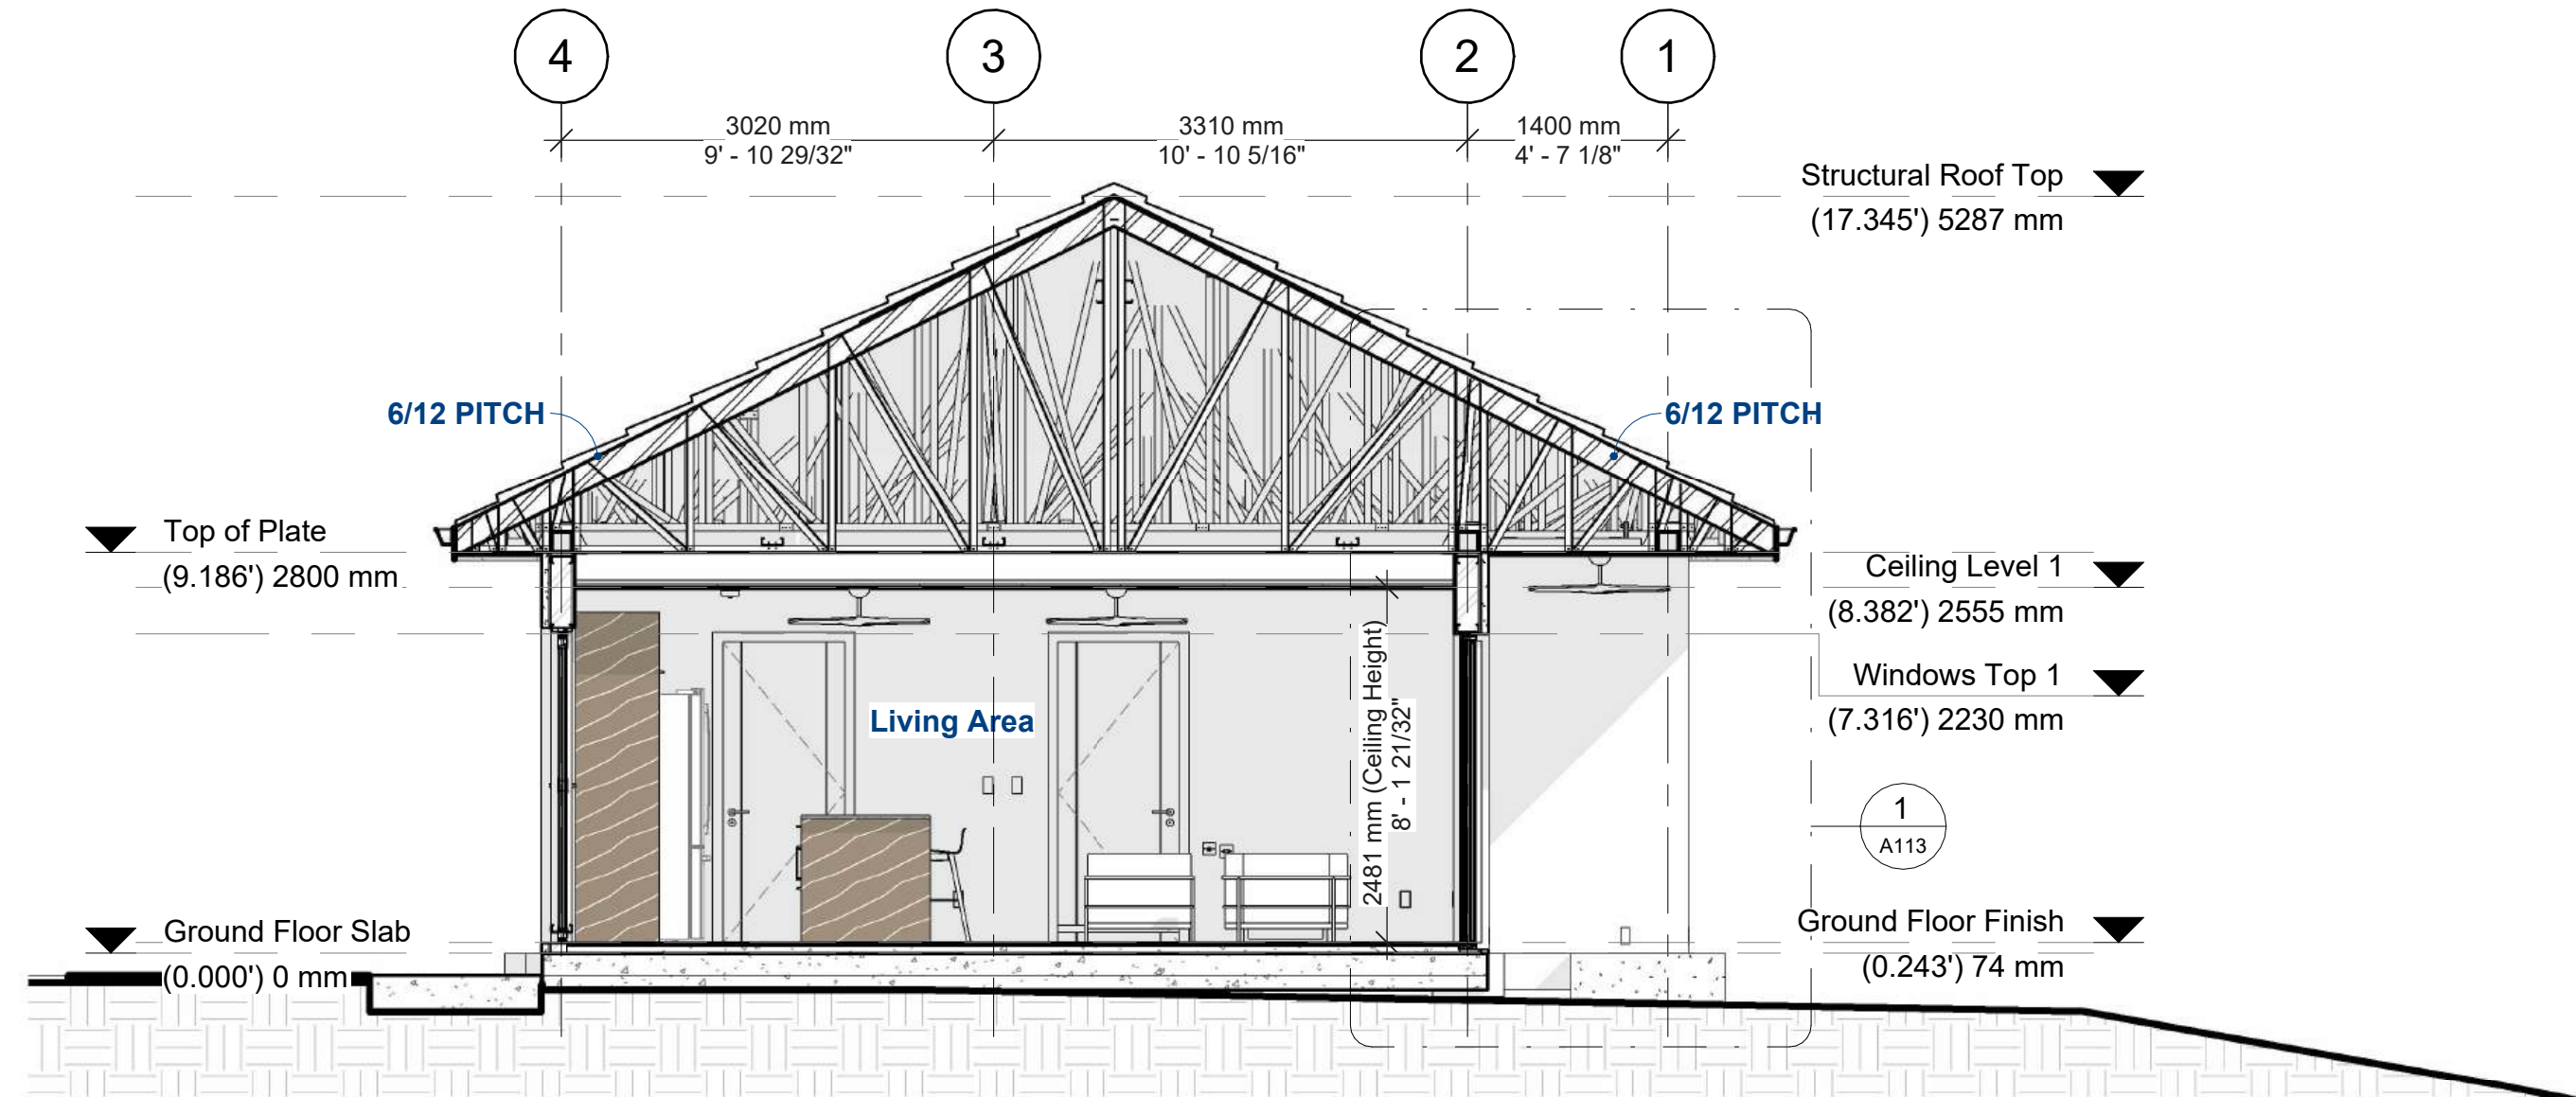

Section 3
1 : 50

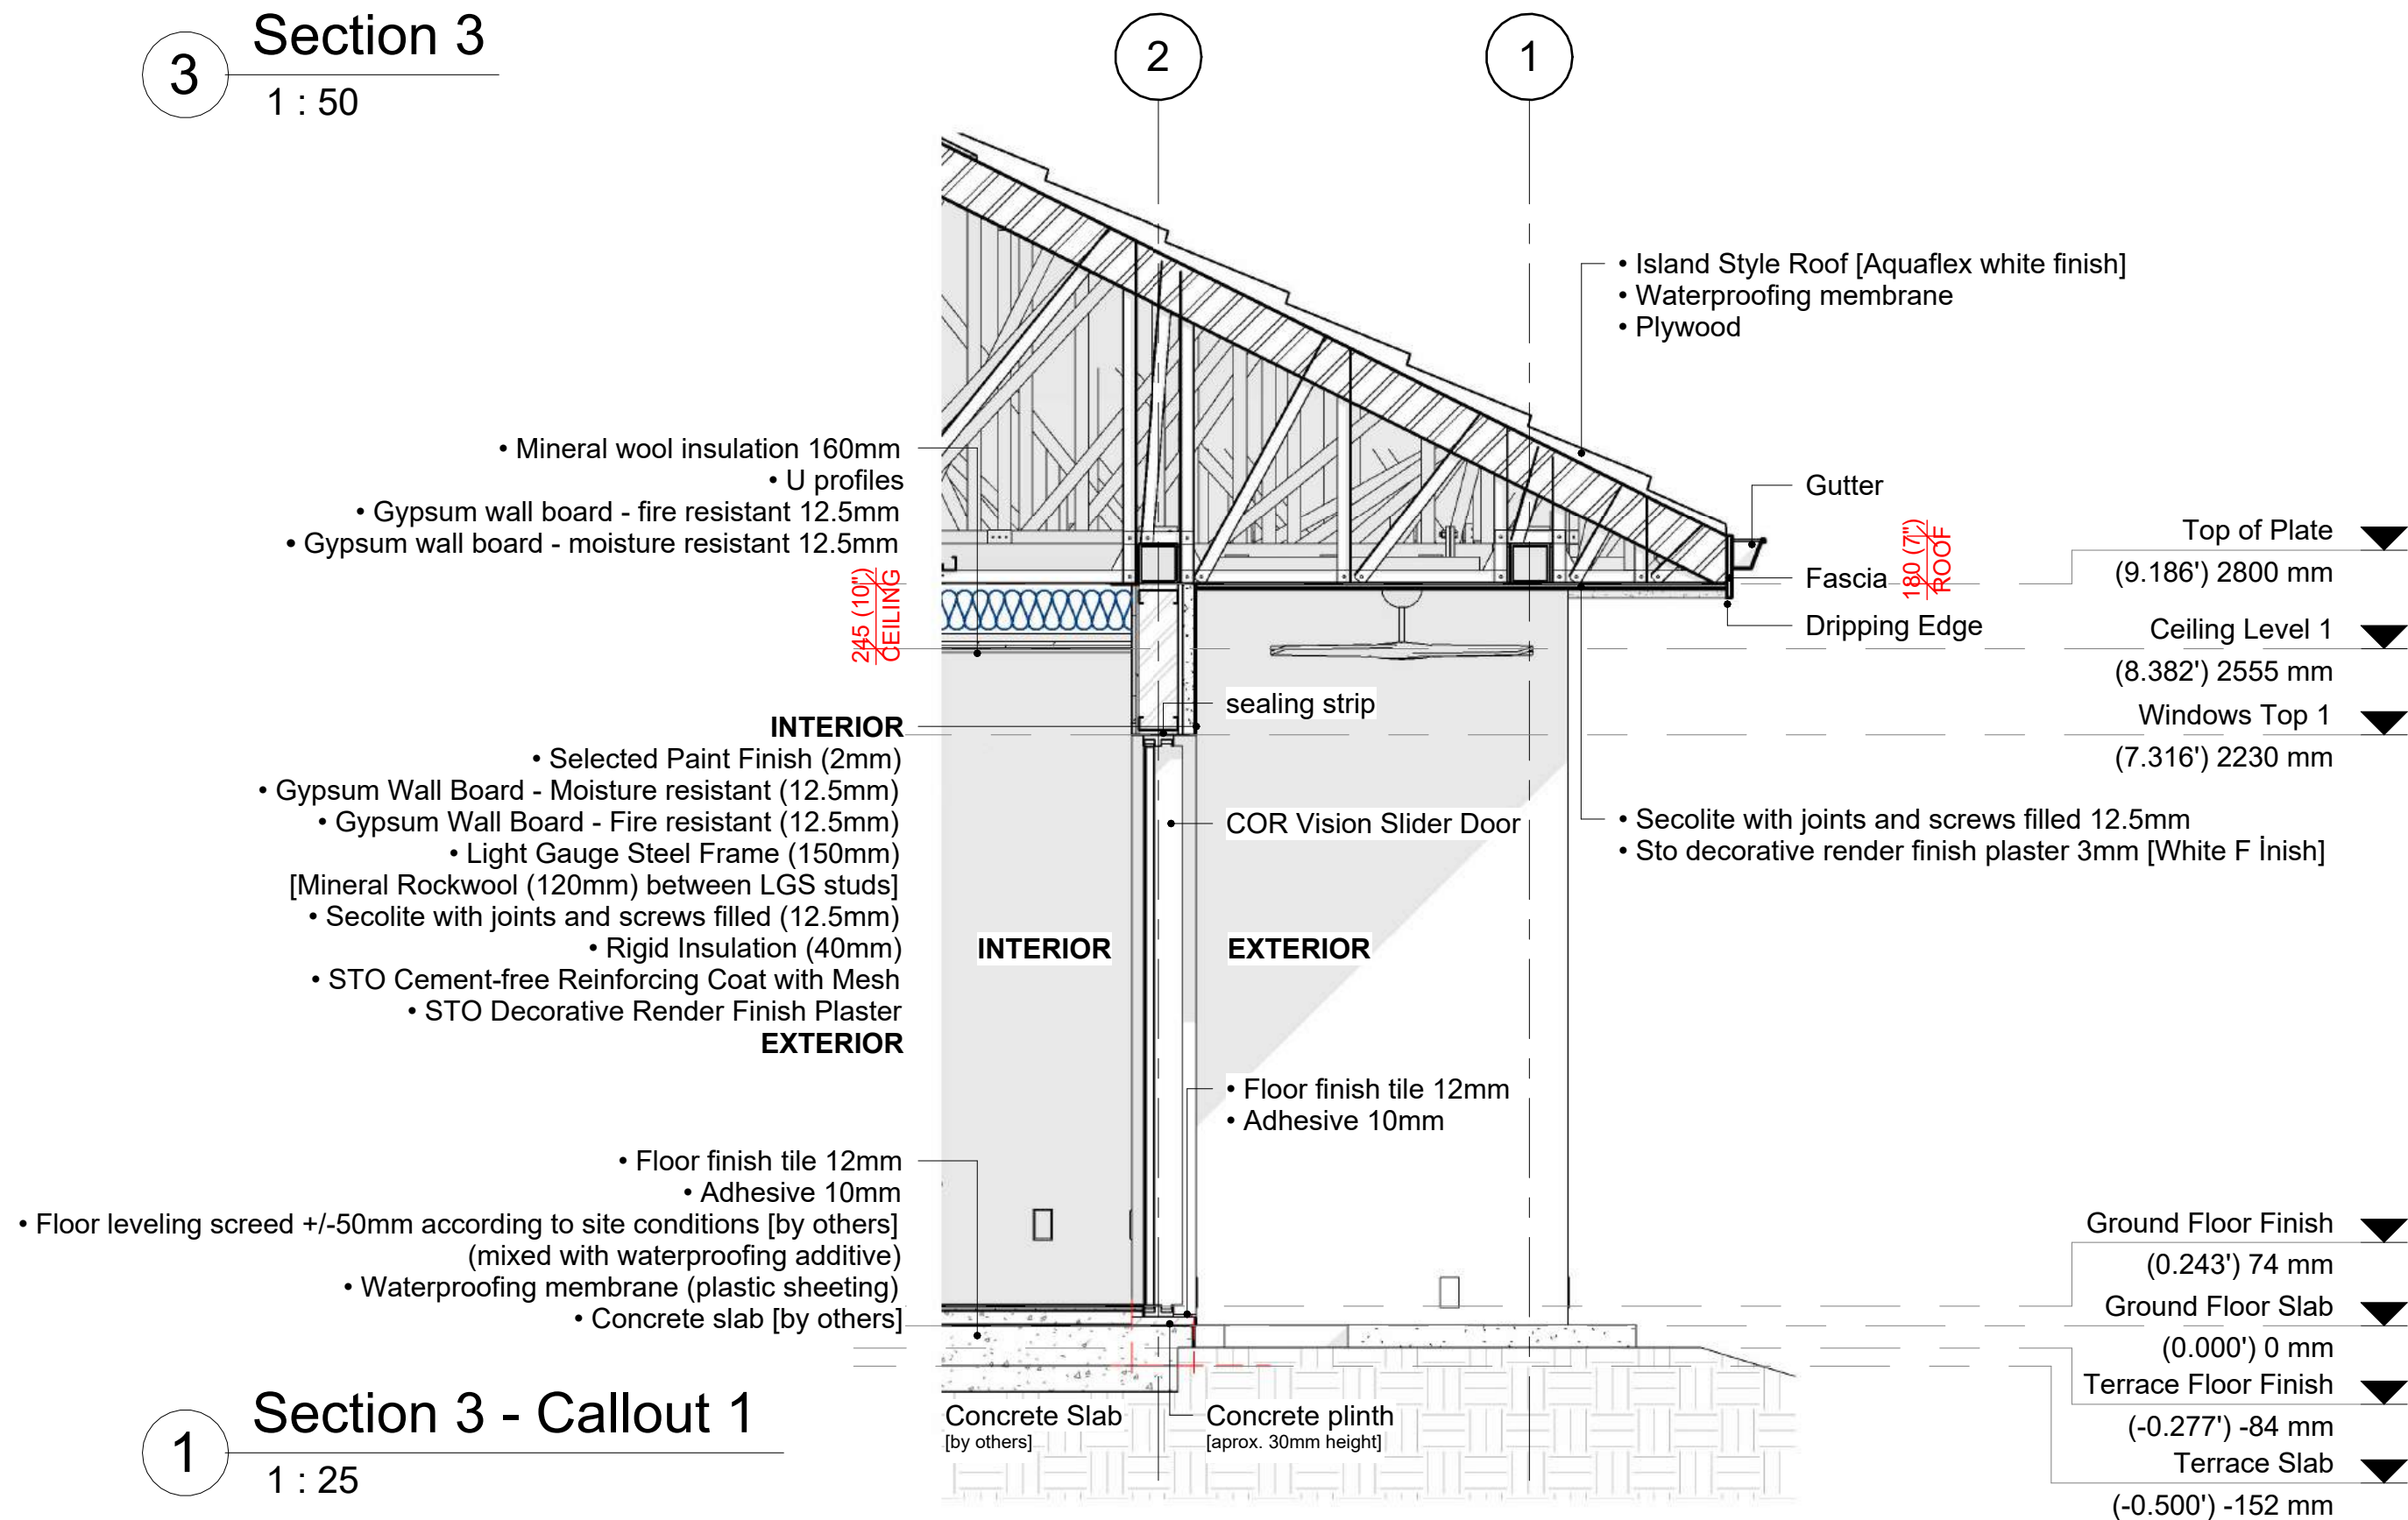

Section 3 - Callout 1
1 : 25

No.	Revision	Date

ISSUED FOR:

Issued for information

Issued for client approval

Issued for fabrication

Issued for construction

Coconut Villa
3 Bed

DRAWING TITLE:

Section 3 & Callout 1

DRAWN BY:

Y.A.Clark

SCALE:

As indicated

DRAWING NO:

A113

DATE:

16/02/2026

Door Schedule													
No	Type	Door Size		Rough Opening Size		Count	Glass	Finishing	No of Leaves	Hinge Side	Sill Height	Level	Lock
		Width	Height	RO Width	RO. Height								
ED-01	COR 70 IND Single Casement Door	1100 mm	2200 mm	1134	2291	1	44.2+16argon we+6 SNX	RAL 9016 Matte	1	LH	74 mm	Ground Floor Slab	Yes
ID-01	Interior Single Casement Door	850 mm	2100 mm	915	2214	3	x	Matt White Lac.	1	LH	74 mm	Ground Floor Slab	Yes
ID-01	Interior Single Casement Door	850 mm	2100 mm	915	2214	1	x	Matt White Lac.	1	RH	74 mm	Ground Floor Slab	Yes
ID-02	Interior Double Casement Door	1000 mm	2100 mm	1065	2214	3	x	Matt White Lac.	2	Both sides	74 mm	Ground Floor Slab	Yes
ID-03	Interior Single Casement Door 3	800 mm	2100 mm	865	2214	1	x	Matt White Lac.	1	LH	74 mm	Ground Floor Slab	Yes
ID-03	Interior Single Casement Door 3	800 mm	2100 mm	865	2214	2	x	Matt White Lac.	1	RH	74 mm	Ground Floor Slab	Yes
Grand total						11							

Window Schedule													
No	Type	Window Size		Rough Opening Size		Count	Glass	Finishing	No of Leaves	Hinge Side	Sill Height	Level	Lock
		Width	Height	RO. Width	RO. Height								
W-01	COR 70 IND Double Casement - 1	900 mm	1200 mm	934	1234	6	44.2+16argon we+6 SNX	RAL 7016 matte	2	Both sides	1030 mm	Ground Floor Slab	Yes
W-02	COR70 IND Single Casement - 2	600 mm	900 mm	634	934	1	44.2+16argon we+6 SNX	RAL 7016 matte	1	LH	1330 mm	Ground Floor Slab	Yes
W-02	COR70 IND Single Casement - 2	600 mm	900 mm	634	934	1	44.2+16argon we+6 SNX	RAL 7016 matte	1	RH	1330 mm	Ground Floor Slab	Yes
W-03	COR Vision w/ Rteel reinforcement 3	2000 mm	2200 mm	2034	2247	2	44.2+16argon we+6 SNX	RAL 7016 matte	2	Interior Panel Left	30 mm	Ground Floor Slab	Yes
W-03	COR Vision w/ Rteel reinforcement 3	2000 mm	2200 mm	2034	2247	3	44.2+16argon we+6 SNX	RAL 7016 matte	2	Interior Panel Right	30 mm	Ground Floor Slab	Yes
Grand total						13							


Compincar Interior Doors

https://compincar.com

Door
Colour: Matt White Lac.
Model: 304



Handle
Model: 1003

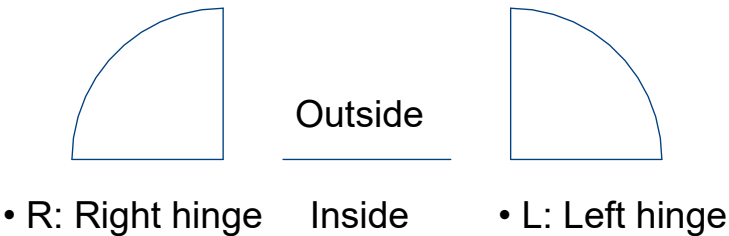

Cortizo Exterior Door/Window

https://www.cortizo.com/paginas/carta_standard

Colour: Traffic White
RAL Code: 9016 matte
(Only entrance door)

Colour: Anthracite Grey
RAL Code: 7016 matte
(All exterior except the entrance door)



Glass
https://www.guardianglass.com/gb/en/our-glass/glass-types/solar-control-glass
• 44.2+16argon we+6 SNX

Note:


- Shutters, insect screens and screening will be provided by others-acquired locally according to dimensions of finished openings after finish application. Drawings are made for design purposes only.
- Garage type doors are excluded and should be sourced by the owner.
- All opening windows open outwards.



1. THESE DRAWINGS MUST BE CHECKED BY THE CUSTOMER OR CONTRACTOR PRIOR TO APPROVAL. ANY ERRORS OR OMISSIONS MUST BE REPORTED IN WRITING TO BAUHU PRIOR TO COMMENCEMENT OF CONSTRUCTION.
2. ARCHITECTURAL DRAWINGS SHOULD BE READ IN CONJUNCTION WITH STRUCTURAL DETAILING AND FABRICATION GENERAL ASSEMBLY DRAWINGS.
3. FOR CONSTRUCTION PURPOSES, USE ONLY THE LATEST APPROVED DRAWINGS LABELED 'ISSUED FOR CONSTRUCTION'.
4. DO NOT SCALE FROM THIS DRAWING.
5. THE COMPANY OPERATES USING METRIC DIMENSIONS AS THE PRINCIPAL DENOMINATION.
6. ALL CONCRETE WORKS ARE OUTSIDE OF THE SCOPE OF THE COMPANY. INFORMATION REGARDING SLAB DESIGN AND CONNECTIONS IN THESE DRAWINGS ARE INTENDED FOR GUIDENCE ONLY. FOUNDATION AND SLAB WORKS SHOULD BE DESIGNED AND APPROVED BY A LOCAL STRUCTURAL ENGINEER.
7. THE COMPANY RETAINS FULL TITLE AND OWNERSHIP OF THESE PLANS AND DESIGNS. ANY UNAUTHORISED USE, REPRODUCTION, OR DISTRIBUTION OF THESE PLANS, WHETHER IN WHOLE OR PART, IS EXPRESSLY PROHIBITED WITHOUT PRIOR WRITTEN CONSENT.
8. THE HYBRID STEEL FRAME CONSTRUCTION SYSTEM AND METHODOLOGY (PATENT PENDING) DESCRIBED IN THESE PLANS HAS BEEN DEVELOPED BY THE COMPANY AND IS SUBJECT TO A PROVISIONAL PATENT APPLICATION & ASSIGNMENT - US APPLICATION NO. 63/722,841

No.	Revision	Date


ISSUED FOR:		
Issued for information Issued for client approval Issued for fabrication Issued for construction		
Coconut Villa 3 Bed		
DRAWING TITLE:		
Openings Schedule		
DRAWN BY:		
Y.A.Clark		
SCALE:		
DRAWING NO:		
A114		
DATE:		
16/02/2026		

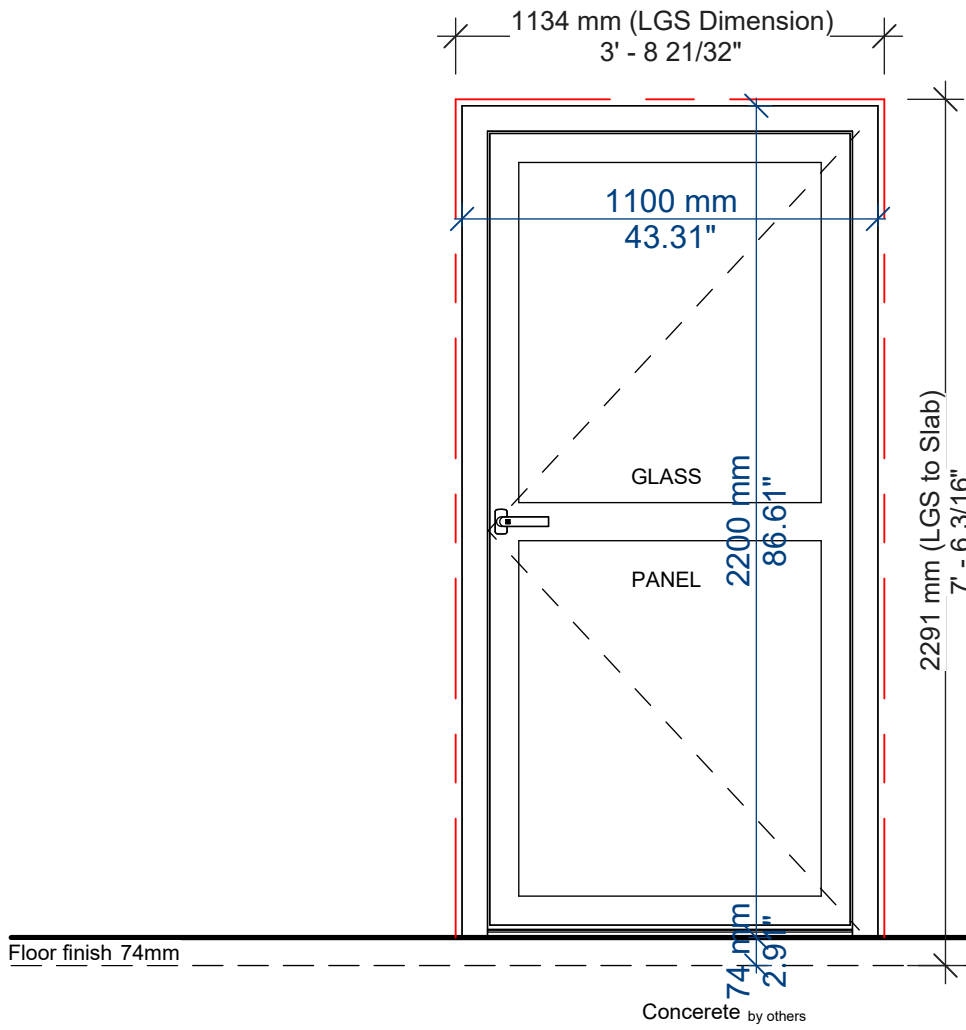


ED01

Type: Exterior COR 70 IND Single Casement
Size: 1100x2200
R.O. Size: 1134x2291
Number of Leaves: 1
Total Piece: 1
Hinge Side: Left (outwards)
Sill Height (from top of slab): 74


ID01

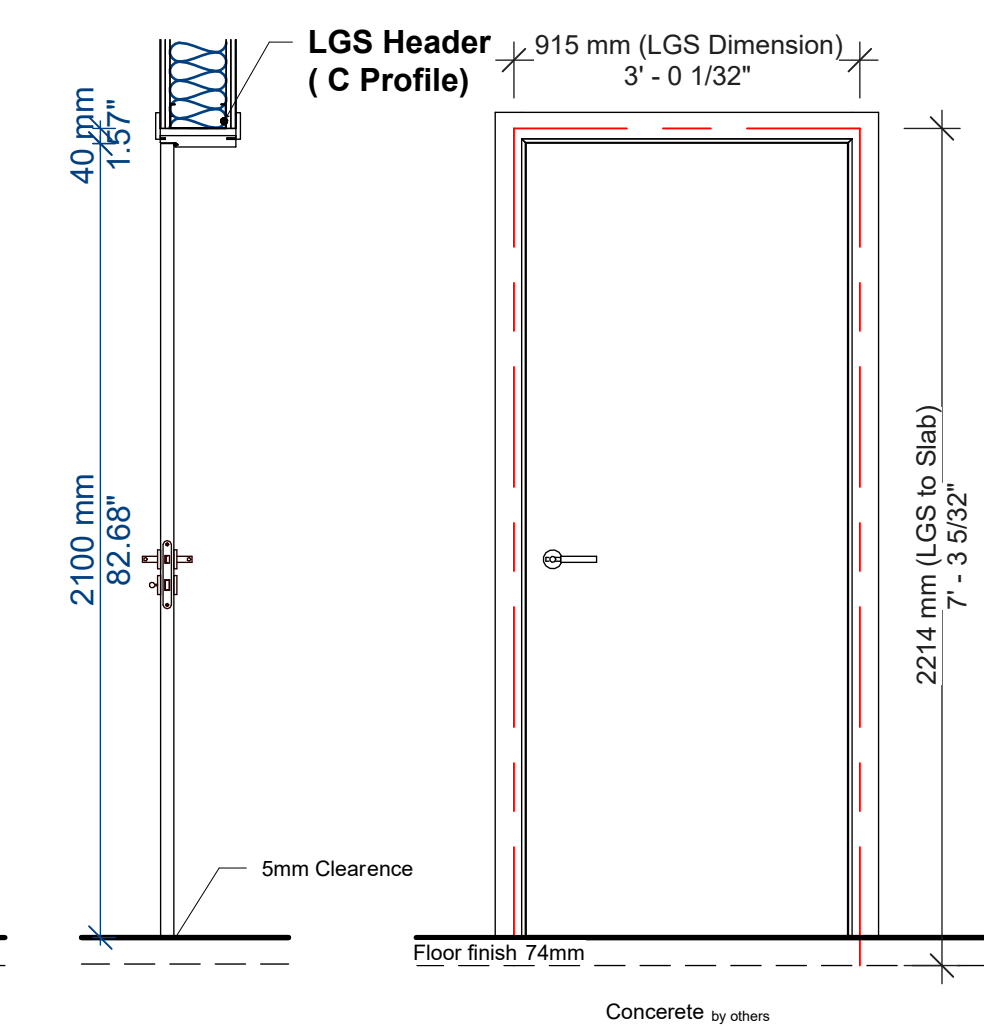

Type: Interior Single Casement
Size: 850x2100
R.O. Size: 915x2214
Number of Leaves: 1
Total Piece: 4
Hinge Side: 3 left, 1 right
Sill Height (from top of slab): 74

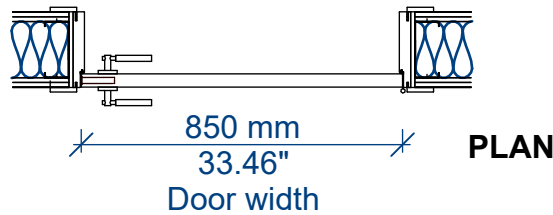


ID02

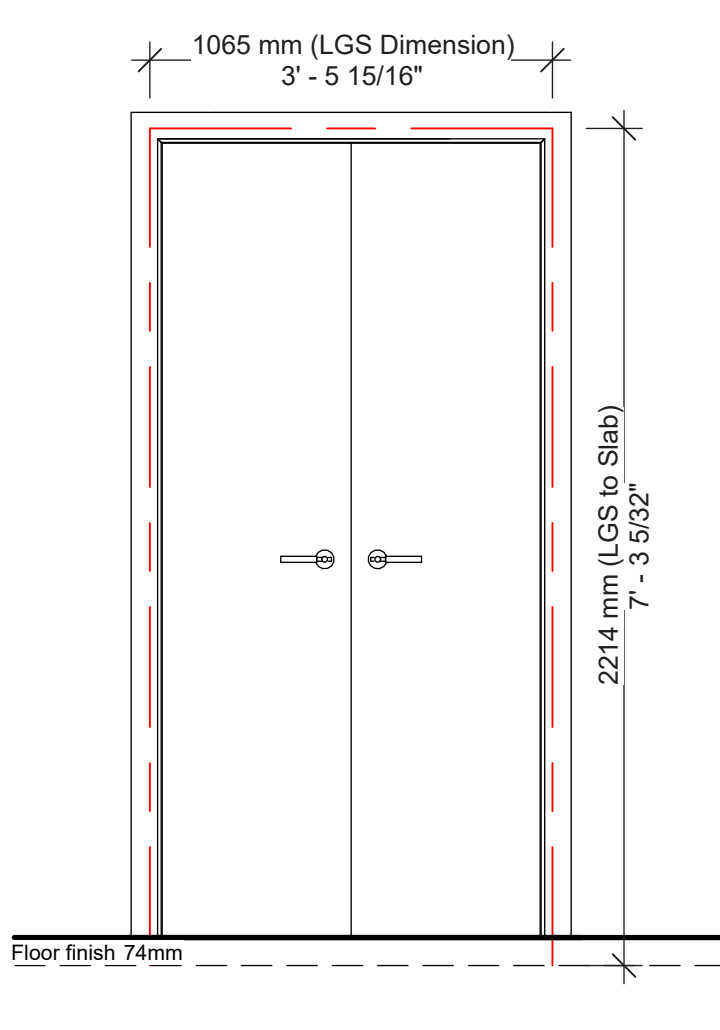


Type: Interior Double Casement
Size: 1000x2100
R.O. Size: 1065x2214
Number of Leaves: 2
Total Piece: 3
Hinge Side: both sides
Sill Height (from top of slab): 74

ID03

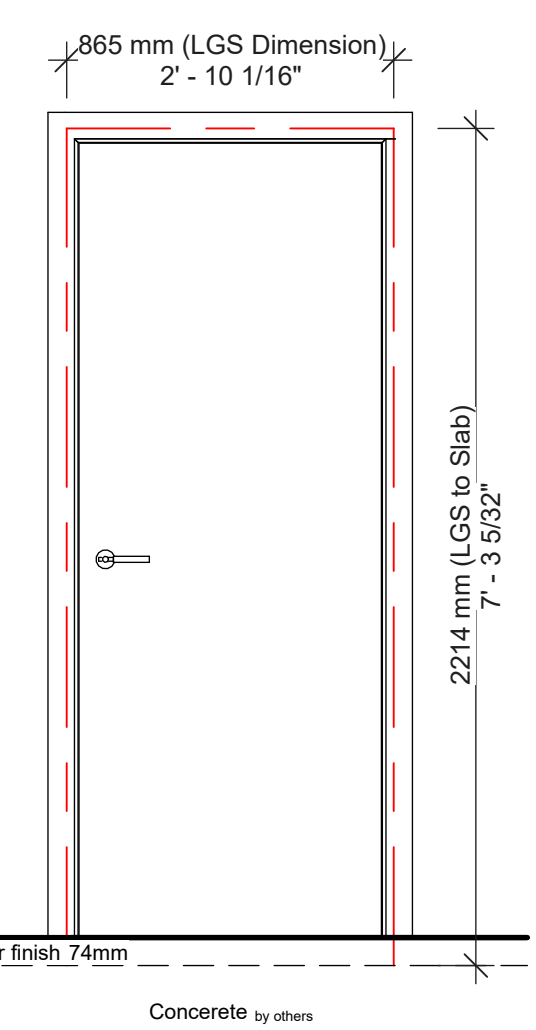


Type: Interior Single Casement
Size: 800x2100
R.O. Size: 865x2214
Number of Leaves: 1
Total Piece: 3
Hinge Side: 2 right, 1 left
Sill Height (from top of slab): 74

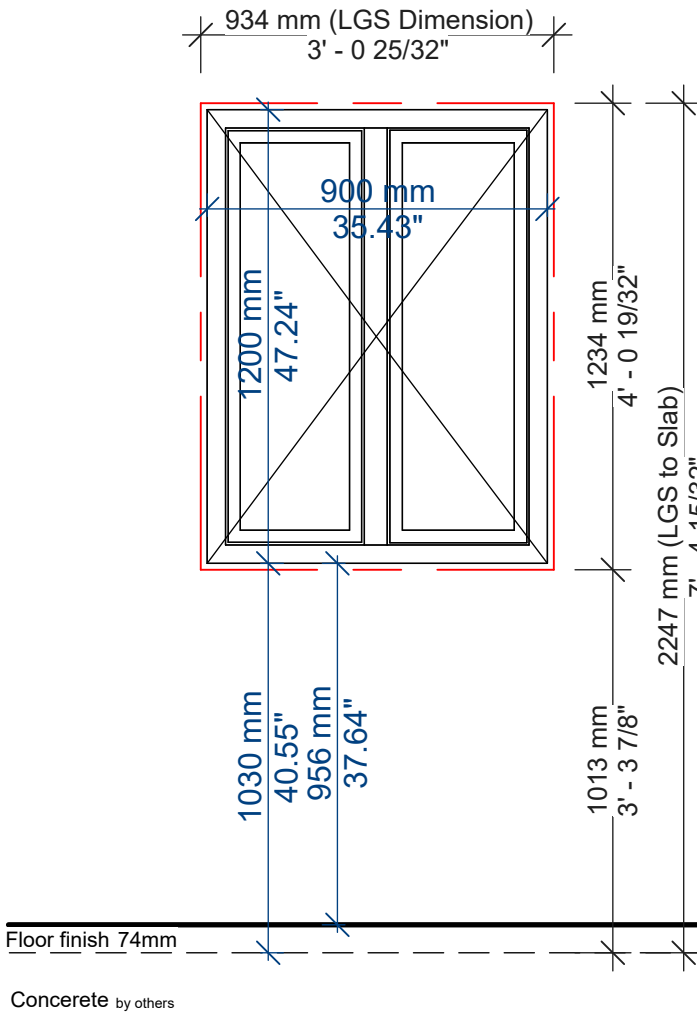

W01


Type: Double Casement
Size: 900x1200
R.O. Size: 934x1234
Number of Leaves: 2
Total Piece: 6
Hinge Side: both sides

W02

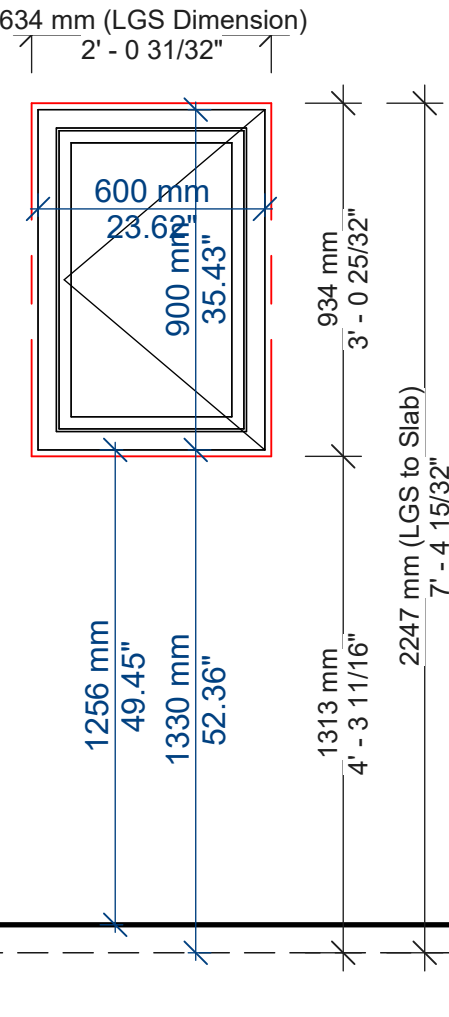

Type: Single Casement
Size: 600x900
R.O. Size: 634x934
Number of Leaves: 1
Total Piece: 2
Hinge Side: 1 right, 1 left

W03

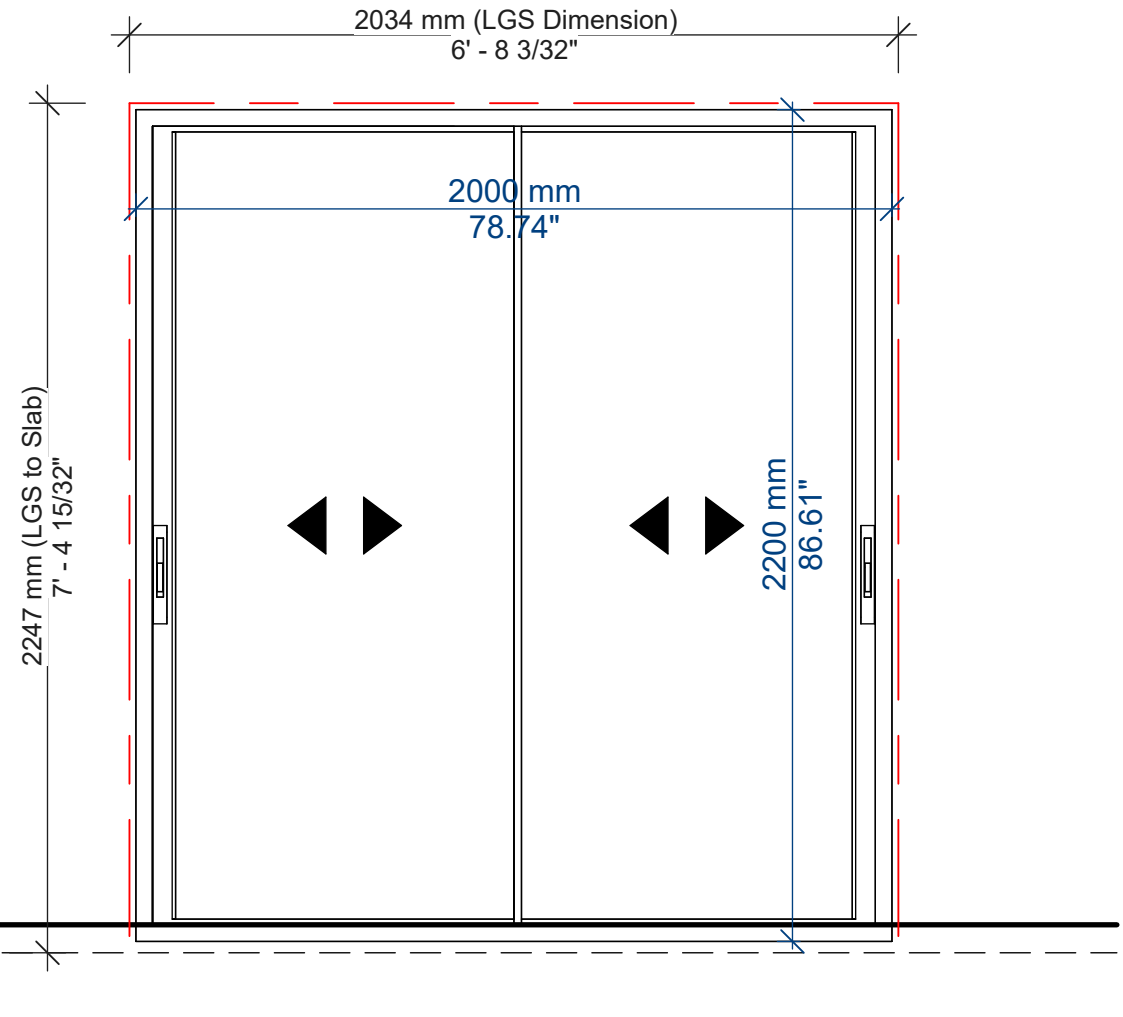

Type: Slider
Size: 2000x2200
R.O. Size: 2034x2247
Number of Leaves: 2
Total Piece: 5
Hinge Side: 2 interior panel left, 3 interior panel right

1. THESE DRAWINGS MUST BE CHECKED BY THE CUSTOMER OR CONTRACTOR PRIOR TO APPROVAL. ANY ERRORS OR OMISSIONS MUST BE REPORTED IN WRITING TO BAUHU PRIOR TO COMMENCEMENT OF CONSTRUCTION.
2. ARCHITECTURAL DRAWINGS SHOULD BE READ IN CONJUNCTION WITH STRUCTURAL DETAILING AND FABRICATION GENERAL ASSEMBLY DRAWINGS.
3. FOR CONSTRUCTION PURPOSES, USE ONLY THE LATEST APPROVED DRAWINGS LABELED 'ISSUED FOR CONSTRUCTION'.
4. DO NOT SCALE FROM THIS DRAWING.
5. THE COMPANY OPERATES USING METRIC DIMENSIONS AS THE PRINCIPAL DENOMINATION.
6. ALL CONCRETE WORKS ARE OUTSIDE OF THE SCOPE OF THE COMPANY. INFORMATION REGARDING SLAB DESIGN AND CONNECTIONS IN THESE DRAWINGS ARE INTENDED FOR GUIDENCE ONLY. FOUNDATION AND SLAB WORKS SHOULD BE DESIGNED AND APPROVED BY A LOCAL STRUCTURAL ENGINEER.
7. THE COMPANY RETAINS FULL TITLE AND OWNERSHIP OF THESE PLANS AND DESIGNS. ANY UNAUTHORISED USE, REPRODUCTION, OR DISTRIBUTION OF THESE PLANS, WHETHER IN WHOLE OR PART, IS EXPRESSLY PROHIBITED WITHOUT PRIOR WRITTEN CONSENT.
8. THE HYBRID STEEL FRAME CONSTRUCTION SYSTEM AND METHODOLOGY (PATENT PENDING) DESCRIBED IN THESE PLANS HAS BEEN DEVELOPED BY THE COMPANY AND IS SUBJECT TO A PROVISIONAL PATENT APPLICATION & ASSIGNMENT - US APPLICATION NO. 63/722,841

No.	Revision	Date

ISSUED FOR:

Issued for information

Issued for client approval

Issued for fabrication

Issued for construction

Coconut Villa 3 Bed

DRAWING TITLE:

Door&Window Openings

DRAWN BY:

Y.A.Clark

SCALE:

1 : 20

DRAWING NO:

A115

DATE:

16/02/2026

1. THESE DRAWINGS MUST BE CHECKED BY THE CUSTOMER OR CONTRACTOR PRIOR TO APPROVAL. ANY ERRORS OR OMISSIONS MUST BE REPORTED IN WRITING TO BAUHU PRIOR TO COMMENCEMENT OF CONSTRUCTION.

2. ARCHITECTURAL DRAWINGS SHOULD BE READ IN CONJUNCTION WITH STRUCTURAL DETAILING AND FABRICATION GENERAL ASSEMBLY DRAWINGS.

3. FOR CONSTRUCTION PURPOSES, USE ONLY THE LATEST APPROVED DRAWINGS LABELED 'ISSUED FOR CONSTRUCTION'.

4. DO NOT SCALE FROM THIS DRAWING.

5. THE COMPANY OPERATES USING METRIC DIMENSIONS AS THE PRINCIPAL DENOMINATION.

6. ALL CONCRETE WORKS ARE OUTSIDE OF THE SCOPE OF THE COMPANY. INFORMATION REGARDING SLAB DESIGN AND CONNECTIONS IN THESE DRAWINGS ARE INTENDED FOR GUIDENCE ONLY. FOUNDATION AND SLAB WORKS SHOULD BE DESIGNED AND APPROVED BY A LOCAL STRUCTURAL ENGINEER.

7. THE COMPANY RETAINS FULL TITLE AND OWNERSHIP OF THESE PLANS AND DESIGNS. ANY UNAUTHORISED USE, REPRODUCTION, OR DISTRIBUTION OF THESE PLANS, WHETHER IN WHOLE OR PART, IS EXPRESSLY PROHIBITED WITHOUT PRIOR WRITTEN CONSENT.

8. THE HYBRID STEEL FRAME CONSTRUCTION SYSTEM AND METHODOLOGY (PATENT PENDING) DESCRIBED IN THESE PLANS HAS BEEN DEVELOPED BY THE COMPANY AND IS SUBJECT TO A PROVISIONAL PATENT APPLICATION & ASSIGNMENT - US APPLICATION NO. 63/722,841

No.	Revision	Date

ISSUED FOR:

Issued for information

Issued for client approval

Issued for fabrication

Issued for construction

Coconut Villa
3 Bed

DRAWING TITLE:

Kitchen Plan&Sections

DRAWN BY:

Y.A.Clark

SCALE:



1 : 25

DRAWING NO:

A116


DATE:

16/02/2026

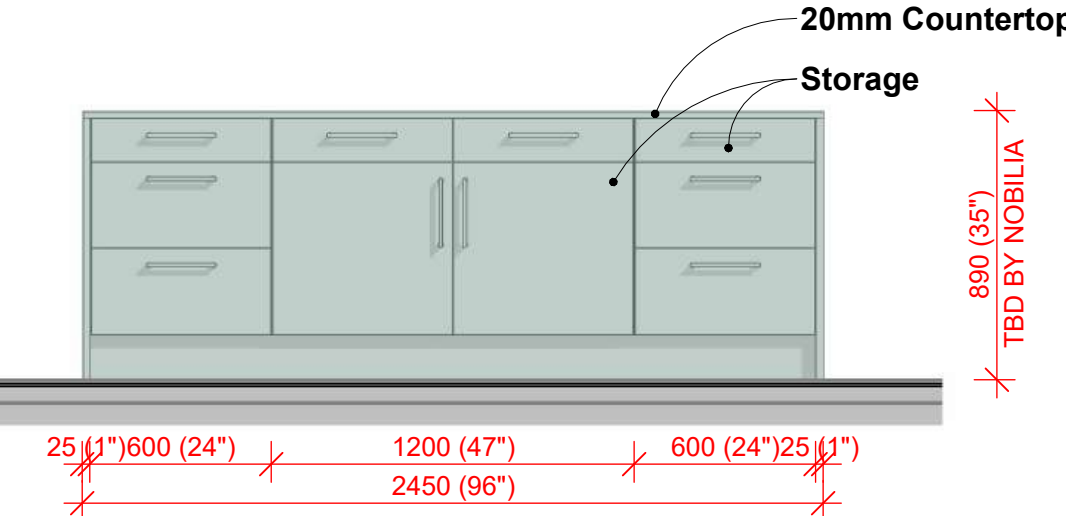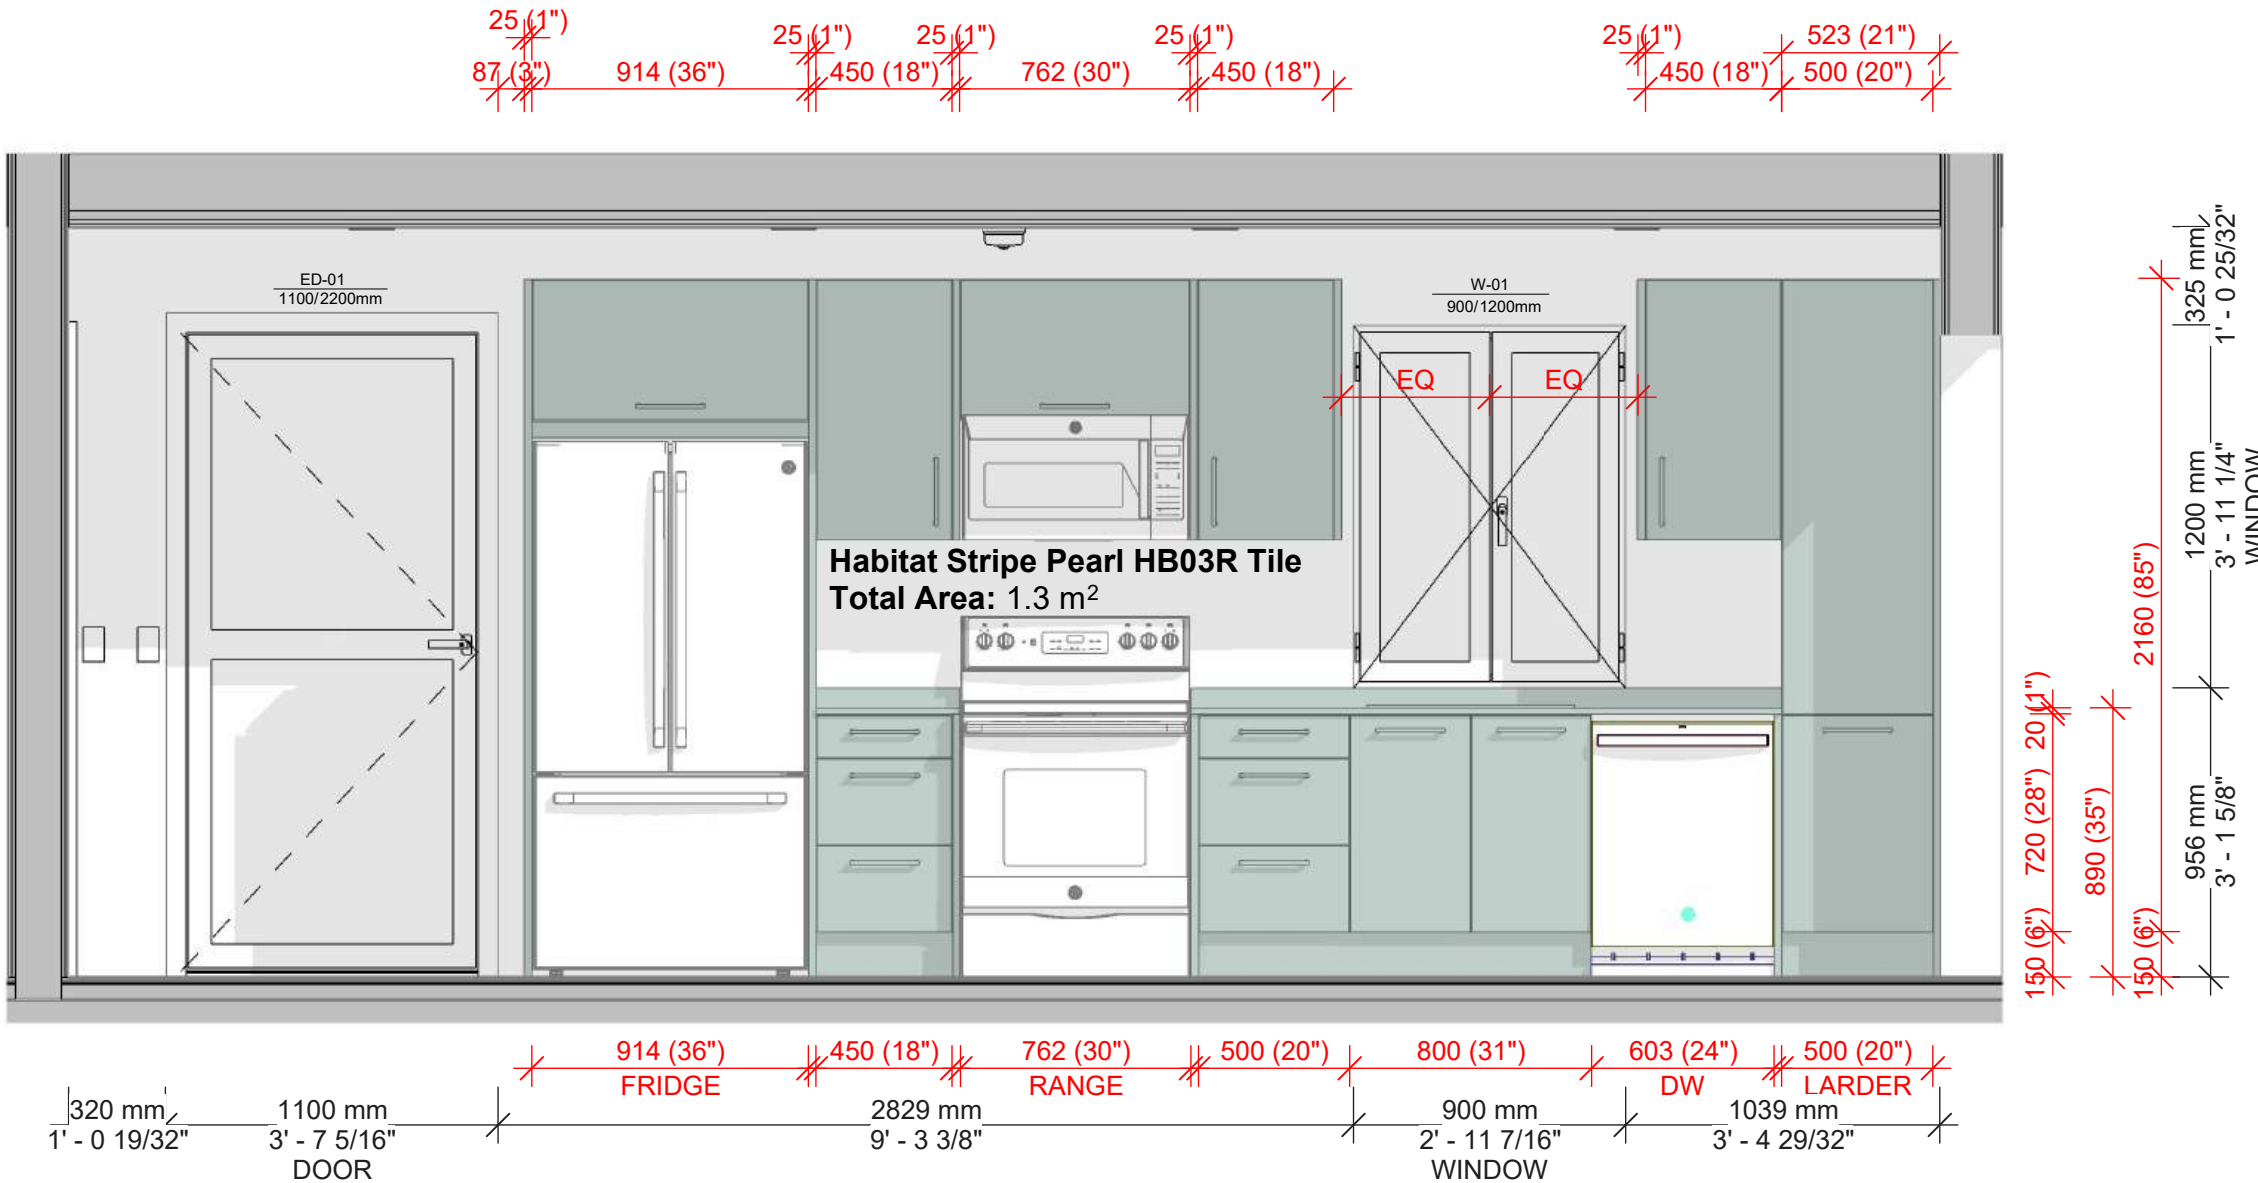

K2 Island Front

1 : 25

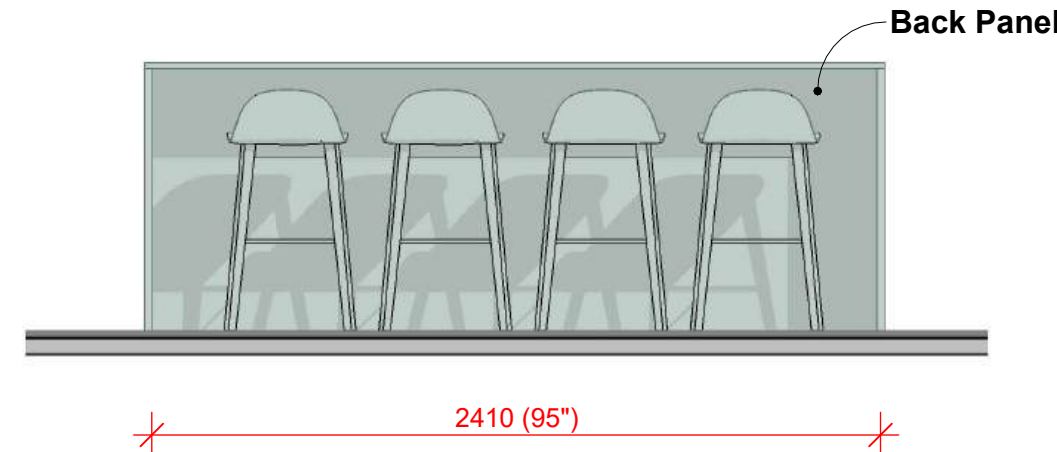


K4 Island Back

1 : 25

K3 Section

1 : 25

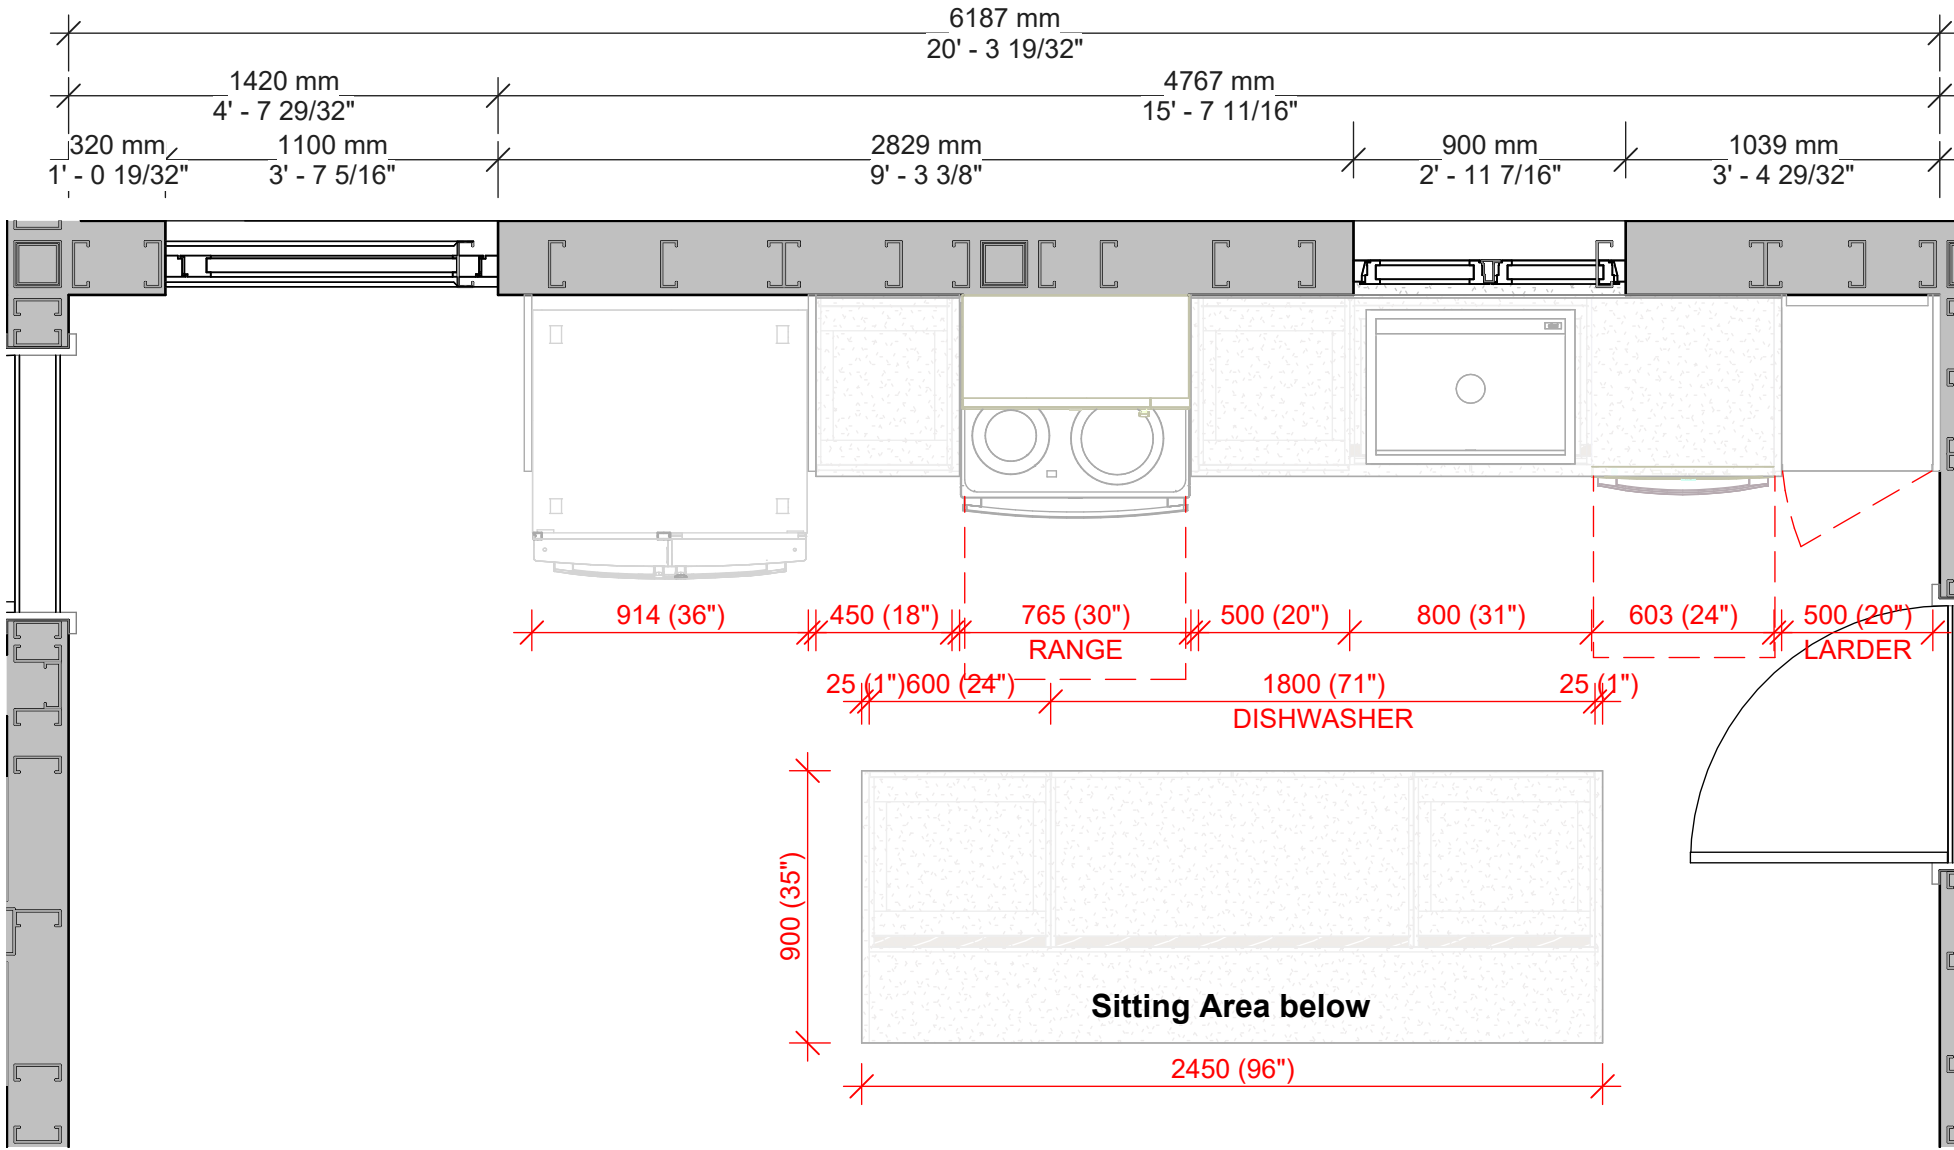


Kitchen Plan

1 : 25

KITCHEN MIXER

https://www.bruma.pt


Bruma
Model: Kitchen Faucets
Name: Sink mixer with swivel spout and pull out handshower -
Ginger
Reference: 122 700 3CR
Colour: Chrome
Count: 1

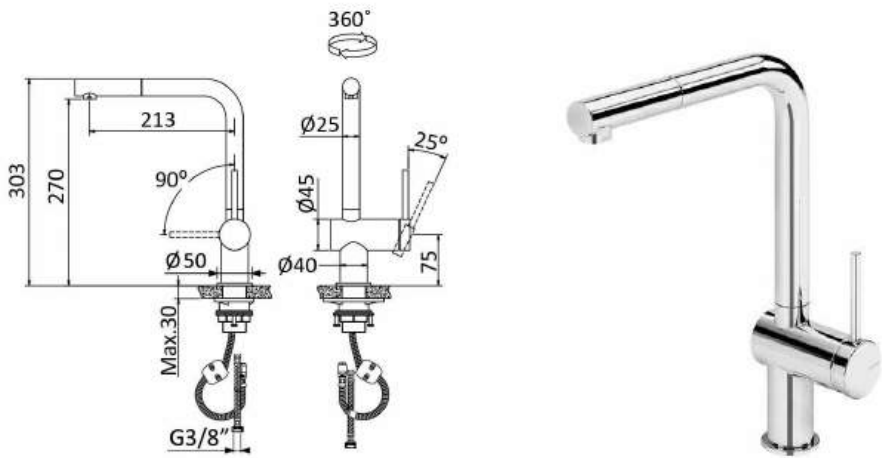

KITCHEN SINK

https://www.elleci.com/products/sinks/

Elleci
Model: Built-in sink Best 130 Keratek
Dimensions: 790 x 510 mm
Base: 800 mm
Colour: Black - K86
Count: 1

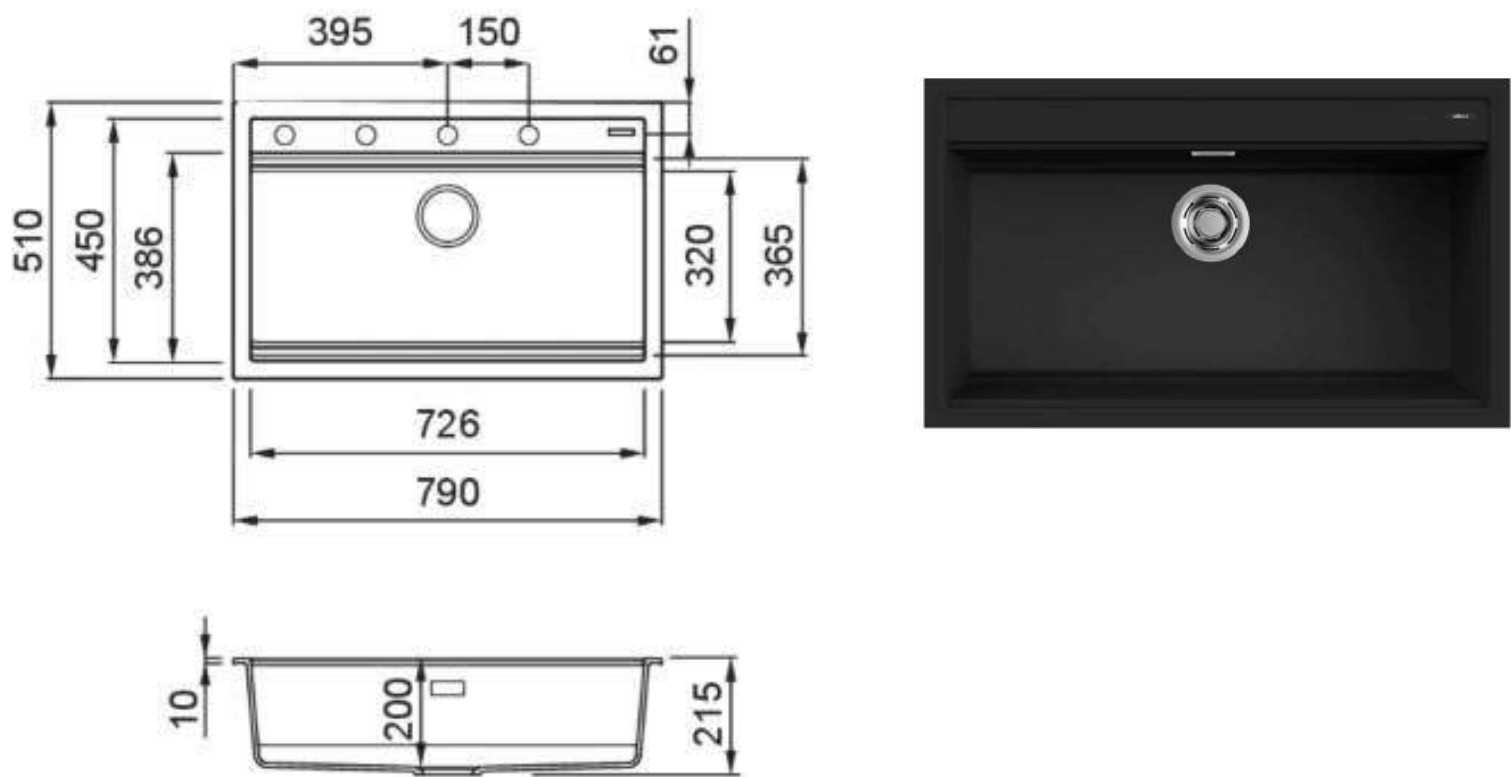

KITCHEN FINISHES

Nobilia cabinetry choices
https://www.nobilia.de/en/products/kitchens



FRONT 402
Havana oak reproduction



CARCASE 097
Havana oak reproduction



HANDLE 250
Bow Handle Black

KITCHEN WORKTOP

https://www.nobilia.de/en/products/design-elements/worktops/





WORKTOP 794
Concrete Satin grey reproduction (Xtra Ceramic)

1. THESE DRAWINGS MUST BE CHECKED BY THE CUSTOMER OR CONTRACTOR PRIOR TO APPROVAL. ANY ERRORS OR OMISSIONS MUST BE REPORTED IN WRITING TO BAUHU PRIOR TO COMMENCEMENT OF CONSTRUCTION.
2. ARCHITECTURAL DRAWINGS SHOULD BE READ IN CONJUNCTION WITH STRUCTURAL DETAILING AND FABRICATION GENERAL ASSEMBLY DRAWINGS.
3. FOR CONSTRUCTION PURPOSES, USE ONLY THE LATEST APPROVED DRAWINGS LABELED 'ISSUED FOR CONSTRUCTION'.
4. DO NOT SCALE FROM THIS DRAWING.
5. THE COMPANY OPERATES USING METRIC DIMENSIONS AS THE PRINCIPAL DENOMINATION.
6. ALL CONCRETE WORKS ARE OUTSIDE OF THE SCOPE OF THE COMPANY. INFORMATION REGARDING SLAB DESIGN AND CONNECTIONS IN THESE DRAWINGS ARE INTENDED FOR GUIDENCE ONLY. FOUNDATION AND SLAB WORKS SHOULD BE DESIGNED AND APPROVED BY A LOCAL STRUCTURAL ENGINEER.
7. THE COMPANY RETAINS FULL TITLE AND OWNERSHIP OF THESE PLANS AND DESIGNS. ANY UNAUTHORISED USE, REPRODUCTION, OR DISTRIBUTION OF THESE PLANS, WHETHER IN WHOLE OR PART, IS EXPRESSLY PROHIBITED WITHOUT PRIOR WRITTEN CONSENT.
8. THE HYBRID STEEL FRAME CONSTRUCTION SYSTEM AND METHODOLOGY (PATENT PENDING) DESCRIBED IN THESE PLANS HAS BEEN DEVELOPED BY THE COMPANY AND IS SUBJECT TO A PROVISIONAL PATENT APPLICATION & ASSIGNMENT - US APPLICATION NO. 63/722,841

No.	Revision	Date

ISSUED FOR: Issued for information Issued for client approval Issued for fabrication Issued for construction Coconut Villa 3 Bed		
DRAWING TITLE: Kitchen Finishes		
DRAWN BY: Y.A.Clark		
SCALE:		
DRAWING NO: A117		
DATE: 16/02/2026		

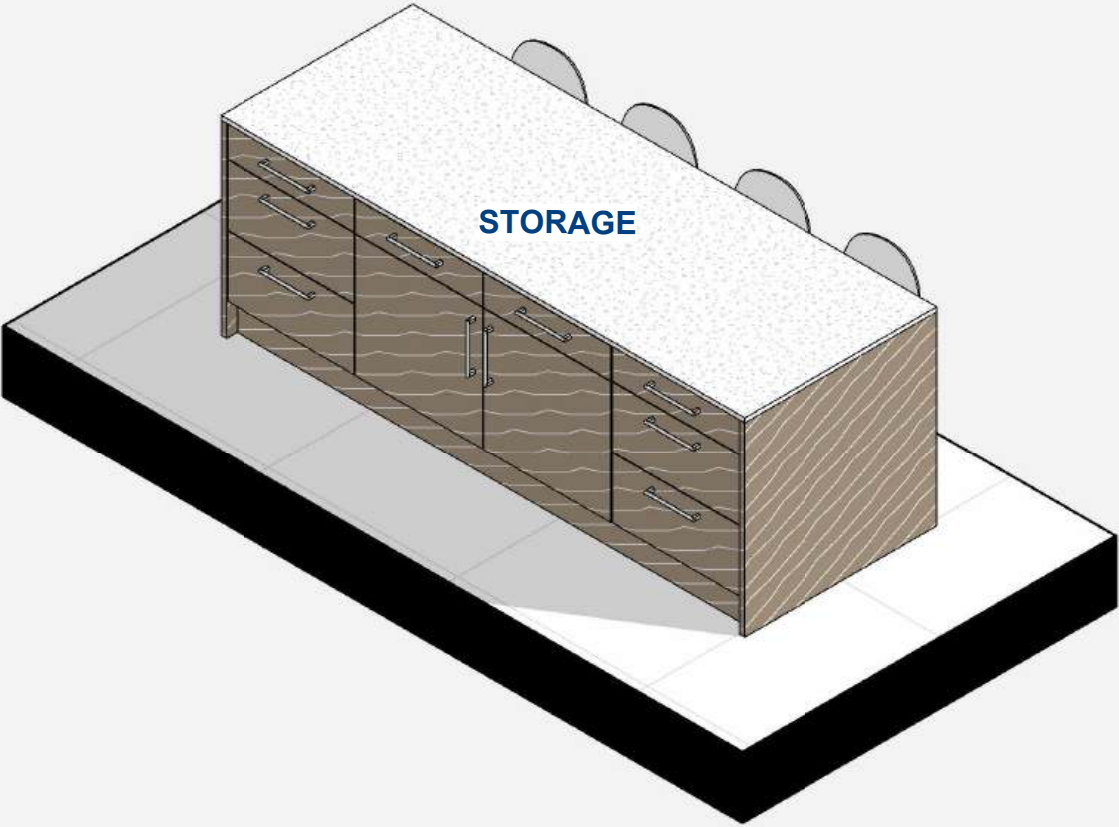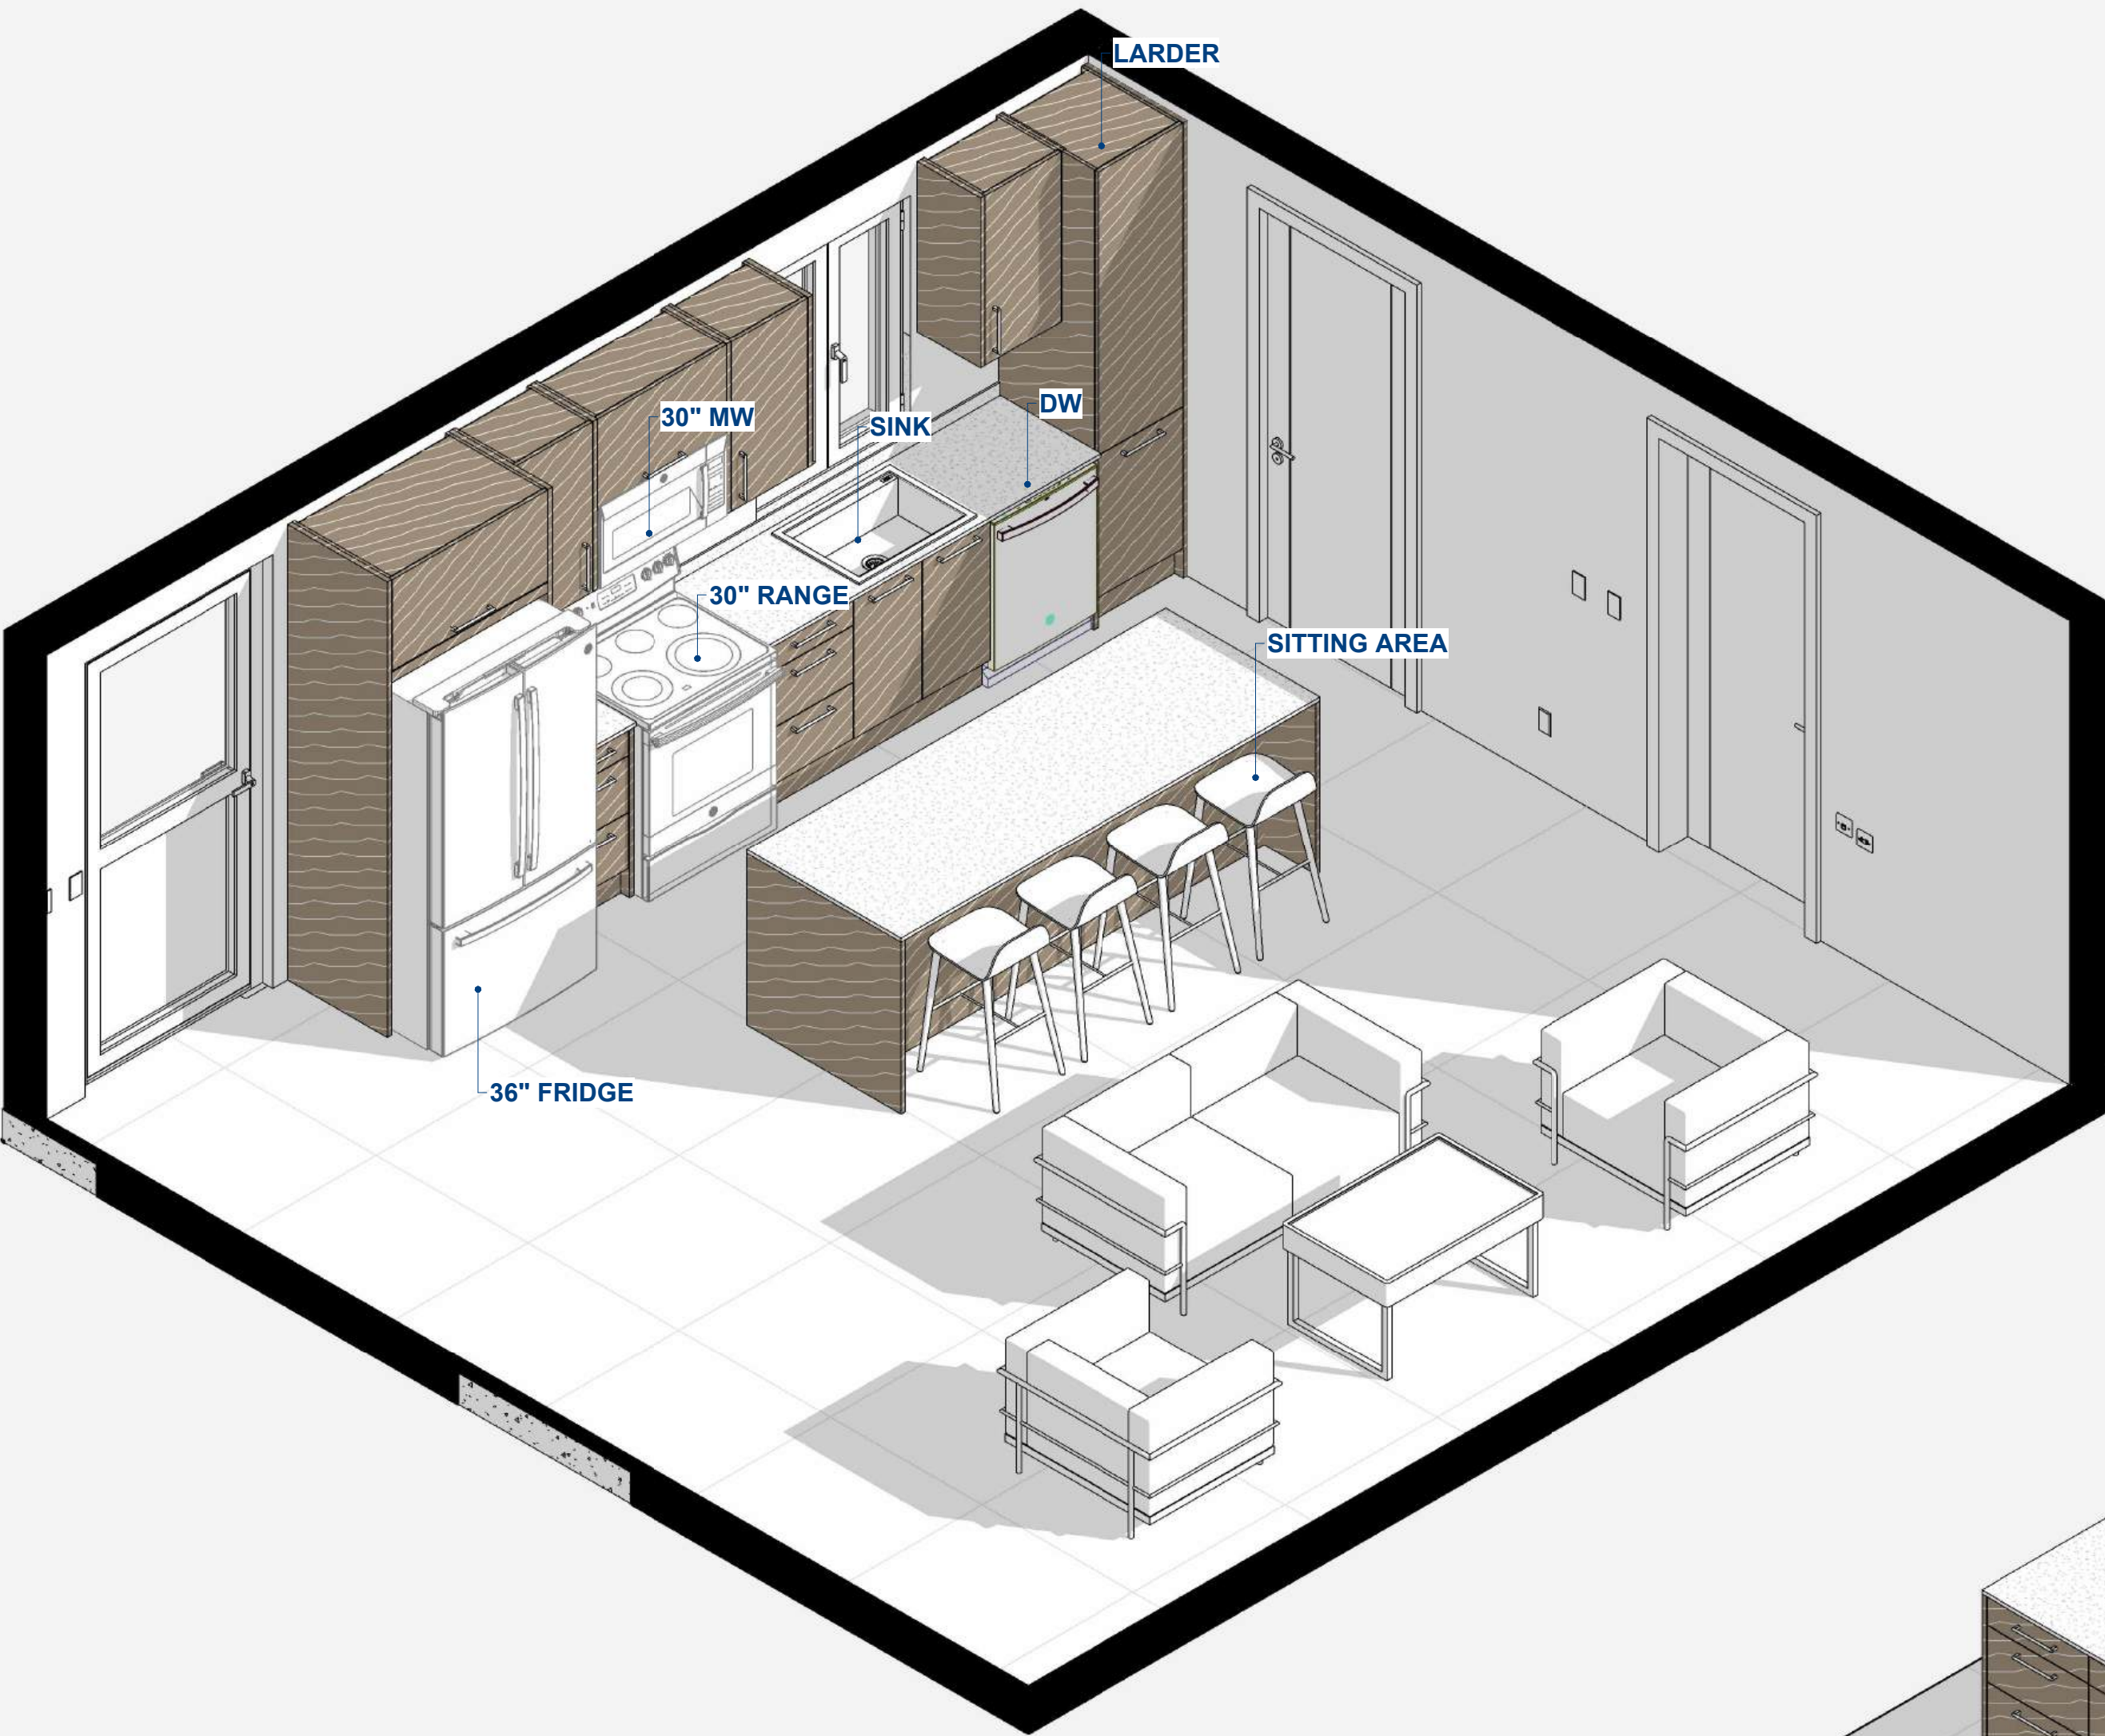

1. THESE DRAWINGS MUST BE CHECKED BY THE CUSTOMER OR CONTRACTOR PRIOR TO APPROVAL. ANY ERRORS OR OMISSIONS MUST BE REPORTED IN WRITING TO BAUHU PRIOR TO COMMENCEMENT OF CONSTRUCTION.
2. ARCHITECTURAL DRAWINGS SHOULD BE READ IN CONJUNCTION WITH STRUCTURAL DETAILING AND FABRICATION GENERAL ASSEMBLY DRAWINGS.
3. FOR CONSTRUCTION PURPOSES, USE ONLY THE LATEST APPROVED DRAWINGS LABELED 'ISSUED FOR CONSTRUCTION'.
4. DO NOT SCALE FROM THIS DRAWING.
5. THE COMPANY OPERATES USING METRIC DIMENSIONS AS THE PRINCIPAL DENOMINATION.
6. ALL CONCRETE WORKS ARE OUTSIDE OF THE SCOPE OF THE COMPANY. INFORMATION REGARDING SLAB DESIGN AND CONNECTIONS IN THESE DRAWINGS ARE INTENDED FOR GUIDENCE ONLY. FOUNDATION AND SLAB WORKS SHOULD BE DESIGNED AND APPROVED BY A LOCAL STRUCTURAL ENGINEER.
7. THE COMPANY RETAINS FULL TITLE AND OWNERSHIP OF THESE PLANS AND DESIGNS. ANY UNAUTHORISED USE, REPRODUCTION, OR DISTRIBUTION OF THESE PLANS, WHETHER IN WHOLE OR PART, IS EXPRESSLY PROHIBITED WITHOUT PRIOR WRITTEN CONSENT.
8. THE HYBRID STEEL FRAME CONSTRUCTION SYSTEM AND METHODOLOGY (PATENT PENDING) DESCRIBED IN THESE PLANS HAS BEEN DEVELOPED BY THE COMPANY AND IS SUBJECT TO A PROVISIONAL PATENT APPLICATION & ASSIGNMENT - US APPLICATION NO. 63/722,841

No.	Revision	Date

ISSUED FOR:

Issued for information

Issued for client approval

Issued for fabrication

Issued for construction

Coconut Villa
3 Bed


DRAWING TITLE:	Kitchen 3D View
DRAWN BY:	Y.A.Clark
SCALE:	
DRAWING NO:	A118
DATE:	16/02/2026

Microwave Over Range


Name: GE® 1.7 Cu. Ft. Over-the-Range Sensor Microwave Oven
Model: JVM6175SKSS
Dimensions: 16 5/16 H x 29 7/8 W x 15 9/16 D
Cabinet Width: 30 in
https://www.geappliances.com/appliance/GE-1-7-Cu-Ft-Over-the-Range-Sensor-Microwave-Oven-JVM6175SKSS

Range

Name: GE® 30" Free-Standing Electric Convection Fingerprint Resistant Range
Model: JB655YKFS
Dimensions: 47 H x 29 7/8 W x 28 D
Cabinet Width: 30 in
https://www.geappliances.com/appliance/GE-30-Free-Standing-Electric-Convection-Fingerprint-Resistant-Range-JB655YKFS



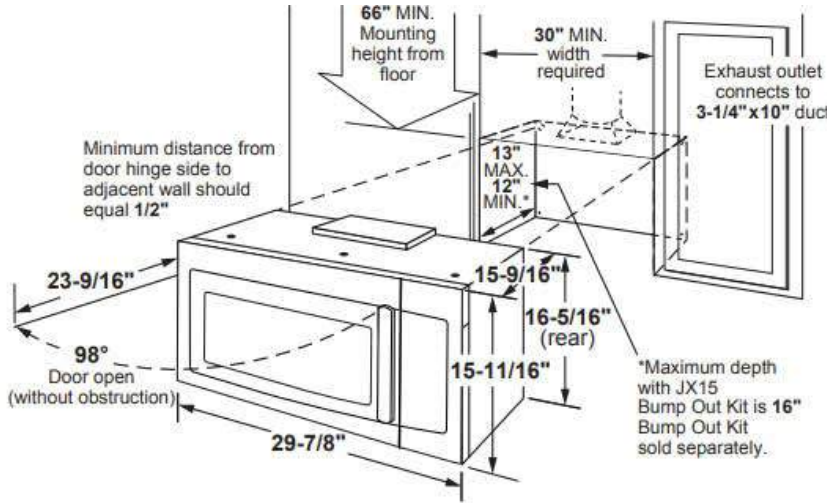


30" Free-Standing Electric Single Oven

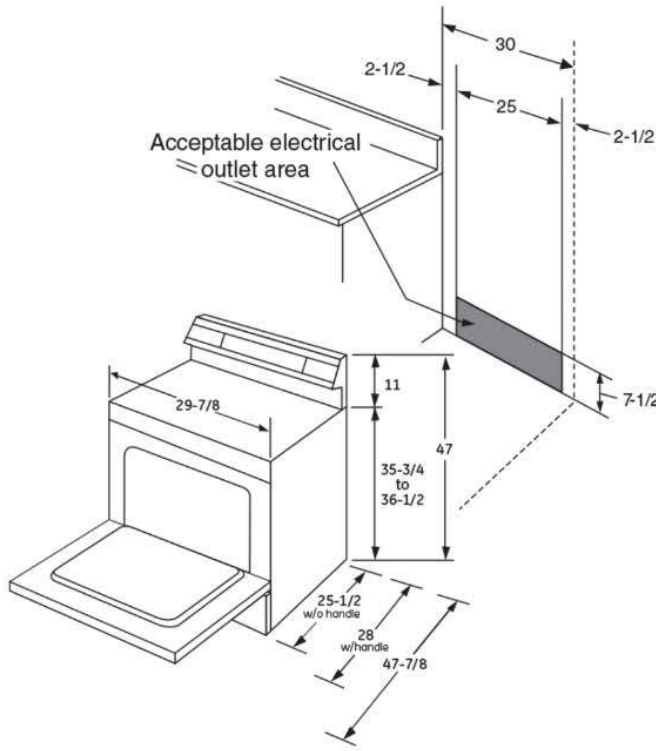

Dishwasher

Name: GE® ENERGY STAR® Top Control with Stainless Steel Interior Dishwasher with Sanitize Cycle & Dry Boost with Fan Assist
Model: GDT645SSNSS
Dimensions: 34 H x 23 3/4 W x 24 D
Cabinet Width: 24 in
https://www.geappliances.com/appliance/GE-ENERGY-STAR-Top-Control-with-Stainless-Steel-Interior-Dishwasher-with-Sanitize-Cycle-Dry-Boost-with-Fan-Assist-GDT645SSNSS

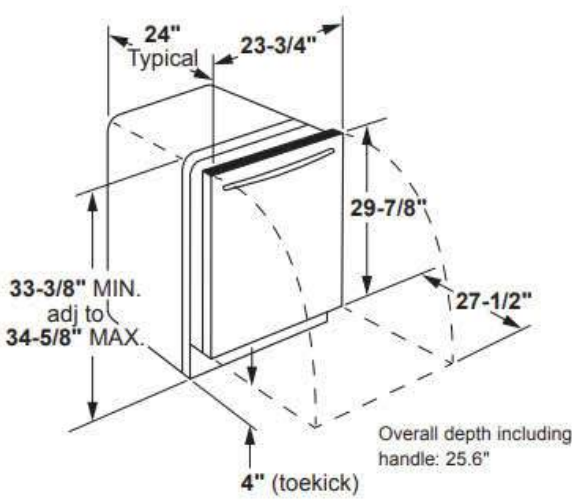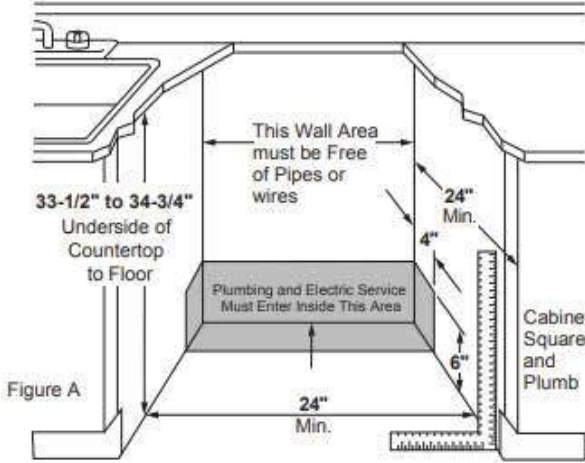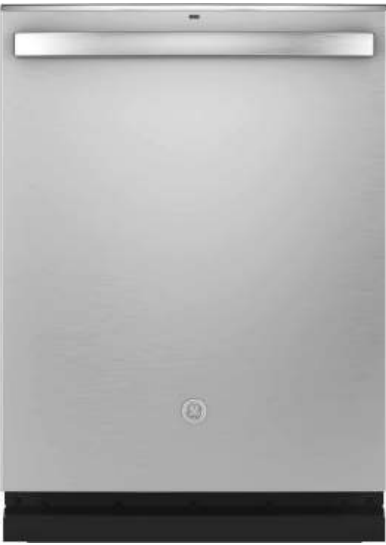



Fridge

Name: GE ENERGY STAR 27.0 Cu. Ft. Fingerprint Resistant French-Door Refrigerator
Model: GNE27JYMFS
Dimensions: 69 7/8 H x 35 3/4 W x 35 7/8 D
https://www.geappliances.com/appliance/GE-ENERGY-STAR-27-0-Cu-Ft-Fingerprint-Resistant-French-Door-Refrigerator-GNE27JYMFS



DIMENSIONS AND INSTALLATION INFORMATION (IN INCHES)

OVERALL DIMENSIONS	Height to top of door - crown or flat (in.) A	69-7/8
	Height to top of hinge (in.) B	69-3/4
	Height to top of case (in.) C	68-5/8
	Case depth without door (in.) D	29
	Case depth less door handle (in.) E	33-3/8
	Case depth with door handle (in.) F	35-7/8
	Depth with fresh food door open 90° (in.) G	48-3/8
	Width (in.) H	35-3/4
	Width with door open 90° inc. door handle (in.) I	43-3/4
AIR CLEARANCES	Each side (in.)	1/8
	Top (in.)	1
	Back (in.)	2

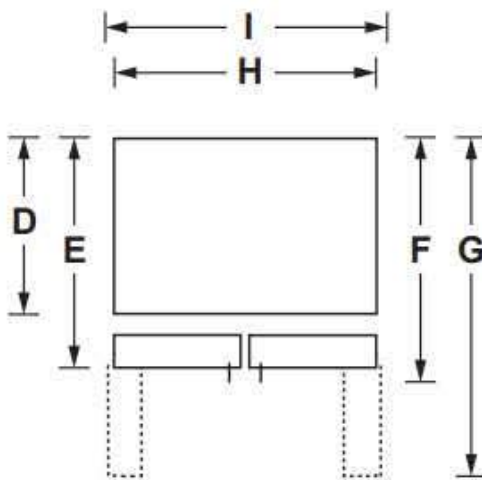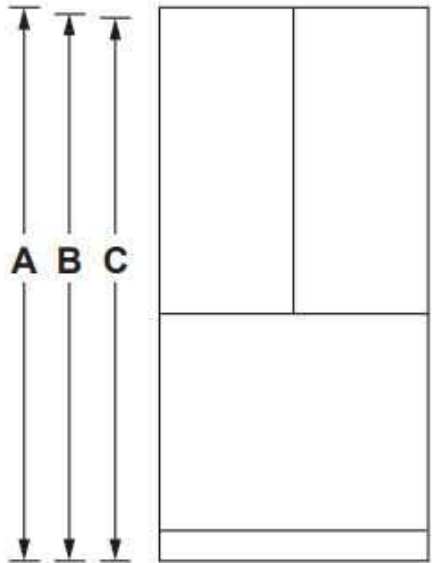

- THESE DRAWINGS MUST BE CHECKED BY THE CUSTOMER OR CONTRACTOR PRIOR TO APPROVAL. ANY ERRORS OR OMISSIONS MUST BE REPORTED IN WRITING TO BAUHU PRIOR TO COMMENCEMENT OF CONSTRUCTION.
- ARCHITECTURAL DRAWINGS SHOULD BE READ IN CONJUNCTION WITH STRUCTURAL DETAILING AND FABRICATION GENERAL ASSEMBLY DRAWINGS.
- FOR CONSTRUCTION PURPOSES, USE ONLY THE LATEST APPROVED DRAWINGS LABELED 'ISSUED FOR CONSTRUCTION'.
- DO NOT SCALE FROM THIS DRAWING.
- THE COMPANY OPERATES USING METRIC DIMENSIONS AS THE PRINCIPAL DENOMINATION.
- ALL CONCRETE WORKS ARE OUTSIDE OF THE SCOPE OF THE COMPANY. INFORMATION REGARDING SLAB DESIGN AND CONNECTIONS IN THESE DRAWINGS ARE INTENDED FOR GUIDENCE ONLY. FOUNDATION AND SLAB WORKS SHOULD BE DESIGNED AND APPROVED BY A LOCAL STRUCTURAL ENGINEER.
- THE COMPANY RETAINS FULL TITLE AND OWNERSHIP OF THESE PLANS AND DESIGNS. ANY UNAUTHORISED USE, REPRODUCTION, OR DISTRIBUTION OF THESE PLANS, WHETHER IN WHOLE OR PART, IS EXPRESSLY PROHIBITED WITHOUT PRIOR WRITTEN CONSENT.
- THE HYBRID STEEL FRAME CONSTRUCTION SYSTEM AND METHODOLOGY (PATENT PENDING) DESCRIBED IN THESE PLANS HAS BEEN DEVELOPED BY THE COMPANY AND IS SUBJECT TO A PROVISIONAL PATENT APPLICATION & ASSIGNMENT - US APPLICATION NO. 63/722,841

No.	Revision	Date

ISSUED FOR:

Issued for information

Issued for client approval

Issued for fabrication

Issued for construction

Coconut Villa
3 Bed

DRAWING TITLE:	Kitchen Appliances
DRAWN BY:	Y.A.Clark
SCALE:	
DRAWING NO:	A119
DATE:	16/02/2026

Note:

- Kitchen appliances are shown for cabinet design purposes only and are not supplied.

- THESE DRAWINGS MUST BE CHECKED BY THE CUSTOMER OR CONTRACTOR PRIOR TO APPROVAL. ANY ERRORS OR OMISSIONS MUST BE REPORTED IN WRITING TO BAUHU PRIOR TO COMMENCEMENT OF CONSTRUCTION.
- ARCHITECTURAL DRAWINGS SHOULD BE READ IN CONJUNCTION WITH STRUCTURAL DETAILING AND FABRICATION GENERAL ASSEMBLY DRAWINGS.
- FOR CONSTRUCTION PURPOSES, USE ONLY THE LATEST APPROVED DRAWINGS LABELED 'ISSUED FOR CONSTRUCTION'.
- DO NOT SCALE FROM THIS DRAWING.
- THE COMPANY OPERATES USING METRIC DIMENSIONS AS THE PRINCIPAL DENOMINATION.
- ALL CONCRETE WORKS ARE OUTSIDE OF THE SCOPE OF THE COMPANY. INFORMATION REGARDING SLAB DESIGN AND CONNECTIONS IN THESE DRAWINGS ARE INTENDED FOR GUIDANCE ONLY. FOUNDATION AND SLAB WORKS SHOULD BE DESIGNED AND APPROVED BY A LOCAL STRUCTURAL ENGINEER.
- THE COMPANY RETAINS FULL TITLE AND OWNERSHIP OF THESE PLANS AND DESIGNS. ANY UNAUTHORISED USE, REPRODUCTION, OR DISTRIBUTION OF THESE PLANS, WHETHER IN WHOLE OR PART, IS EXPRESSLY PROHIBITED WITHOUT PRIOR WRITTEN CONSENT.
- THE HYBRID STEEL FRAME CONSTRUCTION SYSTEM AND METHODOLOGY (PATENT PENDING) DESCRIBED IN THESE PLANS HAS BEEN DEVELOPED BY THE COMPANY AND IS SUBJECT TO A PROVISIONAL PATENT APPLICATION & ASSIGNMENT - US APPLICATION NO. 63/722,841

No.	Revision	Date

ISSUED FOR:

Issued for information

Issued for client approval

Issued for fabrication

Issued for construction

Coconut Villa 3 Bed

DRAWING TITLE:

Dimensions Ground Floor

DRAWN BY:

Y.A.Clark

SCALE:

1 : 50

DRAWING NO:

A120

DATE:

16/02/2026

A110

1 Rear Elevation

2 Front Elevation

A110

A111

1 Left Elevation

2 Right Elevation

A111

CKT. NO.	IDENTIFICATION	CIRCUIT BREAKER		
		BKR.	WIRE	KW.
1	General Lightning and Receptacles	15 A.	# 14	
2	General Lightning and Receptacles	15 A.	# 14	
3	General Lightning and Receptacles	15 A.	# 14	
4	General Lightning and Receptacles	15 A.	# 14	
5	General Lightning and Receptacles	15 A.	# 14	
6	GFI Receptacles	20 A.	# 12	
7	General Lightning and Receptacles	15 A.	# 14	
8	Kitchen Small Appliance Receptacles	20 A.	# 12	
9	Kitchen Small Appliance Receptacles	20 A.	# 12	1.5
10	Garbage Disposer	20 A.	# 12	1.2
11	Outdoor Lightning and Receptacles	20 A.	# 12	1.5
12	Dishwasher	20 A.	# 12	1.2
13	Refrigerator	20 A.	# 12	1.2
14	Microwave	20 A.	# 12	
15 17	Range/Oven	50 A.	# 6	12
16 18	AC/MSCU #1 (Living Room)	30 A.	# 10	3.6
19 21	Water Heater #1	30 A.	# 10	4.5
20 22	AC/MSCU #2 (Dining/Kitchen)	30 A.	# 10	3.6
23 25	AC/MSU #3 (Master Bedroom)	30 A.	# 10	3.6
24 26	AC/MSU #4 (Bedroom 2)	30 A.	# 10	3.6
27	Spare			
28 30	AC/MSU #5 (Bedroom 3)	30 A.	# 10	3.6
29	Spare			

[illegible]

Issued for information

Issued for client approval

Issued for fabrication

Issued for construction

Coconut Villa 3 Bed

Electrical Plan - Ground Floor


Y.A.Clark

As indicated

A121

16/02/2026


Electric Plan Sc: 1/60

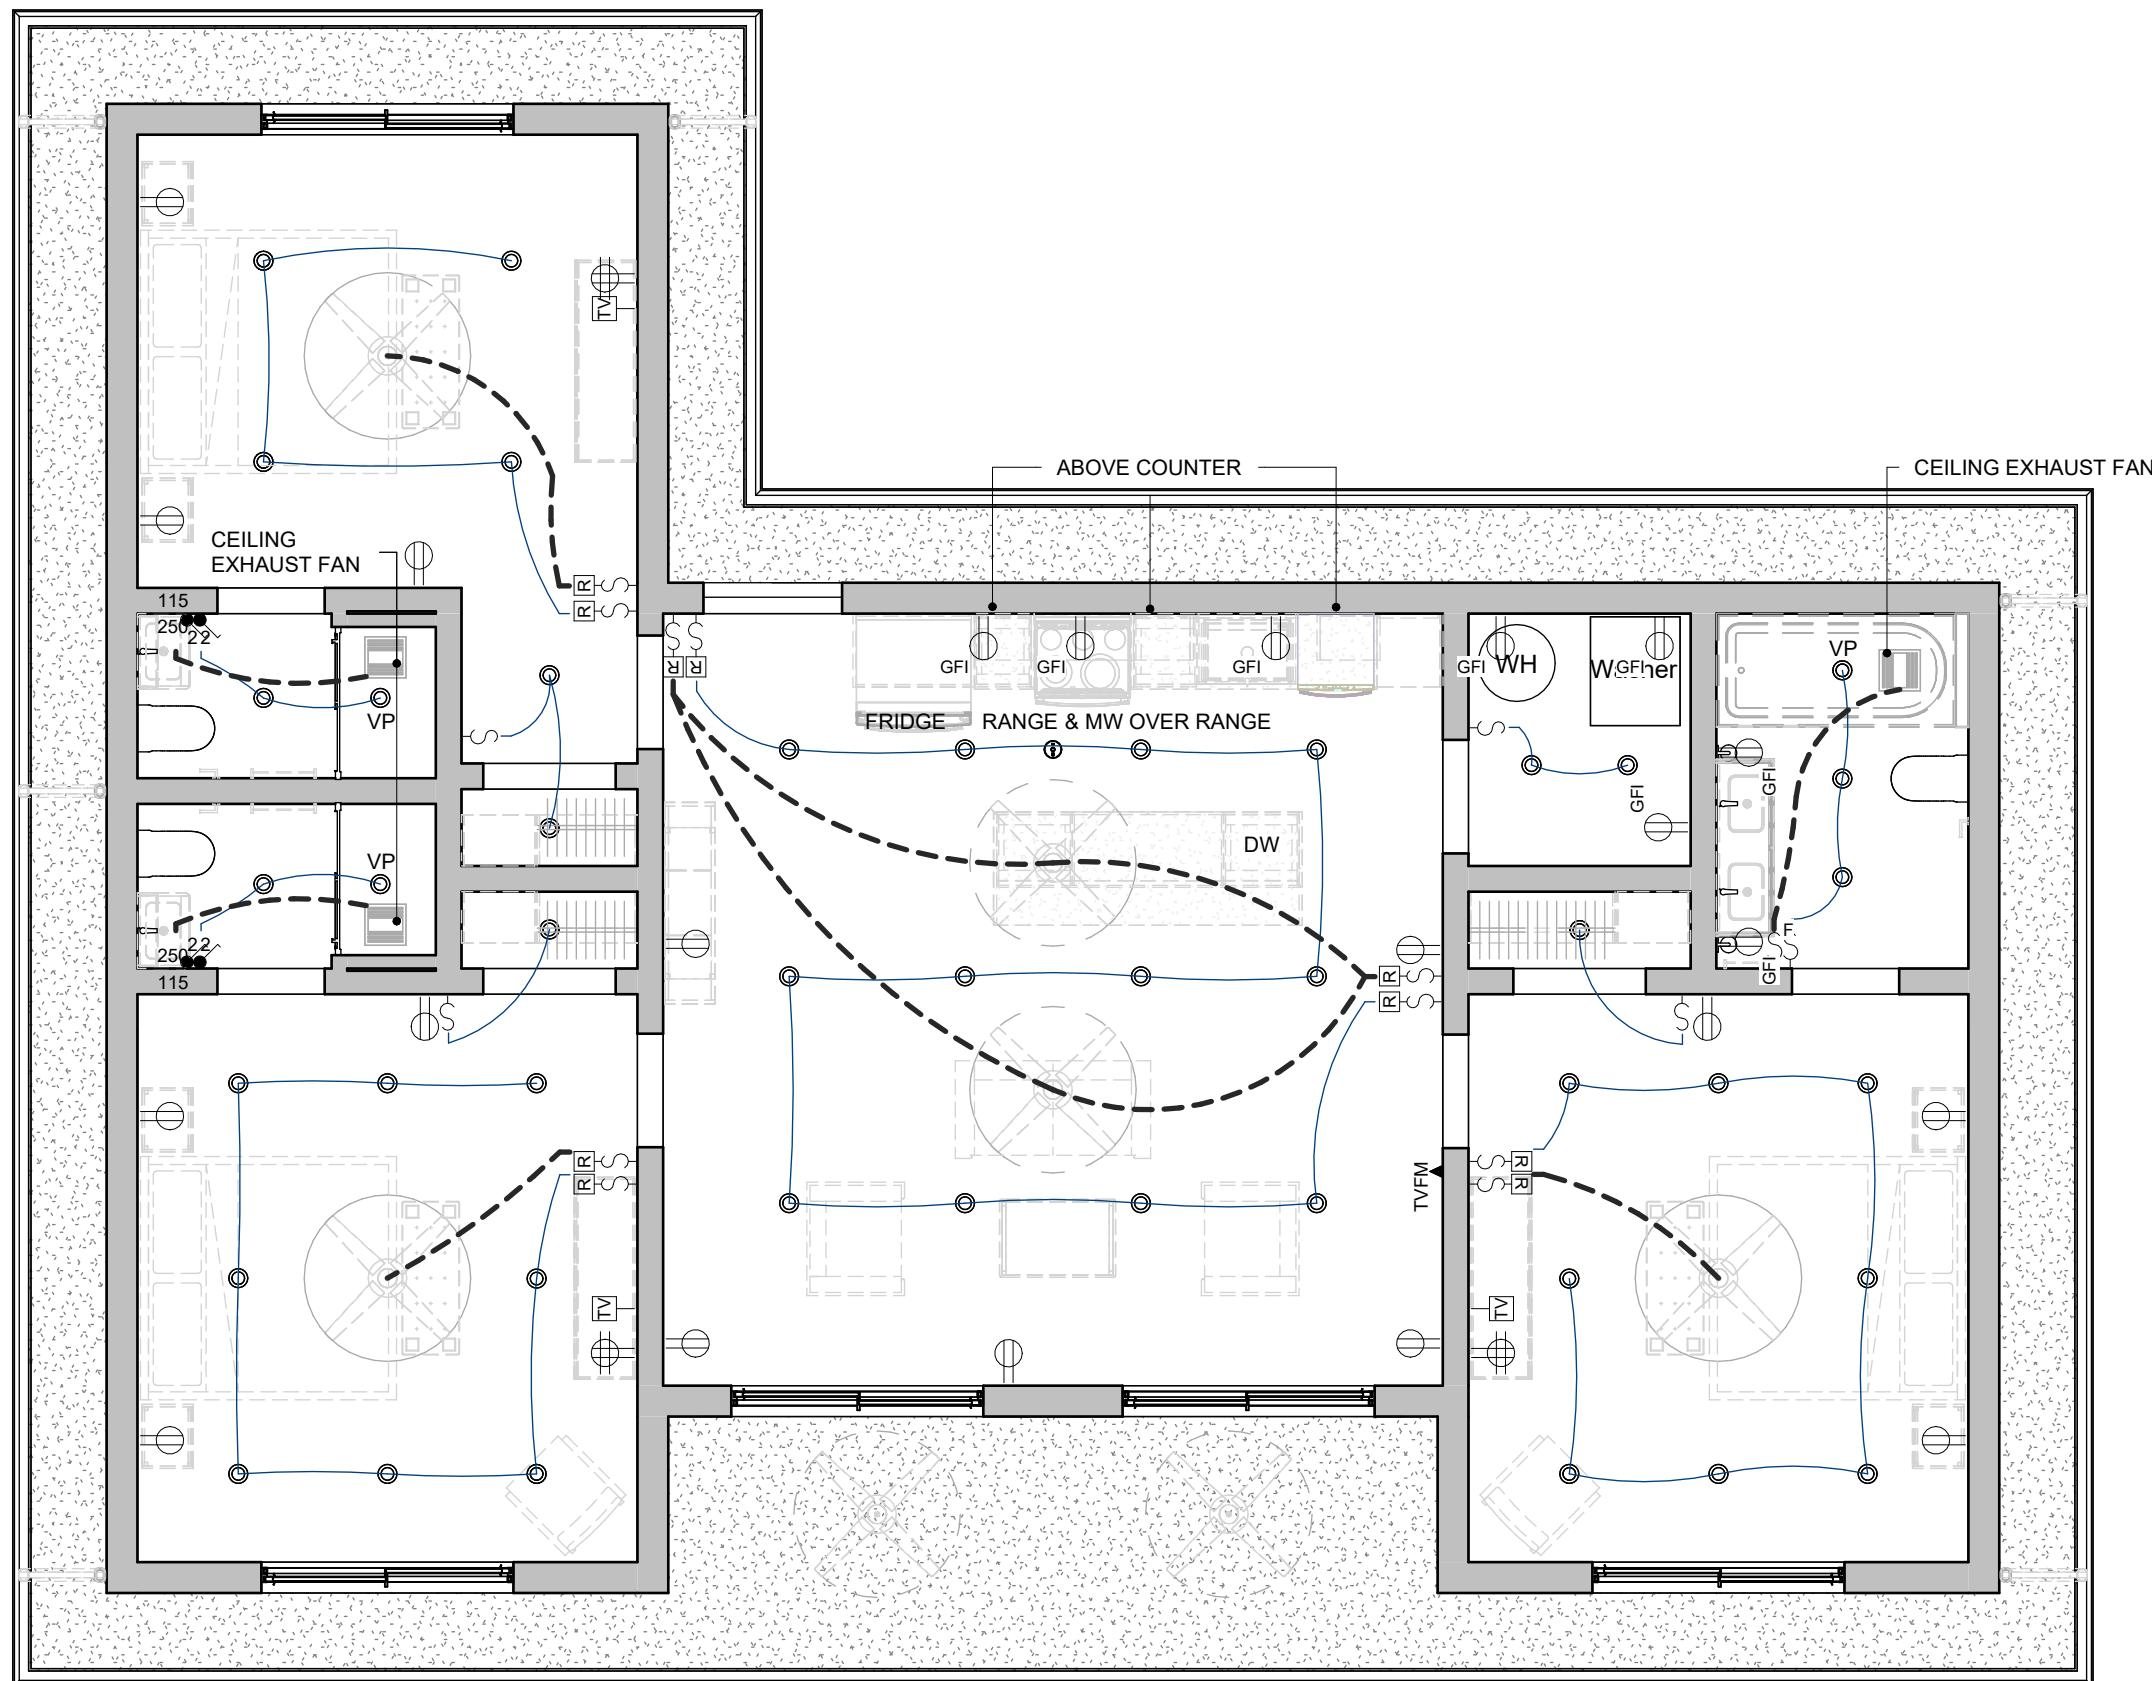


	Television Outlet
	Duplex Outlet
	Quad Outlet
	GFI Outlet
	Waterproof GFI Outlet
	Single Switch
	Double Switch
	Ceiling Exhaust Fan Switch
	Rheostat Switch

- The electrical and HVAC installation including cables, conduits, surface mounted switches, power outlets, light fittings, fans, extractors, water heating equipment, air conditioning equipment, kitchen appliances, solar appliances, data and communication equipment, other electrical fixtures and fittings, are not supplied. Electrical plans are provided as a guide for contractor information only. Electrical system design, supply and installation should be carried out by a competent electrician.
- Electrical engineer to provide adequate grounding to all steel members.
- Air conditioning and flood vents by others.


Panel "B" Feeder
 (3) #3 CU W/
 (1) #8 CU GND. In 2" C.

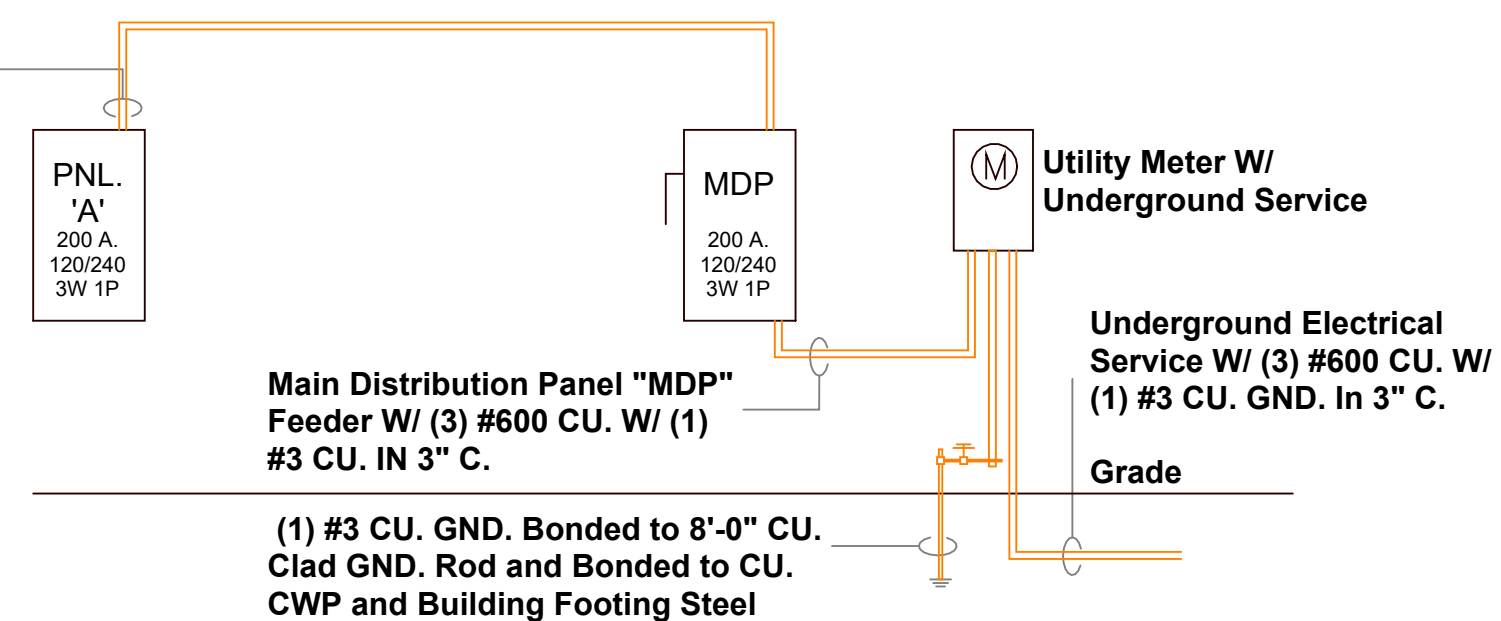


Typical Plumbing Riser Plan

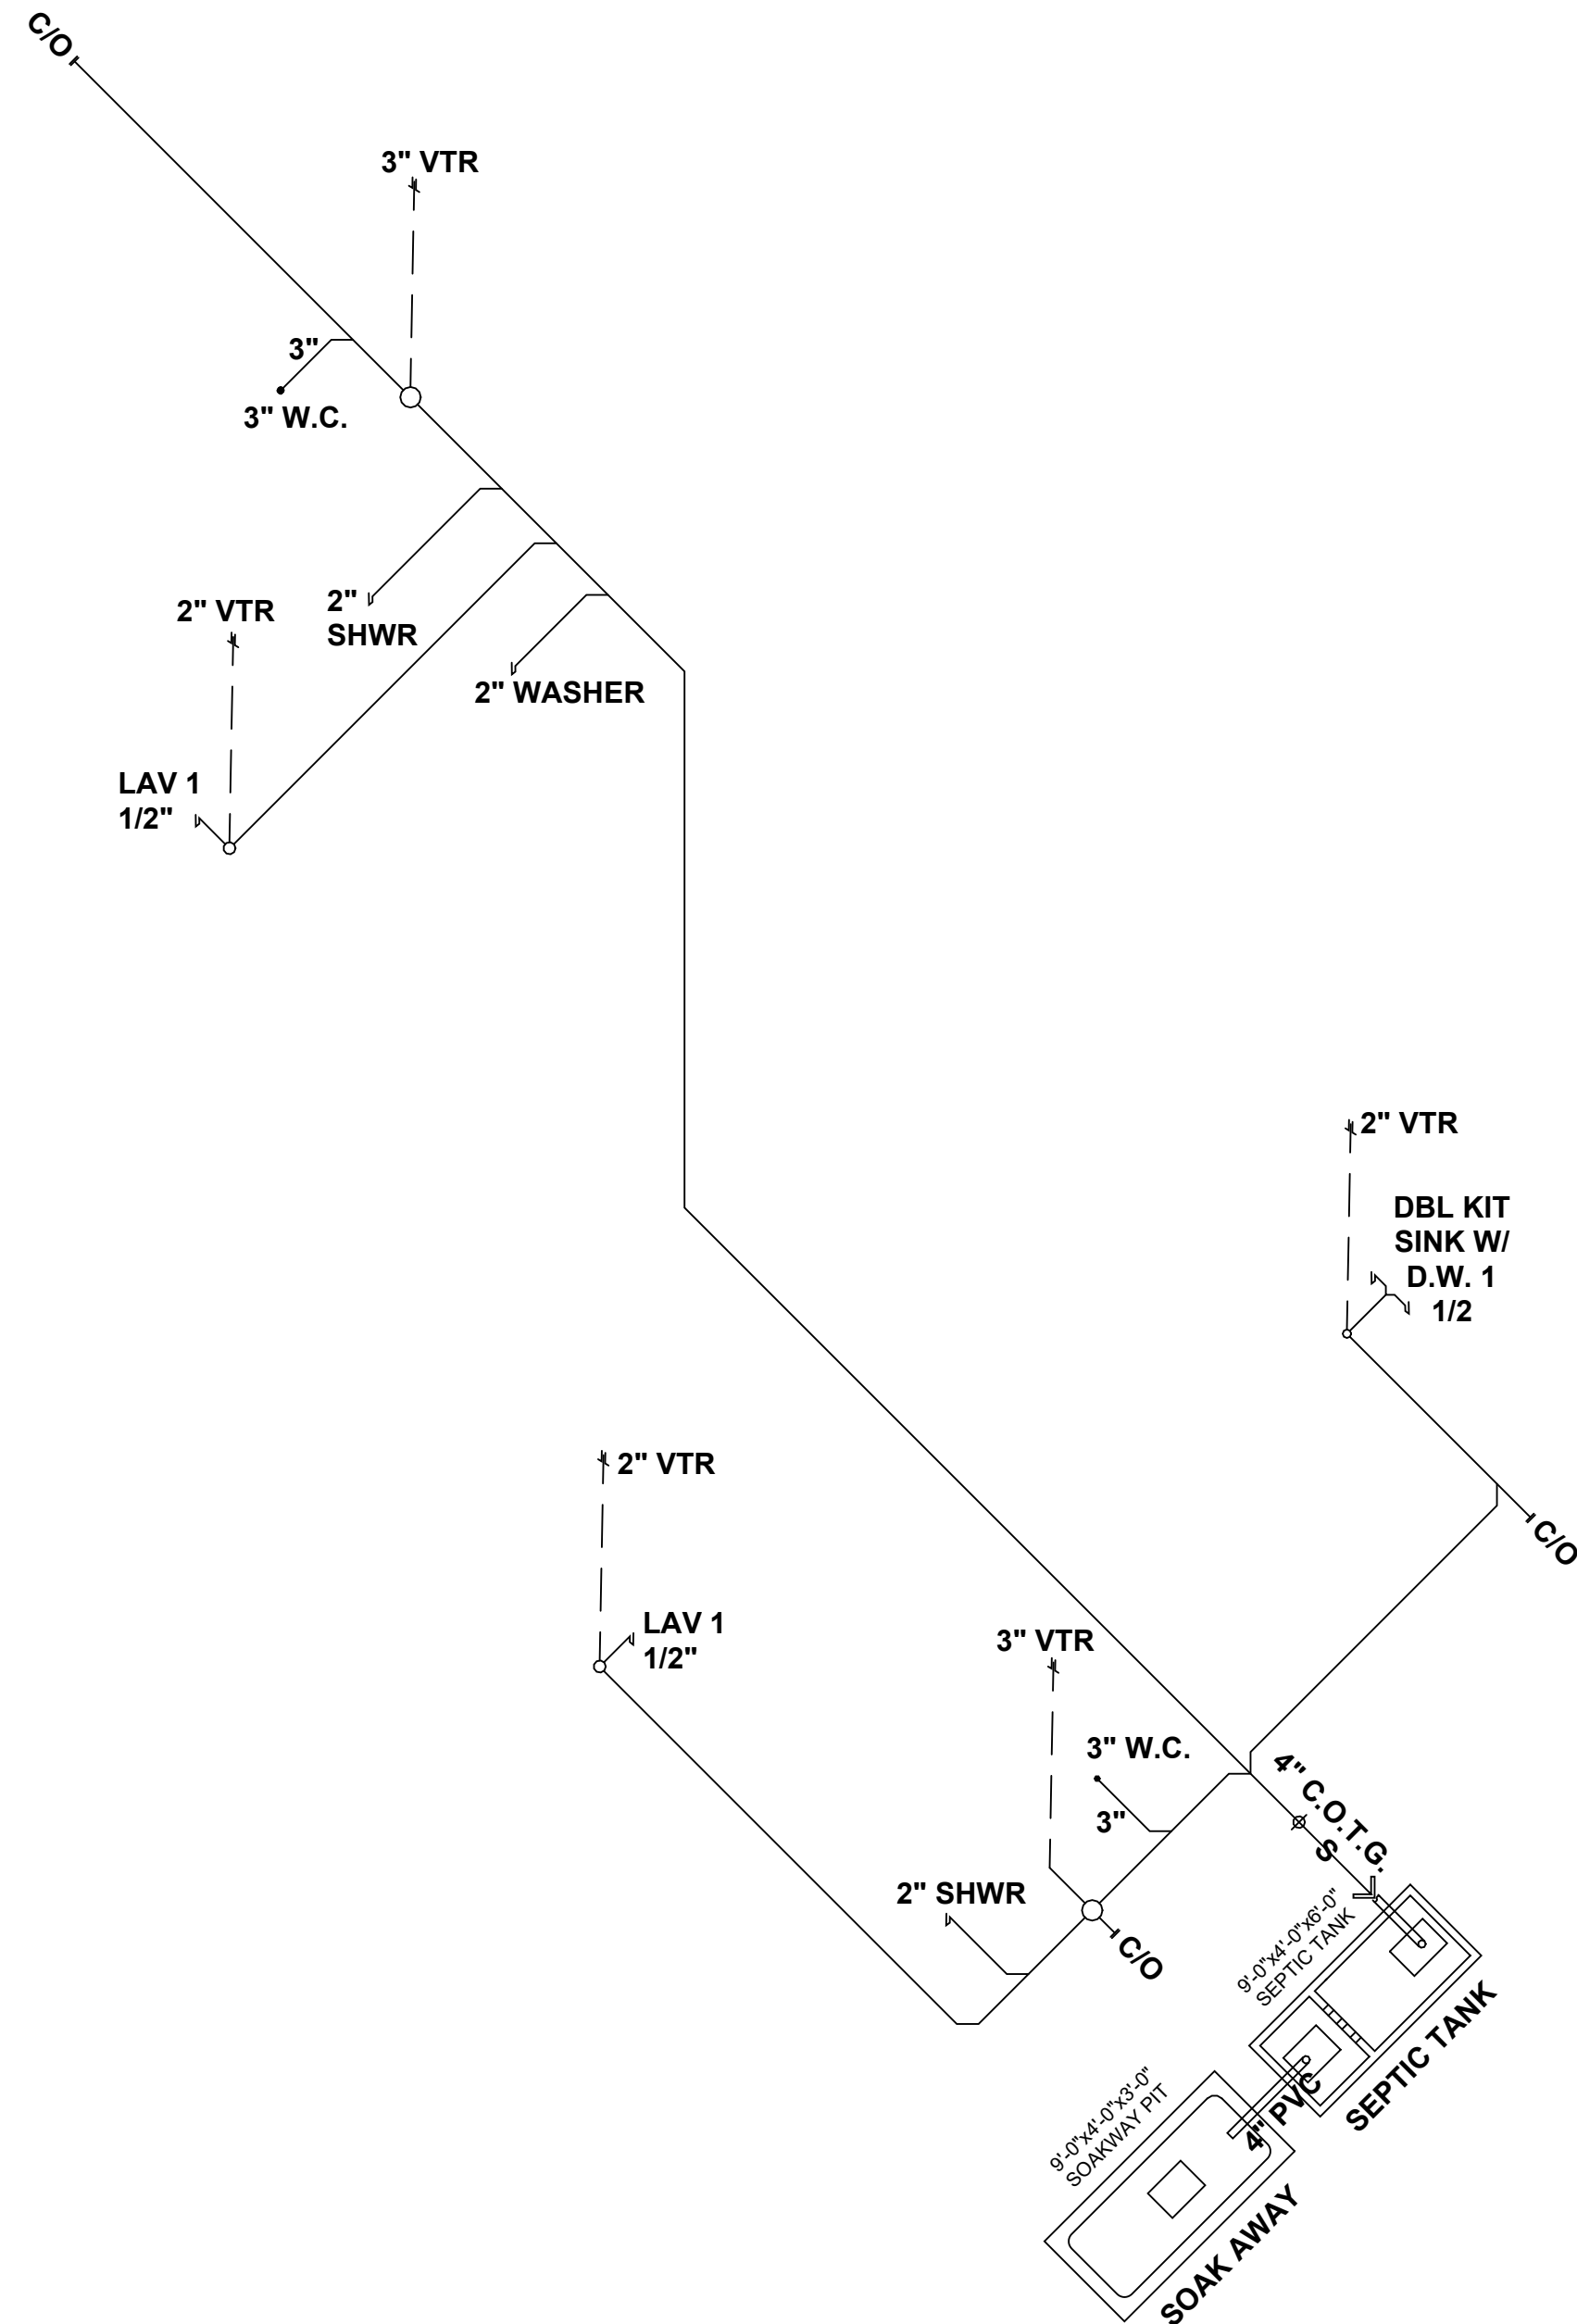

Typical Piping at Water Heater

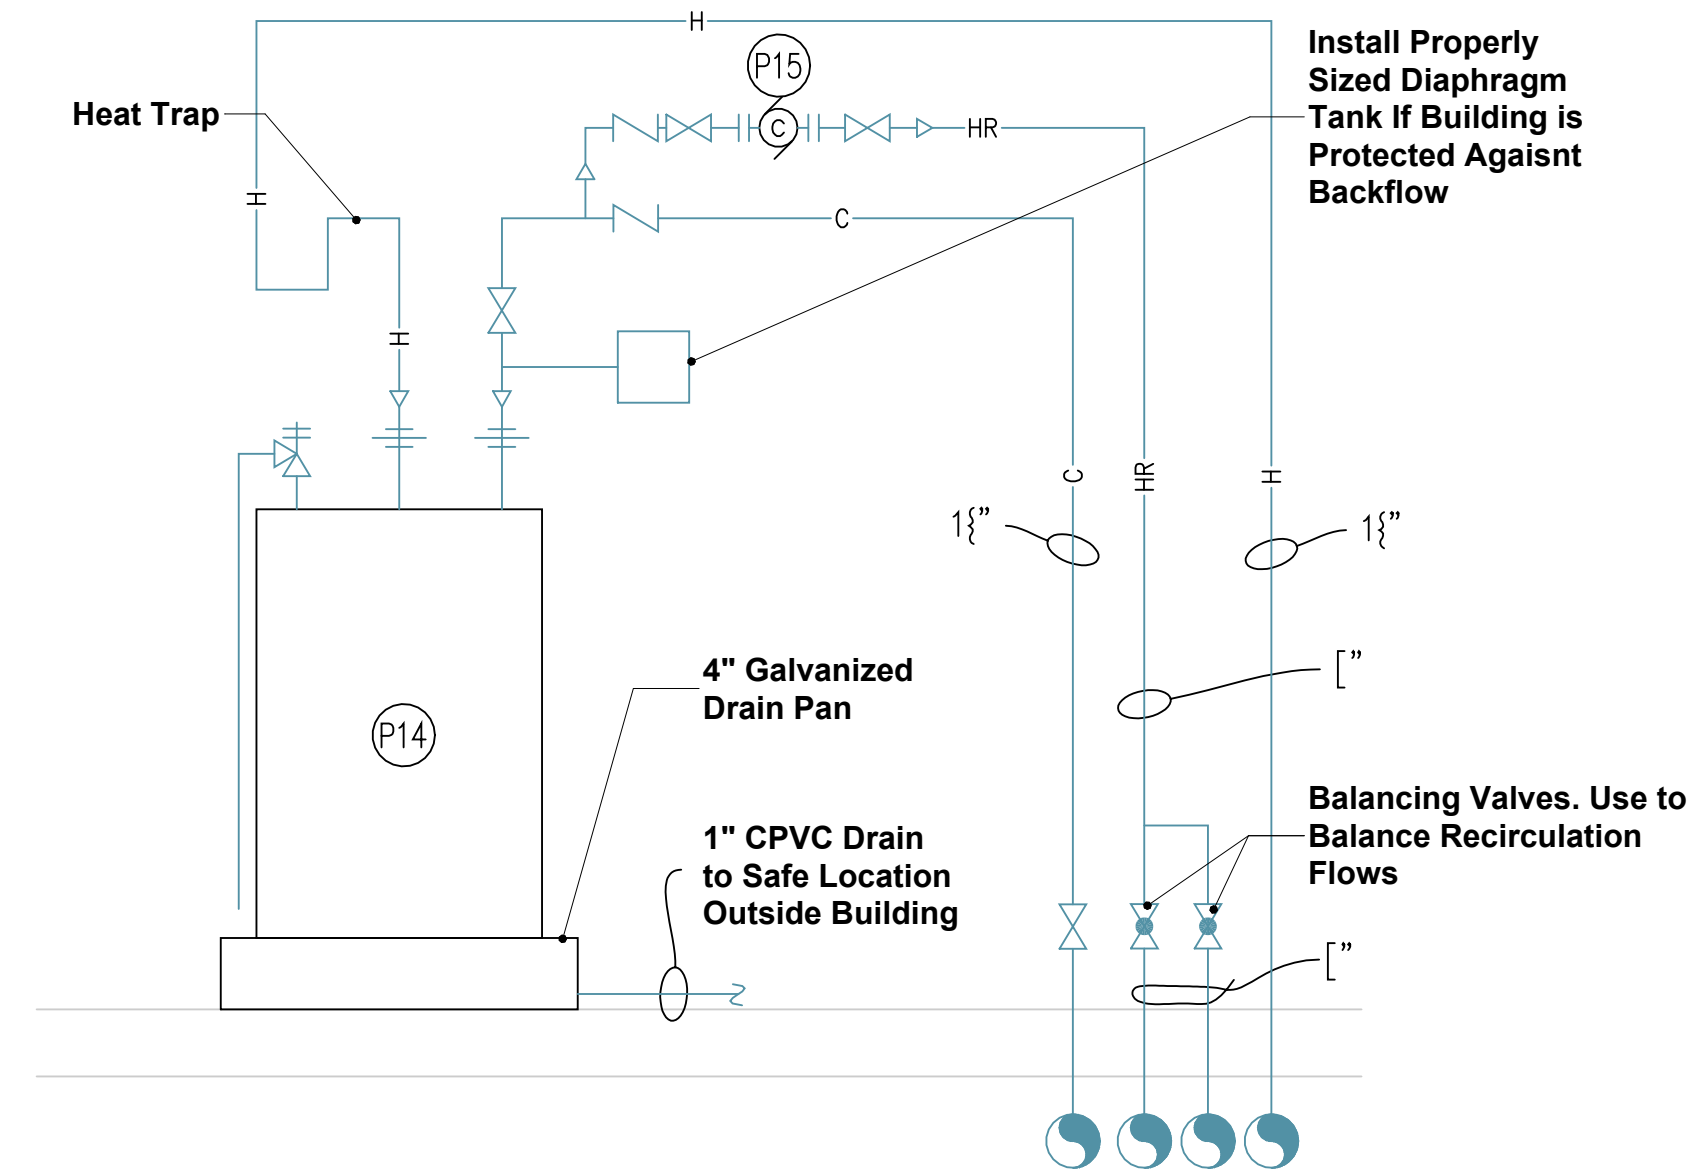

Typical Sceptic Tank & Soak Away Section

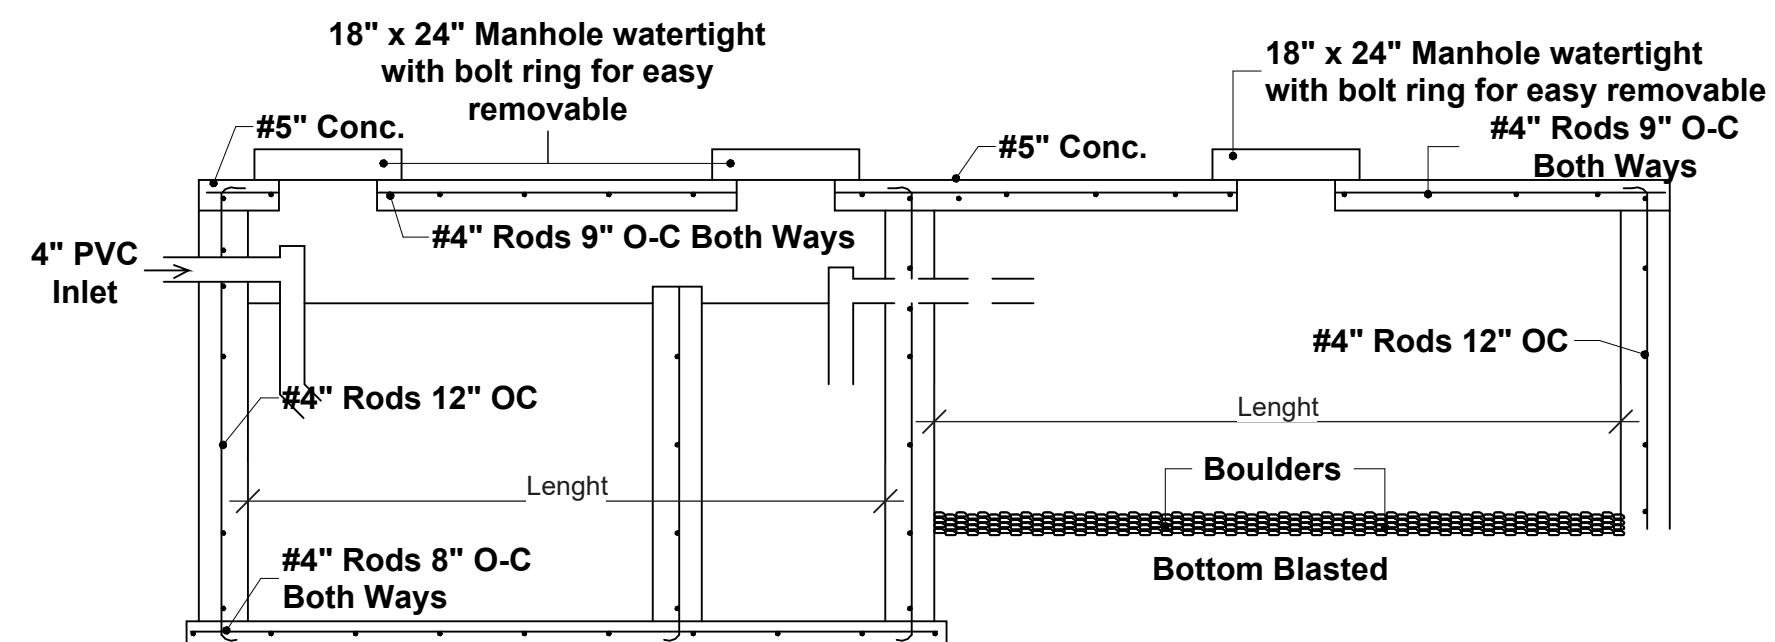

Note: Plumbing supply pipework, waste pipework, rainwater drain pipework, gutters, downpipes, pipe connections and sub-slab roughing 's are excluded. Plumbing plans are provided as a guide for contractor information only.

1. THESE DRAWINGS MUST BE CHECKED BY THE CUSTOMER OR CONTRACTOR PRIOR TO APPROVAL. ANY ERRORS OR OMISSIONS MUST BE REPORTED IN WRITING TO BAUHU PRIOR TO COMMENCEMENT OF CONSTRUCTION.
2. ARCHITECTURAL DRAWINGS SHOULD BE READ IN CONJUNCTION WITH STRUCTURAL DETAILING AND FABRICATION GENERAL ASSEMBLY DRAWINGS.
3. FOR CONSTRUCTION PURPOSES, USE ONLY THE LATEST APPROVED DRAWINGS LABELED 'ISSUED FOR CONSTRUCTION'.
4. DO NOT SCALE FROM THIS DRAWING.
5. THE COMPANY OPERATES USING METRIC DIMENSIONS AS THE PRINCIPAL DENOMINATION.
6. ALL CONCRETE WORKS ARE OUTSIDE OF THE SCOPE OF THE COMPANY. INFORMATION REGARDING SLAB DESIGN AND CONNECTIONS IN THESE DRAWINGS ARE INTENDED FOR GUIDANCE ONLY. FOUNDATION AND SLAB WORKS SHOULD BE DESIGNED AND APPROVED BY A LOCAL STRUCTURAL ENGINEER.
7. THE COMPANY RETAINS FULL TITLE AND OWNERSHIP OF THESE PLANS AND DESIGNS. ANY UNAUTHORISED USE, REPRODUCTION, OR DISTRIBUTION OF THESE PLANS, WHETHER IN WHOLE OR PART, IS EXPRESSLY PROHIBITED WITHOUT PRIOR WRITTEN CONSENT.
8. THE HYBRID STEEL FRAME CONSTRUCTION SYSTEM AND METHODOLOGY (PATENT PENDING) DESCRIBED IN THESE PLANS HAS BEEN DEVELOPED BY THE COMPANY AND IS SUBJECT TO A PROVISIONAL PATENT APPLICATION & ASSIGNMENT - US PATENT NO. 63/722,841

[illegible]

ISSUED FOR:

Issued for information

Issued for client approval

Issued for fabrication

Issued for construction

Coconut Villa 3 Bed

DRAWING TITLE:

Plumbing

DRAWN BY:

Y.A.Clark

SCALE:

DRAWING NO:

A122

DATE:

16/02/2026

Hot Water
Cold Water



Note: Plumbing supply pipework, waste pipework, rainwater drain pipework, gutters, downpipes, pipe connections and sub-slab roughing 's are excluded. Plumbing plans are provided as a guide for contractor information only.

1. THESE DRAWINGS MUST BE CHECKED BY THE CUSTOMER OR CONTRACTOR PRIOR TO APPROVAL. ANY ERRORS OR OMISSIONS MUST BE REPORTED IN WRITING TO BAUHU PRIOR TO COMMENCEMENT OF CONSTRUCTION.
2. ARCHITECTURAL DRAWINGS SHOULD BE READ IN CONJUNCTION WITH STRUCTURAL DETAILING AND FABRICATION GENERAL ASSEMBLY DRAWINGS.
3. FOR CONSTRUCTION PURPOSES, USE ONLY THE LATEST APPROVED DRAWINGS LABELED 'ISSUED FOR CONSTRUCTION'.
4. DO NOT SCALE FROM THIS DRAWING.
5. THE COMPANY OPERATES USING METRIC DIMENSIONS AS THE PRINCIPAL DENOMINATION.
6. ALL CONCRETE WORKS ARE OUTSIDE OF THE SCOPE OF THE COMPANY. INFORMATION REGARDING SLAB DESIGN AND CONNECTIONS IN THESE DRAWINGS ARE INTENDED FOR GUIDANCE ONLY. FOUNDATION AND SLAB WORKS SHOULD BE DESIGNED AND APPROVED BY A LOCAL STRUCTURAL ENGINEER.
7. THE COMPANY RETAINS FULL TITLE AND OWNERSHIP OF THESE PLANS AND DESIGNS. ANY UNAUTHORISED USE, REPRODUCTION, OR DISTRIBUTION OF THESE PLANS, WHETHER IN WHOLE OR PART, IS EXPRESSLY PROHIBITED WITHOUT PRIOR WRITTEN CONSENT.
8. THE HYBRID STEEL FRAME CONSTRUCTION SYSTEM AND METHODOLOGY (PATENT PENDING) DESCRIBED IN THESE PLANS HAS BEEN DEVELOPED BY THE COMPANY AND IS SUBJECT TO A PROVISIONAL PATENT APPLICATION & ASSIGNMENT - US APPLICATION NO. 63/722,841

No.	Revision	Date


- ISSUED FOR:
- ☒ Issued for information
 - ☐ Issued for client approval
 - ☐ Issued for fabrication
 - ☐ Issued for construction

Coconut Villa
3 Bed

DRAWING TITLE:	Plumbing Plan Ground Floor
DRAWN BY:	Y.A.Clark
SCALE:	1 : 50
DRAWING NO:	A123
DATE:	16/02/2026

Toilet


Sanindusa
Model: Winner Confort F|D close coupled toilet
Reference: 144021
Dimensions: L65xW37xH47
Finishes: Vitreous China 00-White
Count: 3

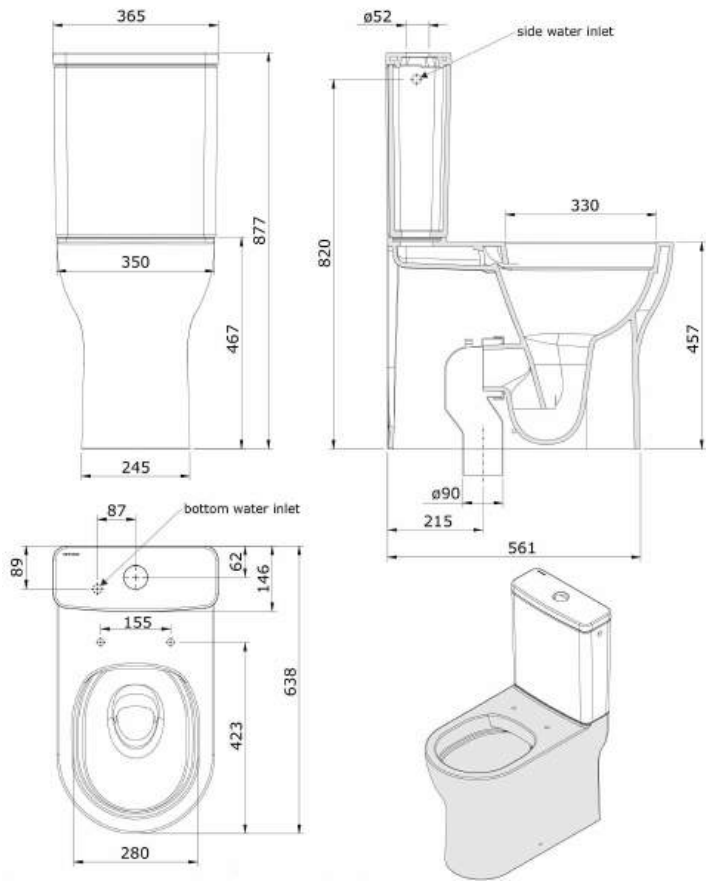

https://www.tec.sanindusa.pt/index.php?id=25&p=4573

Vanity Mixer

Bruma
Model: Nautic
Reference: 181 010 1CR
Finishes: Chrome
Count: 4
Room No: 2&4&10 (2)

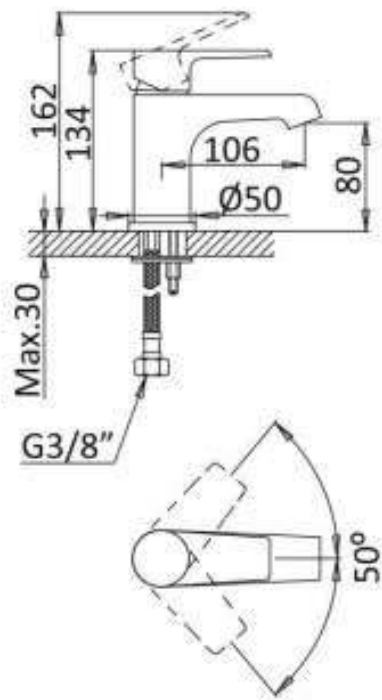

https://www.bruma.pt

Toilet Seat


Sanindusa
Model: Winner toilet seat with easyclip system
Reference: 24231
Finishes: Duroplast - 00-Chrome|White
Count: 3



https://www.tec.sanindusa.pt/index.php?id=25&p=4573

Kitchen Mixer


Bruma
Model: Kitchen Faucets
Name: Sink mixer with swivel spout and pull out handshower - Ginger
Reference: 122 700 3CR
Colour: Chrome
Count: 1

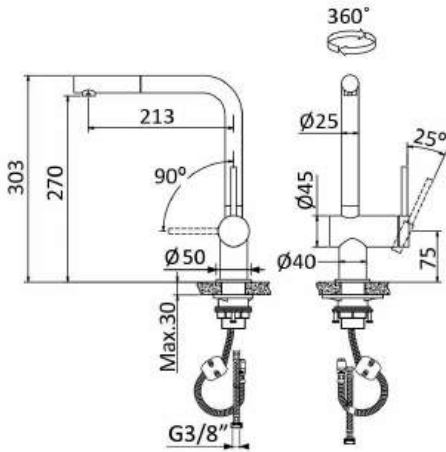

https://www.bruma.pt

Toilet roll holder

Bruma
Model: MARIS
Reference: 177 000 7CR
Finishes: Chrome
Count: 3
Room No: 2&4&10

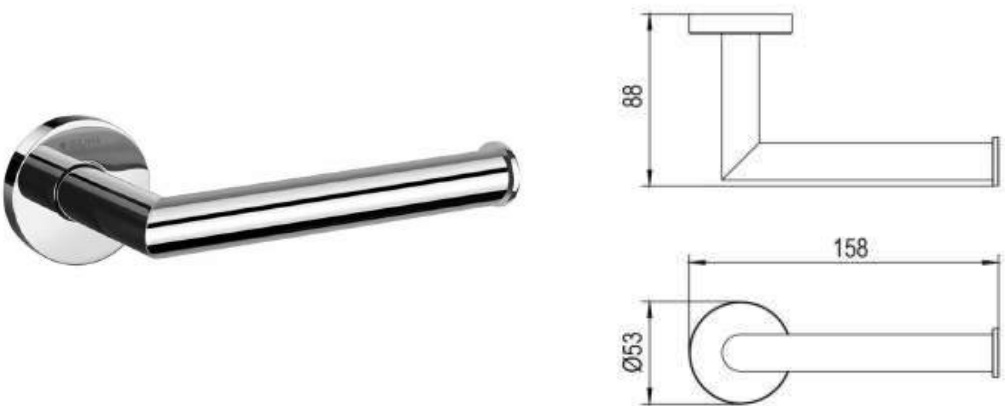

https://www.bruma.pt/index.php?page=products&prod=7734#open_product

Note:
• Sanitary ware, faucets, kitchen and bathroom equipment are provided. Plumbing supply pipework, waste and sub-slab roughings are excluded. Plumbing plan is provided as a guide for contractor information only.
• Shower glass screens are fixed.



1. THESE DRAWINGS MUST BE CHECKED BY THE CUSTOMER OR CONTRACTOR PRIOR TO APPROVAL. ANY ERRORS OR OMISSIONS MUST BE REPORTED IN WRITING TO BAUHU PRIOR TO COMMENCEMENT OF CONSTRUCTION.
2. ARCHITECTURAL DRAWINGS SHOULD BE READ IN CONJUNCTION WITH STRUCTURAL DETAILING AND FABRICATION GENERAL ASSEMBLY DRAWINGS.
3. FOR CONSTRUCTION PURPOSES, USE ONLY THE LATEST APPROVED DRAWINGS LABELED 'ISSUED FOR CONSTRUCTION'.
4. DO NOT SCALE FROM THIS DRAWING.
5. THE COMPANY OPERATES USING METRIC DIMENSIONS AS THE PRINCIPAL DENOMINATION.
6. ALL CONCRETE WORKS ARE OUTSIDE OF THE SCOPE OF THE COMPANY. INFORMATION REGARDING SLAB DESIGN AND CONNECTIONS IN THESE DRAWINGS ARE INTENDED FOR GUIDENCE ONLY. FOUNDATION AND SLAB WORKS SHOULD BE DESIGNED AND APPROVED BY A LOCAL STRUCTURAL ENGINEER.
7. THE COMPANY RETAINS FULL TITLE AND OWNERSHIP OF THESE PLANS AND DESIGNS. ANY UNAUTHORISED USE, REPRODUCTION, OR DISTRIBUTION OF THESE PLANS, WHETHER IN WHOLE OR PART, IS EXPRESSLY PROHIBITED WITHOUT PRIOR WRITTEN CONSENT.
8. THE HYBRID STEEL FRAME CONSTRUCTION SYSTEM AND METHODOLOGY (PATENT PENDING) DESCRIBED IN THESE PLANS HAS BEEN DEVELOPED BY THE COMPANY AND IS SUBJECT TO A PROVISIONAL PATENT APPLICATION & ASSIGNMENT - US APPLICATION NO. 63/722,841

No.	Revision	Date

ISSUED FOR:

Issued for information

Issued for client approval

Issued for fabrication

Issued for construction

Coconut Villa

3 Bed

DRAWING TITLE:	Bathroom Schedule
DRAWN BY:	Y.A.Clark
SCALE:	
DRAWING NO:	A124
DATE:	16/02/2026

Bathtub



Sanindusa
Model: Vértice
Name: 190x90 Vértice bathtub
Reference: 806200
Finishes: 00-White
Dimensions: 900x1900 mm
Count: 1
Room No: 10
Note:
Side panel - Panel Vértice 190 - Code: 806201
50 automatic pop-up waste for bathtub - Code:490
80 fixing kit for bathtub - Code: 813



<https://www.tec.sanindusa.pt/panel-vertice-190>
<https://www.tec.sanindusa.pt/50-automatic-pop-up-for-bathtub>
<https://www.tec.sanindusa.pt/80-fix-kit-feets-for-bathtub>
<https://www.tec.sanindusa.pt/bathtub-vertice-190x90>

Shower Tray

Sanindusa
Model: Piano rectangular shower tray
Reference: 8024300000
Colours: White
Dimensions: 1200x800x75mm
Count: 2
Room No: 2&4

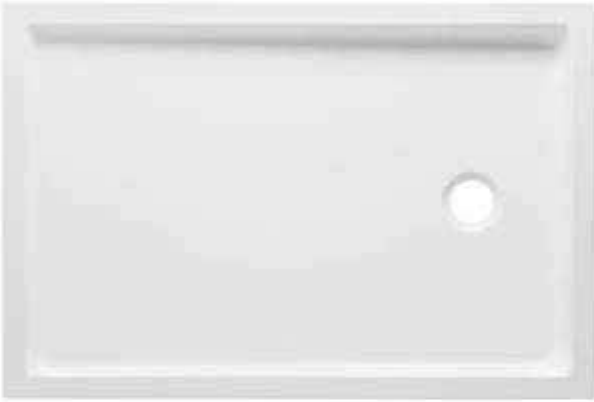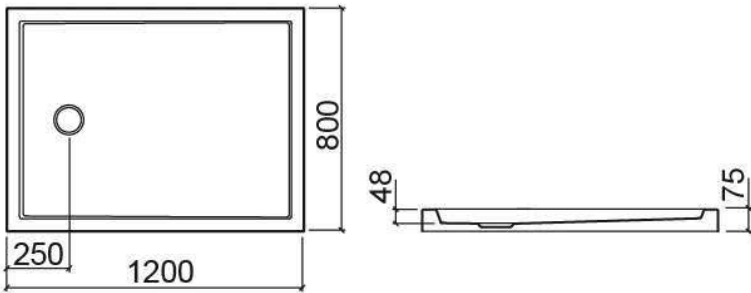


Waste: Ø90 waste for shower tray / REF.48711 / Chrome
Count: 2

<https://sanindusa.com/en/product/90-waste-shower-tray>

<https://sanindusa.com/en/product/piano-rectangular-showertray>

Shower System

Bruma
Model: Nautic
Name: Shower system for wall mounting with adjustable ABS head shower Ø230mm and shower rail
Reference: 181 271 1CR
Colour: Chrome
Count: 2
Room No: 2&4

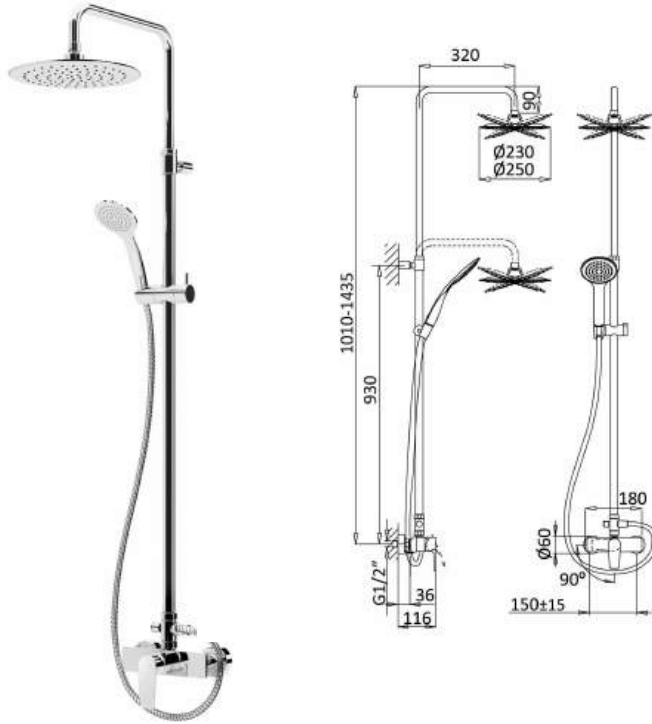


<https://www.bruma.pt>

Note:
• Sanitary ware, faucets, kitchen and bathroom equipment are provided. Plumbing supply pipework, waste and sub-slab roughings are excluded. Plumbing plan is provided as a guide for contractor information only.
• Shower glass screens are fixed.

Bath Screen

Sanindusa
Model: Safira
Name: Safira bath screen
Reference: 89510100
Finishes: Chrome - 5mm tempered glass
Dimensions: 136cm H, 82cm L
Count: 1
Room No: 10

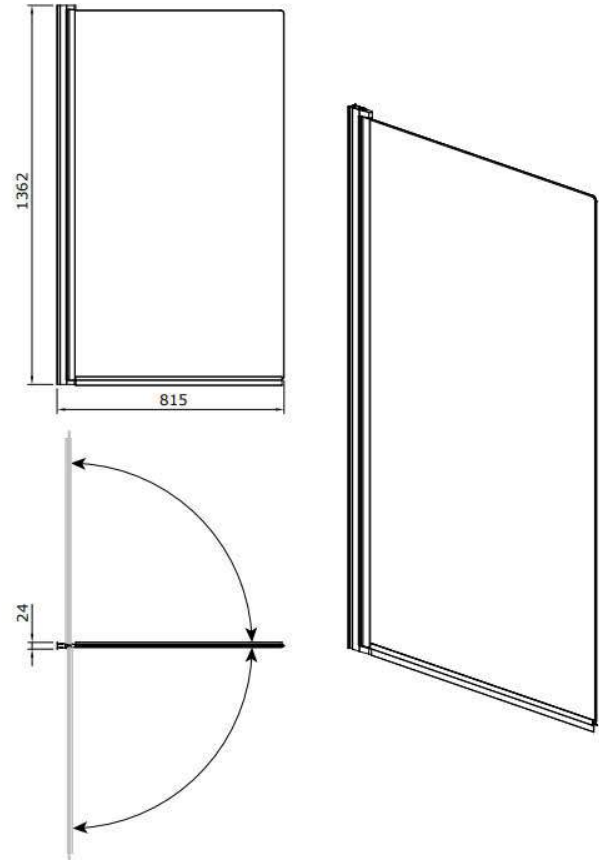

<https://www.tec.sanindusa.pt/safira-bath-screen>

Shower Panel

Sanindusa
Model: Versus enclosure with 1 sliding door
Reference: 8931200011
Finishes: Transparent and Chrome
Dimensions: 1220x25x1900mm
Count: 2
Room No: 2


Note:
Reversible enclosure
Versus 120cm shower door
With adjustable profiles - 0 to 40mm

<https://sanindusa.com/en/product/versus-enclosure-1slidingdoor>



Bath-Shower System

Bruma
Model: Nautic
Name: Bath-shower system for wall mounting with adjustable ABS head shower Ø230mm and shower rail
Reference: 181 261 1CR
Colour: Chrome
Count: 1
Room No: 10

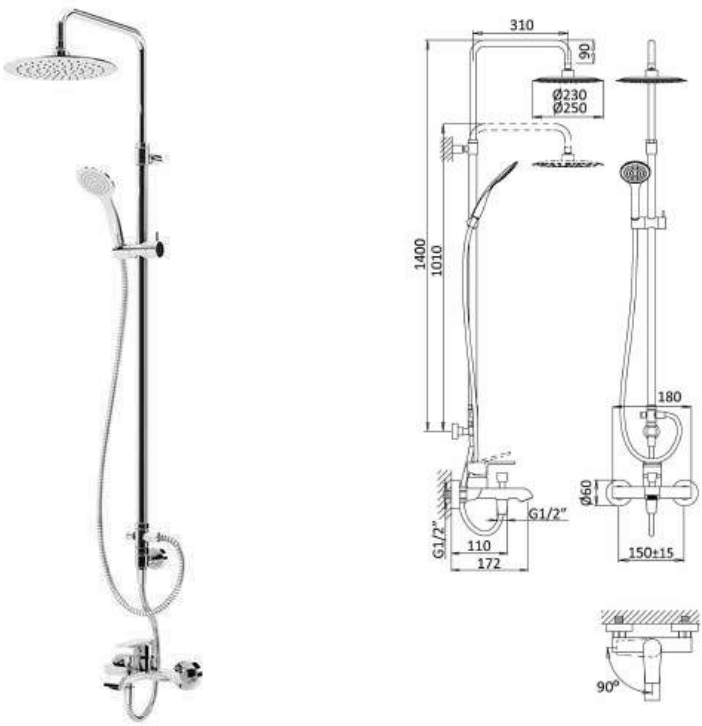

<https://www.bruma.pt>



1. THESE DRAWINGS MUST BE CHECKED BY THE CUSTOMER OR CONTRACTOR PRIOR TO APPROVAL. ANY ERRORS OR OMISSIONS MUST BE REPORTED IN WRITING TO BAUHU PRIOR TO COMMENCEMENT OF CONSTRUCTION.
2. ARCHITECTURAL DRAWINGS SHOULD BE READ IN CONJUNCTION WITH STRUCTURAL DETAILING AND FABRICATION GENERAL ASSEMBLY DRAWINGS.
3. FOR CONSTRUCTION PURPOSES, USE ONLY THE LATEST APPROVED DRAWINGS LABELED 'ISSUED FOR CONSTRUCTION'.
4. DO NOT SCALE FROM THIS DRAWING.
5. THE COMPANY OPERATES USING METRIC DIMENSIONS AS THE PRINCIPAL DENOMINATION.
6. ALL CONCRETE WORKS ARE OUTSIDE OF THE SCOPE OF THE COMPANY. INFORMATION REGARDING SLAB DESIGN AND CONNECTIONS IN THESE DRAWINGS ARE INTENDED FOR GUIDENCE ONLY. FOUNDATION AND SLAB WORKS SHOULD BE DESIGNED AND APPROVED BY A LOCAL STRUCTURAL ENGINEER.
7. THE COMPANY RETAINS FULL TITLE AND OWNERSHIP OF THESE PLANS AND DESIGNS. ANY UNAUTHORISED USE, REPRODUCTION, OR DISTRIBUTION OF THESE PLANS, WHETHER IN WHOLE OR PART, IS EXPRESSLY PROHIBITED WITHOUT PRIOR WRITTEN CONSENT.
8. THE HYBRID STEEL FRAME CONSTRUCTION SYSTEM AND METHODOLOGY (PATENT PENDING) DESCRIBED IN THESE PLANS HAS BEEN DEVELOPED BY THE COMPANY AND IS SUBJECT TO A PROVISIONAL PATENT APPLICATION & ASSIGNMENT - US APPLICATION NO. 63/722,841

No.	Revision	Date

ISSUED FOR:

Issued for information

Issued for client approval

Issued for fabrication

Issued for construction

Coconut Villa
3 Bed

DRAWING TITLE:
Bathroom Schedule 2

DRAWN BY:
Y.A.Clark

SCALE:


DRAWING NO:
A125

DATE:
16/02/2026

Room No:2&4 Bathroom 1&2


Washbasin

Kitbanho
Model: LAVATÓRIO KLOSS STD ALT.2 - 60S
Finishes: White Bright (glossy)
Dimensions: 600mm
Count: 2

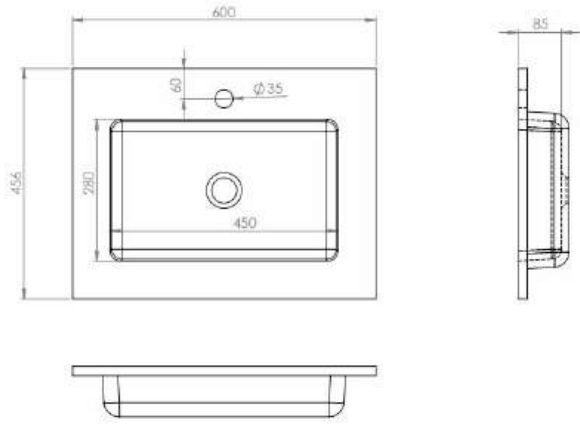

Bathroom Furniture

Kitbanho
Model: SARA ALT. 50 - 60S
Finishes: light grey
Dimensions: 600mm
Count: 2

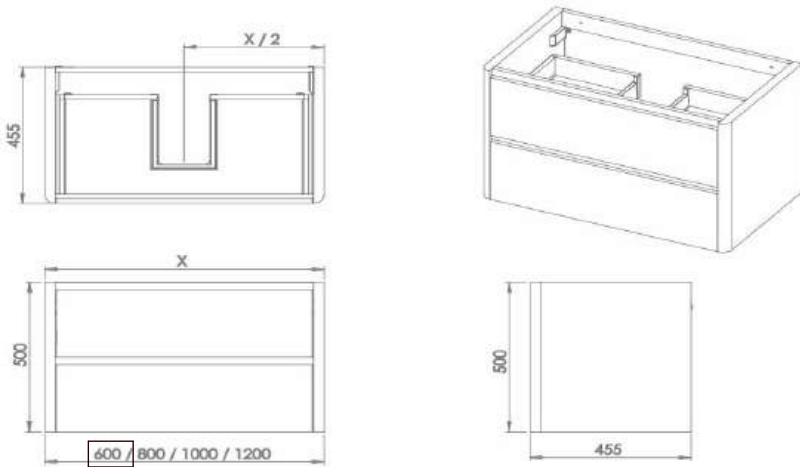

Mirror


Kitbanho
Model: Camarino Kloss alt. 70
Finishes: light grey
Dimension: 600mm
Count: 2



Room No:10 Bathroom 3


Washbasin

Kitbanho
Model: LAV. BANCA KLOSS STD ALT.10 - 140 D
Finishes: White Bright (glossy)
Dimensions: 1400mm
Count: 1

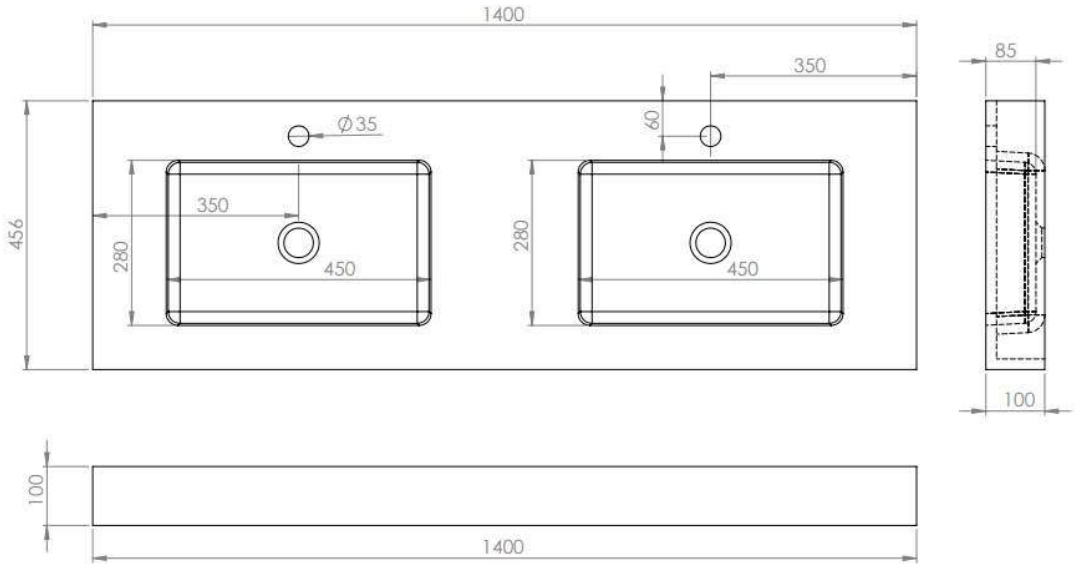

Bathroom Furniture

Kitbanho
Model: OLIMPO ALT. 50 140 DD
Finishes: white
Dimensions: 1400mm
Count: 1

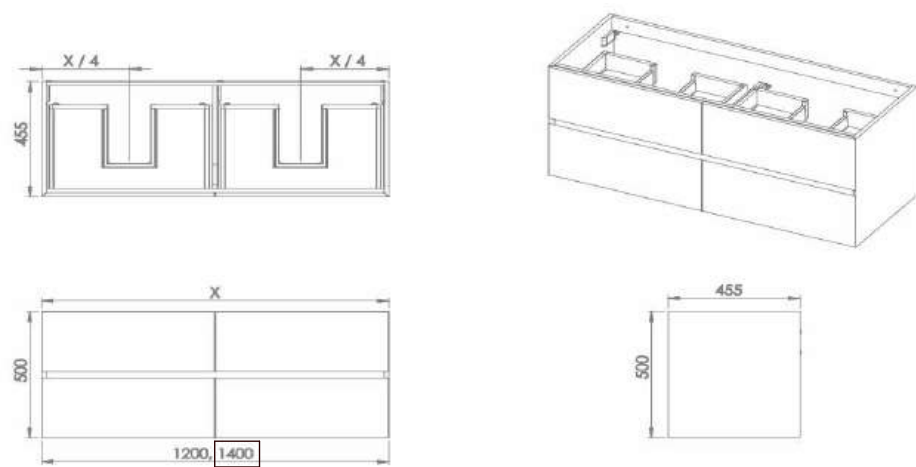

Mirror

Kitbanho
Model: Simple
Dimension: 60x100mm
Count: 2



1. THESE DRAWINGS MUST BE CHECKED BY THE CUSTOMER OR CONTRACTOR PRIOR TO APPROVAL. ANY ERRORS OR OMISSIONS MUST BE REPORTED IN WRITING TO BAUHU PRIOR TO COMMENCEMENT OF CONSTRUCTION.
2. ARCHITECTURAL DRAWINGS SHOULD BE READ IN CONJUNCTION WITH STRUCTURAL DETAILING AND FABRICATION GENERAL ASSEMBLY DRAWINGS.
3. FOR CONSTRUCTION PURPOSES, USE ONLY THE LATEST APPROVED DRAWINGS LABELED 'ISSUED FOR CONSTRUCTION'.
4. DO NOT SCALE FROM THIS DRAWING.
5. THE COMPANY OPERATES USING METRIC DIMENSIONS AS THE PRINCIPAL DENOMINATION.
6. ALL CONCRETE WORKS ARE OUTSIDE OF THE SCOPE OF THE COMPANY. INFORMATION REGARDING SLAB DESIGN AND CONNECTIONS IN THESE DRAWINGS ARE INTENDED FOR GUIDENCE ONLY. FOUNDATION AND SLAB WORKS SHOULD BE DESIGNED AND APPROVED BY A LOCAL STRUCTURAL ENGINEER.
7. THE COMPANY RETAINS FULL TITLE AND OWNERSHIP OF THESE PLANS AND DESIGNS. ANY UNAUTHORISED USE, REPRODUCTION, OR DISTRIBUTION OF THESE PLANS, WHETHER IN WHOLE OR PART, IS EXPRESSLY PROHIBITED WITHOUT PRIOR WRITTEN CONSENT.
8. THE HYBRID STEEL FRAME CONSTRUCTION SYSTEM AND METHODOLOGY (PATENT PENDING) DESCRIBED IN THESE PLANS HAS BEEN DEVELOPED BY THE COMPANY AND IS SUBJECT TO A PROVISIONAL PATENT APPLICATION & ASSIGNMENT - US APPLICATION NO. 63/722,841

No.	Revision	Date

ISSUED FOR:		
Issued for information Issued for client approval Issued for fabrication Issued for construction		
Coconut Villa 3 Bed		
DRAWING TITLE:		
Bathroom Furnitures		
DRAWN BY:		
Y.A.Clark		
SCALE:		
DRAWING NO:		
A127		
DATE:		
16/02/2026		



6



1 : 25



1 : 25



1 : 25







1 : 25



1 : 25




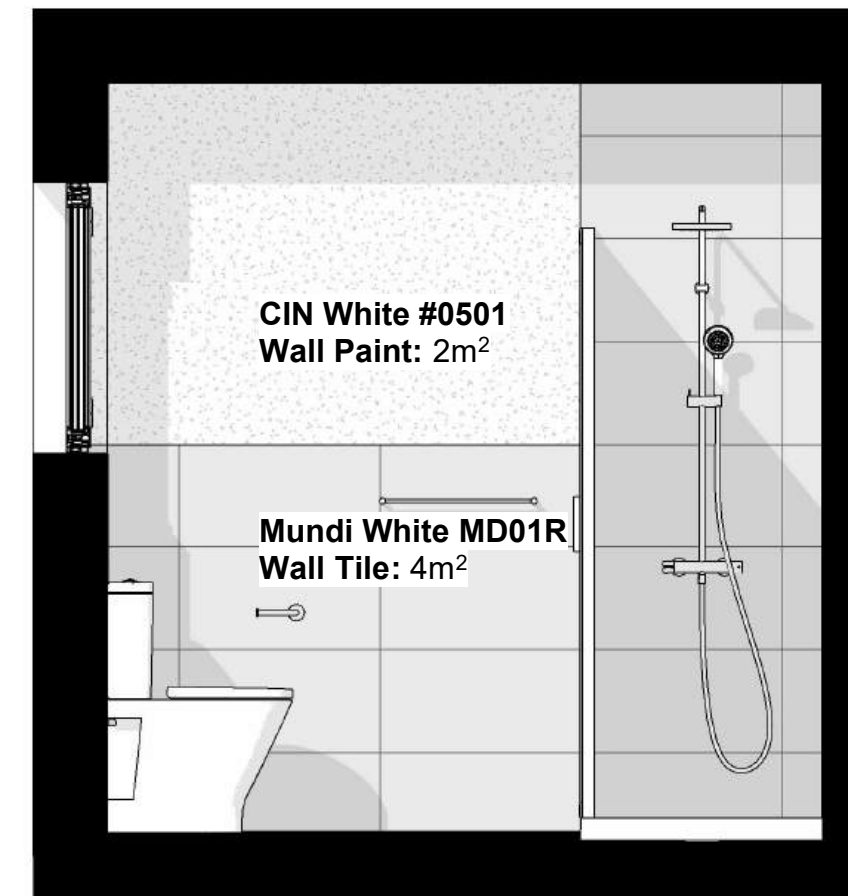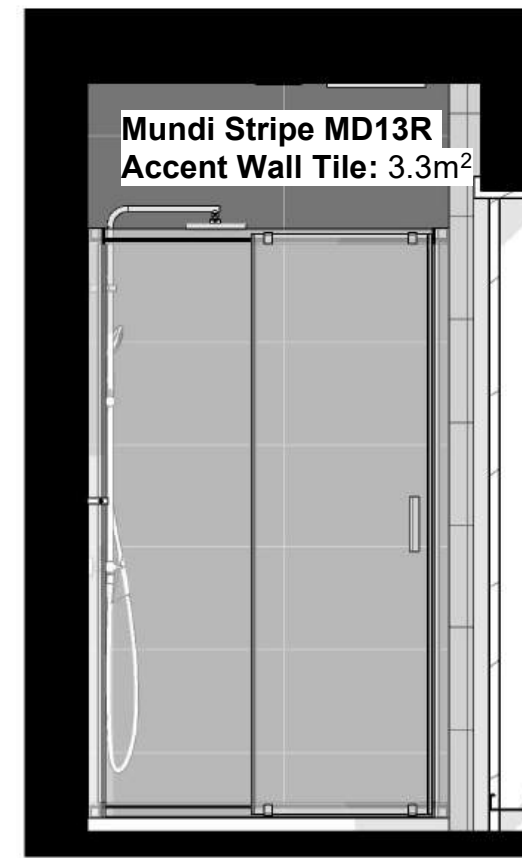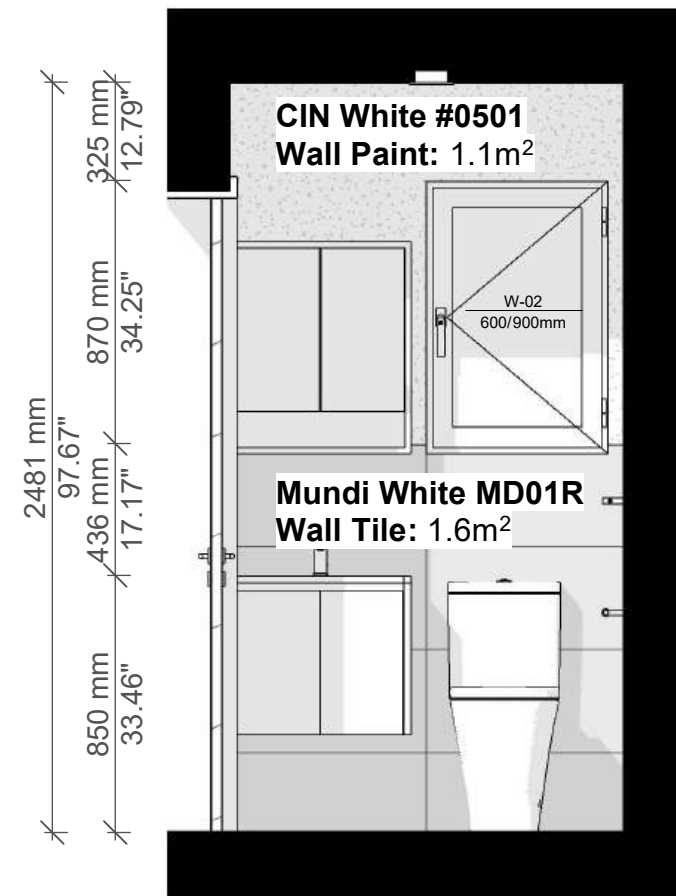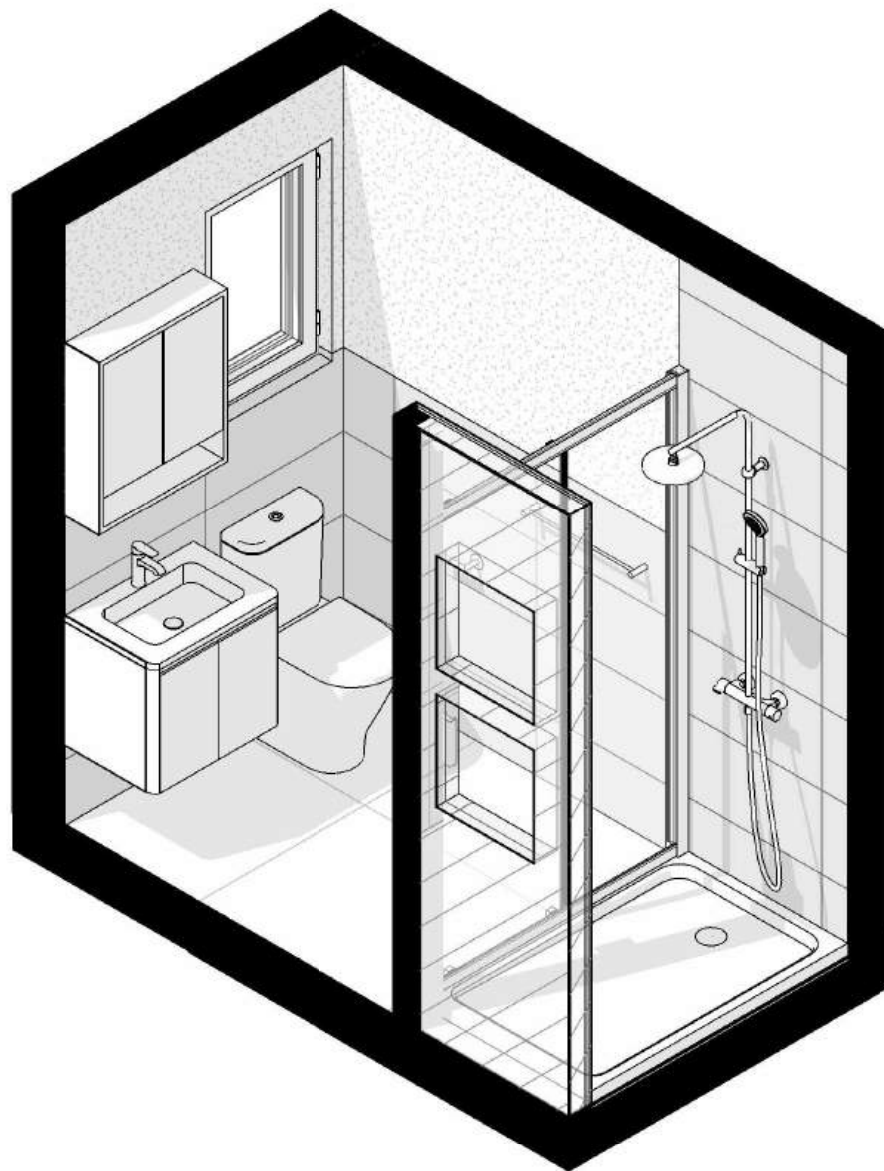

1 Section A'
1 : 25

2 Section B'
1 : 25

3 Section C'
1 : 25

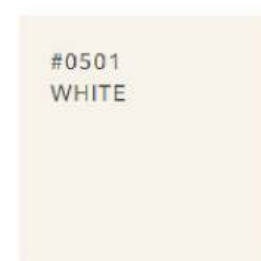

Wall Colour
CIN
White #0501
Area: 4.3m²



Bathroom Floor Tile

- On-Road Fog OR12
- 88,6 x 88,6 cm . 34,9" x 34,9" / C12
- Concrete, Rectified
- Glazed Porcelain Full Color Body, Natural

Grout Colour: 111 silver grey
Area: 2.1m²



Accent Shower Wall Tile

- Mundi Stripe Grey MD13R
- 34 x 66,5 cm . 13,4" x 26,2" / R17
- Decorations, Concrete, Rectified
- White Body Wall Tiles, Mate


Grout Colour: 100 White
Area: 3.3m²



Wall Tile


- Mundi White MD01R
- 34 x 66,5 cm . 13,4" x 26,2" / R16
- Concrete, Not Rectified
- White Body Wall Tiles, Mate

Grout Colour: 100 White
Area: 9.2m²

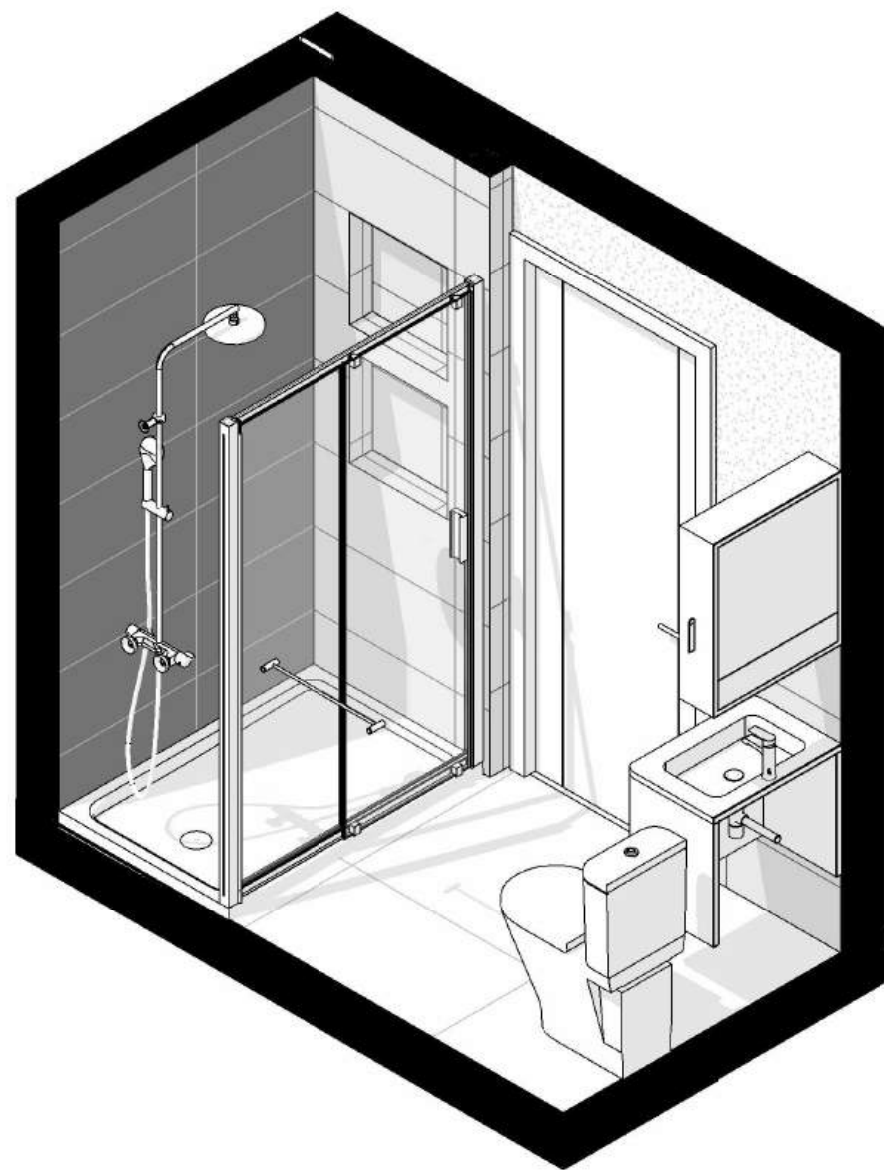


5 Bathroom 2 Isometric View

6 Bathroom 2 Iso.View 2

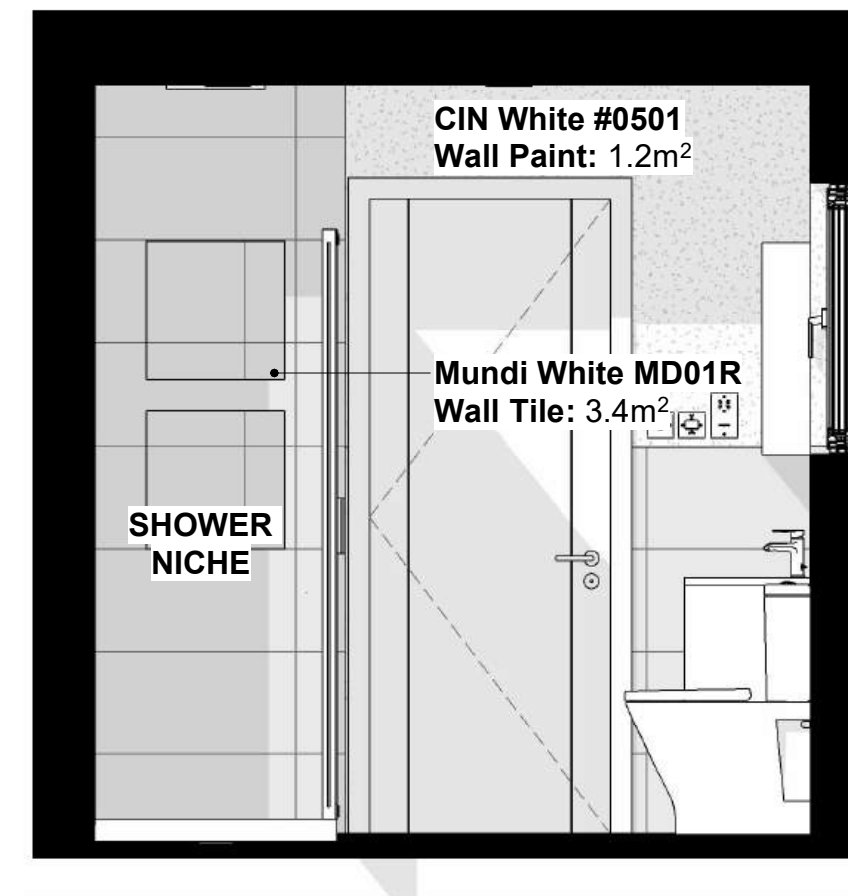

7 Section D'
1 : 25

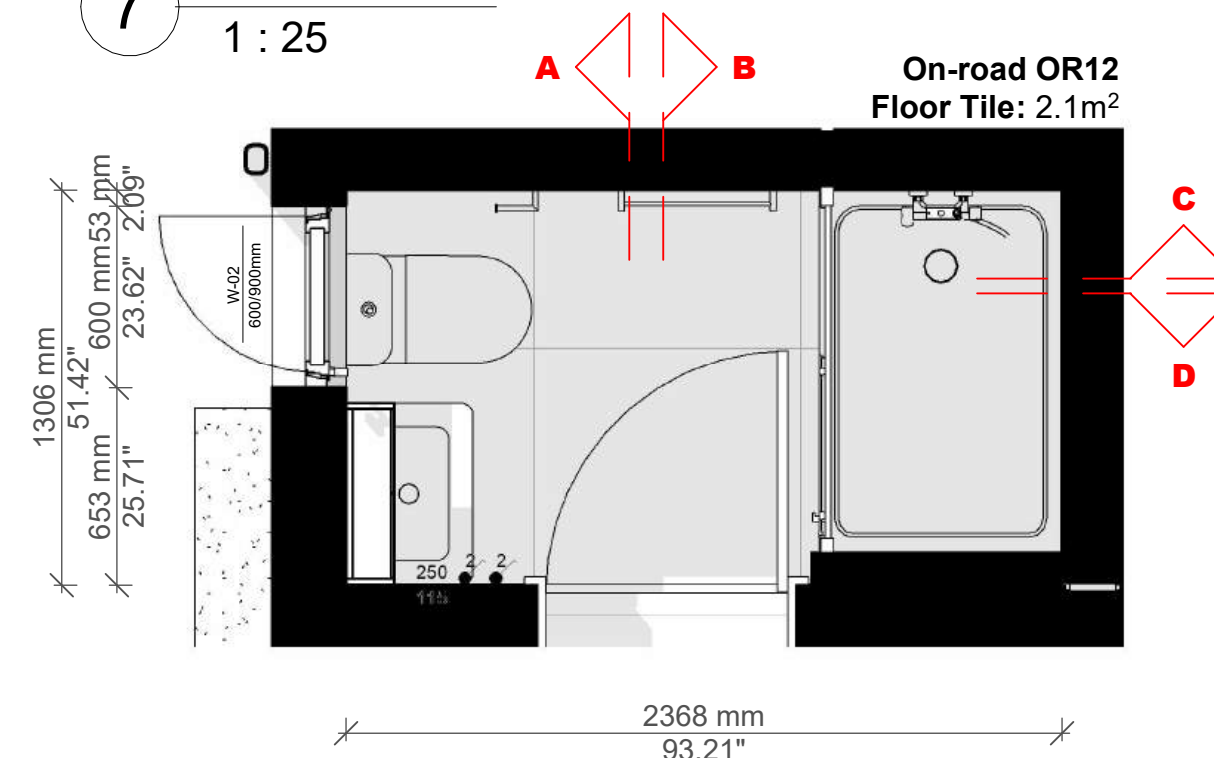

4 Bathroom 2 Plan
1 : 25

- THESE DRAWINGS MUST BE CHECKED BY THE CUSTOMER OR CONTRACTOR PRIOR TO APPROVAL. ANY ERRORS OR OMISSIONS MUST BE REPORTED IN WRITING TO BAUHU PRIOR TO COMMENCEMENT OF CONSTRUCTION.
- ARCHITECTURAL DRAWINGS SHOULD BE READ IN CONJUNCTION WITH STRUCTURAL DETAILING AND FABRICATION GENERAL ASSEMBLY DRAWINGS.
- FOR CONSTRUCTION PURPOSES, USE ONLY THE LATEST APPROVED DRAWINGS LABELED 'ISSUED FOR CONSTRUCTION'.
- DO NOT SCALE FROM THIS DRAWING.
- THE COMPANY OPERATES USING METRIC DIMENSIONS AS THE PRINCIPAL DENOMINATION.
- ALL CONCRETE WORKS ARE OUTSIDE OF THE SCOPE OF THE COMPANY. INFORMATION REGARDING SLAB DESIGN AND CONNECTIONS IN THESE DRAWINGS ARE INTENDED FOR GUIDANCE ONLY. FOUNDATION AND SLAB WORKS SHOULD BE DESIGNED AND APPROVED BY A LOCAL STRUCTURAL ENGINEER.
- THE COMPANY RETAINS FULL TITLE AND OWNERSHIP OF THESE PLANS AND DESIGNS. ANY UNAUTHORIZED USE, REPRODUCTION, OR DISTRIBUTION OF THESE PLANS, WHETHER IN WHOLE OR PART, IS EXPRESSLY PROHIBITED WITHOUT PRIOR WRITTEN CONSENT.
- THE HYBRID STEEL FRAME CONSTRUCTION SYSTEM AND METHODOLOGY (PATENT PENDING) DESCRIBED IN THESE PLANS HAS BEEN DEVELOPED BY THE COMPANY AND IS SUBJECT TO A PROVISIONAL PATENT APPLICATION & ASSIGNMENT - US APPLICATION NO. 63/722,841





No.	Revision	Date

ISSUED FOR:

- Issued for information
- Issued for client approval
- Issued for fabrication
- Issued for construction

Coconut Villa
3 Bed

DRAWING TITLE:	No 4 - Bathroom 2
DRAWN BY:	Y.A.Clark
SCALE:	1 : 25
DRAWING NO:	A129
DATE:	16/02/2026

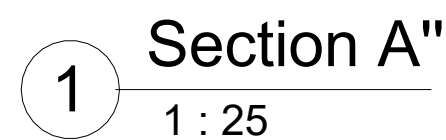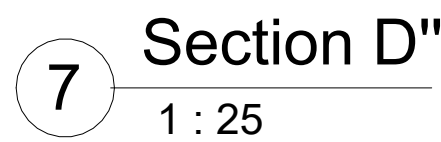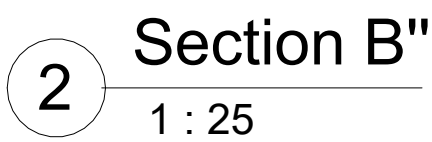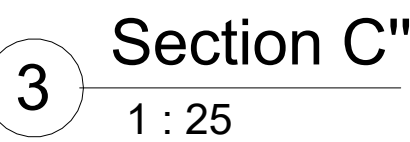

Area: 5.5m^2

- [illegible]

Coconut Villa 3 Bed

No 10 - Bathroom 3

Y.A.Clark


1 : 25

A130

16/02/2026



1 Bathroom 3 Isometric View

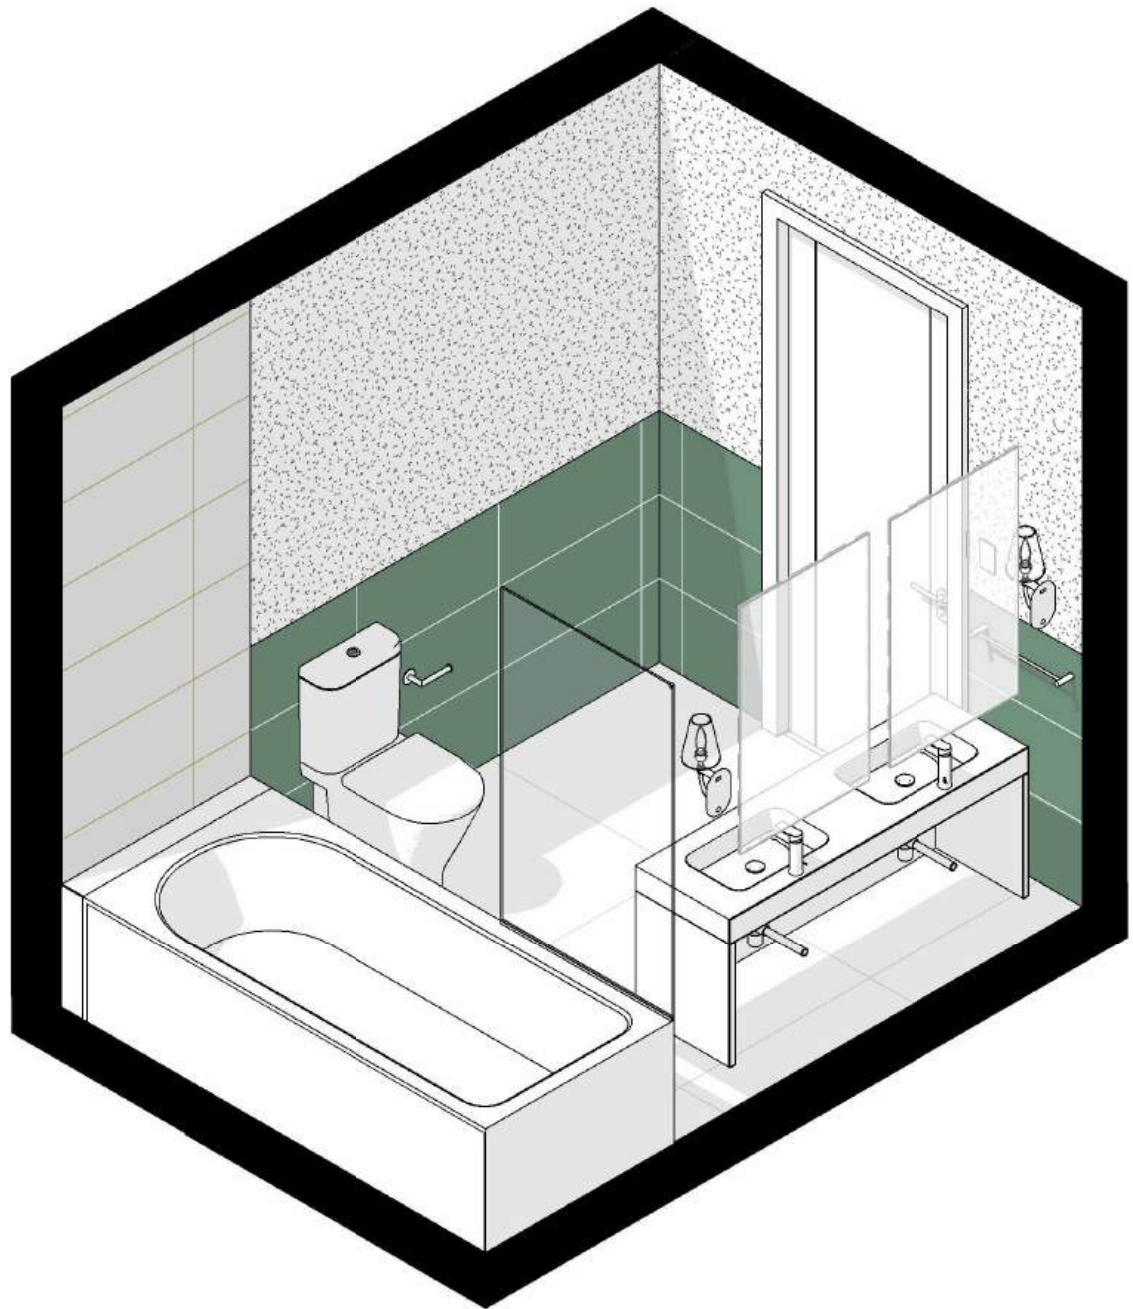

2 Bathroom 3 Iso.View 2

1. THESE DRAWINGS MUST BE CHECKED BY THE CUSTOMER OR CONTRACTOR PRIOR TO APPROVAL. ANY ERRORS OR OMISSIONS MUST BE REPORTED IN WRITING TO BAUHU PRIOR TO COMMENCEMENT OF CONSTRUCTION.
2. ARCHITECTURAL DRAWINGS SHOULD BE READ IN CONJUNCTION WITH STRUCTURAL DETAILING AND FABRICATION GENERAL ASSEMBLY DRAWINGS.
3. FOR CONSTRUCTION PURPOSES, USE ONLY THE LATEST APPROVED DRAWINGS LABELED 'ISSUED FOR CONSTRUCTION'.
4. DO NOT SCALE FROM THIS DRAWING.
5. THE COMPANY OPERATES USING METRIC DIMENSIONS AS THE PRINCIPAL DENOMINATION.
6. ALL CONCRETE WORKS ARE OUTSIDE OF THE SCOPE OF THE COMPANY. INFORMATION REGARDING SLAB DESIGN AND CONNECTIONS IN THESE DRAWINGS ARE INTENDED FOR GUIDENCE ONLY. FOUNDATION AND SLAB WORKS SHOULD BE DESIGNED AND APPROVED BY A LOCAL STRUCTURAL ENGINEER.
7. THE COMPANY RETAINS FULL TITLE AND OWNERSHIP OF THESE PLANS AND DESIGNS. ANY UNAUTHORISED USE, REPRODUCTION, OR DISTRIBUTION OF THESE PLANS, WHETHER IN WHOLE OR PART, IS EXPRESSLY PROHIBITED WITHOUT PRIOR WRITTEN CONSENT.
8. THE HYBRID STEEL FRAME CONSTRUCTION SYSTEM AND METHODOLOGY (PATENT PENDING) DESCRIBED IN THESE PLANS HAS BEEN DEVELOPED BY THE COMPANY AND IS SUBJECT TO A PROVISIONAL PATENT APPLICATION & ASSIGNMENT - US APPLICATION NO. 63/722,841

No.	Revision	Date

ISSUED FOR:

Issued for information

Issued for client approval

Issued for fabrication

Issued for construction

Coconut Villa
3 Bed

DRAWING TITLE:

No 10 - Bathroom 3

DRAWN BY:

Y.A.Clark

SCALE:

DRAWING NO:

A131

DATE:

16/02/2026

Finishes Schedule													
Floor Area				Floor Finish		Ceiling Finish		Wall Finish					
No.	Room Name	Sq.Meter	Sq. Feet	Room Perimeter	Grout Colour	Tiles	Ceiling Colour	Ceiling Height	Wall Colour	Grout Colour	Wall Tile	Grout Colour	Shower Wall Tile
Ground Floor Finish													
1	Bedroom 1	16 m²	174.5 ft²	17913 mm	111 silver grey	On-Road Fog OR12	White #0501	2481	White #0501				
2	Bathroom 1	3 m²	32.4 ft²	7347 mm	111 silver grey	On-Road Fog OR12	White #0501	2481	White #0501	100 White	Mundi White MD01R	100 White	Mundi Stripe Grey MD13R
3	Closet 1	1 m²	9.2 ft²	4011 mm	111 silver grey	On-Road Fog OR12	White #0501	2481	White #0501				
4	Bathroom 2	3 m²	32.4 ft²	7347 mm	111 silver grey	On-Road Fog OR12	White #0501	2481	White #0501	100 White	Mundi White MD01R	100 White	Mundi Stripe Grey MD13R
5	Closet 2	1 m²	9.2 ft²	4011 mm	111 silver grey	On-Road Fog OR12	White #0501	2481	White #0501				
6	Bedroom 2	18 m²	192.4 ft²	16947 mm	111 silver grey	On-Road Fog OR12	White #0501	2481	White #0501				
7	Living Area	38 m²	408.0 ft²	24627 mm	111 silver grey	On-Road Fog OR12	White #0501	2481	White #0501	111 silver grey	Kitchen: Habitat Stripe Pearl HB03R		
8	Utility	4 m²	38.0 ft²	7531 mm	111 silver grey	On-Road Fog OR12	White #0501	2481	White #0501				
9	Closet 3	1 m²	11.6 ft²	4745 mm	111 silver grey	On-Road Fog OR12	White #0501	2481	White #0501				
10	Bathroom 3	6 m²	60.6 ft²	9632 mm	111 silver grey	On-Road Fog OR12	White #0501	2481	White #0501	111 silver grey	Tokyo Green TK65R	111 silver grey	Muro Tokyo Pearl ETK05
11	Bedroom 3	18 m²	192.4 ft²	16946 mm	111 silver grey	On-Road Fog OR12	White #0501	2481	White #0501				
Grand total		108 m²	1160.7 ft²	121058 mm									

Wall Schedule			
Type	Width	Length	Area
BAU Exterior Wall	245 mm	55492 mm	123 m²
BAU Interior Wall	204 mm	37538 mm	77 m²
Drywall	124 mm	2026 mm	3 m²
Grand total		95056 mm	204 m²

Level Schedule		
Name	Elevation(mm)	Elevation(Feet)
Structural Roof Top	5287 mm	17.34'
Top of Plate	2800 mm	9.19'
Ceiling Level 1	2555 mm	8.38'
Windows Top 1	2230 mm	7.32'
Ground Floor Finish	74 mm	0.24'
Ground Floor Slab	0 mm	0.00'
Terrace Floor Finish	-84 mm	-0.28'
Terrace Slab	-152 mm	-0.50'

Roof Soffit Schedule			
Type	Area	Perimeter	Level
Roof Soffit	42 m²	114944 mm	Top of Plate

Roof Schedule			
Type	Base Level	Slope	Area
Main Roof	Top of Plate	6/12 (26.57°)	191 m²


Fascia Schedule		
Type	Length	Count
Fascia	58472 mm	1

- Note:**
- DRYWALL to be used in the bathrooms to fit a shower niche and 1200mm slider shower screen.
 - DRYWALL to be used to fit bathtub.

Paint Area Schedule	
Paint Name	Wall Area
Drywall	3.2 m²
Gypsum Wall Board - Fire resistant	280.5 m²
Gypsum Wall Board - Moisture resistant	280.4 m²
Light Gauge Steel frame	199.4 m²
Mineral Rockwool	200.4 m²
No.1 Bedroom 1 Paint - White 0501	34.4 m²
No.2 Bathroom 1 Accent Wall Tile - Mundi Stripe Grey MD13R	3.2 m²
No.2 Bathroom 1 Paint - White 0501	4.2 m²
No.2 Bathroom 1 Wall Tile - Mundi White MD01R	9.6 m²
No.3 Closet 1 Paint - White 0501	7.9 m²
No.4 Bathroom 2 Accent Wall Tile - Mundi Stripe Grey MD13R	3.2 m²
No.4 Bathroom 2 Paint - White 0501	7.4 m²
No.4 Bathroom 2 Wall Tile - Mundi White MD01R	9.6 m²
No.5 Closet 2 Paint - White 0501	7.8 m²
No.6 Bedroom 2 Paint - White 0501	32.1 m²
No.7 Kitchen Tile - Habitat Stripe Pearl HB03R	0.1 m²
No.7 Living Area Paint - White 0501	50.1 m²
No.8 Utility Paint - White 0501	16.4 m²
No.9 Closet 3 Paint - White 0501	10.9 m²
No.10 Bathroom 3 Bathtub Tile - Muro Tokyo Pearl ETK05	6.6 m²
No.10 Bathroom 3 Paint - White 0501	8.3 m²
No.10 Bathroom 3 Wall Tile - Tokyo Green TK65R	5.5 m²
No.11 Bedroom 3 Paint - White 0501	32.1 m²
Rigid insulation	123.3 m²
Secolite skim coat with embedded mesh	122.7 m²
Secolite with joints and screws filled	122.7 m²
Selected Paint Finish	280.2 m²
STO Cement-free reinforcing coat	123.3 m²
STO Decorative Green Render Finish Plaster	131.7 m²
Vapour Barrier	199.5 m²
Grand total	2316.7 m²

Ceiling Schedule				
Type	Area	Perimeter	Thickness	Description
Ceiling	108 m²	121058 mm	245 mm	Interior

1 Floor Plan
1 : 70

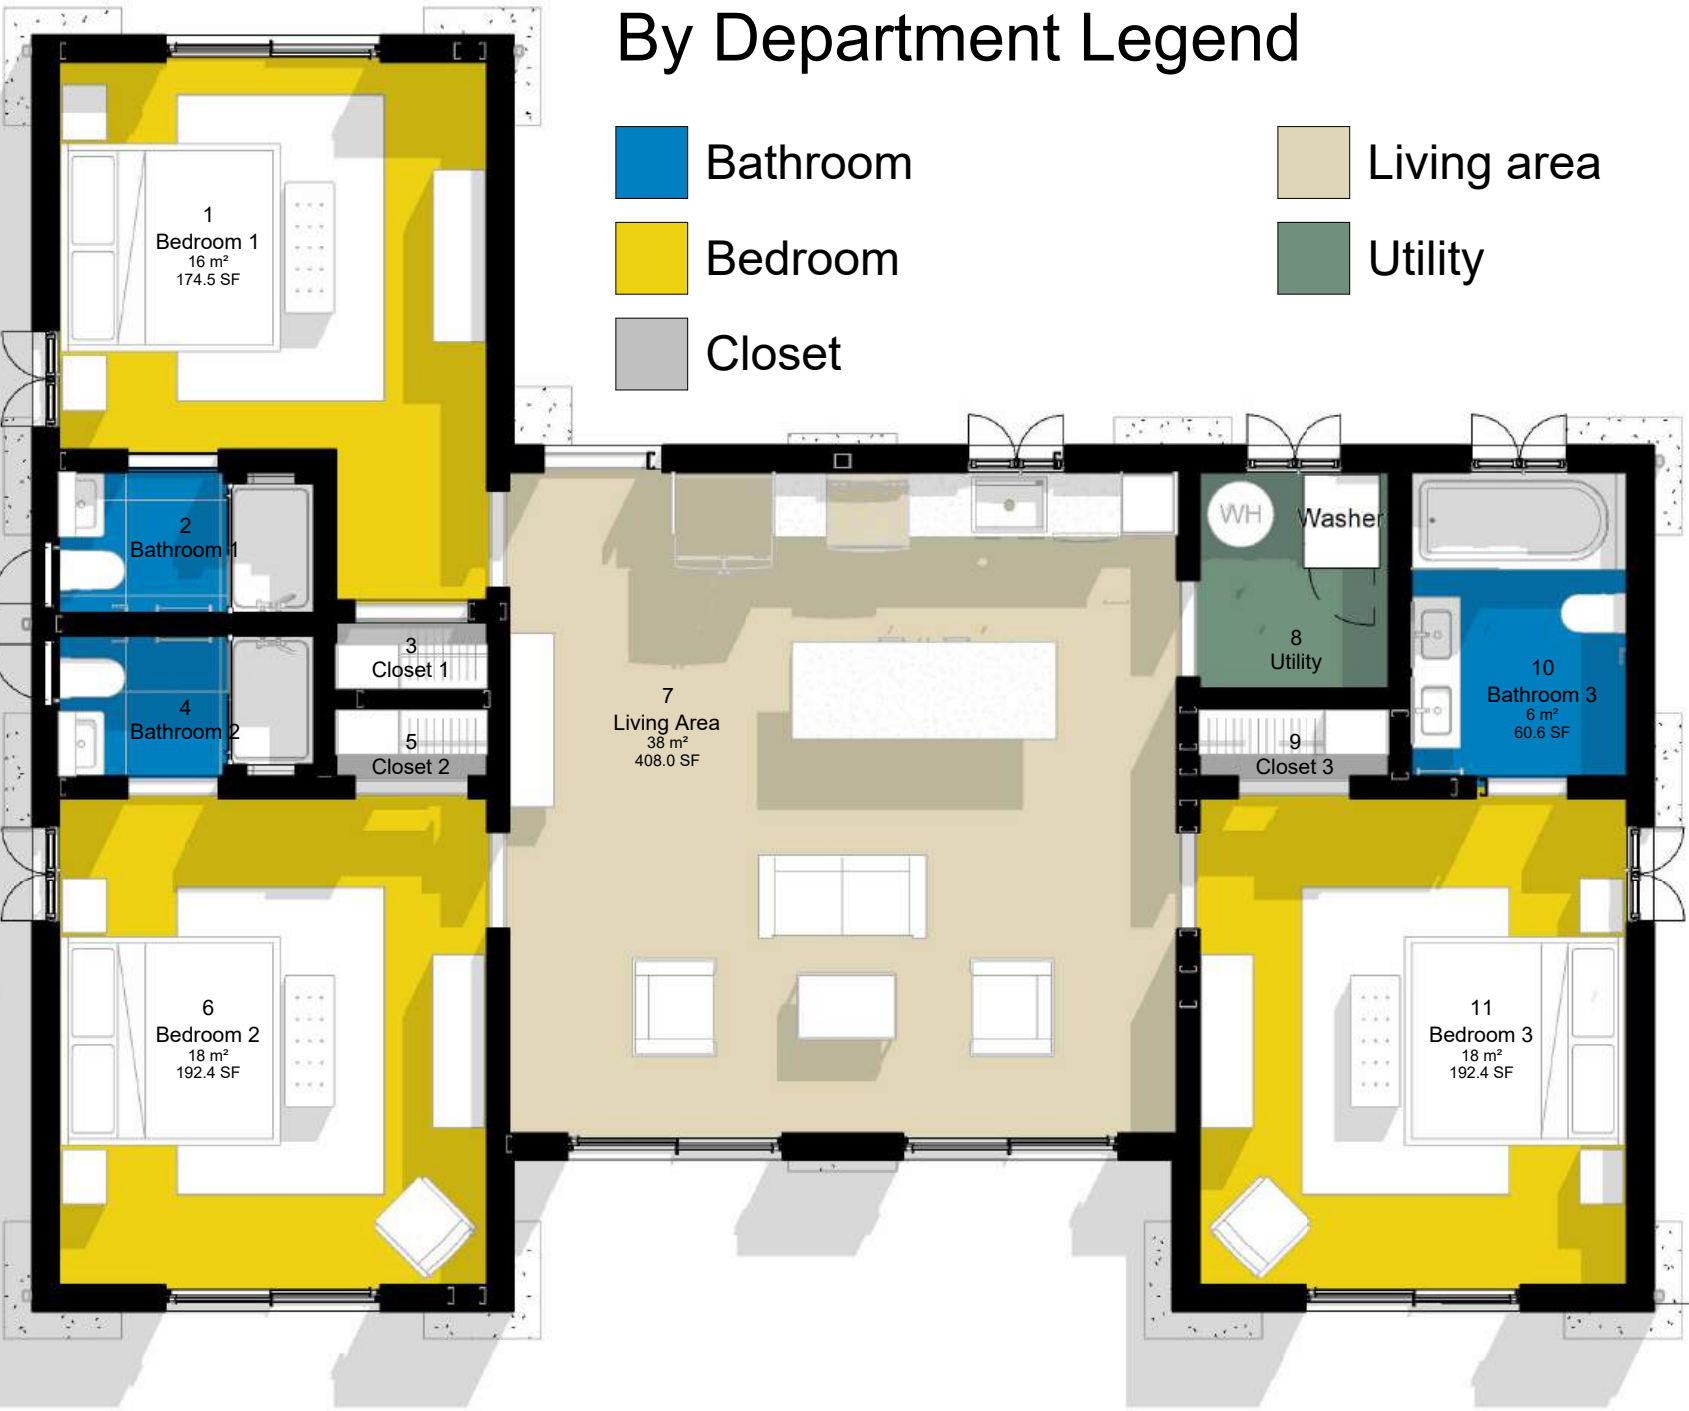

1. THESE DRAWINGS MUST BE CHECKED BY THE CUSTOMER OR CONTRACTOR PRIOR TO APPROVAL. ANY ERRORS OR OMISSIONS MUST BE REPORTED IN WRITING TO BAUHU PRIOR TO COMMENCEMENT OF CONSTRUCTION.
2. ARCHITECTURAL DRAWINGS SHOULD BE READ IN CONJUNCTION WITH STRUCTURAL DETAILING AND FABRICATION GENERAL ASSEMBLY DRAWINGS.
3. FOR CONSTRUCTION PURPOSES, USE ONLY THE LATEST APPROVED DRAWINGS LABELED 'ISSUED FOR CONSTRUCTION'.
4. DO NOT SCALE FROM THIS DRAWING.
5. THE COMPANY OPERATES USING METRIC DIMENSIONS AS THE PRINCIPAL DENOMINATION.
6. ALL CONCRETE WORKS ARE OUTSIDE OF THE SCOPE OF THE COMPANY. INFORMATION REGARDING SLAB DESIGN AND CONNECTIONS IN THESE DRAWINGS ARE INTENDED FOR GUIDENCE ONLY. FOUNDATION AND SLAB WORKS SHOULD BE DESIGNED AND APPROVED BY A LOCAL STRUCTURAL ENGINEER.
7. THE COMPANY RETAINS FULL TITLE AND OWNERSHIP OF THESE PLANS AND DESIGNS. ANY UNAUTHORISED USE, REPRODUCTION, OR DISTRIBUTION OF THESE PLANS, WHETHER IN WHOLE OR PART, IS EXPRESSLY PROHIBITED WITHOUT PRIOR WRITTEN CONSENT.
8. THE HYBRID STEEL FRAME CONSTRUCTION SYSTEM AND METHODOLOGY (PATENT PENDING) DESCRIBED IN THESE PLANS HAS BEEN DEVELOPED BY THE COMPANY AND IS SUBJECT TO A PROVISIONAL PATENT APPLICATION & ASSIGNMENT - US APPLICATION NO. 63/722,841

No.	Revision	Date

ISSUED FOR:

Issued for information

Issued for client approval

Issued for fabrication

Issued for construction

Coconut Villa 3 Bed

DRAWING TITLE:	
Finishes Schedule & Legend	
DRAWN BY:	
Y.A.Clark	
SCALE:	
1 : 70	
DRAWING NO:	
A132	
DATE:	
16/02/2026	

INTERIOR FLOOR TILE <https://www.domino.pt/en/products>

- On-Road Fog OR12
- 88,6 x 88,6 cm . 34,9" x 34,9" / C12
- Concrete, Rectified
- Glazed Porcelain Full Color Body, Natural

Room No: All rooms

Grout Colour: 111 silver grey

Total Area: 109 m²



[https://www.domino.pt/en/products/\[\[type-22-go\]\[collection-79\]\[material-15\]\[ambient-all\]\]/241-on-road/-/1701-on-road-fog-or12/164-886-x-886](https://www.domino.pt/en/products/[[type-22-go][collection-79][material-15][ambient-all]]/241-on-road/-/1701-on-road-fog-or12/164-886-x-886)
<https://www.mapei.com/au/en/tools-and-downloads/coloured-grouts-and-sealants>

BATH WALL TILE

- Muro Tokyo Pearl ETK05
- 34 x 65 cm . 13,4" x 25,6" / P59
- Decorations, Concrete, Color, Not Rectified
- White Body Wall Tiles, Mate

Room No: 10

Grout Colour: 111 silver grey

Total Area: 6.6 m²



[https://www.domino.pt/en/products/\[\[type-21\]\[collection-73\]\[material-28\]\[ambient-all\]\]/206-tokyo/-/1532-muro-tokyo-pearl-etk05/166-34-x-65](https://www.domino.pt/en/products/[[type-21][collection-73][material-28][ambient-all]]/206-tokyo/-/1532-muro-tokyo-pearl-etk05/166-34-x-65)

WALL TILE

- Tokyo Green TK65R
- 34 x 66,5 cm . 13,4" x 26,2" / R16
- Concrete, Color, Not Rectified
- White Body Wall Tiles, Mate

Room No: 10

Grout Colour: 111 silver grey

Total Area: 5.5 m²



[https://www.domino.pt/en/products/\[\[type-21\]\[collection-73\]\[material-19\]\[ambient-all\]\]/205-tokyo/-/1526-tokyo-green-tk65r/147-34-x-665](https://www.domino.pt/en/products/[[type-21][collection-73][material-19][ambient-all]]/205-tokyo/-/1526-tokyo-green-tk65r/147-34-x-665)

ACCENT SHOWER WALL TILE

- Mundi Stripe Grey MD13R
- 34 x 66,5 cm . 13,4" x 26,2" / R17
- Decorations, Concrete, Rectified
- White Body Wall Tiles, Mate

Room No: 2&4

Grout Colour: 100 White

Total Area: 6.6 m²



[https://www.domino.pt/en/products/\[\[type-21\]\[collection-32\]\[material-28\]\[ambient-all\]\]/22-mundi/4-white/342-mundi-stripe-grey-md13r/147-34-x-665](https://www.domino.pt/en/products/[[type-21][collection-32][material-28][ambient-all]]/22-mundi/4-white/342-mundi-stripe-grey-md13r/147-34-x-665)

WALL TILE

- Mundi White MD01R
- 34 x 66,5 cm . 13,4" x 26,2" / R16
- Concrete, Not Rectified
- White Body Wall Tiles, Mate

Room No: 2&4

Grout Colour: 100 White

Total Area: 18.4 m²



[https://www.domino.pt/en/products/\[\[type-21\]\[collection-32\]\[material-53\]\[ambient-all\]\]/146-mundi/-/1200-mundi-white-md01r/147-34-x-665](https://www.domino.pt/en/products/[[type-21][collection-32][material-53][ambient-all]]/146-mundi/-/1200-mundi-white-md01r/147-34-x-665)

KITCHEN BACKSPLASH TILE

- Habitat Stripe Pearl HB03R
- 34 x 66,5 cm . 13,4" x 26,2" / R17
- Decorations, Concrete, Not Rectified
- White Body Wall Tiles, Mate

Room No: 7

Grout Colour: 111 silver grey

Total Area: 1.3 m²



[https://www.domino.pt/en/products/\[\[type-21\]\[collection-27\]\[material-28\]\[ambient-all\]\]/16-innova/4-white/295-habitat-stripe-pearl-hb03r/147-34-x-665](https://www.domino.pt/en/products/[[type-21][collection-27][material-28][ambient-all]]/16-innova/4-white/295-habitat-stripe-pearl-hb03r/147-34-x-665)

CEILING&WALL PAINT FINISH

CIN

- CINAQUA GC 300 #0501 WHITE

Room No: All rooms

Total Ceiling Area: 108 m²

Total Wall Paint Area: 205 m²



<https://cin.com/deco/pt/en/colour>

EXTERIOR WALL FINISH

Exterior Wall Finish

Stolit K fine grain exterior plaster

Colour code: 36105, 62 C1 O

RGB: 182,215,199

Total Exterior Wall Area: 132 m²



PERGOLA/SOFFIT/FASCIA FINISH

Stolit K fine grain exterior plaster

Colour: RAL 9003 Signal White

RGB: 236, 236, 232

HEX Code: #ECECE8

Total Soffit Area: 42.2 m²

Total Fascia Area: 14 m²



<https://www.stocorp.com/sto-color/>

ROOF FINISH

- Acrylabs elastomeric roofing membrane
- Colour: Acrylabs Standard White

Total Roof Area: 192 m²



1. THESE DRAWINGS MUST BE CHECKED BY THE CUSTOMER OR CONTRACTOR PRIOR TO APPROVAL. ANY ERRORS OR OMISSIONS MUST BE REPORTED IN WRITING TO BAUHU PRIOR TO COMMENCEMENT OF CONSTRUCTION.
2. ARCHITECTURAL DRAWINGS SHOULD BE READ IN CONJUNCTION WITH STRUCTURAL DETAILING AND FABRICATION GENERAL ASSEMBLY DRAWINGS.
3. FOR CONSTRUCTION PURPOSES, USE ONLY THE LATEST APPROVED DRAWINGS LABELED 'ISSUED FOR CONSTRUCTION'.
4. DO NOT SCALE FROM THIS DRAWING.
5. THE COMPANY OPERATES USING METRIC DIMENSIONS AS THE PRINCIPAL DENOMINATION.
6. ALL CONCRETE WORKS ARE OUTSIDE OF THE SCOPE OF THE COMPANY. INFORMATION REGARDING SLAB DESIGN AND CONNECTIONS IN THESE DRAWINGS ARE INTENDED FOR GUIDENCE ONLY. FOUNDATION AND SLAB WORKS SHOULD BE DESIGNED AND APPROVED BY A LOCAL STRUCTURAL ENGINEER.
7. THE COMPANY RETAINS FULL TITLE AND OWNERSHIP OF THESE PLANS AND DESIGNS. ANY UNAUTHORISED USE, REPRODUCTION, OR DISTRIBUTION OF THESE PLANS, WHETHER IN WHOLE OR PART, IS EXPRESSLY PROHIBITED WITHOUT PRIOR WRITTEN CONSENT.
8. THE HYBRID STEEL FRAME CONSTRUCTION SYSTEM AND METHODOLOGY (PATENT PENDING) DESCRIBED IN THESE PLANS HAS BEEN DEVELOPED BY THE COMPANY AND IS SUBJECT TO A PROVISIONAL PATENT APPLICATION & ASSIGNMENT - US APPLICATION NO. 63/722,841

No.	Revision	Date

ISSUED FOR:

Issued for information

Issued for client approval

Issued for fabrication

Issued for construction

Coconut Villa
3 Bed

DRAWING TITLE:

Decor Finishes

DRAWN BY:

Y.A.Clark

SCALE:

DRAWING NO:

A133

DATE:

16/02/2026

Wall Details

Exterior Wall

Interior side

- Selected Paint Finish (2mm)
- Gypsum Wall Board - Moisture resistant (12.5mm)
- Gypsum Wall Board - Fire resistant (12.5mm)
- Light Gauge Steel Frame (150mm)
[Mineral Rockwool (120mm) between LGS studs]
- Secolite with joints and screws filled (12.5mm)
- Rigid Insulation (40mm)
- STO Cement-free Reinforcing Coat with Mesh
- STO Decorative Render Finish Plaster

Exterior side


Interior Wall

Interior side


- Selected Paint Finish (2mm)
- Gypsum Wall Board - Moisture resistant (12.5mm)
- Gypsum Wall Board - Fire resistant (12.5mm)
- Light Gauge Steel Frame (150mm)
[Mineral Rockwool (120mm) between LGS studs]
- Gypsum Wall Board - Fire resistant (12.5mm)
- Gypsum Wall Board - Moisture resistant (12.5mm)
- Selected Paint Finish

Interior side


Exterior - Interior Wall Connection Sc: 1/6

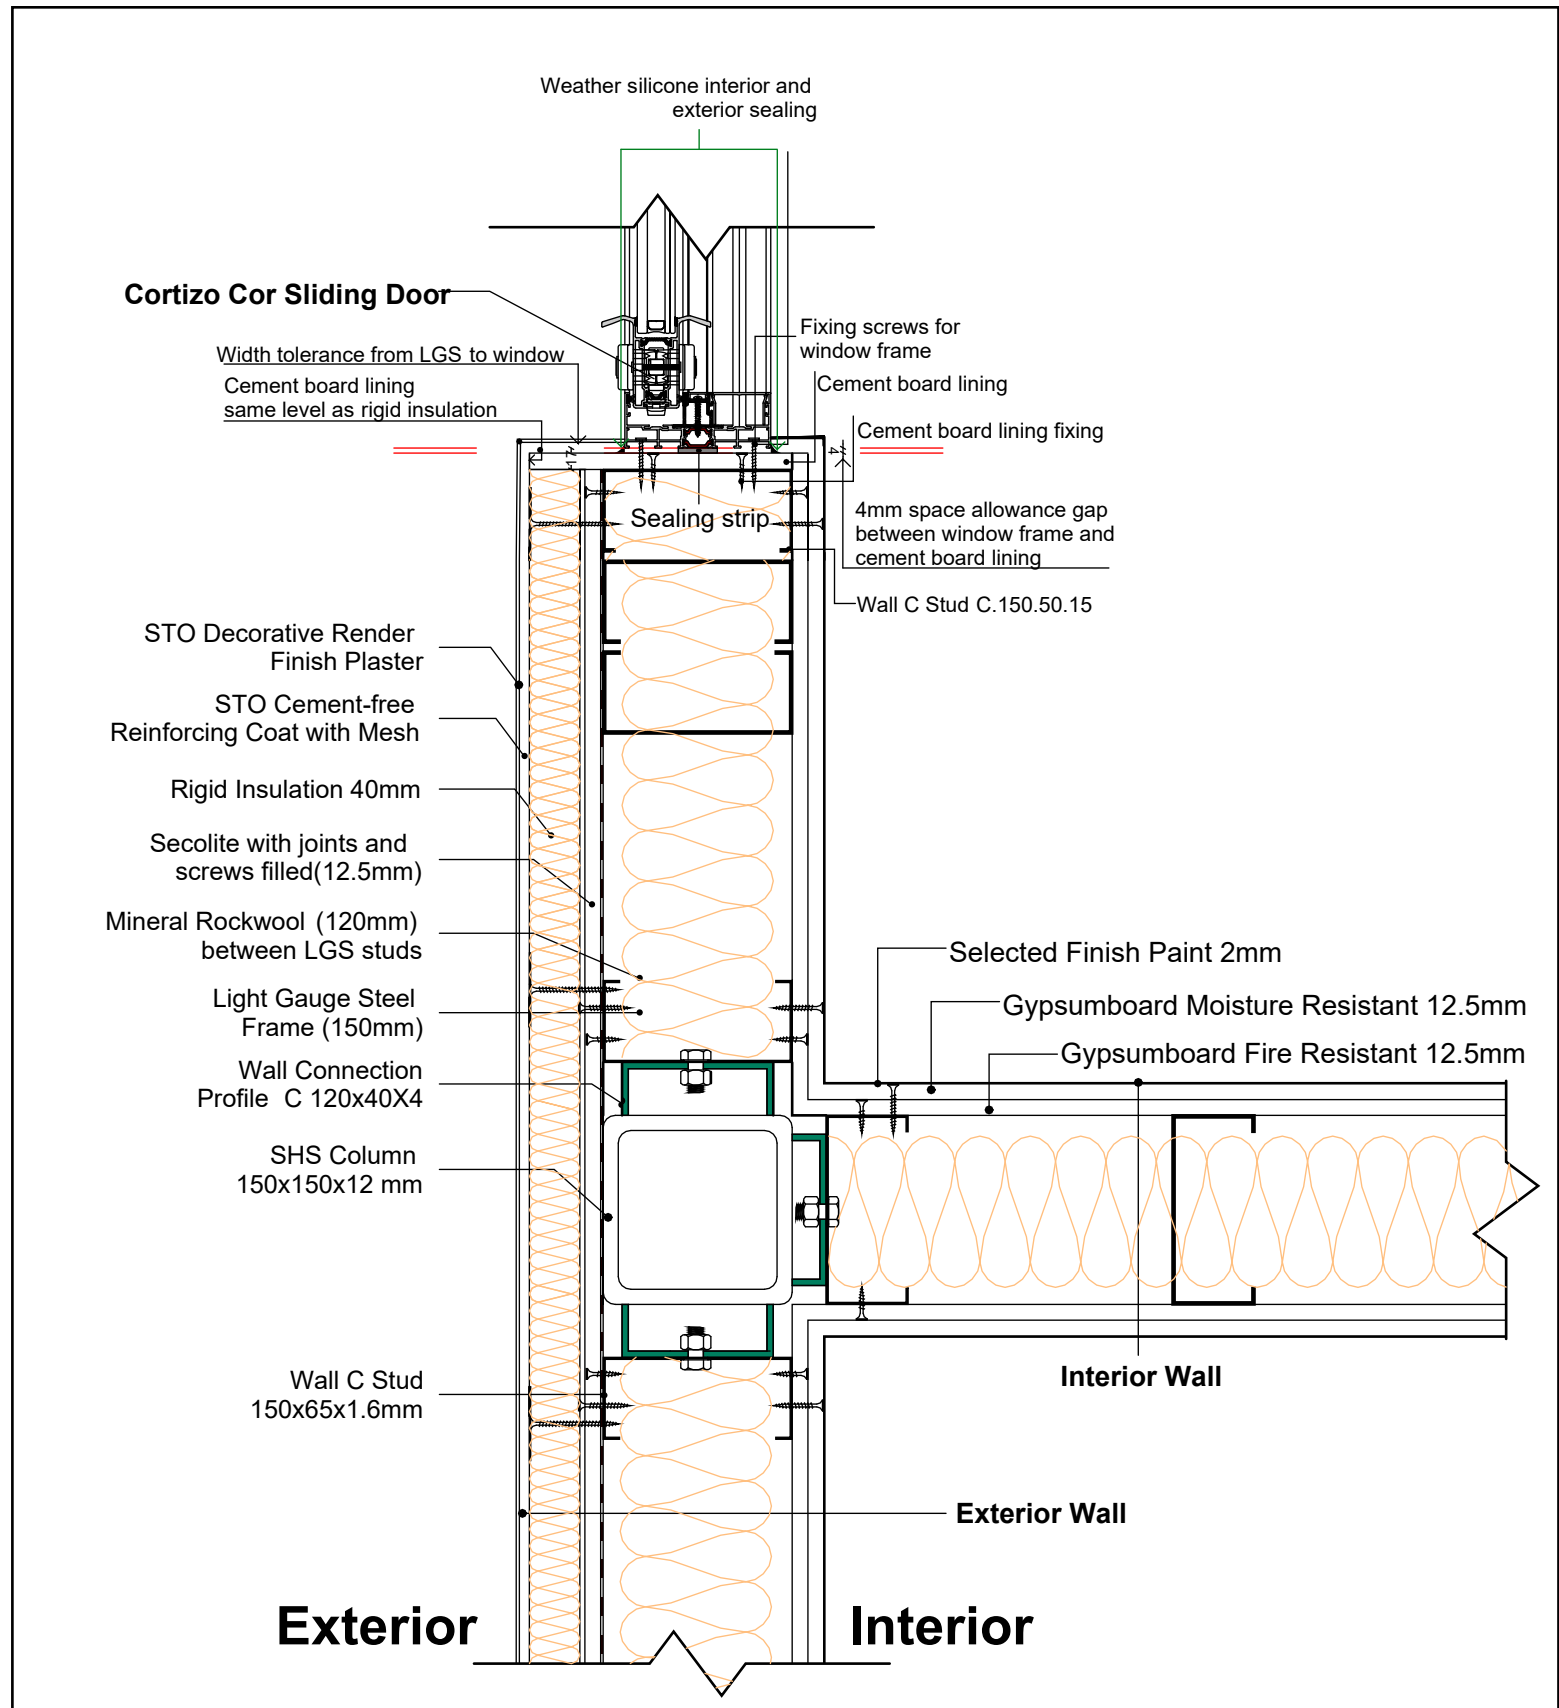

Exterior - Interior Wall Connection Sc: 1/6

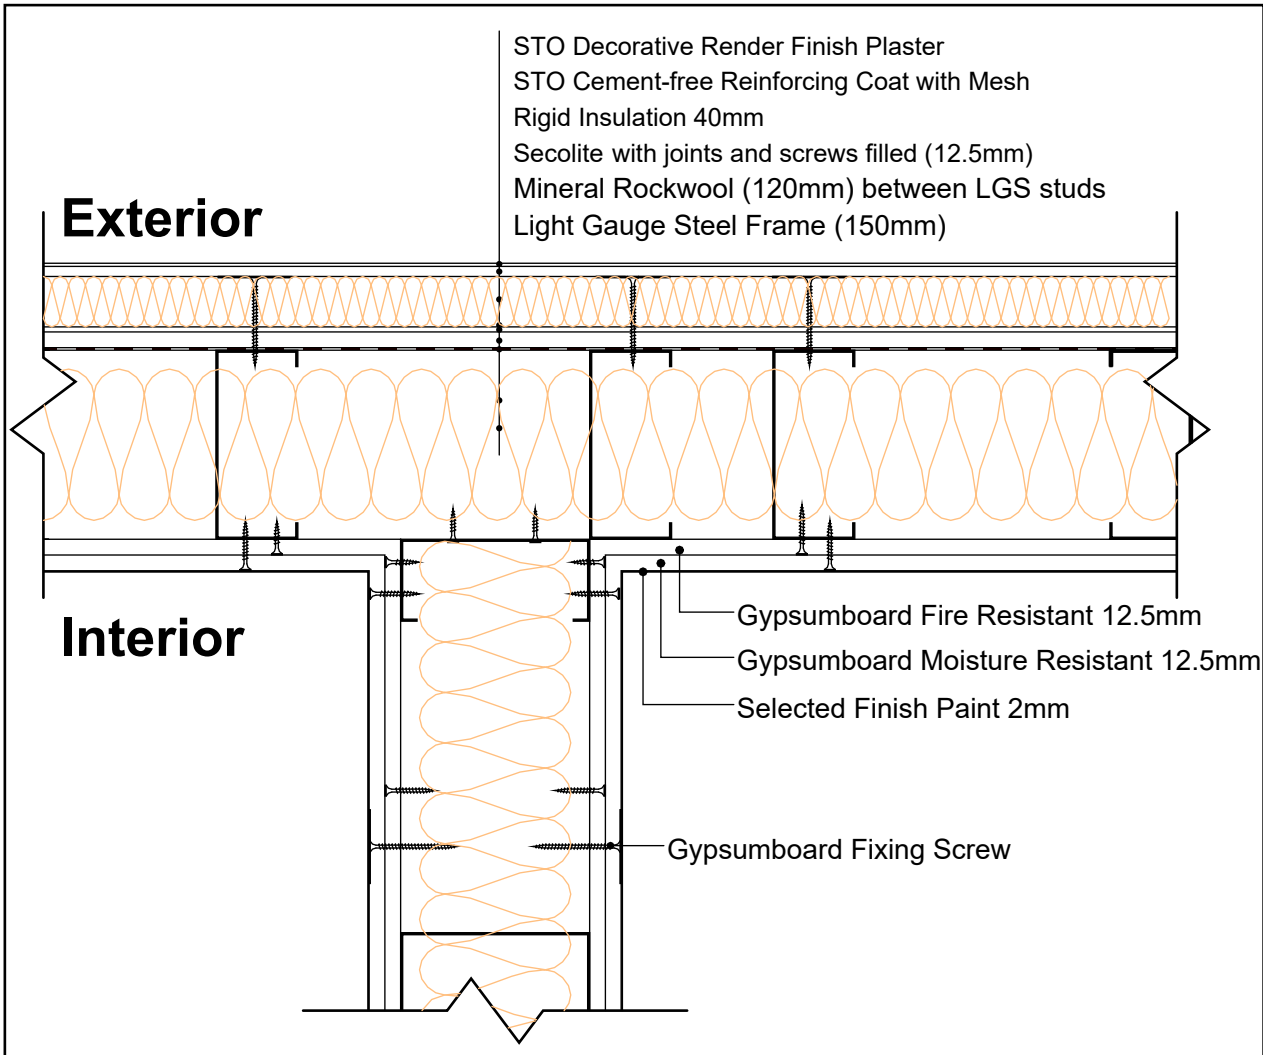

Exterior Corner Wall Sc: 1/6

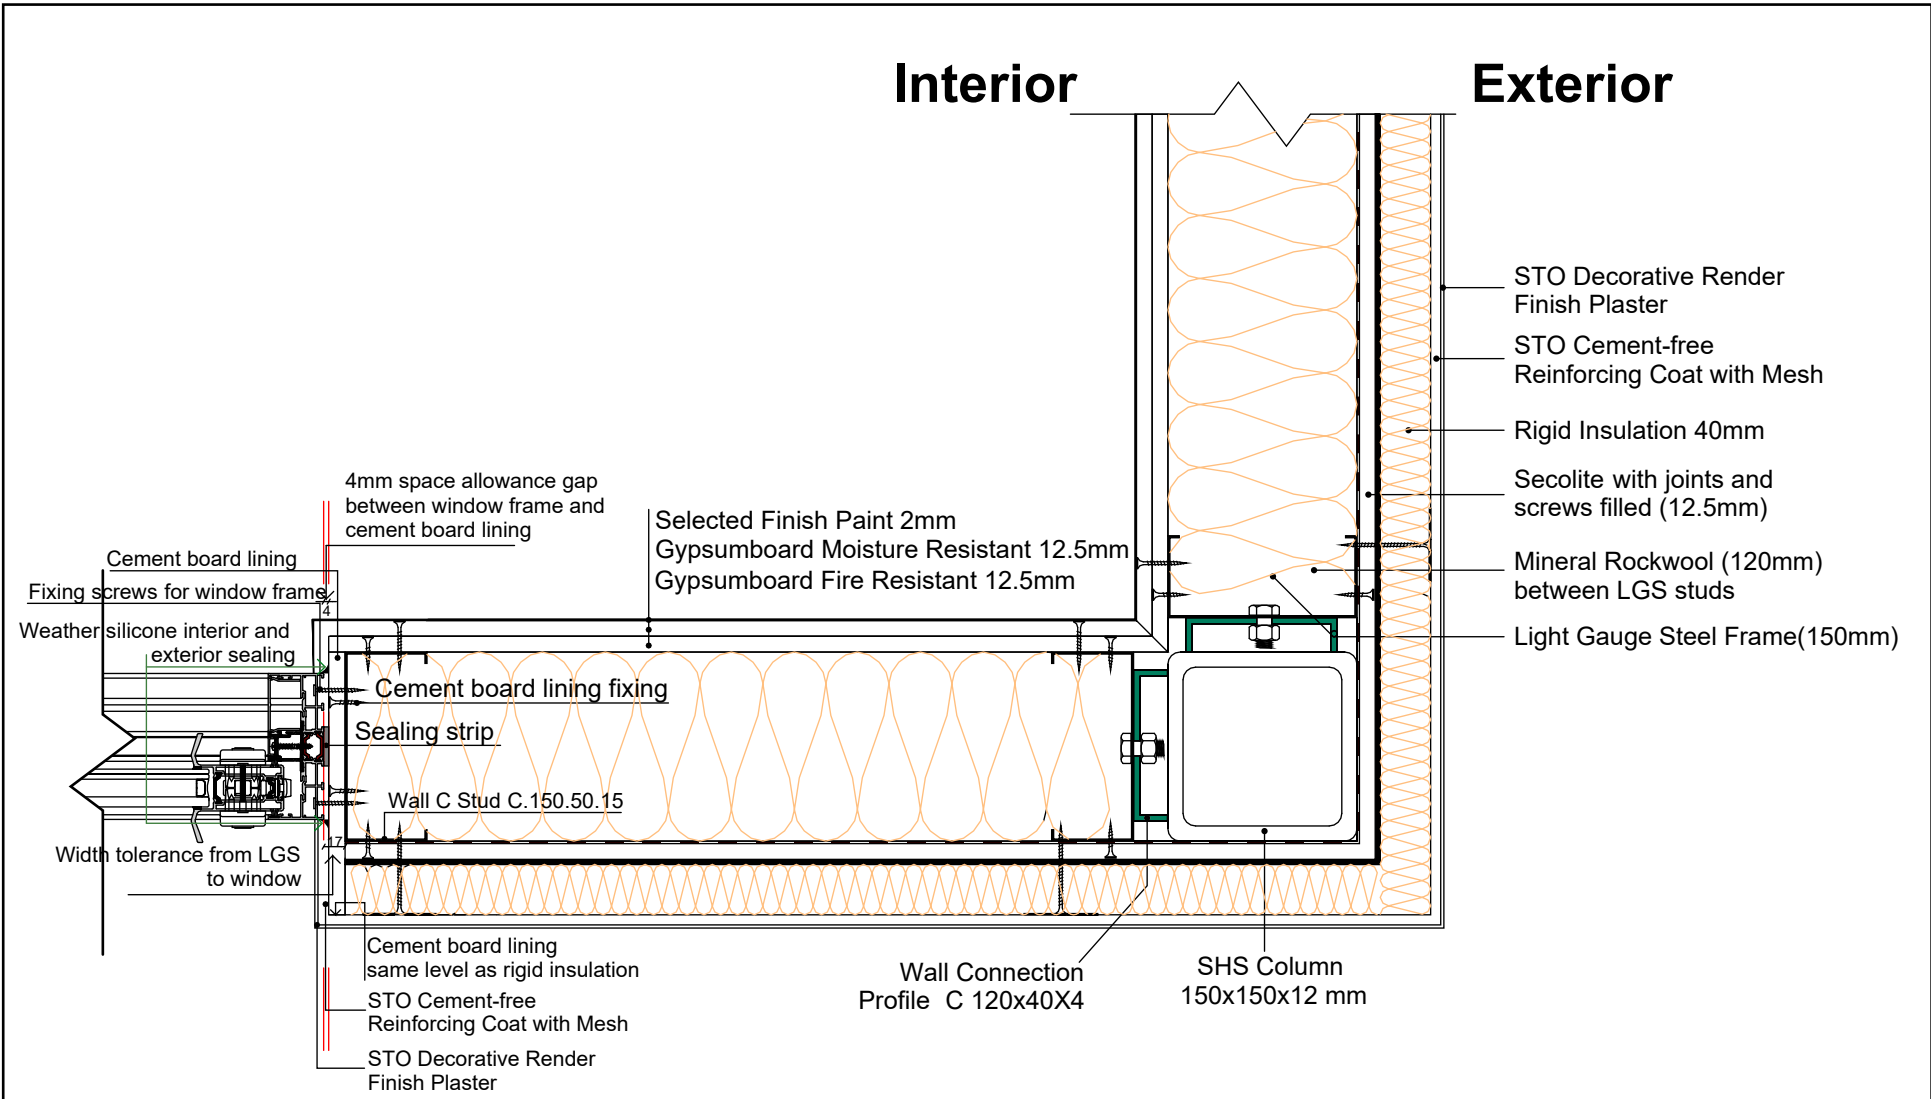

1. THESE DRAWINGS MUST BE CHECKED BY THE CUSTOMER OR CONTRACTOR PRIOR TO APPROVAL. ANY ERRORS OR OMISSIONS MUST BE REPORTED IN WRITING TO BAUHU PRIOR TO COMMENCEMENT OF CONSTRUCTION.
2. ARCHITECTURAL DRAWINGS SHOULD BE READ IN CONJUNCTION WITH STRUCTURAL DETAILING AND FABRICATION GENERAL ASSEMBLY DRAWINGS.
3. FOR CONSTRUCTION PURPOSES, USE ONLY THE LATEST APPROVED DRAWINGS LABELED 'ISSUED FOR CONSTRUCTION'.
4. DO NOT SCALE FROM THIS DRAWING.
5. THE COMPANY OPERATES USING METRIC DIMENSIONS AS THE PRINCIPAL DENOMINATION.
6. ALL CONCRETE WORKS ARE OUTSIDE OF THE SCOPE OF THE COMPANY. INFORMATION REGARDING SLAB DESIGN AND CONNECTIONS IN THESE DRAWINGS ARE INTENDED FOR GUIDENCE ONLY. FOUNDATION AND SLAB WORKS SHOULD BE DESIGNED AND APPROVED BY A LOCAL STRUCTURAL ENGINEER.
7. THE COMPANY RETAINS FULL TITLE AND OWNERSHIP OF THESE PLANS AND DESIGNS. ANY UNAUTHORISED USE, REPRODUCTION, OR DISTRIBUTION OF THESE PLANS, WHETHER IN WHOLE OR PART, IS EXPRESSLY PROHIBITED WITHOUT PRIOR WRITTEN CONSENT.
8. THE HYBRID STEEL FRAME CONSTRUCTION SYSTEM AND METHODOLOGY (PATENT PENDING) DESCRIBED IN THESE PLANS HAS BEEN DEVELOPED BY THE COMPANY AND IS SUBJECT TO A PROVISIONAL PATENT APPLICATION & ASSIGNMENT - US APPLICATION NO. 63/722,841

No.	Revision	Date

ISSUED FOR:

Issued for information

Issued for client approval

Issued for fabrication

Issued for construction

Coconut Villa
3 Bed

DRAWING TITLE: Wall Details

DRAWN BY: Y.A.Clark

SCALE:

DRAWING NO: C101

DATE: 16/02/2026

1. THESE DRAWINGS MUST BE CHECKED BY THE CUSTOMER OR CONTRACTOR PRIOR TO APPROVAL. ANY ERRORS OR OMISSIONS MUST BE REPORTED IN WRITING TO BAUHU PRIOR TO COMMENCEMENT OF CONSTRUCTION.
2. ARCHITECTURAL DRAWINGS SHOULD BE READ IN CONJUNCTION WITH STRUCTURAL DETAILING AND FABRICATION GENERAL ASSEMBLY DRAWINGS.
3. FOR CONSTRUCTION PURPOSES, USE ONLY THE LATEST APPROVED DRAWINGS LABELED 'ISSUED FOR CONSTRUCTION'.
4. DO NOT SCALE FROM THIS DRAWING.
5. THE COMPANY OPERATES USING METRIC DIMENSIONS AS THE PRINCIPAL DENOMINATION.
6. ALL CONCRETE WORKS ARE OUTSIDE OF THE SCOPE OF THE COMPANY. INFORMATION REGARDING SLAB DESIGN AND CONNECTIONS IN THESE DRAWINGS ARE INTENDED FOR GUIDANCE ONLY. FOUNDATION AND SLAB WORKS SHOULD BE DESIGNED AND APPROVED BY A LOCAL STRUCTURAL ENGINEER.
7. THE COMPANY RETAINS FULL TITLE AND OWNERSHIP OF THESE PLANS AND DESIGNS. ANY UNAUTHORISED USE, REPRODUCTION, OR DISTRIBUTION OF THESE PLANS, WHETHER IN WHOLE OR PART, IS EXPRESSLY PROHIBITED WITHOUT PRIOR WRITTEN CONSENT.
8. THE HYBRID STEEL FRAME CONSTRUCTION SYSTEM AND METHODOLOGY (PATENT PENDING) DESCRIBED IN THESE PLANS HAS BEEN DEVELOPED BY THE COMPANY AND IS SUBJECT TO A PROVISIONAL PATENT APPLICATION & ASSIGNMENT - US APPLICATION NO. 63/722,841

No.	Revision	Date

ISSUED FOR:

Issued for information

Issued for client approval

Issued for fabrication

Issued for construction

Coconut Villa
3 Bed

DRAWING TITLE:

Window/Door Plan Detail

DRAWN BY:

Y.A.Clark




SCALE:

DRAWING NO:



C102

DATE:


16/02/2026

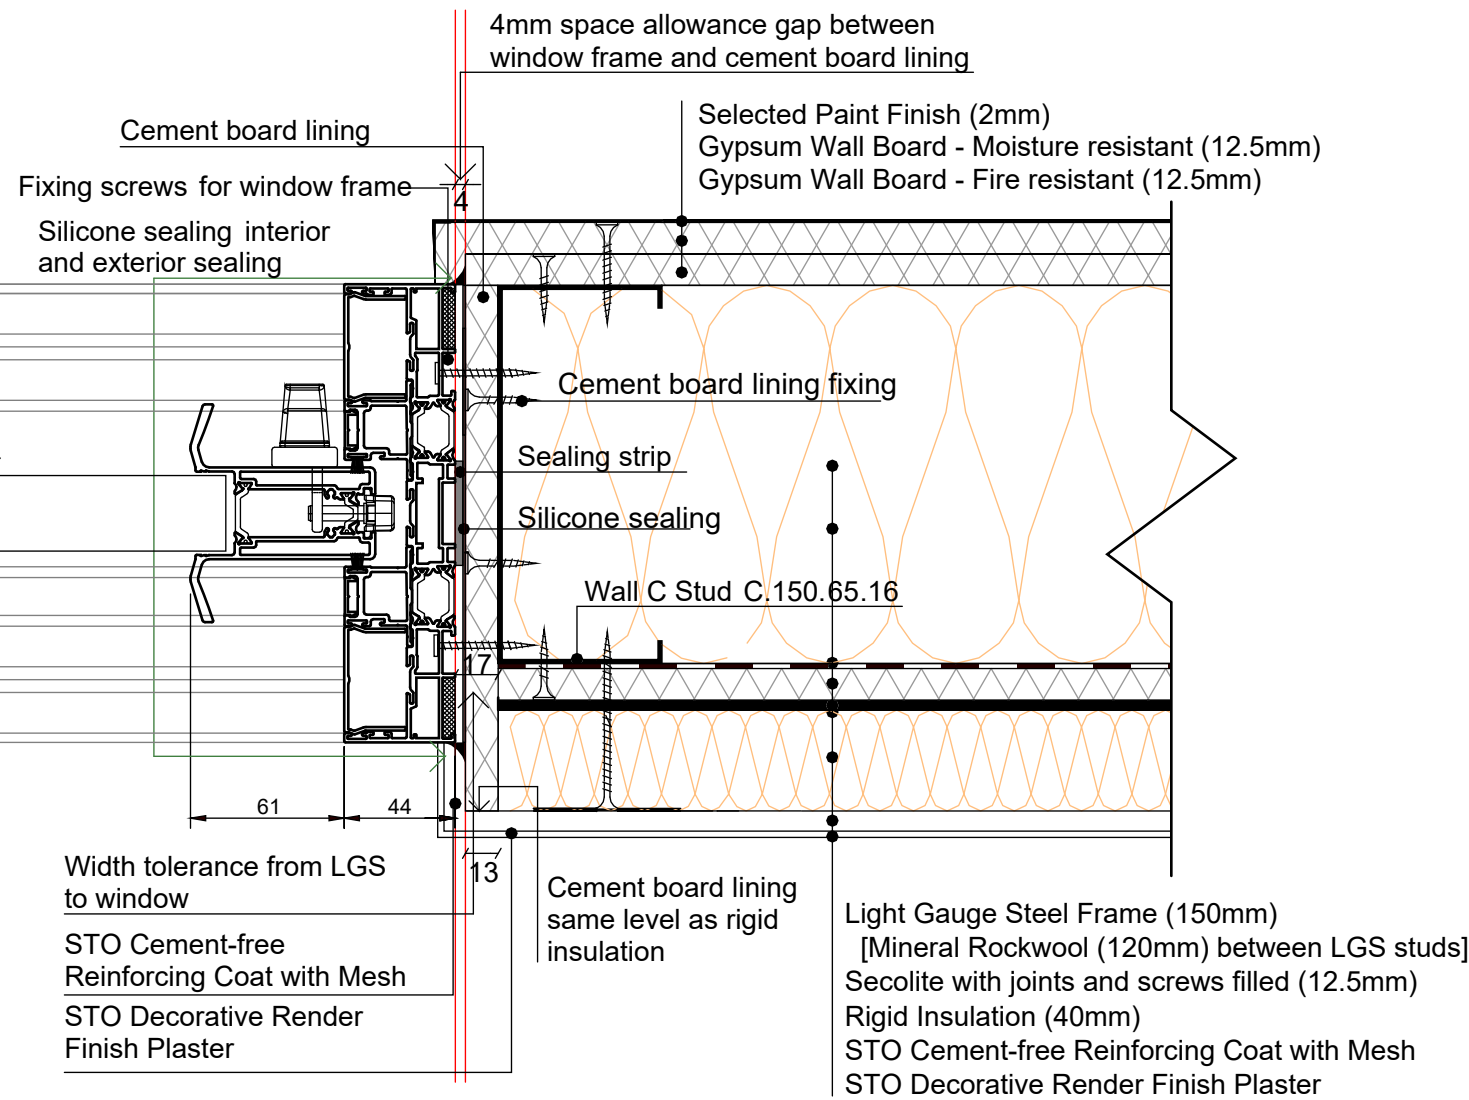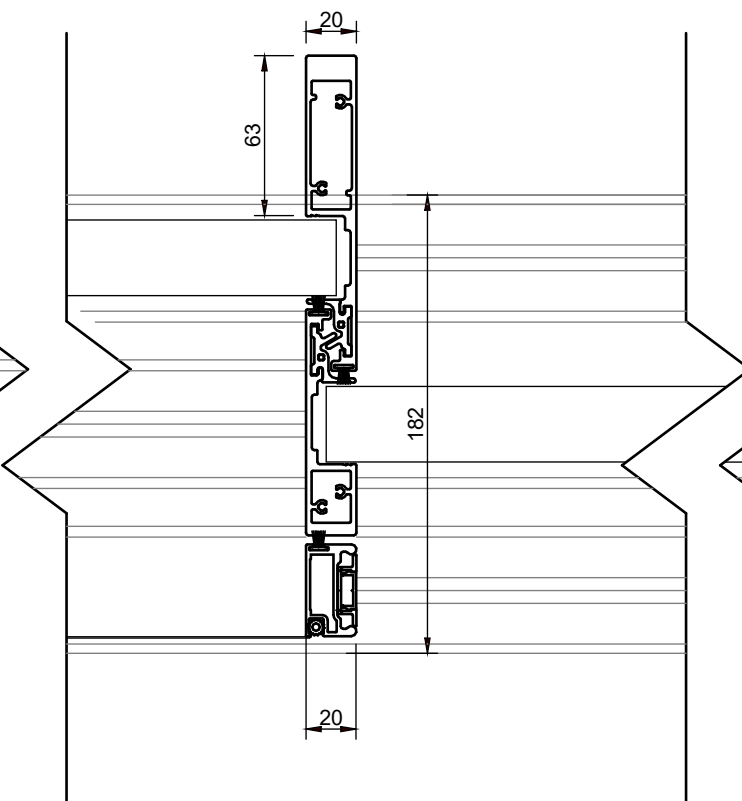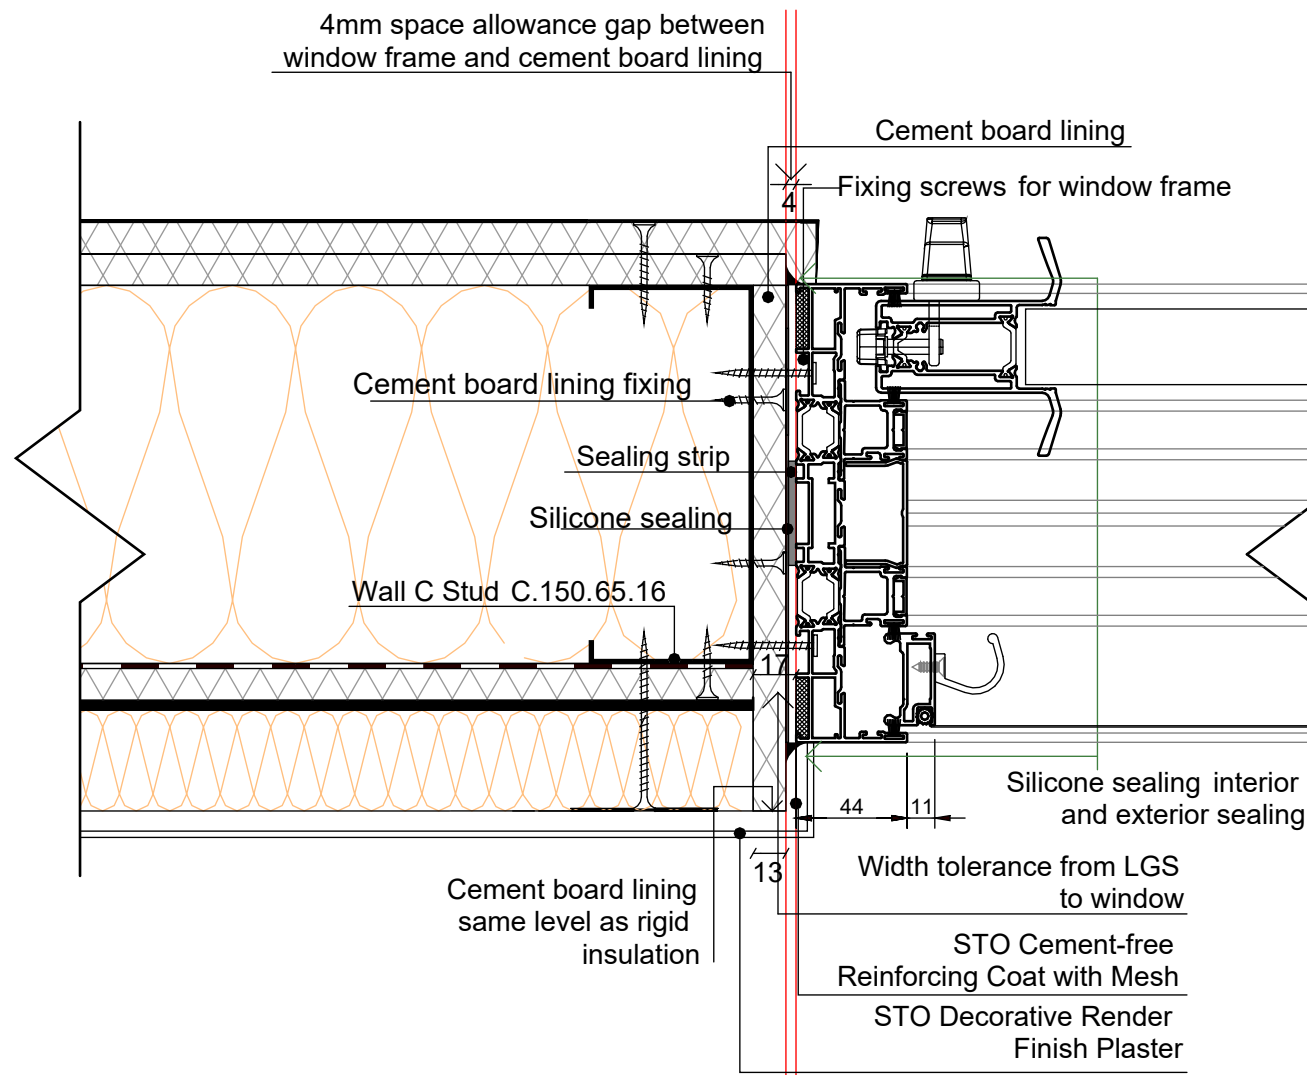

Plan Detail: Slider Door/Window with insect screens

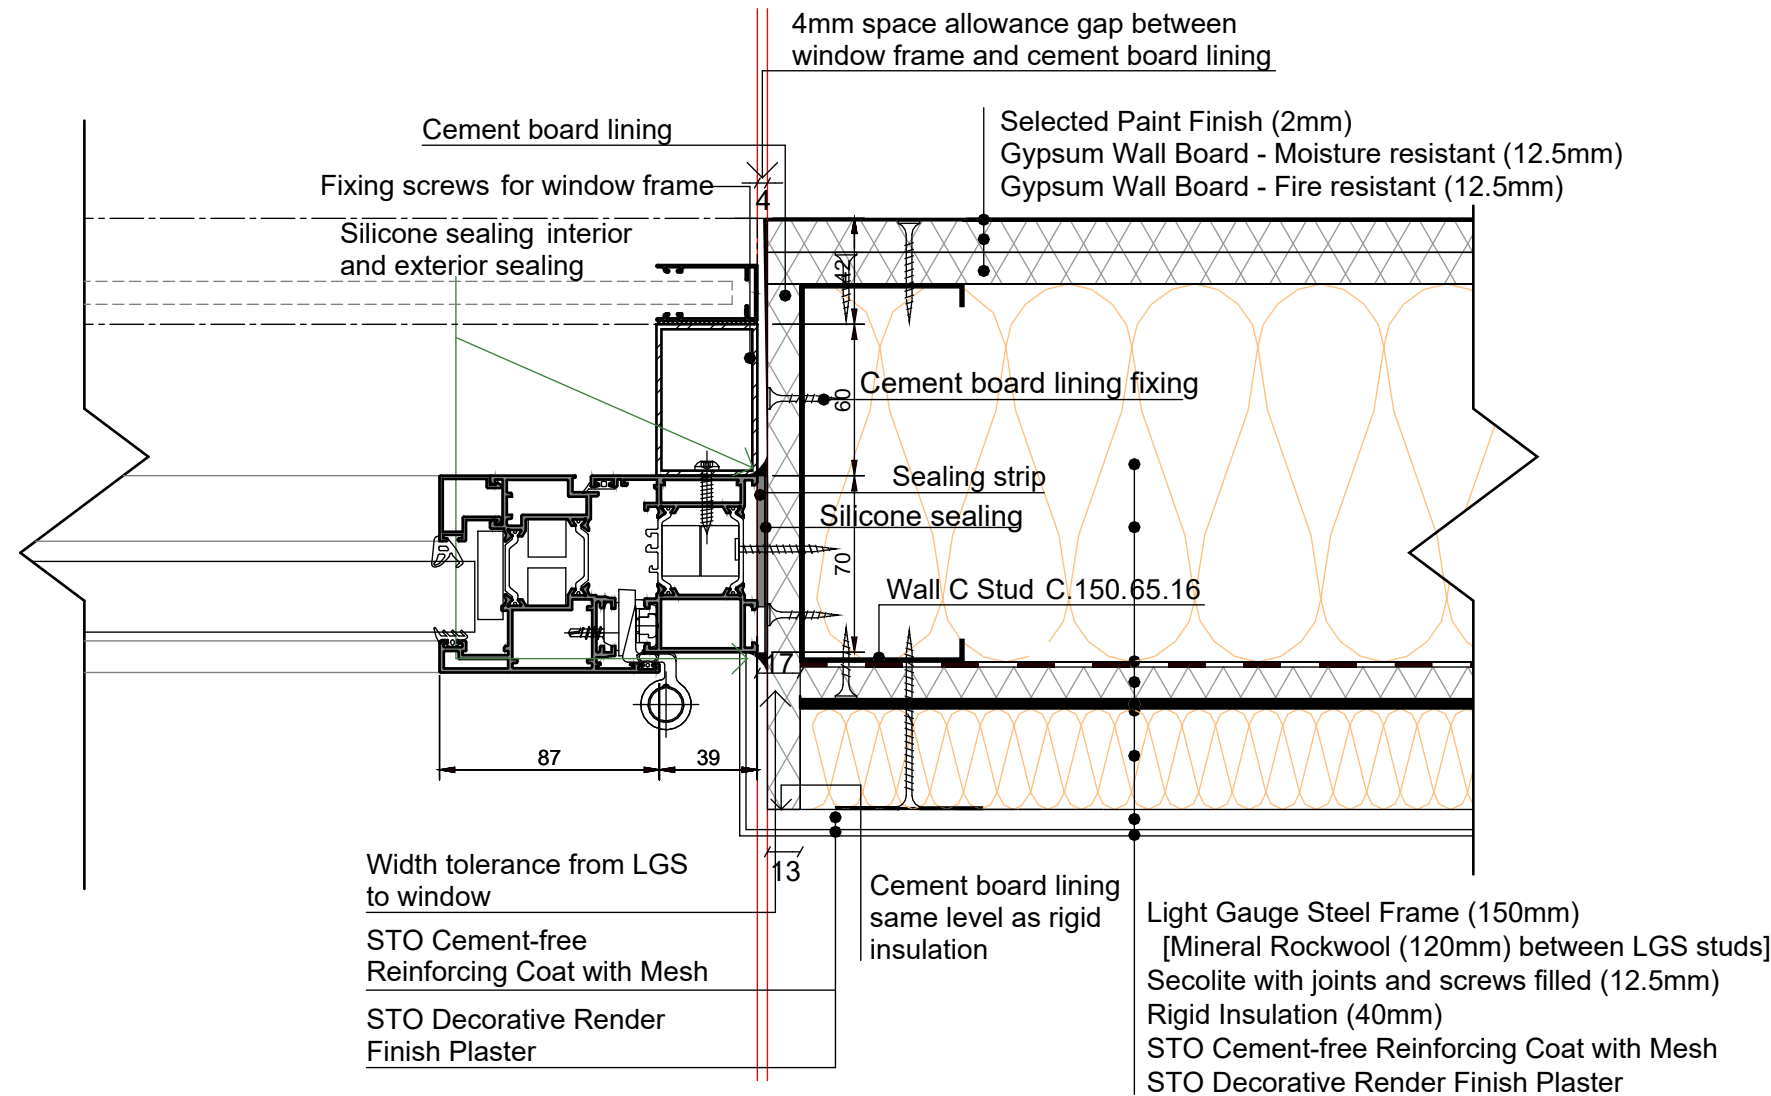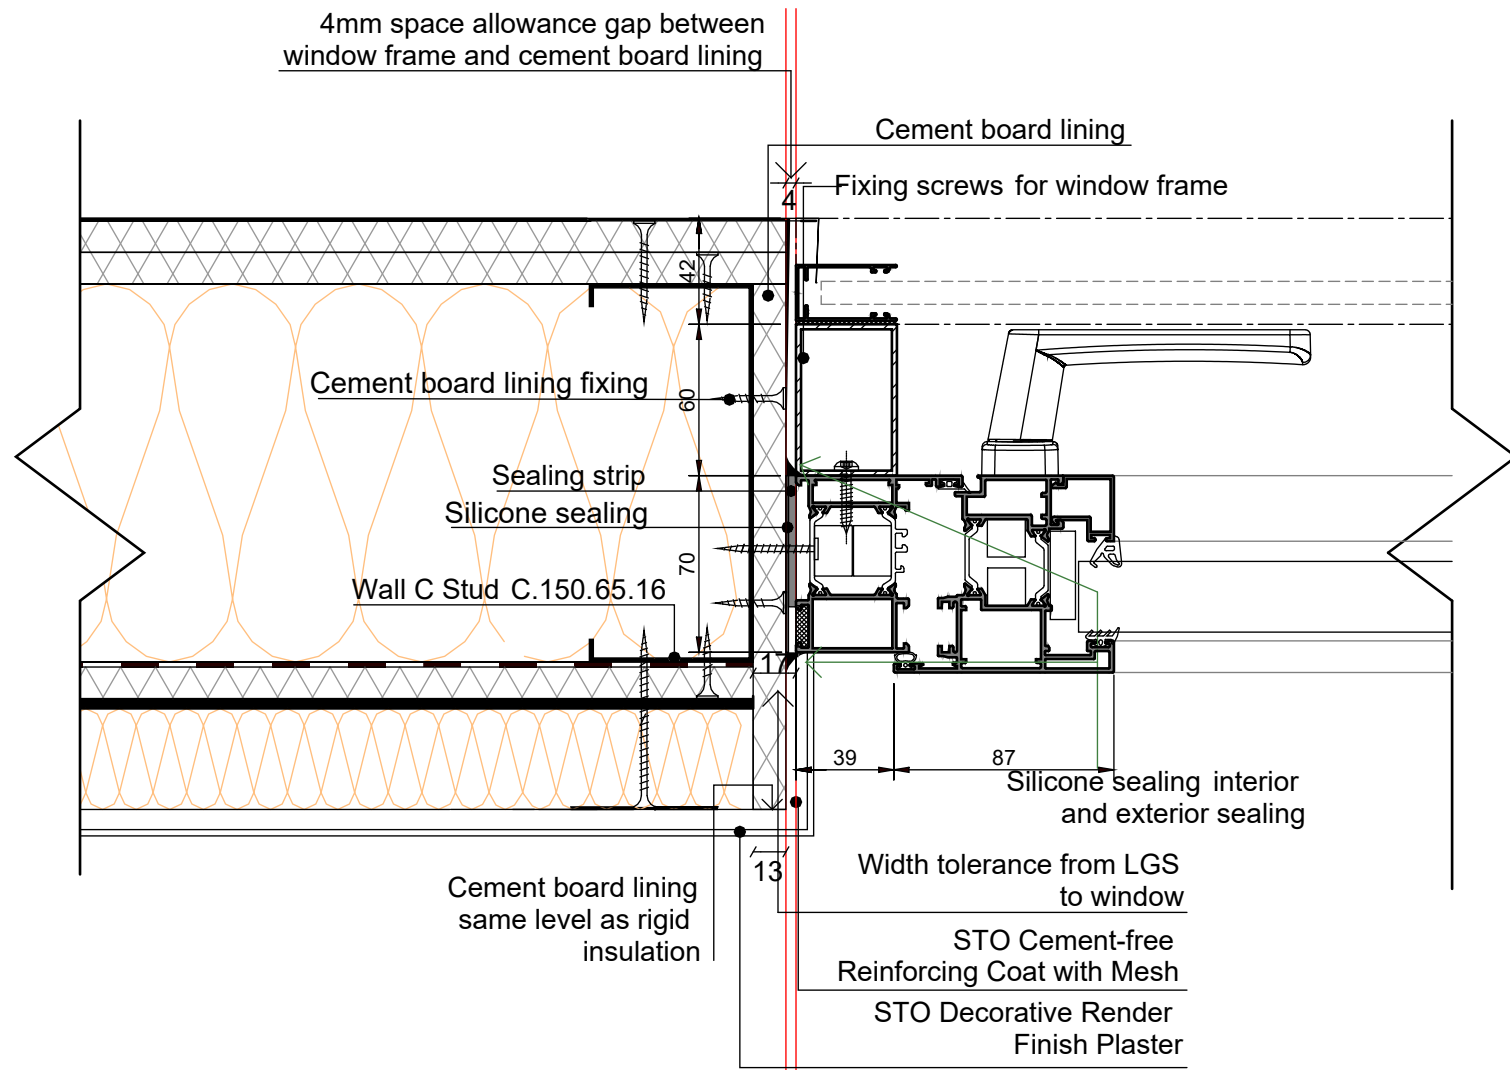

Plan Detail: Casement Door/Window with insect screens

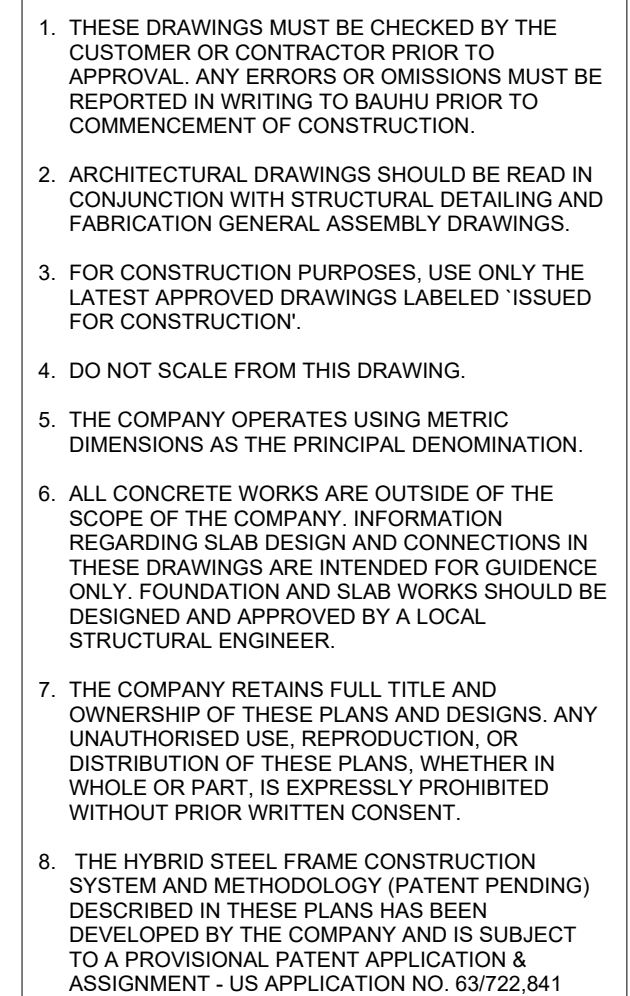[illegible]

Issued for information

Coconut Villa


3 Bed

Slider Door Section Detail





Y.A.Clark

C103

16/02/2026

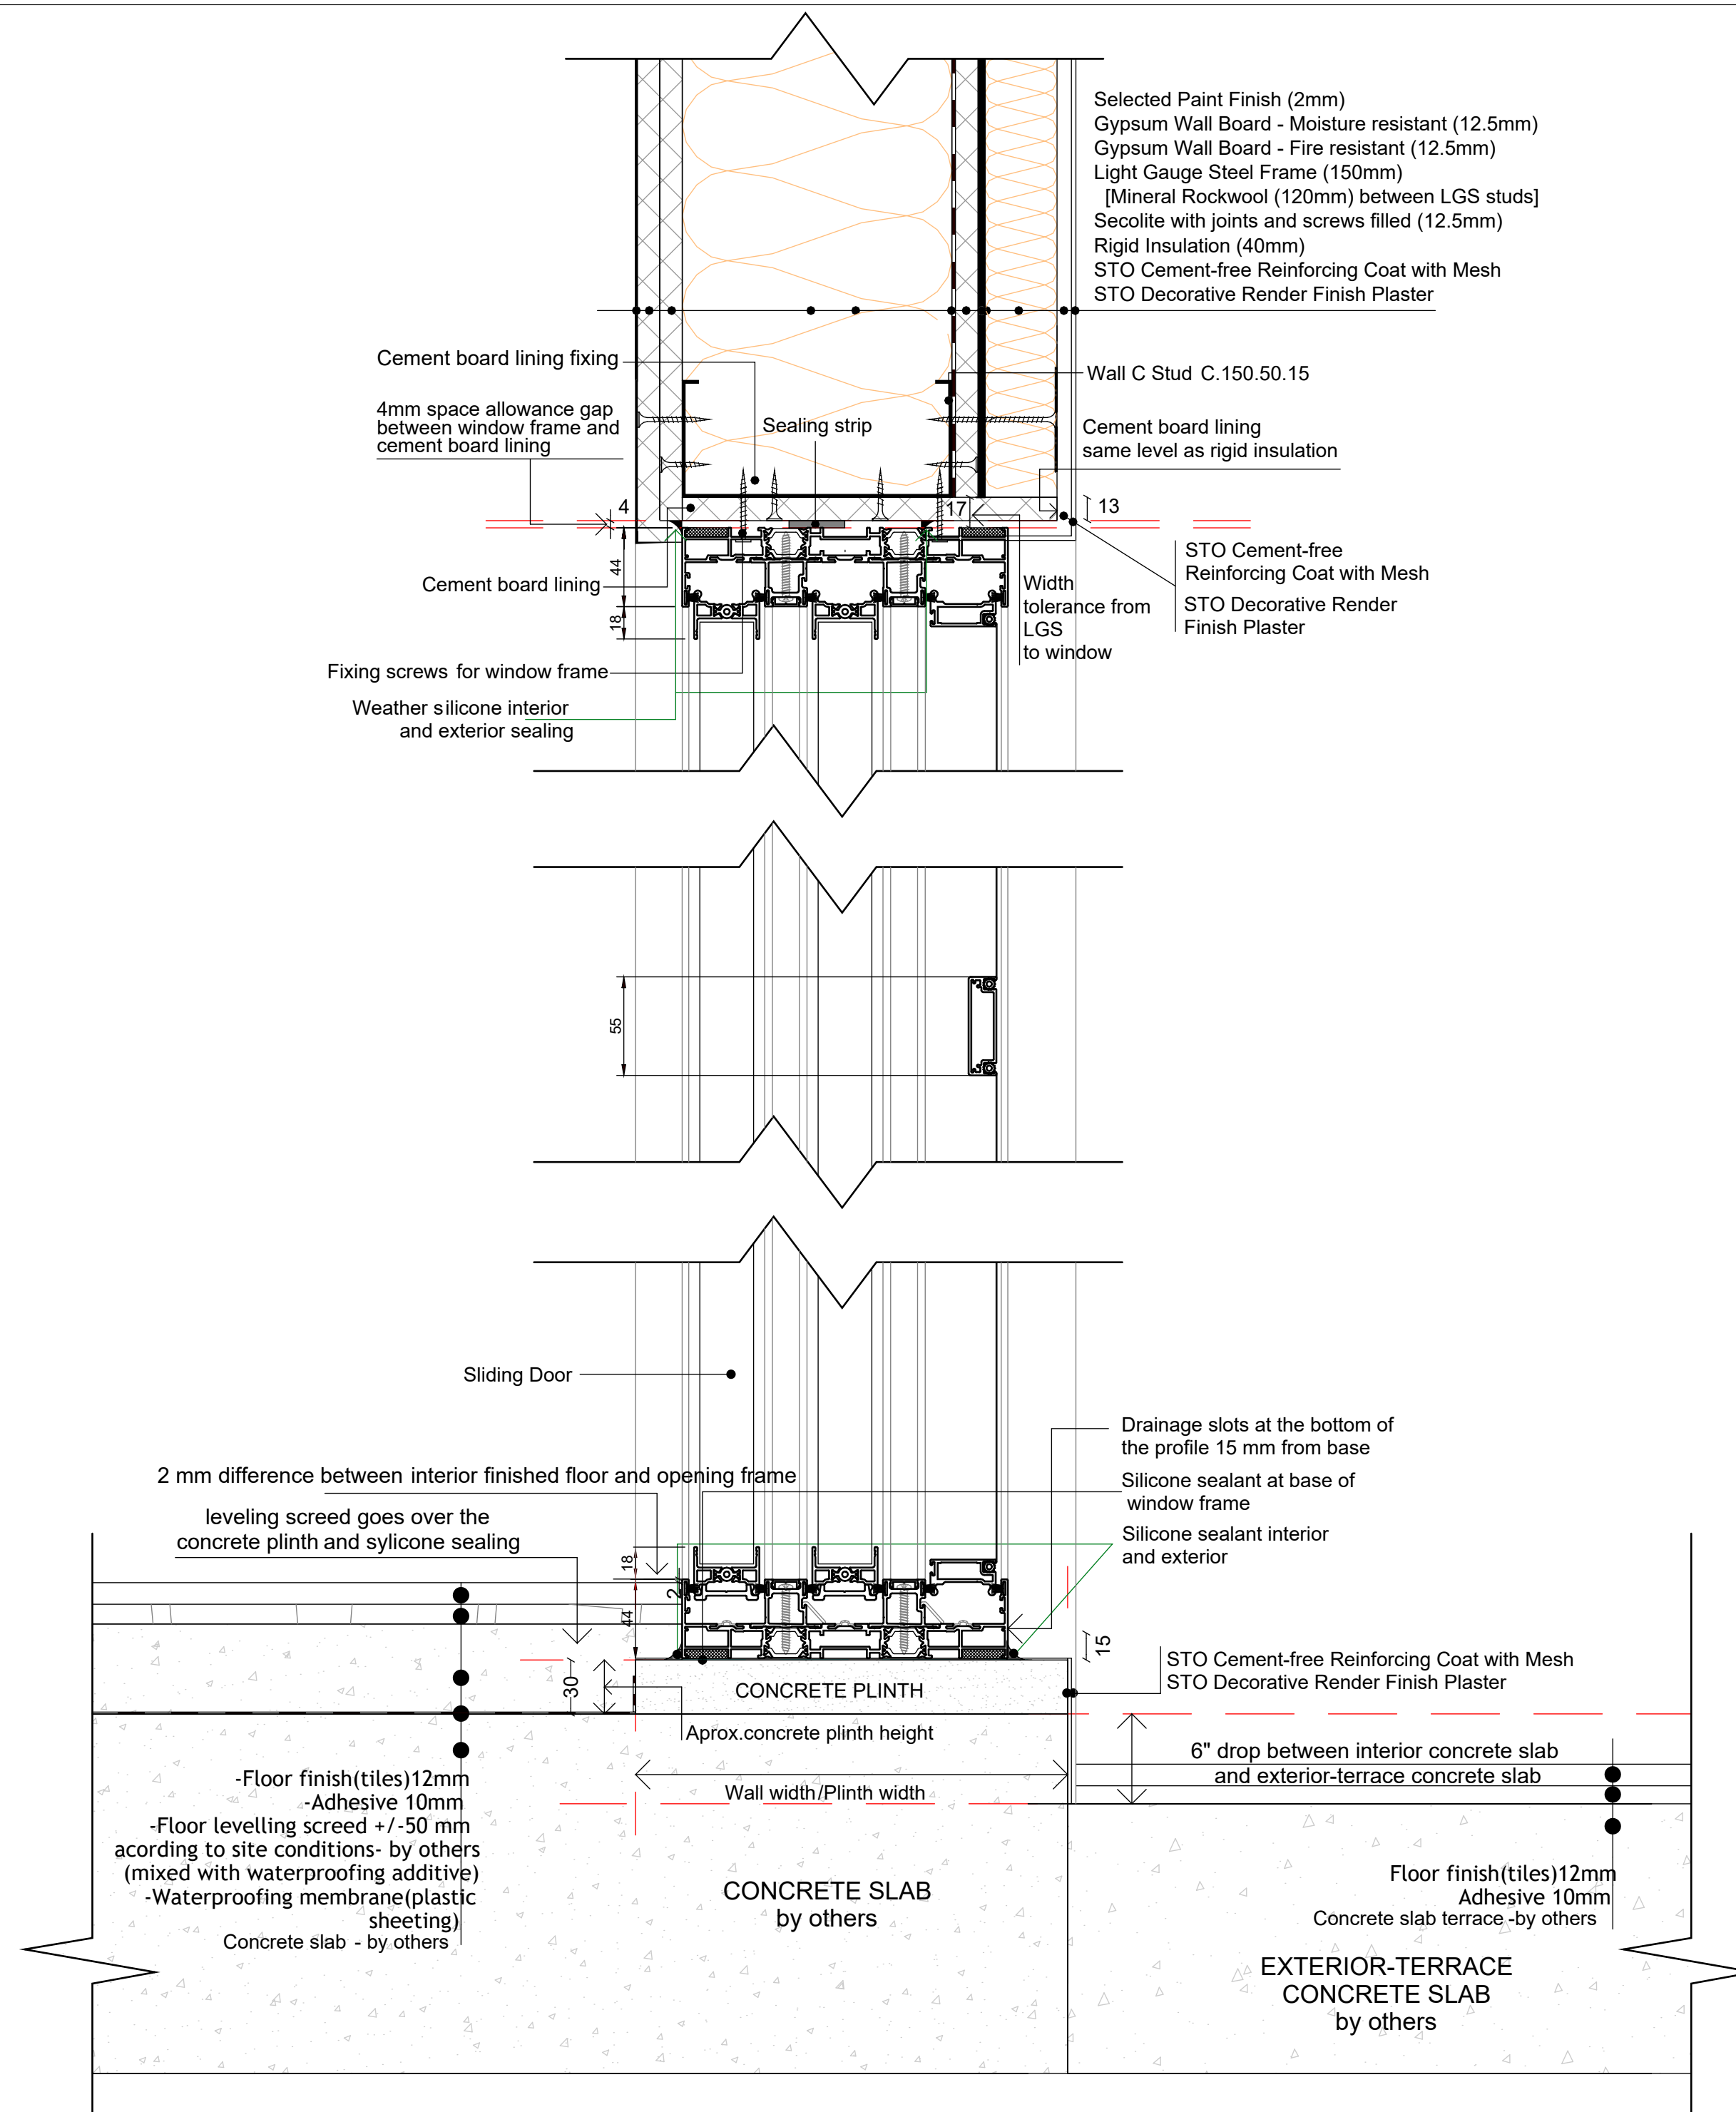

Section Detail: Slider door base fixing detail (with insect screen)

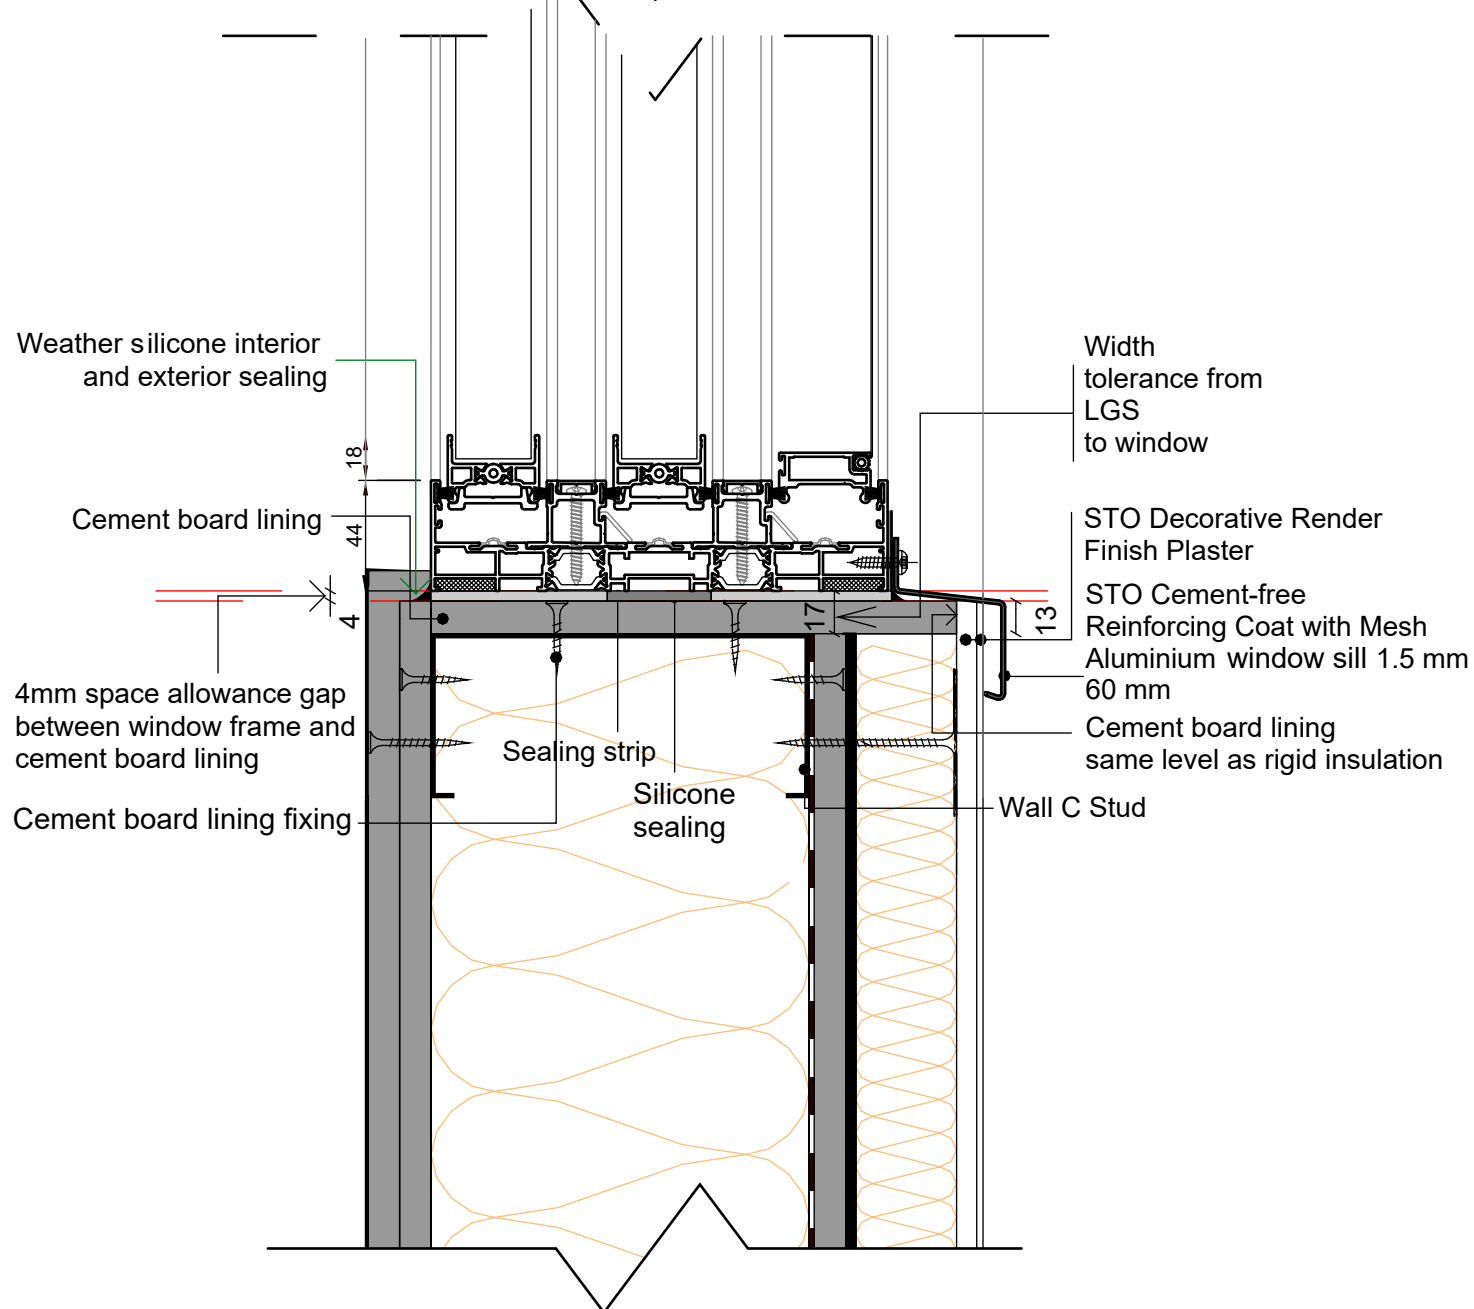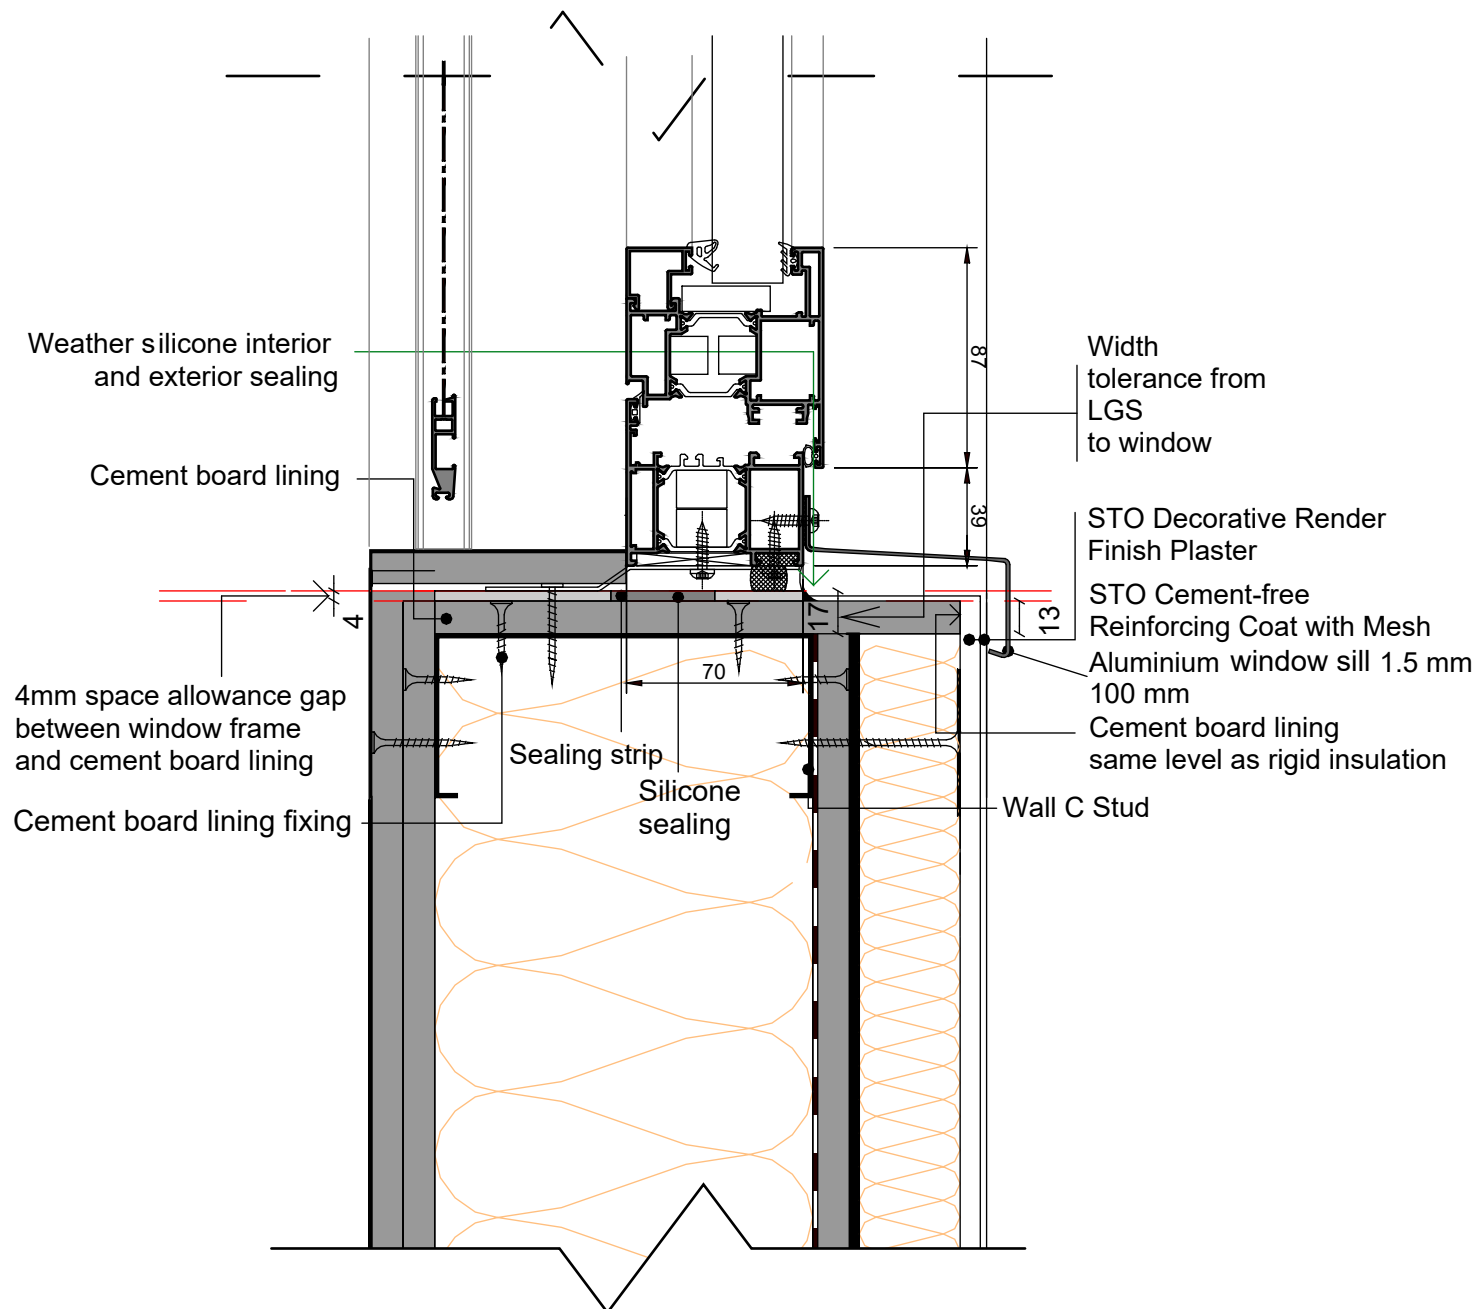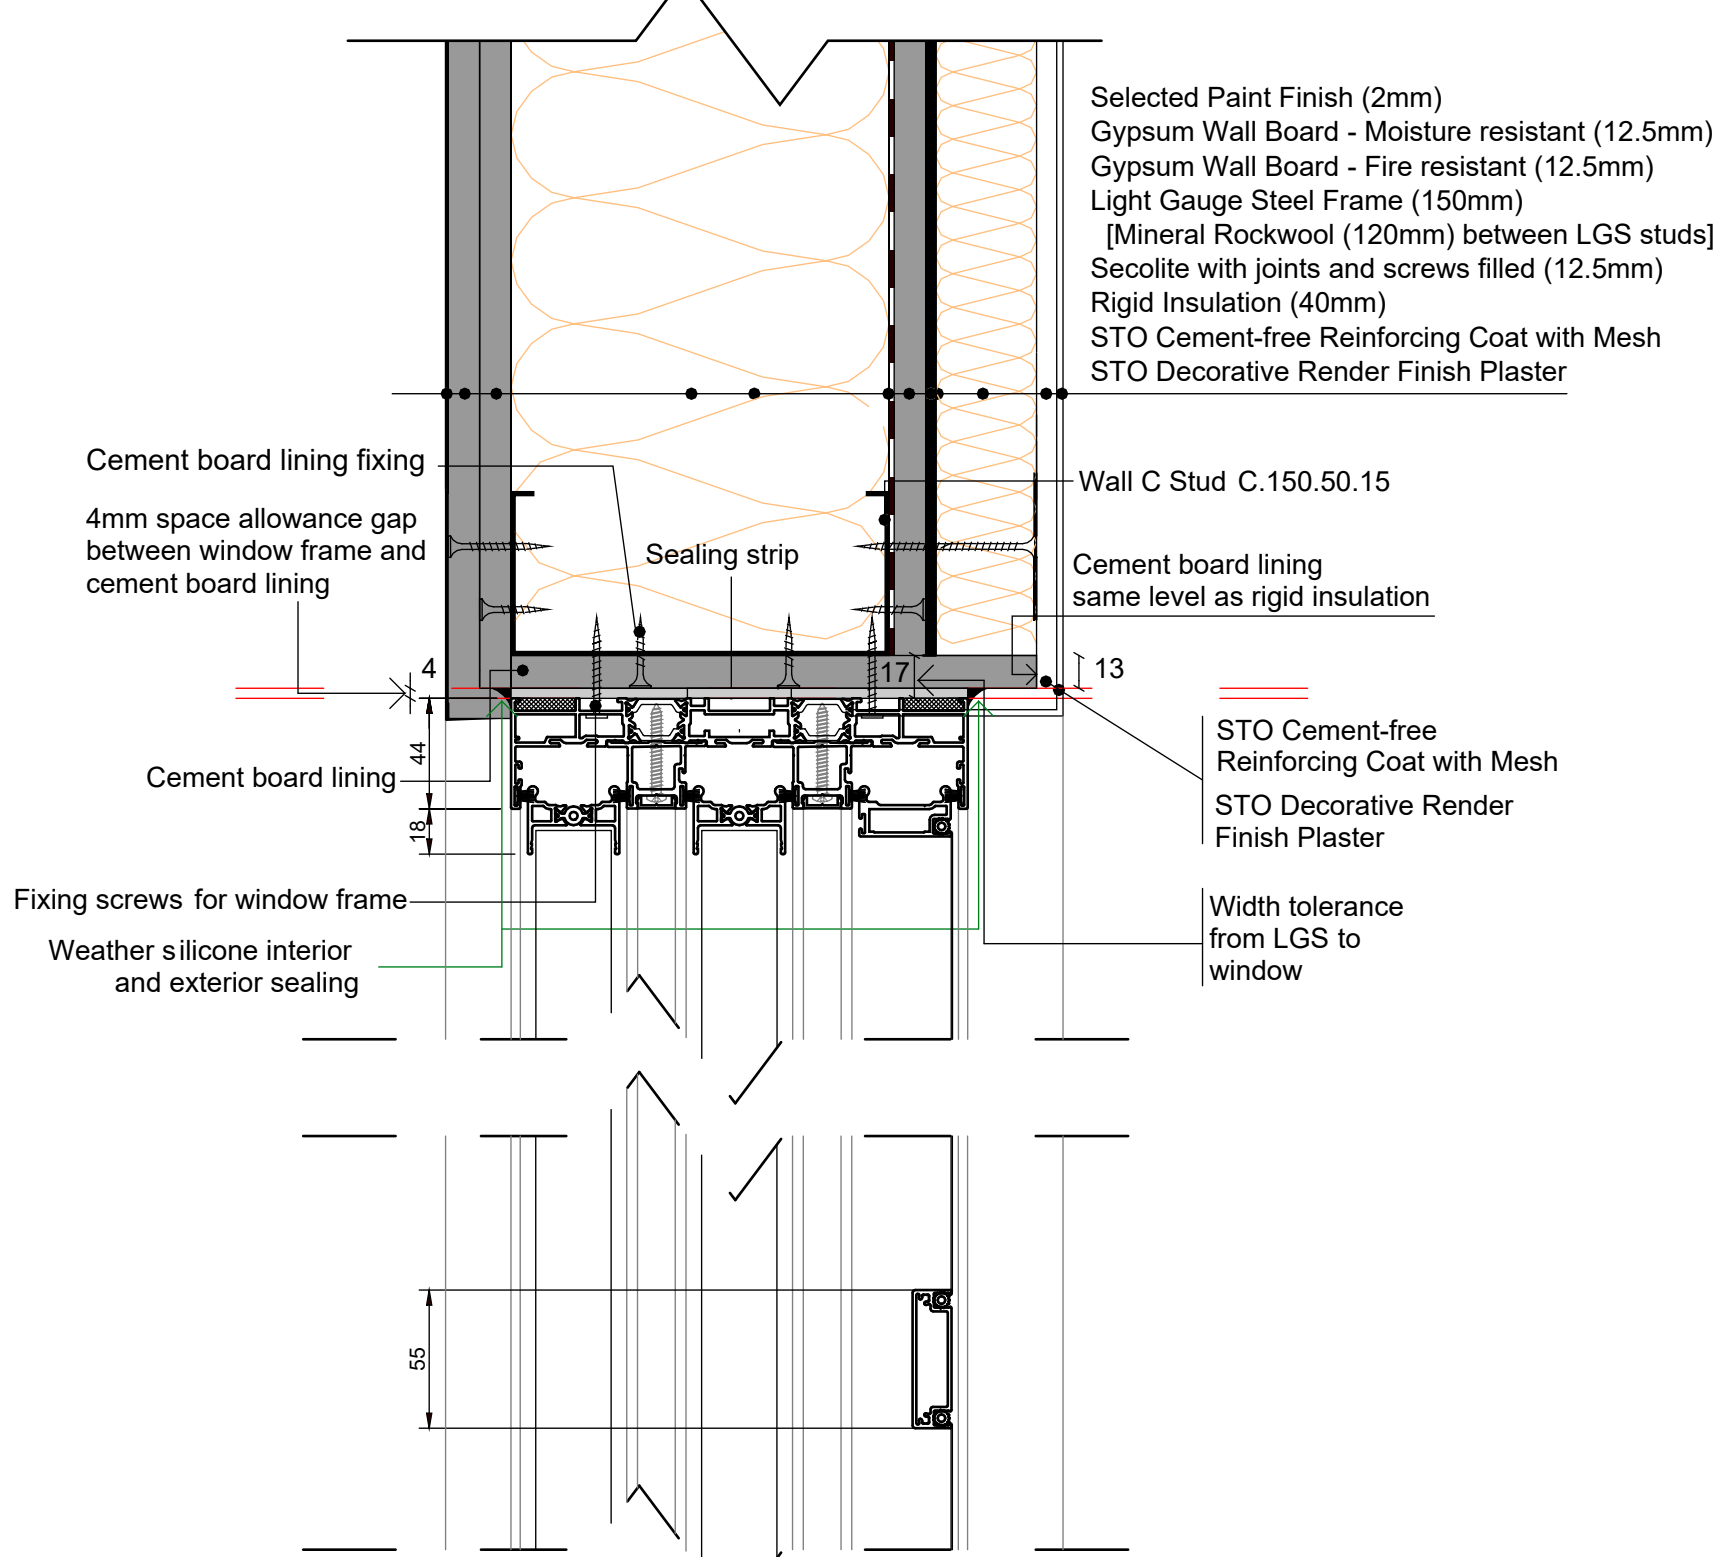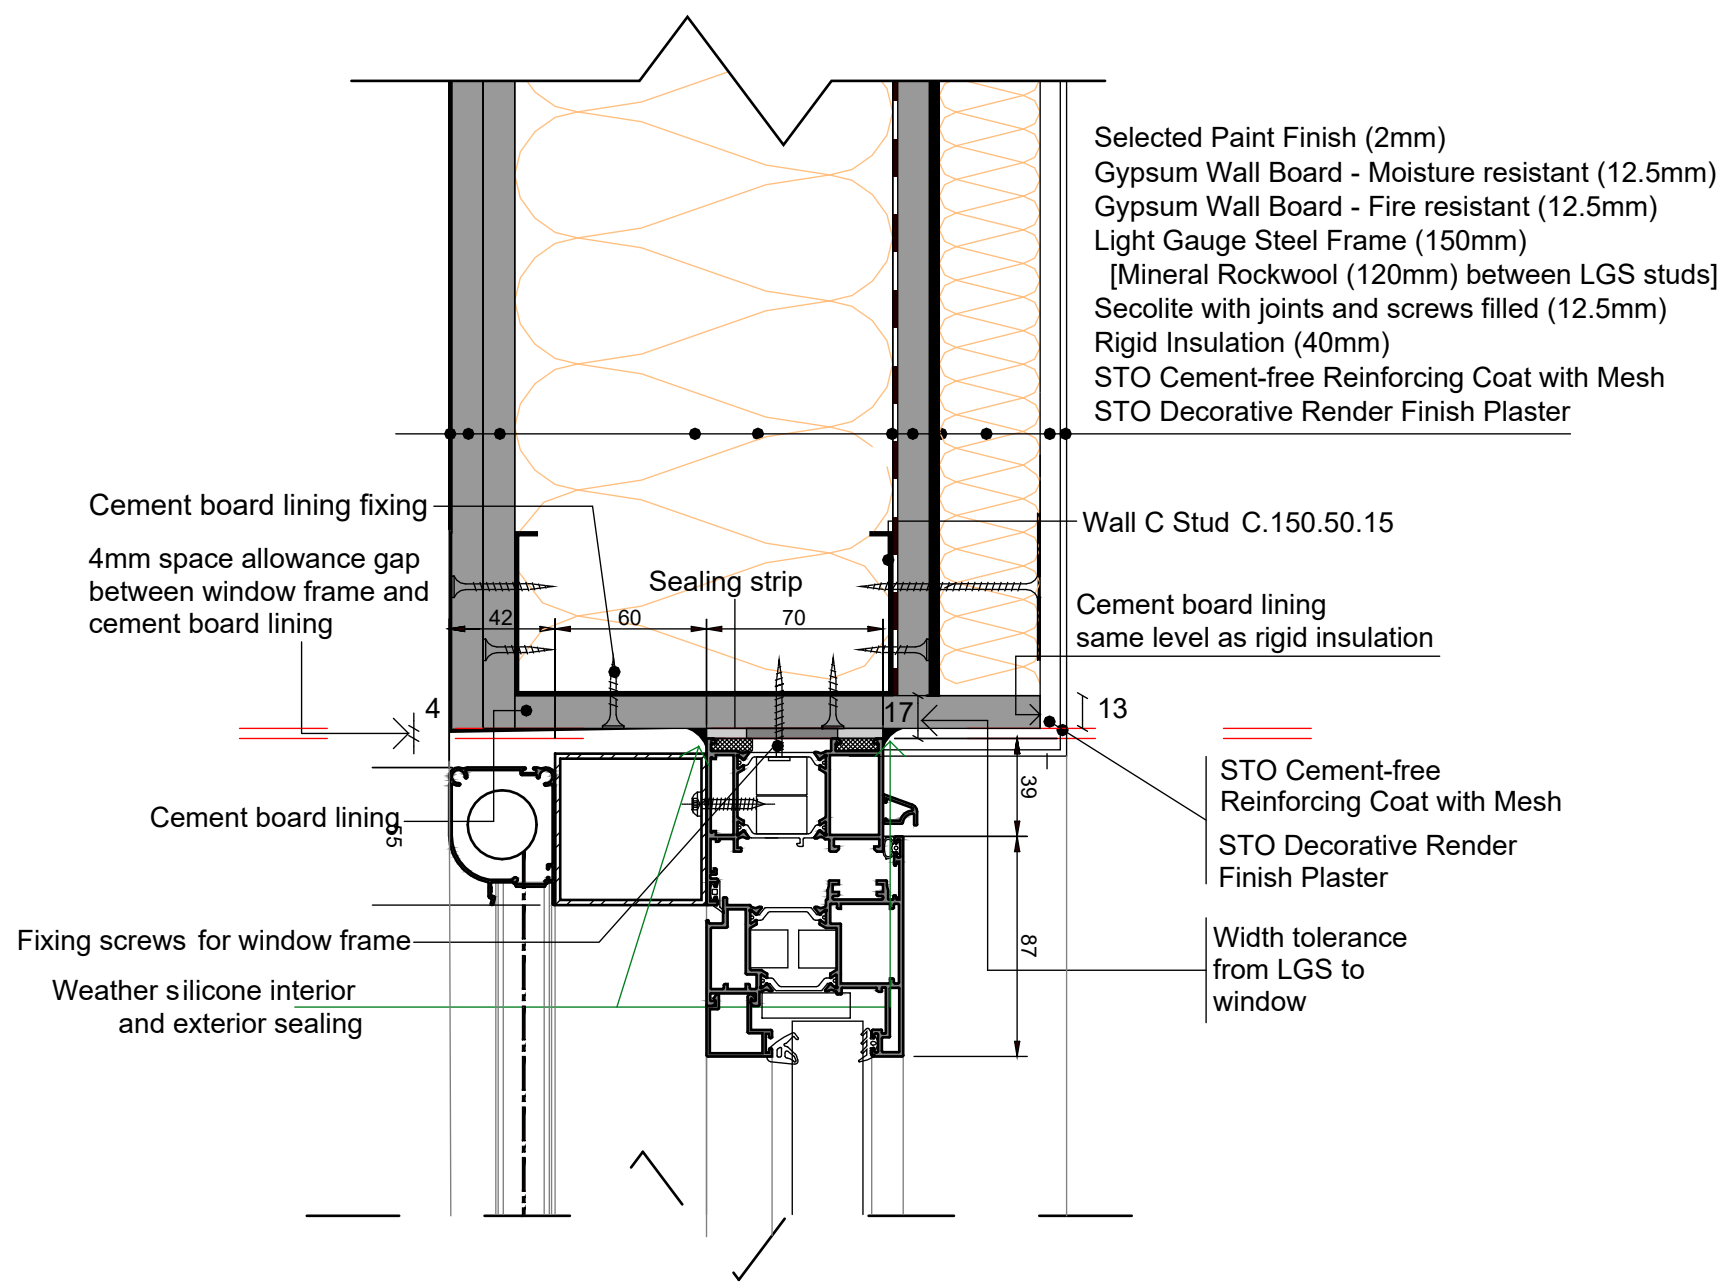

Section Detail: Slider Window with insect screens

Section Detail: Casement Window with insect screens

1. THESE DRAWINGS MUST BE CHECKED BY THE CUSTOMER OR CONTRACTOR PRIOR TO APPROVAL. ANY ERRORS OR OMISSIONS MUST BE REPORTED IN WRITING TO BAUHU PRIOR TO COMMENCEMENT OF CONSTRUCTION.
2. ARCHITECTURAL DRAWINGS SHOULD BE READ IN CONJUNCTION WITH STRUCTURAL DETAILING AND FABRICATION GENERAL ASSEMBLY DRAWINGS.
3. FOR CONSTRUCTION PURPOSES, USE ONLY THE LATEST APPROVED DRAWINGS LABELED 'ISSUED FOR CONSTRUCTION'.
4. DO NOT SCALE FROM THIS DRAWING.
5. THE COMPANY OPERATES USING METRIC DIMENSIONS AS THE PRINCIPAL DENOMINATION.
6. ALL CONCRETE WORKS ARE OUTSIDE OF THE SCOPE OF THE COMPANY. INFORMATION REGARDING SLAB DESIGN AND CONNECTIONS IN THESE DRAWINGS ARE INTENDED FOR GUIDANCE ONLY. FOUNDATION AND SLAB WORKS SHOULD BE DESIGNED AND APPROVED BY A LOCAL STRUCTURAL ENGINEER.
7. THE COMPANY RETAINS FULL TITLE AND OWNERSHIP OF THESE PLANS AND DESIGNS. ANY UNAUTHORISED USE, REPRODUCTION, OR DISTRIBUTION OF THESE PLANS, WHETHER IN WHOLE OR PART, IS EXPRESSLY PROHIBITED WITHOUT PRIOR WRITTEN CONSENT.
8. THE HYBRID STEEL FRAME CONSTRUCTION SYSTEM AND METHODOLOGY (PATENT PENDING) DESCRIBED IN THESE PLANS HAS BEEN DEVELOPED BY THE COMPANY AND IS SUBJECT TO A PROVISIONAL PATENT APPLICATION & ASSIGNMENT - US APPLICATION NO. 63/722,841

No.	Revision	Date

ISSUED FOR:

Issued for information

Issued for client approval

Issued for fabrication

Issued for construction

Coconut Villa 3 Bed

DRAWING TITLE:
Window Section Detail

DRAWN BY:
Y.A.Clark

SCALE:

DRAWING NO:
C104

DATE:
16/02/2026

1. THESE DRAWINGS MUST BE CHECKED BY THE CUSTOMER OR CONTRACTOR PRIOR TO APPROVAL. ANY ERRORS OR OMISSIONS MUST BE REPORTED IN WRITING TO BAUHU PRIOR TO COMMENCEMENT OF CONSTRUCTION.
2. ARCHITECTURAL DRAWINGS SHOULD BE READ IN CONJUNCTION WITH STRUCTURAL DETAILING AND FABRICATION GENERAL ASSEMBLY DRAWINGS.
3. FOR CONSTRUCTION PURPOSES, USE ONLY THE LATEST APPROVED DRAWINGS LABELED 'ISSUED FOR CONSTRUCTION'.
4. DO NOT SCALE FROM THIS DRAWING.
5. THE COMPANY OPERATES USING METRIC DIMENSIONS AS THE PRINCIPAL DENOMINATION.
6. ALL CONCRETE WORKS ARE OUTSIDE OF THE SCOPE OF THE COMPANY. INFORMATION REGARDING SLAB DESIGN AND CONNECTIONS IN THESE DRAWINGS ARE INTENDED FOR GUIDANCE ONLY. FOUNDATION AND SLAB WORKS SHOULD BE DESIGNED AND APPROVED BY A LOCAL STRUCTURAL ENGINEER.
7. THE COMPANY RETAINS FULL TITLE AND OWNERSHIP OF THESE PLANS AND DESIGNS. ANY UNAUTHORISED USE, REPRODUCTION, OR DISTRIBUTION OF THESE PLANS, WHETHER IN WHOLE OR PART, IS EXPRESSLY PROHIBITED WITHOUT PRIOR WRITTEN CONSENT.
8. THE HYBRID STEEL FRAME CONSTRUCTION SYSTEM AND METHODOLOGY (PATENT PENDING) DESCRIBED IN THESE PLANS HAS BEEN DEVELOPED BY THE COMPANY AND IS SUBJECT TO A PROVISIONAL PATENT APPLICATION & ASSIGNMENT - US APPLICATION NO. 63/722,841

No.	Revision	Date

ISSUED FOR:

☐ Issued for information

☐ Issued for client approval

☐ Issued for fabrication

☐ Issued for construction

Coconut Villa 3 Bed

DRAWING TITLE:

Base Detail

DRAWN BY:

Y.A.Clark

SCALE:

1 : 7



DRAWING NO:


C105

DATE:

16/02/2026

Top of the pier is level
with the 6" concrete slab

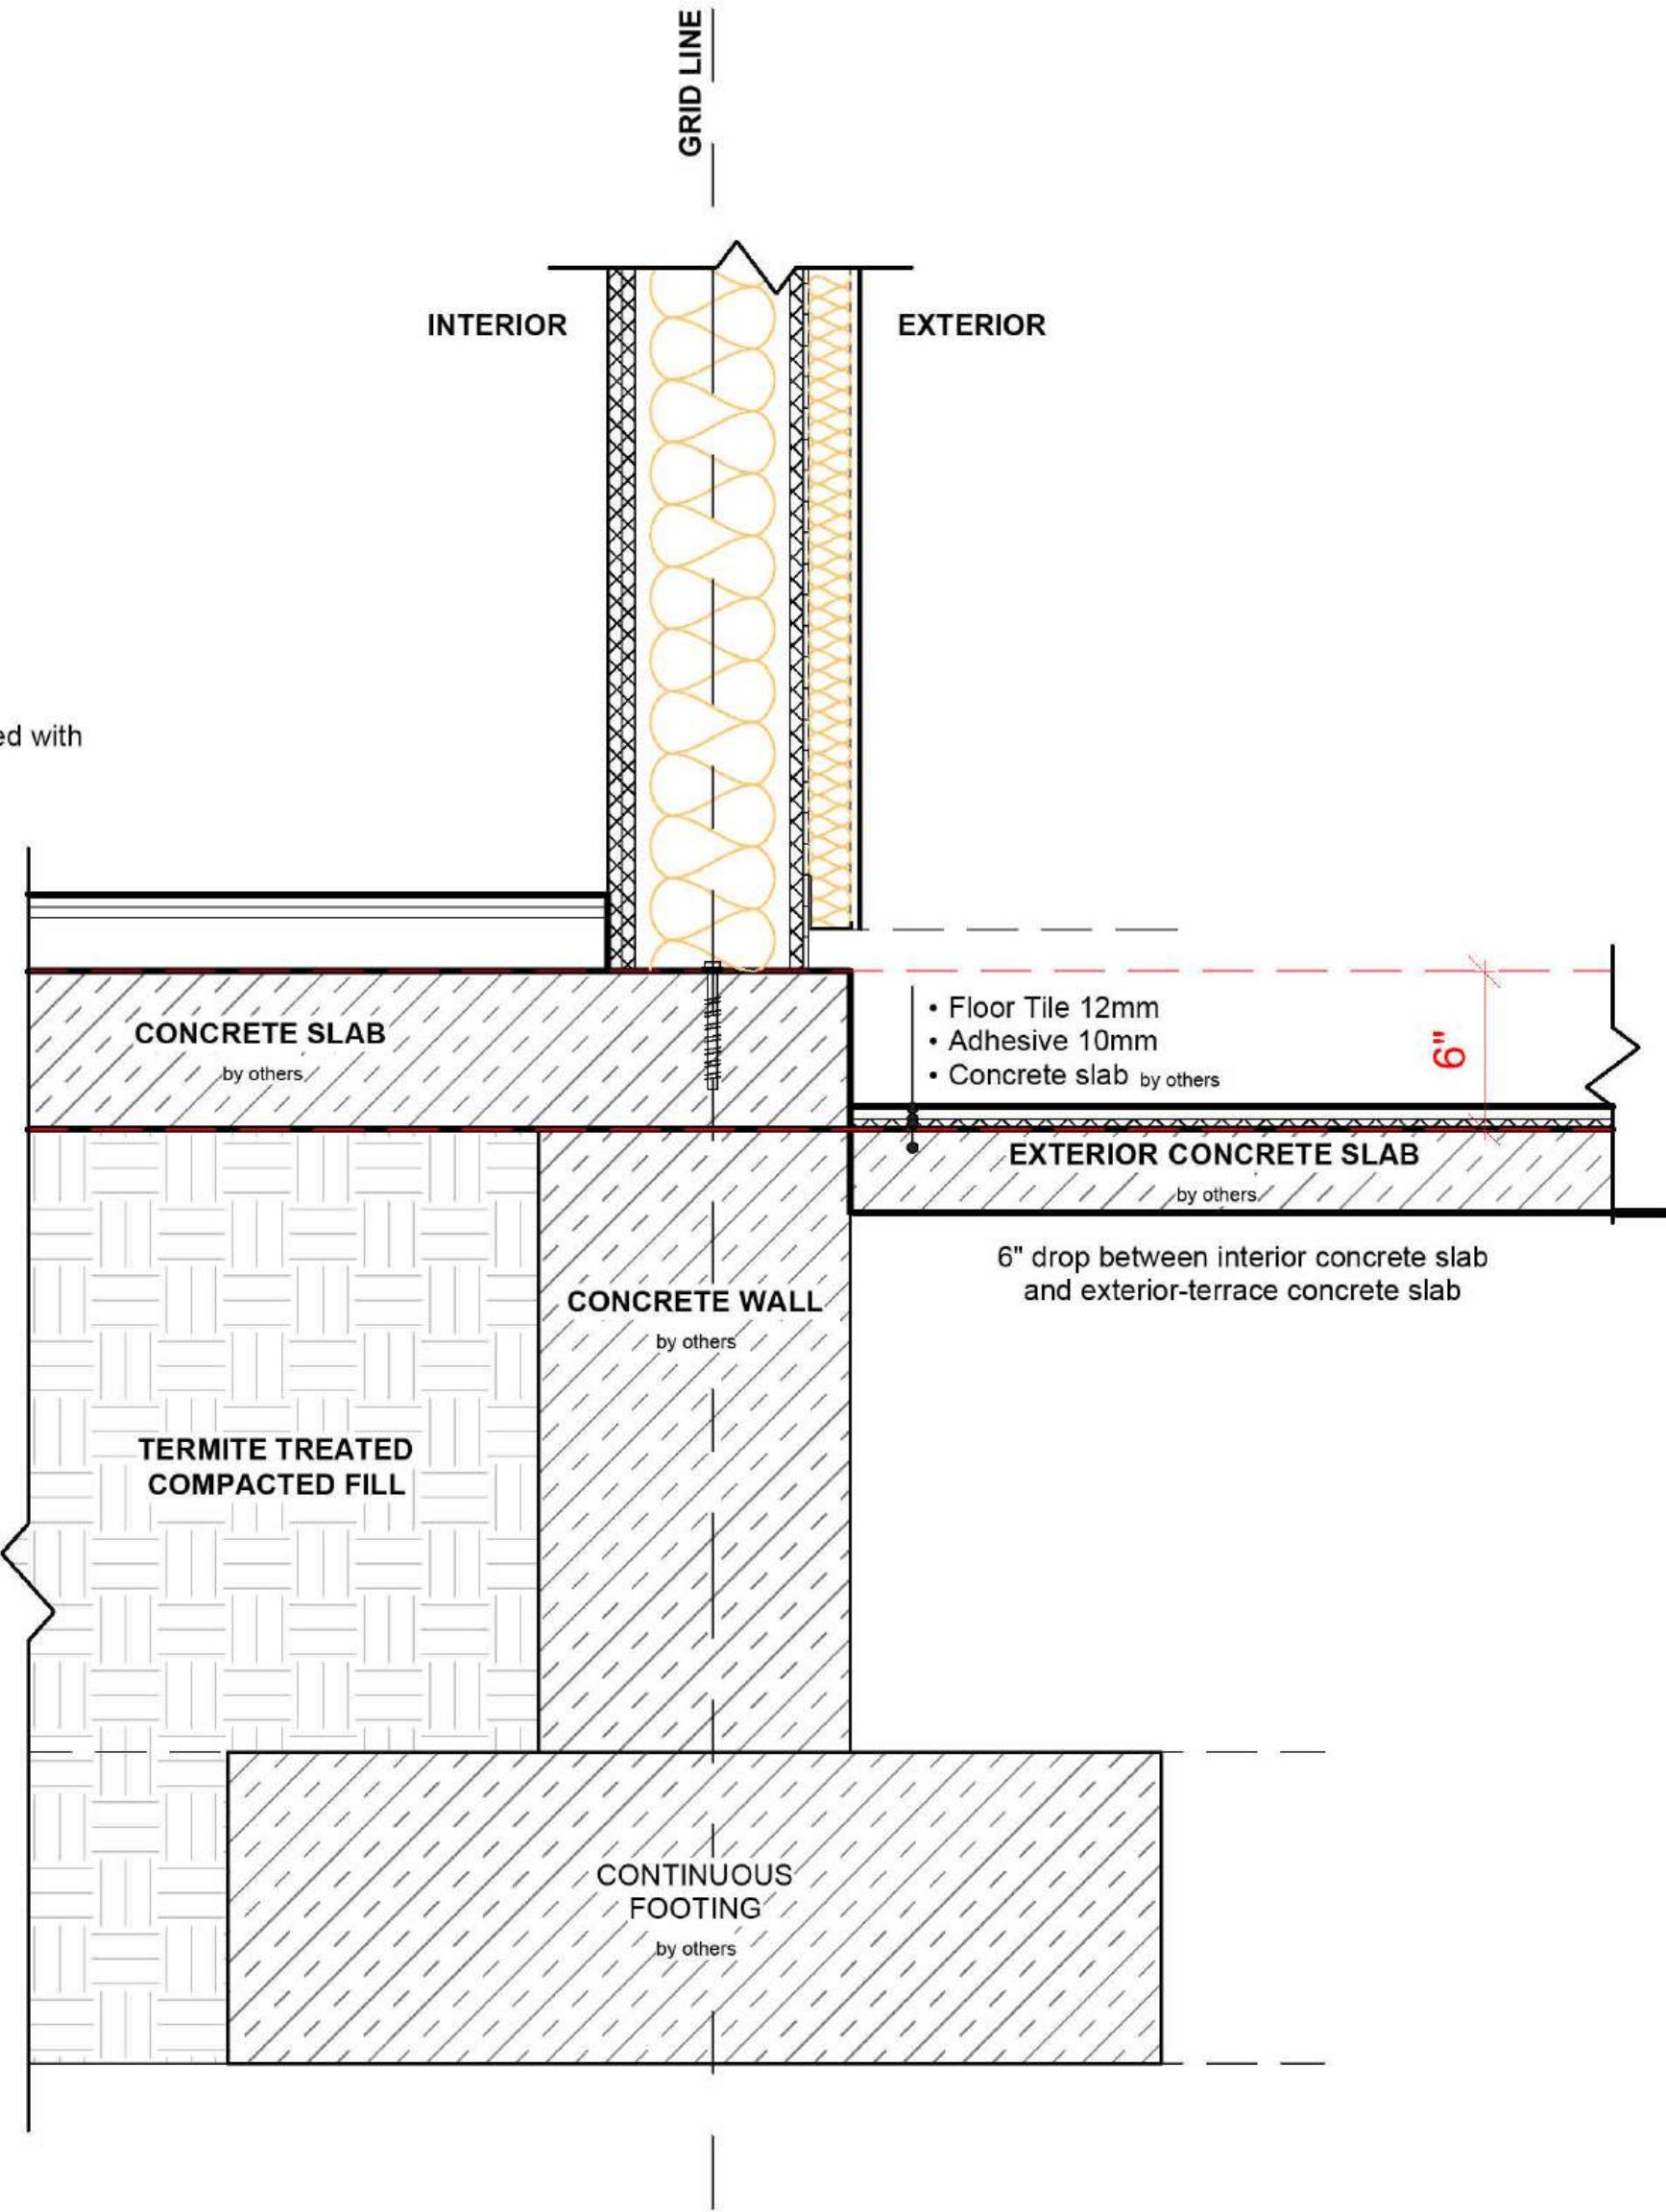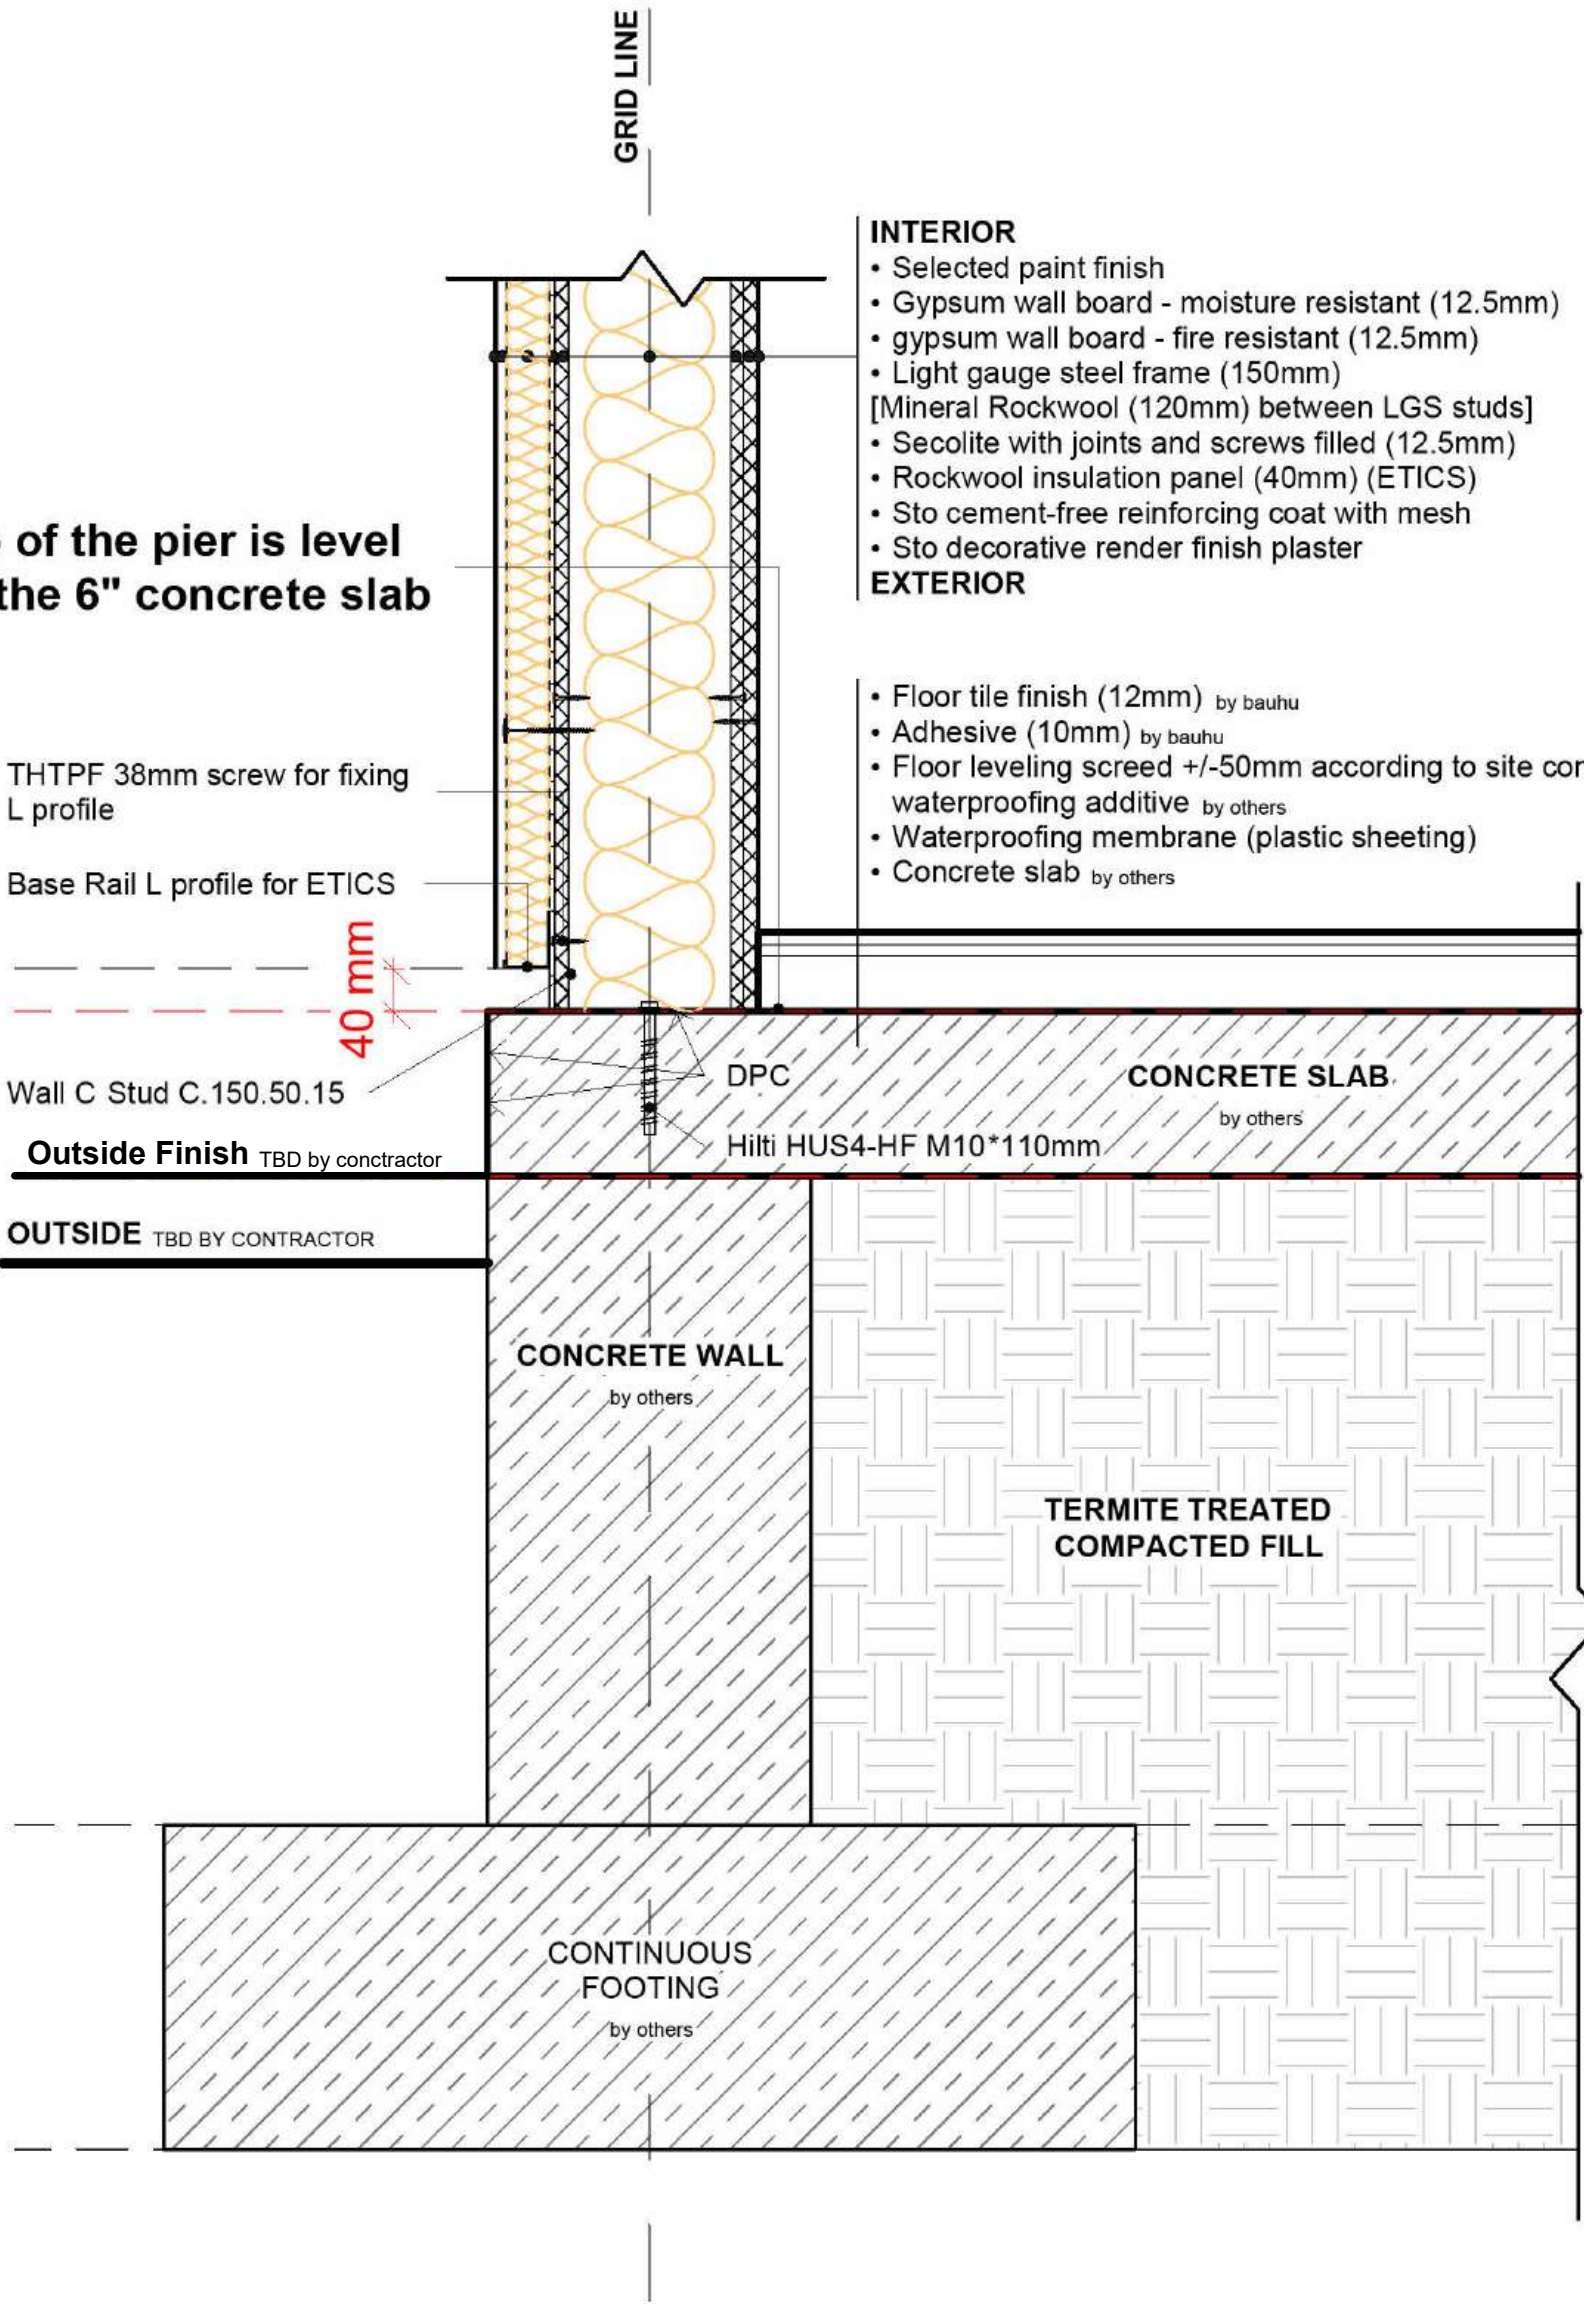

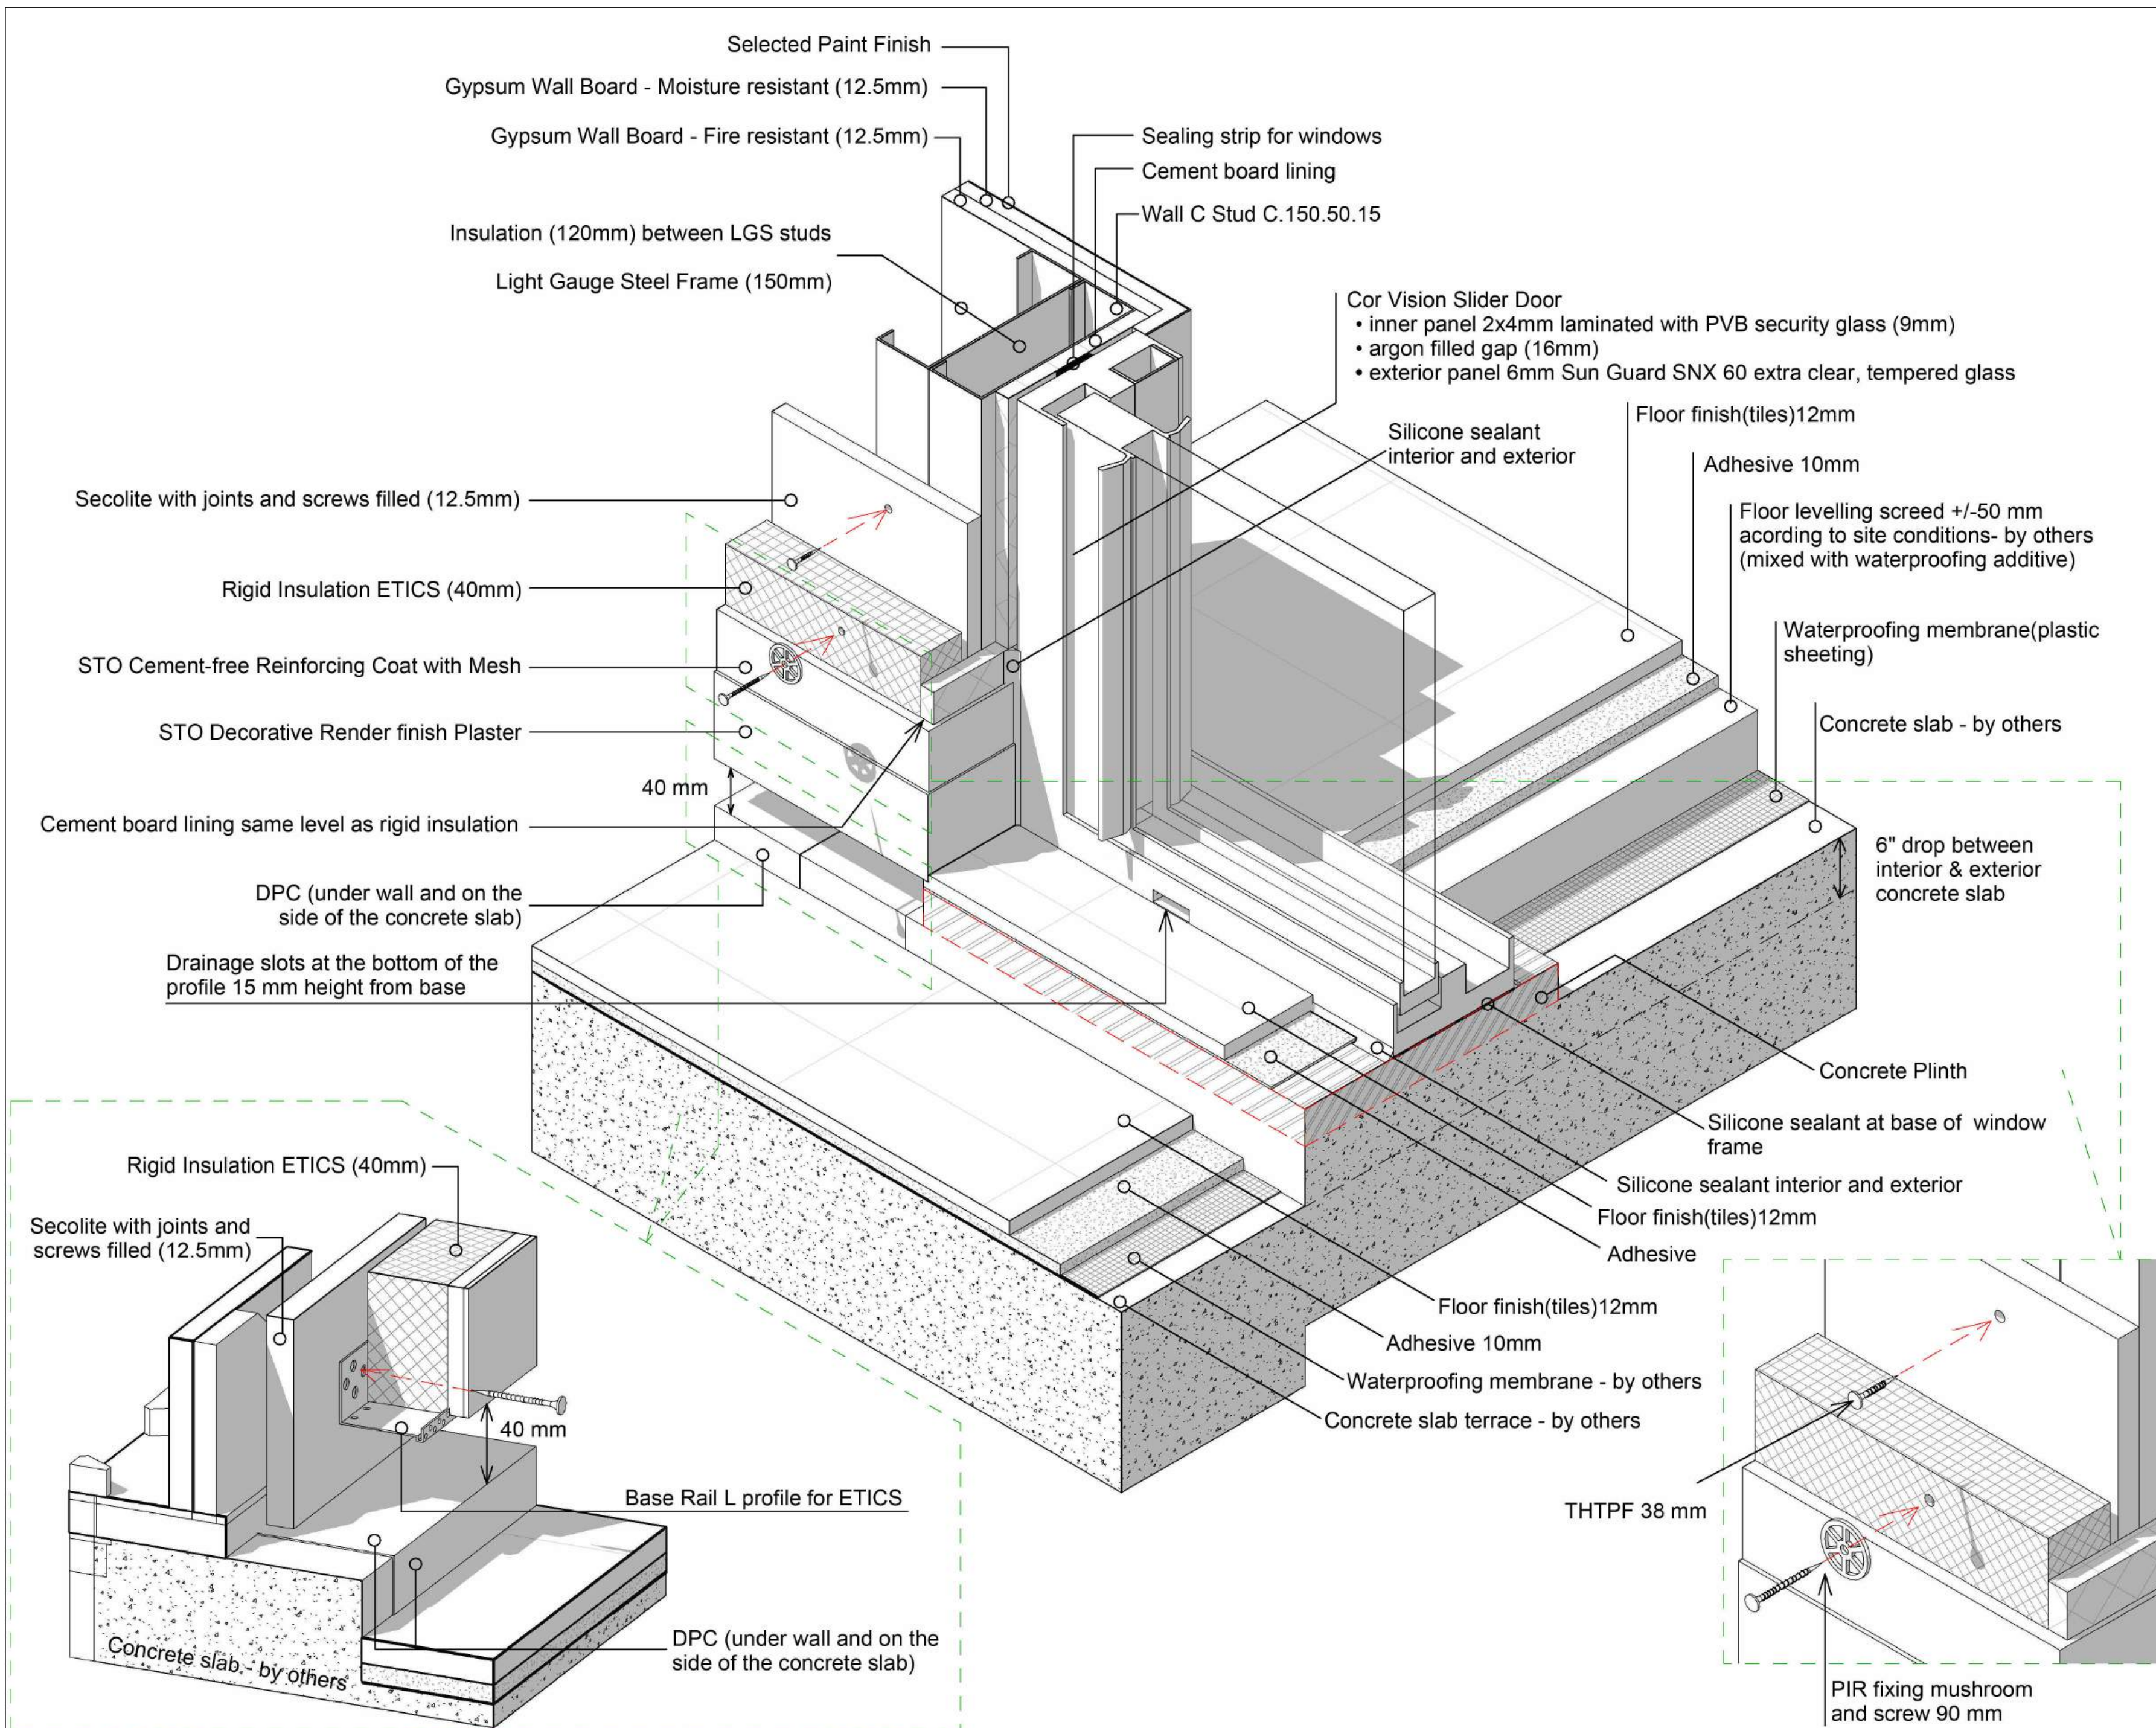

Note: When fixing adjacent boards ensure that there is a 3mm gap between boards. Screws should be at least 15mm in from the edge of the Cement Board and spaced at maximum 250 mm centres for single layer application. Screws should not be over tightened and sit flush with the surface.

1. THESE DRAWINGS MUST BE CHECKED BY THE CUSTOMER OR CONTRACTOR PRIOR TO APPROVAL. ANY ERRORS OR OMISSIONS MUST BE REPORTED IN WRITING TO BAUHU PRIOR TO COMMENCEMENT OF CONSTRUCTION.
2. ARCHITECTURAL DRAWINGS SHOULD BE READ IN CONJUNCTION WITH STRUCTURAL DETAILING AND FABRICATION GENERAL ASSEMBLY DRAWINGS.
3. FOR CONSTRUCTION PURPOSES, USE ONLY THE LATEST APPROVED DRAWINGS LABELED 'ISSUED FOR CONSTRUCTION'.
4. DO NOT SCALE FROM THIS DRAWING.
5. THE COMPANY OPERATES USING METRIC DIMENSIONS AS THE PRINCIPAL DENOMINATION.
6. ALL CONCRETE WORKS ARE OUTSIDE OF THE SCOPE OF THE COMPANY. INFORMATION REGARDING SLAB DESIGN AND CONNECTIONS IN THESE DRAWINGS ARE INTENDED FOR GUIDANCE ONLY. FOUNDATION AND SLAB WORKS SHOULD BE DESIGNED AND APPROVED BY A LOCAL STRUCTURAL ENGINEER.
7. THE COMPANY RETAINS FULL TITLE AND OWNERSHIP OF THESE PLANS AND DESIGNS. ANY UNAUTHORISED USE, REPRODUCTION, OR DISTRIBUTION OF THESE PLANS, WHETHER IN WHOLE OR PART, IS EXPRESSLY PROHIBITED WITHOUT PRIOR WRITTEN CONSENT.
8. THE HYBRID STEEL FRAME CONSTRUCTION SYSTEM AND METHODOLOGY (PATENT PENDING) DESCRIBED IN THESE PLANS HAS BEEN DEVELOPED BY THE COMPANY AND IS SUBJECT TO A PROVISIONAL PATENT APPLICATION & ASSIGNMENT - US APPLICATION NO. 63/722,841

[illegible]

ISSUED FOR:

Issued for information

Issued for client approval

Issued for fabrication

Issued for construction

Coconut Villa 3 Bed

DRAWING TITLE:

3D Detail

DRAWN BY:

Y.A.Clark

SCALE:

DRAWING NO:

C106

DATE:

16/02/2026

HRS CONNECTIONS

1. THESE DRAWINGS MUST BE CHECKED BY THE CUSTOMER OR CONTRACTOR PRIOR TO APPROVAL. ANY ERRORS OR OMISSIONS MUST BE REPORTED IN WRITING TO BAUHU PRIOR TO COMMENCEMENT OF CONSTRUCTION.
2. ARCHITECTURAL DRAWINGS SHOULD BE READ IN CONJUNCTION WITH STRUCTURAL DETAILING AND FABRICATION GENERAL ASSEMBLY DRAWINGS.
3. FOR CONSTRUCTION PURPOSES, USE ONLY THE LATEST APPROVED DRAWINGS LABELED 'ISSUED FOR CONSTRUCTION'.
4. DO NOT SCALE FROM THIS DRAWING.
5. THE COMPANY OPERATES USING METRIC DIMENSIONS AS THE PRINCIPAL DENOMINATION.
6. ALL CONCRETE WORKS ARE OUTSIDE OF THE SCOPE OF THE COMPANY. INFORMATION REGARDING SLAB DESIGN AND CONNECTIONS IN THESE DRAWINGS ARE INTENDED FOR GUIDANCE ONLY. FOUNDATION AND SLAB WORKS SHOULD BE DESIGNED AND APPROVED BY A LOCAL STRUCTURAL ENGINEER.
7. THE COMPANY RETAINS FULL TITLE AND OWNERSHIP OF THESE PLANS AND DESIGNS. ANY UNAUTHORISED USE, REPRODUCTION, OR DISTRIBUTION OF THESE PLANS, WHETHER IN WHOLE OR PART, IS EXPRESSLY PROHIBITED WITHOUT PRIOR WRITTEN CONSENT.
8. THE HYBRID STEEL FRAME CONSTRUCTION SYSTEM AND METHODOLOGY (PATENT PENDING) DESCRIBED IN THESE PLANS HAS BEEN DEVELOPED BY THE COMPANY AND IS SUBJECT TO A PROVISIONAL PATENT APPLICATION & ASSIGNMENT - US APPLICATION NO. 63/722,841

No.	Revision	Date

ISSUED FOR:

Issued for information


Issued for client approval

Issued for fabrication


Issued for construction

Coconut Villa
3 Bed


DRAWING TITLE:	HRS Connections
DRAWN BY:	Y.A.Clark
SCALE:	
DRAWING NO:	C107
DATE:	16/02/2026

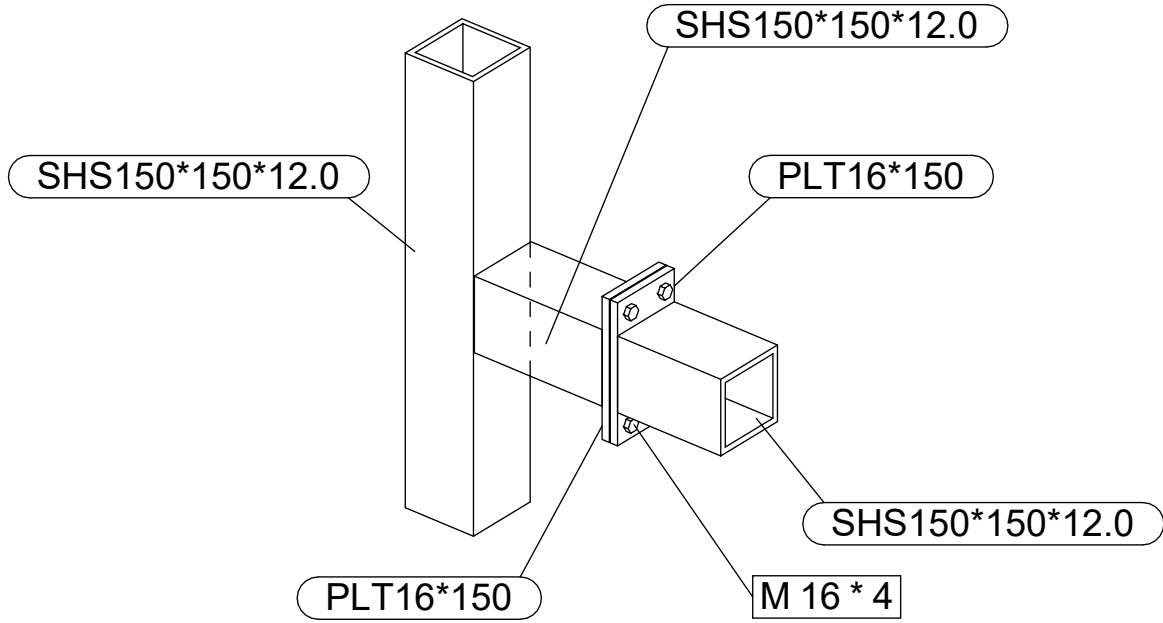


Typical Column Beam Stub Connection

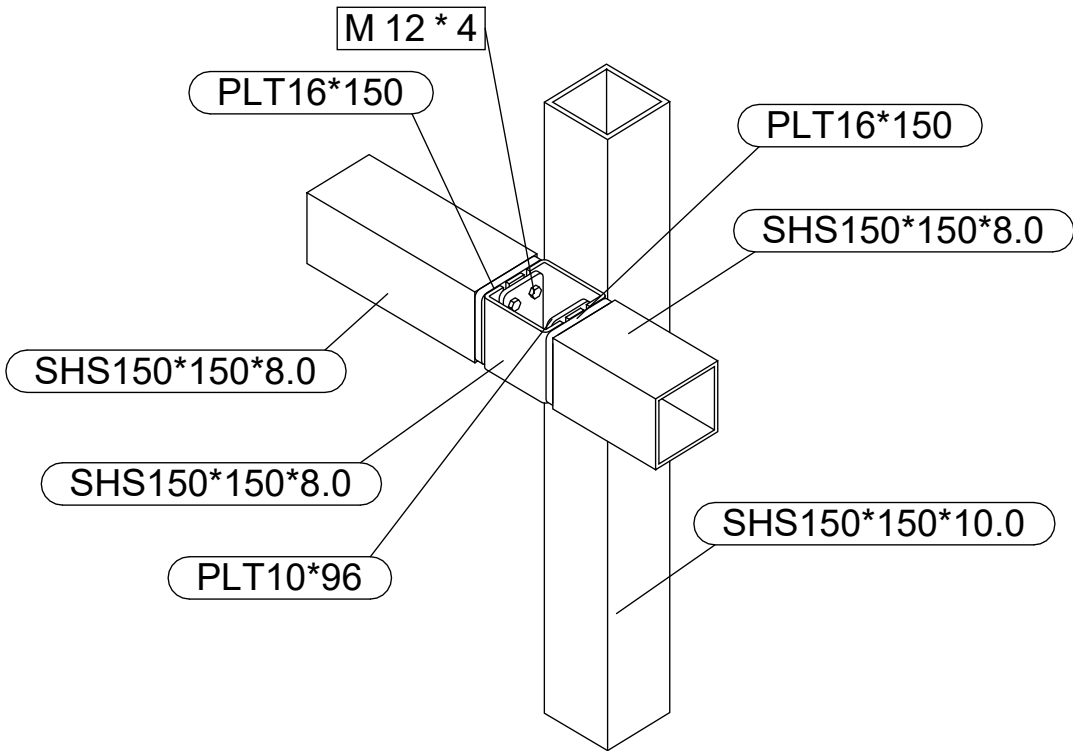


Typical Beam Offset Connection

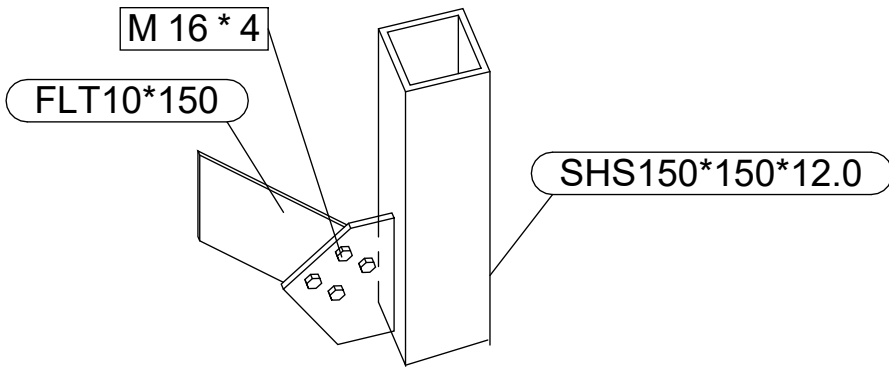


Typical Bracing Connection

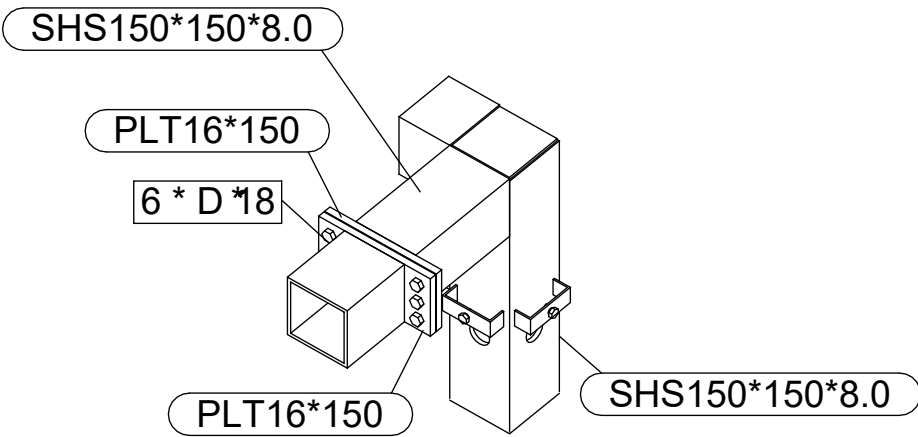


Typical Column to Beam Splice Connection

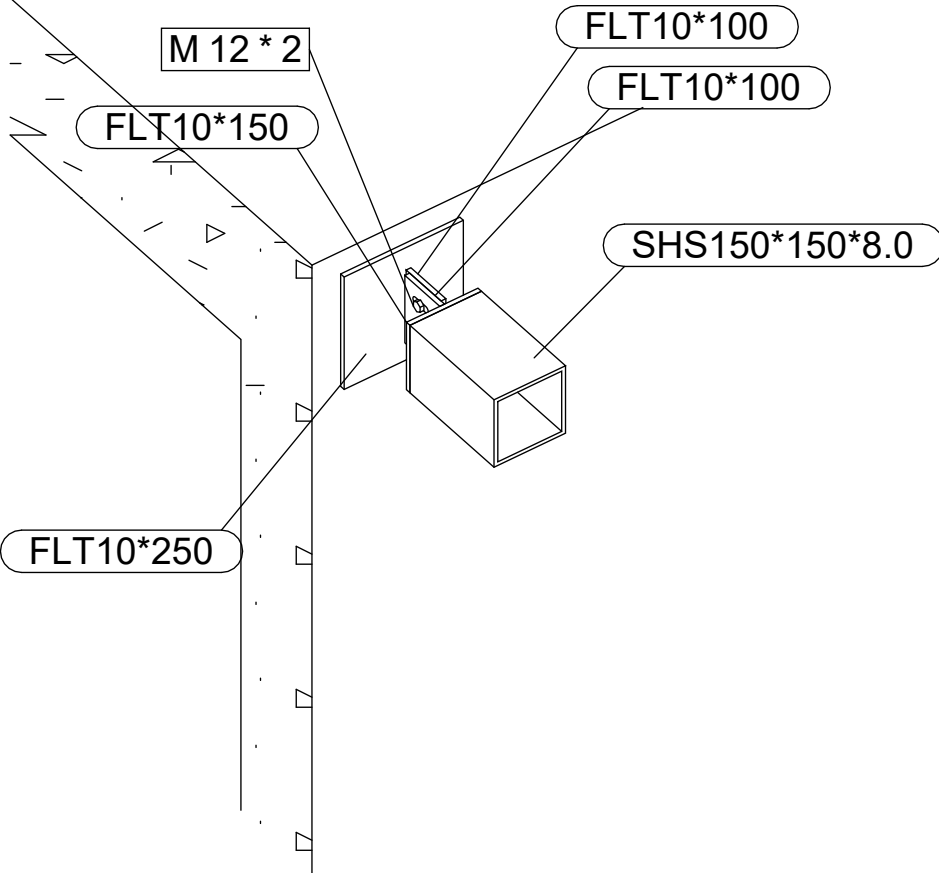


Typical Beam to Concrete Connection

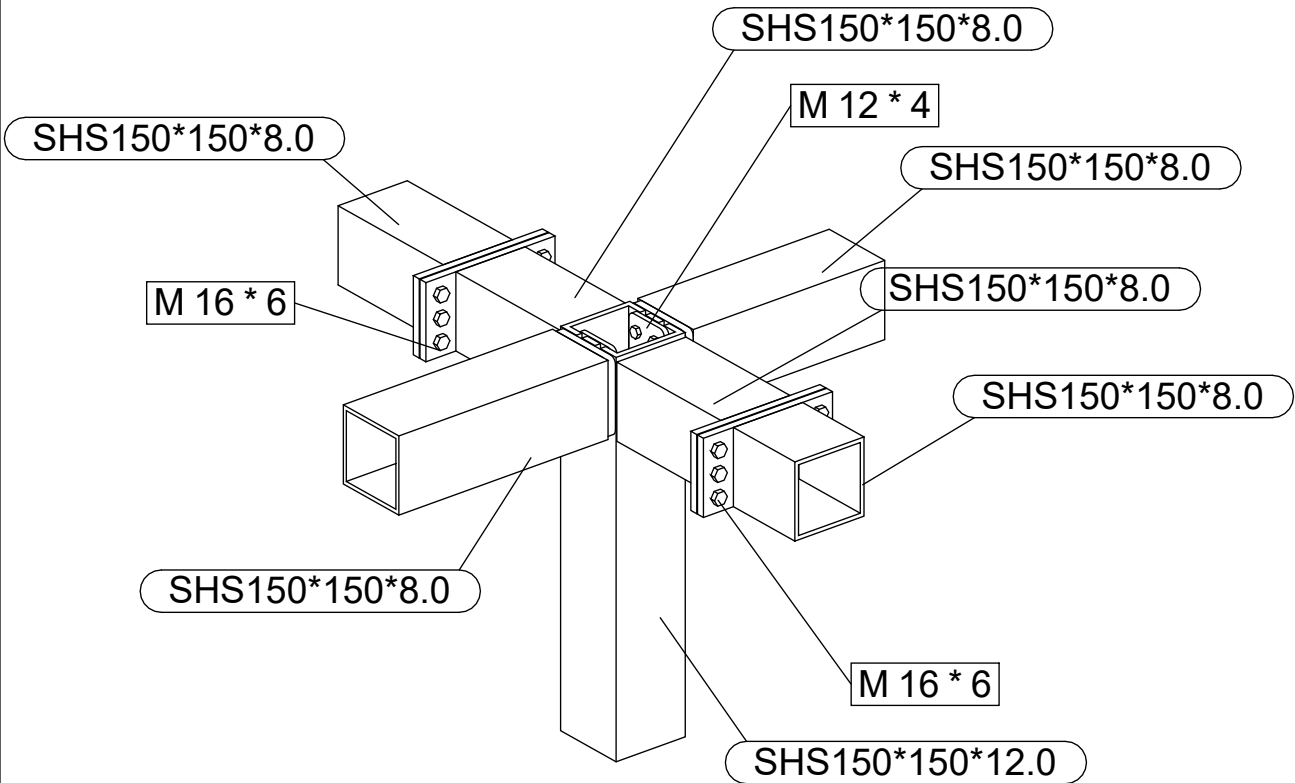

Typical Roof Column Beam Connection

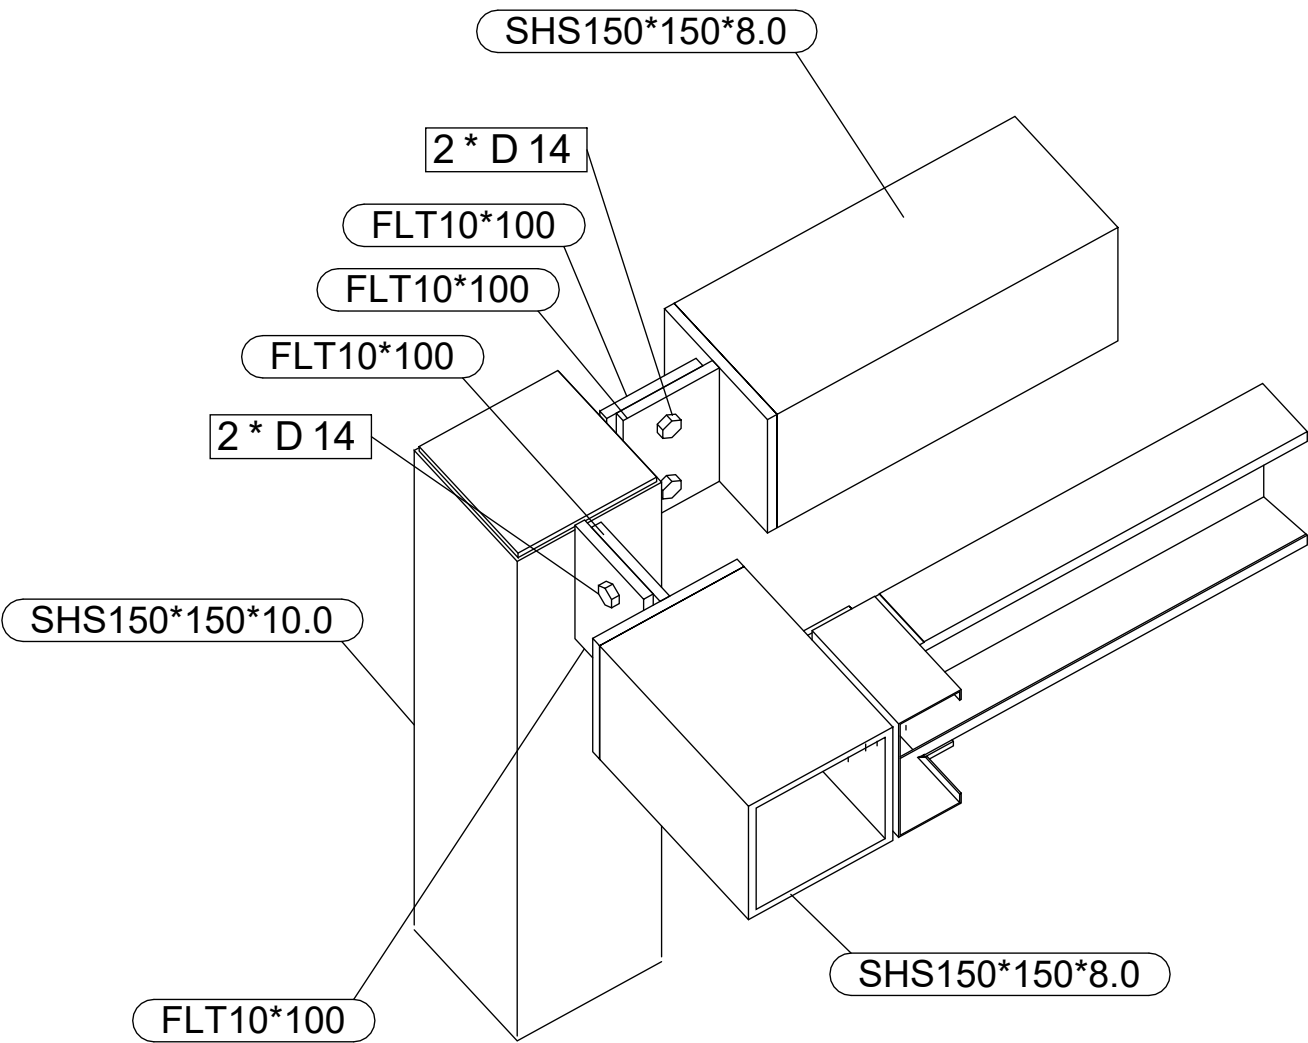


Typical Column to Beam Fine Plate Connection

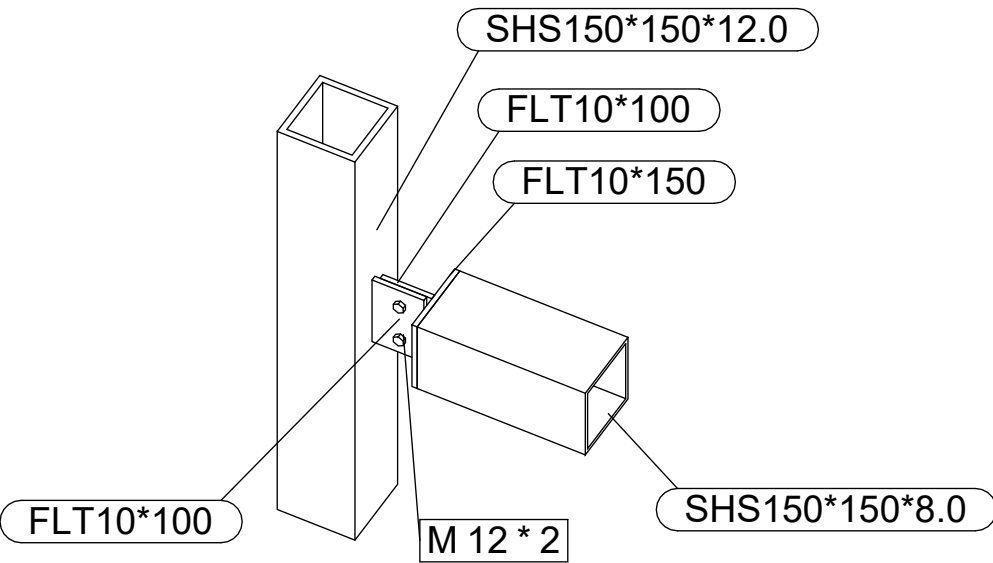


Typical Column Beam Fine Plate Connection


LGS CONNECTIONS

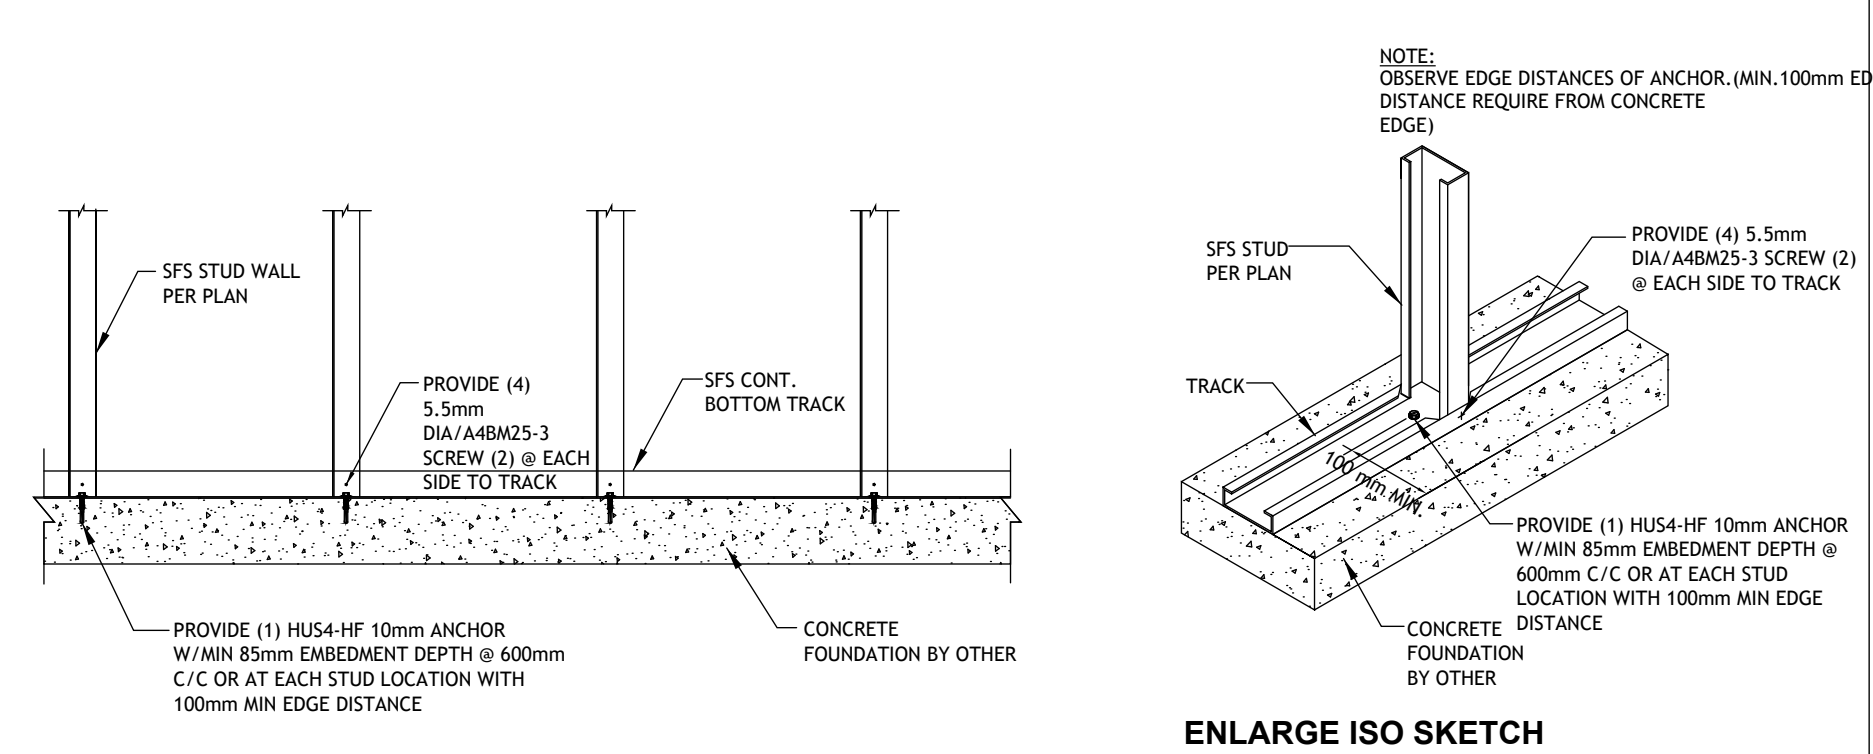


Typical Detail : SFS Bottom Track to Concrete Connection (External Wall)

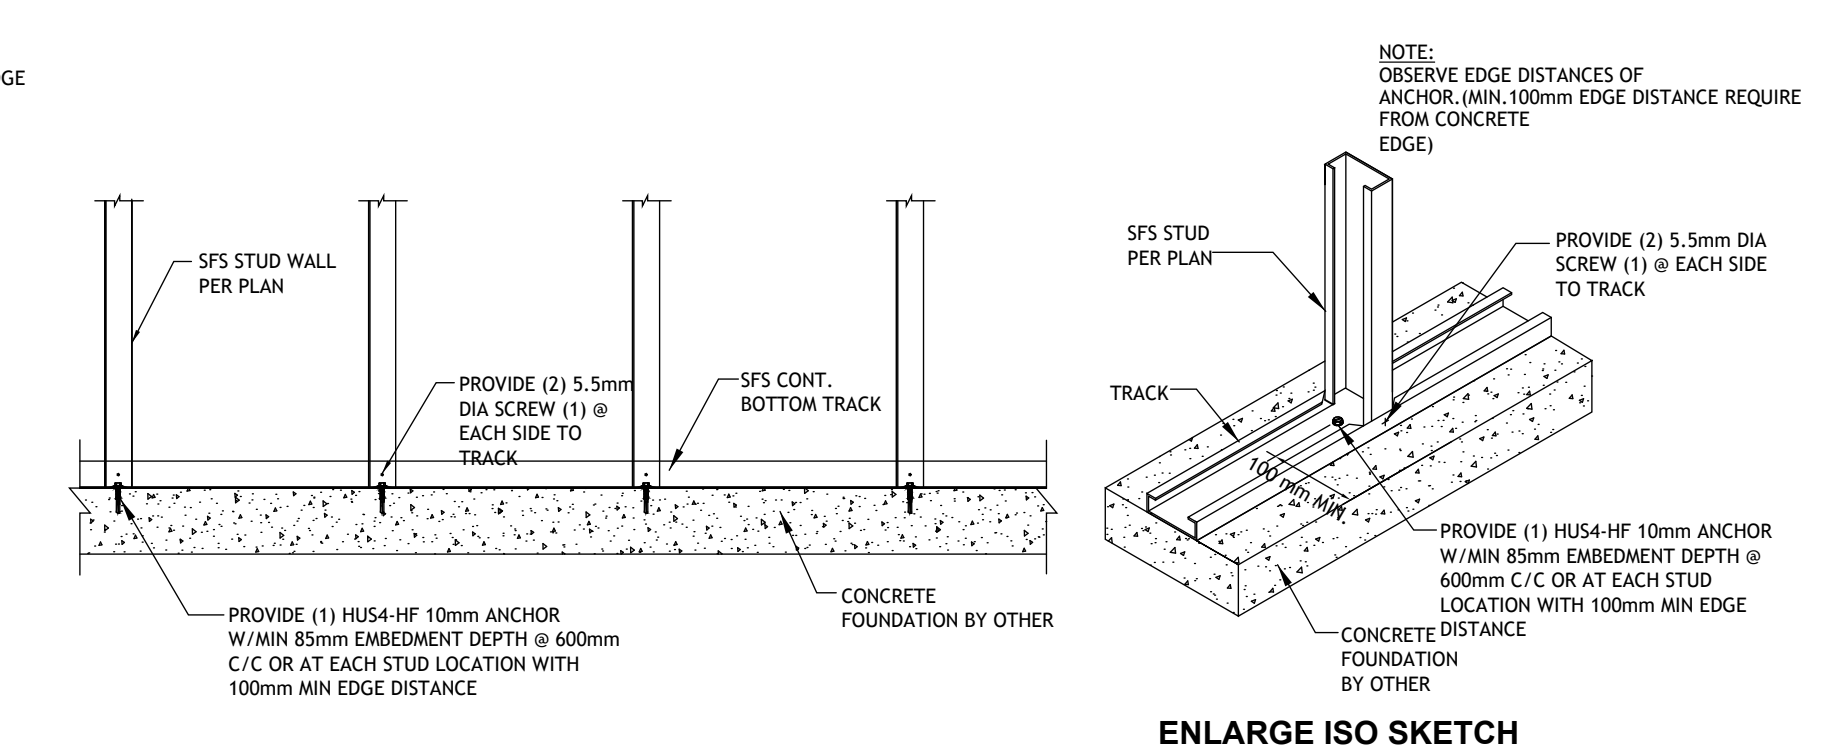


Typical Detail : Bottom Track to Concrete Connection (Internal Wall)

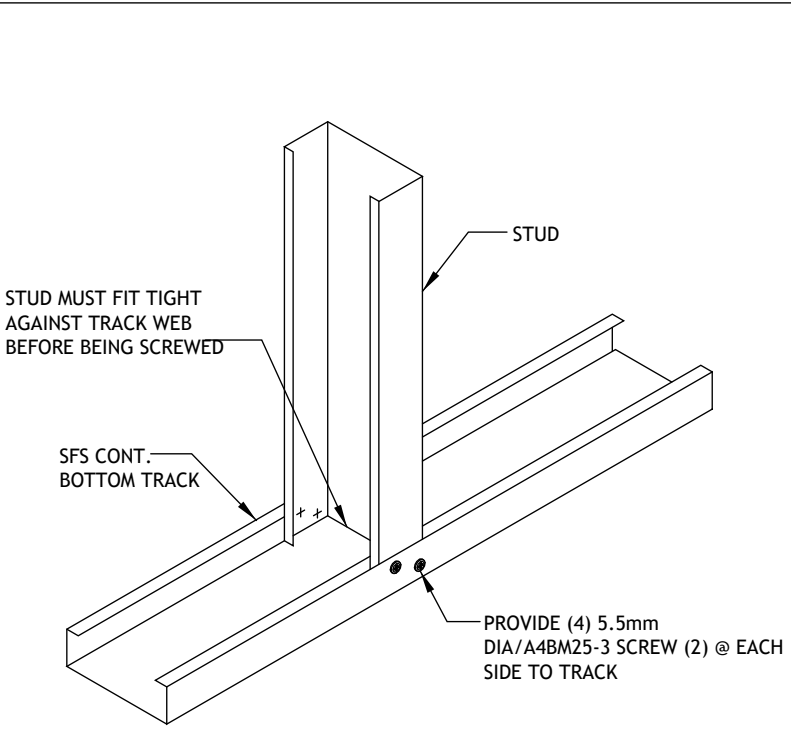


Stud to Bottom Track Connection (External Wall)

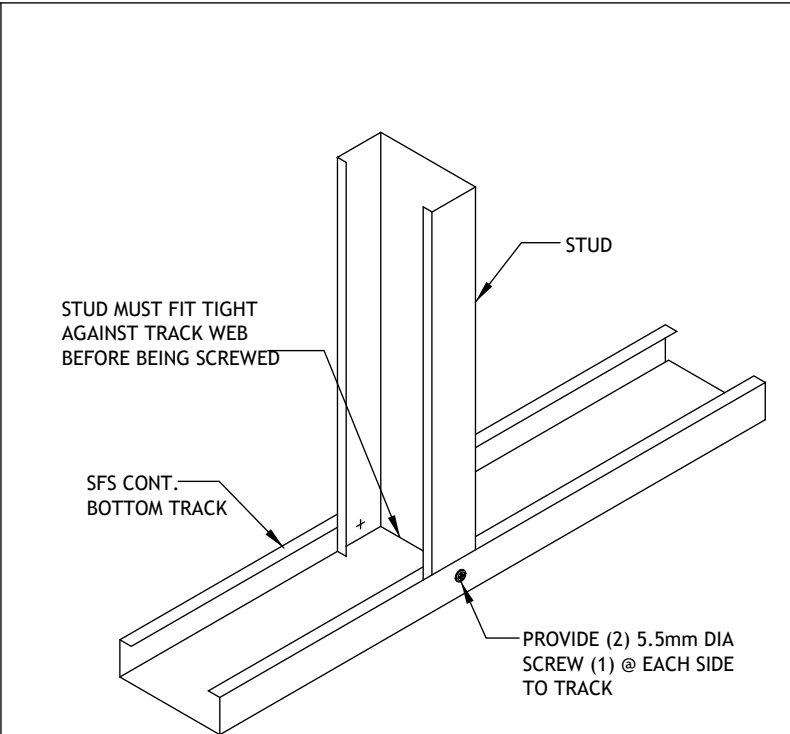


Stud to Bottom Track Connection (Internal Wall)

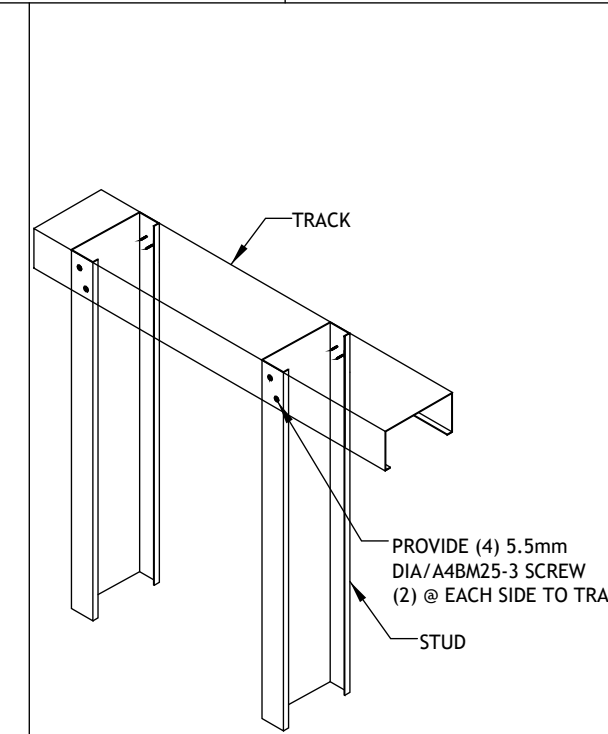


Stud to Top Track Connection (External Wall)

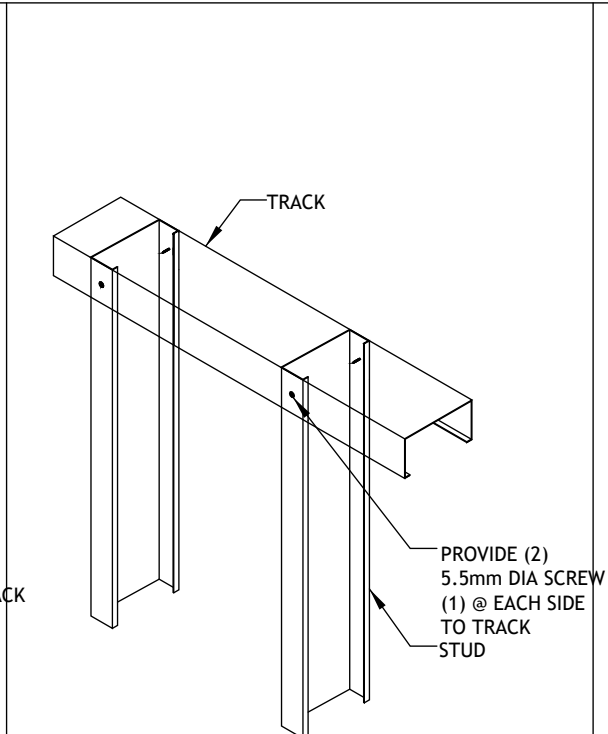


Stud to Top Track Connection (Internal Wall)

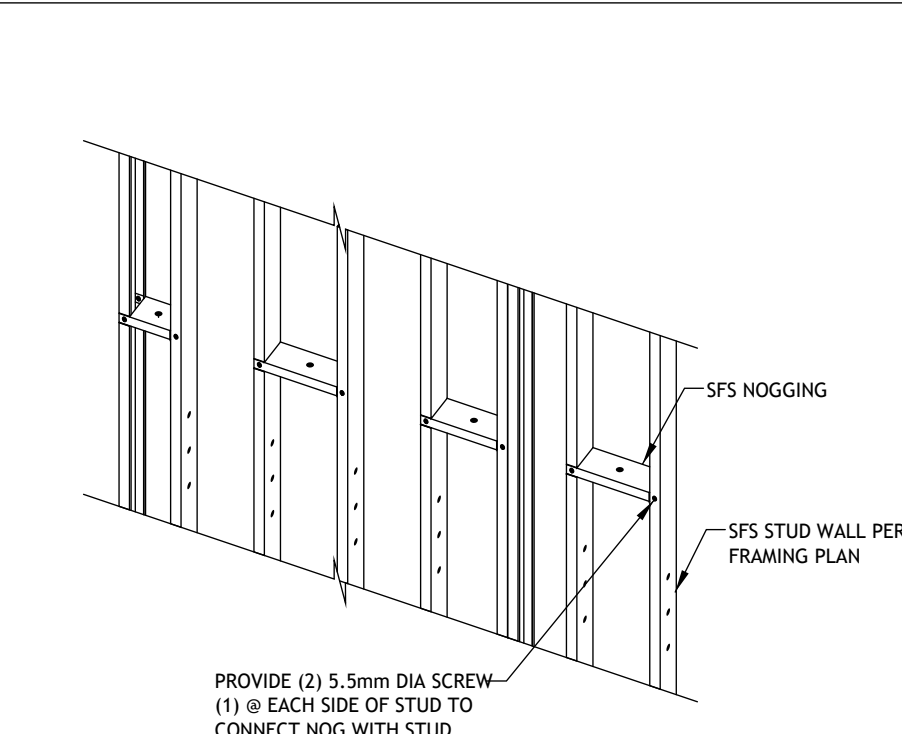


Hit and Miss Nogging to Stud Connection Detail

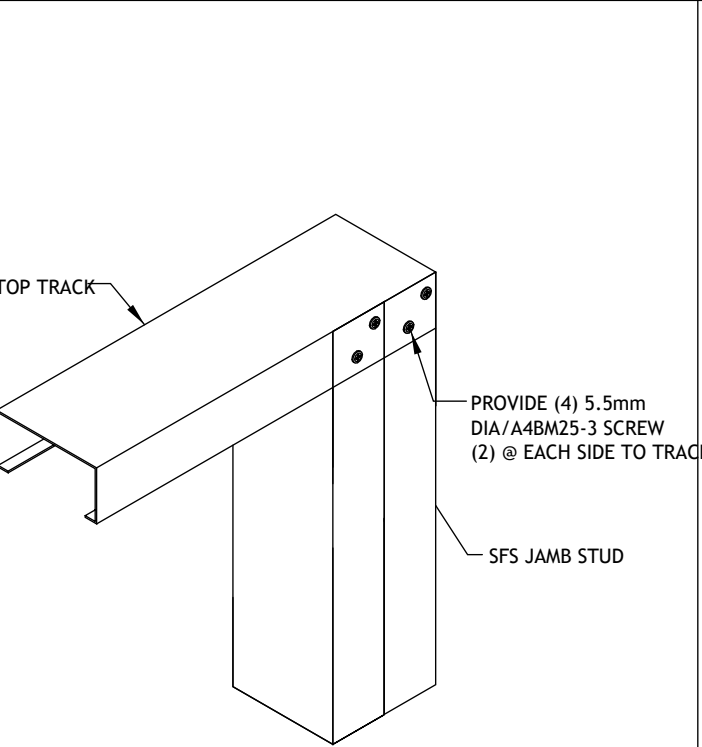


Box Jamb to Top Track Connection

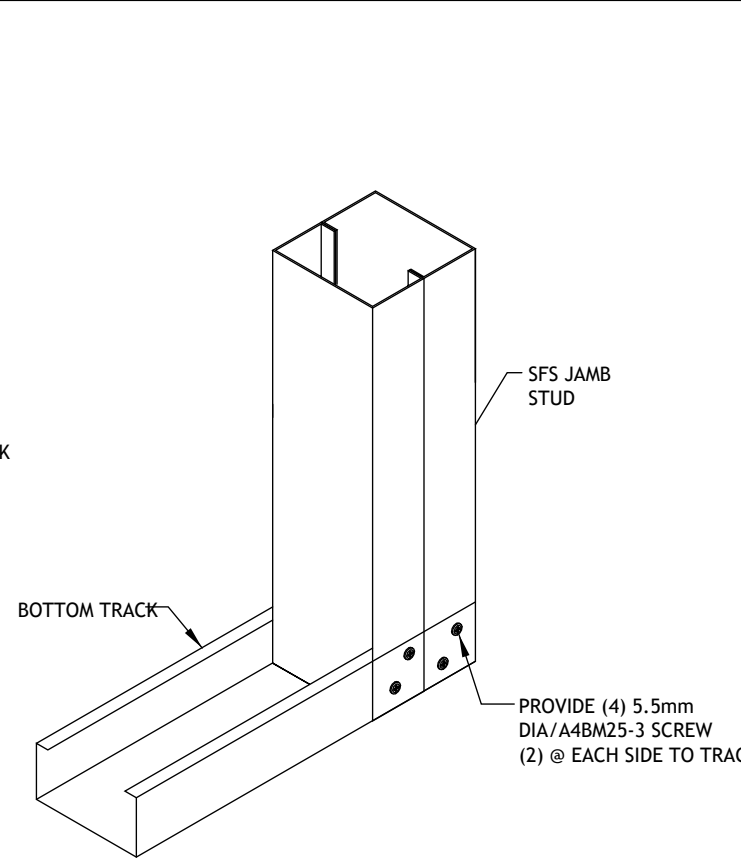


Box Jamb to Bottom Track Connection

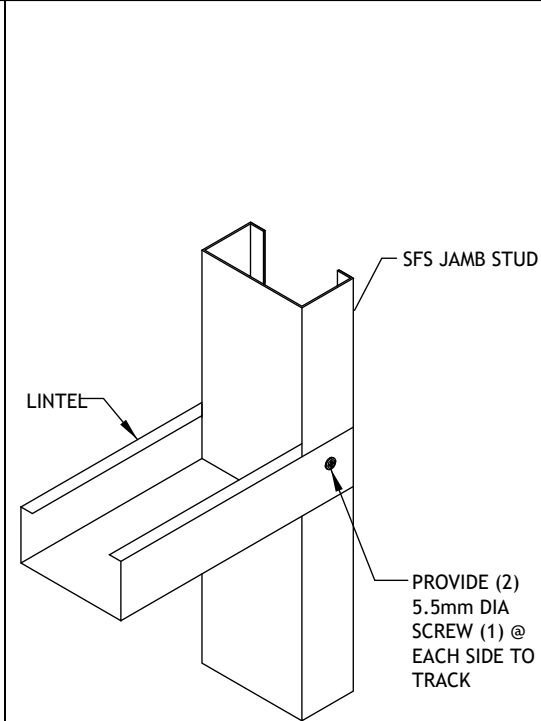


Lintel to Jamb Stud Connection

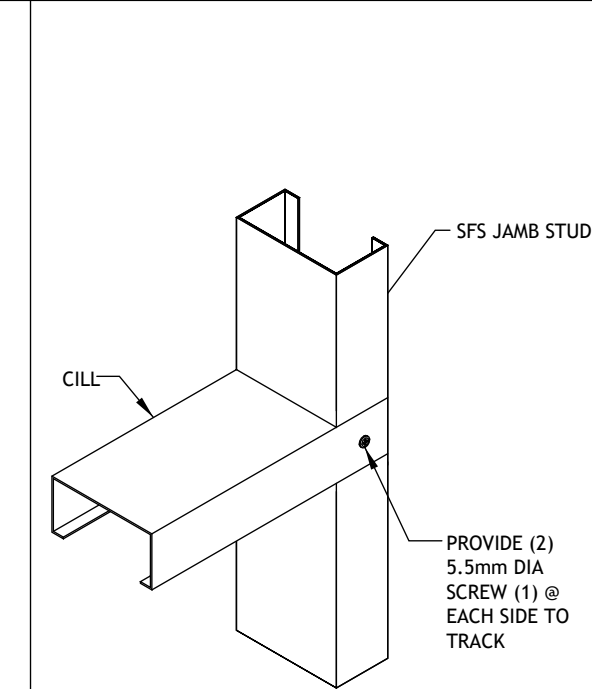

Typ. Cill to Jamb Stud Connection

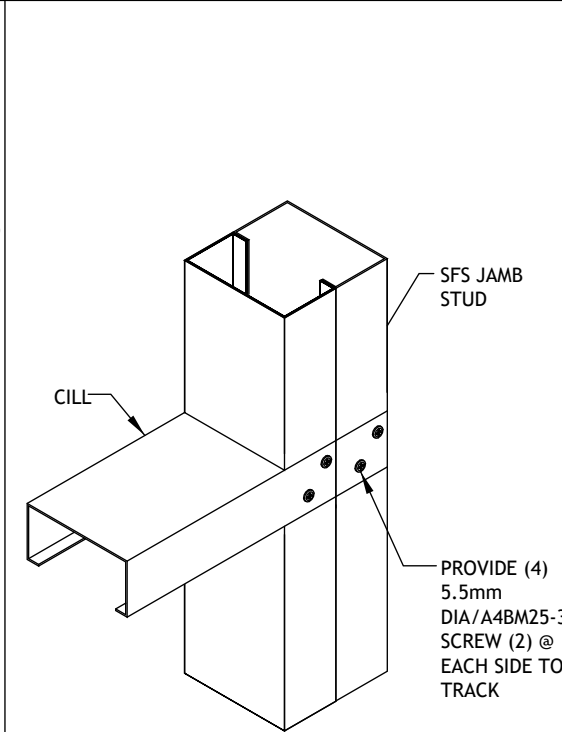

Typ. Cill to Jamb Stud Connection

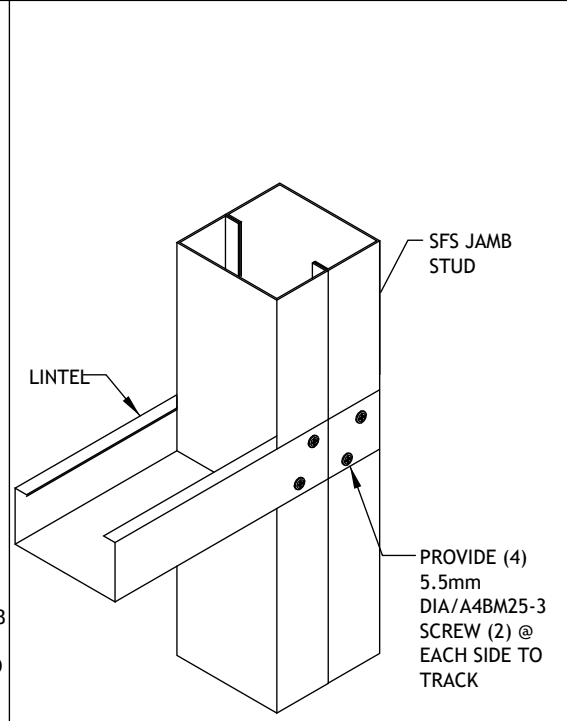

Lintel to Jamb Stud Connection

1. THESE DRAWINGS MUST BE CHECKED BY THE CUSTOMER OR CONTRACTOR PRIOR TO APPROVAL. ANY ERRORS OR OMISSIONS MUST BE REPORTED IN WRITING TO BAUHU PRIOR TO COMMENCEMENT OF CONSTRUCTION.
2. ARCHITECTURAL DRAWINGS SHOULD BE READ IN CONJUNCTION WITH STRUCTURAL DETAILING AND FABRICATION GENERAL ASSEMBLY DRAWINGS.
3. FOR CONSTRUCTION PURPOSES, USE ONLY THE LATEST APPROVED DRAWINGS LABELED 'ISSUED FOR CONSTRUCTION'.
4. DO NOT SCALE FROM THIS DRAWING.
5. THE COMPANY OPERATES USING METRIC DIMENSIONS AS THE PRINCIPAL DENOMINATION.
6. ALL CONCRETE WORKS ARE OUTSIDE OF THE SCOPE OF THE COMPANY. INFORMATION REGARDING SLAB DESIGN AND CONNECTIONS IN THESE DRAWINGS ARE INTENDED FOR GUIDENCE ONLY. FOUNDATION AND SLAB WORKS SHOULD BE DESIGNED AND APPROVED BY A LOCAL STRUCTURAL ENGINEER.
7. THE COMPANY RETAINS FULL TITLE AND OWNERSHIP OF THESE PLANS AND DESIGNS. ANY UNAUTHORISED USE, REPRODUCTION, OR DISTRIBUTION OF THESE PLANS, WHETHER IN WHOLE OR PART, IS EXPRESSLY PROHIBITED WITHOUT PRIOR WRITTEN CONSENT.
8. THE HYBRID STEEL FRAME CONSTRUCTION SYSTEM AND METHODOLOGY (PATENT PENDING) DESCRIBED IN THESE PLANS HAS BEEN DEVELOPED BY THE COMPANY AND IS SUBJECT TO A PROVISIONAL PATENT APPLICATION & ASSIGNMENT - US APPLICATION NO. 63/722,841

No.	Revision	Date

ISSUED FOR:

Issued for information

Issued for client approval

Issued for fabrication

Issued for construction

Coconut Villa
3 Bed

DRAWING TITLE:
LGS Connections

DRAWN BY:
Y.A.Clark


SCALE:

DRAWING NO:
C108


DATE:
16/02/2026

Typical Frame Connections 1


1. THESE DRAWINGS MUST BE CHECKED BY THE CUSTOMER OR CONTRACTOR PRIOR TO APPROVAL. ANY ERRORS OR OMISSIONS MUST BE REPORTED IN WRITING TO BAUHU PRIOR TO COMMENCEMENT OF CONSTRUCTION.
2. ARCHITECTURAL DRAWINGS SHOULD BE READ IN CONJUNCTION WITH STRUCTURAL DETAILING AND FABRICATION GENERAL ASSEMBLY DRAWINGS.
3. FOR CONSTRUCTION PURPOSES, USE ONLY THE LATEST APPROVED DRAWINGS LABELED 'ISSUED FOR CONSTRUCTION'.
4. DO NOT SCALE FROM THIS DRAWING.
5. THE COMPANY OPERATES USING METRIC DIMENSIONS AS THE PRINCIPAL DENOMINATION.
6. ALL CONCRETE WORKS ARE OUTSIDE OF THE SCOPE OF THE COMPANY. INFORMATION REGARDING SLAB DESIGN AND CONNECTIONS IN THESE DRAWINGS ARE INTENDED FOR GUIDENCE ONLY. FOUNDATION AND SLAB WORKS SHOULD BE DESIGNED AND APPROVED BY A LOCAL STRUCTURAL ENGINEER.
7. THE COMPANY RETAINS FULL TITLE AND OWNERSHIP OF THESE PLANS AND DESIGNS. ANY UNAUTHORISED USE, REPRODUCTION, OR DISTRIBUTION OF THESE PLANS, WHETHER IN WHOLE OR PART, IS EXPRESSLY PROHIBITED WITHOUT PRIOR WRITTEN CONSENT.
8. THE HYBRID STEEL FRAME CONSTRUCTION SYSTEM AND METHODOLOGY (PATENT PENDING) DESCRIBED IN THESE PLANS HAS BEEN DEVELOPED BY THE COMPANY AND IS SUBJECT TO A PROVISIONAL PATENT APPLICATION & ASSIGNMENT - US APPLICATION NO. 63/722,841

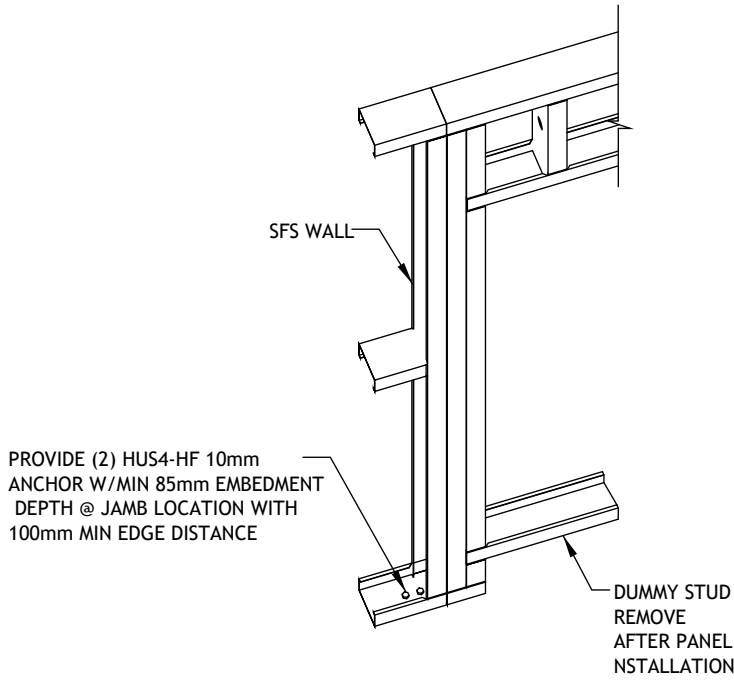


Typical Detail for Two Anchor at Jamb Location

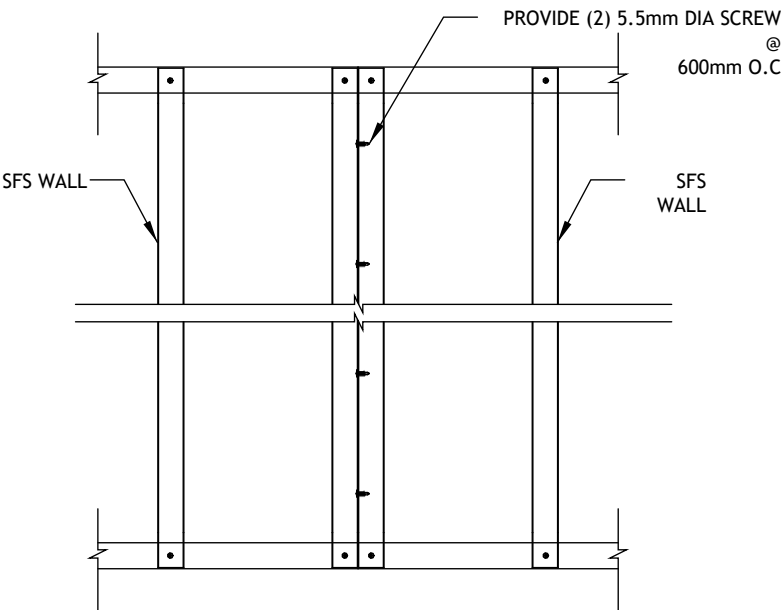


Typical Wall to SFS Wall Connection

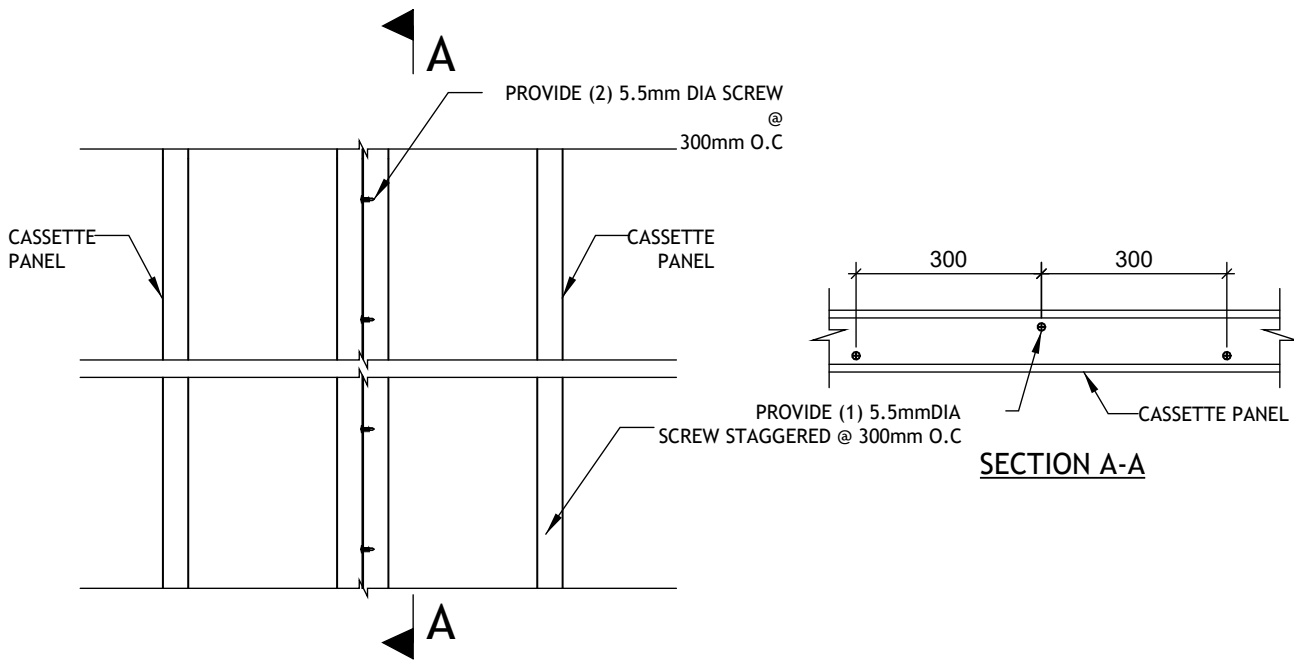


Cassette to Cassette Connection

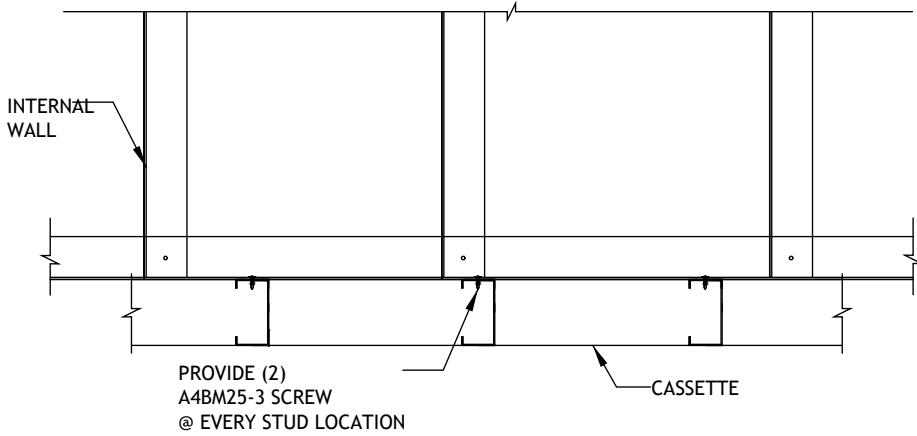


Internal Wall to Cassette Connection at Base

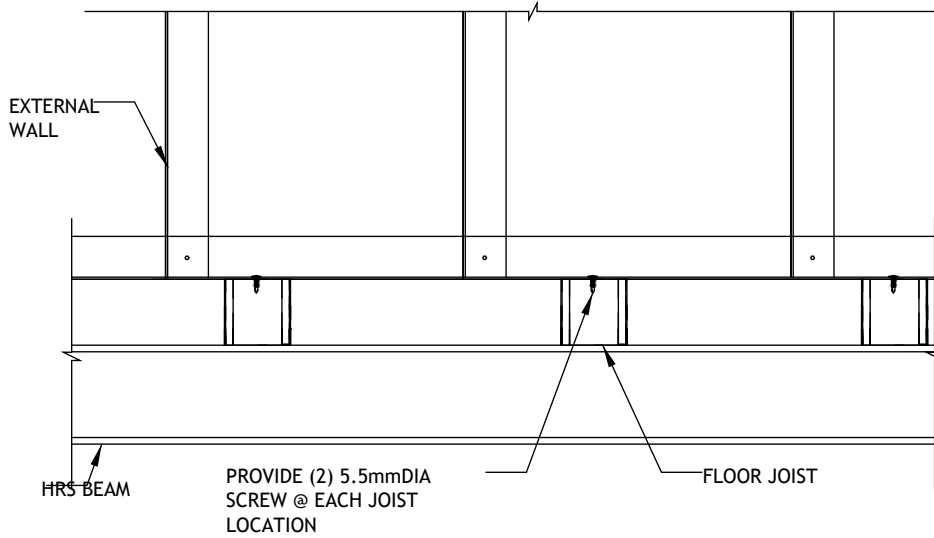


External Wall to Joist Connection at Base

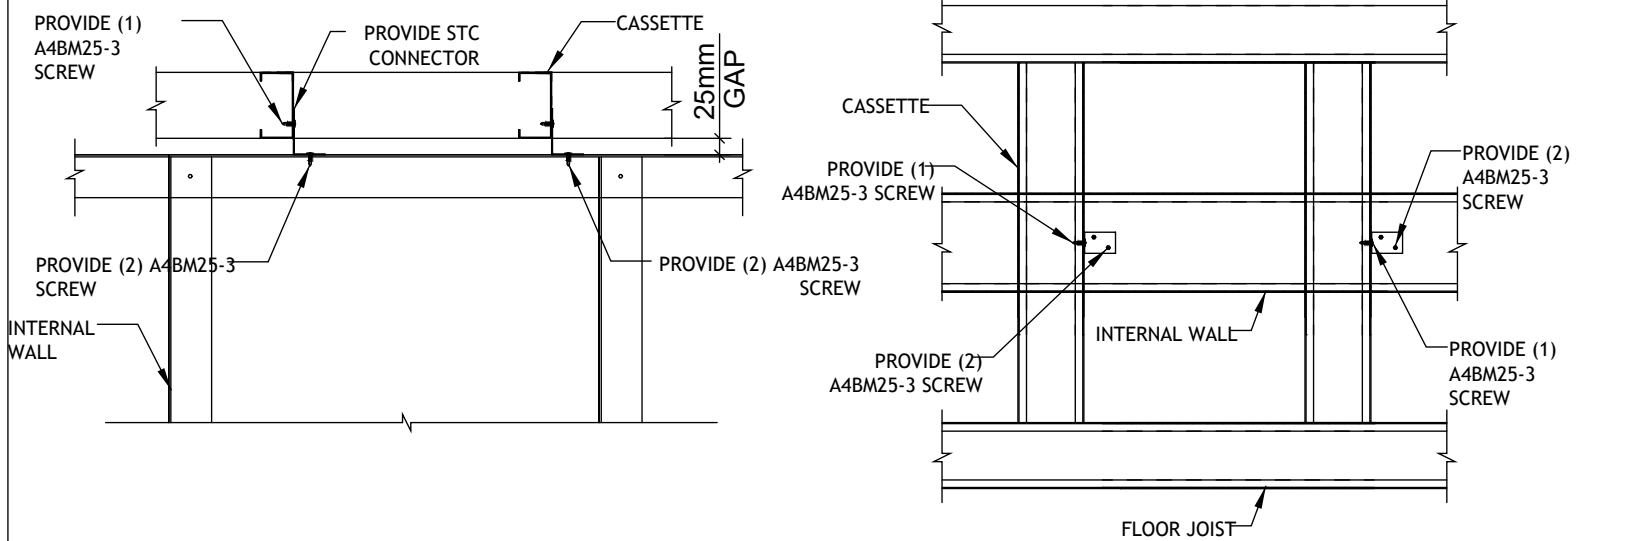


Typ. Internal Wall Connection at Roof Truss at Cassette Location

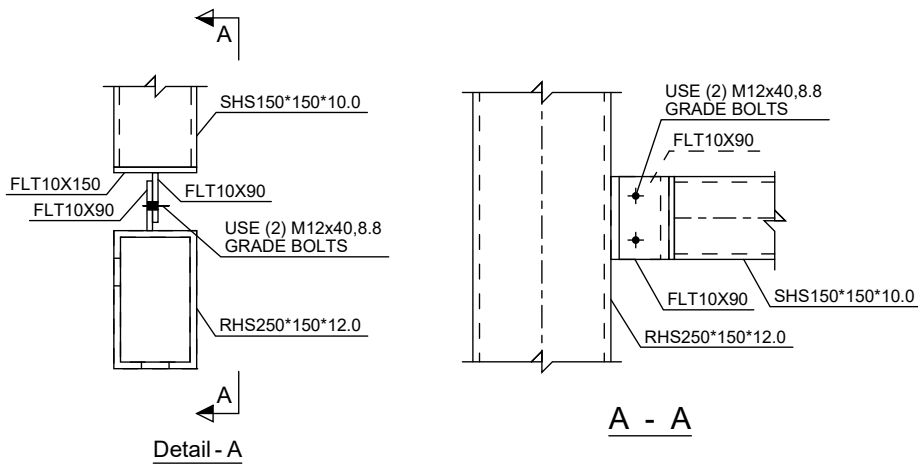

Typ. Fin Plate Connection Detail

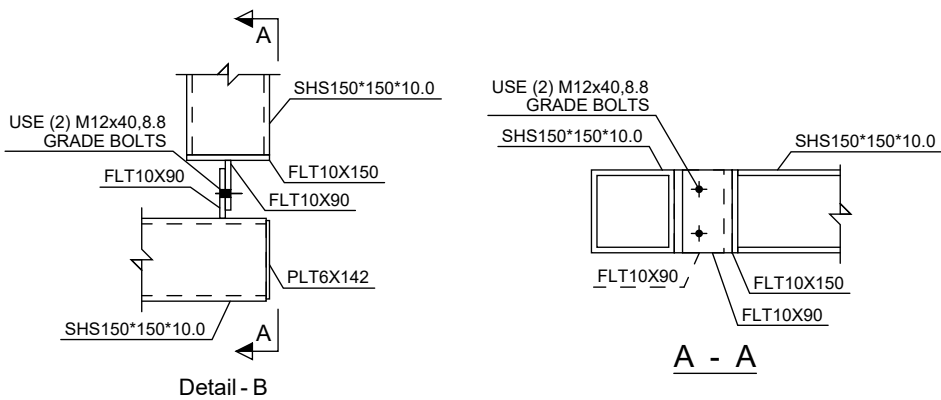

Typ. Fin Plate Connection Detail

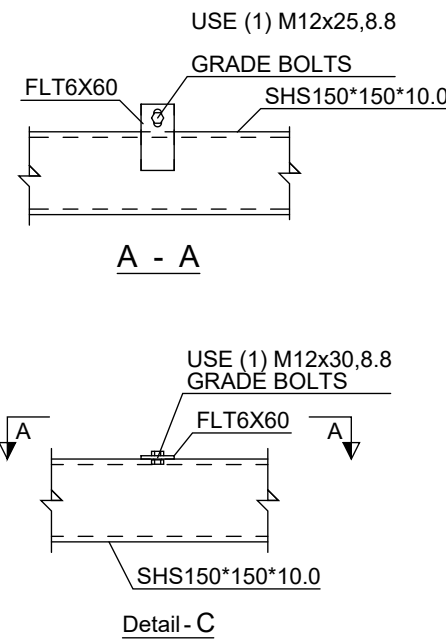

SFS Wall to HRS Beam Connection

No.	Revision	Date

ISSUED FOR:

Issued for information

Issued for client approval




Issued for fabrication

Issued for construction

Coconut Villa
3 Bed

DRAWING TITLE:	Typical Frame Connections
DRAWN BY:	Y.A.Clark
SCALE:	
DRAWING NO:	C109
DATE:	16/02/2026



Typical Frame Connections 2

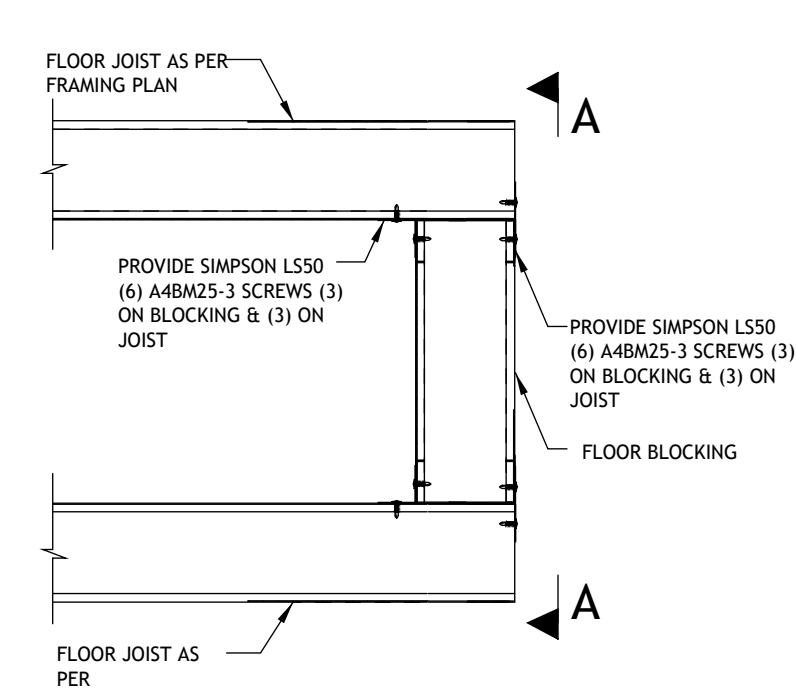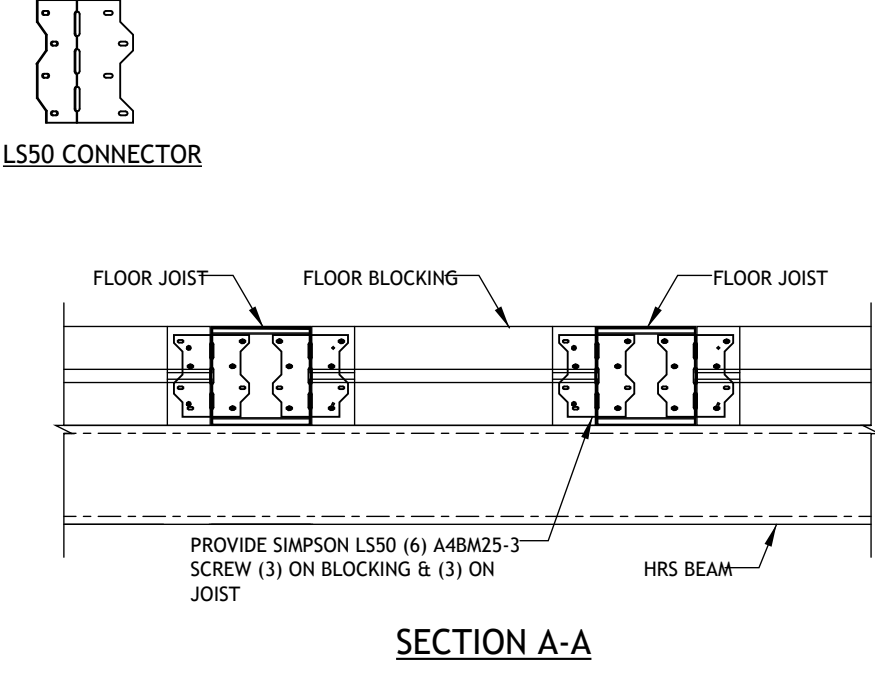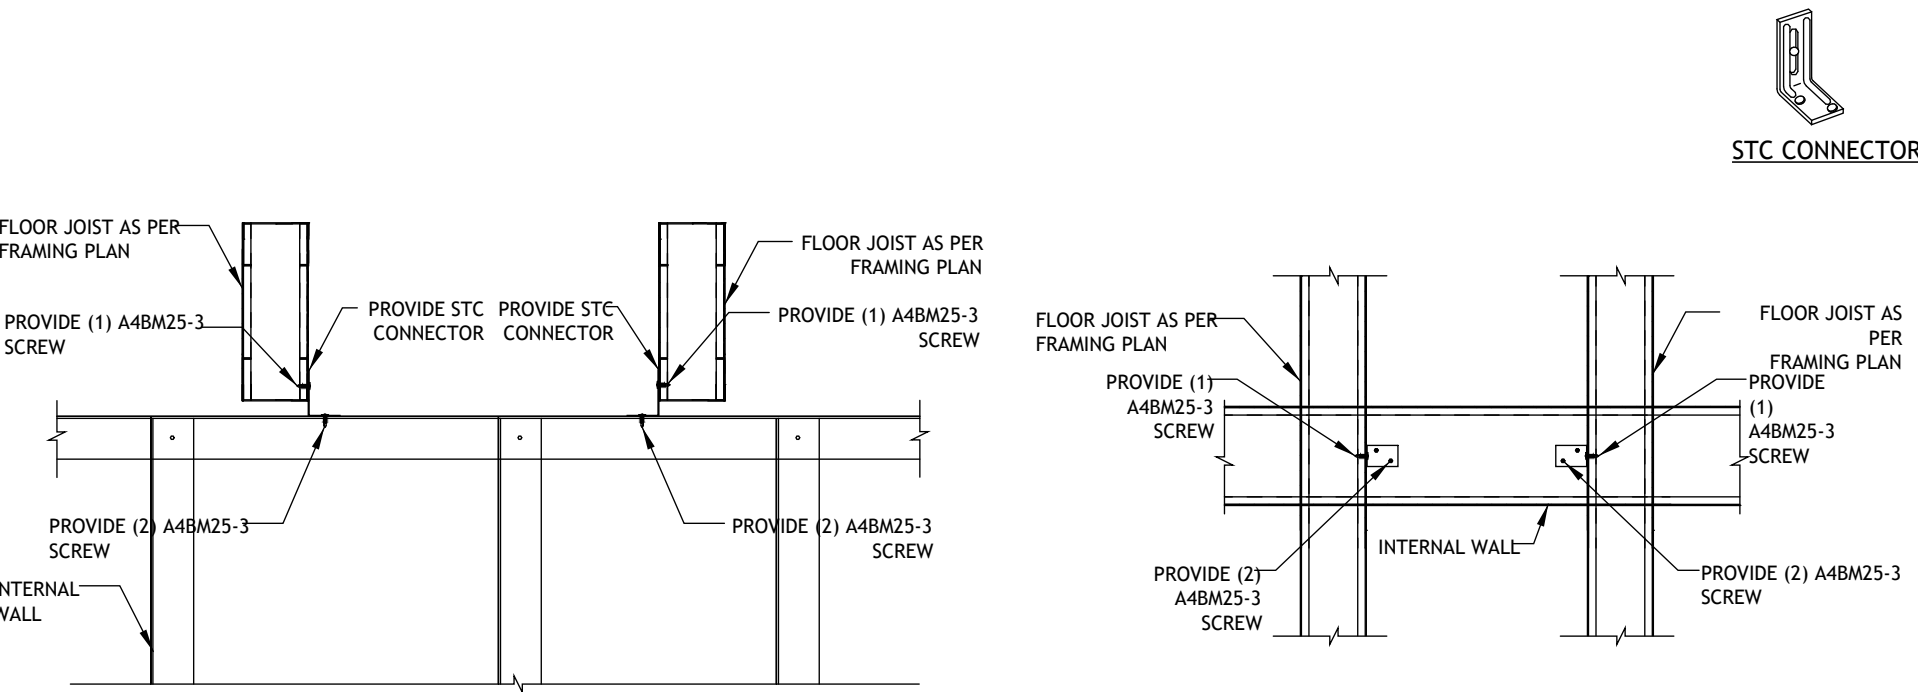

1. THESE DRAWINGS MUST BE CHECKED BY THE CUSTOMER OR CONTRACTOR PRIOR TO APPROVAL. ANY ERRORS OR OMISSIONS MUST BE REPORTED IN WRITING TO BAUHU PRIOR TO COMMENCEMENT OF CONSTRUCTION.
2. ARCHITECTURAL DRAWINGS SHOULD BE READ IN CONJUNCTION WITH STRUCTURAL DETAILING AND FABRICATION GENERAL ASSEMBLY DRAWINGS.
3. FOR CONSTRUCTION PURPOSES, USE ONLY THE LATEST APPROVED DRAWINGS LABELED 'ISSUED FOR CONSTRUCTION'.
4. DO NOT SCALE FROM THIS DRAWING.
5. THE COMPANY OPERATES USING METRIC DIMENSIONS AS THE PRINCIPAL DENOMINATION.
6. ALL CONCRETE WORKS ARE OUTSIDE OF THE SCOPE OF THE COMPANY. INFORMATION REGARDING SLAB DESIGN AND CONNECTIONS IN THESE DRAWINGS ARE INTENDED FOR GUIDANCE ONLY. FOUNDATION AND SLAB WORKS SHOULD BE DESIGNED AND APPROVED BY A LOCAL STRUCTURAL ENGINEER.
7. THE COMPANY RETAINS FULL TITLE AND OWNERSHIP OF THESE PLANS AND DESIGNS. ANY UNAUTHORISED USE, REPRODUCTION, OR DISTRIBUTION OF THESE PLANS, WHETHER IN WHOLE OR PART, IS EXPRESSLY PROHIBITED WITHOUT PRIOR WRITTEN CONSENT.
8. THE HYBRID STEEL FRAME CONSTRUCTION SYSTEM AND METHODOLOGY (PATENT PENDING) DESCRIBED IN THESE PLANS HAS BEEN DEVELOPED BY THE COMPANY AND IS SUBJECT TO A PROVISIONAL PATENT APPLICATION & ASSIGNMENT - US APPLICATION NO. 63/722,841



Typical Internal Wall Connection Floor Joist

Floor Blocking to Floor Joist Connection

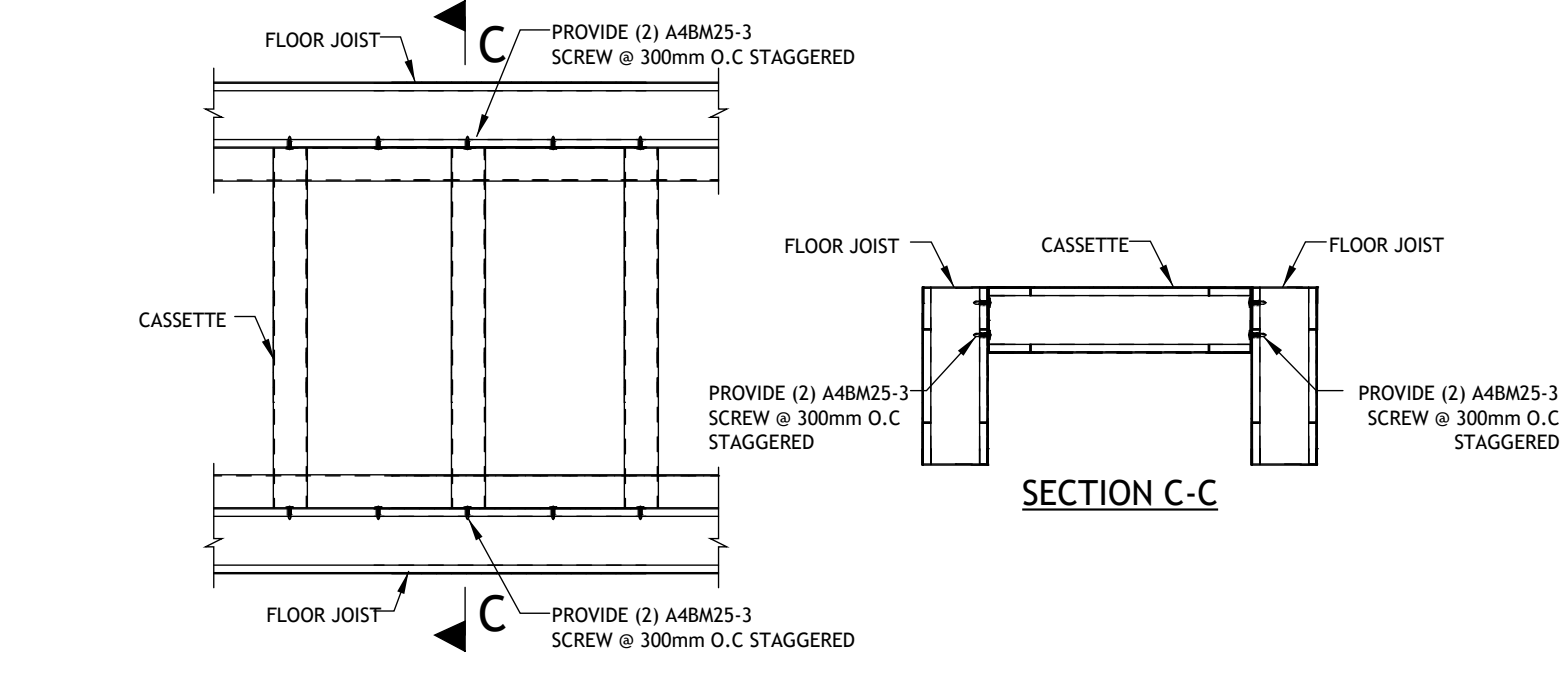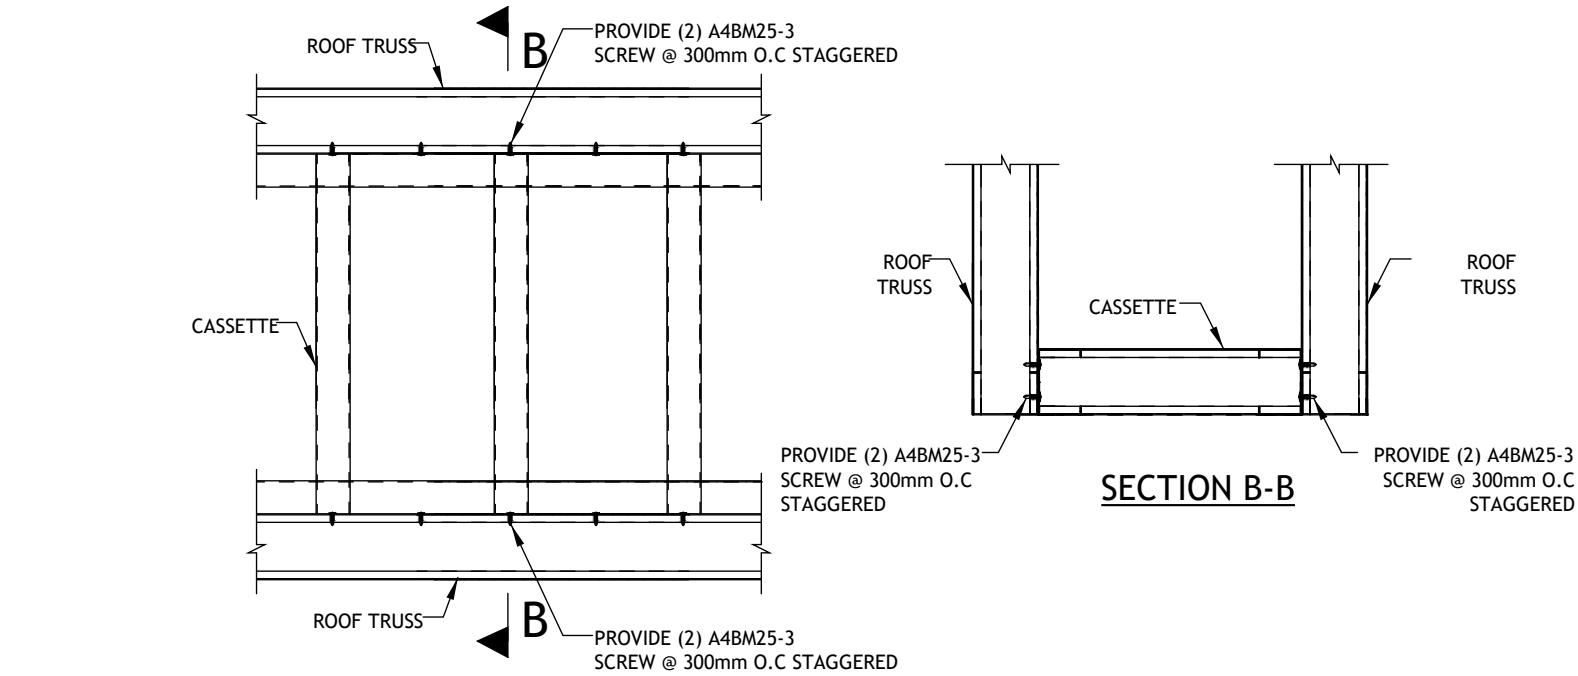

Cassette to Roof Truss Connection

Cassette to Floor Joist Connection

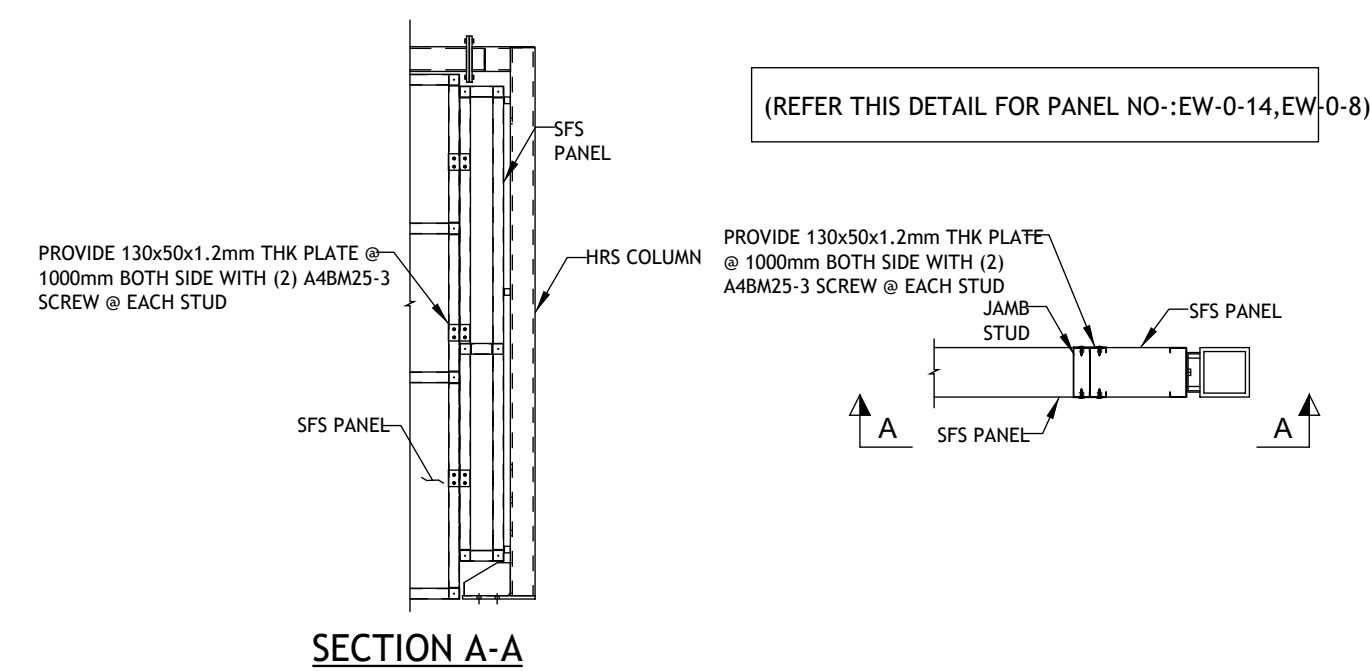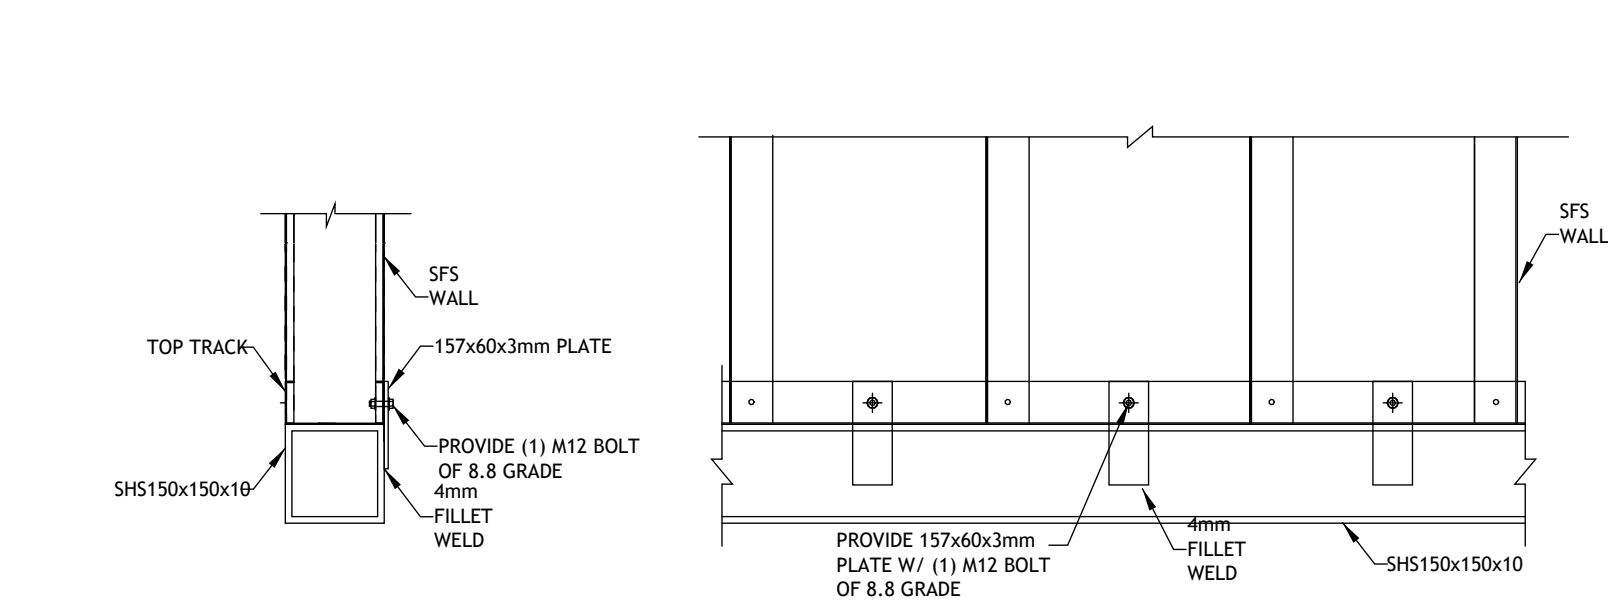

Typical Detail at SFS Bottom Track to HRS Beam Connection (External & Internal Wall)

SFS Panel Connection Detail

No.	Revision	Date

ISSUED FOR:

Issued for information

Issued for client approval

Issued for fabrication



Issued for construction

Coconut Villa
3 Bed



DRAWING TITLE:	Typical Frame Connections
DRAWN BY:	Y.A.Clark
SCALE:	
DRAWING NO:	C110
DATE:	16/02/2026

Typical Frame Connections 3



NOTES:
ALL WELDS FOR CONNECTION OF ASSEMBLY TO BE NOTE FROM FABRICATION DRAWING

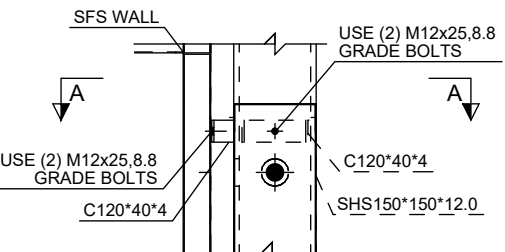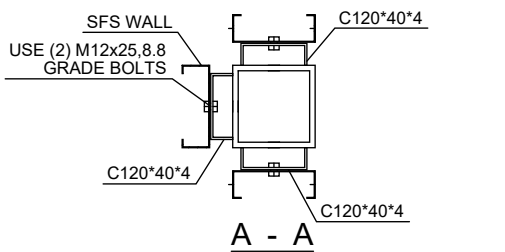



HRS Bracket Detail for Wall Connection

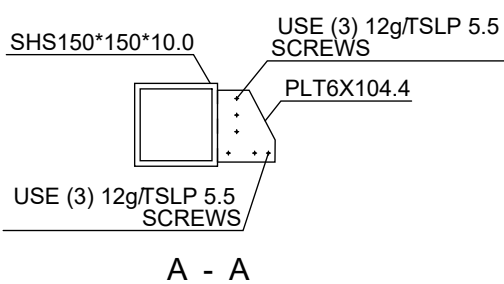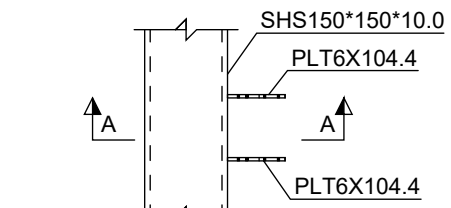


Typ. Truss Outside Plate Connection

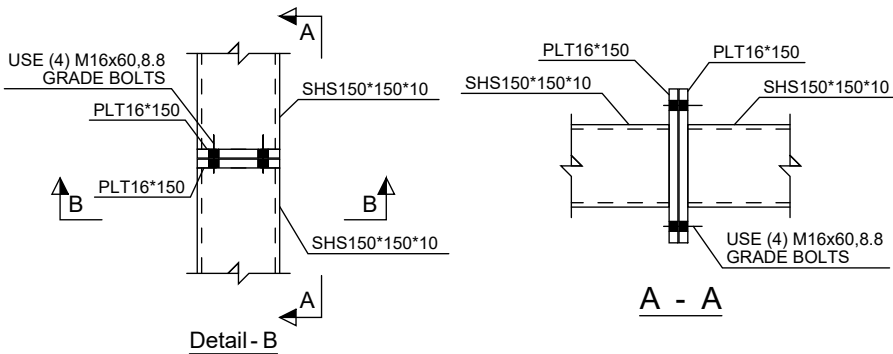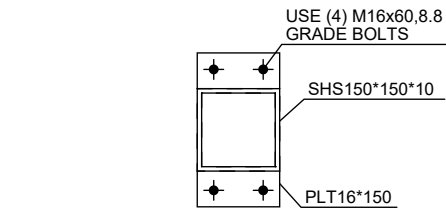


Typ. Vertical Splice Connection

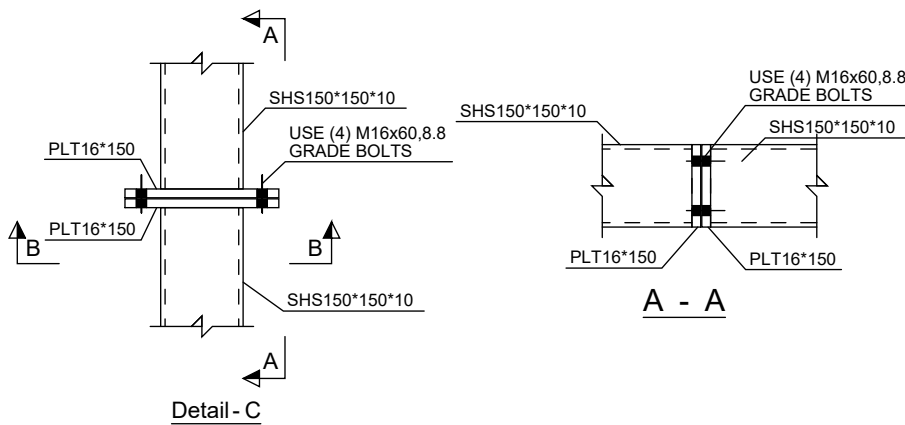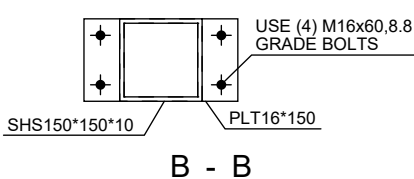


Typ. Horizontal Splice Connection

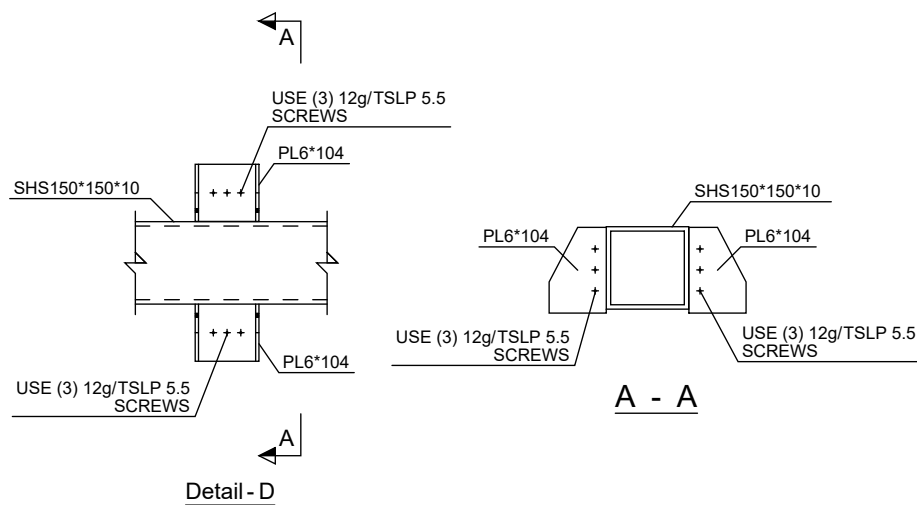


Typ. Truss Bracket Connection

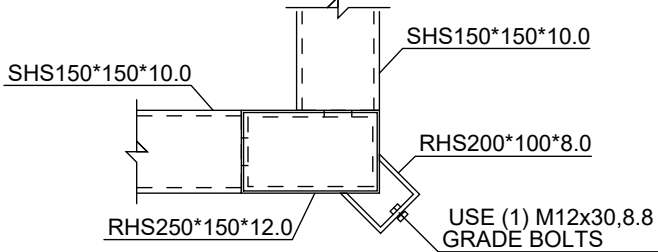


Typ. Corner Truss Connection

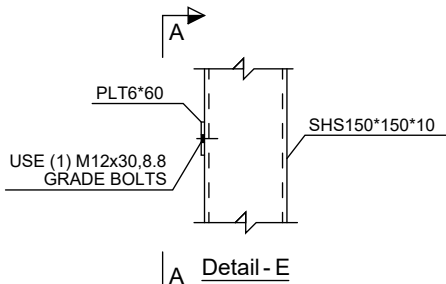


Typ. Wall to Beam Top Plate Connection

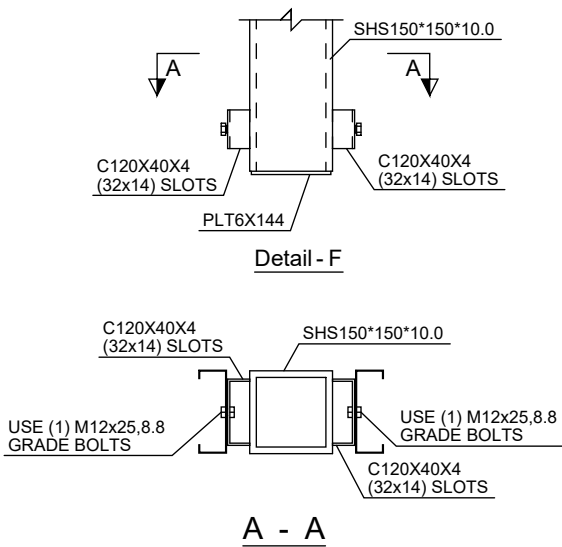


Typ. Lintel to Wind Post Connection

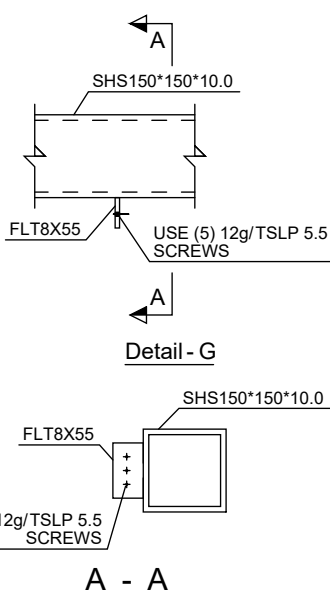


Cassette to Beam Connection

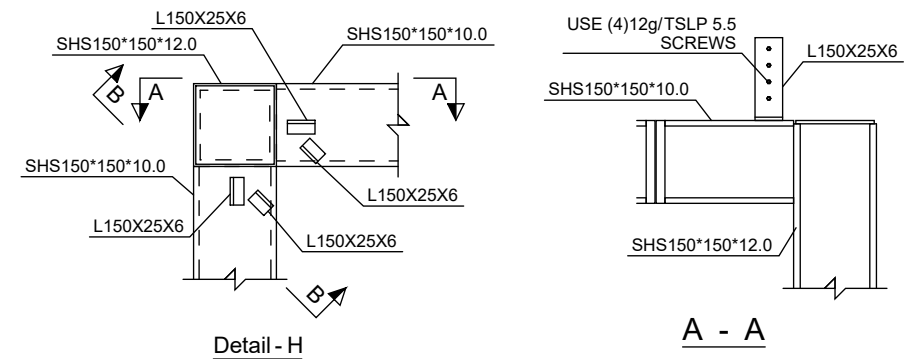

Typ. Beam to Column Connection Using C Bracket

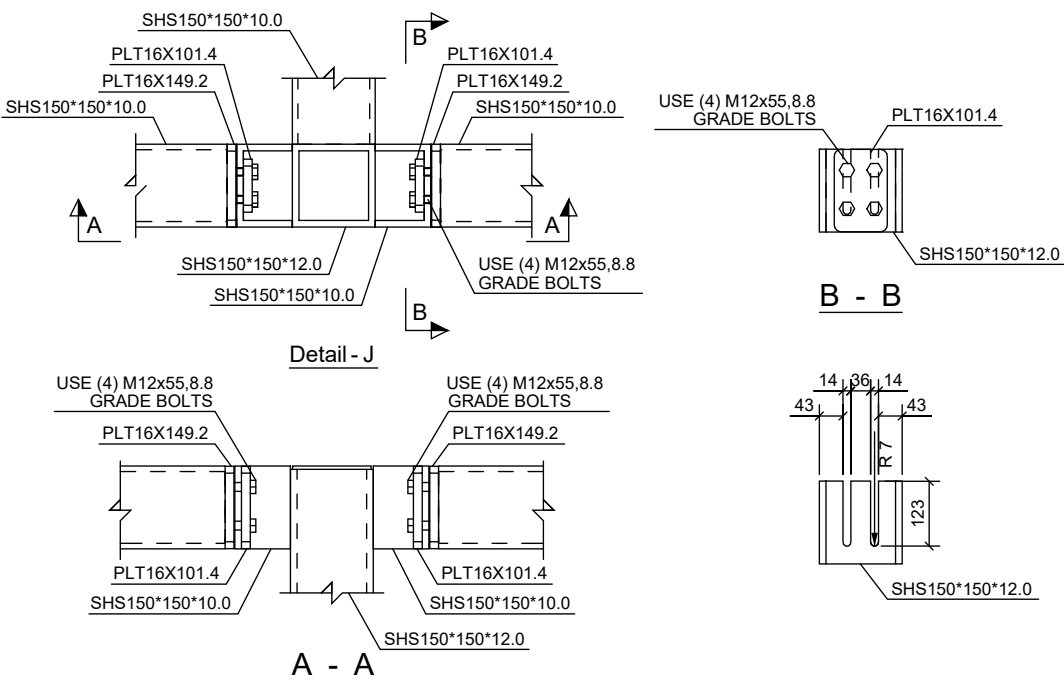

Typ. Beam to Column Connection Using C Bracket

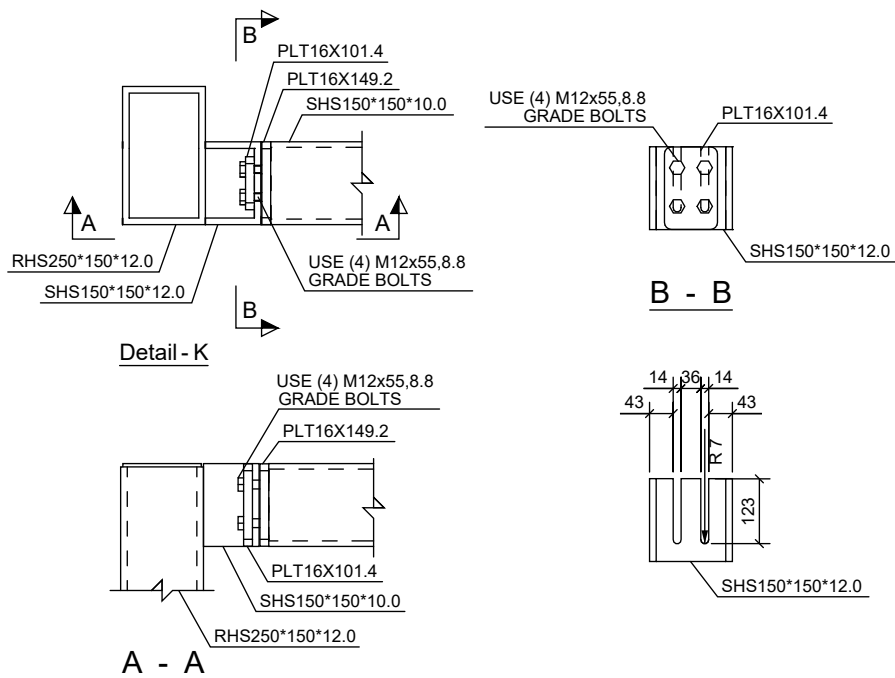

Typ. Beam to Column Connection Using C Bracket

1. THESE DRAWINGS MUST BE CHECKED BY THE CUSTOMER OR CONTRACTOR PRIOR TO APPROVAL. ANY ERRORS OR OMISSIONS MUST BE REPORTED IN WRITING TO BAUHU PRIOR TO COMMENCEMENT OF CONSTRUCTION.
2. ARCHITECTURAL DRAWINGS SHOULD BE READ IN CONJUNCTION WITH STRUCTURAL DETAILING AND FABRICATION GENERAL ASSEMBLY DRAWINGS.
3. FOR CONSTRUCTION PURPOSES, USE ONLY THE LATEST APPROVED DRAWINGS LABELED 'ISSUED FOR CONSTRUCTION'.
4. DO NOT SCALE FROM THIS DRAWING.
5. THE COMPANY OPERATES USING METRIC DIMENSIONS AS THE PRINCIPAL DENOMINATION.
6. ALL CONCRETE WORKS ARE OUTSIDE OF THE SCOPE OF THE COMPANY. INFORMATION REGARDING SLAB DESIGN AND CONNECTIONS IN THESE DRAWINGS ARE INTENDED FOR GUIDENCE ONLY. FOUNDATION AND SLAB WORKS SHOULD BE DESIGNED AND APPROVED BY A LOCAL STRUCTURAL ENGINEER.
7. THE COMPANY RETAINS FULL TITLE AND OWNERSHIP OF THESE PLANS AND DESIGNS. ANY UNAUTHORISED USE, REPRODUCTION, OR DISTRIBUTION OF THESE PLANS, WHETHER IN WHOLE OR PART, IS EXPRESSLY PROHIBITED WITHOUT PRIOR WRITTEN CONSENT.
8. THE HYBRID STEEL FRAME CONSTRUCTION SYSTEM AND METHODOLOGY (PATENT PENDING) DESCRIBED IN THESE PLANS HAS BEEN DEVELOPED BY THE COMPANY AND IS SUBJECT TO A PROVISIONAL PATENT APPLICATION & ASSIGNMENT - US APPLICATION NO. 63/722,841

No.	Revision	Date

ISSUED FOR:

Issued for information

Issued for client approval

Issued for fabrication

Issued for construction

Coconut Villa
3 Bed

DRAWING TITLE:

Typical Frame Connections

DRAWN BY:

Y.A.Clark

SCALE:

DRAWING NO:


C111

DATE:

16/02/2026


Typical Frame Connections 4

Hold Down Detail

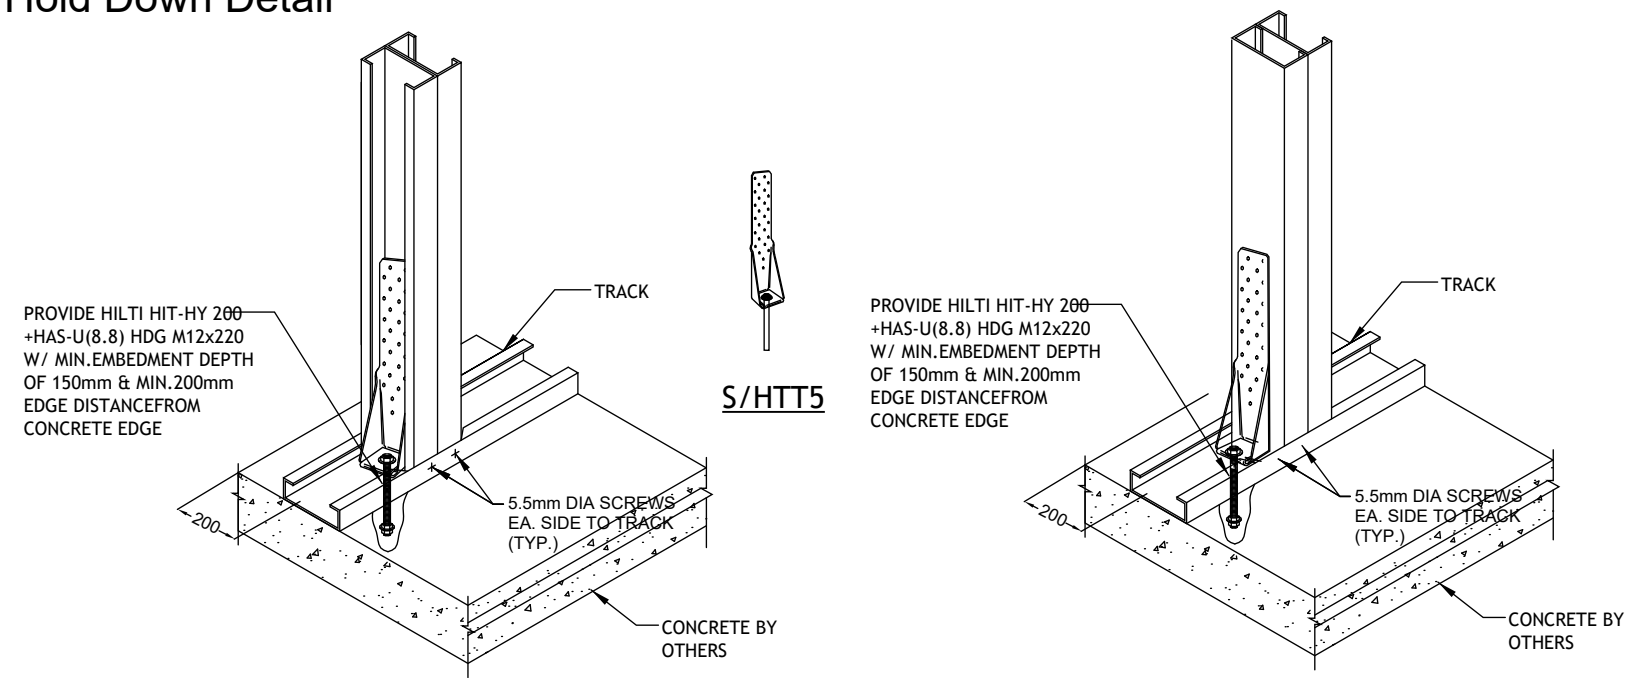

- NOTE -
- 1. ANCHOR & SCREWS SPECIFICATION AS PER SPECIFIED ON STRUCTURAL PLAN
 - 2. FIXING SPECIFICATION SUBJECT TO CHANGE AS PER DESIGN.


Casette to Floor/Roof Joist Connection

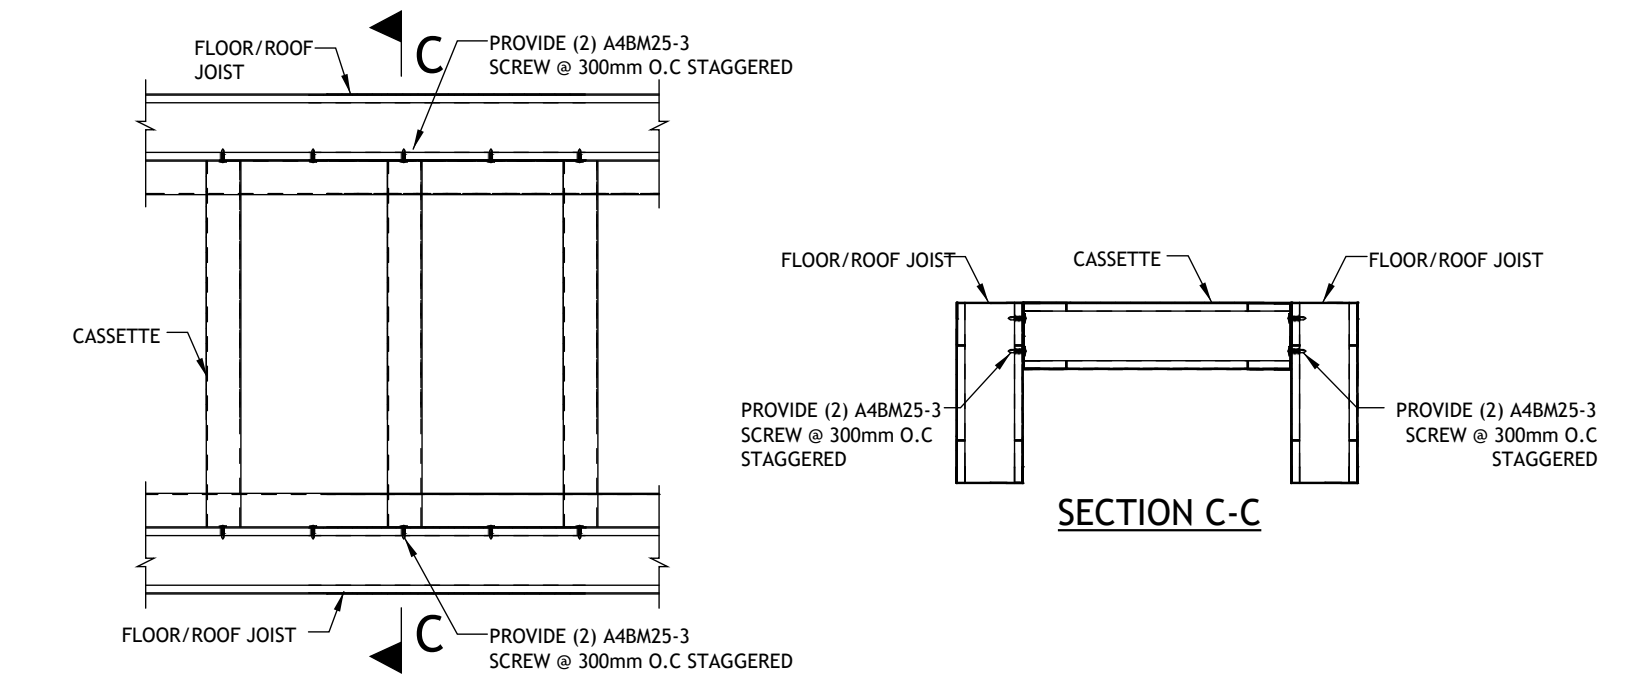

NOTE -FIXING SPECIFICATION SUBJECT TO CHANGE AS PER DESIGN.





Typ. Internal Wall Connection Floor/Roof Joist

(Perpendicular Condition)

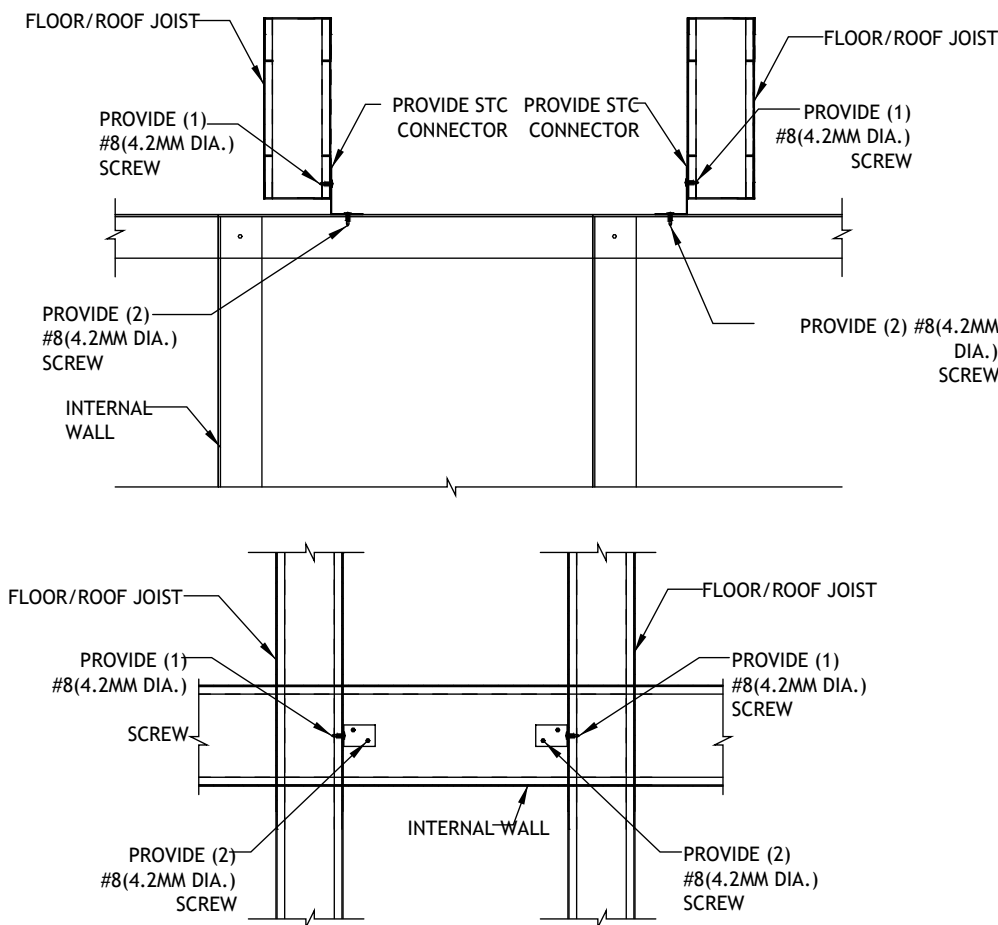


NOTE -FIXING SPECIFICATION SUBJECT TO CHANGE AS PER DESIGN.



Typ. Brace Wall Panel Connection with Treaded Rod

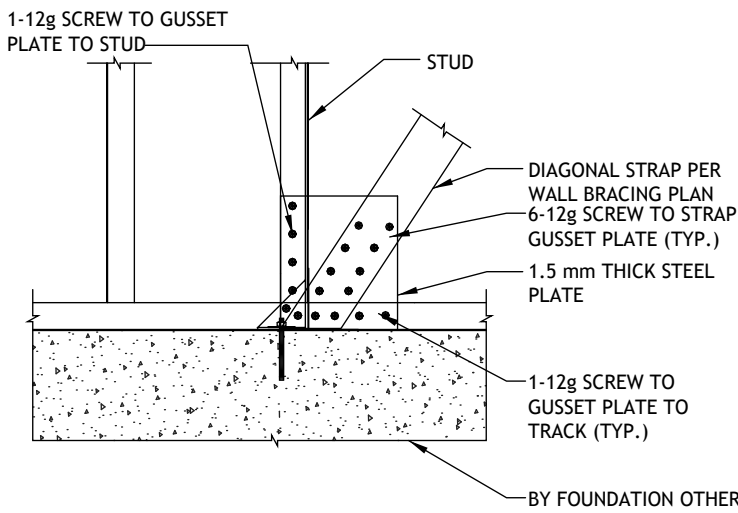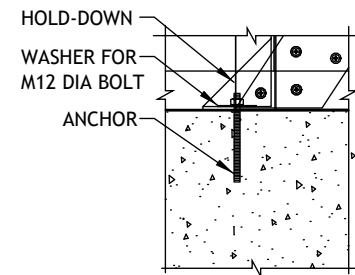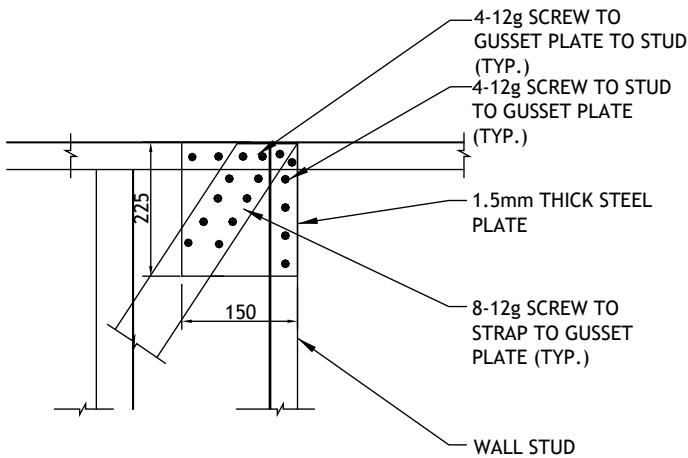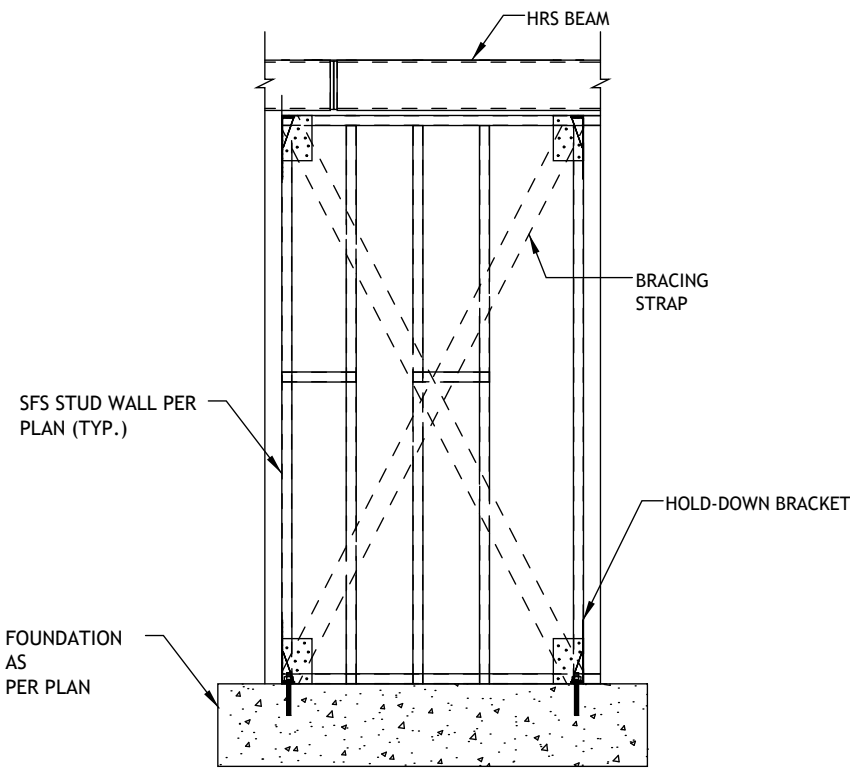

- NOTE -
- 1. ANCHOR & SCREWS SPECIFICATION AS PER SPECIFIED ON STRUCTURAL PLAN
 - 2. FIXING SPECIFICATION SUBJECT TO CHANGE AS PER DESIGN.

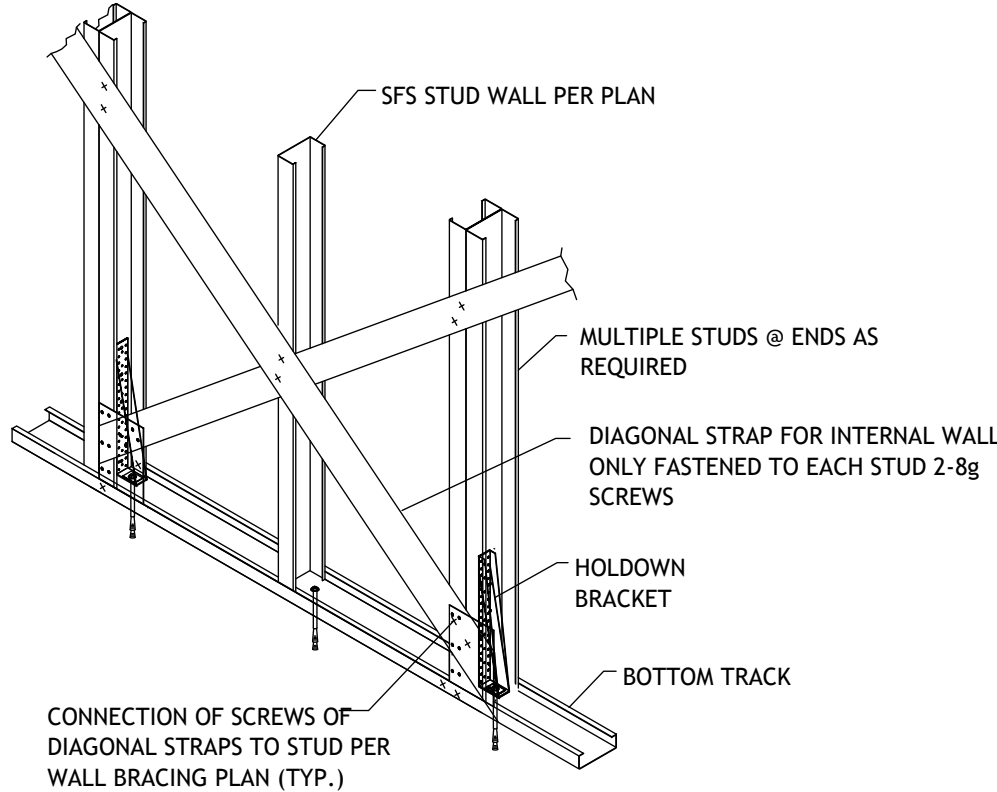

STRAP TO TRACK CONNECTION

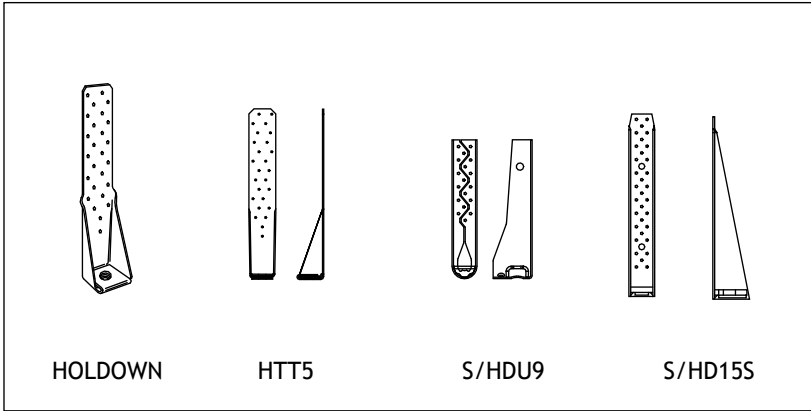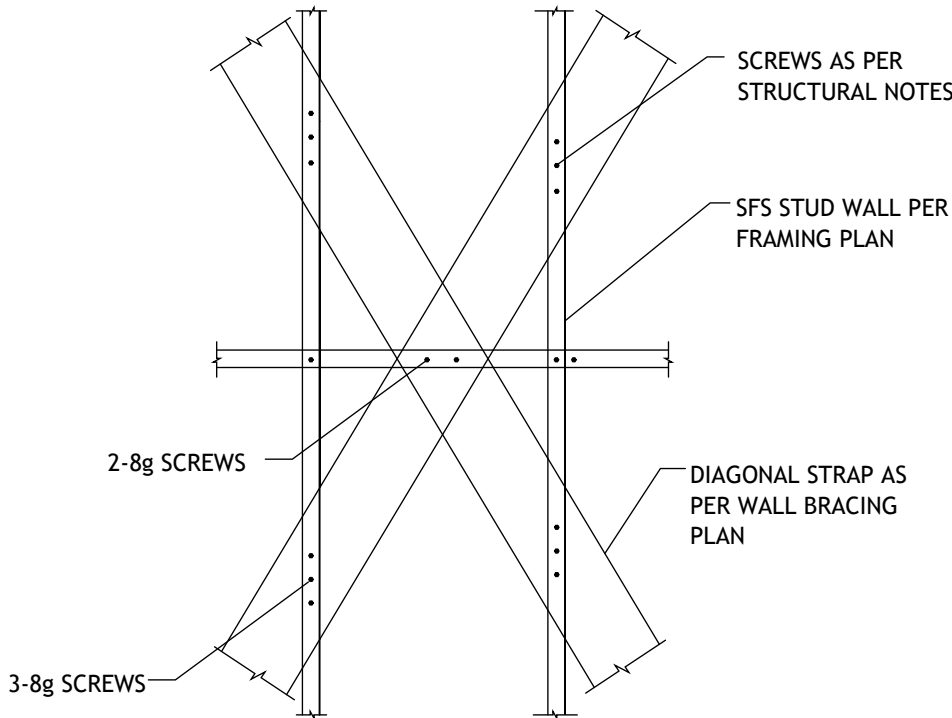

- 1. THESE DRAWINGS MUST BE CHECKED BY THE CUSTOMER OR CONTRACTOR PRIOR TO APPROVAL. ANY ERRORS OR OMISSIONS MUST BE REPORTED IN WRITING TO BAUHU PRIOR TO COMMENCEMENT OF CONSTRUCTION.
- 2. ARCHITECTURAL DRAWINGS SHOULD BE READ IN CONJUNCTION WITH STRUCTURAL DETAILING AND FABRICATION GENERAL ASSEMBLY DRAWINGS.
- 3. FOR CONSTRUCTION PURPOSES, USE ONLY THE LATEST APPROVED DRAWINGS LABELED 'ISSUED FOR CONSTRUCTION'.
- 4. DO NOT SCALE FROM THIS DRAWING.
- 5. THE COMPANY OPERATES USING METRIC DIMENSIONS AS THE PRINCIPAL DENOMINATION.
- 6. ALL CONCRETE WORKS ARE OUTSIDE OF THE SCOPE OF THE COMPANY. INFORMATION REGARDING SLAB DESIGN AND CONNECTIONS IN THESE DRAWINGS ARE INTENDED FOR GUIDANCE ONLY. FOUNDATION AND SLAB WORKS SHOULD BE DESIGNED AND APPROVED BY A LOCAL STRUCTURAL ENGINEER.
- 7. THE COMPANY RETAINS FULL TITLE AND OWNERSHIP OF THESE PLANS AND DESIGNS. ANY UNAUTHORISED USE, REPRODUCTION, OR DISTRIBUTION OF THESE PLANS, WHETHER IN WHOLE OR PART, IS EXPRESSLY PROHIBITED WITHOUT PRIOR WRITTEN CONSENT.
- 8. THE HYBRID STEEL FRAME CONSTRUCTION SYSTEM AND METHODOLOGY (PATENT PENDING) DESCRIBED IN THESE PLANS HAS BEEN DEVELOPED BY THE COMPANY AND IS SUBJECT TO A PROVISIONAL PATENT APPLICATION & ASSIGNMENT - US APPLICATION NO. 63/722,841

No.	Revision	Date

ISSUED FOR:

Issued for information

Issued for client approval

Issued for fabrication

Issued for construction

Coconut Villa
3 Bed

DRAWING TITLE:
Typical Frame Connections

DRAWN BY:
Y.A.Clark

SCALE:

DRAWING NO:
C112

DATE:
16/02/2026

1. THESE DRAWINGS MUST BE CHECKED BY THE CUSTOMER OR CONTRACTOR PRIOR TO APPROVAL. ANY ERRORS OR OMISSIONS MUST BE REPORTED IN WRITING TO BAUHU PRIOR TO COMMENCEMENT OF CONSTRUCTION.
2. ARCHITECTURAL DRAWINGS SHOULD BE READ IN CONJUNCTION WITH STRUCTURAL DETAILING AND FABRICATION GENERAL ASSEMBLY DRAWINGS.
3. FOR CONSTRUCTION PURPOSES, USE ONLY THE LATEST APPROVED DRAWINGS LABELED 'ISSUED FOR CONSTRUCTION'.
4. DO NOT SCALE FROM THIS DRAWING.
5. THE COMPANY OPERATES USING METRIC DIMENSIONS AS THE PRINCIPAL DENOMINATION.
6. ALL CONCRETE WORKS ARE OUTSIDE OF THE SCOPE OF THE COMPANY. INFORMATION REGARDING SLAB DESIGN AND CONNECTIONS IN THESE DRAWINGS ARE INTENDED FOR GUIDANCE ONLY. FOUNDATION AND SLAB WORKS SHOULD BE DESIGNED AND APPROVED BY A LOCAL STRUCTURAL ENGINEER.
7. THE COMPANY RETAINS FULL TITLE AND OWNERSHIP OF THESE PLANS AND DESIGNS. ANY UNAUTHORISED USE, REPRODUCTION, OR DISTRIBUTION OF THESE PLANS, WHETHER IN WHOLE OR PART, IS EXPRESSLY PROHIBITED WITHOUT PRIOR WRITTEN CONSENT.
8. THE HYBRID STEEL FRAME CONSTRUCTION SYSTEM AND METHODOLOGY (PATENT PENDING) DESCRIBED IN THESE PLANS HAS BEEN DEVELOPED BY THE COMPANY AND IS SUBJECT TO A PROVISIONAL PATENT APPLICATION & ASSIGNMENT - US APPLICATION NO. 63/722,841

No.	Revision	Date

ISSUED FOR:

Issued for information

Issued for client approval

Issued for fabrication

Issued for construction

Coconut Villa 3 Bed

DRAWING TITLE:

Concrete Piers&Slab Detail

DRAWN BY:

Y.A.Clark

SCALE:



1 : 60

DRAWING NO:

C113

DATE:

16/02/2026

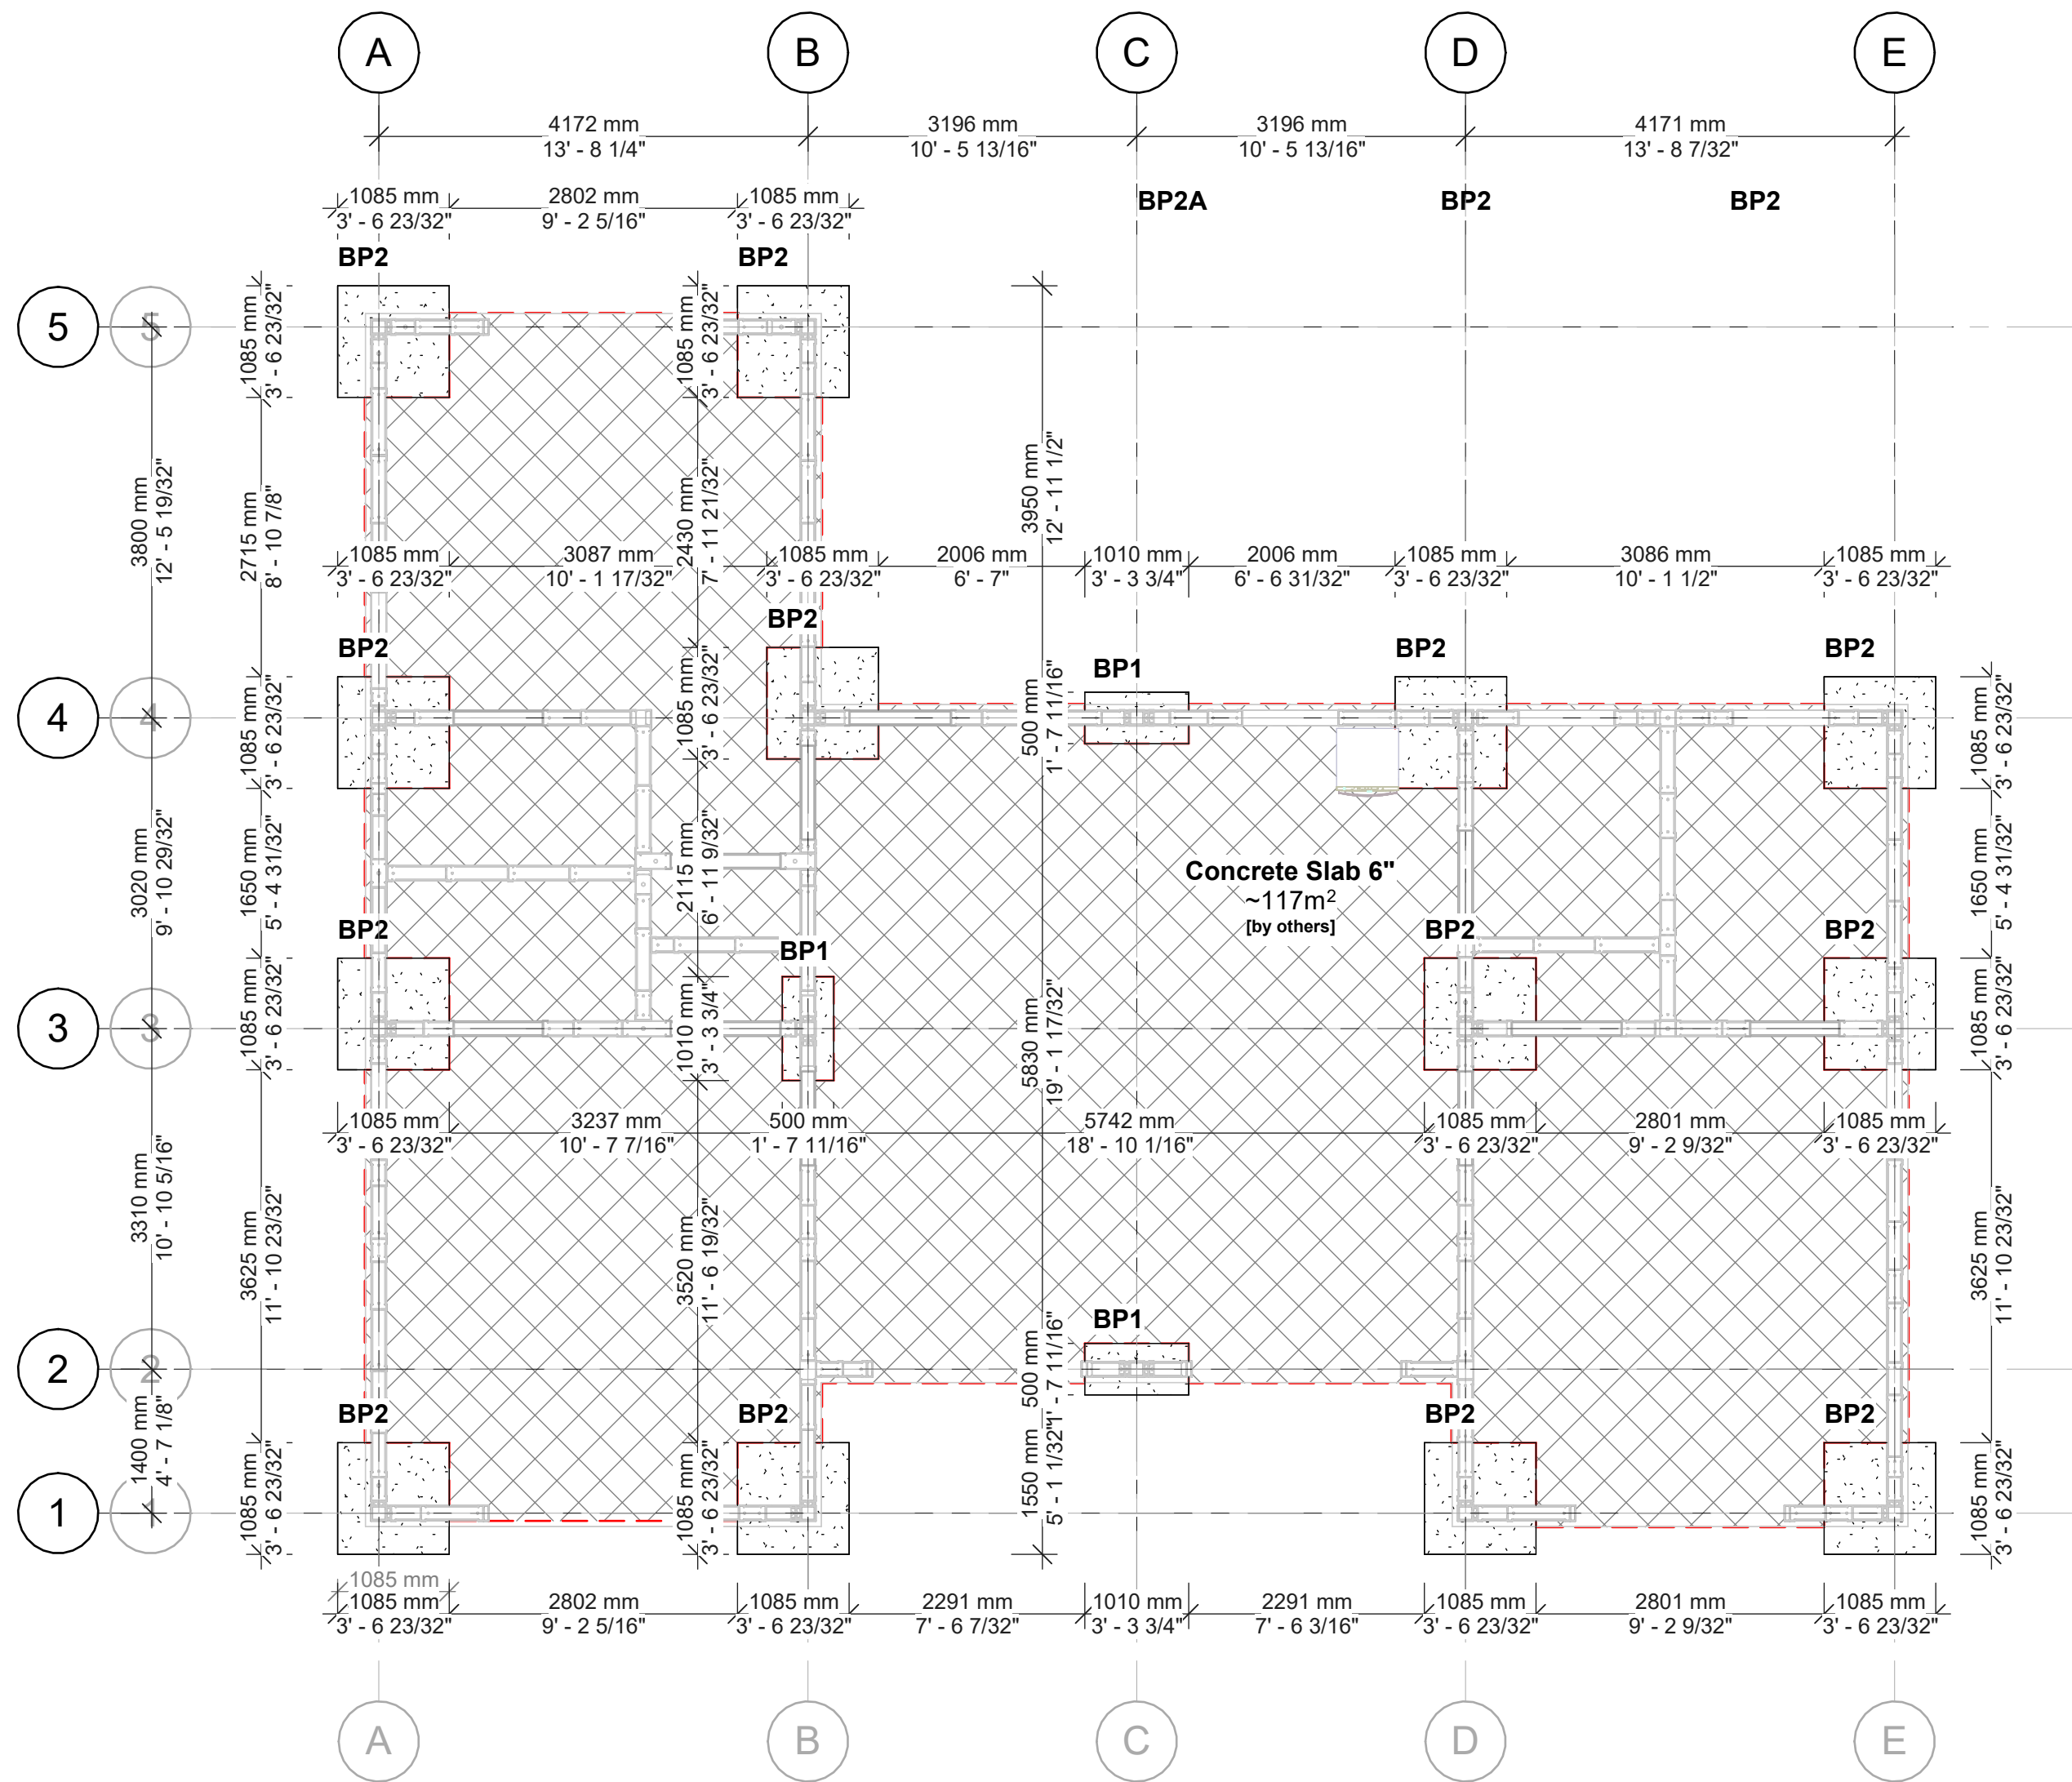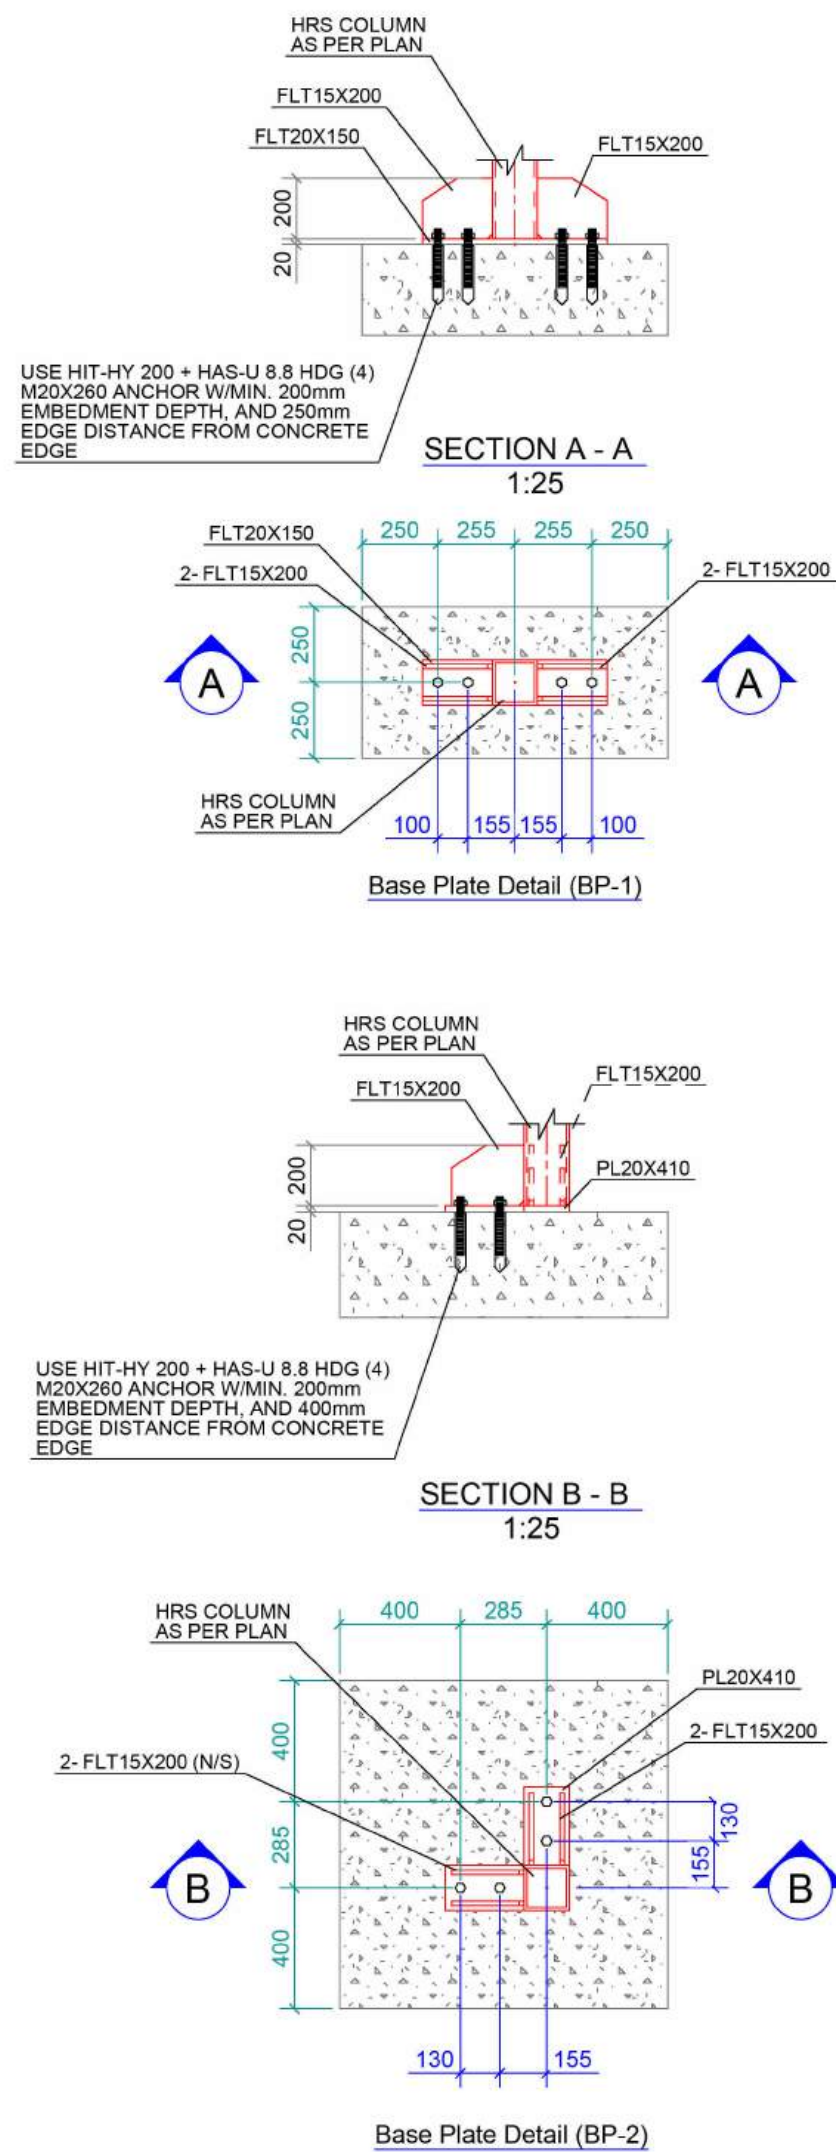

Note:

- Foundation details, slab plans and layout are provided for information only. Refer to structural engineering plans for layout, connection details, stud embedment and edge distances. RC pier and footing to be designed by a local structural engineer according to site conditions.
- All groundworks, landscape and hardscape, fencing, footings, foundation and floor slab works, cisterns and septic tanks are the responsibility of the owner. Building components are provided on the assumption that the site is prepared and an adequate foundation approved by a competent local structural engineer, has been provided. All services and sub- slab conduits should be completed finishing in a perfectly square and level concrete platform to enable the building erection.

1. THESE DRAWINGS MUST BE CHECKED BY THE CUSTOMER OR CONTRACTOR PRIOR TO APPROVAL. ANY ERRORS OR OMISSIONS MUST BE REPORTED IN WRITING TO BAUHU PRIOR TO COMMENCEMENT OF CONSTRUCTION.
2. ARCHITECTURAL DRAWINGS SHOULD BE READ IN CONJUNCTION WITH STRUCTURAL DETAILING AND FABRICATION GENERAL ASSEMBLY DRAWINGS.
3. FOR CONSTRUCTION PURPOSES, USE ONLY THE LATEST APPROVED DRAWINGS LABELED 'ISSUED FOR CONSTRUCTION'.
4. DO NOT SCALE FROM THIS DRAWING.
5. THE COMPANY OPERATES USING METRIC DIMENSIONS AS THE PRINCIPAL DENOMINATION.
6. ALL CONCRETE WORKS ARE OUTSIDE OF THE SCOPE OF THE COMPANY. INFORMATION REGARDING SLAB DESIGN AND CONNECTIONS IN THESE DRAWINGS ARE INTENDED FOR GUIDENCE ONLY. FOUNDATION AND SLAB WORKS SHOULD BE DESIGNED AND APPROVED BY A LOCAL STRUCTURAL ENGINEER.
7. THE COMPANY RETAINS FULL TITLE AND OWNERSHIP OF THESE PLANS AND DESIGNS. ANY UNAUTHORISED USE, REPRODUCTION, OR DISTRIBUTION OF THESE PLANS, WHETHER IN WHOLE OR PART, IS EXPRESSLY PROHIBITED WITHOUT PRIOR WRITTEN CONSENT.
8. THE HYBRID STEEL FRAME CONSTRUCTION SYSTEM AND METHODOLOGY (PATENT PENDING) DESCRIBED IN THESE PLANS HAS BEEN DEVELOPED BY THE COMPANY AND IS SUBJECT TO A PROVISIONAL PATENT APPLICATION & ASSIGNMENT - US APPLICATION NO. 63/722,841


No.	Revision	Date

ISSUED FOR:

- Issued for information
- Issued for client approval
- Issued for fabrication
- Issued for construction

Coconut Villa
3 Bed

DRAWING TITLE:	Concrete Piers&Slab 3D Detail
DRAWN BY:	Y.A.Clark
SCALE:	
DRAWING NO:	C114
DATE:	16/02/2026

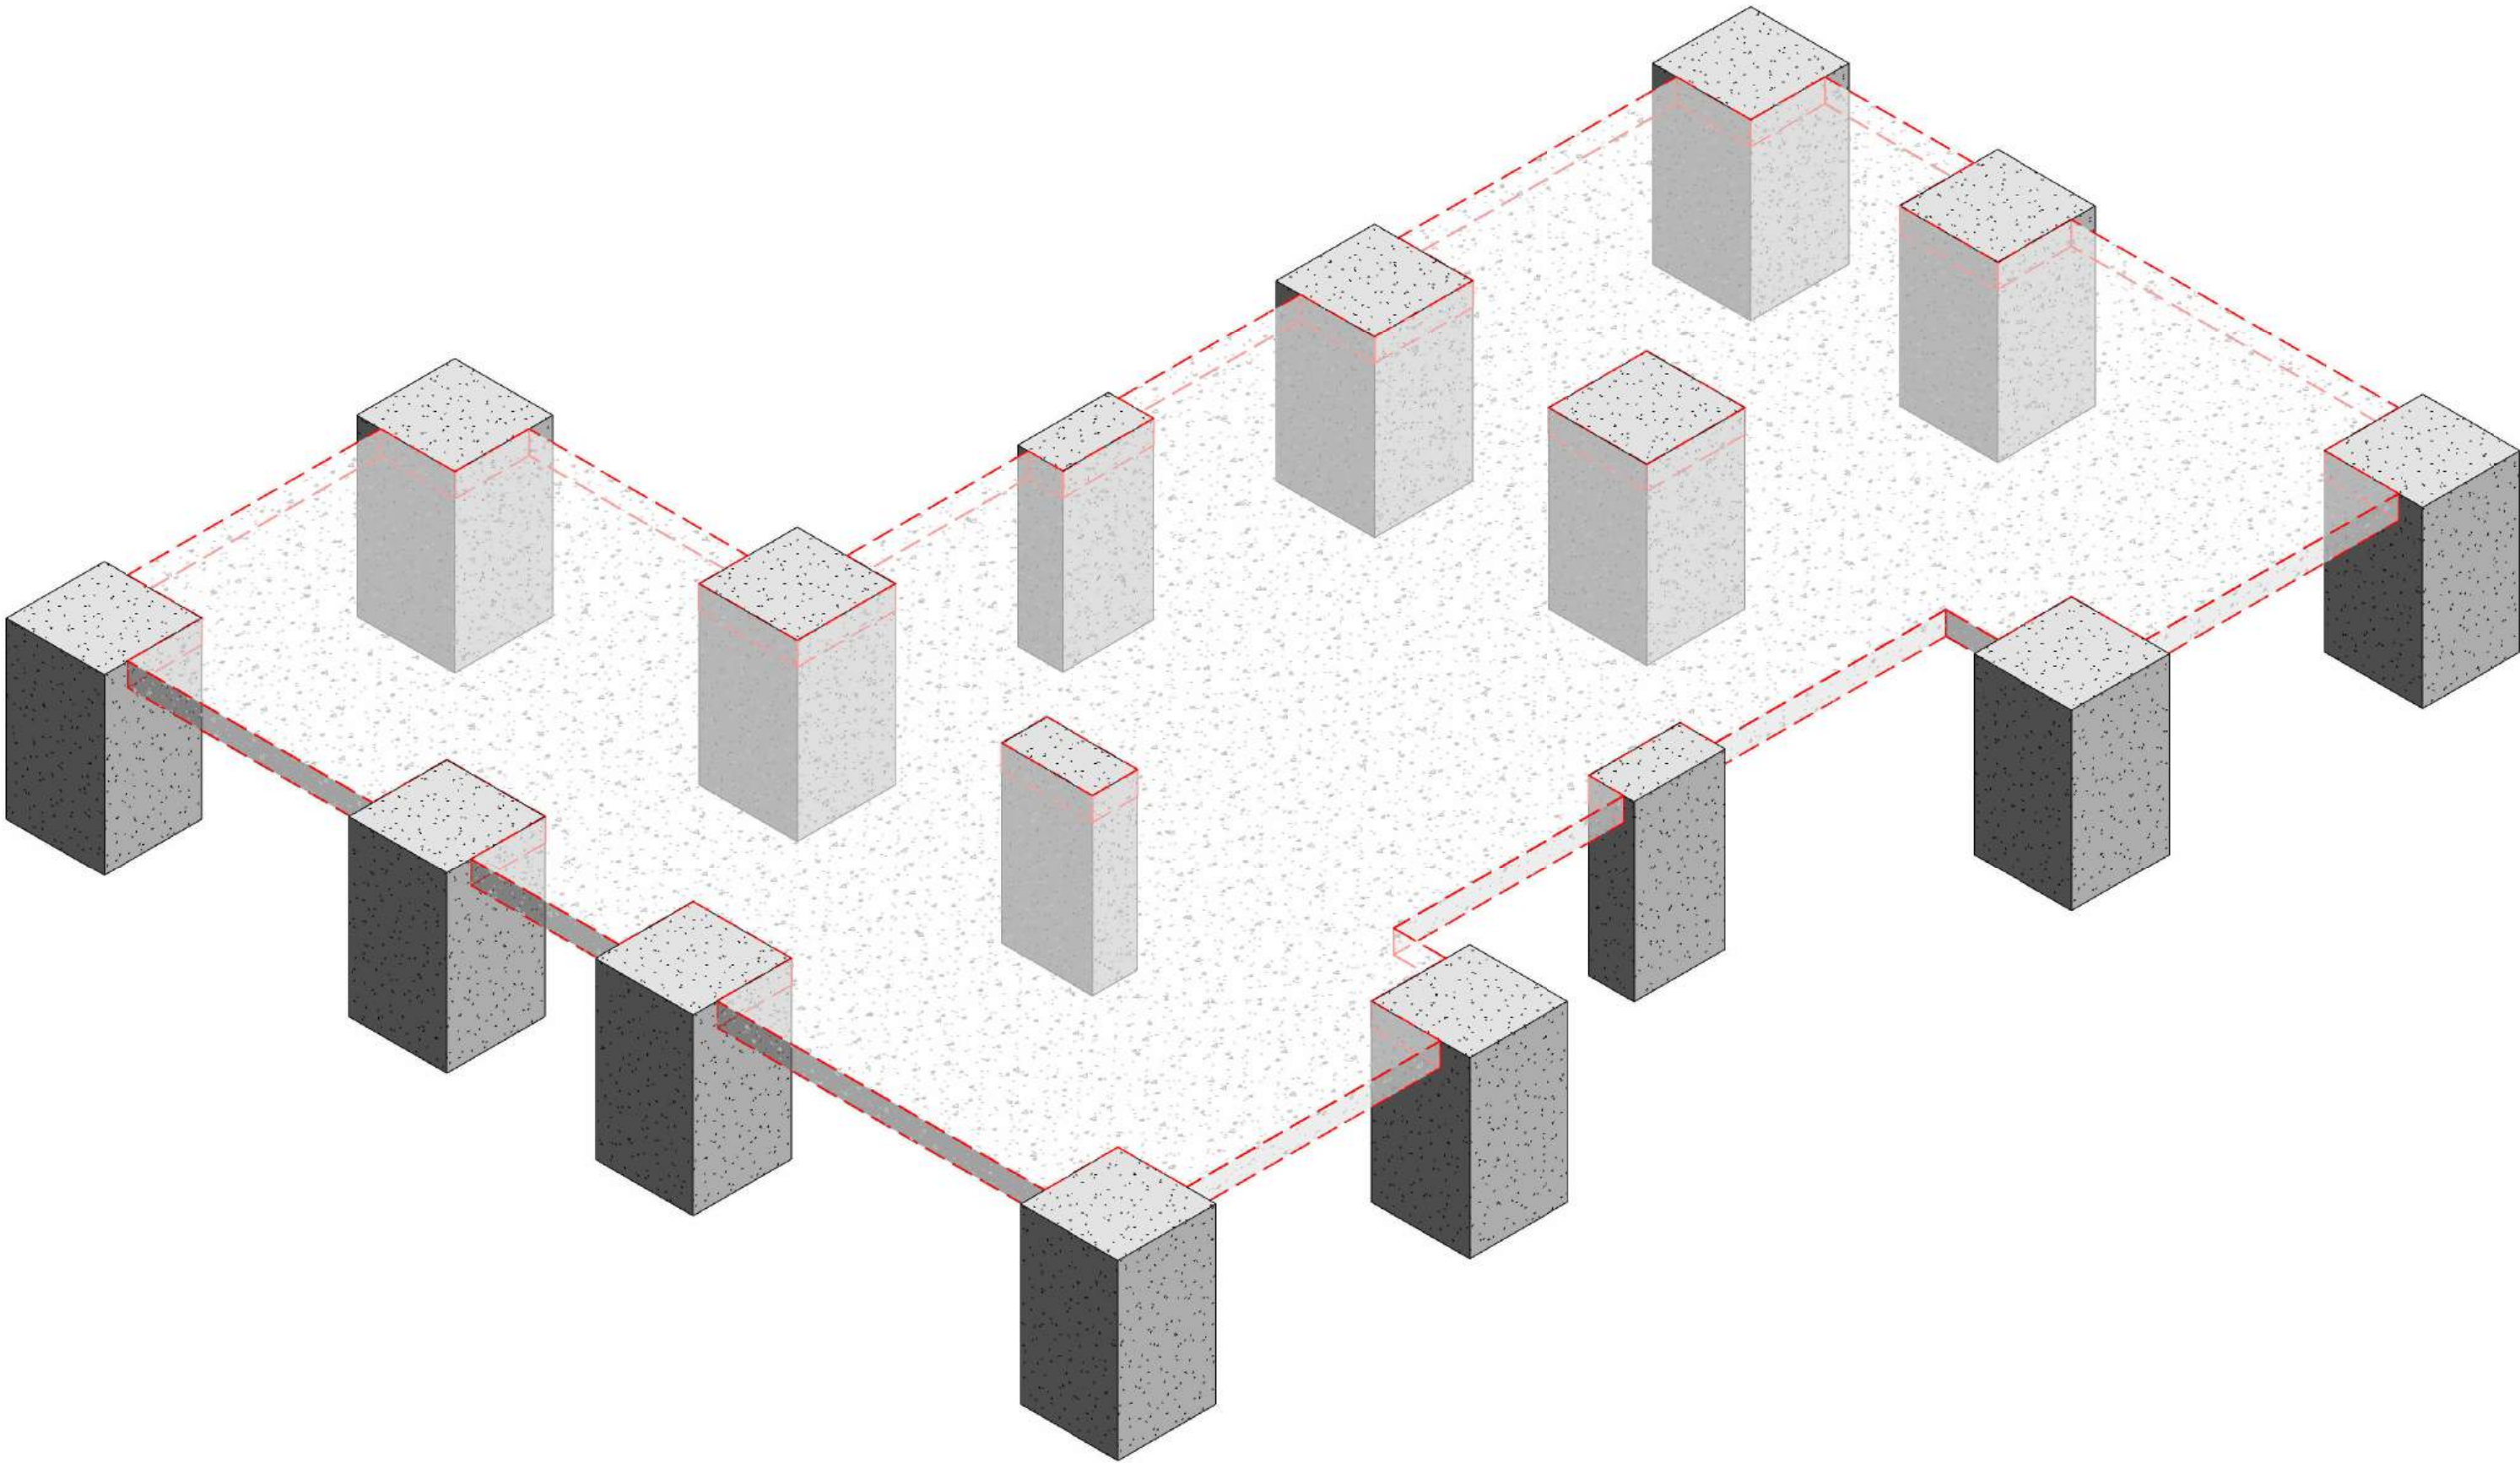

Note:

- The height of the concrete piers is determined by the required minimum anchor depth specified in the structural design drawings.