



Building View




Front View



Rear-Entrance View



Front View

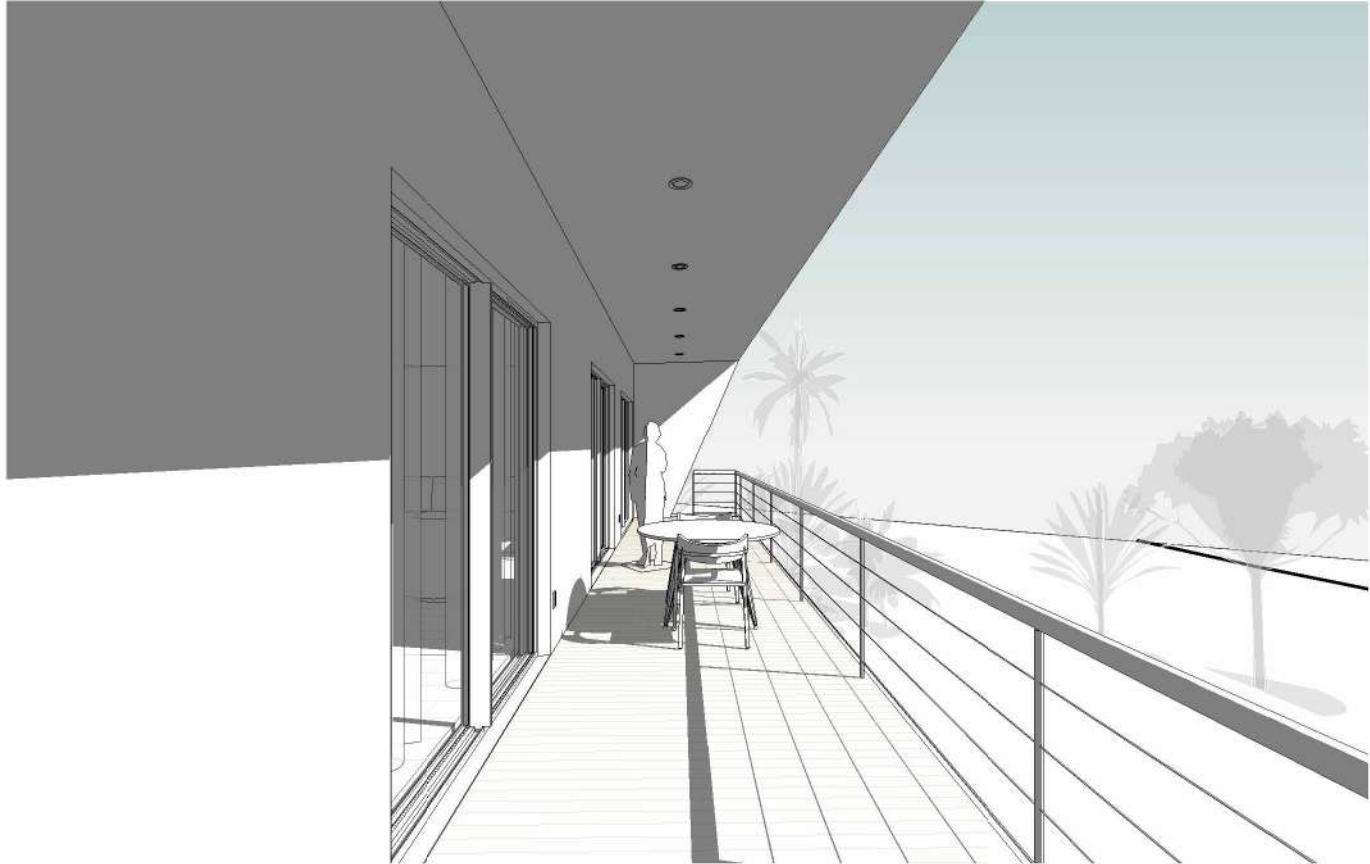

Terrace View

1. THESE DRAWINGS MUST BE CHECKED BY THE CUSTOMER OR CONTRACTOR PRIOR TO APPROVAL. ANY ERRORS OR OMISSIONS MUST BE REPORTED IN WRITING TO BAUHU PRIOR TO COMMENCEMENT OF CONSTRUCTION.
2. ARCHITECTURAL DRAWINGS SHOULD BE READ IN CONJUNCTION WITH STRUCTURAL DETAILING AND FABRICATION GENERAL ASSEMBLY DRAWINGS.
3. FOR CONSTRUCTION PURPOSES, USE ONLY THE LATEST APPROVED DRAWINGS LABELED 'ISSUED FOR CONSTRUCTION'.
4. DO NOT SCALE FROM THIS DRAWING.
5. THE COMPANY OPERATES USING METRIC DIMENSIONS AS THE PRINCIPAL DENOMINATION.
6. ALL CONCRETE WORKS ARE OUTSIDE OF THE SCOPE OF THE COMPANY. INFORMATION REGARDING SLAB DESIGN AND CONNECTIONS IN THESE DRAWINGS ARE INTENDED FOR GUIDANCE ONLY. FOUNDATION AND SLAB WORKS SHOULD BE DESIGNED AND APPROVED BY A LOCAL STRUCTURAL ENGINEER.
7. THE COMPANY RETAINS FULL TITLE AND OWNERSHIP OF THESE PLANS AND DESIGNS. ANY UNAUTHORIZED USE, REPRODUCTION, OR DISTRIBUTION OF THESE PLANS, WHETHER IN WHOLE OR PART, IS EXPRESSLY PROHIBITED WITHOUT PRIOR WRITTEN CONSENT.

No.	Revision	Date

ISSUED FOR:

Issued for information

Issued for client approval

Issued for fabrication

Issued for construction

Angel

DRAWING TITLE:	Title Sheet
DRAWN BY:	Yonca A.Clark
SCALE:	
DRAWING NO:	A101
DATE:	01/05/2024

Living Area Views



Isometric Plan View

1. THESE DRAWINGS MUST BE CHECKED BY THE CUSTOMER OR CONTRACTOR PRIOR TO APPROVAL. ANY ERRORS OR OMISSIONS MUST BE REPORTED IN WRITING TO BAUHU PRIOR TO COMMENCEMENT OF CONSTRUCTION.
2. ARCHITECTURAL DRAWINGS SHOULD BE READ IN CONJUNCTION WITH STRUCTURAL DETAILING AND FABRICATION GENERAL ASSEMBLY DRAWINGS.
3. FOR CONSTRUCTION PURPOSES, USE ONLY THE LATEST APPROVED DRAWINGS LABELED 'ISSUED FOR CONSTRUCTION'.
4. DO NOT SCALE FROM THIS DRAWING.
5. THE COMPANY OPERATES USING METRIC DIMENSIONS AS THE PRINCIPAL DENOMINATION.
6. ALL CONCRETE WORKS ARE OUTSIDE OF THE SCOPE OF THE COMPANY. INFORMATION REGARDING SLAB DESIGN AND CONNECTIONS IN THESE DRAWINGS ARE INTENDED FOR GUIDANCE ONLY. FOUNDATION AND SLAB WORKS SHOULD BE DESIGNED AND APPROVED BY A LOCAL STRUCTURAL ENGINEER.
7. THE COMPANY RETAINS FULL TITLE AND OWNERSHIP OF THESE PLANS AND DESIGNS. ANY UNAUTHORISED USE, REPRODUCTION, OR DISTRIBUTION OF THESE PLANS, WHETHER IN WHOLE OR PART, IS EXPRESSLY PROHIBITED WITHOUT PRIOR WRITTEN CONSENT.

No.	Revision	Date

ISSUED FOR:


- Issued for information
- Issued for client approval
- Issued for fabrication
- Issued for construction

Angel

DRAWING TITLE:	3D Views
DRAWN BY:	Yonca A.Clark
SCALE:	
DRAWING NO:	A102
DATE:	01/05/2024



Bedroom-
Bathroom Section
View

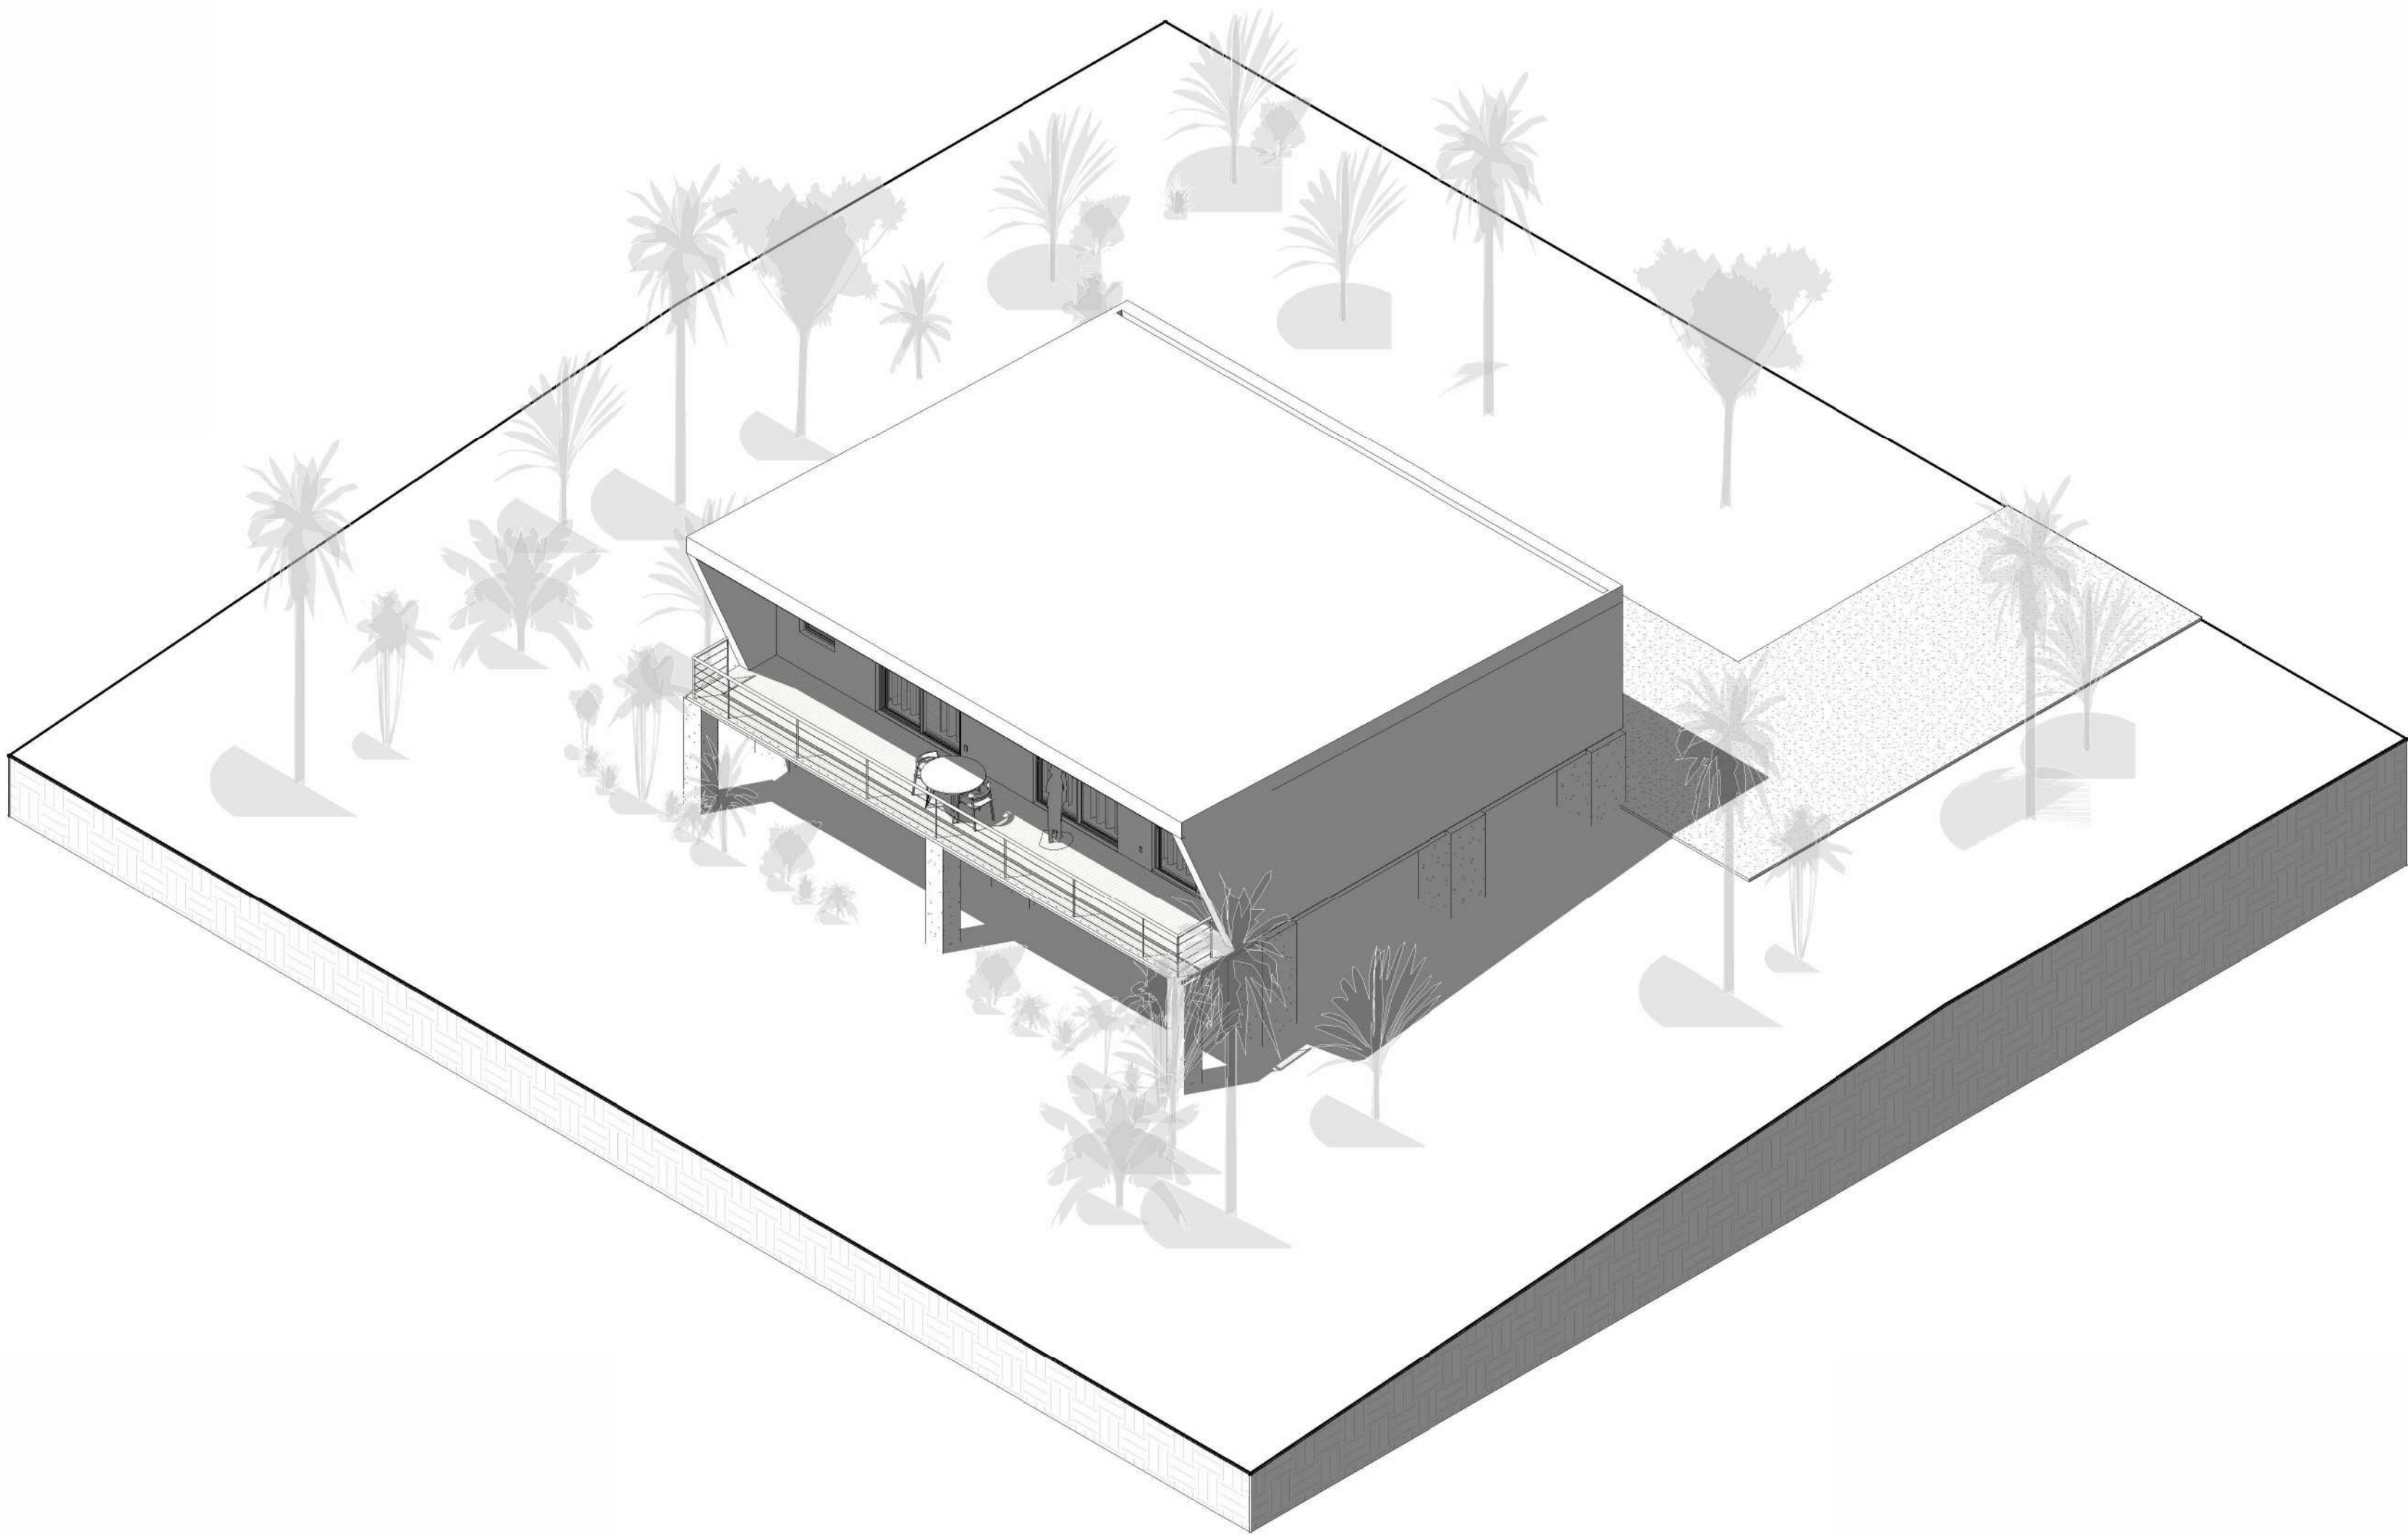

1. THESE DRAWINGS MUST BE CHECKED BY THE CUSTOMER OR CONTRACTOR PRIOR TO APPROVAL. ANY ERRORS OR OMISSIONS MUST BE REPORTED IN WRITING TO BAUHU PRIOR TO COMMENCEMENT OF CONSTRUCTION.
2. ARCHITECTURAL DRAWINGS SHOULD BE READ IN CONJUNCTION WITH STRUCTURAL DETAILING AND FABRICATION GENERAL ASSEMBLY DRAWINGS.
3. FOR CONSTRUCTION PURPOSES, USE ONLY THE LATEST APPROVED DRAWINGS LABELED 'ISSUED FOR CONSTRUCTION'.
4. DO NOT SCALE FROM THIS DRAWING.
5. THE COMPANY OPERATES USING METRIC DIMENSIONS AS THE PRINCIPAL DENOMINATION.
6. ALL CONCRETE WORKS ARE OUTSIDE OF THE SCOPE OF THE COMPANY. INFORMATION REGARDING SLAB DESIGN AND CONNECTIONS IN THESE DRAWINGS ARE INTENDED FOR GUIDENCE ONLY. FOUNDATION AND SLAB WORKS SHOULD BE DESIGNED AND APPROVED BY A LOCAL STRUCTURAL ENGINEER.
7. THE COMPANY RETAINS FULL TITLE AND OWNERSHIP OF THESE PLANS AND DESIGNS. ANY UNAUTHORISED USE, REPRODUCTION, OR DISTRIBUTION OF THESE PLANS, WHETHER IN WHOLE OR PART, IS EXPRESSLY PROHIBITED WITHOUT PRIOR WRITTEN CONSENT.

No.	Revision	Date

ISSUED FOR:

Issued for information


Issued for client approval

Issued for fabrication

Issued for construction

Angel

DRAWING TITLE:	Building Axonometry
DRAWN BY:	Yonca A.Clark
SCALE:	
DRAWING NO:	A103
DATE:	01/05/2024

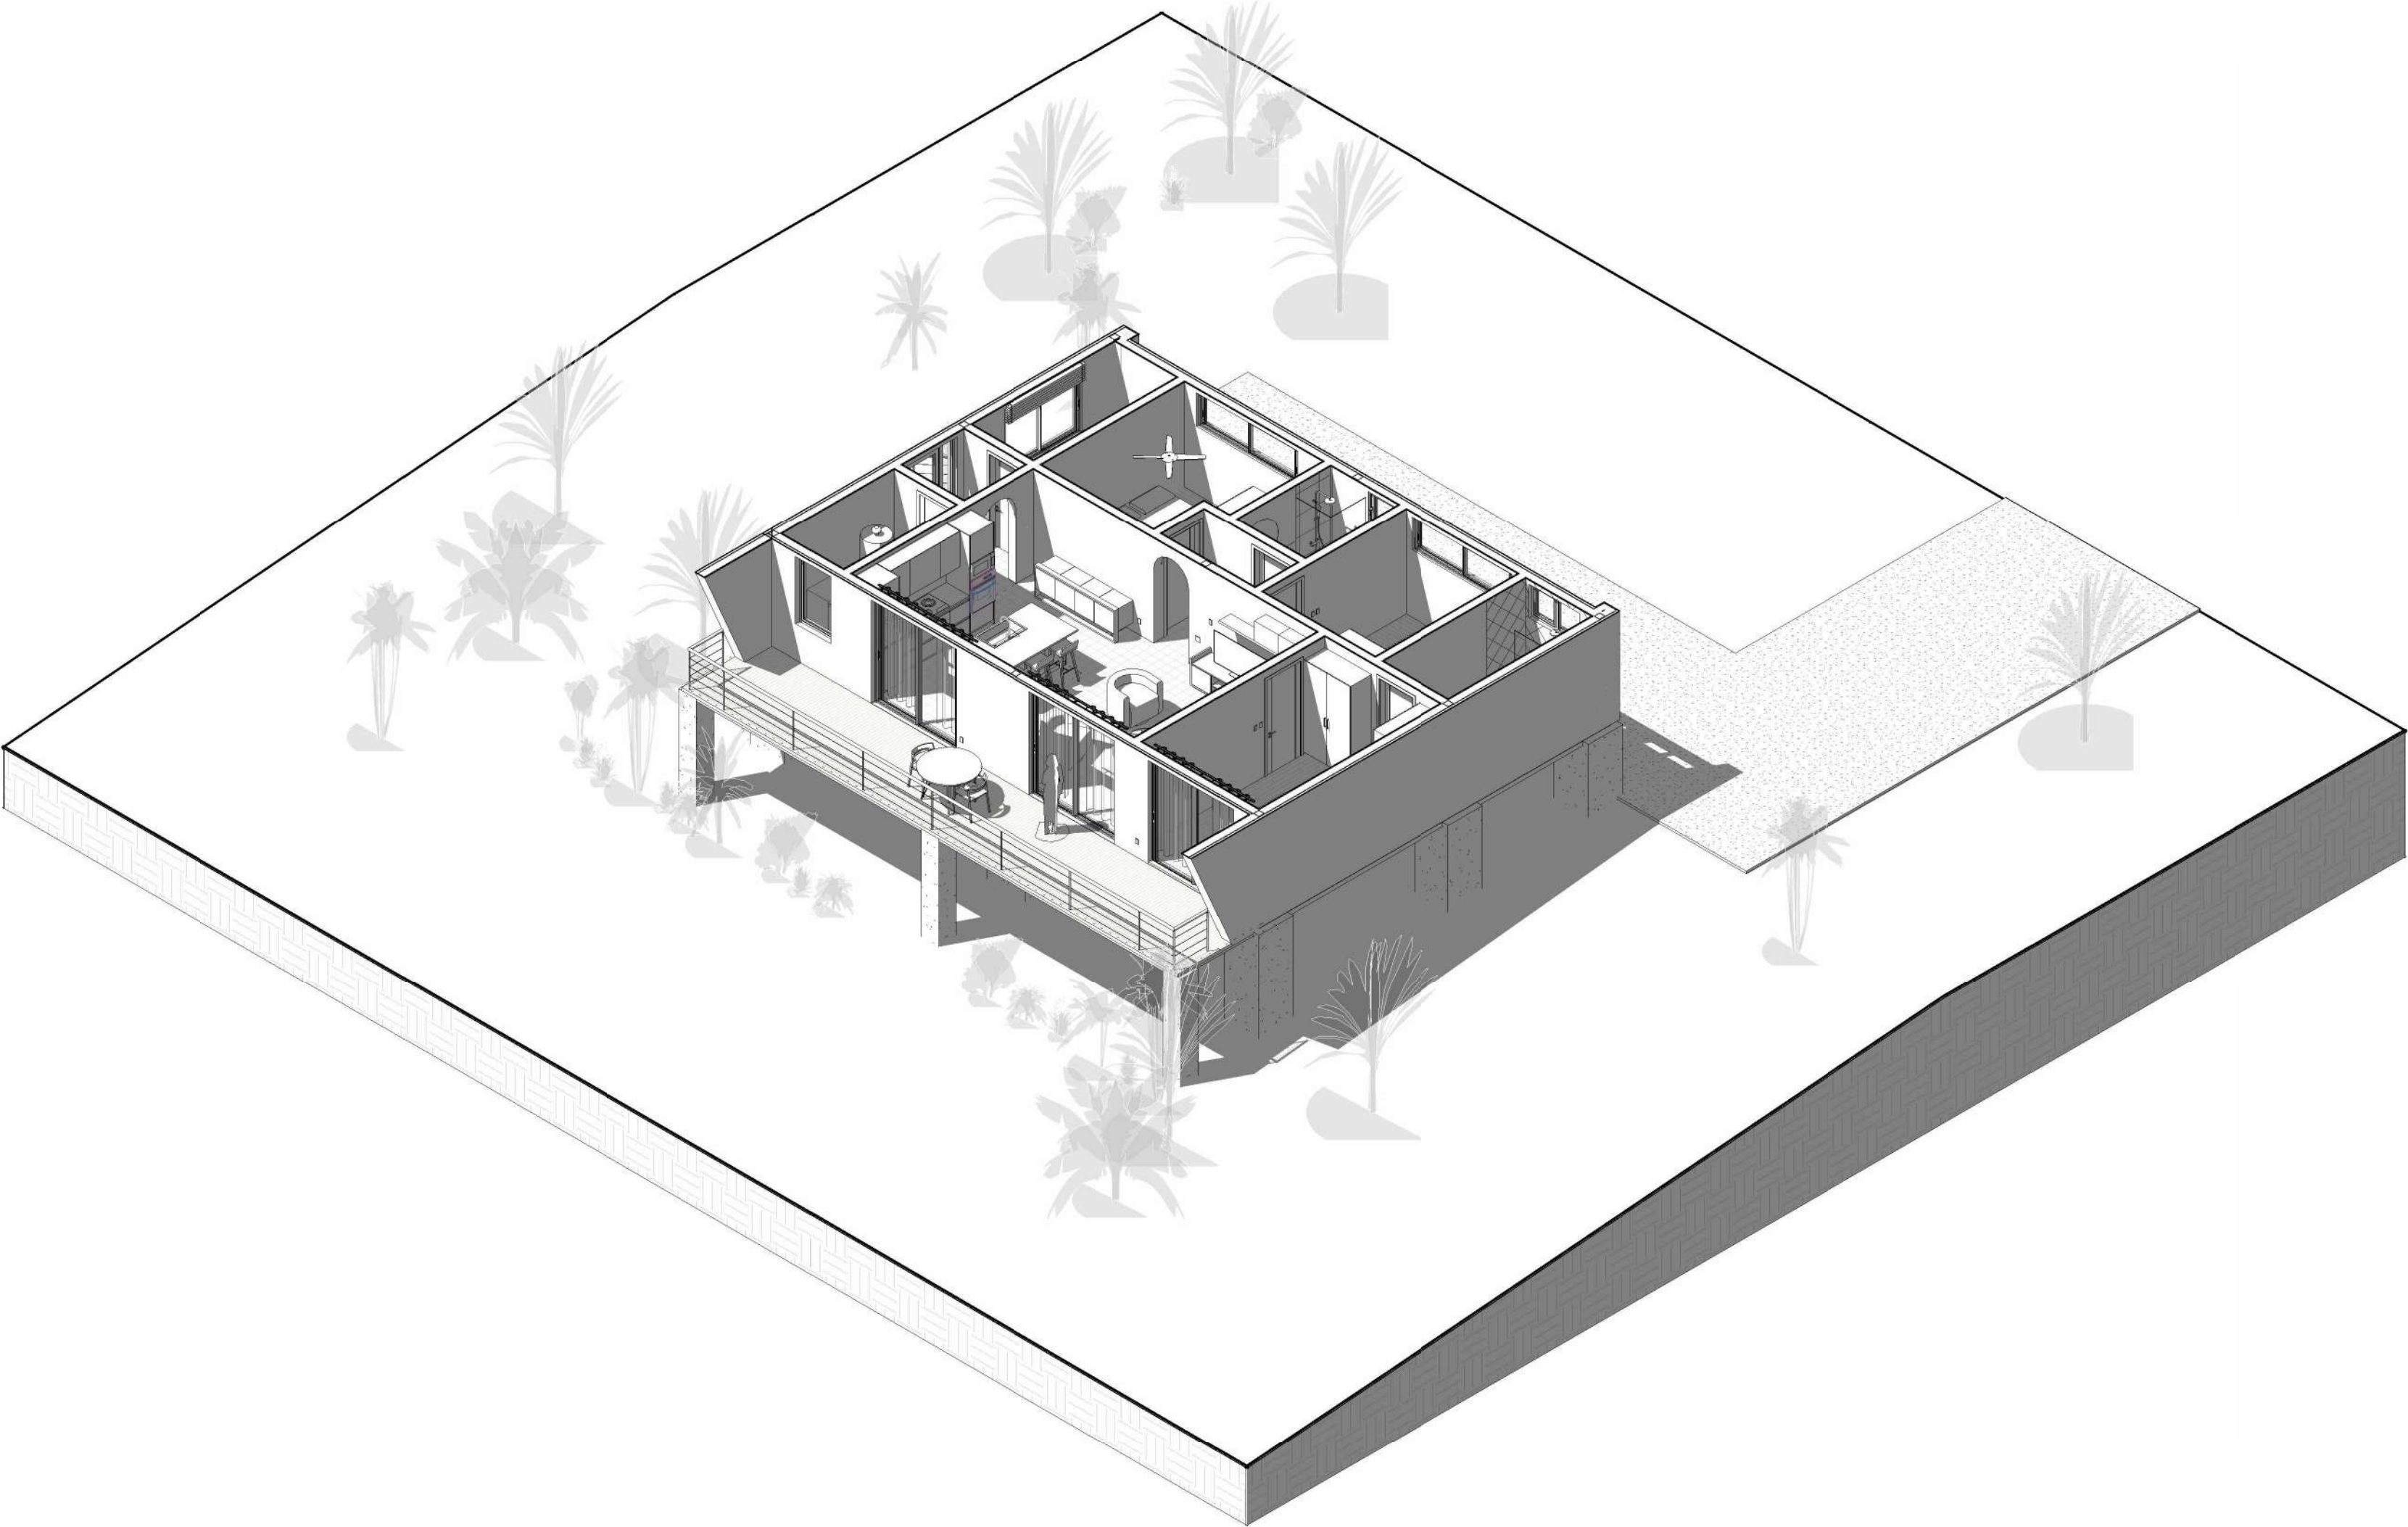

1. THESE DRAWINGS MUST BE CHECKED BY THE CUSTOMER OR CONTRACTOR PRIOR TO APPROVAL. ANY ERRORS OR OMISSIONS MUST BE REPORTED IN WRITING TO BAUHU PRIOR TO COMMENCEMENT OF CONSTRUCTION.
2. ARCHITECTURAL DRAWINGS SHOULD BE READ IN CONJUNCTION WITH STRUCTURAL DETAILING AND FABRICATION GENERAL ASSEMBLY DRAWINGS.
3. FOR CONSTRUCTION PURPOSES, USE ONLY THE LATEST APPROVED DRAWINGS LABELED 'ISSUED FOR CONSTRUCTION'.
4. DO NOT SCALE FROM THIS DRAWING.
5. THE COMPANY OPERATES USING METRIC DIMENSIONS AS THE PRINCIPAL DENOMINATION.
6. ALL CONCRETE WORKS ARE OUTSIDE OF THE SCOPE OF THE COMPANY. INFORMATION REGARDING SLAB DESIGN AND CONNECTIONS IN THESE DRAWINGS ARE INTENDED FOR GUIDENCE ONLY. FOUNDATION AND SLAB WORKS SHOULD BE DESIGNED AND APPROVED BY A LOCAL STRUCTURAL ENGINEER.
7. THE COMPANY RETAINS FULL TITLE AND OWNERSHIP OF THESE PLANS AND DESIGNS. ANY UNAUTHORISED USE, REPRODUCTION, OR DISTRIBUTION OF THESE PLANS, WHETHER IN WHOLE OR PART, IS EXPRESSLY PROHIBITED WITHOUT PRIOR WRITTEN CONSENT.

No.	Revision	Date

ISSUED FOR:

Issued for information

Issued for client approval

Issued for fabrication

Issued for construction

Angel

DRAWING TITLE:	Ground Floor Axo.
DRAWN BY:	Yonca A.Clark
SCALE:	
DRAWING NO:	A104
DATE:	01/05/2024

1. THESE DRAWINGS MUST BE CHECKED BY THE CUSTOMER OR CONTRACTOR PRIOR TO APPROVAL. ANY ERRORS OR OMISSIONS MUST BE REPORTED IN WRITING TO BAUHU PRIOR TO COMMENCEMENT OF CONSTRUCTION.
2. ARCHITECTURAL DRAWINGS SHOULD BE READ IN CONJUNCTION WITH STRUCTURAL DETAILING AND FABRICATION GENERAL ASSEMBLY DRAWINGS.
3. FOR CONSTRUCTION PURPOSES, USE ONLY THE LATEST APPROVED DRAWINGS LABELED 'ISSUED FOR CONSTRUCTION'.
4. DO NOT SCALE FROM THIS DRAWING.
5. THE COMPANY OPERATES USING METRIC DIMENSIONS AS THE PRINCIPAL DENOMINATION.
6. ALL CONCRETE WORKS ARE OUTSIDE OF THE SCOPE OF THE COMPANY. INFORMATION REGARDING SLAB DESIGN AND CONNECTIONS IN THESE DRAWINGS ARE INTENDED FOR GUIDANCE ONLY. FOUNDATION AND SLAB WORKS SHOULD BE DESIGNED AND APPROVED BY A LOCAL STRUCTURAL ENGINEER.
7. THE COMPANY RETAINS FULL TITLE AND OWNERSHIP OF THESE PLANS AND DESIGNS. ANY UNAUTHORISED USE, REPRODUCTION, OR DISTRIBUTION OF THESE PLANS, WHETHER IN WHOLE OR PART, IS EXPRESSLY PROHIBITED WITHOUT PRIOR WRITTEN CONSENT.

No.	Revision	Date

ISSUED FOR:

Issued for information

Issued for client approval

Issued for fabrication

Issued for construction

Angel

DRAWING TITLE:

Floor Plan

DRAWN BY:

Yonca A.Clark

SCALE:


1 : 50

DRAWING NO:

A108

DATE:

01/05/2024

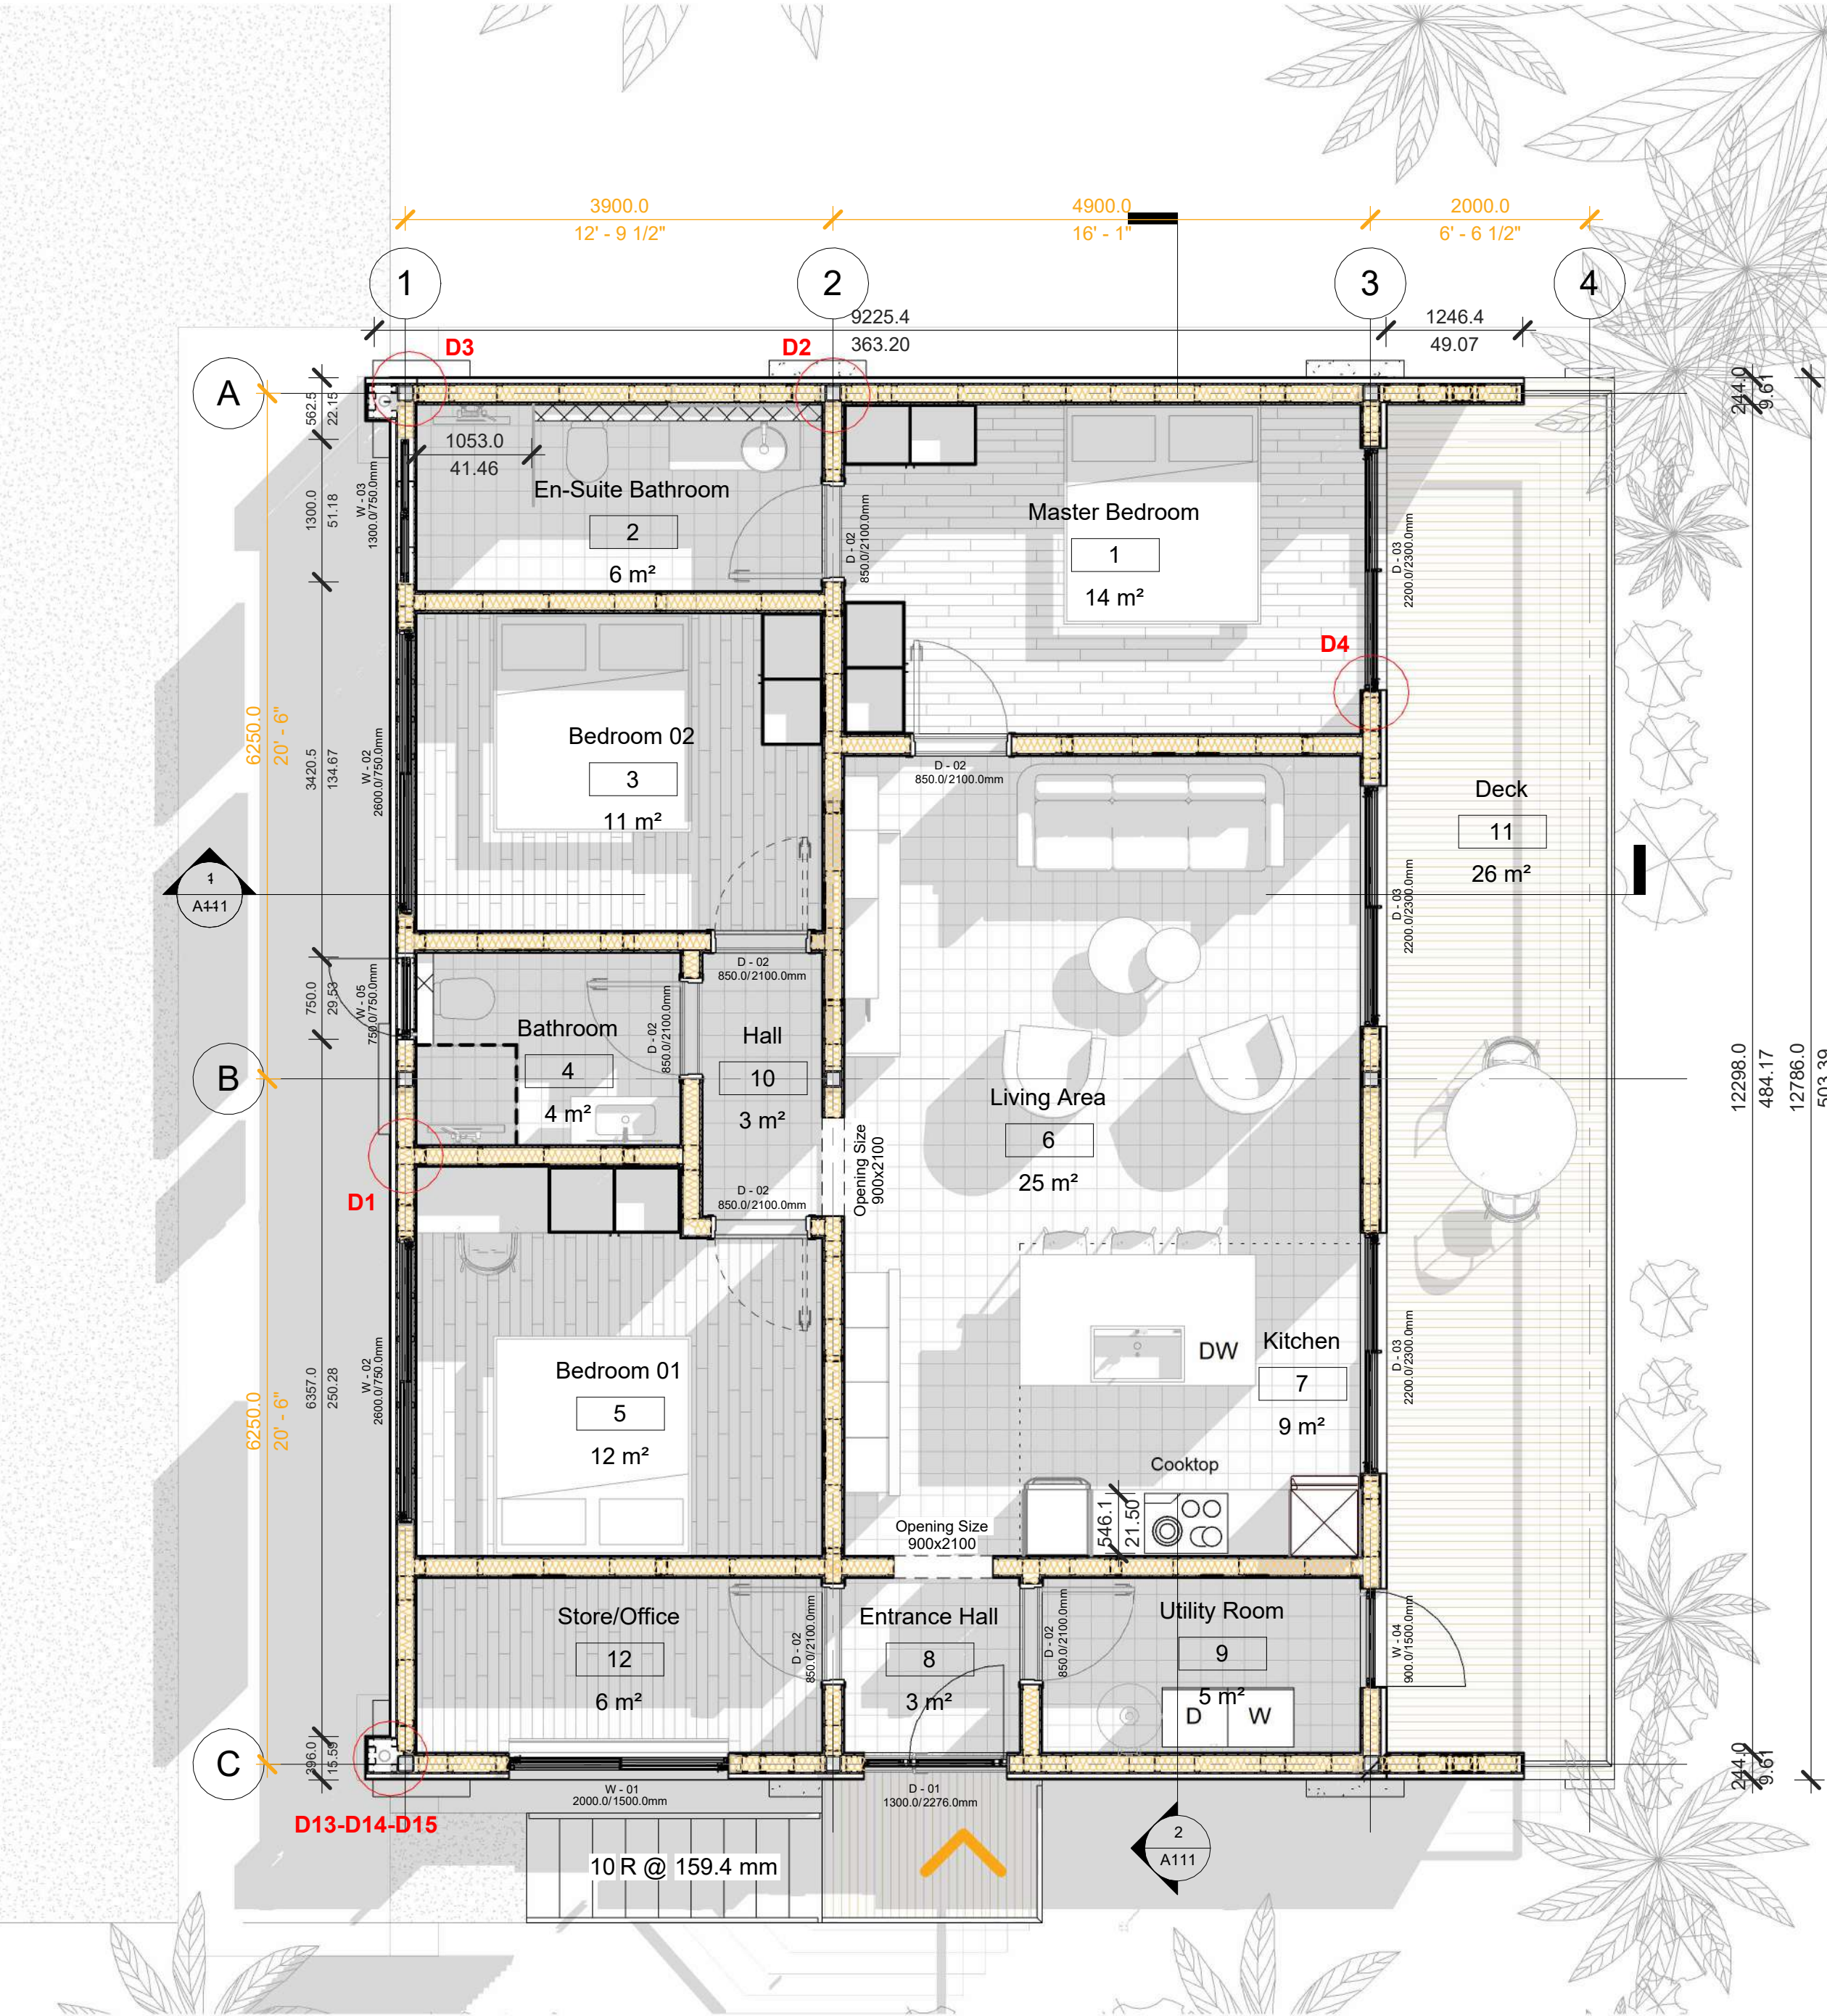

Note:

- Freestanding furniture and equipment is shown for illustrative purposes only
- External railings and handrails to be provided by the general contractor to confirmed site dimensions

1. THESE DRAWINGS MUST BE CHECKED BY THE CUSTOMER OR CONTRACTOR PRIOR TO APPROVAL. ANY ERRORS OR OMISSIONS MUST BE REPORTED IN WRITING TO BAUHU PRIOR TO COMMENCEMENT OF CONSTRUCTION.
2. ARCHITECTURAL DRAWINGS SHOULD BE READ IN CONJUNCTION WITH STRUCTURAL DETAILING AND FABRICATION GENERAL ASSEMBLY DRAWINGS.
3. FOR CONSTRUCTION PURPOSES, USE ONLY THE LATEST APPROVED DRAWINGS LABELED 'ISSUED FOR CONSTRUCTION'.
4. DO NOT SCALE FROM THIS DRAWING.
5. THE COMPANY OPERATES USING METRIC DIMENSIONS AS THE PRINCIPAL DENOMINATION.
6. ALL CONCRETE WORKS ARE OUTSIDE OF THE SCOPE OF THE COMPANY. INFORMATION REGARDING SLAB DESIGN AND CONNECTIONS IN THESE DRAWINGS ARE INTENDED FOR GUIDANCE ONLY. FOUNDATION AND SLAB WORKS SHOULD BE DESIGNED AND APPROVED BY A LOCAL STRUCTURAL ENGINEER.
7. THE COMPANY RETAINS FULL TITLE AND OWNERSHIP OF THESE PLANS AND DESIGNS. ANY UNAUTHORIZED USE, REPRODUCTION, OR DISTRIBUTION OF THESE PLANS, WHETHER IN WHOLE OR PART, IS EXPRESSLY PROHIBITED WITHOUT PRIOR WRITTEN CONSENT.

No.	Revision	Date

ISSUED FOR:

Issued for information

Issued for client approval

Issued for fabrication

Issued for construction

Angel

DRAWING TITLE:

Elevations

DRAWN BY:

Yonca A.Clark

SCALE:


1 : 50

DRAWING NO:

A109


DATE:

01/05/2024

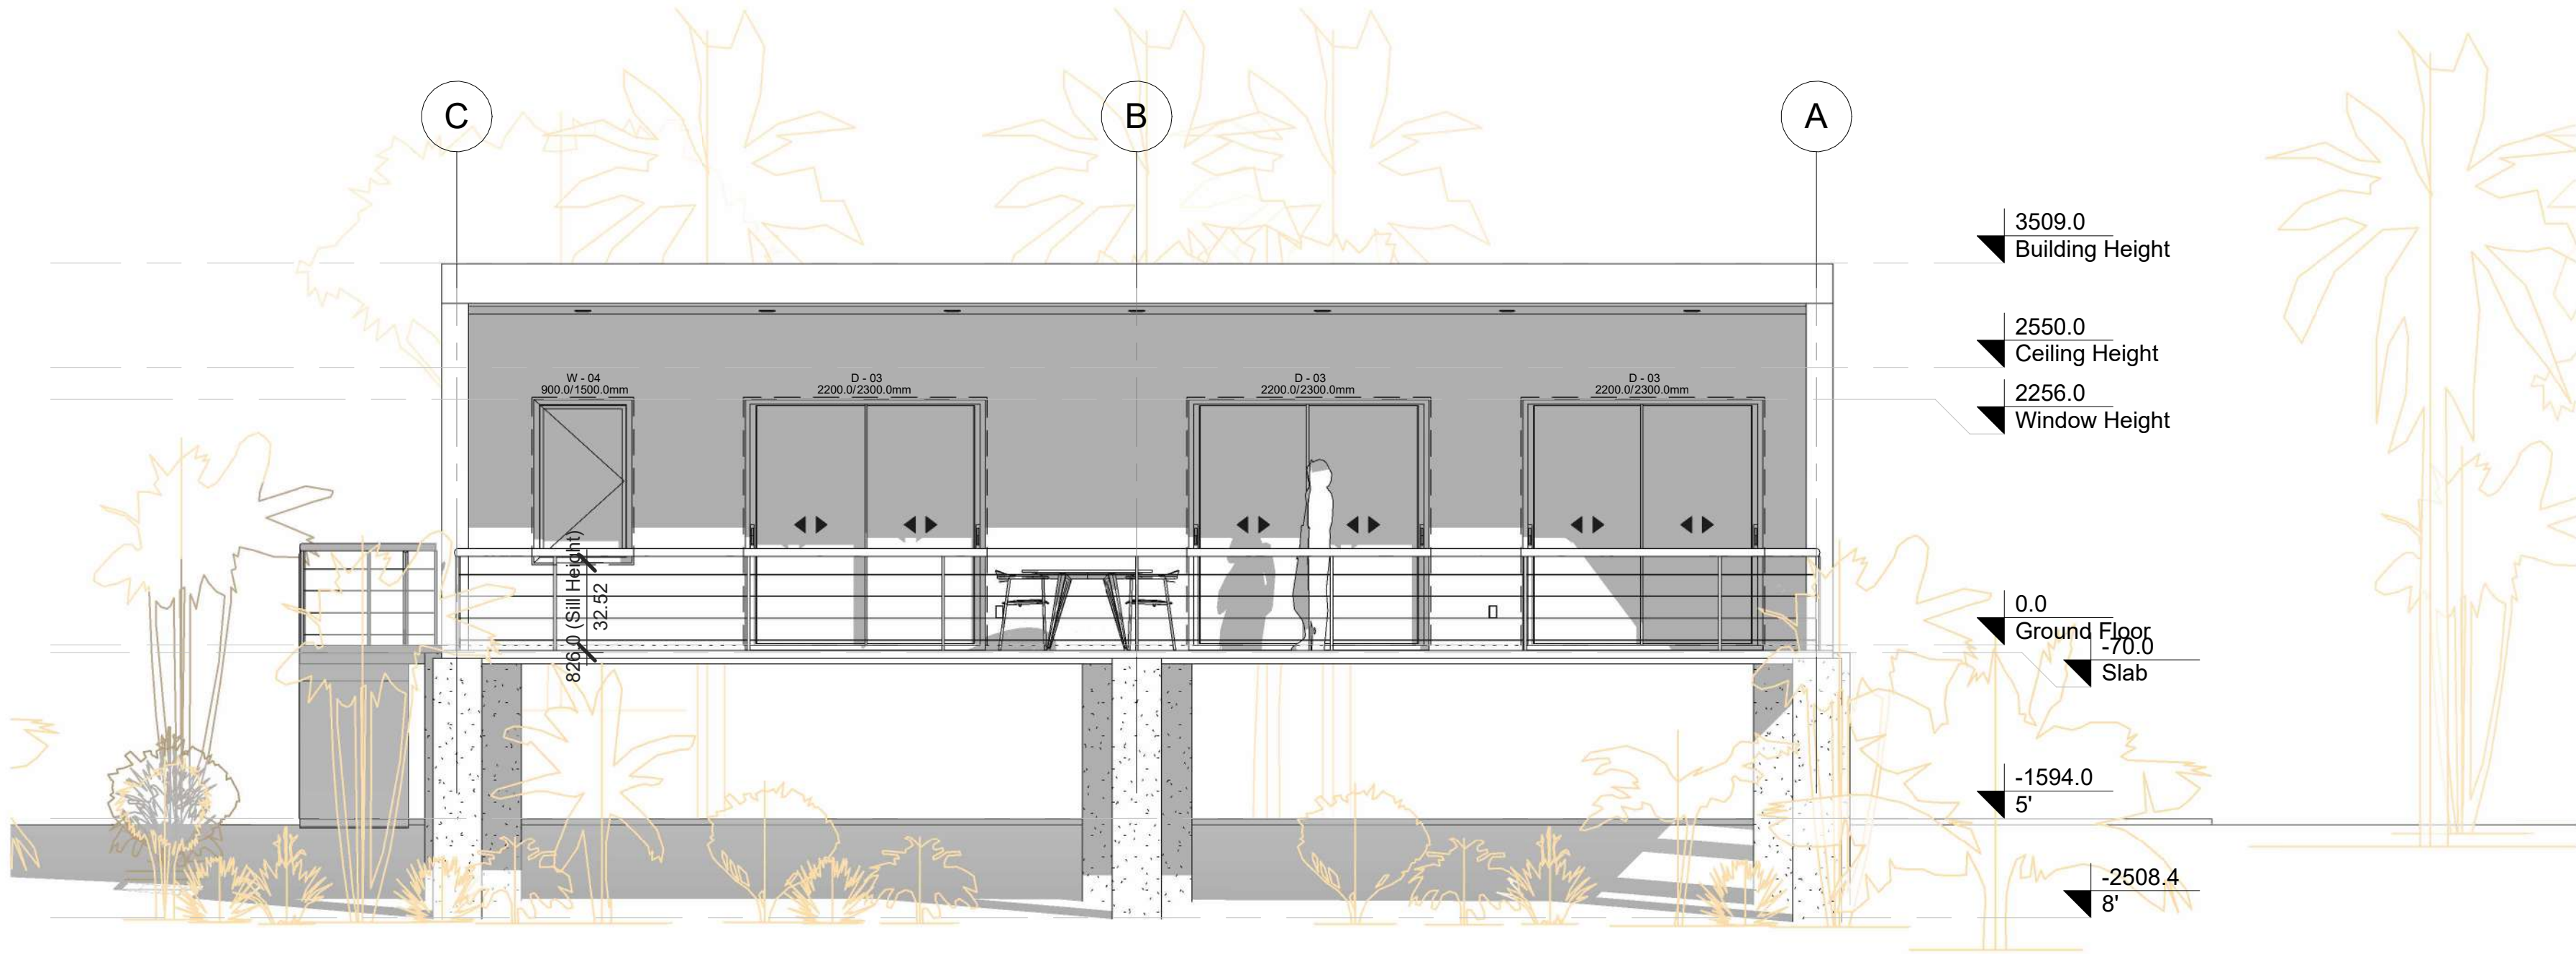


Front Elevation

1 : 50

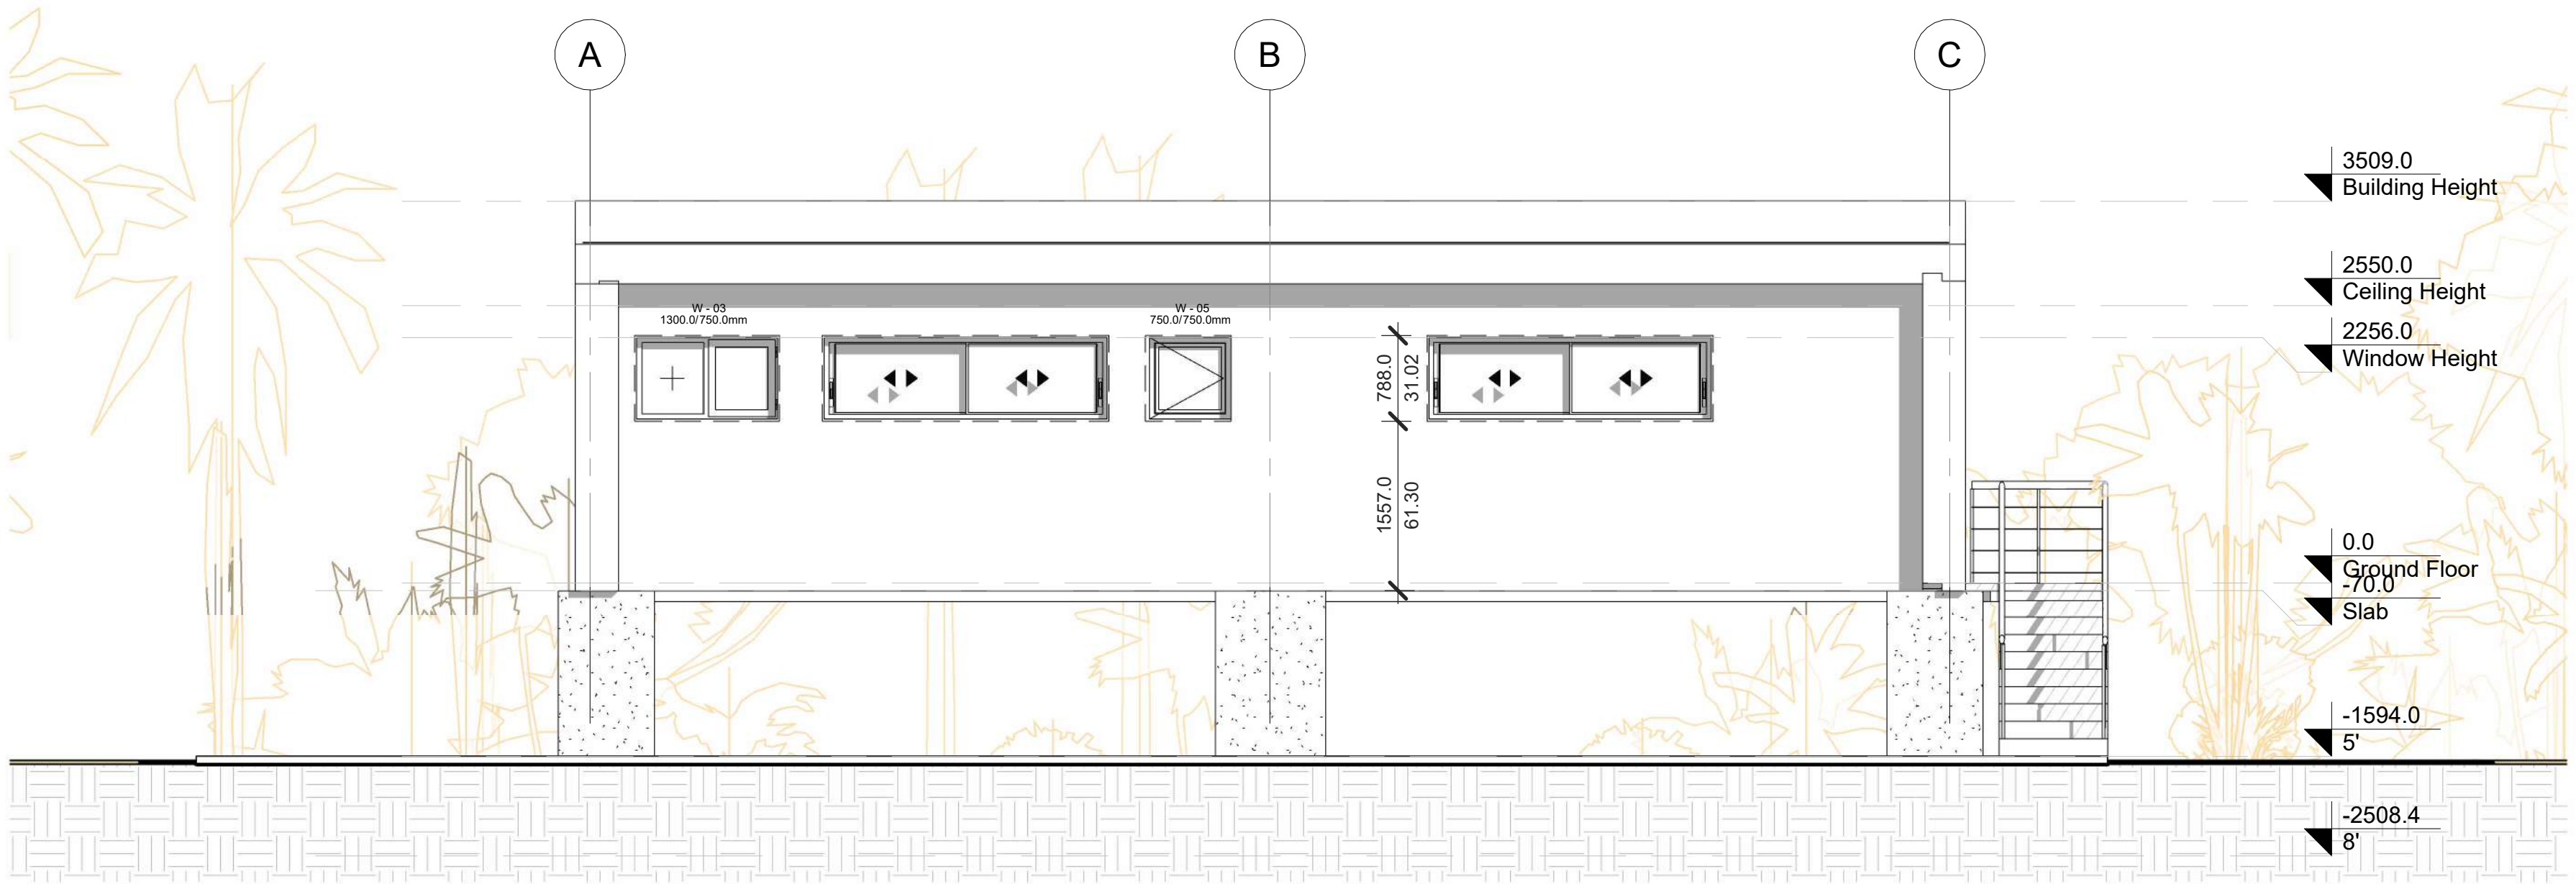


Back Elevation

1 : 50

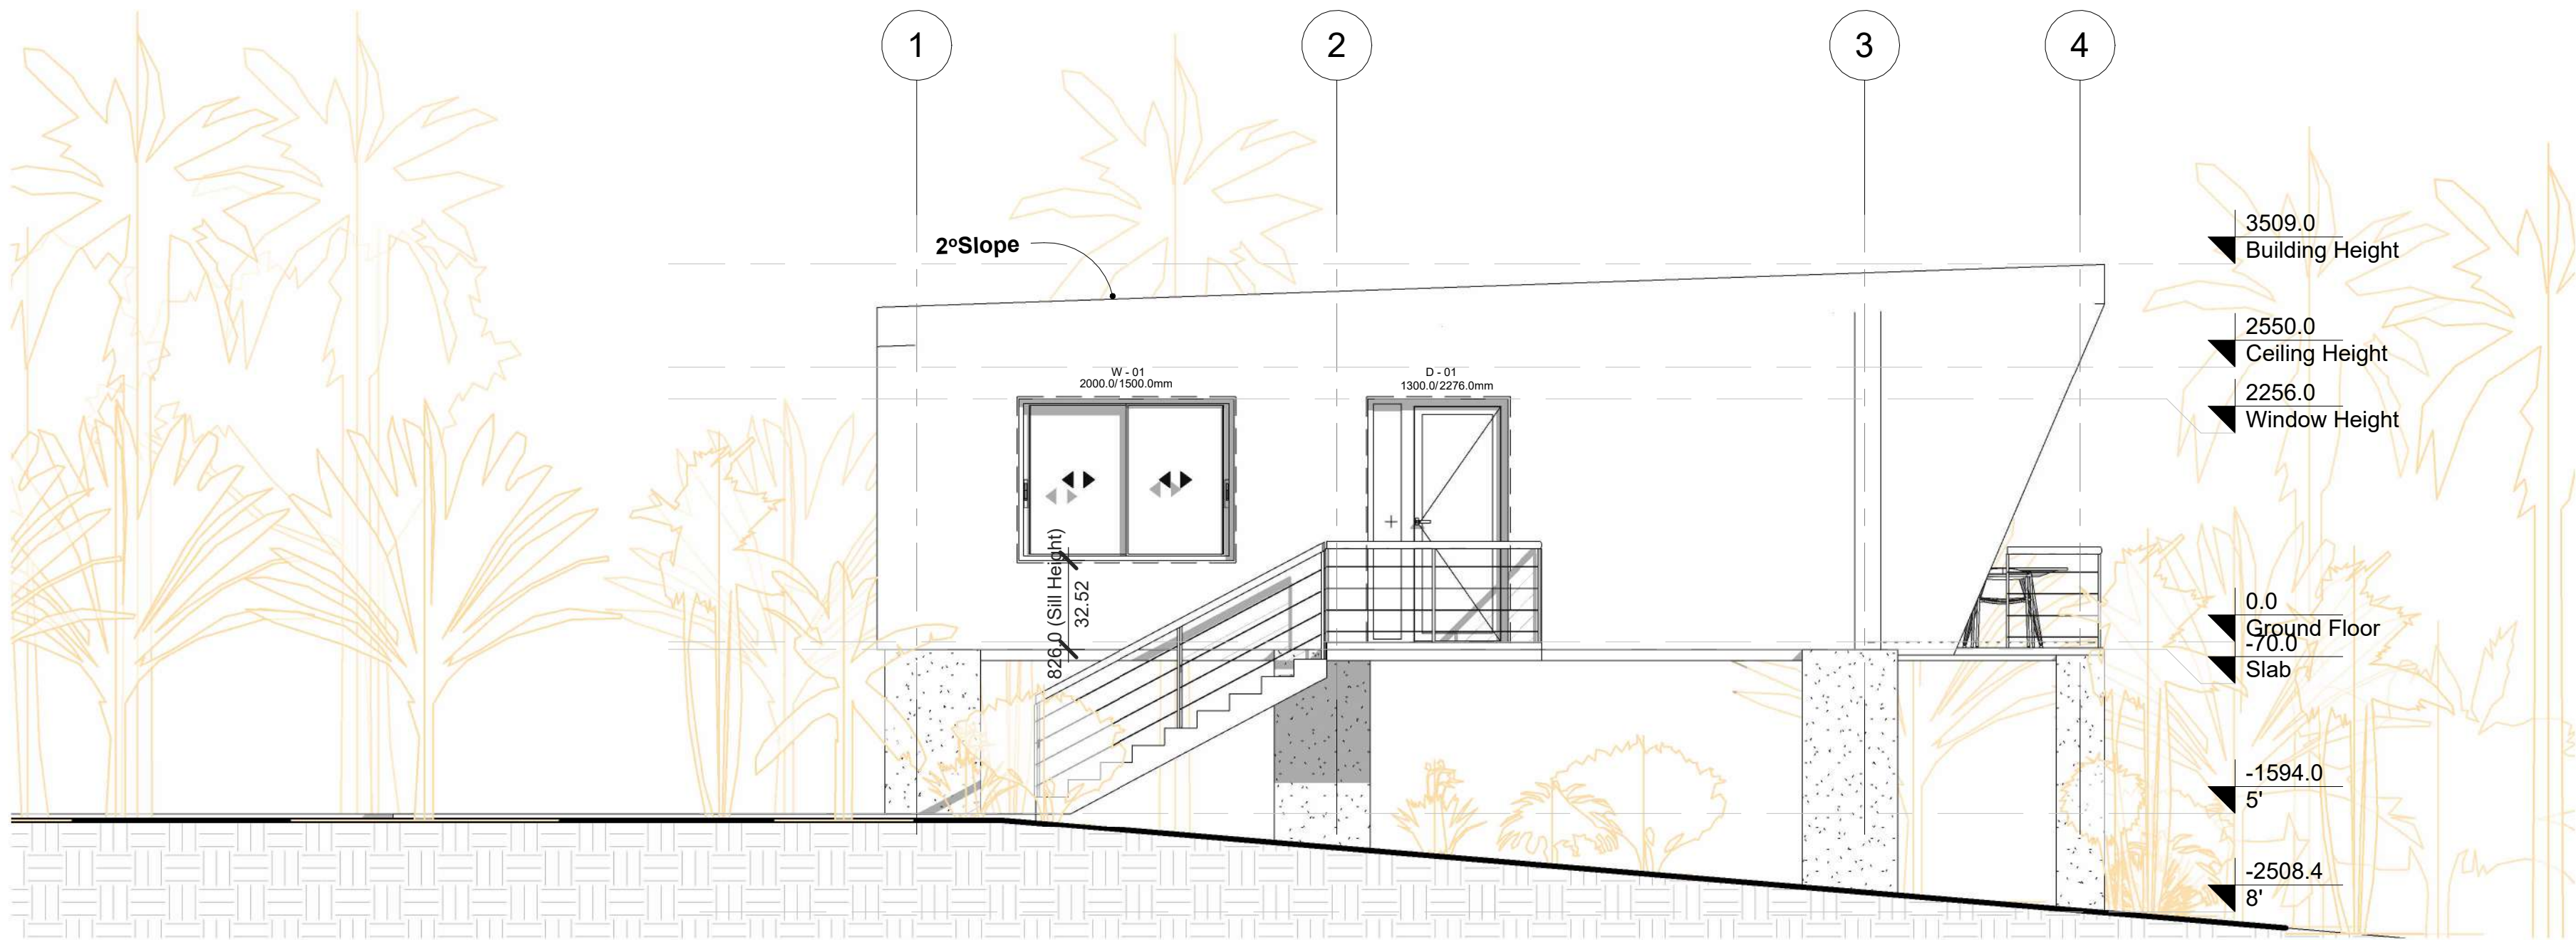

3 Left Elevation
1 : 50

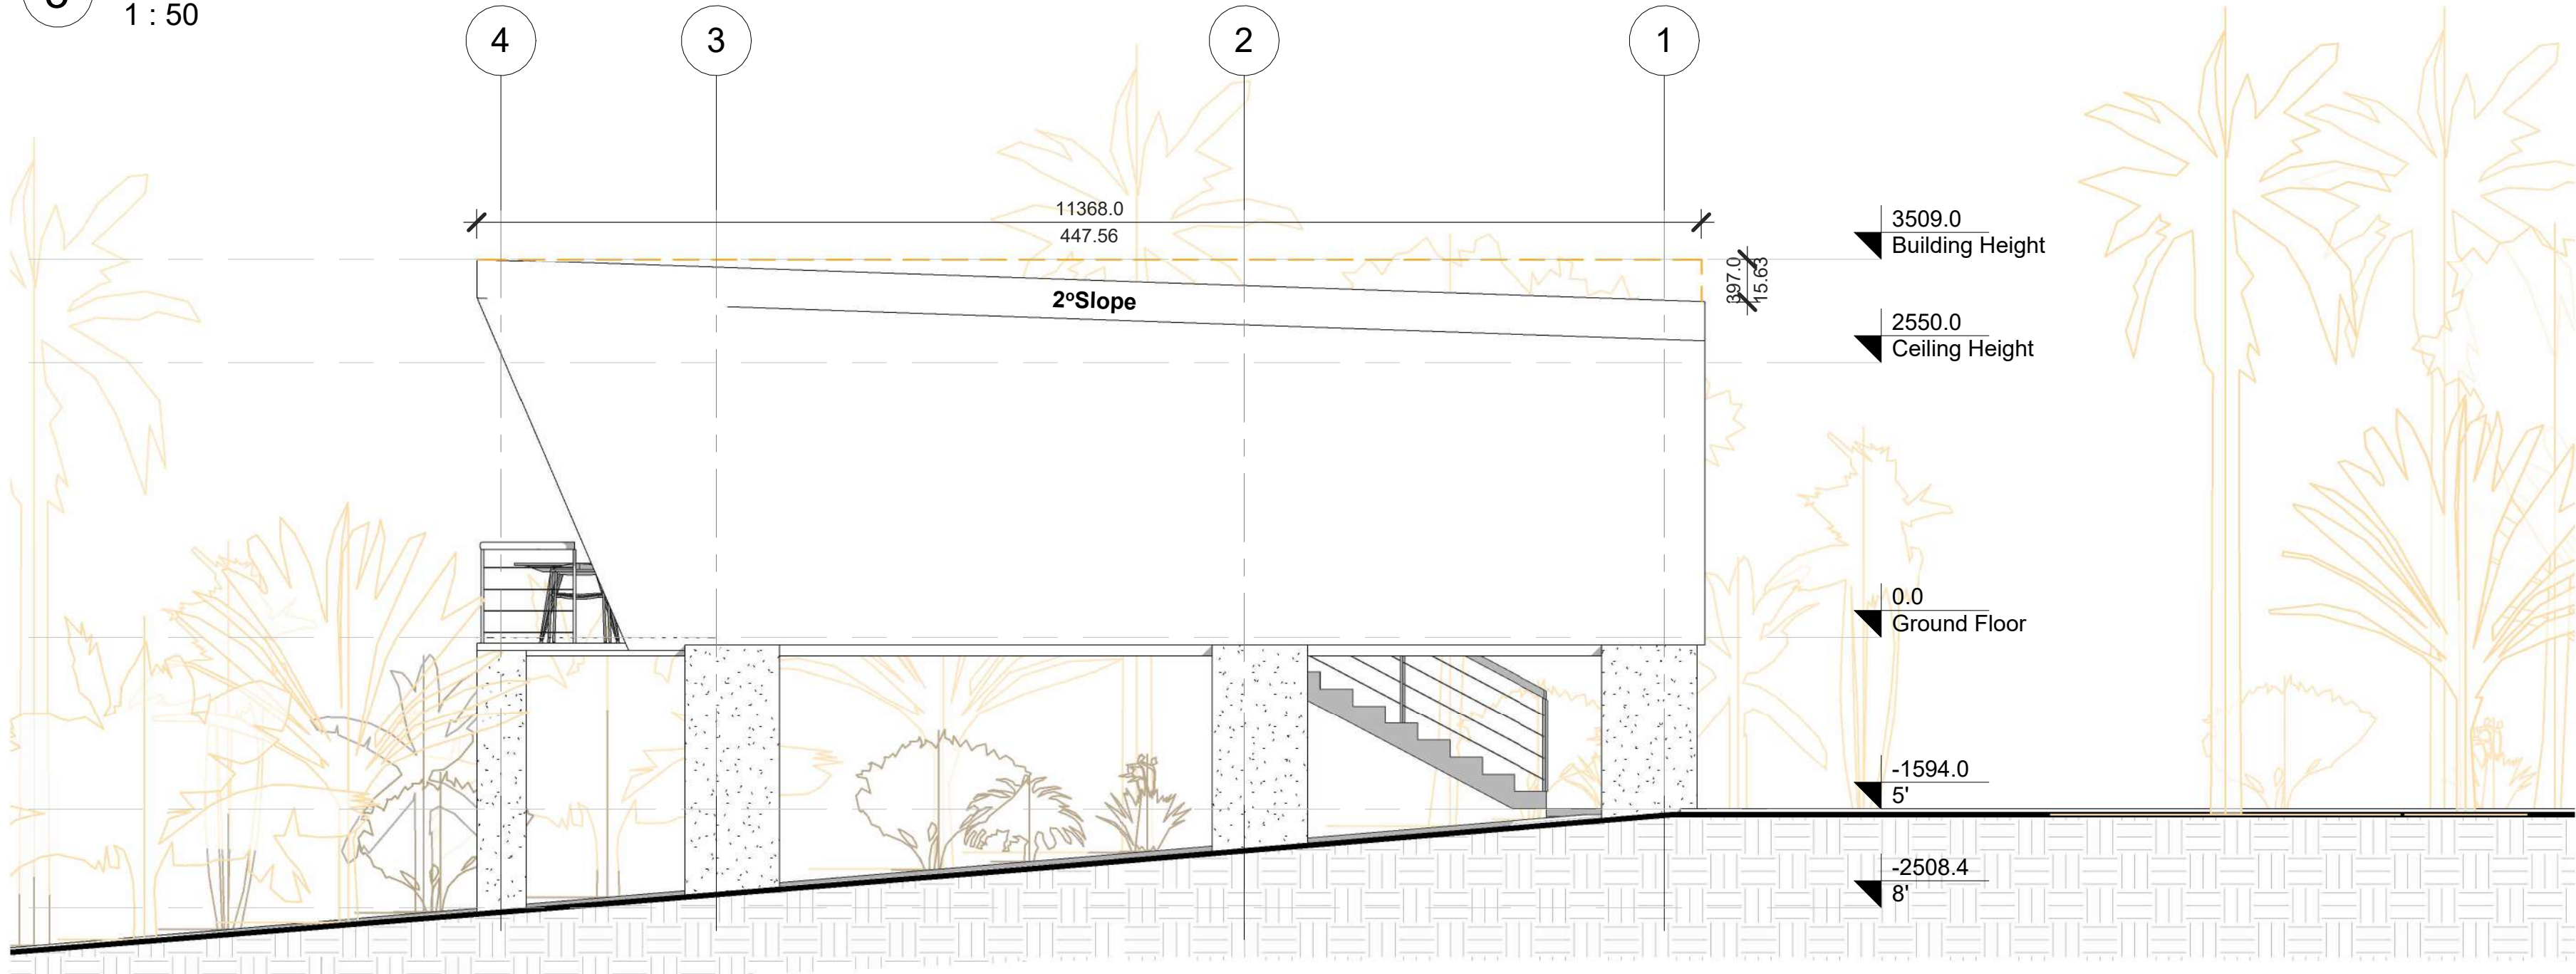

2 Right Elevation
1 : 50

1. THESE DRAWINGS MUST BE CHECKED BY THE CUSTOMER OR CONTRACTOR PRIOR TO APPROVAL. ANY ERRORS OR OMISSIONS MUST BE REPORTED IN WRITING TO BAUHU PRIOR TO COMMENCEMENT OF CONSTRUCTION.
2. ARCHITECTURAL DRAWINGS SHOULD BE READ IN CONJUNCTION WITH STRUCTURAL DETAILING AND FABRICATION GENERAL ASSEMBLY DRAWINGS.
3. FOR CONSTRUCTION PURPOSES, USE ONLY THE LATEST APPROVED DRAWINGS LABELED 'ISSUED FOR CONSTRUCTION'.
4. DO NOT SCALE FROM THIS DRAWING.
5. THE COMPANY OPERATES USING METRIC DIMENSIONS AS THE PRINCIPAL DENOMINATION.
6. ALL CONCRETE WORKS ARE OUTSIDE OF THE SCOPE OF THE COMPANY. INFORMATION REGARDING SLAB DESIGN AND CONNECTIONS IN THESE DRAWINGS ARE INTENDED FOR GUIDANCE ONLY. FOUNDATION AND SLAB WORKS SHOULD BE DESIGNED AND APPROVED BY A LOCAL STRUCTURAL ENGINEER.
7. THE COMPANY RETAINS FULL TITLE AND OWNERSHIP OF THESE PLANS AND DESIGNS. ANY UNAUTHORISED USE, REPRODUCTION, OR DISTRIBUTION OF THESE PLANS, WHETHER IN WHOLE OR PART, IS EXPRESSLY PROHIBITED WITHOUT PRIOR WRITTEN CONSENT.

No.	Revision	Date

ISSUED FOR:

- Issued for information
Issued for client approval
Issued for fabrication
Issued for construction

Angel

DRAWING TITLE:

Elevations

DRAWN BY:

Yonca A.Clark

SCALE:

1 : 50

DRAWING NO:

A110

DATE:

01/05/2024

1. THESE DRAWINGS MUST BE CHECKED BY THE CUSTOMER OR CONTRACTOR PRIOR TO APPROVAL. ANY ERRORS OR OMISSIONS MUST BE REPORTED IN WRITING TO BAUHU PRIOR TO COMMENCEMENT OF CONSTRUCTION.
2. ARCHITECTURAL DRAWINGS SHOULD BE READ IN CONJUNCTION WITH STRUCTURAL DETAILING AND FABRICATION GENERAL ASSEMBLY DRAWINGS.
3. FOR CONSTRUCTION PURPOSES, USE ONLY THE LATEST APPROVED DRAWINGS LABELED 'ISSUED FOR CONSTRUCTION'.
4. DO NOT SCALE FROM THIS DRAWING.
5. THE COMPANY OPERATES USING METRIC DIMENSIONS AS THE PRINCIPAL DENOMINATION.
6. ALL CONCRETE WORKS ARE OUTSIDE OF THE SCOPE OF THE COMPANY. INFORMATION REGARDING SLAB DESIGN AND CONNECTIONS IN THESE DRAWINGS ARE INTENDED FOR GUIDANCE ONLY. FOUNDATION AND SLAB WORKS SHOULD BE DESIGNED AND APPROVED BY A LOCAL STRUCTURAL ENGINEER.
7. THE COMPANY RETAINS FULL TITLE AND OWNERSHIP OF THESE PLANS AND DESIGNS. ANY UNAUTHORISED USE, REPRODUCTION, OR DISTRIBUTION OF THESE PLANS, WHETHER IN WHOLE OR PART, IS EXPRESSLY PROHIBITED WITHOUT PRIOR WRITTEN CONSENT.

No.	Revision	Date

ISSUED FOR:

Issued for information

Issued for client approval

Issued for fabrication

Issued for construction

Angel

DRAWING TITLE:

Sections

DRAWN BY:

Yonca A.Clark

SCALE:



1 : 50

DRAWING NO:

A111

DATE:

01/05/2024

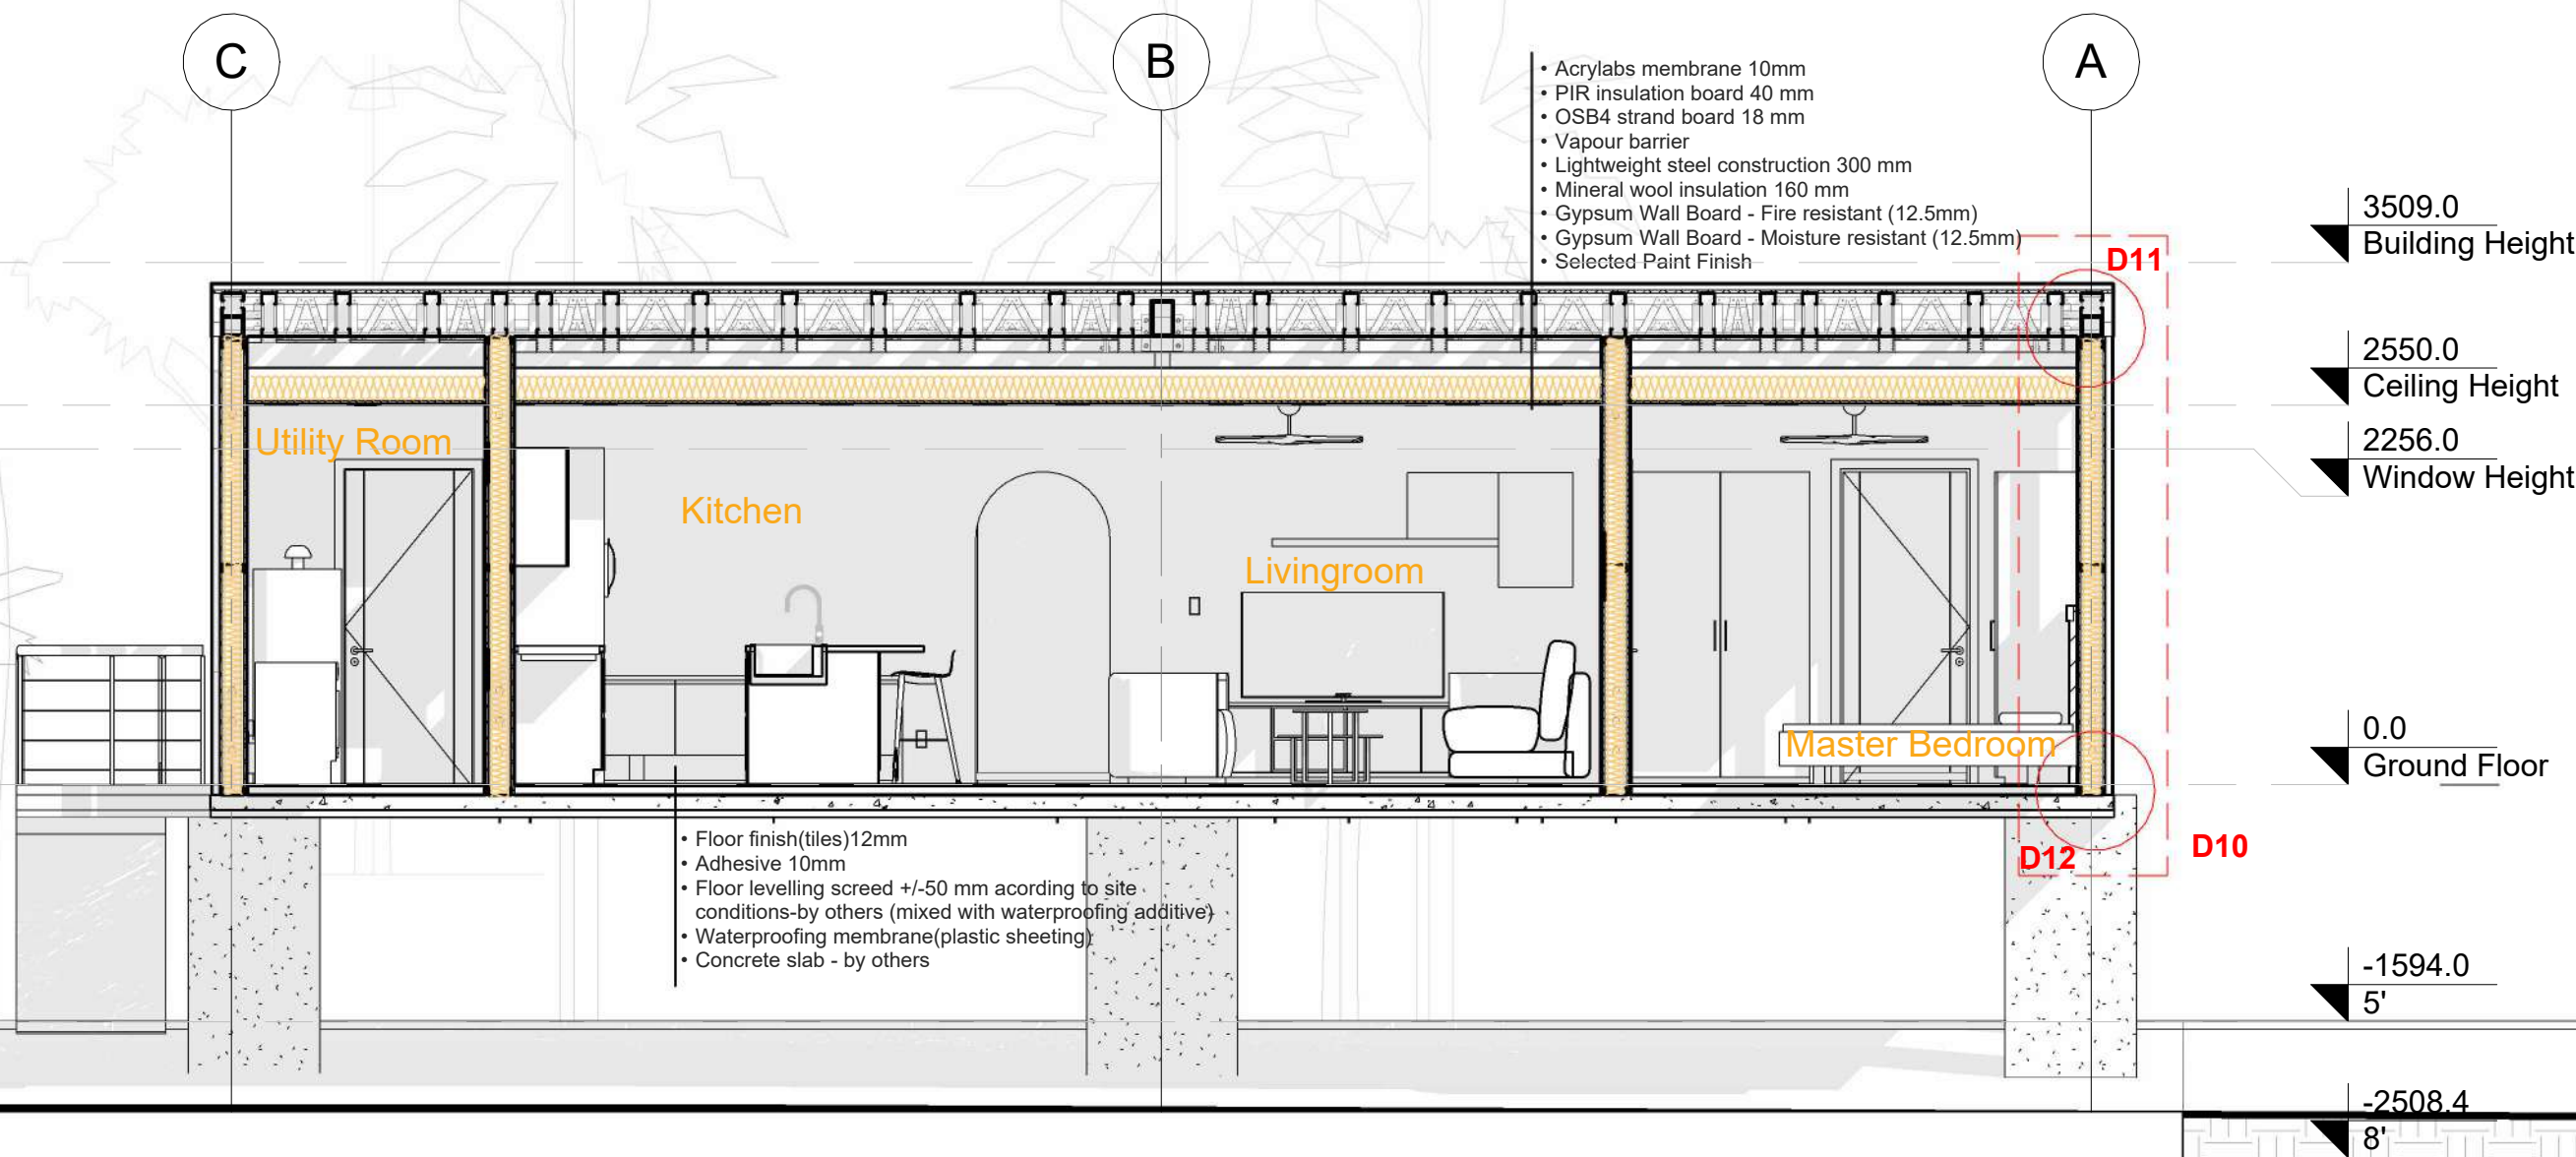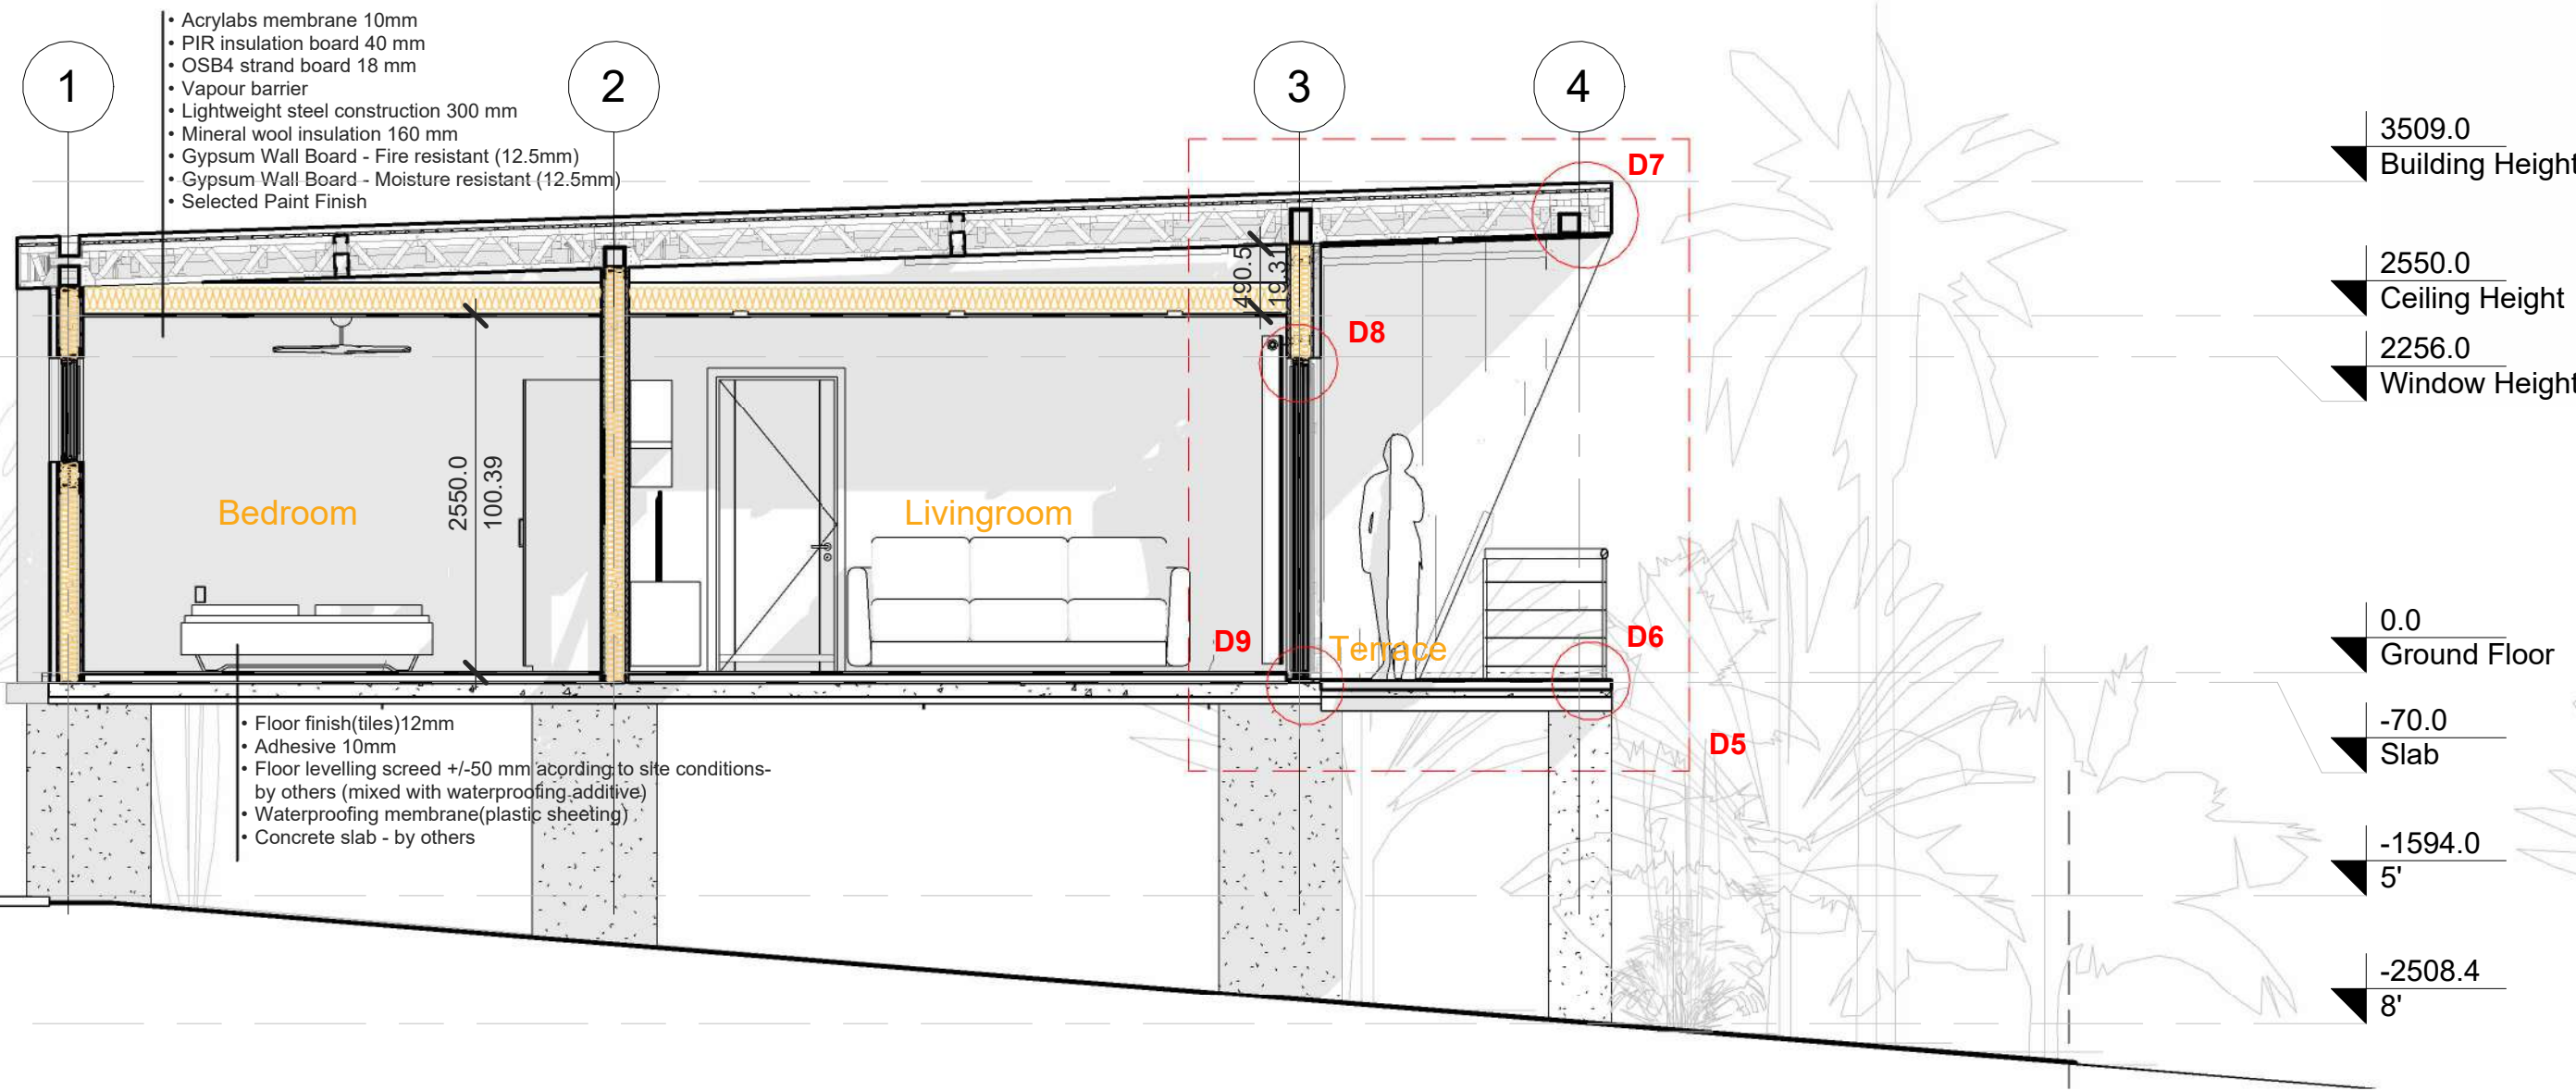

Openings Schedule

Doors

Name	Size	R.O. Size	Count	Type	Frame Colour	No.of leaves	Sill height	Hinge side	Lock	Shutters
D01	1300x2276	1335x2345	1	Entrance - Casement	7016 matt	2	50	-	Yes	-
D02	850x2100	915x2210	7	Interior - Casement	matt white lac.	1	70		Yes	-
D03	2200x2300	2235x2345	3	Exterior - Sliding	7016 matt	2	26	-	Yes	-

Windows

Name	Size	R.O. Size	Count	Opening Direction	Frame Colour	No.of leaves	Sill height	Hinge side	Lock	Shutters
W01	2000x1500	2035x1538	1	Sliding	anthracite 7016 matt	2	826	-	Yes	-
W02	2600x750	2635x788	2	Sliding	anthracite 7016 matt	2	1576	-	Yes	-
W03	1300x750	1335x788	1	1 fixed+ 1 sliding	anthracite 7016 matt	2	1576		Yes	-
W04	900x1500	935x1538	1	Casement	anthracite 7016 matt	1	826		Yes	-
W05	750x750	785x788	1	Casement	anthracite 7016 matt	1	1576		Yes	-

Name	Size	Count	Sill height
Opening Size	900x2100	2	70

Note:
• Shutters will be provided by others-acquired locally according to dimensions of finished openings after finish application. Drawings are made for design purposes only.
• Insect screens to be acquired locally according to dimensions of finished openings after finish application
• All opening windows open outwards.

Cortizo Window/Door Frames


https://www.cortizo.com/paginas/carta_standard



Colour: anthracite matt
model: 7016

Glass

https://www.guardianglass.com/gb/en/our-glass/glass-types/solar-control-glass

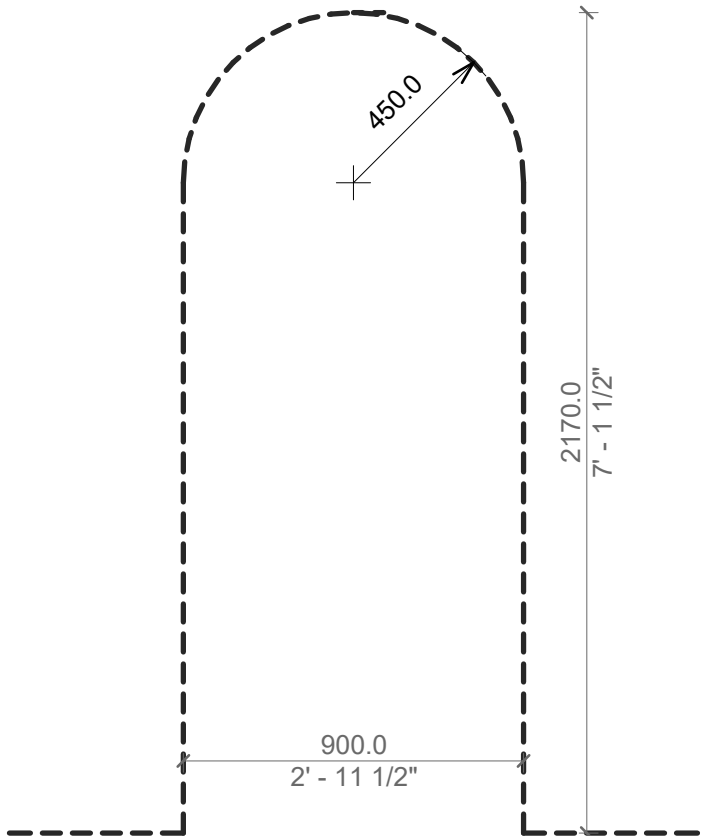

Opening Size

Type: Opening
R.O. Size: 900/2170
Total Piece: 2



- THESE DRAWINGS MUST BE CHECKED BY THE CUSTOMER OR CONTRACTOR PRIOR TO APPROVAL. ANY ERRORS OR OMISSIONS MUST BE REPORTED IN WRITING TO BAUHU PRIOR TO COMMENCEMENT OF CONSTRUCTION.
- ARCHITECTURAL DRAWINGS SHOULD BE READ IN CONJUNCTION WITH STRUCTURAL DETAILING AND FABRICATION GENERAL ASSEMBLY DRAWINGS.
- FOR CONSTRUCTION PURPOSES, USE ONLY THE LATEST APPROVED DRAWINGS LABELED 'ISSUED FOR CONSTRUCTION'.
- DO NOT SCALE FROM THIS DRAWING.
- THE COMPANY OPERATES USING METRIC DIMENSIONS AS THE PRINCIPAL DENOMINATION.
- ALL CONCRETE WORKS ARE OUTSIDE OF THE SCOPE OF THE COMPANY. INFORMATION REGARDING SLAB DESIGN AND CONNECTIONS IN THESE DRAWINGS ARE INTENDED FOR GUIDANCE ONLY. FOUNDATION AND SLAB WORKS SHOULD BE DESIGNED AND APPROVED BY A LOCAL STRUCTURAL ENGINEER.
- THE COMPANY RETAINS FULL TITLE AND OWNERSHIP OF THESE PLANS AND DESIGNS. ANY UNAUTHORISED USE, REPRODUCTION, OR DISTRIBUTION OF THESE PLANS, WHETHER IN WHOLE OR PART, IS EXPRESSLY PROHIBITED WITHOUT PRIOR WRITTEN CONSENT.

No.	Revision	Date

ISSUED FOR:

- Issued for information
- Issued for client approval
- Issued for fabrication
- Issued for construction

Angel

DRAWING TITLE:

Openings Schedule 1

DRAWN BY:

Yonca A.Clark

SCALE:




1 : 20

DRAWING NO:

A112

DATE:

01/05/2024

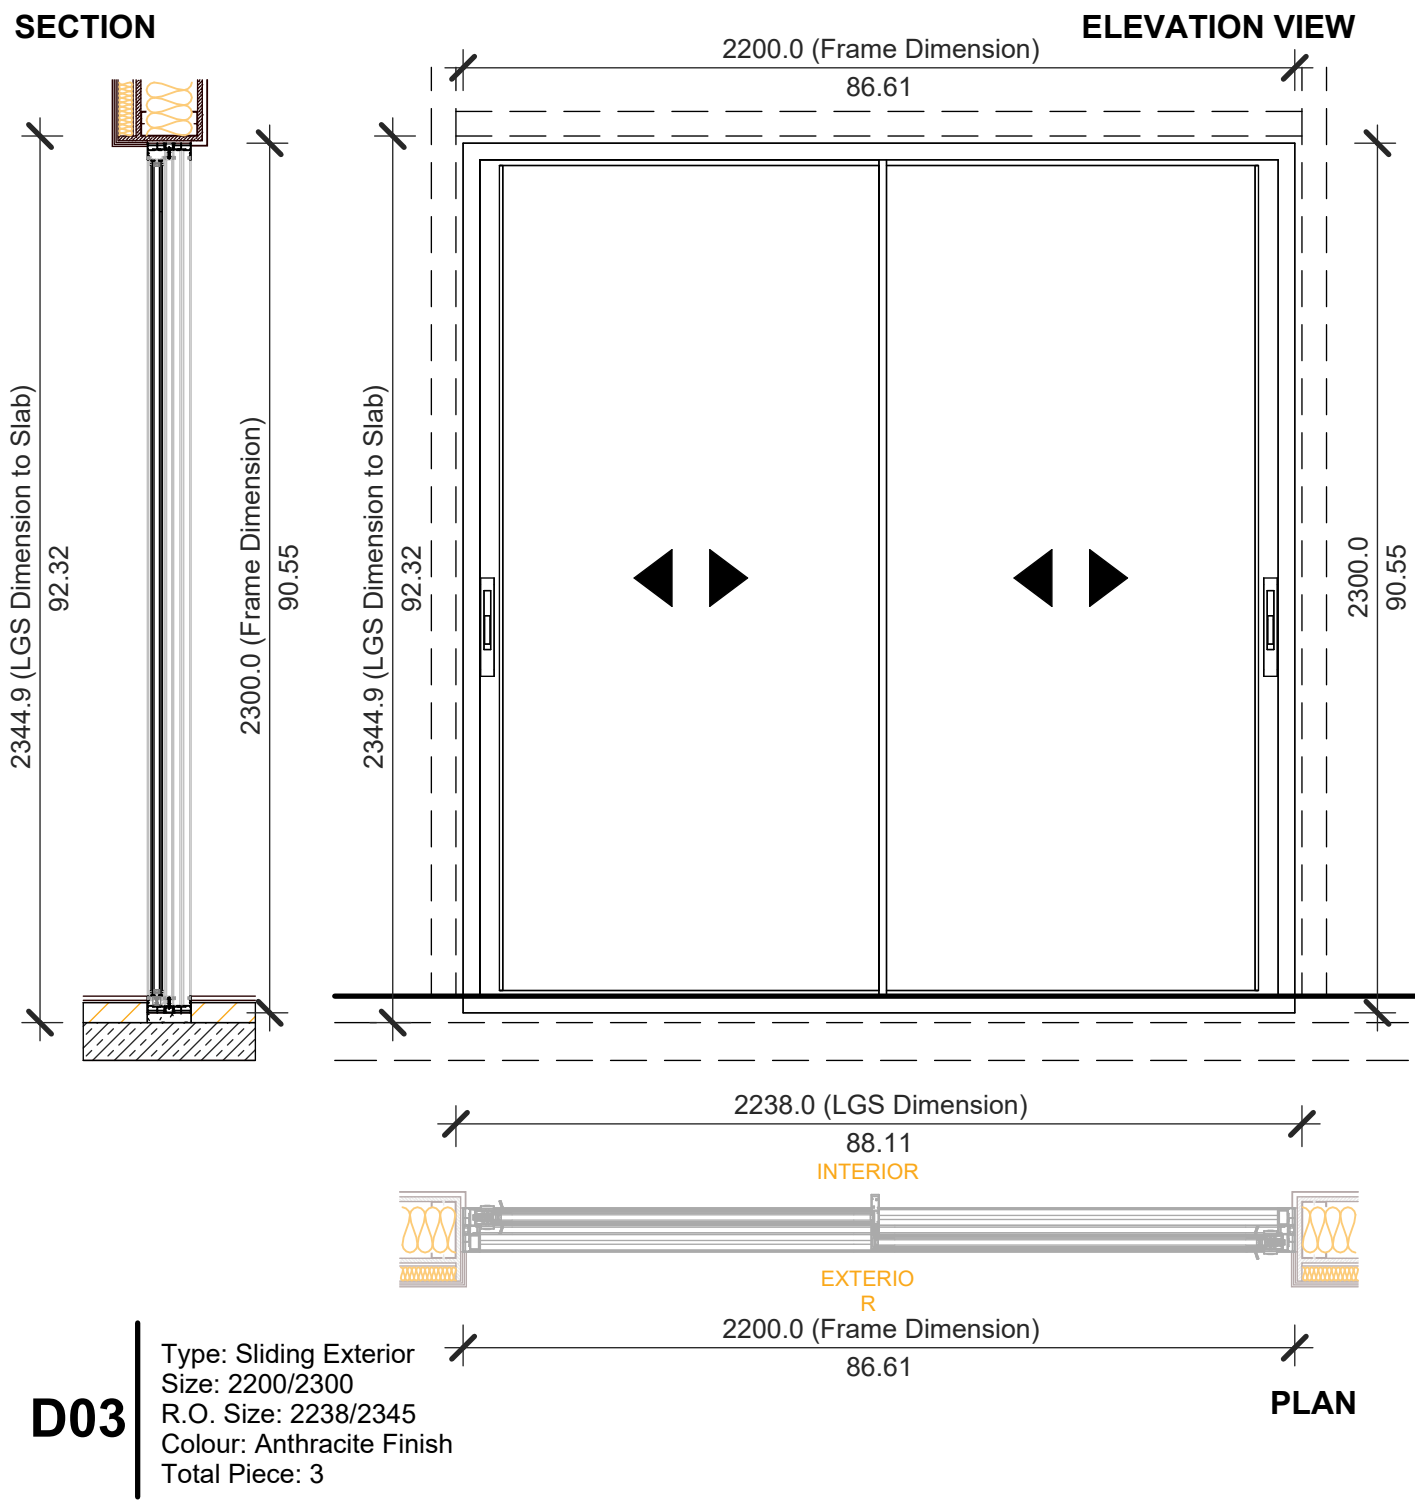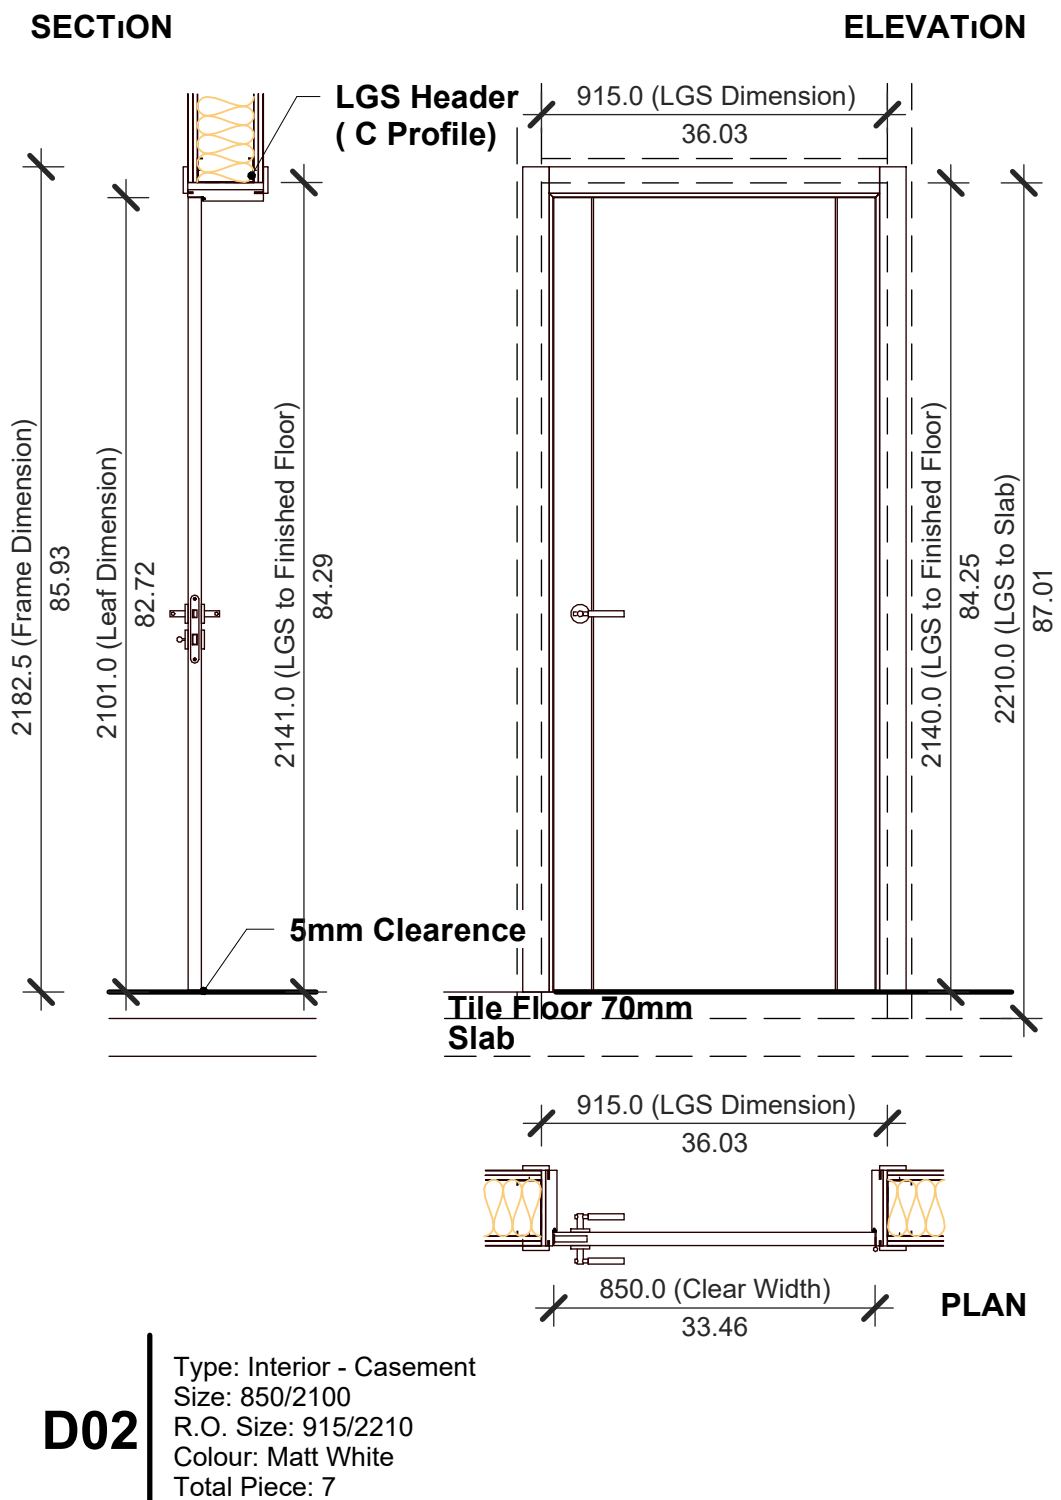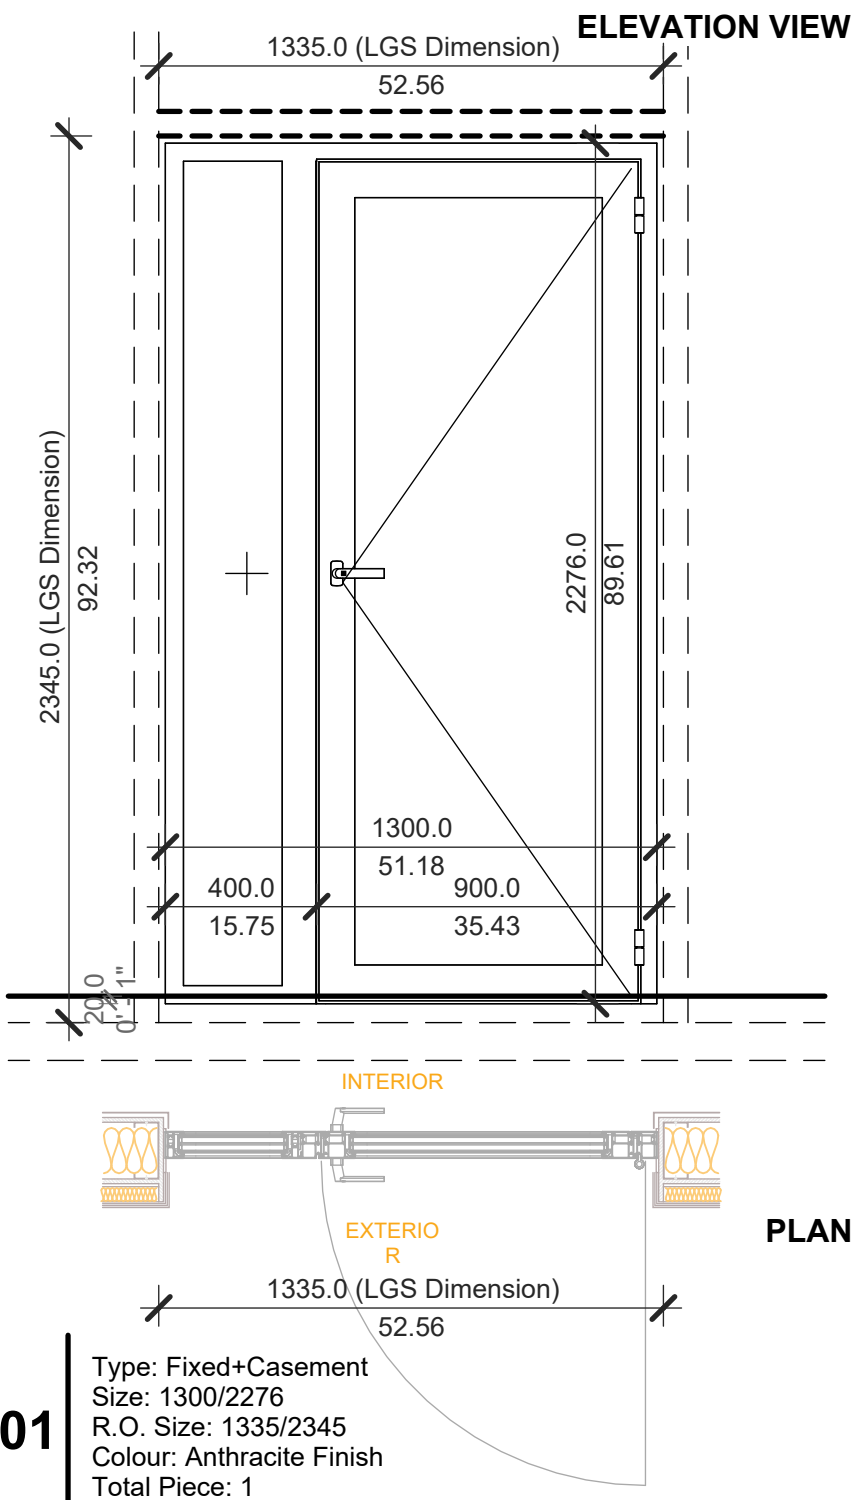

- THESE DRAWINGS MUST BE CHECKED BY THE CUSTOMER OR CONTRACTOR PRIOR TO APPROVAL. ANY ERRORS OR OMISSIONS MUST BE REPORTED IN WRITING TO BAUHU PRIOR TO COMMENCEMENT OF CONSTRUCTION.
- ARCHITECTURAL DRAWINGS SHOULD BE READ IN CONJUNCTION WITH STRUCTURAL DETAILING AND FABRICATION GENERAL ASSEMBLY DRAWINGS.
- FOR CONSTRUCTION PURPOSES, USE ONLY THE LATEST APPROVED DRAWINGS LABELED 'ISSUED FOR CONSTRUCTION'.
- DO NOT SCALE FROM THIS DRAWING.
- THE COMPANY OPERATES USING METRIC DIMENSIONS AS THE PRINCIPAL DENOMINATION.
- ALL CONCRETE WORKS ARE OUTSIDE OF THE SCOPE OF THE COMPANY. INFORMATION REGARDING SLAB DESIGN AND CONNECTIONS IN THESE DRAWINGS ARE INTENDED FOR GUIDANCE ONLY. FOUNDATION AND SLAB WORKS SHOULD BE DESIGNED AND APPROVED BY A LOCAL STRUCTURAL ENGINEER.
- THE COMPANY RETAINS FULL TITLE AND OWNERSHIP OF THESE PLANS AND DESIGNS. ANY UNAUTHORIZED USE, REPRODUCTION, OR DISTRIBUTION OF THESE PLANS, WHETHER IN WHOLE OR PART, IS EXPRESSLY PROHIBITED WITHOUT PRIOR WRITTEN CONSENT.

No.	Revision	Date

ISSUED FOR:

Issued for information

Issued for client approval

Issued for fabrication

Issued for construction

Angel

DRAWING TITLE:

Openings Schedule 2

DRAWN BY:

Yonca A.Clark

SCALE:



1 : 20

DRAWING NO:

A113

DATE:

01/05/2024

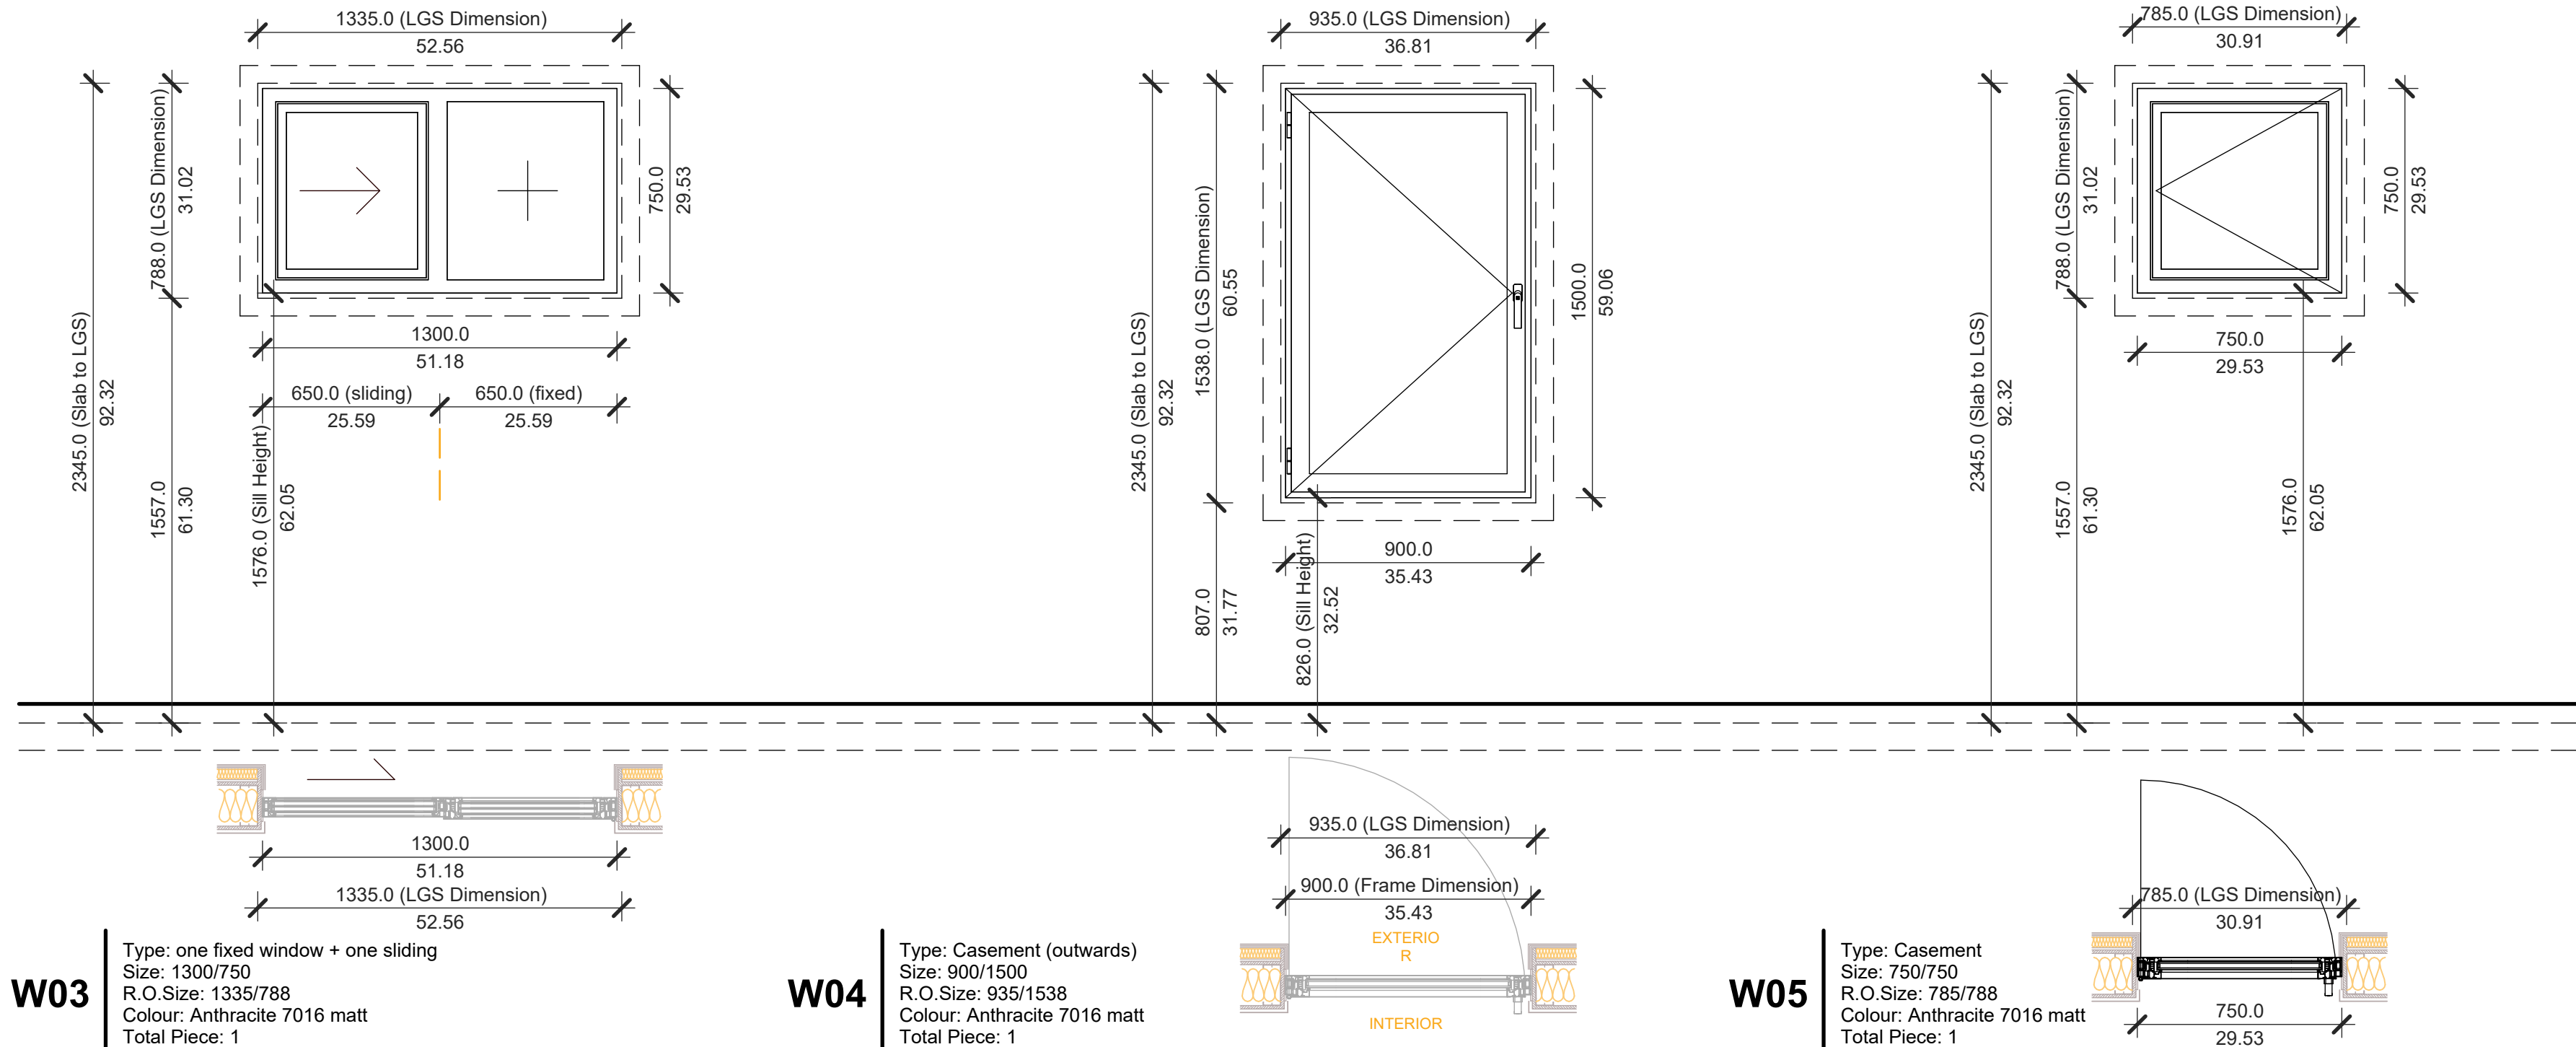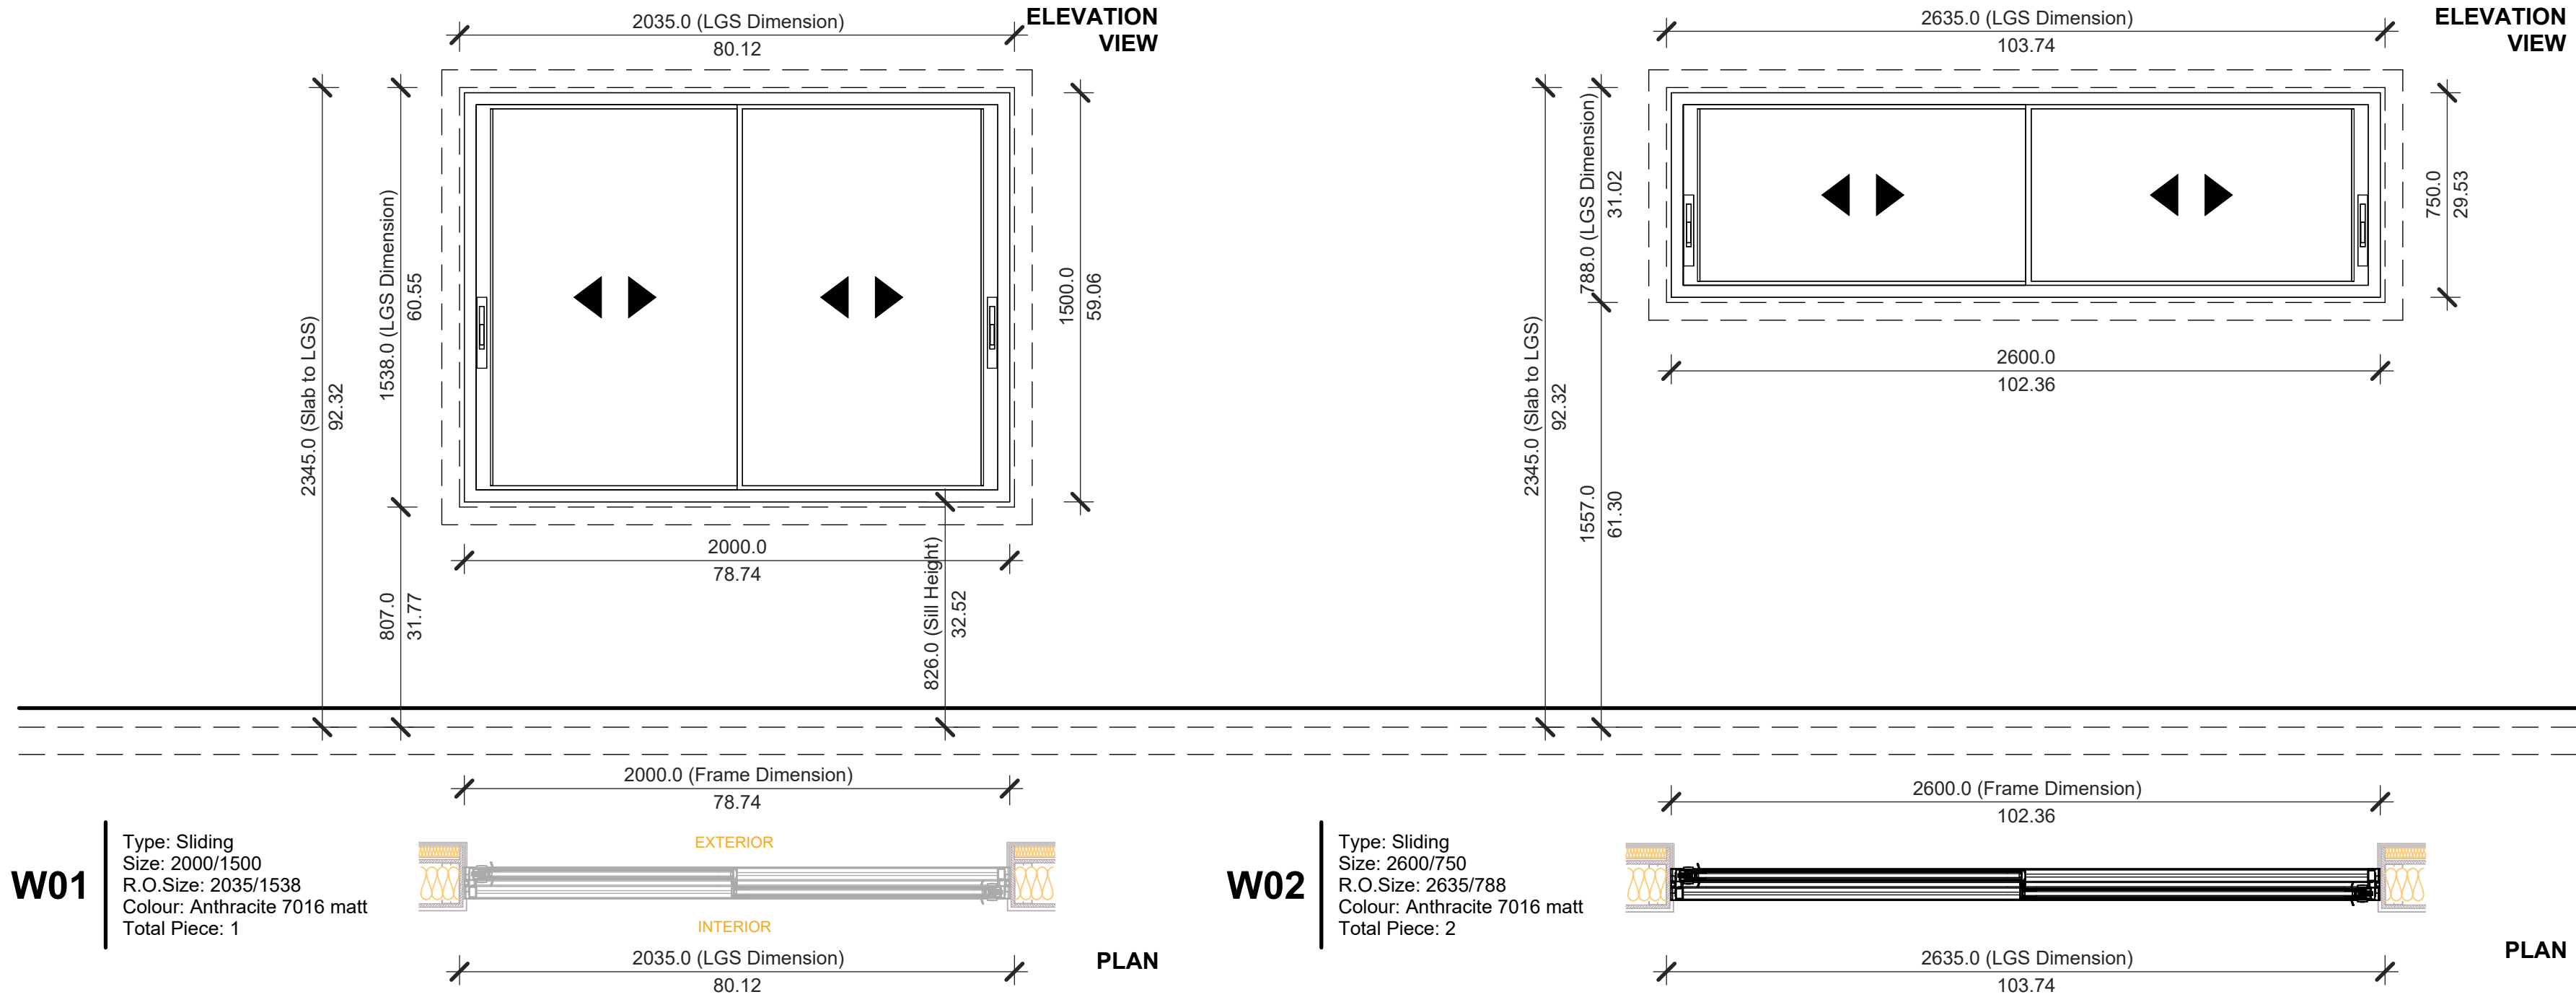

Finishes Schedule								
No.	Room Name	Floor Area	Room Perimeter	Floor Finish (Tiles and Grout Colour)	Ceiling Colour	Ceiling Height	Wall Colour	Wall Finish Wall Tile
Ground Floor								
1	Master Bedroom	14 m²	15392.0	Ecoliving Pearl OG02	CIN Pure White #D787	2550mm	CIN Mirage Beige #E340	Tile 1:Decor Tokyo Brown TK46R & Tile 2:One Beige ON28R
2	En-Suite Bathroom	6 m²	10792.0	Ecoliving Pearl OG02	CIN Pure White #D787	2550mm	CIN Mirage Beige #E340	
3	Bedroom 02	11 m²	13192.0	Ecoliving Pearl OG02	CIN Pure White #D787	2550mm	CIN Mirage Beige #E340	
4	Bathroom	4 m²	8292.0	Ecoliving Pearl OG02	CIN Pure White #D787	2550mm	CIN Green Smoke #E160	
5	Bedroom 01	12 m²	14492.0	Ecoliving Pearl OG02	CIN Pure White #D787	2550mm	CIN Mirage Beige #E340	Mosaico Ecoliving Pearl EOG06
6	Living Area	25 m²	23992.0	Ecoliving Pearl OG02	CIN Pure White #D787	2550mm	CIN Mirage Beige #E340	
7	Kitchen	9 m²	11900.0	Ecoliving Pearl OG02	CIN Pure White #D787	2550mm	x	
8	Entrance Hall	3 m²	6392.0	Ecoliving Pearl OG02	CIN Pure White #D787	2550mm	CIN Mirage Beige #E340	
9	Utility Room	5 m²	8992.0	Ecoliving Pearl OG02	CIN Pure White #D787	2550mm	CIN Mirage Beige #E340	Champagne and Pure White
10	Hall	3 m²	6992.0	Ecoliving Pearl OG02	CIN Pure White #D787	2550mm	CIN Mirage Beige #E340	
11	Deck	26 m²	29184.9	Ecoliving Pearl OG02				
12	Store/Office	6 m²	10592.0	Ecoliving Pearl OG02	CIN Pure White #D787	2550mm	CIN Mirage Beige #E340	
Grand total		124 m²	160204.9					



Room Legend

Bathroom	Bedroom 01	Bedroom 02	Deck	En-Suite Bathroom	Entrance Hall	Hall	Kitchen	Living Area	Master Bedroom	Store/Office	Utility Room
----------	------------	------------	------	-------------------	---------------	------	---------	-------------	----------------	--------------	--------------

Ceiling Schedule			
Type	Perimeter	LengthxWidth	Area
Interior			
01 Master Bedroom	15392.0	4700x3000	14 m²
02 En-Suite Bathroom	10844.0	1700x3700	6 m²
03 Bedroom 02	13192.0	2900x3700	11 m²
04 Bathroom	8292.0	1750x2400	4 m²
05 Bedroom 01	14492.0		12 m²
06/07 Kitchen and Living area	23992.0	4700x7300	34 m²
08 Entrance Hall	6392.0	1600x1600	3 m²
09 Utility Room	8992.0	1600x2900	5 m²
10 Hall	6992.0	1100x2400	3 m²
11 Deck - External Ceiling	28725.3	12790x2090	25 m²
12 Store/Office	10592.0	1600x3700	6 m²
Grand total	147897.3		123 m²

Roof Schedule				
Type	Base Level	Base Offset From Level	Roof Slope	Area
Roof	Ceiling Height	198.8	2.00°	146 m²
Roofs 1				
Wall Area (to the Truss)				
Room			Area	
01 Master Bedroom			23.6 m²	
02 En-Suite Bathroom Paint			11.1 m²	
02 En-Suite Bathroom Tile 2 - One Beige ON28R			10.0 m²	
03 Bedroom 02			34.4 m²	
04 Bathroom Paint			13.6 m²	
04 Bathroom Tile 1 - One Wave Beige ON25R			7.5 m²	
04 Bathroom Tile 2 - One Beige ON28R			1.2 m²	
05 Bedroom 01			38.1 m²	
06-07 Living Area and Kitchen			57.9 m²	
07 Kitchen Tile			1.1 m²	
08 Entrance Hall			8.5 m²	
09 Utility Room			15.5 m²	
10 Hall			13.1 m²	
12 Store/Office			18.0 m²	
Exterior Paint			370.4 m²	
Exterior Textured Paint (Back&Front Side of the Building)			58.8 m²	
Gypsum Wall Board (1)			3.8 m²	

Wall Schedule		
Type	Length	Area
BAU 245 Wall 3		
Conceaed Cistern Wall	3675.0	4 m²
External		
BAU 245 Wall	46701.8	109 m²
BAU 245 Wall 2	645.4	2 m²
Internal		
BAU 200 Wall	42489.0	102 m²
Grand total	94430.3	219 m²



1. THESE DRAWINGS MUST BE CHECKED BY THE CUSTOMER OR CONTRACTOR PRIOR TO APPROVAL. ANY ERRORS OR OMISSIONS MUST BE REPORTED IN WRITING TO BAUHU PRIOR TO COMMENCEMENT OF CONSTRUCTION.
2. ARCHITECTURAL DRAWINGS SHOULD BE READ IN CONJUNCTION WITH STRUCTURAL DETAILING AND FABRICATION GENERAL ASSEMBLY DRAWINGS.
3. FOR CONSTRUCTION PURPOSES, USE ONLY THE LATEST APPROVED DRAWINGS LABELED 'ISSUED FOR CONSTRUCTION'.
4. DO NOT SCALE FROM THIS DRAWING.
5. THE COMPANY OPERATES USING METRIC DIMENSIONS AS THE PRINCIPAL DENOMINATION.
6. ALL CONCRETE WORKS ARE OUTSIDE OF THE SCOPE OF THE COMPANY. INFORMATION REGARDING SLAB DESIGN AND CONNECTIONS IN THESE DRAWINGS ARE INTENDED FOR GUIDENCE ONLY. FOUNDATION AND SLAB WORKS SHOULD BE DESIGNED AND APPROVED BY A LOCAL STRUCTURAL ENGINEER.
7. THE COMPANY RETAINS FULL TITLE AND OWNERSHIP OF THESE PLANS AND DESIGNS. ANY UNAUTHORISED USE, REPRODUCTION, OR DISTRIBUTION OF THESE PLANS, WHETHER IN WHOLE OR PART, IS EXPRESSLY PROHIBITED WITHOUT PRIOR WRITTEN CONSENT.

No.	Revision	Date

- ISSUED FOR:
- Issued for information

Issued for client approval

Issued for fabrication

Issued for construction

Angel

DRAWING TITLE:	Room Legend
DRAWN BY:	Yonca A.Clark
SCALE:	1 : 70
DRAWING NO:	A114
DATE:	01/05/2024


Interior Flooring

• Ecoliving Pearl OG02

• 88,6 x 88,6 cm . 34,9" x 34,9" / C12

• Stone, Rectified

• Glazed Porcelain Full Color Body, Natural

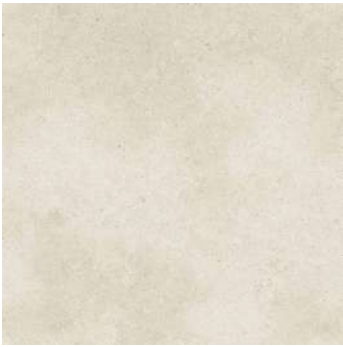

https://www.domino.pt/en/products/[[type-22-go]][collection-84][material-77][ambient-all]]/263-ecoliving/-/1816-ecoliving-pearl-og02/164-886-x-886

Kitchen Tile

• Mosaico Ecoliving Pearl EOG06

• 30 x 30 cm . 11,8" x 11,8" / E29

• Decorations, Stone, Not Rectified

• Glazed Porcelain Full Color Body, Natural



https://www.domino.pt/en/products/[[type-22-go]][collection-84][material-24][ambient-all]]/268-ecoliving/-/1841-mosaico-ecoliving-pearl-eog06/54-

Bathroom Wall Tile 1 (Room No:4)

• One Wave Beige ON25R

• 34 x 91,5 cm . 13,4" x 36" / R20

• Color, Not Rectified

• White Body Wall Tiles, Mate



https://www.domino.pt/en/products/[[type-21-go]][collection-80][material-83][ambient-all]]/249-one/-/1750-one-wave-beige-on25r/157-34-x-915

En-Suite Bathroom&Bathroom Wall Tile 2 (Room No:2&4)

• One Beige ON28R

• 34 x 91,5 cm . 13,4" x 36" / R19

• Color, Not Rectified

• White Body Wall Tiles, Mate



https://www.domino.pt/en/products/[[type-21-go]][collection-80][material-42][ambient-all]]/248-one/-/1747-one-beige-on28r/157-34-x-915

Bathroom Wall Colour

• Colour: Green Smoke #E160



Ceiling Finish

• Colour: Pure white #D787



Interior Wall Finish

• Colour: Mirage Beige #E340



En-Suite Bathroom Wall Tile 1 (Room No:2)

• Decor Tokyo Brown TK46R

• 34 x 66,5 cm . 13,4" x 26,2" / R17

• Decorations, Concrete, Color, Not Rectified

• White Body Wall Tiles, Mate



https://www.domino.pt/en/products/[[type-21-go]][collection-73][material-28][ambient-all]]/206-tokyo/-/1528-decor-tokyo-brown-tk46r/147-34-x-665

En-Suite Bathroom Wall Colour

• Colour: Mirage Beige #E340



Furniture type:

Compincar - model 1003



Interior Doors:


Compincar - model 302



Roof Finish

• Acrylabs elastomeric roofing membrane

• Colour: 'reflective white'

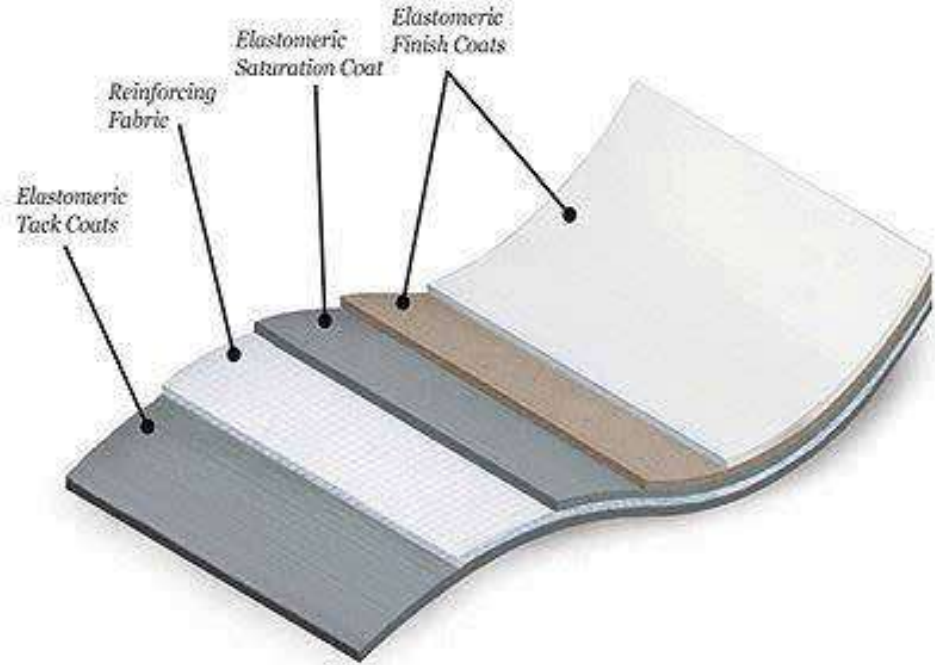

Exterior Wall Finish

Stolit K fine grain exterior plaster

Colour: Pure white



Exterior Front and Back Wall Finish

Stolit K fine grain exterior plaster

Colour: Champagne



BAUHU

MODULAR • BUILDING • SOLUTIONS

1. THESE DRAWINGS MUST BE CHECKED BY THE CUSTOMER OR CONTRACTOR PRIOR TO APPROVAL. ANY ERRORS OR OMISSIONS MUST BE REPORTED IN WRITING TO BAUHU PRIOR TO COMMENCEMENT OF CONSTRUCTION.

2. ARCHITECTURAL DRAWINGS SHOULD BE READ IN CONJUNCTION WITH STRUCTURAL DETAILING AND FABRICATION GENERAL ASSEMBLY DRAWINGS.

3. FOR CONSTRUCTION PURPOSES, USE ONLY THE LATEST APPROVED DRAWINGS LABELED 'ISSUED FOR CONSTRUCTION'.

4. DO NOT SCALE FROM THIS DRAWING.

5. THE COMPANY OPERATES USING METRIC DIMENSIONS AS THE PRINCIPAL DENOMINATION.

6. ALL CONCRETE WORKS ARE OUTSIDE OF THE SCOPE OF THE COMPANY. INFORMATION REGARDING SLAB DESIGN AND CONNECTIONS IN THESE DRAWINGS ARE INTENDED FOR GUIDENCE ONLY. FOUNDATION AND SLAB WORKS SHOULD BE DESIGNED AND APPROVED BY A LOCAL STRUCTURAL ENGINEER.

7. THE COMPANY RETAINS FULL TITLE AND OWNERSHIP OF THESE PLANS AND DESIGNS. ANY UNAUTHORISED USE, REPRODUCTION, OR DISTRIBUTION OF THESE PLANS, WHETHER IN WHOLE OR PART, IS EXPRESSLY PROHIBITED WITHOUT PRIOR WRITTEN CONSENT.

No.	Revision	Date

ISSUED FOR:

Issued for information

Issued for client approval

Issued for fabrication

Issued for construction

Angel

DRAWING TITLE:

Finishes Schedule

DRAWN BY:

Yonca A.Clark


SCALE:

DRAWING NO:


A115

DATE:


01/05/2024

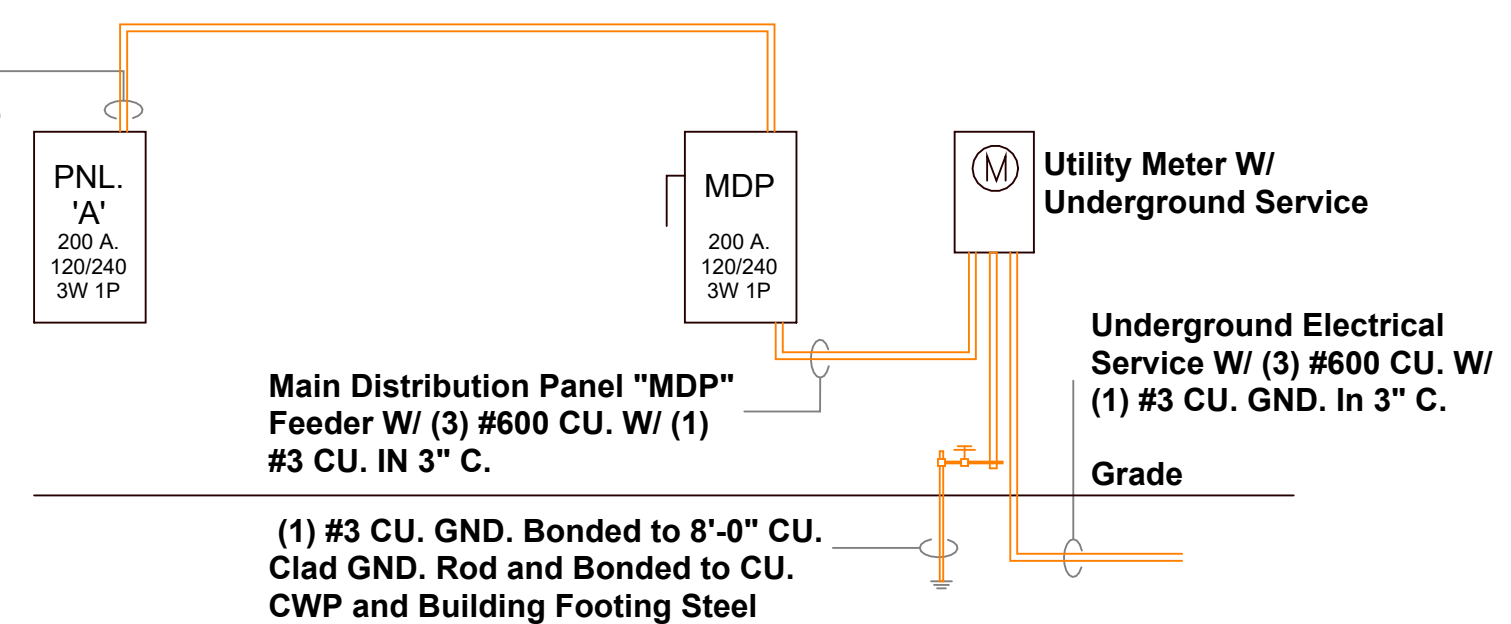


Typical Plumbing Riser Plan

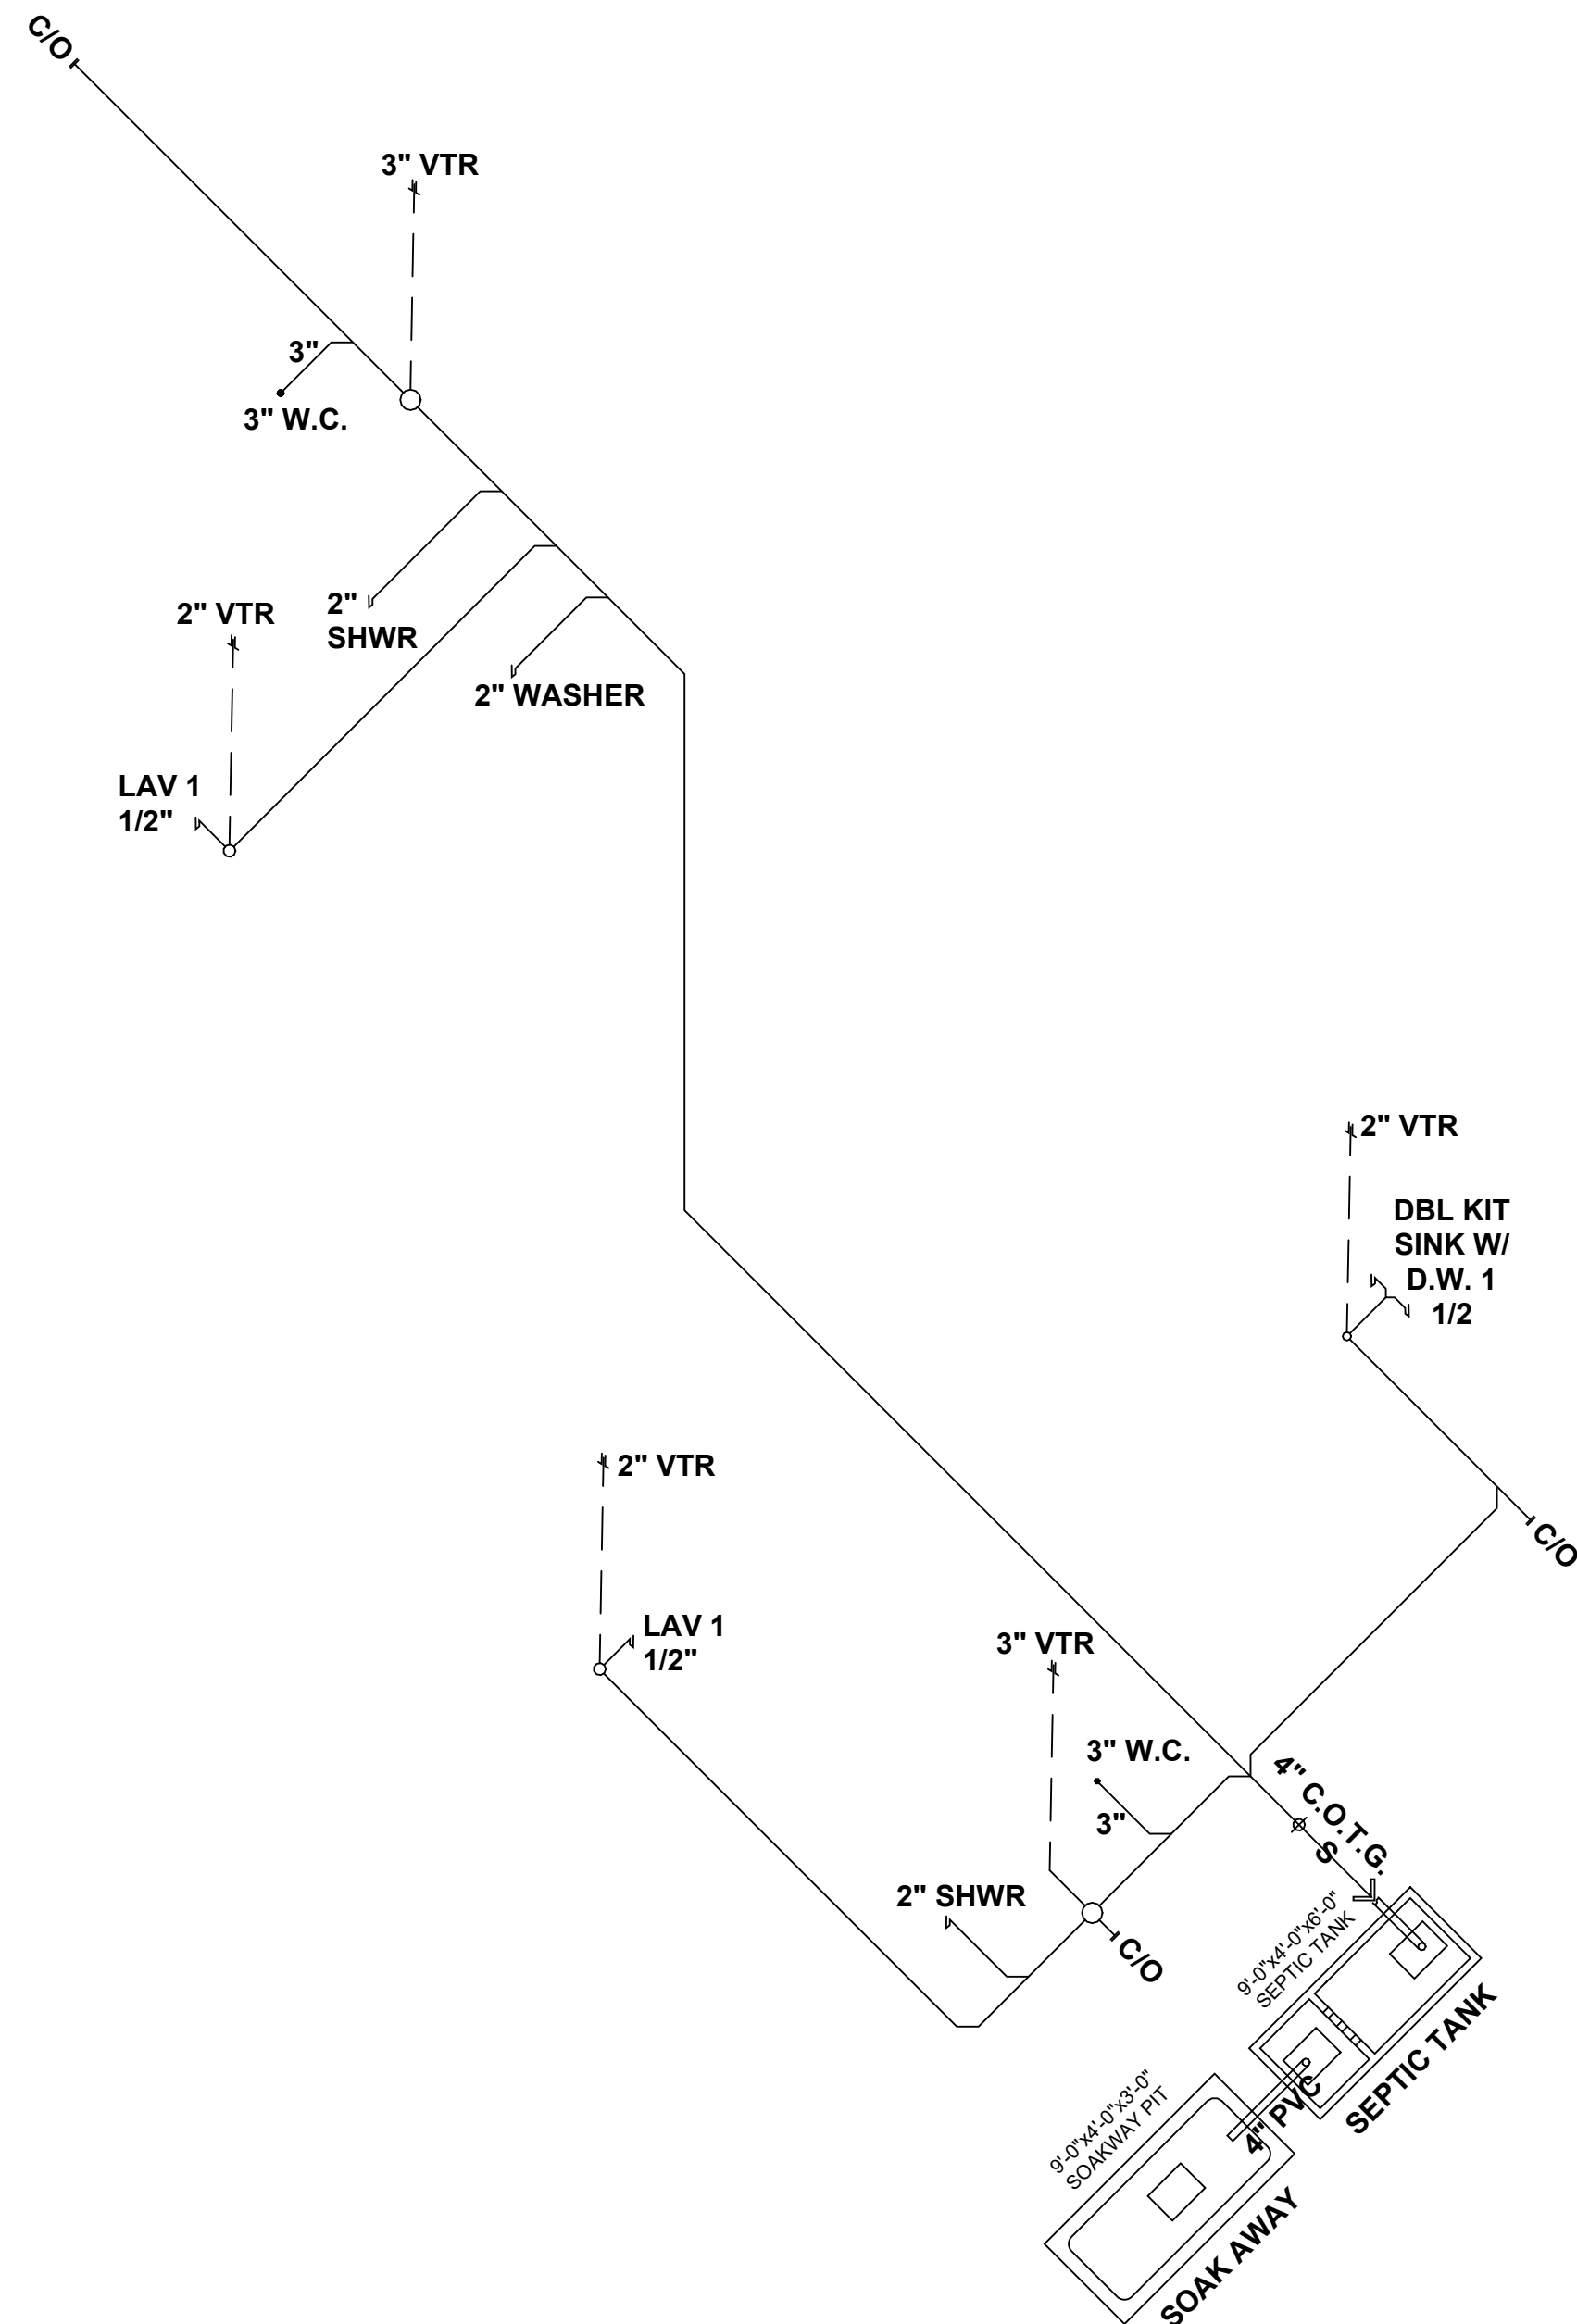

Typical Piping at Water Heater

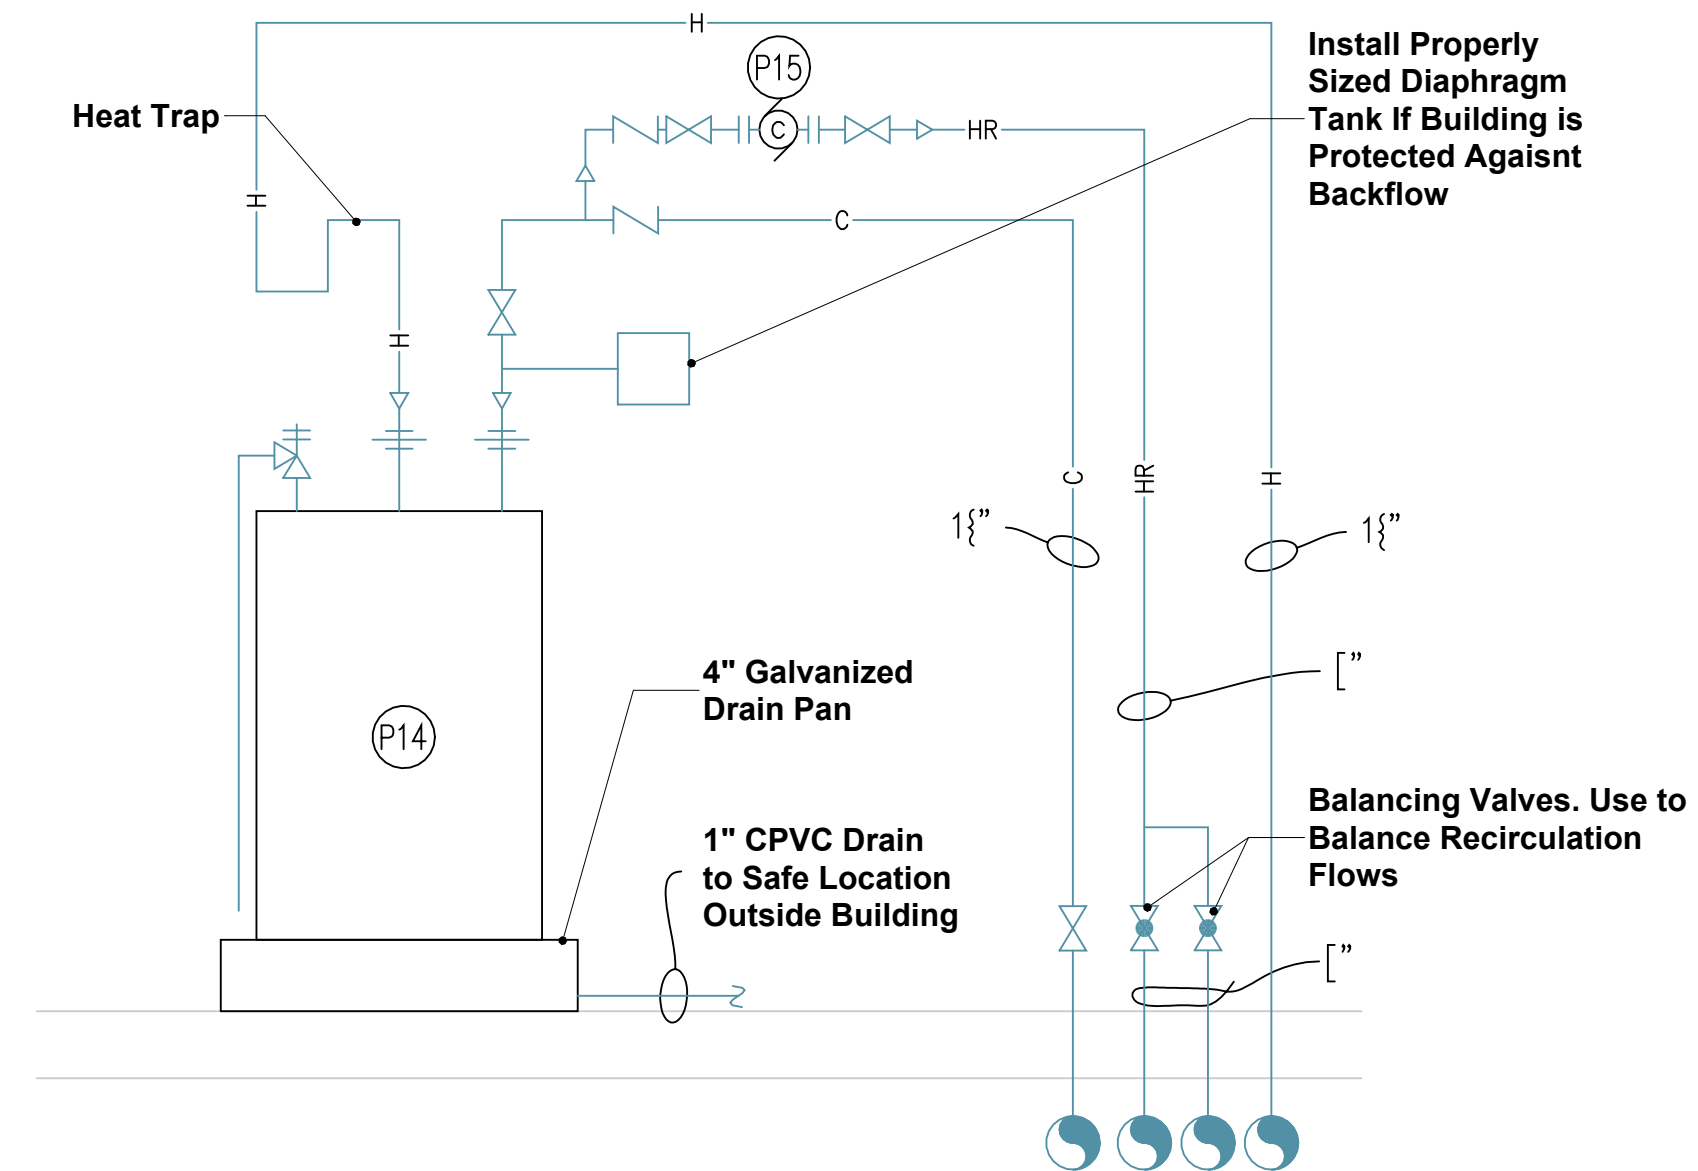

Typical Sceptic Tank & Soak Away Section

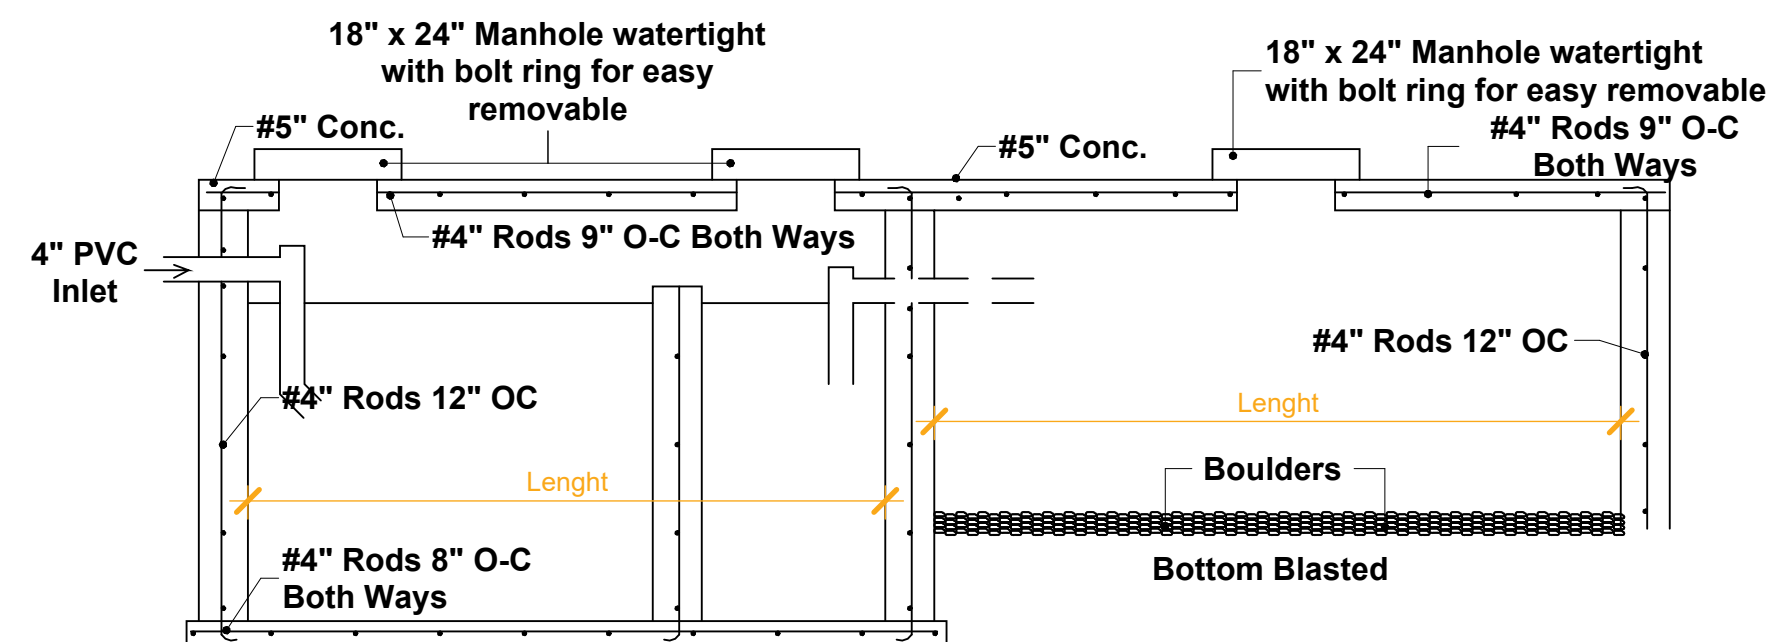

Note: Sanitary ware, faucets, kitchen and bathroom equipment are provided. Plumbing supply pipework, waste and sub-slab roughings are excluded. Plumbing plan is provided as a guide for contractor information only.

1. THESE DRAWINGS MUST BE CHECKED BY THE CUSTOMER OR CONTRACTOR PRIOR TO APPROVAL. ANY ERRORS OR OMISSIONS MUST BE REPORTED IN WRITING TO BAUHU PRIOR TO COMMENCEMENT OF CONSTRUCTION.
2. ARCHITECTURAL DRAWINGS SHOULD BE READ IN CONJUNCTION WITH STRUCTURAL DETAILING AND FABRICATION GENERAL ASSEMBLY DRAWINGS.
3. FOR CONSTRUCTION PURPOSES, USE ONLY THE LATEST APPROVED DRAWINGS LABELED 'ISSUED FOR CONSTRUCTION'.
4. DO NOT SCALE FROM THIS DRAWING.
5. THE COMPANY OPERATES USING METRIC DIMENSIONS AS THE PRINCIPAL DENOMINATION.
6. ALL CONCRETE WORKS ARE OUTSIDE OF THE SCOPE OF THE COMPANY. INFORMATION REGARDING SLAB DESIGN AND CONNECTIONS IN THESE DRAWINGS ARE INTENDED FOR GUIDENCE ONLY. FOUNDATION AND SLAB WORKS SHOULD BE DESIGNED AND APPROVED BY A LOCAL STRUCTURAL ENGINEER.
7. THE COMPANY RETAINS FULL TITLE AND OWNERSHIP OF THESE PLANS AND DESIGNS. ANY UNAUTHORISED USE, REPRODUCTION, OR DISTRIBUTION OF THESE PLANS, WHETHER IN WHOLE OR PART, IS EXPRESSLY PROHIBITED WITHOUT PRIOR WRITTEN CONSENT.

[illegible]

ISSUED FOR:

Issued for information

Issued for client approval

Issued for fabrication

Issued for construction

Angel

DRAWING TITLE:

Plumbing Details

DRAWN BY:

Yonca A.Clark

SCALE:

DRAWING NO:

A117

DATE:

01/05/2024

- Hot Water
- Cold Water
- Waste Water
- Rain Water Collection Pipes (underground)



Note: Sanitary ware, faucets, kitchen and bathroom equipment are provided. Plumbing supply pipework, waste and sub-slab roughings are excluded. Plumbing plan is provided as a guide for contractor information only.

1. THESE DRAWINGS MUST BE CHECKED BY THE CUSTOMER OR CONTRACTOR PRIOR TO APPROVAL. ANY ERRORS OR OMISSIONS MUST BE REPORTED IN WRITING TO BAUHU PRIOR TO COMMENCEMENT OF CONSTRUCTION.
2. ARCHITECTURAL DRAWINGS SHOULD BE READ IN CONJUNCTION WITH STRUCTURAL DETAILING AND FABRICATION GENERAL ASSEMBLY DRAWINGS.
3. FOR CONSTRUCTION PURPOSES, USE ONLY THE LATEST APPROVED DRAWINGS LABELED 'ISSUED FOR CONSTRUCTION'.
4. DO NOT SCALE FROM THIS DRAWING.
5. THE COMPANY OPERATES USING METRIC DIMENSIONS AS THE PRINCIPAL DENOMINATION.
6. ALL CONCRETE WORKS ARE OUTSIDE OF THE SCOPE OF THE COMPANY. INFORMATION REGARDING SLAB DESIGN AND CONNECTIONS IN THESE DRAWINGS ARE INTENDED FOR GUIDENCE ONLY. FOUNDATION AND SLAB WORKS SHOULD BE DESIGNED AND APPROVED BY A LOCAL STRUCTURAL ENGINEER.
7. THE COMPANY RETAINS FULL TITLE AND OWNERSHIP OF THESE PLANS AND DESIGNS. ANY UNAUTHORISED USE, REPRODUCTION, OR DISTRIBUTION OF THESE PLANS, WHETHER IN WHOLE OR PART, IS EXPRESSLY PROHIBITED WITHOUT PRIOR WRITTEN CONSENT.

No.	Revision	Date

ISSUED FOR:

Issued for information

Issued for client approval

Issued for fabrication

Issued for construction

Angel

DRAWING TITLE:

Plumbing Plan

DRAWN BY:

Yonca A.Clark

SCALE:

1 : 50

DRAWING NO:

A118

DATE:

01/05/2024

- THESE DRAWINGS MUST BE CHECKED BY THE CUSTOMER OR CONTRACTOR PRIOR TO APPROVAL. ANY ERRORS OR OMISSIONS MUST BE REPORTED IN WRITING TO BAUHU PRIOR TO COMMENCEMENT OF CONSTRUCTION.
- ARCHITECTURAL DRAWINGS SHOULD BE READ IN CONJUNCTION WITH STRUCTURAL DETAILING AND FABRICATION GENERAL ASSEMBLY DRAWINGS.
- FOR CONSTRUCTION PURPOSES, USE ONLY THE LATEST APPROVED DRAWINGS LABELED 'ISSUED FOR CONSTRUCTION'.
- DO NOT SCALE FROM THIS DRAWING.
- THE COMPANY OPERATES USING METRIC DIMENSIONS AS THE PRINCIPAL DENOMINATION.
- ALL CONCRETE WORKS ARE OUTSIDE OF THE SCOPE OF THE COMPANY. INFORMATION REGARDING SLAB DESIGN AND CONNECTIONS IN THESE DRAWINGS ARE INTENDED FOR GUIDENCE ONLY. FOUNDATION AND SLAB WORKS SHOULD BE DESIGNED AND APPROVED BY A LOCAL STRUCTURAL ENGINEER.
- THE COMPANY RETAINS FULL TITLE AND OWNERSHIP OF THESE PLANS AND DESIGNS. ANY UNAUTHORISED USE, REPRODUCTION, OR DISTRIBUTION OF THESE PLANS, WHETHER IN WHOLE OR PART, IS EXPRESSLY PROHIBITED WITHOUT PRIOR WRITTEN CONSENT.

No.	Revision	Date

ISSUED FOR:

Issued for information

Issued for client approval

Issued for fabrication

Issued for construction

Angel

DRAWING TITLE:

Base Plate Plan

DRAWN BY:

Yonca A.Clark

SCALE:

1 : 50

DRAWING NO:

A119

DATE:

01/05/2024

NOTES:-

- THIS DRAWING IS NOT TO BE SCALED WORK FROM GIVEN DIMENSION ONLY.
- ALL HRS SHOULD BE HOT DIP GALVANIZED
- MINIMUM GRADE OF CONCRETE SLAB C20/25 & MINIMUM GRADE OF CONCRETE PIERS C35/ C45.
- REFER TABLE & MARKUP FOR MINIMUM RC AND ANCHOR REQUIREMENT.
- REFER NOTES FOR MINIMUM ANCHOR REINFORCEMENT REQUIREMENT.
- RC SIZES ARE PROVIDED AS PER ANCHOR DESIGN REQUIREMENT FOR CONCEPTUALIZATION PURPOSE ONLY, REFERS TO RC DRAWING FROM RC DESIGNER FOR FINAL SIZES.
- HEIGHT/ LENGTH OF COLUMN/ RC PIER TO BE CONFIRMED BY FOUNDATION PROVIDER PRIOR TO FABRICATION.
- AT EXTERNAL WALL BASE TRACK TO CONCRETE CONNECTION, PROVIDE (1) HUS4-HF 10X110 ANCHOR W/ MIN 108.4mm EMBEDMENT DEPTH @ 600mm C/ OR AT EACH STUD LOCATION WITH 150mm MIN. EDGE DISTANCE FROM CONCRETE EDGE & 150mm MIN. DEPTH OF CONCRETE.
- AT INTERNAL WALL BASE TRACK TO CONCRETE CONNECTION, PROVIDE (1) HUS4-HF 10X110 ANCHOR W/ MIN 108.4mm EMBEDMENT DEPTH @ 600mm C/ OR AT EACH STUD LOCATION WITH 150mm MIN. EDGE DISTANCE FROM CONCRETE EDGE & 150mm MIN. DEPTH OF CONCRETE.
- ADDITIONAL LENGTH OF ANCHOR NEED TO CUT ON SITE.
- ANCHOR LOCATION NEED TO BE FOLLOWED PRECISELY TO AVOID ANCHOR CLASH WITH REINFORCEMENT.
- RC DESIGNER AND CONTRACTOR TO VERIFY ALL DIMENSIONS BEFORE CONSTRUCTION.



ANCHOR BOLT REQUIREMENT

BASE PLATE	ANCHOR BOLT	EFFECTIVE EMBEDMENT DEPTH IN RC (mm)	ANCHOR LENGTH (mm) (MINIMUM EMBEDMENT DEPTH)
BP-1 (A)	SIMPSON SET-3G™ - SET-3G w/ #6 A615 Gr. 60 Rebar (20mm dia)	431	500
BP-2 (B)	SIMPSON SET-3G™ - SET-3G w/ #6 A615 Gr. 60 Rebar (20mm dia)	431	500
Holddown (C)	HILTY HIT-HY 200+HAS-U8.8 HDG M16	110	190

MINIMUM REQUIREMENT RC

BASE PLATE	MIN EDGE DISTANCES FROM ANCHOR (mm)	MINIMUM RC DEPTH (mm)
BP-1 (A)	200	1220
BP-2 (B)	200	1220
Holddown (C)	240	150

NOTE:-	1. MINIMUM ANCHORAGE REINFORCEMENT - REQUIREMENT #4 BARS OF ASTM A-615, GRADE 60.
	2. MINIMUM GRADE OF CONCRETE SLAB C20/25 & MINIMUM GRADE OF CONCRETE PIERS C35/ C45.
	3. REFER DRAWING S-09 FOR ANCHOR REINFORCEMENT.
	4. ANCHOR REINFORCEMENT PER ACI 318 APPENDIX D.

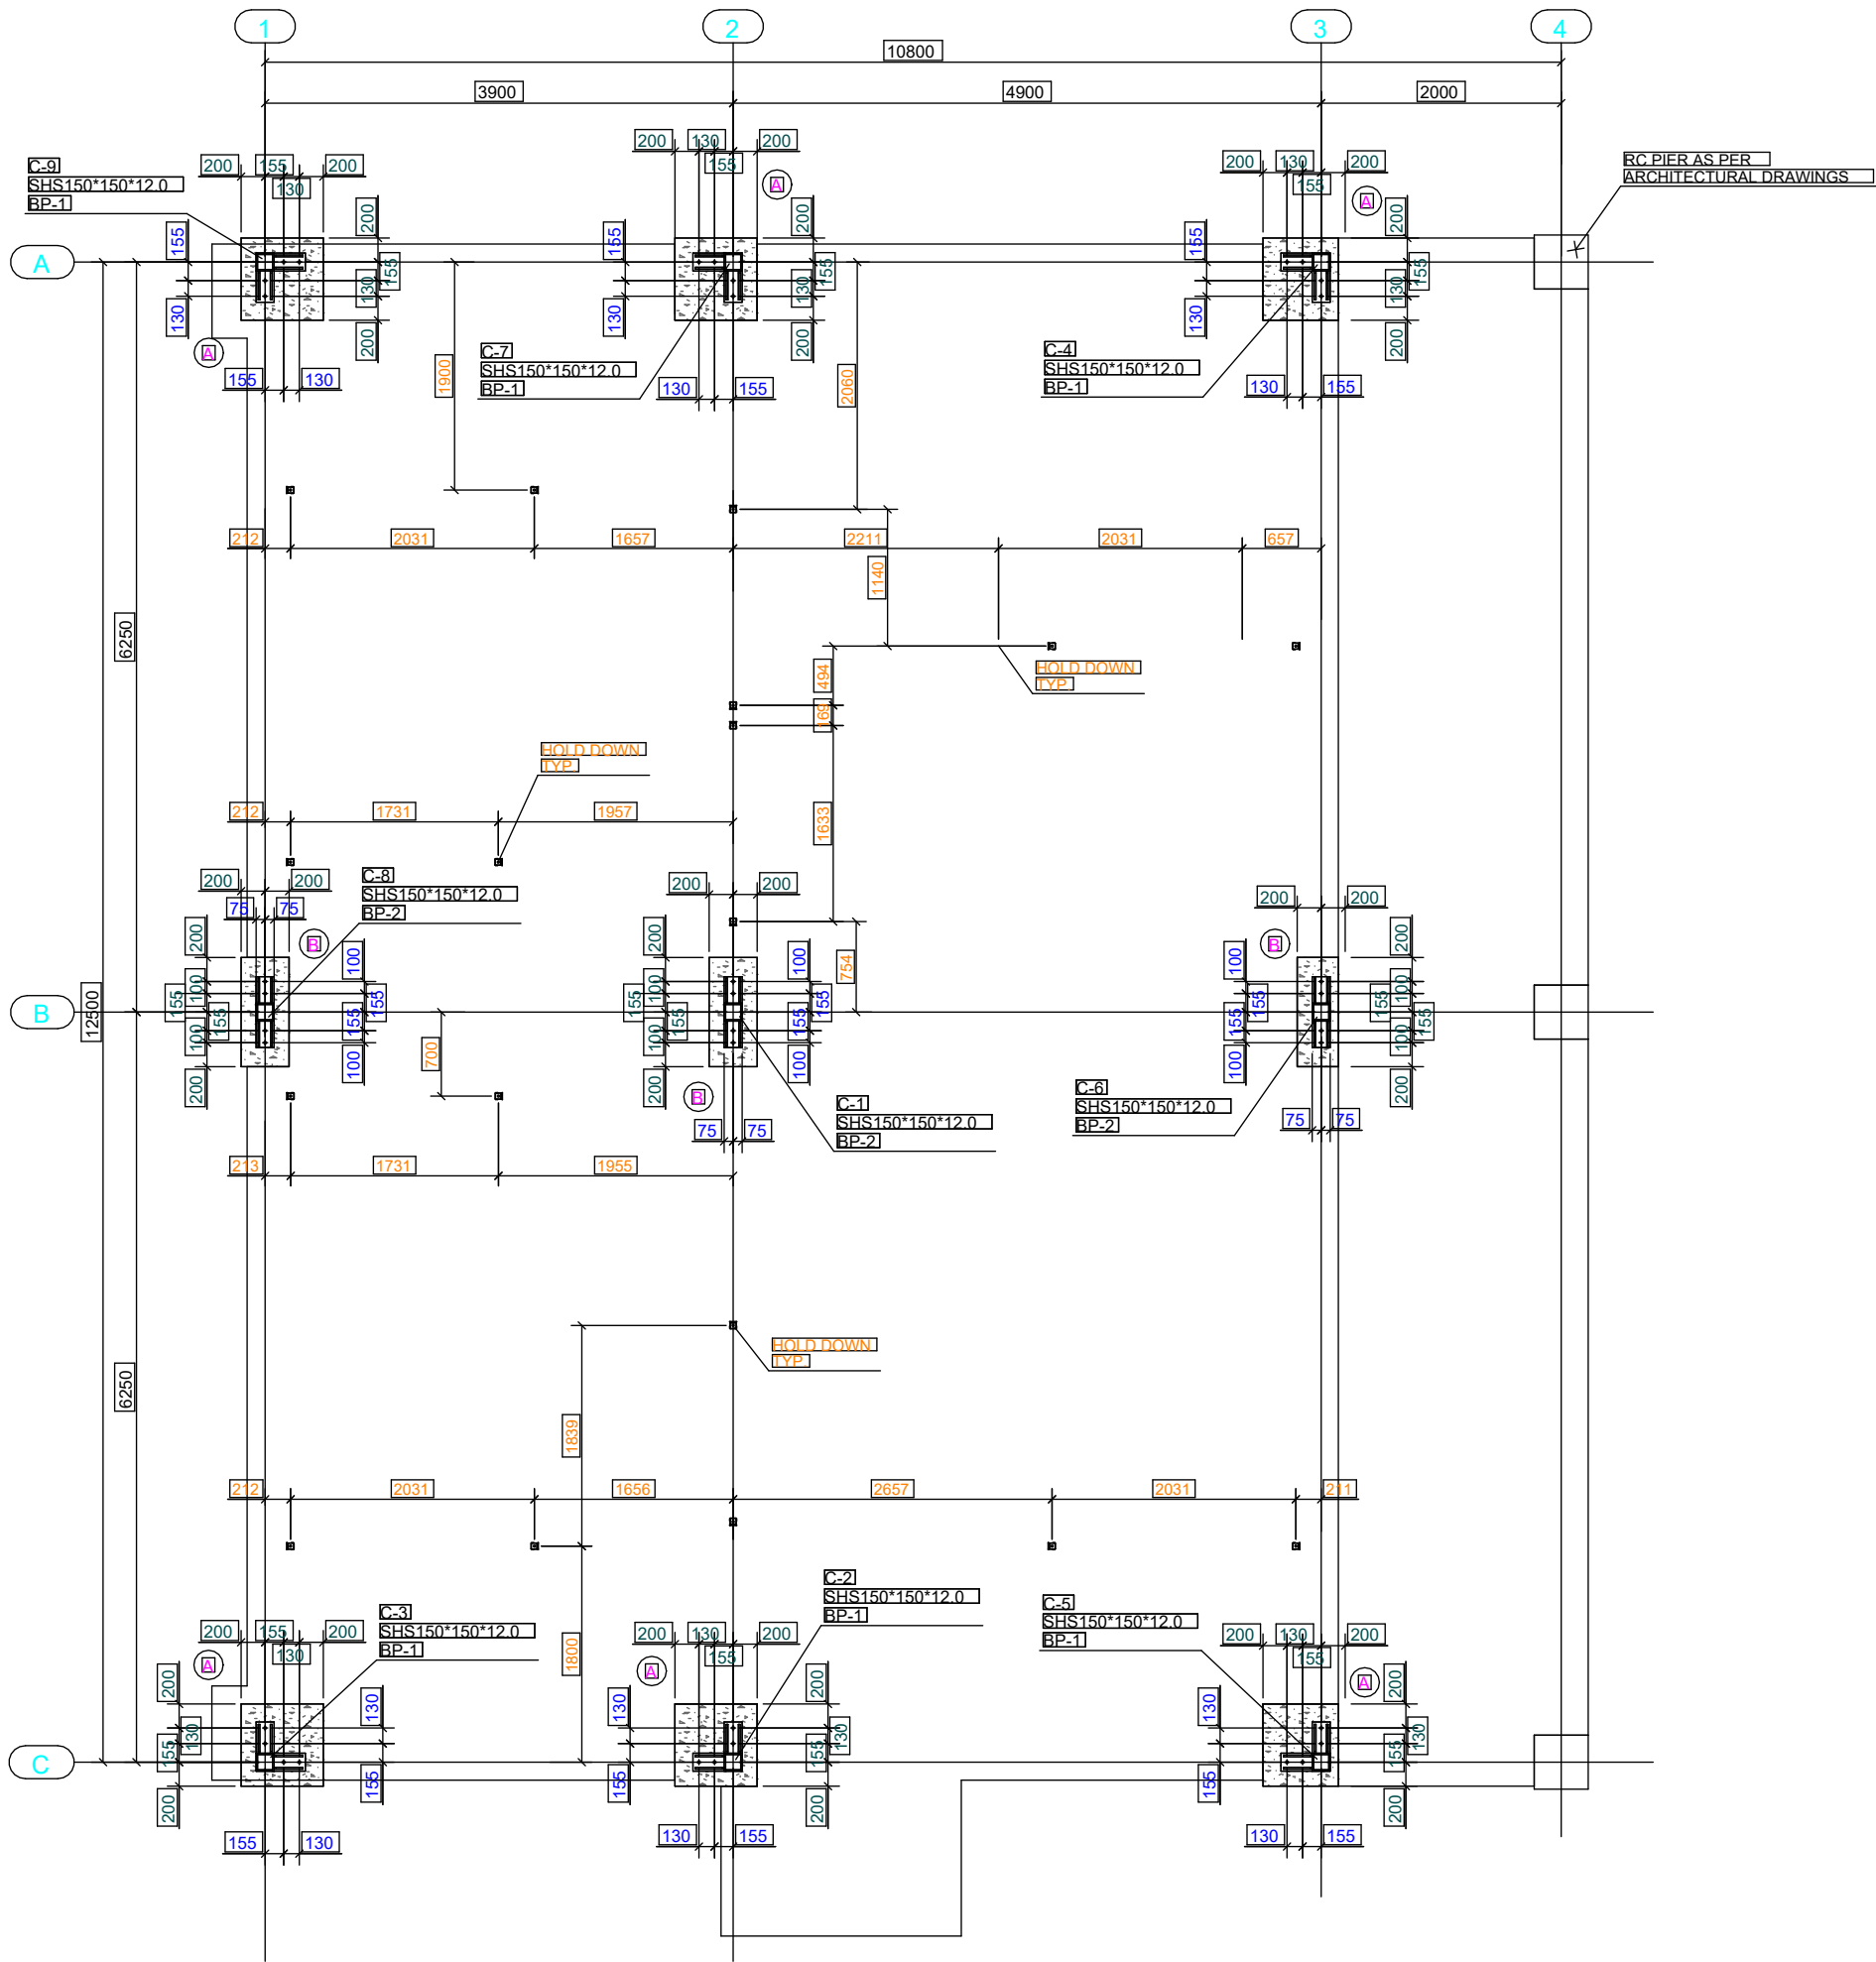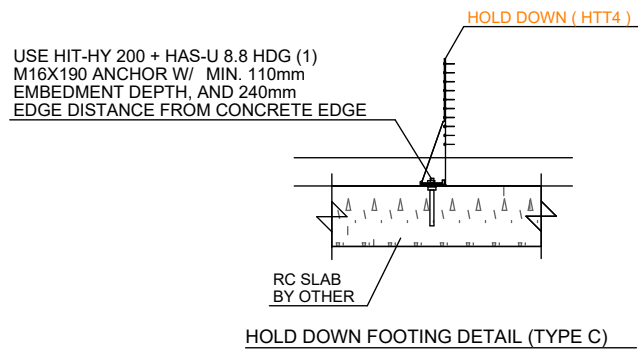

Note:

- Recommended foundation and slab plans and layout provided for information only. Refer to structural engineering plans for layout, connection details, stud embedment and edge distances.
- RC pier and footing depth according to site conditions.
- Baseplate plans and layout provided for information only.
- External columns will be provided assuming a 50mm (2") height drop between internal and external floor slabs

1. THESE DRAWINGS MUST BE CHECKED BY THE CUSTOMER OR CONTRACTOR PRIOR TO APPROVAL. ANY ERRORS OR OMISSIONS MUST BE REPORTED IN WRITING TO BAUHU PRIOR TO COMMENCEMENT OF CONSTRUCTION.
2. ARCHITECTURAL DRAWINGS SHOULD BE READ IN CONJUNCTION WITH STRUCTURAL DETAILING AND FABRICATION GENERAL ASSEMBLY DRAWINGS.
3. FOR CONSTRUCTION PURPOSES, USE ONLY THE LATEST APPROVED DRAWINGS LABELED 'ISSUED FOR CONSTRUCTION'.
4. DO NOT SCALE FROM THIS DRAWING.
5. THE COMPANY OPERATES USING METRIC DIMENSIONS AS THE PRINCIPAL DENOMINATION.
6. ALL CONCRETE WORKS ARE OUTSIDE OF THE SCOPE OF THE COMPANY. INFORMATION REGARDING SLAB DESIGN AND CONNECTIONS IN THESE DRAWINGS ARE INTENDED FOR GUIDANCE ONLY. FOUNDATION AND SLAB WORKS SHOULD BE DESIGNED AND APPROVED BY A LOCAL STRUCTURAL ENGINEER.
7. THE COMPANY RETAINS FULL TITLE AND OWNERSHIP OF THESE PLANS AND DESIGNS. ANY UNAUTHORISED USE, REPRODUCTION, OR DISTRIBUTION OF THESE PLANS, WHETHER IN WHOLE OR PART, IS EXPRESSLY PROHIBITED WITHOUT PRIOR WRITTEN CONSENT.

No.	Revision	Date

ISSUED FOR:

Issued for information

Issued for client approval

Issued for fabrication

Issued for construction

Angel

DRAWING TITLE:

Anchor Reinforcement Detail

DRAWN BY:

Yonca A.Clark

SCALE:


1 : 11

DRAWING NO:




A120

DATE:



01/05/2024

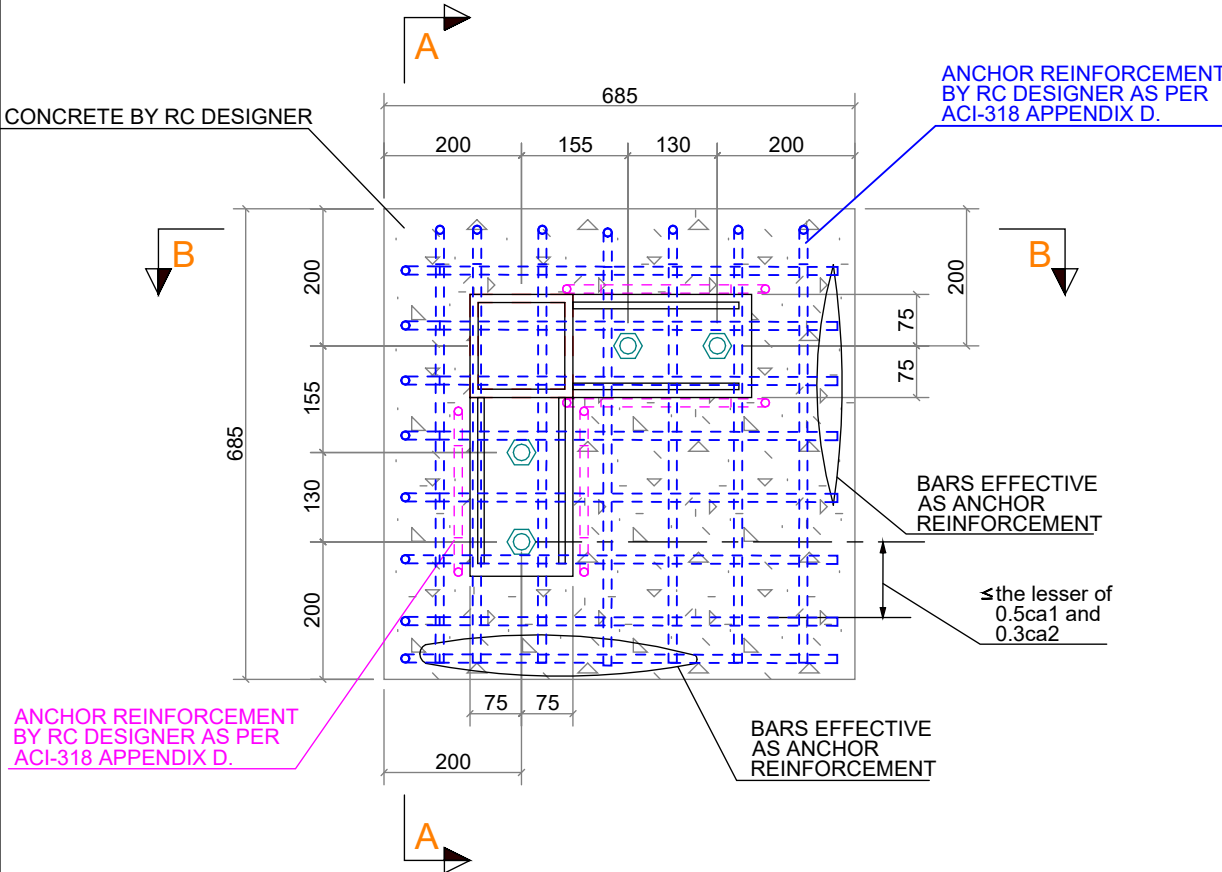

L TYPE BASE PLATE

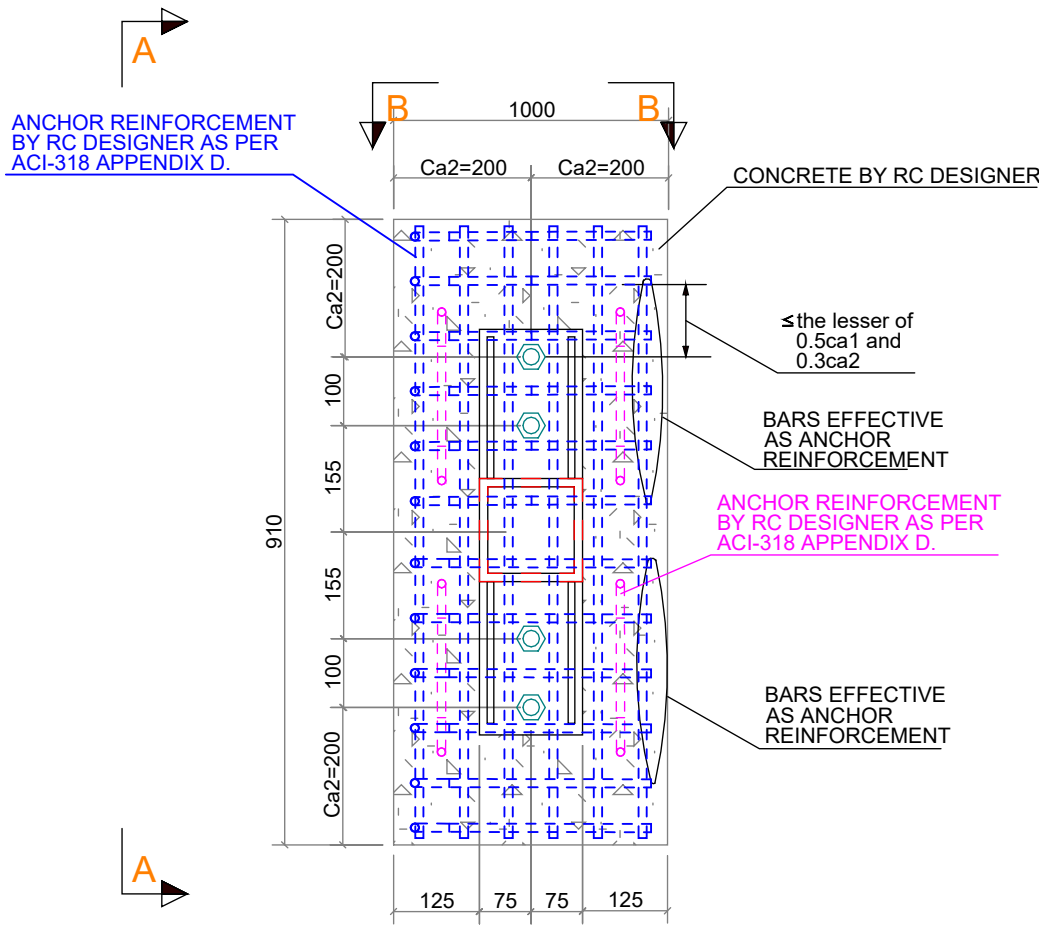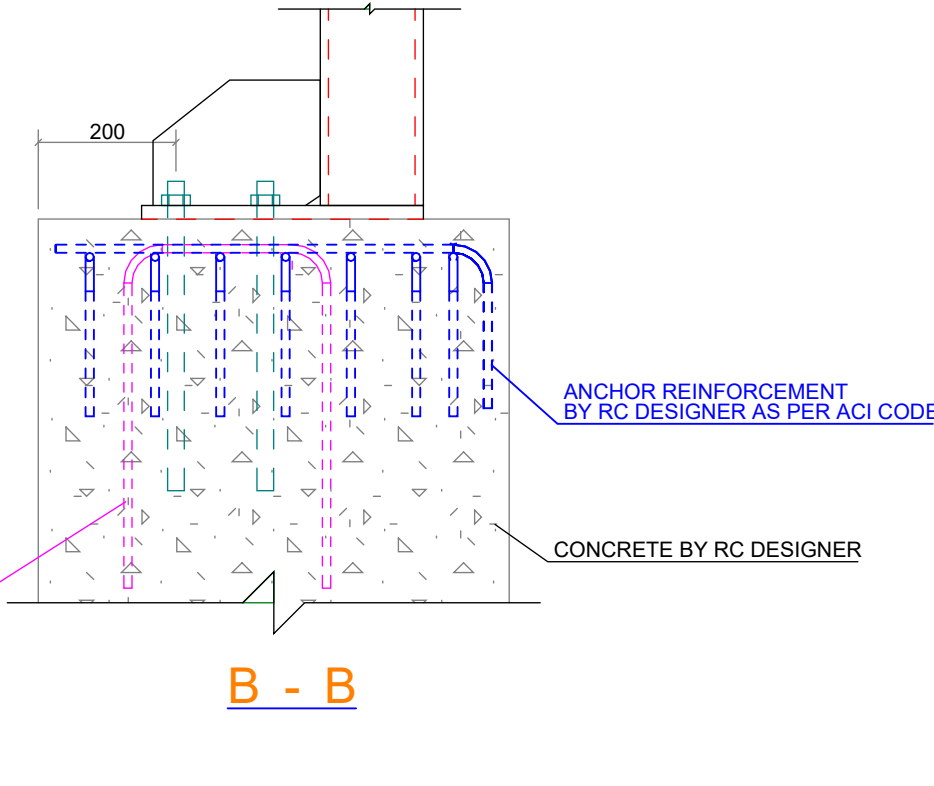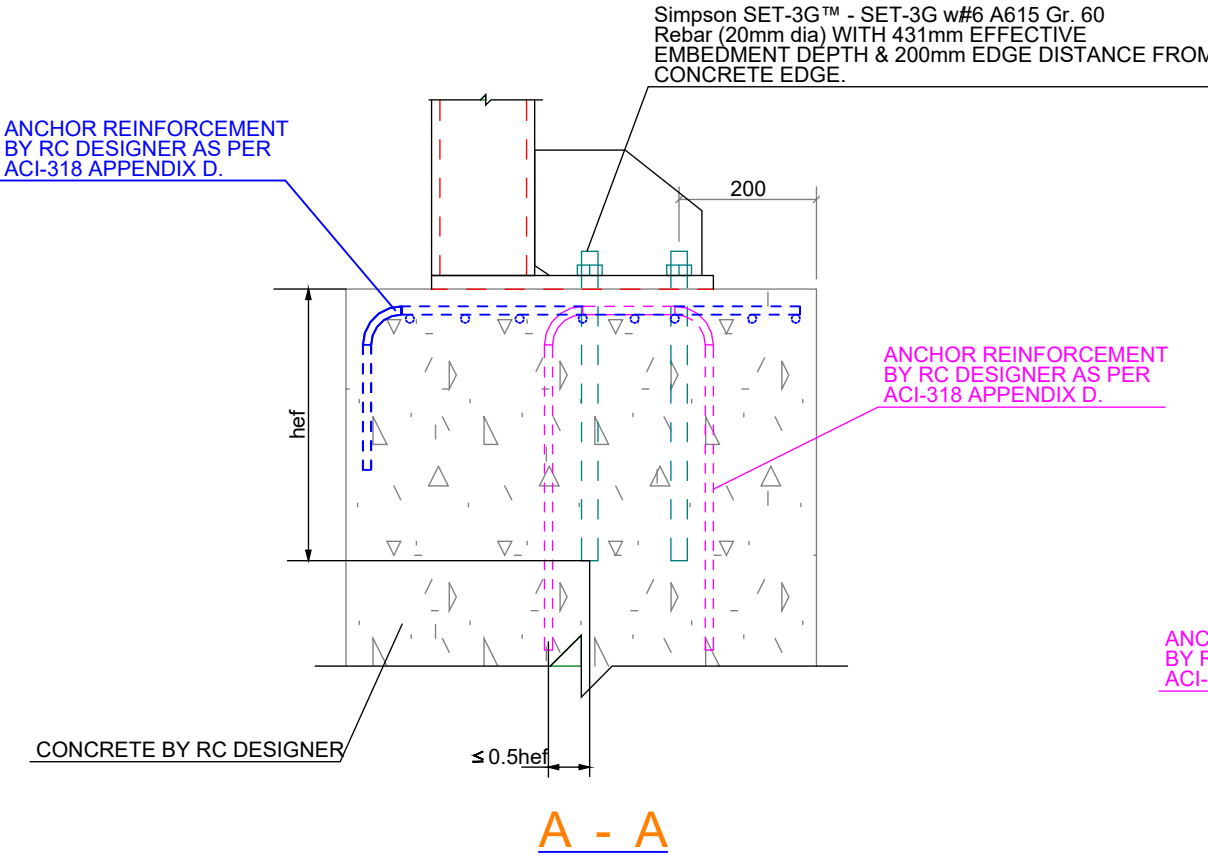

STRAIGHT BASE PLATE

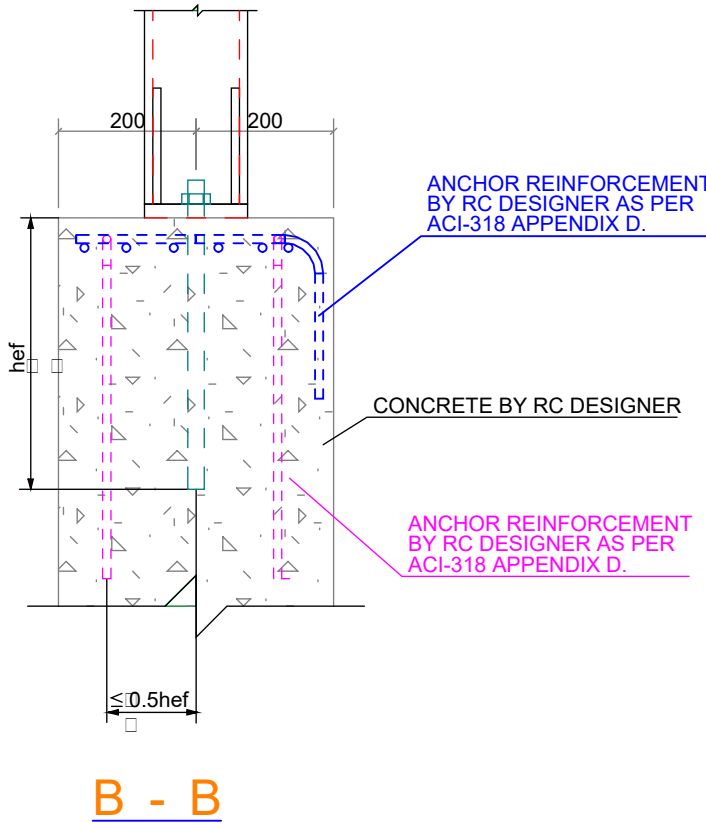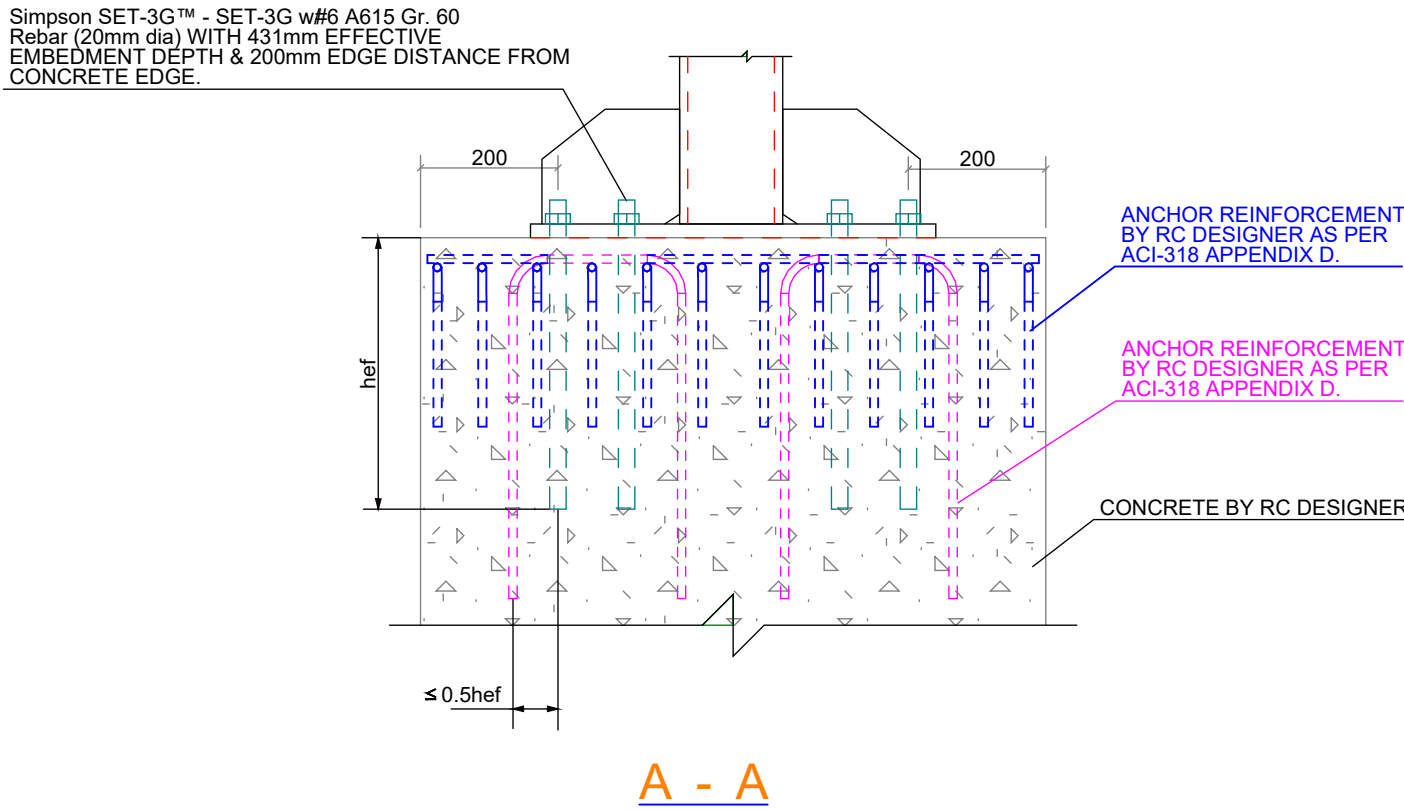

1. THESE DRAWINGS MUST BE CHECKED BY THE CUSTOMER OR CONTRACTOR PRIOR TO APPROVAL. ANY ERRORS OR OMISSIONS MUST BE REPORTED IN WRITING TO BAUHU PRIOR TO COMMENCEMENT OF CONSTRUCTION.
2. ARCHITECTURAL DRAWINGS SHOULD BE READ IN CONJUNCTION WITH STRUCTURAL DETAILING AND FABRICATION GENERAL ASSEMBLY DRAWINGS.
3. FOR CONSTRUCTION PURPOSES, USE ONLY THE LATEST APPROVED DRAWINGS LABELED 'ISSUED FOR CONSTRUCTION'.
4. DO NOT SCALE FROM THIS DRAWING.
5. THE COMPANY OPERATES USING METRIC DIMENSIONS AS THE PRINCIPAL DENOMINATION.
6. ALL CONCRETE WORKS ARE OUTSIDE OF THE SCOPE OF THE COMPANY. INFORMATION REGARDING SLAB DESIGN AND CONNECTIONS IN THESE DRAWINGS ARE INTENDED FOR GUIDENCE ONLY. FOUNDATION AND SLAB WORKS SHOULD BE DESIGNED AND APPROVED BY A LOCAL STRUCTURAL ENGINEER.
7. THE COMPANY RETAINS FULL TITLE AND OWNERSHIP OF THESE PLANS AND DESIGNS. ANY UNAUTHORISED USE, REPRODUCTION, OR DISTRIBUTION OF THESE PLANS, WHETHER IN WHOLE OR PART, IS EXPRESSLY PROHIBITED WITHOUT PRIOR WRITTEN CONSENT.

No.	Revision	Date

ISSUED FOR:

Issued for information

Issued for client approval

Issued for fabrication

Issued for construction

Angel

DRAWING TITLE:

Recommended Foundation
Requirement

DRAWN BY:

Yonca A.Clark


SCALE:

DRAWING NO:

A121

DATE:

01/05/2024

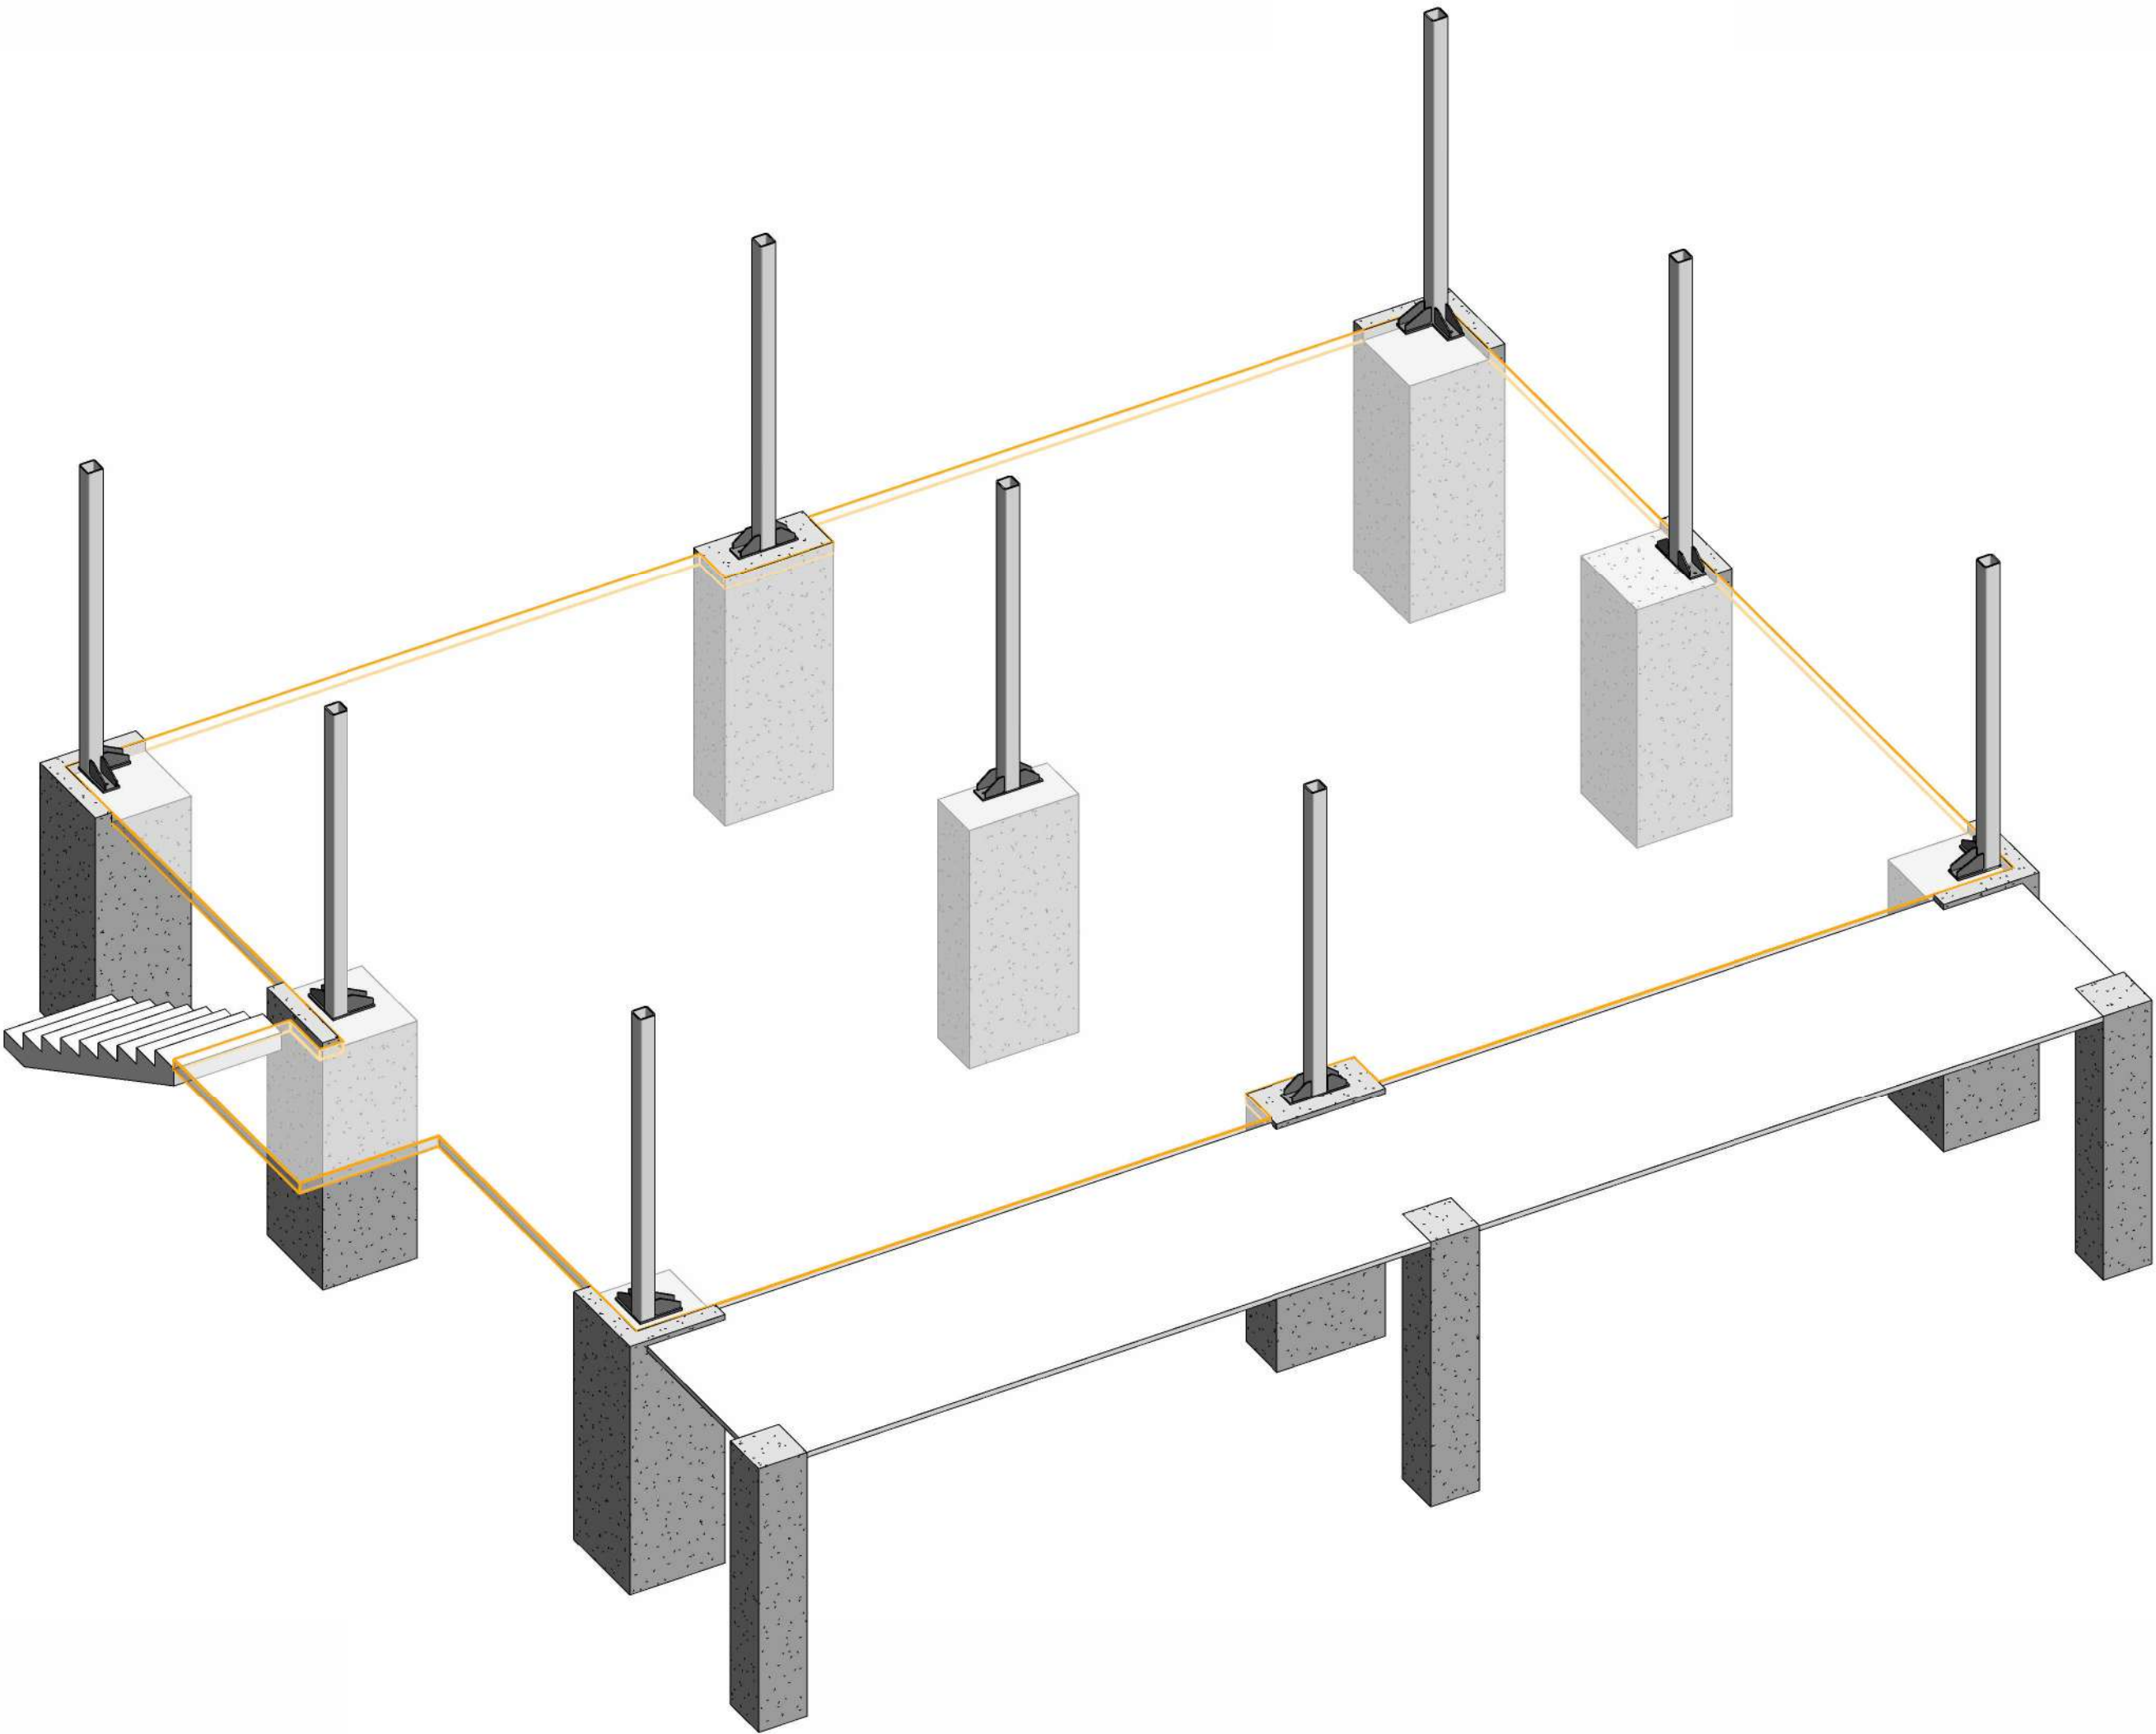

- Note:
- RC pier and footing depth according to site conditions.
 - Recommended foundation and slab plans and layout provided for information only. Refer to structural engineering plans for layout,connection details, stud embedment and edge distances.
 - RC pier and footing depth according to site conditions.
 - Baseplate plans and layout provided for information only.
 - External columns will be provided assuming a 50mm (2") height drop between internal and external floor slabs

Wall Details


Exterior Wall

- Interior side
- Selected Paint Finish
 - Gypsum Wall Board - Moisture resistant (12.5mm)
 - Gypsum Wall Board - Fire resistant (12.5mm)
 - Light Gauge Steel Frame (150mm)
 - Mineral Rockwool (120mm) between LGS studs
 - Vapour barrier
 - Secolite with joints and screws filled (12.5mm)
 - Secolite skim coat with embedded mesh (4mm)
 - Sto level duo plus glue
 - Rigid Insulation 40mm
 - STO Cement-free Reinforcing Coat with Mesh
 - STO Decorative Render Finish Plaster
- Exterior side


Interior Wall

- Interior side
- Selected Paint Finish
 - Gypsum Wall Board - Moisture resistant (12.5mm)
 - Gypsum Wall Board - Fire resistant (12.5mm)
 - Light Gauge Steel Frame (150mm)
 - Mineral Rockwool (150mm)
 - Gypsum Wall Board - Fire resistant (12.5mm)
 - Gypsum Wall Board - Moisture resistant (12.5mm)
 - Selected Paint Finish
- Interior side


D1.Exterior - Interior Wall Connection Sc: 1:6

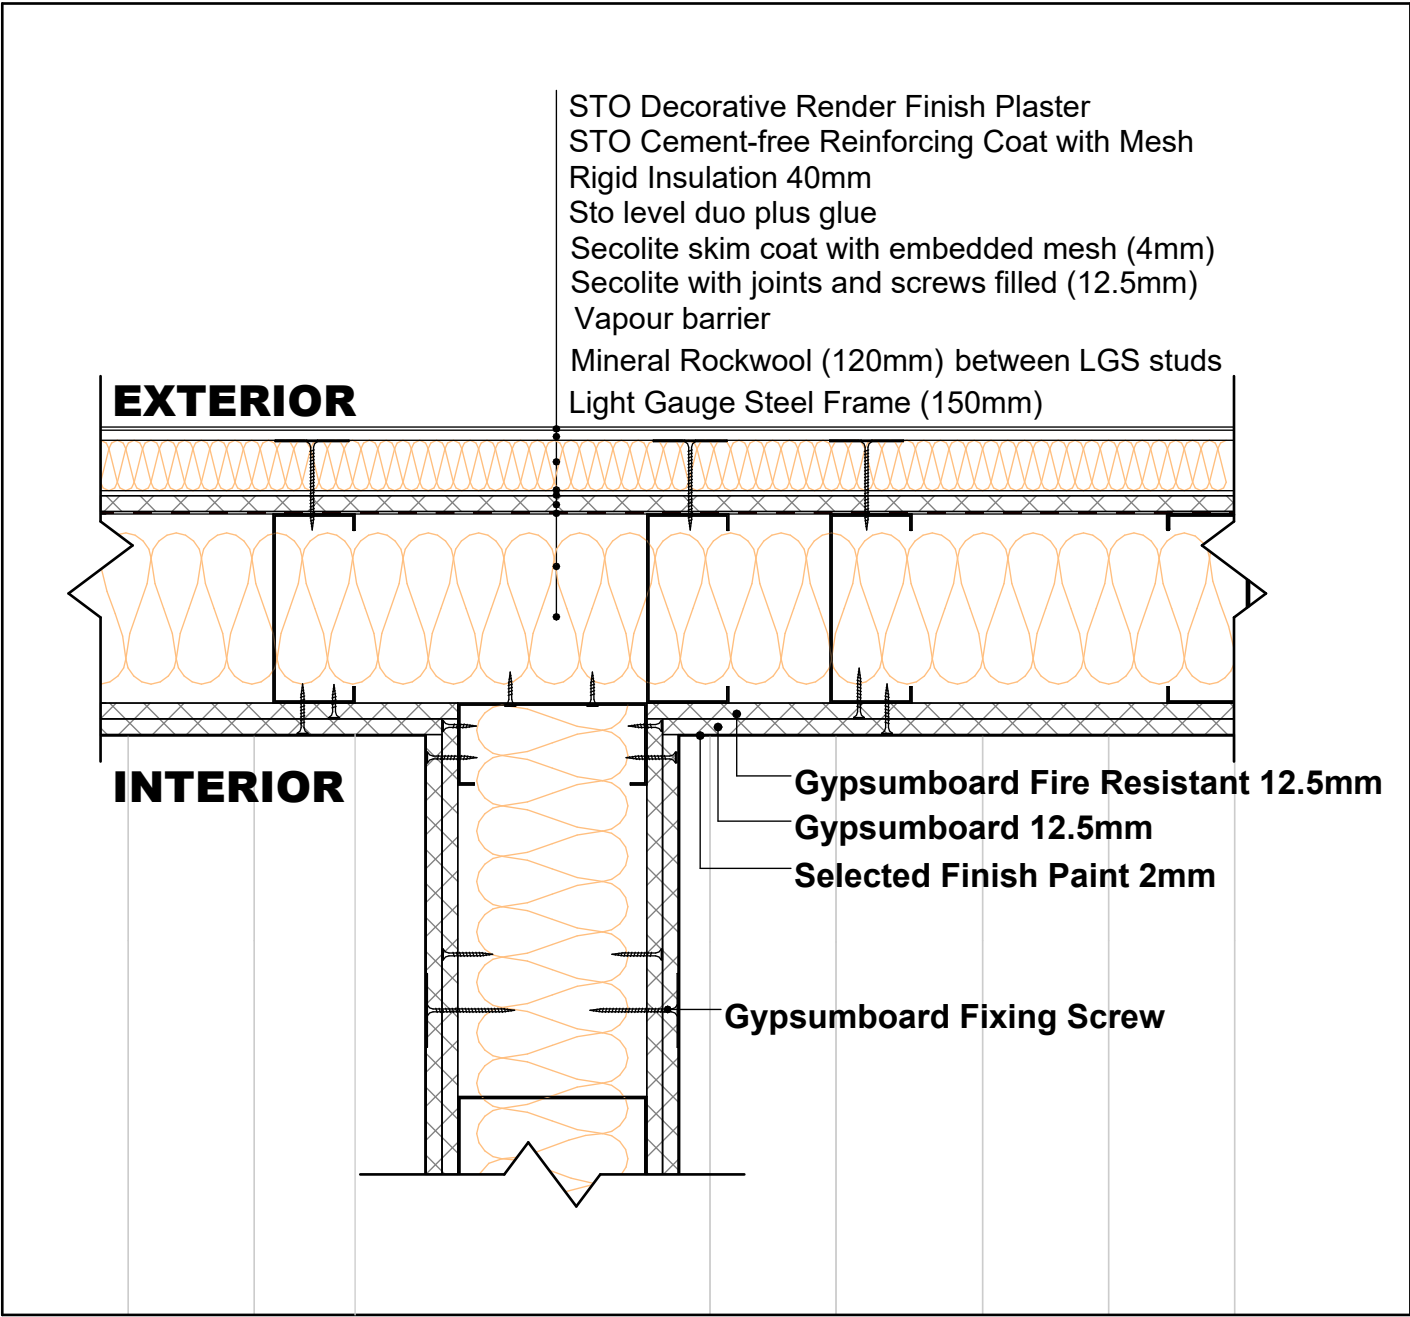

D2.Exterior - Interior Wall Connection Sc: 1:6

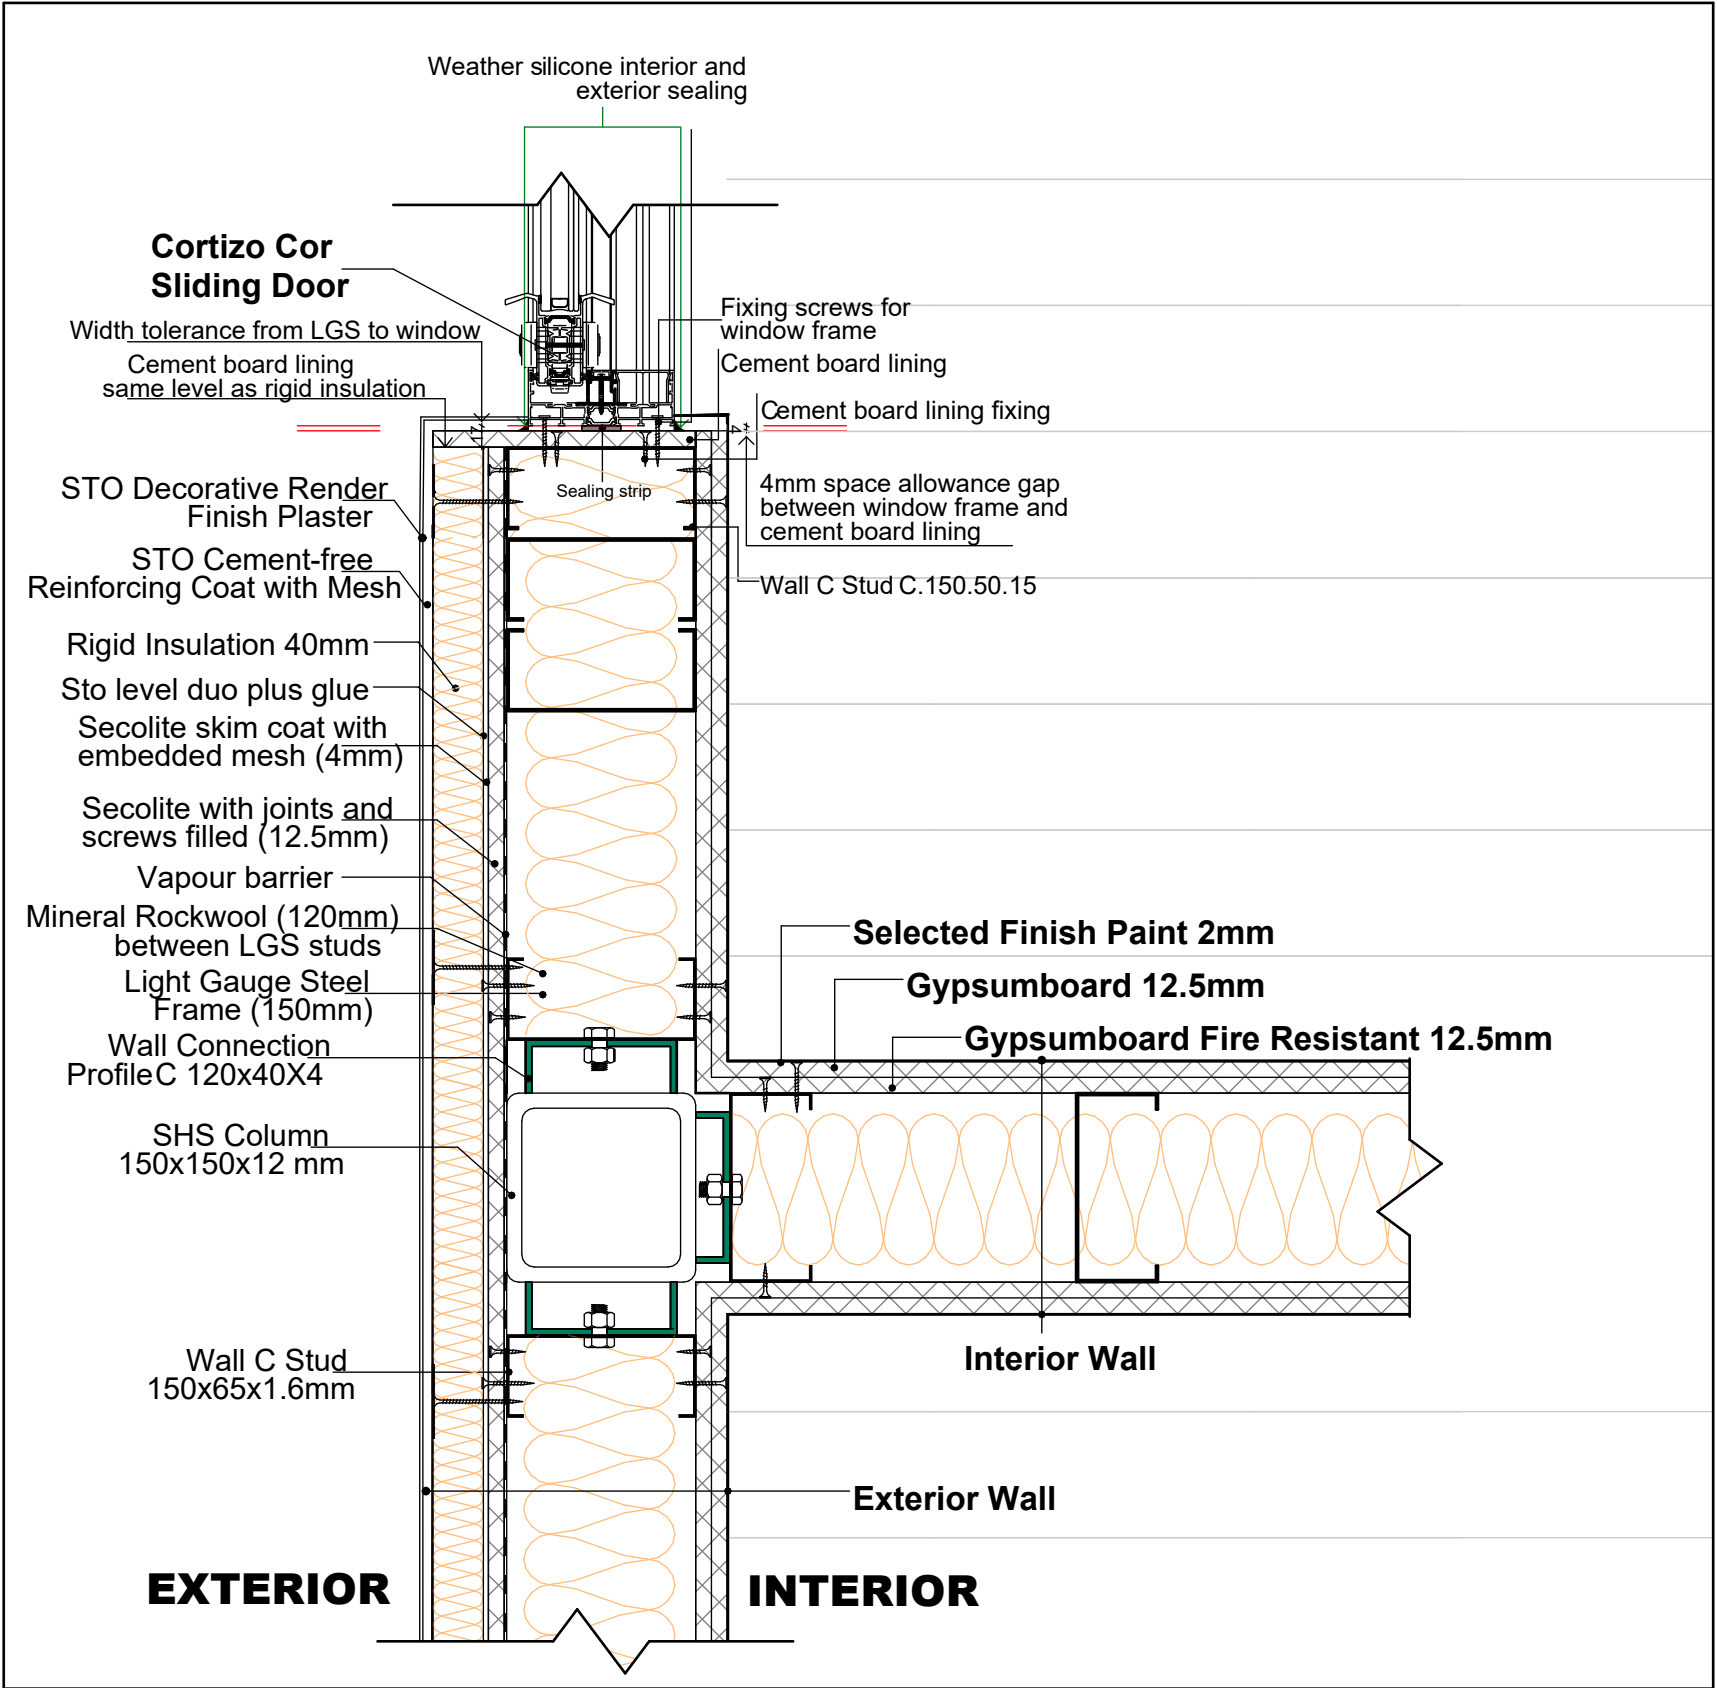

D3.Exterior Corner Wall Sc: 1:6

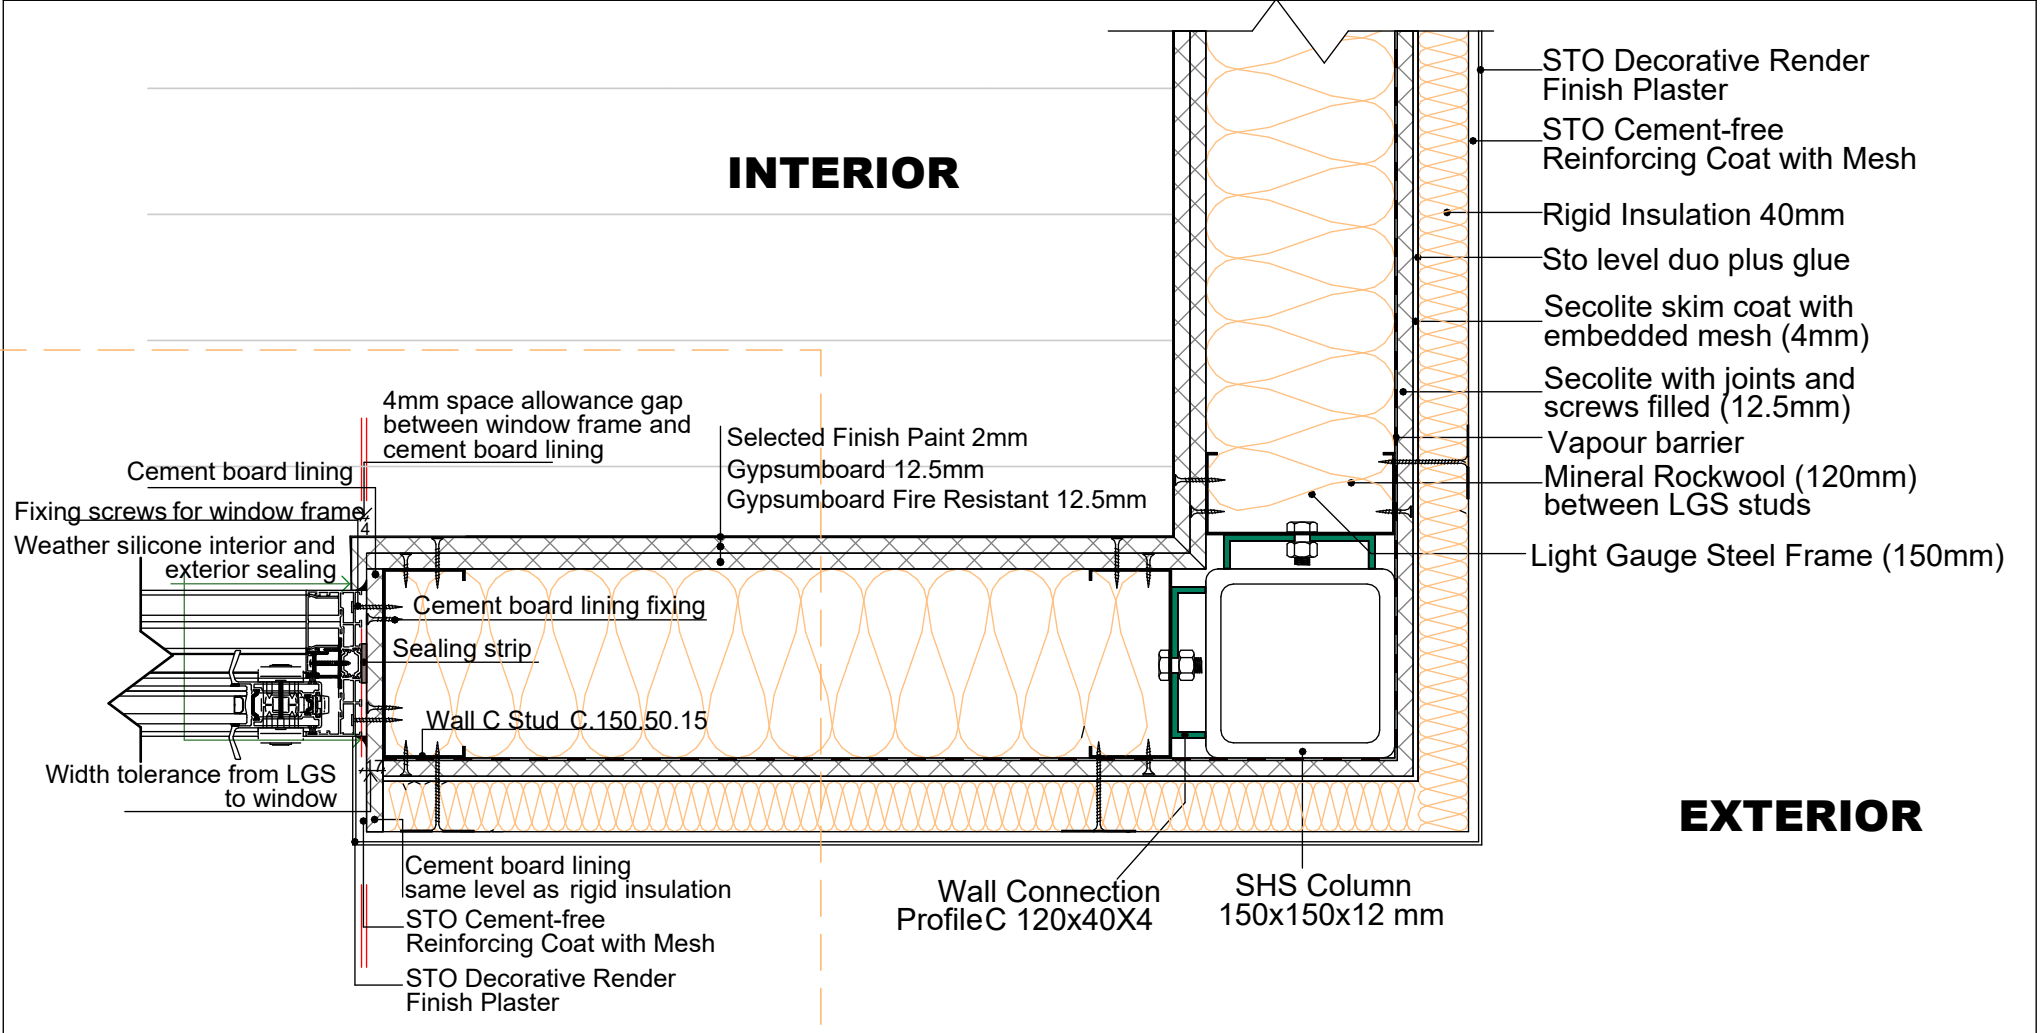

D4

1. THESE DRAWINGS MUST BE CHECKED BY THE CUSTOMER OR CONTRACTOR PRIOR TO APPROVAL. ANY ERRORS OR OMISSIONS MUST BE REPORTED IN WRITING TO BAUHU PRIOR TO COMMENCEMENT OF CONSTRUCTION.
2. ARCHITECTURAL DRAWINGS SHOULD BE READ IN CONJUNCTION WITH STRUCTURAL DETAILING AND FABRICATION GENERAL ASSEMBLY DRAWINGS.
3. FOR CONSTRUCTION PURPOSES, USE ONLY THE LATEST APPROVED DRAWINGS LABELED 'ISSUED FOR CONSTRUCTION'.
4. DO NOT SCALE FROM THIS DRAWING.
5. THE COMPANY OPERATES USING METRIC DIMENSIONS AS THE PRINCIPAL DENOMINATION.
6. ALL CONCRETE WORKS ARE OUTSIDE OF THE SCOPE OF THE COMPANY. INFORMATION REGARDING SLAB DESIGN AND CONNECTIONS IN THESE DRAWINGS ARE INTENDED FOR GUIDANCE ONLY. FOUNDATION AND SLAB WORKS SHOULD BE DESIGNED AND APPROVED BY A LOCAL STRUCTURAL ENGINEER.
7. THE COMPANY RETAINS FULL TITLE AND OWNERSHIP OF THESE PLANS AND DESIGNS. ANY UNAUTHORISED USE, REPRODUCTION, OR DISTRIBUTION OF THESE PLANS, WHETHER IN WHOLE OR PART, IS EXPRESSLY PROHIBITED WITHOUT PRIOR WRITTEN CONSENT.

No.	Revision	Date

ISSUED FOR:

Issued for information

Issued for client approval

Issued for fabrication

Issued for construction

Angel

DRAWING TITLE: Details 1


DRAWN BY: Mladin Monica-Mihaela

SCALE: 1 : 6

DRAWING NO: A122

DATE: 01/05/2024

1. THESE DRAWINGS MUST BE CHECKED BY THE CUSTOMER OR CONTRACTOR PRIOR TO APPROVAL. ANY ERRORS OR OMISSIONS MUST BE REPORTED IN WRITING TO BAUHU PRIOR TO COMMENCEMENT OF CONSTRUCTION.
2. ARCHITECTURAL DRAWINGS SHOULD BE READ IN CONJUNCTION WITH STRUCTURAL DETAILING AND FABRICATION GENERAL ASSEMBLY DRAWINGS.
3. FOR CONSTRUCTION PURPOSES, USE ONLY THE LATEST APPROVED DRAWINGS LABELED 'ISSUED FOR CONSTRUCTION'.
4. DO NOT SCALE FROM THIS DRAWING.
5. THE COMPANY OPERATES USING METRIC DIMENSIONS AS THE PRINCIPAL DENOMINATION.
6. ALL CONCRETE WORKS ARE OUTSIDE OF THE SCOPE OF THE COMPANY. INFORMATION REGARDING SLAB DESIGN AND CONNECTIONS IN THESE DRAWINGS ARE INTENDED FOR GUIDENCE ONLY. FOUNDATION AND SLAB WORKS SHOULD BE DESIGNED AND APPROVED BY A LOCAL STRUCTURAL ENGINEER.
7. THE COMPANY RETAINS FULL TITLE AND OWNERSHIP OF THESE PLANS AND DESIGNS. ANY UNAUTHORISED USE, REPRODUCTION, OR DISTRIBUTION OF THESE PLANS, WHETHER IN WHOLE OR PART, IS EXPRESSLY PROHIBITED WITHOUT PRIOR WRITTEN CONSENT.

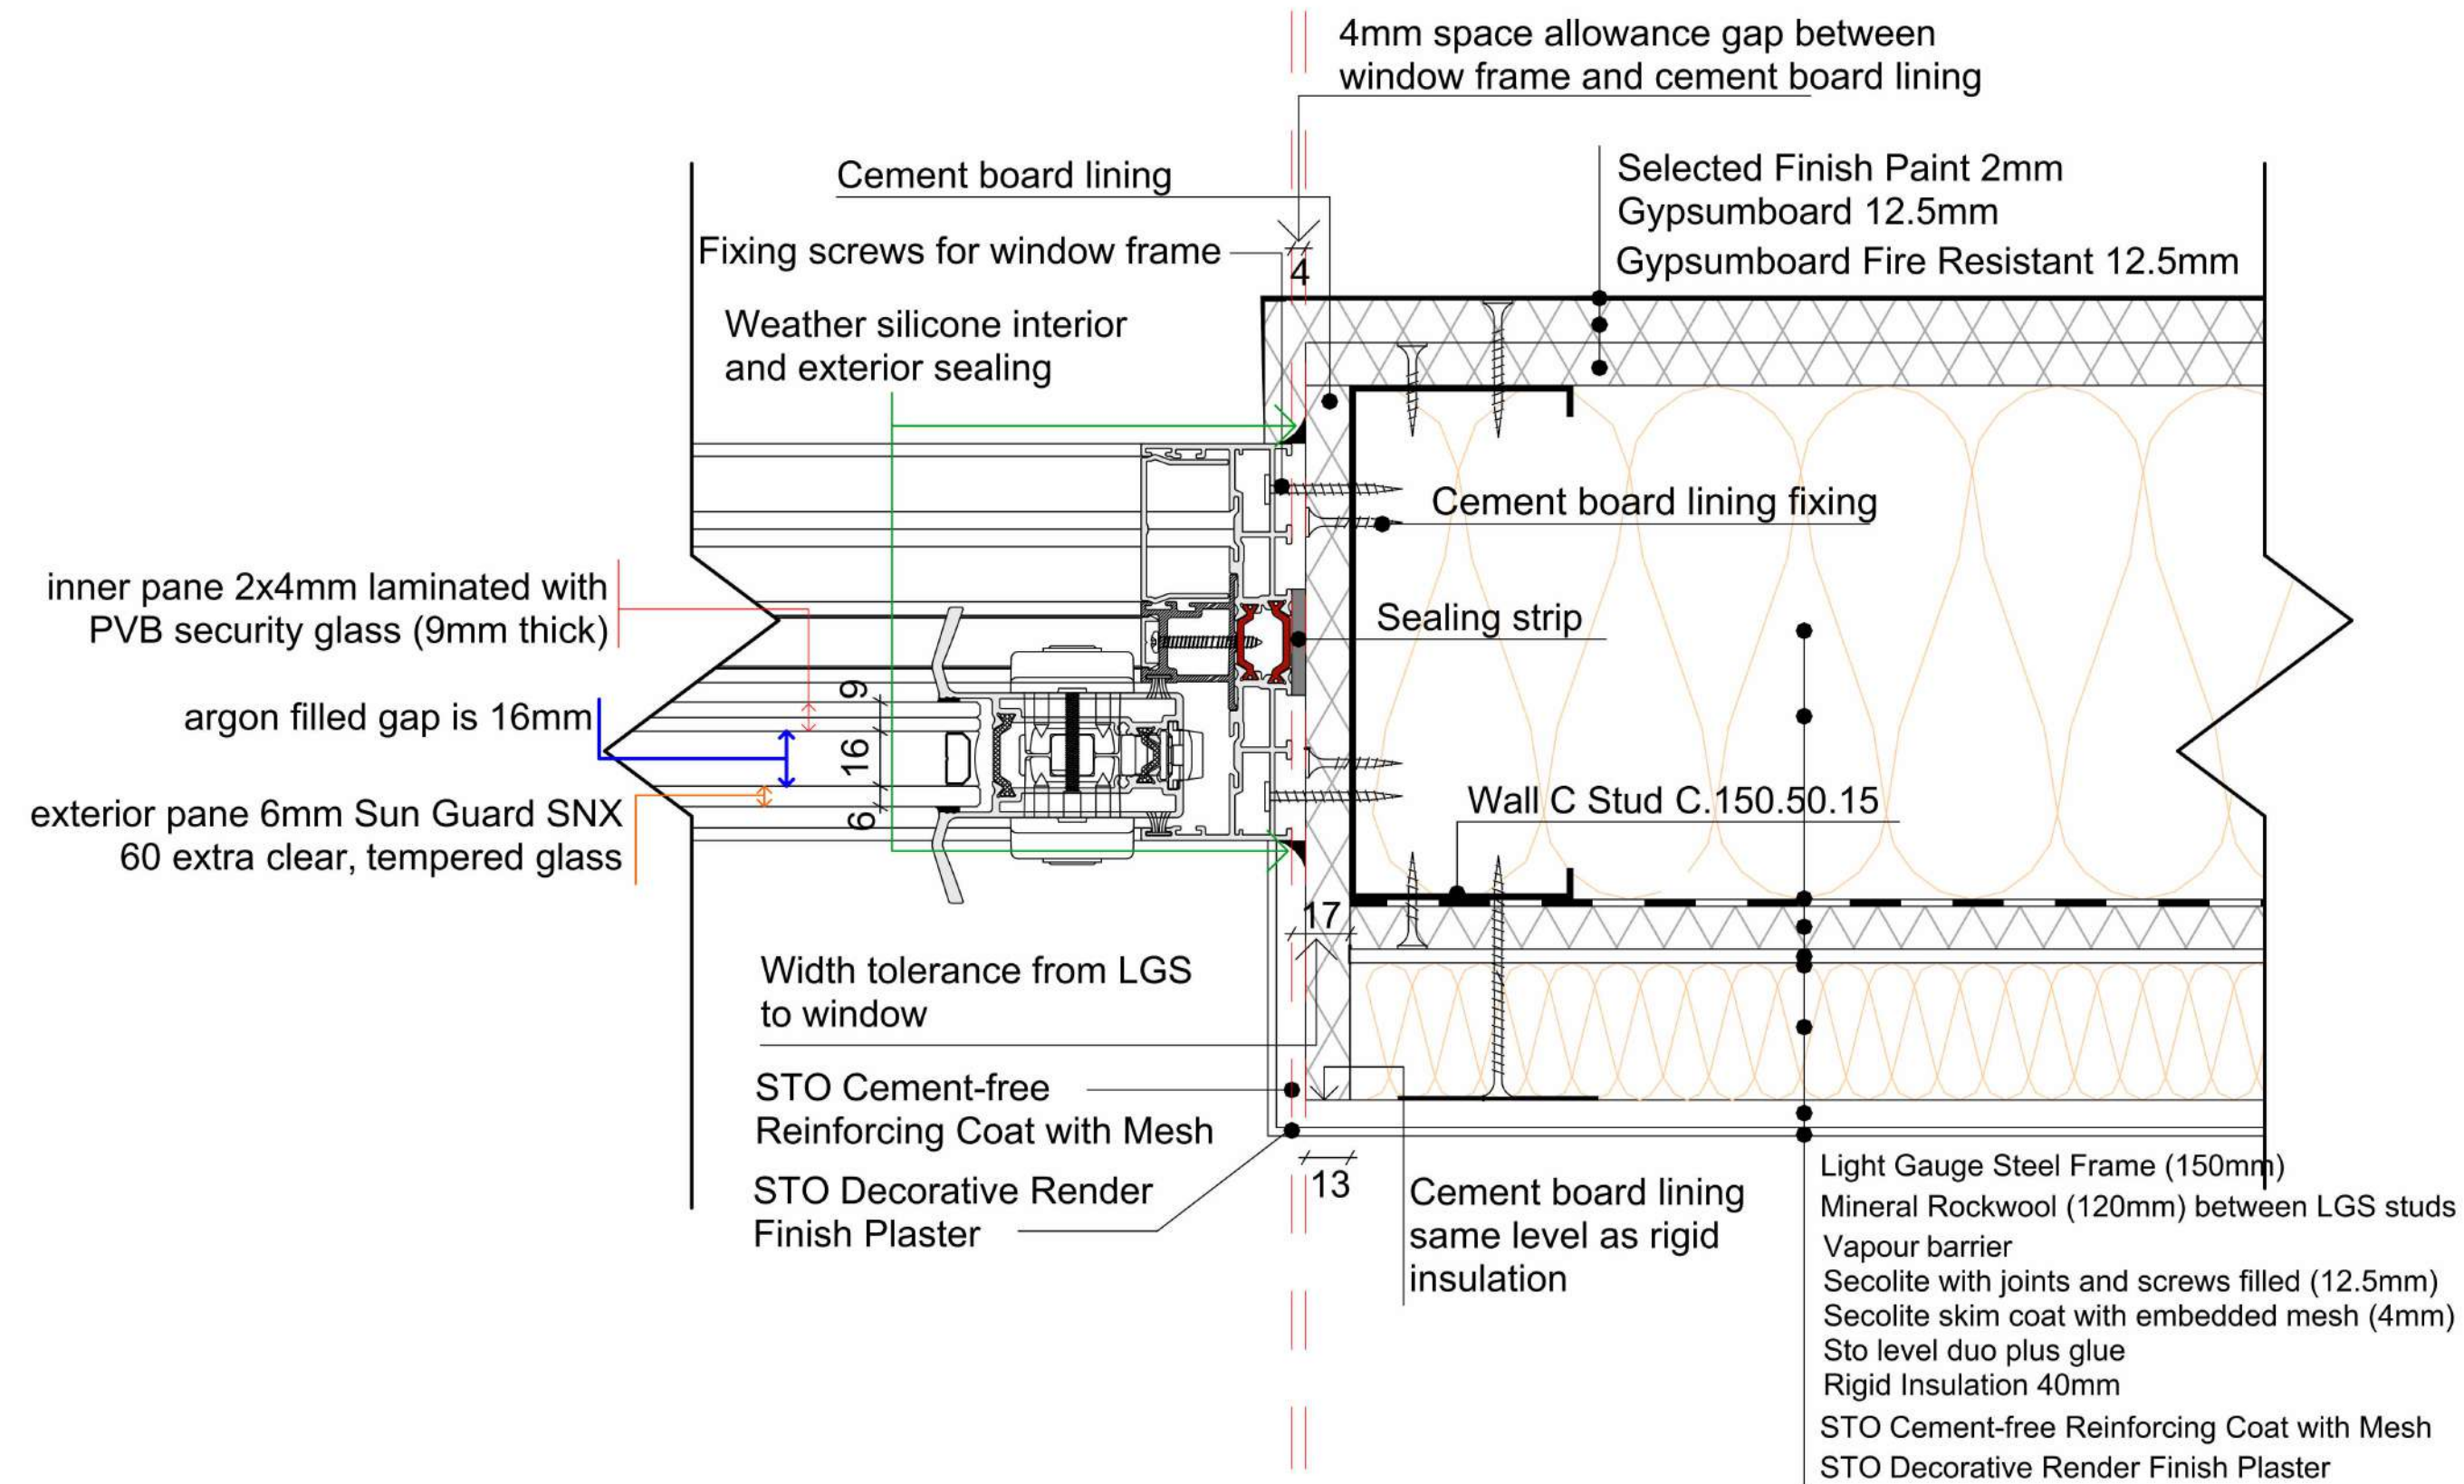

No.	Revision	Date

ISSUED FOR:

Issued for information

Issued for client approval

Issued for fabrication

Issued for construction

Angel

DRAWING TITLE:

Details 2

DRAWN BY:

Mladin Monica-Mihaela

SCALE:

1 : 2

DRAWING NO:

A123

DATE:

01/05/2024

D4. Sliding Window/door side fixing to wall Sc: 1:2

1. THESE DRAWINGS MUST BE CHECKED BY THE CUSTOMER OR CONTRACTOR PRIOR TO APPROVAL. ANY ERRORS OR OMISSIONS MUST BE REPORTED IN WRITING TO BAUHU PRIOR TO COMMENCEMENT OF CONSTRUCTION.
2. ARCHITECTURAL DRAWINGS SHOULD BE READ IN CONJUNCTION WITH STRUCTURAL DETAILING AND FABRICATION GENERAL ASSEMBLY DRAWINGS.
3. FOR CONSTRUCTION PURPOSES, USE ONLY THE LATEST APPROVED DRAWINGS LABELED 'ISSUED FOR CONSTRUCTION'.
4. DO NOT SCALE FROM THIS DRAWING.
5. THE COMPANY OPERATES USING METRIC DIMENSIONS AS THE PRINCIPAL DENOMINATION.
6. ALL CONCRETE WORKS ARE OUTSIDE OF THE SCOPE OF THE COMPANY. INFORMATION REGARDING SLAB DESIGN AND CONNECTIONS IN THESE DRAWINGS ARE INTENDED FOR GUIDENCE ONLY. FOUNDATION AND SLAB WORKS SHOULD BE DESIGNED AND APPROVED BY A LOCAL STRUCTURAL ENGINEER.
7. THE COMPANY RETAINS FULL TITLE AND OWNERSHIP OF THESE PLANS AND DESIGNS. ANY UNAUTHORIZED USE, REPRODUCTION, OR DISTRIBUTION OF THESE PLANS, WHETHER IN WHOLE OR PART, IS EXPRESSLY PROHIBITED WITHOUT PRIOR WRITTEN CONSENT.

No.	Revision	Date

ISSUED FOR:

Issued for information

Issued for client approval

Issued for fabrication

Issued for construction

Angel

DRAWING TITLE:

Details 3

DRAWN BY:

Mladin Monica-Mihaela

SCALE:


As indicated

DRAWING NO:


A124

DATE:


01/05/2024

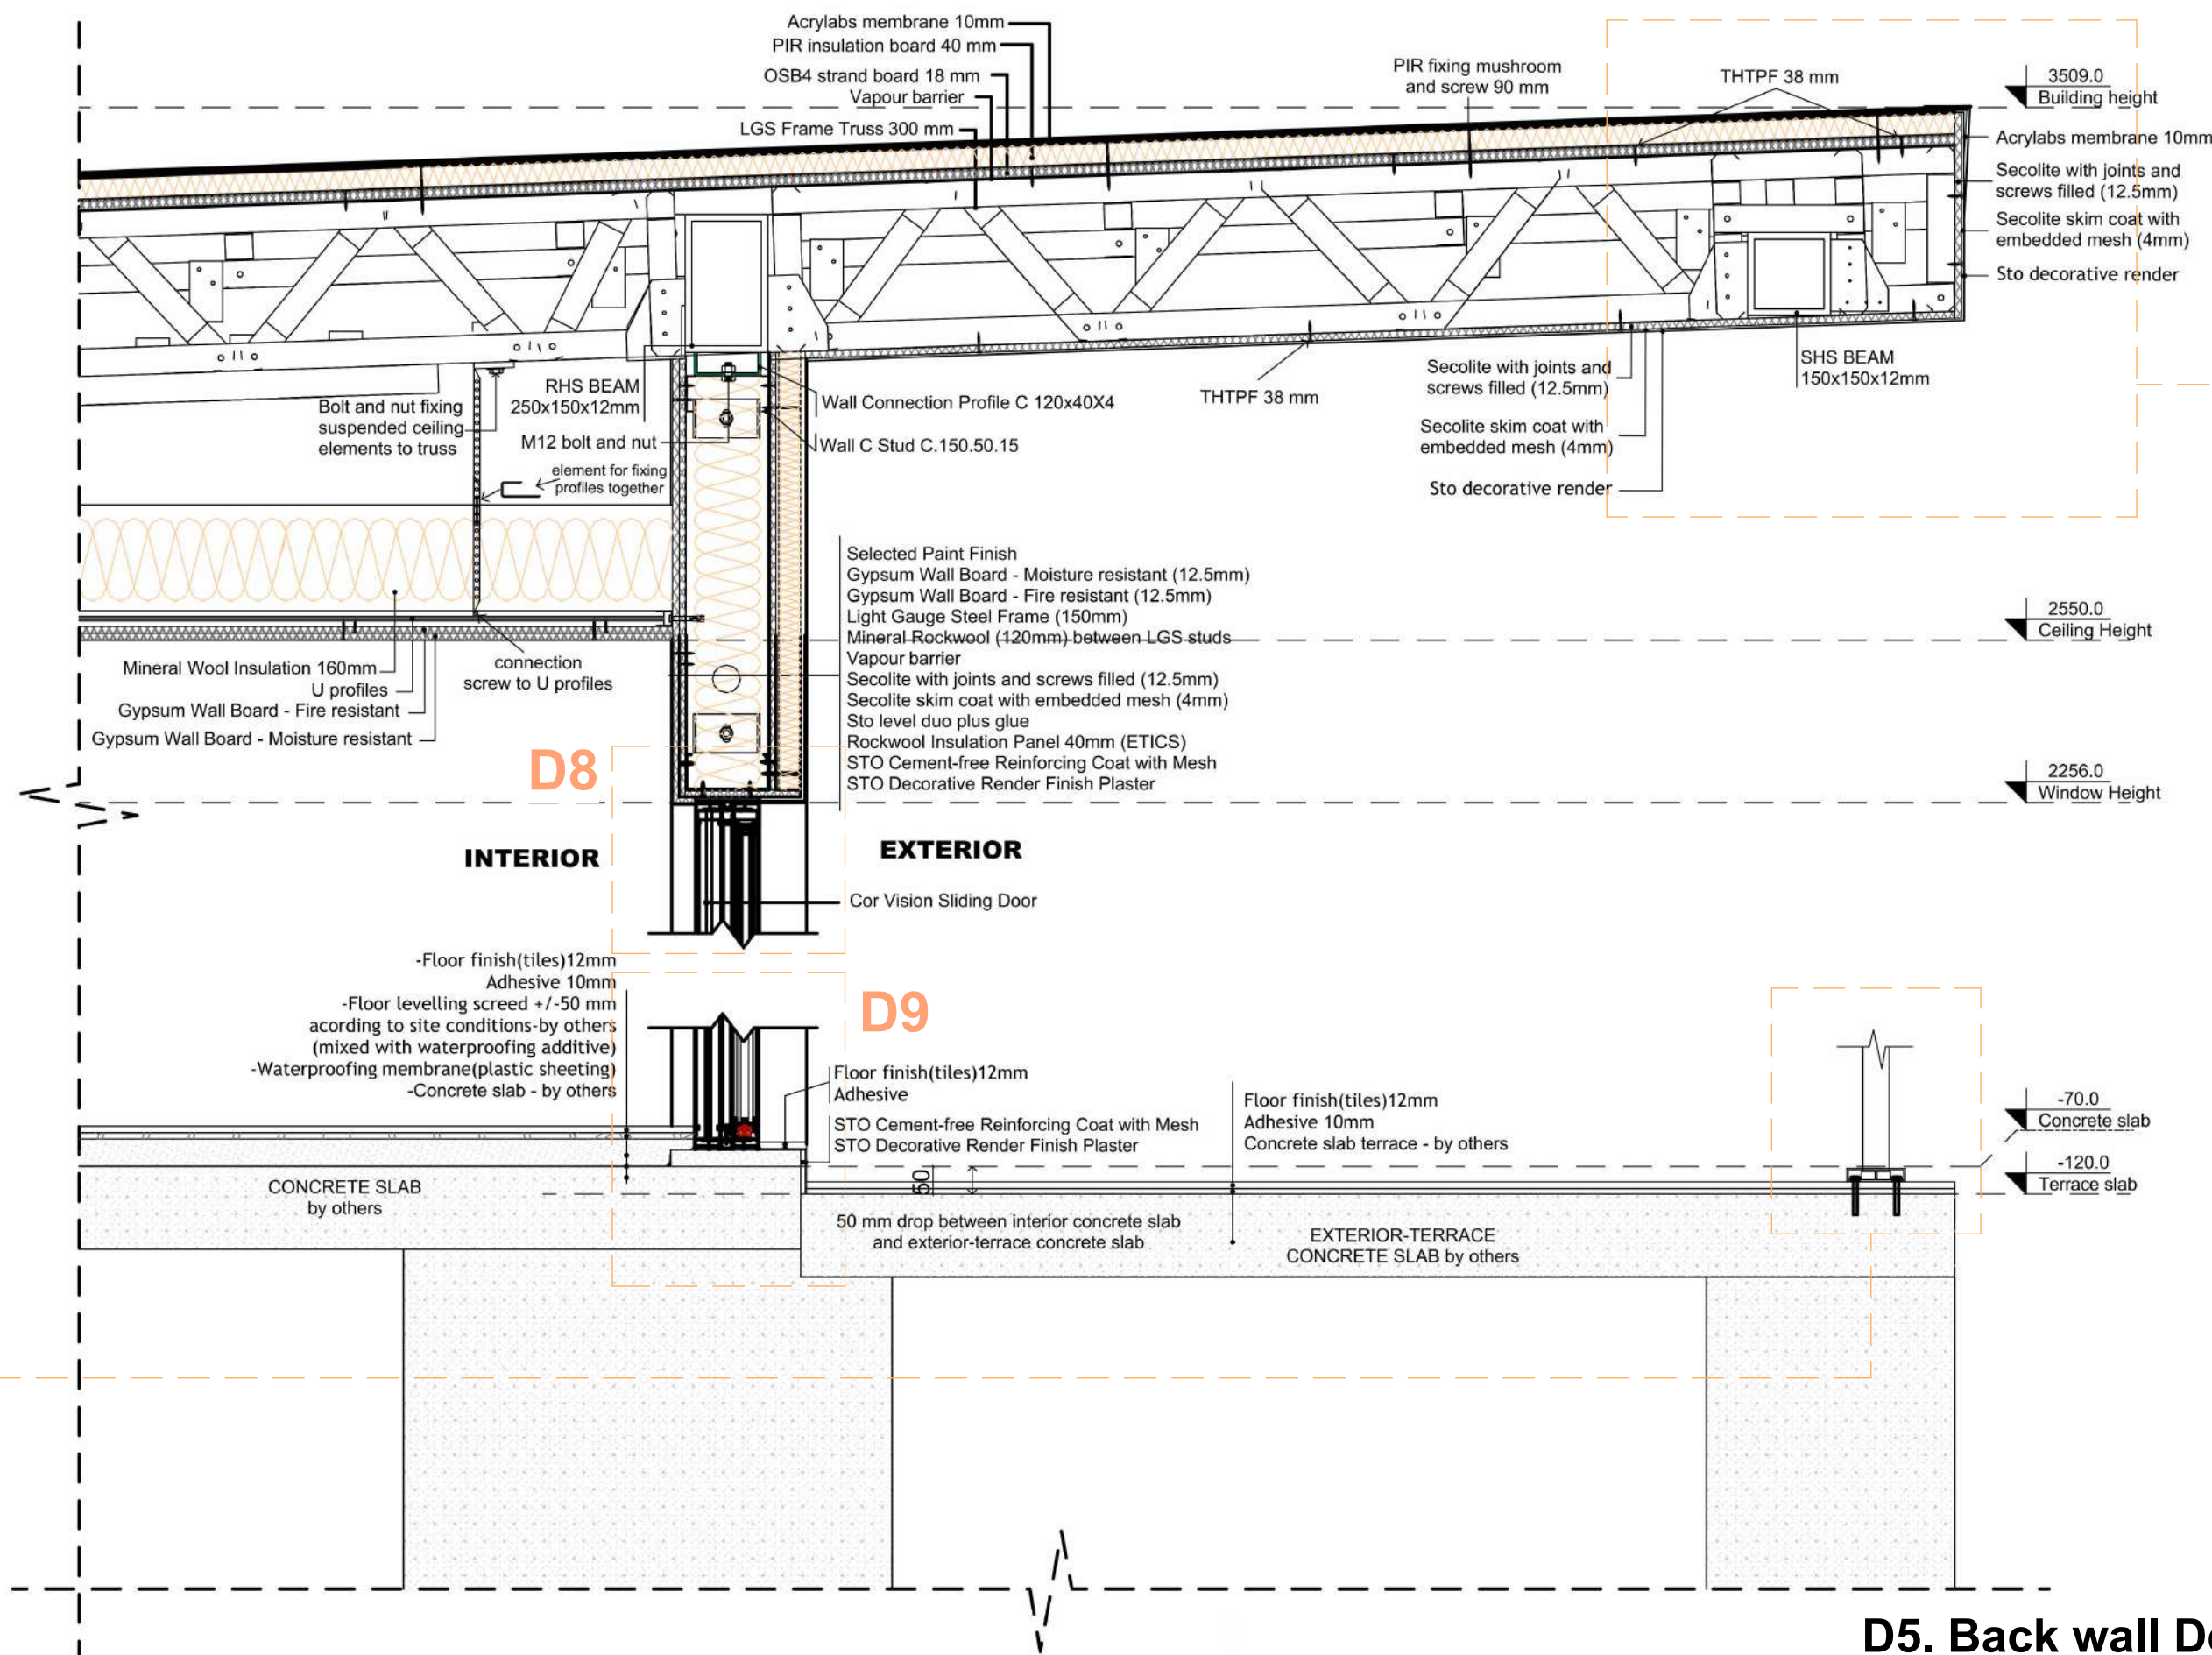

D6. Railing fixing Sc: 1:3

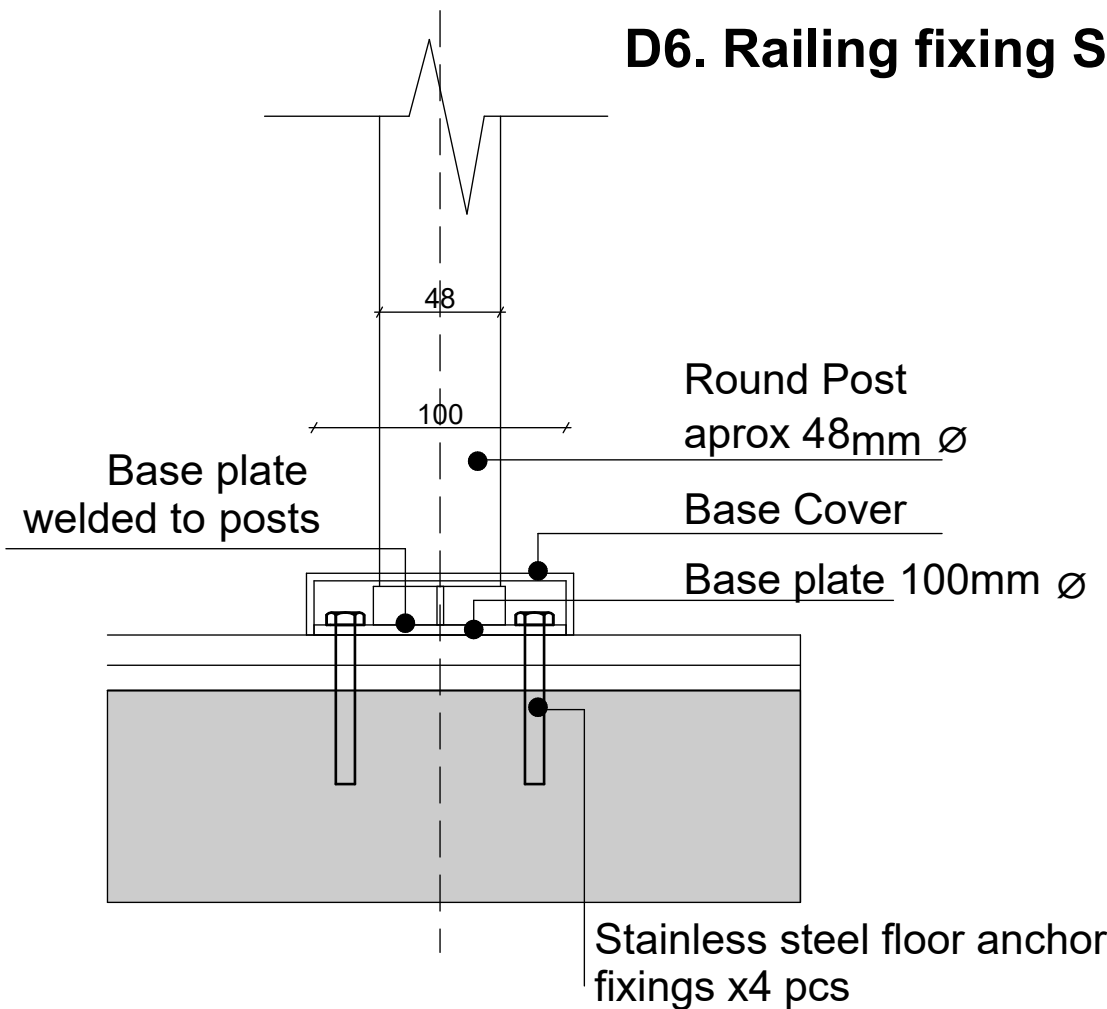

D5. Back wall Detail Sc: 1:12

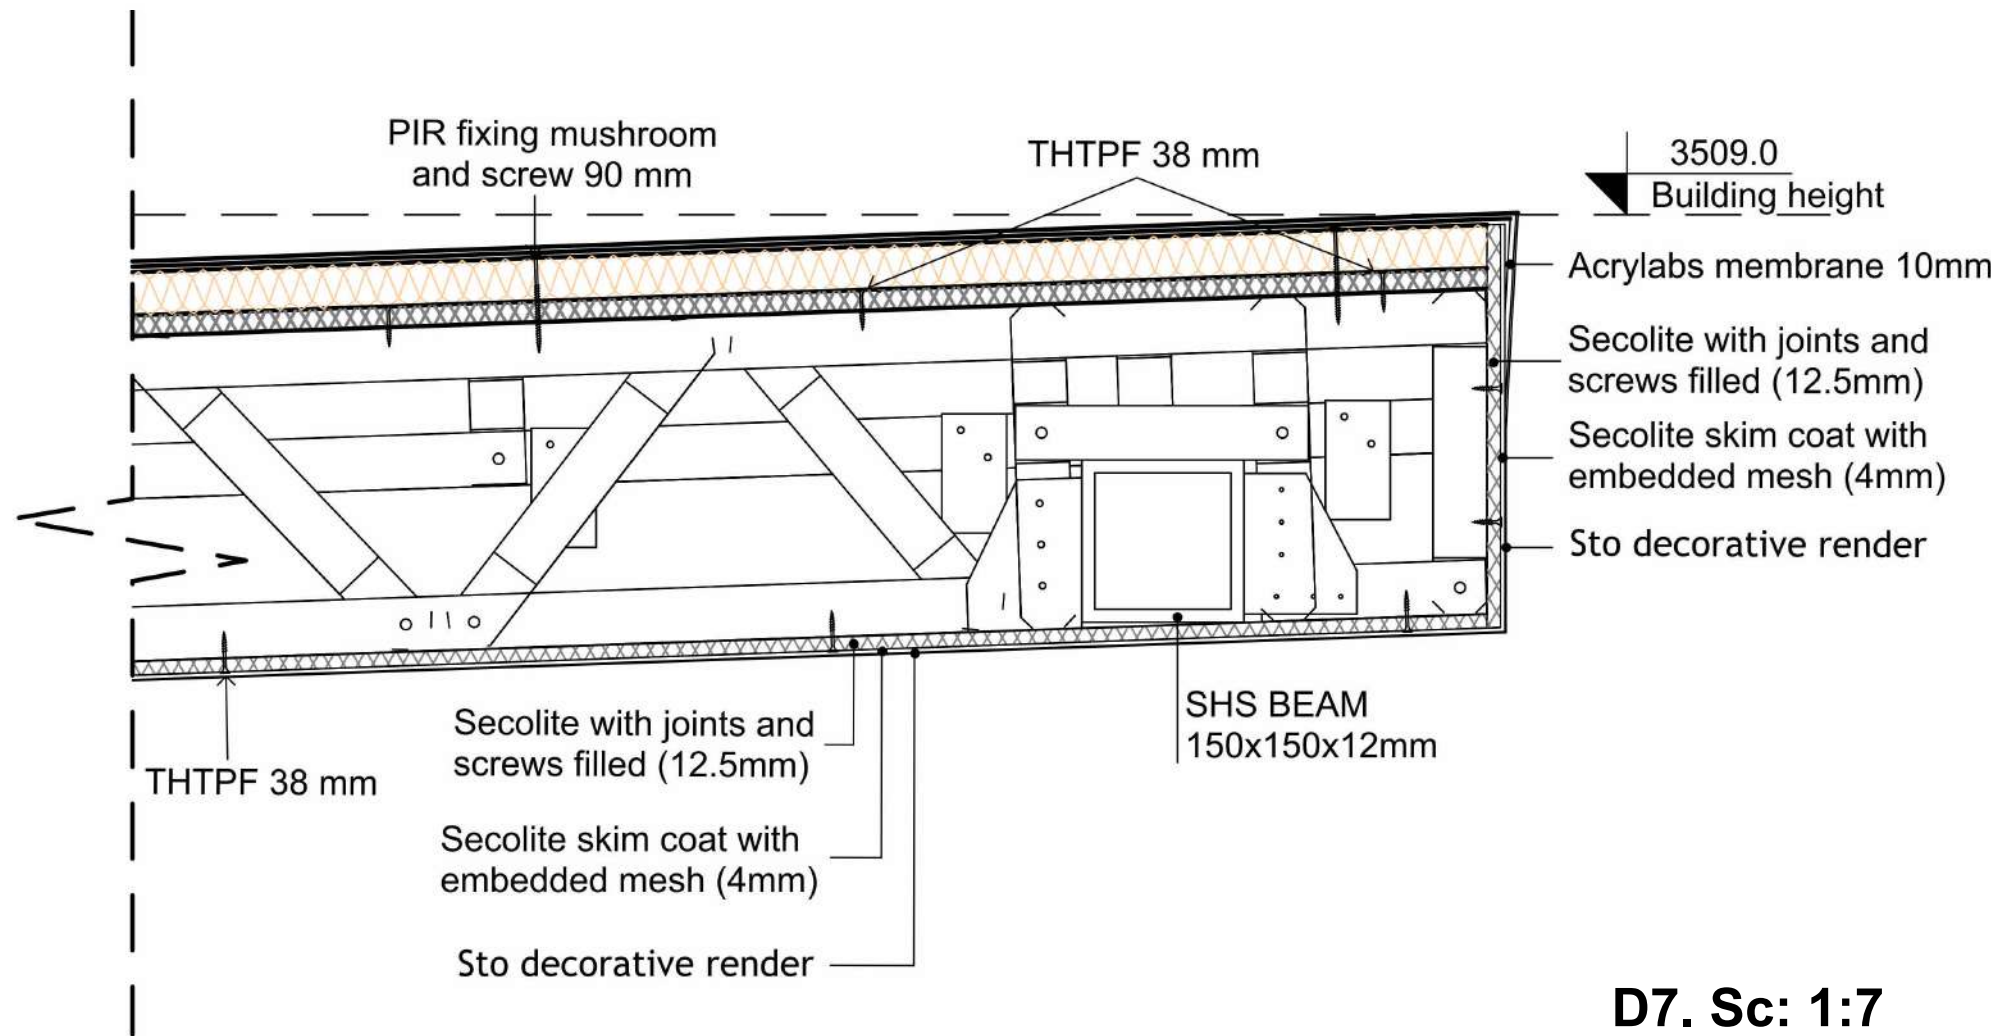

D7. Sc: 1:7

[illegible]

Issued for construction

01/05/2024

1. THESE DRAWINGS MUST BE CHECKED BY THE CUSTOMER OR CONTRACTOR PRIOR TO APPROVAL. ANY ERRORS OR OMISSIONS MUST BE REPORTED IN WRITING TO BAUHU PRIOR TO COMMENCEMENT OF CONSTRUCTION.
2. ARCHITECTURAL DRAWINGS SHOULD BE READ IN CONJUNCTION WITH STRUCTURAL DETAILING AND FABRICATION GENERAL ASSEMBLY DRAWINGS.
3. FOR CONSTRUCTION PURPOSES, USE ONLY THE LATEST APPROVED DRAWINGS LABELED 'ISSUED FOR CONSTRUCTION'.
4. DO NOT SCALE FROM THIS DRAWING.
5. THE COMPANY OPERATES USING METRIC DIMENSIONS AS THE PRINCIPAL DENOMINATION.
6. ALL CONCRETE WORKS ARE OUTSIDE OF THE SCOPE OF THE COMPANY. INFORMATION REGARDING SLAB DESIGN AND CONNECTIONS IN THESE DRAWINGS ARE INTENDED FOR GUIDENCE ONLY. FOUNDATION AND SLAB WORKS SHOULD BE DESIGNED AND APPROVED BY A LOCAL STRUCTURAL ENGINEER.
7. THE COMPANY RETAINS FULL TITLE AND OWNERSHIP OF THESE PLANS AND DESIGNS. ANY UNAUTHORISED USE, REPRODUCTION, OR DISTRIBUTION OF THESE PLANS, WHETHER IN WHOLE OR PART, IS EXPRESSLY PROHIBITED WITHOUT PRIOR WRITTEN CONSENT.

No.	Revision	Date

ISSUED FOR:

Issued for information

Issued for client approval

Issued for fabrication

Issued for construction

Angel

DRAWING TITLE:

Details 5

DRAWN BY:

Mladin Monica-Mihaela

SCALE:


1 : 2

DRAWING NO:

A126

DATE:

01/05/2024

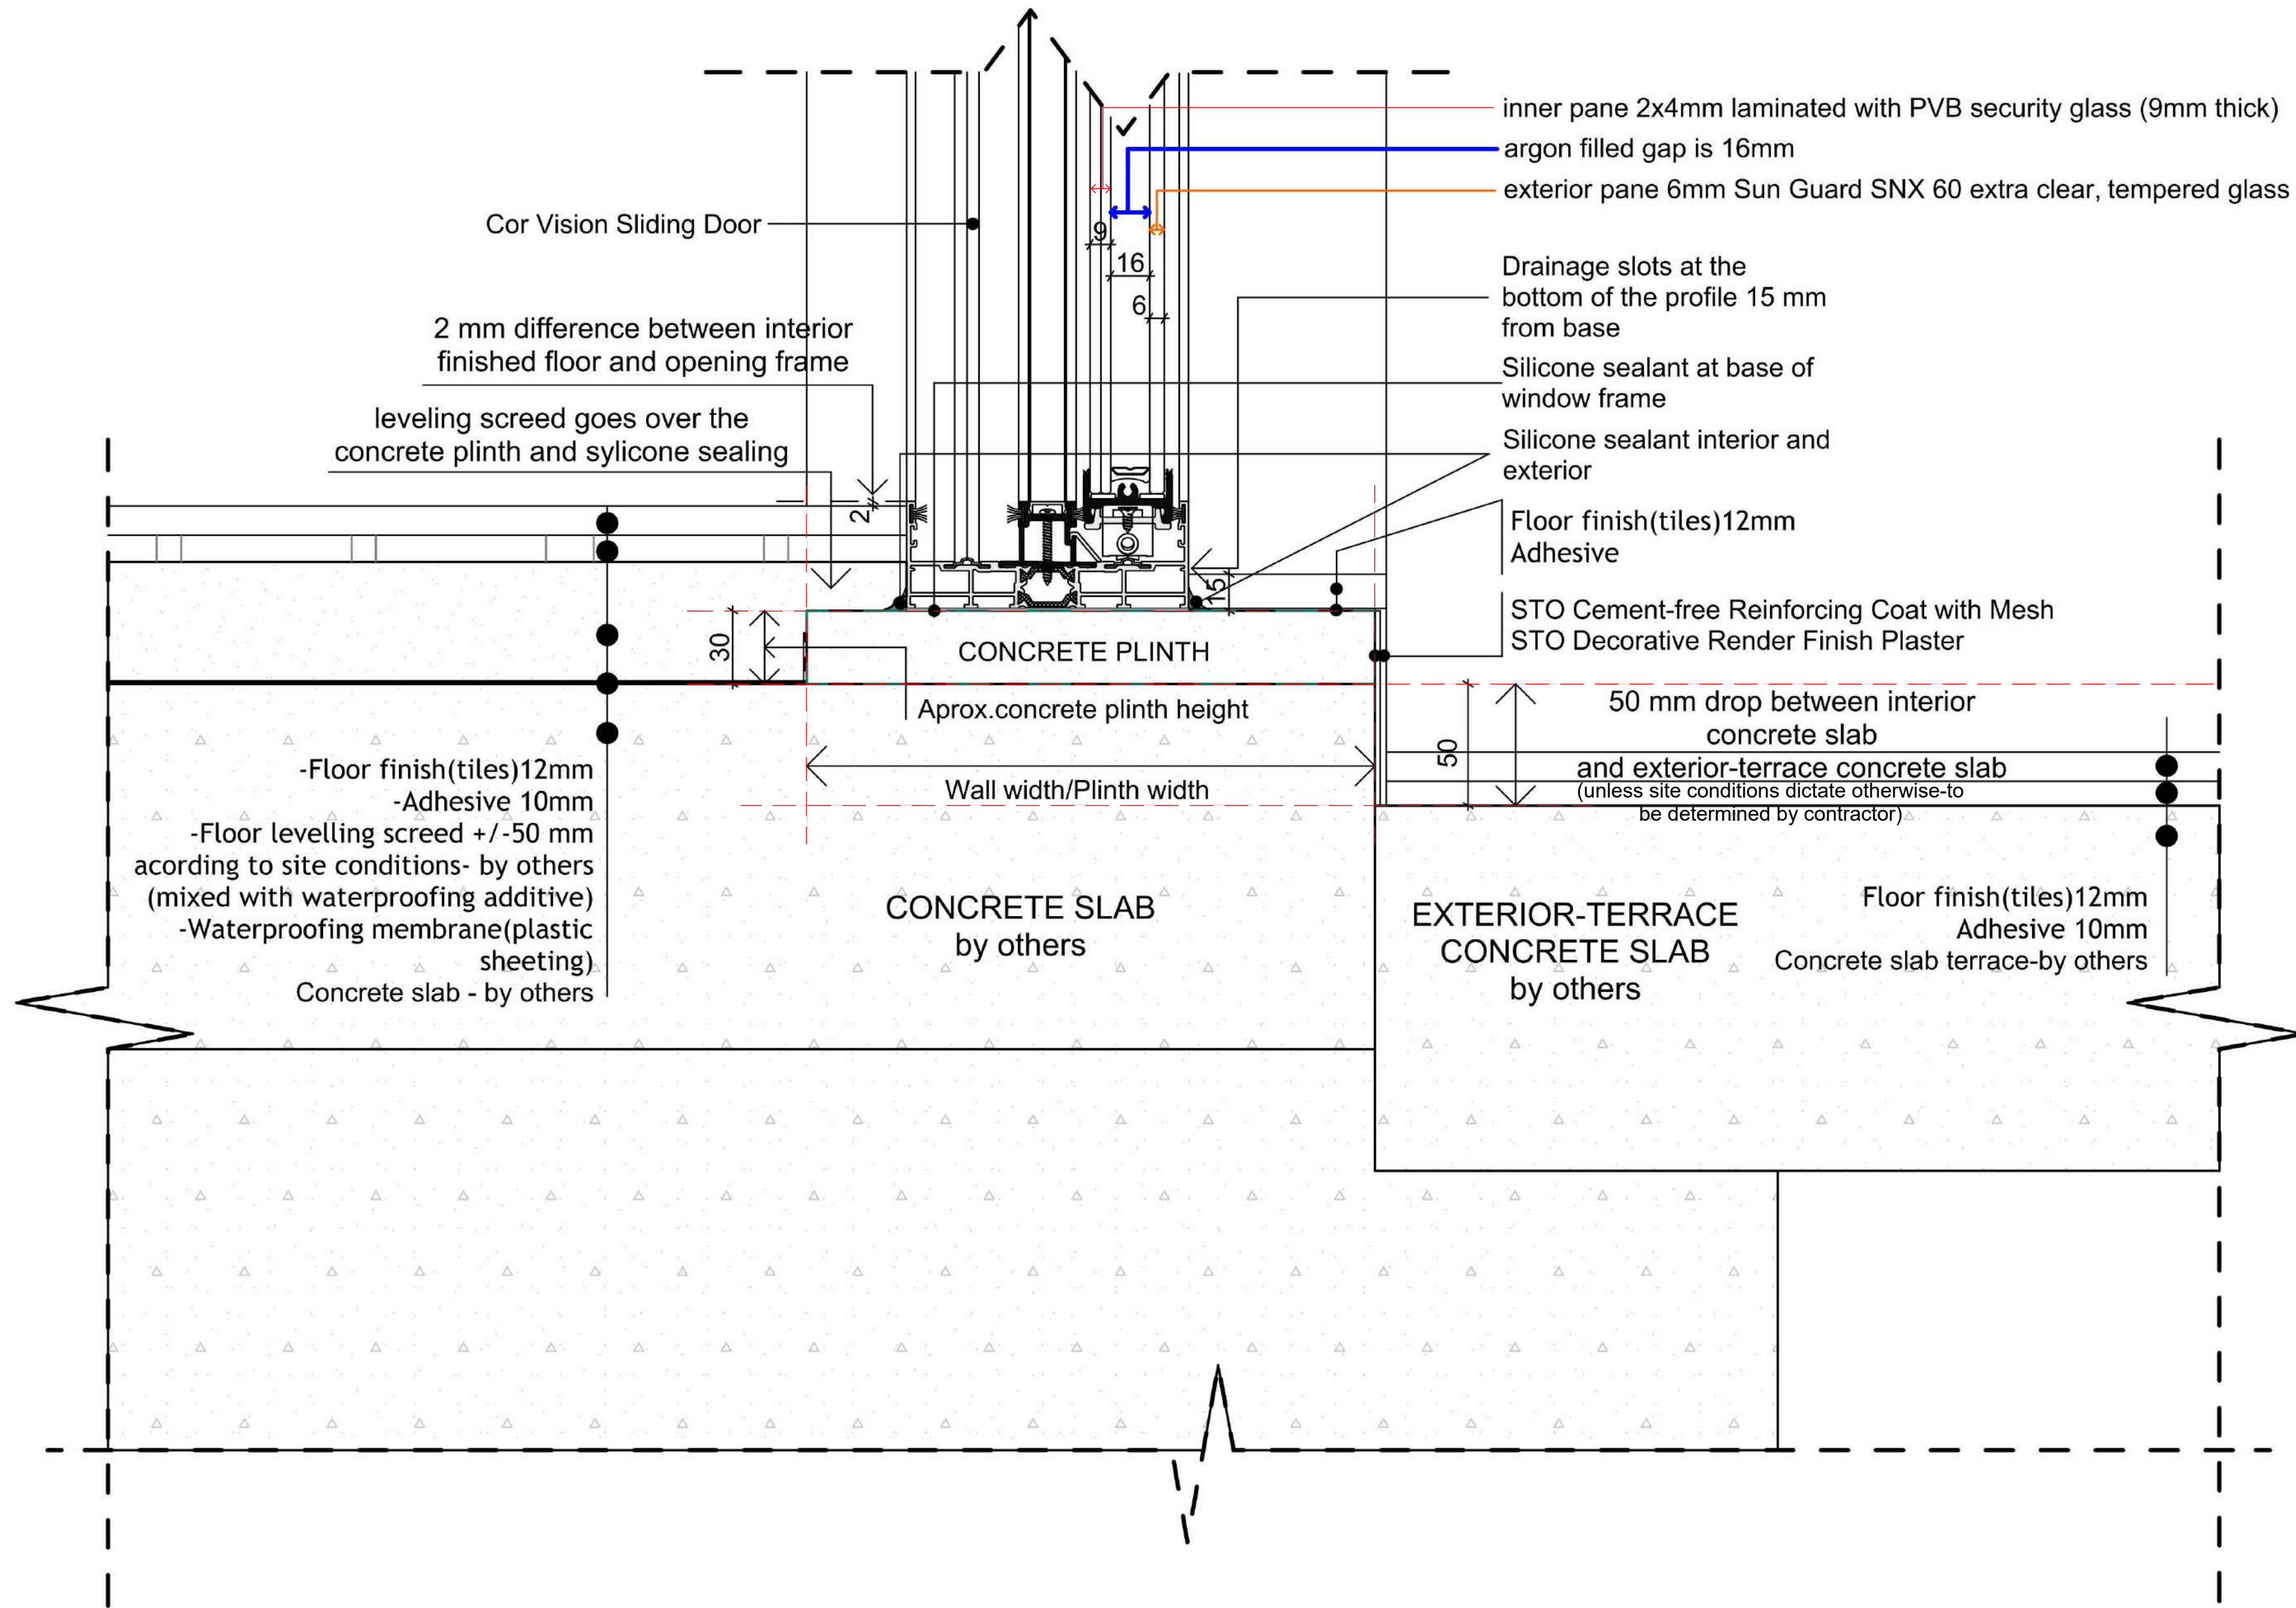

D9.Sliding Window/door fixing to base and concrete
plinth detail Sc: 1:2

1. THESE DRAWINGS MUST BE CHECKED BY THE CUSTOMER OR CONTRACTOR PRIOR TO APPROVAL. ANY ERRORS OR OMISSIONS MUST BE REPORTED IN WRITING TO BAUHU PRIOR TO COMMENCEMENT OF CONSTRUCTION.
2. ARCHITECTURAL DRAWINGS SHOULD BE READ IN CONJUNCTION WITH STRUCTURAL DETAILING AND FABRICATION GENERAL ASSEMBLY DRAWINGS.
3. FOR CONSTRUCTION PURPOSES, USE ONLY THE LATEST APPROVED DRAWINGS LABELED 'ISSUED FOR CONSTRUCTION'.
4. DO NOT SCALE FROM THIS DRAWING.
5. THE COMPANY OPERATES USING METRIC DIMENSIONS AS THE PRINCIPAL DENOMINATION.
6. ALL CONCRETE WORKS ARE OUTSIDE OF THE SCOPE OF THE COMPANY. INFORMATION REGARDING SLAB DESIGN AND CONNECTIONS IN THESE DRAWINGS ARE INTENDED FOR GUIDANCE ONLY. FOUNDATION AND SLAB WORKS SHOULD BE DESIGNED AND APPROVED BY A LOCAL STRUCTURAL ENGINEER.
7. THE COMPANY RETAINS FULL TITLE AND OWNERSHIP OF THESE PLANS AND DESIGNS. ANY UNAUTHORISED USE, REPRODUCTION, OR DISTRIBUTION OF THESE PLANS, WHETHER IN WHOLE OR PART, IS EXPRESSLY PROHIBITED WITHOUT PRIOR WRITTEN CONSENT.


No.	Revision	Date

- ISSUED FOR:
- Issued for information
 - Issued for client approval
 - Issued for fabrication
 - Issued for construction

Angel


DRAWING TITLE:	Details 6
DRAWN BY:	Mladin Monica-Mihaela
SCALE:	As indicated
DRAWING NO:	A127
DATE:	01/05/2024

D11. Sc: 1:8

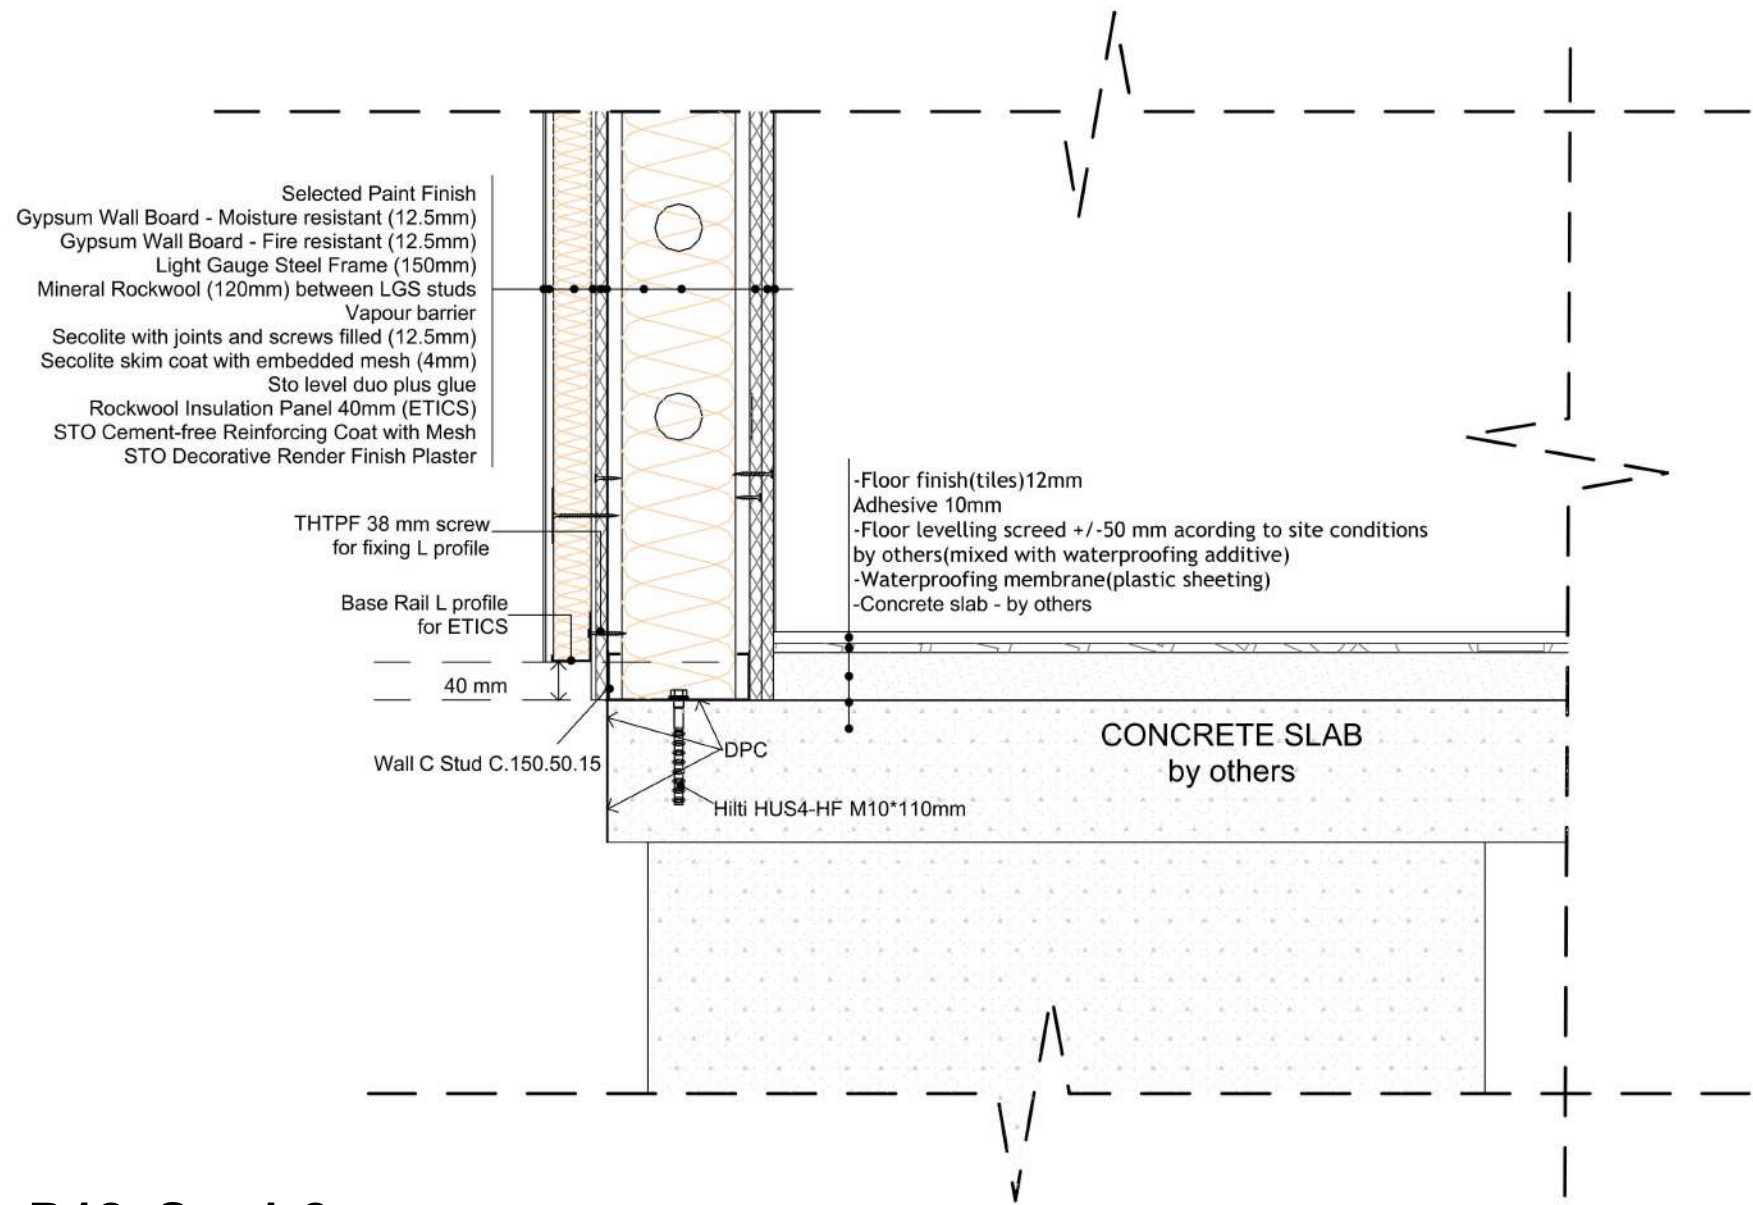

D12. Sc: 1:8

D10.Side wall Detail Sc: 1:12

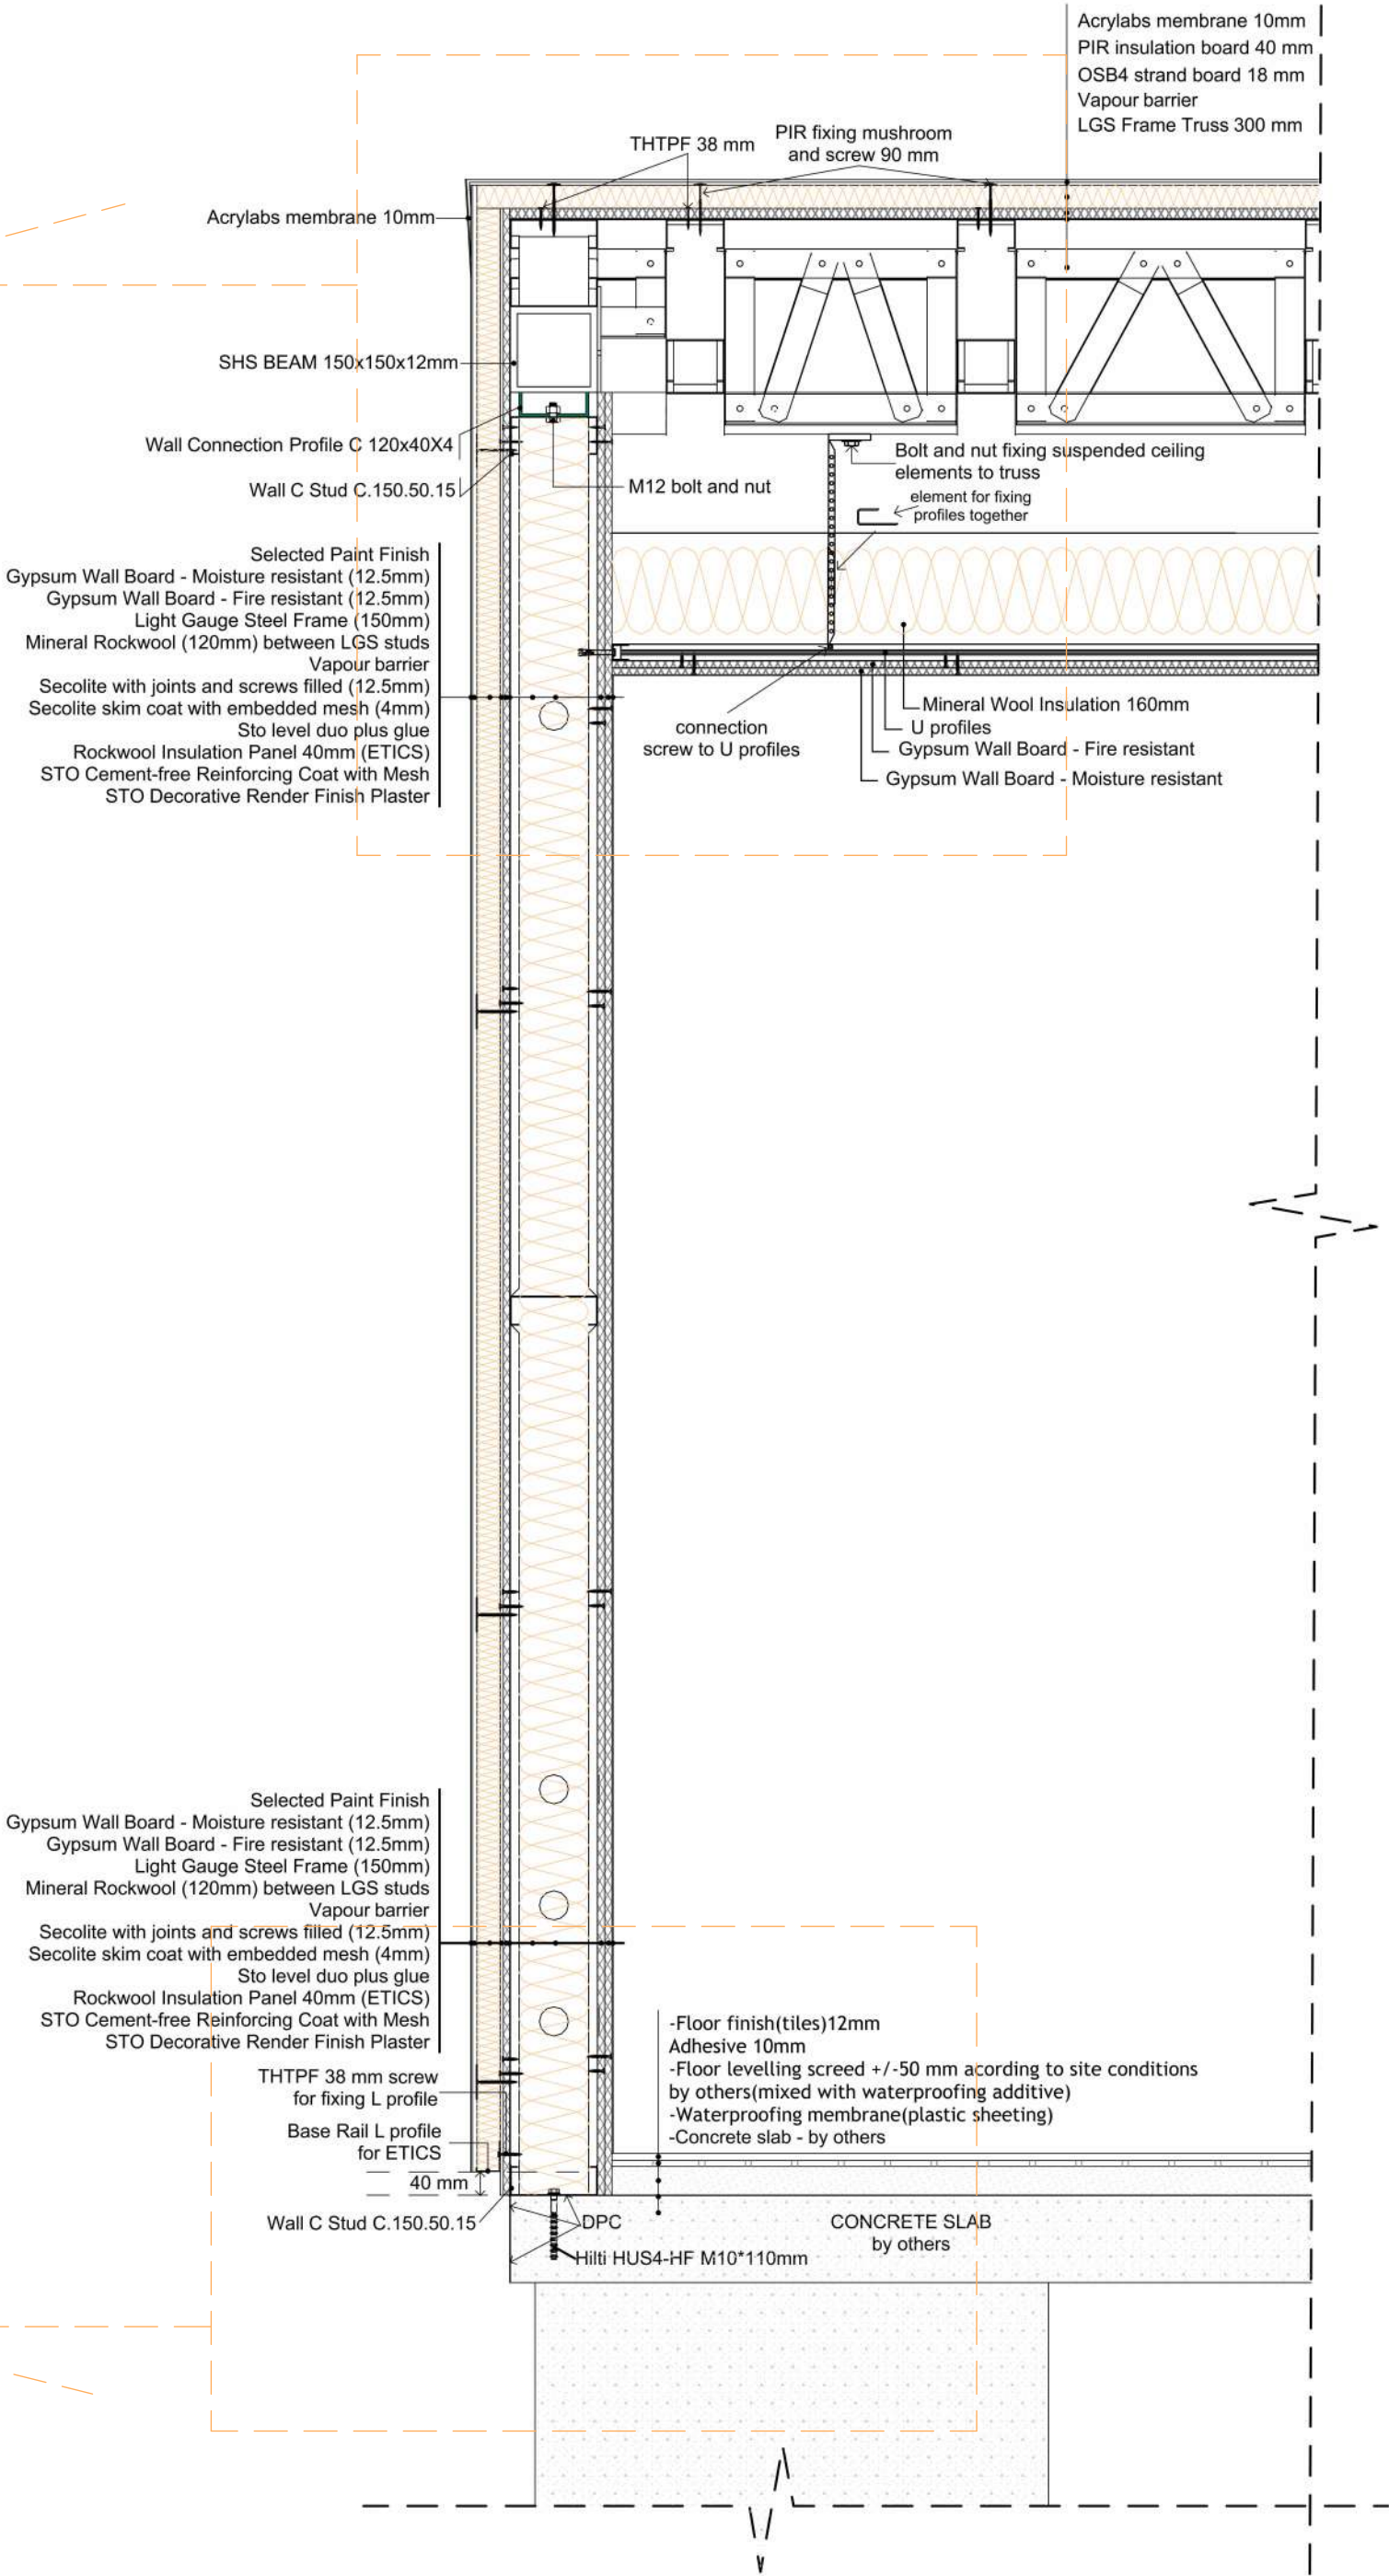

1. THESE DRAWINGS MUST BE CHECKED BY THE CUSTOMER OR CONTRACTOR PRIOR TO APPROVAL. ANY ERRORS OR OMISSIONS MUST BE REPORTED IN WRITING TO BAUHU PRIOR TO COMMENCEMENT OF CONSTRUCTION.
2. ARCHITECTURAL DRAWINGS SHOULD BE READ IN CONJUNCTION WITH STRUCTURAL DETAILING AND FABRICATION GENERAL ASSEMBLY DRAWINGS.
3. FOR CONSTRUCTION PURPOSES, USE ONLY THE LATEST APPROVED DRAWINGS LABELED 'ISSUED FOR CONSTRUCTION'.
4. DO NOT SCALE FROM THIS DRAWING.
5. THE COMPANY OPERATES USING METRIC DIMENSIONS AS THE PRINCIPAL DENOMINATION.
6. ALL CONCRETE WORKS ARE OUTSIDE OF THE SCOPE OF THE COMPANY. INFORMATION REGARDING SLAB DESIGN AND CONNECTIONS IN THESE DRAWINGS ARE INTENDED FOR GUIDANCE ONLY. FOUNDATION AND SLAB WORKS SHOULD BE DESIGNED AND APPROVED BY A LOCAL STRUCTURAL ENGINEER.
7. THE COMPANY RETAINS FULL TITLE AND OWNERSHIP OF THESE PLANS AND DESIGNS. ANY UNAUTHORISED USE, REPRODUCTION, OR DISTRIBUTION OF THESE PLANS, WHETHER IN WHOLE OR PART, IS EXPRESSLY PROHIBITED WITHOUT PRIOR WRITTEN CONSENT.

No.	Revision	Date

ISSUED FOR:

Issued for information

Issued for client approval

Issued for fabrication

Issued for construction

Angel

DRAWING TITLE:

Details 7

DRAWN BY:

Mladin Monica-Mihaela

SCALE:

As indicated


DRAWING NO:

A128



DATE:

01/05/2024


D14. Sc: 1:8

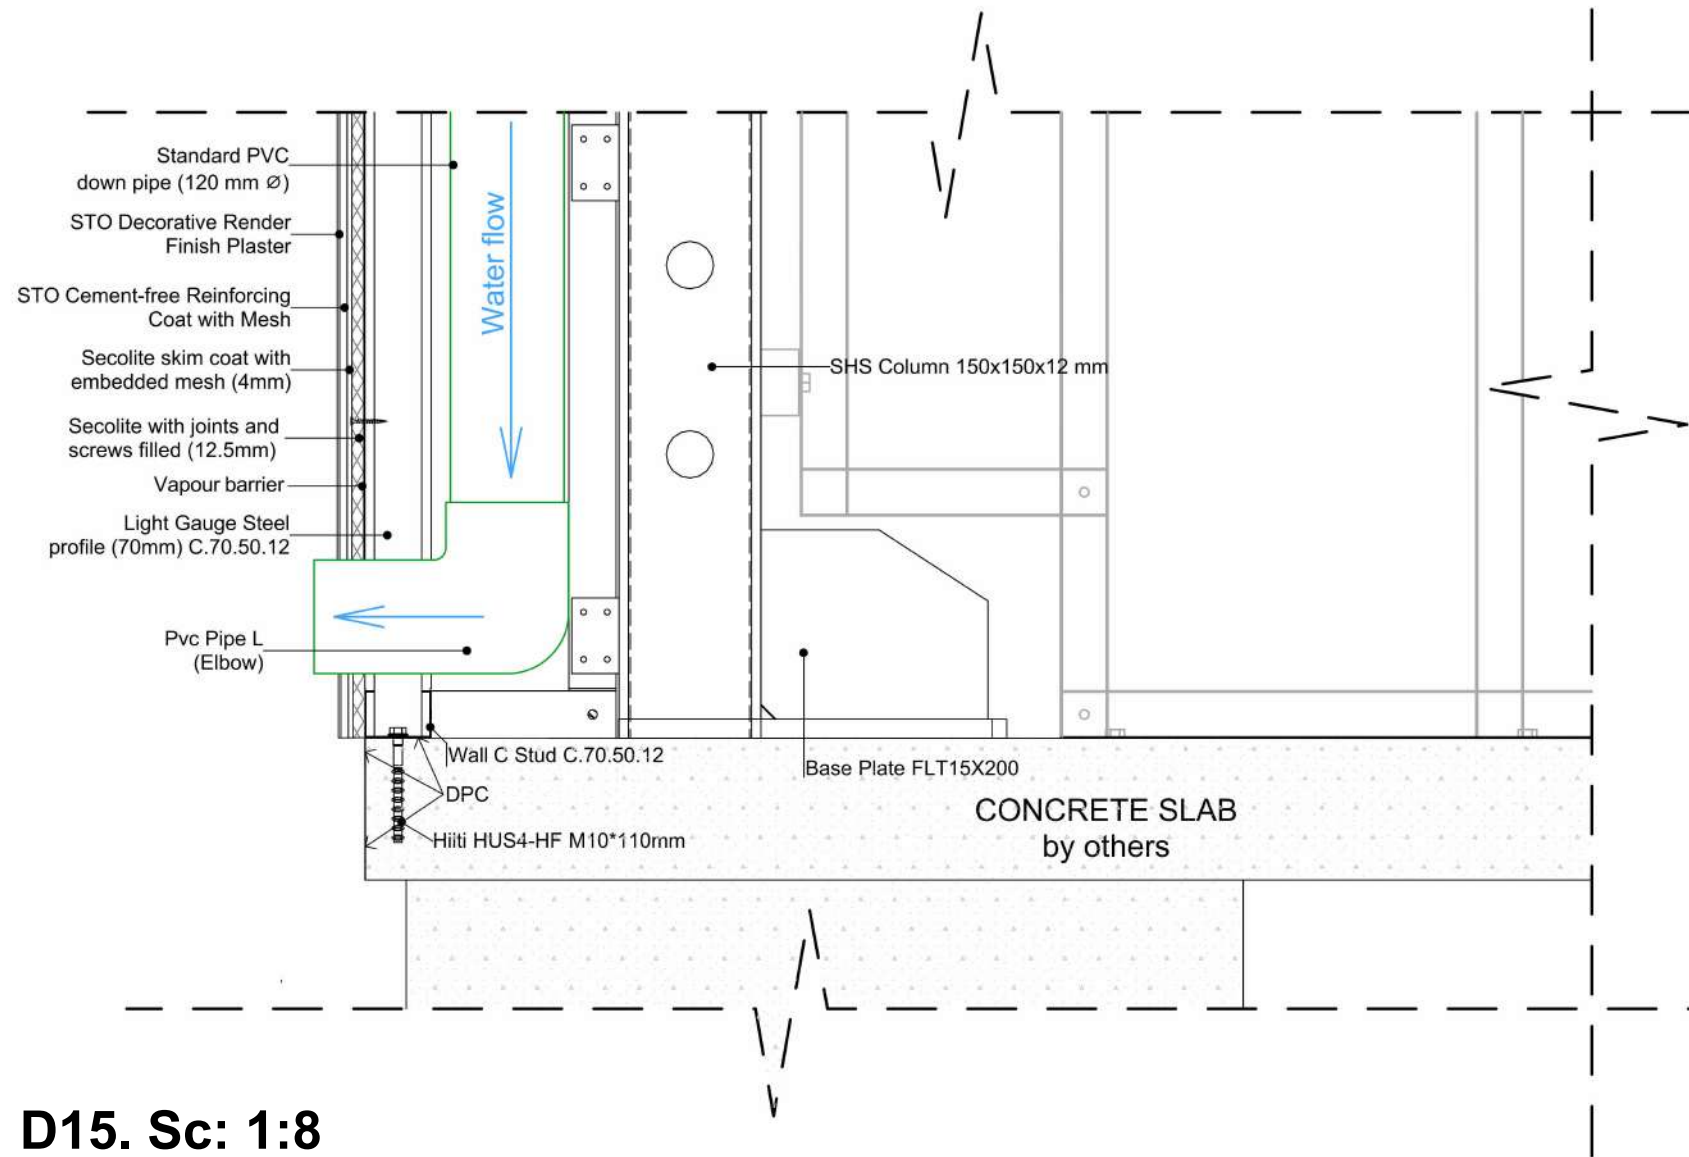

D15. Sc: 1:8

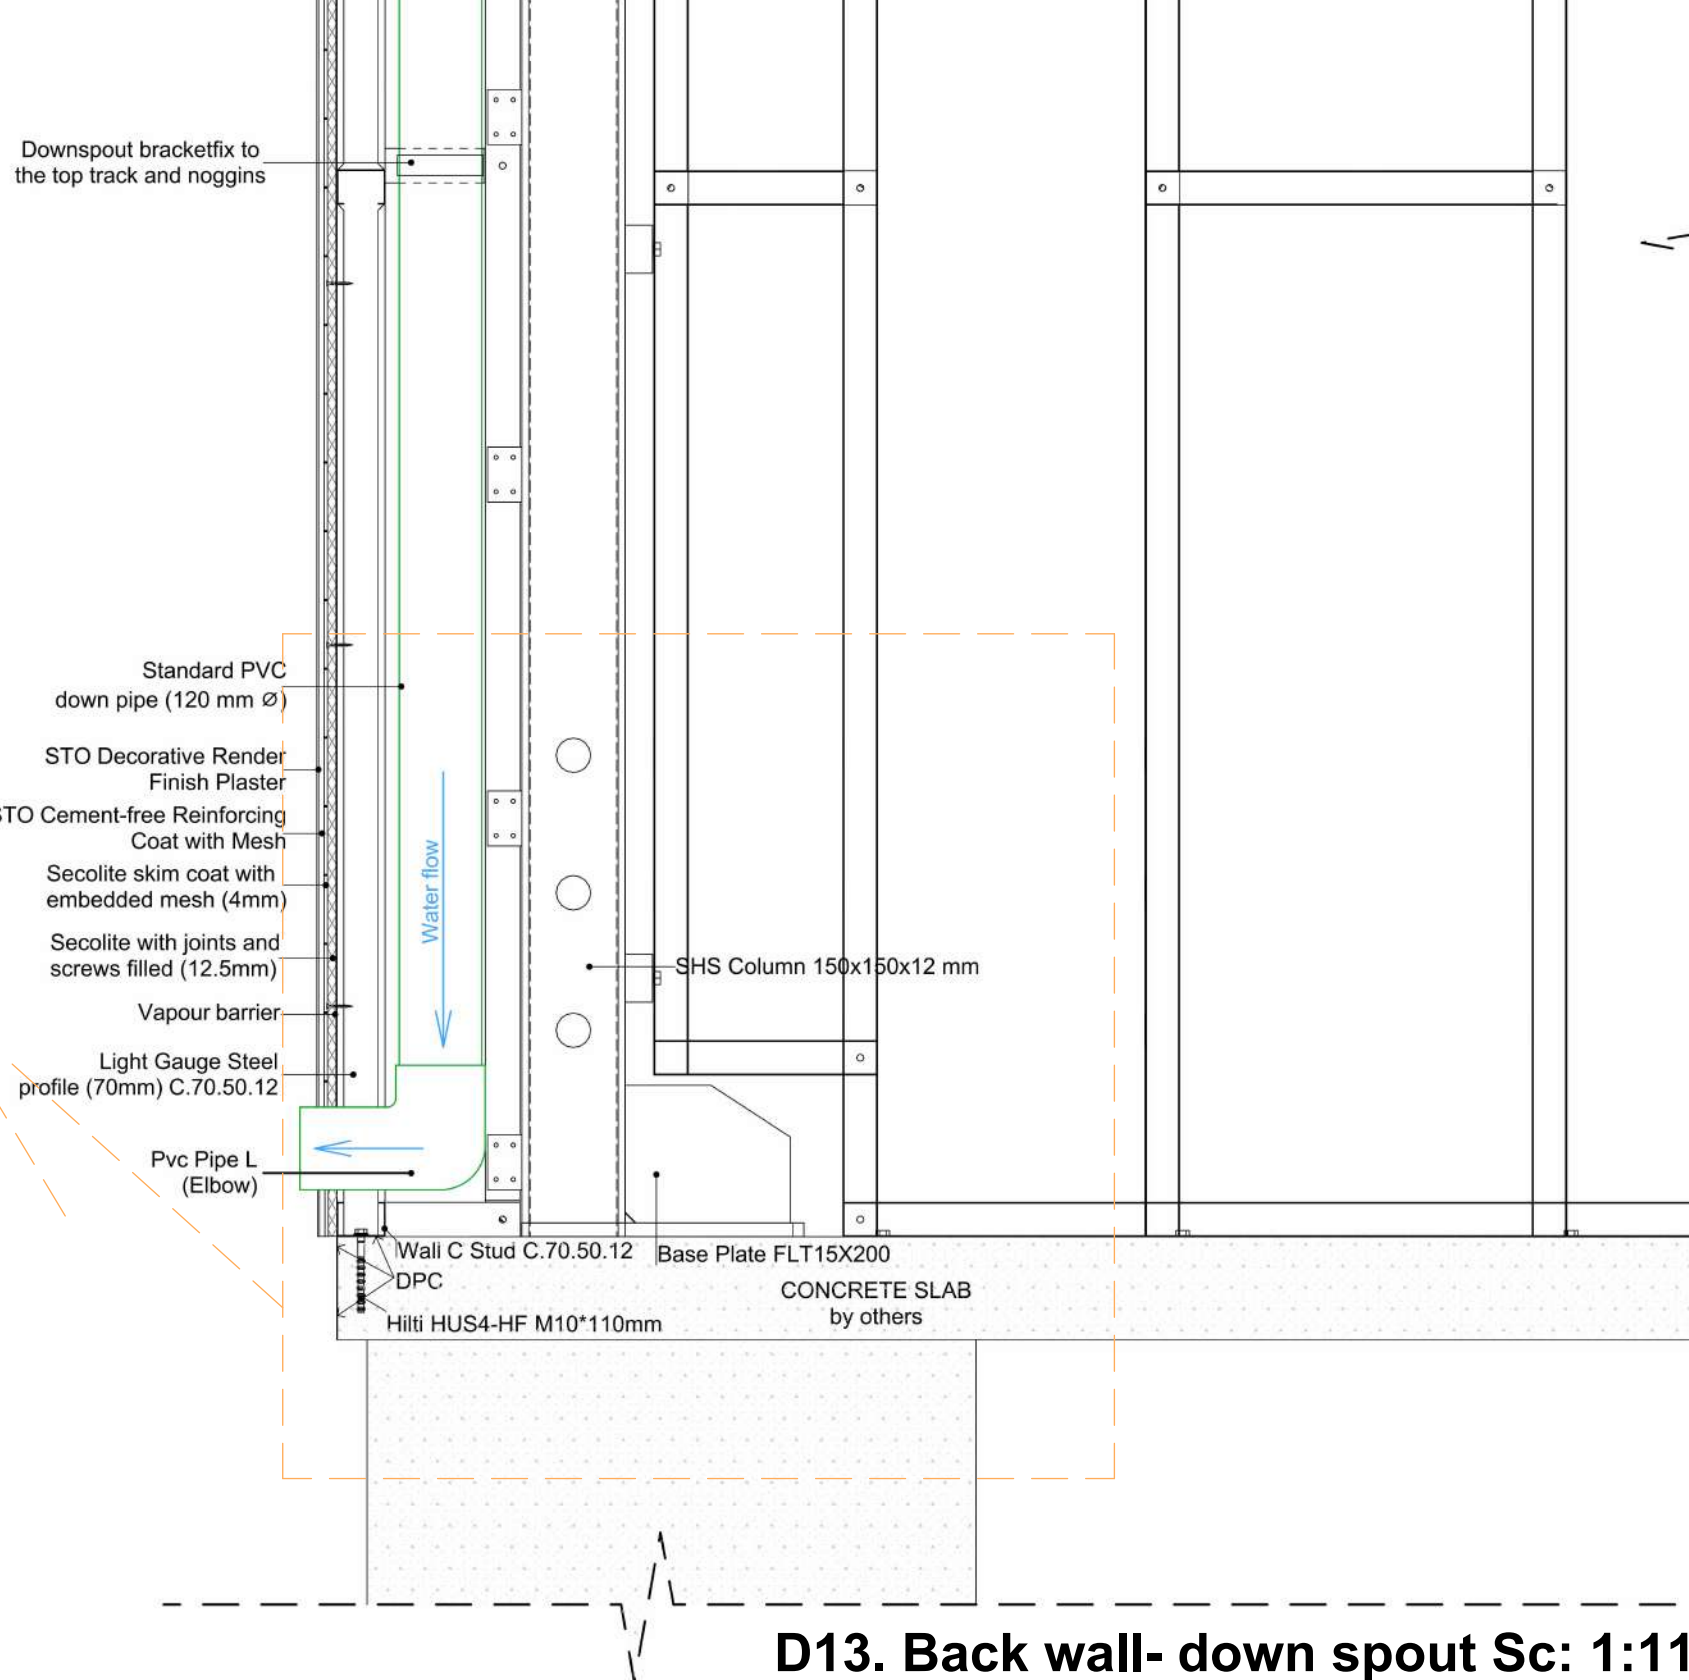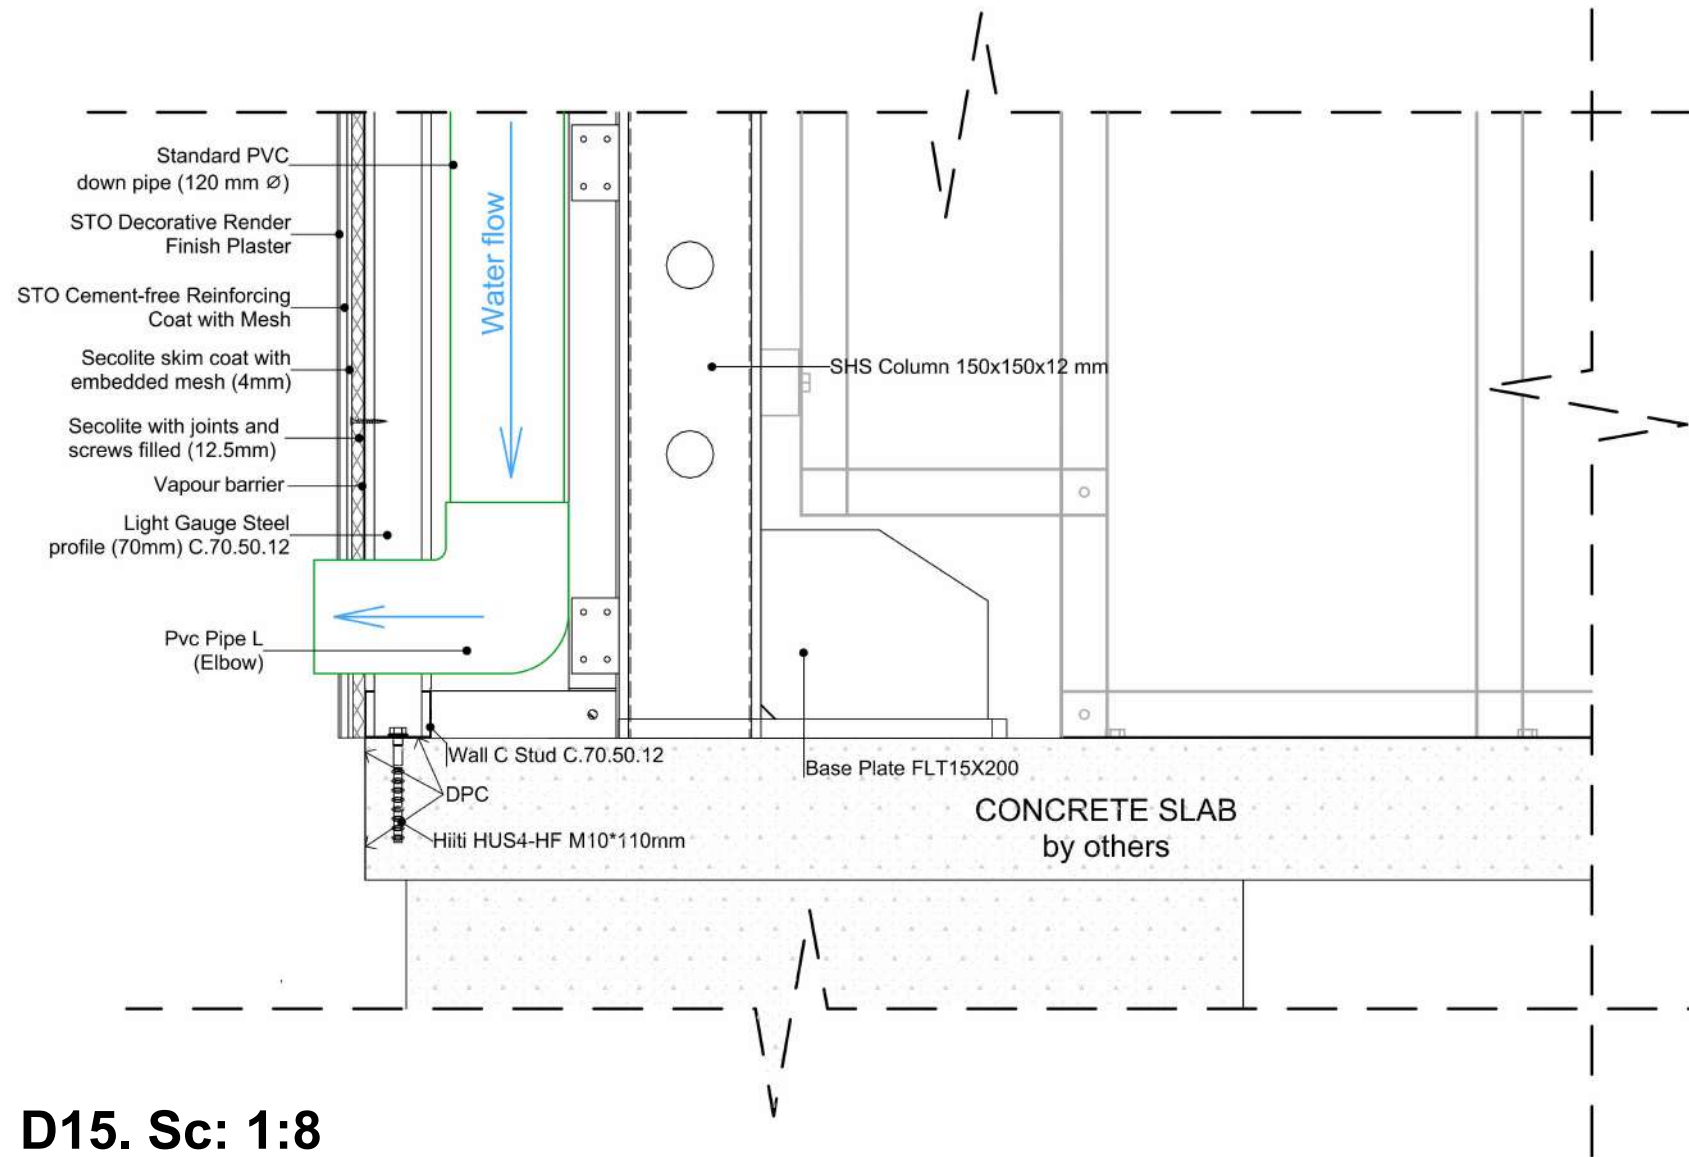

D13. Back wall- down spout Sc: 1:11

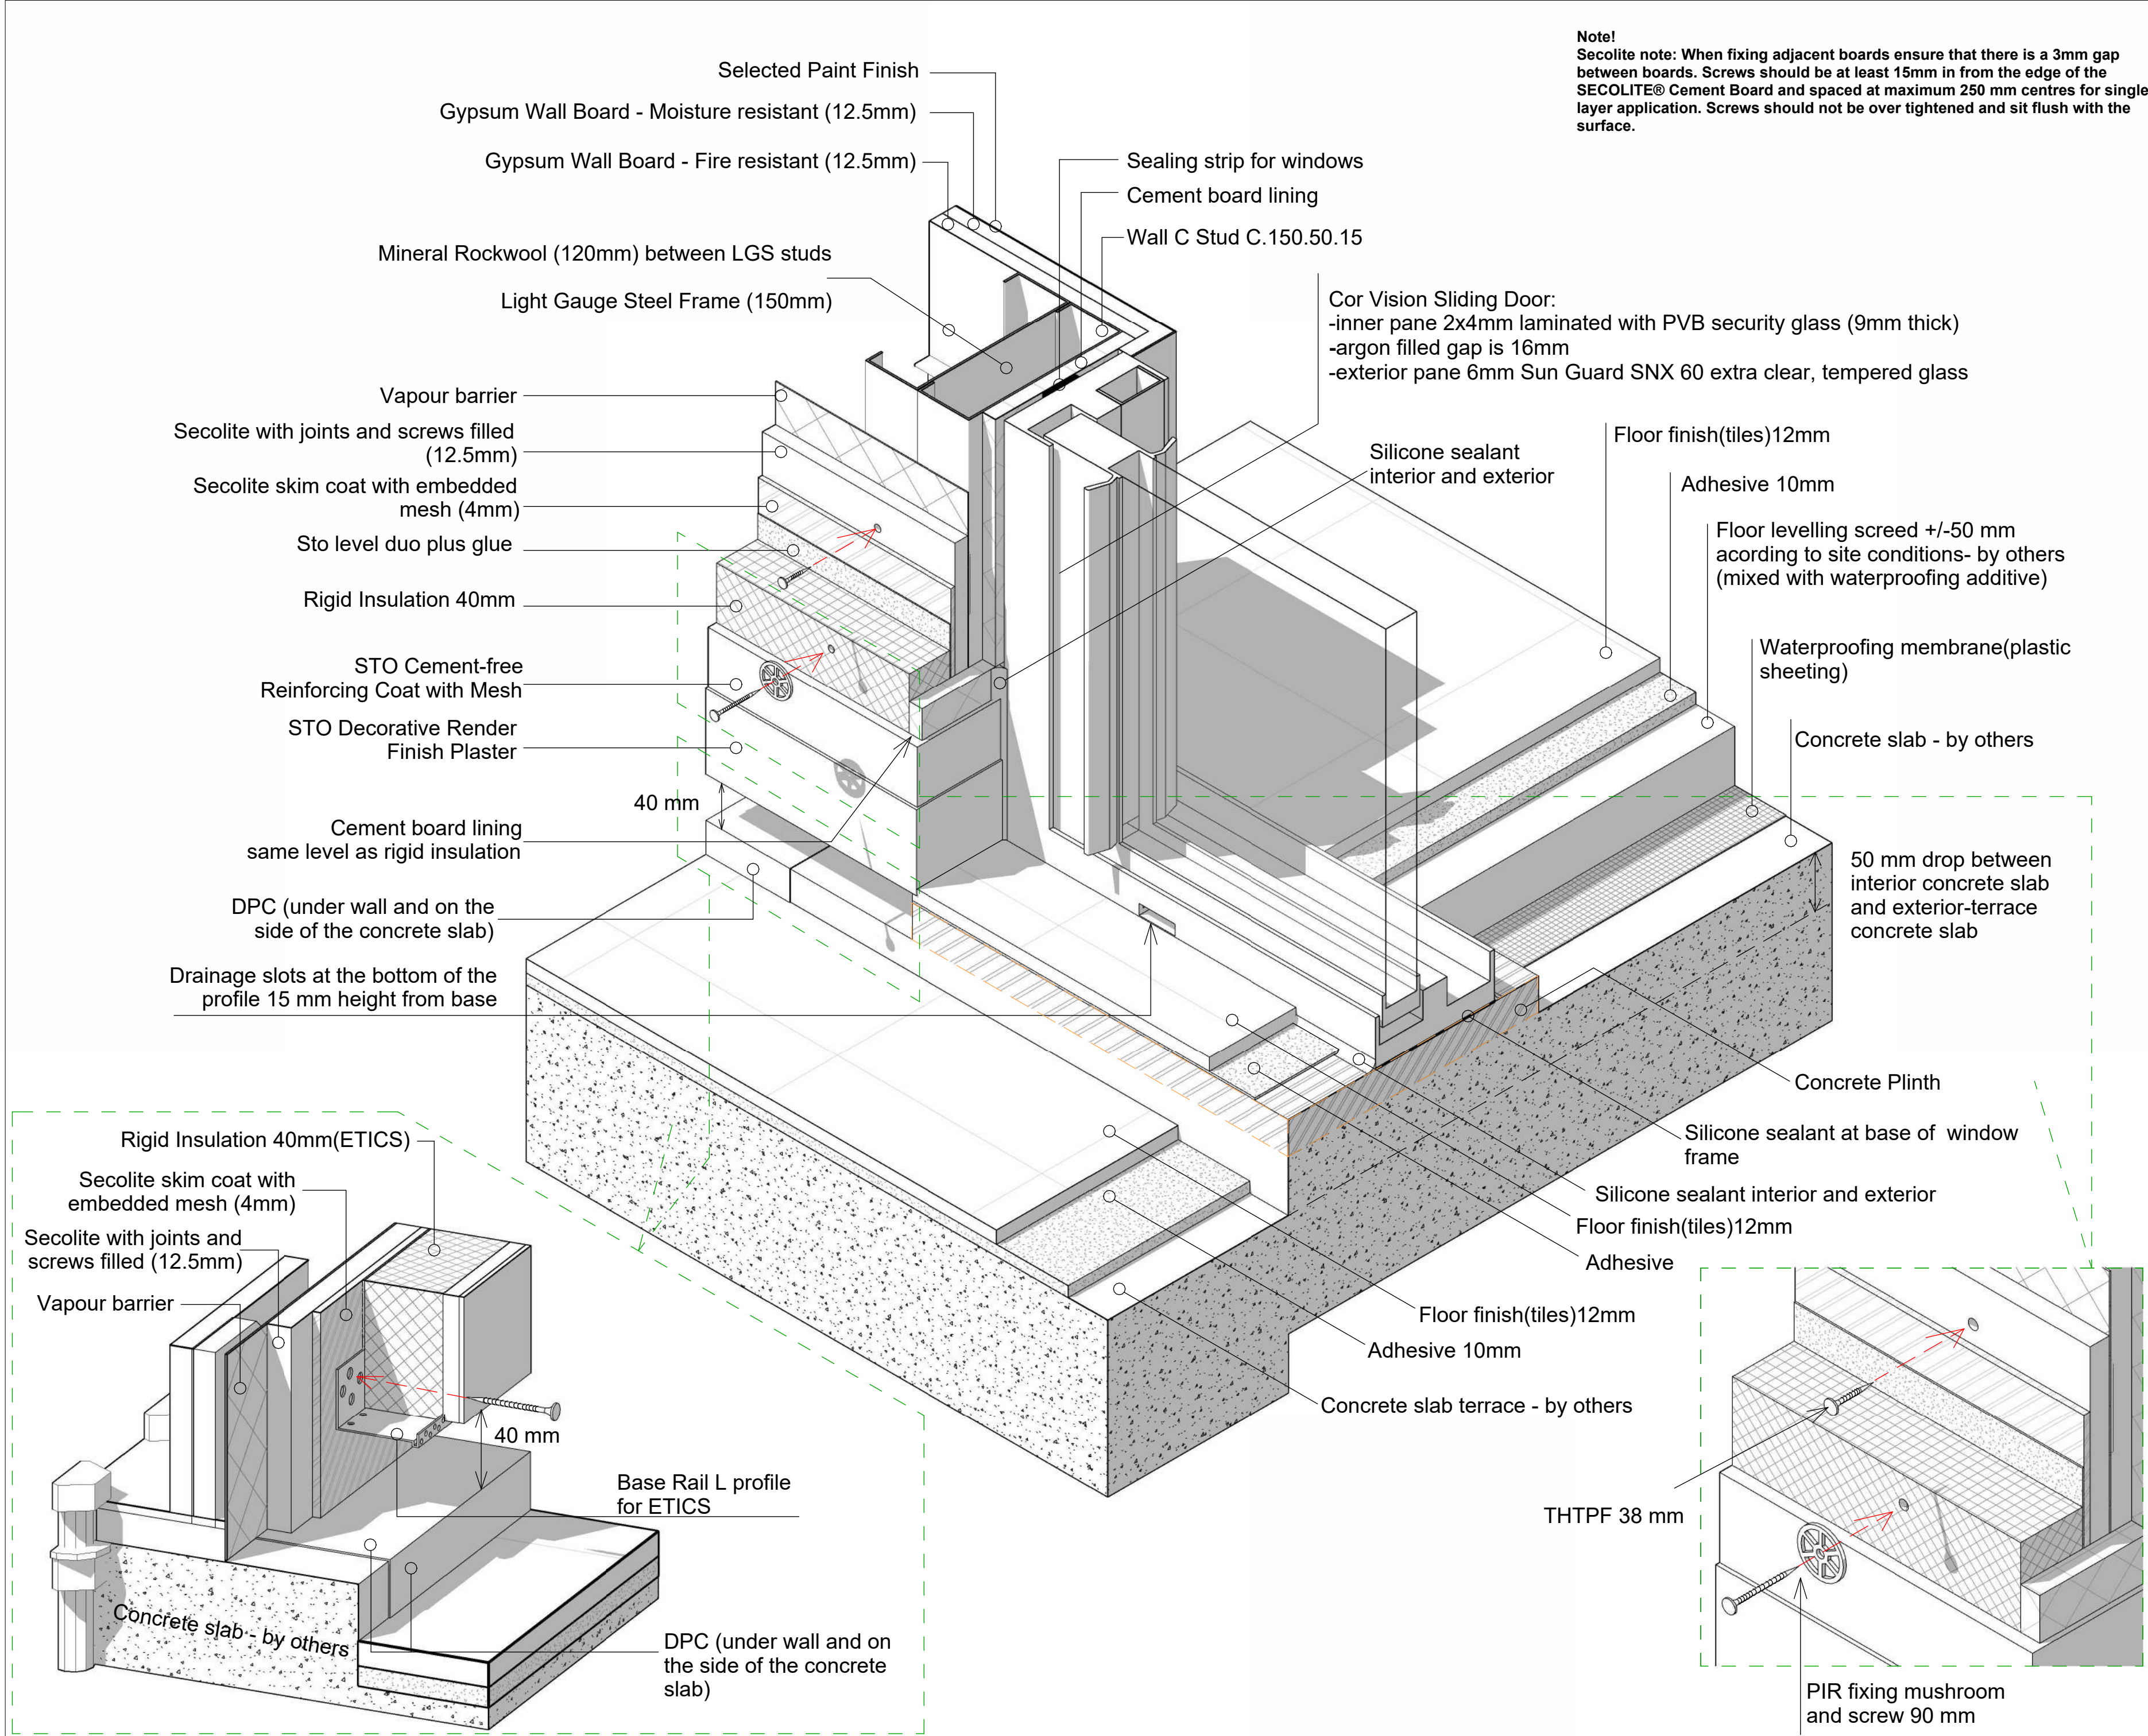

BAUHU

MODULAR • BUILDING • SOLUTIONS

1. THESE DRAWINGS MUST BE CHECKED BY THE CUSTOMER OR CONTRACTOR PRIOR TO APPROVAL. ANY ERRORS OR OMISSIONS MUST BE REPORTED IN WRITING TO BAUHU PRIOR TO COMMENCEMENT OF CONSTRUCTION.

2. ARCHITECTURAL DRAWINGS SHOULD BE READ IN CONJUNCTION WITH STRUCTURAL DETAILING AND FABRICATION GENERAL ASSEMBLY DRAWINGS.

3. FOR CONSTRUCTION PURPOSES, USE ONLY THE LATEST APPROVED DRAWINGS LABELED 'ISSUED FOR CONSTRUCTION'.

4. DO NOT SCALE FROM THIS DRAWING.

5. THE COMPANY OPERATES USING METRIC DIMENSIONS AS THE PRINCIPAL DENOMINATION.

6. ALL CONCRETE WORKS ARE OUTSIDE OF THE SCOPE OF THE COMPANY. INFORMATION REGARDING SLAB DESIGN AND CONNECTIONS IN THESE DRAWINGS ARE INTENDED FOR GUIDANCE ONLY. FOUNDATION AND SLAB WORKS SHOULD BE DESIGNED AND APPROVED BY A LOCAL STRUCTURAL ENGINEER.

7. THE COMPANY RETAINS FULL TITLE AND OWNERSHIP OF THESE PLANS AND DESIGNS. ANY UNAUTHORISED USE, REPRODUCTION, OR DISTRIBUTION OF THESE PLANS, WHETHER IN WHOLE OR PART, IS EXPRESSLY PROHIBITED WITHOUT PRIOR WRITTEN CONSENT.

No.	Revision	Date

ISSUED FOR:

Issued for information

Issued for client approval

Issued for fabrication

Issued for construction

Angel

DRAWING TITLE:

3d Detail

DRAWN BY:

Mladin Monica-Mihaela

SCALE:


DRAWING NO:

A129


DATE:

01/05/2024

Kitchen Plan 1/25

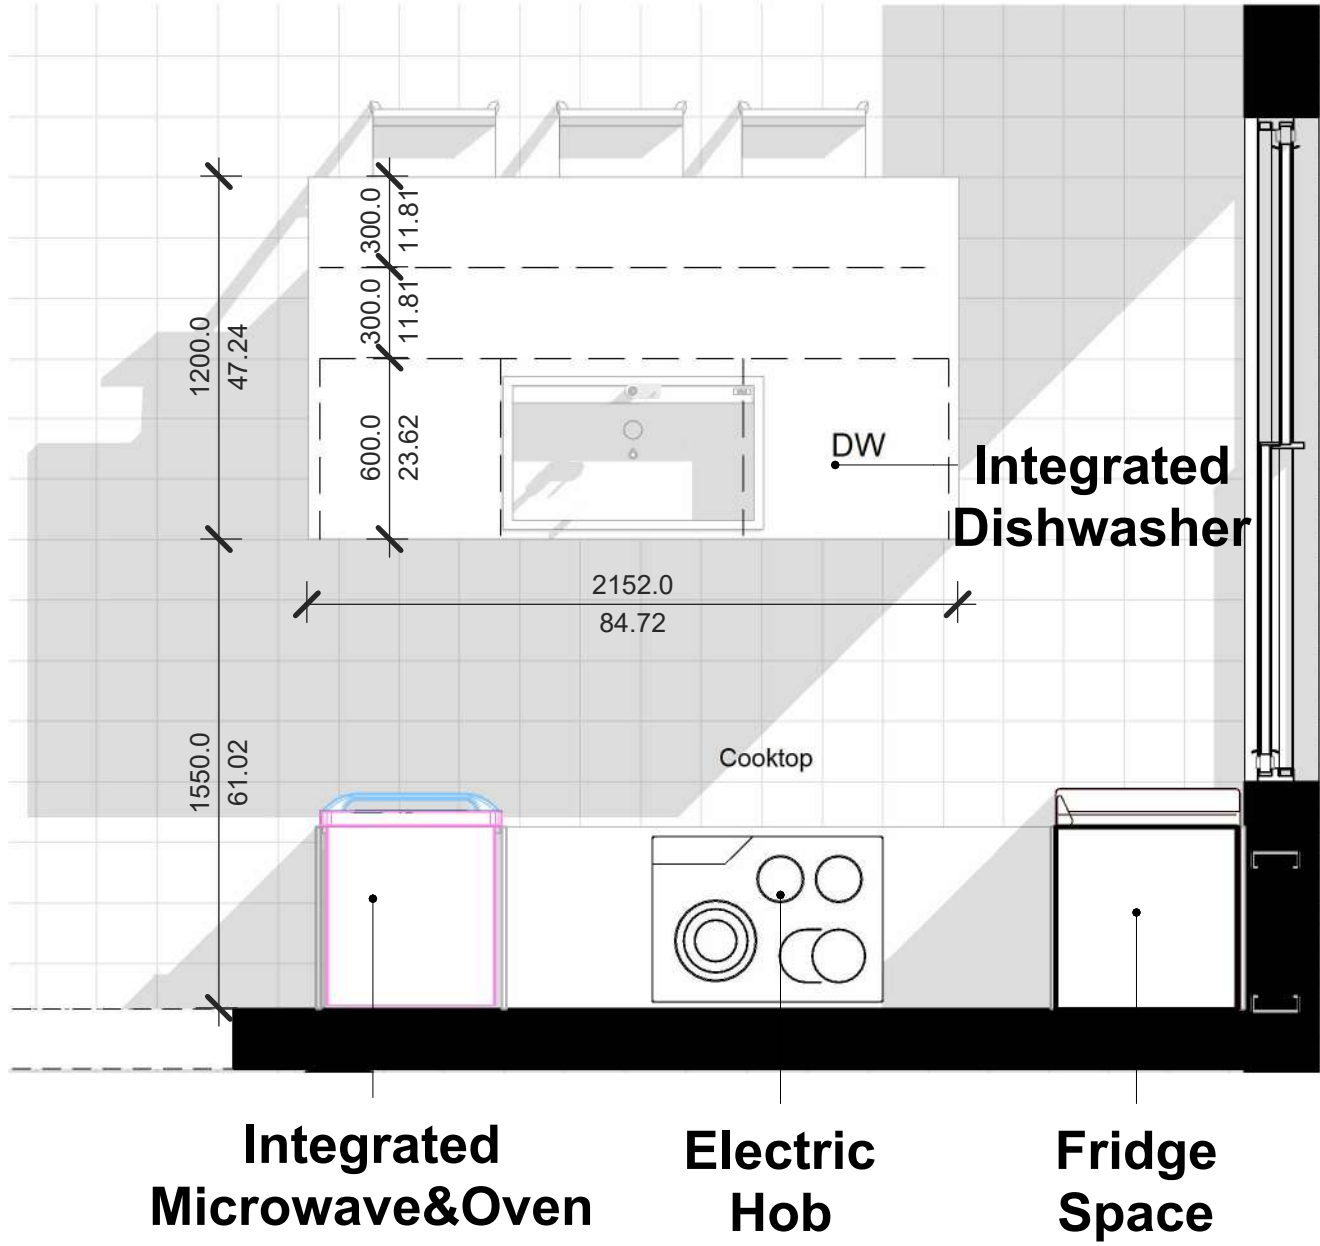

- Tall Units height 3 - 2260
Integrated Microwave and Oven
Count: 1
Fridge space with folding door above
Count: 1
- Wall units height 1 - 720mm high
Count: 2
Slimline cooker hoods
Count: 1
- Base Units in XL height 792mm
Pull-out base units
Count: 2
Pull-out hot plate unit
Count: 1

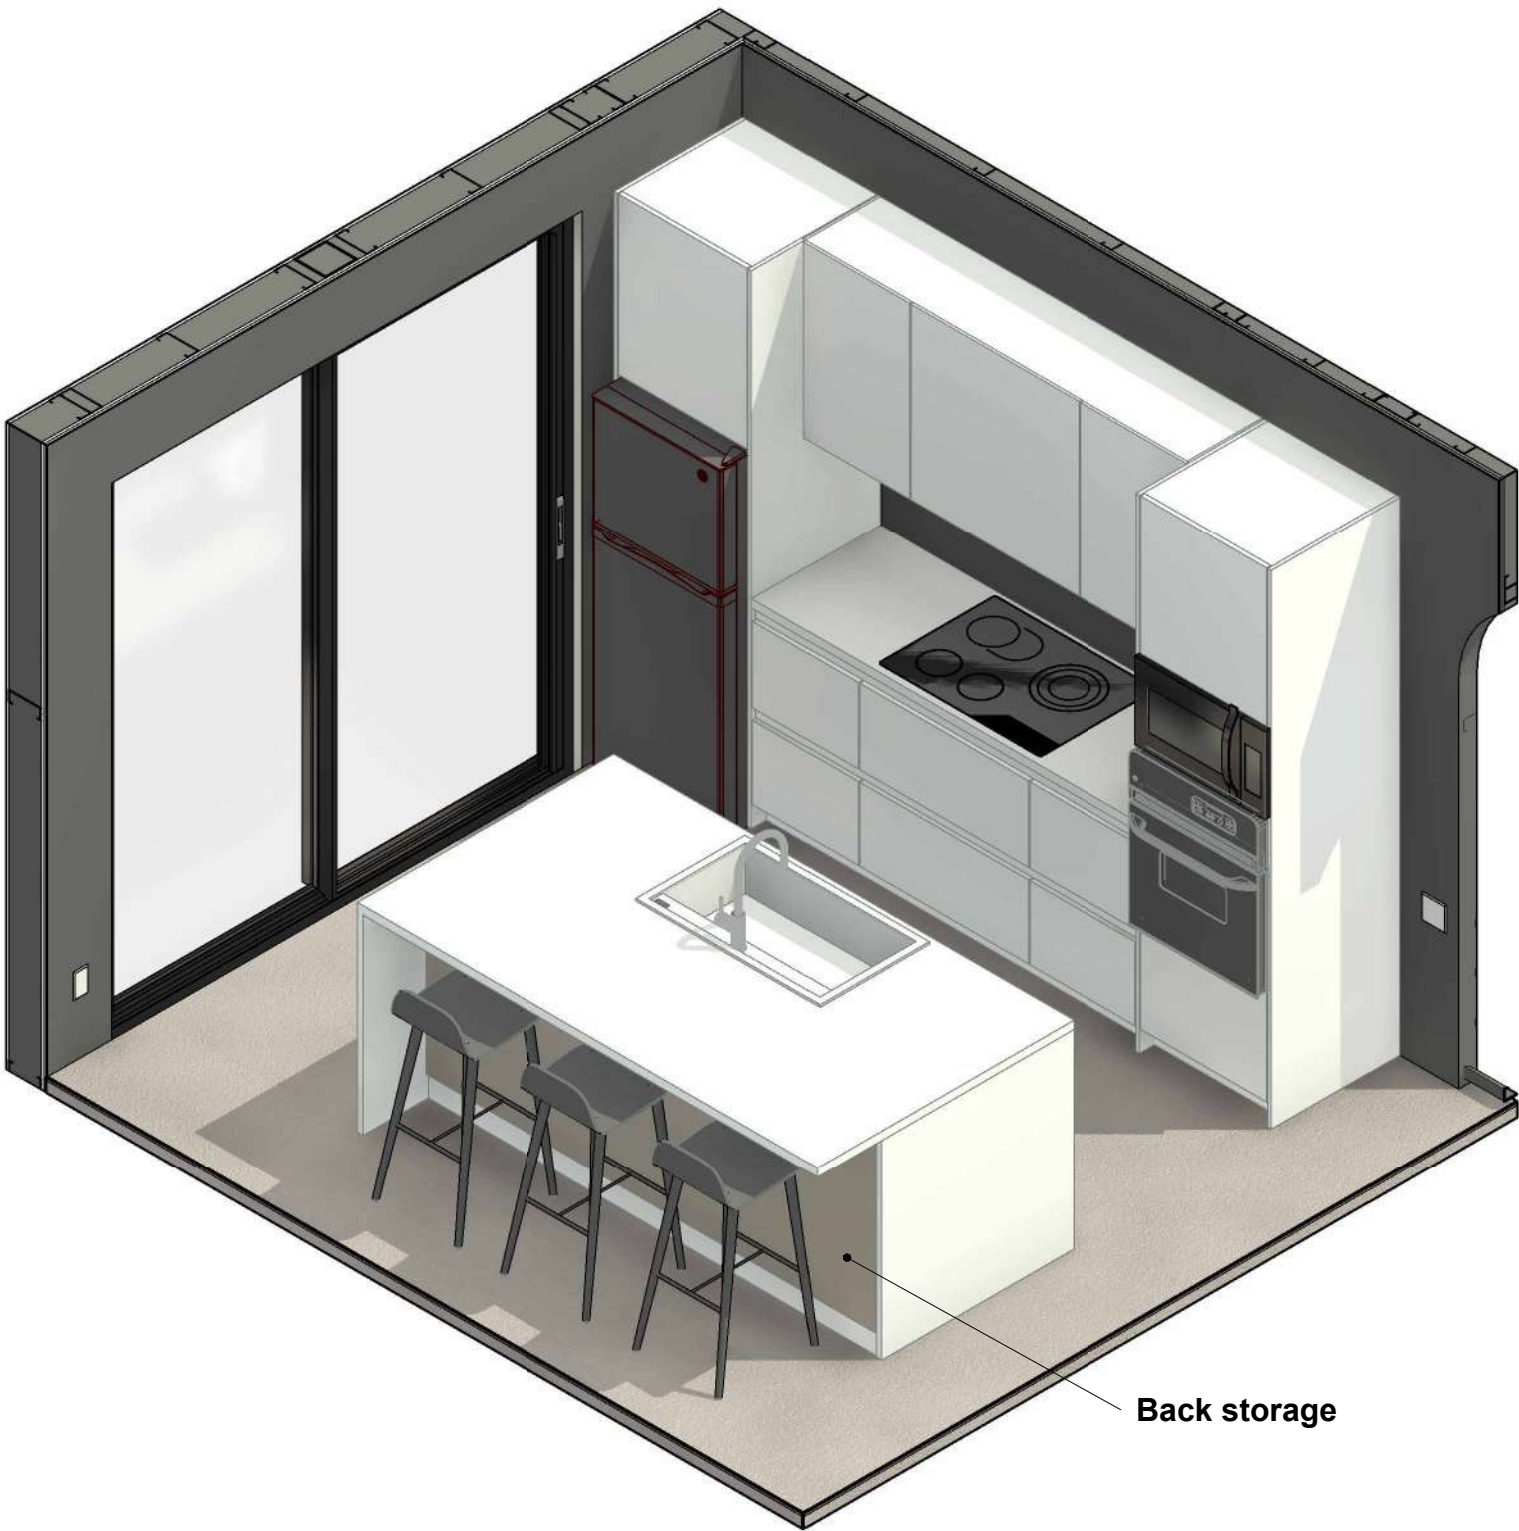

Kitchen 3D 1/25

1. THESE DRAWINGS MUST BE CHECKED BY THE CUSTOMER OR CONTRACTOR PRIOR TO APPROVAL. ANY ERRORS OR OMISSIONS MUST BE REPORTED IN WRITING TO BAUHU PRIOR TO COMMENCEMENT OF CONSTRUCTION.
2. ARCHITECTURAL DRAWINGS SHOULD BE READ IN CONJUNCTION WITH STRUCTURAL DETAILING AND FABRICATION GENERAL ASSEMBLY DRAWINGS.
3. FOR CONSTRUCTION PURPOSES, USE ONLY THE LATEST APPROVED DRAWINGS LABELED 'ISSUED FOR CONSTRUCTION'.
4. DO NOT SCALE FROM THIS DRAWING.
5. THE COMPANY OPERATES USING METRIC DIMENSIONS AS THE PRINCIPAL DENOMINATION.
6. ALL CONCRETE WORKS ARE OUTSIDE OF THE SCOPE OF THE COMPANY. INFORMATION REGARDING SLAB DESIGN AND CONNECTIONS IN THESE DRAWINGS ARE INTENDED FOR GUIDANCE ONLY. FOUNDATION AND SLAB WORKS SHOULD BE DESIGNED AND APPROVED BY A LOCAL STRUCTURAL ENGINEER.
7. THE COMPANY RETAINS FULL TITLE AND OWNERSHIP OF THESE PLANS AND DESIGNS. ANY UNAUTHORISED USE, REPRODUCTION, OR DISTRIBUTION OF THESE PLANS, WHETHER IN WHOLE OR PART, IS EXPRESSLY PROHIBITED WITHOUT PRIOR WRITTEN CONSENT.

No.	Revision	Date

ISSUED FOR:

Issued for information

Issued for client approval

Issued for fabrication

Issued for construction

Angel

DRAWING TITLE:

Kitchen Schedule

DRAWN BY:

Yonca A.Clark

SCALE:

As indicated


DRAWING NO:

A130


DATE:

01/05/2024


Island Back 1/20

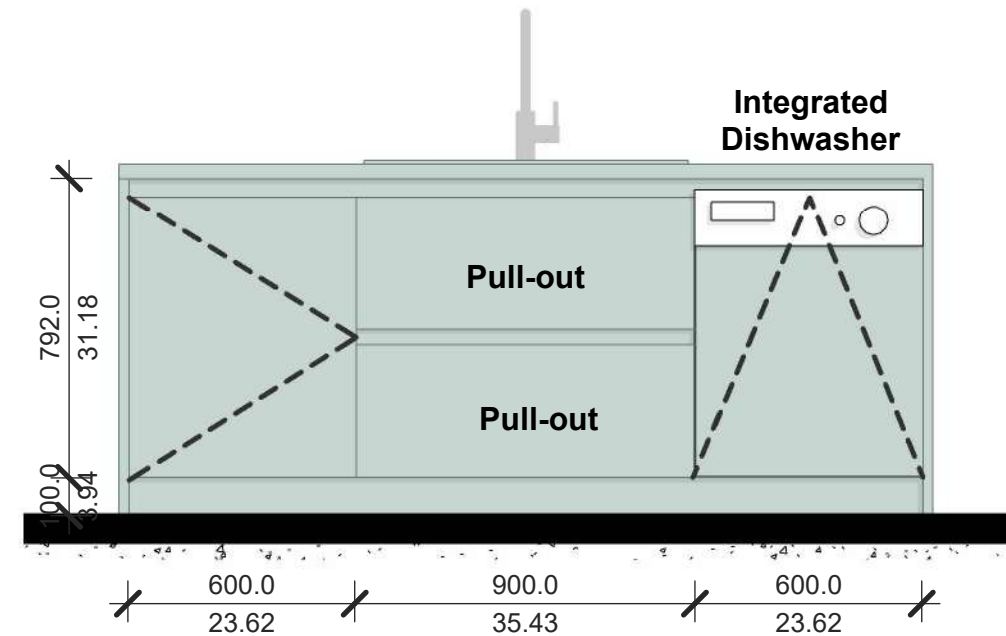

Island Front 1/20

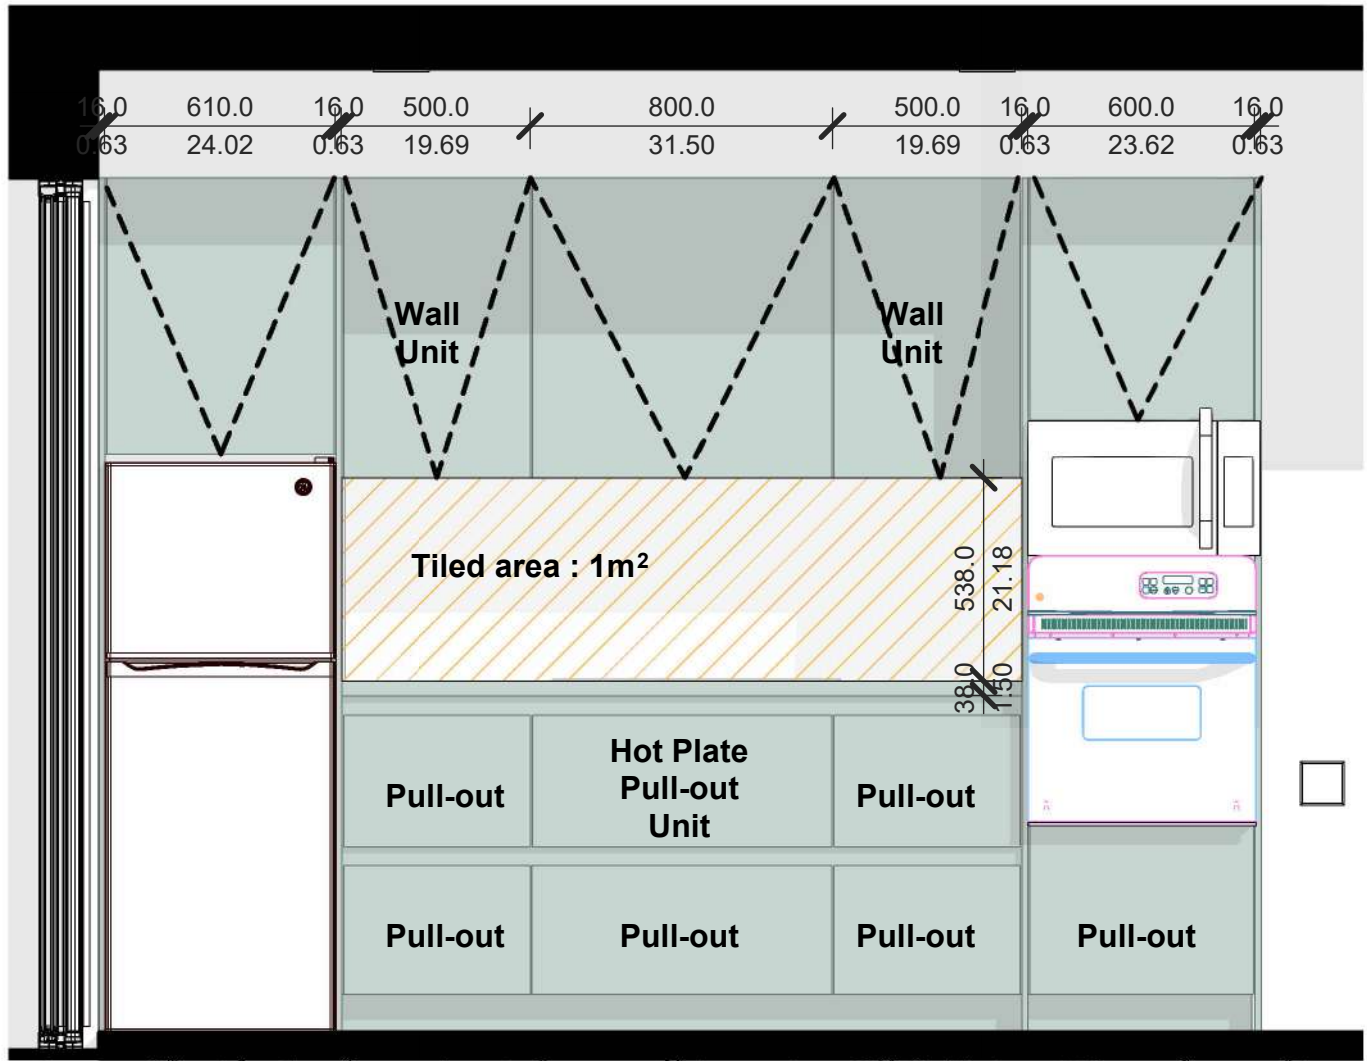

Wall Side Kitchen 1/20

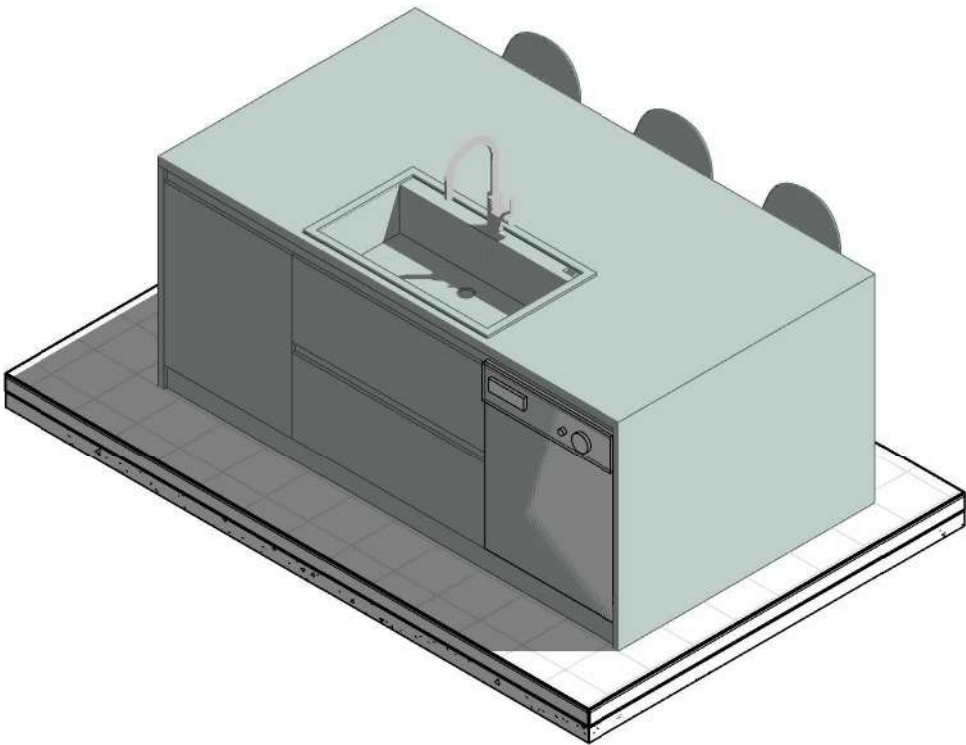


Island Front 1/25

Materials


Handless Linen N range
Front: 171 - Satin grey matt



Carcase Colour: 070 - Satin grey

 

Kitchen Worktop: 806 - Epic White (Quartz stone)

 

Handle: 006 - Recessed Handle (Line N), satin grey




Backside of the Island Colour: 126 - Oak Montreal reproduction



<https://www.nobilia.de/en/products/kitchens/designer-kitchens/fashion-171/>

Kitchen Faucet


Model: Bruma - Sink mixer with swivel spout and pull out aerator
Reference: 107 054 2CR
Finishes: Chrome
Count: 1

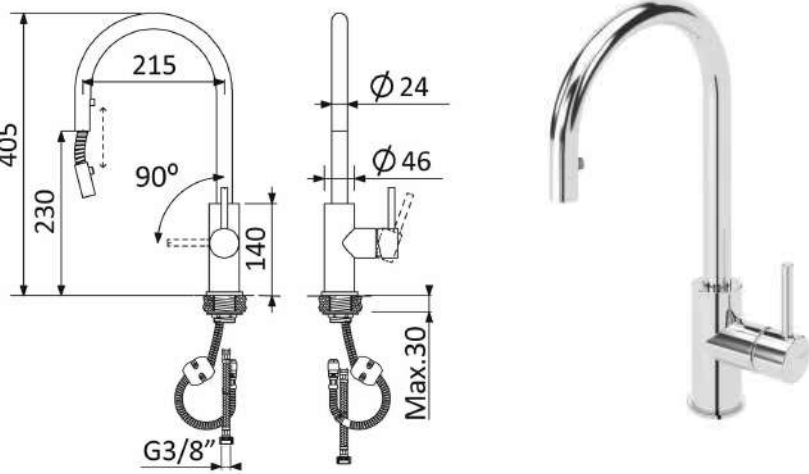

Kitchen Sink

Model: elleci - Lavello 1 vasca
Reference: Best 360
Dimensions (mm): 860 x 510
Finishes: K96 White
Count: 1

<https://www.elleci.com/it/prodotto/best-360/>

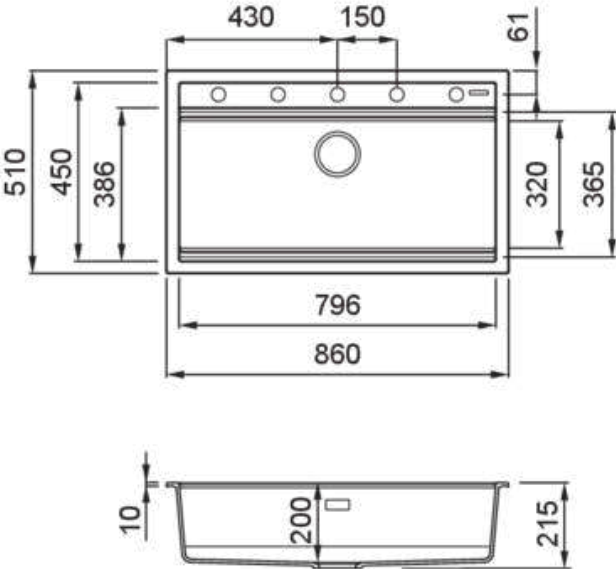

1. THESE DRAWINGS MUST BE CHECKED BY THE CUSTOMER OR CONTRACTOR PRIOR TO APPROVAL. ANY ERRORS OR OMISSIONS MUST BE REPORTED IN WRITING TO BAUHU PRIOR TO COMMENCEMENT OF CONSTRUCTION.
2. ARCHITECTURAL DRAWINGS SHOULD BE READ IN CONJUNCTION WITH STRUCTURAL DETAILING AND FABRICATION GENERAL ASSEMBLY DRAWINGS.
3. FOR CONSTRUCTION PURPOSES, USE ONLY THE LATEST APPROVED DRAWINGS LABELED 'ISSUED FOR CONSTRUCTION'.
4. DO NOT SCALE FROM THIS DRAWING.
5. THE COMPANY OPERATES USING METRIC DIMENSIONS AS THE PRINCIPAL DENOMINATION.
6. ALL CONCRETE WORKS ARE OUTSIDE OF THE SCOPE OF THE COMPANY. INFORMATION REGARDING SLAB DESIGN AND CONNECTIONS IN THESE DRAWINGS ARE INTENDED FOR GUIDENCE ONLY. FOUNDATION AND SLAB WORKS SHOULD BE DESIGNED AND APPROVED BY A LOCAL STRUCTURAL ENGINEER.
7. THE COMPANY RETAINS FULL TITLE AND OWNERSHIP OF THESE PLANS AND DESIGNS. ANY UNAUTHORISED USE, REPRODUCTION, OR DISTRIBUTION OF THESE PLANS, WHETHER IN WHOLE OR PART, IS EXPRESSLY PROHIBITED WITHOUT PRIOR WRITTEN CONSENT.

No.	Revision	Date

ISSUED FOR:

Issued for information

Issued for client approval

Issued for fabrication

Issued for construction

Angel

DRAWING TITLE:
Kitchen Schedule 2

DRAWN BY:
Yonca A.Clark

SCALE:

DRAWING NO:
A131

DATE:
01/05/2024

Wall Oven

Model: GE® 24" Electric Single Self-Cleaning Wall Oven
Reference: JRP20BJBB
Dimensions: 28 3/16 H x 23 3/4 W x 23 1/8 D



https://www.geappliances.com/appliance/GE-24-Electric-Single-Self-Cleaning-Wall-Oven-JRP20BJBB

Built-in Microwave (over oven)

Model: GE Profile™ 2.2 Cu. Ft. Built-In Sensor Microwave Oven
Reference: PEB7227ANDD
Dimensions: 14 H x 24 1/8 W x 19 3/4 D



https://www.geappliances.com/appliance/GE-Profile-2-2-Cu-Ft-Built-In-Sensor-Microwave-Oven-PEB7227ANDD

Fridge

Model: GE® ENERGY STAR® 11.6 cu. ft. Top-Freezer Refrigerator
Reference: GPE12FGKWW
Dimensions: 59 7/8 H x 24 W x 28 5/8 D

https://www.geappliances.com/appliance/GE-ENERGY-STAR-11-6-cu-ft-Top-Freezer-Refrigerator-GPE12FGKWW



Dishwasher

Model: GE Profile™ ENERGY STAR® Fingerprint Resistant Top Control Stainless Interior Dishwasher with Microban™ Antimicrobial Protection with Sanitize Cycle
Reference: PDT715SYVFS
Dimensions: 34 H x 23 3/4 W x 24 D



https://www.geappliances.com/appliance/GE-Profile-ENERGY-STAR-Fingerprint-Resistant-Top-Control-Stainless-Interior-Dishwasher-with-Microban-Antimicrobial-Protection-with-Sanitize-Cycle-PDT715SYVFS

Cooktop

Model: GE Profile™ 30" Built-In Touch Control Electric Cooktop
Reference: PEP9030STSS
Dimensions: 3 1/4 H x 29 7/8 W x 21 1/2 D



https://www.geappliances.com/appliance/GE-Profile-30-Built-In-Touch-Control-Electric-Cooktop-PEP9030STSS

- 1. THESE DRAWINGS MUST BE CHECKED BY THE CUSTOMER OR CONTRACTOR PRIOR TO APPROVAL. ANY ERRORS OR OMISSIONS MUST BE REPORTED IN WRITING TO BAUHU PRIOR TO COMMENCEMENT OF CONSTRUCTION.
- 2. ARCHITECTURAL DRAWINGS SHOULD BE READ IN CONJUNCTION WITH STRUCTURAL DETAILING AND FABRICATION GENERAL ASSEMBLY DRAWINGS.
- 3. FOR CONSTRUCTION PURPOSES, USE ONLY THE LATEST APPROVED DRAWINGS LABELED 'ISSUED FOR CONSTRUCTION'.
- 4. DO NOT SCALE FROM THIS DRAWING.
- 5. THE COMPANY OPERATES USING METRIC DIMENSIONS AS THE PRINCIPAL DENOMINATION.
- 6. ALL CONCRETE WORKS ARE OUTSIDE OF THE SCOPE OF THE COMPANY. INFORMATION REGARDING SLAB DESIGN AND CONNECTIONS IN THESE DRAWINGS ARE INTENDED FOR GUIDENCE ONLY. FOUNDATION AND SLAB WORKS SHOULD BE DESIGNED AND APPROVED BY A LOCAL STRUCTURAL ENGINEER.
- 7. THE COMPANY RETAINS FULL TITLE AND OWNERSHIP OF THESE PLANS AND DESIGNS. ANY UNAUTHORISED USE, REPRODUCTION, OR DISTRIBUTION OF THESE PLANS, WHETHER IN WHOLE OR PART, IS EXPRESSLY PROHIBITED WITHOUT PRIOR WRITTEN CONSENT.

No.	Revision	Date

ISSUED FOR:

Issued for information

Issued for client approval

Issued for fabrication


Issued for construction

Angel

DRAWING TITLE:	Kitchen Appliances
DRAWN BY:	Yonca A.Clark
SCALE:	
DRAWING NO:	A132
DATE:	01/05/2024

Toilet

Sanindusa
Model: Sanlife F|D low level toilet
Reference: 136011
Finish: Vitreous China - 00 White
Count: 2

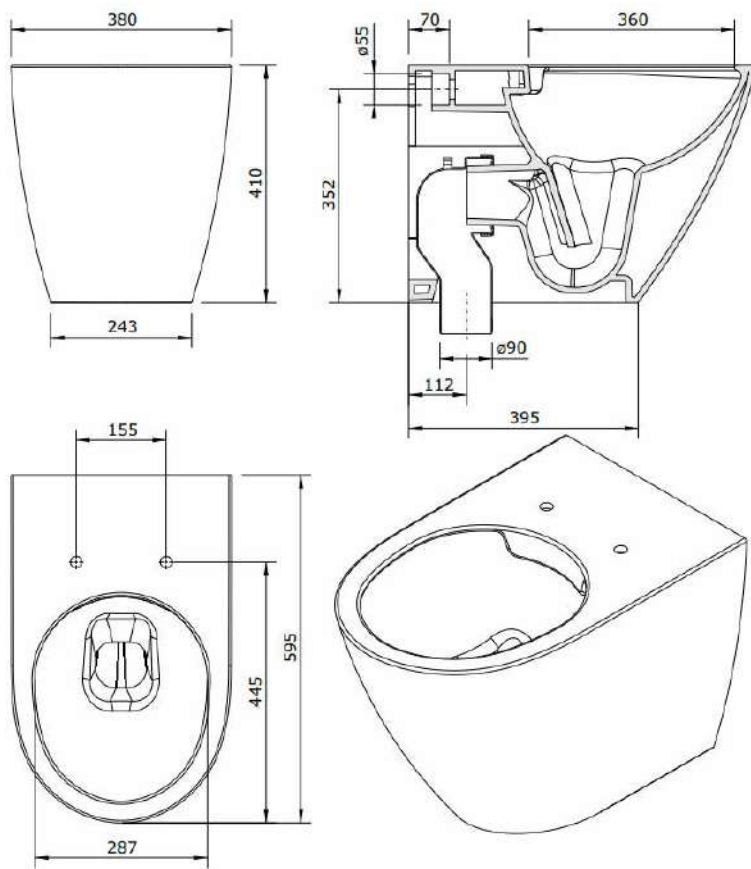

<https://www.tec.sanindusa.pt/w-d-low-level-toilet-sanlife>

Cistern


Sanindusa
Model: Switch built-in cistern for low level toilet
Reference: 40133
Series: Switch
Count: 2

<https://www.tec.sanindusa.pt/switch-built-in-cistern-for-low-level-wc>

Flush Plate

Sanindusa
Model: Plan dual flush plate
Reference: 40013XX
Series: Plan
Finish: Chrome
Count: 2


<https://www.tec.sanindusa.pt/index.php?id=25&p=600>

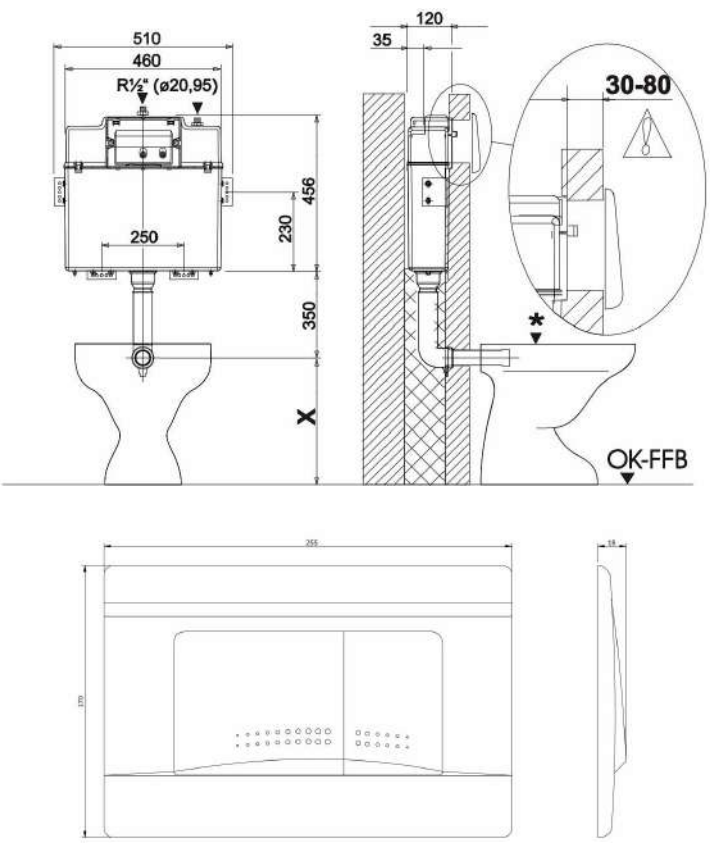

1. THESE DRAWINGS MUST BE CHECKED BY THE CUSTOMER OR CONTRACTOR PRIOR TO APPROVAL. ANY ERRORS OR OMISSIONS MUST BE REPORTED IN WRITING TO BAUHU PRIOR TO COMMENCEMENT OF CONSTRUCTION.
2. ARCHITECTURAL DRAWINGS SHOULD BE READ IN CONJUNCTION WITH STRUCTURAL DETAILING AND FABRICATION GENERAL ASSEMBLY DRAWINGS.
3. FOR CONSTRUCTION PURPOSES, USE ONLY THE LATEST APPROVED DRAWINGS LABELED 'ISSUED FOR CONSTRUCTION'.
4. DO NOT SCALE FROM THIS DRAWING.
5. THE COMPANY OPERATES USING METRIC DIMENSIONS AS THE PRINCIPAL DENOMINATION.
6. ALL CONCRETE WORKS ARE OUTSIDE OF THE SCOPE OF THE COMPANY. INFORMATION REGARDING SLAB DESIGN AND CONNECTIONS IN THESE DRAWINGS ARE INTENDED FOR GUIDANCE ONLY. FOUNDATION AND SLAB WORKS SHOULD BE DESIGNED AND APPROVED BY A LOCAL STRUCTURAL ENGINEER.
7. THE COMPANY RETAINS FULL TITLE AND OWNERSHIP OF THESE PLANS AND DESIGNS. ANY UNAUTHORISED USE, REPRODUCTION, OR DISTRIBUTION OF THESE PLANS, WHETHER IN WHOLE OR PART, IS EXPRESSLY PROHIBITED WITHOUT PRIOR WRITTEN CONSENT.

Shower Taps

Bruma
Model: Shower system for wall mounting with adjustable ABS head shower Ø230mm and shower rail
Reference: 107 281 1CR
Finishes: Chrome
Count: 2

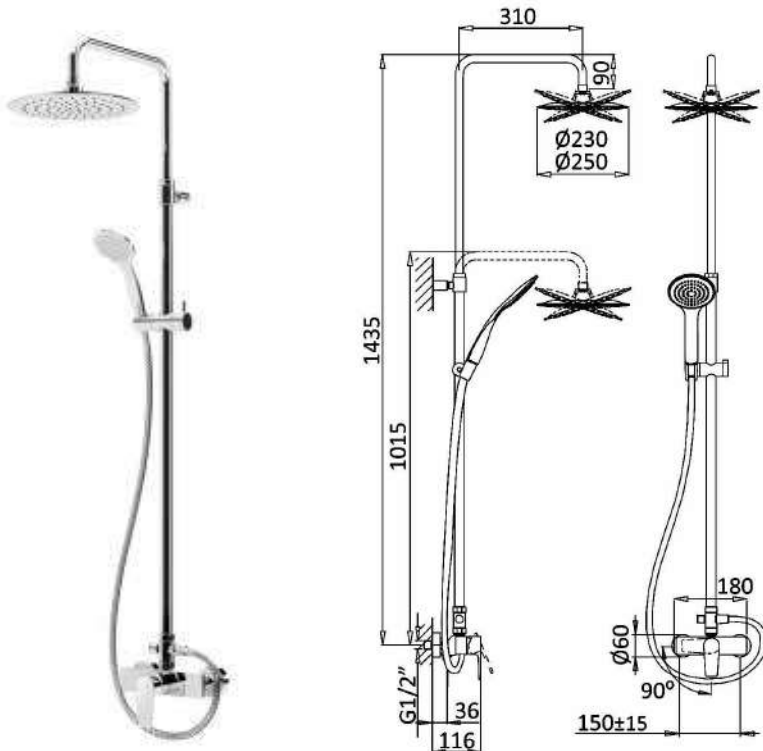


https://www.bruma.pt/index.php?page=products&prod=5482#open_product

Shower enclosure

Sanindusa
Model: SAFIRA SHOWER PANEL
Reference: 8966802211
EAN CODE. 5604815458190
Finish: Transparent and Chrome
Count: 1
Model:SAFIRA SUPPORT ARM
Reference: 8A966000011
Count: 1

Shower enclosure


Sanindusa
Model: Versus 90cm shower enclosure
Reference: 8930400000
EAN CODE. 5604815438123
Finish: Transparent and White
Count: 1

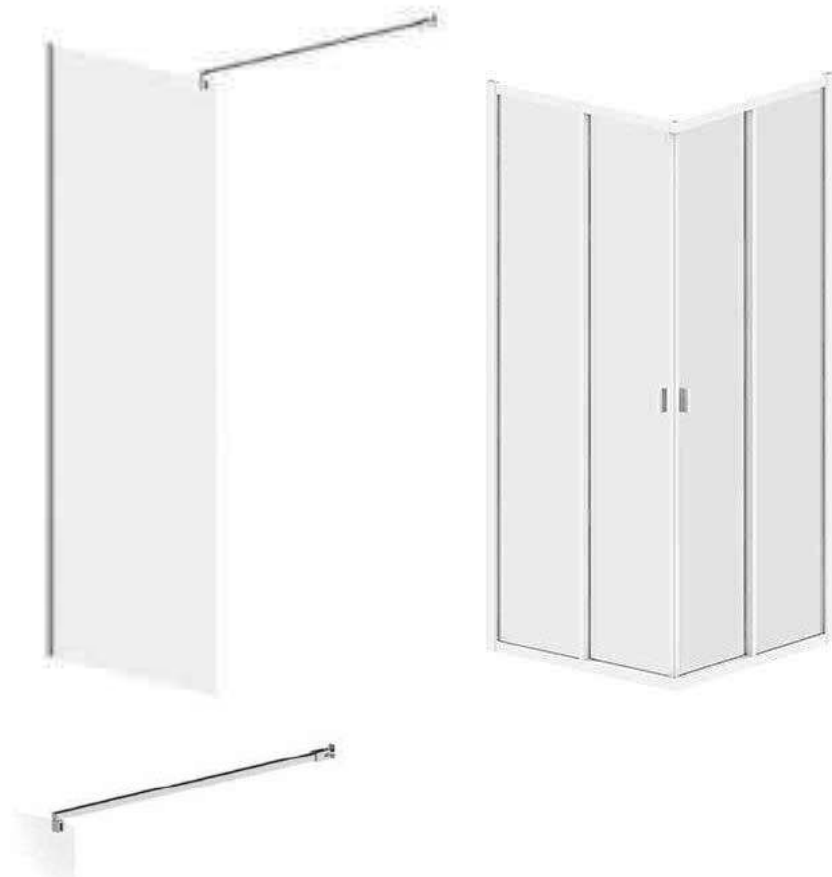

Shower Drain

Sanindusa
Model: Shower channel drain with grid 700
Reference: 49070
Finishes: Brushed Stainless Steel
Count: 2

Note: Italian Shower floors should have the specified Metric shower channel drain inset into the floor slab/screed before applying the selected floor tile finish. Contractors should provide a shallow fall towards the shower channel drain.

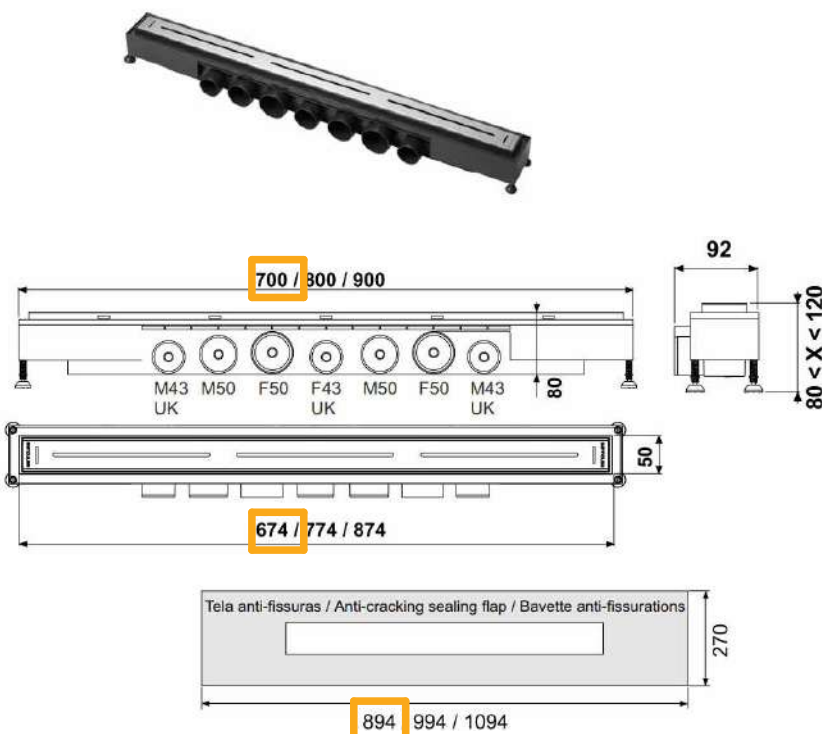


<https://www.tec.sanindusa.pt/metric-70-shower-channel-with-grid>

Vanity Faucet

Bruma
Model: Nautic
Reference: 181 010 1CR
Finishes: Chrome
Count: 1

Bruma
Model: Nautic
Reference: 181 210 1CR
Finishes: Chrome
Count: 1

https://www.bruma.pt/index.php?page=products&prod=5426#open_product

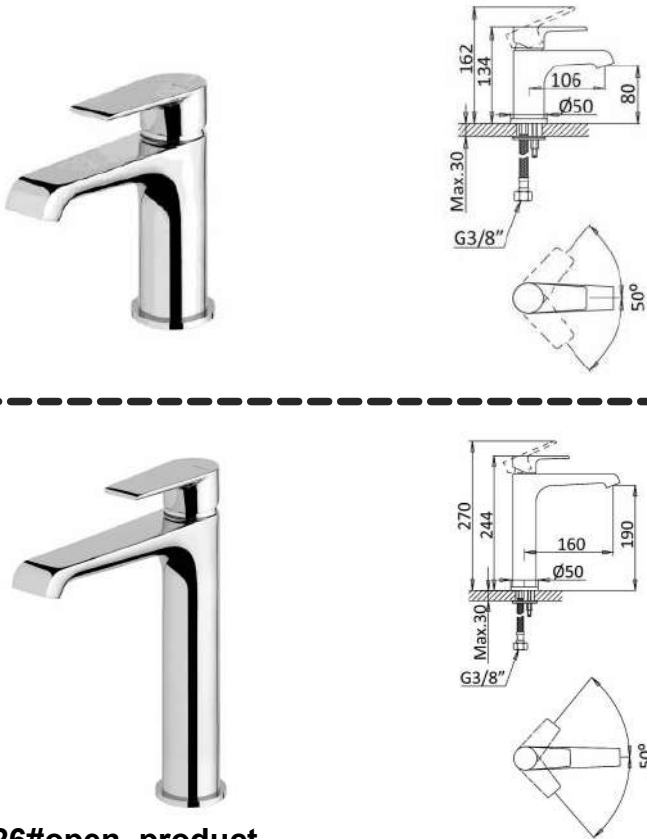

Angel

DRAWING TITLE:
Bathroom Furnitures

DRAWN BY:
Yonca A.Clark

SCALE:


DRAWING NO:
A133

DATE:
01/05/2024

Note: Sanitary ware, faucets, kitchen and bathroom equipment are provided. Plumbing supply pipework, waste and sub-slab roughings are excluded. Plumbing plan is provided as a guide for contractor information only.

En-suite Bathroom Vanity Unit


Kitbanho
Model: ANCARA ALT. 50
Reference:100 S
Dimension: 1000
Front: Hercules
Countertop/Sides: White
Count: 1
• same as the reference image
• sink on the right side

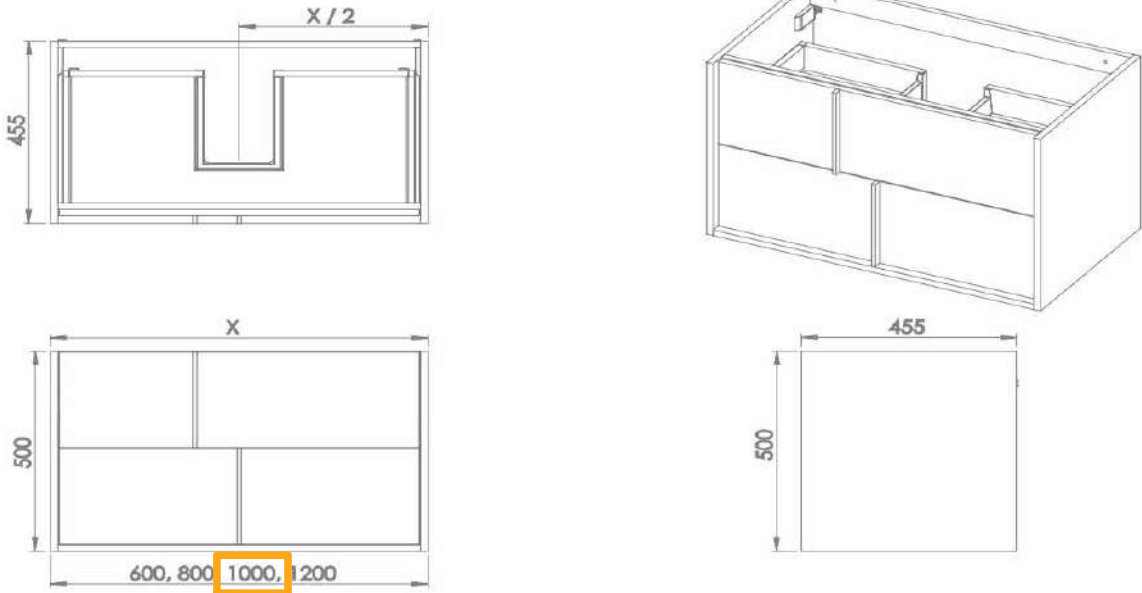

https://www.kitbanho.com/en/products/bathroom-furniture/ancara-2

En-suite Bathroom Countertop Washbasin

Model: ZAMORA
Dimension:1000
Reference: 100 S
Finish: White bright
Count: 1

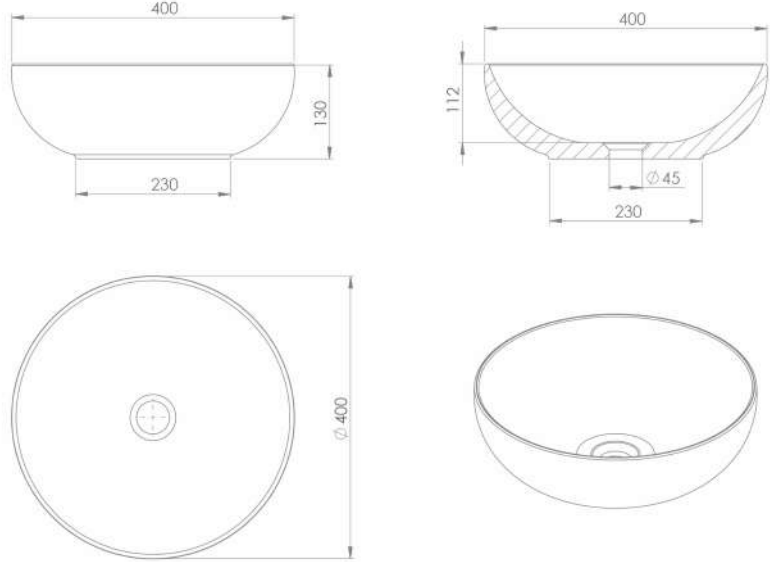


https://www.kitbanho.com/en/products/countertop-washbasin/zamora-3

1. THESE DRAWINGS MUST BE CHECKED BY THE CUSTOMER OR CONTRACTOR PRIOR TO APPROVAL. ANY ERRORS OR OMISSIONS MUST BE REPORTED IN WRITING TO BAUHU PRIOR TO COMMENCEMENT OF CONSTRUCTION.
2. ARCHITECTURAL DRAWINGS SHOULD BE READ IN CONJUNCTION WITH STRUCTURAL DETAILING AND FABRICATION GENERAL ASSEMBLY DRAWINGS.
3. FOR CONSTRUCTION PURPOSES, USE ONLY THE LATEST APPROVED DRAWINGS LABELED 'ISSUED FOR CONSTRUCTION'.
4. DO NOT SCALE FROM THIS DRAWING.
5. THE COMPANY OPERATES USING METRIC DIMENSIONS AS THE PRINCIPAL DENOMINATION.
6. ALL CONCRETE WORKS ARE OUTSIDE OF THE SCOPE OF THE COMPANY. INFORMATION REGARDING SLAB DESIGN AND CONNECTIONS IN THESE DRAWINGS ARE INTENDED FOR GUIDENCE ONLY. FOUNDATION AND SLAB WORKS SHOULD BE DESIGNED AND APPROVED BY A LOCAL STRUCTURAL ENGINEER.
7. THE COMPANY RETAINS FULL TITLE AND OWNERSHIP OF THESE PLANS AND DESIGNS. ANY UNAUTHORISED USE, REPRODUCTION, OR DISTRIBUTION OF THESE PLANS, WHETHER IN WHOLE OR PART, IS EXPRESSLY PROHIBITED WITHOUT PRIOR WRITTEN CONSENT.

Bathroom Vanity Unit


Kitbanho
Model: ODESSA
Reference:100 SD
Dimension: 1000
Melamine: Oak 06
• same as the reference image
Count: 1

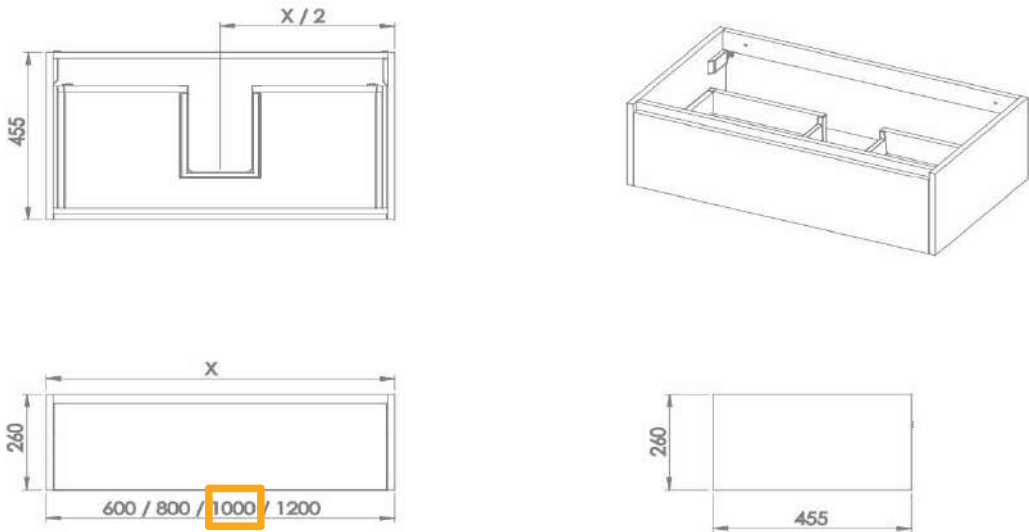

https://www.kitbanho.com/en/products/bathroom-furniture/odessa-3

Bathroom Vanity Washbasin

Model: : LAV. BANCA KLOSS STD ALT.10
Dimension:1000
Reference: 100 S
Count: 1

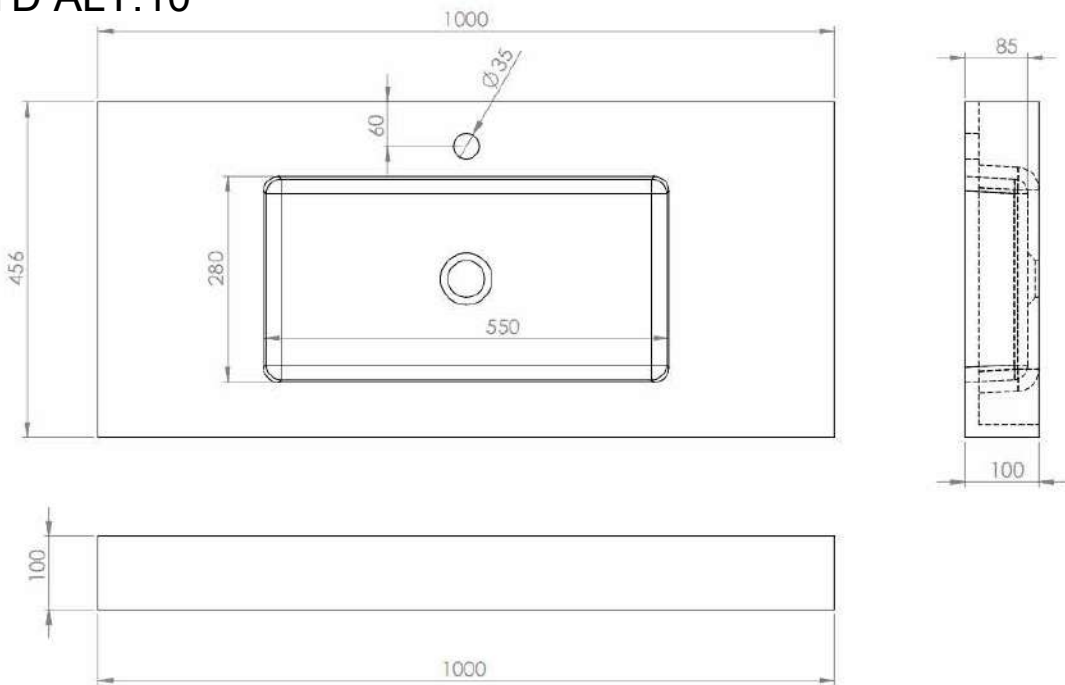

https://www.kitbanho.com/en/products/washbasins/kloss-std-alt-10-1

No.	Revision	Date

ISSUED FOR:

Issued for information

Issued for client approval

Issued for fabrication

Issued for construction

Complement


Kitbanho
Model: Turim
Reference: CUBES INFERIORS SKY
Dimension:1000
Finish: White
Count: 1



https://www.kitbanho.com/en/products/complement/cubes


Mirror

Kitbanho
Model: ESPELHO POMPEIA
Dimension:1000
Count: 1

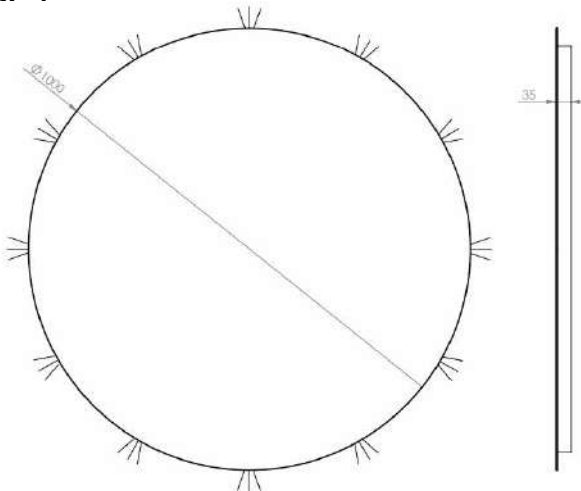

https://www.kitbanho.com/en/products/mirrors

Kitbanho
Model: Dali Mirror
Dimension: 1000
Count: 1

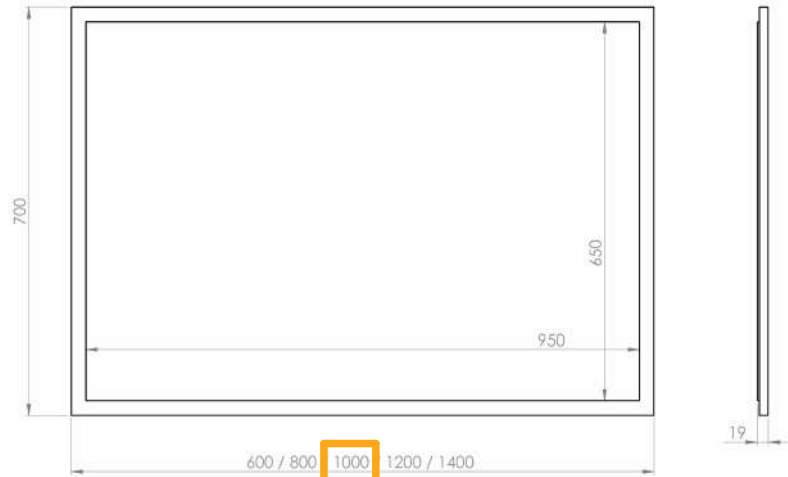

Angel

DRAWING TITLE:

Bathroom Furnitures 2

DRAWN BY:

Yonca A.Clark

SCALE:

DRAWING NO:

A134

DATE:

01/05/2024

Note: Sanitary ware, faucets, kitchen and bathroom equipment are provided. Plumbing supply pipework, waste and sub-slab roughings are excluded. Plumbing plan is provided as a guide for contractor information only.

1. THESE DRAWINGS MUST BE CHECKED BY THE CUSTOMER OR CONTRACTOR PRIOR TO APPROVAL. ANY ERRORS OR OMISSIONS MUST BE REPORTED IN WRITING TO BAUHU PRIOR TO COMMENCEMENT OF CONSTRUCTION.
2. ARCHITECTURAL DRAWINGS SHOULD BE READ IN CONJUNCTION WITH STRUCTURAL DETAILING AND FABRICATION GENERAL ASSEMBLY DRAWINGS.
3. FOR CONSTRUCTION PURPOSES, USE ONLY THE LATEST APPROVED DRAWINGS LABELED 'ISSUED FOR CONSTRUCTION'.
4. DO NOT SCALE FROM THIS DRAWING.
5. THE COMPANY OPERATES USING METRIC DIMENSIONS AS THE PRINCIPAL DENOMINATION.
6. ALL CONCRETE WORKS ARE OUTSIDE OF THE SCOPE OF THE COMPANY. INFORMATION REGARDING SLAB DESIGN AND CONNECTIONS IN THESE DRAWINGS ARE INTENDED FOR GUIDANCE ONLY. FOUNDATION AND SLAB WORKS SHOULD BE DESIGNED AND APPROVED BY A LOCAL STRUCTURAL ENGINEER.
7. THE COMPANY RETAINS FULL TITLE AND OWNERSHIP OF THESE PLANS AND DESIGNS. ANY UNAUTHORISED USE, REPRODUCTION, OR DISTRIBUTION OF THESE PLANS, WHETHER IN WHOLE OR PART, IS EXPRESSLY PROHIBITED WITHOUT PRIOR WRITTEN CONSENT.

No.	Revision	Date

ISSUED FOR:

Issued for information

Issued for client approval

Issued for fabrication

Issued for construction

Angel

DRAWING TITLE:	En-suite Bathroom
DRAWN BY:	Yonca A.Clark
SCALE:	1 : 25
DRAWING NO:	A135
DATE:	01/05/2024

Tile

- En-Suite Bathroom Wall Tile 1**
- Decor Tokyo Brown TK46R
 - 34 x 66,5 cm . 13,4" x 26,2" / R17
 - Decorations, Concrete, Color, Not Rectified
 - White Body Wall Tiles, Mate





Total Tiled Area 1: 9.6m²

- En-Suite Bathroom Wall Tile 2**
- One Beige ON28R
 - 34 x 91,5 cm . 13,4" x 36" / R19
 - Color, Not Rectified
 - White Body Wall Tiles, Mate




Total Tiled Area 2: 6.5m²

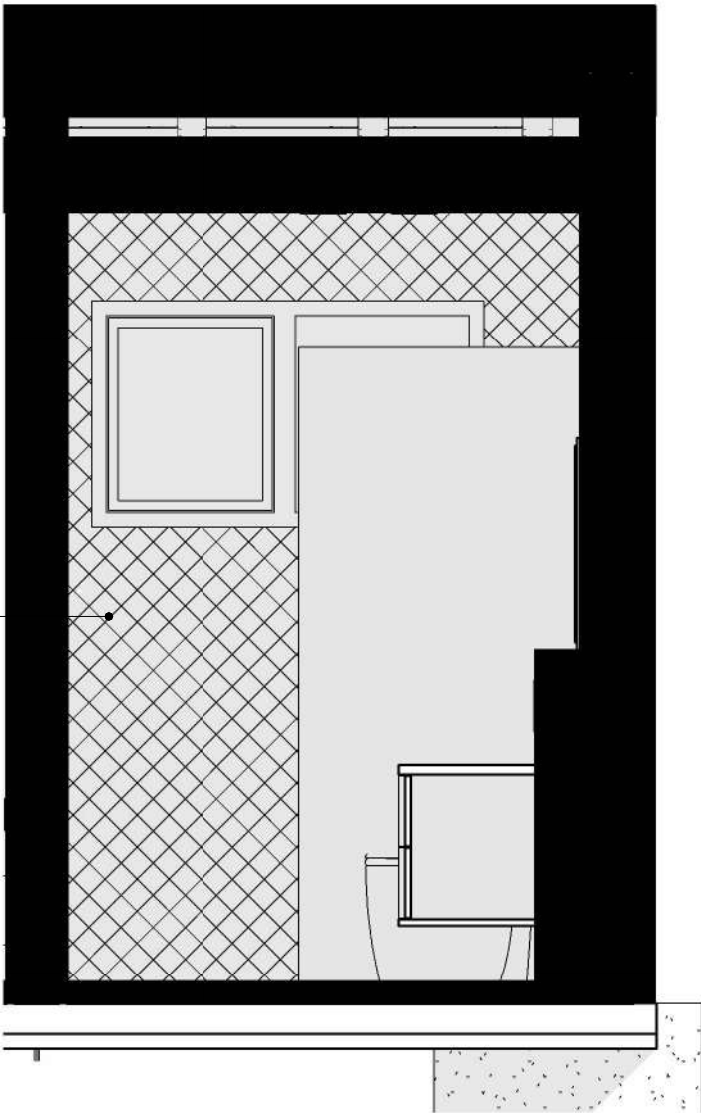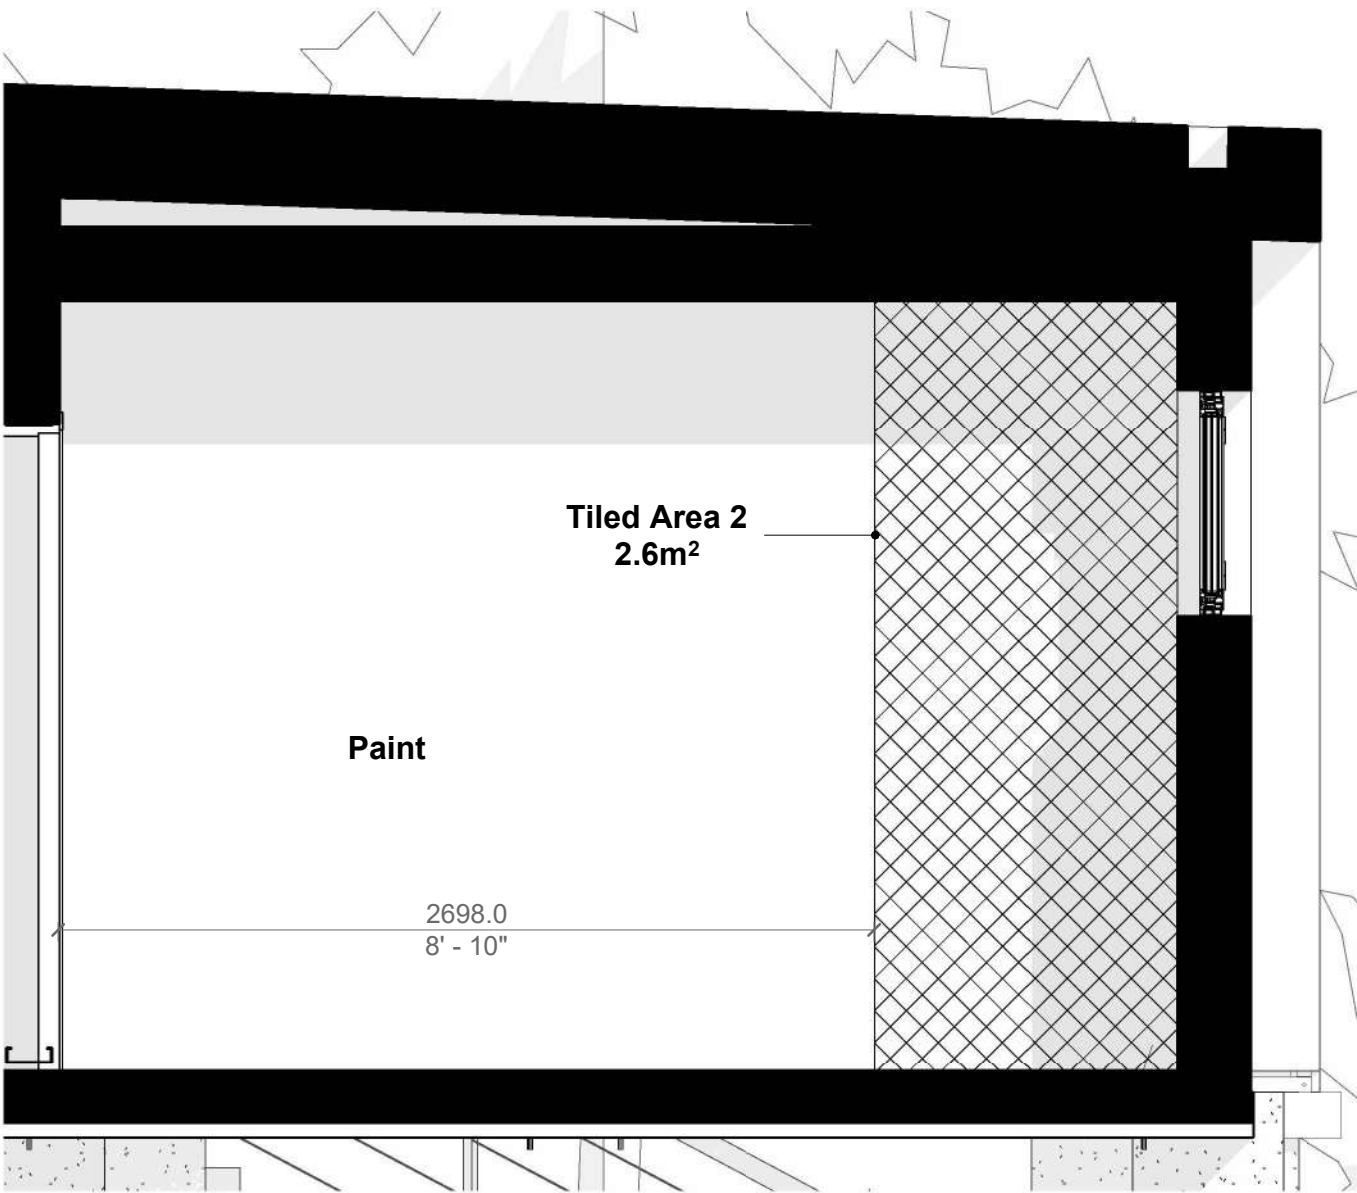


Tiled Area 2
3.3m²

3 Section 11
1 : 25

4 Section 12
1 : 25

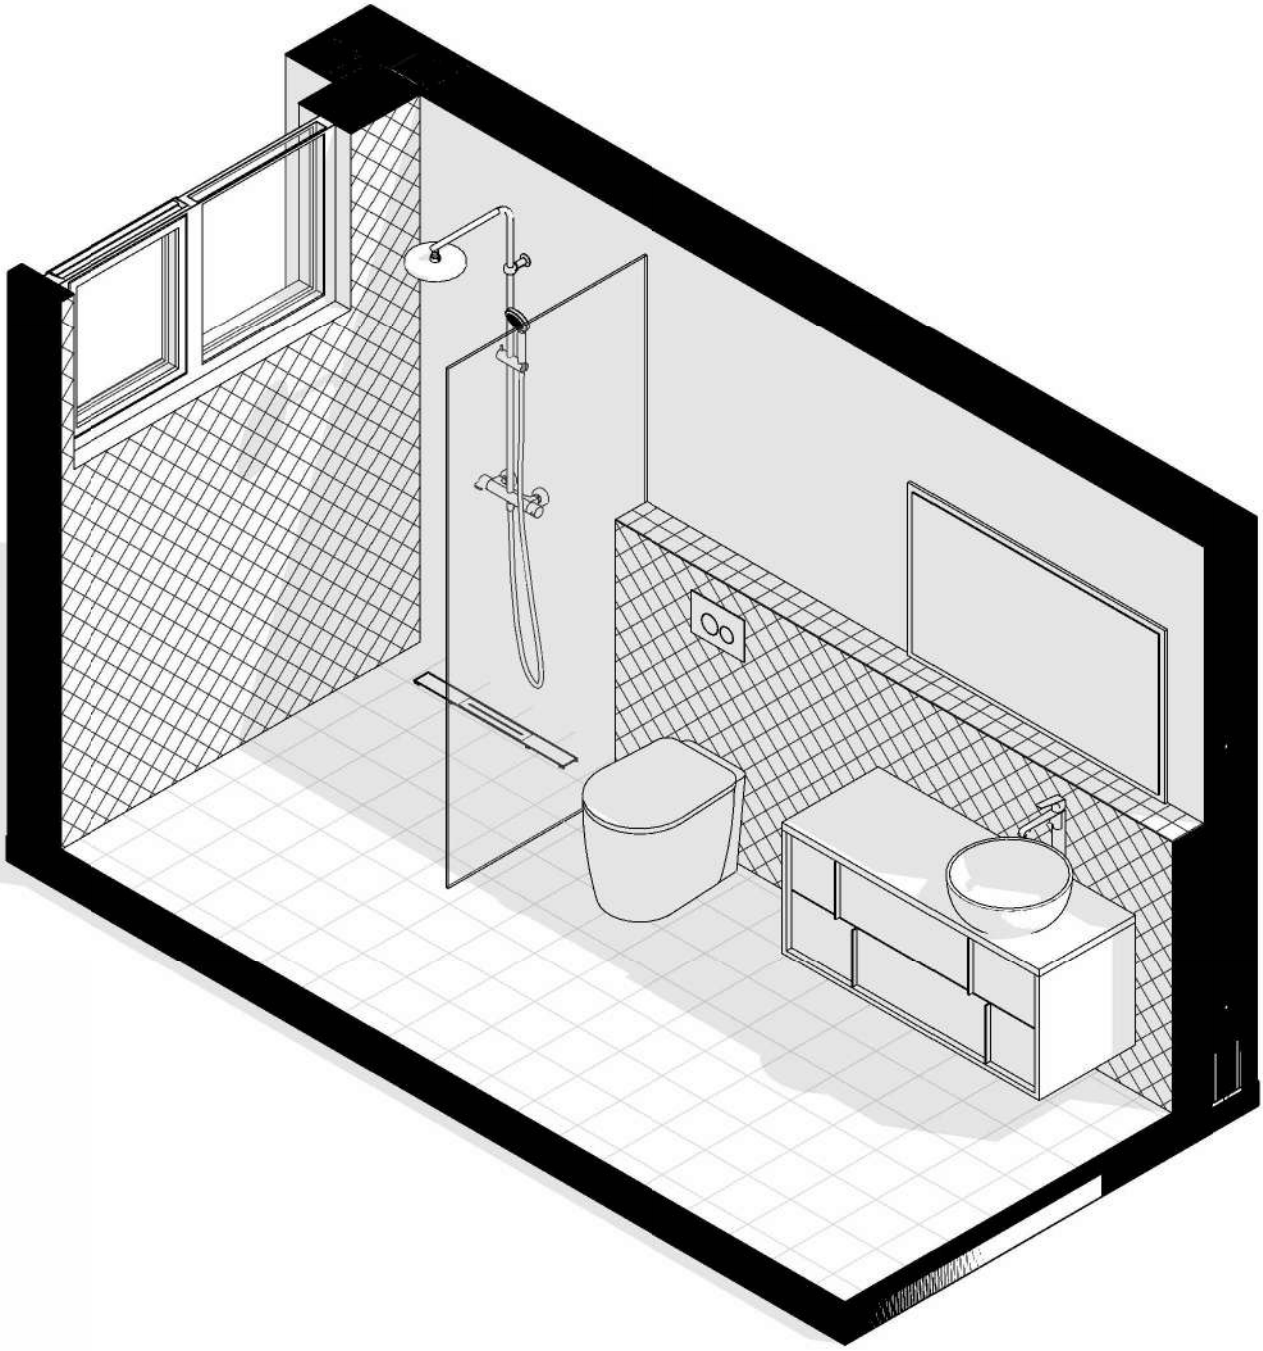

2 EN SUITE BATHROOM

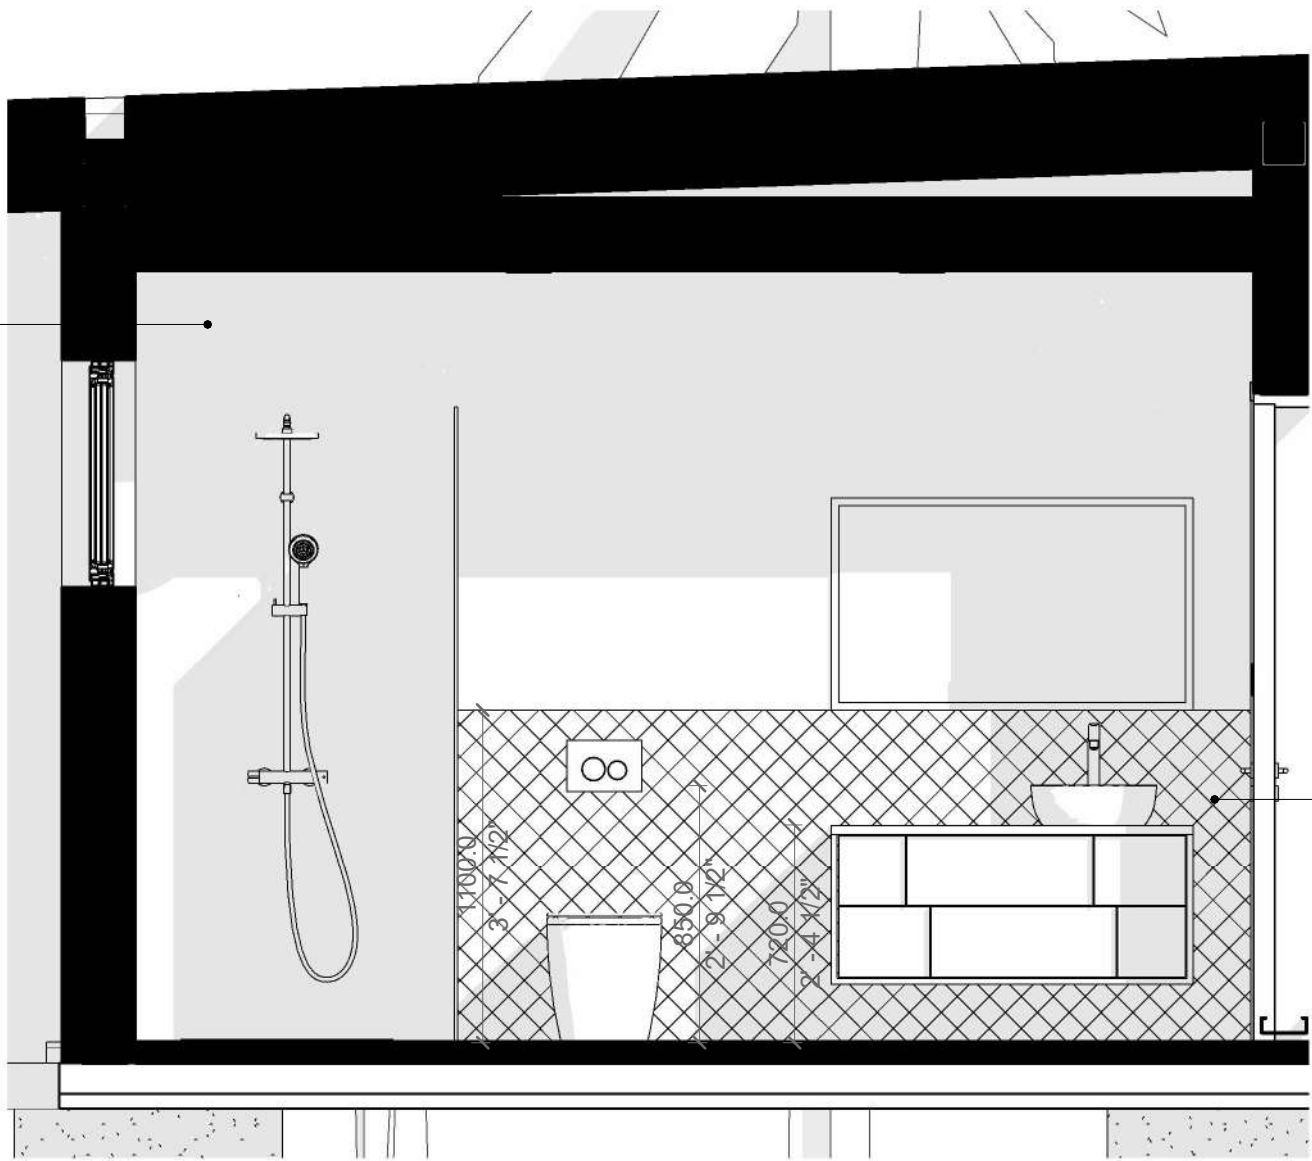

Tiled Area 1
6.5m²

Tiled Area 2
3.6m²

1 Section 6
1 : 25

1. THESE DRAWINGS MUST BE CHECKED BY THE CUSTOMER OR CONTRACTOR PRIOR TO APPROVAL. ANY ERRORS OR OMISSIONS MUST BE REPORTED IN WRITING TO BAUHU PRIOR TO COMMENCEMENT OF CONSTRUCTION.
2. ARCHITECTURAL DRAWINGS SHOULD BE READ IN CONJUNCTION WITH STRUCTURAL DETAILING AND FABRICATION GENERAL ASSEMBLY DRAWINGS.
3. FOR CONSTRUCTION PURPOSES, USE ONLY THE LATEST APPROVED DRAWINGS LABELED 'ISSUED FOR CONSTRUCTION'.
4. DO NOT SCALE FROM THIS DRAWING.
5. THE COMPANY OPERATES USING METRIC DIMENSIONS AS THE PRINCIPAL DENOMINATION.
6. ALL CONCRETE WORKS ARE OUTSIDE OF THE SCOPE OF THE COMPANY. INFORMATION REGARDING SLAB DESIGN AND CONNECTIONS IN THESE DRAWINGS ARE INTENDED FOR GUIDANCE ONLY. FOUNDATION AND SLAB WORKS SHOULD BE DESIGNED AND APPROVED BY A LOCAL STRUCTURAL ENGINEER.
7. THE COMPANY RETAINS FULL TITLE AND OWNERSHIP OF THESE PLANS AND DESIGNS. ANY UNAUTHORISED USE, REPRODUCTION, OR DISTRIBUTION OF THESE PLANS, WHETHER IN WHOLE OR PART, IS EXPRESSLY PROHIBITED WITHOUT PRIOR WRITTEN CONSENT.

No.	Revision	Date

ISSUED FOR:

Issued for information

Issued for client approval

Issued for fabrication

Issued for construction

Angel

DRAWING TITLE:

Bathroom

DRAWN BY:

Yonca A.Clark

SCALE:


1 : 25

DRAWING NO:


A136

DATE:


01/05/2024

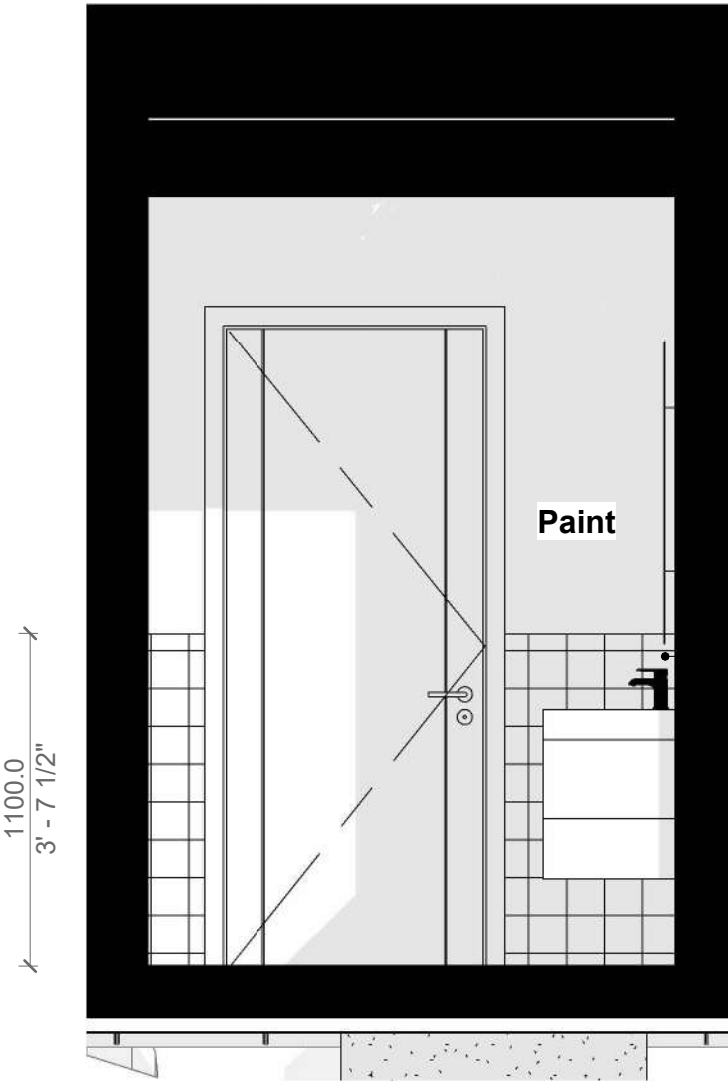

Tiled Area 1:
0.8m²

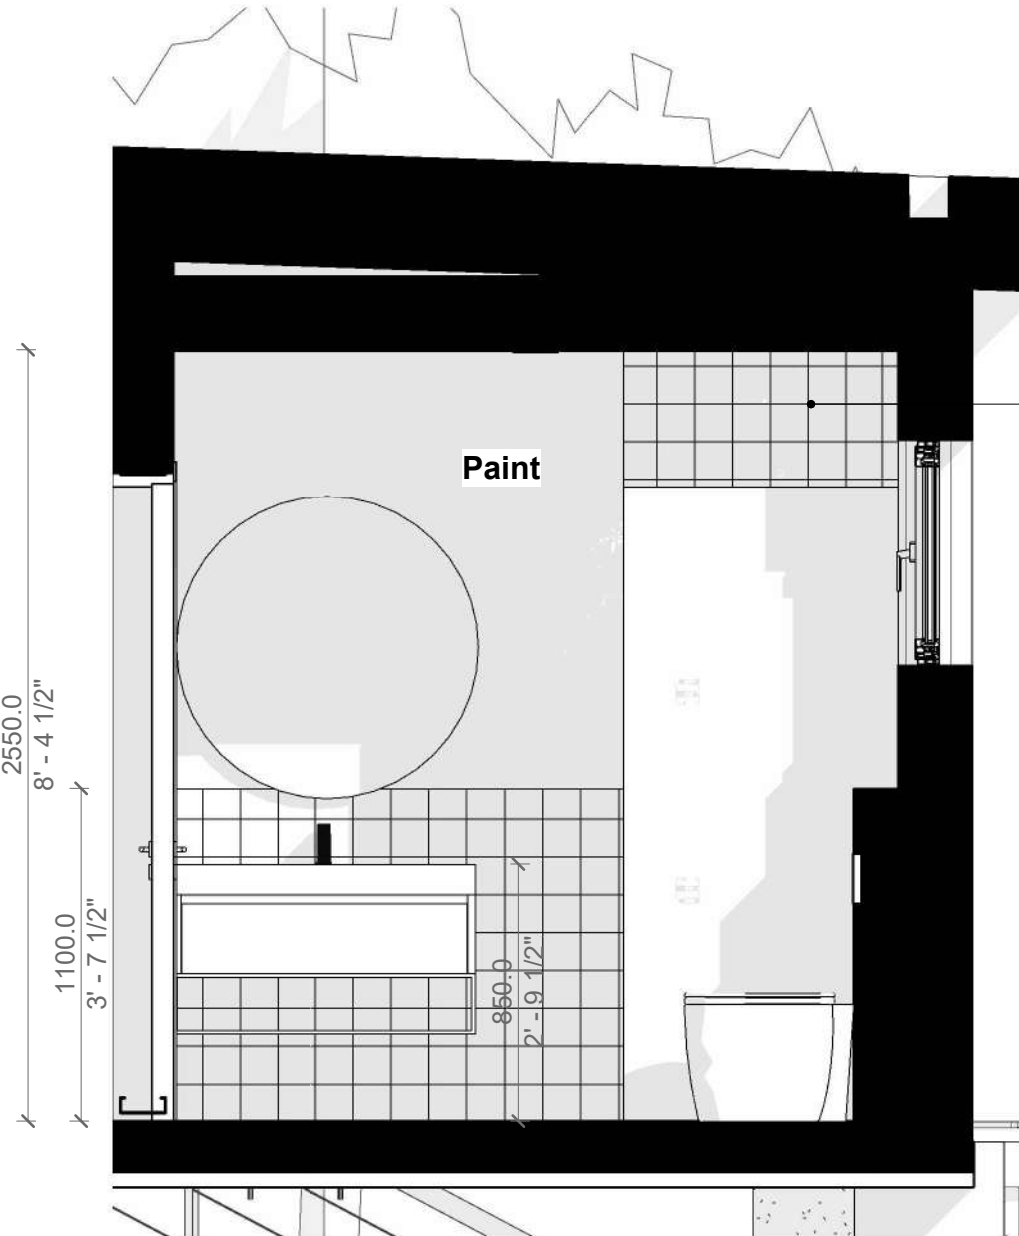

Tiled Area 1:
4m²

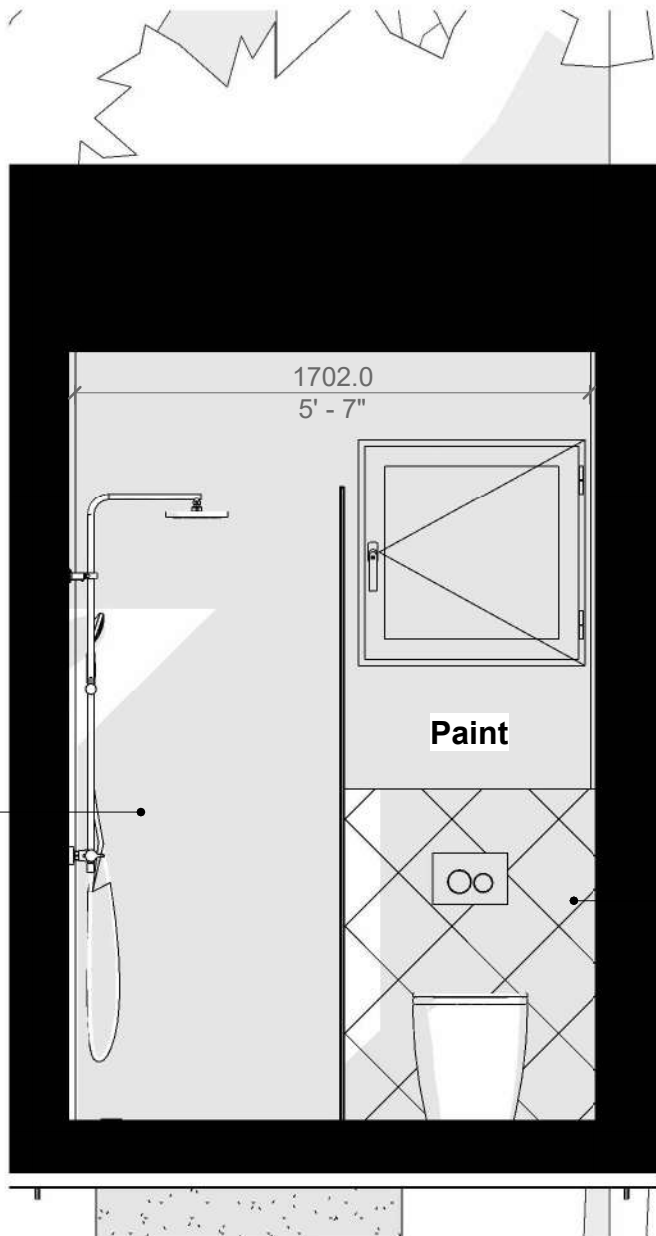


Tiled Area 1:
2.3m²

Tiled Area 2:
1.4m²


3 Section 9
1 : 25

2 Section 8
1 : 25

1 Section 7
1 : 25

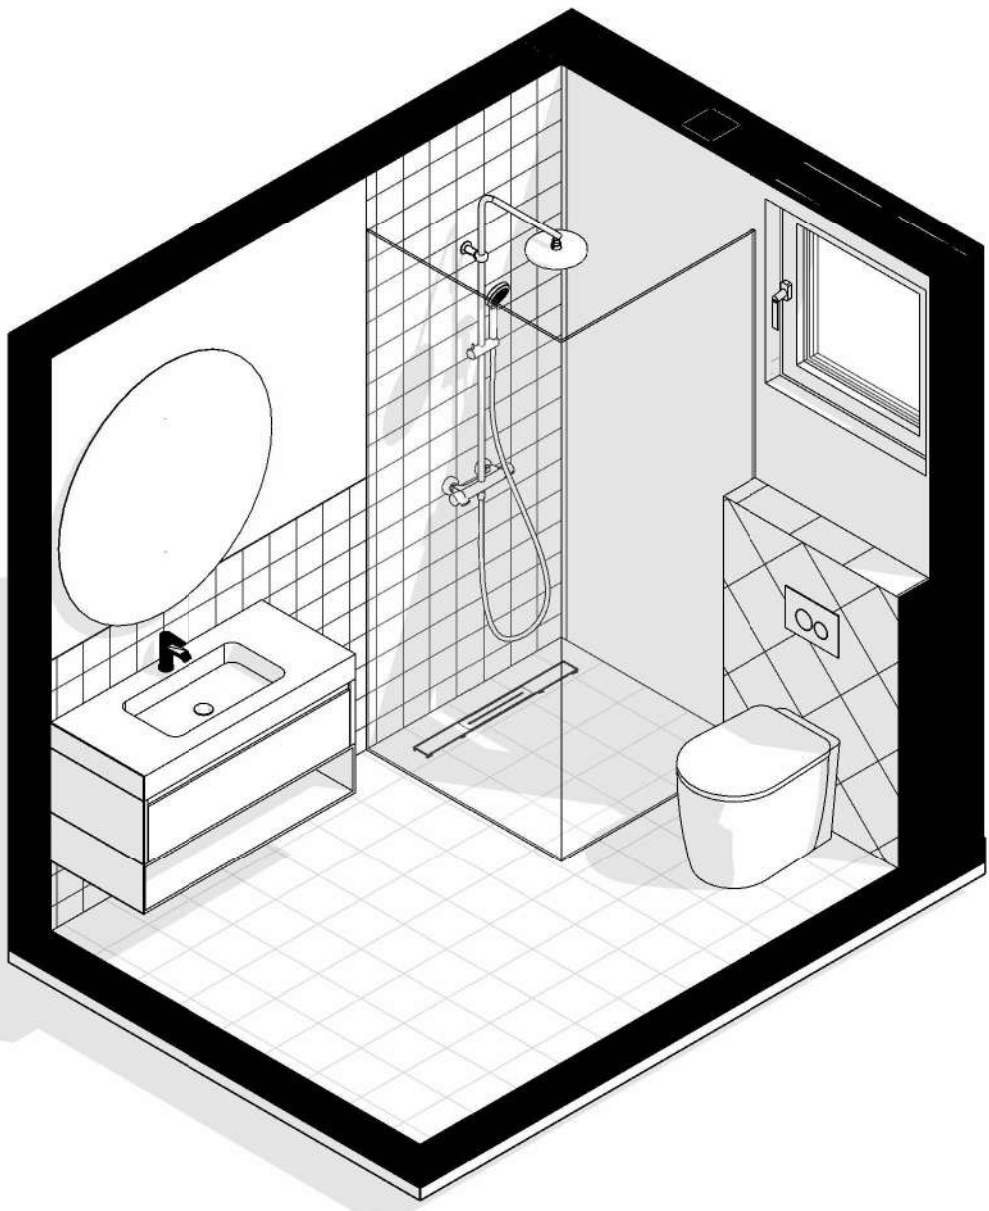

5 BATHROOM

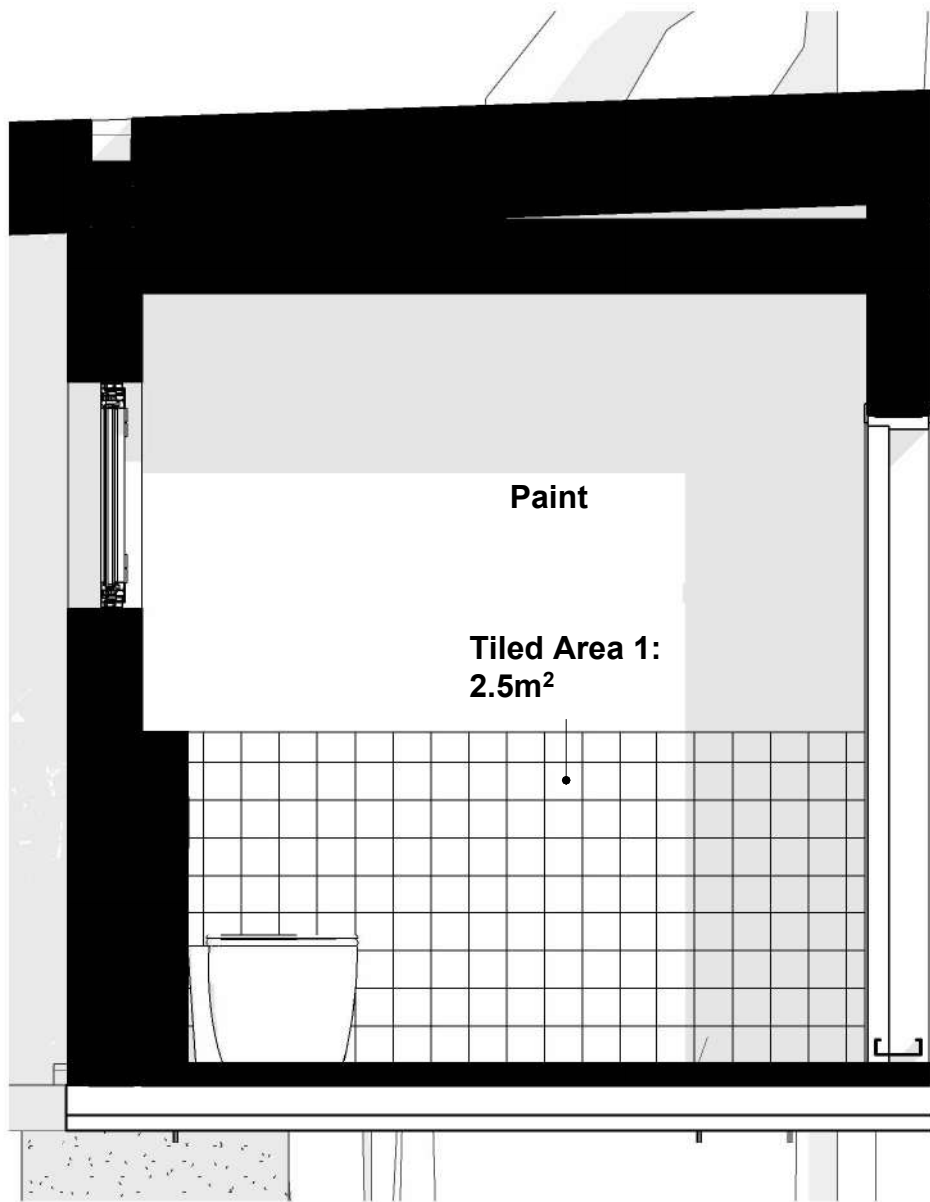

Tiled Area 1:
2.5m²

4 Section 10
1 : 25

Tiles

Bathroom Wall Tile 1

- One Wave Beige ON25R
- 34 x 91,5 cm . 13,4" x 36" / R20
- Color, Not Rectified
- White Body Wall Tiles, Mate



Tiled Area: 9.6m²

Bathroom Wall Tile 2

- One Beige ON28R
- 34 x 91,5 cm . 13,4" x 36" / R19
- Color, Not Rectified
- White Body Wall Tiles, Mate



Tiled Area: 1.4m²

1. THESE DRAWINGS MUST BE CHECKED BY THE CUSTOMER OR CONTRACTOR PRIOR TO APPROVAL. ANY ERRORS OR OMISSIONS MUST BE REPORTED IN WRITING TO BAUHU PRIOR TO COMMENCEMENT OF CONSTRUCTION.
2. ARCHITECTURAL DRAWINGS SHOULD BE READ IN CONJUNCTION WITH STRUCTURAL DETAILING AND FABRICATION GENERAL ASSEMBLY DRAWINGS.
3. FOR CONSTRUCTION PURPOSES, USE ONLY THE LATEST APPROVED DRAWINGS LABELED 'ISSUED FOR CONSTRUCTION'.
4. DO NOT SCALE FROM THIS DRAWING.
5. THE COMPANY OPERATES USING METRIC DIMENSIONS AS THE PRINCIPAL DENOMINATION.
6. ALL CONCRETE WORKS ARE OUTSIDE OF THE SCOPE OF THE COMPANY. INFORMATION REGARDING SLAB DESIGN AND CONNECTIONS IN THESE DRAWINGS ARE INTENDED FOR GUIDENCE ONLY. FOUNDATION AND SLAB WORKS SHOULD BE DESIGNED AND APPROVED BY A LOCAL STRUCTURAL ENGINEER.
7. THE COMPANY RETAINS FULL TITLE AND OWNERSHIP OF THESE PLANS AND DESIGNS. ANY UNAUTHORISED USE, REPRODUCTION, OR DISTRIBUTION OF THESE PLANS, WHETHER IN WHOLE OR PART, IS EXPRESSLY PROHIBITED WITHOUT PRIOR WRITTEN CONSENT.

No.	Revision	Date

ISSUED FOR:

Issued for information

Issued for client approval

Issued for fabrication

Issued for construction

Angel

DRAWING TITLE:

Building Dimensions

DRAWN BY:

Yonca A.Clark

SCALE:


1 : 50

DRAWING NO:

A137

DATE:

01/05/2024

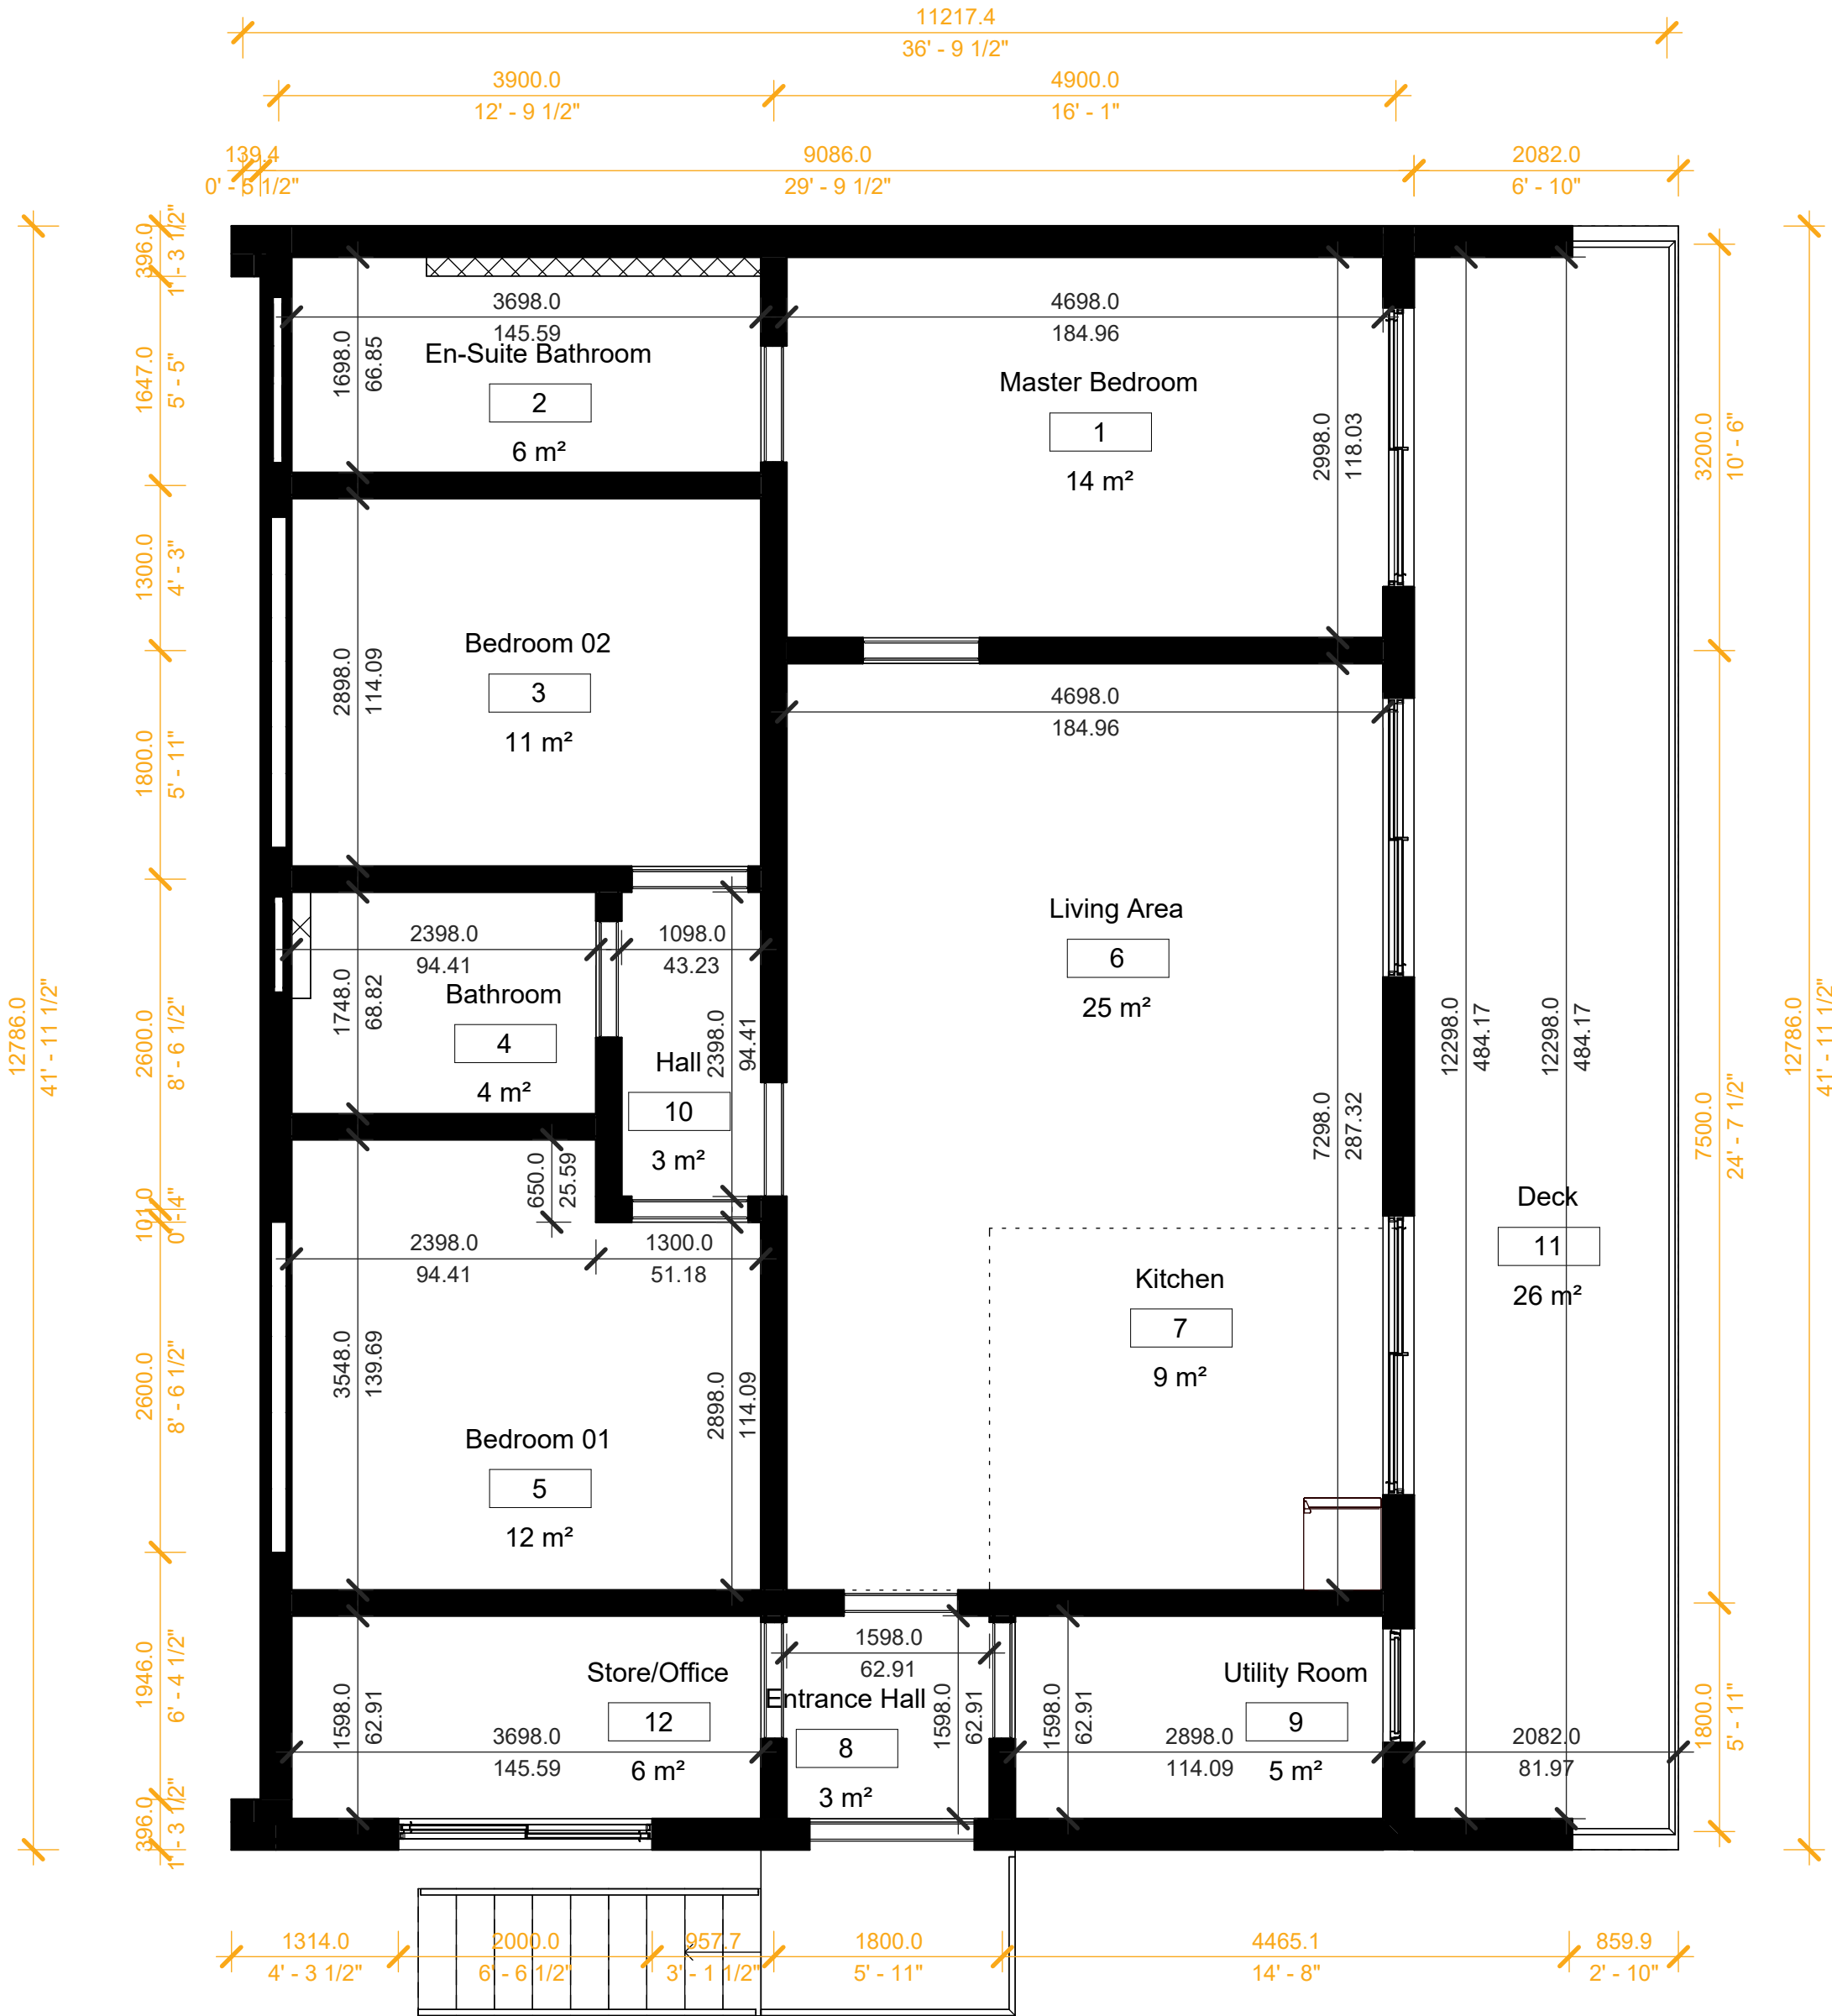

HRS CONNECTIONS

1. THESE DRAWINGS MUST BE CHECKED BY THE CUSTOMER OR CONTRACTOR PRIOR TO APPROVAL. ANY ERRORS OR OMISSIONS MUST BE REPORTED IN WRITING TO BAUHU PRIOR TO COMMENCEMENT OF CONSTRUCTION.
2. ARCHITECTURAL DRAWINGS SHOULD BE READ IN CONJUNCTION WITH STRUCTURAL DETAILING AND FABRICATION GENERAL ASSEMBLY DRAWINGS.
3. FOR CONSTRUCTION PURPOSES, USE ONLY THE LATEST APPROVED DRAWINGS LABELED 'ISSUED FOR CONSTRUCTION'.
4. DO NOT SCALE FROM THIS DRAWING.
5. THE COMPANY OPERATES USING METRIC DIMENSIONS AS THE PRINCIPAL DENOMINATION.
6. ALL CONCRETE WORKS ARE OUTSIDE OF THE SCOPE OF THE COMPANY. INFORMATION REGARDING SLAB DESIGN AND CONNECTIONS IN THESE DRAWINGS ARE INTENDED FOR GUIDANCE ONLY. FOUNDATION AND SLAB WORKS SHOULD BE DESIGNED AND APPROVED BY A LOCAL STRUCTURAL ENGINEER.
7. THE COMPANY RETAINS FULL TITLE AND OWNERSHIP OF THESE PLANS AND DESIGNS. ANY UNAUTHORISED USE, REPRODUCTION, OR DISTRIBUTION OF THESE PLANS, WHETHER IN WHOLE OR PART, IS EXPRESSLY PROHIBITED WITHOUT PRIOR WRITTEN CONSENT.

No.	Revision	Date

ISSUED FOR:


Issued for information

Issued for client approval


Issued for fabrication

Issued for construction


DRAWING TITLE:
HRS Connections 3D
DRAWN BY:
Yonca A.Clark
SCALE:
DRAWING NO:
A138
DATE:
01/05/2024

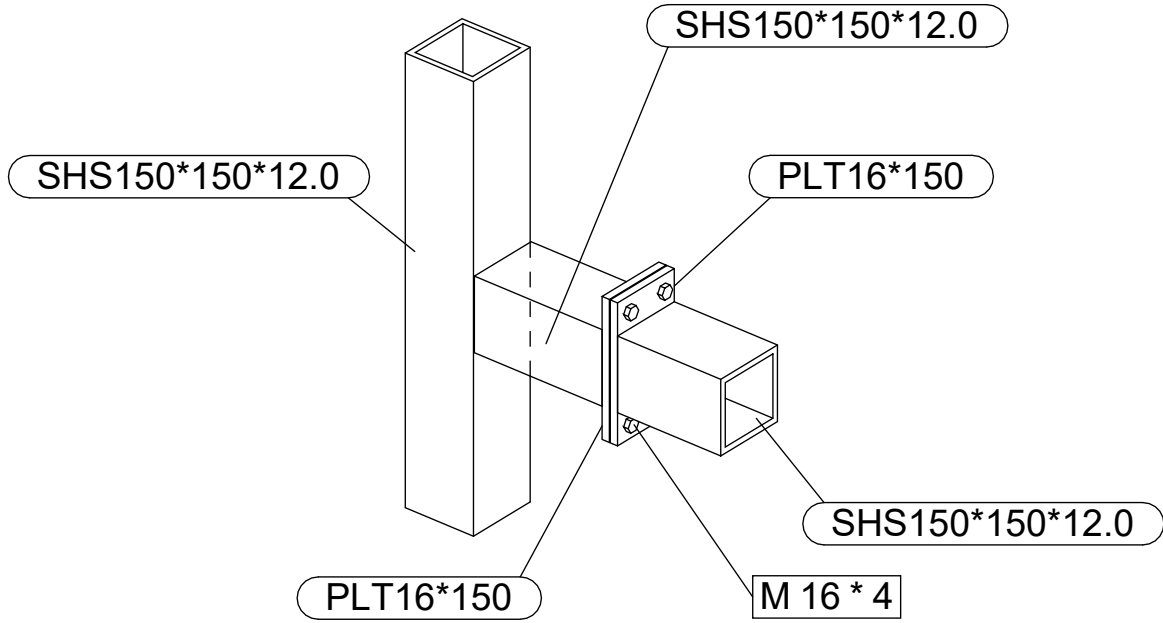


Typical Column Beam Stub Connection

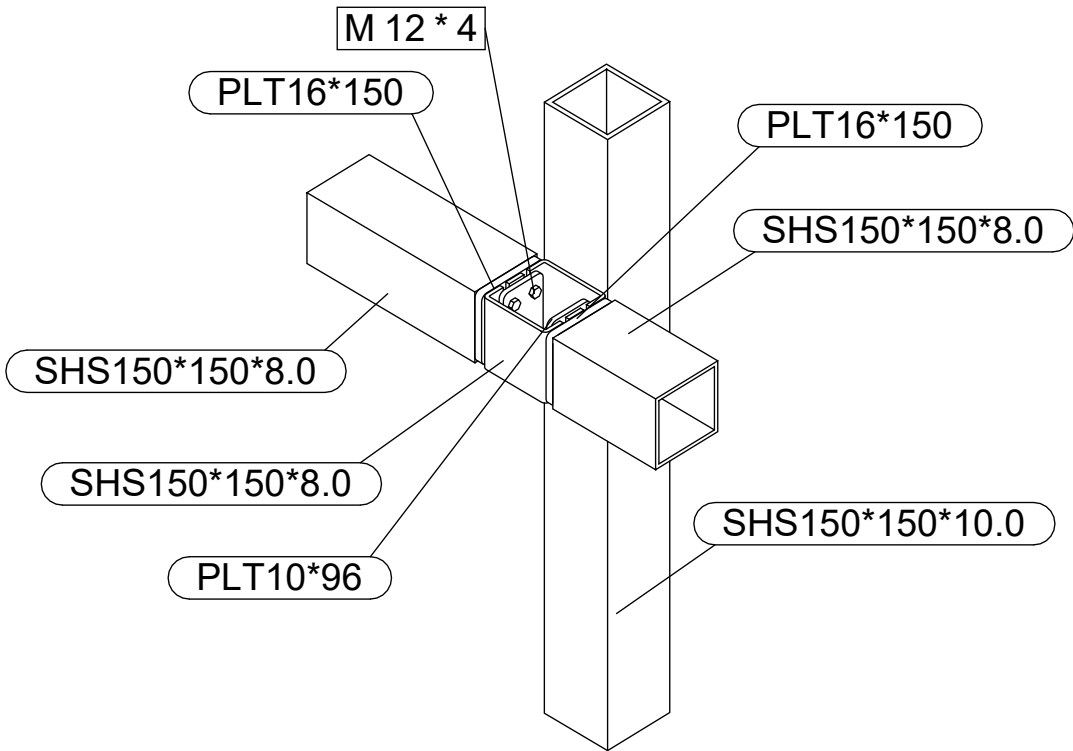


Typical Beam Offset Connection

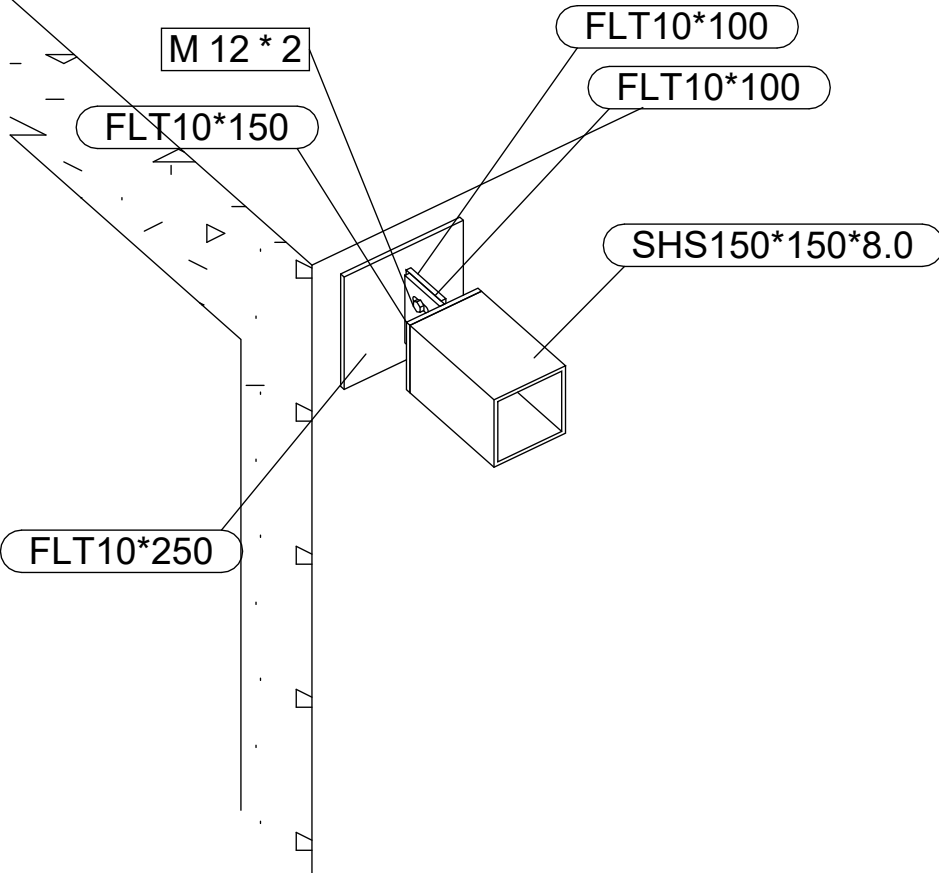


Typical Beam to Concrete Connection

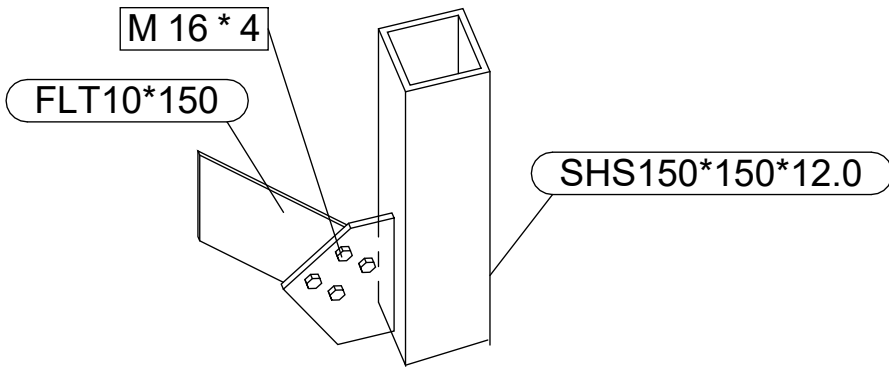


Typical Bracing Connection

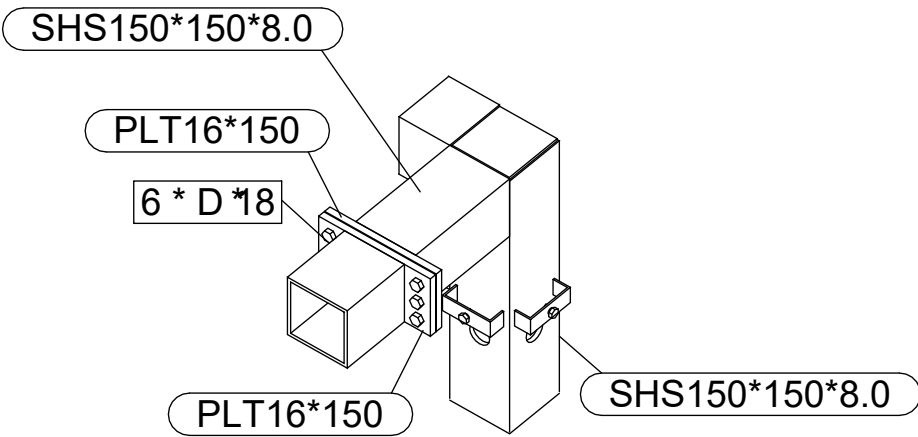


Typical Column to Beam Splice Connection

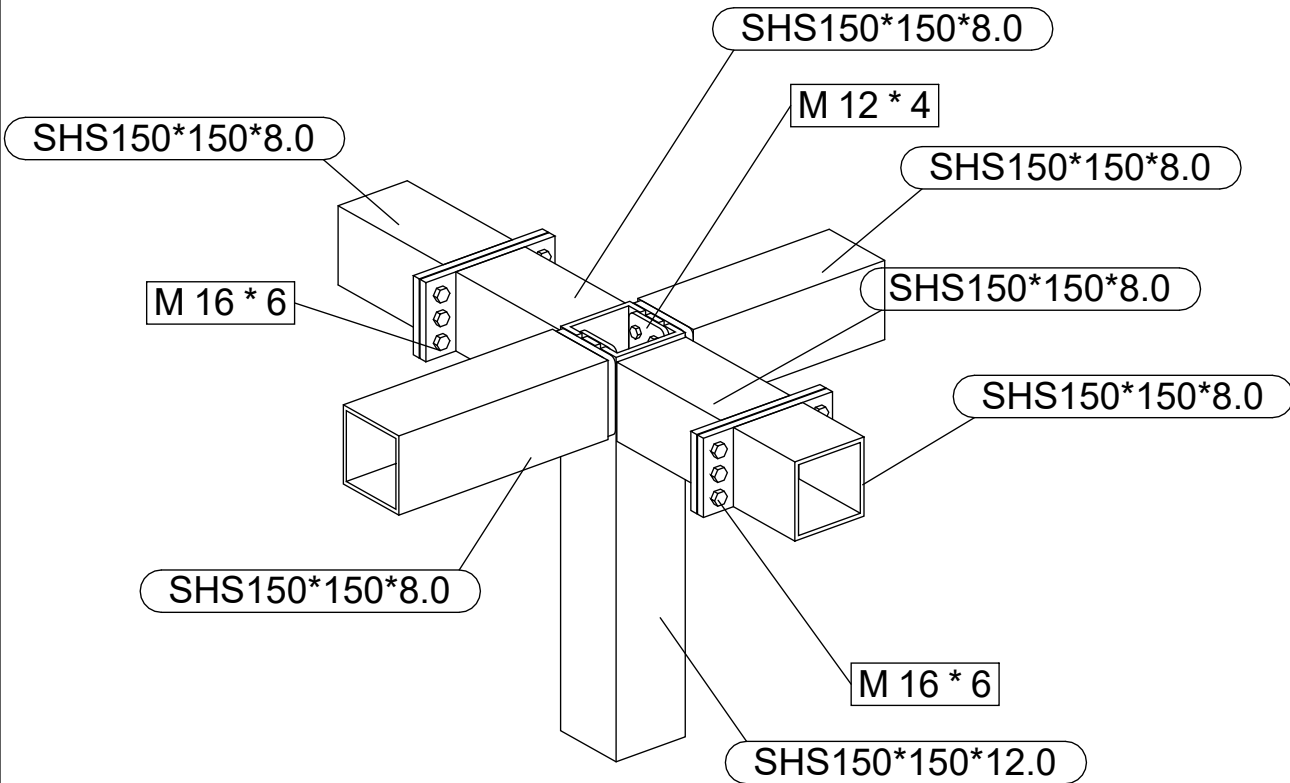

Typical Roof Column Beam Connection


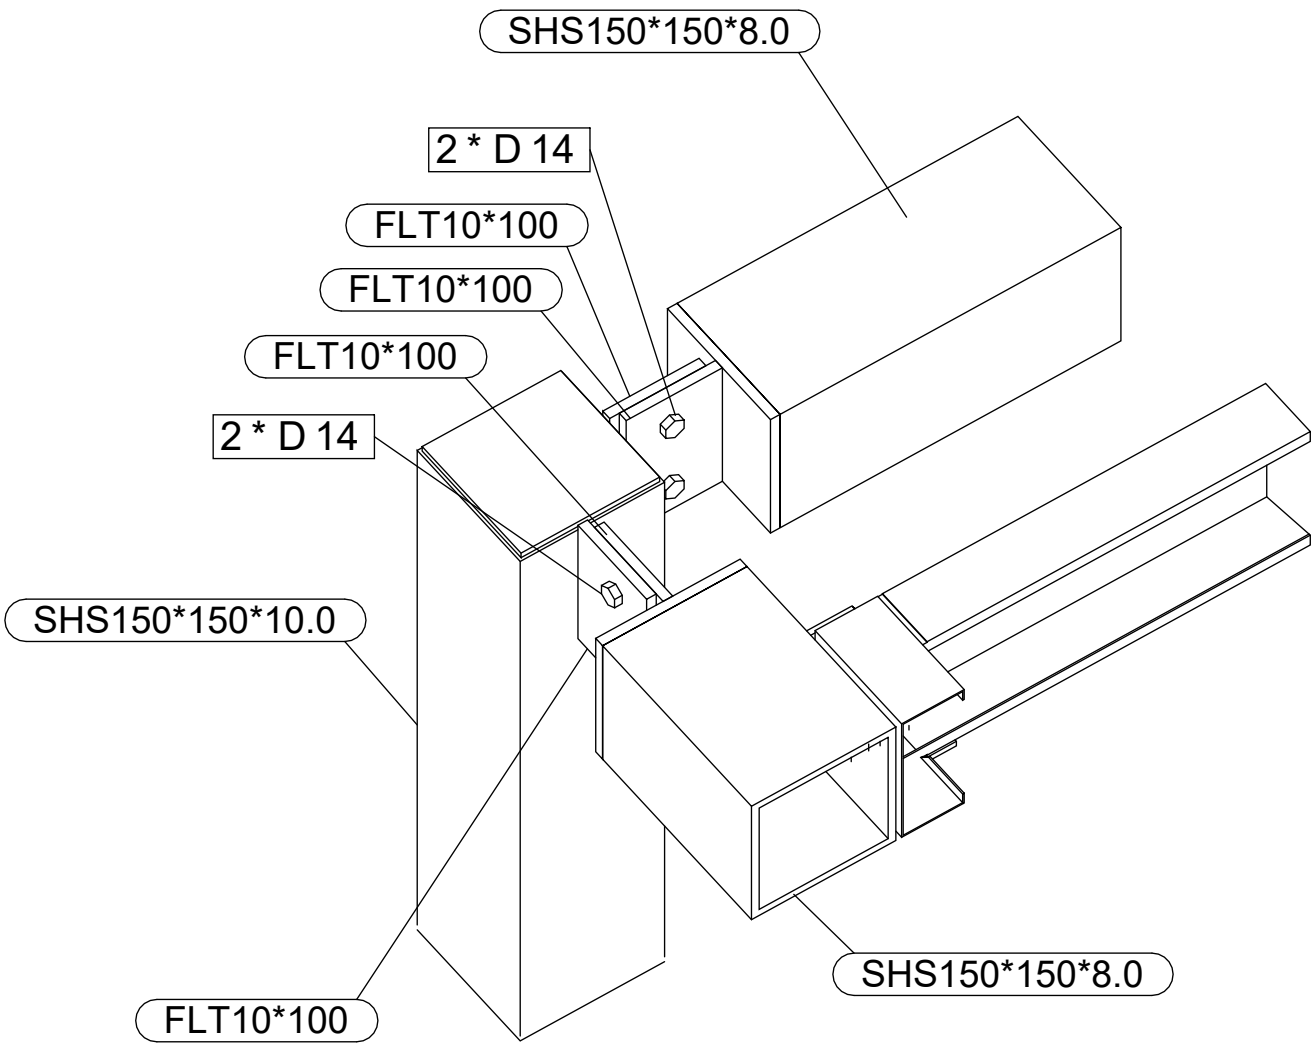


Typical Column to Beam Fine Plate Connection


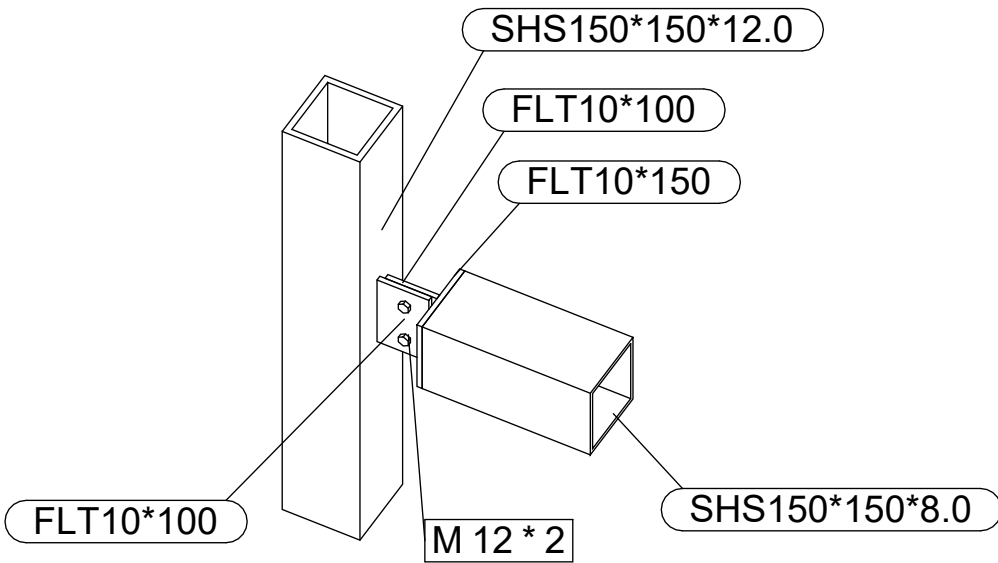


Typical Column Beam Fine Plate Connection

LGS CONNECTIONS

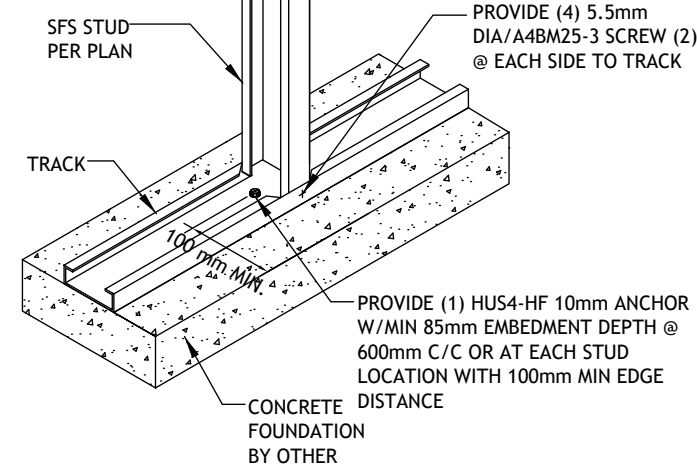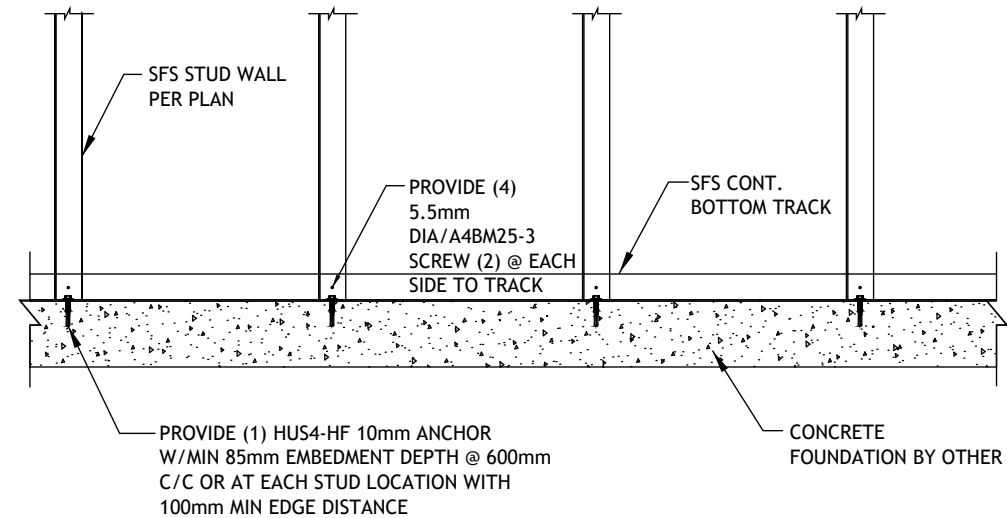

ENLARGE ISO SKETCH

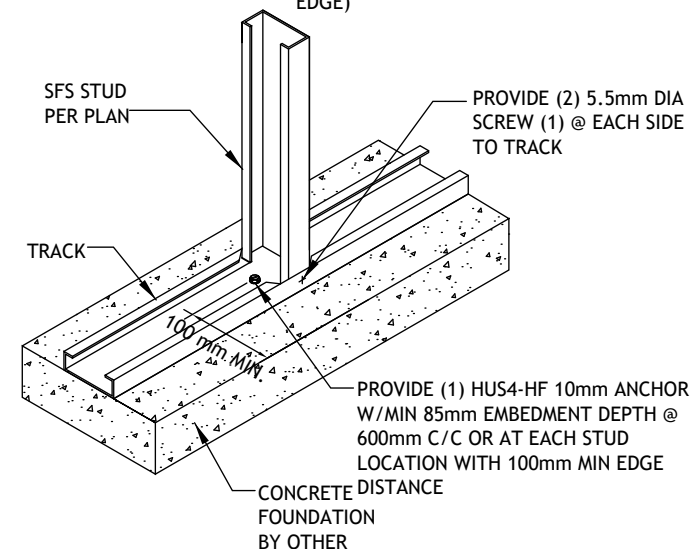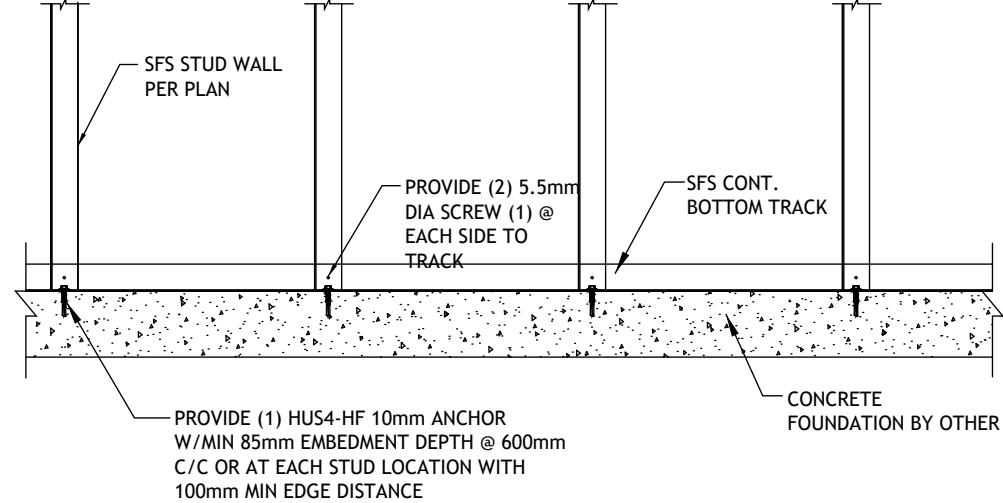


ENLARGE ISO SKETCH


1. THESE DRAWINGS MUST BE CHECKED BY THE CUSTOMER OR CONTRACTOR PRIOR TO APPROVAL. ANY ERRORS OR OMISSIONS MUST BE REPORTED IN WRITING TO BAUHU PRIOR TO COMMENCEMENT OF CONSTRUCTION.
2. ARCHITECTURAL DRAWINGS SHOULD BE READ IN CONJUNCTION WITH STRUCTURAL DETAILING AND FABRICATION GENERAL ASSEMBLY DRAWINGS.
3. FOR CONSTRUCTION PURPOSES, USE ONLY THE LATEST APPROVED DRAWINGS LABELED 'ISSUED FOR CONSTRUCTION'.
4. DO NOT SCALE FROM THIS DRAWING.
5. THE COMPANY OPERATES USING METRIC DIMENSIONS AS THE PRINCIPAL DENOMINATION.
6. ALL CONCRETE WORKS ARE OUTSIDE OF THE SCOPE OF THE COMPANY. INFORMATION REGARDING SLAB DESIGN AND CONNECTIONS IN THESE DRAWINGS ARE INTENDED FOR GUIDENCE ONLY. FOUNDATION AND SLAB WORKS SHOULD BE DESIGNED AND APPROVED BY A LOCAL STRUCTURAL ENGINEER.
7. THE COMPANY RETAINS FULL TITLE AND OWNERSHIP OF THESE PLANS AND DESIGNS. ANY UNAUTHORISED USE, REPRODUCTION, OR DISTRIBUTION OF THESE PLANS, WHETHER IN WHOLE OR PART, IS EXPRESSLY PROHIBITED WITHOUT PRIOR WRITTEN CONSENT.

Typical Detail : SFS Bottom Track to Concerete Connection (External Wall)


Typical Detail : Bottom Track to Concerrete Connection (Internal Wall)

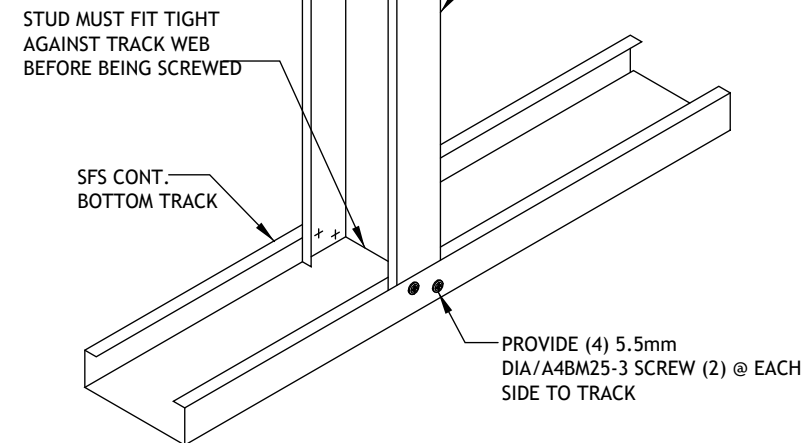


Stud to Bottom Track Connection (External Wall)

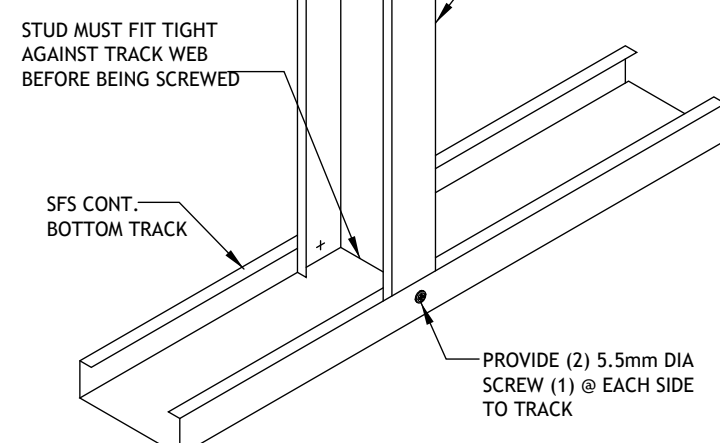


Stud to Bottom Track Connection (Internal Wall)

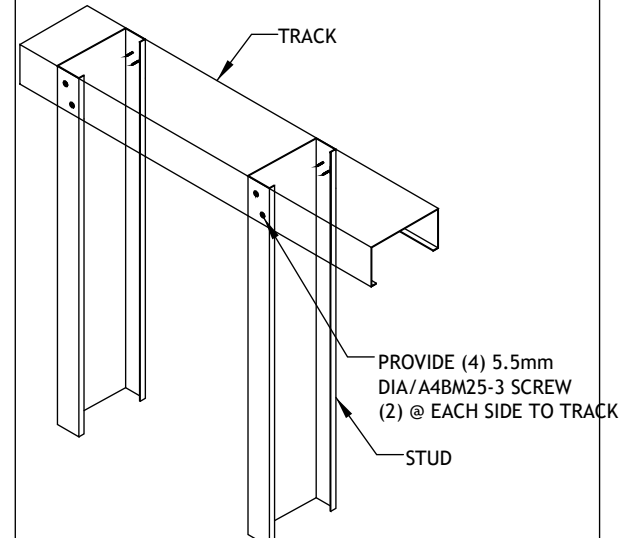

Stud to Top Track Connection (External Wall)

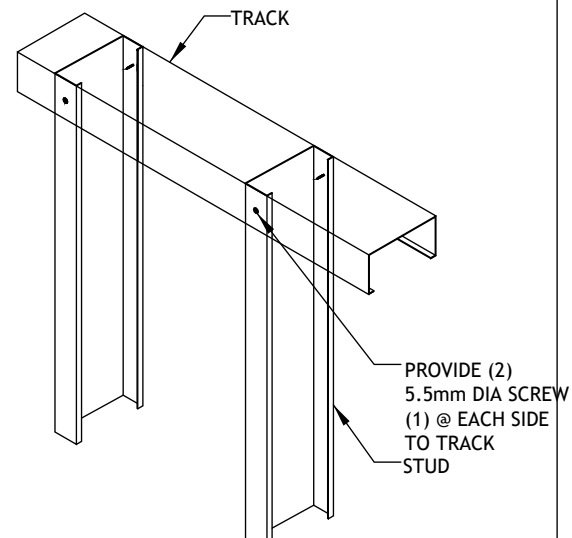

Stud to Top Track Connection (Internal Wall)

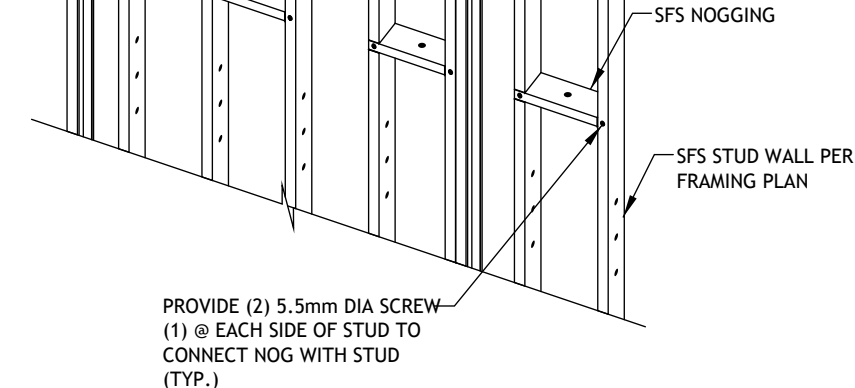

Hit and Miss Nogging to Stud Connection Detail

[illegible]

ISSUED FOR:

Issued for information

Issued for client approval

Issued for fabrication

Issued for construction

Angel

DRAWING TITLE:

LGS Connections 3D

DRAWN BY:

Yonca A.Clark


SCALE:

DRAWING NO:


A139

DATE:


01/05/2024

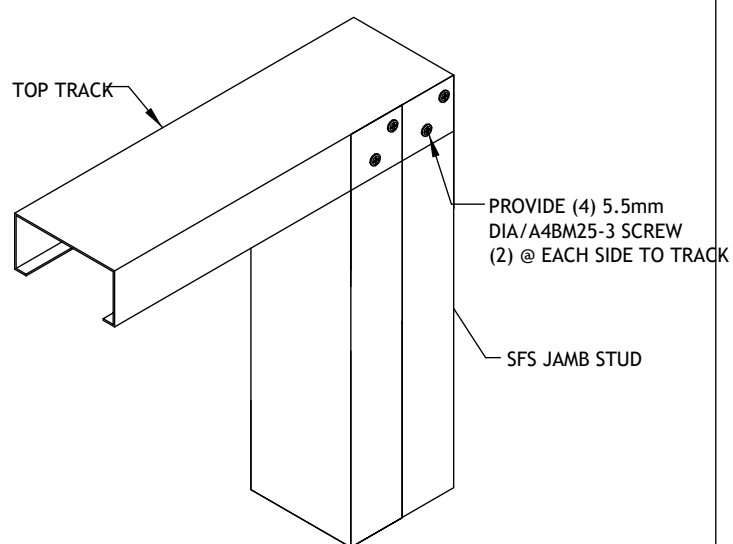


Box Jamb to Top Track Connection

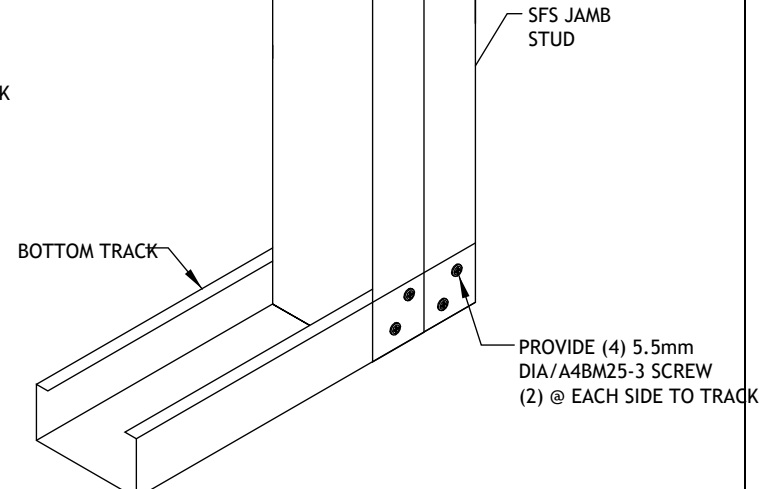


Box Jamb to Bottom Track Connection

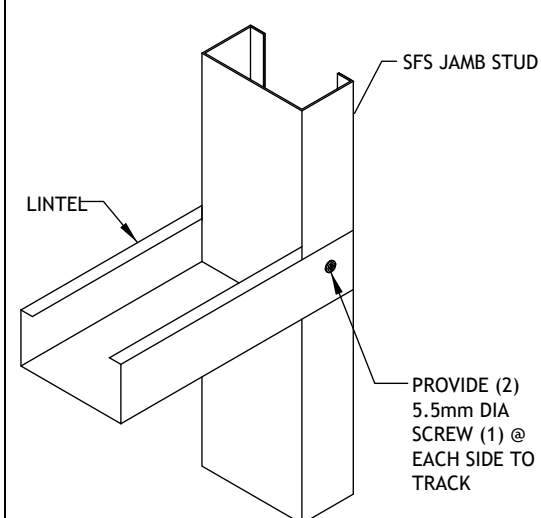


Lintel to Jamb Stud Connection

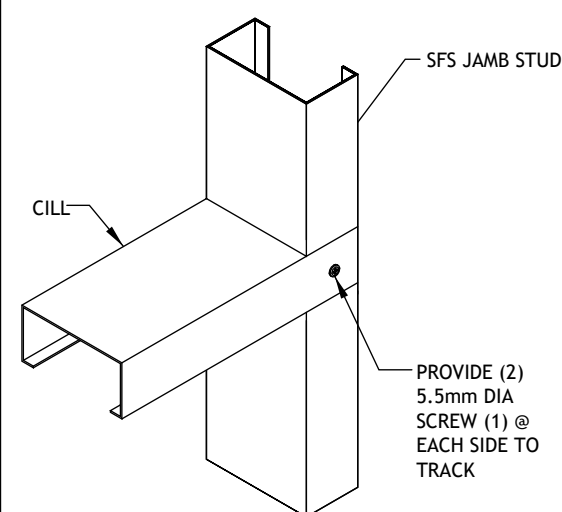

Typ. Cill to Jamb Stud Connection

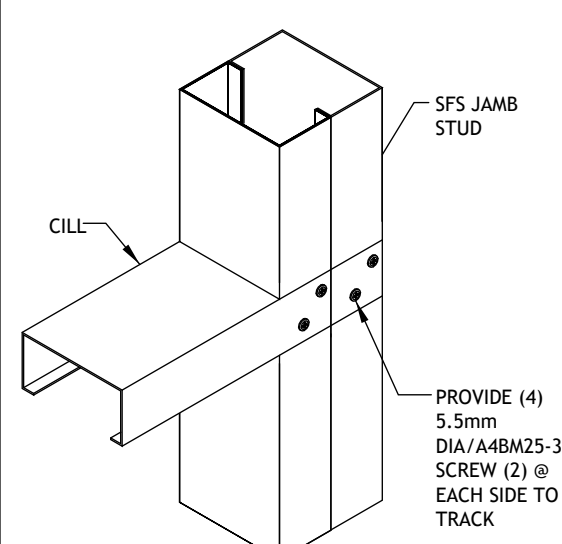


Typ. Cill to Jamb Stud Connection

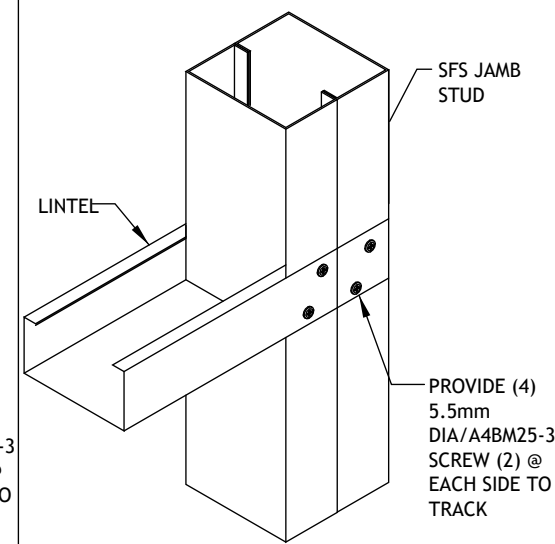


Lintel to Jamb Stud Connection

Typical Frame Connections 1


1. THESE DRAWINGS MUST BE CHECKED BY THE CUSTOMER OR CONTRACTOR PRIOR TO APPROVAL. ANY ERRORS OR OMISSIONS MUST BE REPORTED IN WRITING TO BAUHU PRIOR TO COMMENCEMENT OF CONSTRUCTION.
2. ARCHITECTURAL DRAWINGS SHOULD BE READ IN CONJUNCTION WITH STRUCTURAL DETAILING AND FABRICATION GENERAL ASSEMBLY DRAWINGS.
3. FOR CONSTRUCTION PURPOSES, USE ONLY THE LATEST APPROVED DRAWINGS LABELED 'ISSUED FOR CONSTRUCTION'.
4. DO NOT SCALE FROM THIS DRAWING.
5. THE COMPANY OPERATES USING METRIC DIMENSIONS AS THE PRINCIPAL DENOMINATION.
6. ALL CONCRETE WORKS ARE OUTSIDE OF THE SCOPE OF THE COMPANY. INFORMATION REGARDING SLAB DESIGN AND CONNECTIONS IN THESE DRAWINGS ARE INTENDED FOR GUIDENCE ONLY. FOUNDATION AND SLAB WORKS SHOULD BE DESIGNED AND APPROVED BY A LOCAL STRUCTURAL ENGINEER.
7. THE COMPANY RETAINS FULL TITLE AND OWNERSHIP OF THESE PLANS AND DESIGNS. ANY UNAUTHORISED USE, REPRODUCTION, OR DISTRIBUTION OF THESE PLANS, WHETHER IN WHOLE OR PART, IS EXPRESSLY PROHIBITED WITHOUT PRIOR WRITTEN CONSENT.

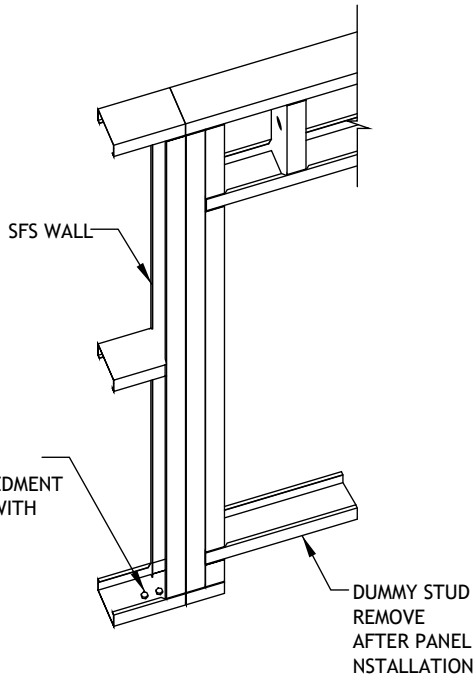


Typical Detail for Two Anchor at Jamb Location

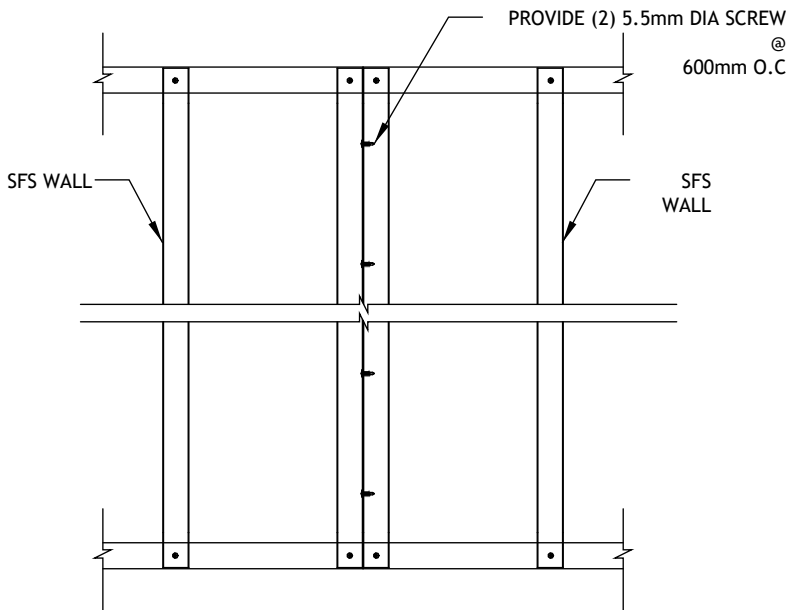


Typical Wall to SFS Wall Connection

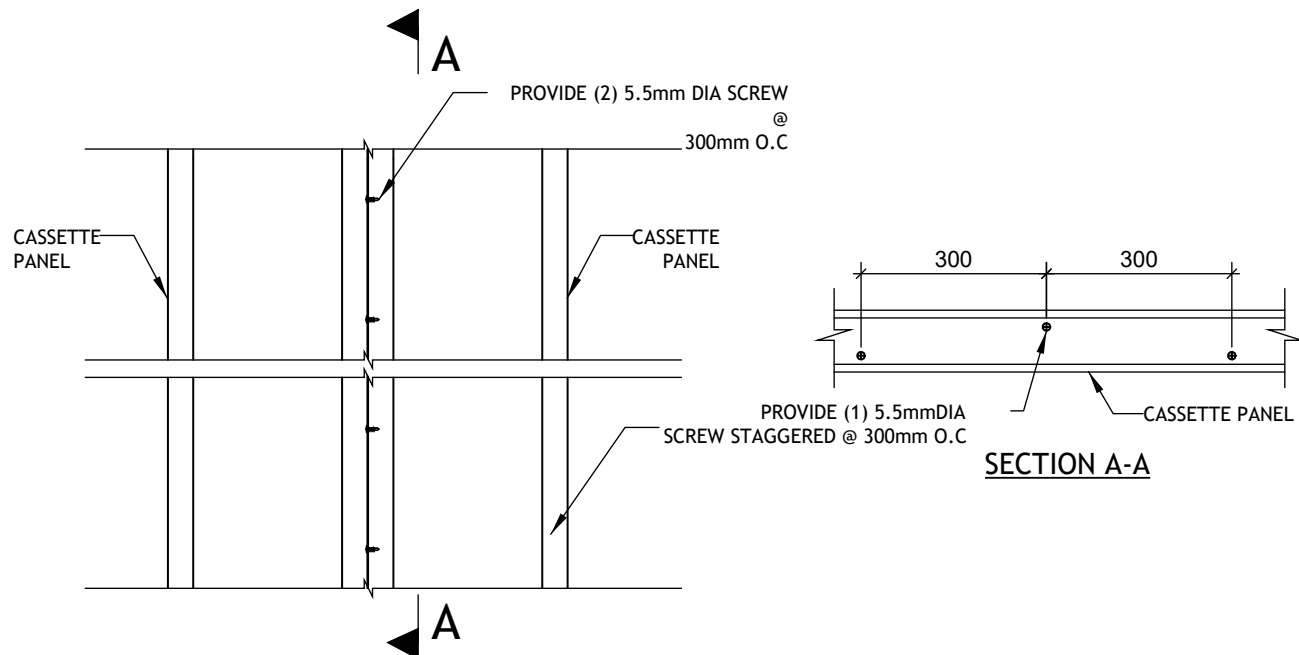


Cassette to Cassette Connection

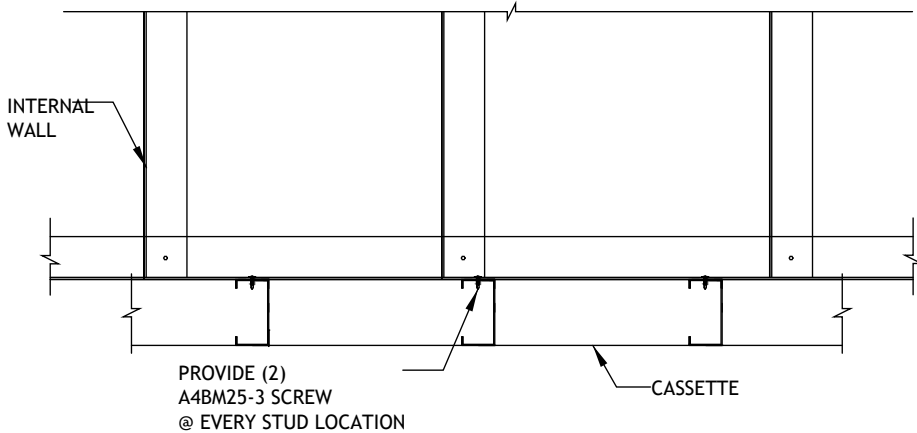


Internal Wall to Cassette Connection at Base

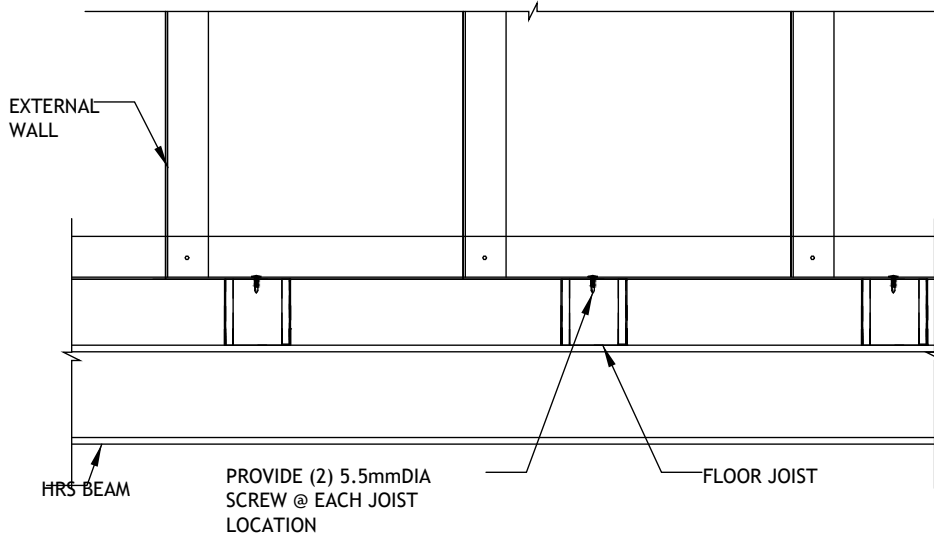


External Wall to Joist Connection at Base

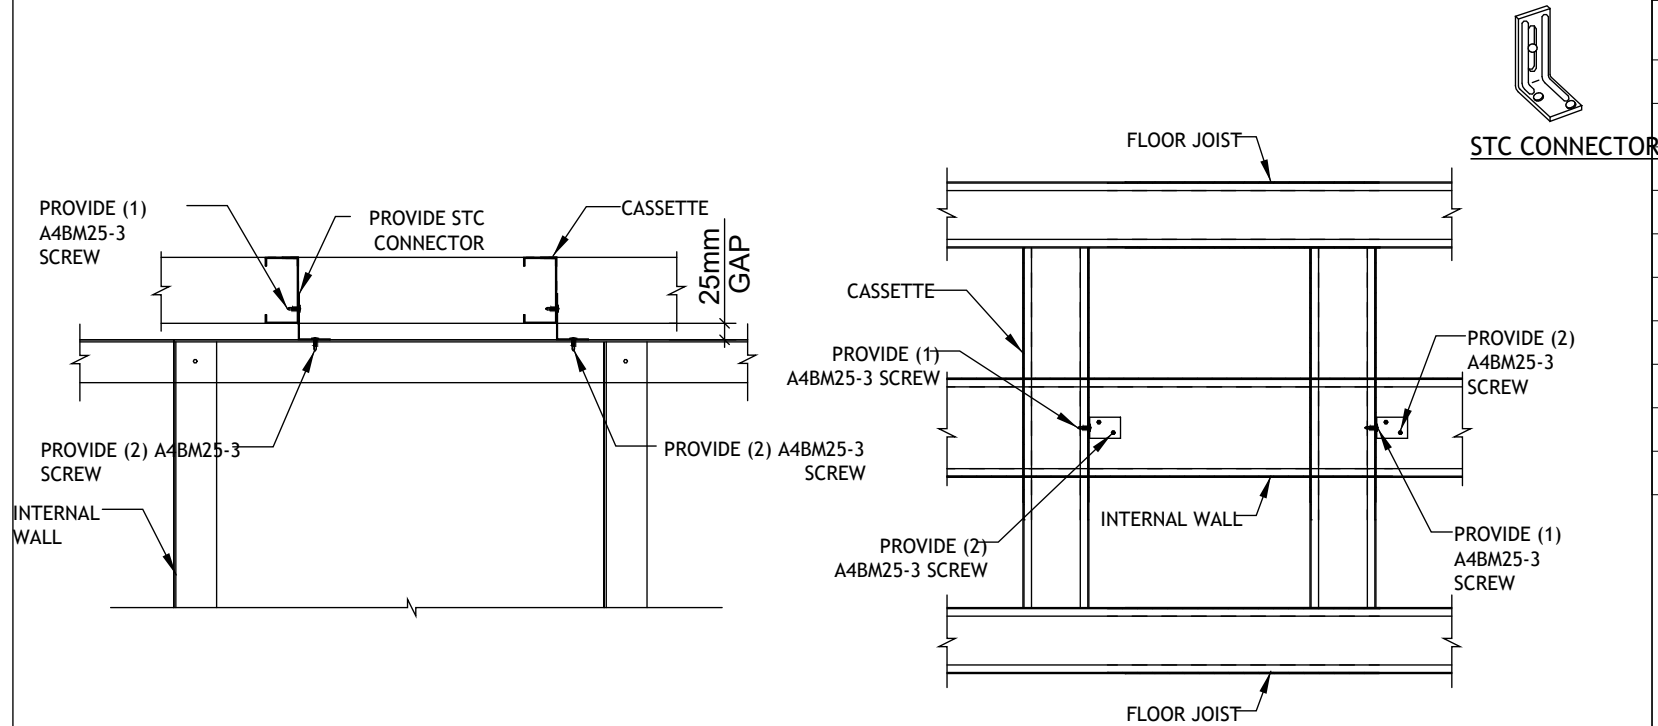


Typ. Internal Wall Connection at Roof Truss at Cassette Location

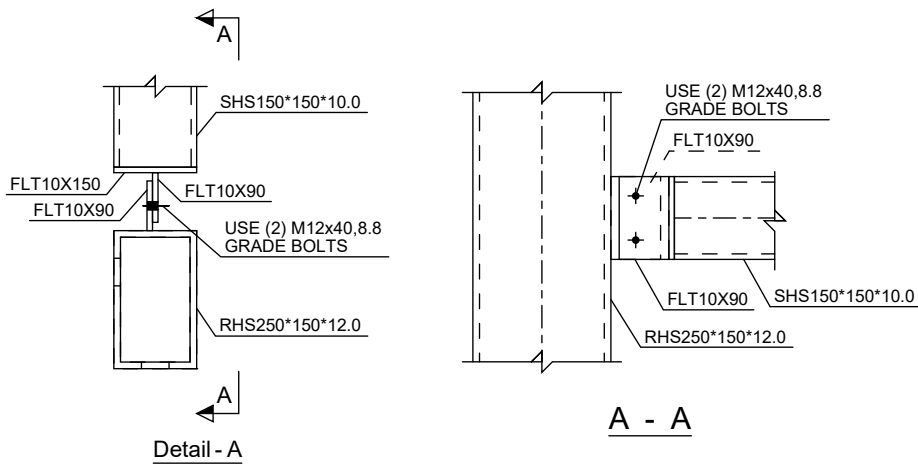

Typ. Fin Plate Connection Detail

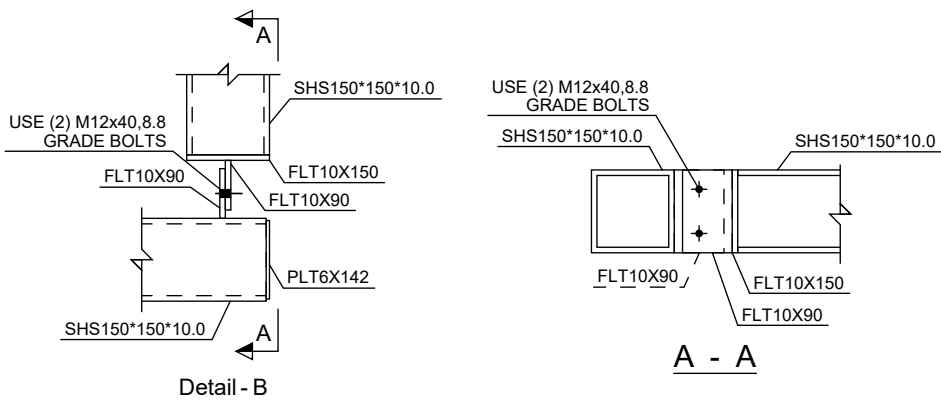

Typ. Fin Plate Connection Detail

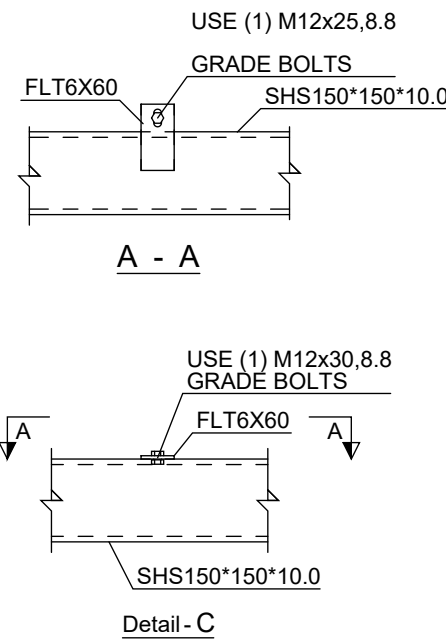

SFS Wall to HRS Beam Connection

No.	Revision	Date

ISSUED FOR:

Issued for information

Issued for client approval

Issued for fabrication

Issued for construction

Angel

DRAWING TITLE:
Typical Frame Connections 1


DRAWN BY:
Yonca A.Clark

SCALE:


DRAWING NO:
A140

DATE:
01/05/2024

Typical Frame Connections 2

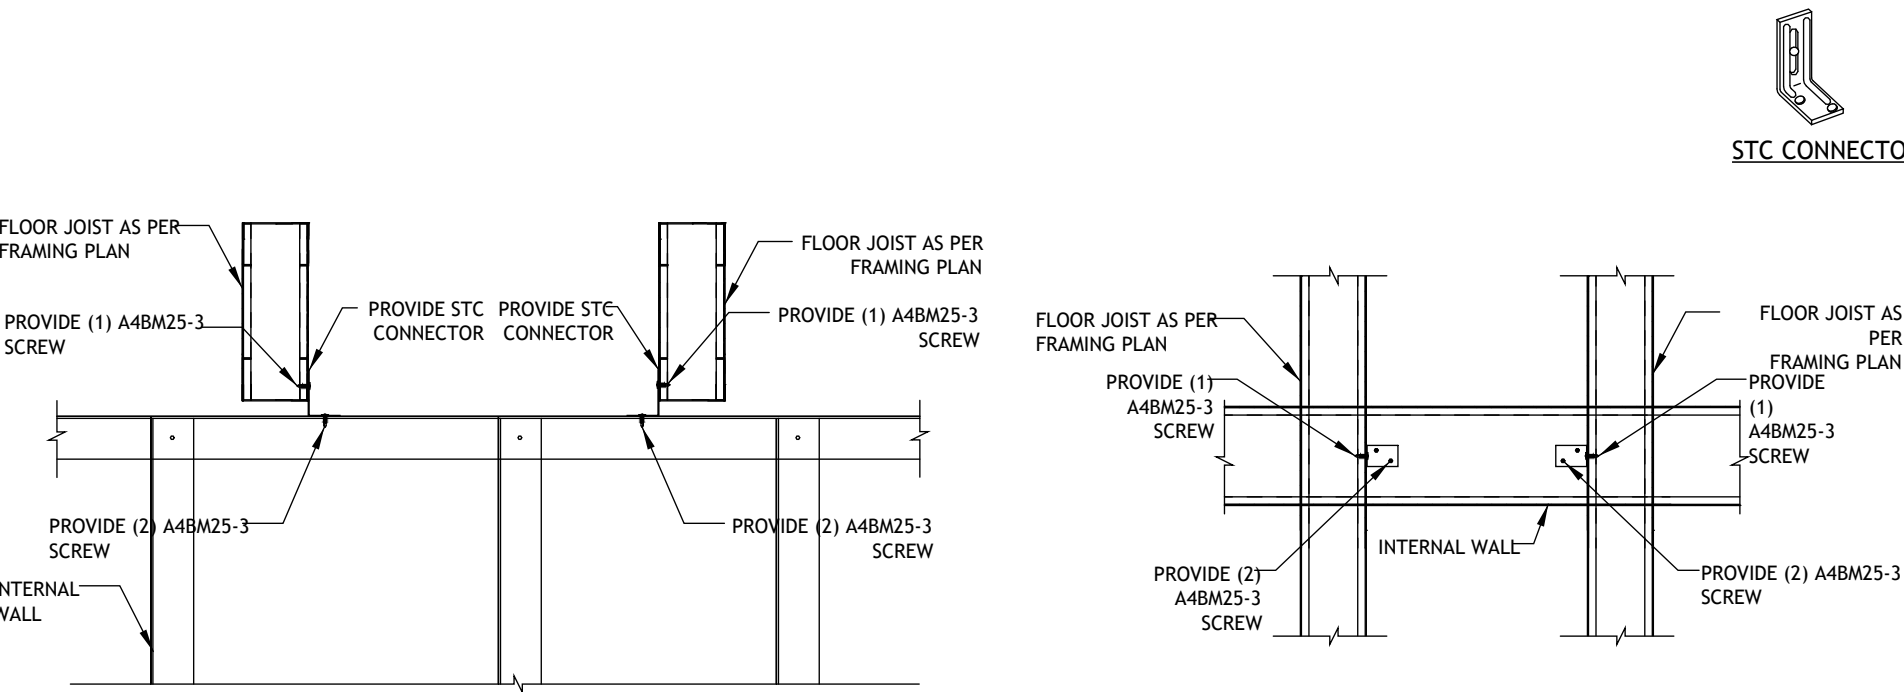


Typical Internal Wall Connection Floor Joist

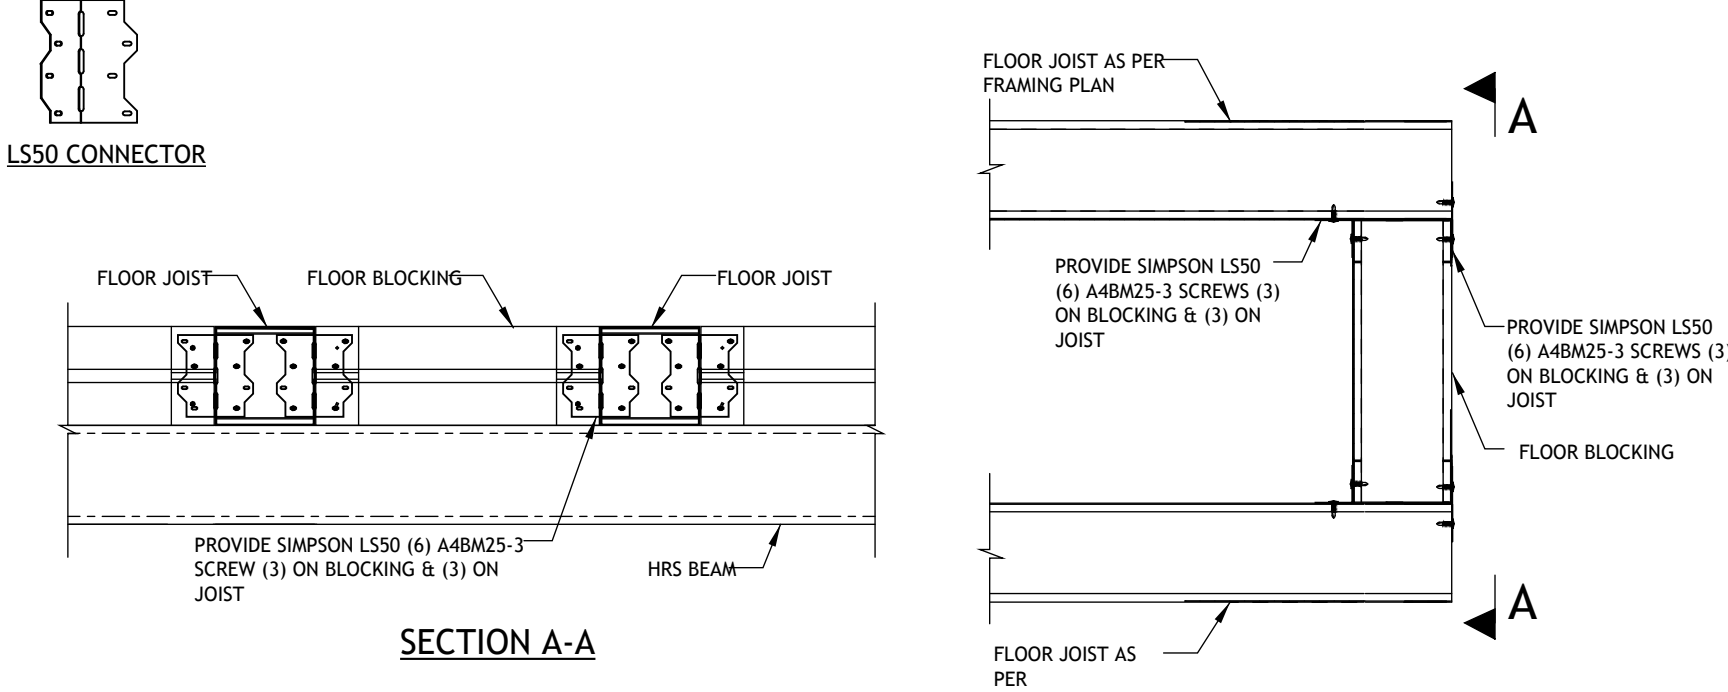


Floor Blocking to Floor Joist Connection

1. THESE DRAWINGS MUST BE CHECKED BY THE CUSTOMER OR CONTRACTOR PRIOR TO APPROVAL. ANY ERRORS OR OMISSIONS MUST BE REPORTED IN WRITING TO BAUHU PRIOR TO COMMENCEMENT OF CONSTRUCTION.
2. ARCHITECTURAL DRAWINGS SHOULD BE READ IN CONJUNCTION WITH STRUCTURAL DETAILING AND FABRICATION GENERAL ASSEMBLY DRAWINGS.
3. FOR CONSTRUCTION PURPOSES, USE ONLY THE LATEST APPROVED DRAWINGS LABELED 'ISSUED FOR CONSTRUCTION'.
4. DO NOT SCALE FROM THIS DRAWING.
5. THE COMPANY OPERATES USING METRIC DIMENSIONS AS THE PRINCIPAL DENOMINATION.
6. ALL CONCRETE WORKS ARE OUTSIDE OF THE SCOPE OF THE COMPANY. INFORMATION REGARDING SLAB DESIGN AND CONNECTIONS IN THESE DRAWINGS ARE INTENDED FOR GUIDANCE ONLY. FOUNDATION AND SLAB WORKS SHOULD BE DESIGNED AND APPROVED BY A LOCAL STRUCTURAL ENGINEER.
7. THE COMPANY RETAINS FULL TITLE AND OWNERSHIP OF THESE PLANS AND DESIGNS. ANY UNAUTHORISED USE, REPRODUCTION, OR DISTRIBUTION OF THESE PLANS, WHETHER IN WHOLE OR PART, IS EXPRESSLY PROHIBITED WITHOUT PRIOR WRITTEN CONSENT.

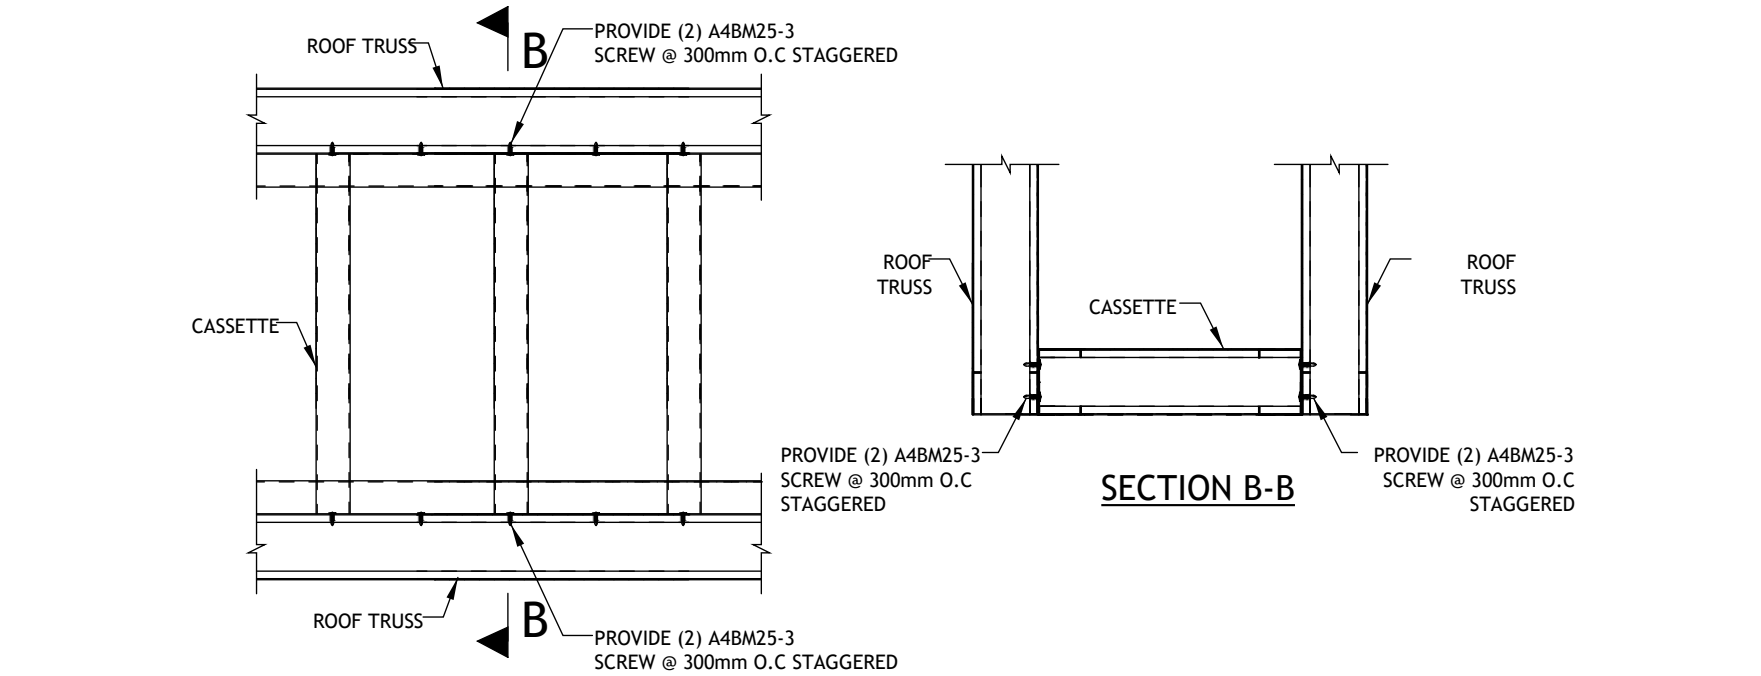

Cassette to Roof Trusses Connection

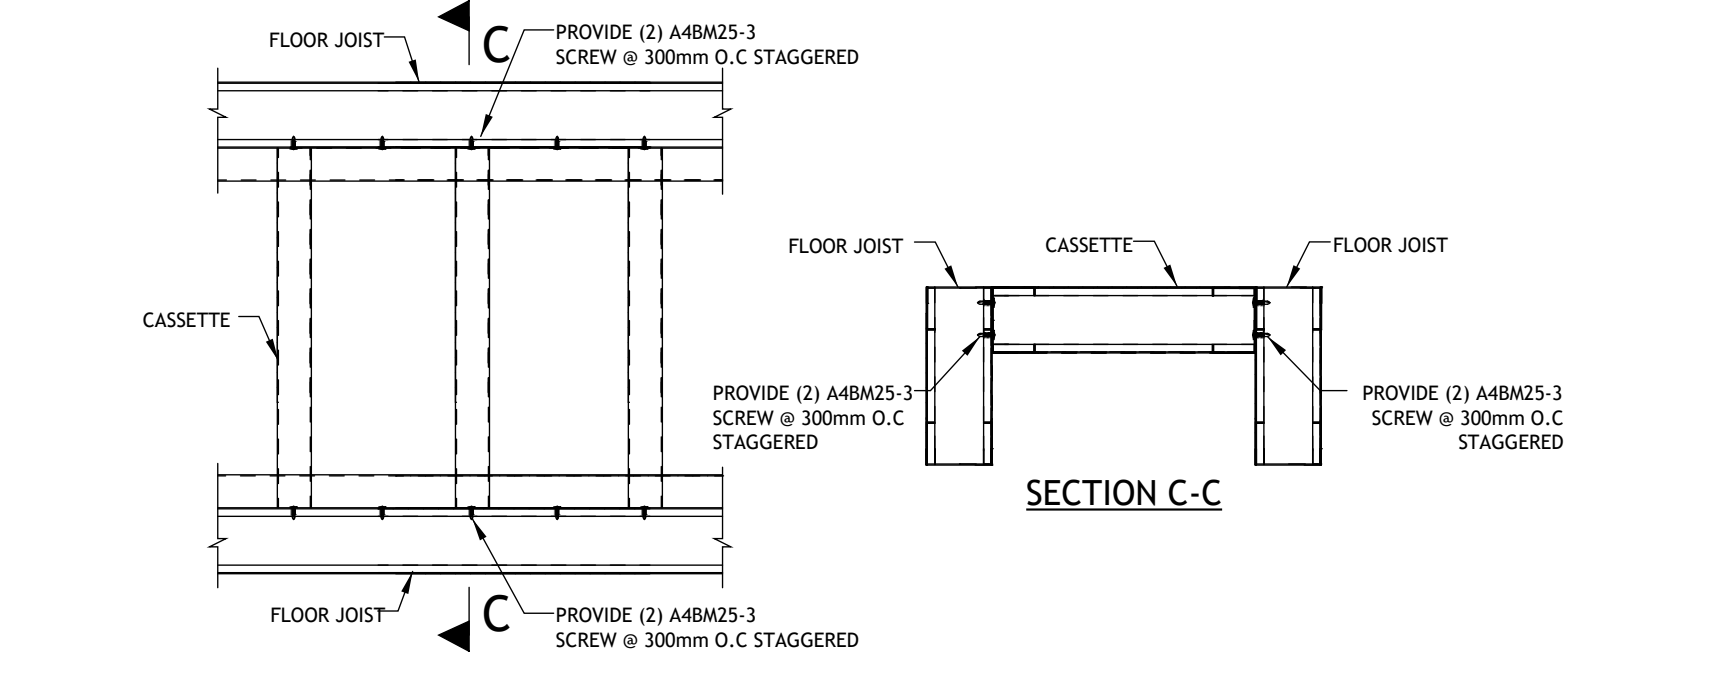

Cassette to Floor Joist Connection

No.	Revision	Date


ISSUED FOR:

Issued for information


Issued for client approval

Issued for fabrication

Issued for construction

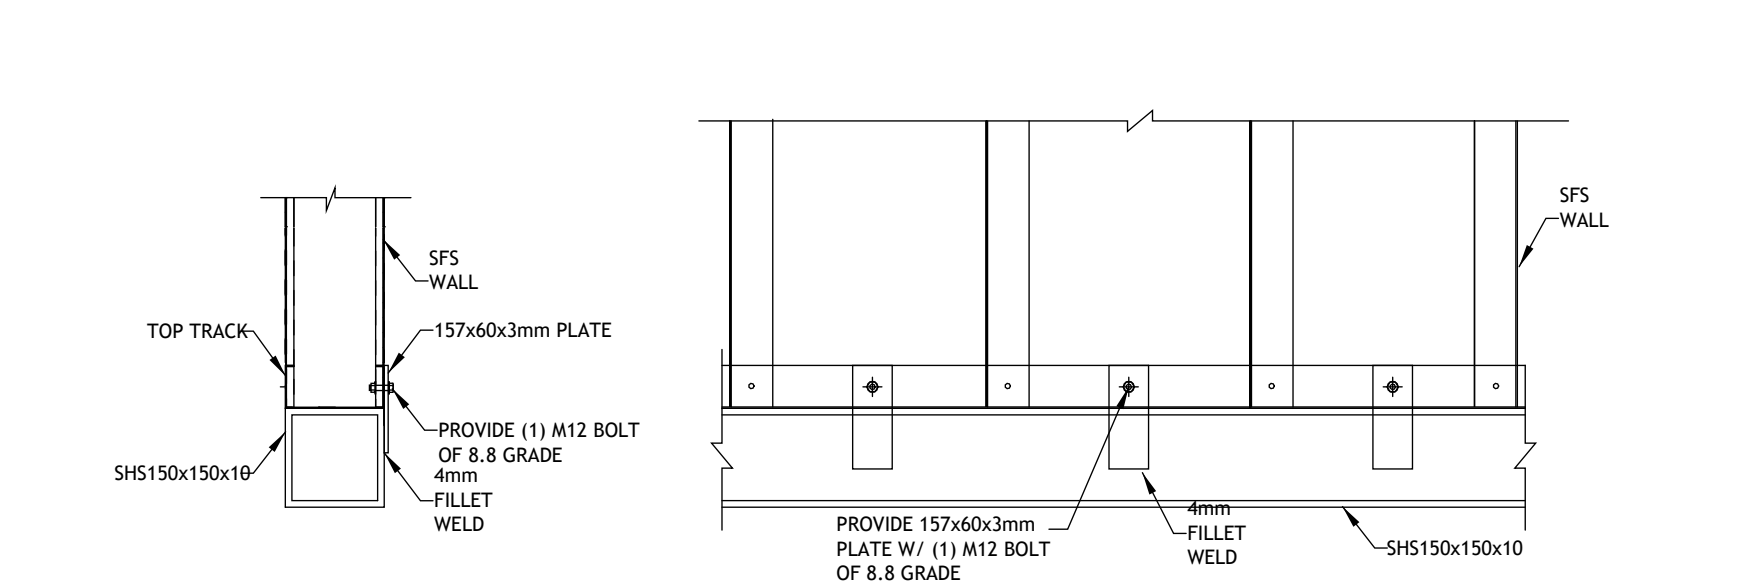

Typical Detail at SFS Bottom Track to HRS Beam Connection (External & Internal Wall)

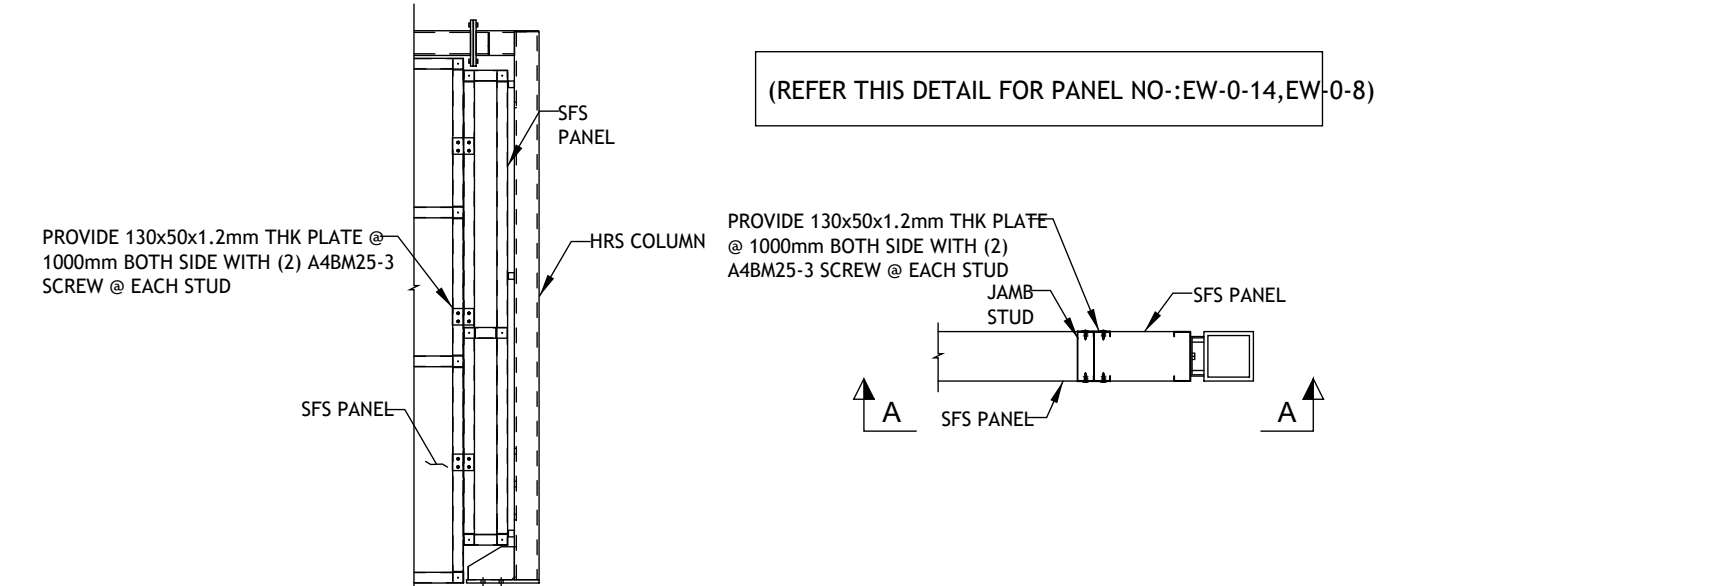

SFS Panel Connection Detail

Angel

DRAWING TITLE:
Typical Frame Connections 2

DRAWN BY:
Yonca A.Clark


SCALE:

DRAWING NO:
A141


DATE:
01/05/2024

Typical Frame Connections 3


NOTES:
ALL WELDS FOR CONNECTION OF ASSEMBLY TO BE NOTE FROM FABRICATION DRAWING

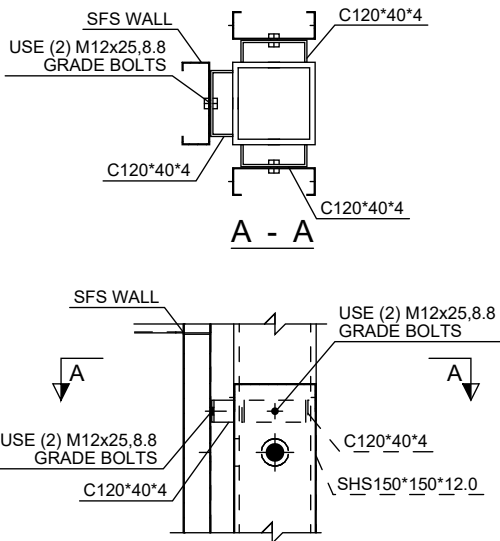


HRS Bracket Detail for Wall Connection

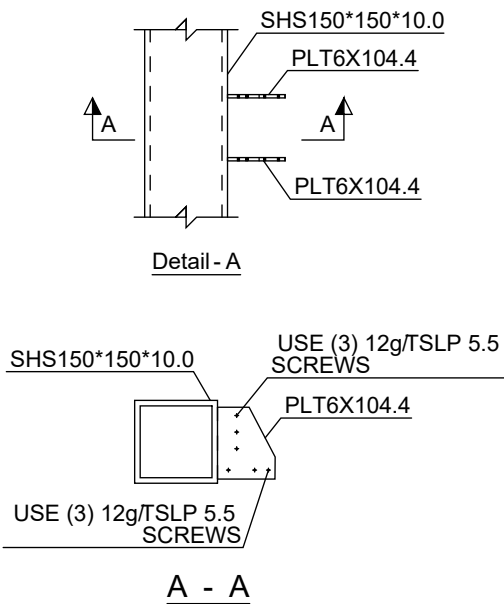


Typ. Truss Outside Plate Connection

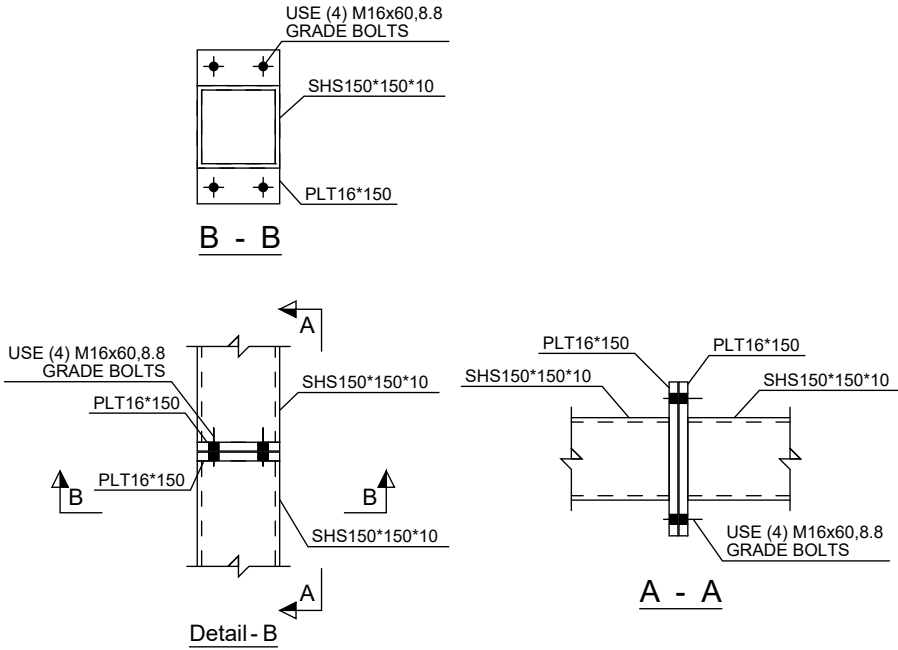


Typ. Vertical Splice Connection

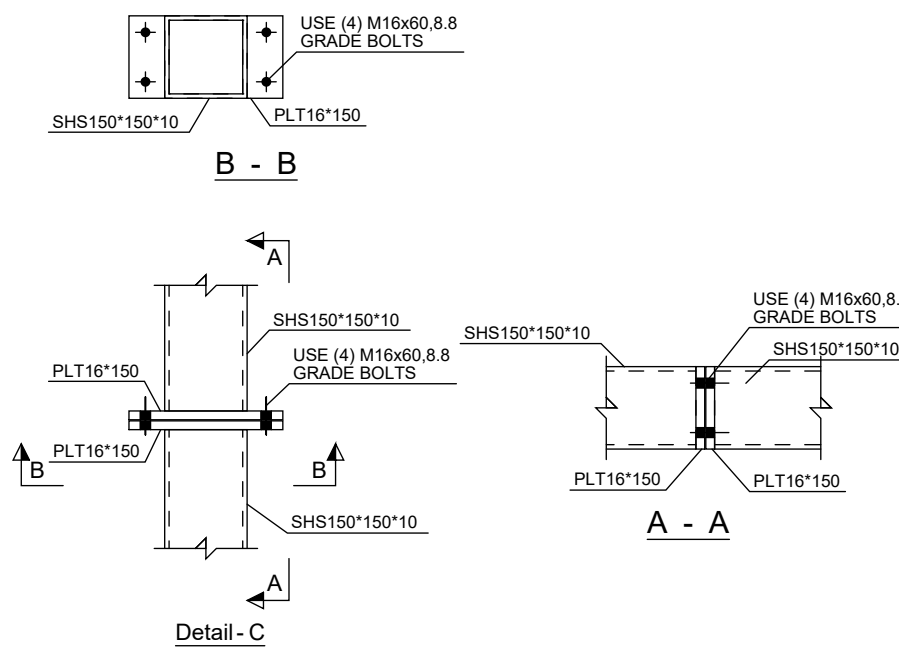


Typ. Horizontal Splice Connection

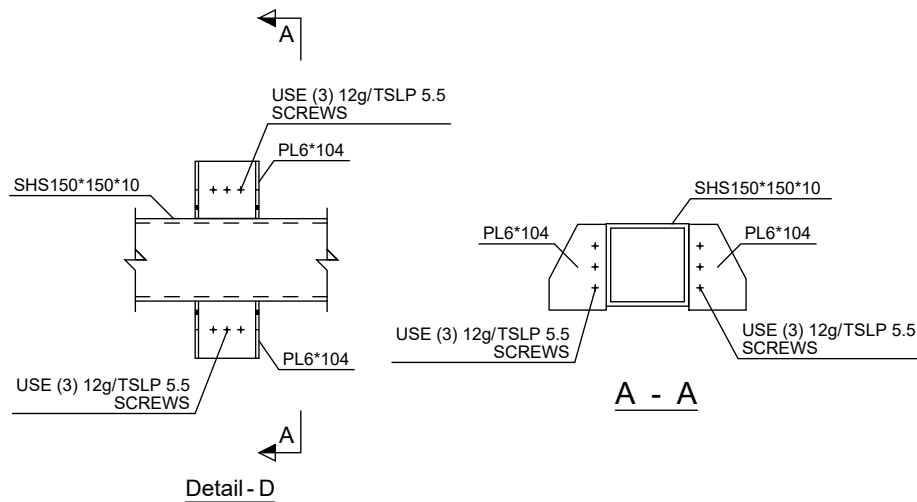


Typ. Truss Bracket Connection

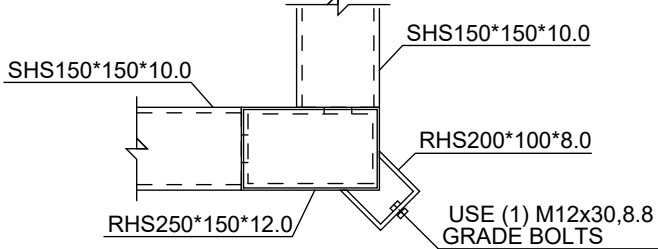


Typ. Corner Truss Connection

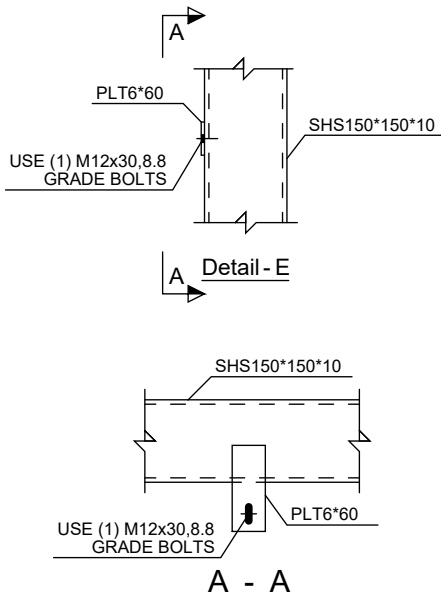


Typ. Wall to Beam Top Plate Connection

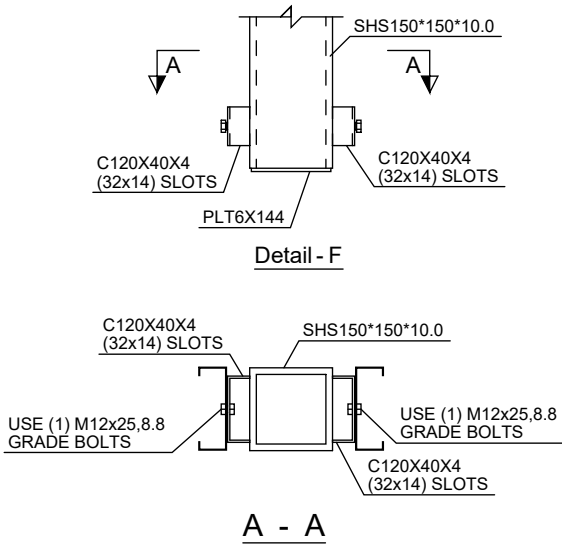


Typ. Lintel to Wind Post Connection

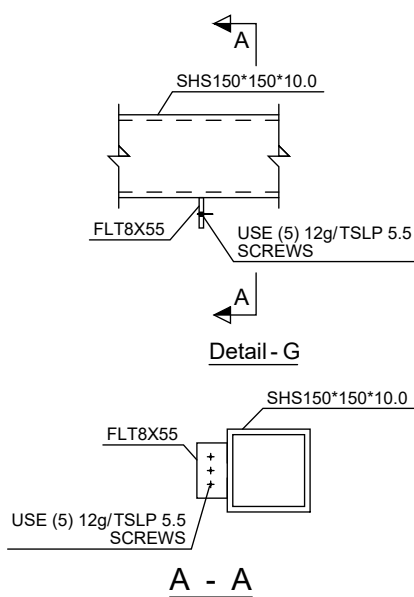


Cassette to Beam Connection

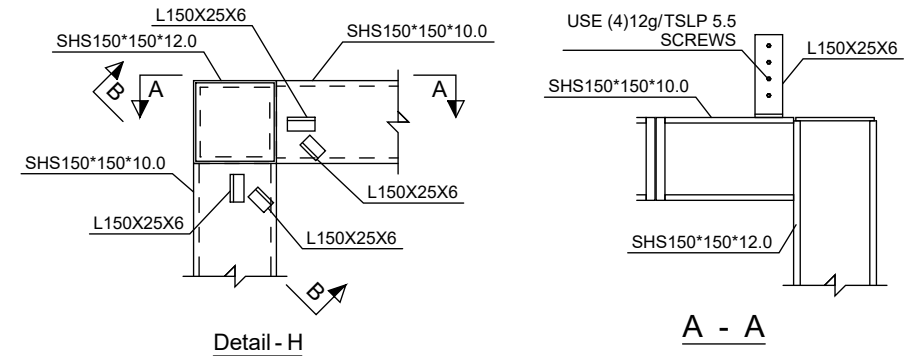

Typ. Beam to Column Connection Using C Bracket

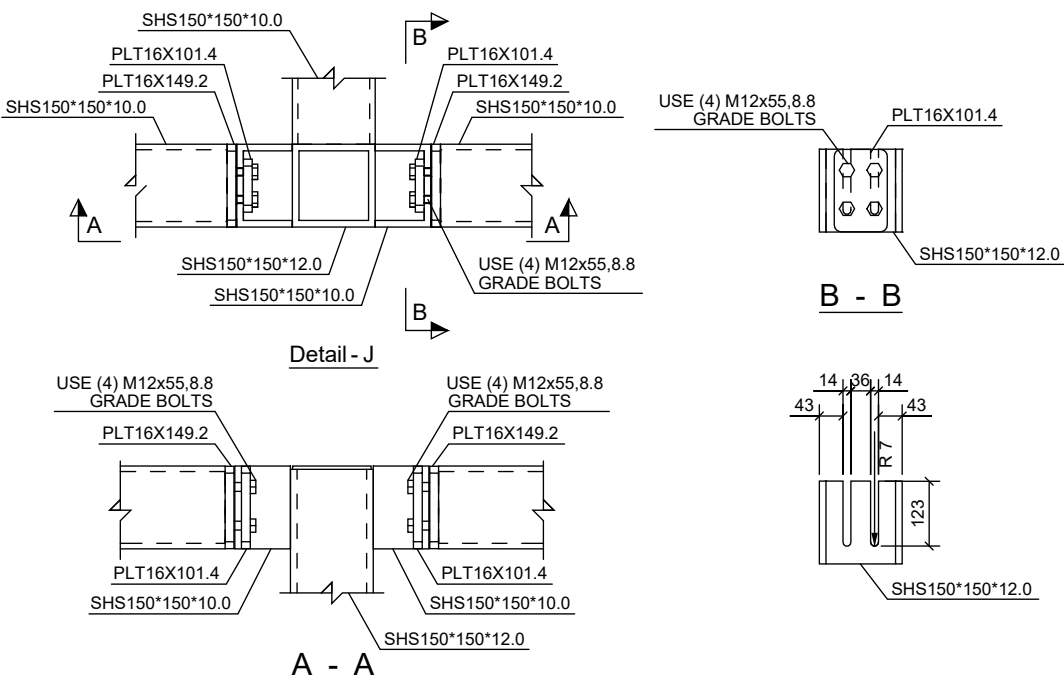

Typ. Beam to Column Connection Using C Bracket

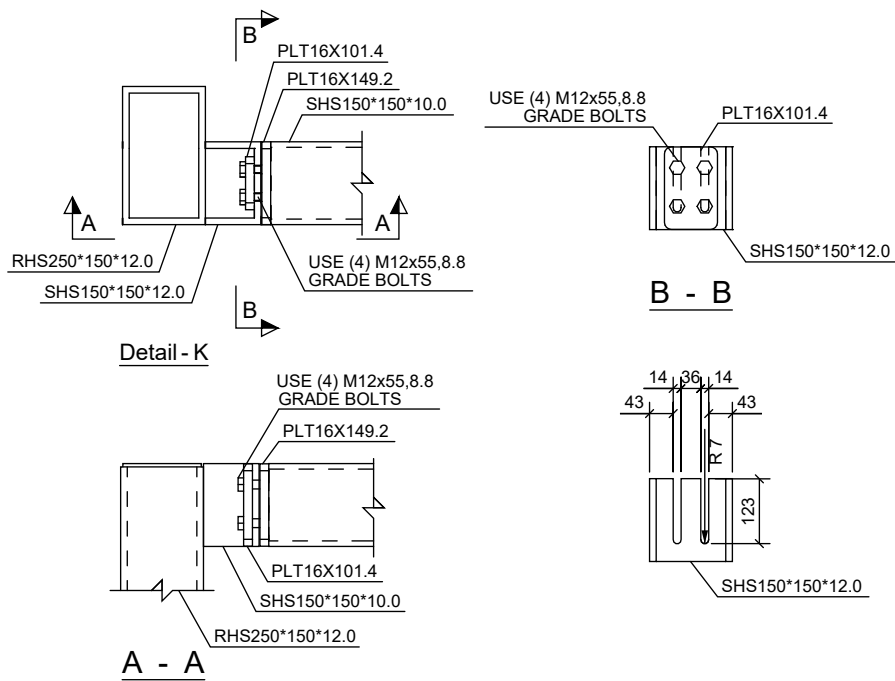

Typ. Beam to Column Connection Using C Bracket

1. THESE DRAWINGS MUST BE CHECKED BY THE CUSTOMER OR CONTRACTOR PRIOR TO APPROVAL. ANY ERRORS OR OMISSIONS MUST BE REPORTED IN WRITING TO BAUHU PRIOR TO COMMENCEMENT OF CONSTRUCTION.
2. ARCHITECTURAL DRAWINGS SHOULD BE READ IN CONJUNCTION WITH STRUCTURAL DETAILING AND FABRICATION GENERAL ASSEMBLY DRAWINGS.
3. FOR CONSTRUCTION PURPOSES, USE ONLY THE LATEST APPROVED DRAWINGS LABELED 'ISSUED FOR CONSTRUCTION'.
4. DO NOT SCALE FROM THIS DRAWING.
5. THE COMPANY OPERATES USING METRIC DIMENSIONS AS THE PRINCIPAL DENOMINATION.
6. ALL CONCRETE WORKS ARE OUTSIDE OF THE SCOPE OF THE COMPANY. INFORMATION REGARDING SLAB DESIGN AND CONNECTIONS IN THESE DRAWINGS ARE INTENDED FOR GUIDANCE ONLY. FOUNDATION AND SLAB WORKS SHOULD BE DESIGNED AND APPROVED BY A LOCAL STRUCTURAL ENGINEER.
7. THE COMPANY RETAINS FULL TITLE AND OWNERSHIP OF THESE PLANS AND DESIGNS. ANY UNAUTHORISED USE, REPRODUCTION, OR DISTRIBUTION OF THESE PLANS, WHETHER IN WHOLE OR PART, IS EXPRESSLY PROHIBITED WITHOUT PRIOR WRITTEN CONSENT.

No.	Revision	Date

ISSUED FOR:

Issued for information

Issued for client approval

Issued for fabrication


Issued for construction

Angel

DRAWING TITLE:
Typical Frame Connections 3
DRAWN BY:
Yonca A.Clark
SCALE:
DRAWING NO:
A142
DATE:
01/05/2024


Typical Frame Connections 4

Hold Down Detail

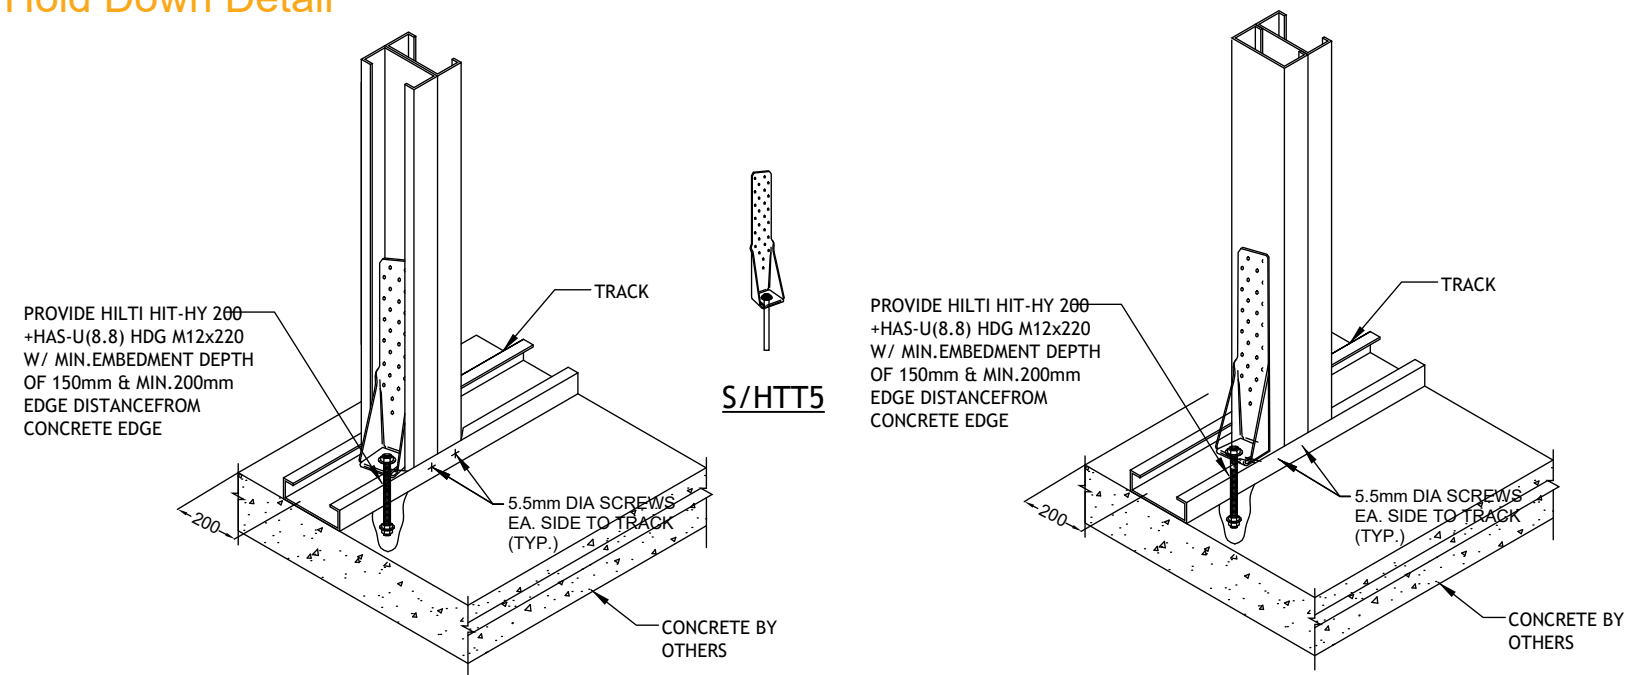

- NOTE -
- 1. ANCHOR & SCREWS SPECIFICATION AS PER SPECIFIED ON STRUCTURAL PLAN
 - 2. FIXING SPECIFICATION SUBJECT TO CHANGE AS PER DESIGN.


Casette to Floor/Roof Joist Connection

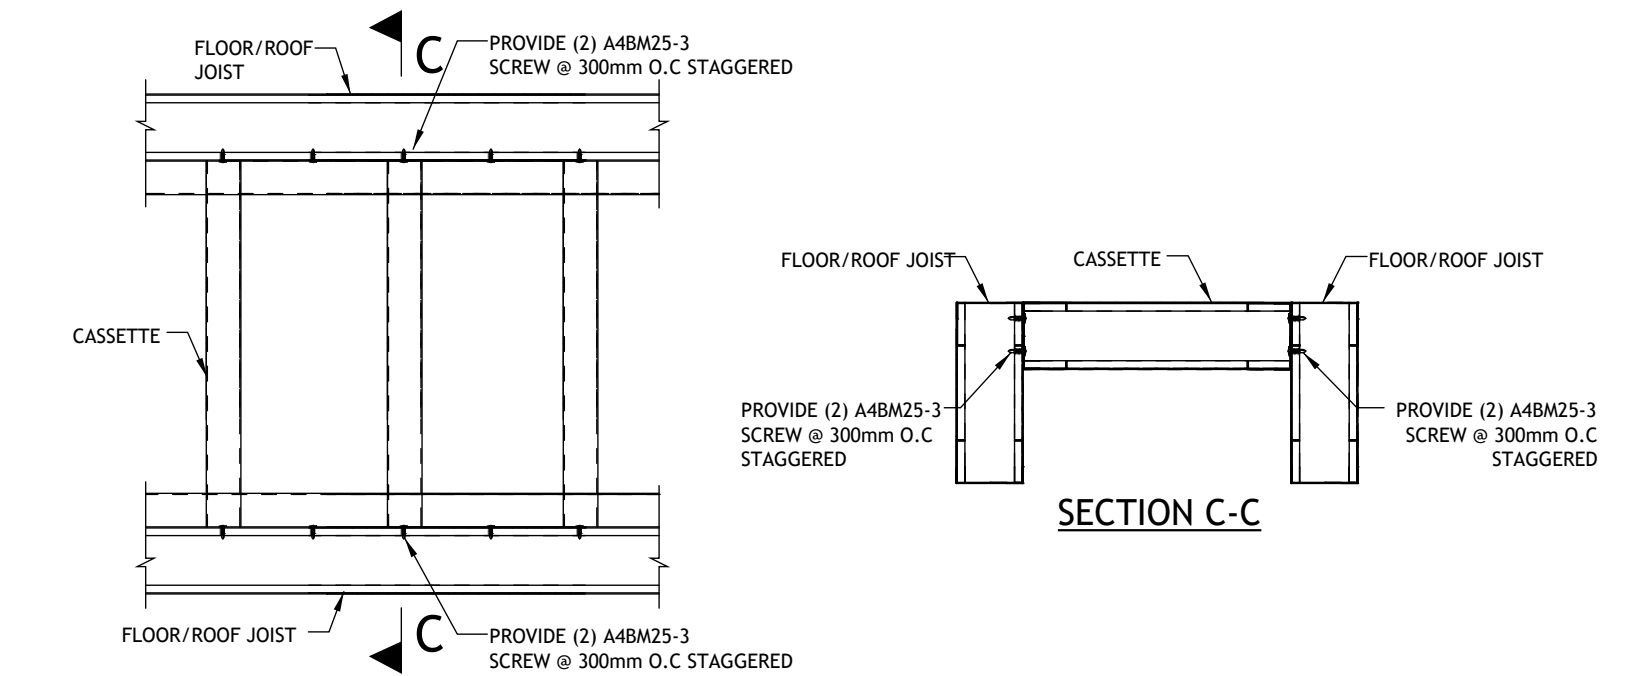

NOTE -FIXING SPECIFICATION SUBJECT TO CHANGE AS PER DESIGN.





Typ. Internal Wall Connection Floor/Roof Joist

(Perpendicular Condition)



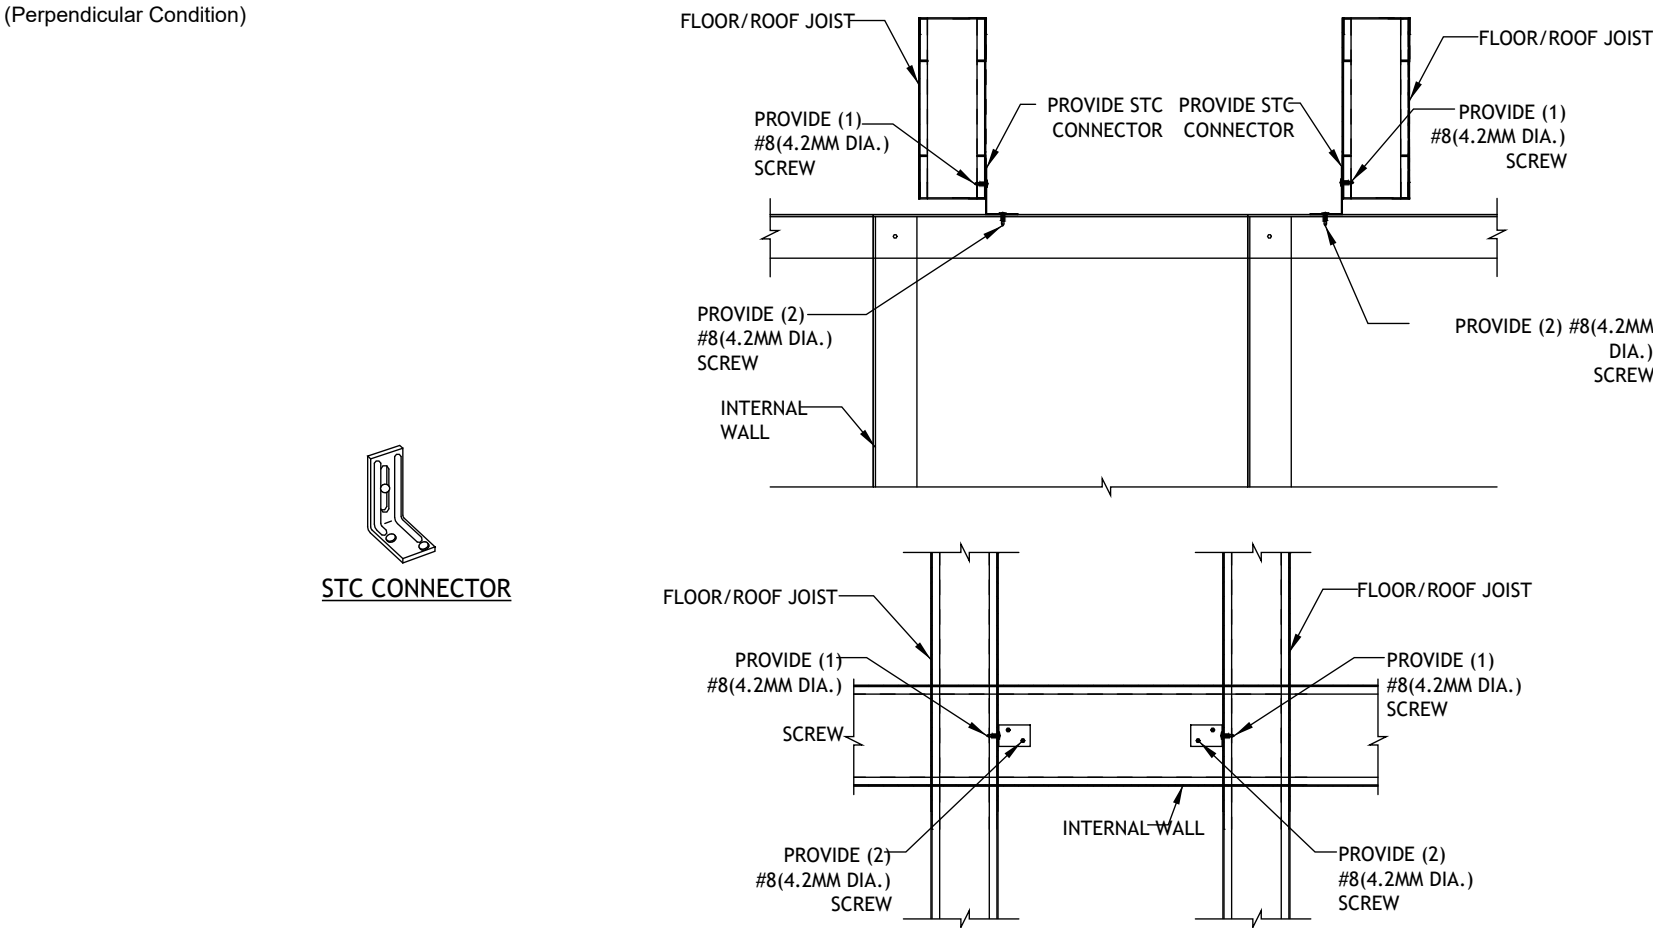


NOTE -FIXING SPECIFICATION SUBJECT TO CHANGE AS PER DESIGN.

Typ. Brace Wall Panel Connection with Treaded Rod

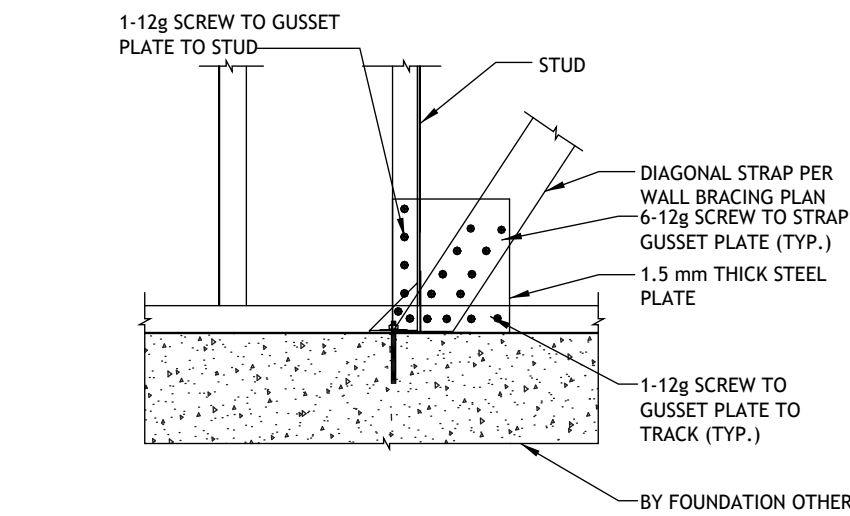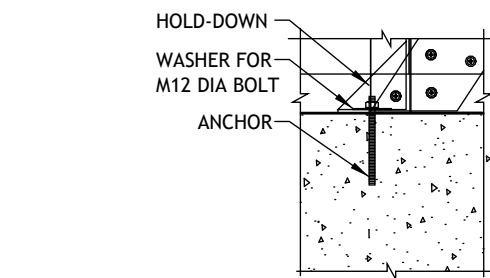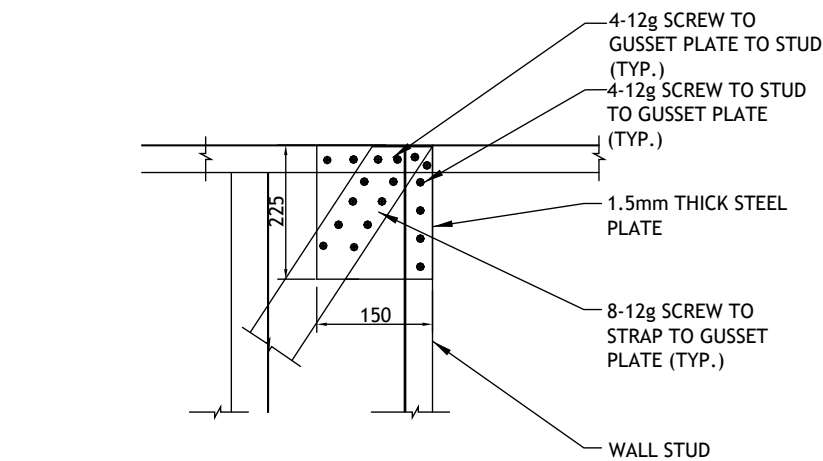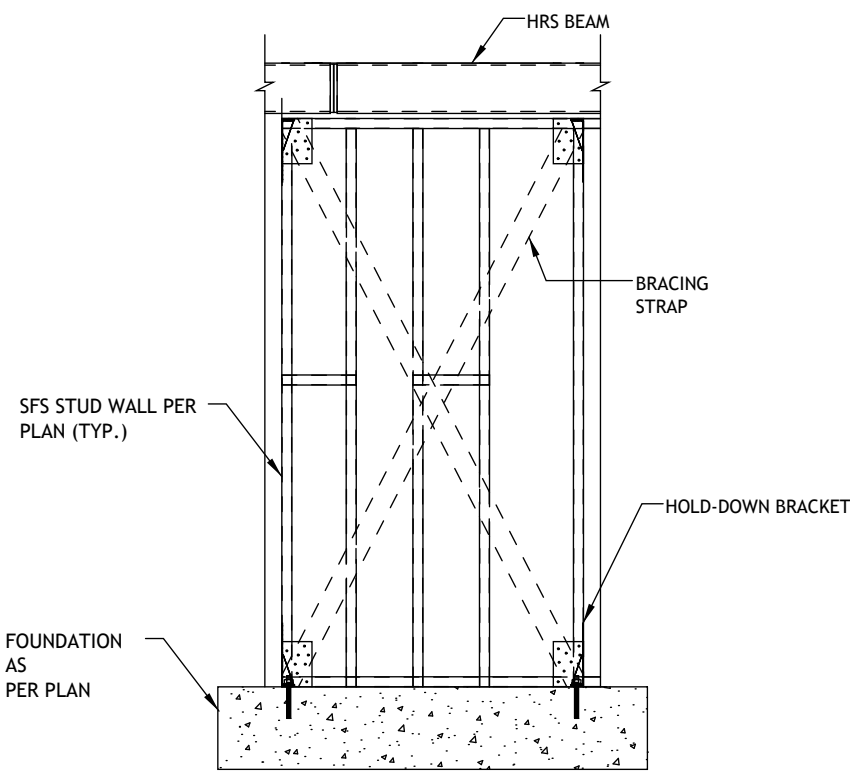

- NOTE -
- 1. ANCHOR & SCREWS SPECIFICATION AS PER SPECIFIED ON STRUCTURAL PLAN
 - 2. FIXING SPECIFICATION SUBJECT TO CHANGE AS PER DESIGN.

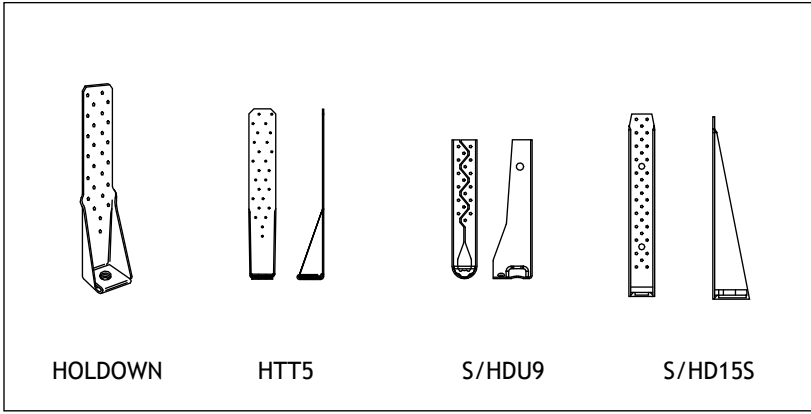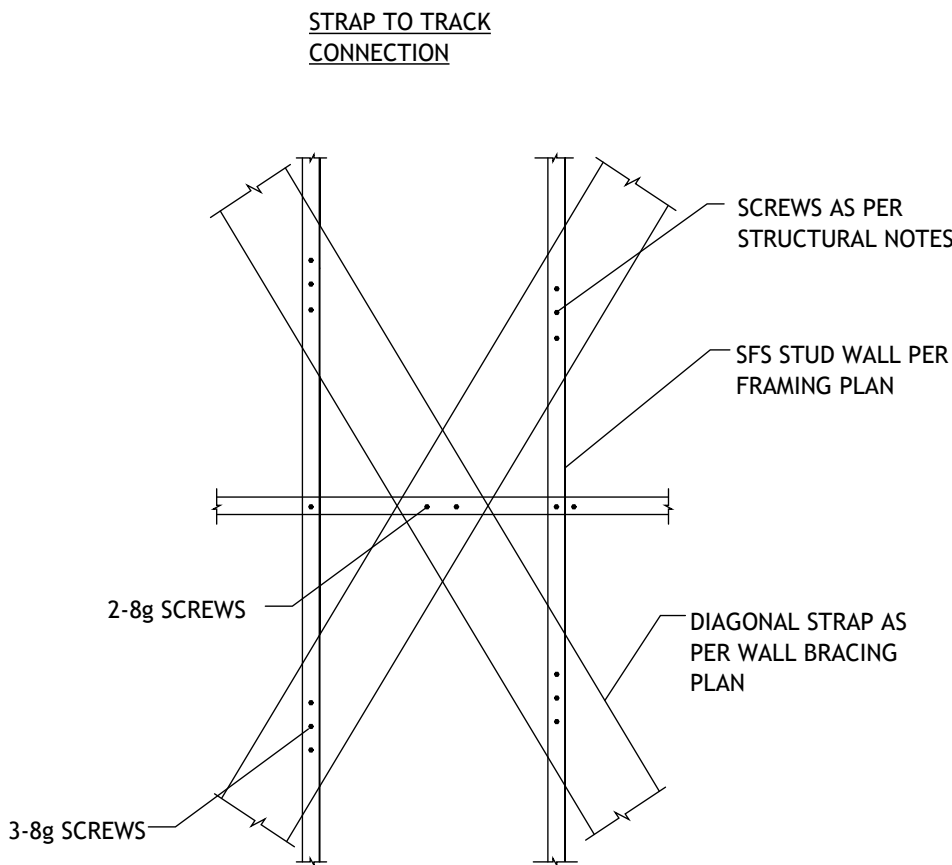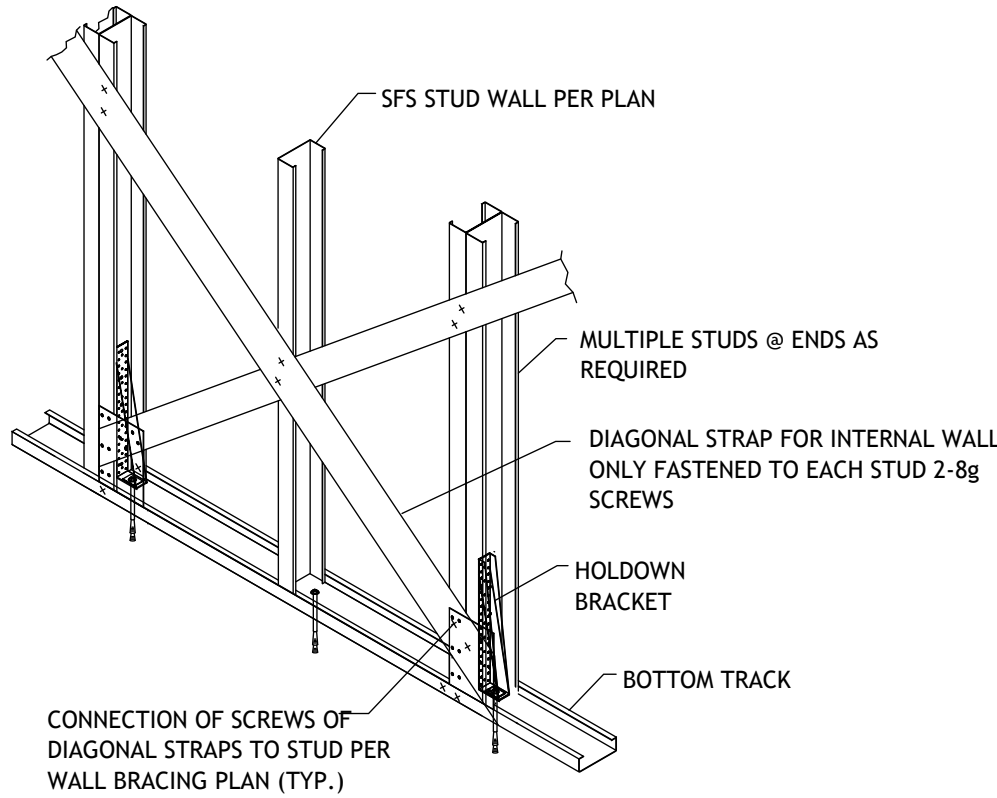

1. THESE DRAWINGS MUST BE CHECKED BY THE CUSTOMER OR CONTRACTOR PRIOR TO APPROVAL. ANY ERRORS OR OMISSIONS MUST BE REPORTED IN WRITING TO BAUHU PRIOR TO COMMENCEMENT OF CONSTRUCTION.
2. ARCHITECTURAL DRAWINGS SHOULD BE READ IN CONJUNCTION WITH STRUCTURAL DETAILING AND FABRICATION GENERAL ASSEMBLY DRAWINGS.
3. FOR CONSTRUCTION PURPOSES, USE ONLY THE LATEST APPROVED DRAWINGS LABELED 'ISSUED FOR CONSTRUCTION'.
4. DO NOT SCALE FROM THIS DRAWING.
5. THE COMPANY OPERATES USING METRIC DIMENSIONS AS THE PRINCIPAL DENOMINATION.
6. ALL CONCRETE WORKS ARE OUTSIDE OF THE SCOPE OF THE COMPANY. INFORMATION REGARDING SLAB DESIGN AND CONNECTIONS IN THESE DRAWINGS ARE INTENDED FOR GUIDANCE ONLY. FOUNDATION AND SLAB WORKS SHOULD BE DESIGNED AND APPROVED BY A LOCAL STRUCTURAL ENGINEER.
7. THE COMPANY RETAINS FULL TITLE AND OWNERSHIP OF THESE PLANS AND DESIGNS. ANY UNAUTHORISED USE, REPRODUCTION, OR DISTRIBUTION OF THESE PLANS, WHETHER IN WHOLE OR PART, IS EXPRESSLY PROHIBITED WITHOUT PRIOR WRITTEN CONSENT.

No.	Revision	Date

ISSUED FOR:

Issued for information

Issued for client approval

Issued for fabrication

Issued for construction

Angel

DRAWING TITLE:	Typical Frame Connections 4
DRAWN BY:	Yonca A.Clark
SCALE:	
DRAWING NO:	A143
DATE:	01/05/2024

General Construction notes

STANDARDS AND CODES OF PRACTICE

- International Building Code (IBC) 2015
- ASCE 7-16- American Society of civil Engineers (Minimum Design loads for buildings & other structures)
- AISC 360-10 - American Institute of steel construction (Specification for structural steel buildings)
- AISI -100-16 - American Iron and Steel Institute (Design of Cold Formed steel & structural members)
- ASTM - American Society for Testing and materials.
- All CFS frame will be designed to AISI LRFD CFS design standard

COLD FORMED STEEL (LGS)

Walls panels and trusses are made up by roll-formed cold rolled, galvanised steel sections fabricated and assembled into frames. Section properties in accordance with BS EN 1993-1-3:2006.

Steel grade S450GD + Z275.

C 70 -50/70- 1.2/1.5/2

C 100 -50/70- 1.2/1.5/2

C 150 -50/70- 1.2/1.5/2

LGS frames are fixed to each other and to the HRS members with specified mechanical fixings.

HOT ROLLED STEEL (HRS)

Material Availability of Hot Rolled Steel Sections is as per European/British sections with grade of S275.

Plate thickness 6, 8, 10,12mm grade S275, S355.

HRS members are hot dip galvanised and fixed to each other with specified mechanical fixings to form a portal frame.

SLAB FIXINGS

Concrete slab and foundation design is carried out by relevant local engineers and falls outside of the scope of Bauhu construction. HRS columns are supplied with pre-drilled column base plates for ground fixing with specified chemical anchor bolts.

LGS frame base rails are pre-punched for mechanical fixing to a concrete slab using the specified expanding bolts. A damp proof membrane is required.

CONSTRUCTIVE CLADDING

12.5mm lightweight, fire resistant, high density cement board is fixed to the entire exterior wall surface of the assembled building. Cement board is fixed at 300mm CTS to LGS studs and track profiles with AISI C1022 grade coated steel wing tip TEK-3 self-drilling and countersinking fixings 4.8mmx48mm.

Cement board spanning HRS members is adhered to the HRS outer surface.

Constructive cladding joints are sealed with mastic.

OPENING REVEALS CLADDING

12.5mm lightweight, fire resistant, high density cement board is fixed to opening reveals in the same manner. See assembly information and section drawings for dimension details.

CEILINGS

Ceilings are suspended from LGS roof or intermediate floor joists using Knauf C-Form suspended ceiling system mechanically fixed to joists. An insulation layer of 160mm mineral wool insulation is laid inside the ceiling void. Ceilings are finished in two layers of 12.5mm gypsumboard.

Knauf moisture panel + Knauf fire panel fixed at 300mm CTS to suspended ceiling profiles with AISI C1022 grade coated steel wing tip TEK-3 self drilling and countersinking fixings 4.8mmx48mm with joints taped and filled.

Internal low VOC acrylic paint finishes are applied per customer selection.

INTERMEDIATE FLOORS

Intermediate floor structures are supported by LGS lattice frame joists mechanically fixed to HRS beams typically at 500mm CTS according to project engineering.

18mm OSB4, termite treated, oriented strand board is fixed to the entire floor surface of the assembled building. OSB4 board is fixed at 300mm CTS to LGS joists with AISI C1022 grade coated steel wing tip TEK-3 self drilling and countersinking fixings 4.8mmx48mm.

6mm cement board floor backer sheets are mechanically fixed to the floor surface to accept client specified floor finishes.

EXTERIOR WALLS

Exterior walls are formed by pre-assembled 150mm x1.5mm profile LGS frames mechanically fixed to adjacent frames, floors and roof/floor joists. Section properties in accordance with BS EN 1993-1-3:2006. Steel grade S450GD + Z275. Frame profiles have pre-punched service holes for cable and pipe passage.

120mm mineral wool insulation is applied in the frame web.

The exterior wall surfaces are clad in a cement board constructive coating (see CONSTRUCTIVE COATING)

The interior wall surfaces are finished in two layers of 12.5mm gypsumboard Knauf moisture panel applied in horizontal format + Knauf fire panel applied in vertical format fixed at 300mm CTS to LGS

profiles with AISI C1022 grade coated steel wing tip TEK-3 self drilling and countersinking fixings 4.8mmx48mm with joints taped and filled.

Internal low VOC acrylic paint finishes are applied per customer selection.

INTERIOR WALLS

Interior walls are formed by pre-assembled 150mm x1.5mm profile LGS frames mechanically fixed to adjacent walls, floors and roof/floor joists. Section properties in accordance with BS EN 1993-1-3:2006. Steel grade S450GD + Z275. Frame profiles have pre-punched service holes for cable and pipe passage.

120mm mineral wool insulation is applied in the frame web.

Internal walls are finished in two opposing layers of 12.5mm gypsumboard fixed at 300mm CTS to LGS profiles with AISI C1022 grade coated steel wing tip TEK-3 self drilling and countersinking fixings 4.8mmx48mm.

Knauf moisture panel applied in horizontal format + Knauf fire panel applied in vertical format with joints taped and filled.

Internal low VOC acrylic paint finishes are applied per customer selection.

EXTERIOR FACADE (ETICs)

The external facade is finished in an impact resistant, self colour, thermal and acoustic ETICs (External thermal insulation composite system) coating. An insulation layer of 40mm rigid Rockwool is applied to the cement board constructive coating with mechanical fixings. STO impact resistant plaster base coat is applied with fiberglass mesh and finished in STOLIT finish plaster coat.

FLAT ROOF STRUCTURE (EPDM)

Flat roof structures are supported by LGS lattice frame joists mechanically fixed to HRS beams typically at 500mm CTS according to project engineering.

18mm OSB4, termite treated, oriented strand board is fixed to the entire exterior roof surface of the assembled building. OSB4 is fixed at 300mm CTS to LGS joists with AISI C1022 grade coated steel wing tip TEK-3 self drilling and countersinking fixings 4.8mmx38mm.

A rigid 40mm PIR insulation board is mechanically fixed to the cement board constructive cladding.

Firestone 1.5mm heavy duty EPDM waterproofing membrane is fully bonded to the roof surface

and parapet sides with rain water outlets and breather pipe boots at appropriate locations.

Leaf guards are installed in rain water outlets.

PARAPET DETAIL

LGS panels are mechanically fixed to HRS beams to form a parapet extension of exterior walls.

LGS parapet frames are clad in SECOLITE 12.5mm cement board on inner and top faces. A metal capping or acrylic render finishes parapet tops.

ACCESSIBLE ROOFS

Accessible roofs have the same properties as flat (EPDM) roofs. Final floor finishes of ceramic tile or composite decking should be laid over a supplementary geotextile membrane to protect the EPDM membrane. Refer to project files for specific details.

GREEN ROOFS

Green roofs have the same properties as flat (EPDM) roofs. Vegetation in specified containers is added over a textile membrane.

Vegetation is NOT supplied.

SOLAR ROOFS

Projects requiring solar (PV) arrays to be roof mounted are subject to specialist analysis.



1. THESE DRAWINGS MUST BE CHECKED BY THE CUSTOMER OR CONTRACTOR PRIOR TO APPROVAL. ANY ERRORS OR OMISSIONS MUST BE REPORTED IN WRITING TO BAUHU PRIOR TO COMMENCEMENT OF CONSTRUCTION.
2. ARCHITECTURAL DRAWINGS SHOULD BE READ IN CONJUNCTION WITH STRUCTURAL DETAILING AND FABRICATION GENERAL ASSEMBLY DRAWINGS.
3. FOR CONSTRUCTION PURPOSES, USE ONLY THE LATEST APPROVED DRAWINGS LABELED 'ISSUED FOR CONSTRUCTION'.
4. DO NOT SCALE FROM THIS DRAWING.
5. THE COMPANY OPERATES USING METRIC DIMENSIONS AS THE PRINCIPAL DENOMINATION.
6. ALL CONCRETE WORKS ARE OUTSIDE OF THE SCOPE OF THE COMPANY. INFORMATION REGARDING SLAB DESIGN AND CONNECTIONS IN THESE DRAWINGS ARE INTENDED FOR GUIDENCE ONLY. FOUNDATION AND SLAB WORKS SHOULD BE DESIGNED AND APPROVED BY A LOCAL STRUCTURAL ENGINEER.
7. THE COMPANY RETAINS FULL TITLE AND OWNERSHIP OF THESE PLANS AND DESIGNS. ANY UNAUTHORISED USE, REPRODUCTION, OR DISTRIBUTION OF THESE PLANS, WHETHER IN WHOLE OR PART, IS EXPRESSLY PROHIBITED WITHOUT PRIOR WRITTEN CONSENT.

No.	Revision	Date

ISSUED FOR:

Issued for information

Issued for client approval

Issued for fabrication

Issued for construction

Angel

DRAWING TITLE:

General Construction Notes

DRAWN BY:

Yonca A.Clark

SCALE:

DRAWING NO:

A144

DATE:

01/05/2024