




Rear View



Primary Bedroom

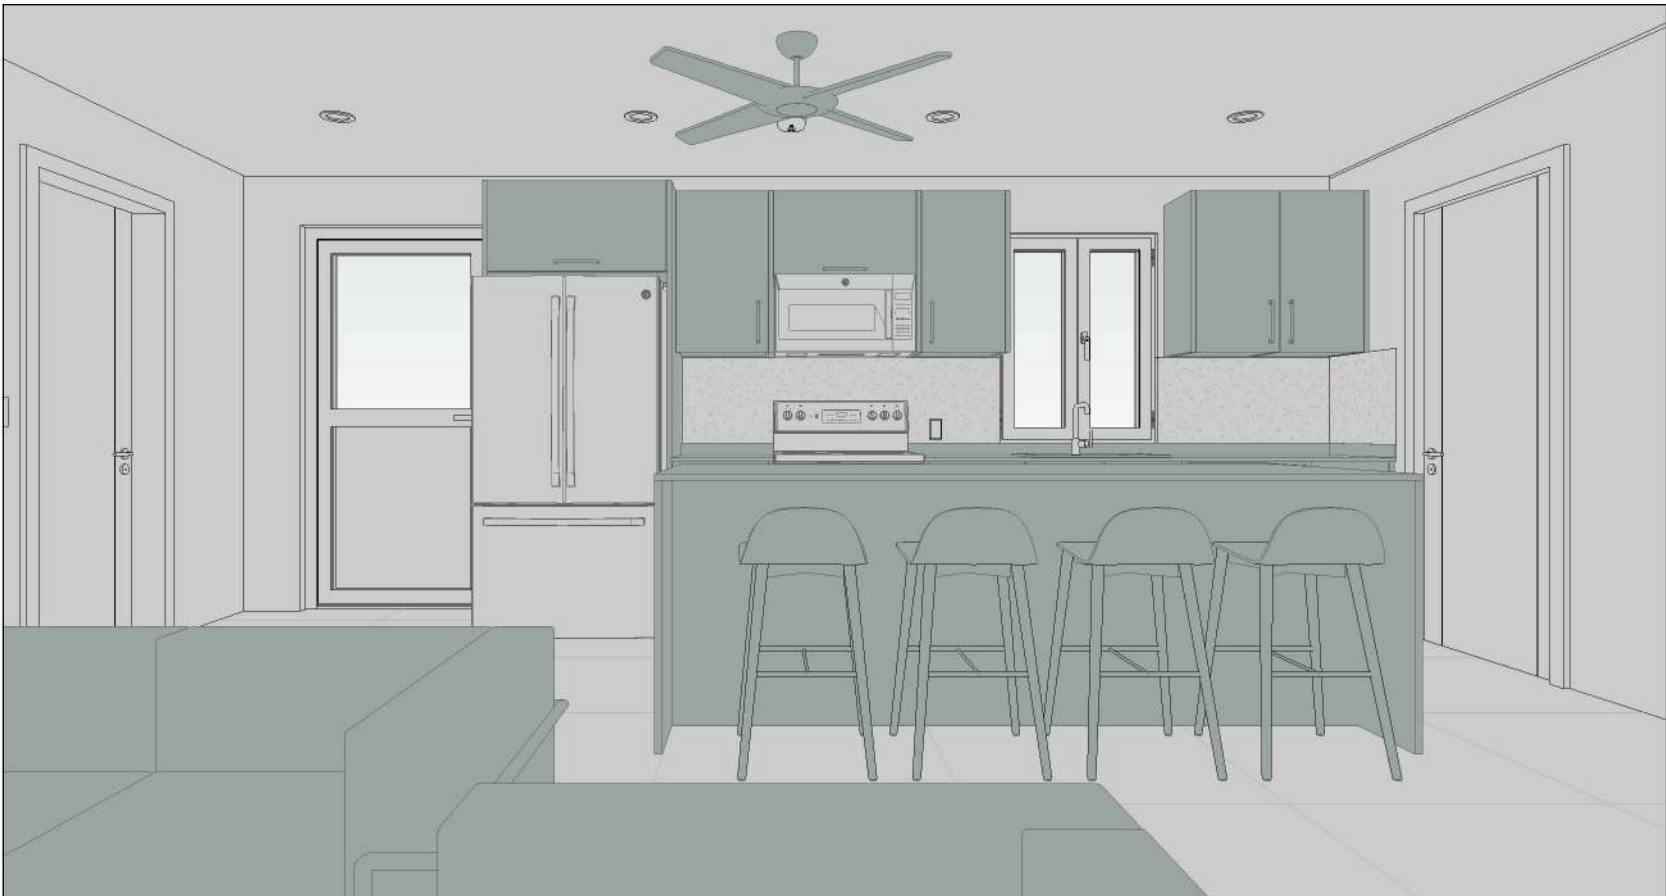

Living Area



Living Area

1. THESE DRAWINGS MUST BE CHECKED BY THE CUSTOMER OR CONTRACTOR PRIOR TO APPROVAL. ANY ERRORS OR OMISSIONS MUST BE REPORTED IN WRITING TO BAUHU PRIOR TO COMMENCEMENT OF CONSTRUCTION.
2. ARCHITECTURAL DRAWINGS SHOULD BE READ IN CONJUNCTION WITH STRUCTURAL DETAILING AND FABRICATION GENERAL ASSEMBLY DRAWINGS.
3. FOR CONSTRUCTION PURPOSES, USE ONLY THE LATEST APPROVED DRAWINGS LABELED 'ISSUED FOR CONSTRUCTION'.
4. DO NOT SCALE FROM THIS DRAWING.
5. THE COMPANY OPERATES USING METRIC DIMENSIONS AS THE PRINCIPAL DENOMINATION.
6. ALL CONCRETE WORKS ARE OUTSIDE OF THE SCOPE OF THE COMPANY. INFORMATION REGARDING SLAB DESIGN AND CONNECTIONS IN THESE DRAWINGS ARE INTENDED FOR GUIDENCE ONLY. FOUNDATION AND SLAB WORKS SHOULD BE DESIGNED AND APPROVED BY A LOCAL STRUCTURAL ENGINEER.
7. THE COMPANY RETAINS FULL TITLE AND OWNERSHIP OF THESE PLANS AND DESIGNS. ANY UNAUTHORISED USE, REPRODUCTION, OR DISTRIBUTION OF THESE PLANS, WHETHER IN WHOLE OR PART, IS EXPRESSLY PROHIBITED WITHOUT PRIOR WRITTEN CONSENT.
8. THE HYBRID STEEL FRAME CONSTRUCTION SYSTEM AND METHODOLOGY (PATENT PENDING) DESCRIBED IN THESE PLANS HAS BEEN DEVELOPED BY THE COMPANY AND IS SUBJECT TO A PROVISIONAL PATENT APPLICATION & ASSIGNMENT - US APPLICATION NO. 63/722,841

No.	Revision	Date

ISSUED FOR:

Issued for information


Issued for client approval

Issued for fabrication

Issued for construction

The Charlston

DRAWING TITLE:	Views
DRAWN BY:	Y.A.Clark
SCALE:	
DRAWING NO:	A101
DATE:	18/03/2026

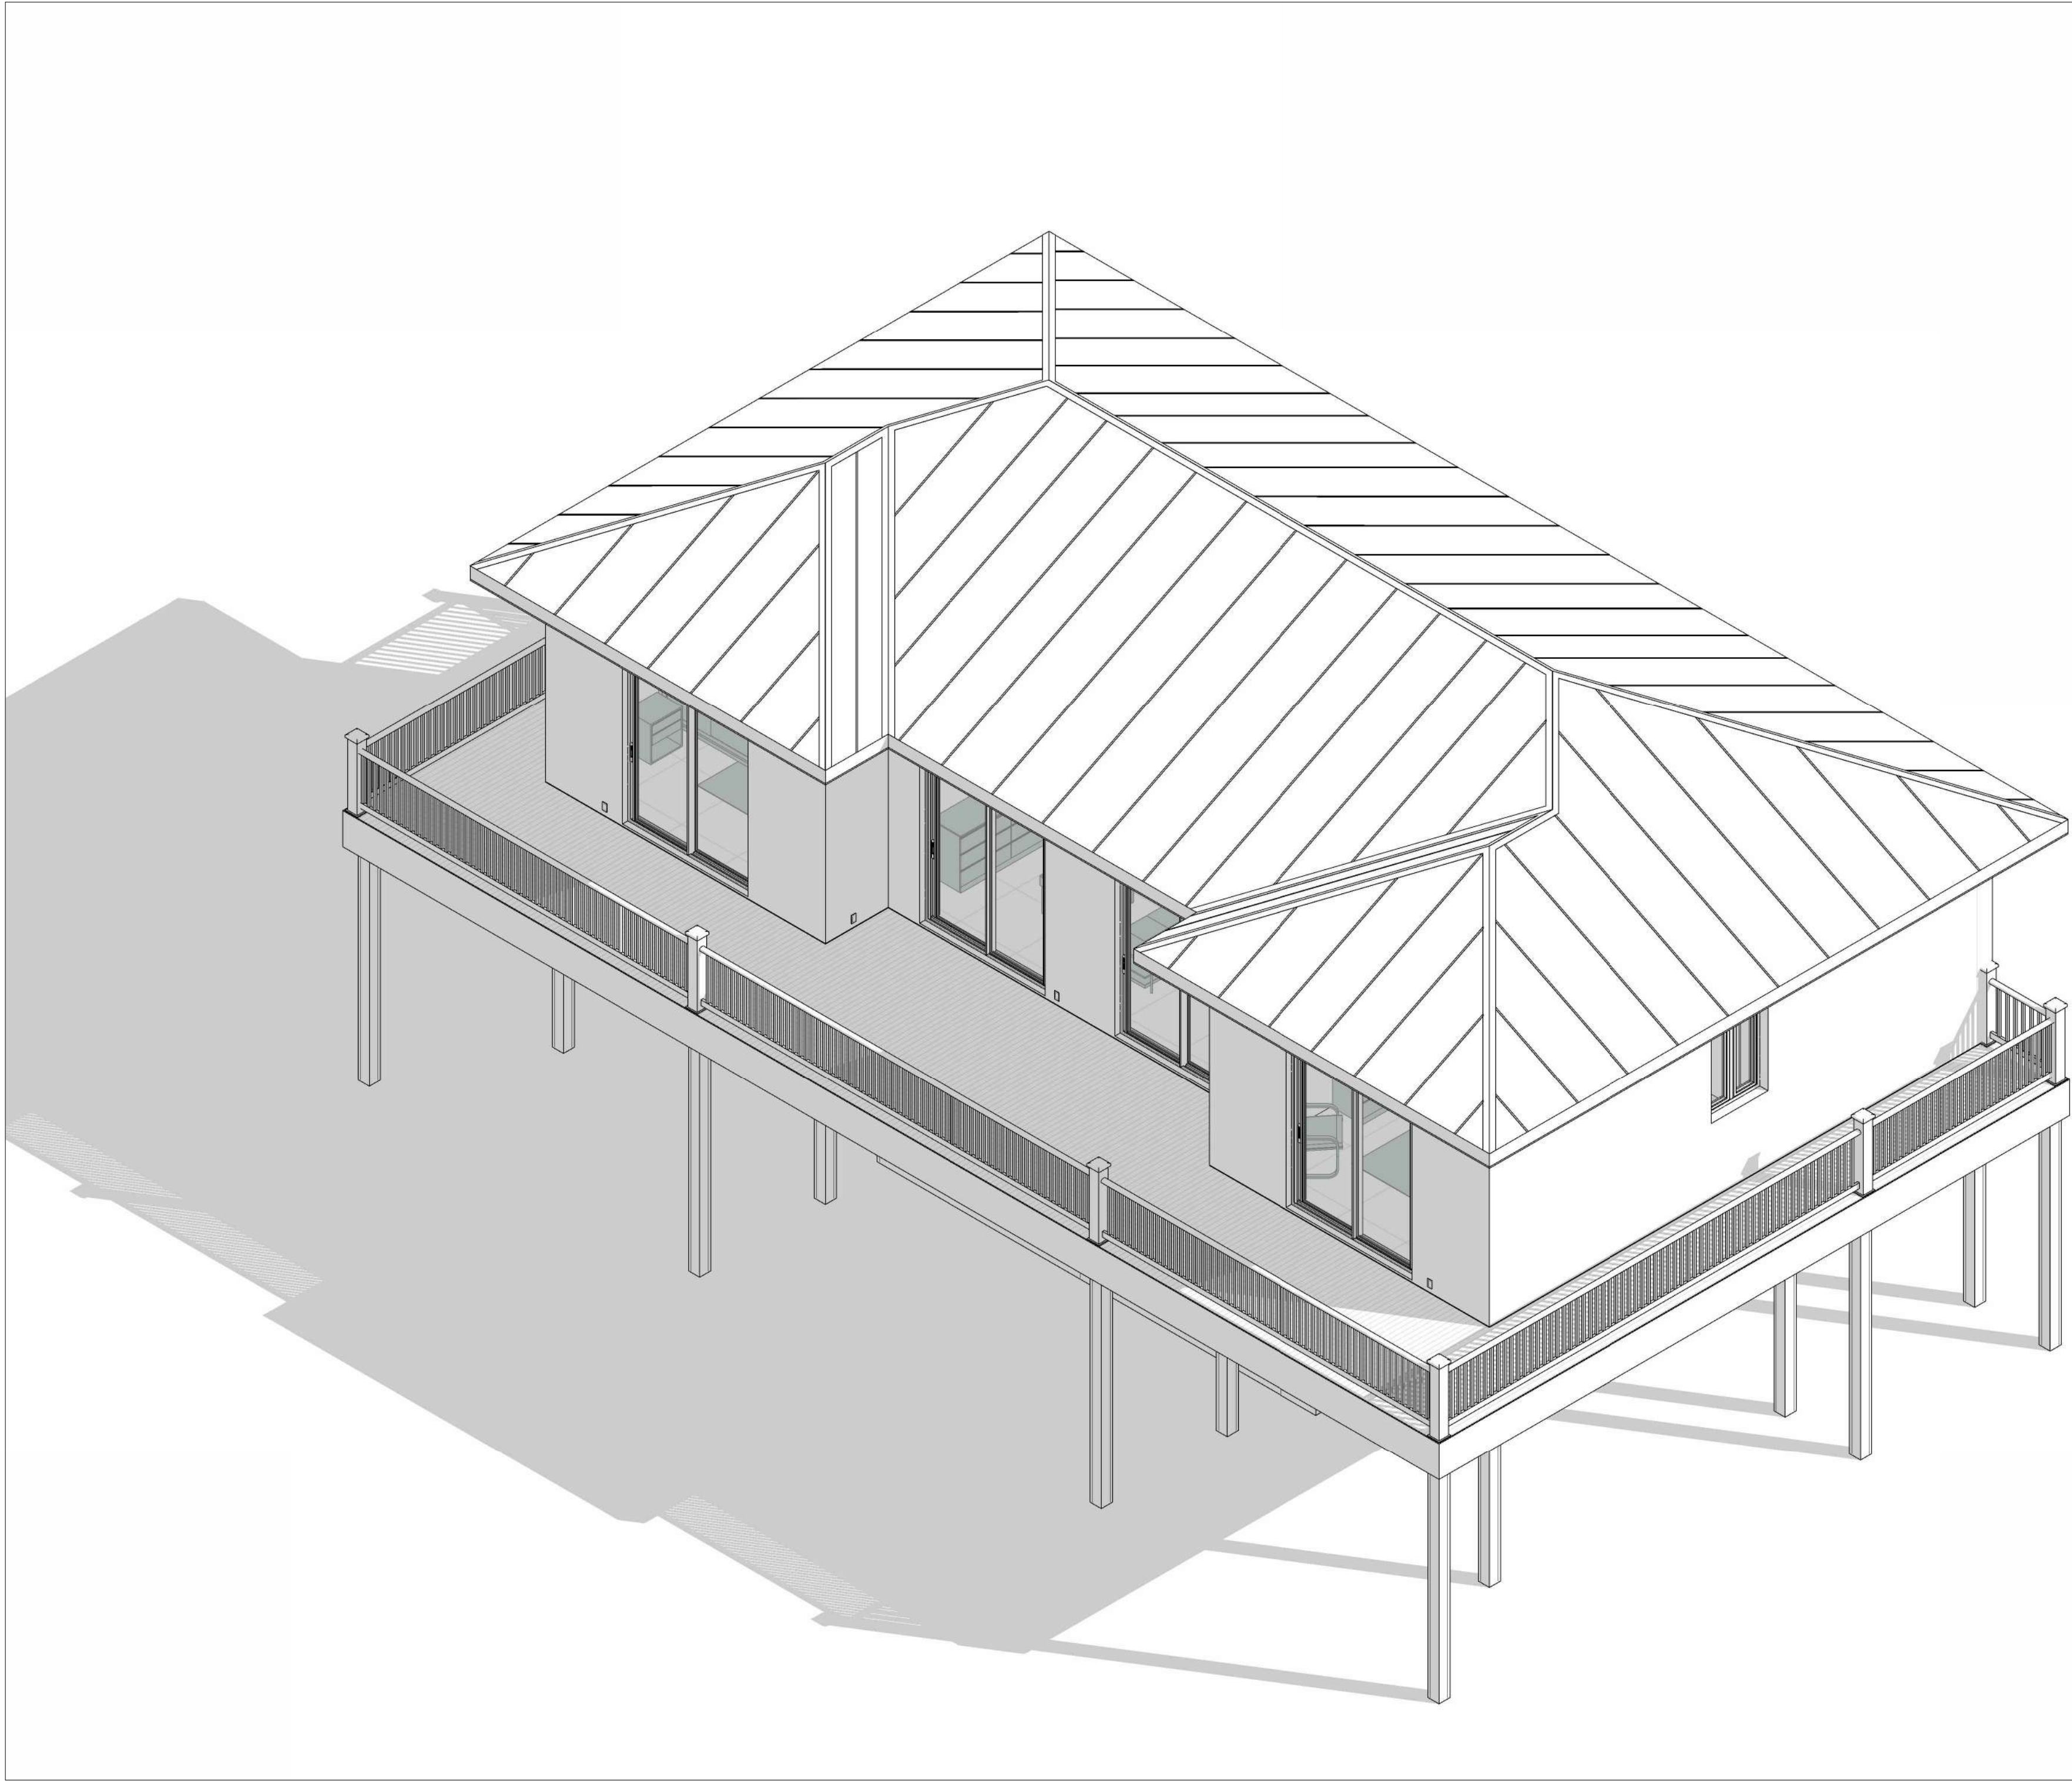

1. THESE DRAWINGS MUST BE CHECKED BY THE CUSTOMER OR CONTRACTOR PRIOR TO APPROVAL. ANY ERRORS OR OMISSIONS MUST BE REPORTED IN WRITING TO BAUHU PRIOR TO COMMENCEMENT OF CONSTRUCTION.
2. ARCHITECTURAL DRAWINGS SHOULD BE READ IN CONJUNCTION WITH STRUCTURAL DETAILING AND FABRICATION GENERAL ASSEMBLY DRAWINGS.
3. FOR CONSTRUCTION PURPOSES, USE ONLY THE LATEST APPROVED DRAWINGS LABELED 'ISSUED FOR CONSTRUCTION'.
4. DO NOT SCALE FROM THIS DRAWING.
5. THE COMPANY OPERATES USING METRIC DIMENSIONS AS THE PRINCIPAL DENOMINATION.
6. ALL CONCRETE WORKS ARE OUTSIDE OF THE SCOPE OF THE COMPANY. INFORMATION REGARDING SLAB DESIGN AND CONNECTIONS IN THESE DRAWINGS ARE INTENDED FOR GUIDENCE ONLY. FOUNDATION AND SLAB WORKS SHOULD BE DESIGNED AND APPROVED BY A LOCAL STRUCTURAL ENGINEER.
7. THE COMPANY RETAINS FULL TITLE AND OWNERSHIP OF THESE PLANS AND DESIGNS. ANY UNAUTHORISED USE, REPRODUCTION, OR DISTRIBUTION OF THESE PLANS, WHETHER IN WHOLE OR PART, IS EXPRESSLY PROHIBITED WITHOUT PRIOR WRITTEN CONSENT.
8. THE HYBRID STEEL FRAME CONSTRUCTION SYSTEM AND METHODOLOGY (PATENT PENDING) DESCRIBED IN THESE PLANS HAS BEEN DEVELOPED BY THE COMPANY AND IS SUBJECT TO A PROVISIONAL PATENT APPLICATION & ASSIGNMENT - US APPLICATION NO. 63/722,841

No.	Revision	Date

ISSUED FOR:

Issued for information

Issued for client approval

Issued for fabrication

Issued for construction

The Charlston

DRAWING TITLE:	Front View
DRAWN BY:	Y.A.Clark
SCALE:	
DRAWING NO:	A102
DATE:	18/03/2026



1. THESE DRAWINGS MUST BE CHECKED BY THE CUSTOMER OR CONTRACTOR PRIOR TO APPROVAL. ANY ERRORS OR OMISSIONS MUST BE REPORTED IN WRITING TO BAUHU PRIOR TO COMMENCEMENT OF CONSTRUCTION.
2. ARCHITECTURAL DRAWINGS SHOULD BE READ IN CONJUNCTION WITH STRUCTURAL DETAILING AND FABRICATION GENERAL ASSEMBLY DRAWINGS.
3. FOR CONSTRUCTION PURPOSES, USE ONLY THE LATEST APPROVED DRAWINGS LABELED 'ISSUED FOR CONSTRUCTION'.
4. DO NOT SCALE FROM THIS DRAWING.
5. THE COMPANY OPERATES USING METRIC DIMENSIONS AS THE PRINCIPAL DENOMINATION.
6. ALL CONCRETE WORKS ARE OUTSIDE OF THE SCOPE OF THE COMPANY. INFORMATION REGARDING SLAB DESIGN AND CONNECTIONS IN THESE DRAWINGS ARE INTENDED FOR GUIDENCE ONLY. FOUNDATION AND SLAB WORKS SHOULD BE DESIGNED AND APPROVED BY A LOCAL STRUCTURAL ENGINEER.
7. THE COMPANY RETAINS FULL TITLE AND OWNERSHIP OF THESE PLANS AND DESIGNS. ANY UNAUTHORISED USE, REPRODUCTION, OR DISTRIBUTION OF THESE PLANS, WHETHER IN WHOLE OR PART, IS EXPRESSLY PROHIBITED WITHOUT PRIOR WRITTEN CONSENT.
8. THE HYBRID STEEL FRAME CONSTRUCTION SYSTEM AND METHODOLOGY (PATENT PENDING) DESCRIBED IN THESE PLANS HAS BEEN DEVELOPED BY THE COMPANY AND IS SUBJECT TO A PROVISIONAL PATENT APPLICATION & ASSIGNMENT - US APPLICATION NO. 63/722,841

No.	Revision	Date

ISSUED FOR:

Issued for information

Issued for client approval

Issued for fabrication

Issued for construction

The Charlston

DRAWING TITLE:	Rear View
DRAWN BY:	Y.A.Clark
SCALE:	
DRAWING NO:	A103
DATE:	18/03/2026



1. THESE DRAWINGS MUST BE CHECKED BY THE CUSTOMER OR CONTRACTOR PRIOR TO APPROVAL. ANY ERRORS OR OMISSIONS MUST BE REPORTED IN WRITING TO BAUHU PRIOR TO COMMENCEMENT OF CONSTRUCTION.
2. ARCHITECTURAL DRAWINGS SHOULD BE READ IN CONJUNCTION WITH STRUCTURAL DETAILING AND FABRICATION GENERAL ASSEMBLY DRAWINGS.
3. FOR CONSTRUCTION PURPOSES, USE ONLY THE LATEST APPROVED DRAWINGS LABELED 'ISSUED FOR CONSTRUCTION'.
4. DO NOT SCALE FROM THIS DRAWING.
5. THE COMPANY OPERATES USING METRIC DIMENSIONS AS THE PRINCIPAL DENOMINATION.
6. ALL CONCRETE WORKS ARE OUTSIDE OF THE SCOPE OF THE COMPANY. INFORMATION REGARDING SLAB DESIGN AND CONNECTIONS IN THESE DRAWINGS ARE INTENDED FOR GUIDENCE ONLY. FOUNDATION AND SLAB WORKS SHOULD BE DESIGNED AND APPROVED BY A LOCAL STRUCTURAL ENGINEER.
7. THE COMPANY RETAINS FULL TITLE AND OWNERSHIP OF THESE PLANS AND DESIGNS. ANY UNAUTHORISED USE, REPRODUCTION, OR DISTRIBUTION OF THESE PLANS, WHETHER IN WHOLE OR PART, IS EXPRESSLY PROHIBITED WITHOUT PRIOR WRITTEN CONSENT.
8. THE HYBRID STEEL FRAME CONSTRUCTION SYSTEM AND METHODOLOGY (PATENT PENDING) DESCRIBED IN THESE PLANS HAS BEEN DEVELOPED BY THE COMPANY AND IS SUBJECT TO A PROVISIONAL PATENT APPLICATION & ASSIGNMENT - US APPLICATION NO. 63/722,841

No.	Revision	Date

ISSUED FOR:

Issued for information


Issued for client approval

Issued for fabrication

Issued for construction

The Charlston

DRAWING TITLE:	Building Axonometry
DRAWN BY:	Y.A.Clark
SCALE:	
DRAWING NO:	A104
DATE:	18/03/2026

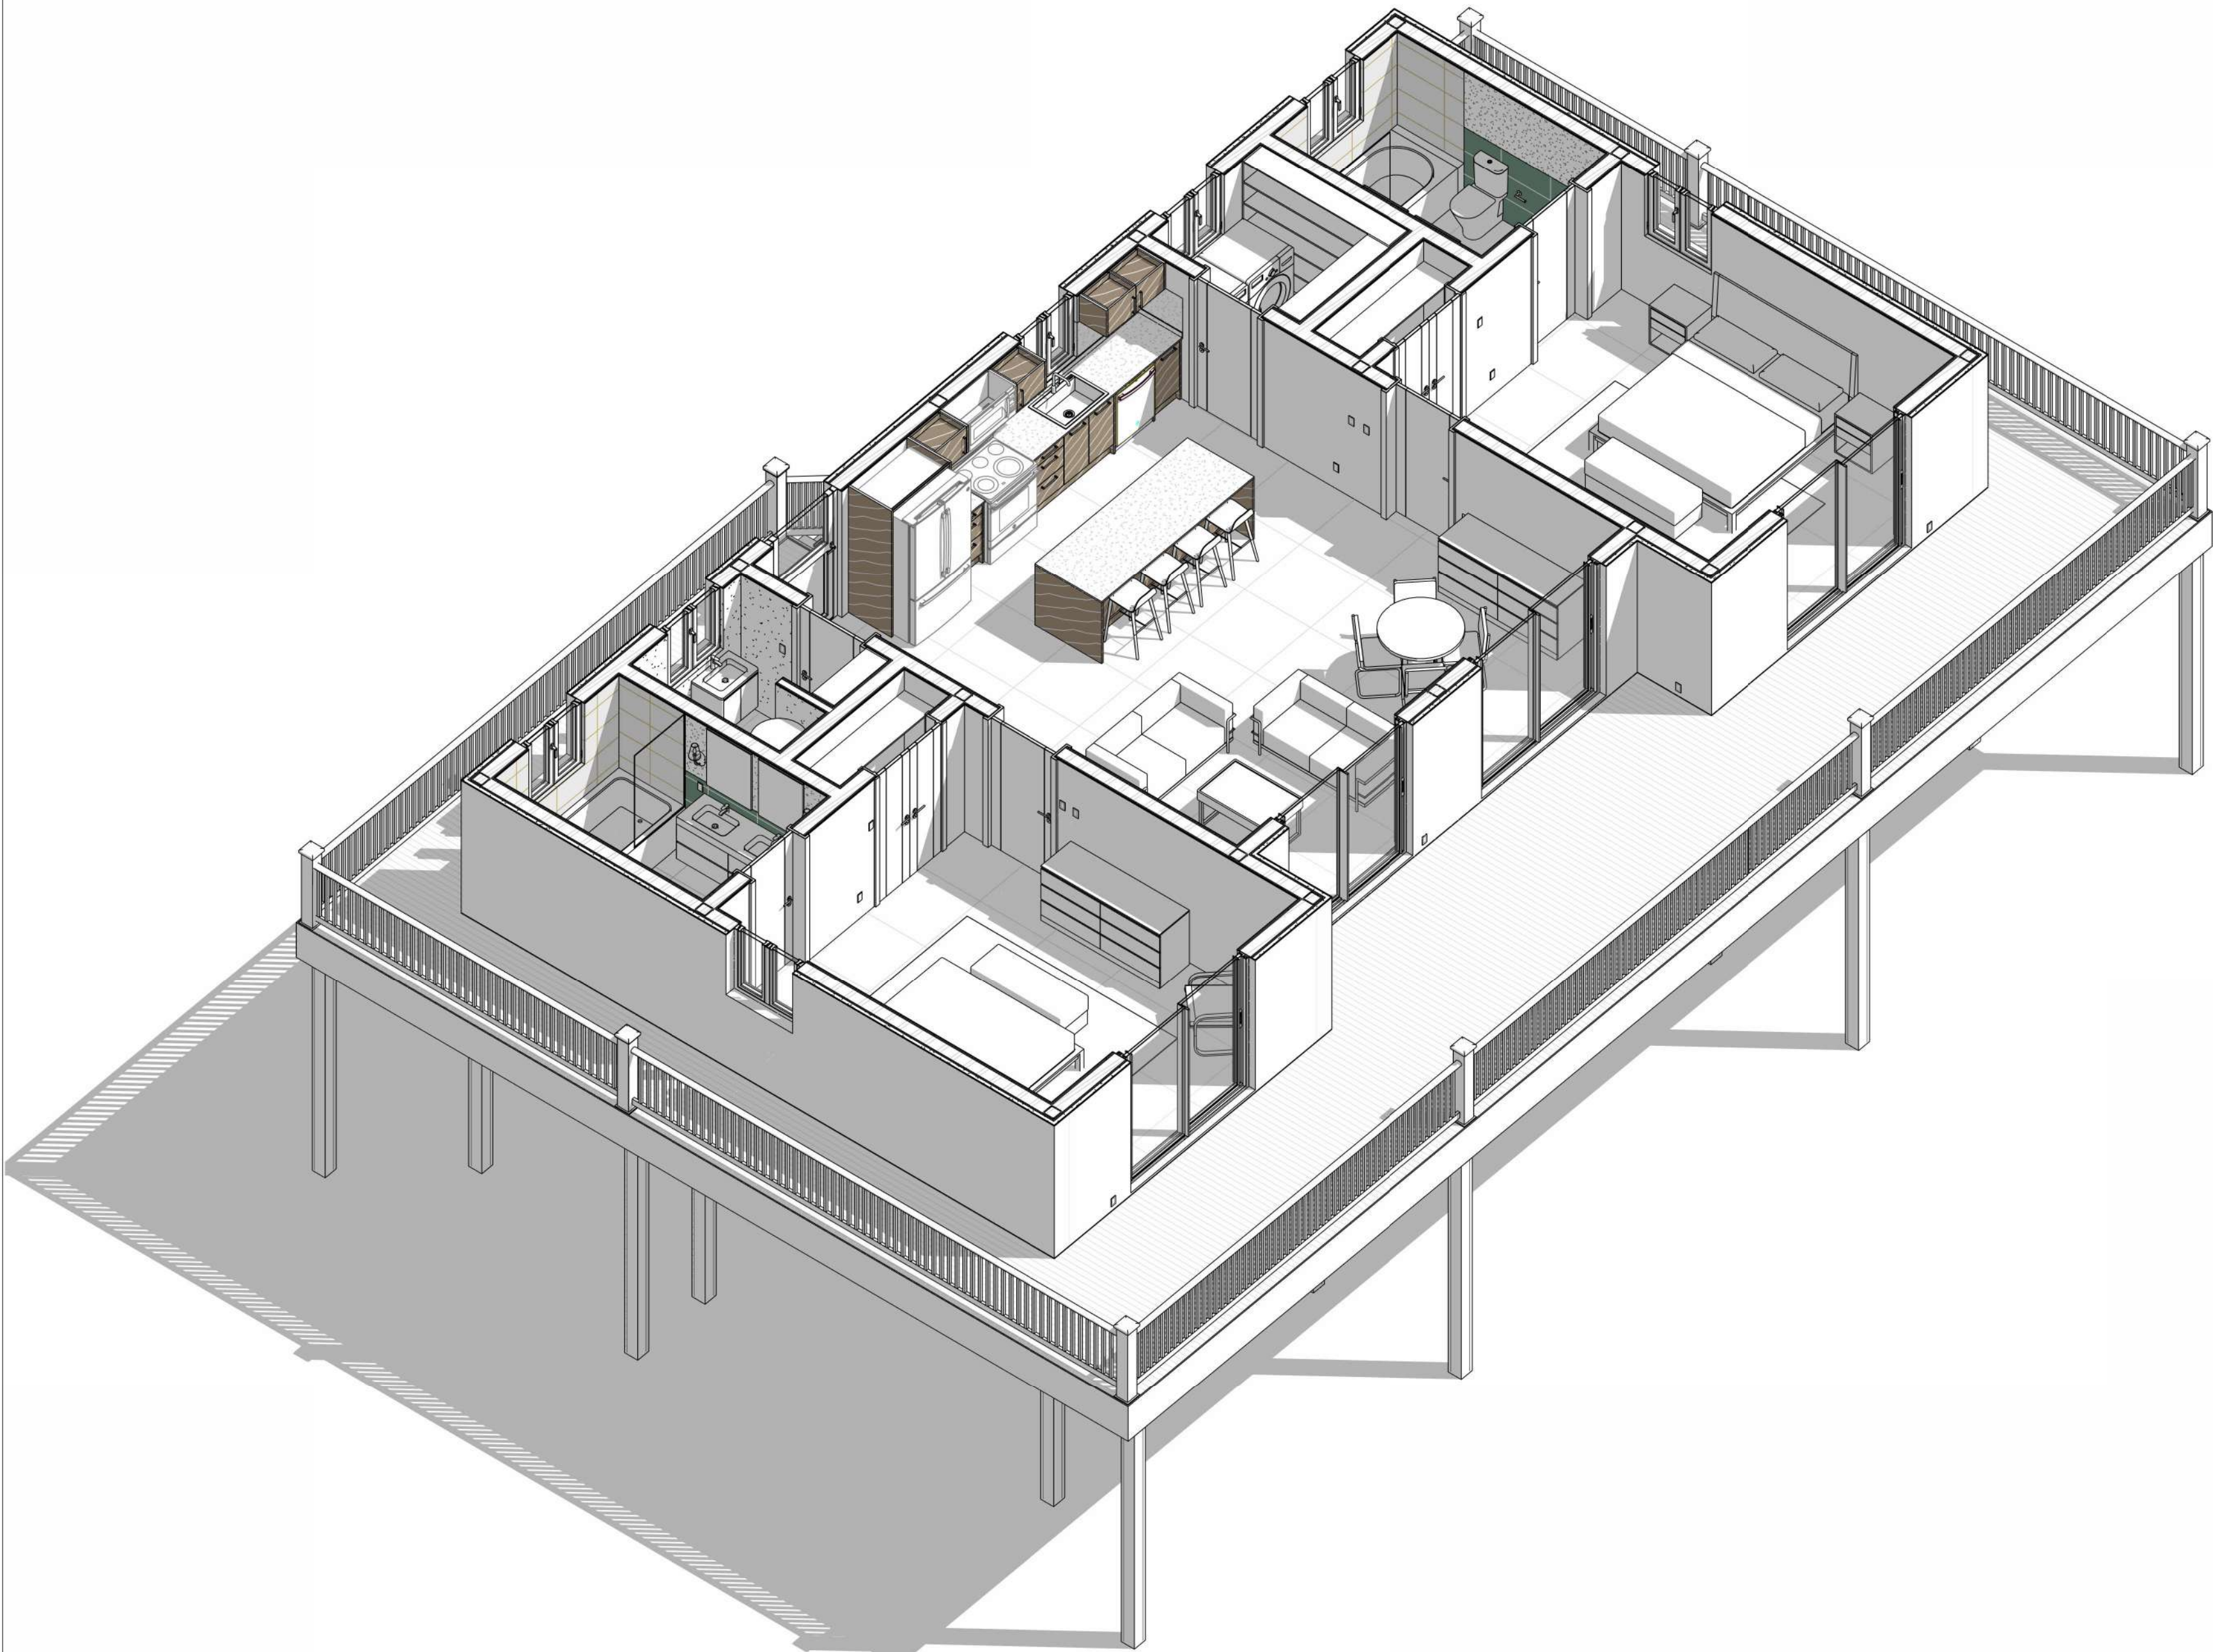

1. THESE DRAWINGS MUST BE CHECKED BY THE CUSTOMER OR CONTRACTOR PRIOR TO APPROVAL. ANY ERRORS OR OMISSIONS MUST BE REPORTED IN WRITING TO BAUHU PRIOR TO COMMENCEMENT OF CONSTRUCTION.
2. ARCHITECTURAL DRAWINGS SHOULD BE READ IN CONJUNCTION WITH STRUCTURAL DETAILING AND FABRICATION GENERAL ASSEMBLY DRAWINGS.
3. FOR CONSTRUCTION PURPOSES, USE ONLY THE LATEST APPROVED DRAWINGS LABELED 'ISSUED FOR CONSTRUCTION'.
4. DO NOT SCALE FROM THIS DRAWING.
5. THE COMPANY OPERATES USING METRIC DIMENSIONS AS THE PRINCIPAL DENOMINATION.
6. ALL CONCRETE WORKS ARE OUTSIDE OF THE SCOPE OF THE COMPANY. INFORMATION REGARDING SLAB DESIGN AND CONNECTIONS IN THESE DRAWINGS ARE INTENDED FOR GUIDENCE ONLY. FOUNDATION AND SLAB WORKS SHOULD BE DESIGNED AND APPROVED BY A LOCAL STRUCTURAL ENGINEER.
7. THE COMPANY RETAINS FULL TITLE AND OWNERSHIP OF THESE PLANS AND DESIGNS. ANY UNAUTHORISED USE, REPRODUCTION, OR DISTRIBUTION OF THESE PLANS, WHETHER IN WHOLE OR PART, IS EXPRESSLY PROHIBITED WITHOUT PRIOR WRITTEN CONSENT.
8. THE HYBRID STEEL FRAME CONSTRUCTION SYSTEM AND METHODOLOGY (PATENT PENDING) DESCRIBED IN THESE PLANS HAS BEEN DEVELOPED BY THE COMPANY AND IS SUBJECT TO A PROVISIONAL PATENT APPLICATION & ASSIGNMENT - US APPLICATION NO. 63/722,841

No.	Revision	Date

ISSUED FOR:

Issued for information

Issued for client approval

Issued for fabrication

Issued for construction

The Charlston

DRAWING TITLE:

Floor Plan Axonometry

DRAWN BY:

Y.A.Clark

SCALE:

DRAWING NO:

A105

DATE:

18/03/2026

1. THESE DRAWINGS MUST BE CHECKED BY THE CUSTOMER OR CONTRACTOR PRIOR TO APPROVAL. ANY ERRORS OR OMISSIONS MUST BE REPORTED IN WRITING TO BAUHU PRIOR TO COMMENCEMENT OF CONSTRUCTION.
2. ARCHITECTURAL DRAWINGS SHOULD BE READ IN CONJUNCTION WITH STRUCTURAL DETAILING AND FABRICATION GENERAL ASSEMBLY DRAWINGS.
3. FOR CONSTRUCTION PURPOSES, USE ONLY THE LATEST APPROVED DRAWINGS LABELED 'ISSUED FOR CONSTRUCTION'.
4. DO NOT SCALE FROM THIS DRAWING.
5. THE COMPANY OPERATES USING METRIC DIMENSIONS AS THE PRINCIPAL DENOMINATION.
6. ALL CONCRETE WORKS ARE OUTSIDE OF THE SCOPE OF THE COMPANY. INFORMATION REGARDING SLAB DESIGN AND CONNECTIONS IN THESE DRAWINGS ARE INTENDED FOR GUIDENCE ONLY. FOUNDATION AND SLAB WORKS SHOULD BE DESIGNED AND APPROVED BY A LOCAL STRUCTURAL ENGINEER.
7. THE COMPANY RETAINS FULL TITLE AND OWNERSHIP OF THESE PLANS AND DESIGNS. ANY UNAUTHORISED USE, REPRODUCTION, OR DISTRIBUTION OF THESE PLANS, WHETHER IN WHOLE OR PART, IS EXPRESSLY PROHIBITED WITHOUT PRIOR WRITTEN CONSENT.
8. THE HYBRID STEEL FRAME CONSTRUCTION SYSTEM AND METHODOLOGY (PATENT PENDING) DESCRIBED IN THESE PLANS HAS BEEN DEVELOPED BY THE COMPANY AND IS SUBJECT TO A PROVISIONAL PATENT APPLICATION & ASSIGNMENT - US APPLICATION NO. 63/722,841

No.	Revision	Date

ISSUED FOR:

Issued for information

Issued for client approval

Issued for fabrication

Issued for construction

The Charlston

DRAWING TITLE:

Roof Plan

DRAWN BY:

Y.A.Clark

SCALE:


1 : 50


DRAWING NO:

A107

DATE:

18/03/2026

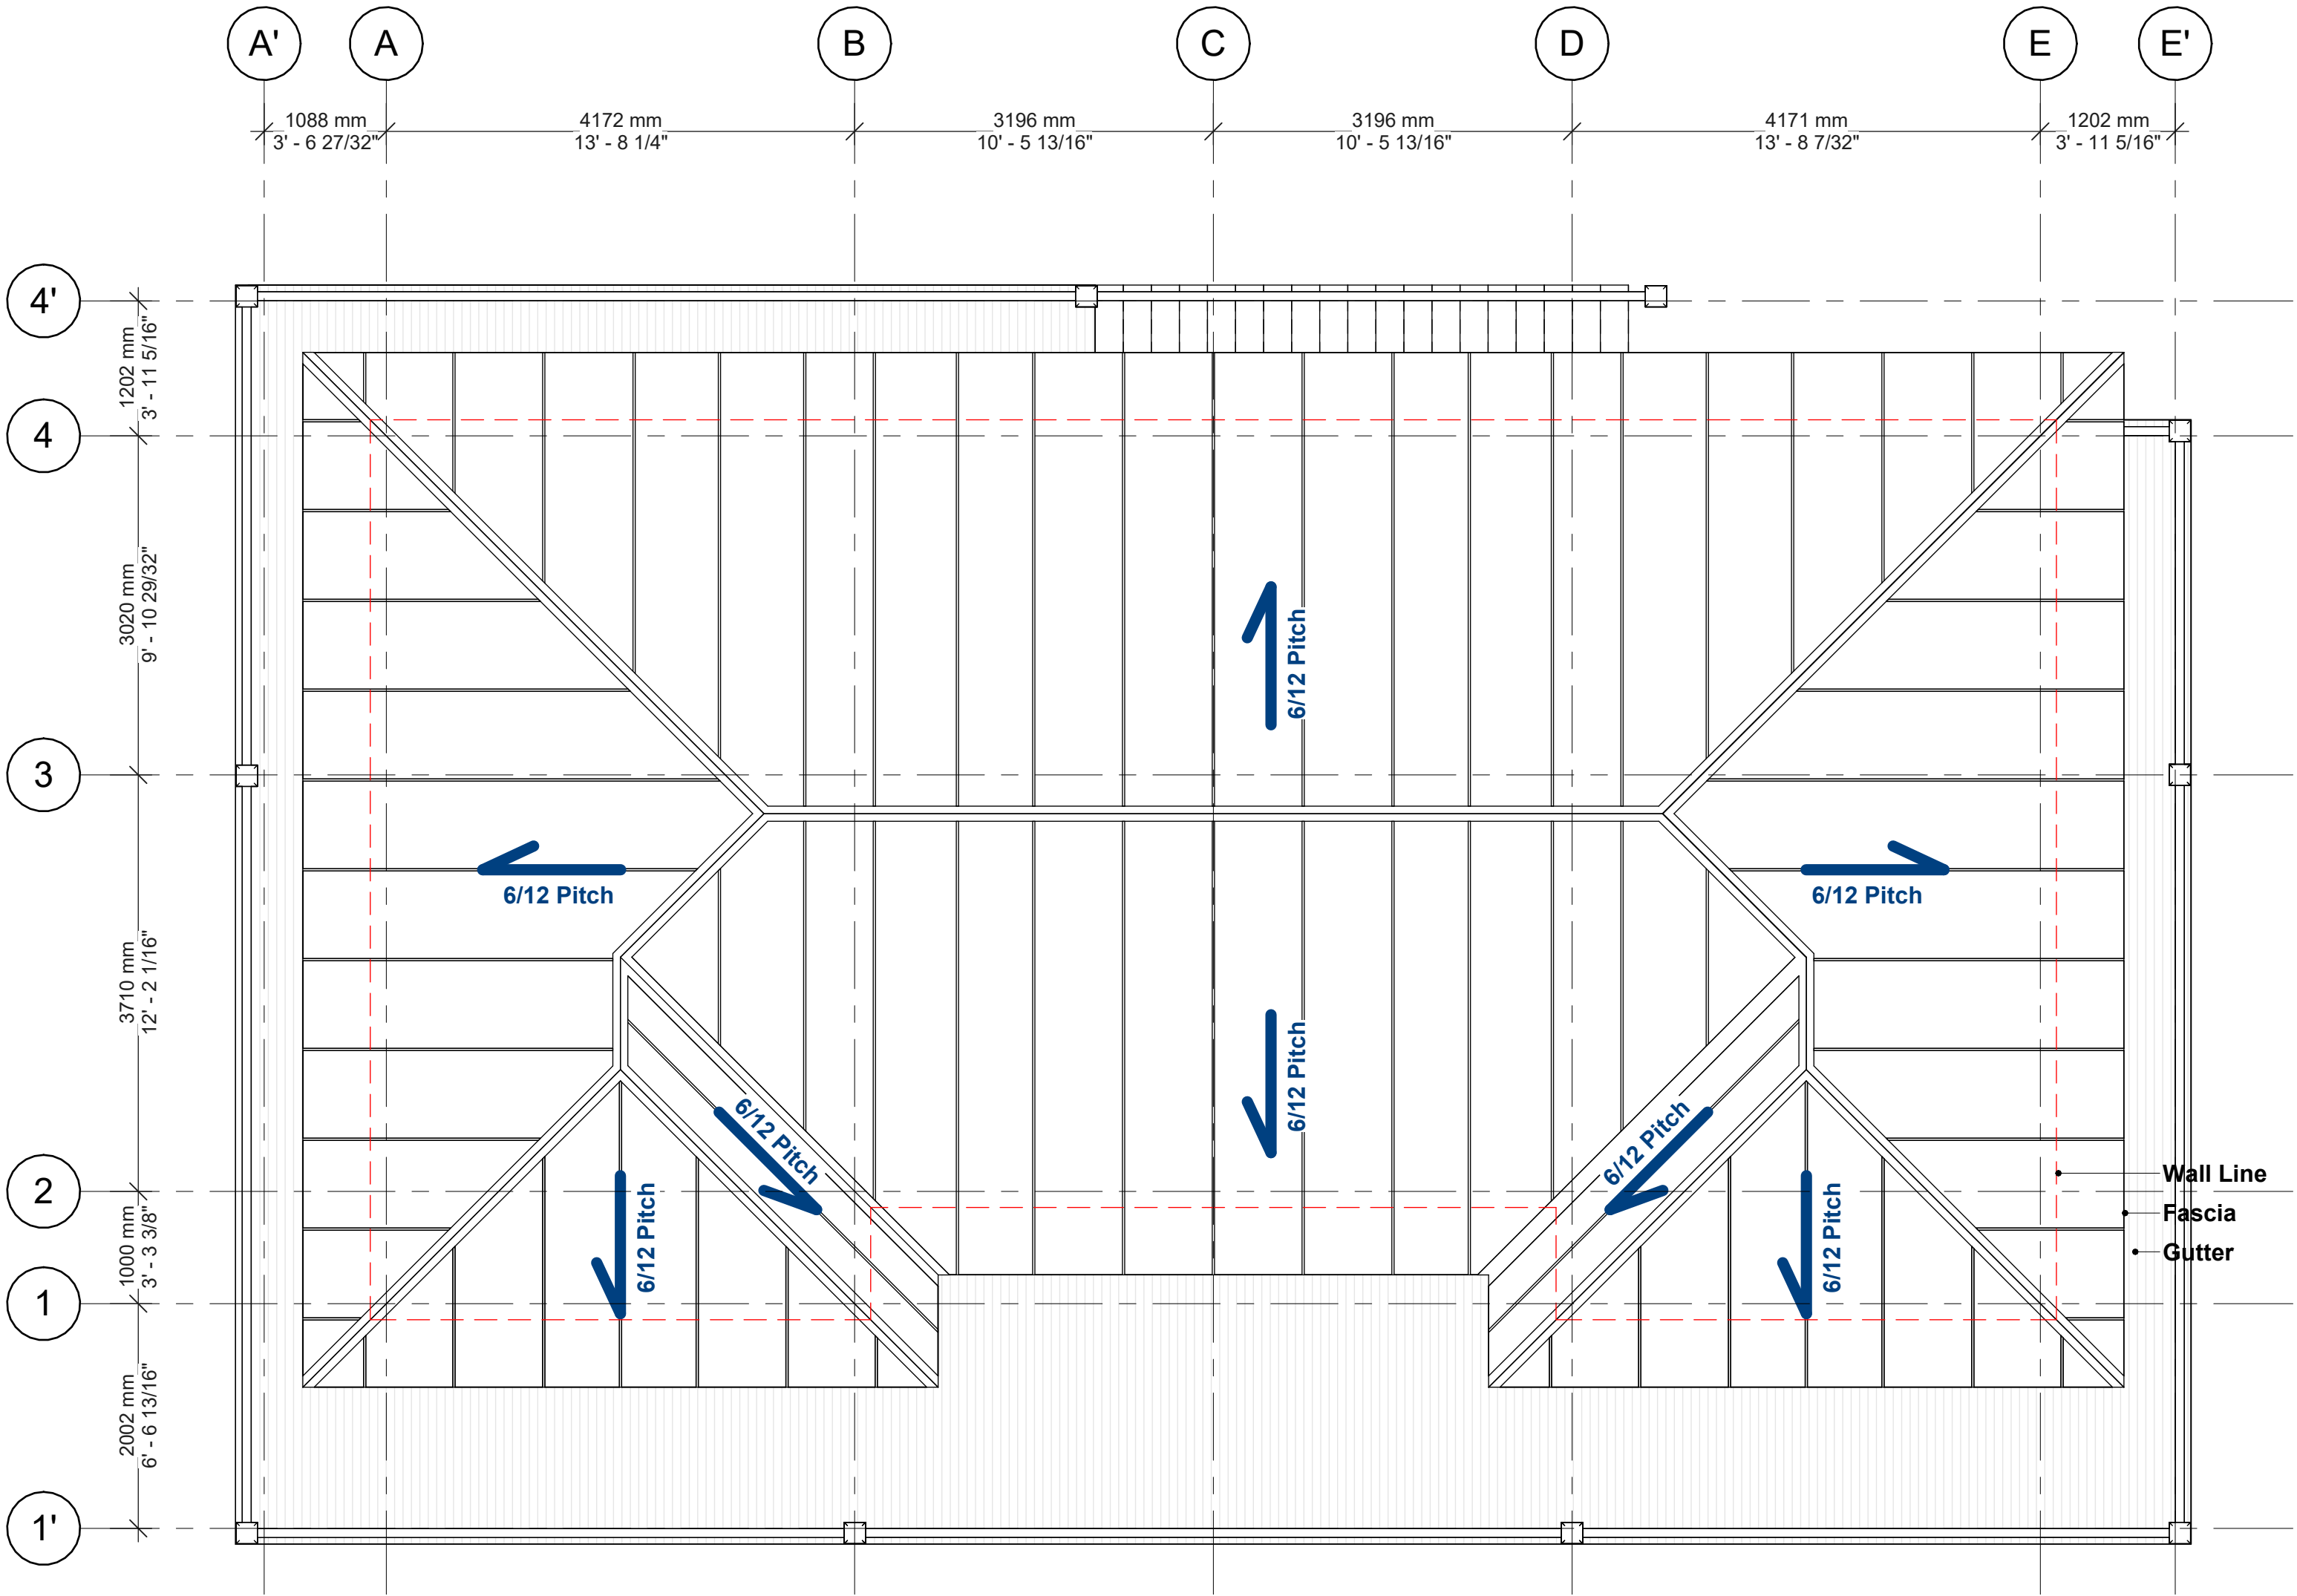

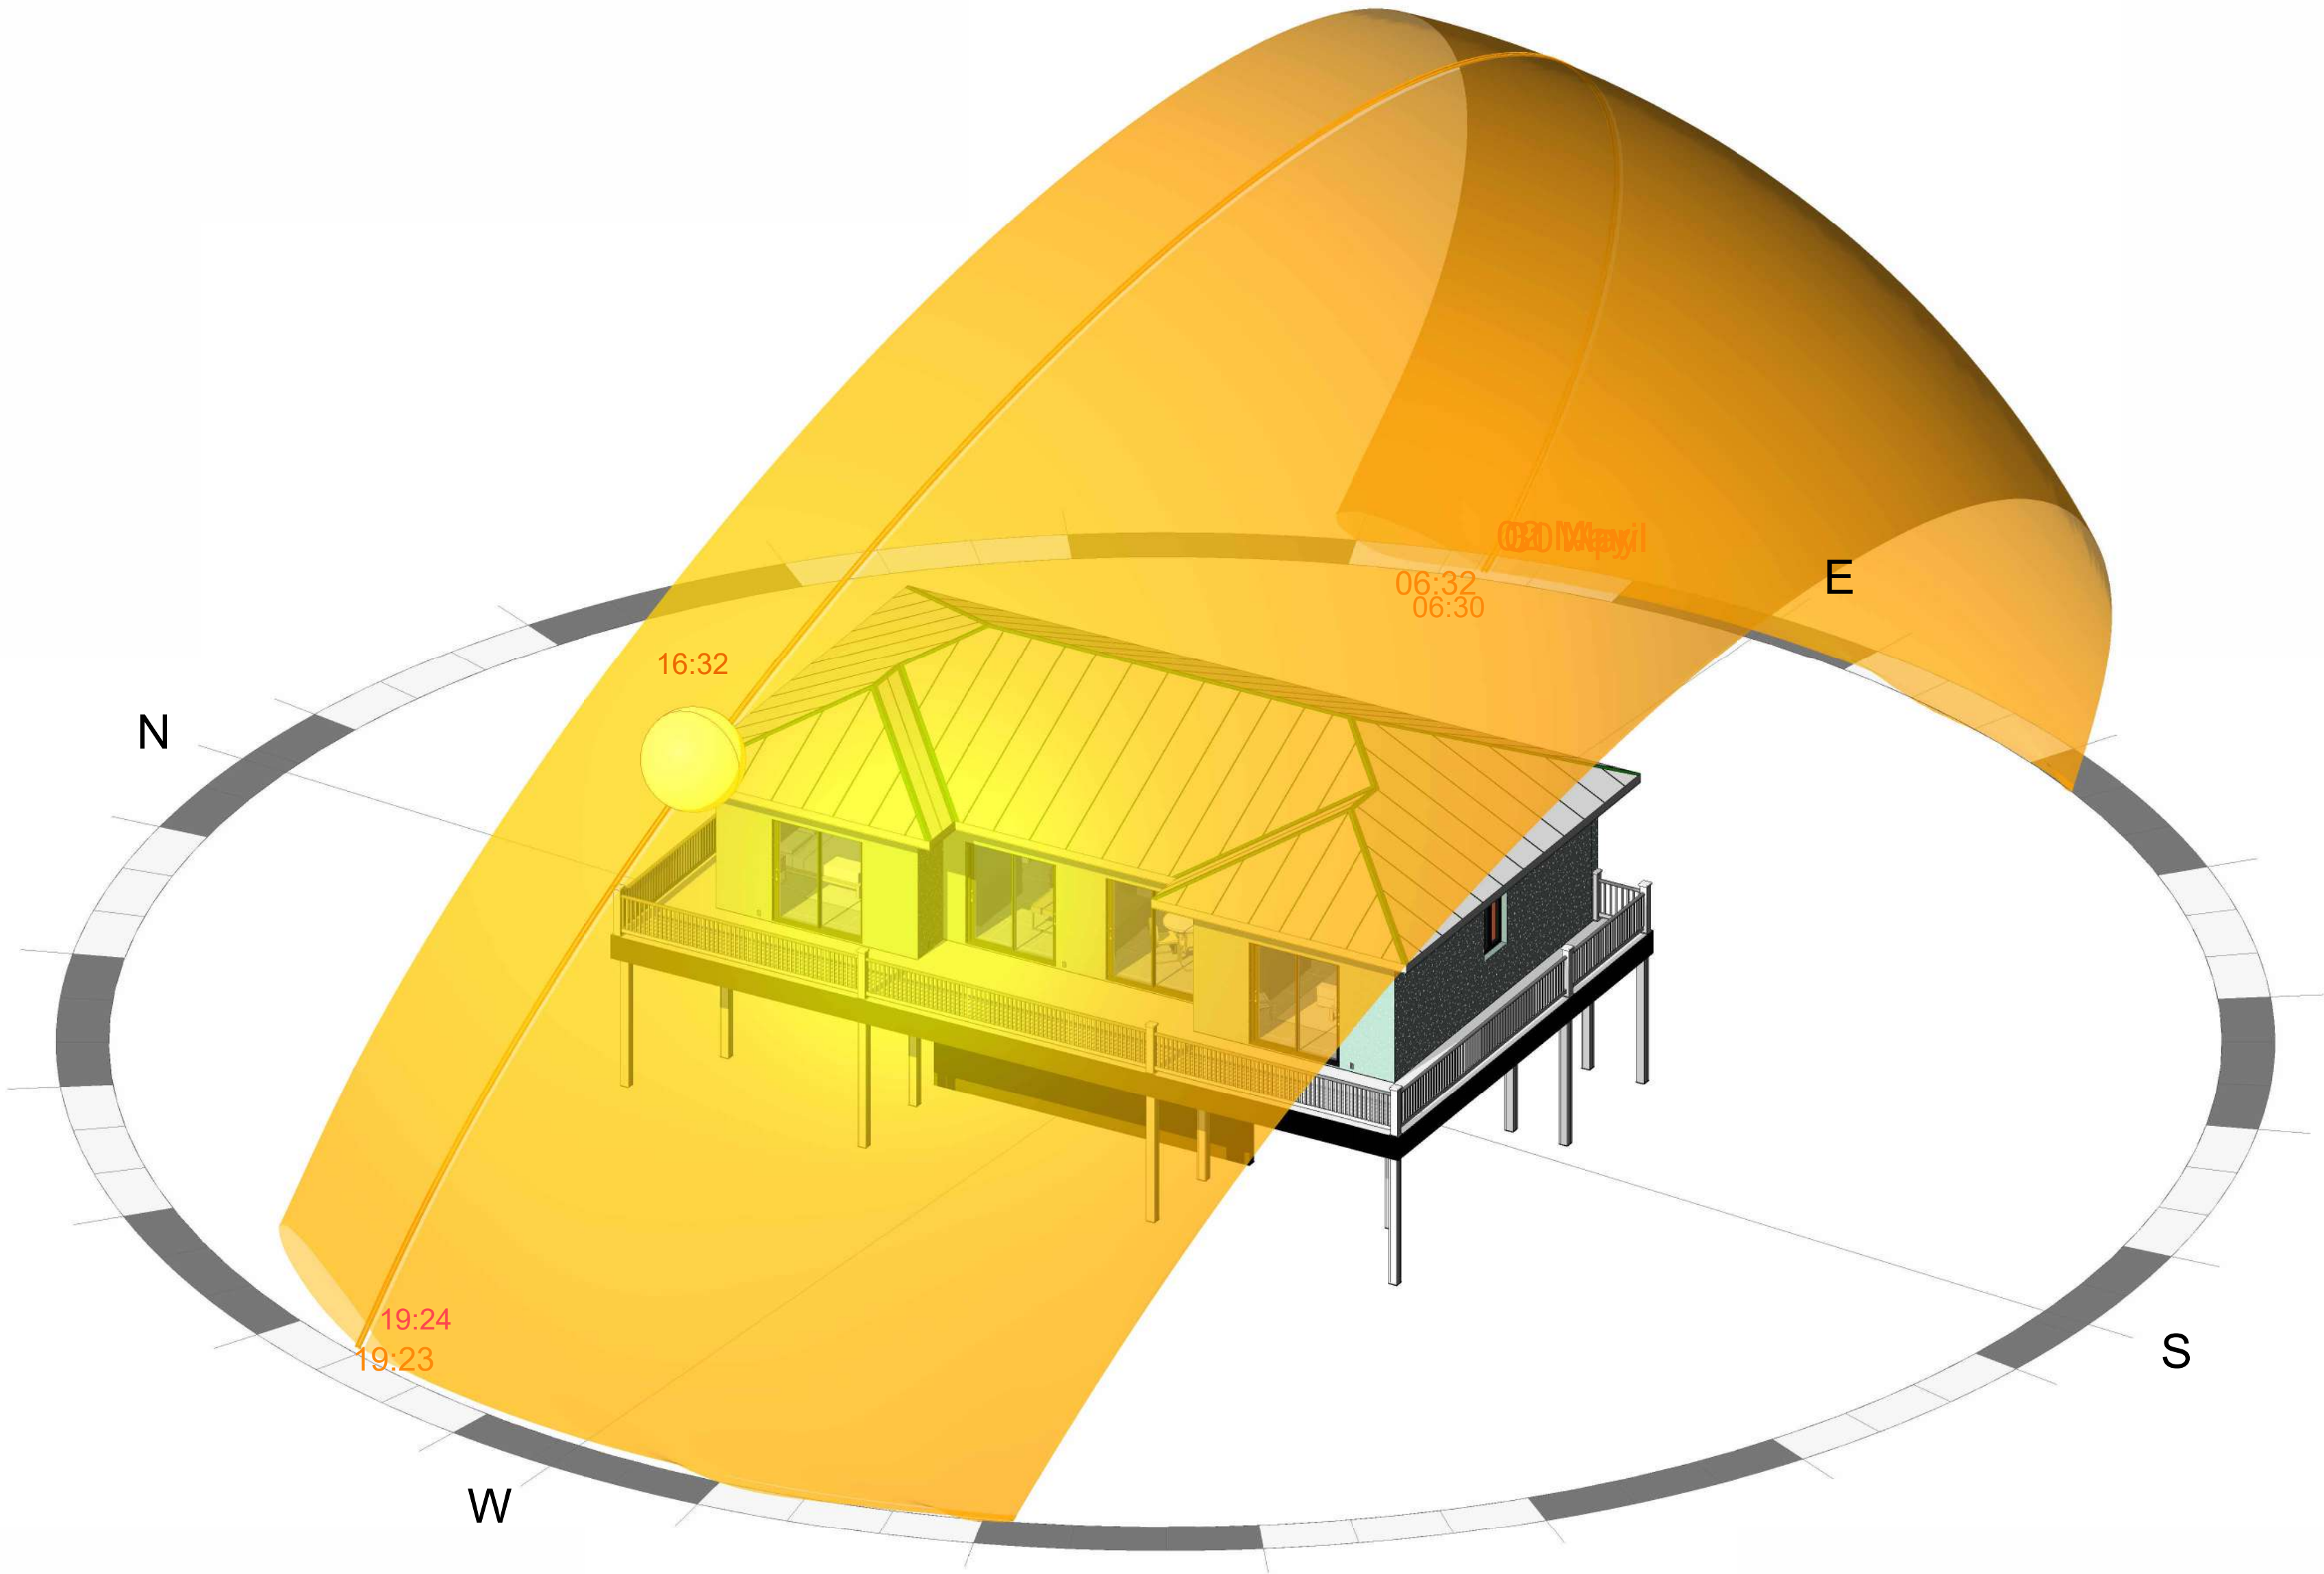

1. THESE DRAWINGS MUST BE CHECKED BY THE CUSTOMER OR CONTRACTOR PRIOR TO APPROVAL. ANY ERRORS OR OMISSIONS MUST BE REPORTED IN WRITING TO BAUHU PRIOR TO COMMENCEMENT OF CONSTRUCTION.
2. ARCHITECTURAL DRAWINGS SHOULD BE READ IN CONJUNCTION WITH STRUCTURAL DETAILING AND FABRICATION GENERAL ASSEMBLY DRAWINGS.
3. FOR CONSTRUCTION PURPOSES, USE ONLY THE LATEST APPROVED DRAWINGS LABELED 'ISSUED FOR CONSTRUCTION'.
4. DO NOT SCALE FROM THIS DRAWING.
5. THE COMPANY OPERATES USING METRIC DIMENSIONS AS THE PRINCIPAL DENOMINATION.
6. ALL CONCRETE WORKS ARE OUTSIDE OF THE SCOPE OF THE COMPANY. INFORMATION REGARDING SLAB DESIGN AND CONNECTIONS IN THESE DRAWINGS ARE INTENDED FOR GUIDENCE ONLY. FOUNDATION AND SLAB WORKS SHOULD BE DESIGNED AND APPROVED BY A LOCAL STRUCTURAL ENGINEER.
7. THE COMPANY RETAINS FULL TITLE AND OWNERSHIP OF THESE PLANS AND DESIGNS. ANY UNAUTHORISED USE, REPRODUCTION, OR DISTRIBUTION OF THESE PLANS, WHETHER IN WHOLE OR PART, IS EXPRESSLY PROHIBITED WITHOUT PRIOR WRITTEN CONSENT.
8. THE HYBRID STEEL FRAME CONSTRUCTION SYSTEM AND METHODOLOGY (PATENT PENDING) DESCRIBED IN THESE PLANS HAS BEEN DEVELOPED BY THE COMPANY AND IS SUBJECT TO A PROVISIONAL PATENT APPLICATION & ASSIGNMENT - US APPLICATION NO. 63/722,841

No.	Revision	Date

ISSUED FOR:

Issued for information

Issued for client approval

Issued for fabrication

Issued for construction

The Charlston

DRAWING TITLE:

Sun Analysis

DRAWN BY:

Y.A.Clark


SCALE:

DRAWING NO:

A108


DATE:

18/03/2026

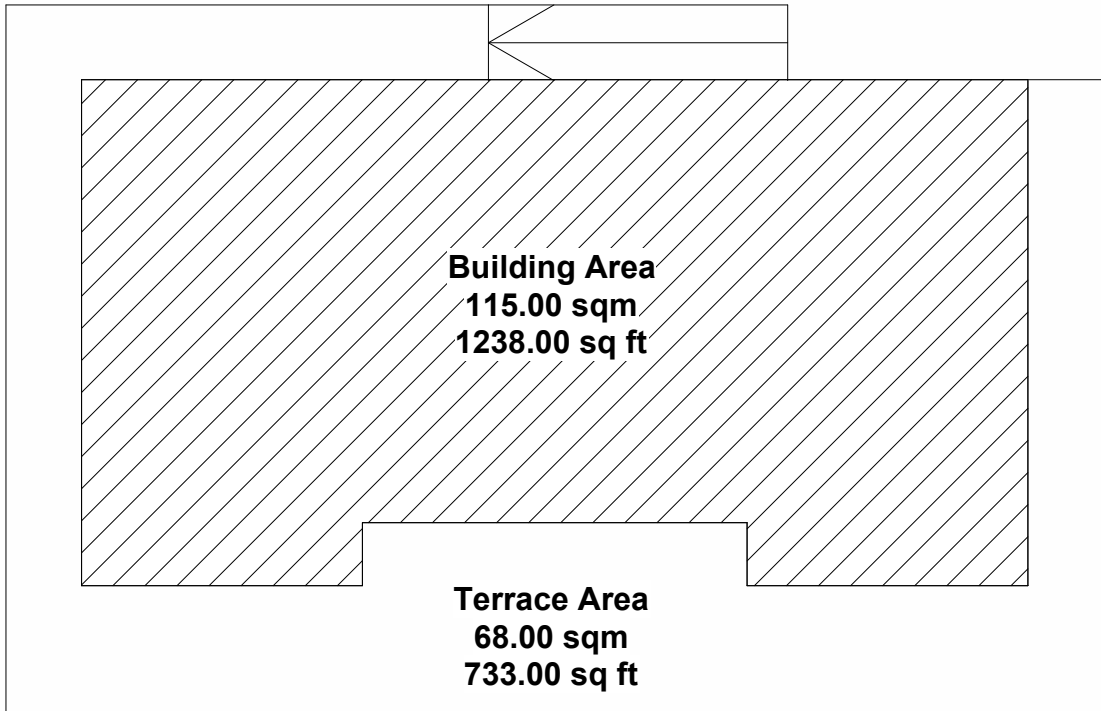

Room Schedule			
No.	Room Name	Sq. Meter	Sq. Feet
1	Bathroom 1	6 m ²	60.64 ft ²
2	Bedroom 1	18 m ²	192.44 ft ²
3	Closet 1	1 m ²	11.57 ft ²
4	Powder Room	3 m ²	37.10 ft ²
5	Living Area	40 m ²	434.63 ft ²
6	Pantry	4 m ²	38.00 ft ²
7	Closet 2	1 m ²	11.57 ft ²
8	Bathroom 2	6 m ²	60.62 ft ²
9	Bedroom 2	18 m ²	192.41 ft ²
10	Exterior Terrace	68 m ²	733.02 ft ²
Grand total		165 m ²	1772.00 ft ²

- THESE DRAWINGS MUST BE CHECKED BY THE CUSTOMER OR CONTRACTOR PRIOR TO APPROVAL. ANY ERRORS OR OMISSIONS MUST BE REPORTED IN WRITING TO BAUHU PRIOR TO COMMENCEMENT OF CONSTRUCTION.
- ARCHITECTURAL DRAWINGS SHOULD BE READ IN CONJUNCTION WITH STRUCTURAL DETAILING AND FABRICATION GENERAL ASSEMBLY DRAWINGS.
- FOR CONSTRUCTION PURPOSES, USE ONLY THE LATEST APPROVED DRAWINGS LABELED 'ISSUED FOR CONSTRUCTION'.
- DO NOT SCALE FROM THIS DRAWING.
- THE COMPANY OPERATES USING METRIC DIMENSIONS AS THE PRINCIPAL DENOMINATION.
- ALL CONCRETE WORKS ARE OUTSIDE OF THE SCOPE OF THE COMPANY. INFORMATION REGARDING SLAB DESIGN AND CONNECTIONS IN THESE DRAWINGS ARE INTENDED FOR GUIDANCE ONLY. FOUNDATION AND SLAB WORKS SHOULD BE DESIGNED AND APPROVED BY A LOCAL STRUCTURAL ENGINEER.
- THE COMPANY RETAINS FULL TITLE AND OWNERSHIP OF THESE PLANS AND DESIGNS. ANY UNAUTHORISED USE, REPRODUCTION, OR DISTRIBUTION OF THESE PLANS, WHETHER IN WHOLE OR PART, IS EXPRESSLY PROHIBITED WITHOUT PRIOR WRITTEN CONSENT.
- THE HYBRID STEEL FRAME CONSTRUCTION SYSTEM AND METHODOLOGY (PATENT PENDING) DESCRIBED IN THESE PLANS HAS BEEN DEVELOPED BY THE COMPANY AND IS SUBJECT TO A PROVISIONAL PATENT APPLICATION & ASSIGNMENT - US APPLICATION NO. 63/722,841

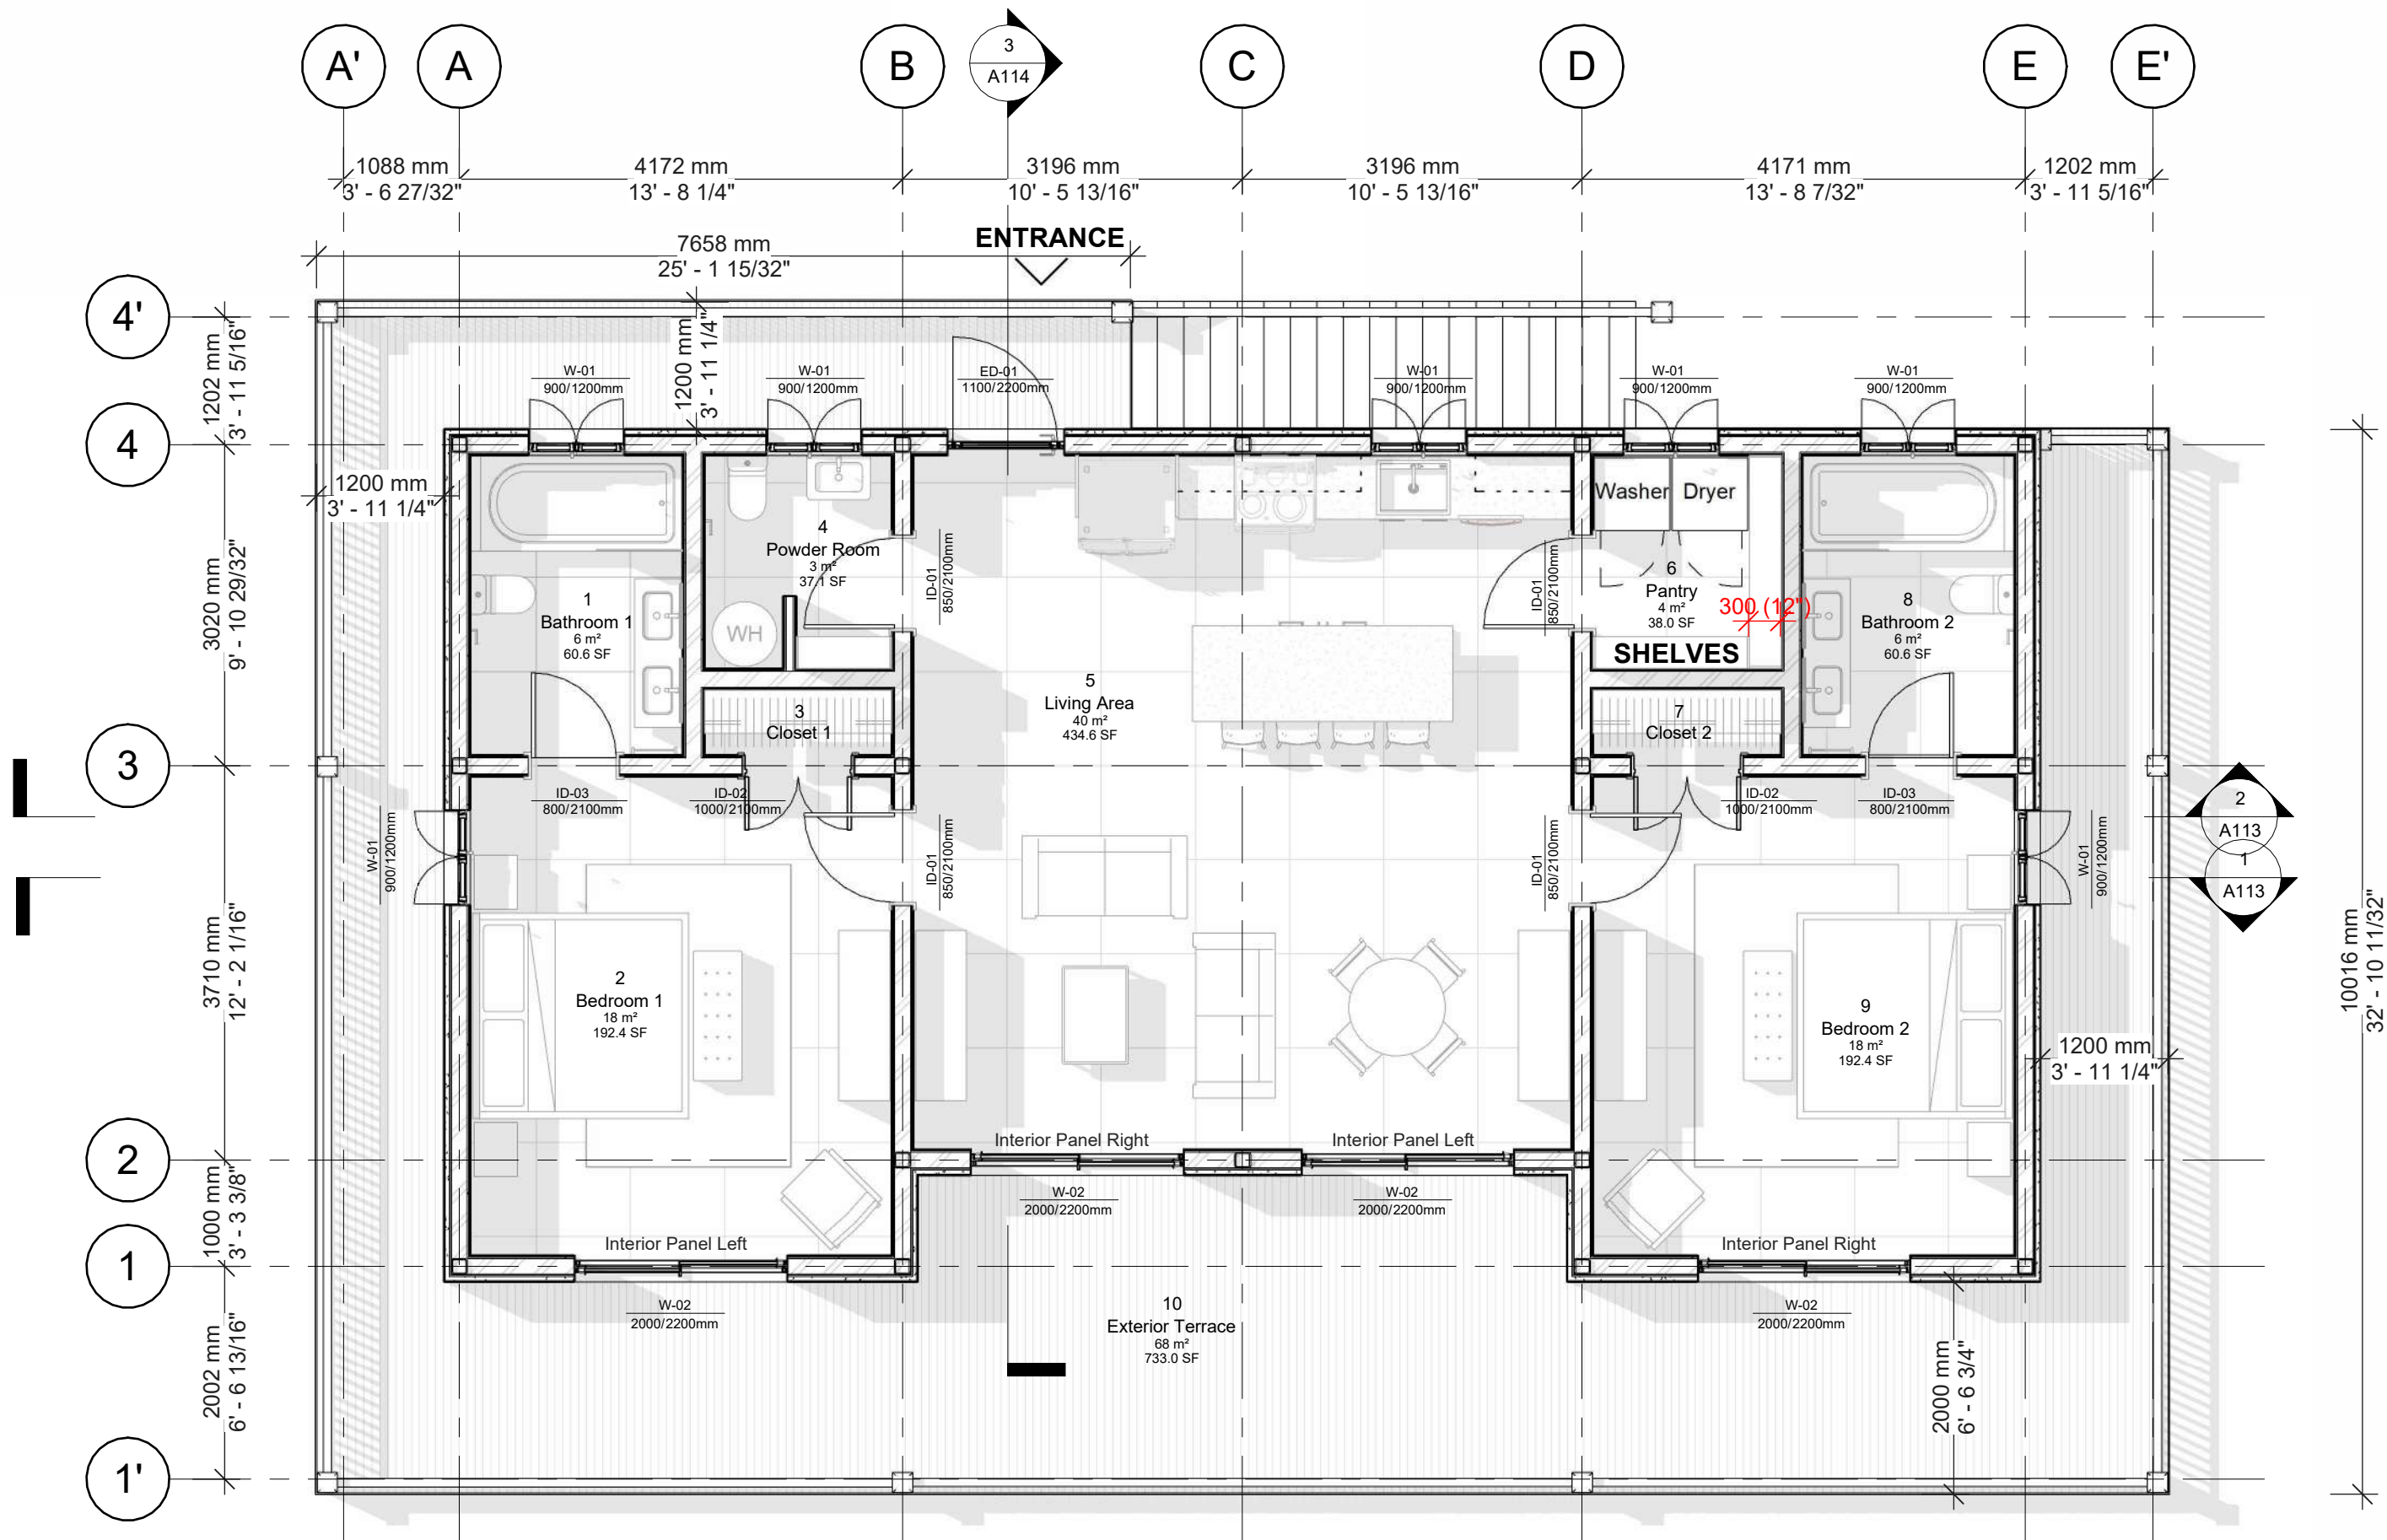

- Note:**
- Freestanding furniture and equipment are shown for illustrative purposes only. Renderings and reference images are for guidance only.
 - Artisanal timber and carpentry requirements such as fretwork, architectural timber finishes, baseboards, decorative railings, deck and pergola structures, shade louvres, interior stairs and hand railing are to be provided by others.
 - Railings and balustrades will be provided by others. Drawings are made for design purposes only. Refer to structural design drawings for post fixing dimensions.
 - External HRS columns will be provided assuming a 50mm (2") height drop between interior concrete slab and exterior terrace concrete slab unless site conditions dictate otherwise.
 - Final exterior slab height to be determined by the contractor. Internal floor screed and waterproofing membrane is to be supplied by the contractor.
 - Contractors should ensure a correct fall is applied to external tiled terrace areas to facilitate rainwater drainage.
 - Contractors should read these drawings in conjunction with structural engineering design drawings.

No.	Revision	Date

ISSUED FOR:

☐ Issued for information

☐ Issued for client approval

☐ Issued for fabrication

☐ Issued for construction

The Charlston

DRAWING TITLE:	Ground Floor Plan
DRAWN BY:	Y.A.Clark
SCALE:	As indicated
DRAWING NO:	A109
DATE:	18/03/2026

1. THESE DRAWINGS MUST BE CHECKED BY THE CUSTOMER OR CONTRACTOR PRIOR TO APPROVAL. ANY ERRORS OR OMISSIONS MUST BE REPORTED IN WRITING TO BAUHU PRIOR TO COMMENCEMENT OF CONSTRUCTION.
2. ARCHITECTURAL DRAWINGS SHOULD BE READ IN CONJUNCTION WITH STRUCTURAL DETAILING AND FABRICATION GENERAL ASSEMBLY DRAWINGS.
3. FOR CONSTRUCTION PURPOSES, USE ONLY THE LATEST APPROVED DRAWINGS LABELED 'ISSUED FOR CONSTRUCTION'.
4. DO NOT SCALE FROM THIS DRAWING.
5. THE COMPANY OPERATES USING METRIC DIMENSIONS AS THE PRINCIPAL DENOMINATION.
6. ALL CONCRETE WORKS ARE OUTSIDE OF THE SCOPE OF THE COMPANY. INFORMATION REGARDING SLAB DESIGN AND CONNECTIONS IN THESE DRAWINGS ARE INTENDED FOR GUIDANCE ONLY. FOUNDATION AND SLAB WORKS SHOULD BE DESIGNED AND APPROVED BY A LOCAL STRUCTURAL ENGINEER.
7. THE COMPANY RETAINS FULL TITLE AND OWNERSHIP OF THESE PLANS AND DESIGNS. ANY UNAUTHORISED USE, REPRODUCTION, OR DISTRIBUTION OF THESE PLANS, WHETHER IN WHOLE OR PART, IS EXPRESSLY PROHIBITED WITHOUT PRIOR WRITTEN CONSENT.
8. THE HYBRID STEEL FRAME CONSTRUCTION SYSTEM AND METHODOLOGY (PATENT PENDING) DESCRIBED IN THESE PLANS HAS BEEN DEVELOPED BY THE COMPANY AND IS SUBJECT TO A PROVISIONAL PATENT APPLICATION & ASSIGNMENT - US APPLICATION NO. 63/722,841

No.	Revision	Date

ISSUED FOR:

Issued for information

Issued for client approval

Issued for fabrication

Issued for construction

The Charlston

DRAWING TITLE:

Site Level Floor Plan - Parking

DRAWN BY:

Y.A.Clark

SCALE:


1 : 60

DRAWING NO:

A110

DATE:

18/03/2026

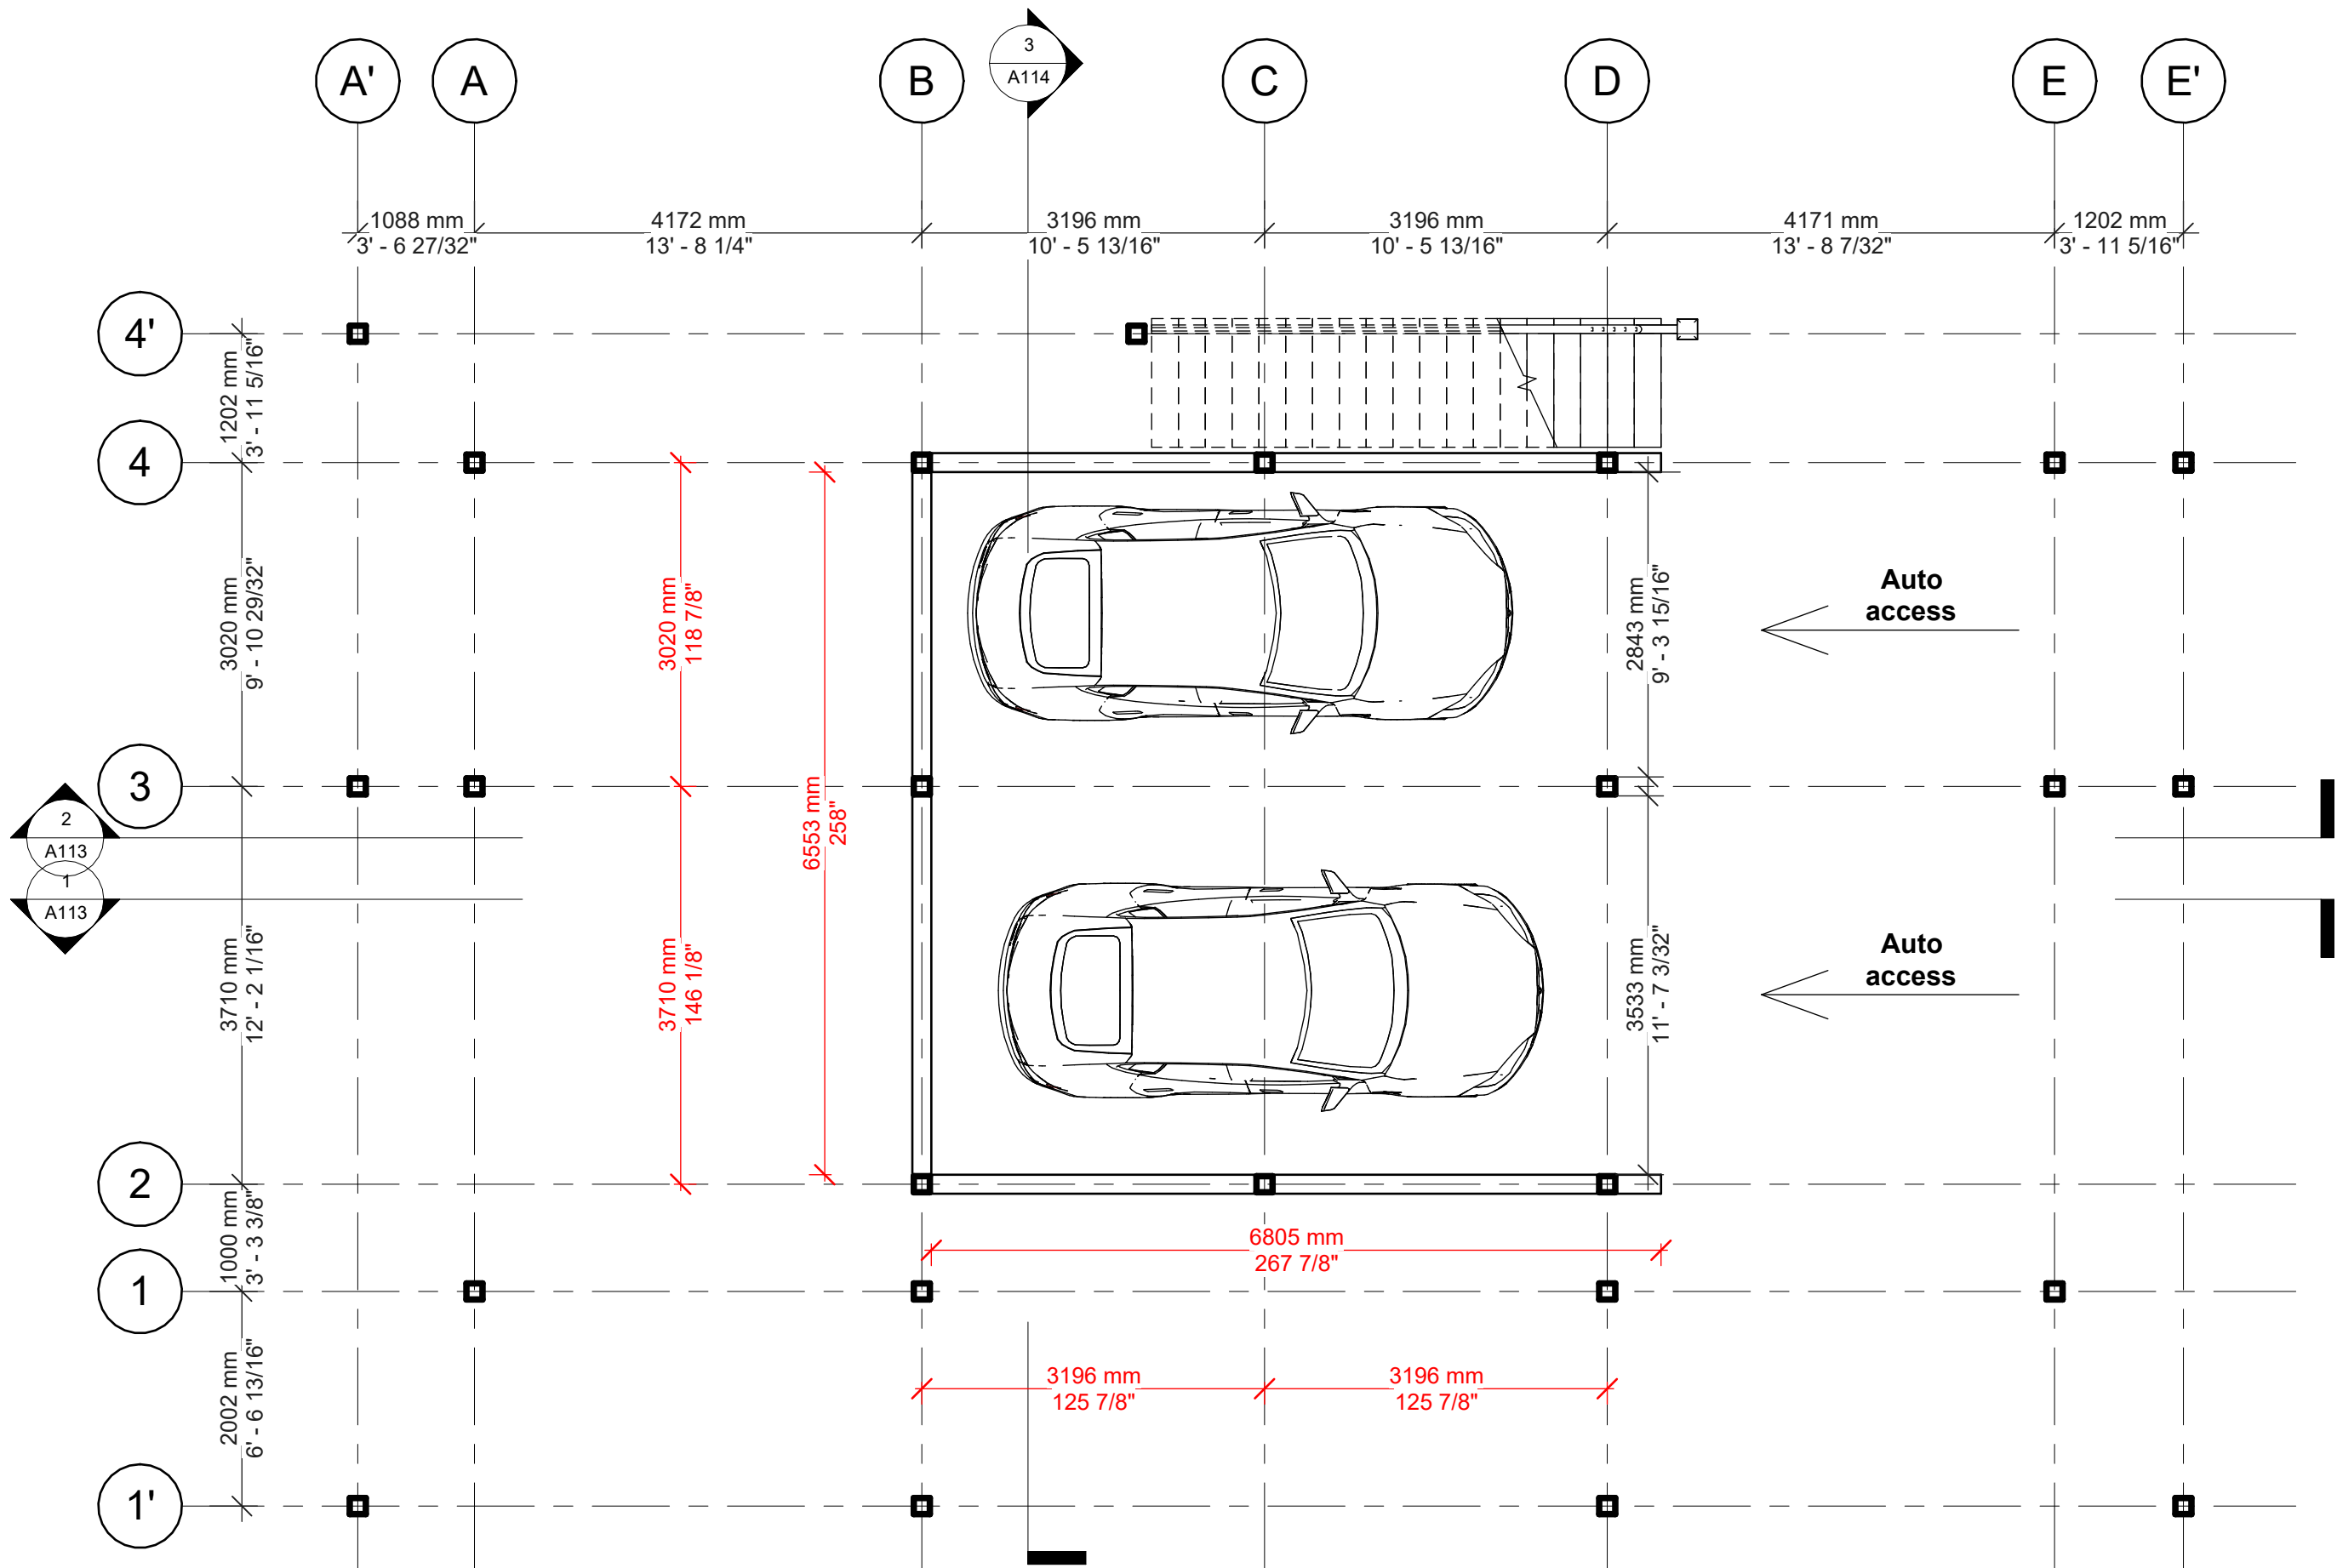

- Note:**
- Freestanding furniture and equipment are shown for illustrative purposes only. Renderings and reference images are for guidance only.
 - Artisanal timber and carpentry requirements such as fretwork, architectural timber finishes, baseboards, decorative railings, deck and pergola structures, shade louvres, interior stairs and hand railing are to be provided by others.
 - Railings and balustrades will be provided by others. Drawings are made for design purposes only. Refer to structural design drawings for post fixing dimensions.
 - External HRS columns will be provided assuming a 50mm (2") height drop between interior concrete slab and exterior terrace concrete slab unless site conditions dictate otherwise.
 - Final exterior slab height to be determined by the contractor. Internal floor screed and waterproofing membrane is to be supplied by the contractor.
 - Contractors should ensure a correct fall is applied to external tiled terrace areas to facilitate rainwater drainage.
 - Contractors should read these drawings in conjunction with structural engineering design drawings.

1. THESE DRAWINGS MUST BE CHECKED BY THE CUSTOMER OR CONTRACTOR PRIOR TO APPROVAL. ANY ERRORS OR OMISSIONS MUST BE REPORTED IN WRITING TO BAUHU PRIOR TO COMMENCEMENT OF CONSTRUCTION.
2. ARCHITECTURAL DRAWINGS SHOULD BE READ IN CONJUNCTION WITH STRUCTURAL DETAILING AND FABRICATION GENERAL ASSEMBLY DRAWINGS.
3. FOR CONSTRUCTION PURPOSES, USE ONLY THE LATEST APPROVED DRAWINGS LABELED 'ISSUED FOR CONSTRUCTION'.
4. DO NOT SCALE FROM THIS DRAWING.
5. THE COMPANY OPERATES USING METRIC DIMENSIONS AS THE PRINCIPAL DENOMINATION.
6. ALL CONCRETE WORKS ARE OUTSIDE OF THE SCOPE OF THE COMPANY. INFORMATION REGARDING SLAB DESIGN AND CONNECTIONS IN THESE DRAWINGS ARE INTENDED FOR GUIDANCE ONLY. FOUNDATION AND SLAB WORKS SHOULD BE DESIGNED AND APPROVED BY A LOCAL STRUCTURAL ENGINEER.
7. THE COMPANY RETAINS FULL TITLE AND OWNERSHIP OF THESE PLANS AND DESIGNS. ANY UNAUTHORISED USE, REPRODUCTION, OR DISTRIBUTION OF THESE PLANS, WHETHER IN WHOLE OR PART, IS EXPRESSLY PROHIBITED WITHOUT PRIOR WRITTEN CONSENT.
8. THE HYBRID STEEL FRAME CONSTRUCTION SYSTEM AND METHODOLOGY (PATENT PENDING) DESCRIBED IN THESE PLANS HAS BEEN DEVELOPED BY THE COMPANY AND IS SUBJECT TO A PROVISIONAL PATENT APPLICATION & ASSIGNMENT - US APPLICATION NO. 63/722,841

No.	Revision	Date

ISSUED FOR:

Issued for information

Issued for client approval

Issued for fabrication

Issued for construction

The Charlston

DRAWING TITLE:

Front&Rear Elevation

DRAWN BY:

Y.A.Clark

SCALE:


1 : 70

DRAWING NO:


A111

DATE:

18/03/2026

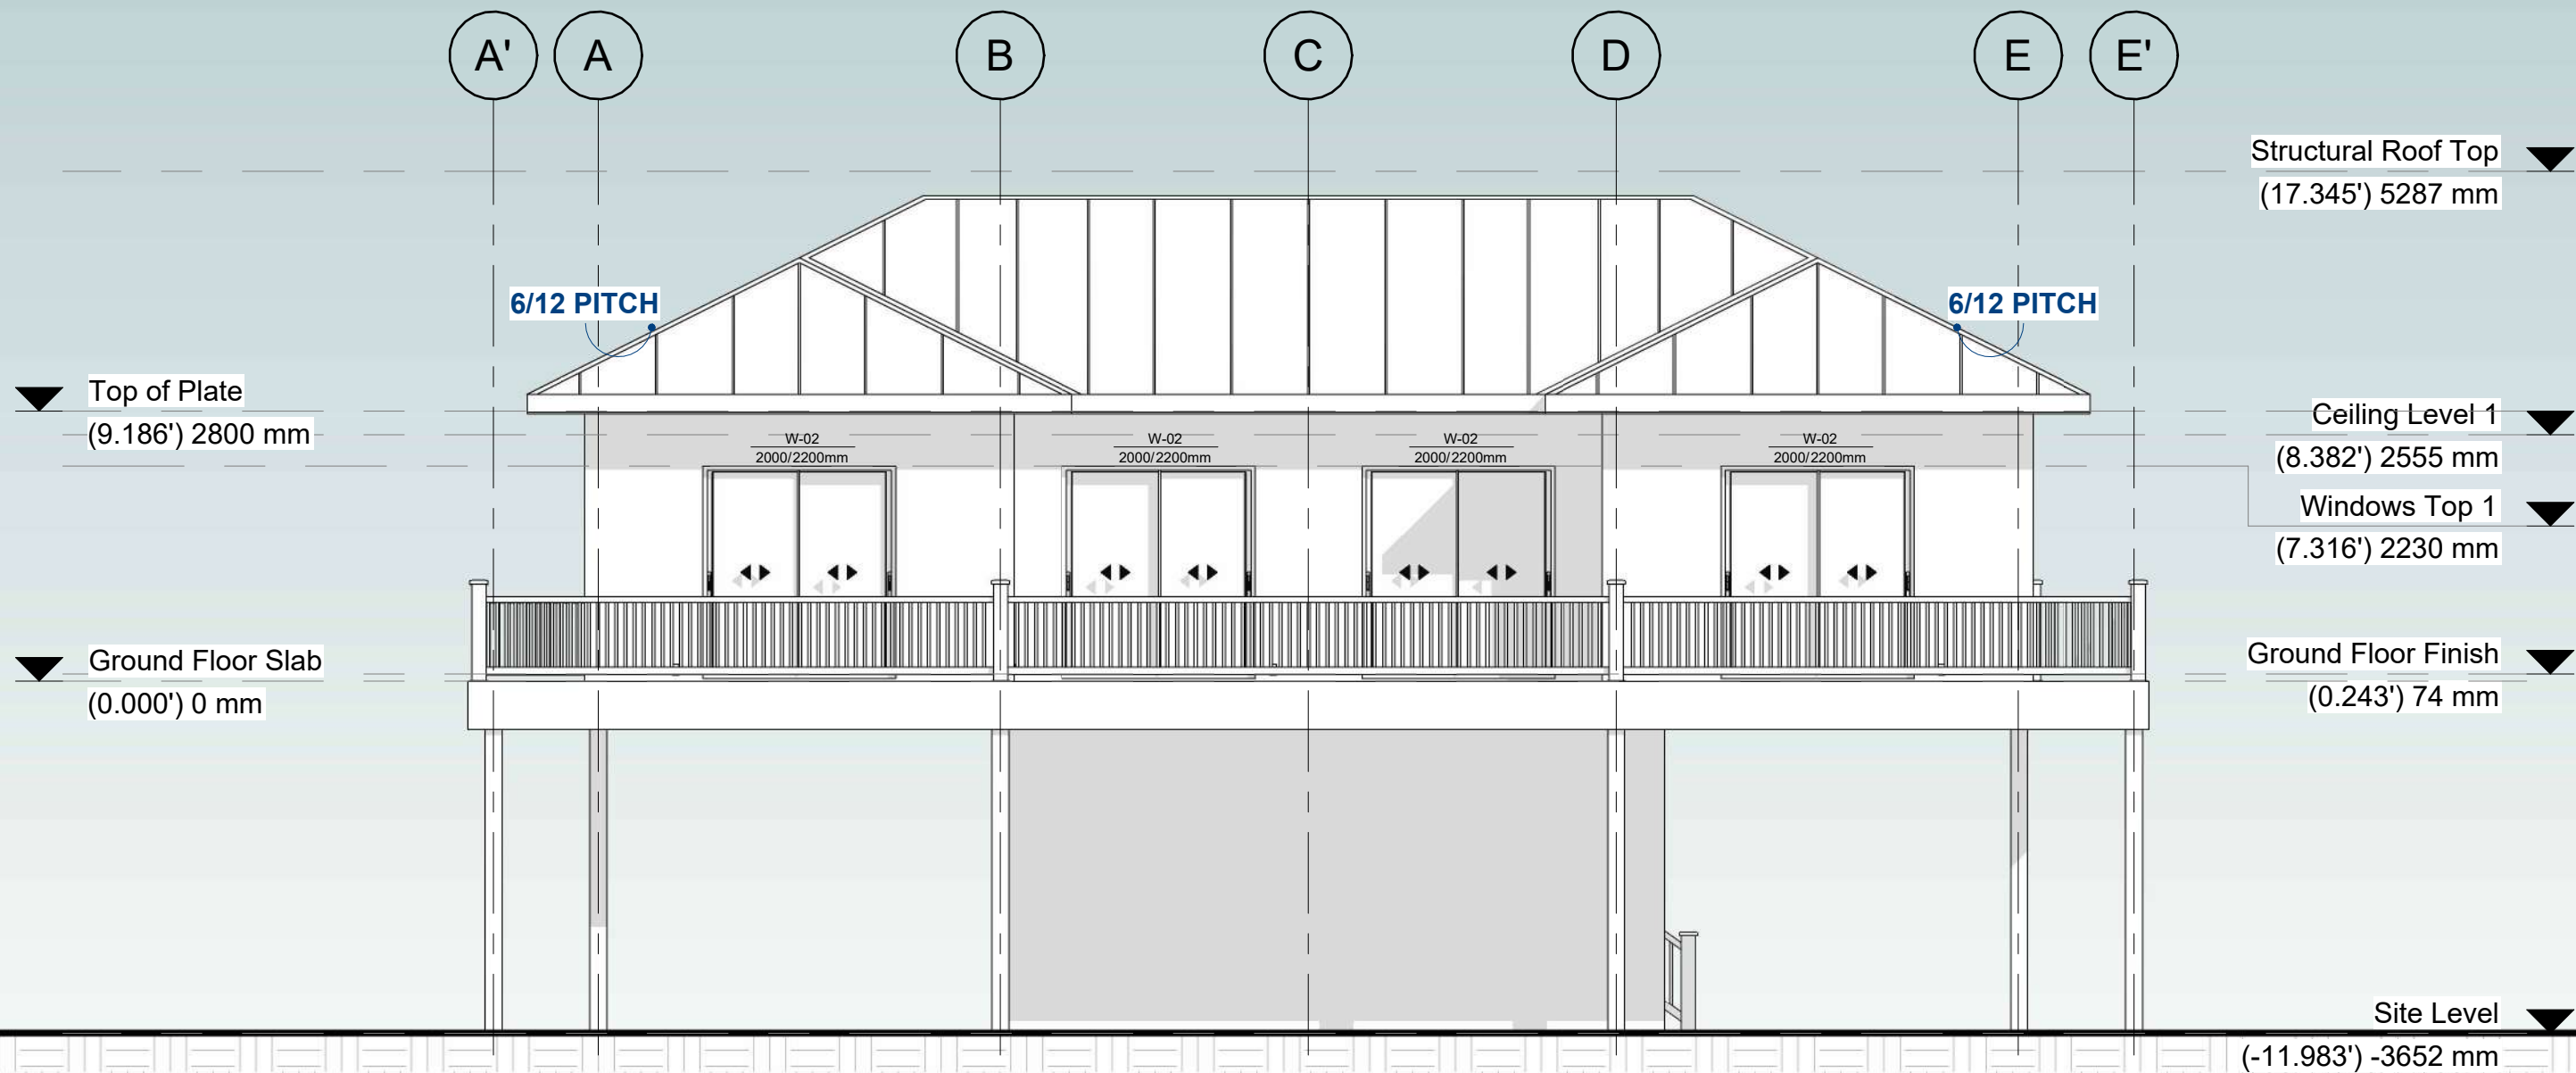

2 Front Elevation
1 : 70

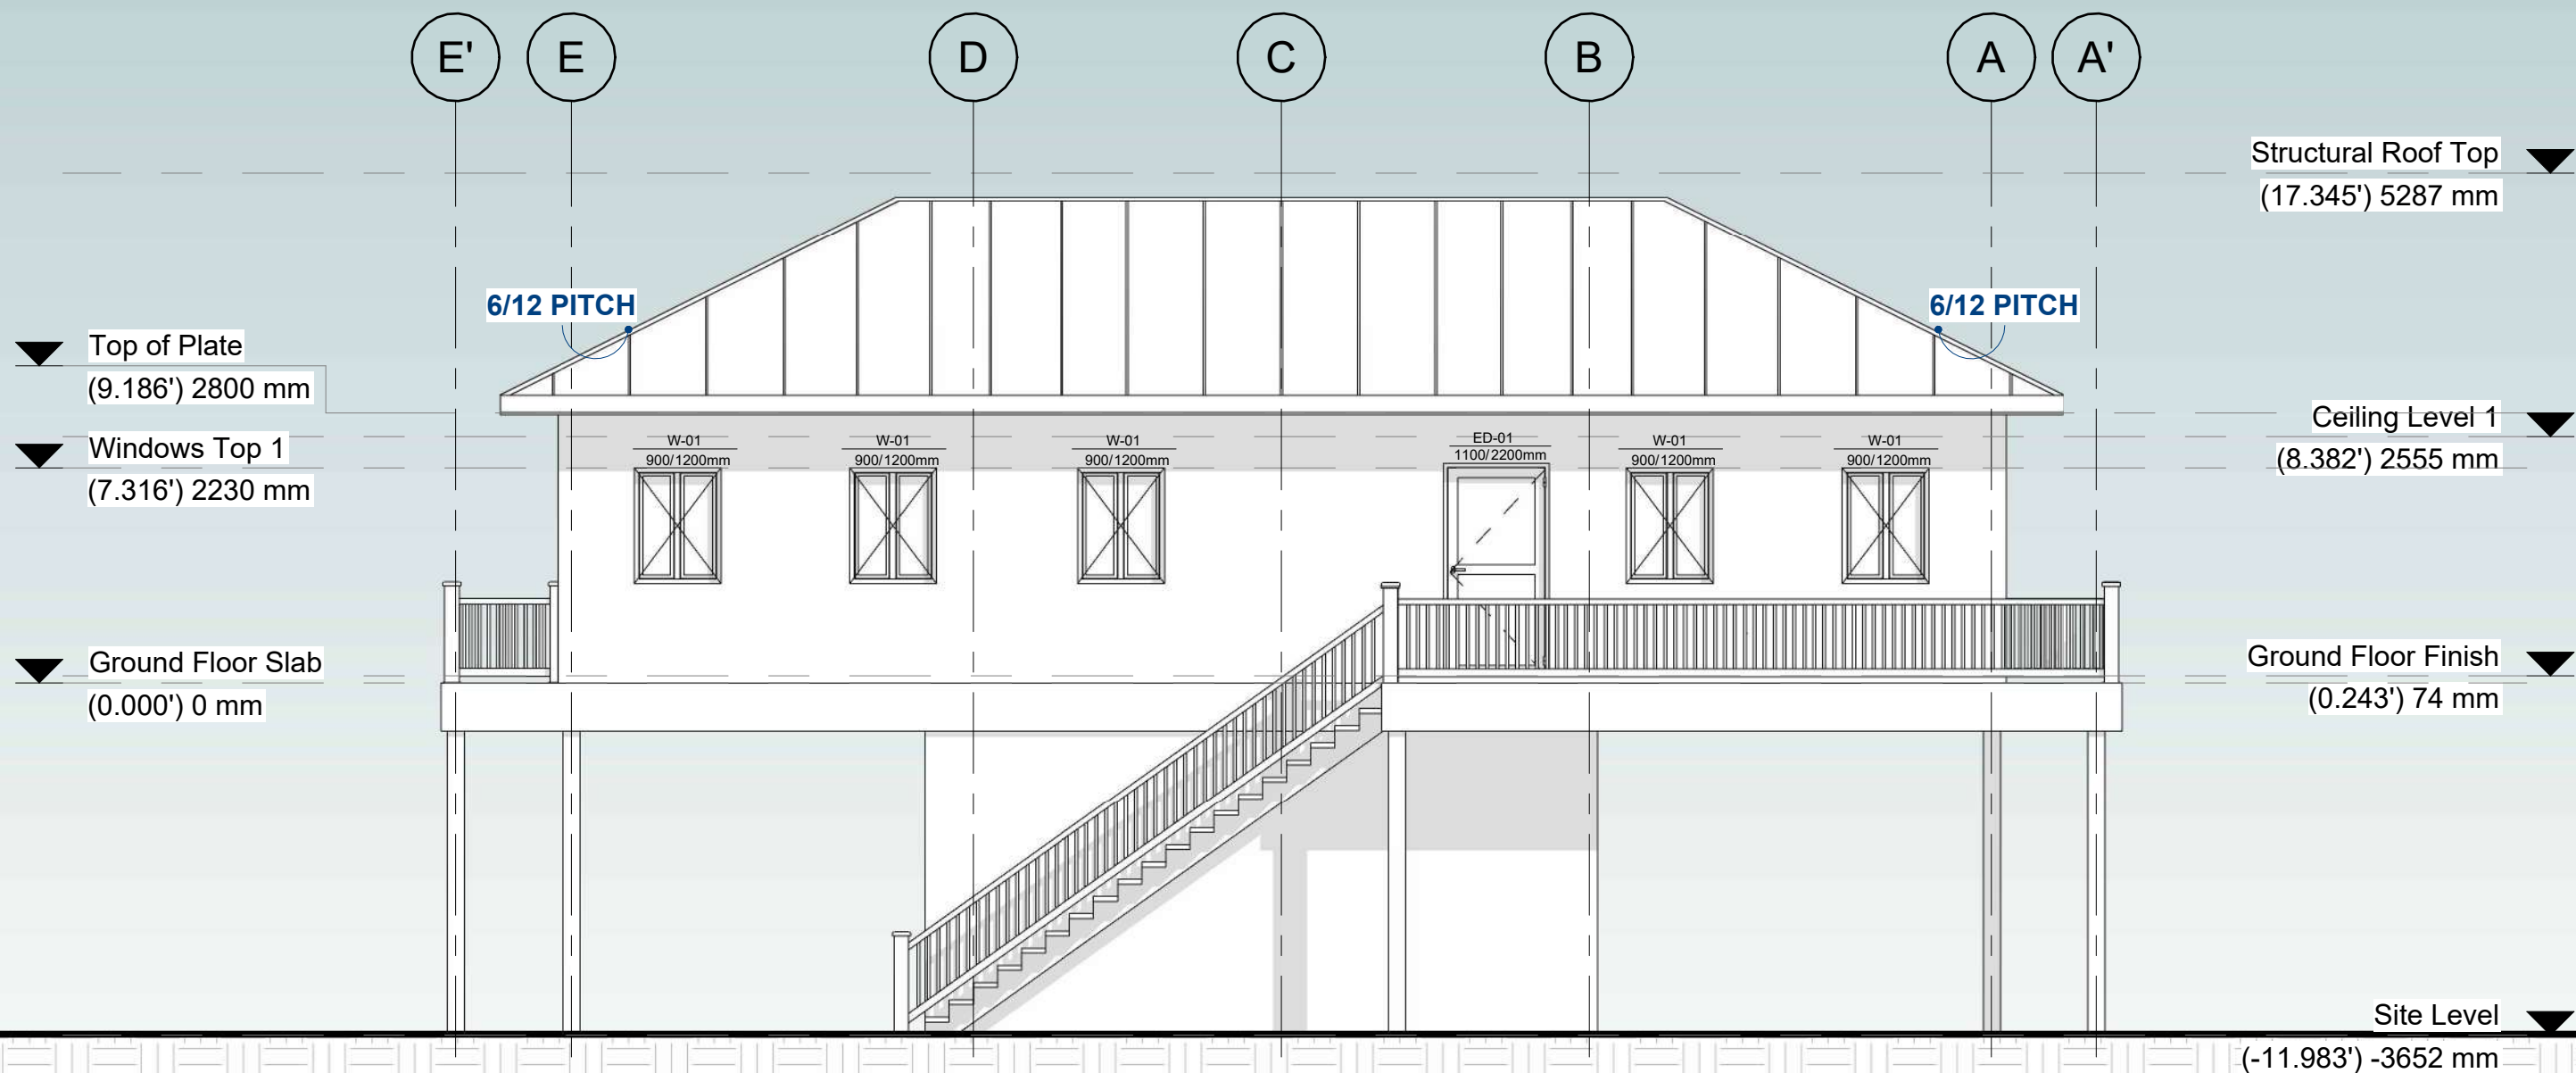

1 Rear Elevation
1 : 70

[illegible]

The Charlston

Left&Right Elevation

Y.A.Clark

1 : 70

A112

18/03/2026

1. THESE DRAWINGS MUST BE CHECKED BY THE CUSTOMER OR CONTRACTOR PRIOR TO APPROVAL. ANY ERRORS OR OMISSIONS MUST BE REPORTED IN WRITING TO BAUHU PRIOR TO COMMENCEMENT OF CONSTRUCTION.
2. ARCHITECTURAL DRAWINGS SHOULD BE READ IN CONJUNCTION WITH STRUCTURAL DETAILING AND FABRICATION GENERAL ASSEMBLY DRAWINGS.
3. FOR CONSTRUCTION PURPOSES, USE ONLY THE LATEST APPROVED DRAWINGS LABELED 'ISSUED FOR CONSTRUCTION'.
4. DO NOT SCALE FROM THIS DRAWING.
5. THE COMPANY OPERATES USING METRIC DIMENSIONS AS THE PRINCIPAL DENOMINATION.
6. ALL CONCRETE WORKS ARE OUTSIDE OF THE SCOPE OF THE COMPANY. INFORMATION REGARDING SLAB DESIGN AND CONNECTIONS IN THESE DRAWINGS ARE INTENDED FOR GUIDANCE ONLY. FOUNDATION AND SLAB WORKS SHOULD BE DESIGNED AND APPROVED BY A LOCAL STRUCTURAL ENGINEER.
7. THE COMPANY RETAINS FULL TITLE AND OWNERSHIP OF THESE PLANS AND DESIGNS. ANY UNAUTHORISED USE, REPRODUCTION, OR DISTRIBUTION OF THESE PLANS, WHETHER IN WHOLE OR PART, IS EXPRESSLY PROHIBITED WITHOUT PRIOR WRITTEN CONSENT.
8. THE HYBRID STEEL FRAME CONSTRUCTION SYSTEM AND METHODOLOGY (PATENT PENDING) DESCRIBED IN THESE PLANS HAS BEEN DEVELOPED BY THE COMPANY AND IS SUBJECT TO A PROVISIONAL PATENT APPLICATION & ASSIGNMENT - US APPLICATION NO. 63/722,841

No.	Revision	Date

ISSUED FOR:

☐ Issued for information

☐ Issued for client approval

☐ Issued for fabrication

☐ Issued for construction

The Charlston

DRAWING TITLE:

Section 1&2

DRAWN BY:

Y.A.Clark

SCALE:


1 : 70

DRAWING NO:


A113

DATE:

18/03/2026

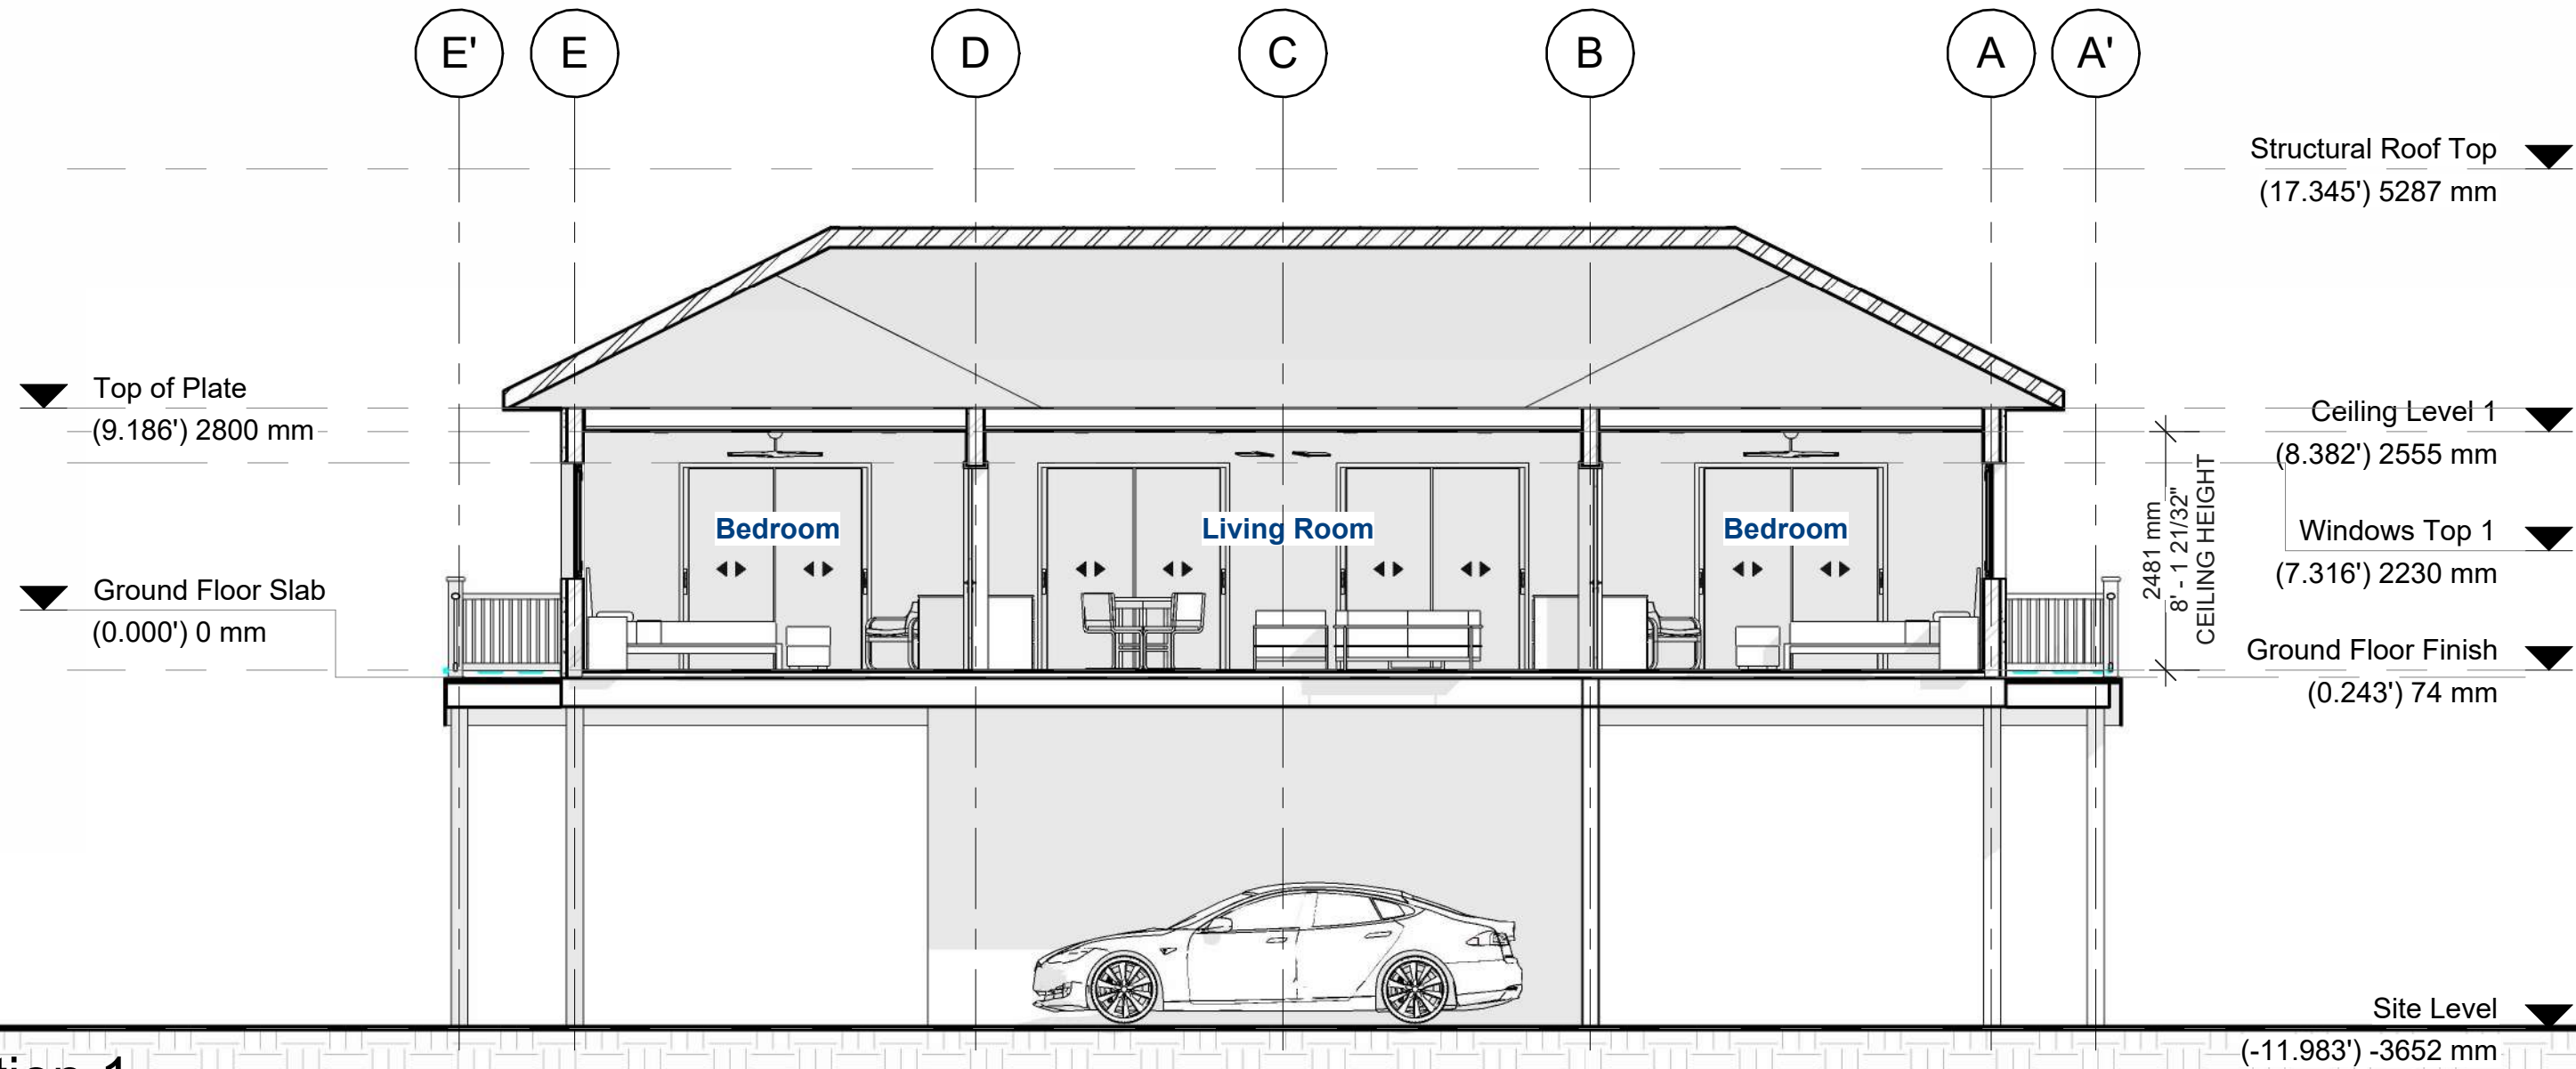

1 Section 1
1 : 70

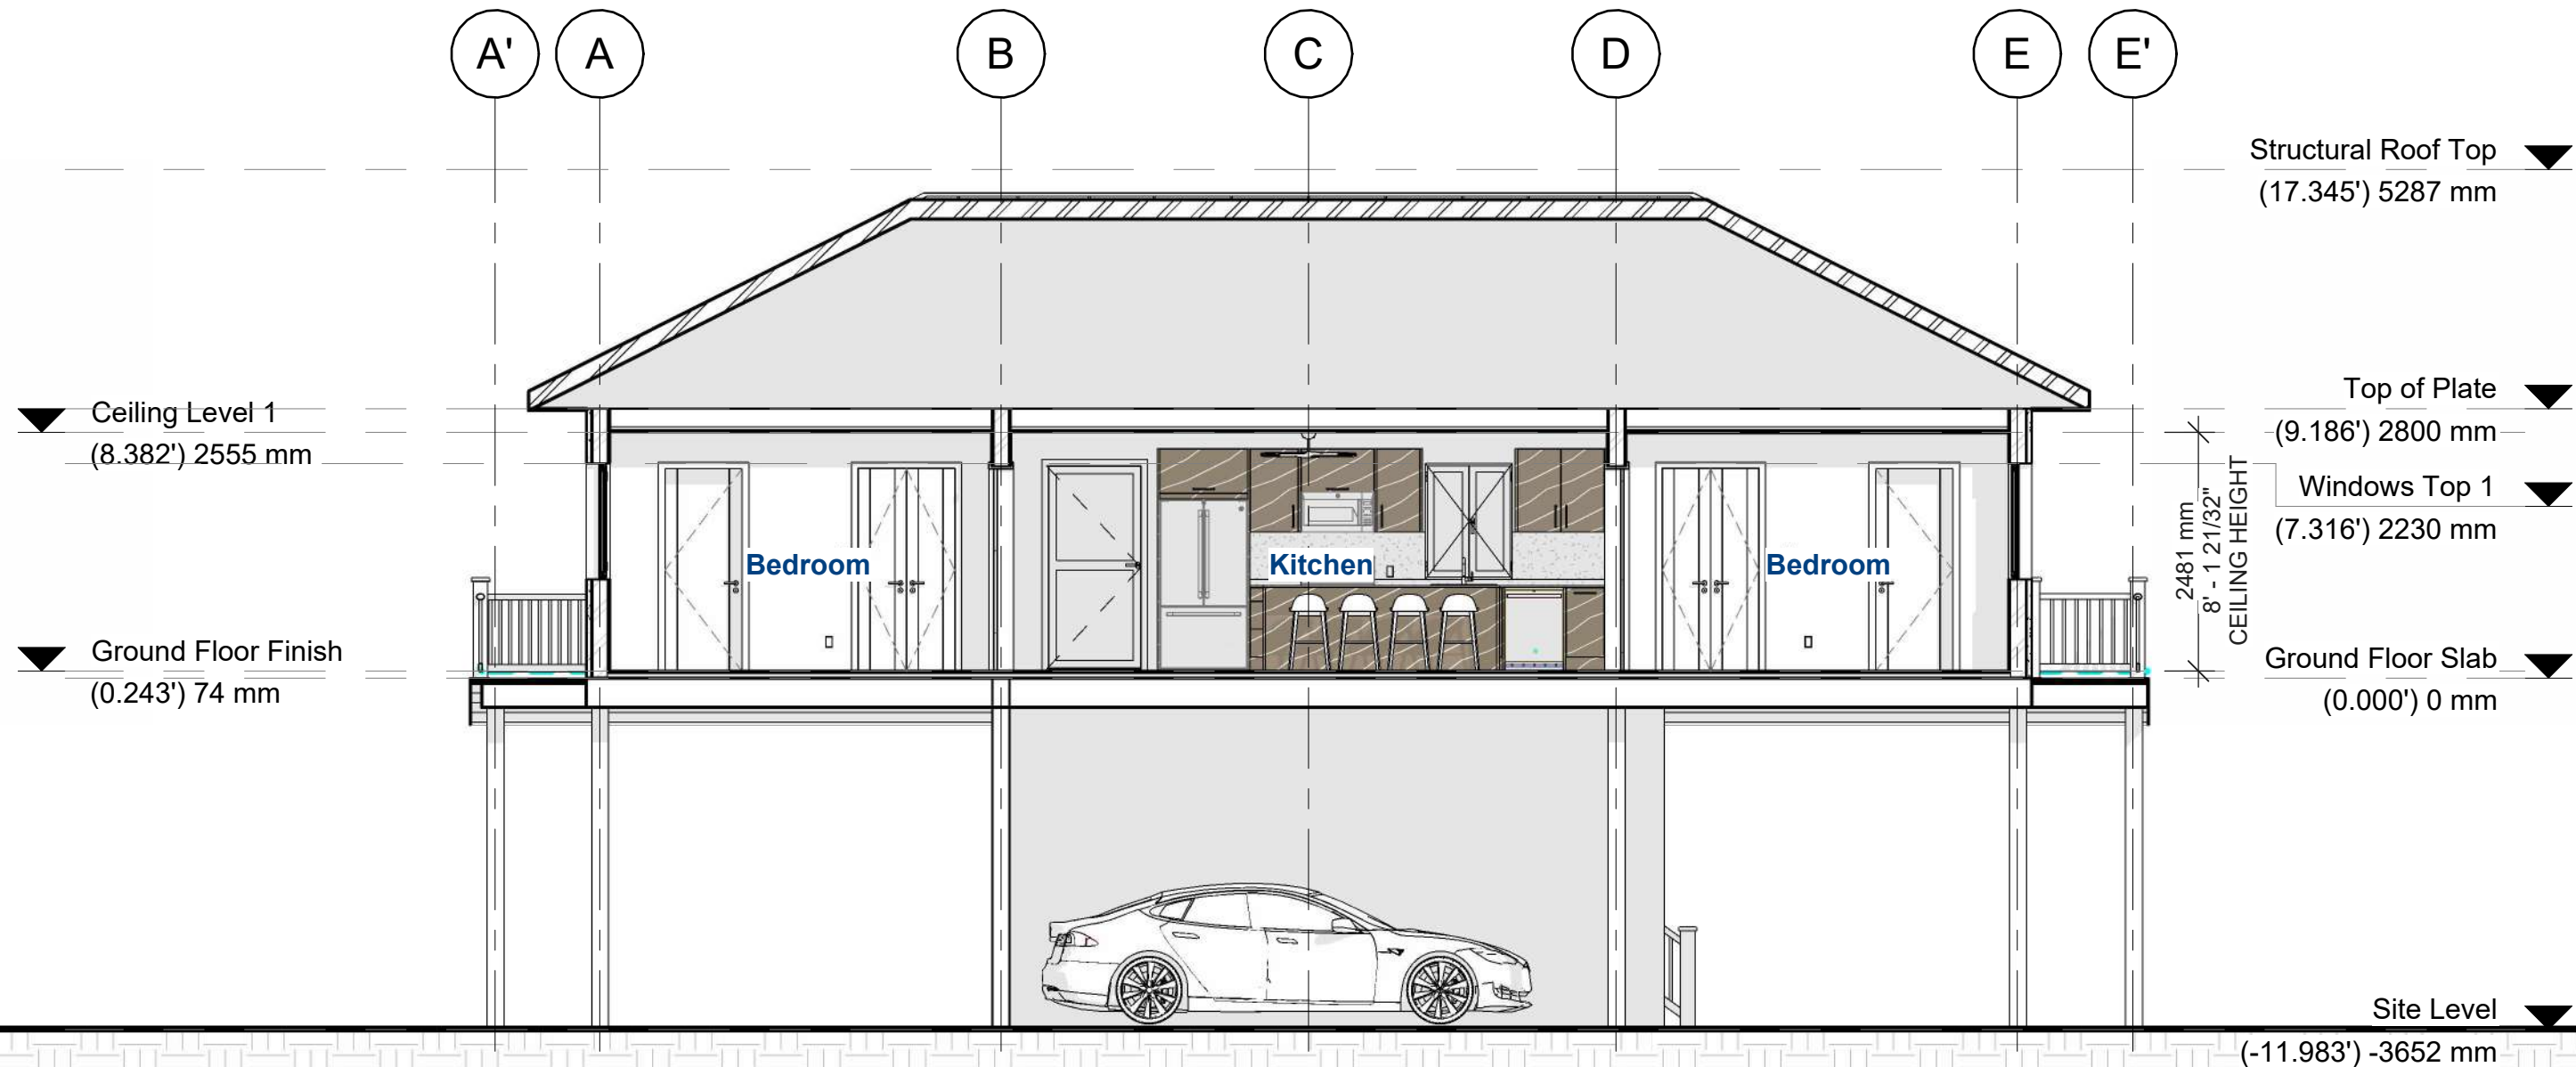

2 Section 2
1 : 70

1. THESE DRAWINGS MUST BE CHECKED BY THE CUSTOMER OR CONTRACTOR PRIOR TO APPROVAL. ANY ERRORS OR OMISSIONS MUST BE REPORTED IN WRITING TO BAUHU PRIOR TO COMMENCEMENT OF CONSTRUCTION.
2. ARCHITECTURAL DRAWINGS SHOULD BE READ IN CONJUNCTION WITH STRUCTURAL DETAILING AND FABRICATION GENERAL ASSEMBLY DRAWINGS.
3. FOR CONSTRUCTION PURPOSES, USE ONLY THE LATEST APPROVED DRAWINGS LABELED 'ISSUED FOR CONSTRUCTION'.
4. DO NOT SCALE FROM THIS DRAWING.
5. THE COMPANY OPERATES USING METRIC DIMENSIONS AS THE PRINCIPAL DENOMINATION.
6. ALL CONCRETE WORKS ARE OUTSIDE OF THE SCOPE OF THE COMPANY. INFORMATION REGARDING SLAB DESIGN AND CONNECTIONS IN THESE DRAWINGS ARE INTENDED FOR GUIDANCE ONLY. FOUNDATION AND SLAB WORKS SHOULD BE DESIGNED AND APPROVED BY A LOCAL STRUCTURAL ENGINEER.
7. THE COMPANY RETAINS FULL TITLE AND OWNERSHIP OF THESE PLANS AND DESIGNS. ANY UNAUTHORISED USE, REPRODUCTION, OR DISTRIBUTION OF THESE PLANS, WHETHER IN WHOLE OR PART, IS EXPRESSLY PROHIBITED WITHOUT PRIOR WRITTEN CONSENT.
8. THE HYBRID STEEL FRAME CONSTRUCTION SYSTEM AND METHODOLOGY (PATENT PENDING) DESCRIBED IN THESE PLANS HAS BEEN DEVELOPED BY THE COMPANY AND IS SUBJECT TO A PROVISIONAL PATENT APPLICATION & ASSIGNMENT - US APPLICATION NO. 63/722,841

No.	Revision	Date

ISSUED FOR:

Issued for information

Issued for client approval

Issued for fabrication

Issued for construction

The Charlston

DRAWING TITLE:

Section 3

DRAWN BY:

Y.A.Clark

SCALE:


1 : 50

DRAWING NO:

A114

DATE:

18/03/2026

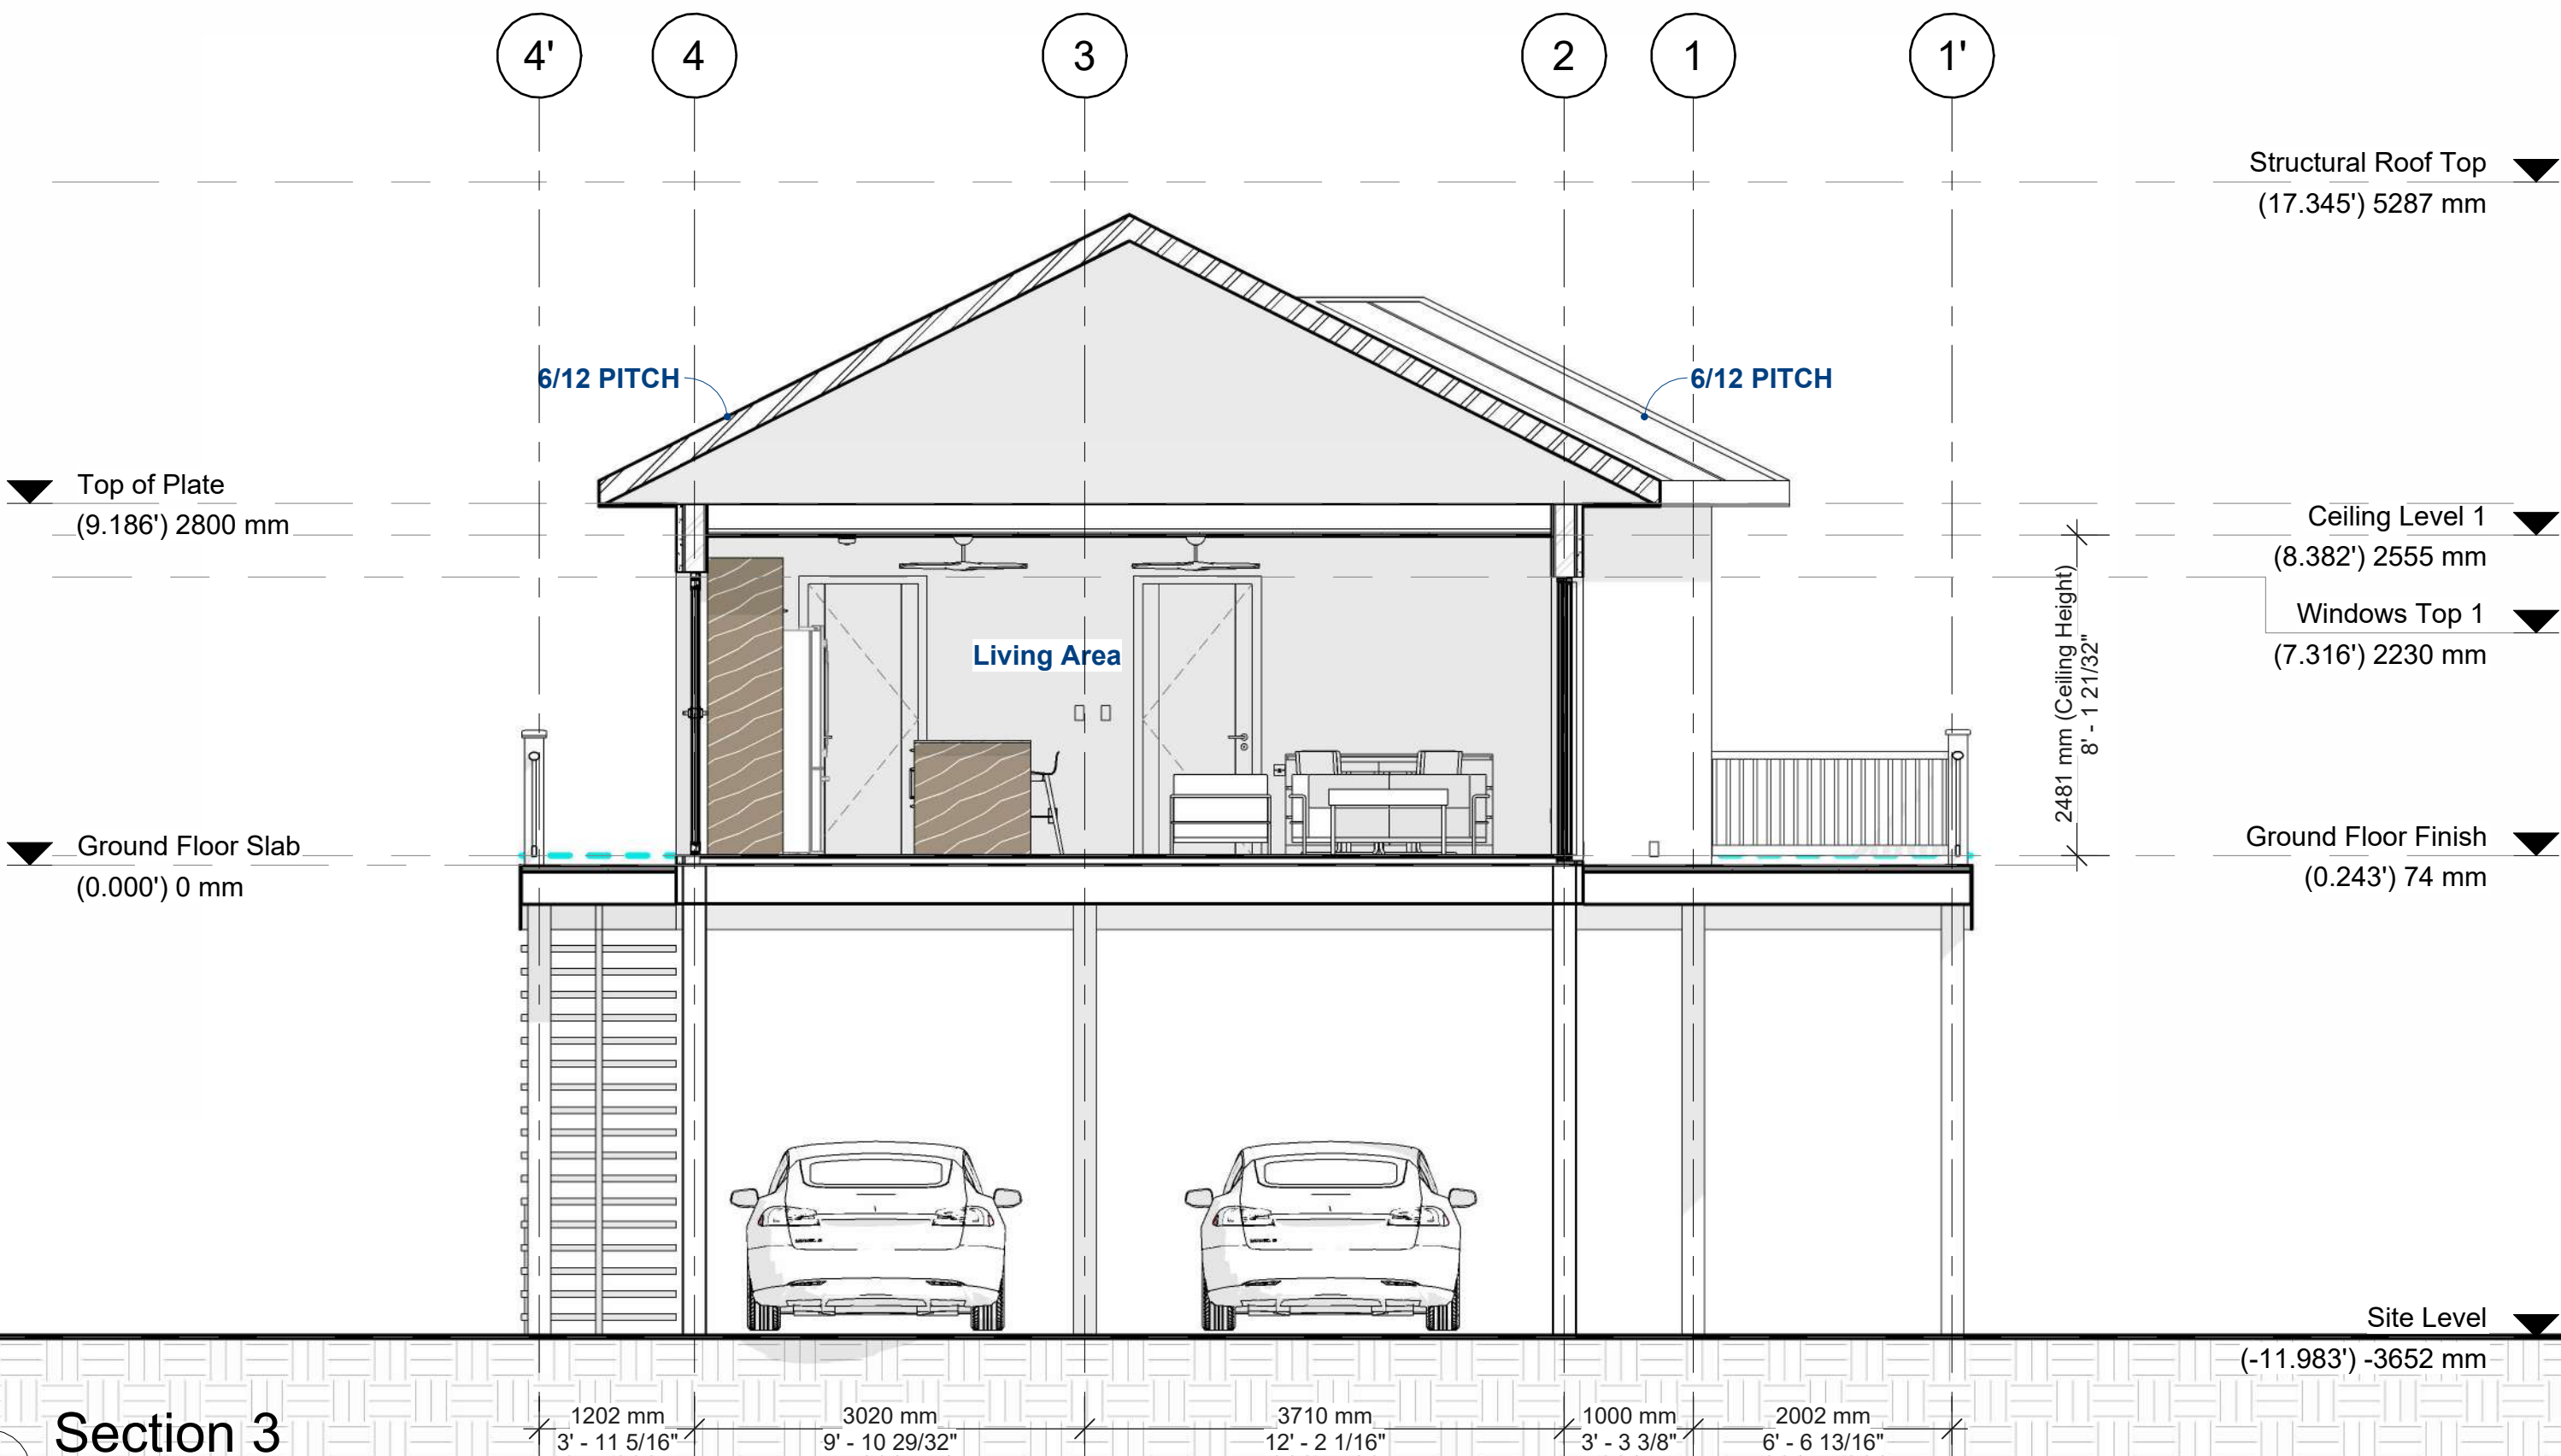

Section 3
1 : 50

Door Schedule													
No	Type	Door Size		Rough Opening Size		Count	Glass	Finishing	No of Leaves	Hinge Side	Sill Height	Level	Lock
		Width	Height	RO Width	RO. Height								
ED-01	COR 70 IND Single Casement Door	1100 mm	2200 mm	1134	2291	1	44.2+16argon we+6 SNX	RAL 7016 matte	1	RH	74 mm	Ground Floor Slab	Yes
ID-01	Interior Single Casement Door	850 mm	2100 mm	915	2214	3	x	Matt White Lac.	1	LH	74 mm	Ground Floor Slab	Yes
ID-01	Interior Single Casement Door	850 mm	2100 mm	915	2214	1	x	Matt White Lac.	1	RH	74 mm	Ground Floor Slab	Yes
ID-02	Interior Double Casement Door	1000 mm	2100 mm	1065	2214	2	x	Matt White Lac.	2	Both sides	74 mm	Ground Floor Slab	Yes
ID-03	Interior Single Casement Door 3	800 mm	2100 mm	865	2214	1	x	Matt White Lac.	1	LH	74 mm	Ground Floor Slab	Yes
ID-03	Interior Single Casement Door 3	800 mm	2100 mm	865	2214	1	x	Matt White Lac.	1	RH	74 mm	Ground Floor Slab	Yes
Grand total						9							

Window Schedule													
No	Type	Window Size		Rough Opening Size		Count	Glass	Finishing	No of Leaves	Hinge Side	Sill Height	Level	Lock
		Width	Height	RO. Width	RO. Height								
W-01	COR 70 IND Double Casement - 1	900 mm	1200 mm	934	1234	7	44.2+16argon we+6 SNX	RAL 7016 matte	2	Both sides	1030 mm	Ground Floor Slab	Yes
W-02	COR Vision w/ Rteel reinforcement 2	2000 mm	2200 mm	2034	2247	2	44.2+16argon we+6 SNX	RAL 7016 matte	2	Interior Panel Left	30 mm	Ground Floor Slab	Yes
W-02	COR Vision w/ Rteel reinforcement 2	2000 mm	2200 mm	2034	2247	2	44.2+16argon we+6 SNX	RAL 7016 matte	2	Interior Panel Right	30 mm	Ground Floor Slab	Yes
Grand total						11							

Compincar Interior Doors
https://compincar.com

Door
Colour: Matt White Lac.
Model: 304



Handle
Model: 1003



Cortizo Exterior Door/Window
https://www.cortizo.com/paginas/carta_standard

Colour: Anthracite Grey
RAL Code: 7016 matte



Glass
https://www.guardianglass.com/gb/en/our-glass/glass-types/solar-control-glass
• 44.2+16argon we+6 SNX



- THESE DRAWINGS MUST BE CHECKED BY THE CUSTOMER OR CONTRACTOR PRIOR TO APPROVAL. ANY ERRORS OR OMISSIONS MUST BE REPORTED IN WRITING TO BAUHU PRIOR TO COMMENCEMENT OF CONSTRUCTION.
- ARCHITECTURAL DRAWINGS SHOULD BE READ IN CONJUNCTION WITH STRUCTURAL DETAILING AND FABRICATION GENERAL ASSEMBLY DRAWINGS.
- FOR CONSTRUCTION PURPOSES, USE ONLY THE LATEST APPROVED DRAWINGS LABELED 'ISSUED FOR CONSTRUCTION'.
- DO NOT SCALE FROM THIS DRAWING.
- THE COMPANY OPERATES USING METRIC DIMENSIONS AS THE PRINCIPAL DENOMINATION.
- ALL CONCRETE WORKS ARE OUTSIDE OF THE SCOPE OF THE COMPANY. INFORMATION REGARDING SLAB DESIGN AND CONNECTIONS IN THESE DRAWINGS ARE INTENDED FOR GUIDENCE ONLY. FOUNDATION AND SLAB WORKS SHOULD BE DESIGNED AND APPROVED BY A LOCAL STRUCTURAL ENGINEER.
- THE COMPANY RETAINS FULL TITLE AND OWNERSHIP OF THESE PLANS AND DESIGNS. ANY UNAUTHORISED USE, REPRODUCTION, OR DISTRIBUTION OF THESE PLANS, WHETHER IN WHOLE OR PART, IS EXPRESSLY PROHIBITED WITHOUT PRIOR WRITTEN CONSENT.
- THE HYBRID STEEL FRAME CONSTRUCTION SYSTEM AND METHODOLOGY (PATENT PENDING) DESCRIBED IN THESE PLANS HAS BEEN DEVELOPED BY THE COMPANY AND IS SUBJECT TO A PROVISIONAL PATENT APPLICATION & ASSIGNMENT - US APPLICATION NO. 63/722,841

No.	Revision	Date

ISSUED FOR:

Issued for information

Issued for client approval

Issued for fabrication


Issued for construction

The Charlston

DRAWING TITLE:	Openings Schedule
DRAWN BY:	Y.A.Clark
SCALE:	
DRAWING NO:	A115
DATE:	18/03/2026

Note:

- Shutters, insect screens and screening will be provided by others-acquired locally according to dimensions of finished openings after finish application. Drawings are made for design purposes only.
- Garage type doors are excluded and should be sourced by the owner.
- All opening windows open outwards.

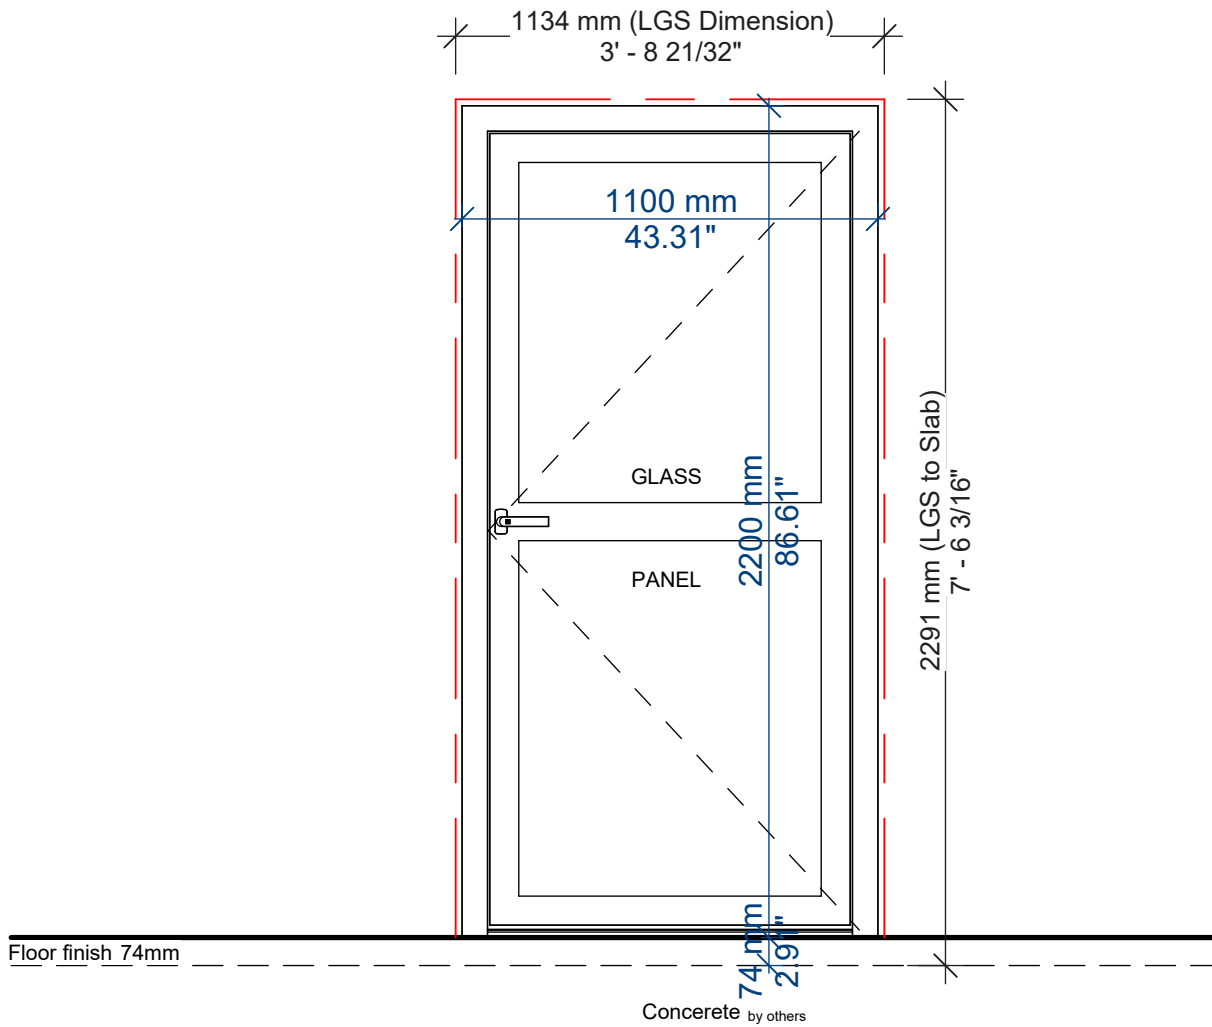


ED01

Type: Exterior COR 70 IND Single Casement
Size: 1100x2200
R.O. Size: 1134x2291
Number of Leaves: 1
Total Piece: 1
Hinge Side: Right (outwards)
Sill Height (from top of slab): 74

ID01

Type: Interior Single Casement
Size: 850x2100
R.O. Size: 915x2214
Number of Leaves: 1
Total Piece: 4
Hinge Side: 3 left, 1 right
Sill Height (from top of slab): 74


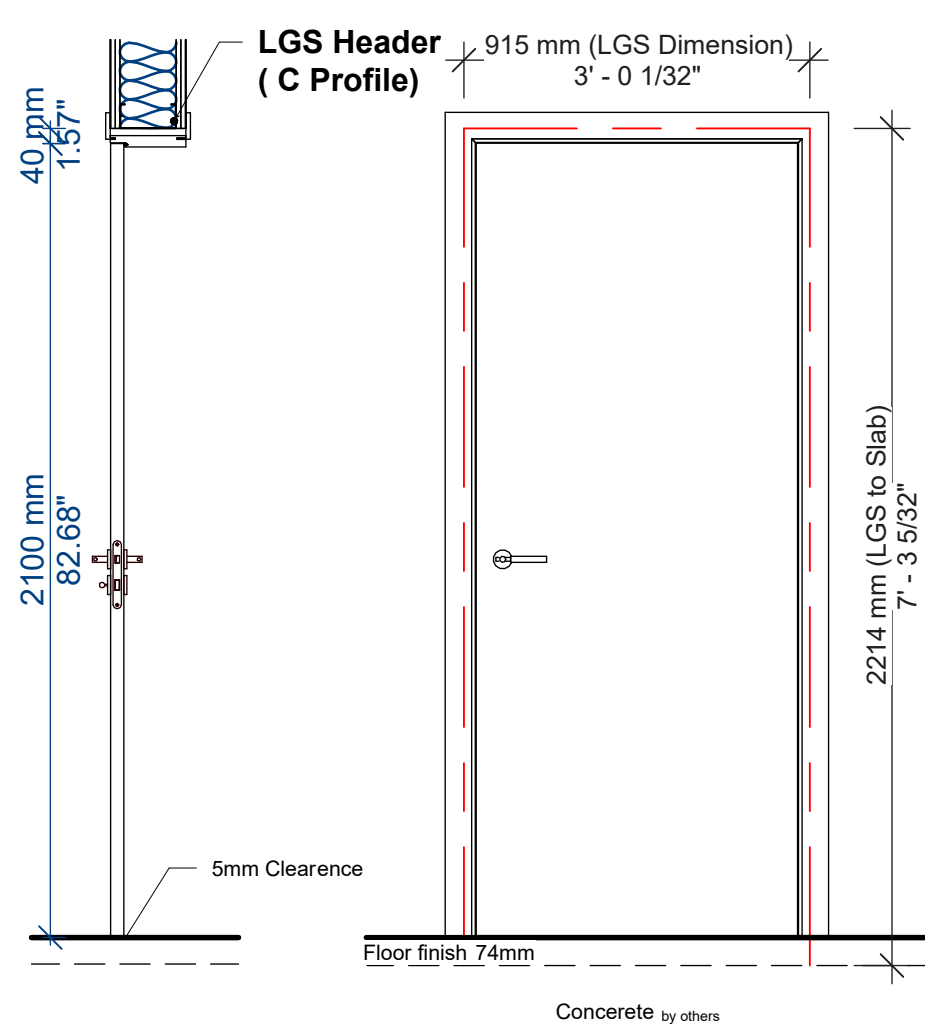


ID02

Type: Interior Double Casement
Size: 1000x2100
R.O. Size: 1065x2214
Number of Leaves: 2
Total Piece: 2
Hinge Side: both sides
Sill Height (from top of slab): 74

ID03

Type: Interior Single Casement
Size: 800x2100
R.O. Size: 865x2214
Number of Leaves: 1
Total Piece: 2
Hinge Side: 1 right, 1 left
Sill Height (from top of slab): 74

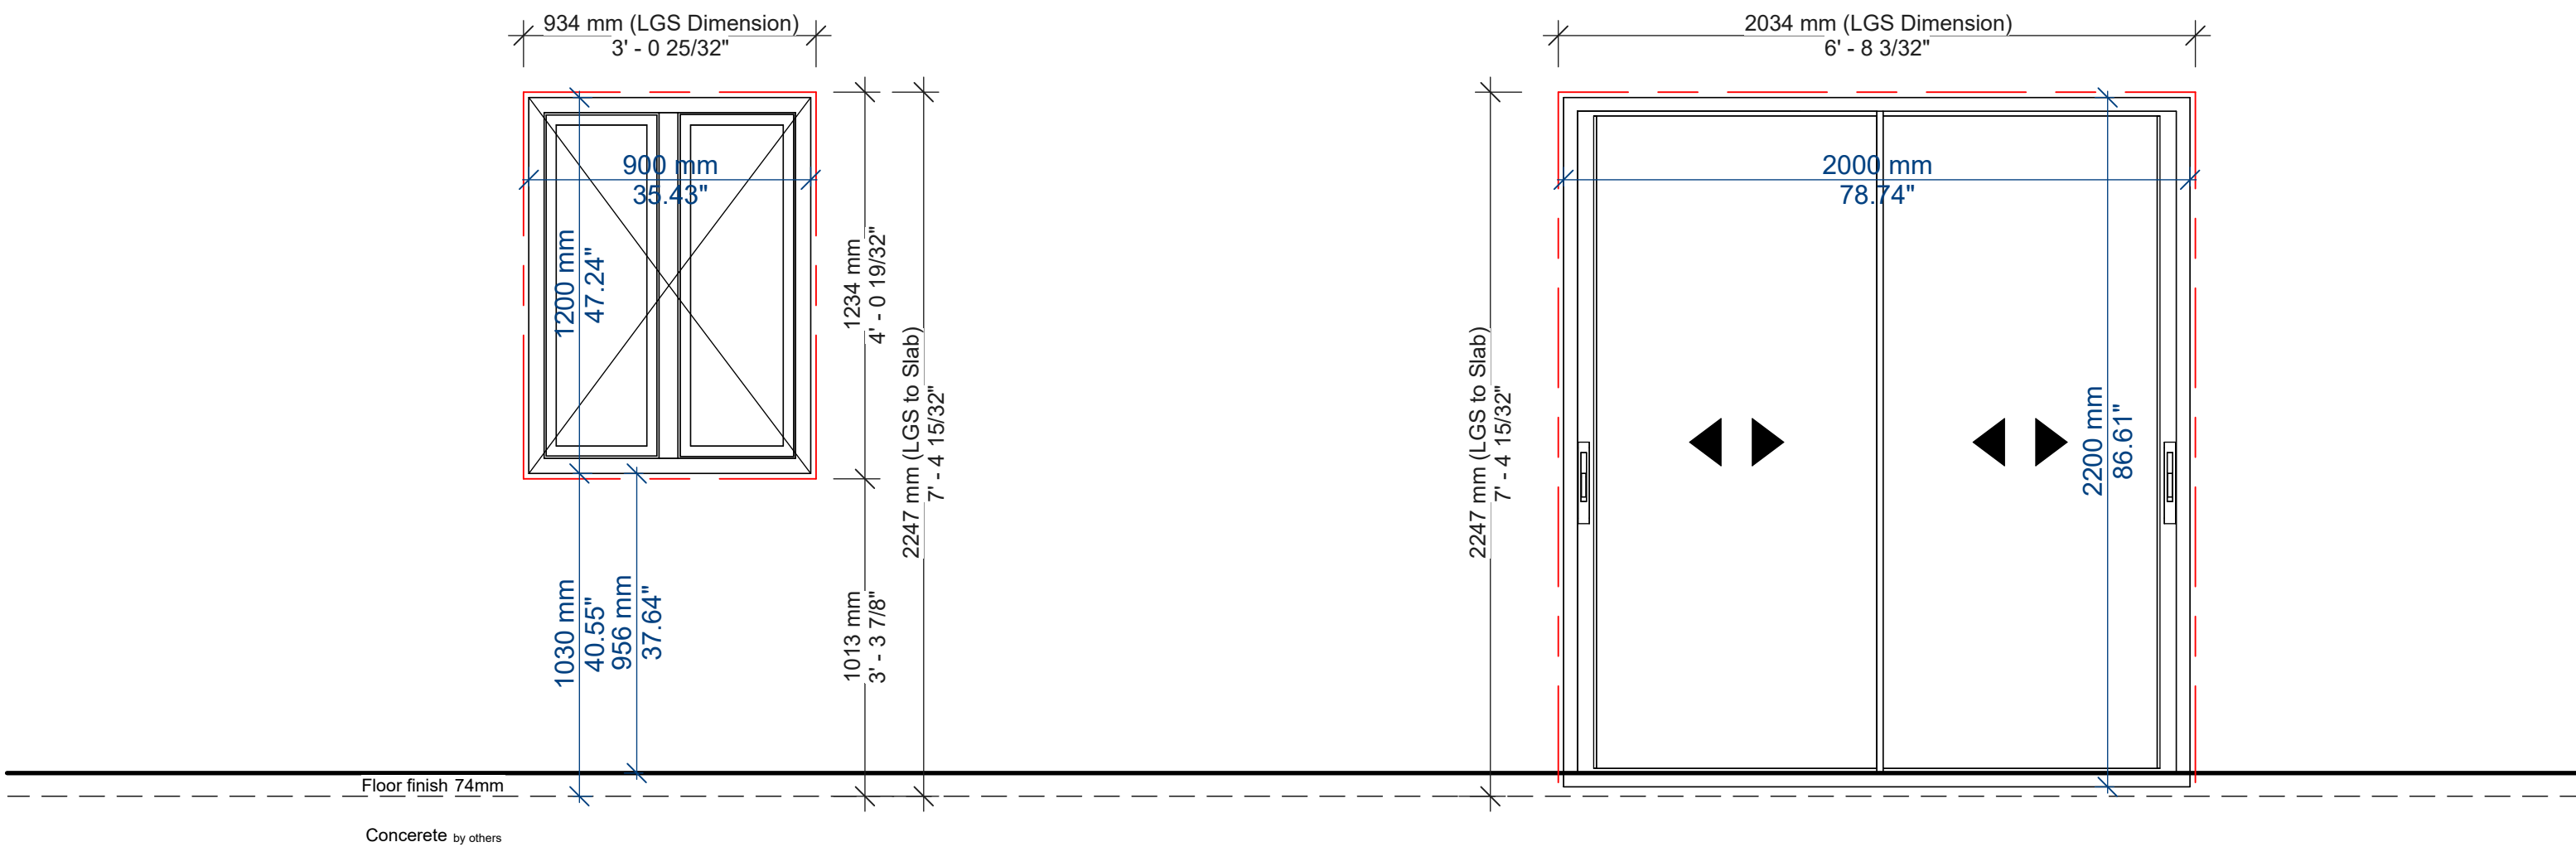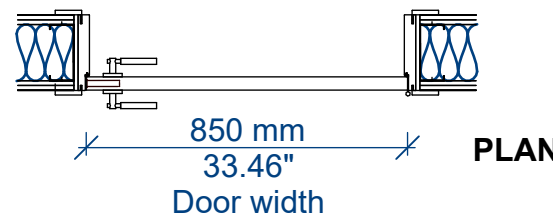

W01

Type: Double Casement
Size: 900x1200
R.O. Size: 934x1234
Number of Leaves: 2
Total Piece: 7
Hinge Side: both sides

W02

Type: Slider
Size: 2000x2200
R.O. Size: 2034x2247
Number of Leaves: 2
Total Piece: 4
Hinge Side: 2 interior panel left, 2 interior panel right

1. THESE DRAWINGS MUST BE CHECKED BY THE CUSTOMER OR CONTRACTOR PRIOR TO APPROVAL. ANY ERRORS OR OMISSIONS MUST BE REPORTED IN WRITING TO BAUHU PRIOR TO COMMENCEMENT OF CONSTRUCTION.
2. ARCHITECTURAL DRAWINGS SHOULD BE READ IN CONJUNCTION WITH STRUCTURAL DETAILING AND FABRICATION GENERAL ASSEMBLY DRAWINGS.
3. FOR CONSTRUCTION PURPOSES, USE ONLY THE LATEST APPROVED DRAWINGS LABELED 'ISSUED FOR CONSTRUCTION'.
4. DO NOT SCALE FROM THIS DRAWING.
5. THE COMPANY OPERATES USING METRIC DIMENSIONS AS THE PRINCIPAL DENOMINATION.
6. ALL CONCRETE WORKS ARE OUTSIDE OF THE SCOPE OF THE COMPANY. INFORMATION REGARDING SLAB DESIGN AND CONNECTIONS IN THESE DRAWINGS ARE INTENDED FOR GUIDENCE ONLY. FOUNDATION AND SLAB WORKS SHOULD BE DESIGNED AND APPROVED BY A LOCAL STRUCTURAL ENGINEER.
7. THE COMPANY RETAINS FULL TITLE AND OWNERSHIP OF THESE PLANS AND DESIGNS. ANY UNAUTHORISED USE, REPRODUCTION, OR DISTRIBUTION OF THESE PLANS, WHETHER IN WHOLE OR PART, IS EXPRESSLY PROHIBITED WITHOUT PRIOR WRITTEN CONSENT.
8. THE HYBRID STEEL FRAME CONSTRUCTION SYSTEM AND METHODOLOGY (PATENT PENDING) DESCRIBED IN THESE PLANS HAS BEEN DEVELOPED BY THE COMPANY AND IS SUBJECT TO A PROVISIONAL PATENT APPLICATION & ASSIGNMENT - US APPLICATION NO. 63/722,841

No.	Revision	Date

ISSUED FOR:

Issued for information

Issued for client approval

Issued for fabrication

Issued for construction

The Charlston

DRAWING TITLE:
Door&Window Openings

DRAWN BY:
Y.A.Clark

SCALE:
1 : 20

DRAWING NO:
A116

DATE:
18/03/2026

1. THESE DRAWINGS MUST BE CHECKED BY THE CUSTOMER OR CONTRACTOR PRIOR TO APPROVAL. ANY ERRORS OR OMISSIONS MUST BE REPORTED IN WRITING TO BAUHU PRIOR TO COMMENCEMENT OF CONSTRUCTION.

2. ARCHITECTURAL DRAWINGS SHOULD BE READ IN CONJUNCTION WITH STRUCTURAL DETAILING AND FABRICATION GENERAL ASSEMBLY DRAWINGS.

3. FOR CONSTRUCTION PURPOSES, USE ONLY THE LATEST APPROVED DRAWINGS LABELED 'ISSUED FOR CONSTRUCTION'.

4. DO NOT SCALE FROM THIS DRAWING.

5. THE COMPANY OPERATES USING METRIC DIMENSIONS AS THE PRINCIPAL DENOMINATION.

6. ALL CONCRETE WORKS ARE OUTSIDE OF THE SCOPE OF THE COMPANY. INFORMATION REGARDING SLAB DESIGN AND CONNECTIONS IN THESE DRAWINGS ARE INTENDED FOR GUIDENCE ONLY. FOUNDATION AND SLAB WORKS SHOULD BE DESIGNED AND APPROVED BY A LOCAL STRUCTURAL ENGINEER.

7. THE COMPANY RETAINS FULL TITLE AND OWNERSHIP OF THESE PLANS AND DESIGNS. ANY UNAUTHORISED USE, REPRODUCTION, OR DISTRIBUTION OF THESE PLANS, WHETHER IN WHOLE OR PART, IS EXPRESSLY PROHIBITED WITHOUT PRIOR WRITTEN CONSENT.

8. THE HYBRID STEEL FRAME CONSTRUCTION SYSTEM AND METHODOLOGY (PATENT PENDING) DESCRIBED IN THESE PLANS HAS BEEN DEVELOPED BY THE COMPANY AND IS SUBJECT TO A PROVISIONAL PATENT APPLICATION & ASSIGNMENT - US APPLICATION NO. 63/722,841

No.	Revision	Date

ISSUED FOR:

Issued for information

Issued for client approval

Issued for fabrication

Issued for construction

The Charlston

DRAWING TITLE:

Kitchen Plan&Sections

DRAWN BY:

Y.A.Clark

SCALE:




1 : 25

DRAWING NO:

A117

DATE:

18/03/2026

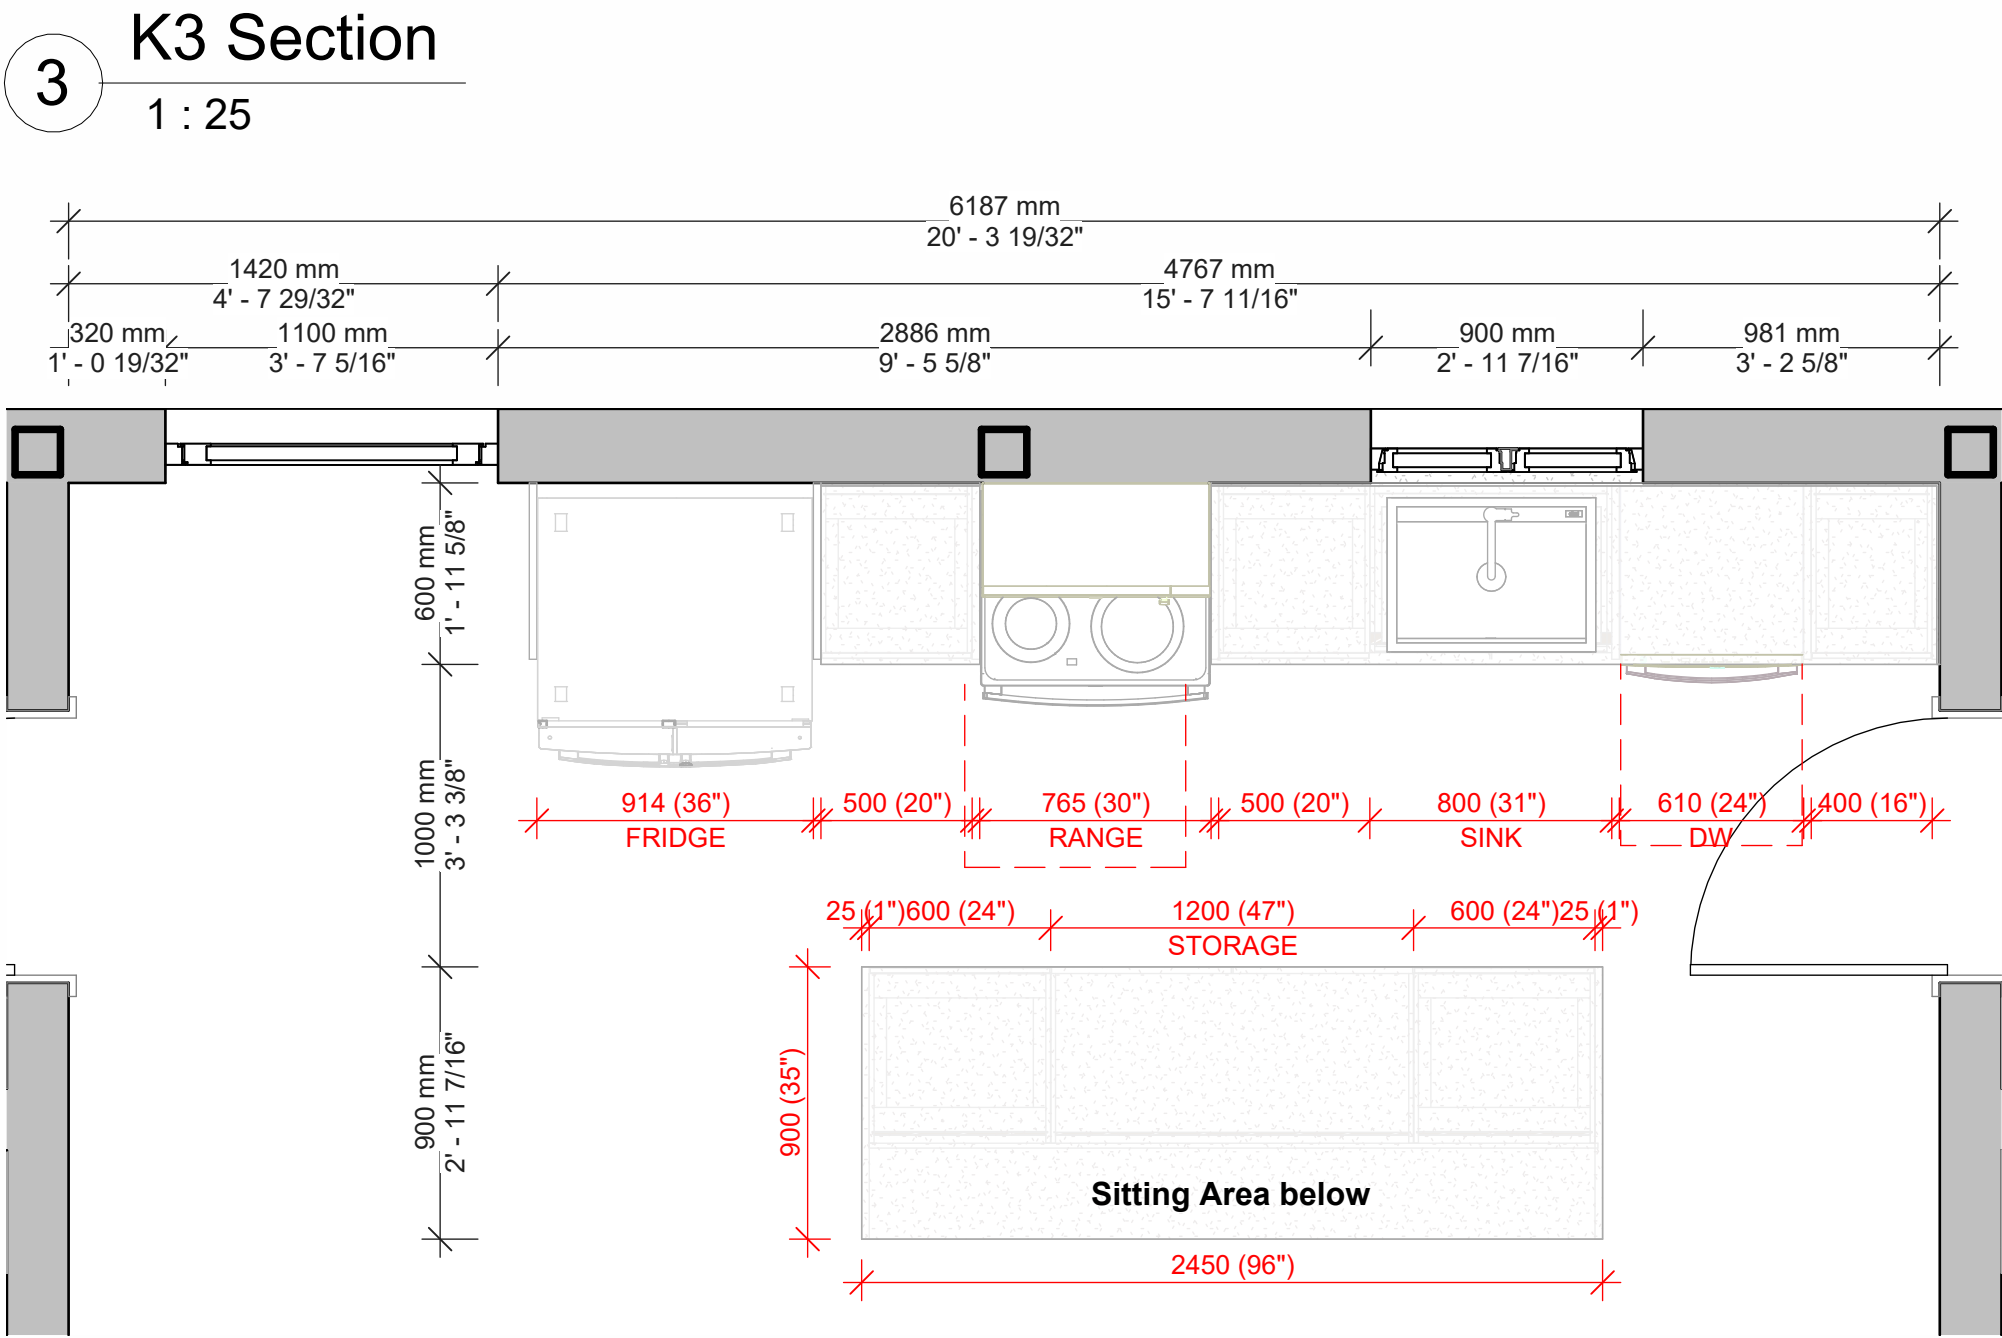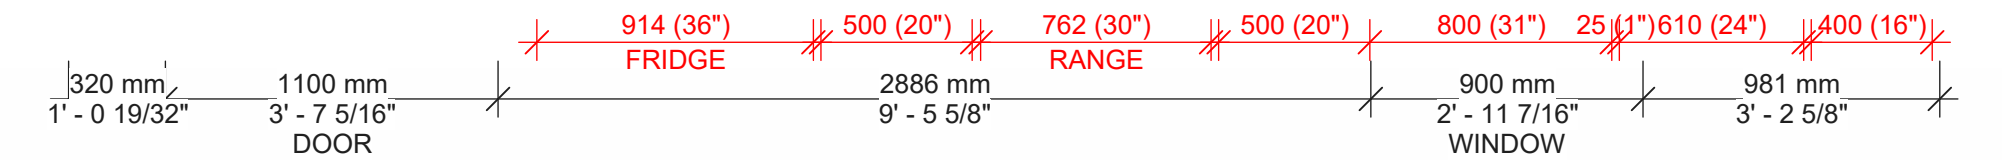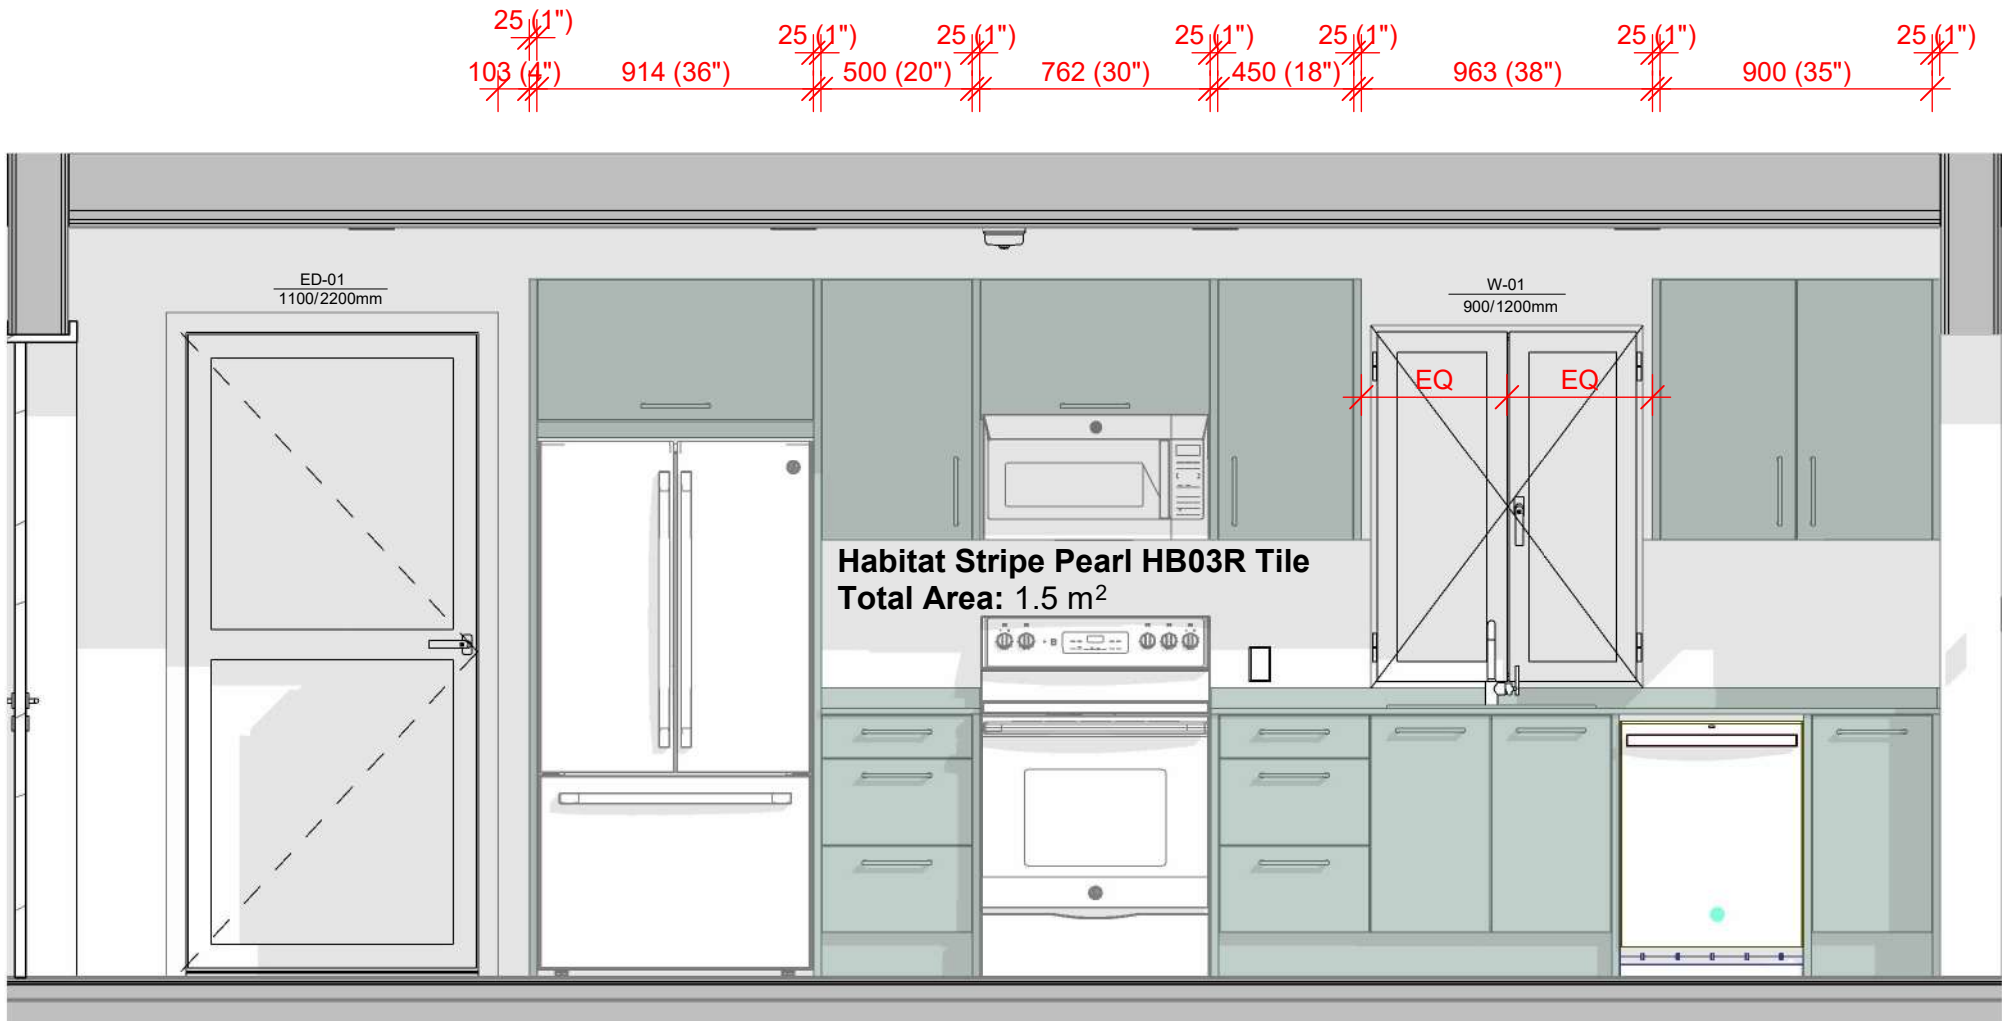

1 Kitchen Plan
1 : 25


2 K2 Island Front
1 : 25

4 K4 Island Back
1 : 25

KITCHEN MIXER

https://www.bruma.pt


Bruma
Model: Kitchen Faucets
Name: Sink mixer with swivel spout and pull out handshower -
Ginger
Reference: 122 700 3CR
Colour: Chrome
Count: 1

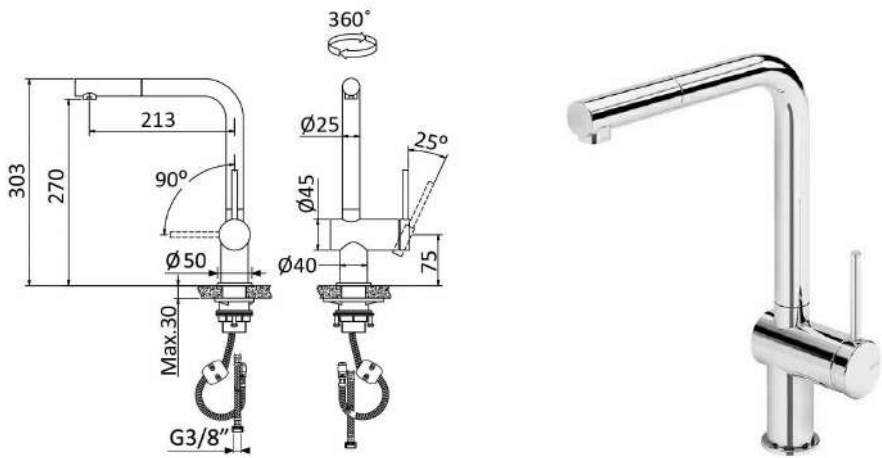

KITCHEN SINK

https://www.elleci.com/products/sinks/

Elleci
Model: Built-in sink Best 130 Keratek
Dimensions: 790 x 510 mm
Base: 800 mm
Colour: Black - K86
Count: 1

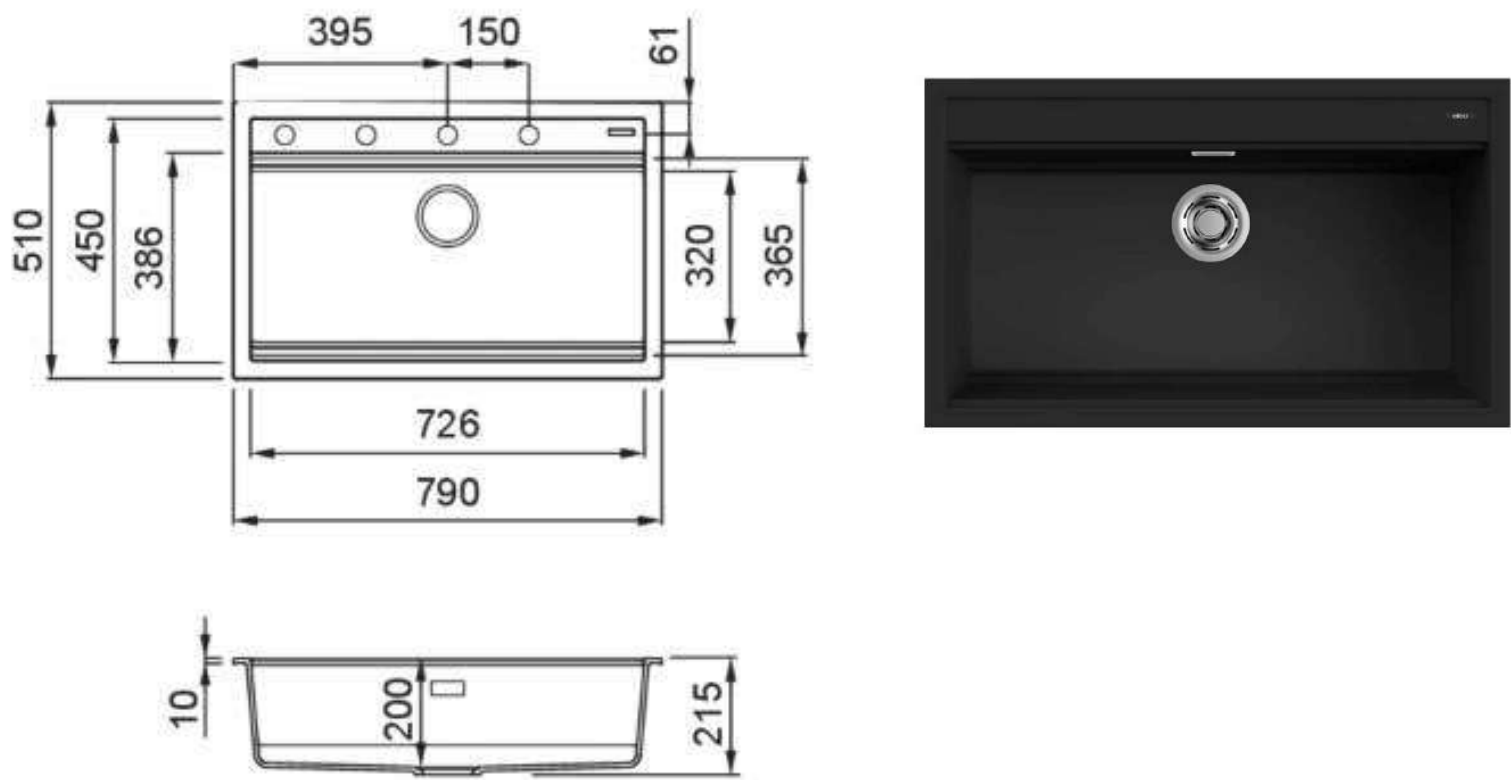

KITCHEN FINISHES

Nobilia cabinetry choices
https://www.nobilia.de/en/products/kitchens



FRONT 402
Havana oak reproduction



CARCASE 097
Havana oak reproduction



HANDLE 250
Bow Handle Black

KITCHEN WORKTOP

https://www.nobilia.de/en/products/design-elements/worktops/



WORKTOP 794
Concrete Satin grey reproduction (Xtra Ceramic)

1. THESE DRAWINGS MUST BE CHECKED BY THE CUSTOMER OR CONTRACTOR PRIOR TO APPROVAL. ANY ERRORS OR OMISSIONS MUST BE REPORTED IN WRITING TO BAUHU PRIOR TO COMMENCEMENT OF CONSTRUCTION.
2. ARCHITECTURAL DRAWINGS SHOULD BE READ IN CONJUNCTION WITH STRUCTURAL DETAILING AND FABRICATION GENERAL ASSEMBLY DRAWINGS.
3. FOR CONSTRUCTION PURPOSES, USE ONLY THE LATEST APPROVED DRAWINGS LABELED 'ISSUED FOR CONSTRUCTION'.
4. DO NOT SCALE FROM THIS DRAWING.
5. THE COMPANY OPERATES USING METRIC DIMENSIONS AS THE PRINCIPAL DENOMINATION.
6. ALL CONCRETE WORKS ARE OUTSIDE OF THE SCOPE OF THE COMPANY. INFORMATION REGARDING SLAB DESIGN AND CONNECTIONS IN THESE DRAWINGS ARE INTENDED FOR GUIDENCE ONLY. FOUNDATION AND SLAB WORKS SHOULD BE DESIGNED AND APPROVED BY A LOCAL STRUCTURAL ENGINEER.
7. THE COMPANY RETAINS FULL TITLE AND OWNERSHIP OF THESE PLANS AND DESIGNS. ANY UNAUTHORISED USE, REPRODUCTION, OR DISTRIBUTION OF THESE PLANS, WHETHER IN WHOLE OR PART, IS EXPRESSLY PROHIBITED WITHOUT PRIOR WRITTEN CONSENT.
8. THE HYBRID STEEL FRAME CONSTRUCTION SYSTEM AND METHODOLOGY (PATENT PENDING) DESCRIBED IN THESE PLANS HAS BEEN DEVELOPED BY THE COMPANY AND IS SUBJECT TO A PROVISIONAL PATENT APPLICATION & ASSIGNMENT - US APPLICATION NO. 63/722,841

No.	Revision	Date

ISSUED FOR:

Issued for information

Issued for client approval

Issued for fabrication

Issued for construction

The Charlston

DRAWING TITLE:	Kitchen Finishes
DRAWN BY:	Y.A.Clark
SCALE:	
DRAWING NO:	A118
DATE:	18/03/2026

1. THESE DRAWINGS MUST BE CHECKED BY THE CUSTOMER OR CONTRACTOR PRIOR TO APPROVAL. ANY ERRORS OR OMISSIONS MUST BE REPORTED IN WRITING TO BAUHU PRIOR TO COMMENCEMENT OF CONSTRUCTION.
2. ARCHITECTURAL DRAWINGS SHOULD BE READ IN CONJUNCTION WITH STRUCTURAL DETAILING AND FABRICATION GENERAL ASSEMBLY DRAWINGS.
3. FOR CONSTRUCTION PURPOSES, USE ONLY THE LATEST APPROVED DRAWINGS LABELED 'ISSUED FOR CONSTRUCTION'.
4. DO NOT SCALE FROM THIS DRAWING.
5. THE COMPANY OPERATES USING METRIC DIMENSIONS AS THE PRINCIPAL DENOMINATION.
6. ALL CONCRETE WORKS ARE OUTSIDE OF THE SCOPE OF THE COMPANY. INFORMATION REGARDING SLAB DESIGN AND CONNECTIONS IN THESE DRAWINGS ARE INTENDED FOR GUIDENCE ONLY. FOUNDATION AND SLAB WORKS SHOULD BE DESIGNED AND APPROVED BY A LOCAL STRUCTURAL ENGINEER.
7. THE COMPANY RETAINS FULL TITLE AND OWNERSHIP OF THESE PLANS AND DESIGNS. ANY UNAUTHORISED USE, REPRODUCTION, OR DISTRIBUTION OF THESE PLANS, WHETHER IN WHOLE OR PART, IS EXPRESSLY PROHIBITED WITHOUT PRIOR WRITTEN CONSENT.
8. THE HYBRID STEEL FRAME CONSTRUCTION SYSTEM AND METHODOLOGY (PATENT PENDING) DESCRIBED IN THESE PLANS HAS BEEN DEVELOPED BY THE COMPANY AND IS SUBJECT TO A PROVISIONAL PATENT APPLICATION & ASSIGNMENT - US APPLICATION NO. 63/722,841

No.	Revision	Date

ISSUED FOR:

Issued for information

Issued for client approval

Issued for fabrication

Issued for construction

The Charlston

DRAWING TITLE:

Kitchen 3D View

DRAWN BY:

Y.A.Clark



SCALE:

DRAWING NO:

A119

DATE:

18/03/2026

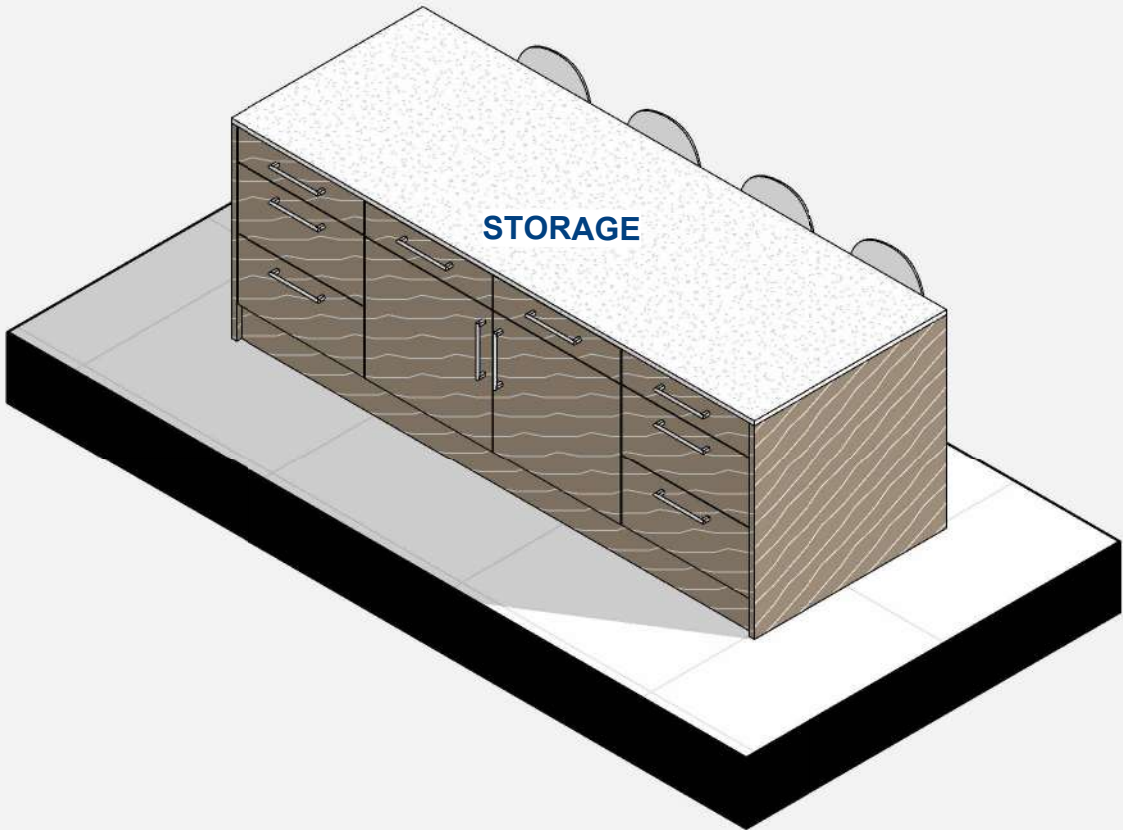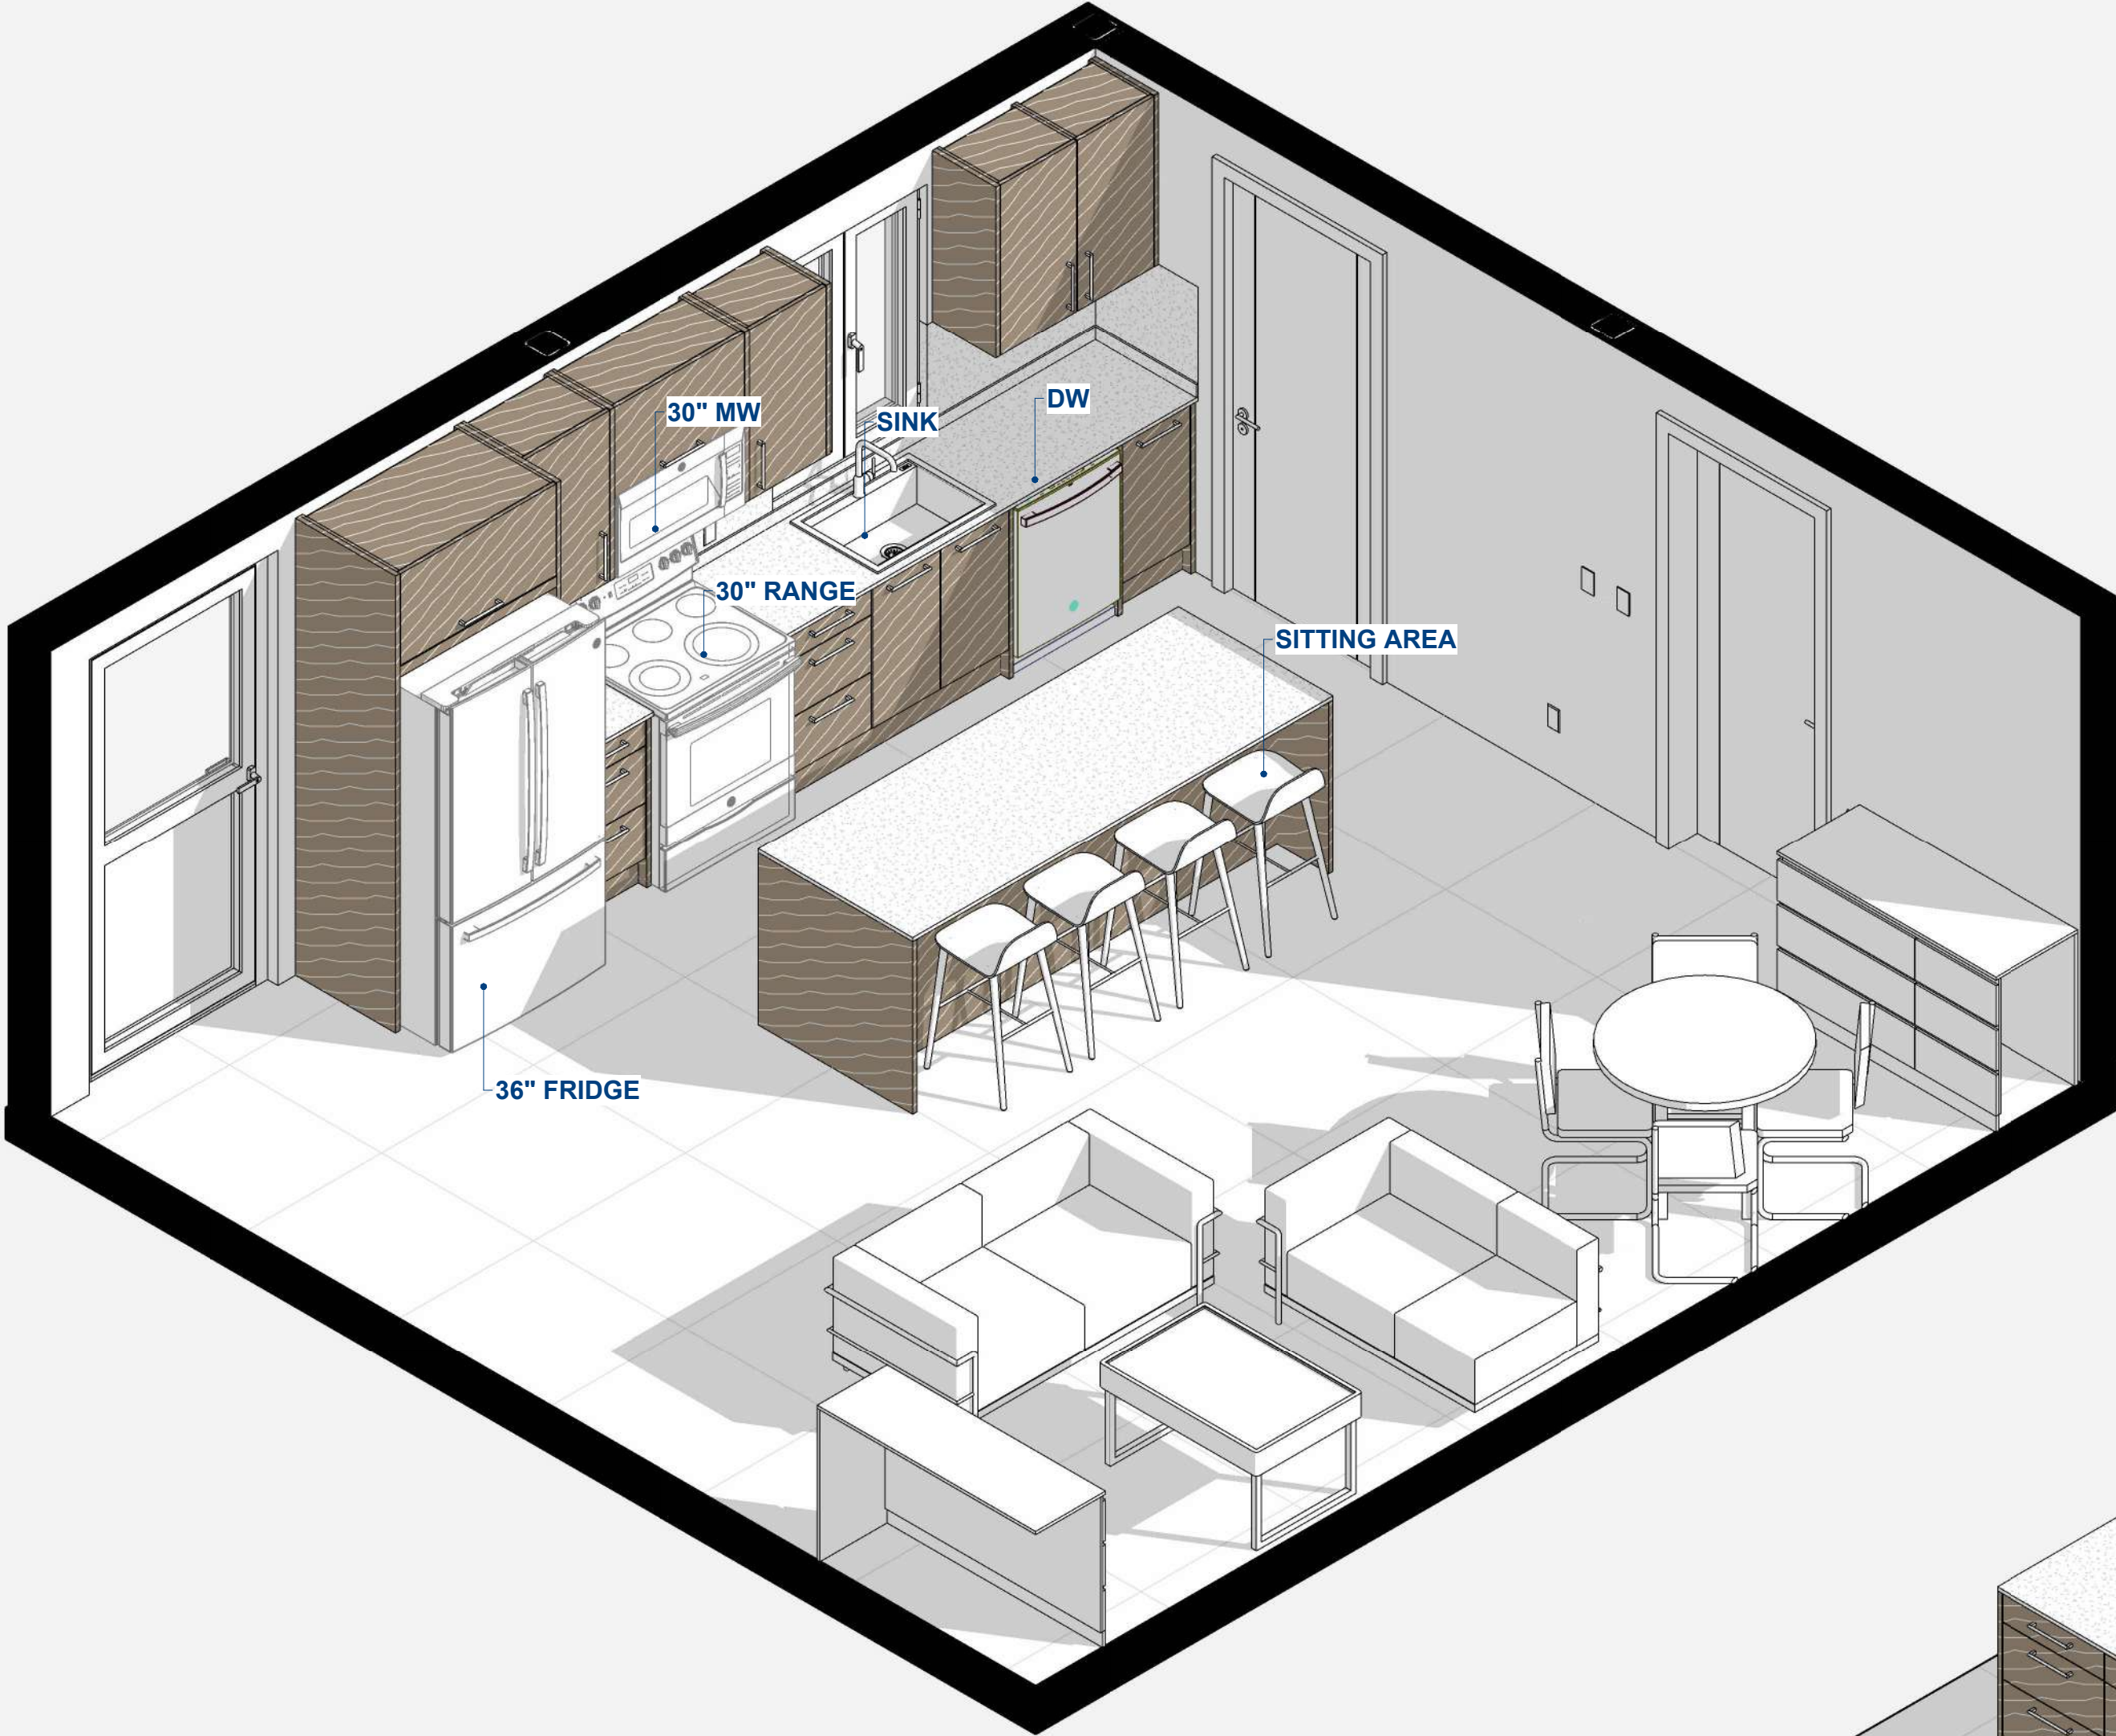


Microwave Over Range


Name: GE® 1.7 Cu. Ft. Over-the-Range Sensor Microwave Oven
Model: JVM6175SKSS
Dimensions: 16 5/16 H x 29 7/8 W x 15 9/16 D
Cabinet Width: 30 in
<https://www.geappliances.com/appliance/GE-1-7-Cu-Ft-Over-the-Range-Sensor-Microwave-Oven-JVM6175SKSS>

Range

Name: GE® 30" Free-Standing Electric Convection Fingerprint Resistant Range
Model: JB655YKFS
Dimensions: 47 H x 29 7/8 W x 28 D
Cabinet Width: 30 in
<https://www.geappliances.com/appliance/GE-30-Free-Standing-Electric-Convection-Fingerprint-Resistant-Range-JB655YKFS>


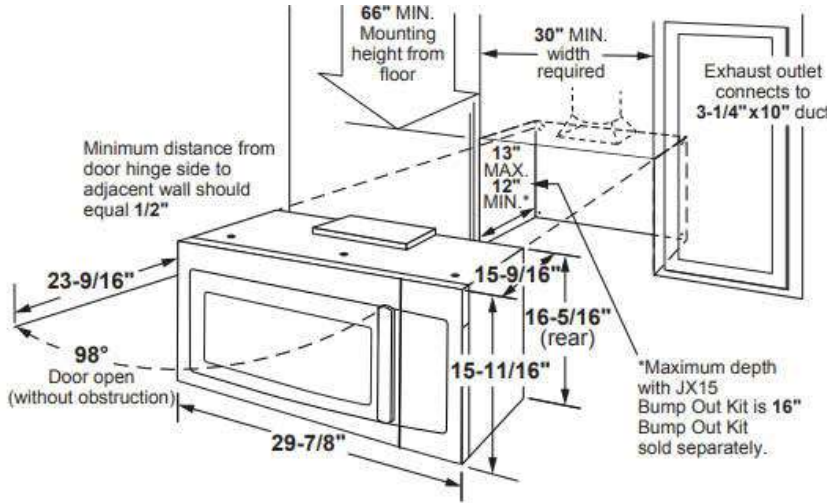


30" Free-Standing Electric Single Oven

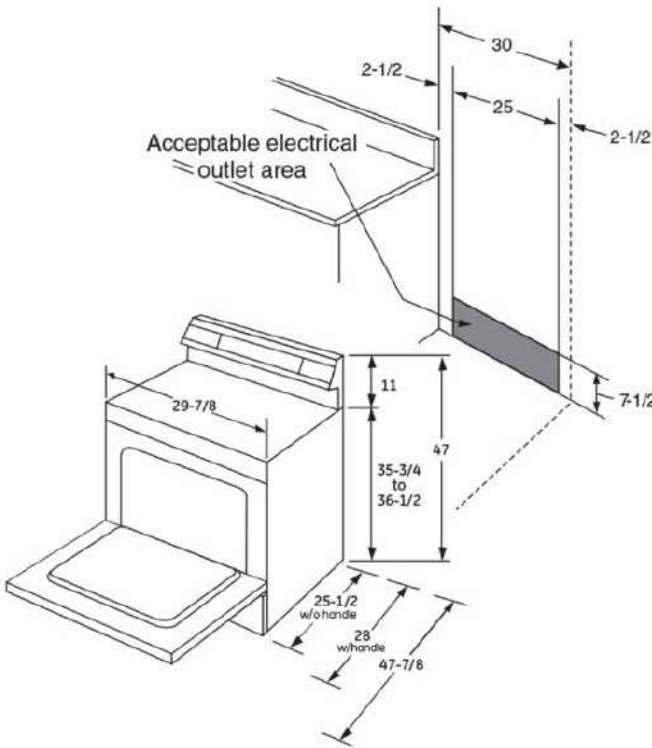

Dishwasher

Name: GE® ENERGY STAR® Top Control with Stainless Steel Interior Dishwasher with Sanitize Cycle & Dry Boost with Fan Assist
Model: GDT645SSNSS
Dimensions: 34 H x 23 3/4 W x 24 D
Cabinet Width: 24 in
[https://www.geappliances.com/appliance/GE-ENERGY-STAR-Top-Control-with-Stainless-Steel-Interior-Dishwasher-with-Sanitize-](https://www.geappliances.com/appliance/GE-ENERGY-STAR-Top-Control-with-Stainless-Steel-Interior-Dishwasher-with-Sanitize-Cycle-Dry-Boost-with-Fan-Assist-GDT645SSNSS)

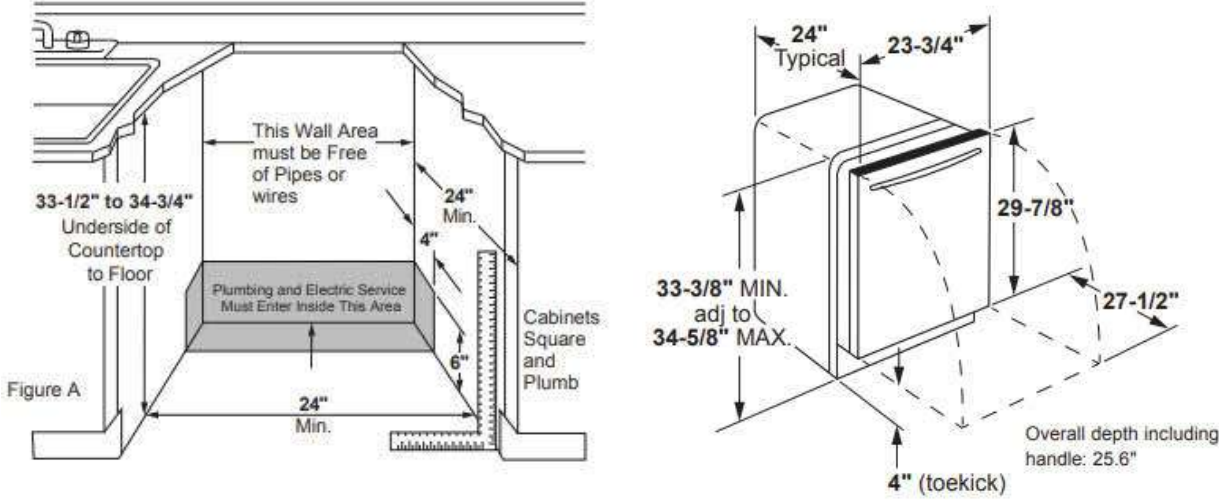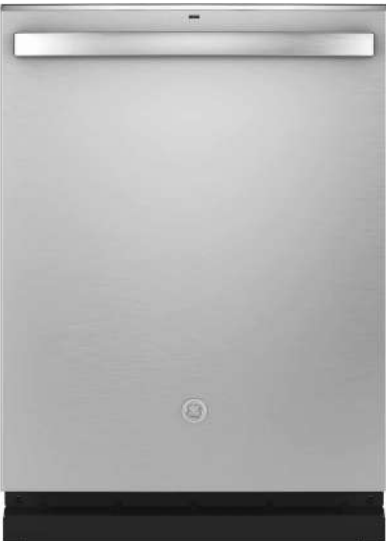



Fridge

Name: GE ENERGY STAR 27.0 Cu. Ft. Fingerprint Resistant French-Door Refrigerator
Model: GNE27JYMFS
Dimensions: 69 7/8 H x 35 3/4 W x 35 7/8 D
[https://www.geappliances.com/appliance/GE-ENERGY-STAR-27-0-Cu-Ft-](https://www.geappliances.com/appliance/GE-ENERGY-STAR-27-0-Cu-Ft-Fingerprint-Resistant-French-Door-Refrigerator-GNE27JYMFS)



DIMENSIONS AND INSTALLATION INFORMATION (IN INCHES)

OVERALL DIMENSIONS	Height to top of door - crown or flat (in.) A	69-7/8
	Height to top of hinge (in.) B	69-3/4
	Height to top of case (in.) C	68-5/8
	Case depth without door (in.) D	29
	Case depth less door handle (in.) E	33-3/8
	Case depth with door handle (in.) F	35-7/8
	Depth with fresh food door open 90° (in.) G	48-3/8
	Width (in.) H	35-3/4
	Width with door open 90° inc. door handle (in.) I	43-3/4
AIR CLEARANCES	Each side (in.)	1/8
	Top (in.)	1
	Back (in.)	2

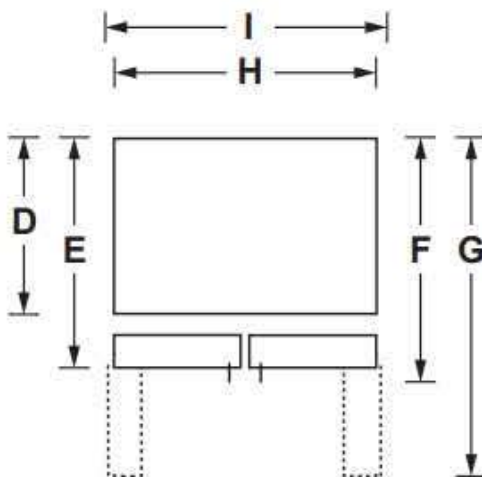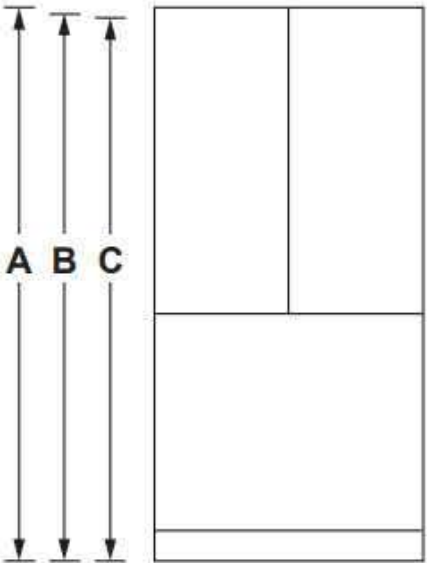

- THESE DRAWINGS MUST BE CHECKED BY THE CUSTOMER OR CONTRACTOR PRIOR TO APPROVAL. ANY ERRORS OR OMISSIONS MUST BE REPORTED IN WRITING TO BAUHU PRIOR TO COMMENCEMENT OF CONSTRUCTION.
- ARCHITECTURAL DRAWINGS SHOULD BE READ IN CONJUNCTION WITH STRUCTURAL DETAILING AND FABRICATION GENERAL ASSEMBLY DRAWINGS.
- FOR CONSTRUCTION PURPOSES, USE ONLY THE LATEST APPROVED DRAWINGS LABELED 'ISSUED FOR CONSTRUCTION'.
- DO NOT SCALE FROM THIS DRAWING.
- THE COMPANY OPERATES USING METRIC DIMENSIONS AS THE PRINCIPAL DENOMINATION.
- ALL CONCRETE WORKS ARE OUTSIDE OF THE SCOPE OF THE COMPANY. INFORMATION REGARDING SLAB DESIGN AND CONNECTIONS IN THESE DRAWINGS ARE INTENDED FOR GUIDANCE ONLY. FOUNDATION AND SLAB WORKS SHOULD BE DESIGNED AND APPROVED BY A LOCAL STRUCTURAL ENGINEER.
- THE COMPANY RETAINS FULL TITLE AND OWNERSHIP OF THESE PLANS AND DESIGNS. ANY UNAUTHORISED USE, REPRODUCTION, OR DISTRIBUTION OF THESE PLANS, WHETHER IN WHOLE OR PART, IS EXPRESSLY PROHIBITED WITHOUT PRIOR WRITTEN CONSENT.
- THE HYBRID STEEL FRAME CONSTRUCTION SYSTEM AND METHODOLOGY (PATENT PENDING) DESCRIBED IN THESE PLANS HAS BEEN DEVELOPED BY THE COMPANY AND IS SUBJECT TO A PROVISIONAL PATENT APPLICATION & ASSIGNMENT - US APPLICATION NO. 63/722,841

No.	Revision	Date

ISSUED FOR:

Issued for information

Issued for client approval

Issued for fabrication

Issued for construction

The Charlston

DRAWING TITLE:	Kitchen Appliances
DRAWN BY:	Y.A.Clark
SCALE:	
DRAWING NO:	A120
DATE:	18/03/2026

Note:

- Kitchen appliances are shown for cabinet design purposes only and are not supplied.

1. THESE DRAWINGS MUST BE CHECKED BY THE CUSTOMER OR CONTRACTOR PRIOR TO APPROVAL. ANY ERRORS OR OMISSIONS MUST BE REPORTED IN WRITING TO BAUHU PRIOR TO COMMENCEMENT OF CONSTRUCTION.
2. ARCHITECTURAL DRAWINGS SHOULD BE READ IN CONJUNCTION WITH STRUCTURAL DETAILING AND FABRICATION GENERAL ASSEMBLY DRAWINGS.
3. FOR CONSTRUCTION PURPOSES, USE ONLY THE LATEST APPROVED DRAWINGS LABELED 'ISSUED FOR CONSTRUCTION'.
4. DO NOT SCALE FROM THIS DRAWING.
5. THE COMPANY OPERATES USING METRIC DIMENSIONS AS THE PRINCIPAL DENOMINATION.
6. ALL CONCRETE WORKS ARE OUTSIDE OF THE SCOPE OF THE COMPANY. INFORMATION REGARDING SLAB DESIGN AND CONNECTIONS IN THESE DRAWINGS ARE INTENDED FOR GUIDENCE ONLY. FOUNDATION AND SLAB WORKS SHOULD BE DESIGNED AND APPROVED BY A LOCAL STRUCTURAL ENGINEER.
7. THE COMPANY RETAINS FULL TITLE AND OWNERSHIP OF THESE PLANS AND DESIGNS. ANY UNAUTHORISED USE, REPRODUCTION, OR DISTRIBUTION OF THESE PLANS, WHETHER IN WHOLE OR PART, IS EXPRESSLY PROHIBITED WITHOUT PRIOR WRITTEN CONSENT.
8. THE HYBRID STEEL FRAME CONSTRUCTION SYSTEM AND METHODOLOGY (PATENT PENDING) DESCRIBED IN THESE PLANS HAS BEEN DEVELOPED BY THE COMPANY AND IS SUBJECT TO A PROVISIONAL PATENT APPLICATION & ASSIGNMENT - US APPLICATION NO. 63/722,841

No.	Revision	Date

ISSUED FOR:

Issued for information

Issued for client approval

Issued for fabrication

Issued for construction

The Charlston

DRAWING TITLE:

Dimensions Ground Floor

DRAWN BY:

Y.A.Clark

SCALE:


1 : 50

DRAWING NO:


A122

DATE:

18/03/2026

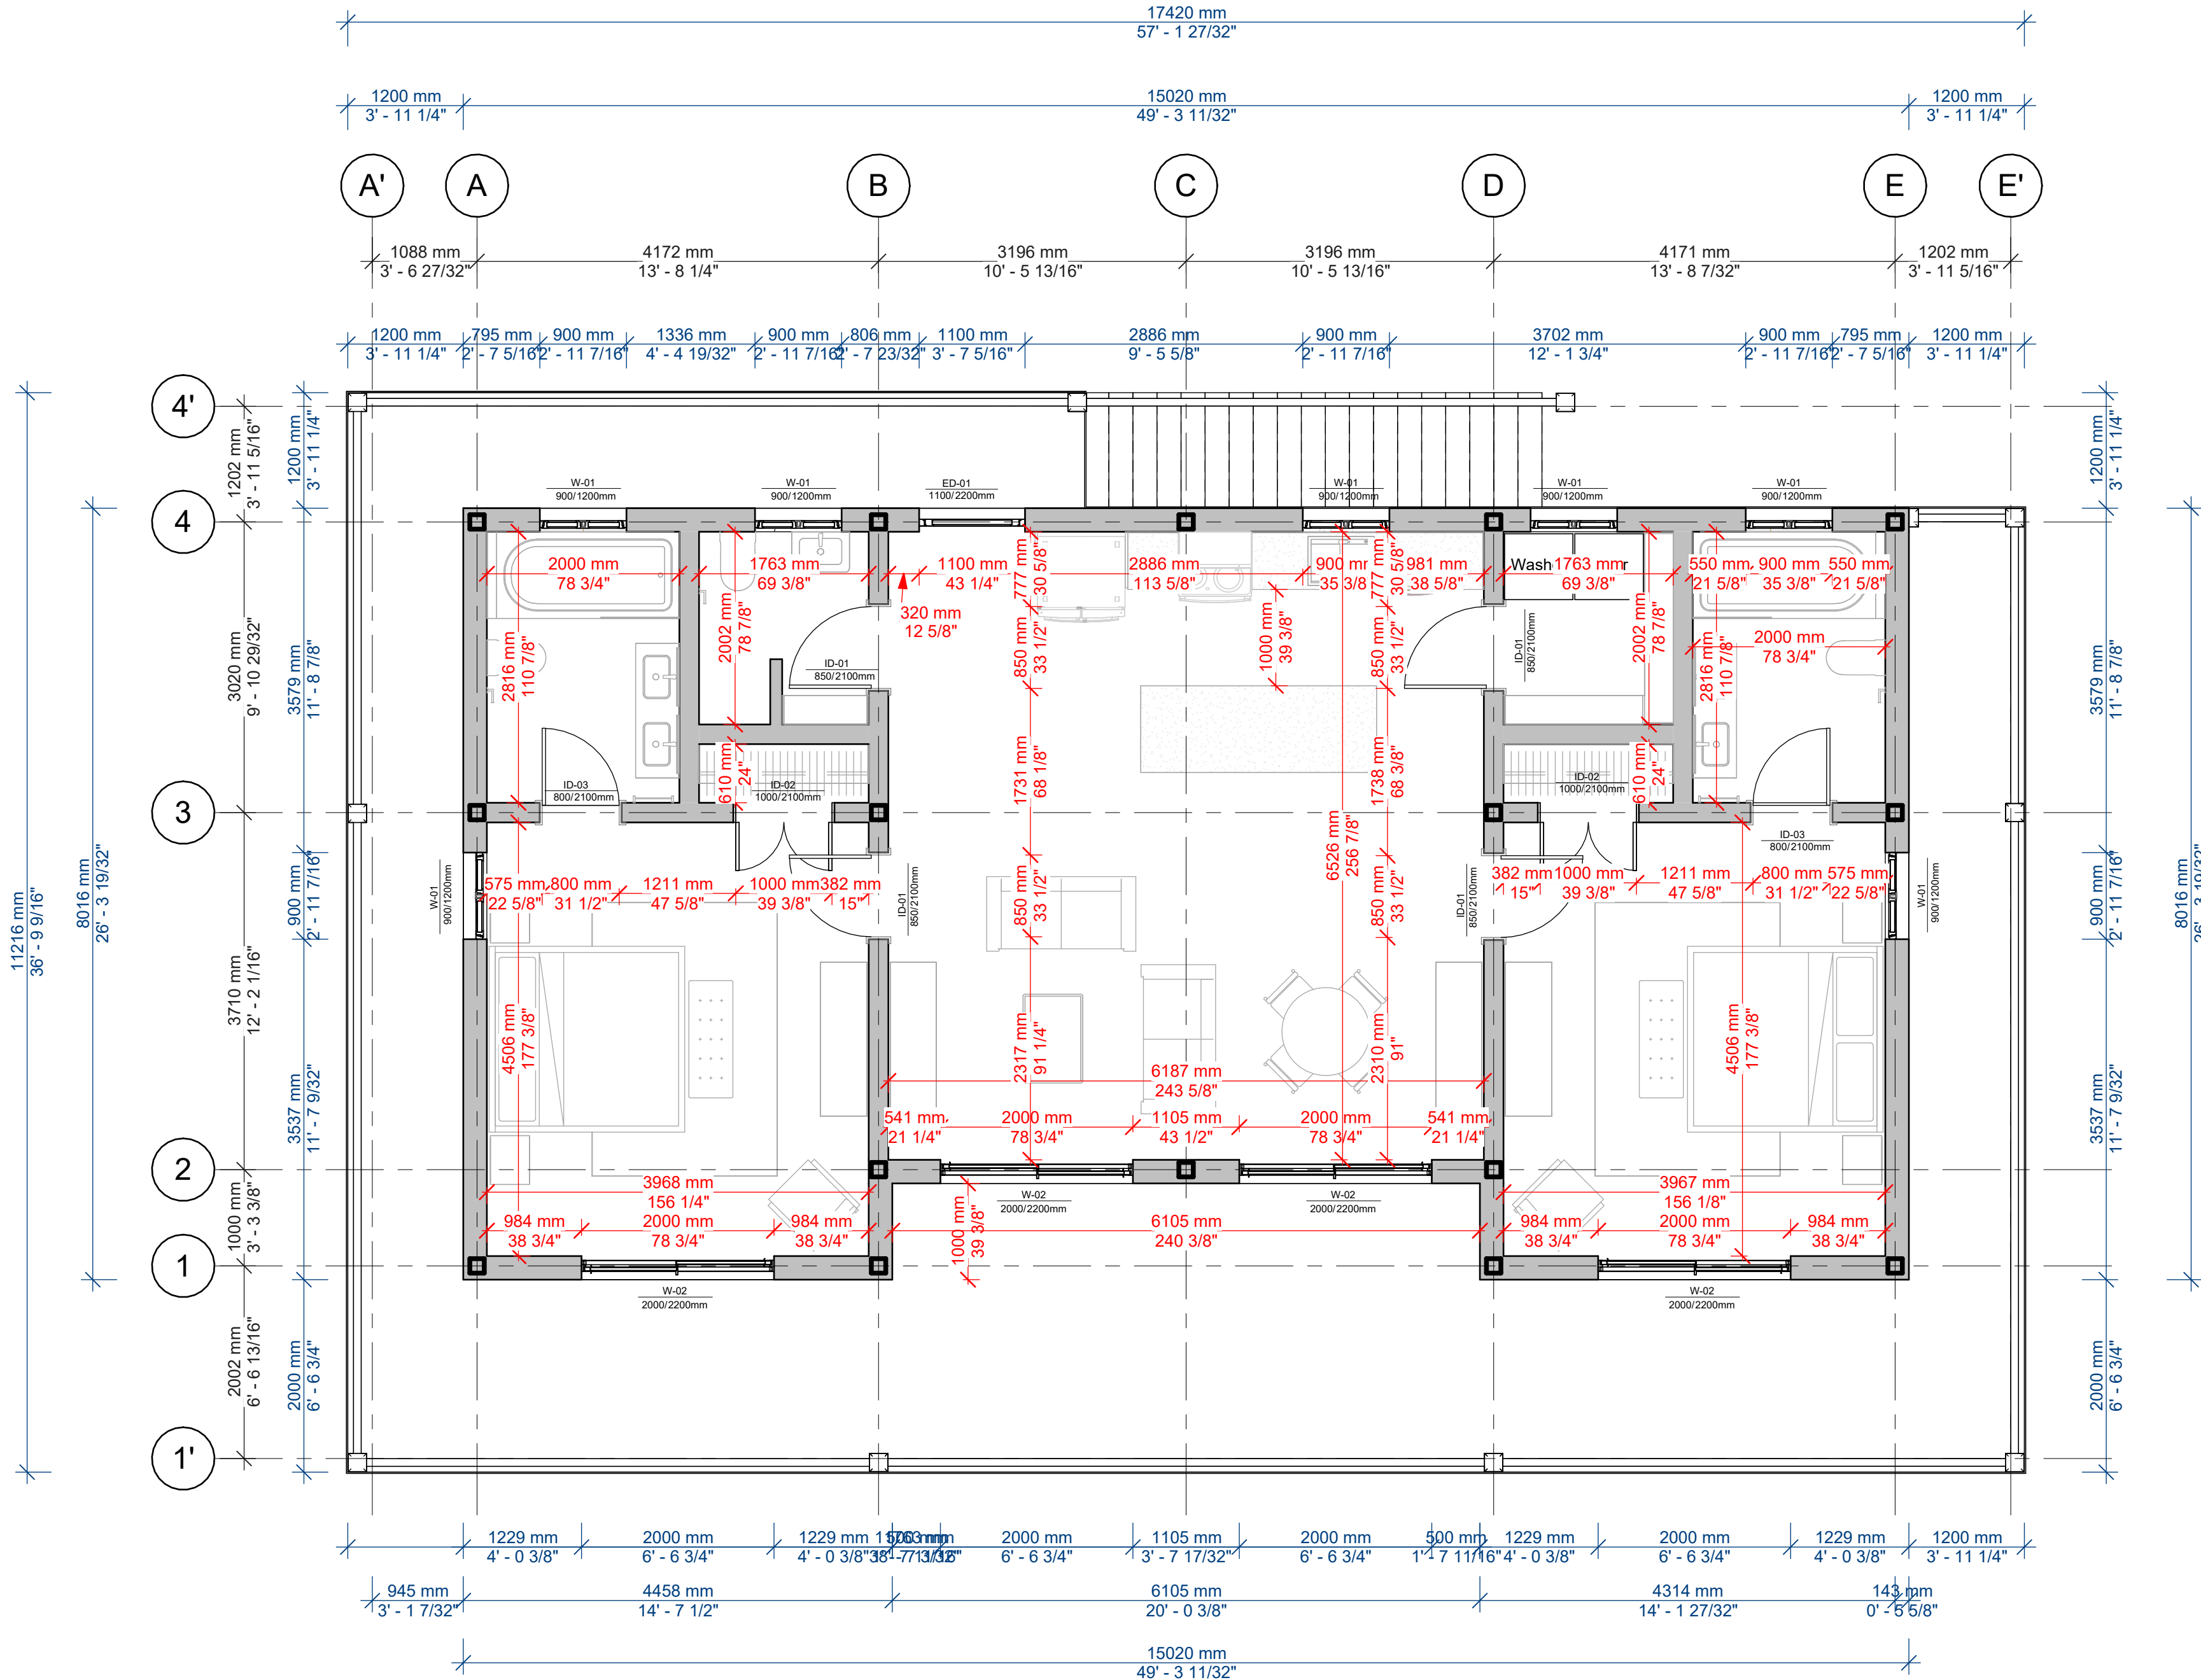

Electric Plan Sc: 1/60

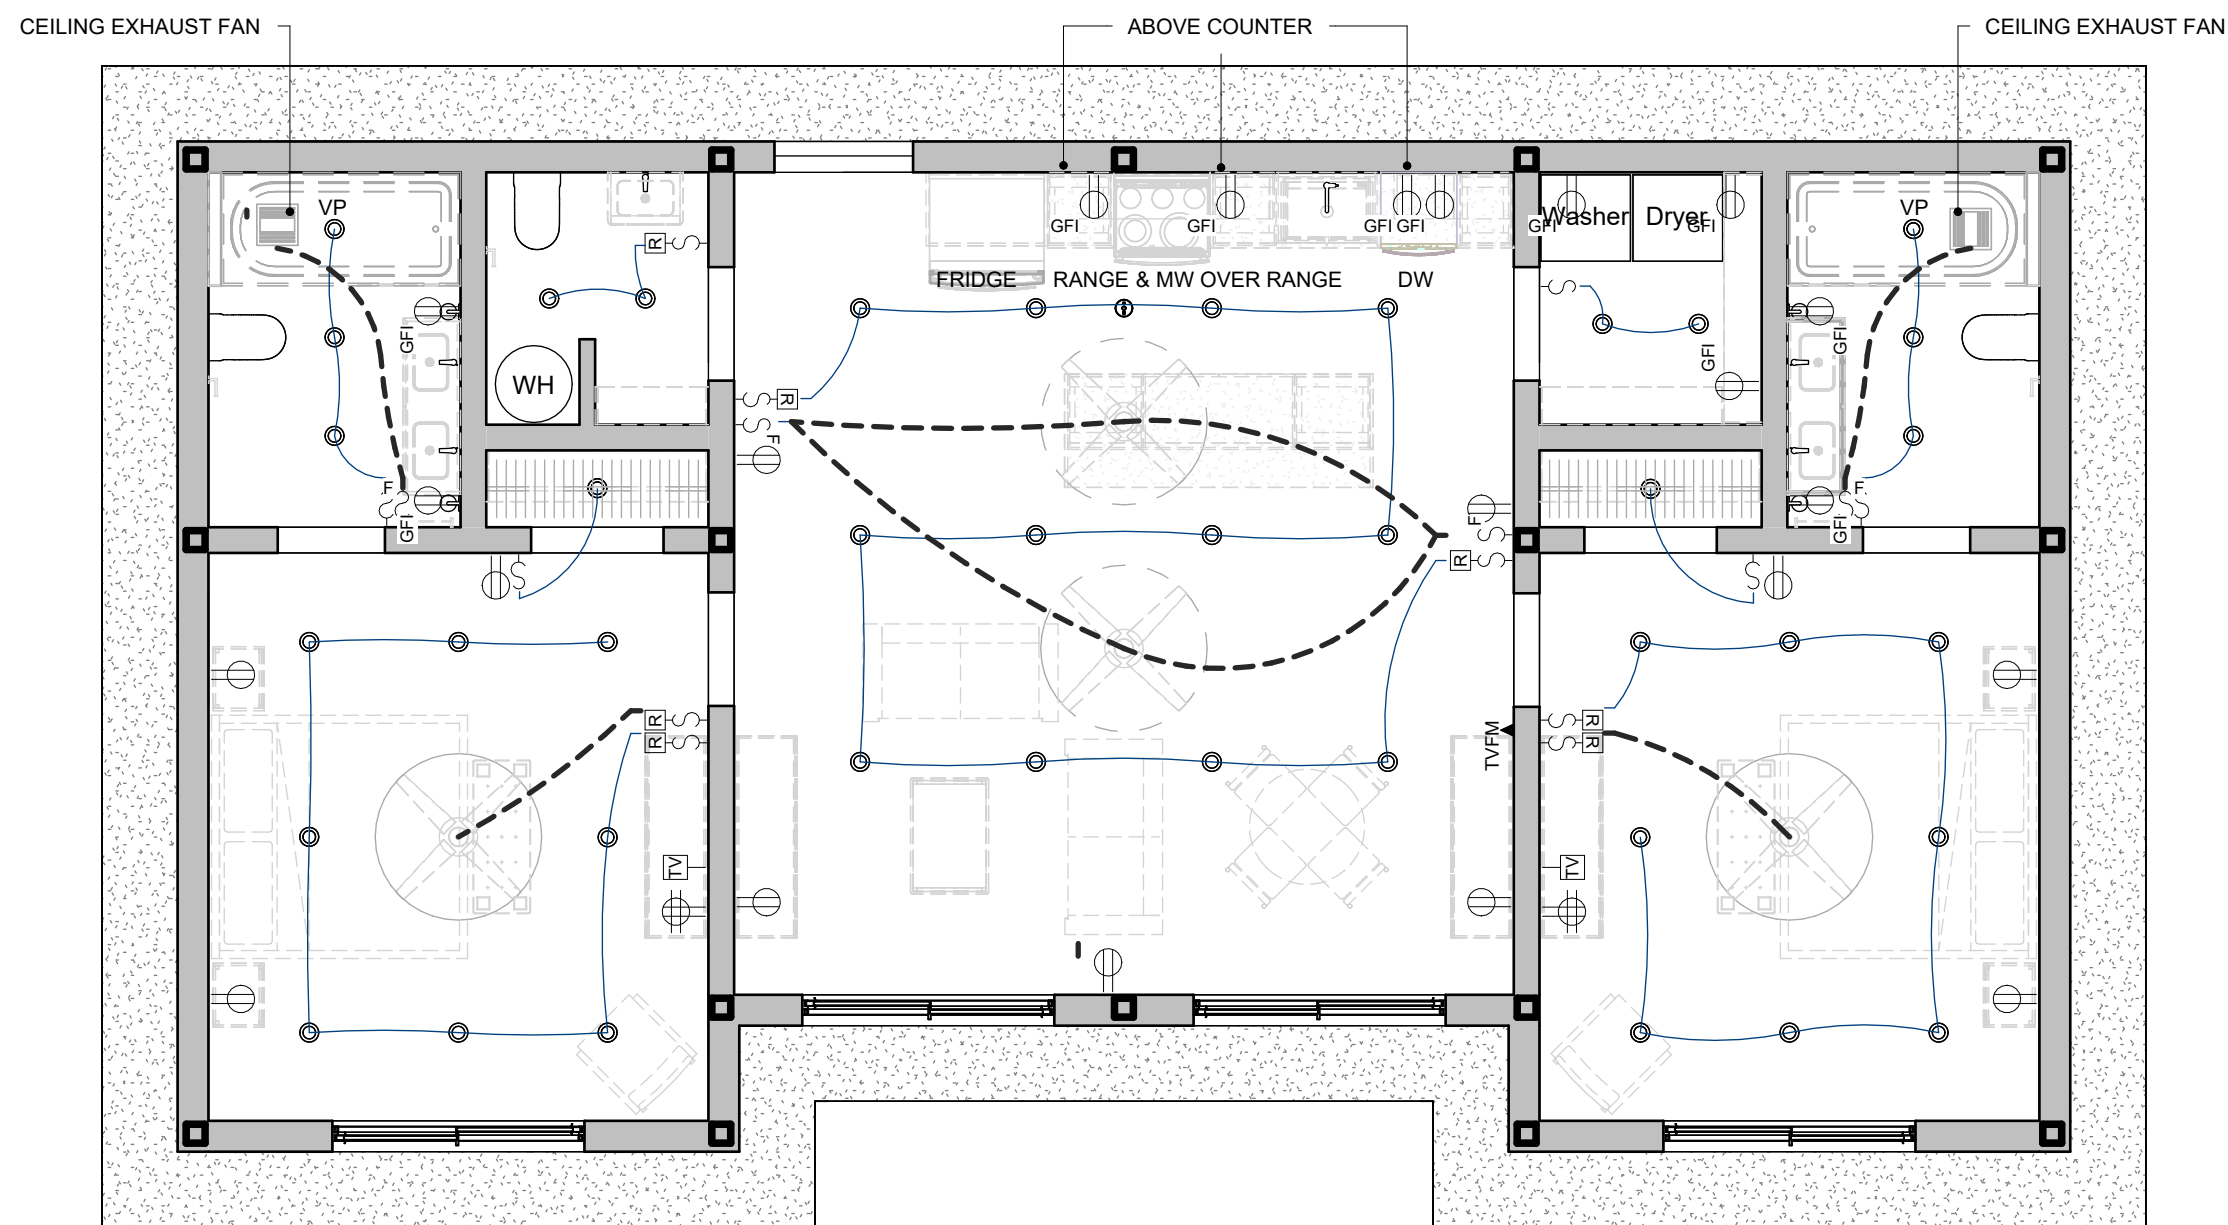

Symbols

	Television Outlet
	Duplex Outlet
	Quad Outlet
	GFI Outlet
	Waterproof GFI Outlet
	Single Switch
	Double Switch
	Ceiling Exhaust Fan Switch
	Rheostat Switch


Note:

- The electrical and HVAC installation including cables, conduits, surface mounted switches, power outlets, light fittings, fans, extractors, water heating equipment, air conditioning equipment, kitchen appliances, solar appliances, data and communication equipment, other electrical fixtures and fittings, are not supplied. Electrical plans are provided as a guide for contractor information only. Electrical system design, supply and installation should be carried out by a competent electrician.
- Electrical engineer to provide adequate grounding to all steel members.
- Air conditioning and flood vents by others.

Typical Panel 120/240 1 60h 3W

CKT. NO.	IDENTIFICATION	CIRCUIT BREAKER		
		BKR.	WIRE	KW.
1	General Lightning and Receptacles	15 A.	# 14	
2	General Lightning and Receptacles	15 A.	# 14	
3	General Lightning and Receptacles	15 A.	# 14	
4	General Lightning and Receptacles	15 A.	# 14	
5	General Lightning and Receptacles	15 A.	# 14	
6	GFI Receptacles	20 A.	# 12	
7	General Lightning and Receptacles	15 A.	# 14	
8	Kitchen Small Appliance Receptacles	20 A.	# 12	
9	Kitchen Small Appliance Receptacles	20 A.	# 12	1.5
10	Garbage Disposer	20 A.	# 12	1.2
11	Outdoor Lightning and Receptacles	20 A.	# 12	1.5
12	Dishwasher	20 A.	# 12	1.2
13	Refrigerator	20 A.	# 12	1.2
14	Microwave	20 A.	# 12	
15 17	Range/Oven	50 A.	# 6	12
16 18	AC/MSCU #1 (Living Room)	30 A.	# 10	3.6
19 21	Water Heater #1	30 A.	# 10	4.5
20 22	AC/MSCU #2 (Dining/Kitchen)	30 A.	# 10	3.6
23 25	AC/MSU #3 (Master Bedroom)	30 A.	# 10	3.6
24 26	AC/MSU #4 (Bedroom 2)	30 A.	# 10	3.6
27	Spare			
28 30	AC/MSU #5 (Bedroom 3)	30 A.	# 10	3.6
29	Spare			

Service Riser

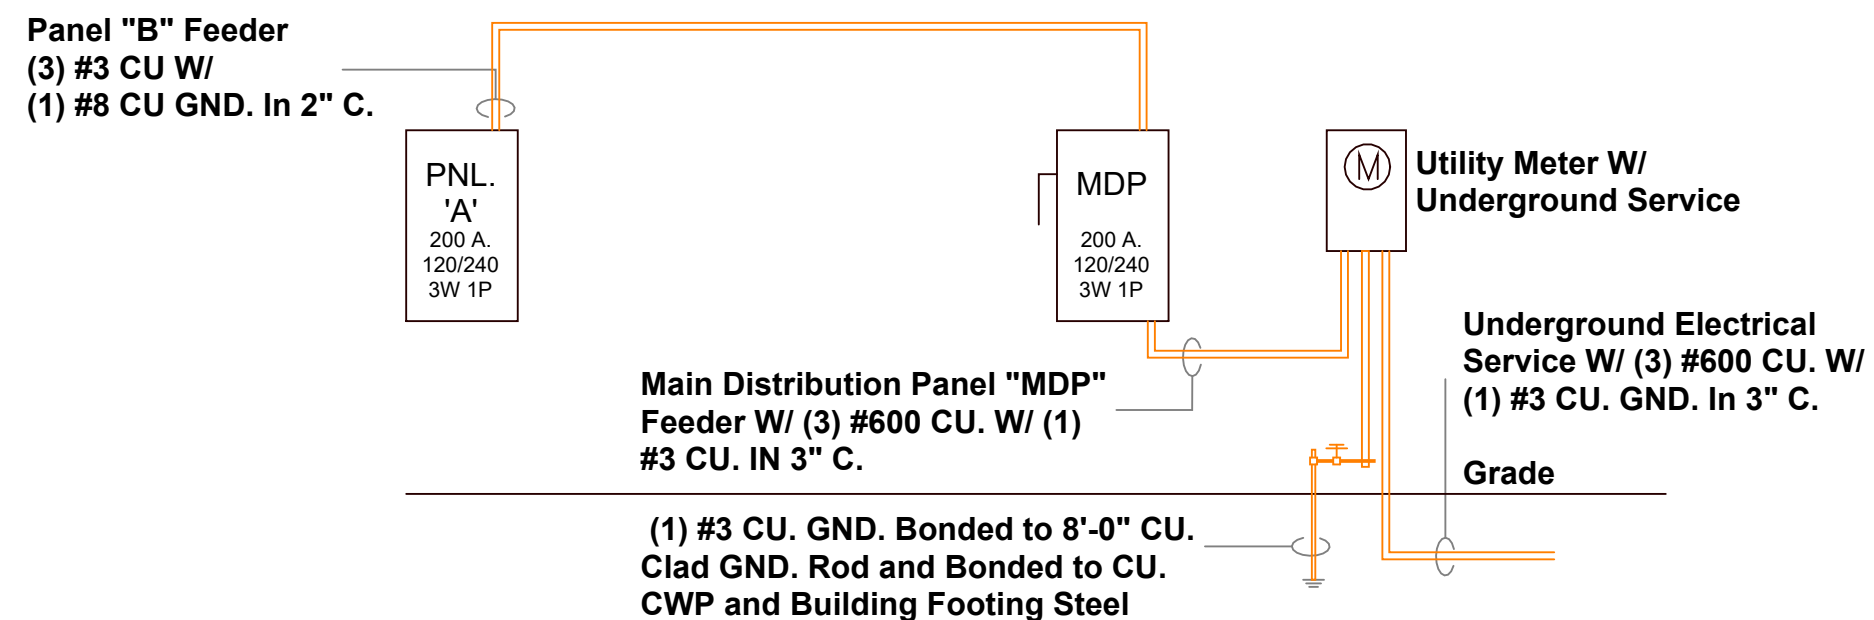

BAUHU
MODULAR • BUILDING • SOLUTIONS

1. THESE DRAWINGS MUST BE CHECKED BY THE CUSTOMER OR CONTRACTOR PRIOR TO APPROVAL. ANY ERRORS OR OMISSIONS MUST BE REPORTED IN WRITING TO BAUHU PRIOR TO COMMENCEMENT OF CONSTRUCTION.
2. ARCHITECTURAL DRAWINGS SHOULD BE READ IN CONJUNCTION WITH STRUCTURAL DETAILING AND FABRICATION GENERAL ASSEMBLY DRAWINGS.
3. FOR CONSTRUCTION PURPOSES, USE ONLY THE LATEST APPROVED DRAWINGS LABELED 'ISSUED FOR CONSTRUCTION'.
4. DO NOT SCALE FROM THIS DRAWING.
5. THE COMPANY OPERATES USING METRIC DIMENSIONS AS THE PRINCIPAL DENOMINATION.
6. ALL CONCRETE WORKS ARE OUTSIDE OF THE SCOPE OF THE COMPANY. INFORMATION REGARDING SLAB DESIGN AND CONNECTIONS IN THESE DRAWINGS ARE INTENDED FOR GUIDANCE ONLY. FOUNDATION AND SLAB WORKS SHOULD BE DESIGNED AND APPROVED BY A LOCAL STRUCTURAL ENGINEER.
7. THE COMPANY RETAINS FULL TITLE AND OWNERSHIP OF THESE PLANS AND DESIGNS. ANY UNAUTHORISED USE, REPRODUCTION, OR DISTRIBUTION OF THESE PLANS, WHETHER IN WHOLE OR PART, IS EXPRESSLY PROHIBITED WITHOUT PRIOR WRITTEN CONSENT.
8. THE HYBRID STEEL FRAME CONSTRUCTION SYSTEM AND METHODOLOGY (PATENT PENDING) DESCRIBED IN THESE PLANS HAS BEEN DEVELOPED BY THE COMPANY AND IS SUBJECT TO A PROVISIONAL PATENT APPLICATION & ASSIGNMENT - US APPLICATION NO. 63/722,841

[illegible]

ISSUED FOR:

Issued for information

Issued for client approval

Issued for fabrication

Issued for construction

The Charlston

DRAWING TITLE:

Electrical Plan

DRAWN BY:

Y.A.Clark

SCALE:

As indicated

DRAWING NO:


A123

DATE:

18/03/2026

Hot Water
Cold Water

1. THESE DRAWINGS MUST BE CHECKED BY THE CUSTOMER OR CONTRACTOR PRIOR TO APPROVAL. ANY ERRORS OR OMISSIONS MUST BE REPORTED IN WRITING TO BAUHU PRIOR TO COMMENCEMENT OF CONSTRUCTION.
2. ARCHITECTURAL DRAWINGS SHOULD BE READ IN CONJUNCTION WITH STRUCTURAL DETAILING AND FABRICATION GENERAL ASSEMBLY DRAWINGS.
3. FOR CONSTRUCTION PURPOSES, USE ONLY THE LATEST APPROVED DRAWINGS LABELED 'ISSUED FOR CONSTRUCTION'.
4. DO NOT SCALE FROM THIS DRAWING.
5. THE COMPANY OPERATES USING METRIC DIMENSIONS AS THE PRINCIPAL DENOMINATION.
6. ALL CONCRETE WORKS ARE OUTSIDE OF THE SCOPE OF THE COMPANY. INFORMATION REGARDING SLAB DESIGN AND CONNECTIONS IN THESE DRAWINGS ARE INTENDED FOR GUIDANCE ONLY. FOUNDATION AND SLAB WORKS SHOULD BE DESIGNED AND APPROVED BY A LOCAL STRUCTURAL ENGINEER.
7. THE COMPANY RETAINS FULL TITLE AND OWNERSHIP OF THESE PLANS AND DESIGNS. ANY UNAUTHORISED USE, REPRODUCTION, OR DISTRIBUTION OF THESE PLANS, WHETHER IN WHOLE OR PART, IS EXPRESSLY PROHIBITED WITHOUT PRIOR WRITTEN CONSENT.
8. THE HYBRID STEEL FRAME CONSTRUCTION SYSTEM AND METHODOLOGY (PATENT PENDING) DESCRIBED IN THESE PLANS HAS BEEN DEVELOPED BY THE COMPANY AND IS SUBJECT TO A PROVISIONAL PATENT APPLICATION & ASSIGNMENT - US APPLICATION NO. 63/722,841

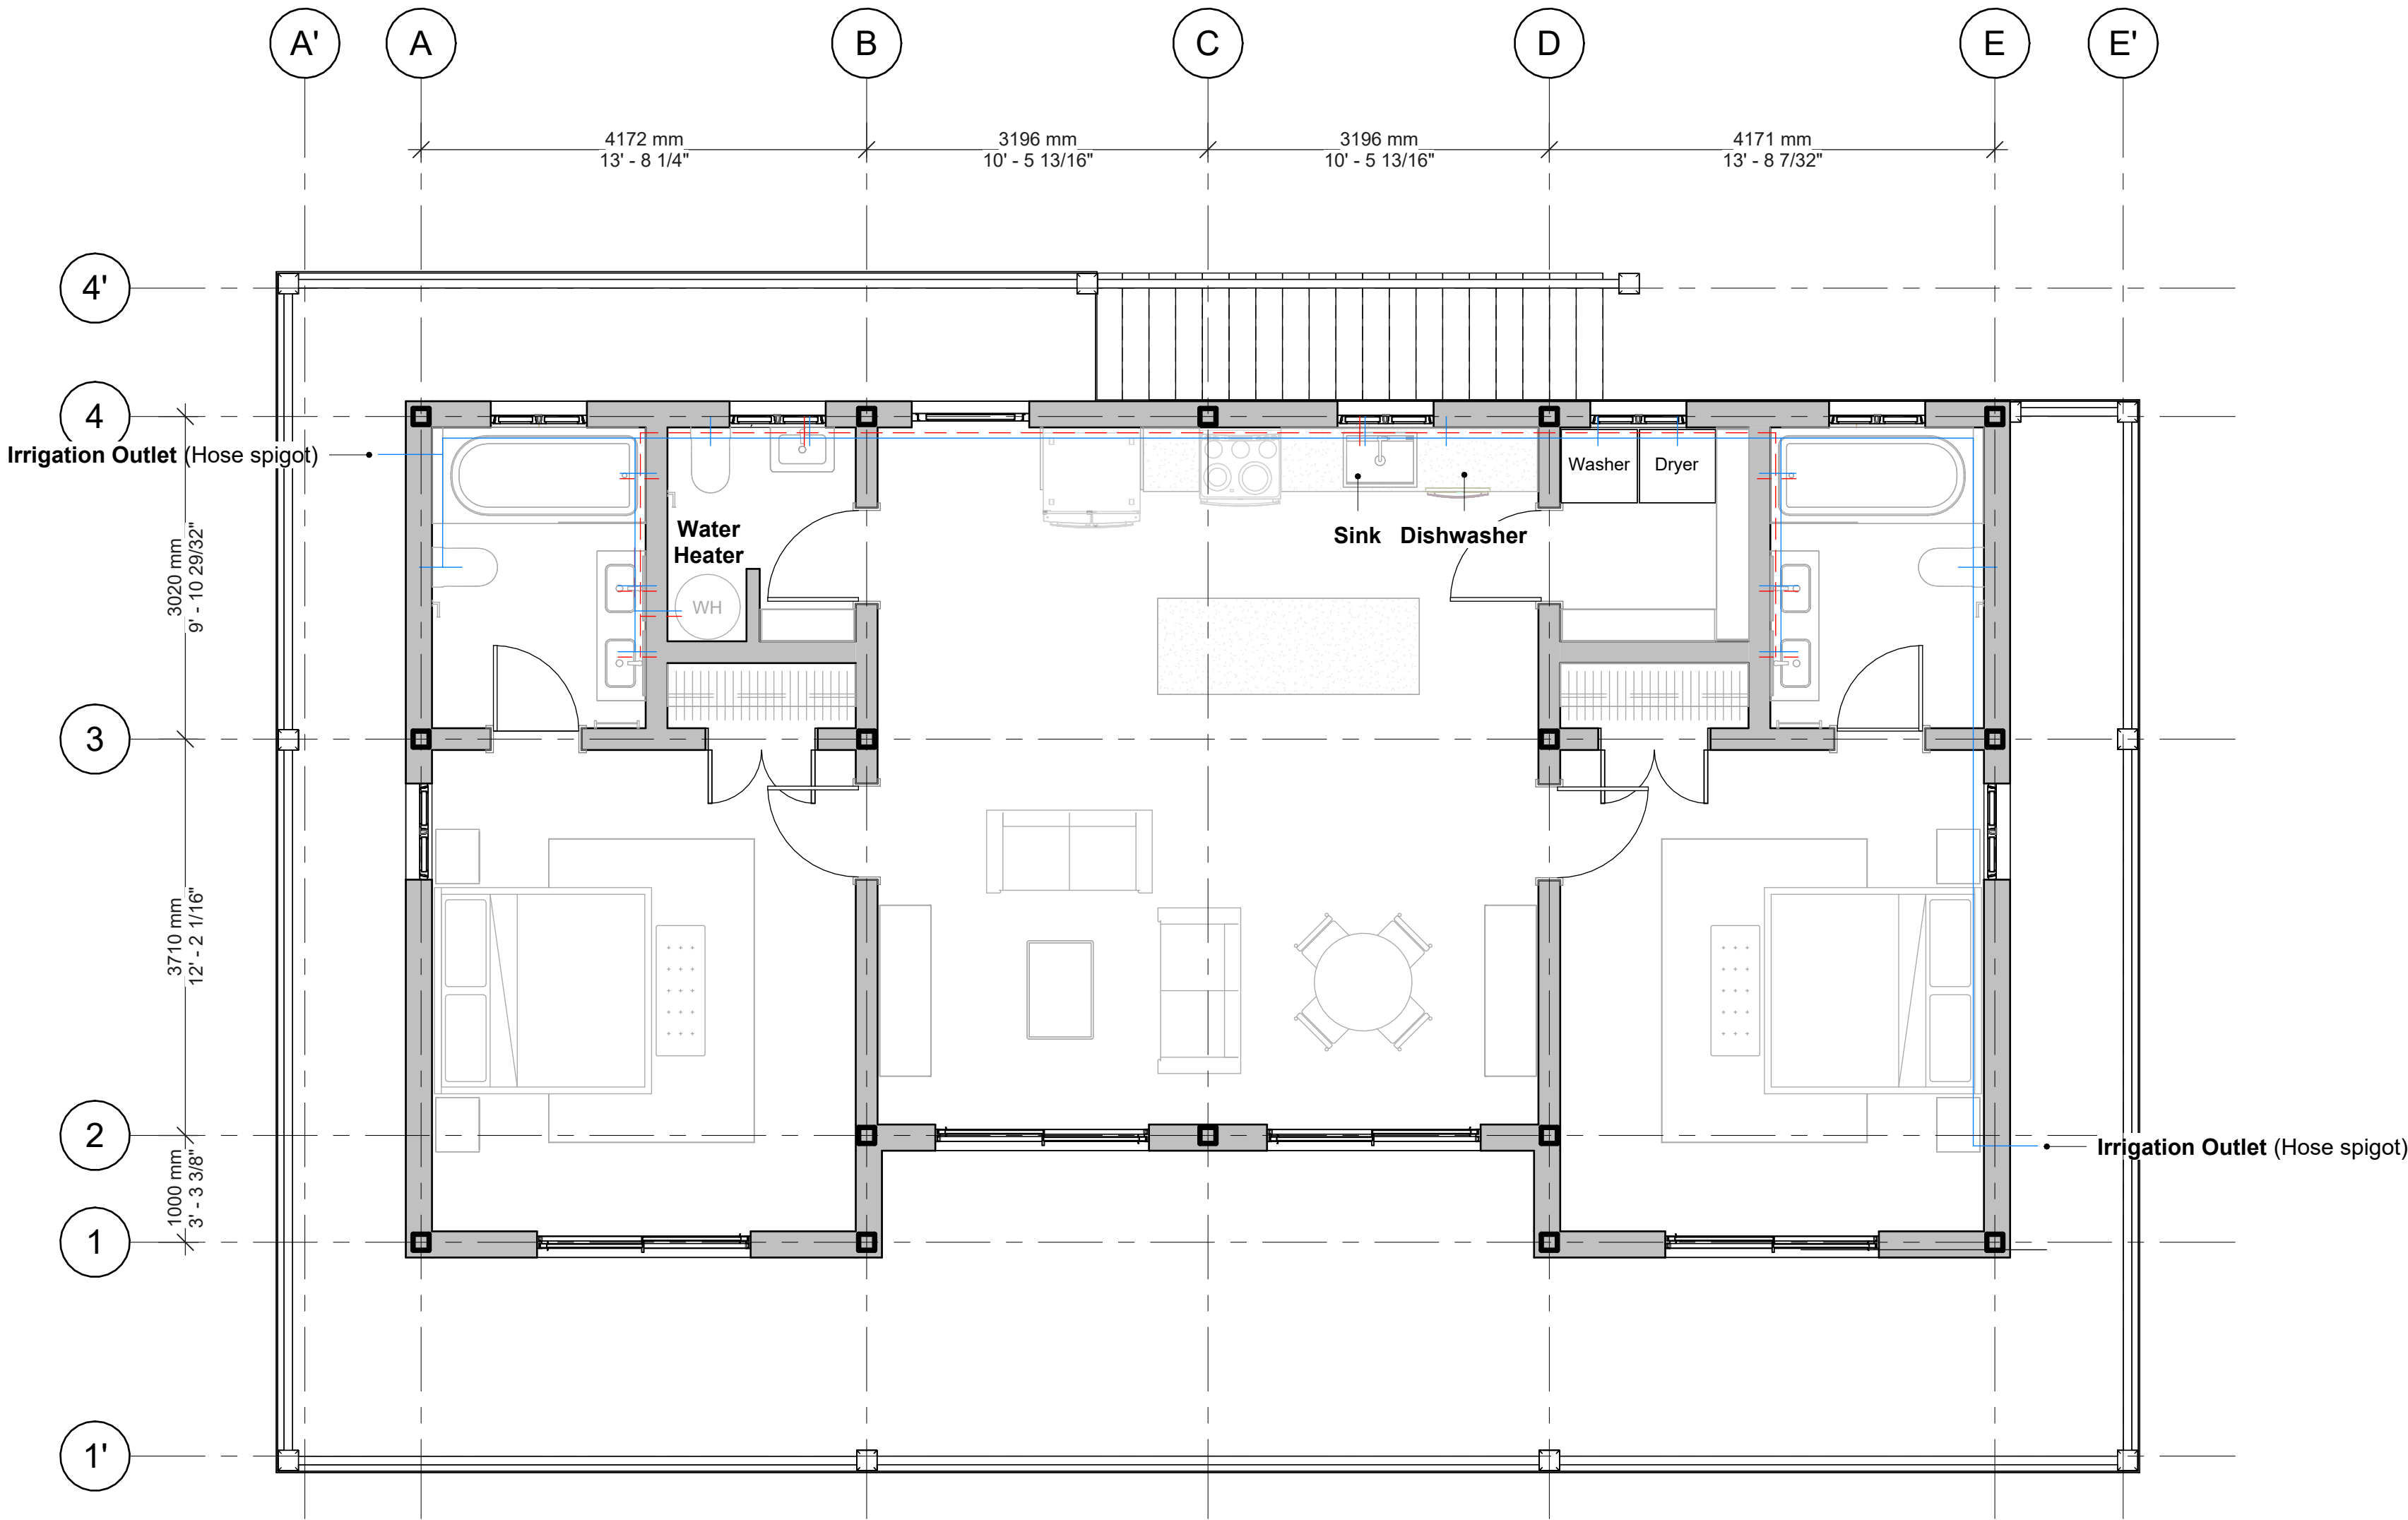

Note: Plumbing supply pipework, waste pipework, rainwater drain pipework, gutters, downpipes, pipe connections and sub-slab roughing 's are excluded. Plumbing plans are provided as a guide for contractor information only.

No.	Revision	Date

ISSUED FOR:

Issued for information

Issued for client approval

Issued for fabrication

Issued for construction

The Charlston

DRAWING TITLE:

Plumbing Plan

DRAWN BY:

Y.A.Clark

SCALE:

1 : 50

DRAWING NO:


A124

DATE:

18/03/2026

Toilet


Sanindusa
Model: Winner Confort F|D close coupled toilet
Reference: 144021
Dimensions: L65xW37xH47
Finishes: Vitreous China 00-White
Count: 3

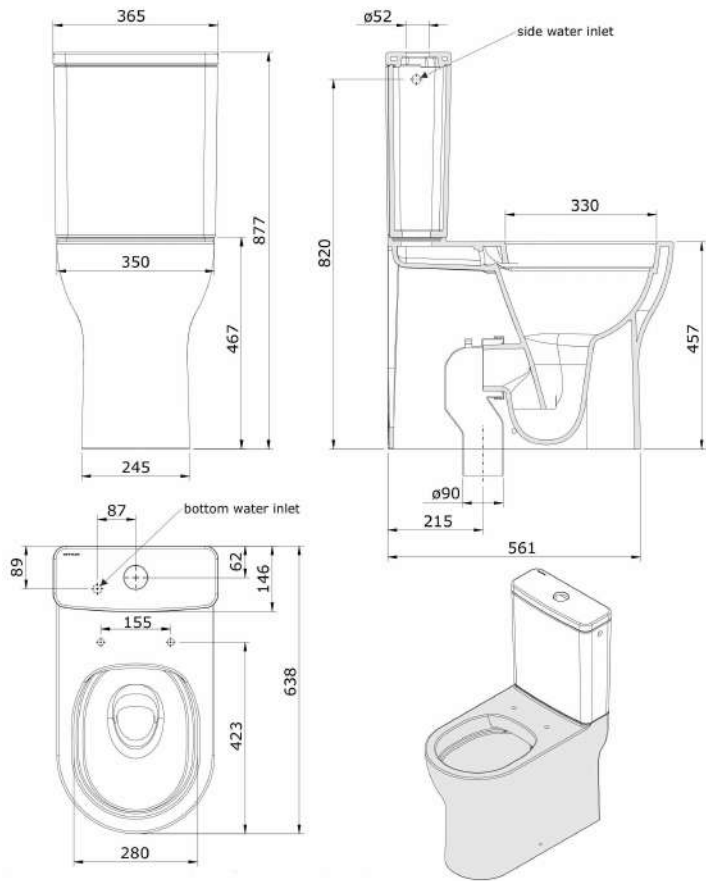

https://www.tec.sanindusa.pt/index.php?id=25&p=4573

Vanity Mixer

Bruma
Model: Nautic
Reference: 181 010 1CR
Finishes: Chrome
Count: 5
Room No: 1(2)&4&8(2)

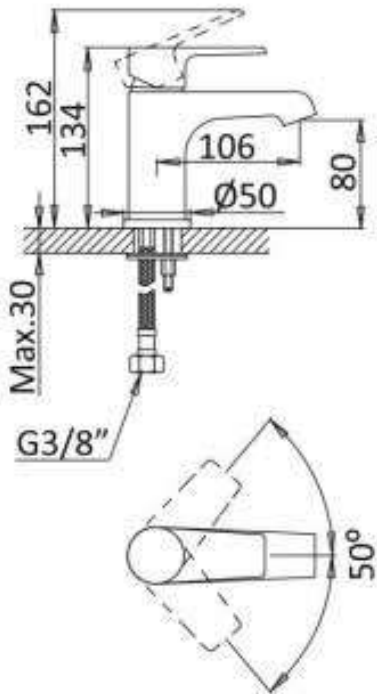

https://www.bruma.pt

Toilet Seat


Sanindusa
Model: Winner toilet seat with easyclip system
Reference: 24231
Finishes: Duroplast - 00-Chrome|White
Count: 3



https://www.tec.sanindusa.pt/index.php?id=25&p=4573

Kitchen Mixer


Bruma
Model: Kitchen Faucets
Name: Sink mixer with swivel spout and pull out handshower - Ginger
Reference: 122 700 3CR
Colour: Chrome
Count: 1

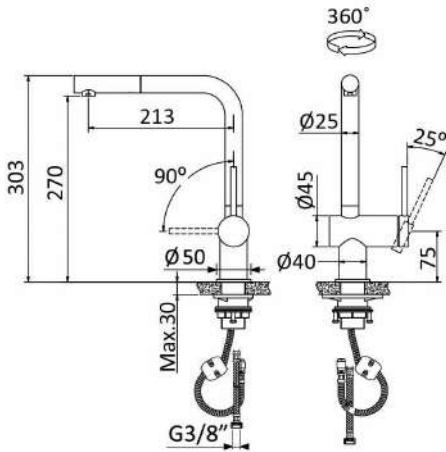

https://www.bruma.pt

Toilet roll holder

Bruma
Model: MARIS
Reference: 177 000 7CR
Finishes: Chrome
Count: 3
Room No: 1&4&8

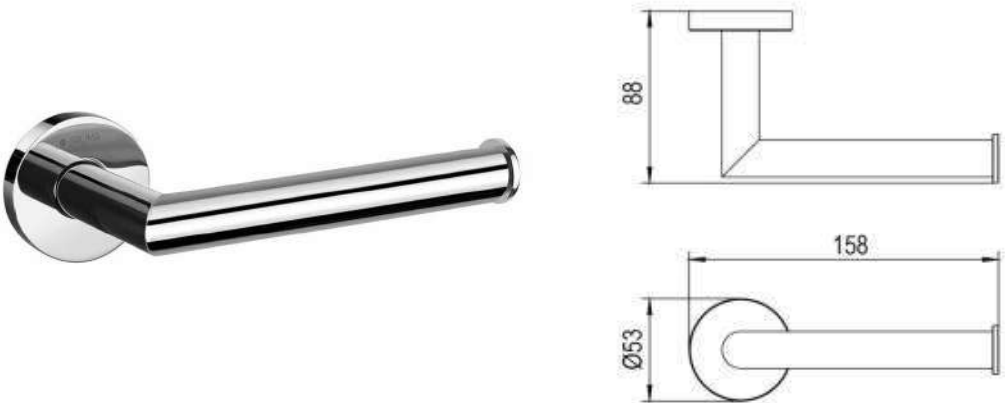

https://www.bruma.pt/index.php?page=products&prod=7734#open_product

Note:

- Sanitary ware, faucets, kitchen and bathroom equipment are provided. Plumbing supply pipework, waste and sub-slab roughings are excluded. Plumbing plan is provided as a guide for contractor information only.
- Shower glass screens are fixed.



- THESE DRAWINGS MUST BE CHECKED BY THE CUSTOMER OR CONTRACTOR PRIOR TO APPROVAL. ANY ERRORS OR OMISSIONS MUST BE REPORTED IN WRITING TO BAUHU PRIOR TO COMMENCEMENT OF CONSTRUCTION.
- ARCHITECTURAL DRAWINGS SHOULD BE READ IN CONJUNCTION WITH STRUCTURAL DETAILING AND FABRICATION GENERAL ASSEMBLY DRAWINGS.
- FOR CONSTRUCTION PURPOSES, USE ONLY THE LATEST APPROVED DRAWINGS LABELED 'ISSUED FOR CONSTRUCTION'.
- DO NOT SCALE FROM THIS DRAWING.
- THE COMPANY OPERATES USING METRIC DIMENSIONS AS THE PRINCIPAL DENOMINATION.
- ALL CONCRETE WORKS ARE OUTSIDE OF THE SCOPE OF THE COMPANY. INFORMATION REGARDING SLAB DESIGN AND CONNECTIONS IN THESE DRAWINGS ARE INTENDED FOR GUIDENCE ONLY. FOUNDATION AND SLAB WORKS SHOULD BE DESIGNED AND APPROVED BY A LOCAL STRUCTURAL ENGINEER.
- THE COMPANY RETAINS FULL TITLE AND OWNERSHIP OF THESE PLANS AND DESIGNS. ANY UNAUTHORISED USE, REPRODUCTION, OR DISTRIBUTION OF THESE PLANS, WHETHER IN WHOLE OR PART, IS EXPRESSLY PROHIBITED WITHOUT PRIOR WRITTEN CONSENT.
- THE HYBRID STEEL FRAME CONSTRUCTION SYSTEM AND METHODOLOGY (PATENT PENDING) DESCRIBED IN THESE PLANS HAS BEEN DEVELOPED BY THE COMPANY AND IS SUBJECT TO A PROVISIONAL PATENT APPLICATION & ASSIGNMENT - US APPLICATION NO. 63/722,841

No.	Revision	Date

ISSUED FOR:

Issued for information

Issued for client approval

Issued for fabrication

Issued for construction

The Charlston

DRAWING TITLE:	Bathroom Schedule
DRAWN BY:	Y.A.Clark
SCALE:	
DRAWING NO:	A125
DATE:	18/03/2026

Bathtub


Sanindusa
Model: Vértice
Name: 190x90 Vértice bathtub
Reference: 806200
Finishes: 00-White
Dimensions: 900x1900 mm
Count: 2
Note:
Side panel - Panel Vértice 190 - Code: 806201
50 automatic pop-up waste for bathtub - Code:490
80 fixing kit for bathtub - Code: 813



<https://www.tec.sanindusa.pt/panel-vertice-190>
<https://www.tec.sanindusa.pt/50-automatic-pop-up-for-bathtub>
<https://www.tec.sanindusa.pt/80-fix-kit-feets-for-bathtub>
<https://www.tec.sanindusa.pt/bathtub-vertice-190x90>

Bath-Shower System

Bruma
Model: Nautic
Name: Bath-shower system for wall mounting with adjustable ABS head shower Ø230mm and shower rail
Reference: 181 261 1CR
Colour: Chrome
Count: 2

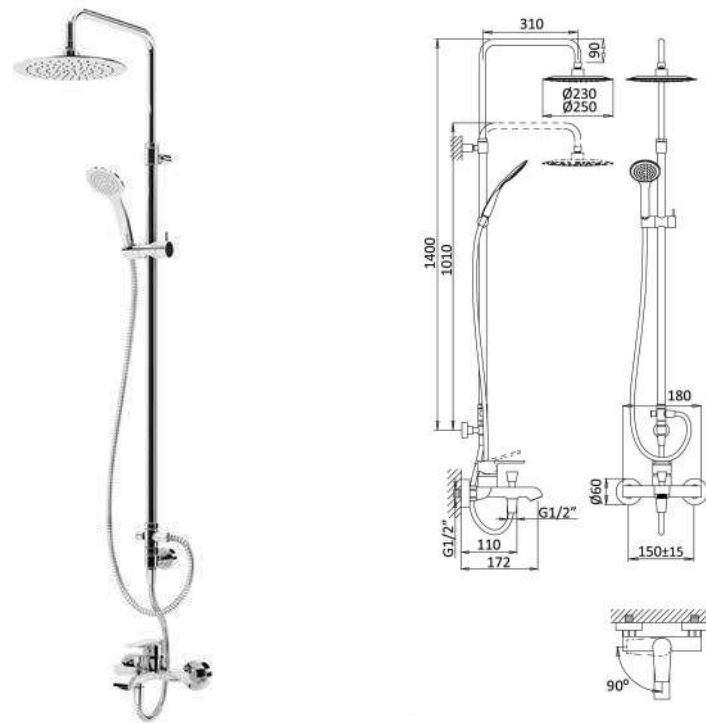

<https://www.bruma.pt>

Bath Screen

Sanindusa
Model: Safira
Name: Safira bath screen
Reference: 89510100
Finishes: Chrome - 5mm tempered glass
Dimensions: 136cm H, 82cm L
Count: 2



<https://www.tec.sanindusa.pt/safira-bath-screen>



1. THESE DRAWINGS MUST BE CHECKED BY THE CUSTOMER OR CONTRACTOR PRIOR TO APPROVAL. ANY ERRORS OR OMISSIONS MUST BE REPORTED IN WRITING TO BAUHU PRIOR TO COMMENCEMENT OF CONSTRUCTION.
2. ARCHITECTURAL DRAWINGS SHOULD BE READ IN CONJUNCTION WITH STRUCTURAL DETAILING AND FABRICATION GENERAL ASSEMBLY DRAWINGS.
3. FOR CONSTRUCTION PURPOSES, USE ONLY THE LATEST APPROVED DRAWINGS LABELED 'ISSUED FOR CONSTRUCTION'.
4. DO NOT SCALE FROM THIS DRAWING.
5. THE COMPANY OPERATES USING METRIC DIMENSIONS AS THE PRINCIPAL DENOMINATION.
6. ALL CONCRETE WORKS ARE OUTSIDE OF THE SCOPE OF THE COMPANY. INFORMATION REGARDING SLAB DESIGN AND CONNECTIONS IN THESE DRAWINGS ARE INTENDED FOR GUIDENCE ONLY. FOUNDATION AND SLAB WORKS SHOULD BE DESIGNED AND APPROVED BY A LOCAL STRUCTURAL ENGINEER.
7. THE COMPANY RETAINS FULL TITLE AND OWNERSHIP OF THESE PLANS AND DESIGNS. ANY UNAUTHORISED USE, REPRODUCTION, OR DISTRIBUTION OF THESE PLANS, WHETHER IN WHOLE OR PART, IS EXPRESSLY PROHIBITED WITHOUT PRIOR WRITTEN CONSENT.
8. THE HYBRID STEEL FRAME CONSTRUCTION SYSTEM AND METHODOLOGY (PATENT PENDING) DESCRIBED IN THESE PLANS HAS BEEN DEVELOPED BY THE COMPANY AND IS SUBJECT TO A PROVISIONAL PATENT APPLICATION & ASSIGNMENT - US APPLICATION NO. 63/722,841

No.	Revision	Date

ISSUED FOR:

Issued for information

Issued for client approval

Issued for fabrication

Issued for construction

The Charlston

DRAWING TITLE:	Bathroom Schedule 2
DRAWN BY:	Y.A.Clark
SCALE:	
DRAWING NO:	A126
DATE:	18/03/2026


Note:

- Sanitary ware, faucets, kitchen and bathroom equipment are provided. Plumbing supply pipework, waste and sub-slab roughings are excluded. Plumbing plan is provided as a guide for contractor information only.
- Shower glass screens are fixed.

Room No:4 Powder Room


Washbasin

Kitbanho
Model: LAVATÓRIO KLOSS STD ALT.2 - 60S
Finishes: White Bright (glossy)
Dimensions: 600mm
Count: 1

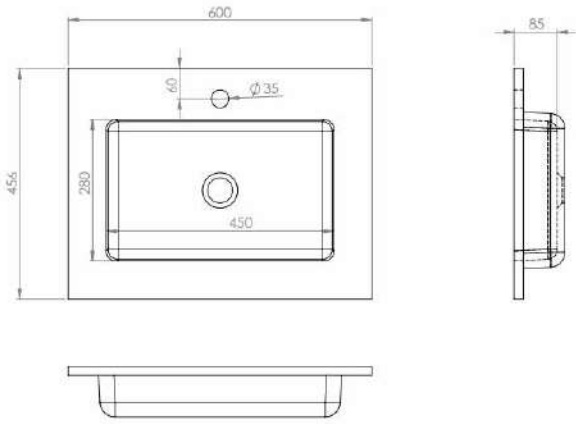

Bathroom Furniture


Kitbanho
Model: SARA ALT. 50 - 60S
Finishes: light grey
Dimensions: 600mm
Count: 1

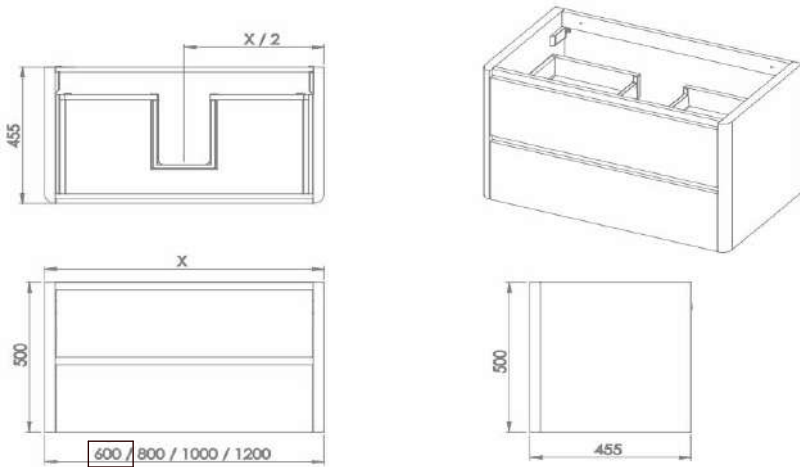

Room No:1&8 Bathrooms


Washbasin

Kitbanho
Model: LAV. BANCA KLOSS STD ALT.10 - 140 D
Finishes: White Bright (glossy)
Dimensions: 1400mm
Count: 2

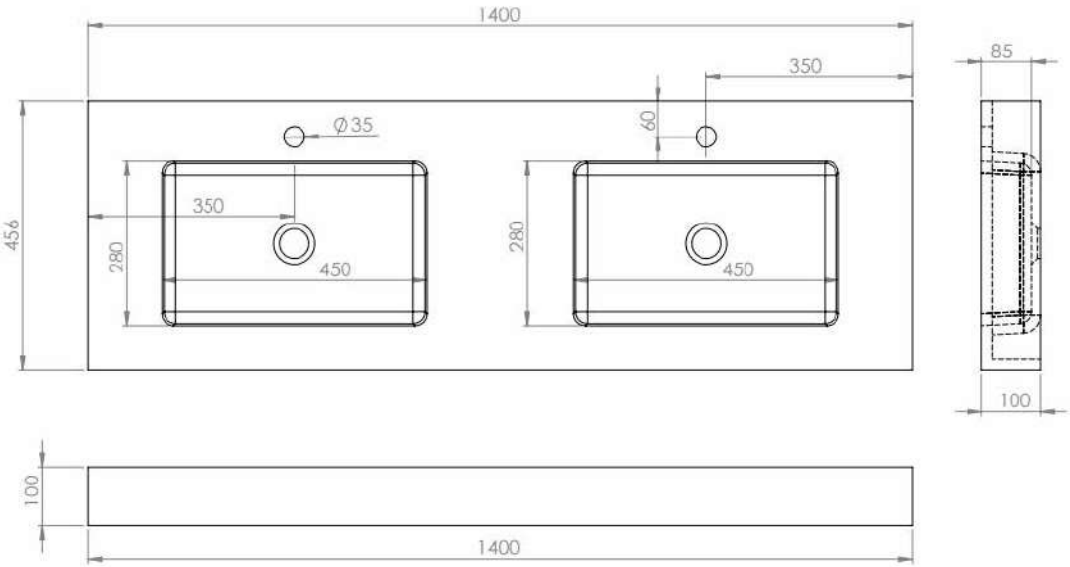

Bathroom Furniture

Kitbanho
Model: OLIMPO ALT. 50 140 DD
Finishes: white
Dimensions: 1400mm
Count: 2

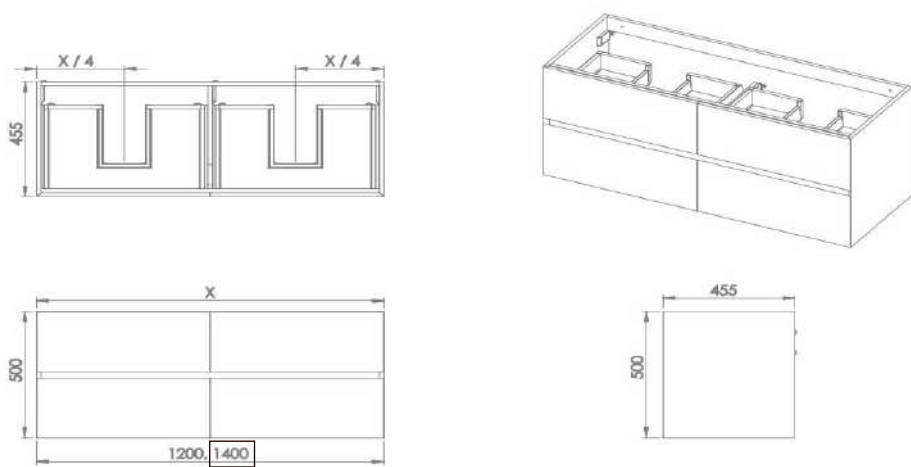

Mirror

Kitbanho
Model: Simple
Dimension: 60x100mm
Count: 4



1. THESE DRAWINGS MUST BE CHECKED BY THE CUSTOMER OR CONTRACTOR PRIOR TO APPROVAL. ANY ERRORS OR OMISSIONS MUST BE REPORTED IN WRITING TO BAUHU PRIOR TO COMMENCEMENT OF CONSTRUCTION.
2. ARCHITECTURAL DRAWINGS SHOULD BE READ IN CONJUNCTION WITH STRUCTURAL DETAILING AND FABRICATION GENERAL ASSEMBLY DRAWINGS.
3. FOR CONSTRUCTION PURPOSES, USE ONLY THE LATEST APPROVED DRAWINGS LABELED 'ISSUED FOR CONSTRUCTION'.
4. DO NOT SCALE FROM THIS DRAWING.
5. THE COMPANY OPERATES USING METRIC DIMENSIONS AS THE PRINCIPAL DENOMINATION.
6. ALL CONCRETE WORKS ARE OUTSIDE OF THE SCOPE OF THE COMPANY. INFORMATION REGARDING SLAB DESIGN AND CONNECTIONS IN THESE DRAWINGS ARE INTENDED FOR GUIDENCE ONLY. FOUNDATION AND SLAB WORKS SHOULD BE DESIGNED AND APPROVED BY A LOCAL STRUCTURAL ENGINEER.
7. THE COMPANY RETAINS FULL TITLE AND OWNERSHIP OF THESE PLANS AND DESIGNS. ANY UNAUTHORISED USE, REPRODUCTION, OR DISTRIBUTION OF THESE PLANS, WHETHER IN WHOLE OR PART, IS EXPRESSLY PROHIBITED WITHOUT PRIOR WRITTEN CONSENT.
8. THE HYBRID STEEL FRAME CONSTRUCTION SYSTEM AND METHODOLOGY (PATENT PENDING) DESCRIBED IN THESE PLANS HAS BEEN DEVELOPED BY THE COMPANY AND IS SUBJECT TO A PROVISIONAL PATENT APPLICATION & ASSIGNMENT - US APPLICATION NO. 63/722,841

No.	Revision	Date

ISSUED FOR:

Issued for information

Issued for client approval

Issued for fabrication

Issued for construction

The Charlston

DRAWING TITLE:	Bathroom Furnitures
DRAWN BY:	Y.A.Clark
SCALE:	
DRAWING NO:	A127
DATE:	18/03/2026

1. THESE DRAWINGS MUST BE CHECKED BY THE CUSTOMER OR CONTRACTOR PRIOR TO APPROVAL. ANY ERRORS OR OMISSIONS MUST BE REPORTED IN WRITING TO BAUHU PRIOR TO COMMENCEMENT OF CONSTRUCTION.
2. ARCHITECTURAL DRAWINGS SHOULD BE READ IN CONJUNCTION WITH STRUCTURAL DETAILING AND FABRICATION GENERAL ASSEMBLY DRAWINGS.
3. FOR CONSTRUCTION PURPOSES, USE ONLY THE LATEST APPROVED DRAWINGS LABELED 'ISSUED FOR CONSTRUCTION'.
4. DO NOT SCALE FROM THIS DRAWING.
5. THE COMPANY OPERATES USING METRIC DIMENSIONS AS THE PRINCIPAL DENOMINATION.
6. ALL CONCRETE WORKS ARE OUTSIDE OF THE SCOPE OF THE COMPANY. INFORMATION REGARDING SLAB DESIGN AND CONNECTIONS IN THESE DRAWINGS ARE INTENDED FOR GUIDENCE ONLY. FOUNDATION AND SLAB WORKS SHOULD BE DESIGNED AND APPROVED BY A LOCAL STRUCTURAL ENGINEER.
7. THE COMPANY RETAINS FULL TITLE AND OWNERSHIP OF THESE PLANS AND DESIGNS. ANY UNAUTHORISED USE, REPRODUCTION, OR DISTRIBUTION OF THESE PLANS, WHETHER IN WHOLE OR PART, IS EXPRESSLY PROHIBITED WITHOUT PRIOR WRITTEN CONSENT.
8. THE HYBRID STEEL FRAME CONSTRUCTION SYSTEM AND METHODOLOGY (PATENT PENDING) DESCRIBED IN THESE PLANS HAS BEEN DEVELOPED BY THE COMPANY AND IS SUBJECT TO A PROVISIONAL PATENT APPLICATION & ASSIGNMENT - US APPLICATION NO. 63/722,841

No.	Revision	Date

ISSUED FOR:

Issued for information

Issued for client approval

Issued for fabrication

Issued for construction

The Charlston

DRAWING TITLE:

No 4 - Powder Room

DRAWN BY:

Y.A.Clark

SCALE:


1 : 25

DRAWING NO:

A128


DATE:

18/03/2026

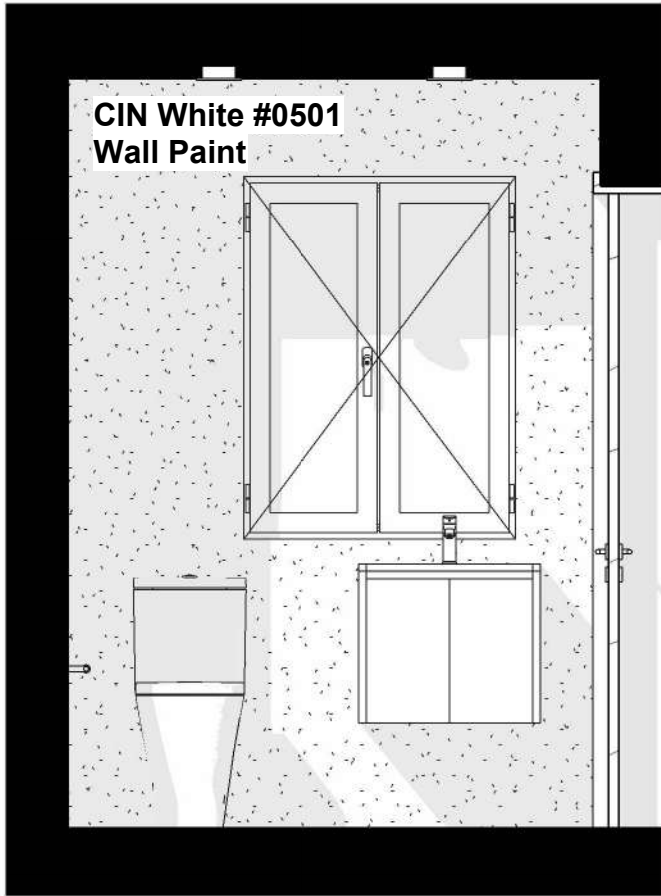


Section A

1 : 25

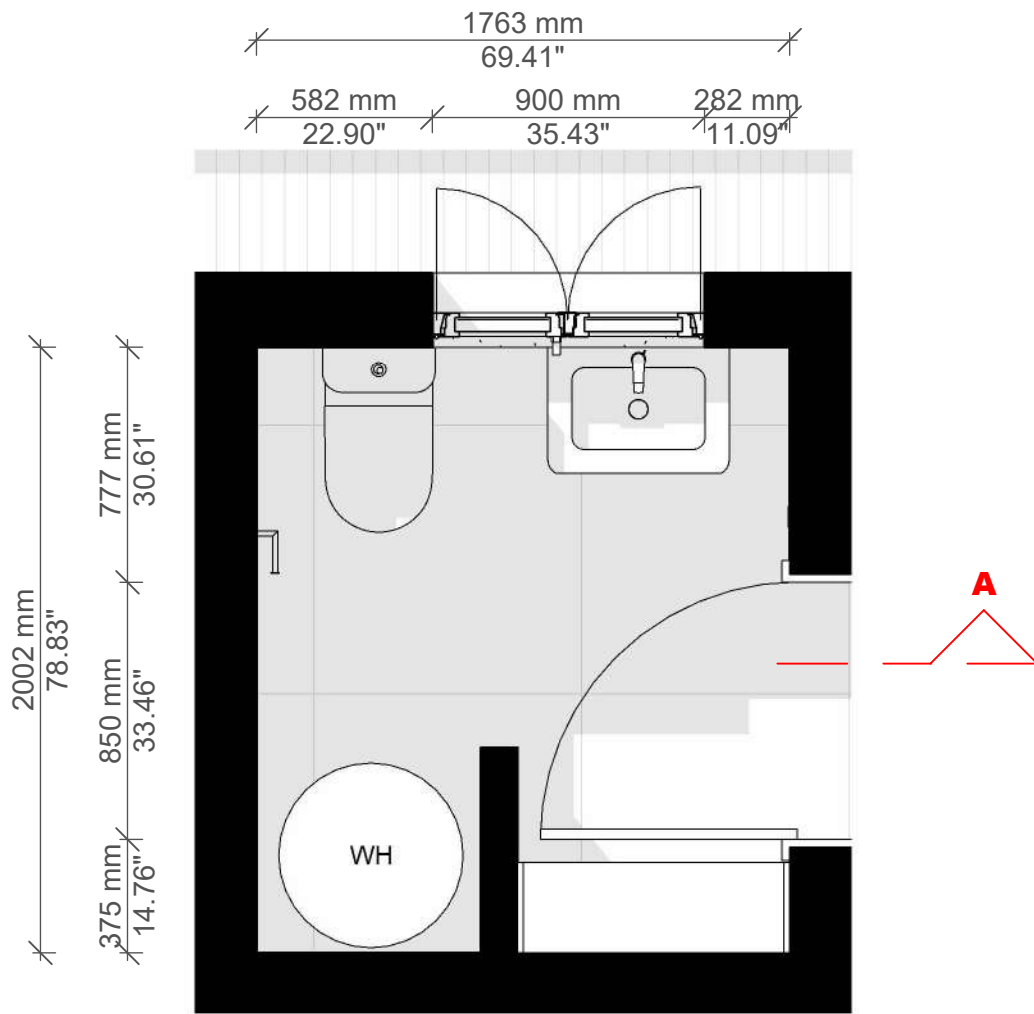

Bathroom 1 Plan

1 : 25

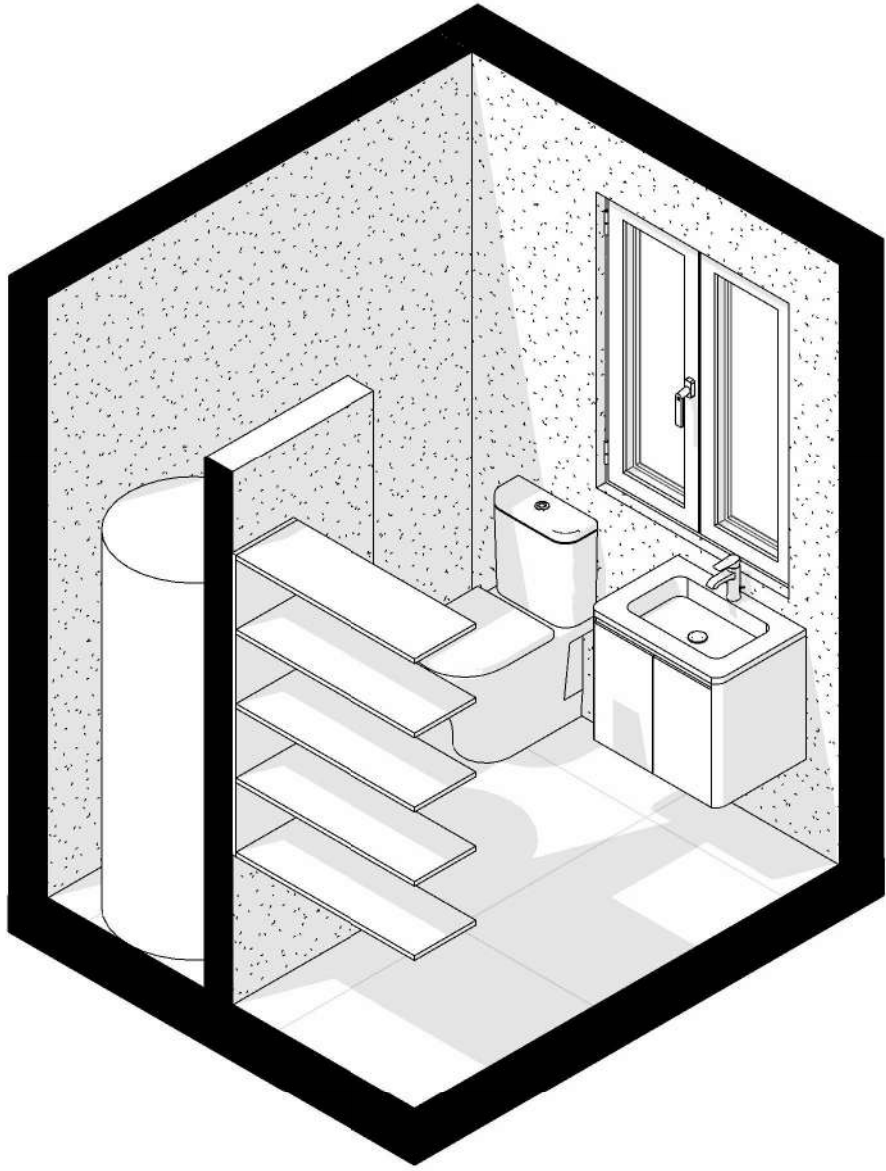

Bathroom 1 Isometric View

#0501
WHITE

Wall Colour

CIN

White #0501

Area: -m²











Bathroom Floor Tile

- On-Road Fog OR12
- 88,6 x 88,6 cm . 34,9" x 34,9" / C12
- Concrete, Rectified
- Glazed Porcelain Full Color Body, Natural

Grout Colour: 111 silver grey

Area: 3.6m²

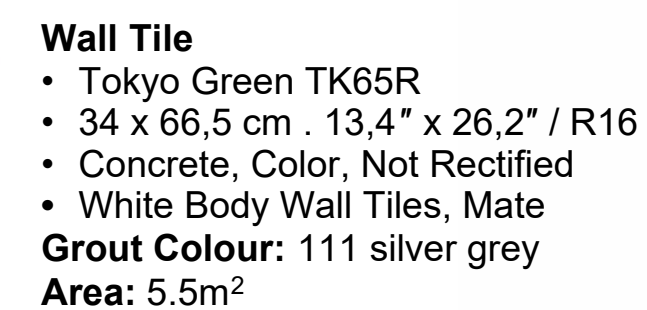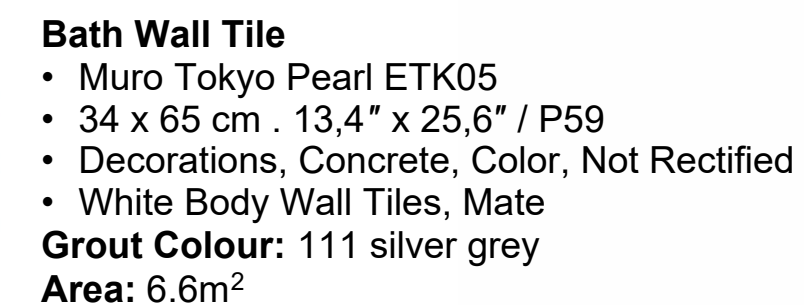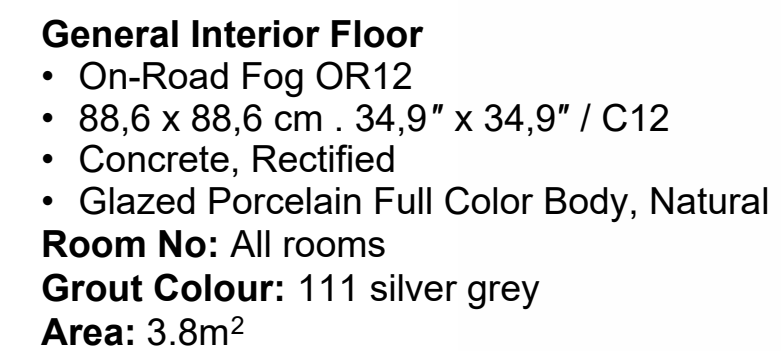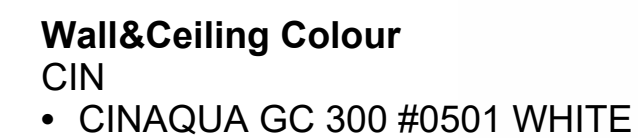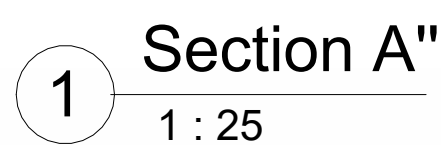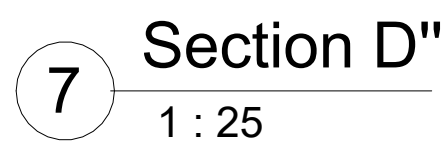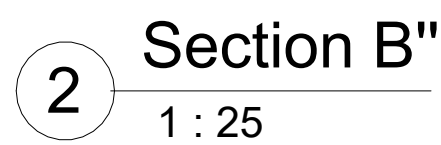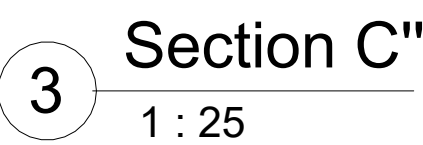

- BAUHU**
MODULAR • BUILDING • SOLUTIONS

1. THESE DRAWINGS MUST BE CHECKED BY THE CUSTOMER OR CONTRACTOR PRIOR TO APPROVAL. ANY ERRORS OR OMISSIONS MUST BE REPORTED IN WRITING TO BAUHU PRIOR TO COMMENCEMENT OF CONSTRUCTION.
2. ARCHITECTURAL DRAWINGS SHOULD BE READ IN CONJUNCTION WITH STRUCTURAL DETAILING AND FABRICATION GENERAL ASSEMBLY DRAWINGS.
3. FOR CONSTRUCTION PURPOSES, USE ONLY THE LATEST APPROVED DRAWINGS LABELED 'ISSUED FOR CONSTRUCTION'.
4. DO NOT SCALE FROM THIS DRAWING.
5. THE COMPANY OPERATES USING METRIC DIMENSIONS AS THE PRINCIPAL DENOMINATION.
6. ALL CONCRETE WORKS ARE OUTSIDE OF THE SCOPE OF THE COMPANY. INFORMATION REGARDING SLAB DESIGN AND CONNECTIONS IN THESE DRAWINGS ARE INTENDED FOR GUIDANCE ONLY. FOUNDATION AND SLAB WORKS SHOULD BE DESIGNED AND APPROVED BY A LOCAL STRUCTURAL ENGINEER.
7. THE COMPANY RETAINS FULL TITLE AND OWNERSHIP OF THESE PLANS AND DESIGNS. ANY UNAUTHORISED USE, REPRODUCTION, OR DISTRIBUTION OF THESE PLANS, WHETHER IN WHOLE OR PART, IS EXPRESSLY PROHIBITED WITHOUT PRIOR WRITTEN CONSENT.
8. THE HYBRID STEEL FRAME CONSTRUCTION SYSTEM AND METHODOLOGY (PATENT PENDING) DESCRIBED IN THESE PLANS HAS BEEN DEVELOPED BY THE COMPANY AND IS SUBJECT TO A PROVISIONAL PATENT APPLICATION & ASSIGNMENT - US APPLICATION NO. 63/722,841

[illegible]

ISSUED FOR:

Issued for information

Issued for client approval

Issued for fabrication

Issued for construction

The Charlston

DRAWING TITLE:

No 1&8 - Bathrooms

DRAWN BY:

Y.A.Clark

SCALE:

1 : 25

DRAWING NO:


A130

DATE:

18/03/2026



1 Bathroom Isometric View

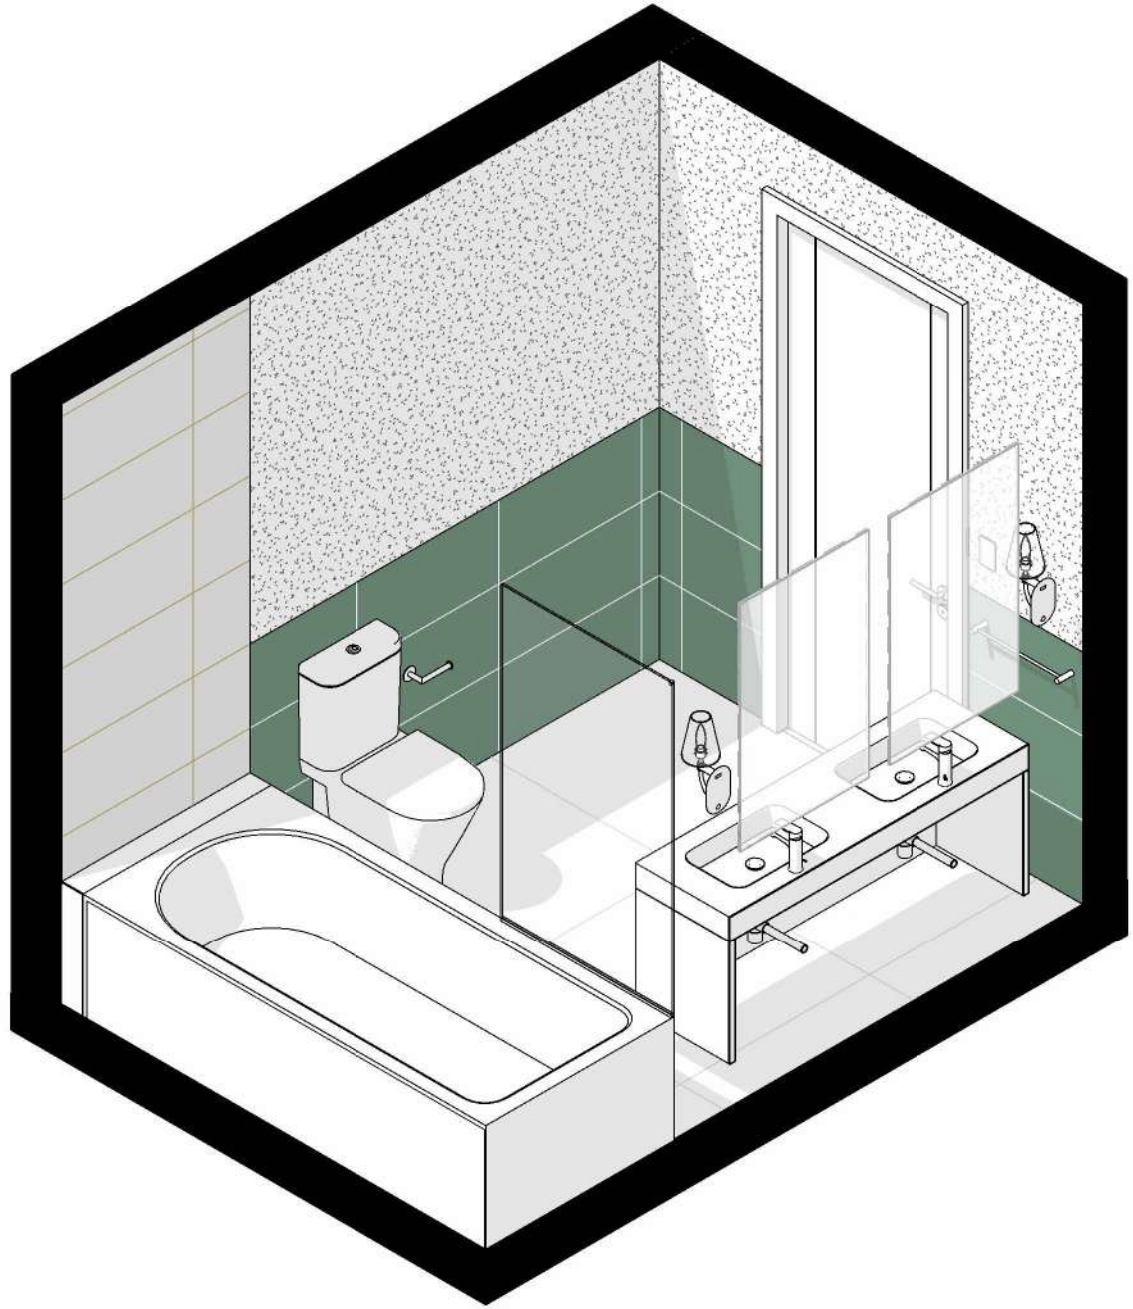

2 Bathroom Iso.View 2

1. THESE DRAWINGS MUST BE CHECKED BY THE CUSTOMER OR CONTRACTOR PRIOR TO APPROVAL. ANY ERRORS OR OMISSIONS MUST BE REPORTED IN WRITING TO BAUHU PRIOR TO COMMENCEMENT OF CONSTRUCTION.
2. ARCHITECTURAL DRAWINGS SHOULD BE READ IN CONJUNCTION WITH STRUCTURAL DETAILING AND FABRICATION GENERAL ASSEMBLY DRAWINGS.
3. FOR CONSTRUCTION PURPOSES, USE ONLY THE LATEST APPROVED DRAWINGS LABELED 'ISSUED FOR CONSTRUCTION'.
4. DO NOT SCALE FROM THIS DRAWING.
5. THE COMPANY OPERATES USING METRIC DIMENSIONS AS THE PRINCIPAL DENOMINATION.
6. ALL CONCRETE WORKS ARE OUTSIDE OF THE SCOPE OF THE COMPANY. INFORMATION REGARDING SLAB DESIGN AND CONNECTIONS IN THESE DRAWINGS ARE INTENDED FOR GUIDENCE ONLY. FOUNDATION AND SLAB WORKS SHOULD BE DESIGNED AND APPROVED BY A LOCAL STRUCTURAL ENGINEER.
7. THE COMPANY RETAINS FULL TITLE AND OWNERSHIP OF THESE PLANS AND DESIGNS. ANY UNAUTHORISED USE, REPRODUCTION, OR DISTRIBUTION OF THESE PLANS, WHETHER IN WHOLE OR PART, IS EXPRESSLY PROHIBITED WITHOUT PRIOR WRITTEN CONSENT.
8. THE HYBRID STEEL FRAME CONSTRUCTION SYSTEM AND METHODOLOGY (PATENT PENDING) DESCRIBED IN THESE PLANS HAS BEEN DEVELOPED BY THE COMPANY AND IS SUBJECT TO A PROVISIONAL PATENT APPLICATION & ASSIGNMENT - US APPLICATION NO. 63/722,841

No.	Revision	Date

ISSUED FOR:

Issued for information

Issued for client approval

Issued for fabrication

Issued for construction

The Charlston

DRAWING TITLE:	No 1&8 - Bathrooms
DRAWN BY:	Y.A.Clark
SCALE:	
DRAWING NO:	A131
DATE:	18/03/2026

Finishes Schedule													
Floor Area				Floor Finish		Ceiling Finish		Wall Finish					
No.	Room Name	Sq.Meter	Sq. Feet	Room Perimeter	Grout Colour	Tiles	Ceiling Colour	Ceiling Height	Wall Colour	Grout Colour	Wall Tile	Grout Colour	Shower Wall Tile
Ground Floor Finish													
1	Bathroom 1	6 m²	60.6 ft²	9633 mm	111 silver grey	On-Road Fog OR12	White #0501	2481	White #0501	111 silver grey	Tokyo Green TK65R	111 silver grey	Muro Tokyo Pearl ETK05
2	Bedroom 1	18 m²	192.4 ft²	16947 mm	111 silver grey	On-Road Fog OR12	White #0501	2481	White #0501				
3	Closet 1	1 m²	11.6 ft²	4745 mm	111 silver grey	On-Road Fog OR12	White #0501	2481	White #0501				
4	Powder Room	3 m²	37.1 ft²	8887 mm	111 silver grey	On-Road Fog OR12	White #0501	2481	White #0501				
5	Living Area	40 m²	434.6 ft²	25427 mm	111 silver grey	On-Road Fog OR12	White #0501	2481	White #0501	111 silver grey	Kitchen: Habitat Stripe Pearl HB03R		
6	Pantry	4 m²	38.0 ft²	7531 mm	111 silver grey	On-Road Fog OR12	White #0501	2481	White #0501				
7	Closet 2	1 m²	11.6 ft²	4745 mm	111 silver grey	On-Road Fog OR12	White #0501	2481	White #0501				
8	Bathroom 2	6 m²	60.6 ft²	9632 mm	111 silver grey	On-Road Fog OR12	White #0501	2481	White #0501	111 silver grey	Tokyo Green TK65R	111 silver grey	Muro Tokyo Pearl ETK05
9	Bedroom 2	18 m²	192.4 ft²	16946 mm	111 silver grey	On-Road Fog OR12	White #0501	2481	White #0501				
10	Exterior Terrace	68 m²	733.0 ft²	87992 mm									
Grand total		165 m²	1772.0 ft²	192486 mm									

Wall Schedule			
Type	Width	Length	Area
BAU Exterior Wall	245 mm	47092 mm	104 m²
BAU Interior Wall	204 mm	31941 mm	67 m²
Drywall	124 mm	780 mm	1 m²
Exterior - Brick on Mtl. Stud 2	14 mm	69097 mm	70 m²
Grand total		148910 mm	242 m²

Level Schedule		
Name	Elevation(mm)	Elevation(Feet)
Structural Roof Top	5287 mm	17.34'
Top of Plate	2800 mm	9.19'
Ceiling Level 1	2555 mm	8.38'
Windows Top 1	2230 mm	7.32'
Ground Floor Finish	74 mm	0.24'
Ground Floor Slab	0 mm	0.00'
Terrace Floor Finish	-84 mm	-0.28'
Terrace Slab	-152 mm	-0.50'
Site Level	-3652 mm	-11.98'

Roof Soffit Schedule			
Type	Area	Perimeter	Level
Roof Soffit	30 m²	100944 mm	Top of Plate


Roof Schedule			
Type	Base Level	Slope	Area
Roofs 2			5 m²
Main Roof	Structural Roof Top		162 m²

Fascia Schedule		
Type	Length	Count
Roofs 1		8 m²

- Note:**
- DRYWALL to be used in the powder room to fit water heater.
 - DRYWALL to be used to fit bathtubs.

Paint Area Schedule	
Paint Name	Wall Area
Drywall	1.5 m²
Gypsum Wall Board	69.7 m²
Gypsum Wall Board - Fire resistant	238.4 m²
Gypsum Wall Board - Moisture resistant	238.3 m²
Light Gauge Steel frame	170.4 m²
Mineral Rockwool	171.2 m²
No.1&8 Bathroom 3 Wall Tile - Tokyo Green TK65R	10.6 m²
No.1&8 Bathroom Bathtub Tile - Muro Tokyo Pearl ETK05	13.3 m²
No.1&8 Bathroom Paint - White 0501	15.2 m²
No.2 Bedroom 1 Paint - White 0501	32.2 m²
No.3 Closet 1 Paint - White 0501	9.7 m²
No.4 Powder Room Paint - White 0501	19.2 m²
No.5 Kitchen Tile - Habitat Stripe Pearl HB03R	1.8 m²
No.5 Living Area Paint - White 0501	44.5 m²
No.6 Pantry - White 0501	16.1 m²
No.7 Closet 2 Paint - White 0501	9.7 m²
No.9 Bedroom 2 Paint - White 0501	32.1 m²
Rigid insulation	104.2 m²
Secolite skim coat with embedded mesh	103.7 m²
Secolite with joints and screws filled	103.7 m²
Selected Paint Finish	417.8 m²
STO Cement-free reinforcing coat	104.2 m²
STO Decorative Green Render Finish Plaster	112.1 m²
Vapour Barrier	170.4 m²
Grand total	2209.8 m²

Ceiling Schedule				
Type	Area	Perimeter	Thickness	Description
Ceiling	97 m²	103138 mm	245 mm	Interior

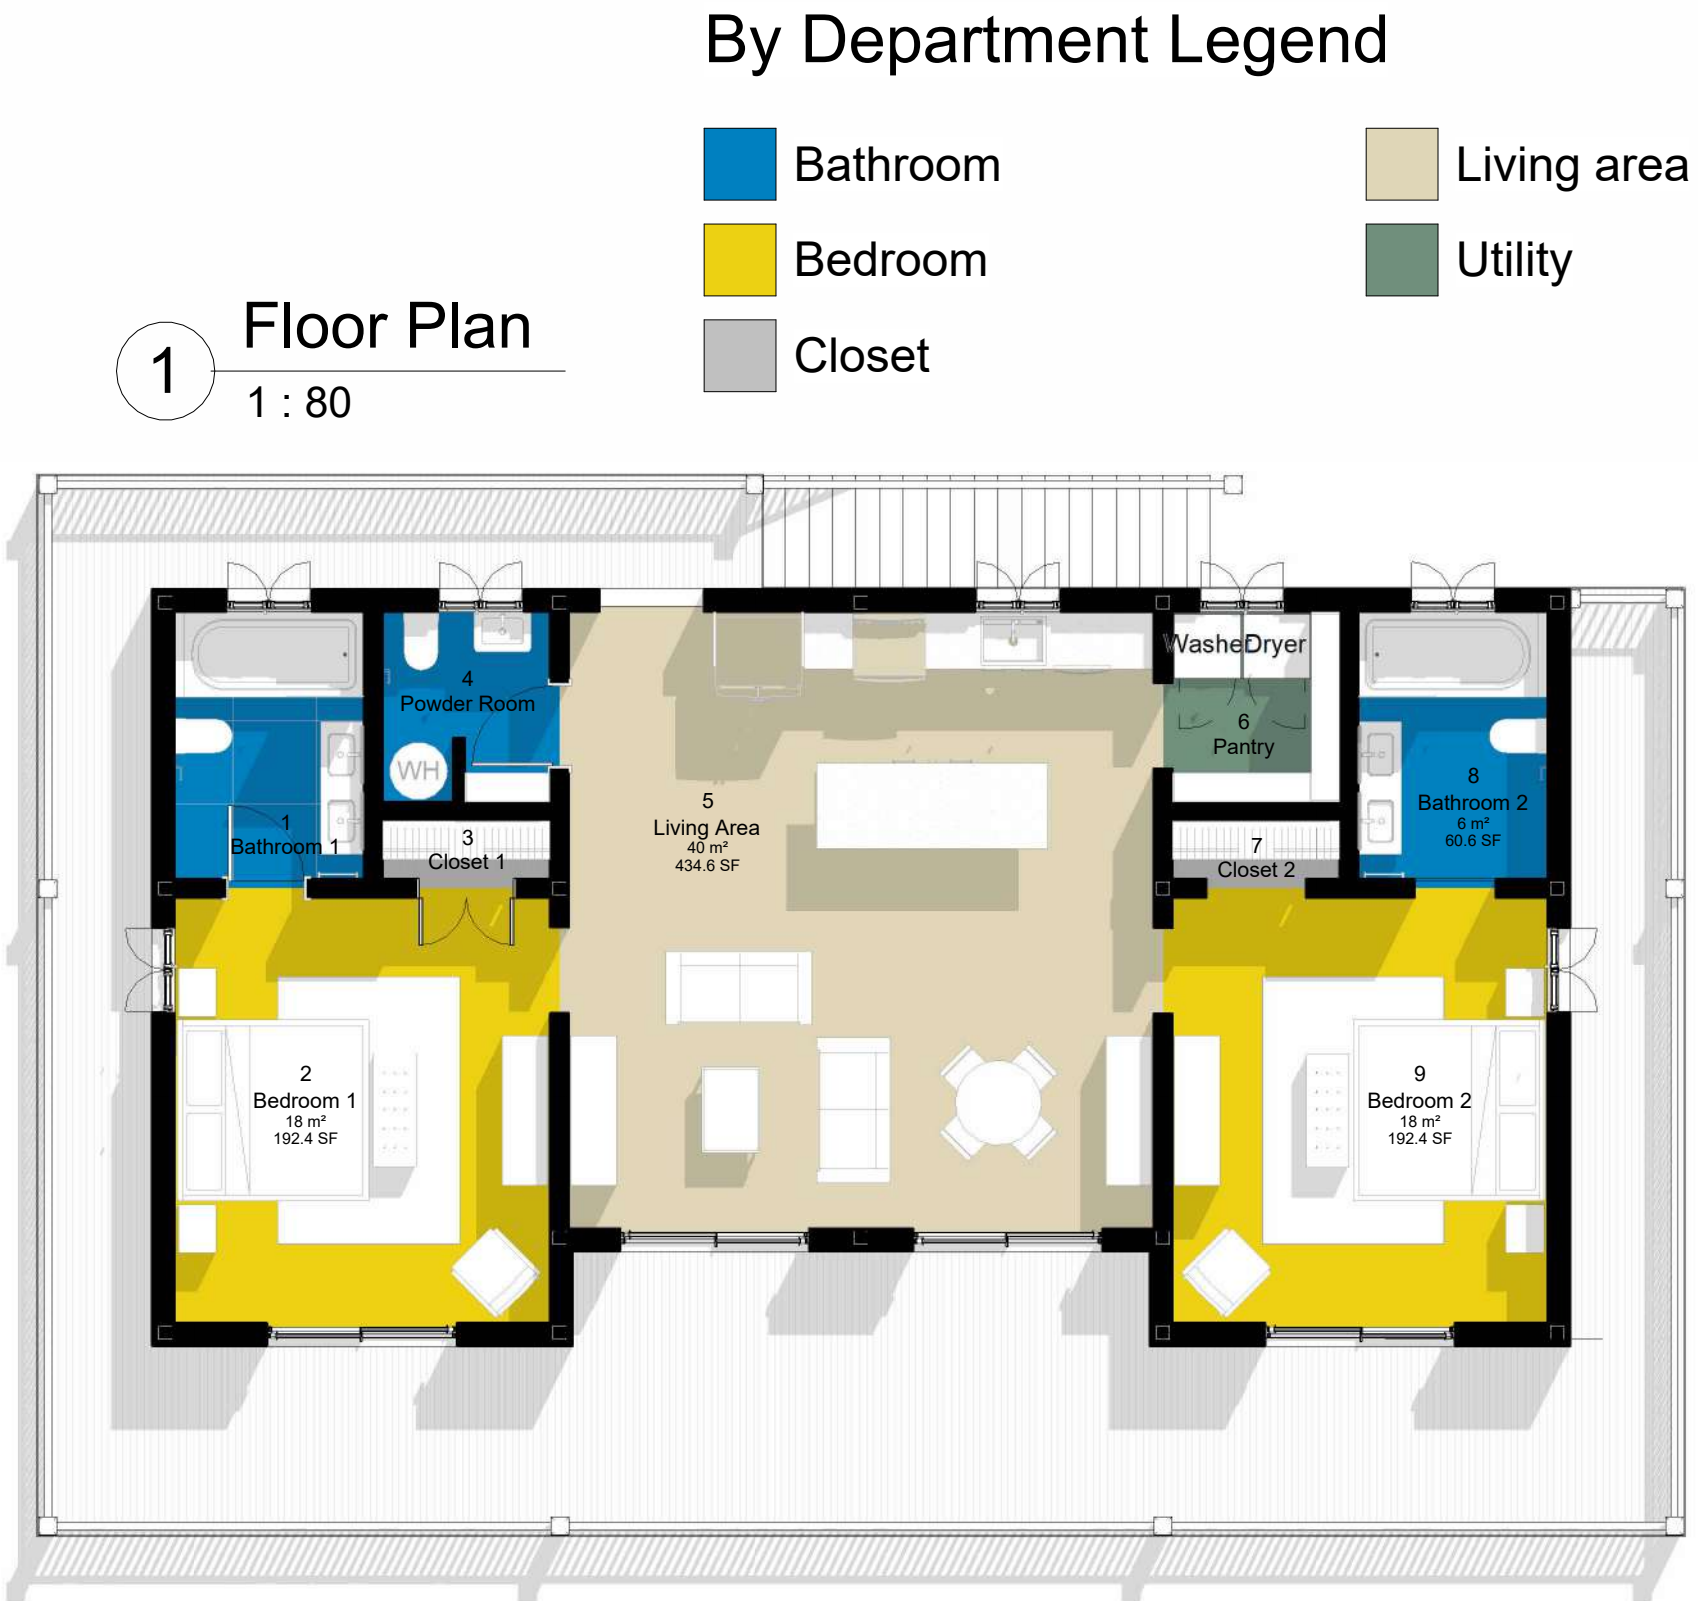

1. THESE DRAWINGS MUST BE CHECKED BY THE CUSTOMER OR CONTRACTOR PRIOR TO APPROVAL. ANY ERRORS OR OMISSIONS MUST BE REPORTED IN WRITING TO BAUHU PRIOR TO COMMENCEMENT OF CONSTRUCTION.
2. ARCHITECTURAL DRAWINGS SHOULD BE READ IN CONJUNCTION WITH STRUCTURAL DETAILING AND FABRICATION GENERAL ASSEMBLY DRAWINGS.
3. FOR CONSTRUCTION PURPOSES, USE ONLY THE LATEST APPROVED DRAWINGS LABELED 'ISSUED FOR CONSTRUCTION'.
4. DO NOT SCALE FROM THIS DRAWING.
5. THE COMPANY OPERATES USING METRIC DIMENSIONS AS THE PRINCIPAL DENOMINATION.
6. ALL CONCRETE WORKS ARE OUTSIDE OF THE SCOPE OF THE COMPANY. INFORMATION REGARDING SLAB DESIGN AND CONNECTIONS IN THESE DRAWINGS ARE INTENDED FOR GUIDENCE ONLY. FOUNDATION AND SLAB WORKS SHOULD BE DESIGNED AND APPROVED BY A LOCAL STRUCTURAL ENGINEER.
7. THE COMPANY RETAINS FULL TITLE AND OWNERSHIP OF THESE PLANS AND DESIGNS. ANY UNAUTHORISED USE, REPRODUCTION, OR DISTRIBUTION OF THESE PLANS, WHETHER IN WHOLE OR PART, IS EXPRESSLY PROHIBITED WITHOUT PRIOR WRITTEN CONSENT.
8. THE HYBRID STEEL FRAME CONSTRUCTION SYSTEM AND METHODOLOGY (PATENT PENDING) DESCRIBED IN THESE PLANS HAS BEEN DEVELOPED BY THE COMPANY AND IS SUBJECT TO A PROVISIONAL PATENT APPLICATION & ASSIGNMENT - US APPLICATION NO. 63/722,841

No.	Revision	Date

ISSUED FOR:

Issued for information

Issued for client approval

Issued for fabrication

Issued for construction

The Charlston

DRAWING TITLE:	Finishes Schedule & Legend
DRAWN BY:	Y.A.Clark
SCALE:	1 : 80
DRAWING NO:	A132
DATE:	18/03/2026

INTERIOR FLOOR TILE <https://www.domino.pt/en/products>

- On-Road Fog OR12
- 88,6 x 88,6 cm . 34,9" x 34,9" / C12
- Concrete, Rectified
- Glazed Porcelain Full Color Body, Natural

Room No: All rooms

Grout Colour: 111 silver grey

Total Area: 98 m²



[https://www.domino.pt/en/products/\[\[type-22-go\]\[collection-79\]\[material-15\]\[ambient-all\]\]/241-on-road/-/1701-on-road-fog-or12/164-886-x-886](https://www.domino.pt/en/products/[[type-22-go][collection-79][material-15][ambient-all]]/241-on-road/-/1701-on-road-fog-or12/164-886-x-886)
<https://www.mapei.com/au/en/tools-and-downloads/coloured-grouts-and-sealants>


BATH WALL TILE

- Muro Tokyo Pearl ETK05
- 34 x 65 cm . 13,4" x 25,6" / P59
- Decorations, Concrete, Color, Not Rectified
- White Body Wall Tiles, Mate

Room No: 1&8

Grout Colour: 111 silver grey

Total Area: 13.2 m²

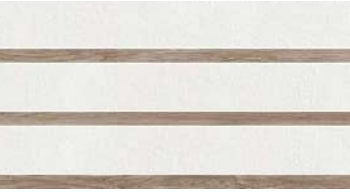

[https://www.domino.pt/en/products/\[\[type-21\]\[collection-73\]\[material-28\]\[ambient-all\]\]/206-tokyo/-/1532-muro-tokyo-pearl-etk05/166-34-x-65](https://www.domino.pt/en/products/[[type-21][collection-73][material-28][ambient-all]]/206-tokyo/-/1532-muro-tokyo-pearl-etk05/166-34-x-65)

WALL TILE

- Tokyo Green TK65R
- 34 x 66,5 cm . 13,4" x 26,2" / R16
- Concrete, Color, Not Rectified
- White Body Wall Tiles, Mate

Room No: 1&8

Grout Colour: 111 silver grey

Total Area: 11 m²



[https://www.domino.pt/en/products/\[\[type-21\]\[collection-73\]\[material-19\]\[ambient-all\]\]/205-tokyo/-/1526-tokyo-green-tk65r/147-34-x-665](https://www.domino.pt/en/products/[[type-21][collection-73][material-19][ambient-all]]/205-tokyo/-/1526-tokyo-green-tk65r/147-34-x-665)

KITCHEN BACKSPLASH TILE

- Habitat Stripe Pearl HB03R
- 34 x 66,5 cm . 13,4" x 26,2" / R17
- Decorations, Concrete, Not Rectified
- White Body Wall Tiles, Mate

Room No: 7

Grout Colour: 111 silver grey

Total Area: 1.5 m²



[https://www.domino.pt/en/products/\[\[type-21\]\[collection-27\]\[material-28\]\[ambient-all\]\]/16-innova/4-white/295-habitat-stripe-pearl-hb03r/147-34-x-665](https://www.domino.pt/en/products/[[type-21][collection-27][material-28][ambient-all]]/16-innova/4-white/295-habitat-stripe-pearl-hb03r/147-34-x-665)

CEILING&WALL PAINT FINISH

CIN

- CINAQUA GC 300 #0501 WHITE

Room No: All rooms

Total Ceiling Area: 108 m²

Total Wall Paint Area: - m²



<https://cin.com/deco/pt/en/colour>

EXTERIOR WALL FINISH

Exterior Wall Finish

Stolit K fine grain exterior plaster

Colour code: 36105, 62 C1 O

RGB: 182,215,199

Total Exterior Wall Area: 113 m²



PERGOLA/SOFFIT/FASCIA FINISH

Stolit K fine grain exterior plaster

Colour: RAL 9003 Signal White

RGB: 236, 236, 232

HEX Code: #ECECE8

Total Soffit Area: 35.2 m²

Total Fascia Area: 9 m²



<https://www.stocorp.com/sto-color/>

ROOF FINISH

- Acrylabs elastomeric roofing membrane
- Colour: Acrylabs Standard White

Total Roof Area: 168 m²

BAUHU
MODULAR • BUILDING • SOLUTIONS

1. THESE DRAWINGS MUST BE CHECKED BY THE CUSTOMER OR CONTRACTOR PRIOR TO APPROVAL. ANY ERRORS OR OMISSIONS MUST BE REPORTED IN WRITING TO BAUHU PRIOR TO COMMENCEMENT OF CONSTRUCTION.
2. ARCHITECTURAL DRAWINGS SHOULD BE READ IN CONJUNCTION WITH STRUCTURAL DETAILING AND FABRICATION GENERAL ASSEMBLY DRAWINGS.
3. FOR CONSTRUCTION PURPOSES, USE ONLY THE LATEST APPROVED DRAWINGS LABELED 'ISSUED FOR CONSTRUCTION'.
4. DO NOT SCALE FROM THIS DRAWING.
5. THE COMPANY OPERATES USING METRIC DIMENSIONS AS THE PRINCIPAL DENOMINATION.
6. ALL CONCRETE WORKS ARE OUTSIDE OF THE SCOPE OF THE COMPANY. INFORMATION REGARDING SLAB DESIGN AND CONNECTIONS IN THESE DRAWINGS ARE INTENDED FOR GUIDENCE ONLY. FOUNDATION AND SLAB WORKS SHOULD BE DESIGNED AND APPROVED BY A LOCAL STRUCTURAL ENGINEER.
7. THE COMPANY RETAINS FULL TITLE AND OWNERSHIP OF THESE PLANS AND DESIGNS. ANY UNAUTHORISED USE, REPRODUCTION, OR DISTRIBUTION OF THESE PLANS, WHETHER IN WHOLE OR PART, IS EXPRESSLY PROHIBITED WITHOUT PRIOR WRITTEN CONSENT.
8. THE HYBRID STEEL FRAME CONSTRUCTION SYSTEM AND METHODOLOGY (PATENT PENDING) DESCRIBED IN THESE PLANS HAS BEEN DEVELOPED BY THE COMPANY AND IS SUBJECT TO A PROVISIONAL PATENT APPLICATION & ASSIGNMENT - US APPLICATION NO. 63/722,841

No.	Revision	Date

ISSUED FOR:

Issued for information

Issued for client approval

Issued for fabrication

Issued for construction

The Charlston

DRAWING TITLE:

Decor Finishes

DRAWN BY:

Y.A.Clark

SCALE:

DRAWING NO:

A133

DATE:

18/03/2026

Wall Details

Exterior Wall

Interior side

- Selected Finish Paint (2mm)
- Gypsumboard Moisture Resistant (12.5mm)
- Gypsumboard Fire Resistant (12.5mm)
- Light Gauge Stelel Frame (150mm)
- Mineral Rockwool (120mm) between LGS studs
- Secolite with joints and screws filled (12.5mm)
- Rigid Insulation 40mm
- STO Cement-free Reinforcing Coat with Mesh
- STO Decorative Render Finish Plaster


Exterior side

Interior Wall


Interior side

- Selected Paint Finish
 - Gypsum Wall Board - Moisture resistant (12.5mm)
 - Gypsum Wall Board - Fire resistant (12.5mm)
 - Light Gauge Steel Frame (150mm)
 - Mineral Rockwool (120mm) between LGS studs
 - Gypsum Wall Board - Fire resistant (12.5mm)
 - Gypsum Wall Board - Moisture resistant (12.5mm)
 - Selected Paint Finish
- Interior side


D8.Exterior - Interior Wall Connection Sc: 1/6

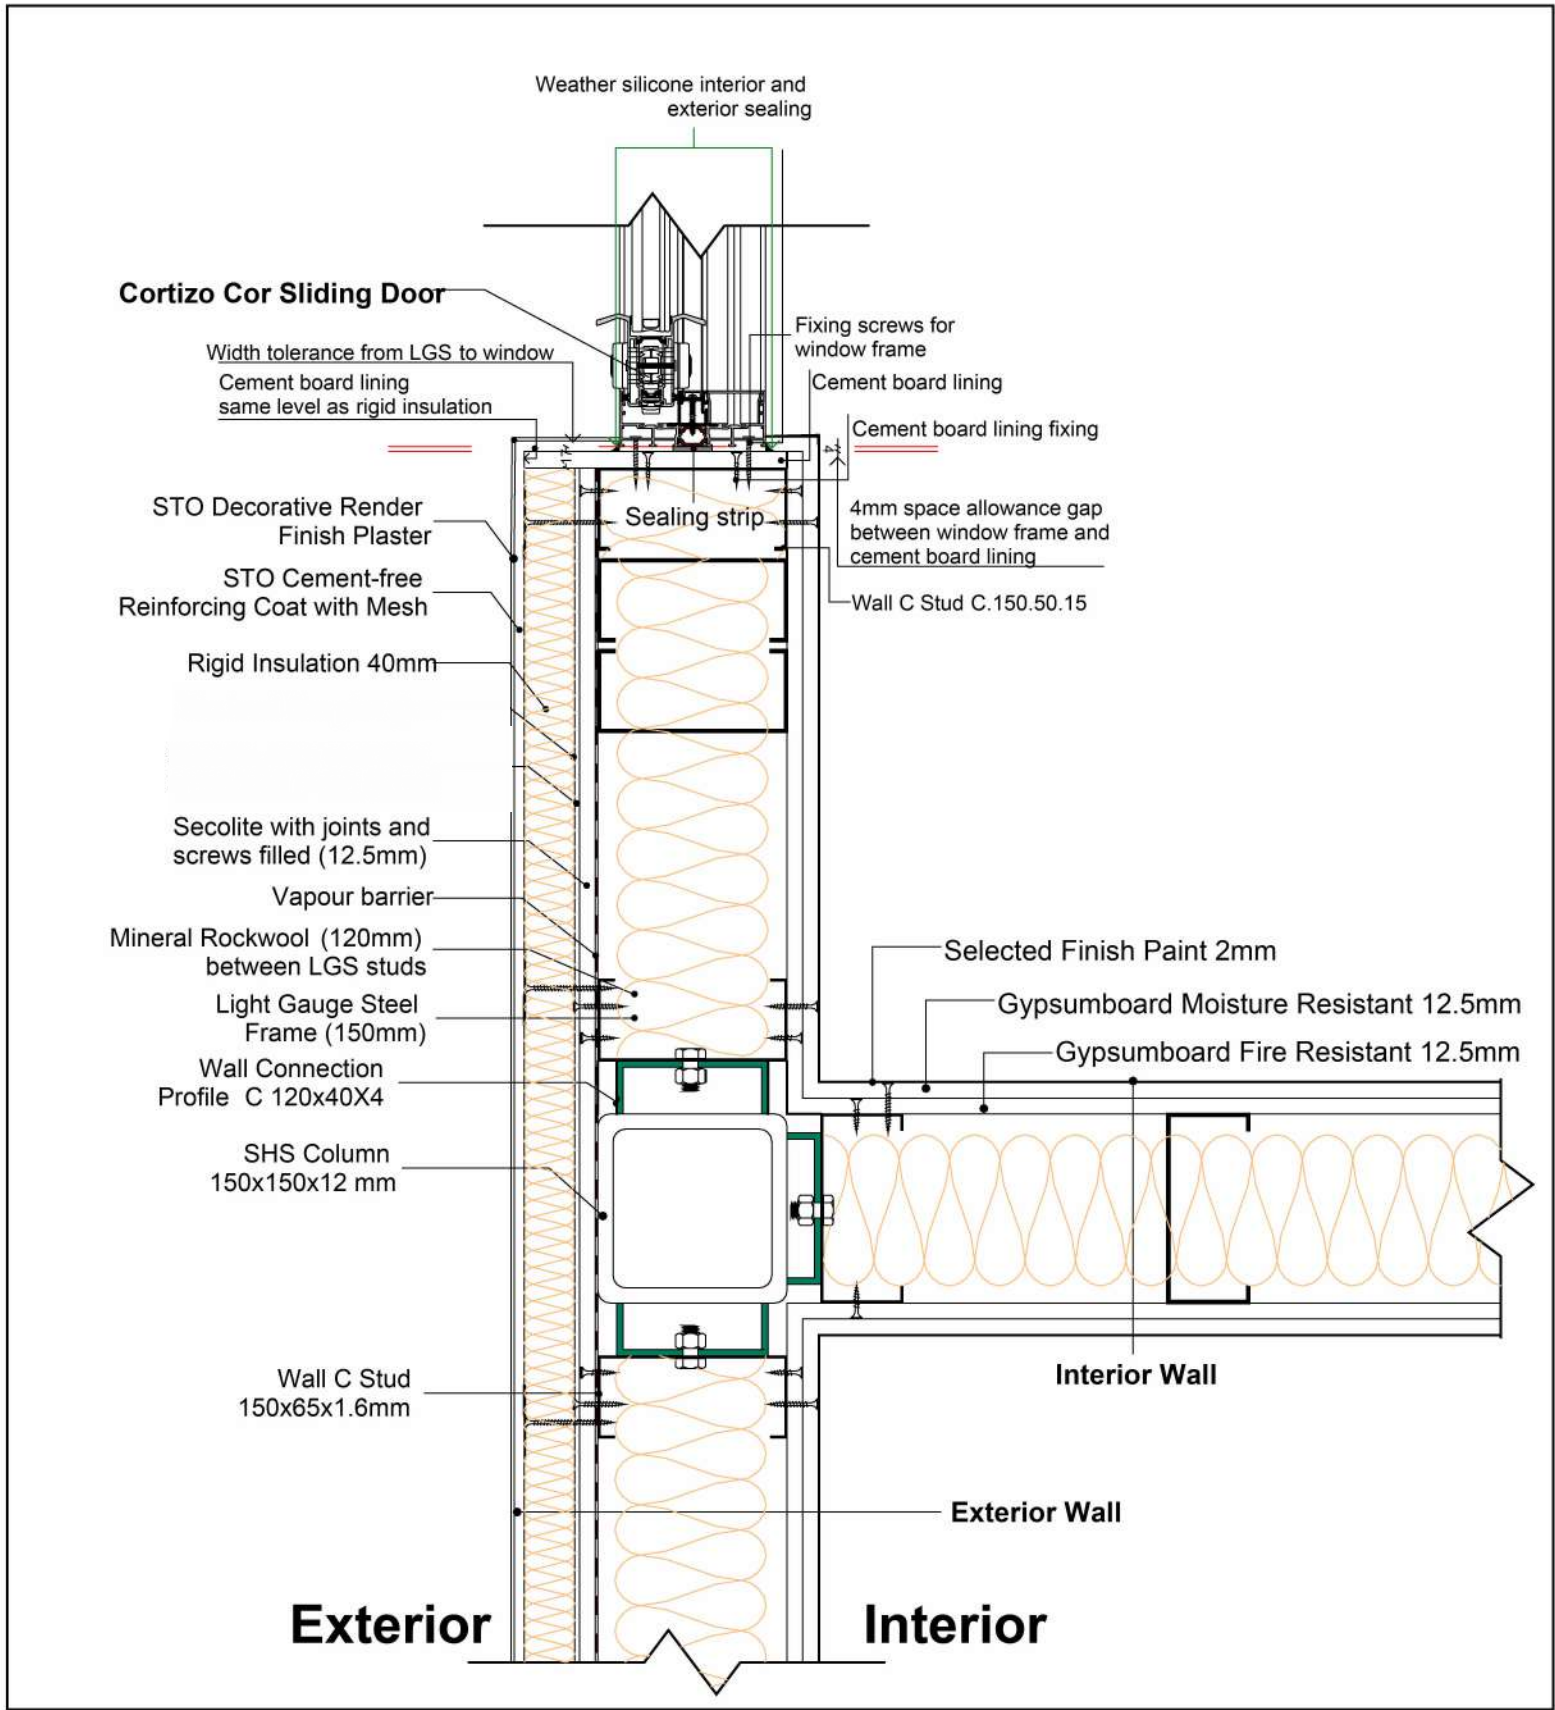

D7.Exterior - Interior Wall Connection Sc: 1/6

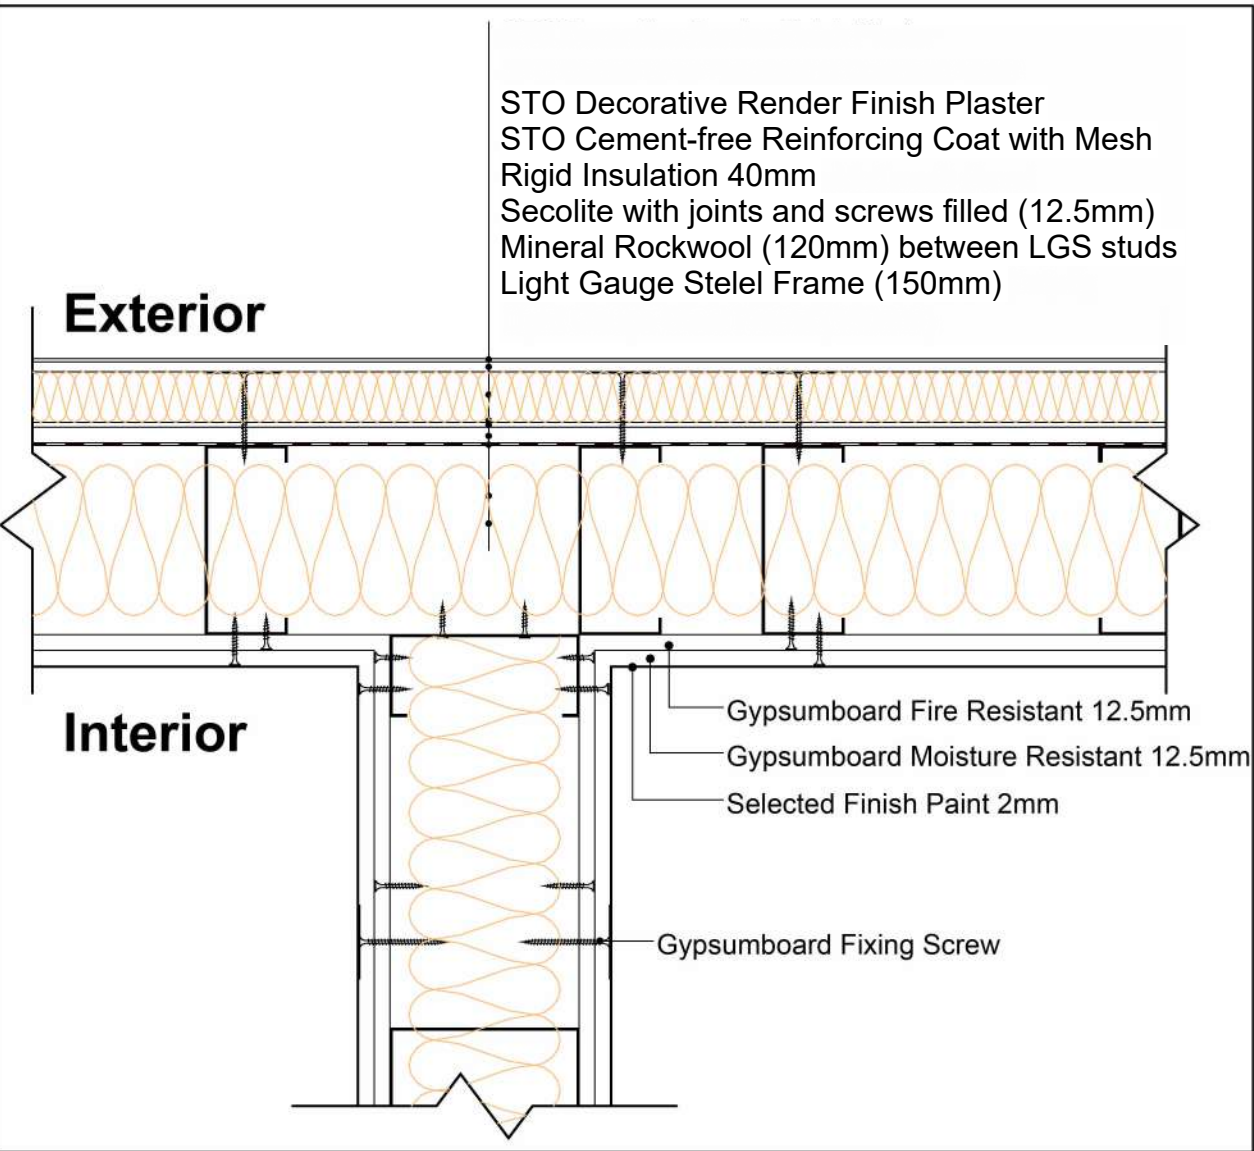

D9.Exterior Corner Wall Sc: 1/6

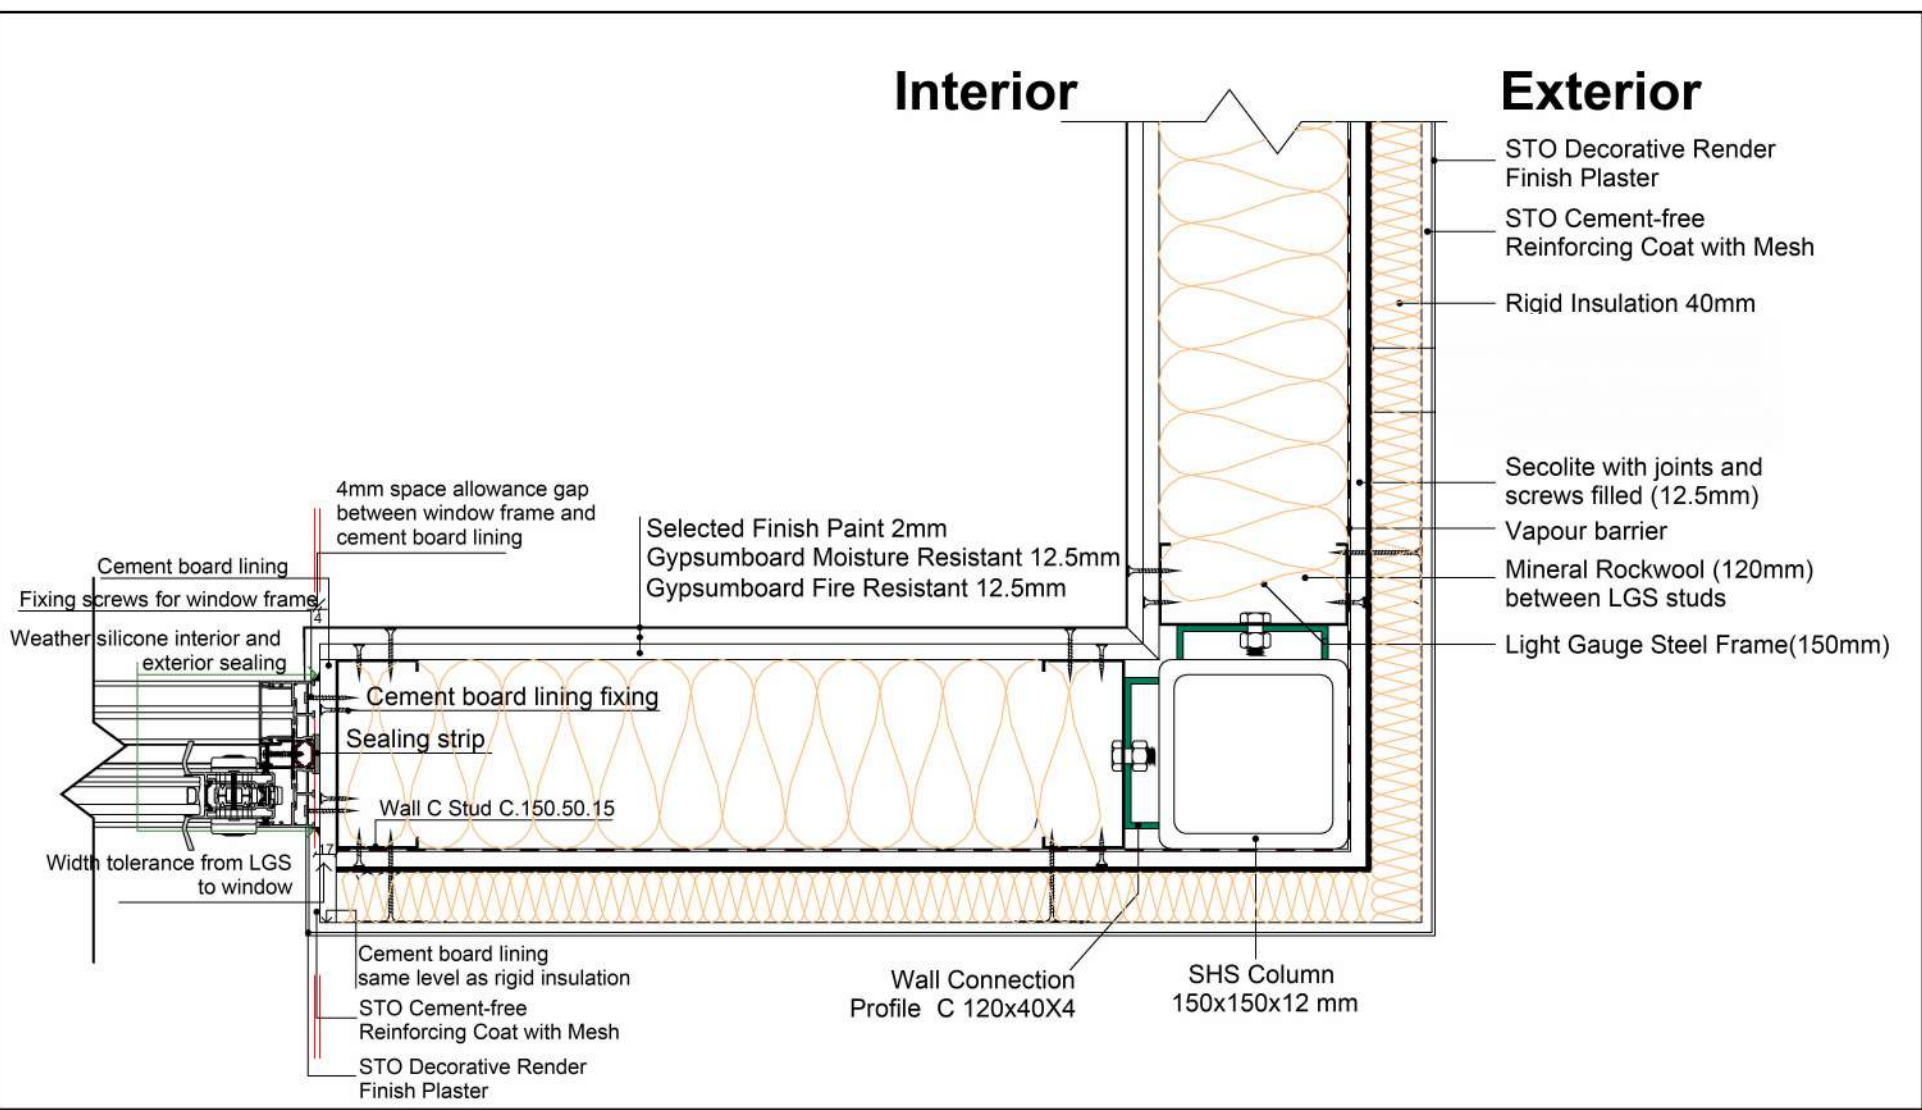

1. THESE DRAWINGS MUST BE CHECKED BY THE CUSTOMER OR CONTRACTOR PRIOR TO APPROVAL. ANY ERRORS OR OMISSIONS MUST BE REPORTED IN WRITING TO BAUHU PRIOR TO COMMENCEMENT OF CONSTRUCTION.
2. ARCHITECTURAL DRAWINGS SHOULD BE READ IN CONJUNCTION WITH STRUCTURAL DETAILING AND FABRICATION GENERAL ASSEMBLY DRAWINGS.
3. FOR CONSTRUCTION PURPOSES, USE ONLY THE LATEST APPROVED DRAWINGS LABELED 'ISSUED FOR CONSTRUCTION'.
4. DO NOT SCALE FROM THIS DRAWING.
5. THE COMPANY OPERATES USING METRIC DIMENSIONS AS THE PRINCIPAL DENOMINATION.
6. ALL CONCRETE WORKS ARE OUTSIDE OF THE SCOPE OF THE COMPANY. INFORMATION REGARDING SLAB DESIGN AND CONNECTIONS IN THESE DRAWINGS ARE INTENDED FOR GUIDENCE ONLY. FOUNDATION AND SLAB WORKS SHOULD BE DESIGNED AND APPROVED BY A LOCAL STRUCTURAL ENGINEER.
7. THE COMPANY RETAINS FULL TITLE AND OWNERSHIP OF THESE PLANS AND DESIGNS. ANY UNAUTHORISED USE, REPRODUCTION, OR DISTRIBUTION OF THESE PLANS, WHETHER IN WHOLE OR PART, IS EXPRESSLY PROHIBITED WITHOUT PRIOR WRITTEN CONSENT.
8. THE HYBRID STEEL FRAME CONSTRUCTION SYSTEM AND METHODOLOGY (PATENT PENDING) DESCRIBED IN THESE PLANS HAS BEEN DEVELOPED BY THE COMPANY AND IS SUBJECT TO A PROVISIONAL PATENT APPLICATION & ASSIGNMENT - US APPLICATION NO. 63/722,841

No.	Revision	Date

ISSUED FOR:

- Issued for information
- Issued for client approval
- Issued for fabrication
- Issued for construction

The Charlston

DRAWING TITLE:

Wall Details

DRAWN BY:

Y.A.Clark

SCALE:

DRAWING NO:

C101

DATE:

18/03/2026

1. THESE DRAWINGS MUST BE CHECKED BY THE CUSTOMER OR CONTRACTOR PRIOR TO APPROVAL. ANY ERRORS OR OMISSIONS MUST BE REPORTED IN WRITING TO BAUHU PRIOR TO COMMENCEMENT OF CONSTRUCTION.
2. ARCHITECTURAL DRAWINGS SHOULD BE READ IN CONJUNCTION WITH STRUCTURAL DETAILING AND FABRICATION GENERAL ASSEMBLY DRAWINGS.
3. FOR CONSTRUCTION PURPOSES, USE ONLY THE LATEST APPROVED DRAWINGS LABELED 'ISSUED FOR CONSTRUCTION'.
4. DO NOT SCALE FROM THIS DRAWING.
5. THE COMPANY OPERATES USING METRIC DIMENSIONS AS THE PRINCIPAL DENOMINATION.
6. ALL CONCRETE WORKS ARE OUTSIDE OF THE SCOPE OF THE COMPANY. INFORMATION REGARDING SLAB DESIGN AND CONNECTIONS IN THESE DRAWINGS ARE INTENDED FOR GUIDANCE ONLY. FOUNDATION AND SLAB WORKS SHOULD BE DESIGNED AND APPROVED BY A LOCAL STRUCTURAL ENGINEER.
7. THE COMPANY RETAINS FULL TITLE AND OWNERSHIP OF THESE PLANS AND DESIGNS. ANY UNAUTHORISED USE, REPRODUCTION, OR DISTRIBUTION OF THESE PLANS, WHETHER IN WHOLE OR PART, IS EXPRESSLY PROHIBITED WITHOUT PRIOR WRITTEN CONSENT.
8. THE HYBRID STEEL FRAME CONSTRUCTION SYSTEM AND METHODOLOGY (PATENT PENDING) DESCRIBED IN THESE PLANS HAS BEEN DEVELOPED BY THE COMPANY AND IS SUBJECT TO A PROVISIONAL PATENT APPLICATION & ASSIGNMENT - US APPLICATION NO. 63/722,841

No.	Revision	Date

ISSUED FOR:

Issued for information

Issued for client approval

Issued for fabrication

Issued for construction

The Charlston

DRAWING TITLE:

Window/Door Plan Detail

DRAWN BY:

Y.A.Clark


SCALE:

DRAWING NO:

C102

DATE:

18/03/2026

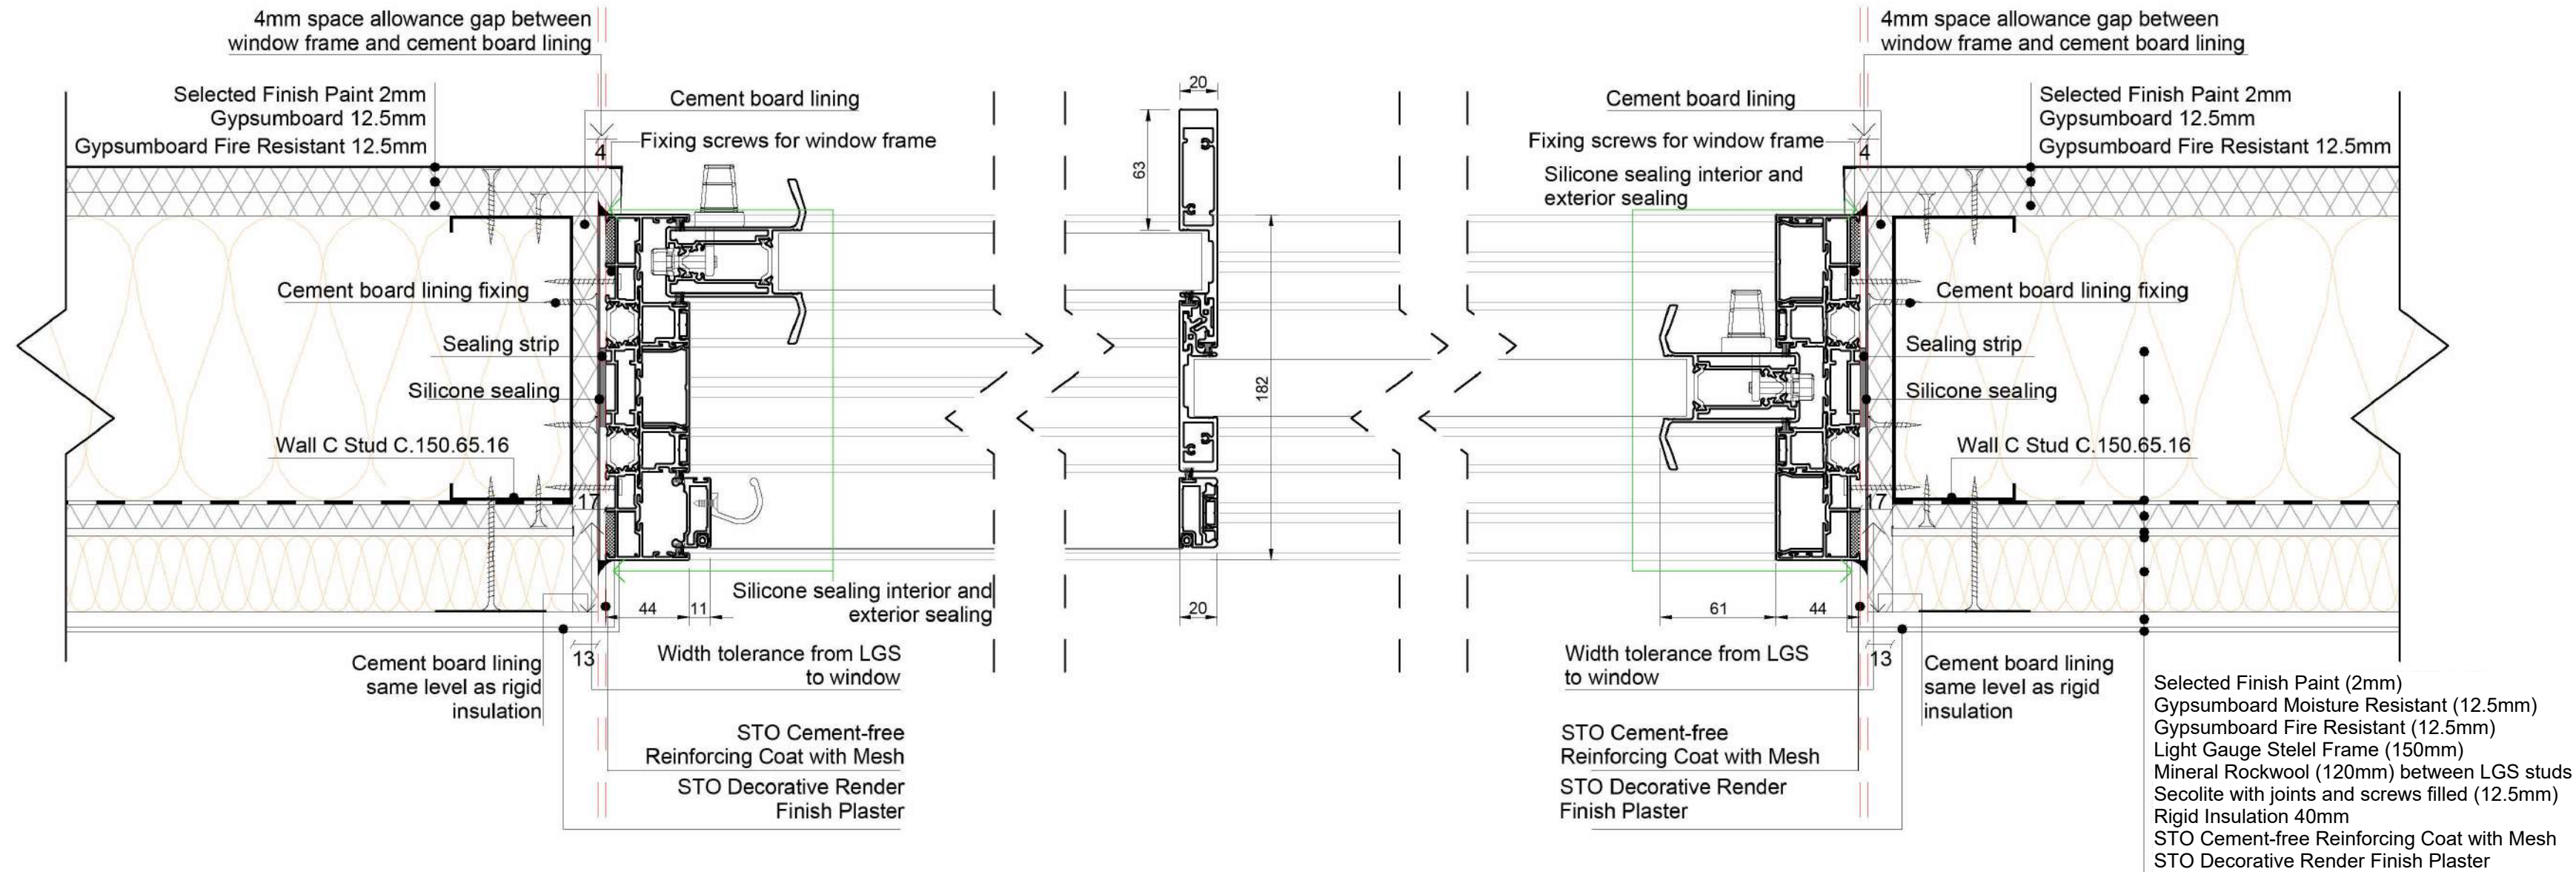

D.Sliding Door/Window Floor Plan with insect screens


Note:

*Openings are provided without insect screens as standard. Insect screens can be provided at additional cost.


*Shutters are excluded. If required these will be provided by others-acquired locally according to dimensions of finished openings after finish application. Drawings are made for design purposes only. Garage type doors are excluded and should be sourced by the owner.

All opening windows open outwards.


All opening drawings are viewed from the outside

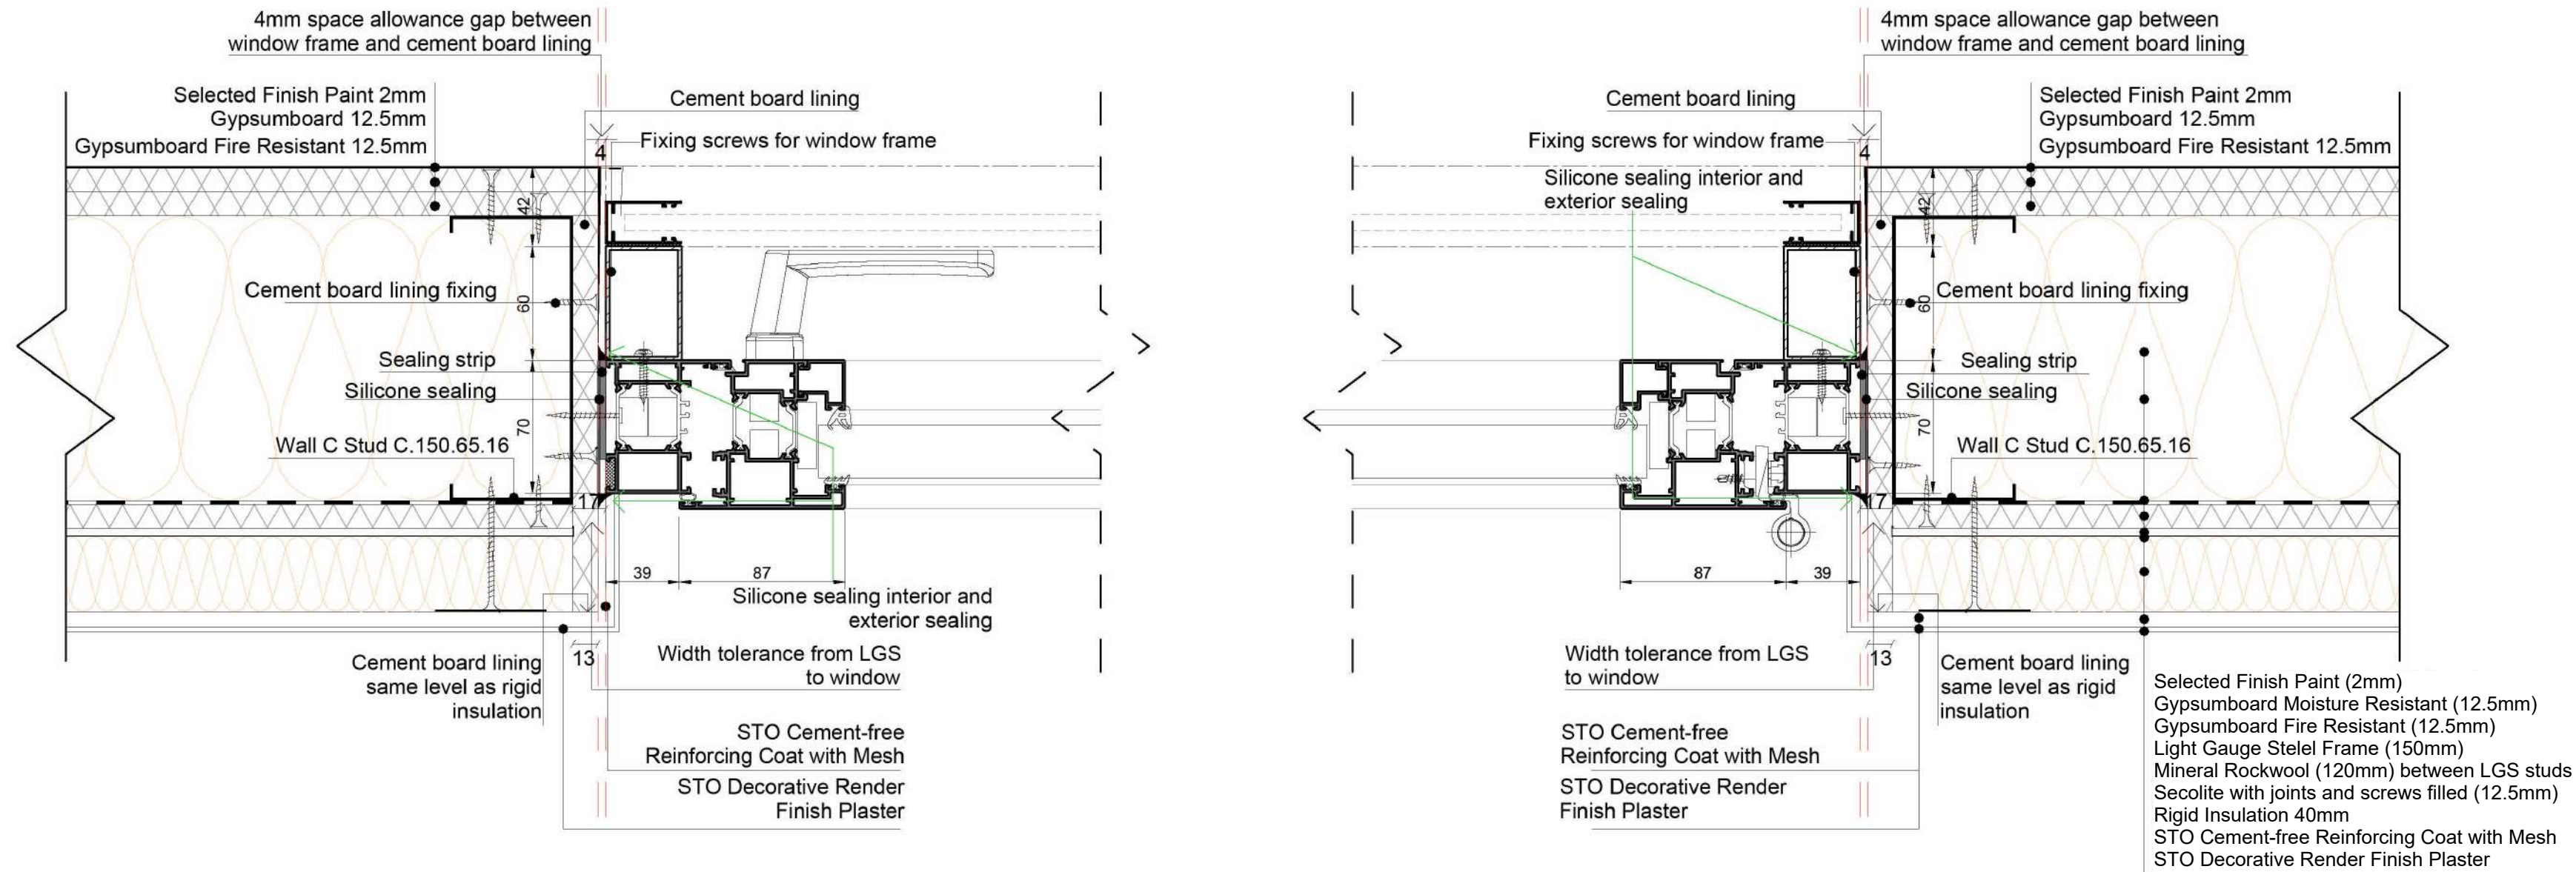


D.Casement Window Floor Plan with insect screens

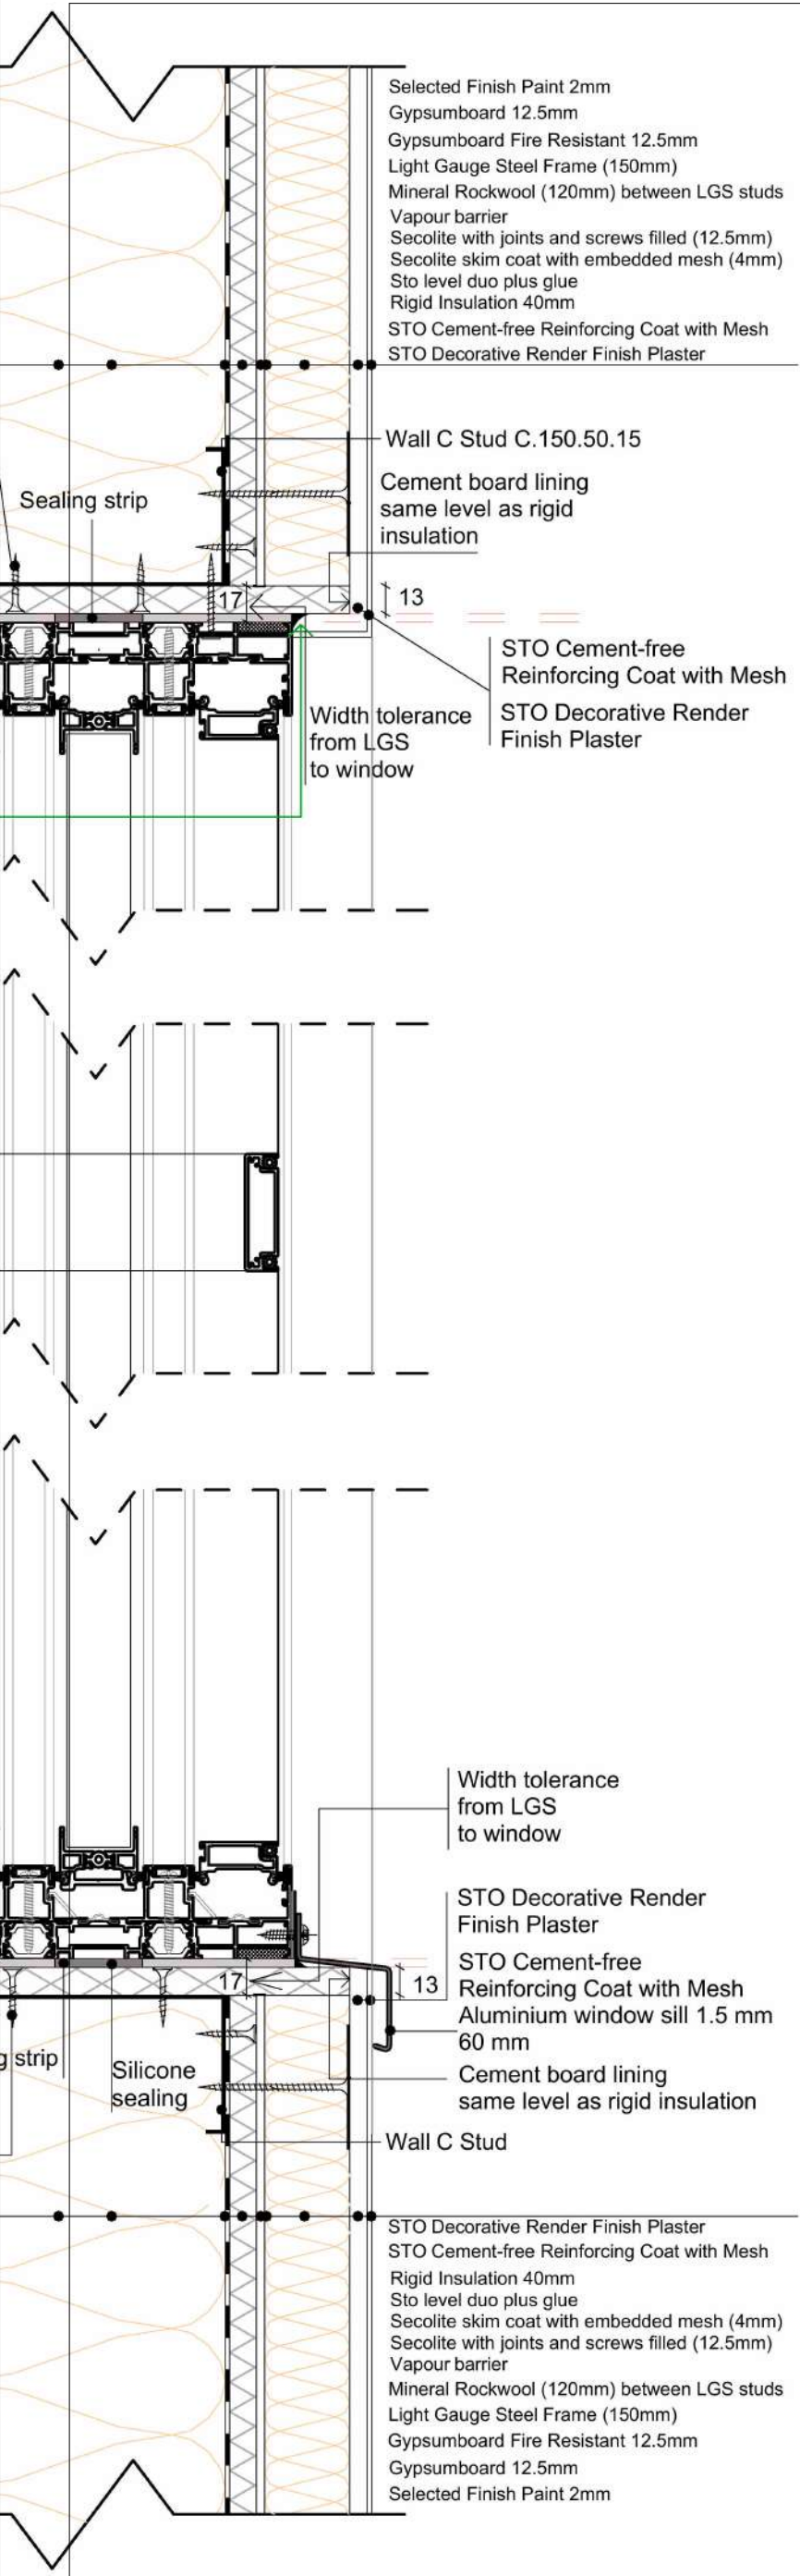

Windows with insect screens

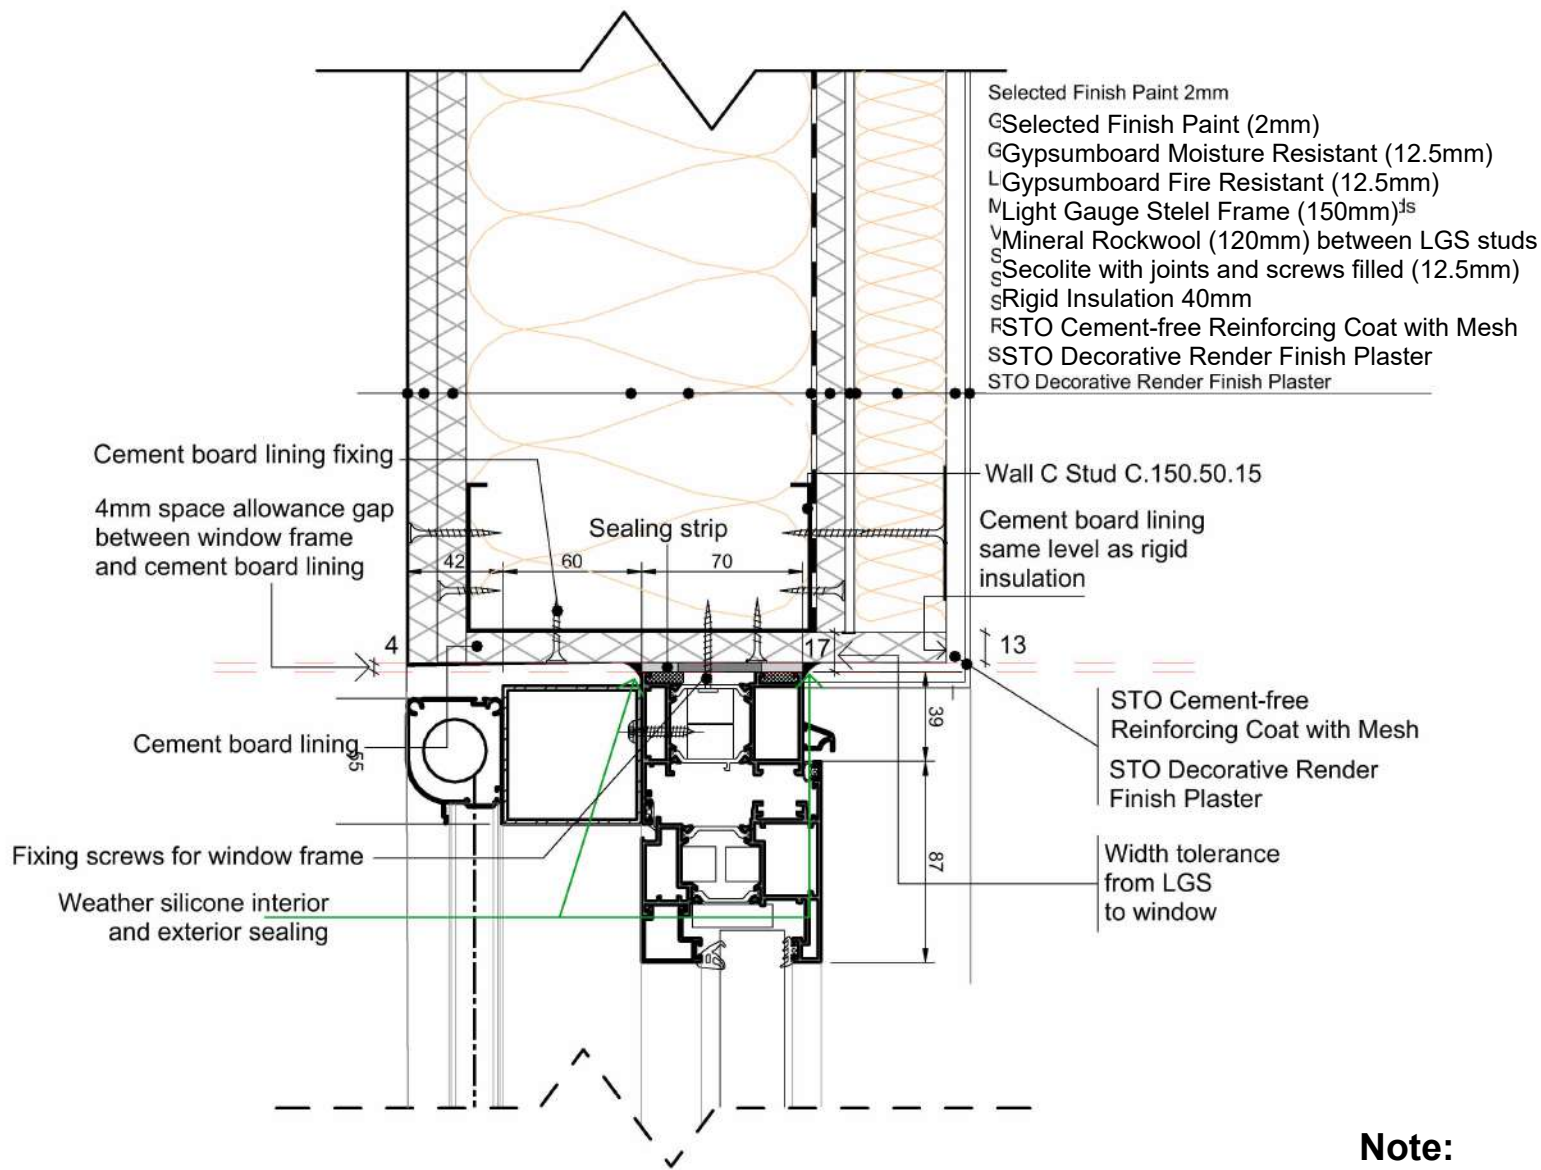

D.Casement Window Section with insect screens

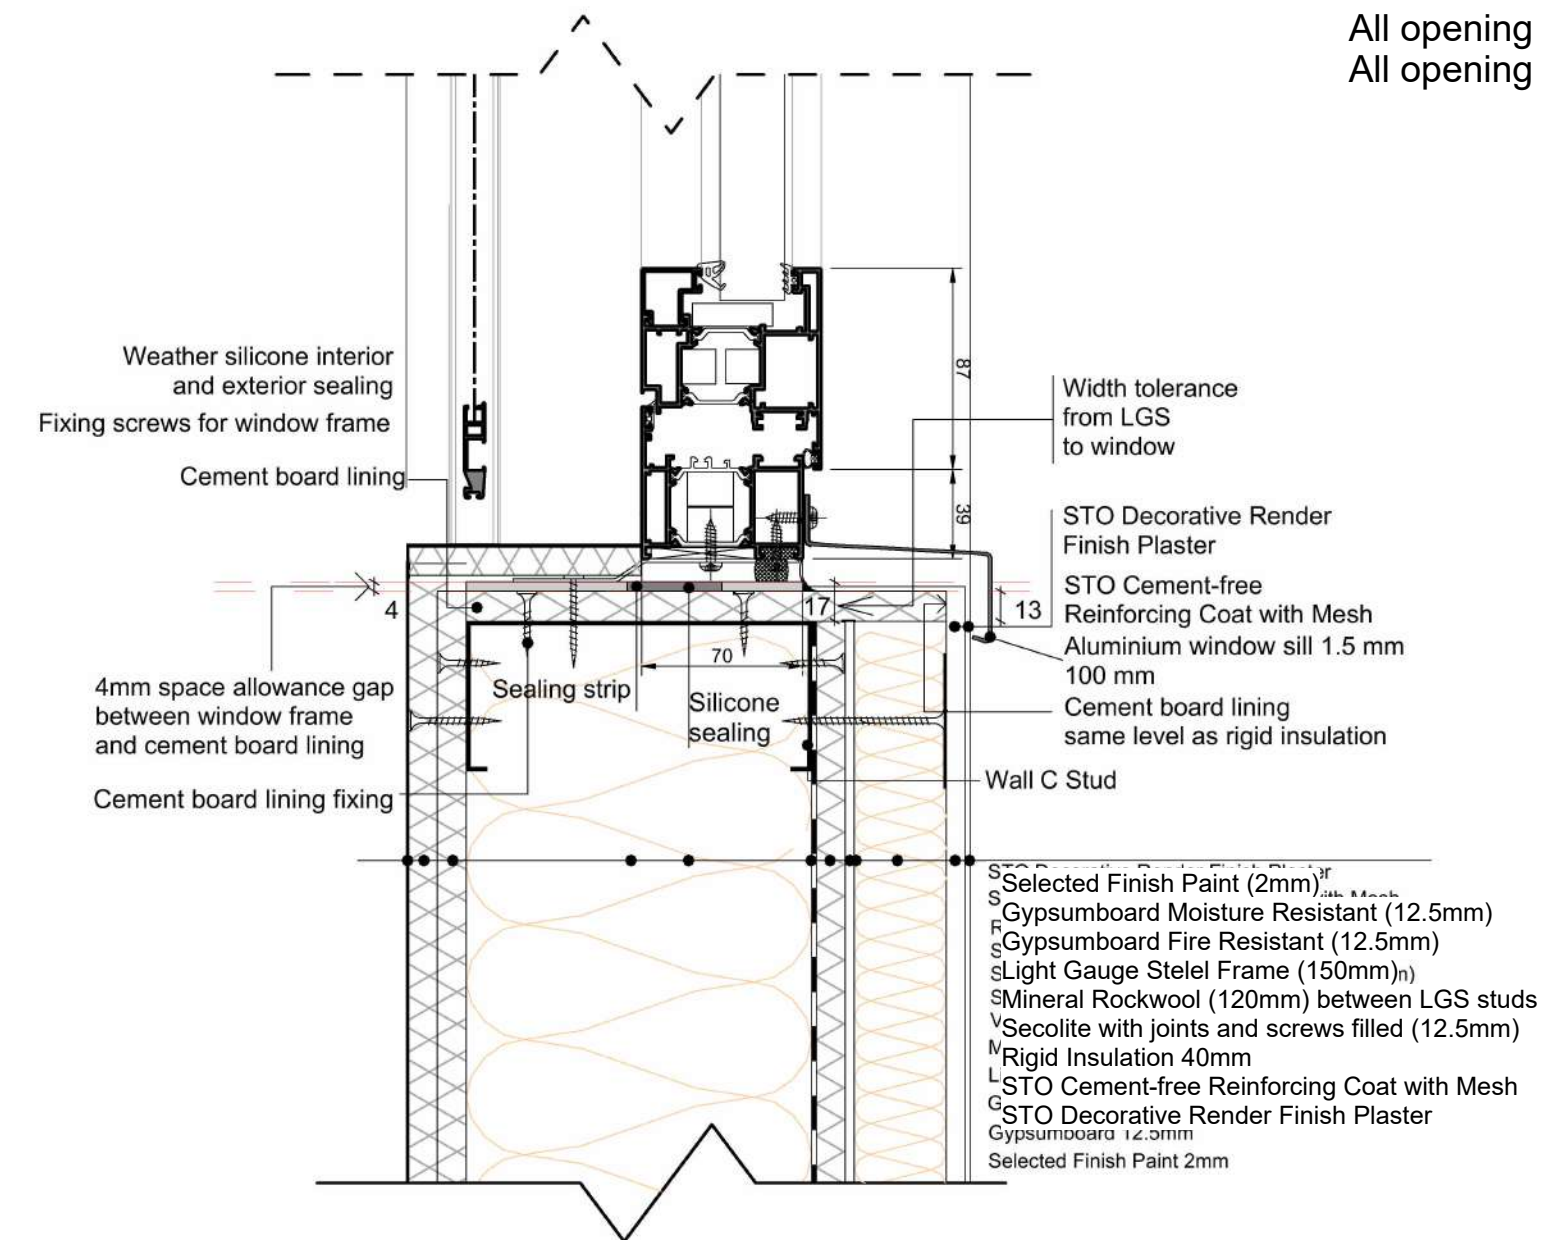

Note:

- *Openings are provided without insect screens as standard. Insect screens can be provided at additional cost.
- *Shutters are excluded. If required these will be provided by others-acquired locally according to dimensions of finished openings after finish application. Drawings are made for design purposes only. Garage type doors are excluded and should be sourced by the owner.
- All opening windows open outwards.
- All opening drawings are viewed from the outside

- THESE DRAWINGS MUST BE CHECKED BY THE CUSTOMER OR CONTRACTOR PRIOR TO APPROVAL. ANY ERRORS OR OMISSIONS MUST BE REPORTED IN WRITING TO BAUHU PRIOR TO COMMENCEMENT OF CONSTRUCTION.
- ARCHITECTURAL DRAWINGS SHOULD BE READ IN CONJUNCTION WITH STRUCTURAL DETAILING AND FABRICATION GENERAL ASSEMBLY DRAWINGS.
- FOR CONSTRUCTION PURPOSES, USE ONLY THE LATEST APPROVED DRAWINGS LABELED 'ISSUED FOR CONSTRUCTION'.
- DO NOT SCALE FROM THIS DRAWING.
- THE COMPANY OPERATES USING METRIC DIMENSIONS AS THE PRINCIPAL DENOMINATION.
- ALL CONCRETE WORKS ARE OUTSIDE OF THE SCOPE OF THE COMPANY. INFORMATION REGARDING SLAB DESIGN AND CONNECTIONS IN THESE DRAWINGS ARE INTENDED FOR GUIDANCE ONLY. FOUNDATION AND SLAB WORKS SHOULD BE DESIGNED AND APPROVED BY A LOCAL STRUCTURAL ENGINEER.
- THE COMPANY RETAINS FULL TITLE AND OWNERSHIP OF THESE PLANS AND DESIGNS. ANY UNAUTHORISED USE, REPRODUCTION, OR DISTRIBUTION OF THESE PLANS, WHETHER IN WHOLE OR PART, IS EXPRESSLY PROHIBITED WITHOUT PRIOR WRITTEN CONSENT.
- THE HYBRID STEEL FRAME CONSTRUCTION SYSTEM AND METHODOLOGY (PATENT PENDING) DESCRIBED IN THESE PLANS HAS BEEN DEVELOPED BY THE COMPANY AND IS SUBJECT TO A PROVISIONAL PATENT APPLICATION & ASSIGNMENT - US APPLICATION NO. 63/722,841

No.	Revision	Date

ISSUED FOR:

- Issued for information
- Issued for client approval
- Issued for fabrication
- Issued for construction

The Charlston

DRAWING TITLE:

Slider Door Section Detail

DRAWN BY:

Y.A.Clark

SCALE:

DRAWING NO:

C103

DATE:

18/03/2026

HRS CONNECTIONS

1. THESE DRAWINGS MUST BE CHECKED BY THE CUSTOMER OR CONTRACTOR PRIOR TO APPROVAL. ANY ERRORS OR OMISSIONS MUST BE REPORTED IN WRITING TO BAUHU PRIOR TO COMMENCEMENT OF CONSTRUCTION.
2. ARCHITECTURAL DRAWINGS SHOULD BE READ IN CONJUNCTION WITH STRUCTURAL DETAILING AND FABRICATION GENERAL ASSEMBLY DRAWINGS.
3. FOR CONSTRUCTION PURPOSES, USE ONLY THE LATEST APPROVED DRAWINGS LABELED 'ISSUED FOR CONSTRUCTION'.
4. DO NOT SCALE FROM THIS DRAWING.
5. THE COMPANY OPERATES USING METRIC DIMENSIONS AS THE PRINCIPAL DENOMINATION.
6. ALL CONCRETE WORKS ARE OUTSIDE OF THE SCOPE OF THE COMPANY. INFORMATION REGARDING SLAB DESIGN AND CONNECTIONS IN THESE DRAWINGS ARE INTENDED FOR GUIDANCE ONLY. FOUNDATION AND SLAB WORKS SHOULD BE DESIGNED AND APPROVED BY A LOCAL STRUCTURAL ENGINEER.
7. THE COMPANY RETAINS FULL TITLE AND OWNERSHIP OF THESE PLANS AND DESIGNS. ANY UNAUTHORISED USE, REPRODUCTION, OR DISTRIBUTION OF THESE PLANS, WHETHER IN WHOLE OR PART, IS EXPRESSLY PROHIBITED WITHOUT PRIOR WRITTEN CONSENT.
8. THE HYBRID STEEL FRAME CONSTRUCTION SYSTEM AND METHODOLOGY (PATENT PENDING) DESCRIBED IN THESE PLANS HAS BEEN DEVELOPED BY THE COMPANY AND IS SUBJECT TO A PROVISIONAL PATENT APPLICATION & ASSIGNMENT - US APPLICATION NO. 63/722,841

No.	Revision	Date

ISSUED FOR:

Issued for information

Issued for client approval

Issued for fabrication

Issued for construction

The Charlston

DRAWING TITLE:

HRS Connections

DRAWN BY:

Y.A.Clark


SCALE:

DRAWING NO:


C107

DATE:


18/03/2026

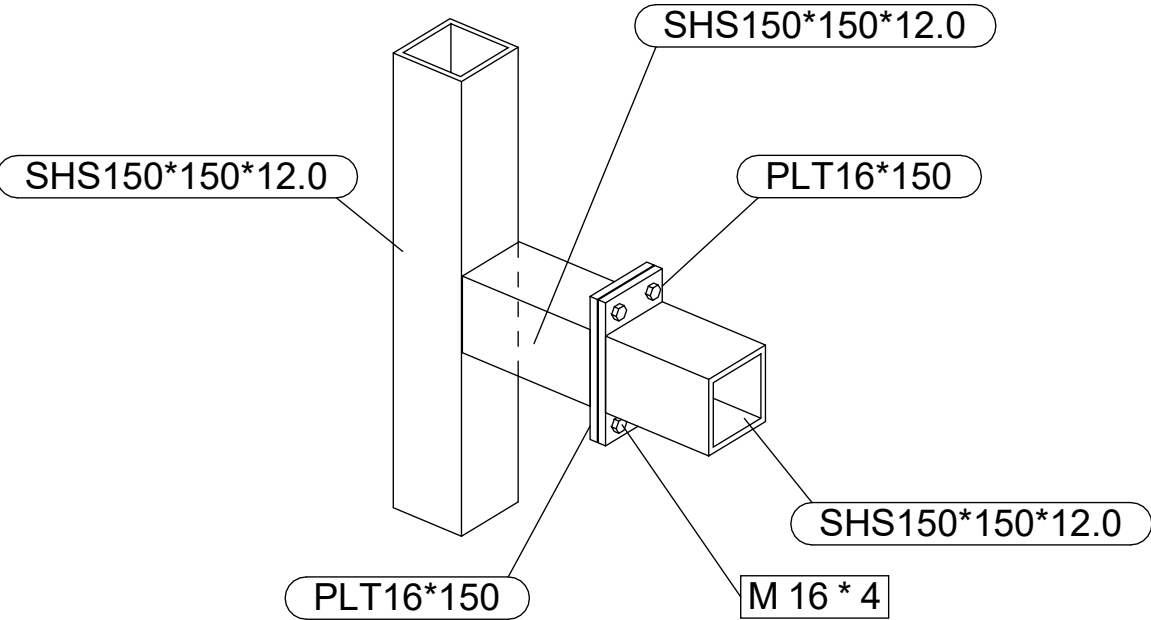


Typical Column Beam Stub Connection

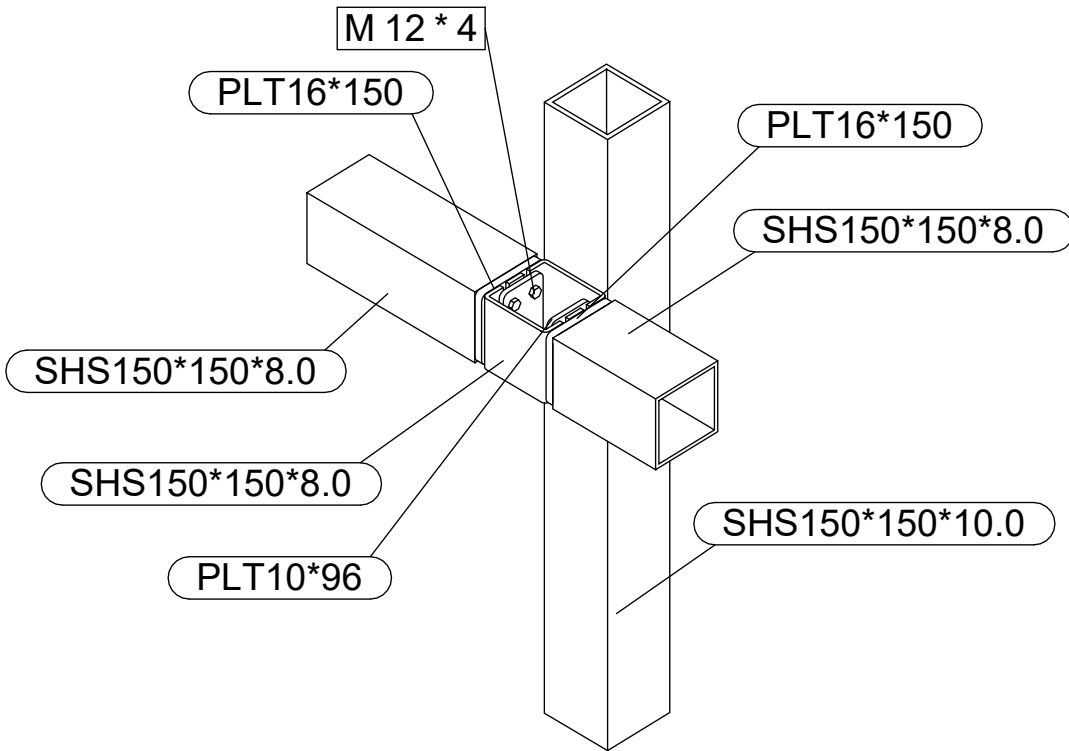


Typical Beam Offset Connection

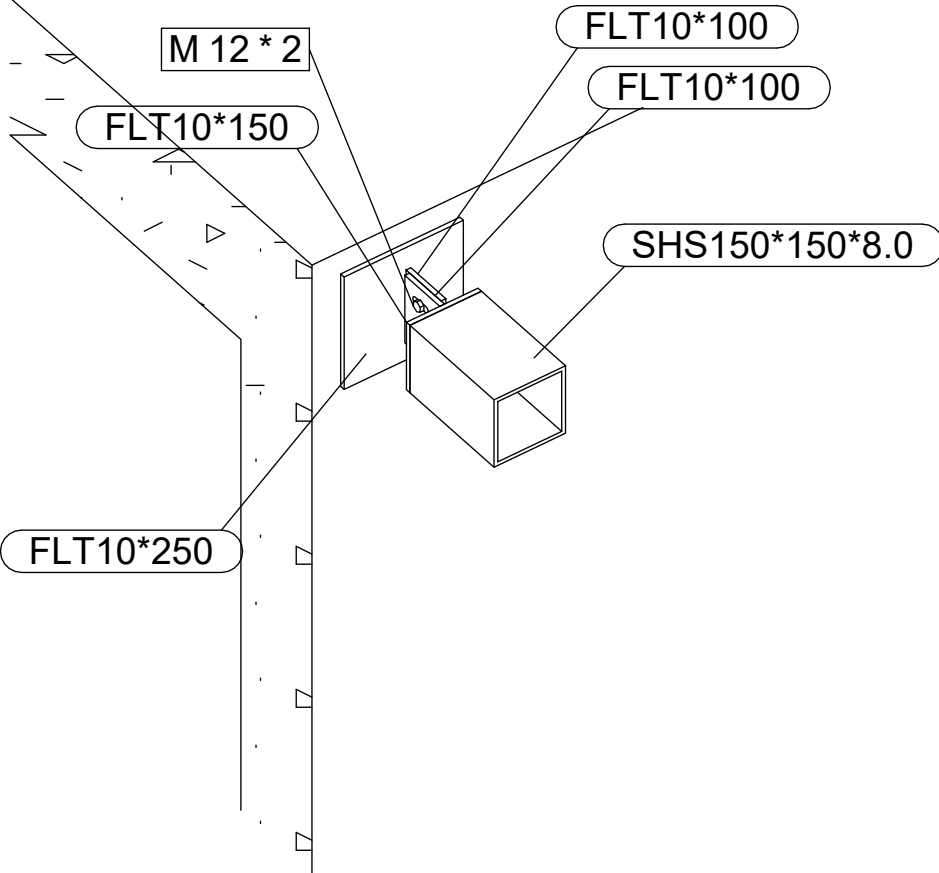


Typical Beam to Concrete Connection

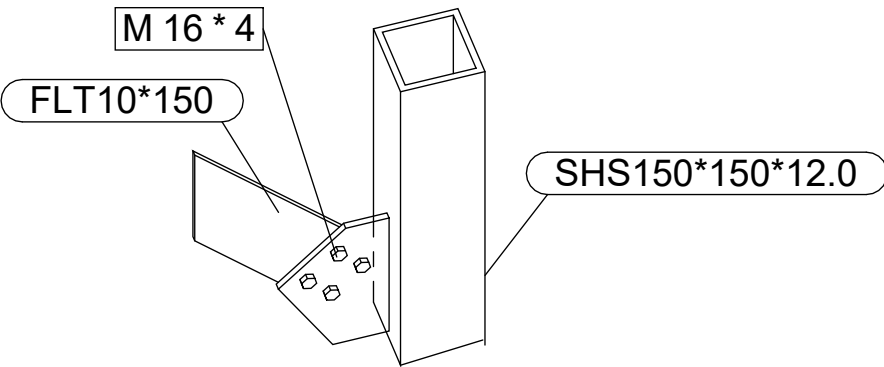


Typical Bracing Connection

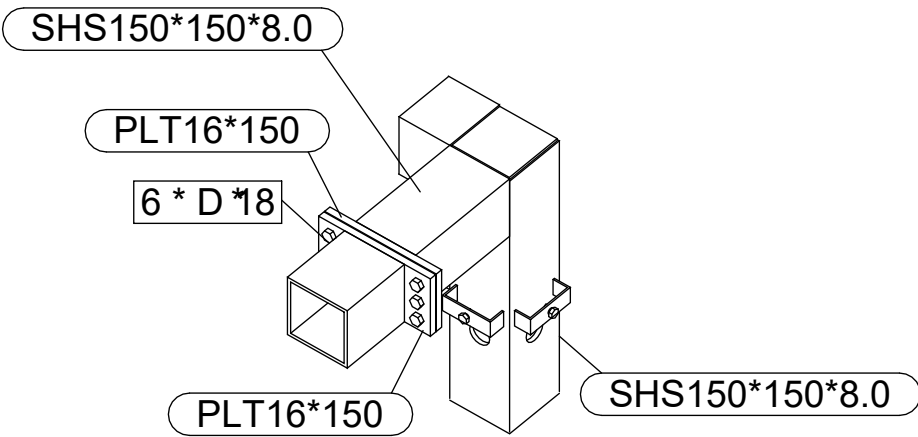


Typical Column to Beam Splice Connection

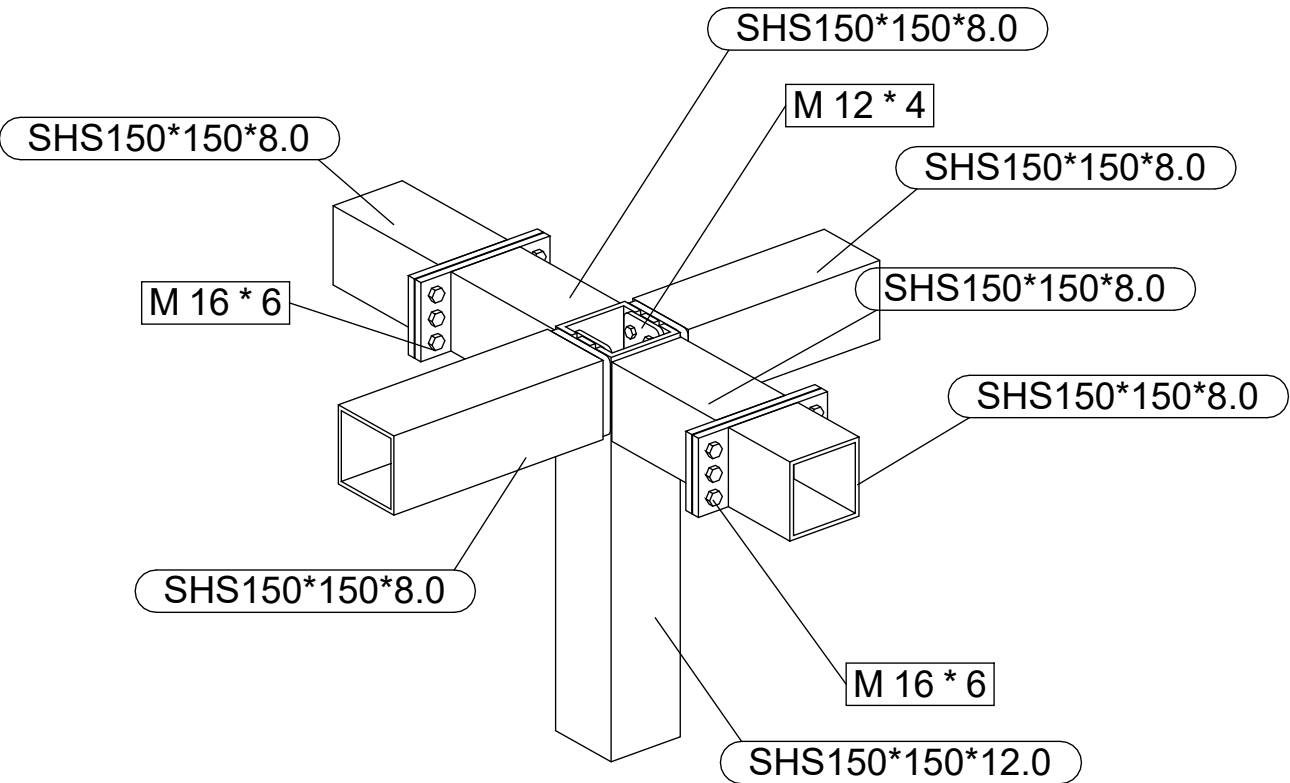

Typical Roof Column Beam Connection

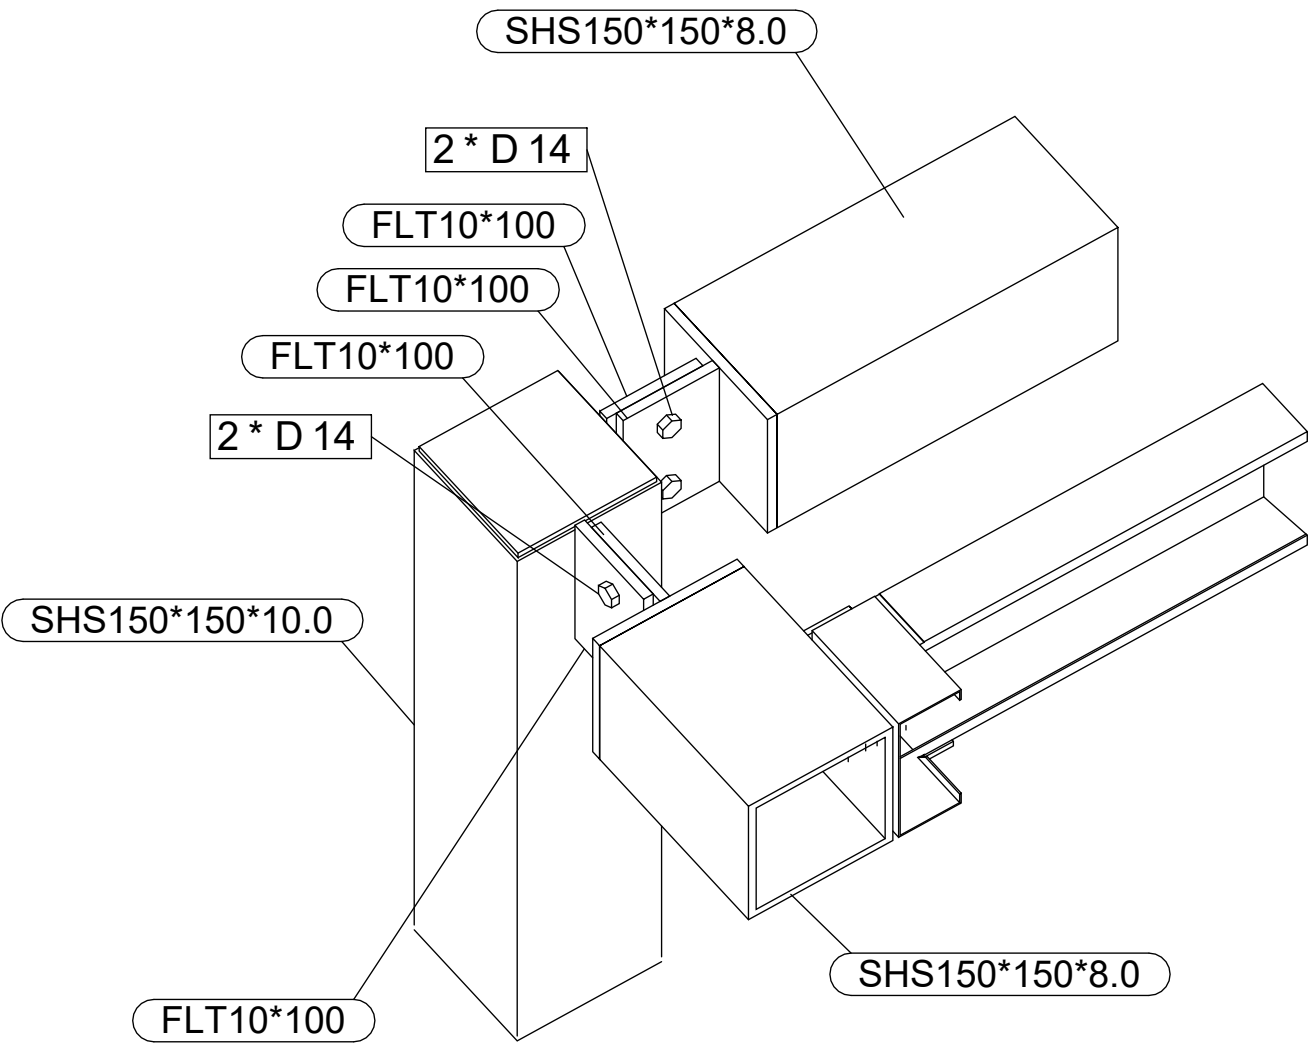


Typical Column to Beam Fine Plate Connection

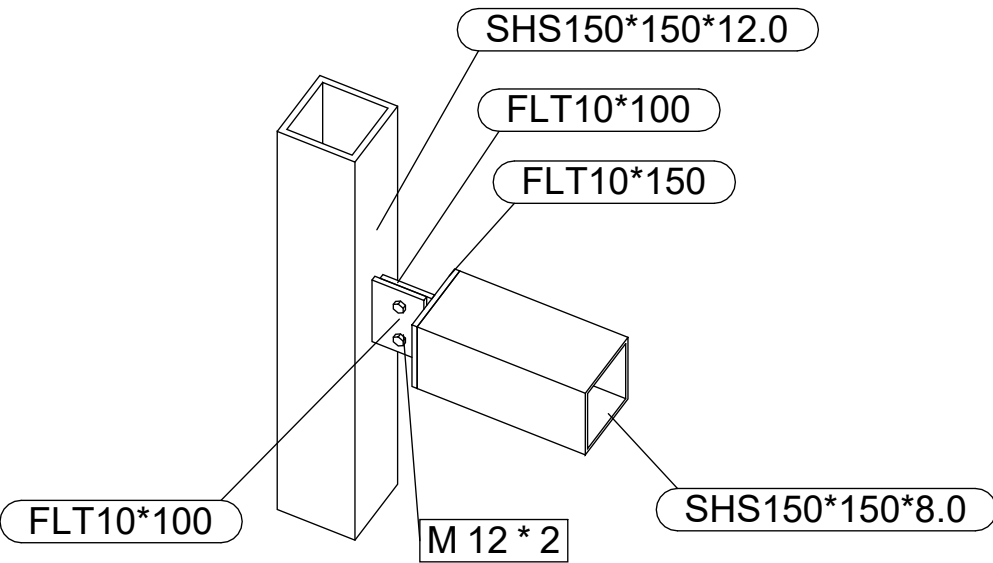


Typical Column Beam Fine Plate Connection


LGS CONNECTIONS

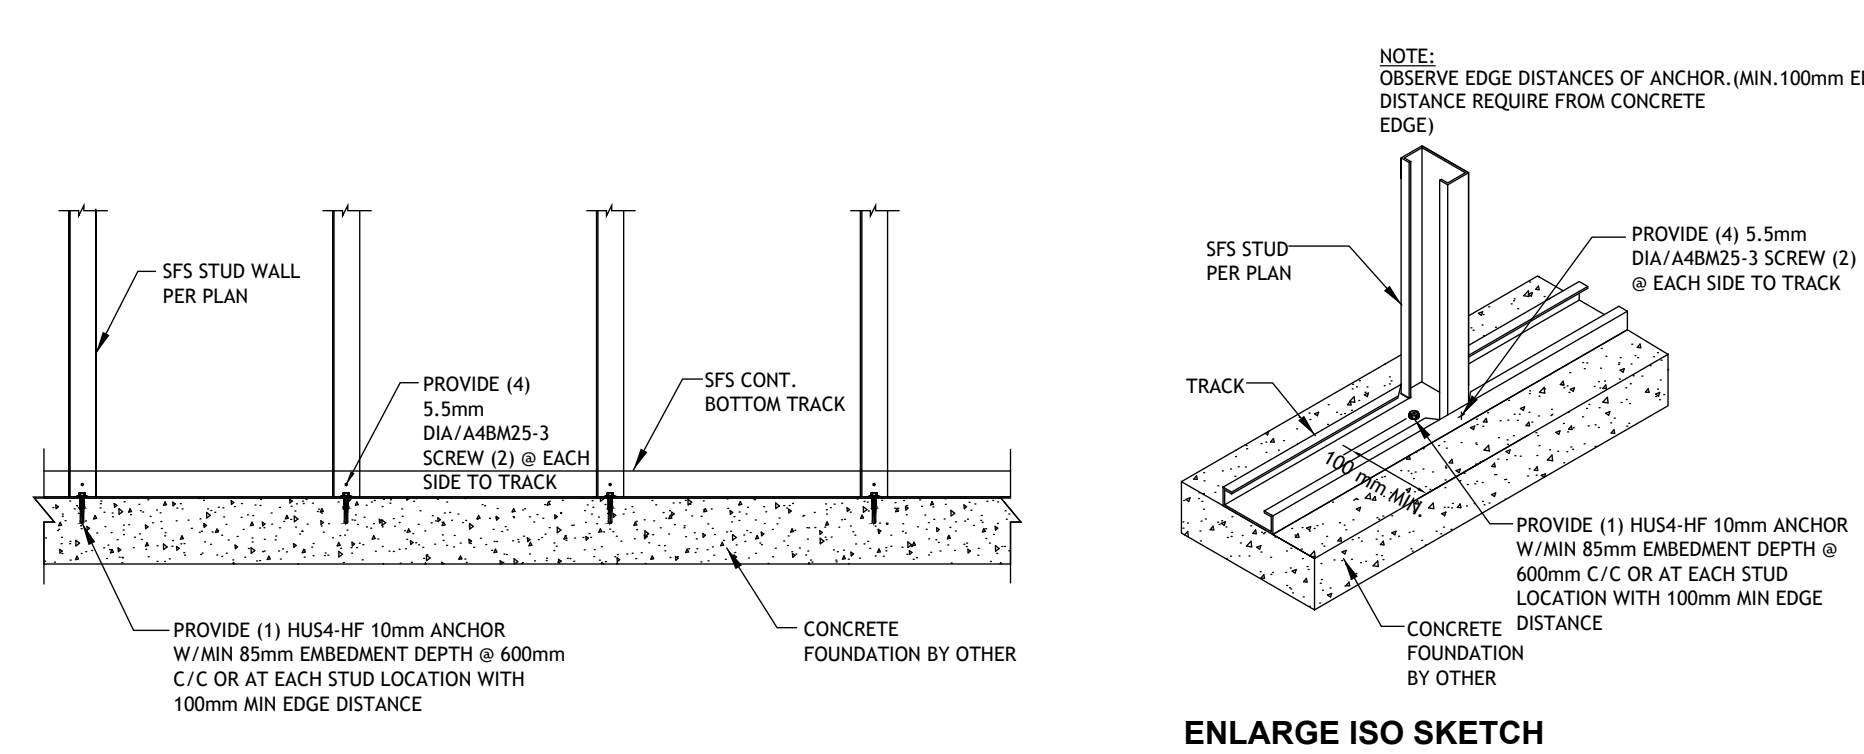


Typical Detail : SFS Bottom Track to Concrete Connection (External Wall)

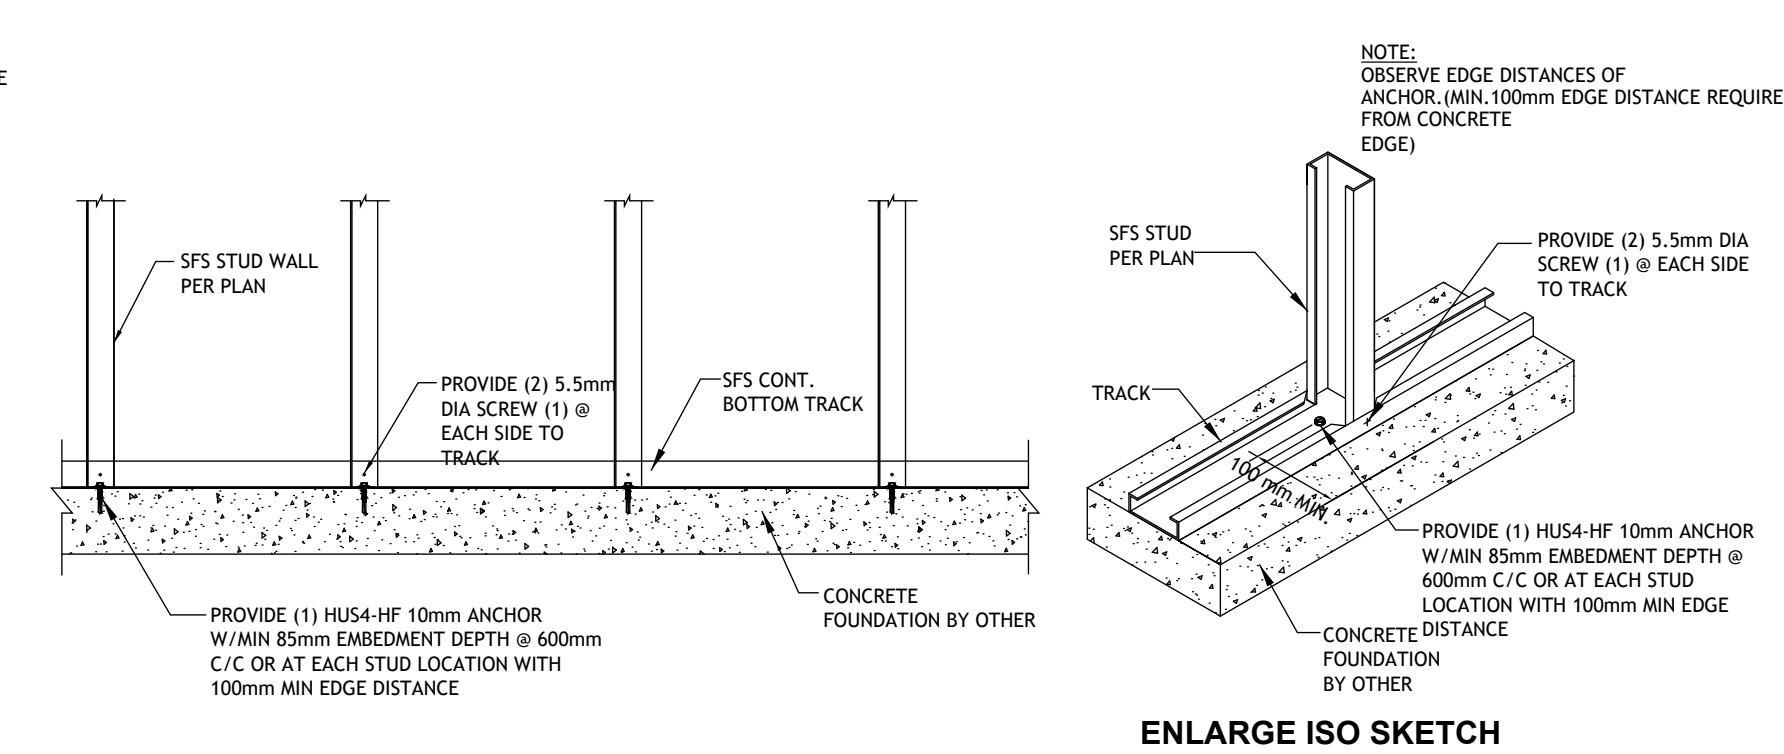


Typical Detail : Bottom Track to Concrete Connection (Internal Wall)

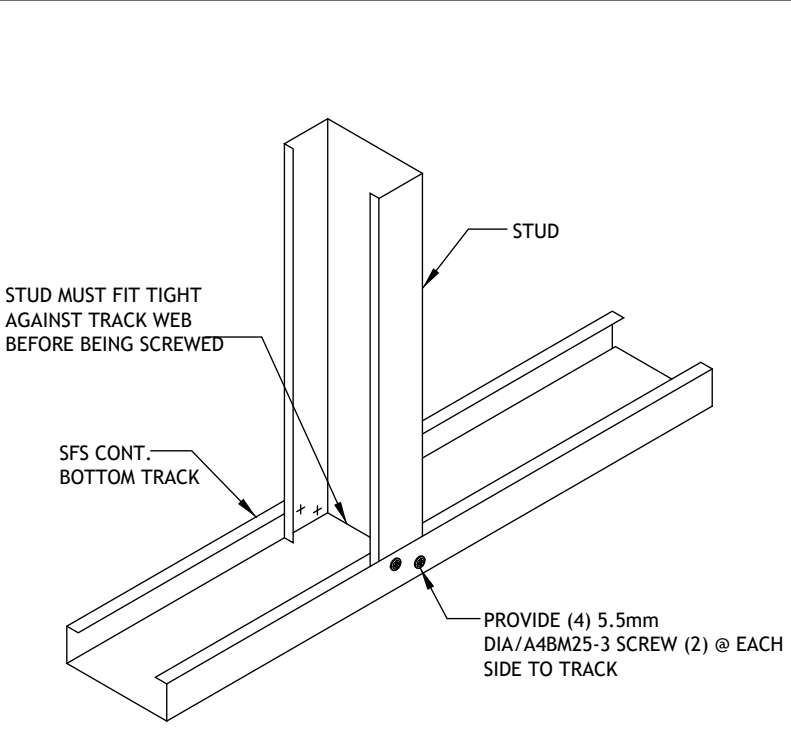


Stud to Bottom Track Connection (External Wall)

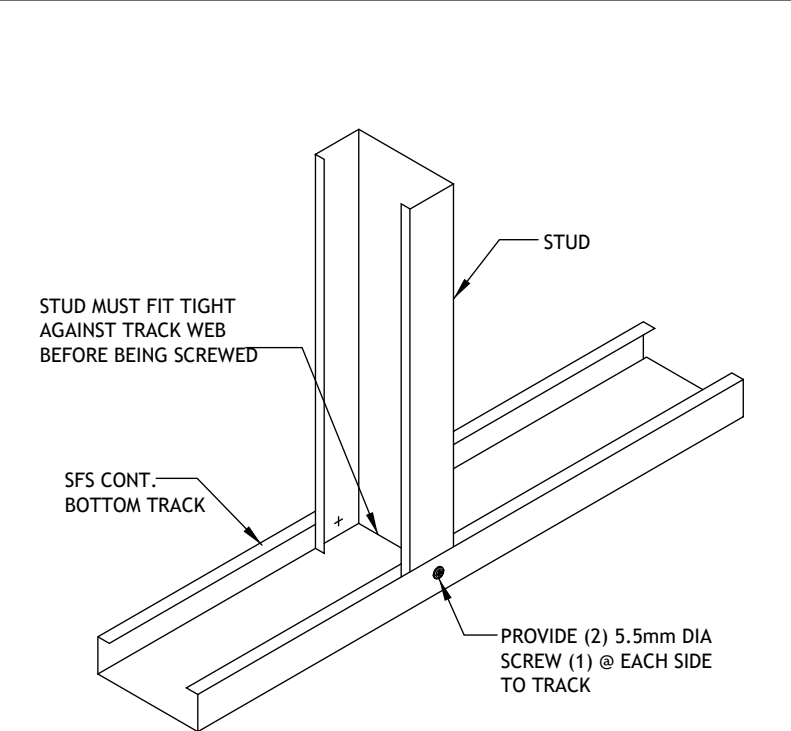


Stud to Bottom Track Connection (Internal Wall)

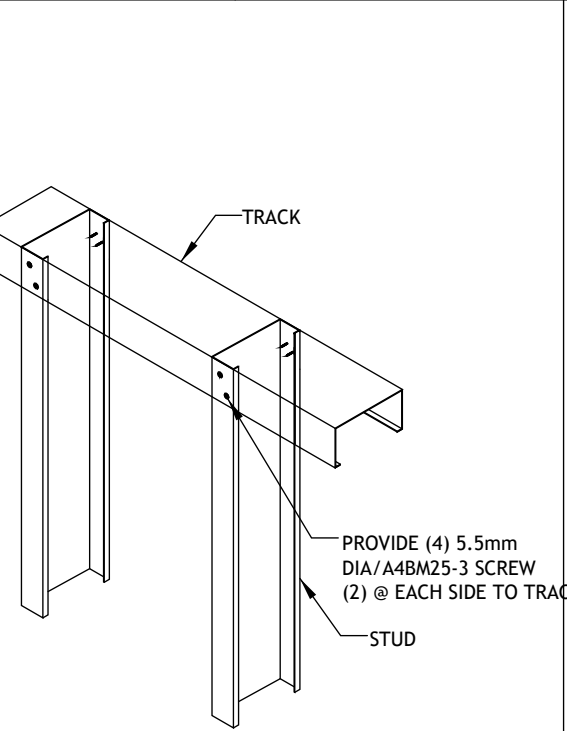


Stud to Top Track Connection (External Wall)

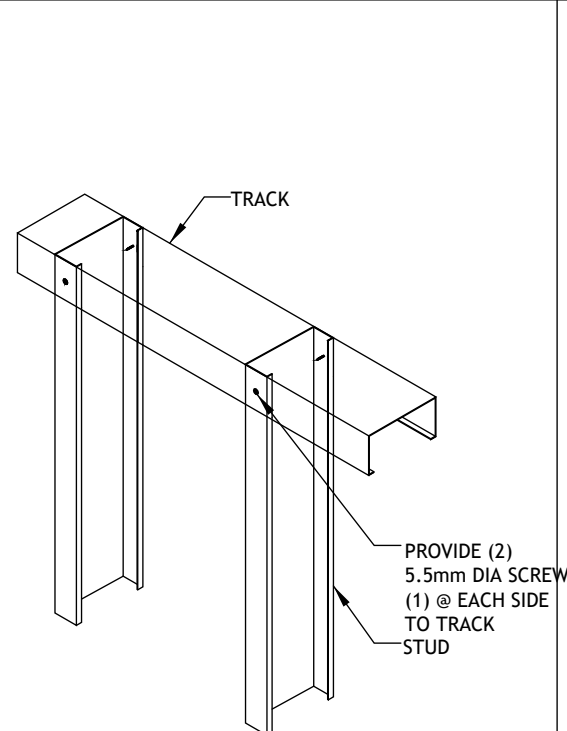


Stud to Top Track Connection (Internal Wall)

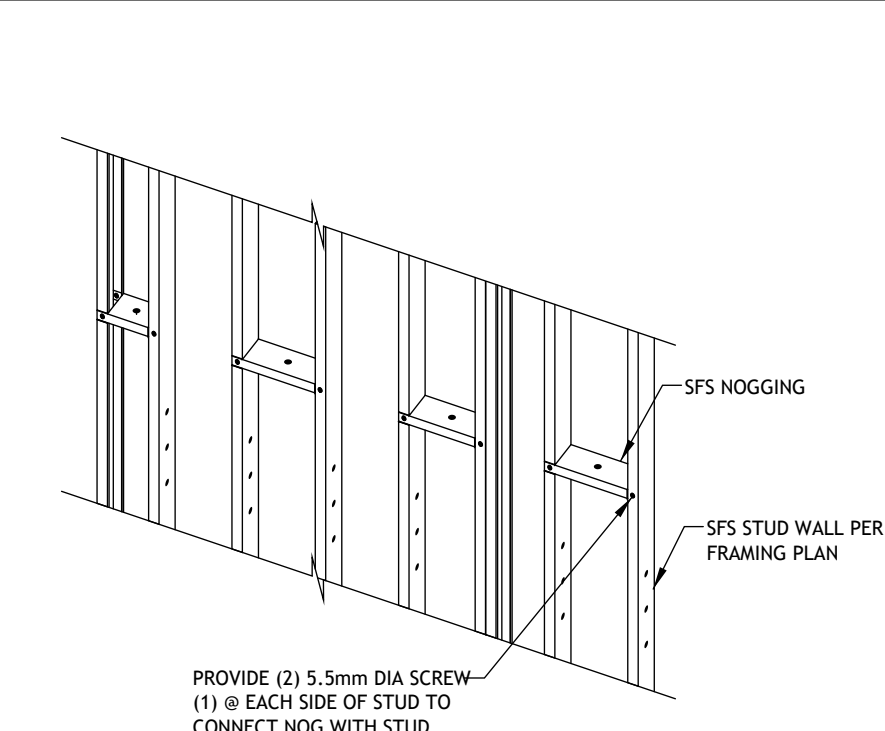


Hit and Miss Nogging to Stud Connection Detail

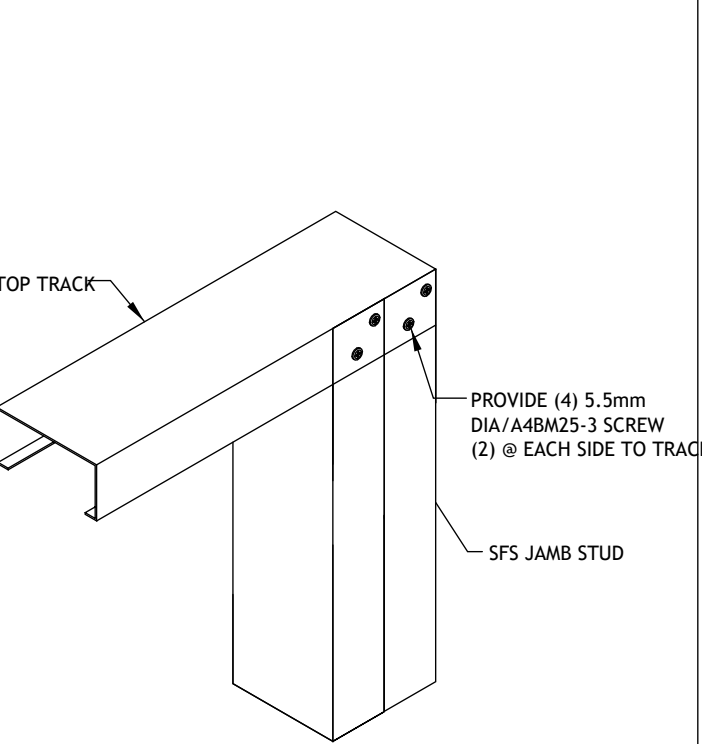


Box Jamb to Top Track Connection

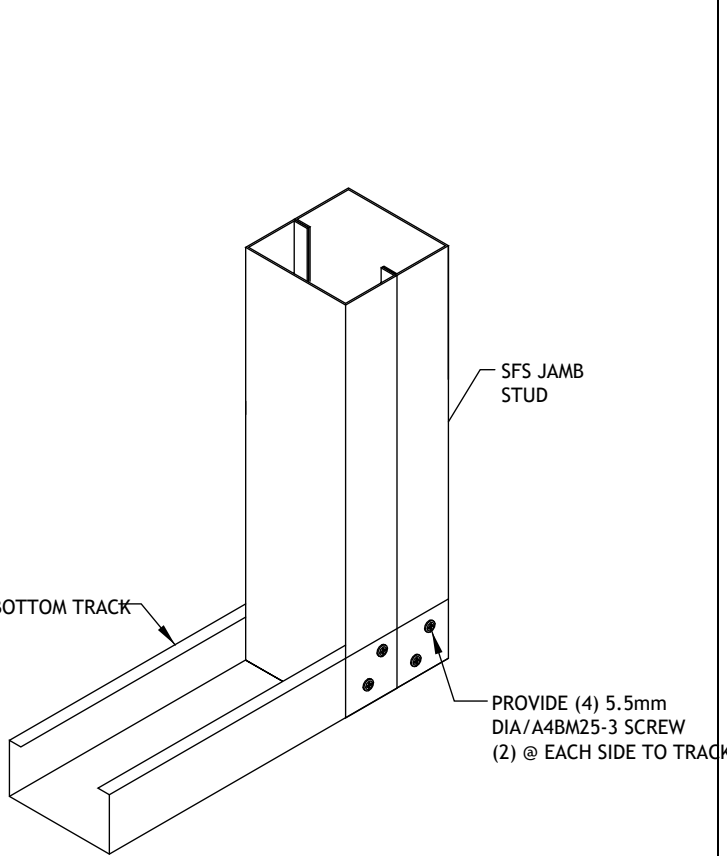


Box Jamb to Bottom Track Connection

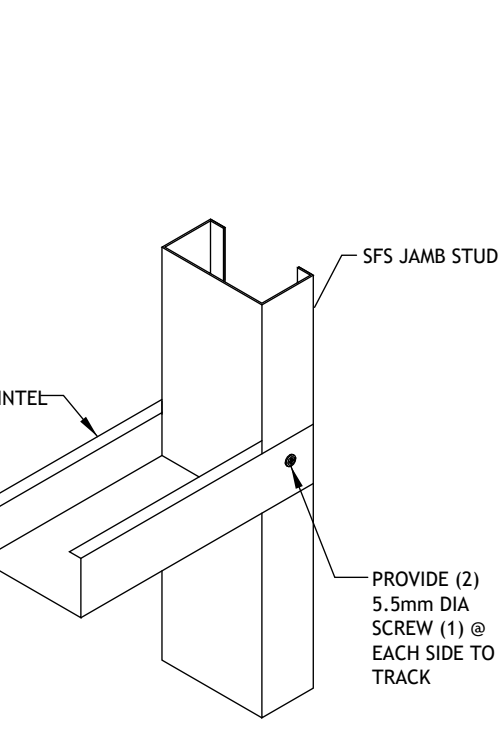


Lintel to Jamb Stud Connection

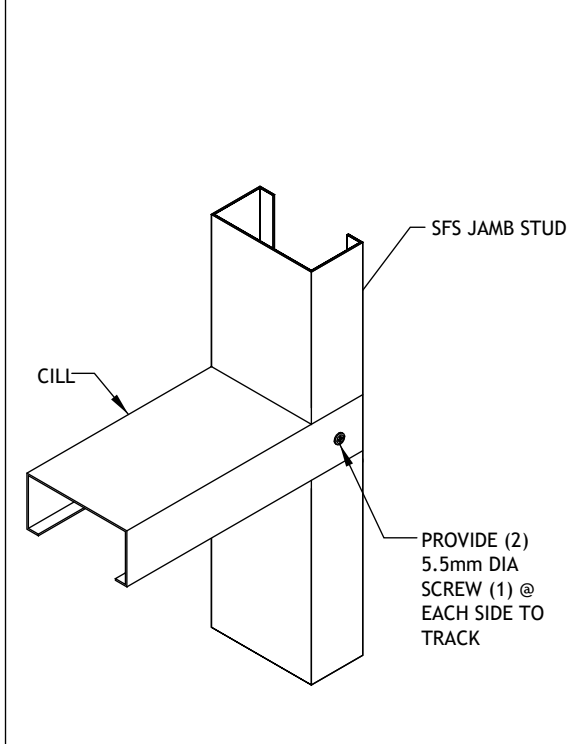

Typ. Cill to Jamb Stud Connection

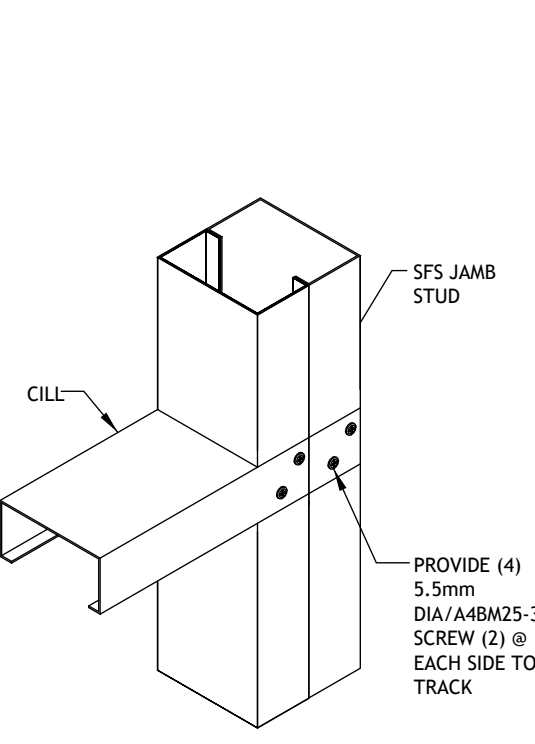

Typ. Cill to Jamb Stud Connection

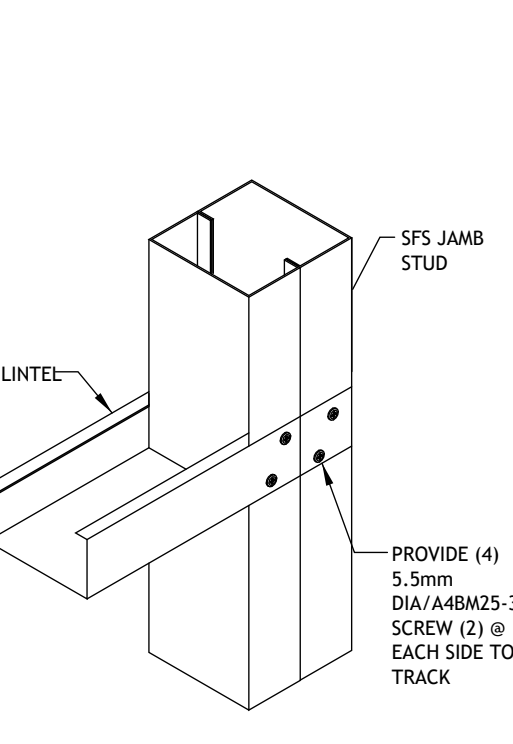

Lintel to Jamb Stud Connection

1. THESE DRAWINGS MUST BE CHECKED BY THE CUSTOMER OR CONTRACTOR PRIOR TO APPROVAL. ANY ERRORS OR OMISSIONS MUST BE REPORTED IN WRITING TO BAUHU PRIOR TO COMMENCEMENT OF CONSTRUCTION.
2. ARCHITECTURAL DRAWINGS SHOULD BE READ IN CONJUNCTION WITH STRUCTURAL DETAILING AND FABRICATION GENERAL ASSEMBLY DRAWINGS.
3. FOR CONSTRUCTION PURPOSES, USE ONLY THE LATEST APPROVED DRAWINGS LABELED 'ISSUED FOR CONSTRUCTION'.
4. DO NOT SCALE FROM THIS DRAWING.
5. THE COMPANY OPERATES USING METRIC DIMENSIONS AS THE PRINCIPAL DENOMINATION.
6. ALL CONCRETE WORKS ARE OUTSIDE OF THE SCOPE OF THE COMPANY. INFORMATION REGARDING SLAB DESIGN AND CONNECTIONS IN THESE DRAWINGS ARE INTENDED FOR GUIDANCE ONLY. FOUNDATION AND SLAB WORKS SHOULD BE DESIGNED AND APPROVED BY A LOCAL STRUCTURAL ENGINEER.
7. THE COMPANY RETAINS FULL TITLE AND OWNERSHIP OF THESE PLANS AND DESIGNS. ANY UNAUTHORISED USE, REPRODUCTION, OR DISTRIBUTION OF THESE PLANS, WHETHER IN WHOLE OR PART, IS EXPRESSLY PROHIBITED WITHOUT PRIOR WRITTEN CONSENT.
8. THE HYBRID STEEL FRAME CONSTRUCTION SYSTEM AND METHODOLOGY (PATENT PENDING) DESCRIBED IN THESE PLANS HAS BEEN DEVELOPED BY THE COMPANY AND IS SUBJECT TO A PROVISIONAL PATENT APPLICATION & ASSIGNMENT - US APPLICATION NO. 63/722,841

No.	Revision	Date

ISSUED FOR:

Issued for information

Issued for client approval

Issued for fabrication

Issued for construction

The Charlston

DRAWING TITLE:
LGS Connections

DRAWN BY:
Y.A.Clark


SCALE:

DRAWING NO:
C108


DATE:
18/03/2026

Typical Frame Connections 1


1. THESE DRAWINGS MUST BE CHECKED BY THE CUSTOMER OR CONTRACTOR PRIOR TO APPROVAL. ANY ERRORS OR OMISSIONS MUST BE REPORTED IN WRITING TO BAUHU PRIOR TO COMMENCEMENT OF CONSTRUCTION.
2. ARCHITECTURAL DRAWINGS SHOULD BE READ IN CONJUNCTION WITH STRUCTURAL DETAILING AND FABRICATION GENERAL ASSEMBLY DRAWINGS.
3. FOR CONSTRUCTION PURPOSES, USE ONLY THE LATEST APPROVED DRAWINGS LABELED 'ISSUED FOR CONSTRUCTION'.
4. DO NOT SCALE FROM THIS DRAWING.
5. THE COMPANY OPERATES USING METRIC DIMENSIONS AS THE PRINCIPAL DENOMINATION.
6. ALL CONCRETE WORKS ARE OUTSIDE OF THE SCOPE OF THE COMPANY. INFORMATION REGARDING SLAB DESIGN AND CONNECTIONS IN THESE DRAWINGS ARE INTENDED FOR GUIDENCE ONLY. FOUNDATION AND SLAB WORKS SHOULD BE DESIGNED AND APPROVED BY A LOCAL STRUCTURAL ENGINEER.
7. THE COMPANY RETAINS FULL TITLE AND OWNERSHIP OF THESE PLANS AND DESIGNS. ANY UNAUTHORISED USE, REPRODUCTION, OR DISTRIBUTION OF THESE PLANS, WHETHER IN WHOLE OR PART, IS EXPRESSLY PROHIBITED WITHOUT PRIOR WRITTEN CONSENT.
8. THE HYBRID STEEL FRAME CONSTRUCTION SYSTEM AND METHODOLOGY (PATENT PENDING) DESCRIBED IN THESE PLANS HAS BEEN DEVELOPED BY THE COMPANY AND IS SUBJECT TO A PROVISIONAL PATENT APPLICATION & ASSIGNMENT - US APPLICATION NO. 63/722,841

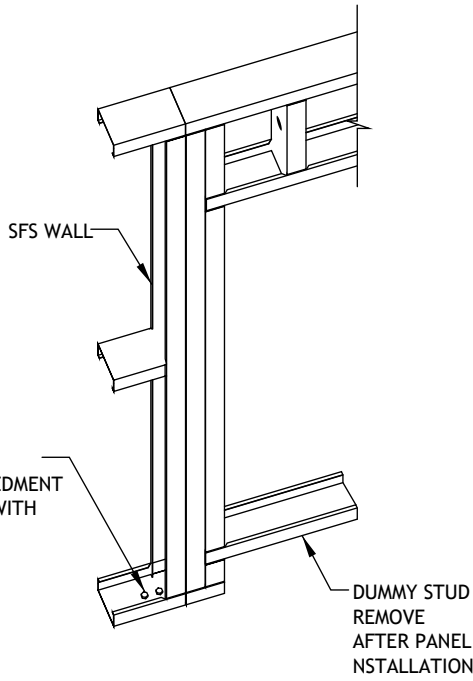


Typical Detail for Two Anchor at Jamb Location

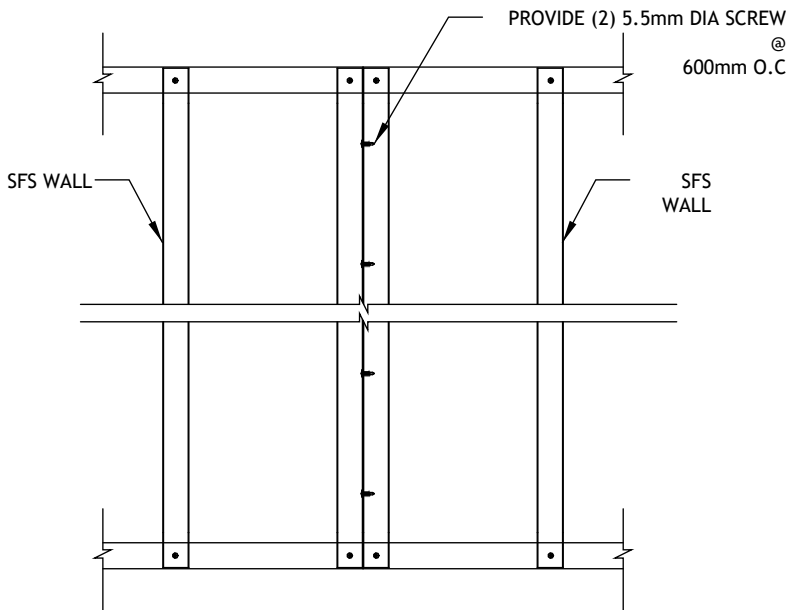


Typical Wall to SFS Wall Connection

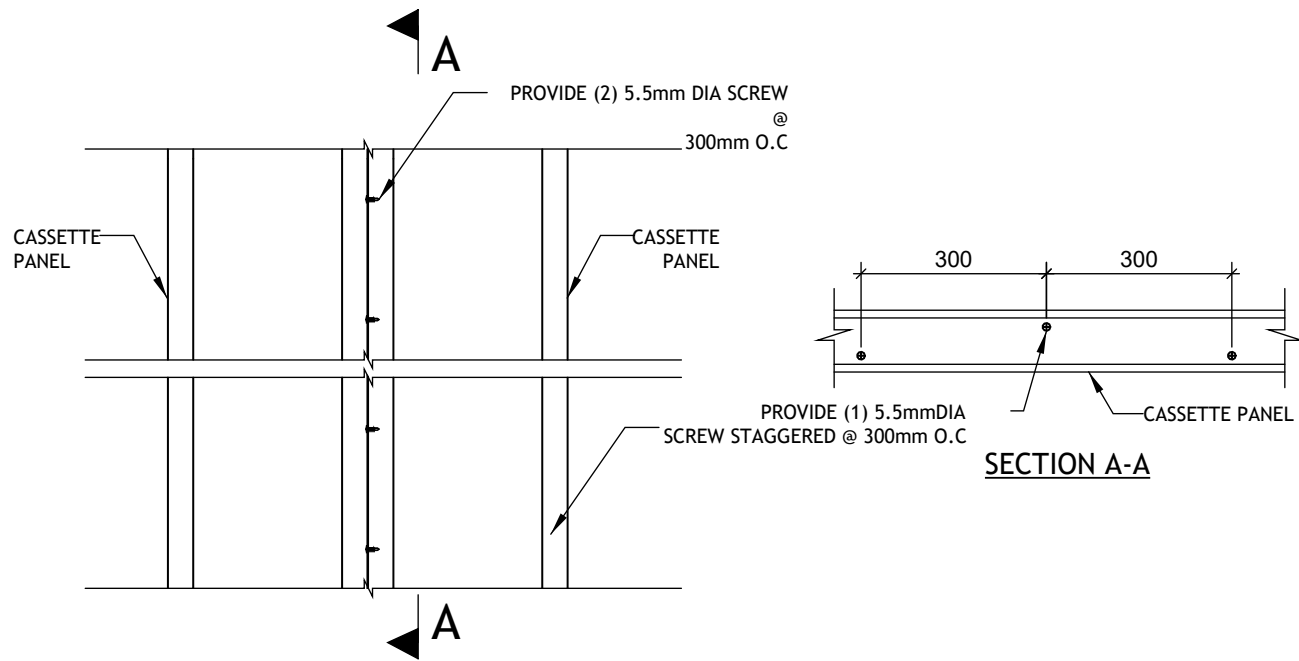


Cassette to Cassette Connection

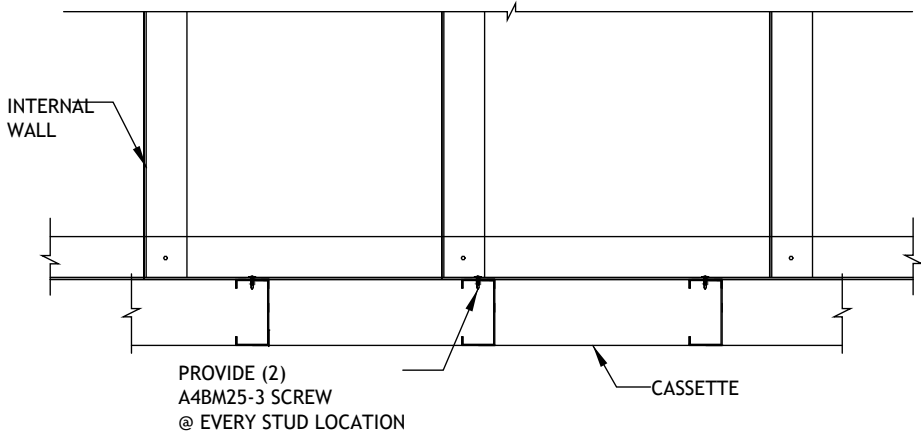


Internal Wall to Cassette Connection at Base

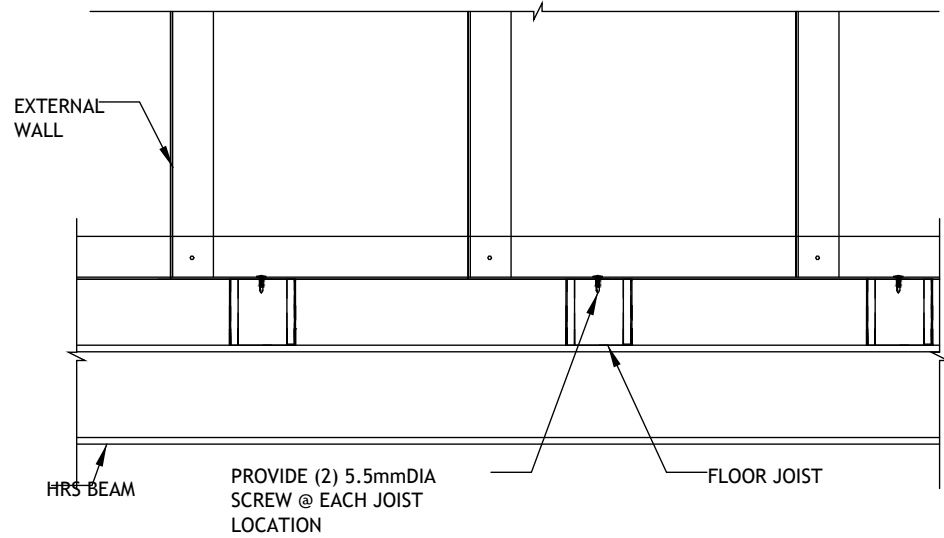


External Wall to Joist Connection at Base

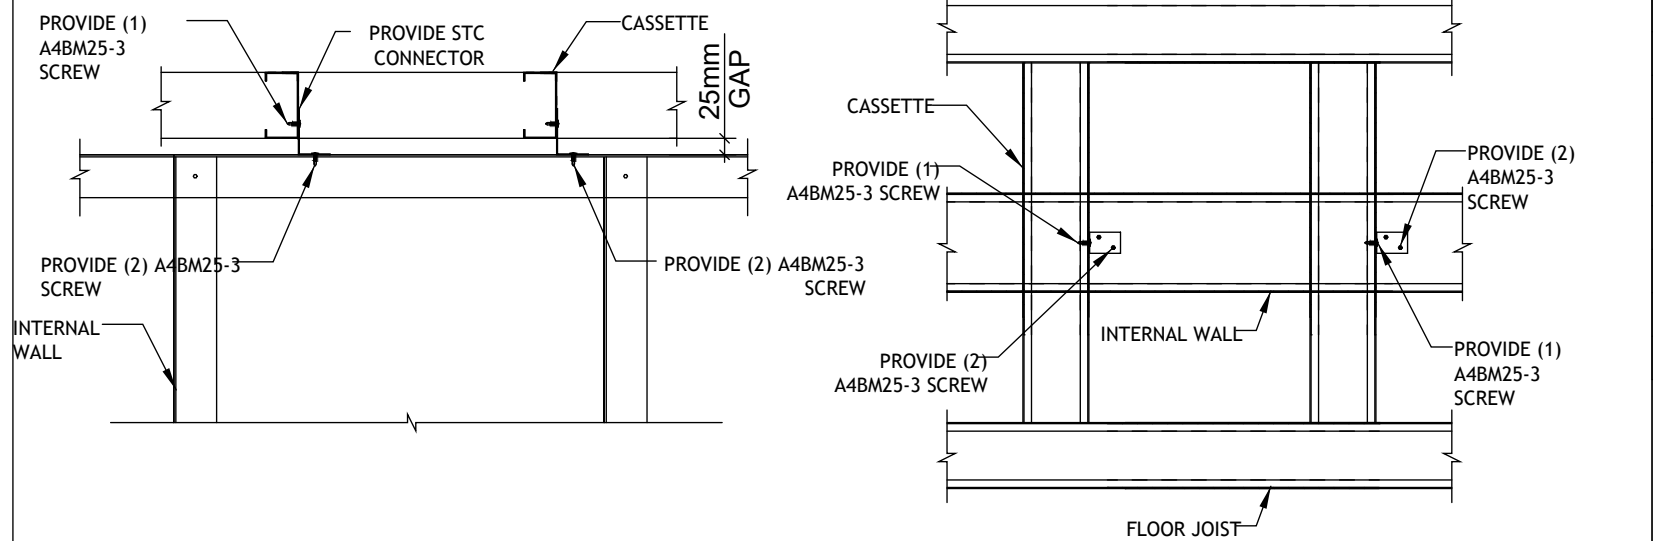


Typ. Internal Wall Connection at Roof Truss at Cassette Location

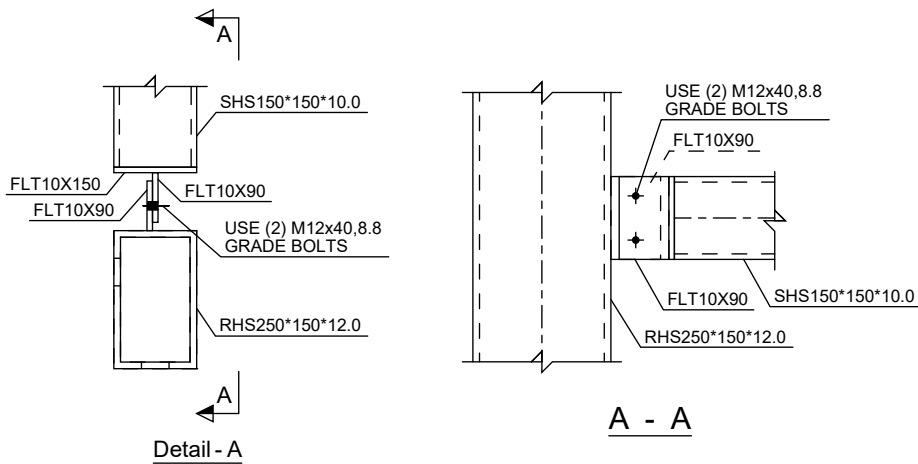

Typ. Fin Plate Connection Detail

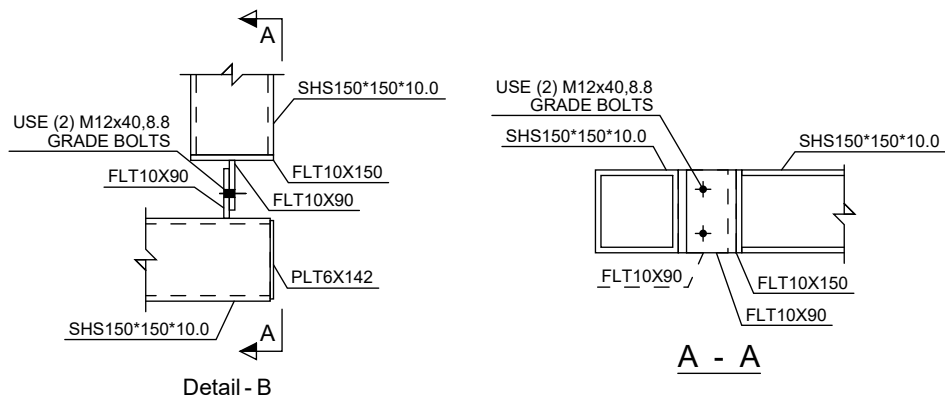

Typ. Fin Plate Connection Detail

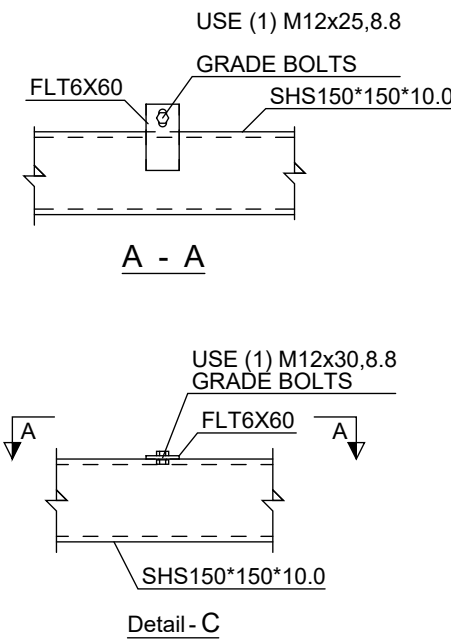

SFS Wall to HRS Beam Connection

No.	Revision	Date

ISSUED FOR:

Issued for information

Issued for client approval



Issued for fabrication

Issued for construction

The Charlston

DRAWING TITLE:
Typical Frame Connections
DRAWN BY:
Y.A.Clark
SCALE:
DRAWING NO:
C109
DATE:
18/03/2026



Typical Frame Connections 2

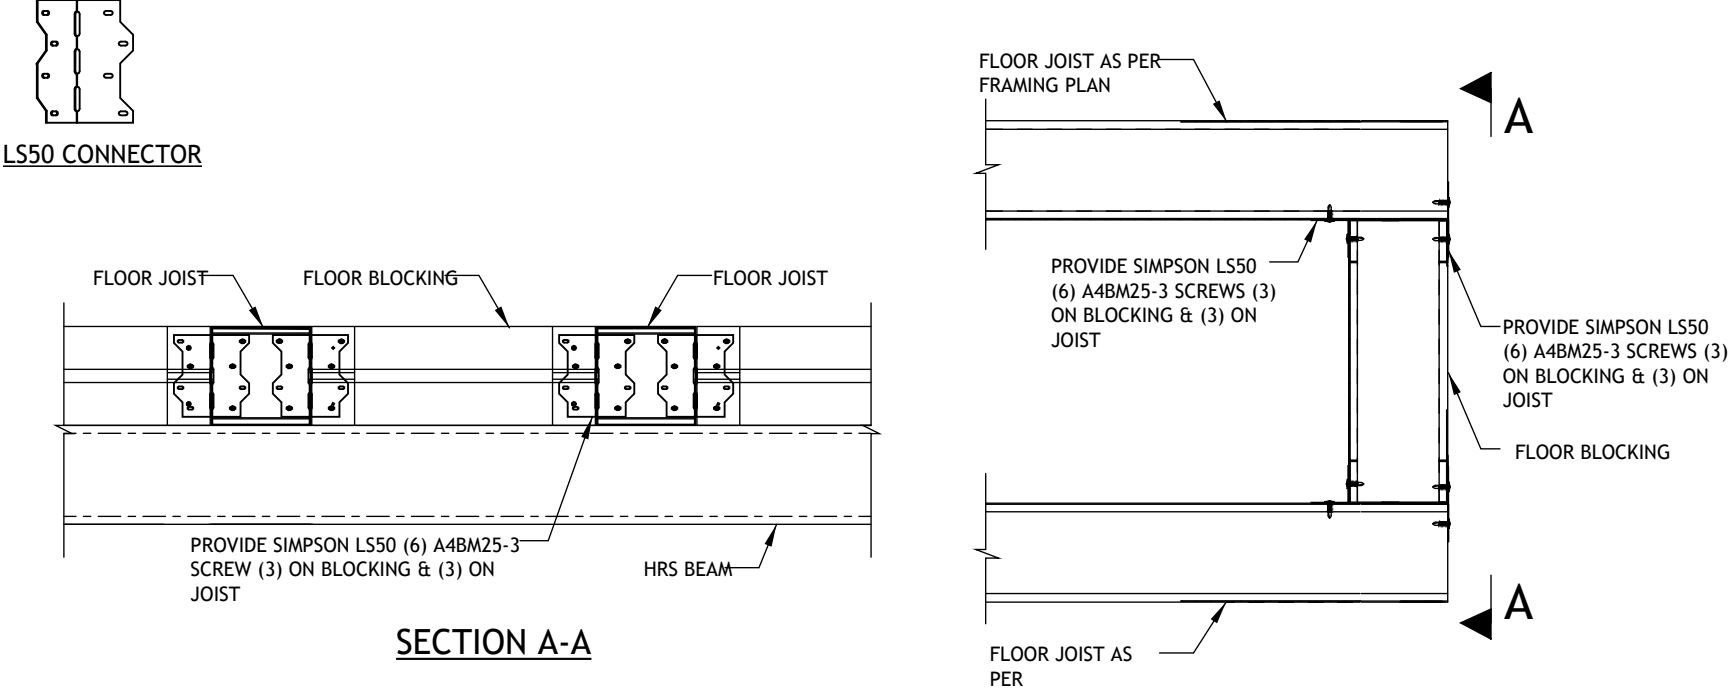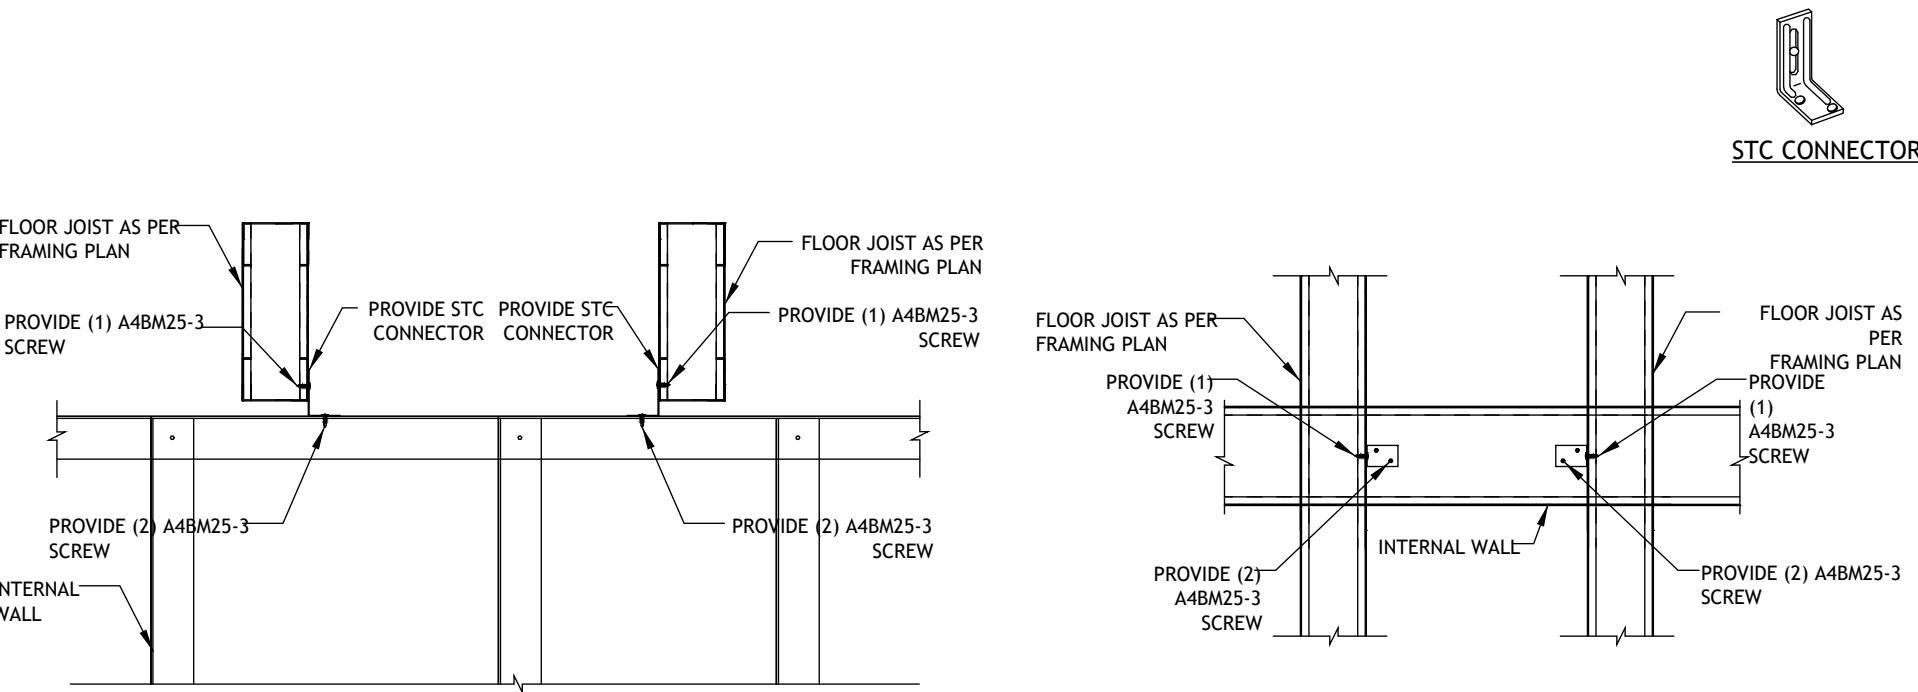

1. THESE DRAWINGS MUST BE CHECKED BY THE CUSTOMER OR CONTRACTOR PRIOR TO APPROVAL. ANY ERRORS OR OMISSIONS MUST BE REPORTED IN WRITING TO BAUHU PRIOR TO COMMENCEMENT OF CONSTRUCTION.
2. ARCHITECTURAL DRAWINGS SHOULD BE READ IN CONJUNCTION WITH STRUCTURAL DETAILING AND FABRICATION GENERAL ASSEMBLY DRAWINGS.
3. FOR CONSTRUCTION PURPOSES, USE ONLY THE LATEST APPROVED DRAWINGS LABELED 'ISSUED FOR CONSTRUCTION'.
4. DO NOT SCALE FROM THIS DRAWING.
5. THE COMPANY OPERATES USING METRIC DIMENSIONS AS THE PRINCIPAL DENOMINATION.
6. ALL CONCRETE WORKS ARE OUTSIDE OF THE SCOPE OF THE COMPANY. INFORMATION REGARDING SLAB DESIGN AND CONNECTIONS IN THESE DRAWINGS ARE INTENDED FOR GUIDANCE ONLY. FOUNDATION AND SLAB WORKS SHOULD BE DESIGNED AND APPROVED BY A LOCAL STRUCTURAL ENGINEER.
7. THE COMPANY RETAINS FULL TITLE AND OWNERSHIP OF THESE PLANS AND DESIGNS. ANY UNAUTHORISED USE, REPRODUCTION, OR DISTRIBUTION OF THESE PLANS, WHETHER IN WHOLE OR PART, IS EXPRESSLY PROHIBITED WITHOUT PRIOR WRITTEN CONSENT.
8. THE HYBRID STEEL FRAME CONSTRUCTION SYSTEM AND METHODOLOGY (PATENT PENDING) DESCRIBED IN THESE PLANS HAS BEEN DEVELOPED BY THE COMPANY AND IS SUBJECT TO A PROVISIONAL PATENT APPLICATION & ASSIGNMENT - US APPLICATION NO. 63/722,841



Typical Internal Wall Connection Floor Joist

Floor Blocking to Floor Joist Connection

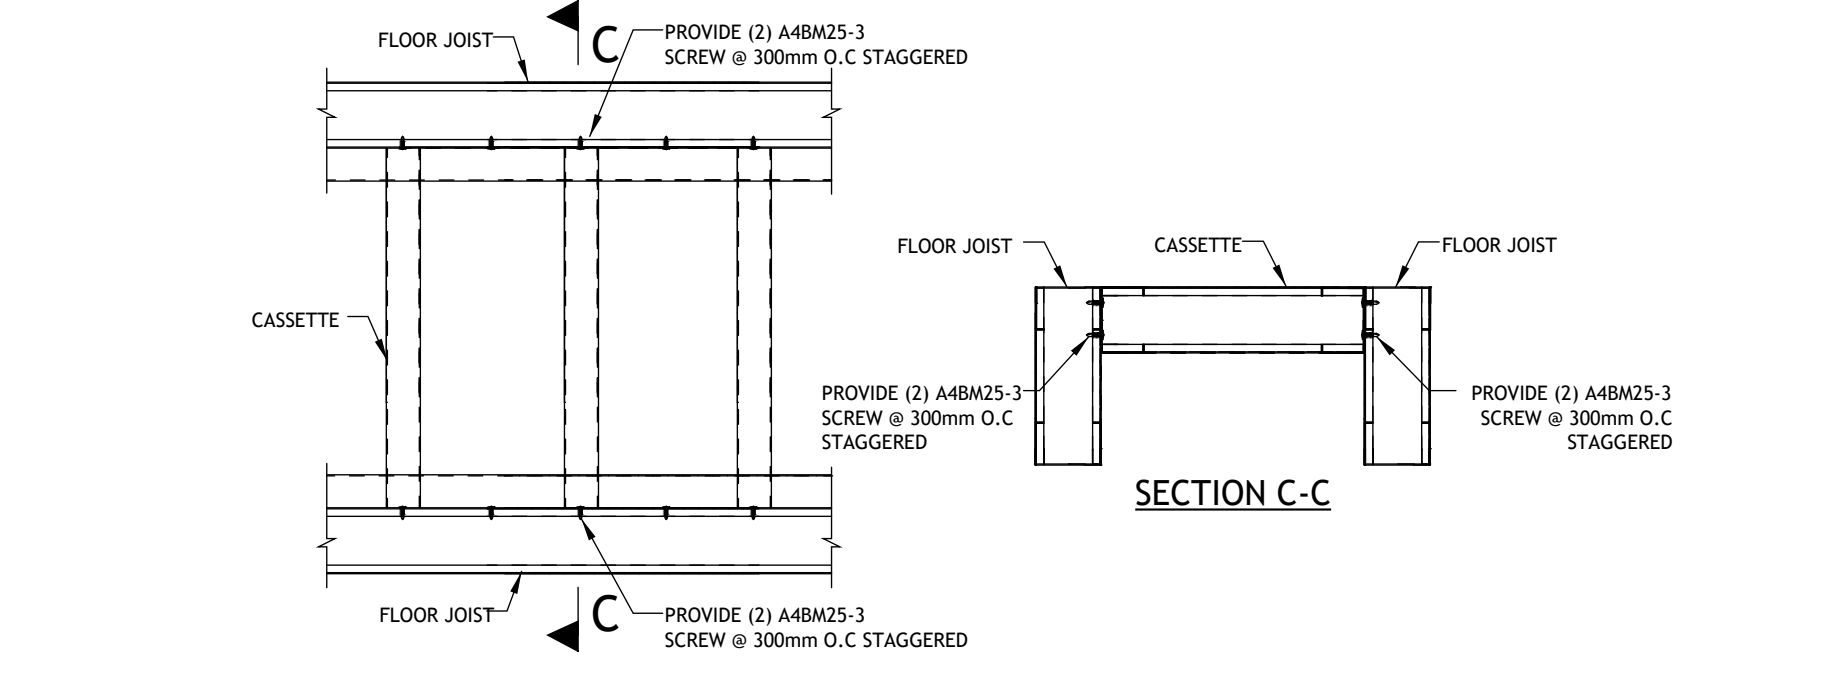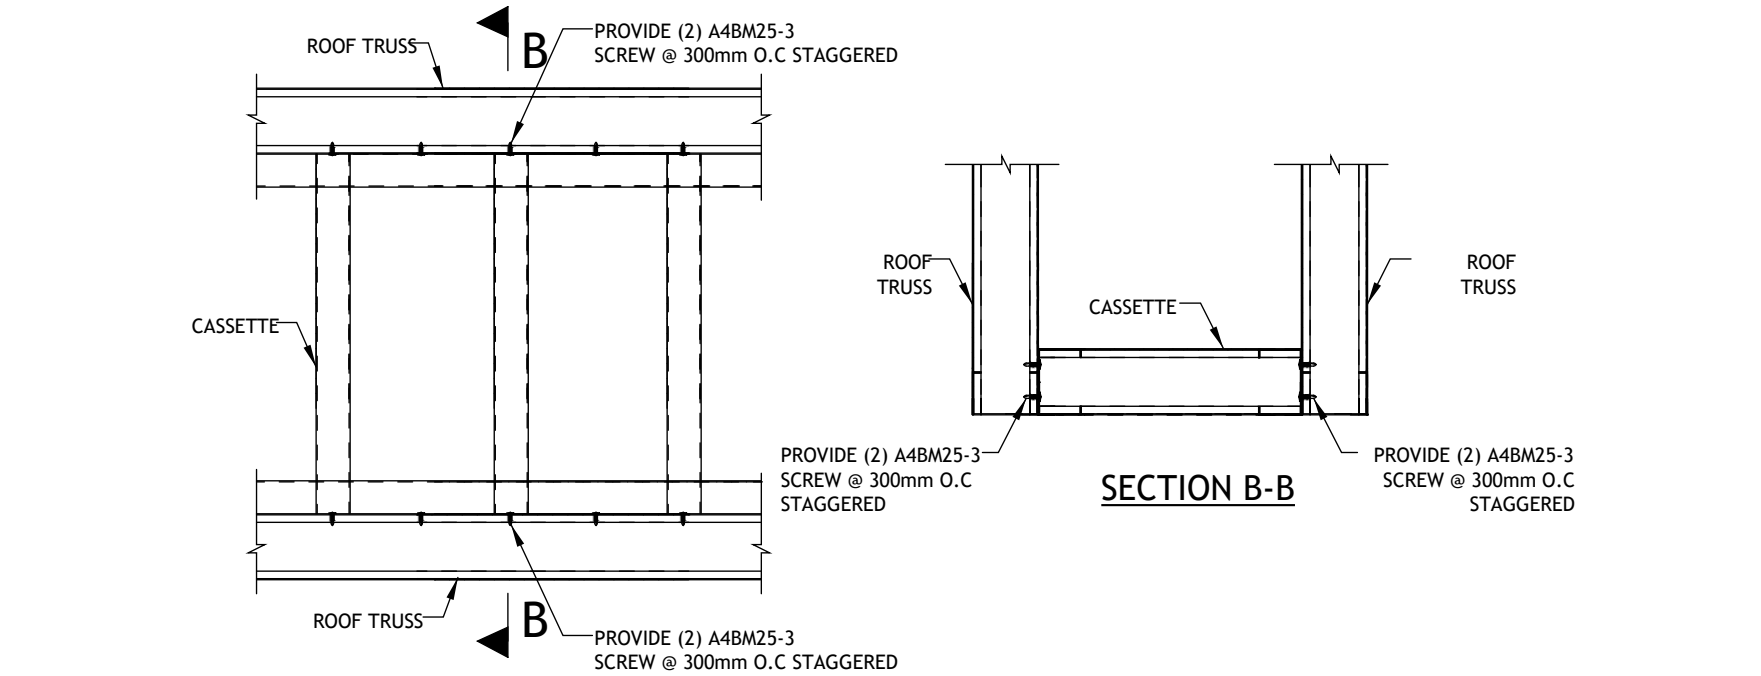

Cassette to Roof Truss Connection

Cassette to Floor Joist Connection

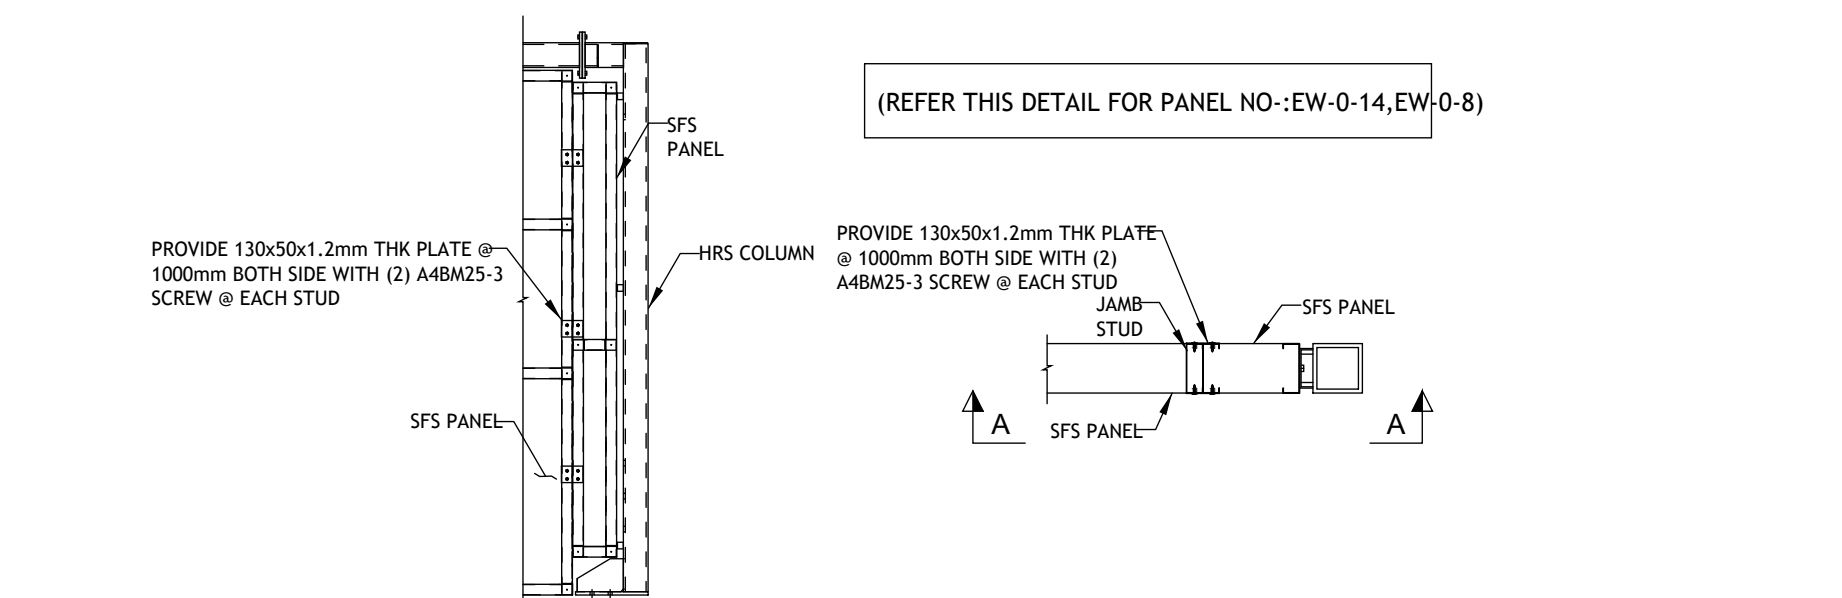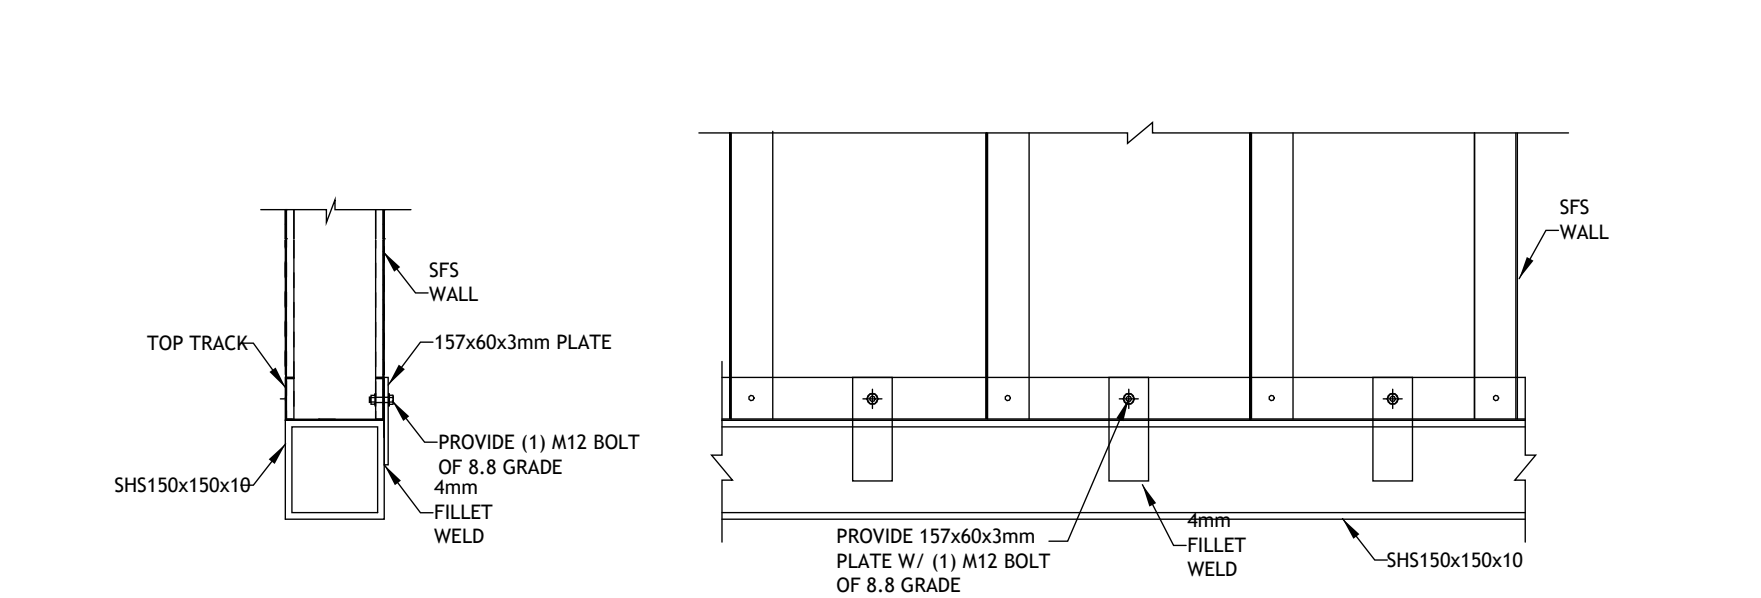

Typical Detail at SFS Bottom Track to HRS Beam Connection (External & Internal Wall)

SFS Panel Connection Detail

No.	Revision	Date

ISSUED FOR:

Issued for information

Issued for client approval

Issued for fabrication

Issued for construction

The Charlston

DRAWING TITLE:

Typical Frame Connections

DRAWN BY:

Y.A.Clark

SCALE:

DRAWING NO:



C110

DATE:



18/03/2026

Typical Frame Connections 3



NOTES:
ALL WELDS FOR CONNECTION OF ASSEMBLY TO BE NOTE FROM FABRICATION DRAWING

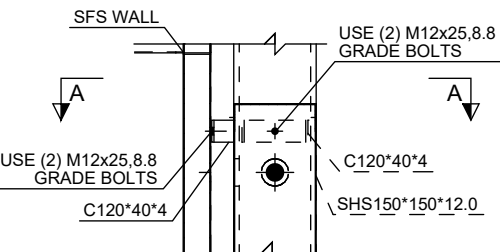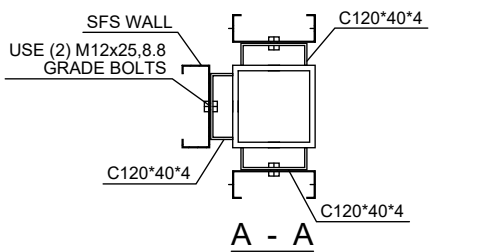



HRS Bracket Detail for Wall Connection

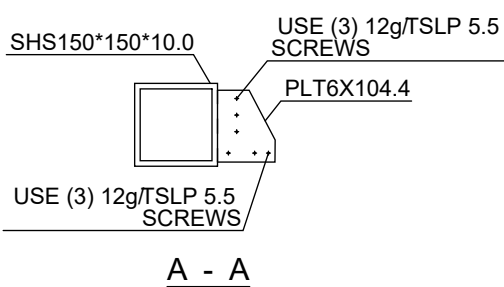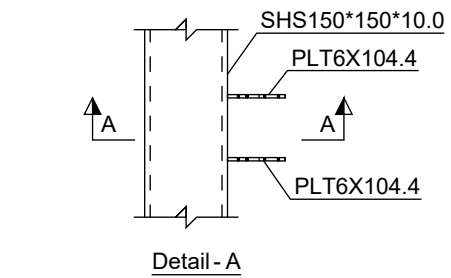


Typ. Truss Outside Plate Connection

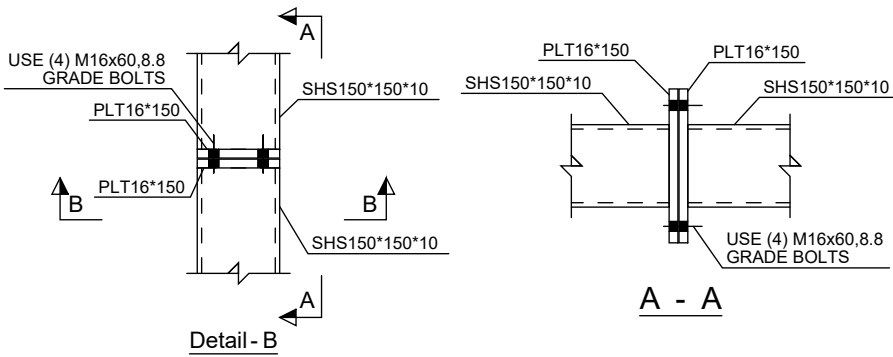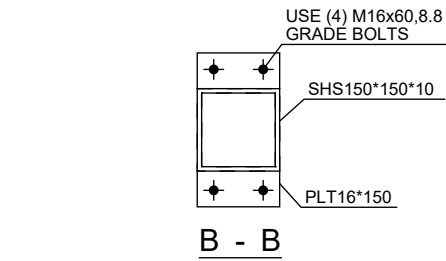


Typ. Vertical Splice Connection

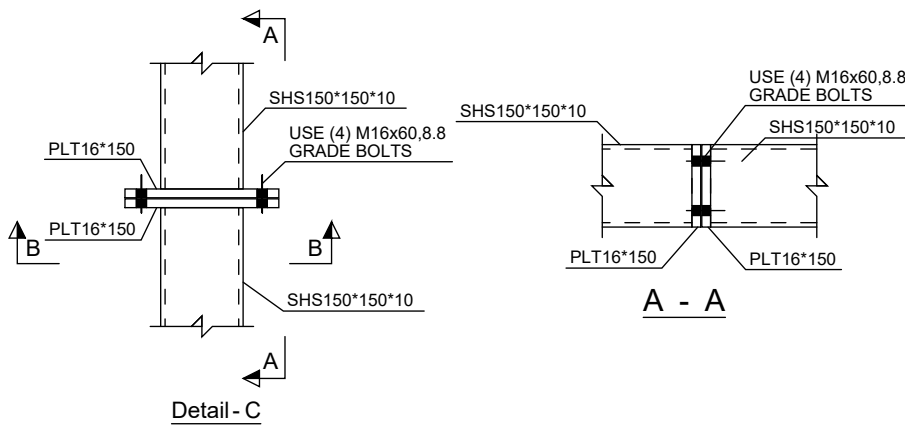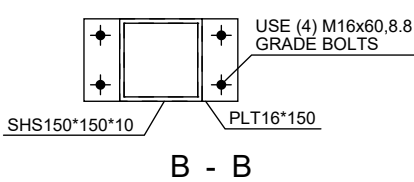


Typ. Horizontal Splice Connection

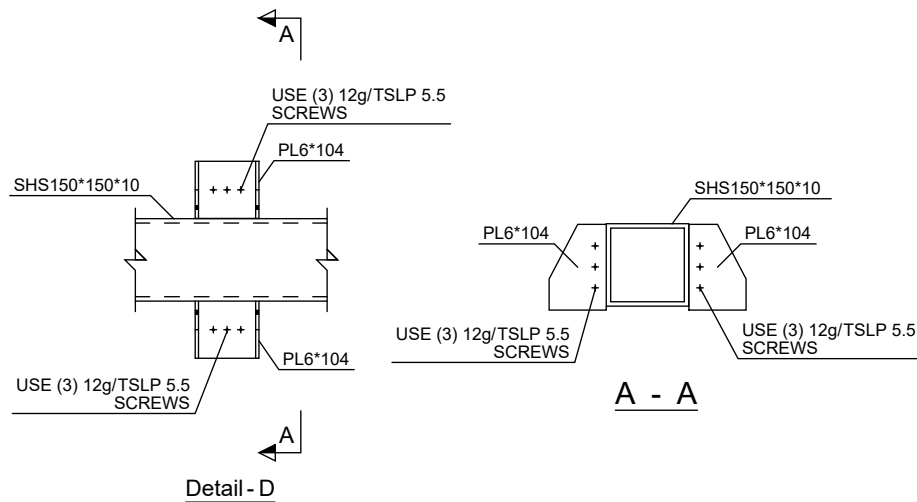


Typ. Truss Bracket Connection

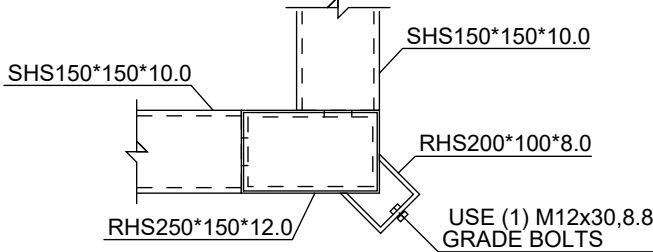


Typ. Corner Truss Connection

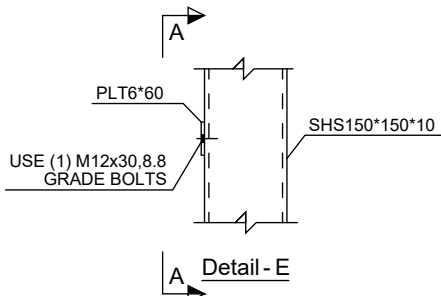


Typ. Wall to Beam Top Plate Connection

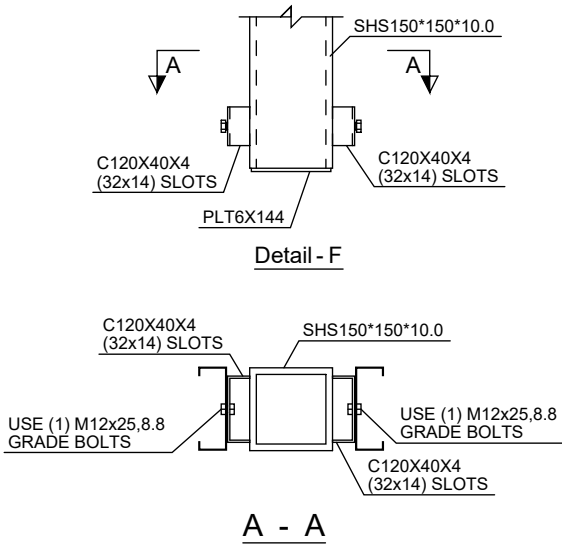


Typ. Lintel to Wind Post Connection

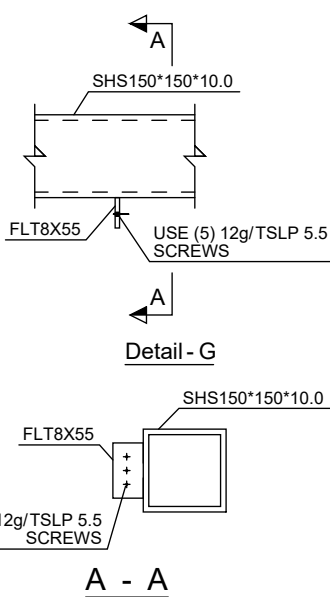


Cassette to Beam Connection

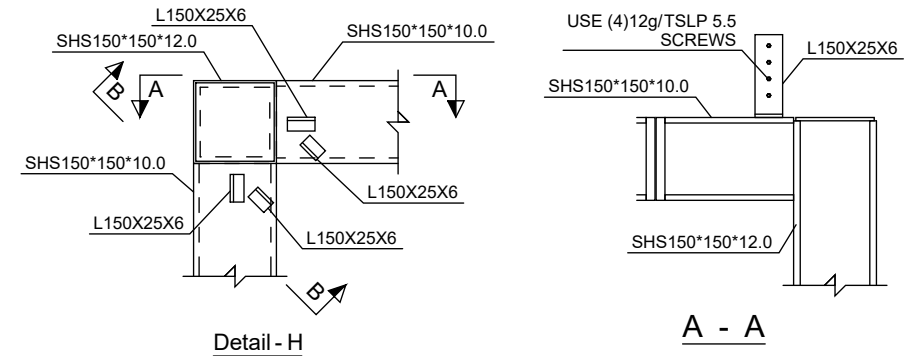

Typ. Beam to Column Connection Using C Bracket

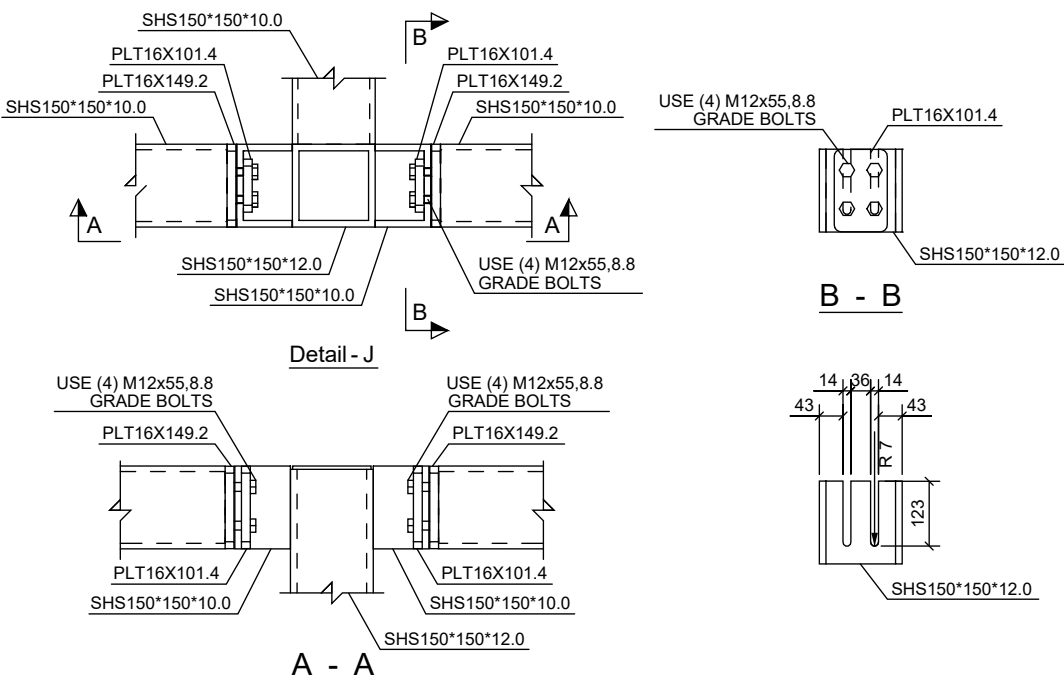

Typ. Beam to Column Connection Using C Bracket

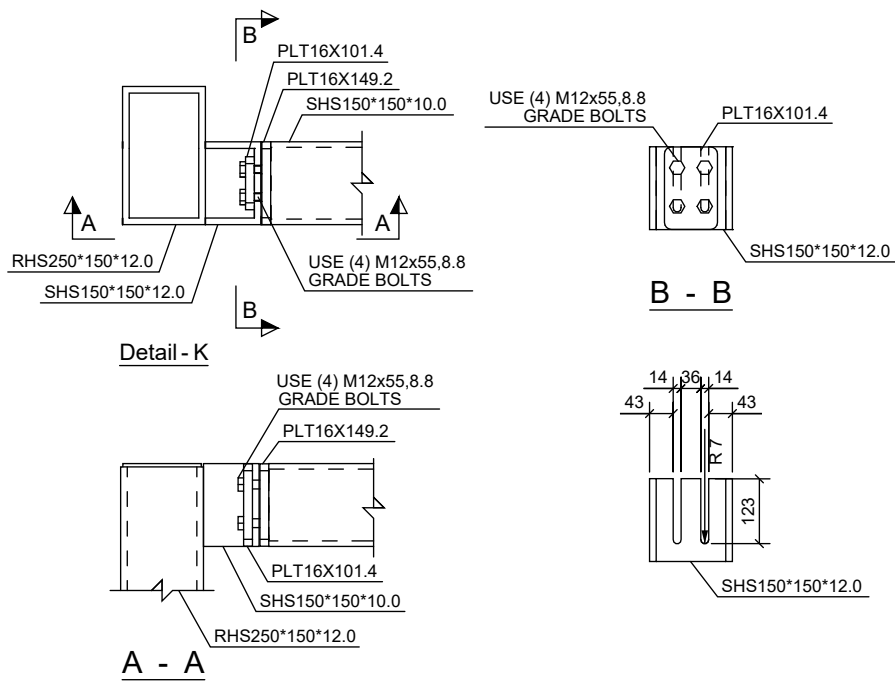

Typ. Beam to Column Connection Using C Bracket

1. THESE DRAWINGS MUST BE CHECKED BY THE CUSTOMER OR CONTRACTOR PRIOR TO APPROVAL. ANY ERRORS OR OMISSIONS MUST BE REPORTED IN WRITING TO BAUHU PRIOR TO COMMENCEMENT OF CONSTRUCTION.
2. ARCHITECTURAL DRAWINGS SHOULD BE READ IN CONJUNCTION WITH STRUCTURAL DETAILING AND FABRICATION GENERAL ASSEMBLY DRAWINGS.
3. FOR CONSTRUCTION PURPOSES, USE ONLY THE LATEST APPROVED DRAWINGS LABELED 'ISSUED FOR CONSTRUCTION'.
4. DO NOT SCALE FROM THIS DRAWING.
5. THE COMPANY OPERATES USING METRIC DIMENSIONS AS THE PRINCIPAL DENOMINATION.
6. ALL CONCRETE WORKS ARE OUTSIDE OF THE SCOPE OF THE COMPANY. INFORMATION REGARDING SLAB DESIGN AND CONNECTIONS IN THESE DRAWINGS ARE INTENDED FOR GUIDANCE ONLY. FOUNDATION AND SLAB WORKS SHOULD BE DESIGNED AND APPROVED BY A LOCAL STRUCTURAL ENGINEER.
7. THE COMPANY RETAINS FULL TITLE AND OWNERSHIP OF THESE PLANS AND DESIGNS. ANY UNAUTHORISED USE, REPRODUCTION, OR DISTRIBUTION OF THESE PLANS, WHETHER IN WHOLE OR PART, IS EXPRESSLY PROHIBITED WITHOUT PRIOR WRITTEN CONSENT.
8. THE HYBRID STEEL FRAME CONSTRUCTION SYSTEM AND METHODOLOGY (PATENT PENDING) DESCRIBED IN THESE PLANS HAS BEEN DEVELOPED BY THE COMPANY AND IS SUBJECT TO A PROVISIONAL PATENT APPLICATION & ASSIGNMENT - US APPLICATION NO. 63/722,841

No.	Revision	Date

ISSUED FOR:

Issued for information

Issued for client approval

Issued for fabrication

Issued for construction

The Charlston

DRAWING TITLE:

Typical Frame Connections

DRAWN BY:

Y.A.Clark

SCALE:

DRAWING NO:


C111

DATE:

18/03/2026


Typical Frame Connections 4

Hold Down Detail

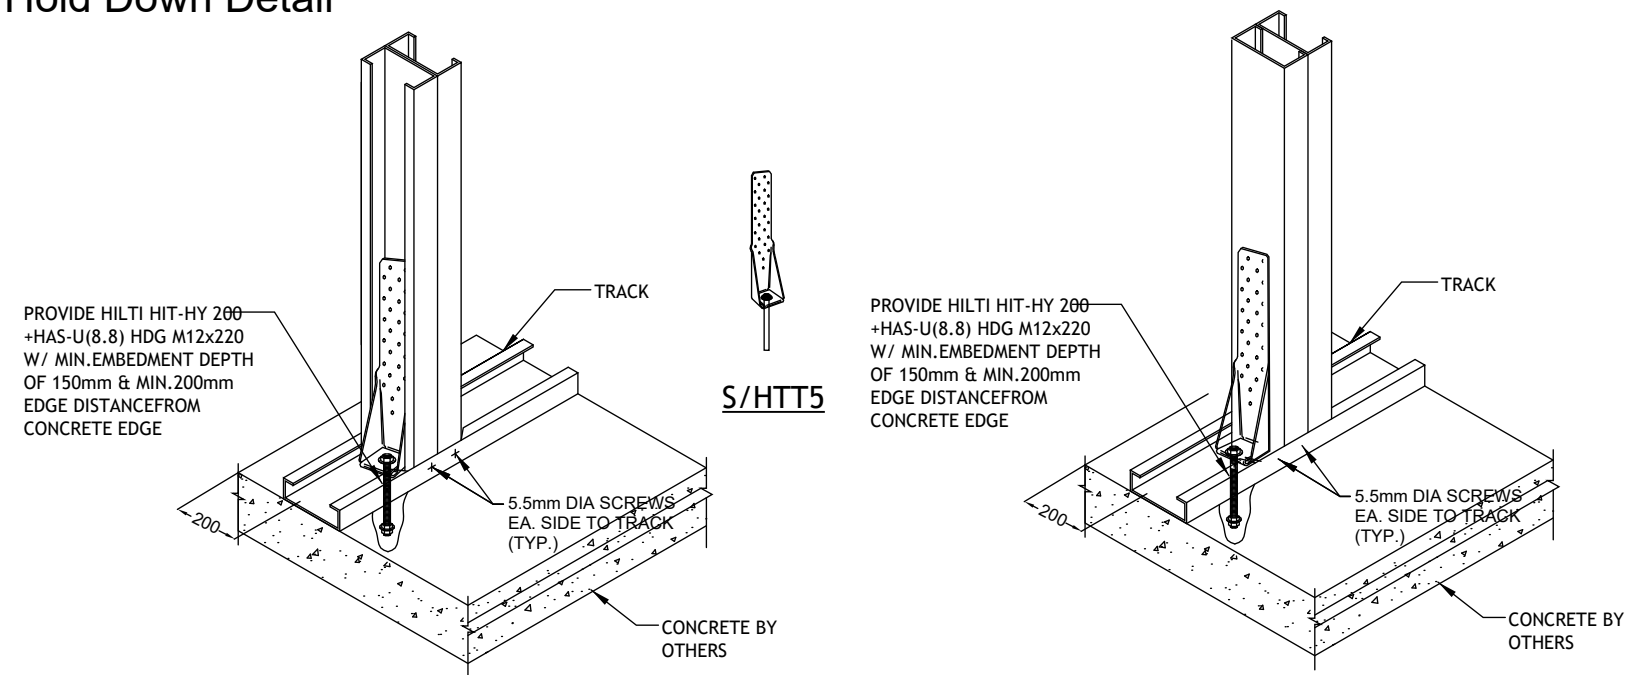

- NOTE -
- 1. ANCHOR & SCREWS SPECIFICATION AS PER SPECIFIED ON STRUCTURAL PLAN
 - 2. FIXING SPECIFICATION SUBJECT TO CHANGE AS PER DESIGN.


Casette to Floor/Roof Joist Connection

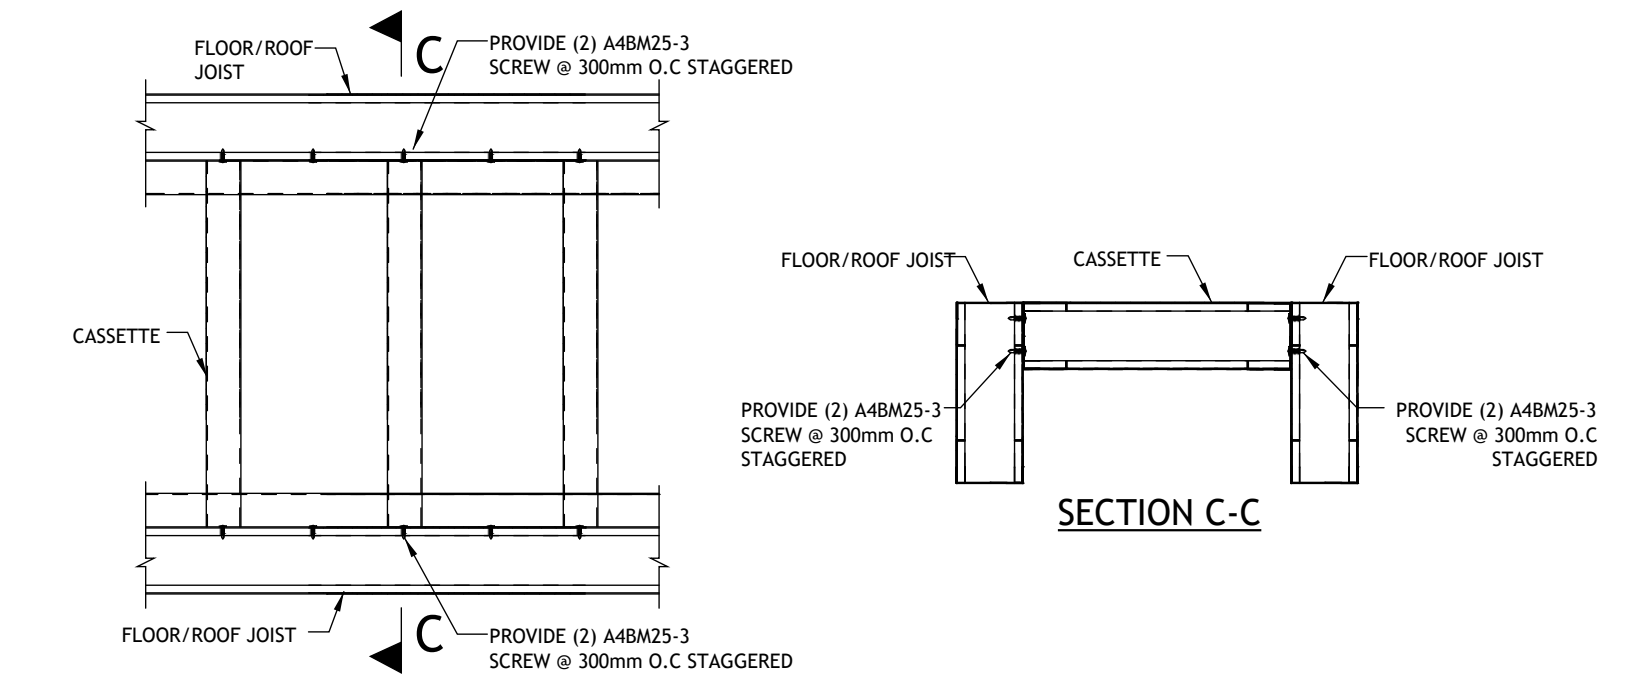

- NOTE -FIXING SPECIFICATION SUBJECT TO CHANGE AS PER DESIGN.





Typ. Internal Wall Connection Floor/Roof Joist

(Perpendicular Condition)



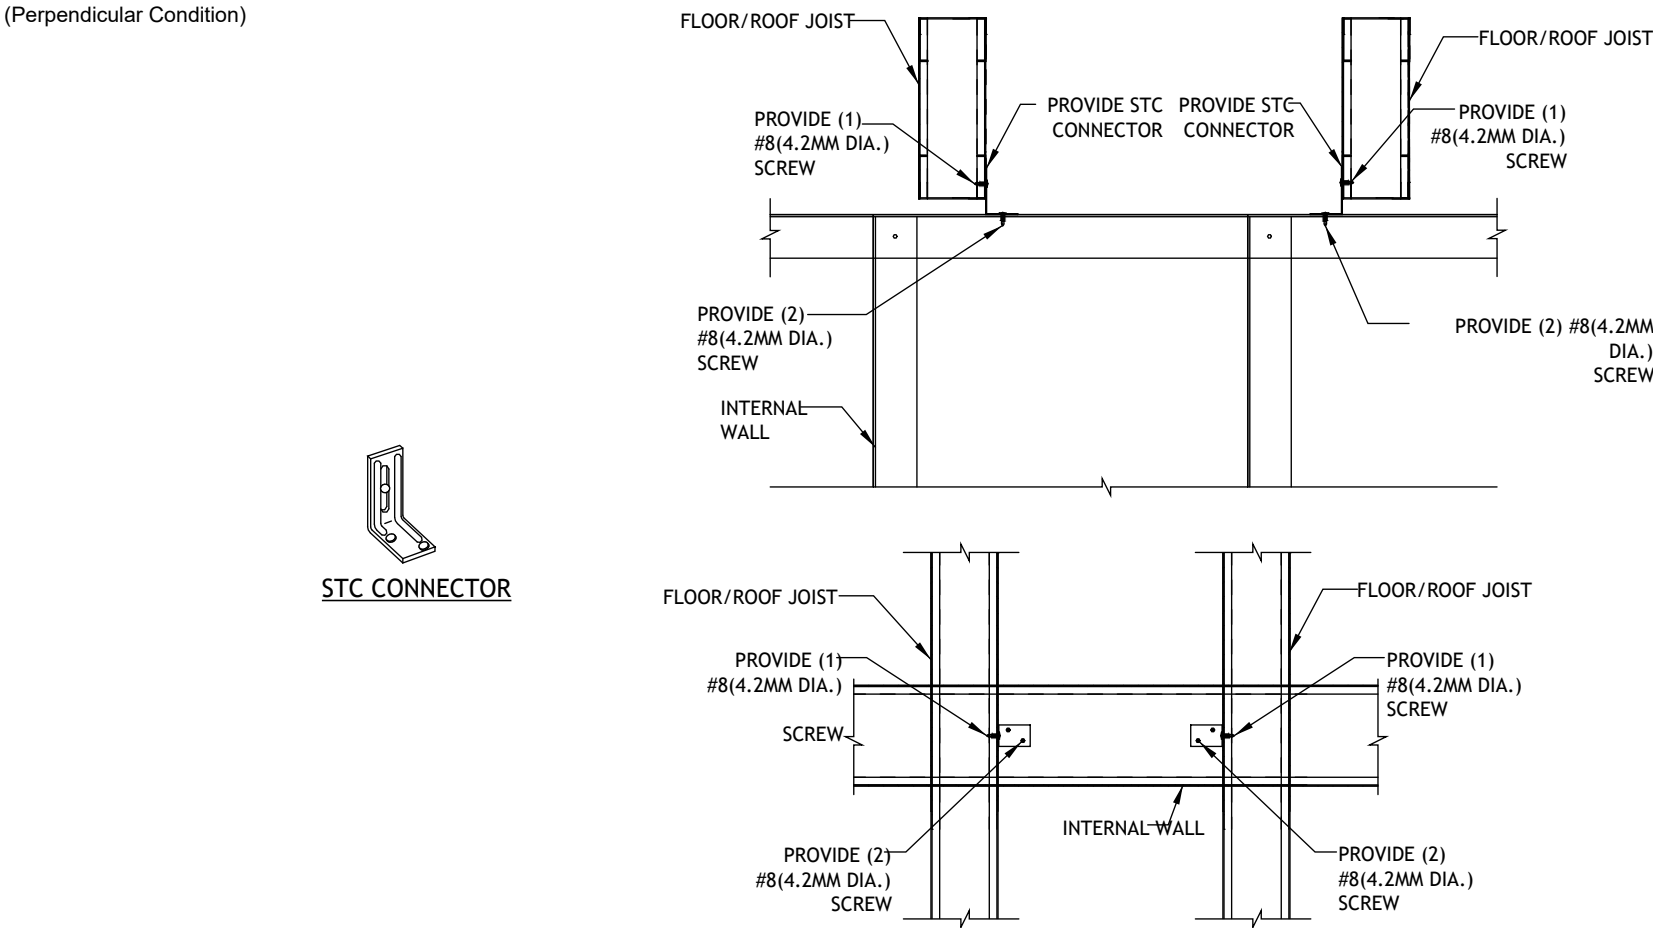


- NOTE -FIXING SPECIFICATION SUBJECT TO CHANGE AS PER DESIGN.

Typ. Brace Wall Panel Connection with Treaded Rod

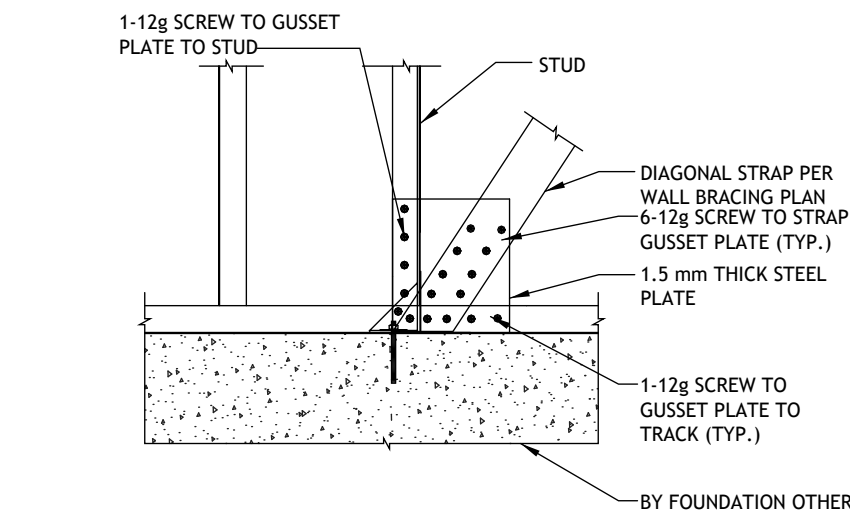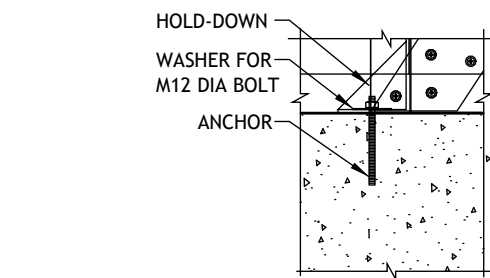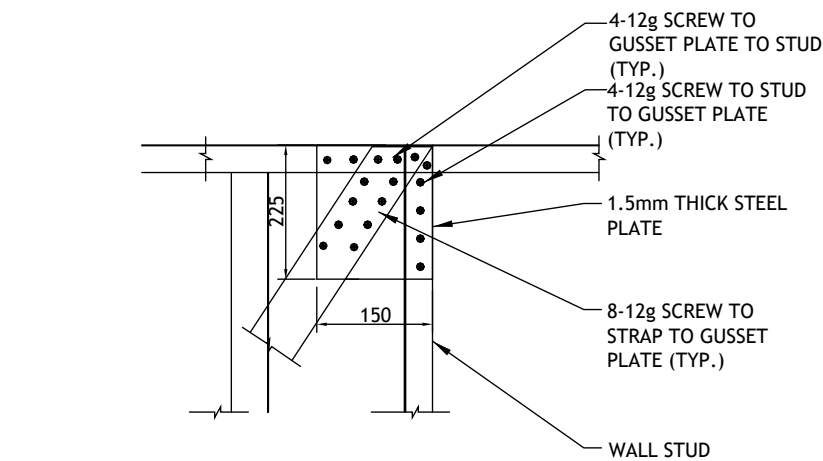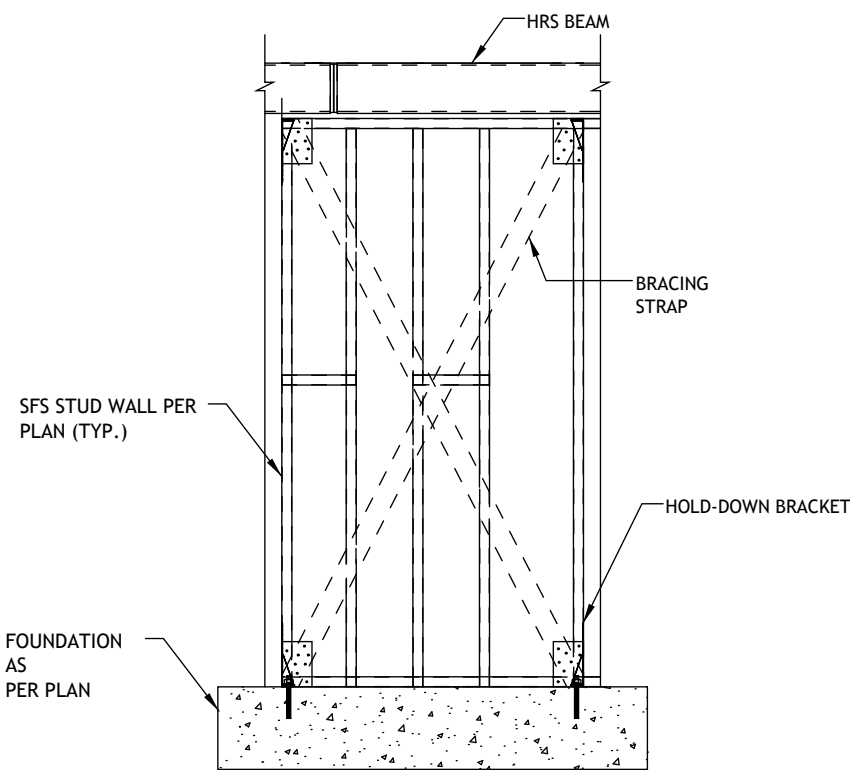

- NOTE -
- 1. ANCHOR & SCREWS SPECIFICATION AS PER SPECIFIED ON STRUCTURAL PLAN
 - 2. FIXING SPECIFICATION SUBJECT TO CHANGE AS PER DESIGN.

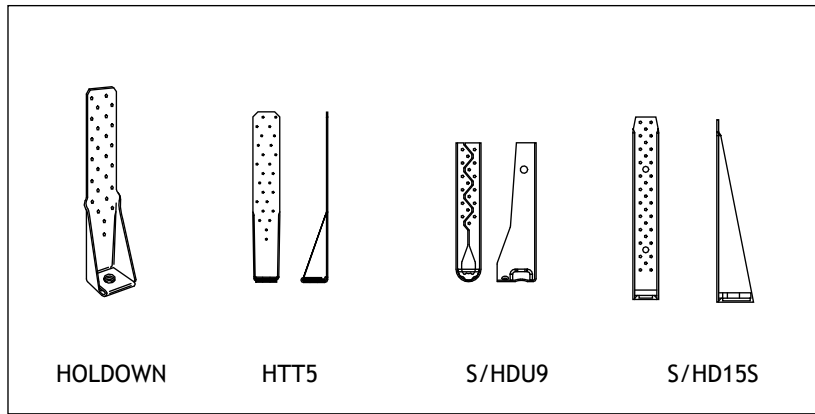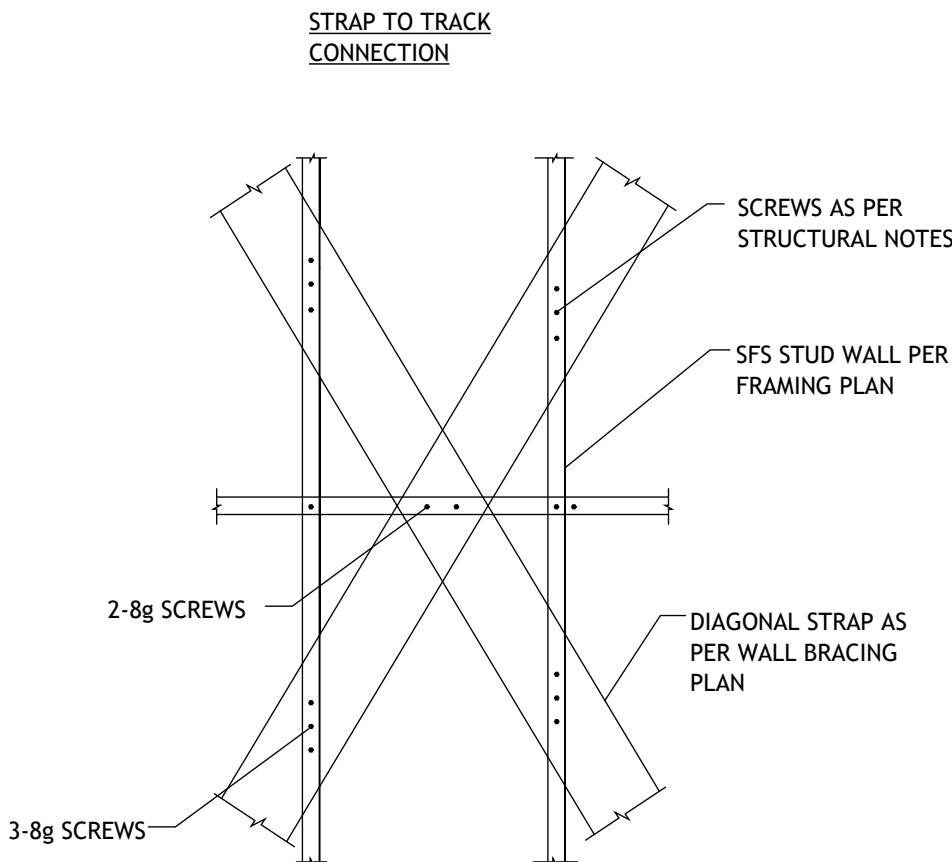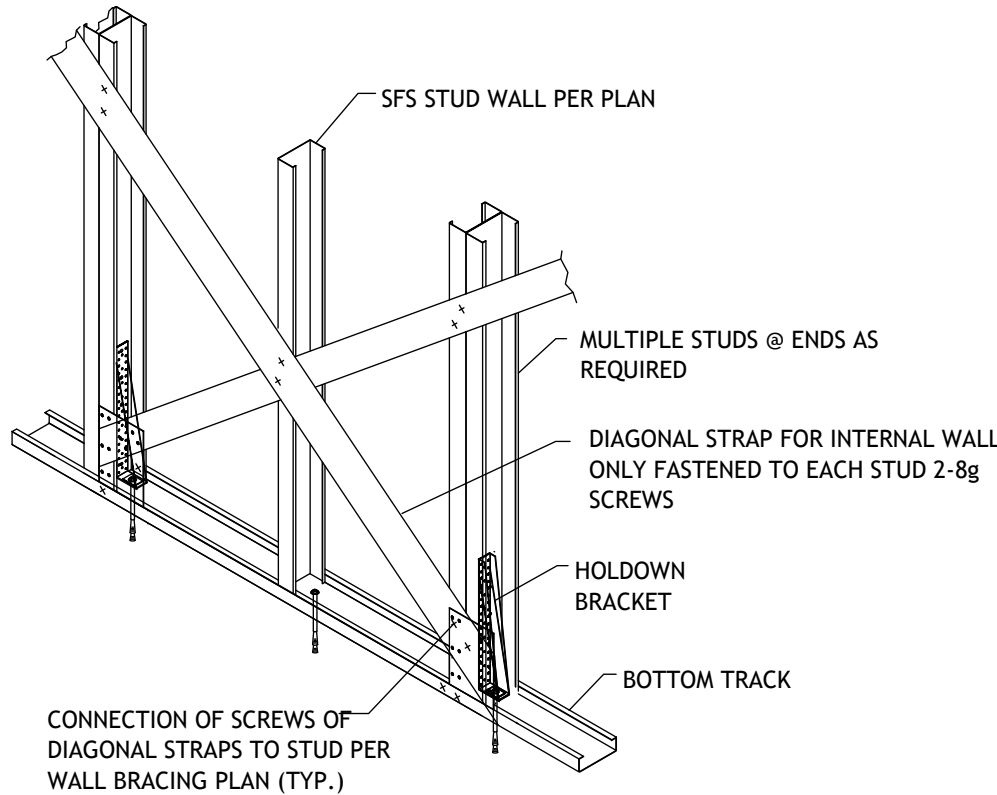

- 1. THESE DRAWINGS MUST BE CHECKED BY THE CUSTOMER OR CONTRACTOR PRIOR TO APPROVAL. ANY ERRORS OR OMISSIONS MUST BE REPORTED IN WRITING TO BAUHU PRIOR TO COMMENCEMENT OF CONSTRUCTION.
- 2. ARCHITECTURAL DRAWINGS SHOULD BE READ IN CONJUNCTION WITH STRUCTURAL DETAILING AND FABRICATION GENERAL ASSEMBLY DRAWINGS.
- 3. FOR CONSTRUCTION PURPOSES, USE ONLY THE LATEST APPROVED DRAWINGS LABELED 'ISSUED FOR CONSTRUCTION'.
- 4. DO NOT SCALE FROM THIS DRAWING.
- 5. THE COMPANY OPERATES USING METRIC DIMENSIONS AS THE PRINCIPAL DENOMINATION.
- 6. ALL CONCRETE WORKS ARE OUTSIDE OF THE SCOPE OF THE COMPANY. INFORMATION REGARDING SLAB DESIGN AND CONNECTIONS IN THESE DRAWINGS ARE INTENDED FOR GUIDANCE ONLY. FOUNDATION AND SLAB WORKS SHOULD BE DESIGNED AND APPROVED BY A LOCAL STRUCTURAL ENGINEER.
- 7. THE COMPANY RETAINS FULL TITLE AND OWNERSHIP OF THESE PLANS AND DESIGNS. ANY UNAUTHORISED USE, REPRODUCTION, OR DISTRIBUTION OF THESE PLANS, WHETHER IN WHOLE OR PART, IS EXPRESSLY PROHIBITED WITHOUT PRIOR WRITTEN CONSENT.
- 8. THE HYBRID STEEL FRAME CONSTRUCTION SYSTEM AND METHODOLOGY (PATENT PENDING) DESCRIBED IN THESE PLANS HAS BEEN DEVELOPED BY THE COMPANY AND IS SUBJECT TO A PROVISIONAL PATENT APPLICATION & ASSIGNMENT - US APPLICATION NO. 63/722,841

No.	Revision	Date

ISSUED FOR:

Issued for information

Issued for client approval

Issued for fabrication

Issued for construction

The Charlston

DRAWING TITLE:

Typical Frame Connections

DRAWN BY:

Y.A.Clark

SCALE:

DRAWING NO:

C112

DATE:

18/03/2026