

1. THESE DRAWINGS MUST BE CHECKED BY THE CUSTOMER OR CONTRACTOR PRIOR TO APPROVAL. ANY ERRORS OR OMISSIONS MUST BE REPORTED IN WRITING TO BAUHU PRIOR TO COMMENCEMENT OF CONSTRUCTION.
2. ARCHITECTURAL DRAWINGS SHOULD BE READ IN CONJUNCTION WITH STRUCTURAL DETAILING AND FABRICATION GENERAL ASSEMBLY DRAWINGS.
3. FOR CONSTRUCTION PURPOSES, USE ONLY THE LATEST APPROVED DRAWINGS LABELED 'ISSUED FOR CONSTRUCTION'.
4. DO NOT SCALE FROM THIS DRAWING.
5. THE COMPANY OPERATES USING METRIC DIMENSIONS AS THE PRINCIPAL DENOMINATION.
6. ALL CONCRETE WORKS ARE OUTSIDE OF THE SCOPE OF THE COMPANY. INFORMATION REGARDING SLAB DESIGN AND CONNECTIONS IN THESE DRAWINGS ARE INTENDED FOR GUIDENCE ONLY. FOUNDATION AND SLAB WORKS SHOULD BE DESIGNED AND APPROVED BY A LOCAL STRUCTURAL ENGINEER.
7. THE COMPANY RETAINS FULL TITLE AND OWNERSHIP OF THESE PLANS AND DESIGNS. ANY UNAUTHORISED USE, REPRODUCTION, OR DISTRIBUTION OF THESE PLANS, WHETHER IN WHOLE OR PART, IS EXPRESSLY PROHIBITED WITHOUT PRIOR WRITTEN CONSENT.

| No. | Revision | Date |
|-----|----------|------|
|     |          |      |
|     |          |      |
ISSUED FOR:

☐ Issued for information


☒ Issued for client approval

☐ Issued for fabrication

☐ Issued for construction

Firefly

|                |                       |
|----------------|-----------------------|
| DRAWING TITLE: | Title Sheet           |
| DRAWN BY:      | Mladin Monica-Mihaela |
| SCALE:         |                       |
| DRAWING NO:    | A01                   |
| DATE:          | 04.03.2024            |

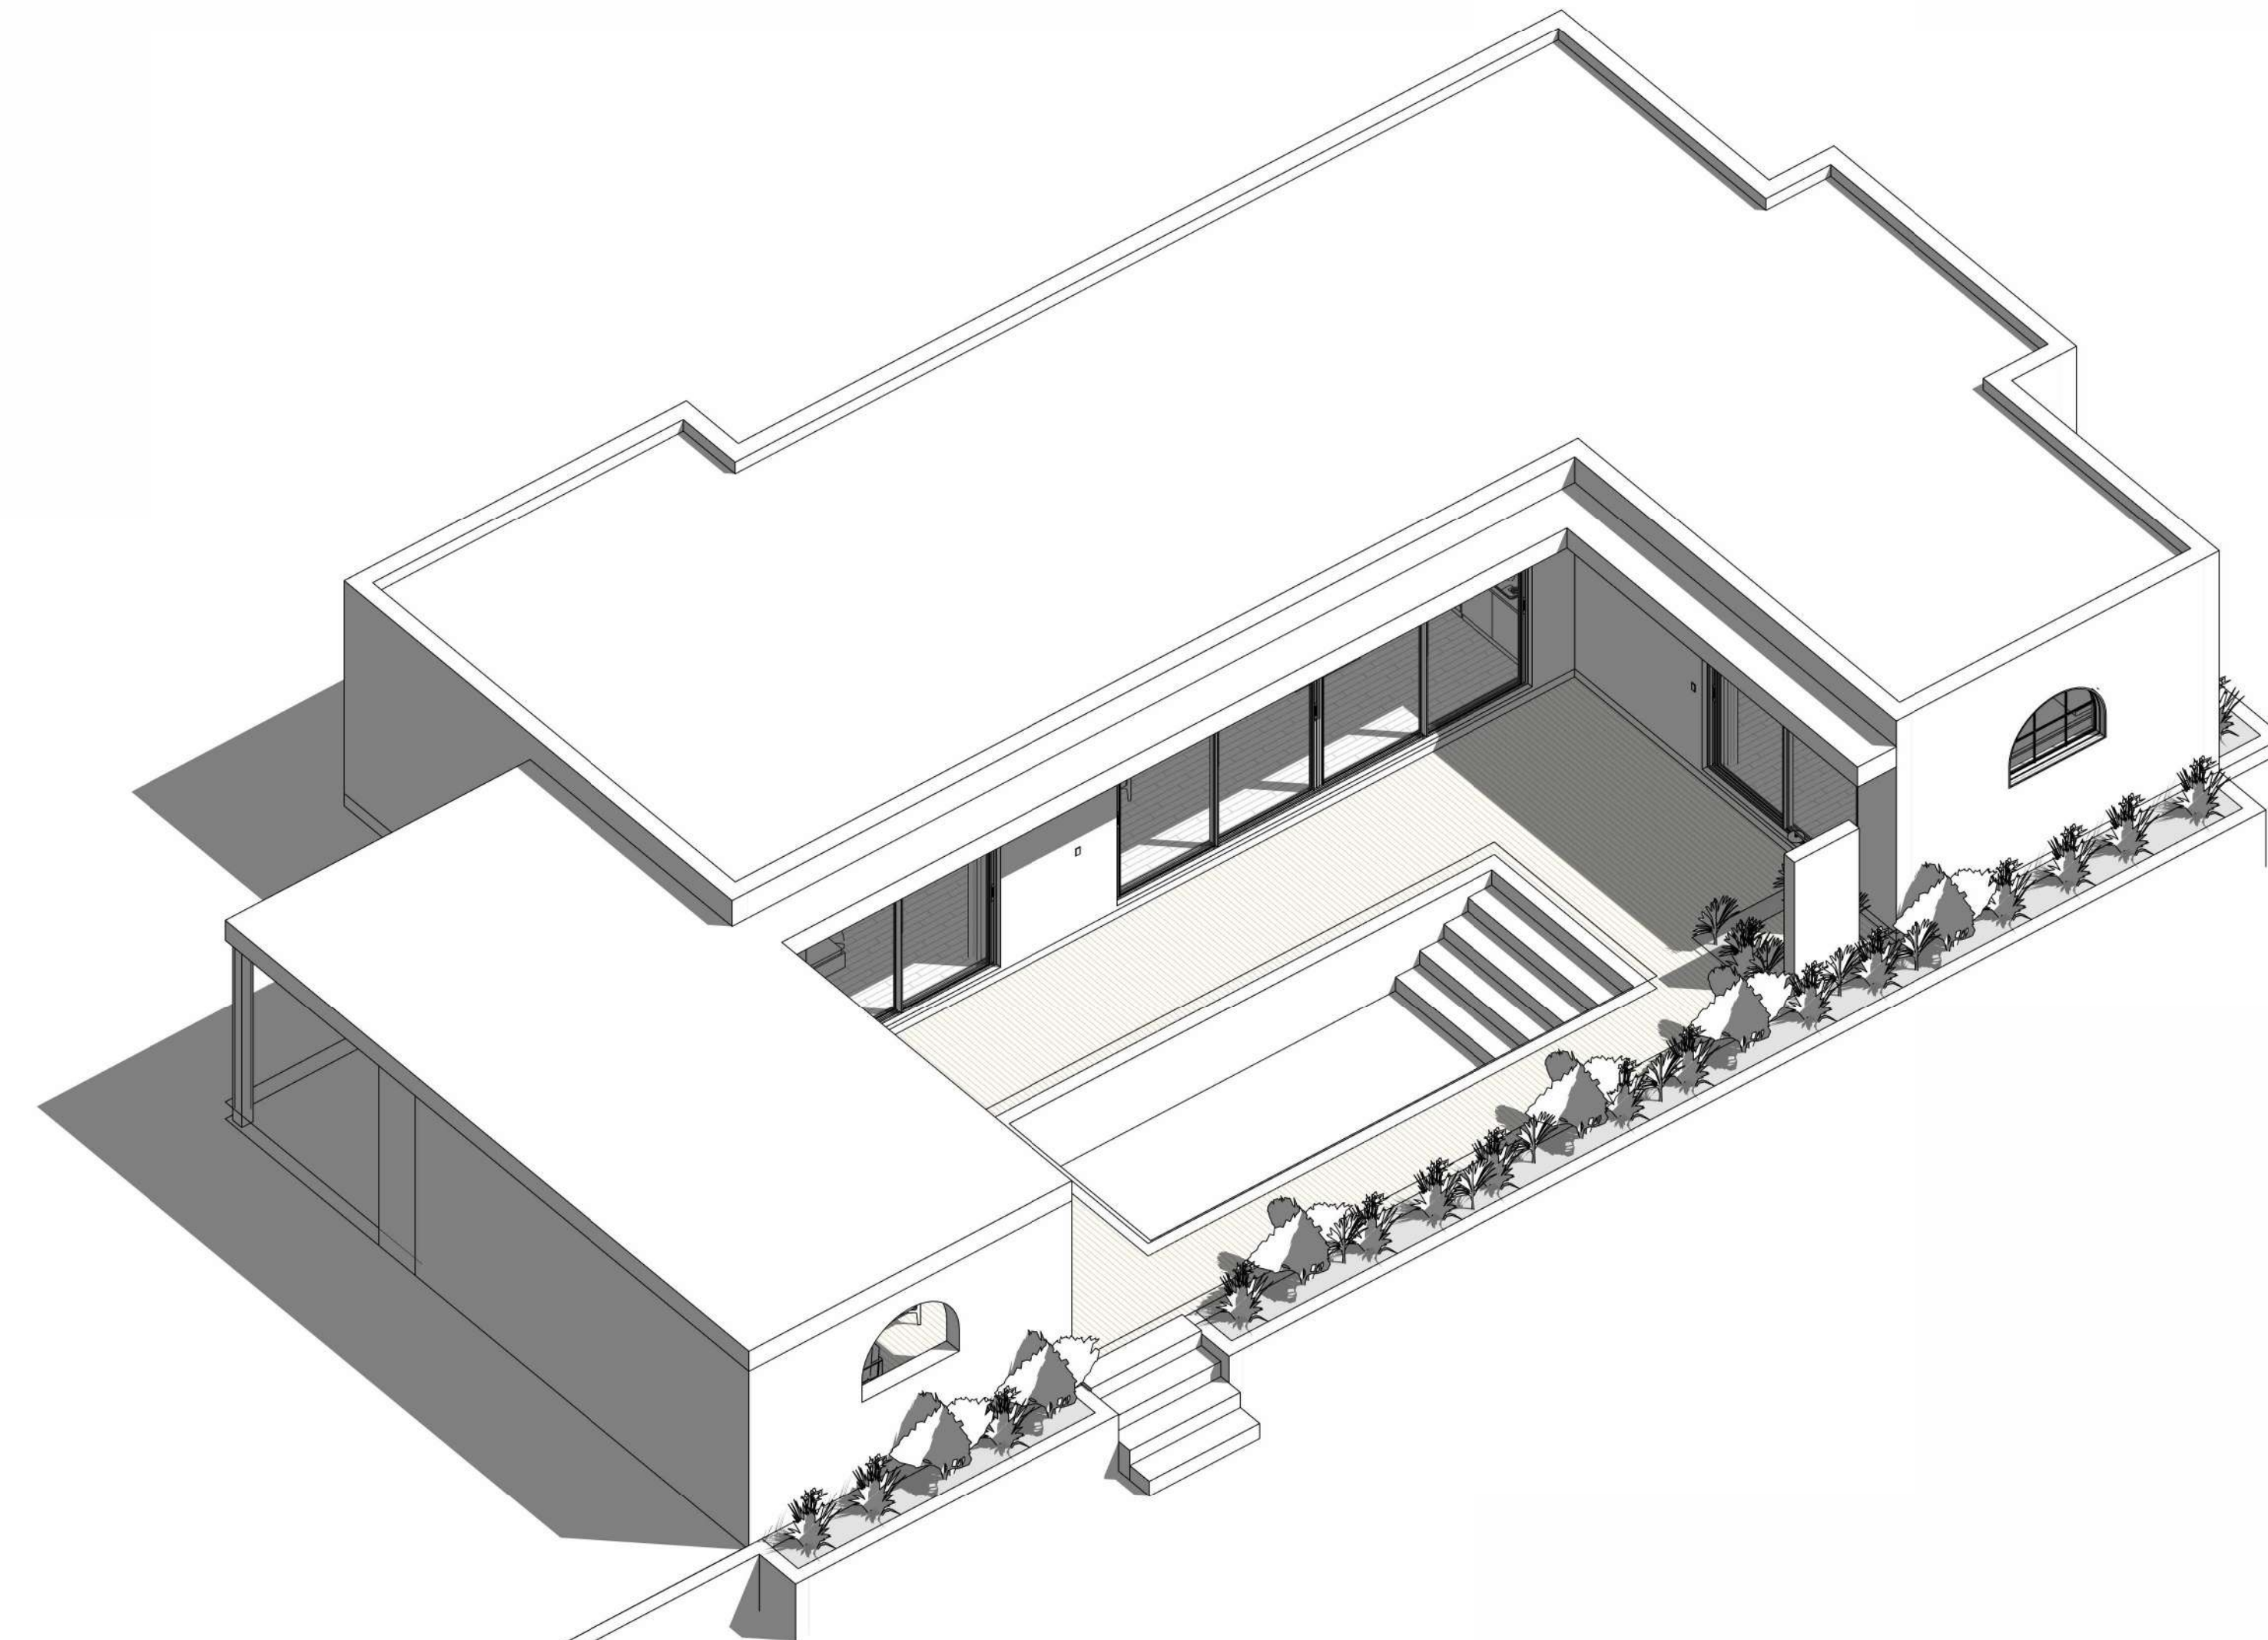

1. THESE DRAWINGS MUST BE CHECKED BY THE CUSTOMER OR CONTRACTOR PRIOR TO APPROVAL. ANY ERRORS OR OMISSIONS MUST BE REPORTED IN WRITING TO BAUHU PRIOR TO COMMENCEMENT OF CONSTRUCTION.
2. ARCHITECTURAL DRAWINGS SHOULD BE READ IN CONJUNCTION WITH STRUCTURAL DETAILING AND FABRICATION GENERAL ASSEMBLY DRAWINGS.
3. FOR CONSTRUCTION PURPOSES, USE ONLY THE LATEST APPROVED DRAWINGS LABELED 'ISSUED FOR CONSTRUCTION'.
4. DO NOT SCALE FROM THIS DRAWING.
5. THE COMPANY OPERATES USING METRIC DIMENSIONS AS THE PRINCIPAL DENOMINATION.
6. ALL CONCRETE WORKS ARE OUTSIDE OF THE SCOPE OF THE COMPANY. INFORMATION REGARDING SLAB DESIGN AND CONNECTIONS IN THESE DRAWINGS ARE INTENDED FOR GUIDENCE ONLY. FOUNDATION AND SLAB WORKS SHOULD BE DESIGNED AND APPROVED BY A LOCAL STRUCTURAL ENGINEER.
7. THE COMPANY RETAINS FULL TITLE AND OWNERSHIP OF THESE PLANS AND DESIGNS. ANY UNAUTHORISED USE, REPRODUCTION, OR DISTRIBUTION OF THESE PLANS, WHETHER IN WHOLE OR PART, IS EXPRESSLY PROHIBITED WITHOUT PRIOR WRITTEN CONSENT.

| No. | Revision | Date |
|-----|----------|------|
|     |          |      |
|     |          |      |
ISSUED FOR:

Issued for information

Issued for client approval

Issued for fabrication

Issued for construction

Firefly

DRAWING TITLE:

Building Axonometry

DRAWN BY:

Mladin Monica-Mihaela

SCALE:

DRAWING NO:

A02

DATE:

04.03.2024

1

Axonometric View

1. THESE DRAWINGS MUST BE CHECKED BY THE CUSTOMER OR CONTRACTOR PRIOR TO APPROVAL. ANY ERRORS OR OMISSIONS MUST BE REPORTED IN WRITING TO BAUHU PRIOR TO COMMENCEMENT OF CONSTRUCTION.
2. ARCHITECTURAL DRAWINGS SHOULD BE READ IN CONJUNCTION WITH STRUCTURAL DETAILING AND FABRICATION GENERAL ASSEMBLY DRAWINGS.
3. FOR CONSTRUCTION PURPOSES, USE ONLY THE LATEST APPROVED DRAWINGS LABELED 'ISSUED FOR CONSTRUCTION'.
4. DO NOT SCALE FROM THIS DRAWING.
5. THE COMPANY OPERATES USING METRIC DIMENSIONS AS THE PRINCIPAL DENOMINATION.
6. ALL CONCRETE WORKS ARE OUTSIDE OF THE SCOPE OF THE COMPANY. INFORMATION REGARDING SLAB DESIGN AND CONNECTIONS IN THESE DRAWINGS ARE INTENDED FOR GUIDANCE ONLY. FOUNDATION AND SLAB WORKS SHOULD BE DESIGNED AND APPROVED BY A LOCAL STRUCTURAL ENGINEER.
7. THE COMPANY RETAINS FULL TITLE AND OWNERSHIP OF THESE PLANS AND DESIGNS. ANY UNAUTHORISED USE, REPRODUCTION, OR DISTRIBUTION OF THESE PLANS, WHETHER IN WHOLE OR PART, IS EXPRESSLY PROHIBITED WITHOUT PRIOR WRITTEN CONSENT.

| No. | Revision | Date |
|-----|----------|------|
|     |          |      |
|     |          |      |
ISSUED FOR:

- Issued for information
- Issued for client approval
- Issued for fabrication
- Issued for construction

Firefly

DRAWING TITLE:

Ground Floor Axonometry

DRAWN BY:

Mladin Monica-Mihaela


SCALE:

DRAWING NO:

A03

DATE:

04.03.2024

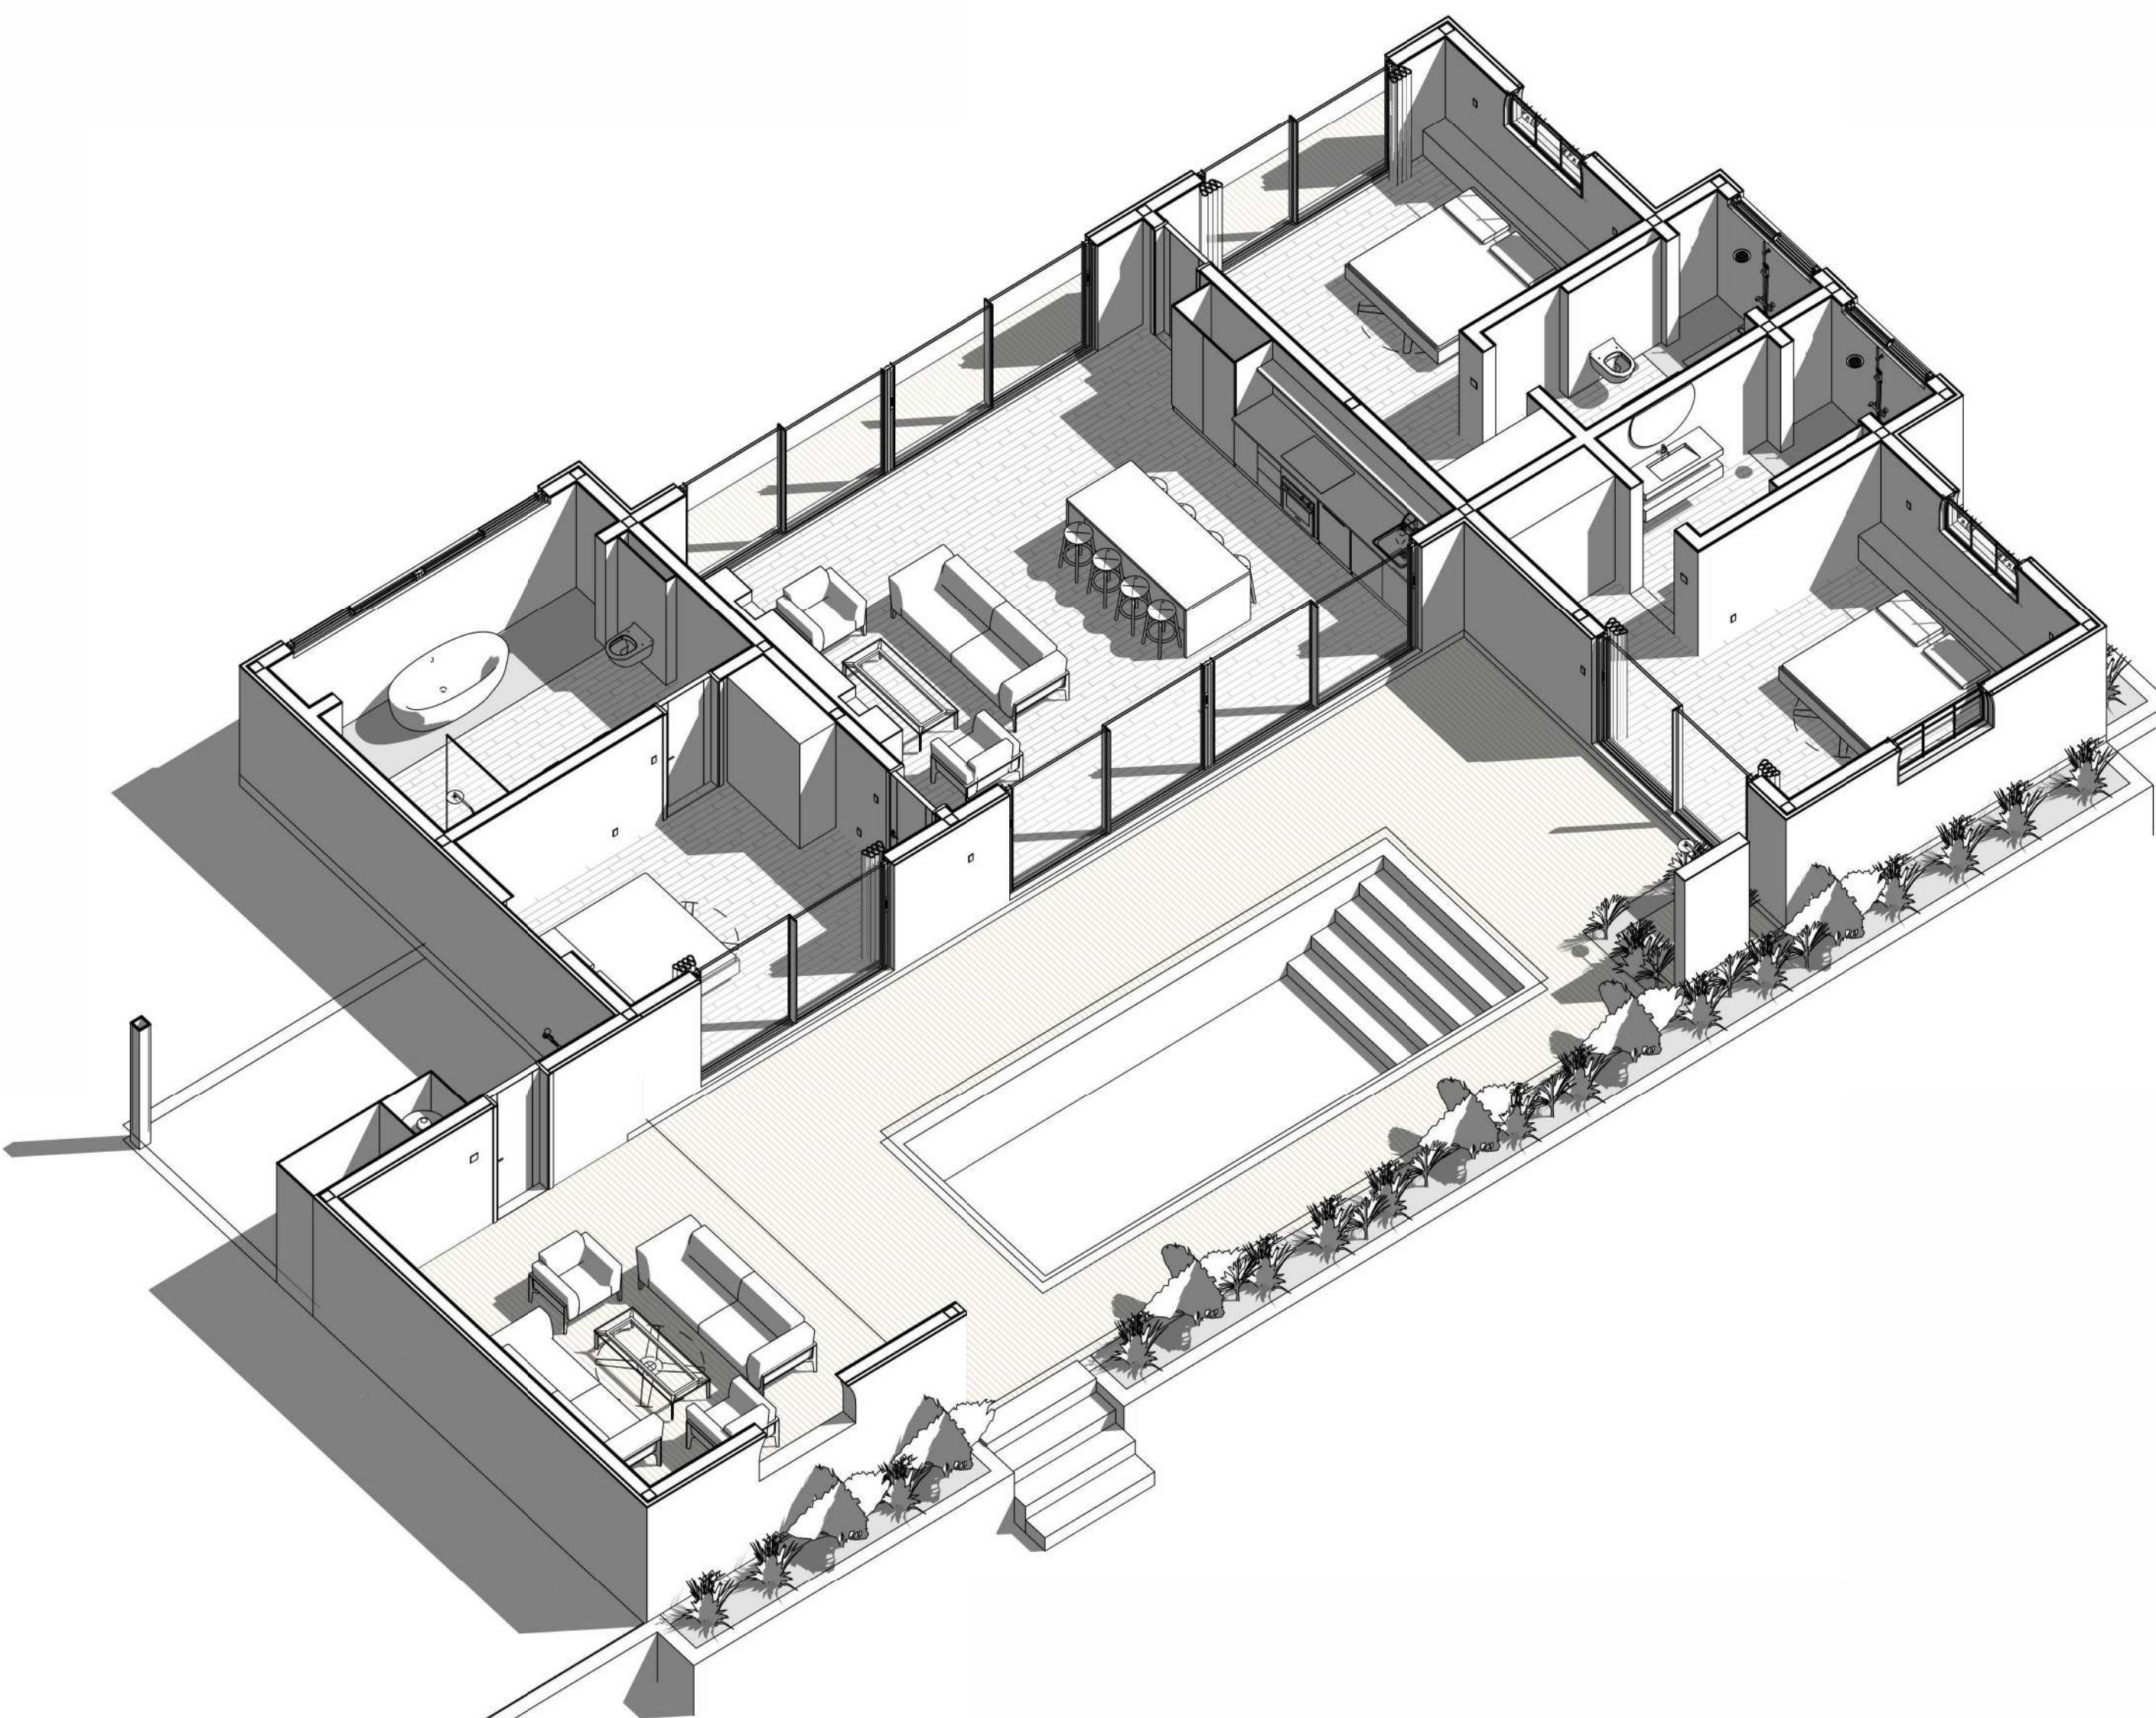

1 Axonometric Ground Floor View

1. THESE DRAWINGS MUST BE CHECKED BY THE CUSTOMER OR CONTRACTOR PRIOR TO APPROVAL. ANY ERRORS OR OMISSIONS MUST BE REPORTED IN WRITING TO BAUHU PRIOR TO COMMENCEMENT OF CONSTRUCTION.
2. ARCHITECTURAL DRAWINGS SHOULD BE READ IN CONJUNCTION WITH STRUCTURAL DETAILING AND FABRICATION GENERAL ASSEMBLY DRAWINGS.
3. FOR CONSTRUCTION PURPOSES, USE ONLY THE LATEST APPROVED DRAWINGS LABELED 'ISSUED FOR CONSTRUCTION'.
4. DO NOT SCALE FROM THIS DRAWING.
5. THE COMPANY OPERATES USING METRIC DIMENSIONS AS THE PRINCIPAL DENOMINATION.
6. ALL CONCRETE WORKS ARE OUTSIDE OF THE SCOPE OF THE COMPANY. INFORMATION REGARDING SLAB DESIGN AND CONNECTIONS IN THESE DRAWINGS ARE INTENDED FOR GUIDENCE ONLY. FOUNDATION AND SLAB WORKS SHOULD BE DESIGNED AND APPROVED BY A LOCAL STRUCTURAL ENGINEER.
7. THE COMPANY RETAINS FULL TITLE AND OWNERSHIP OF THESE PLANS AND DESIGNS. ANY UNAUTHORISED USE, REPRODUCTION, OR DISTRIBUTION OF THESE PLANS, WHETHER IN WHOLE OR PART, IS EXPRESSLY PROHIBITED WITHOUT PRIOR WRITTEN CONSENT.

| No. | Revision | Date |
|-----|----------|------|
|     |          |      |
|     |          |      |
ISSUED FOR:

Issued for information

Issued for client approval

Issued for fabrication

Issued for construction

Firefly

DRAWING TITLE:

Site Plan

DRAWN BY:

Mladin Monica-Mihaela

SCALE:

1 : 70

DRAWING NO:

A05

DATE:

04.03.2024


REAR ELEVATION

LEFT ELEVATION

RIGHT ELEVATION

FRONT ELEVATION

Building Footprint: 157.542 Sqm , 1695.766 Sq feet  
Outdoor Covered Terrace: 28.25 Sqm, 304.080 Sq feet  
Pool Terrace Area: 54.02 Sqm, 581.466 Sq feet  
Carport: 15.46 Sqm, 166.410 Sq feet  
Pool Area: 24.60 Sqm, 264.792 Sq feet  
Total construction footprint: 279.872 Sqm, 3012.514 Sq feet

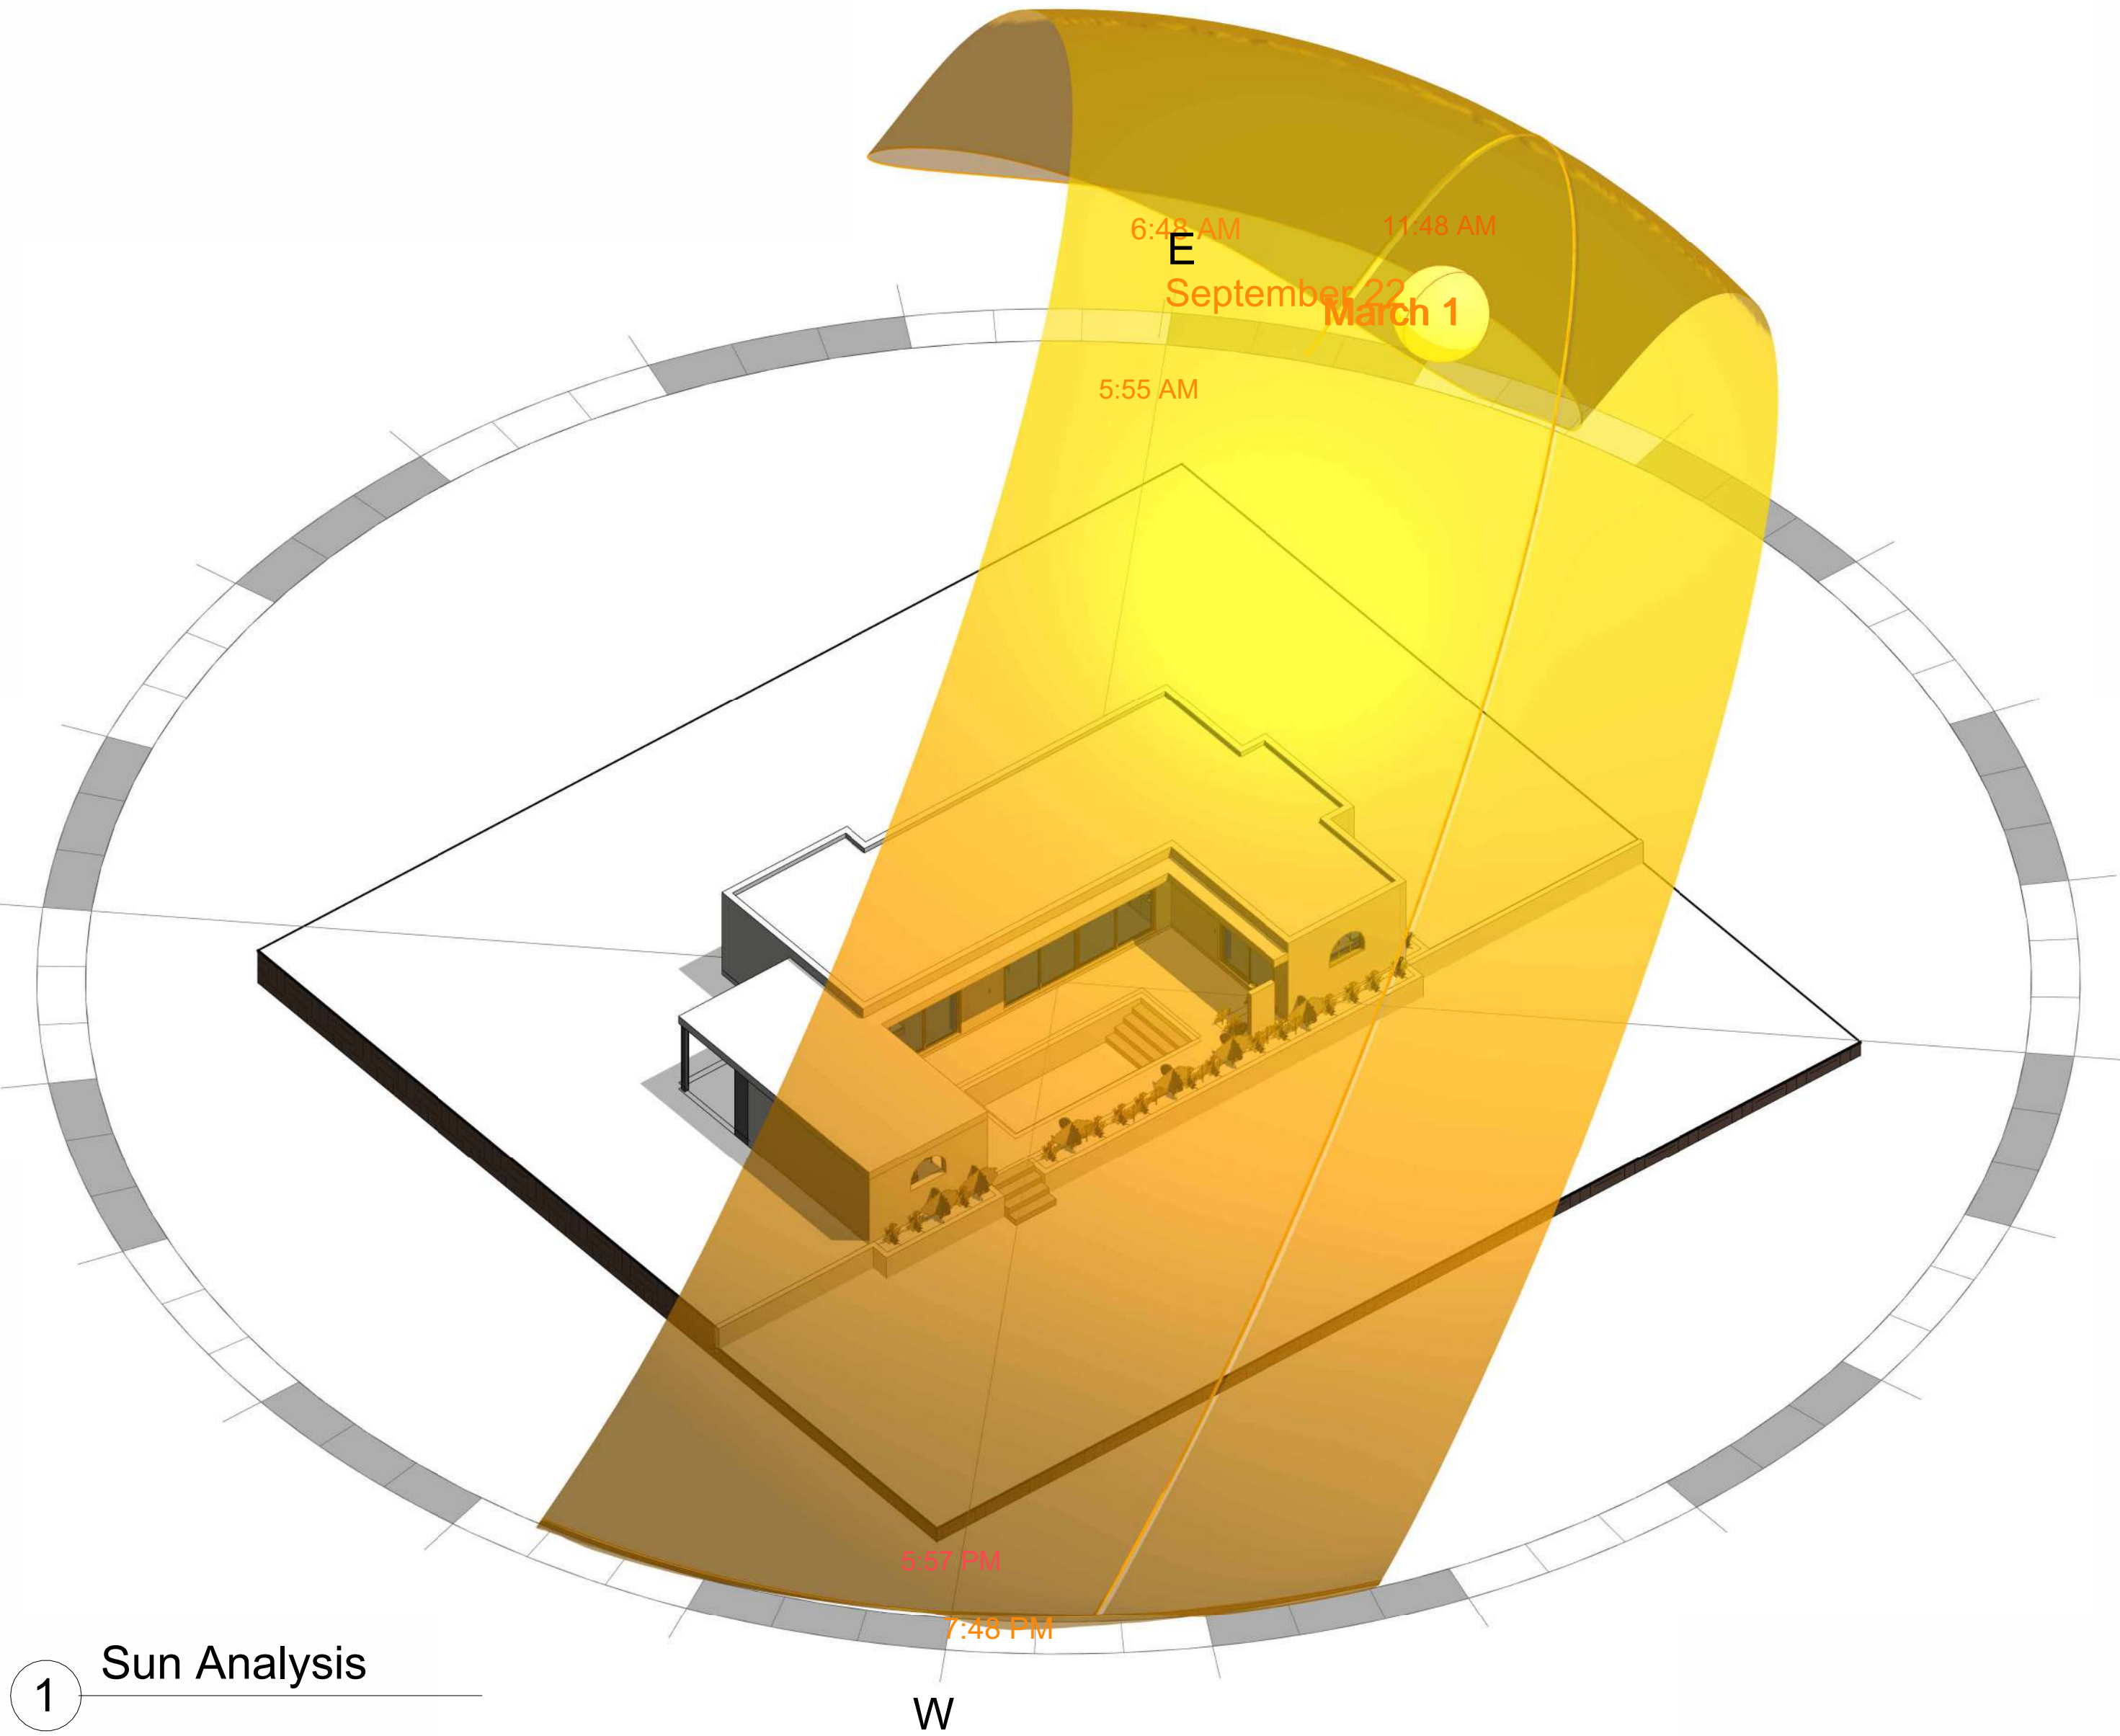

1 Sun Analysis

1. THESE DRAWINGS MUST BE CHECKED BY THE CUSTOMER OR CONTRACTOR PRIOR TO APPROVAL. ANY ERRORS OR OMISSIONS MUST BE REPORTED IN WRITING TO BAUHU PRIOR TO COMMENCEMENT OF CONSTRUCTION.
2. ARCHITECTURAL DRAWINGS SHOULD BE READ IN CONJUNCTION WITH STRUCTURAL DETAILING AND FABRICATION GENERAL ASSEMBLY DRAWINGS.
3. FOR CONSTRUCTION PURPOSES, USE ONLY THE LATEST APPROVED DRAWINGS LABELED 'ISSUED FOR CONSTRUCTION'.
4. DO NOT SCALE FROM THIS DRAWING.
5. THE COMPANY OPERATES USING METRIC DIMENSIONS AS THE PRINCIPAL DENOMINATION.
6. ALL CONCRETE WORKS ARE OUTSIDE OF THE SCOPE OF THE COMPANY. INFORMATION REGARDING SLAB DESIGN AND CONNECTIONS IN THESE DRAWINGS ARE INTENDED FOR GUIDENCE ONLY. FOUNDATION AND SLAB WORKS SHOULD BE DESIGNED AND APPROVED BY A LOCAL STRUCTURAL ENGINEER.
7. THE COMPANY RETAINS FULL TITLE AND OWNERSHIP OF THESE PLANS AND DESIGNS. ANY UNAUTHORISED USE, REPRODUCTION, OR DISTRIBUTION OF THESE PLANS, WHETHER IN WHOLE OR PART, IS EXPRESSLY PROHIBITED WITHOUT PRIOR WRITTEN CONSENT.

| No. | Revision | Date |
|-----|----------|------|
|     |          |      |
|     |          |      |
ISSUED FOR:

- ☐ Issued for information  
☒ Issued for client approval  
☐ Issued for fabrication  
☐ Issued for construction

Firefly

|                |                       |
|----------------|-----------------------|
| DRAWING TITLE: | Sun Analysis          |
| DRAWN BY:      | Mladin Monica-Mihaela |
| SCALE:         |                       |
| DRAWING NO:    | A06                   |
| DATE:          | 04.03.2024            |

## FRONT ELEVATION

1. THESE DRAWINGS MUST BE CHECKED BY THE CUSTOMER OR CONTRACTOR PRIOR TO APPROVAL. ANY ERRORS OR OMISSIONS MUST BE REPORTED IN WRITING TO BAUHU PRIOR TO COMMENCEMENT OF CONSTRUCTION.
2. ARCHITECTURAL DRAWINGS SHOULD BE READ IN CONJUNCTION WITH STRUCTURAL DETAILING AND FABRICATION GENERAL ASSEMBLY DRAWINGS.
3. FOR CONSTRUCTION PURPOSES, USE ONLY THE LATEST APPROVED DRAWINGS LABELED 'ISSUED FOR CONSTRUCTION'.
4. DO NOT SCALE FROM THIS DRAWING.
5. THE COMPANY OPERATES USING METRIC DIMENSIONS AS THE PRINCIPAL DENOMINATION.
6. ALL CONCRETE WORKS ARE OUTSIDE OF THE SCOPE OF THE COMPANY. INFORMATION REGARDING SLAB DESIGN AND CONNECTIONS IN THESE DRAWINGS ARE INTENDED FOR GUIDANCE ONLY. FOUNDATION AND SLAB WORKS SHOULD BE DESIGNED AND APPROVED BY A LOCAL STRUCTURAL ENGINEER.
7. THE COMPANY RETAINS FULL TITLE AND OWNERSHIP OF THESE PLANS AND DESIGNS. ANY UNAUTHORISED USE, REPRODUCTION, OR DISTRIBUTION OF THESE PLANS, WHETHER IN WHOLE OR PART, IS EXPRESSLY PROHIBITED WITHOUT PRIOR WRITTEN CONSENT.

| No. | Revision | Date |
|-----|----------|------|
|     |          |      |
|     |          |      |
## ISSUED FOR:

Issued for information

Issued for client approval

Issued for fabrication

Issued for construction

Firefly

## DRAWING TITLE:

Ground Floor Plan

## DRAWN BY:

Mladin Monica-Mihaela

## SCALE:

1 : 70

## DRAWING NO:

A07

## DATE:

04.03.2024


## RIGHT ELEVATION

## LEFT ELEVATION


## BACK ELEVATION

Building Footprint: 157.542 Sqm , 1695.766 Sq feet  
Outdoor Covered Terrace: 28.25 Sqm, 304.080 Sq feet  
Pool Terrace Area: 54.02 Sqm, 581.466 Sq feet  
Carport: 15.46 Sqm, 166.410 Sq feet  
Pool Area: 24.60 Sqm, 264.792 Sq feet  
Total construction footprint: 279.872 Sqm, 3012.514 Sq feet

Freestanding furniture and equipment is shown for illustrative purposes only.

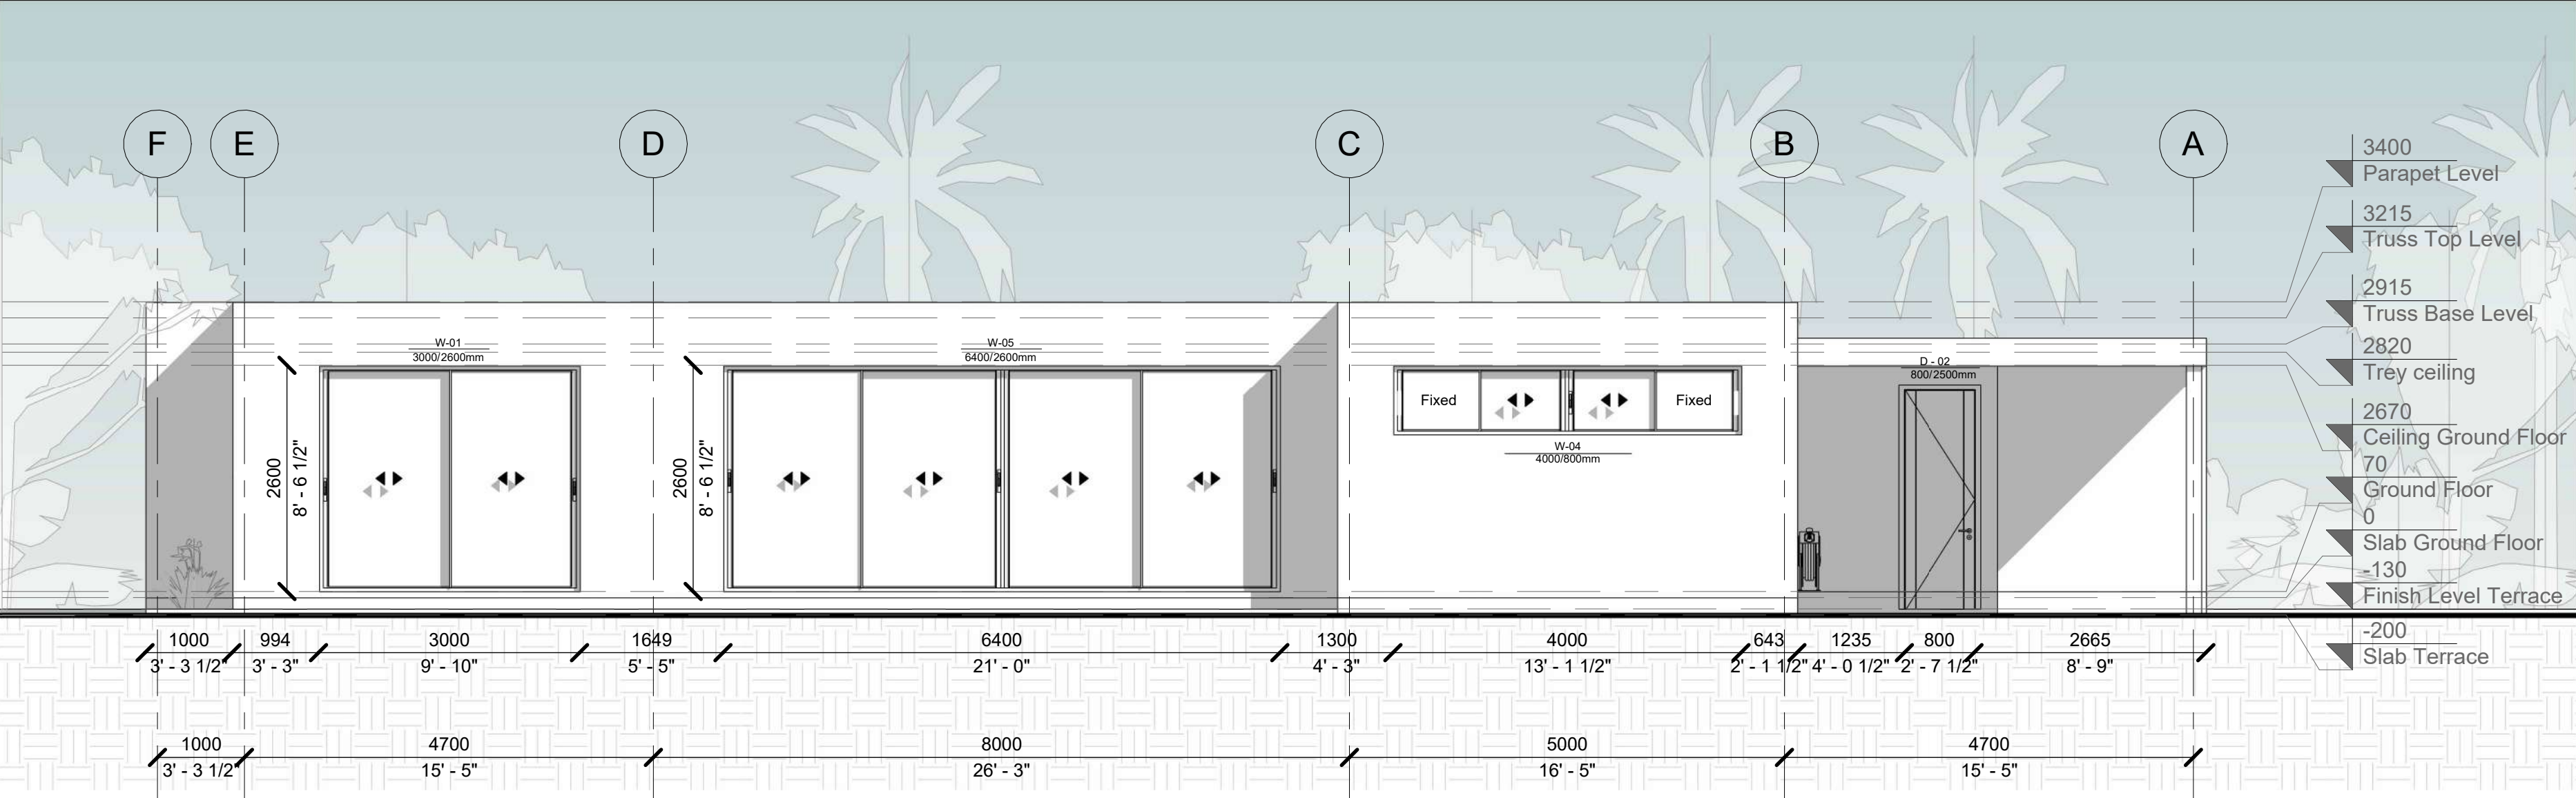

1 Front Elevation  
1 : 60

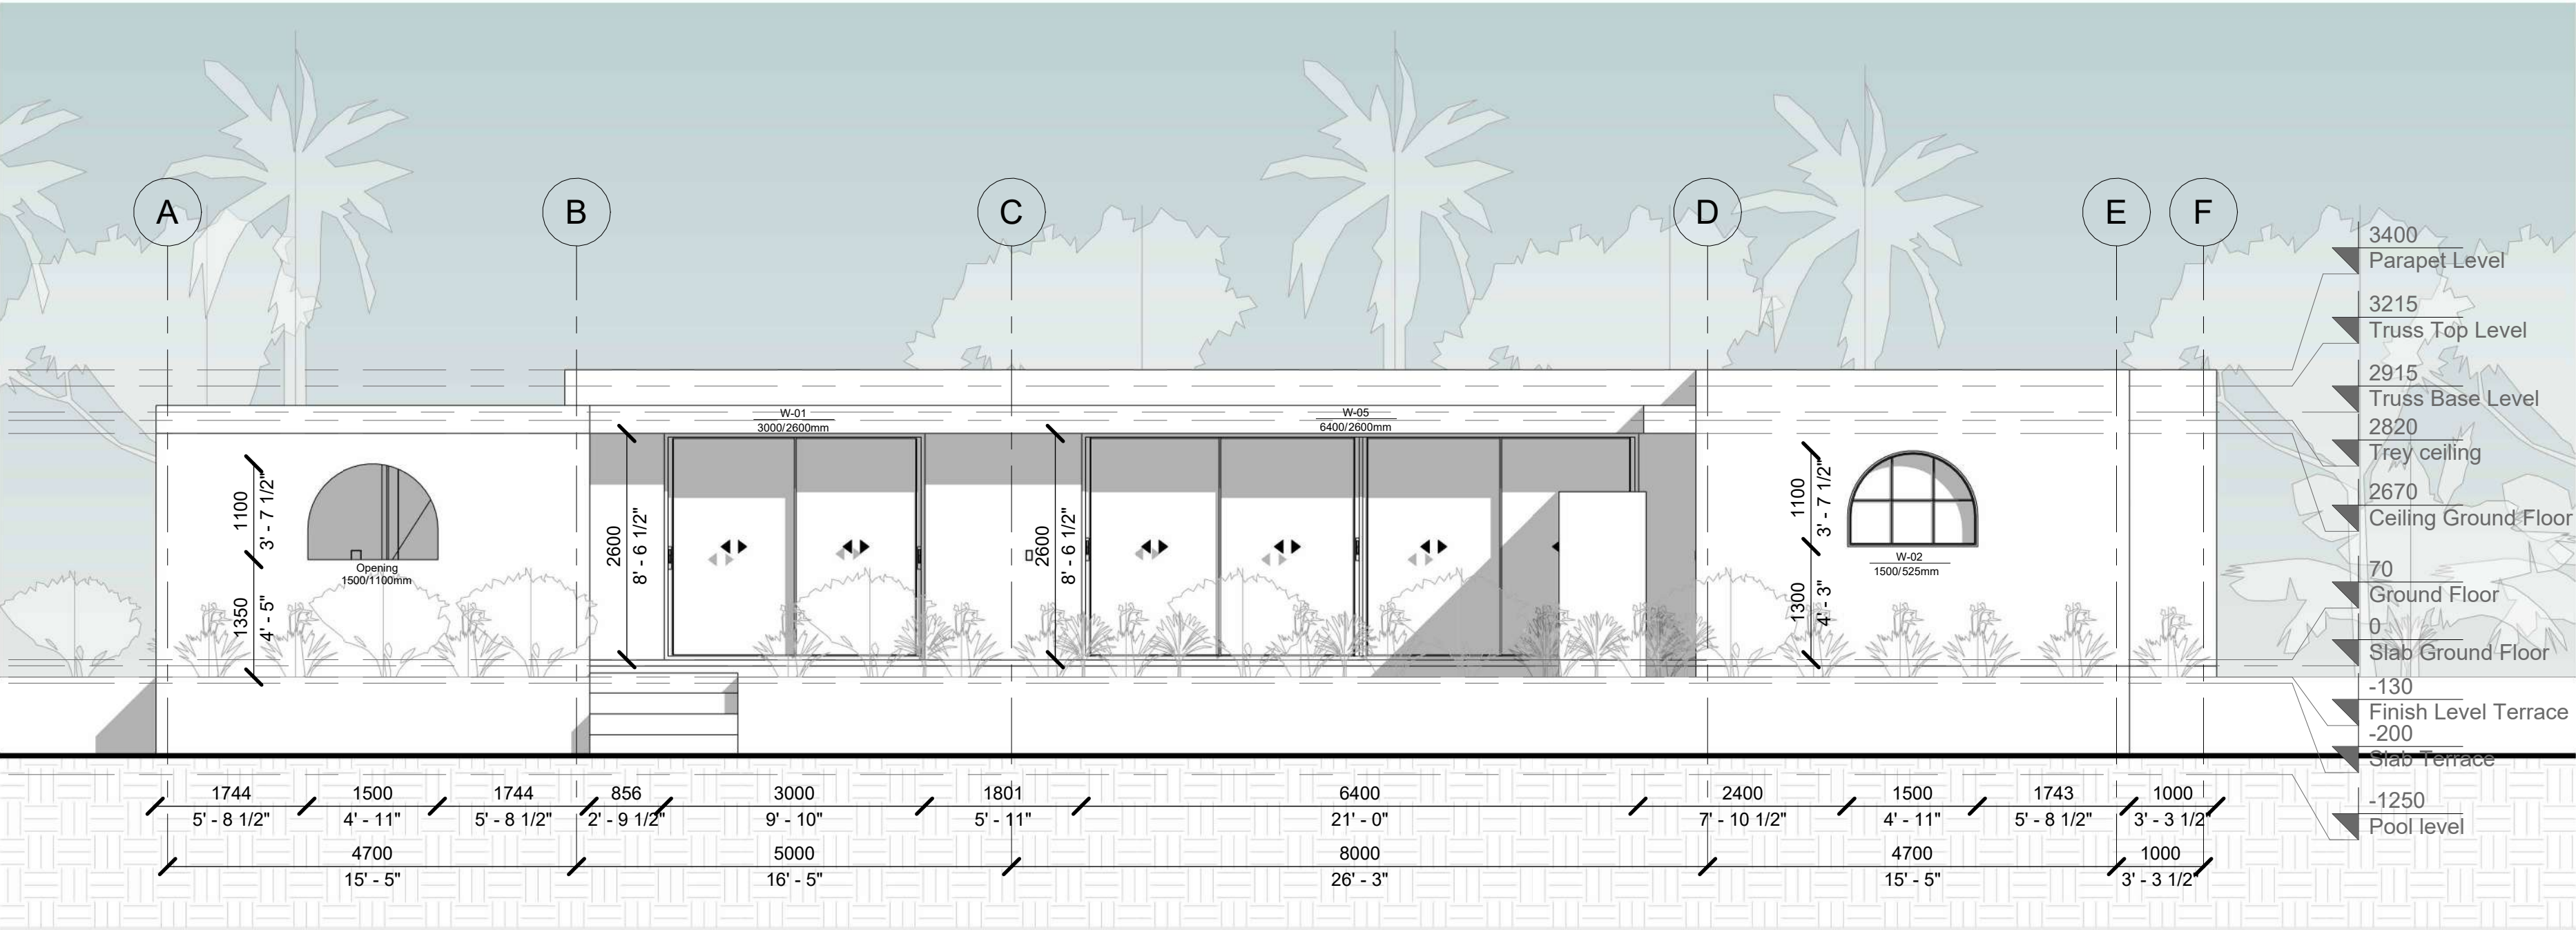

2 Back Elevation  
1 : 60

1. THESE DRAWINGS MUST BE CHECKED BY THE CUSTOMER OR CONTRACTOR PRIOR TO APPROVAL. ANY ERRORS OR OMISSIONS MUST BE REPORTED IN WRITING TO BAUHU PRIOR TO COMMENCEMENT OF CONSTRUCTION.
2. ARCHITECTURAL DRAWINGS SHOULD BE READ IN CONJUNCTION WITH STRUCTURAL DETAILING AND FABRICATION GENERAL ASSEMBLY DRAWINGS.
3. FOR CONSTRUCTION PURPOSES, USE ONLY THE LATEST APPROVED DRAWINGS LABELED 'ISSUED FOR CONSTRUCTION'.
4. DO NOT SCALE FROM THIS DRAWING.
5. THE COMPANY OPERATES USING METRIC DIMENSIONS AS THE PRINCIPAL DENOMINATION.
6. ALL CONCRETE WORKS ARE OUTSIDE OF THE SCOPE OF THE COMPANY. INFORMATION REGARDING SLAB DESIGN AND CONNECTIONS IN THESE DRAWINGS ARE INTENDED FOR GUIDANCE ONLY. FOUNDATION AND SLAB WORKS SHOULD BE DESIGNED AND APPROVED BY A LOCAL STRUCTURAL ENGINEER.
7. THE COMPANY RETAINS FULL TITLE AND OWNERSHIP OF THESE PLANS AND DESIGNS. ANY UNAUTHORISED USE, REPRODUCTION, OR DISTRIBUTION OF THESE PLANS, WHETHER IN WHOLE OR PART, IS EXPRESSLY PROHIBITED WITHOUT PRIOR WRITTEN CONSENT.

| No. | Revision | Date |
|-----|----------|------|
|     |          |      |
|     |          |      |
ISSUED FOR:

Issued for information

Issued for client approval

Issued for fabrication

Issued for construction

Firefly

DRAWING TITLE:

Elevations

DRAWN BY:

Mladin Monica-Mihaela

SCALE:

1 : 60

DRAWING NO:

A08

DATE:

04.03.2024

1. THESE DRAWINGS MUST BE CHECKED BY THE CUSTOMER OR CONTRACTOR PRIOR TO APPROVAL. ANY ERRORS OR OMISSIONS MUST BE REPORTED IN WRITING TO BAUHU PRIOR TO COMMENCEMENT OF CONSTRUCTION.
2. ARCHITECTURAL DRAWINGS SHOULD BE READ IN CONJUNCTION WITH STRUCTURAL DETAILING AND FABRICATION GENERAL ASSEMBLY DRAWINGS.
3. FOR CONSTRUCTION PURPOSES, USE ONLY THE LATEST APPROVED DRAWINGS LABELED 'ISSUED FOR CONSTRUCTION'.
4. DO NOT SCALE FROM THIS DRAWING.
5. THE COMPANY OPERATES USING METRIC DIMENSIONS AS THE PRINCIPAL DENOMINATION.
6. ALL CONCRETE WORKS ARE OUTSIDE OF THE SCOPE OF THE COMPANY. INFORMATION REGARDING SLAB DESIGN AND CONNECTIONS IN THESE DRAWINGS ARE INTENDED FOR GUIDENCE ONLY. FOUNDATION AND SLAB WORKS SHOULD BE DESIGNED AND APPROVED BY A LOCAL STRUCTURAL ENGINEER.
7. THE COMPANY RETAINS FULL TITLE AND OWNERSHIP OF THESE PLANS AND DESIGNS. ANY UNAUTHORISED USE, REPRODUCTION, OR DISTRIBUTION OF THESE PLANS, WHETHER IN WHOLE OR PART, IS EXPRESSLY PROHIBITED WITHOUT PRIOR WRITTEN CONSENT.

| No. | Revision | Date |
|-----|----------|------|
|     |          |      |
|     |          |      |
ISSUED FOR:

Issued for information

Issued for client approval

Issued for fabrication

Issued for construction

Firefly

DRAWING TITLE:

Elevations

DRAWN BY:

Mladin Monica-Mihaela

SCALE:


1 : 60

DRAWING NO:


A09

DATE:

04.03.2024

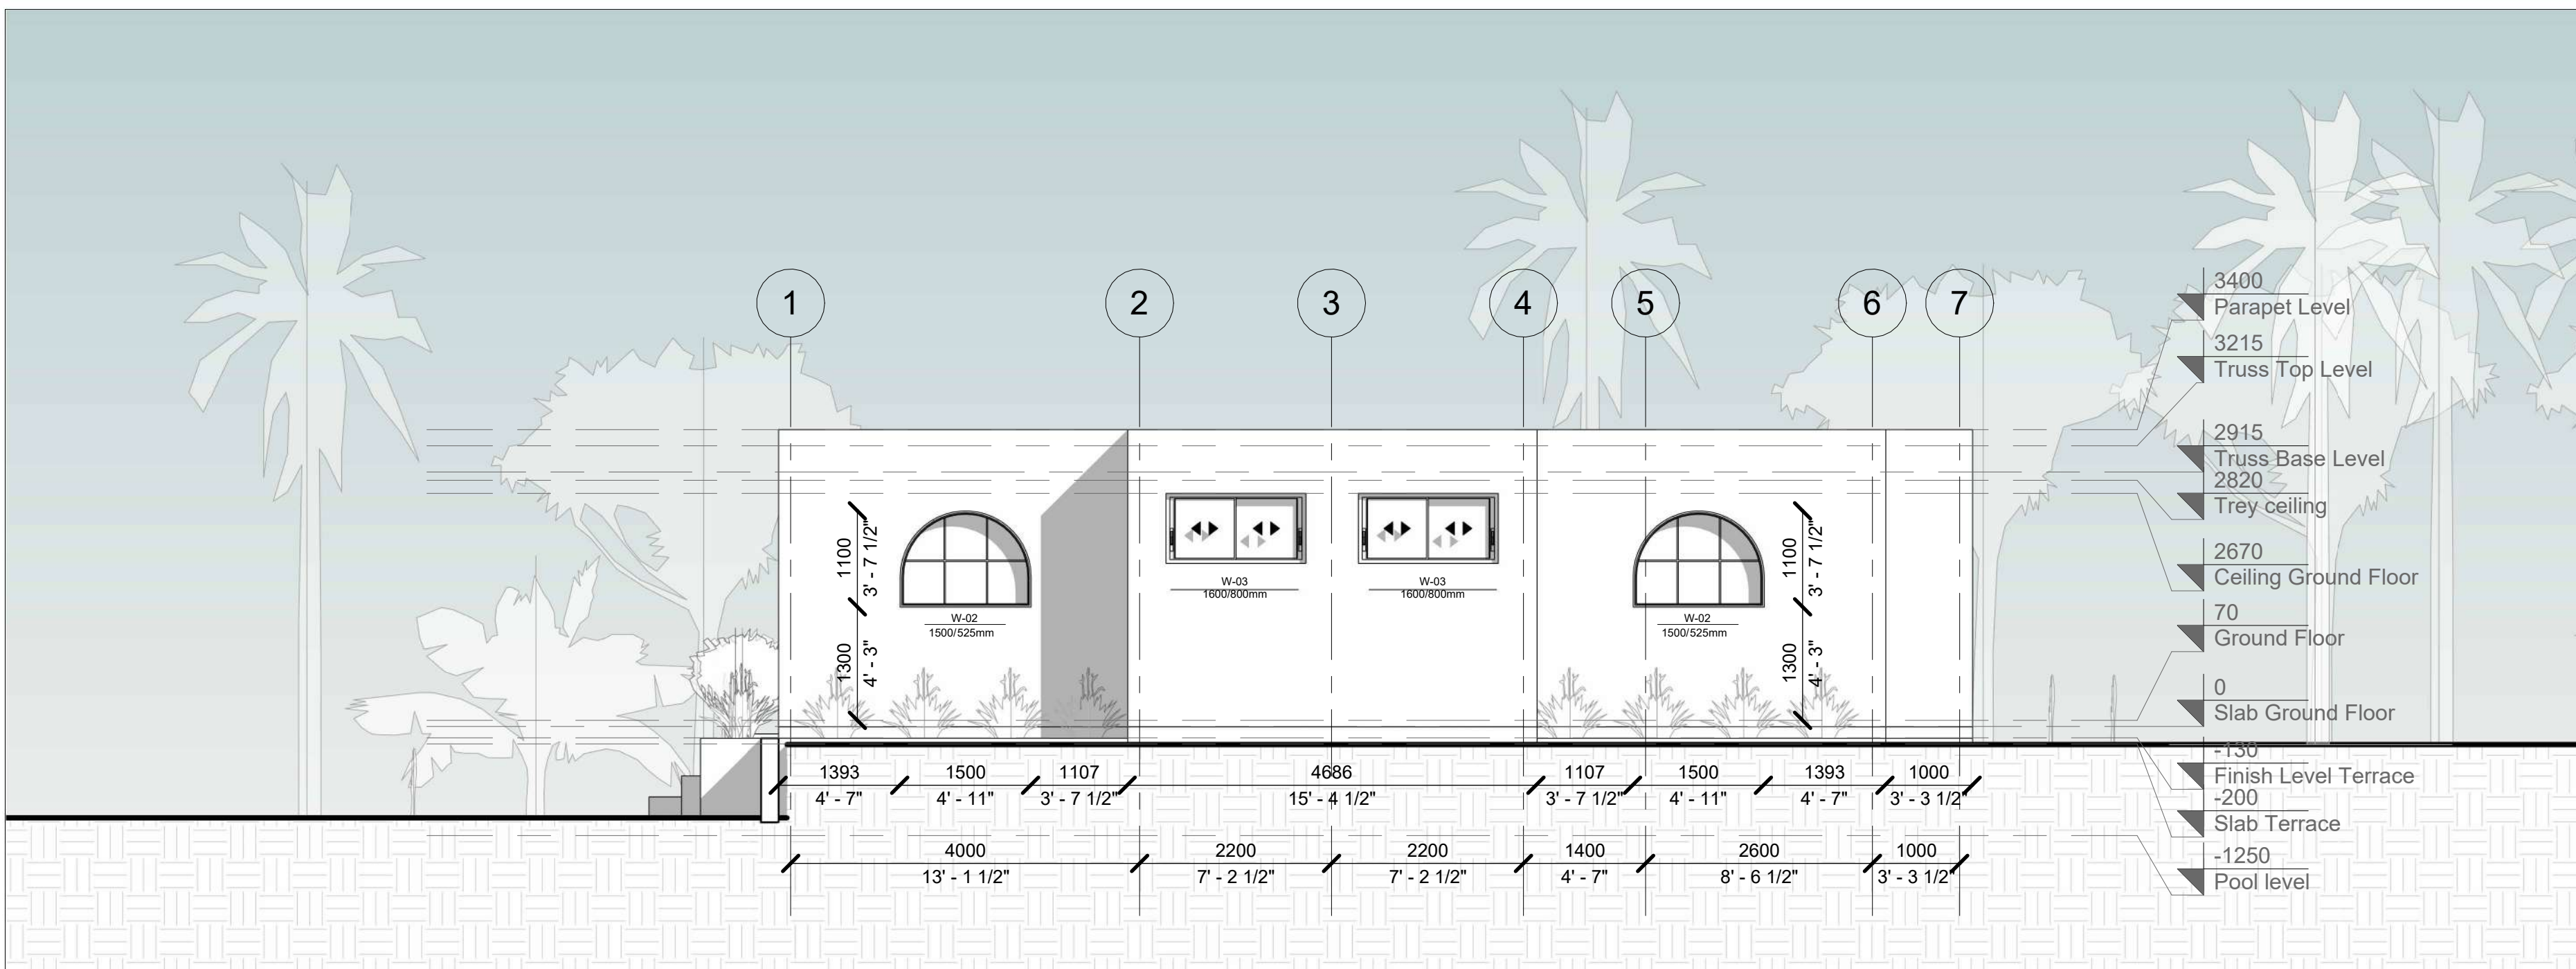

1 Left Elevation  
1 : 60

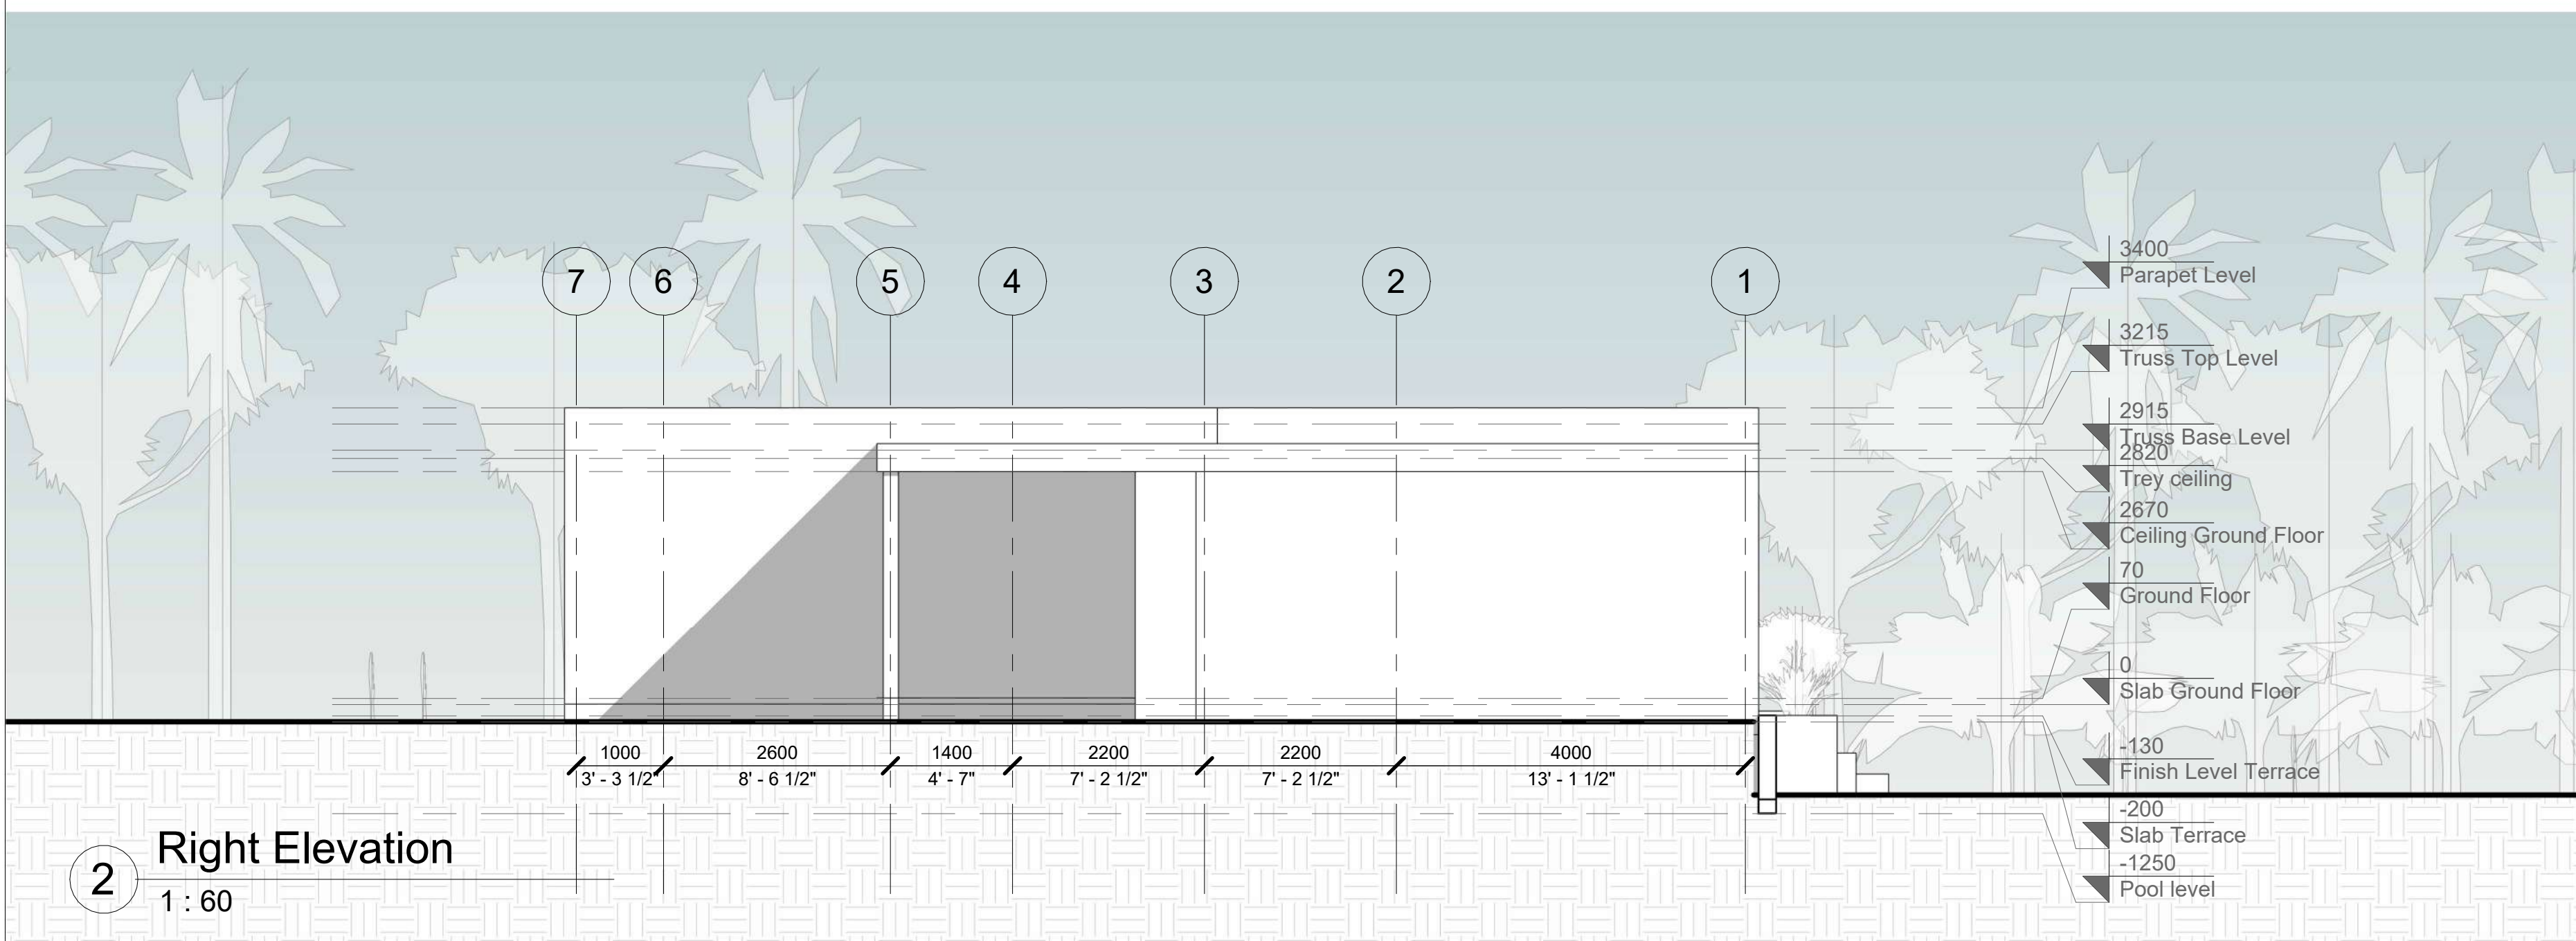

2 Right Elevation  
1 : 60

1. THESE DRAWINGS MUST BE CHECKED BY THE CUSTOMER OR CONTRACTOR PRIOR TO APPROVAL. ANY ERRORS OR OMISSIONS MUST BE REPORTED IN WRITING TO BAUHU PRIOR TO COMMENCEMENT OF CONSTRUCTION.
2. ARCHITECTURAL DRAWINGS SHOULD BE READ IN CONJUNCTION WITH STRUCTURAL DETAILING AND FABRICATION GENERAL ASSEMBLY DRAWINGS.
3. FOR CONSTRUCTION PURPOSES, USE ONLY THE LATEST APPROVED DRAWINGS LABELED 'ISSUED FOR CONSTRUCTION'.
4. DO NOT SCALE FROM THIS DRAWING.
5. THE COMPANY OPERATES USING METRIC DIMENSIONS AS THE PRINCIPAL DENOMINATION.
6. ALL CONCRETE WORKS ARE OUTSIDE OF THE SCOPE OF THE COMPANY. INFORMATION REGARDING SLAB DESIGN AND CONNECTIONS IN THESE DRAWINGS ARE INTENDED FOR GUIDANCE ONLY. FOUNDATION AND SLAB WORKS SHOULD BE DESIGNED AND APPROVED BY A LOCAL STRUCTURAL ENGINEER.
7. THE COMPANY RETAINS FULL TITLE AND OWNERSHIP OF THESE PLANS AND DESIGNS. ANY UNAUTHORISED USE, REPRODUCTION, OR DISTRIBUTION OF THESE PLANS, WHETHER IN WHOLE OR PART, IS EXPRESSLY PROHIBITED WITHOUT PRIOR WRITTEN CONSENT.

| No. | Revision | Date |
|-----|----------|------|
|     |          |      |
|     |          |      |
ISSUED FOR:

Issued for information

Issued for client approval

Issued for fabrication

Issued for construction

Firefly

DRAWING TITLE:

Sections

DRAWN BY:

Mladin Monica-Mihaela

SCALE:


1 : 65

DRAWING NO:

A10


DATE:

04.03.2024

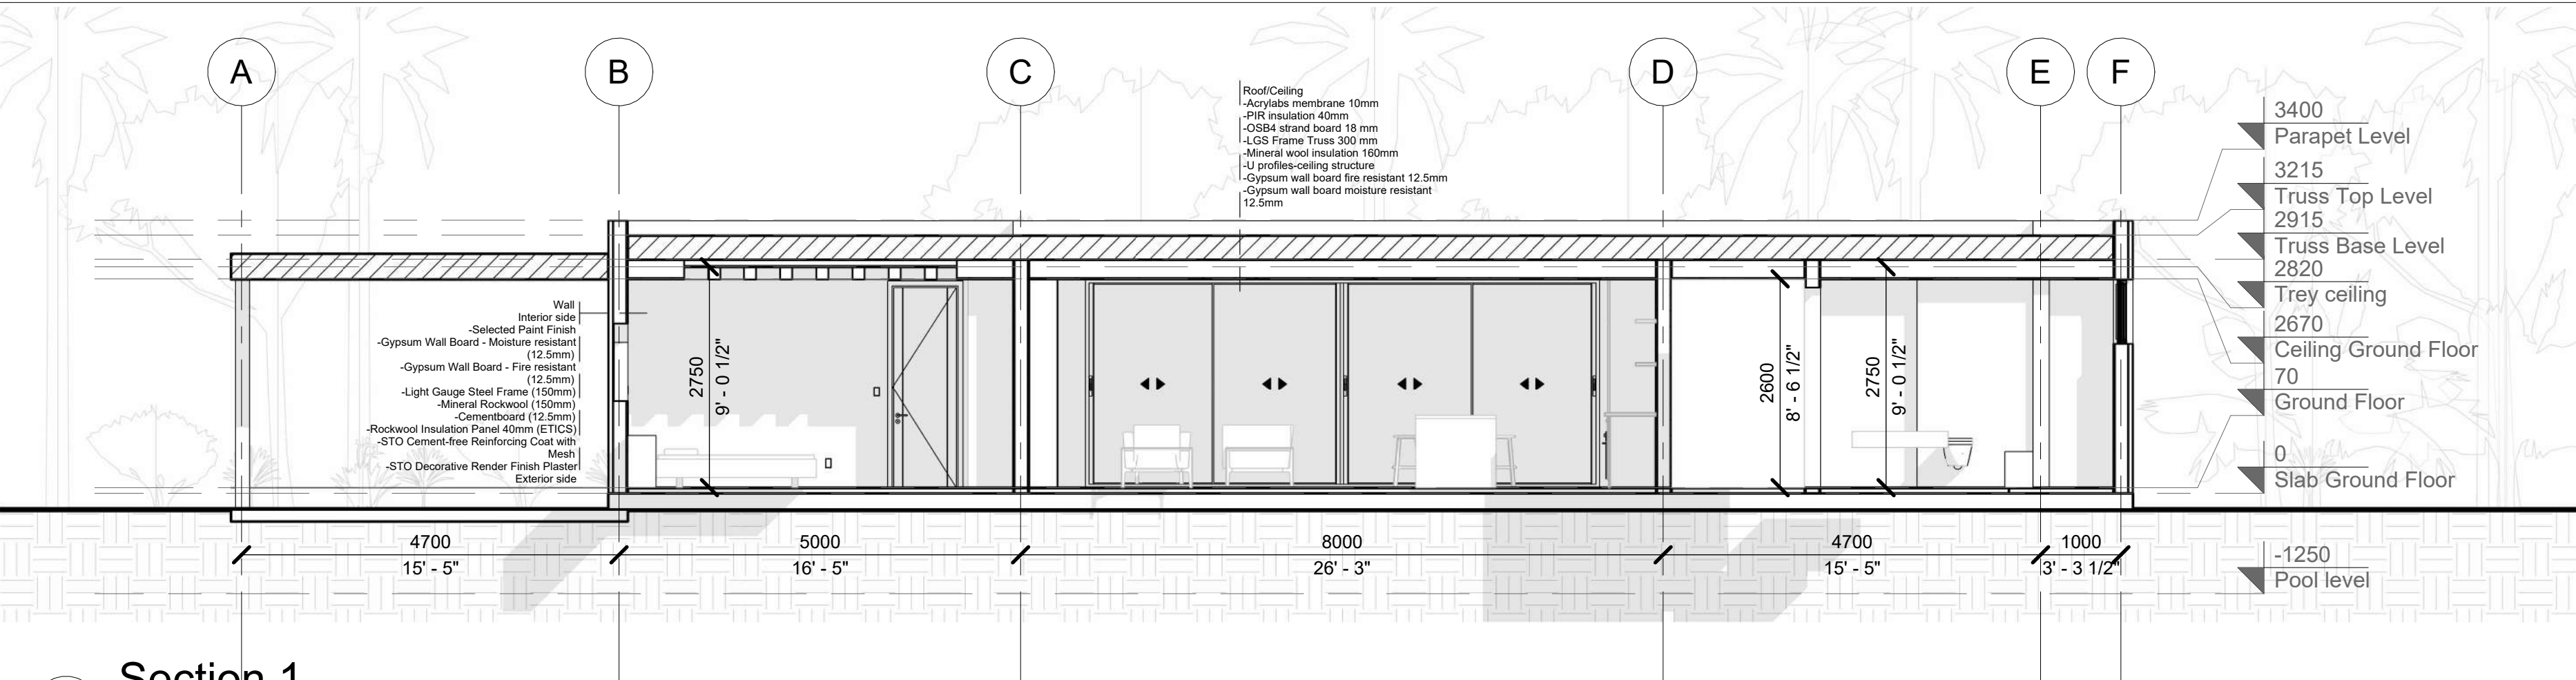


Section 1

1 : 65

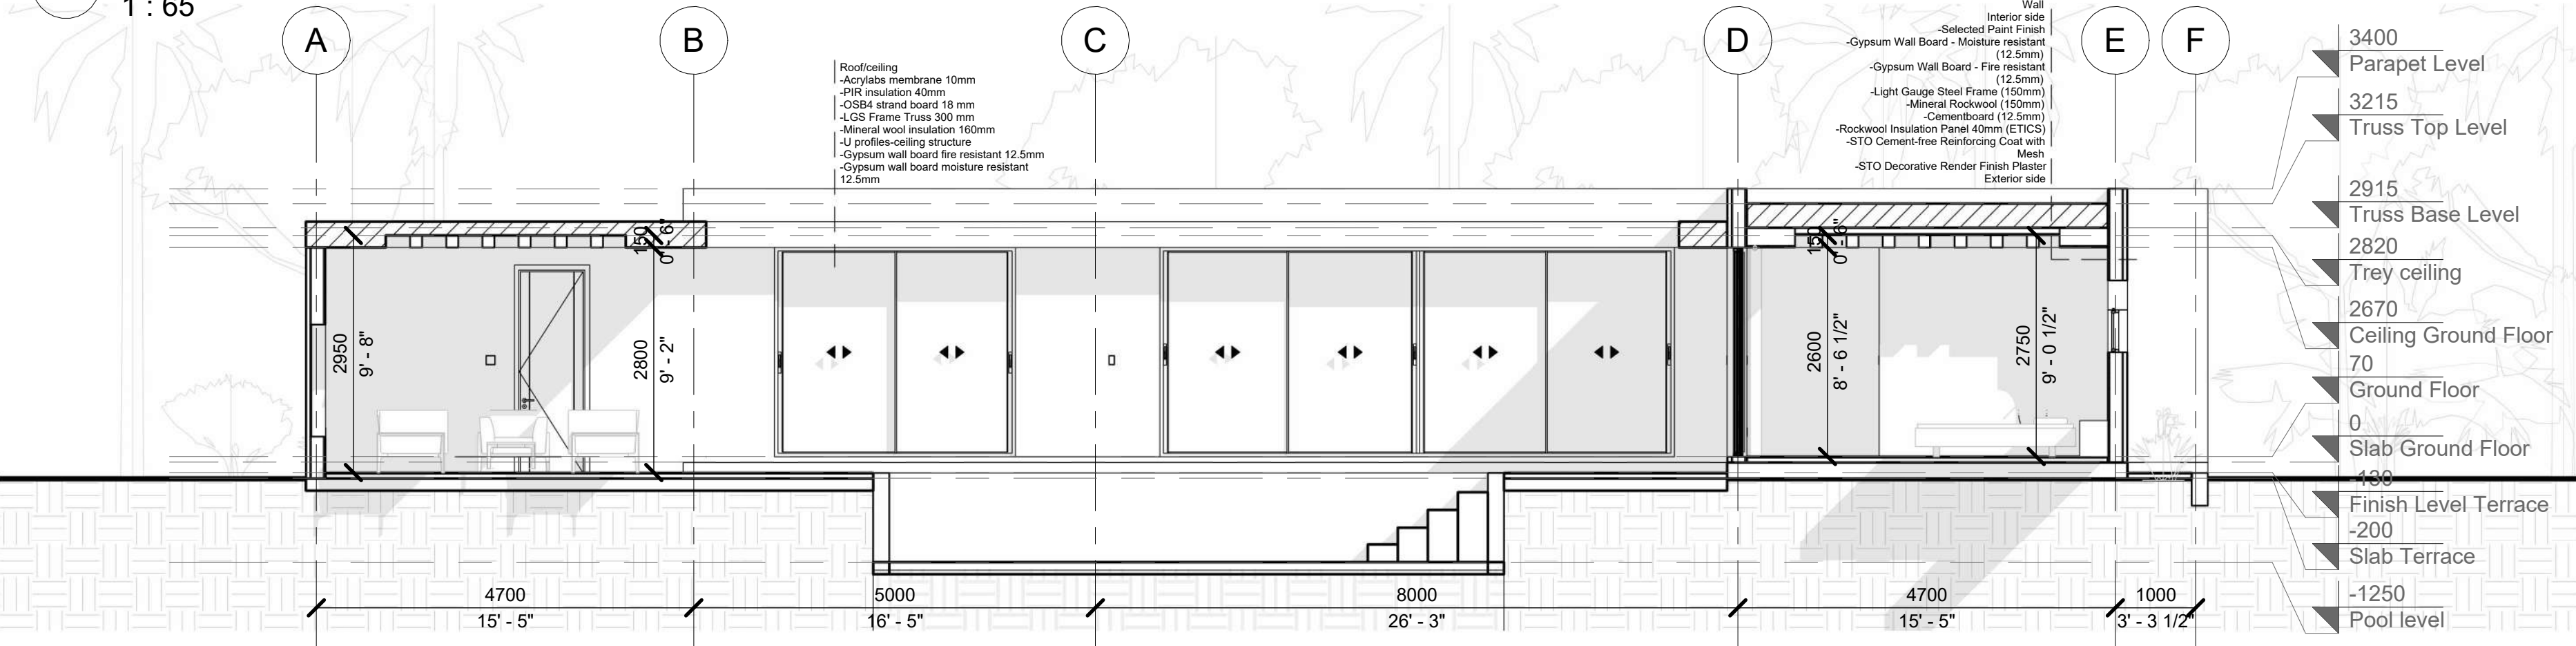

Section 2

1 : 65

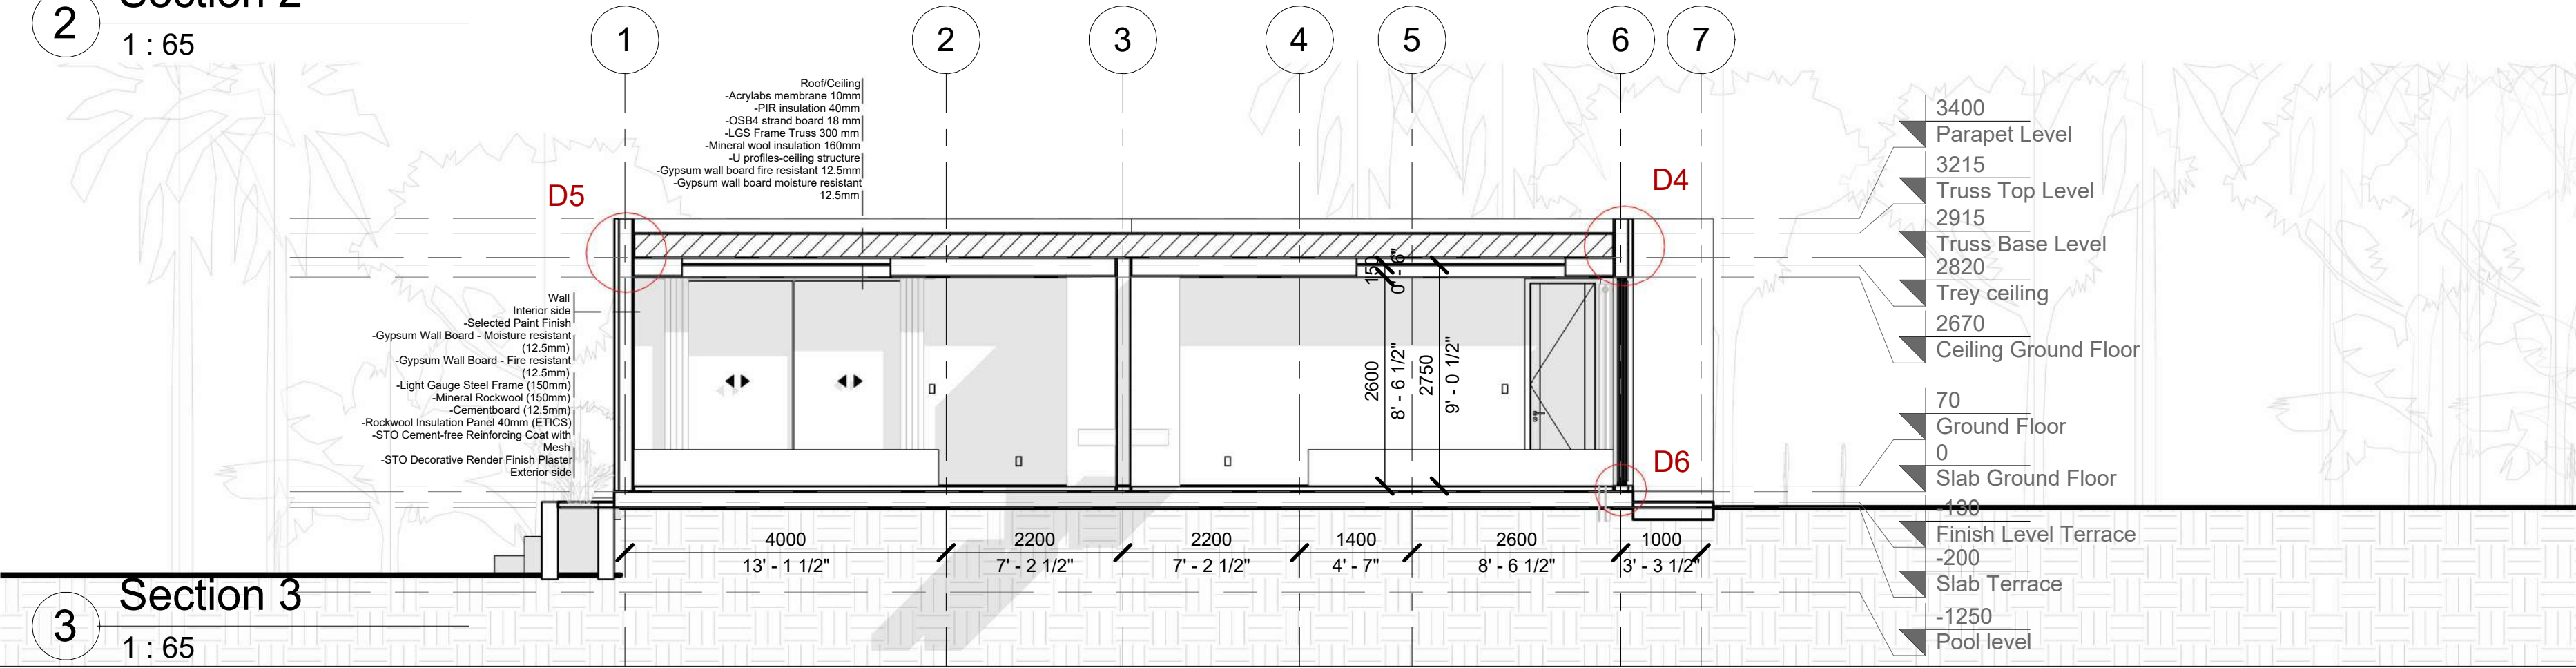

Section 3

1 : 65

- THESE DRAWINGS MUST BE CHECKED BY THE CUSTOMER OR CONTRACTOR PRIOR TO APPROVAL. ANY ERRORS OR OMISSIONS MUST BE REPORTED IN WRITING TO BAUHU PRIOR TO COMMENCEMENT OF CONSTRUCTION.
- ARCHITECTURAL DRAWINGS SHOULD BE READ IN CONJUNCTION WITH STRUCTURAL DETAILING AND FABRICATION GENERAL ASSEMBLY DRAWINGS.
- FOR CONSTRUCTION PURPOSES, USE ONLY THE LATEST APPROVED DRAWINGS LABELED 'ISSUED FOR CONSTRUCTION'.
- DO NOT SCALE FROM THIS DRAWING.
- THE COMPANY OPERATES USING METRIC DIMENSIONS AS THE PRINCIPAL DENOMINATION.
- ALL CONCRETE WORKS ARE OUTSIDE OF THE SCOPE OF THE COMPANY. INFORMATION REGARDING SLAB DESIGN AND CONNECTIONS IN THESE DRAWINGS ARE INTENDED FOR GUIDENCE ONLY. FOUNDATION AND SLAB WORKS SHOULD BE DESIGNED AND APPROVED BY A LOCAL STRUCTURAL ENGINEER.
- THE COMPANY RETAINS FULL TITLE AND OWNERSHIP OF THESE PLANS AND DESIGNS. ANY UNAUTHORISED USE, REPRODUCTION, OR DISTRIBUTION OF THESE PLANS, WHETHER IN WHOLE OR PART, IS EXPRESSLY PROHIBITED WITHOUT PRIOR WRITTEN CONSENT.

| No. | Revision | Date |
|-----|----------|------|
|     |          |      |
|     |          |      |
ISSUED FOR:

Issued for information

Issued for client approval

Issued for fabrication

Issued for construction

Firefly

DRAWING TITLE:

Openings Schedule

DRAWN BY:

Mladin Monica-Mihaela

SCALE:

As indicated

DRAWING NO:

A11

DATE:

04.03.2024

## Openings Schedule


### Doors

| Name | Size     | R.O. Size | Count | Type                | Frame Colour | No.of leaves | Hinge side              | Sill height | Lock |
|------|----------|-----------|-------|---------------------|--------------|--------------|-------------------------|-------------|------|
| D01  | 800x2600 | 843x2690  | 1     | Exterior - Casement | -            | 1            | right                   | 70          | Yes  |
| D02  | 800x2500 | 843x2590  | 3     | Interior - Casement | -            | 1            | 1pcs right<br>2pcs left | 70          | Yes  |

### Windows




| Name | Size      | R.O. Size | Count | Opening Direction     | Frame Colour | No.of leaves | Hinge side    | Sill height | Lock |
|------|-----------|-----------|-------|-----------------------|--------------|--------------|---------------|-------------|------|
| W01  | 3000x2600 | 3040x2690 | 3     | Sliding               | Anthracite   | 2            | Sliding       | 70          | Yes  |
| W02  | 1500x1100 | 1540x1140 | 3     | Fixed- with mulitions | Anthracite   | 1            | Fixed         | 1350        | -    |
| W03  | 1600x800  | 1640x840  | 2     | Sliding               | Anthracite   | 2            | Sliding       | 1850        | Yes  |
| W04  | 4000x800  | 4040x840  | 1     | Fixed/Sliding         | Anthracite   | 4            | Fixed/Sliding | 1850        | Yes  |
| W05  | 6400x2600 | 6440x2640 | 2     | Sliding               | Anthracite   | 4            | Sliding       | 70          | Yes  |

- Note:
- Hinge Side - Always viewed from inside
  - Sill height is from top of slab/structure

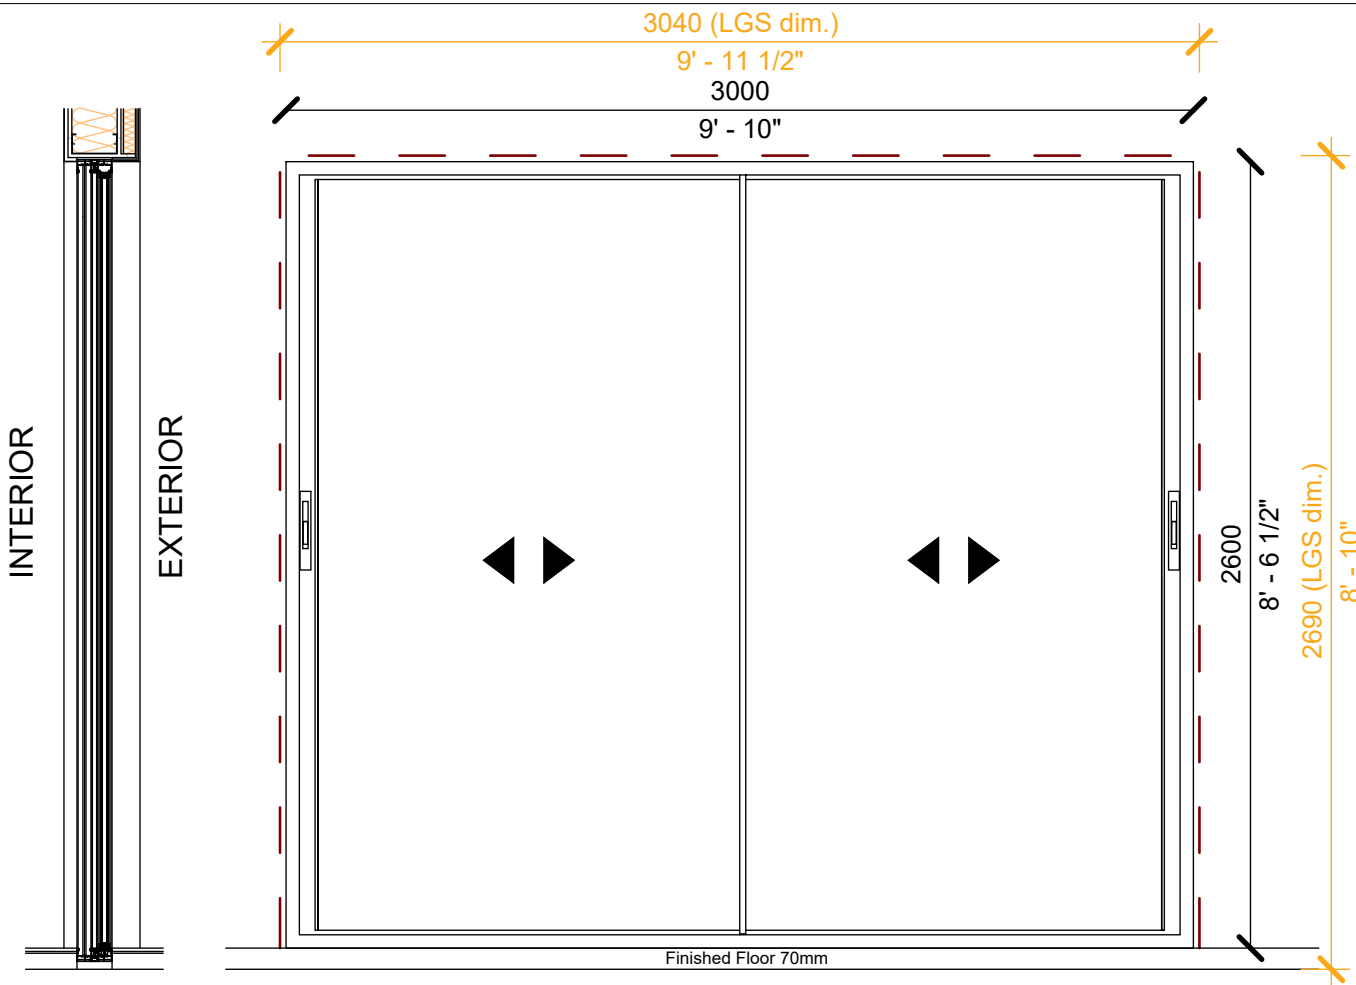




W01

Type: Cor Vision  
Size: 3000/2600 mm  
R.O.Size: 3040/2690 mm  
Colour: Anthracite  
Nr. of leaves: 2  
Total Piece: 3  
Hinge Side: Sliding  
Sill Height (from top of slab): 70 mm

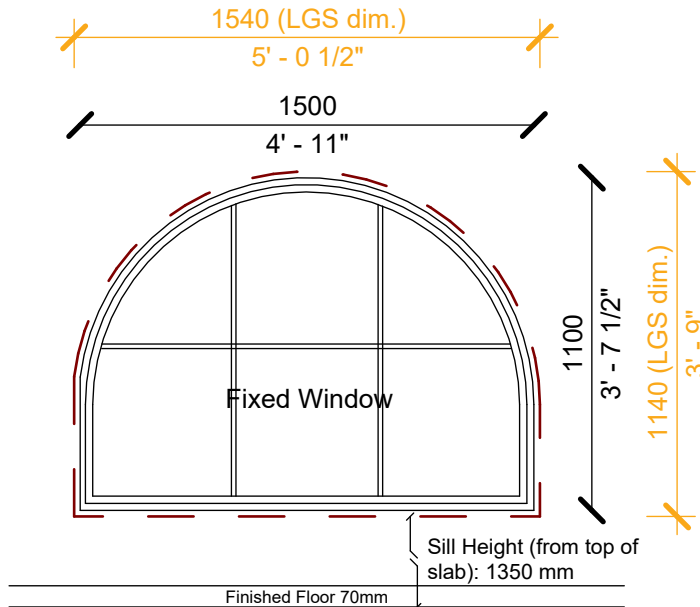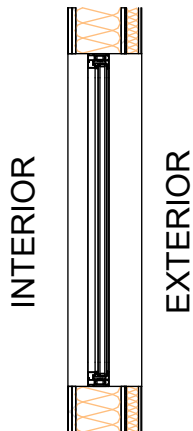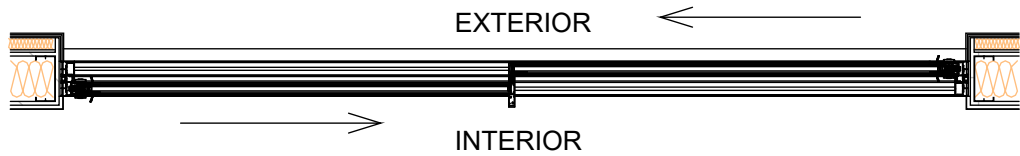





W02

Type: Cor Vision  
Size: 1500/1100 mm  
R.O.Size: 1540/1140 mm  
Colour: Anthracite  
Nr. of leaves: 1  
Total Piece: 3  
Hinge Side: Fixed  
Sill Height (from top of slab): 1350 mm  
With mulitions

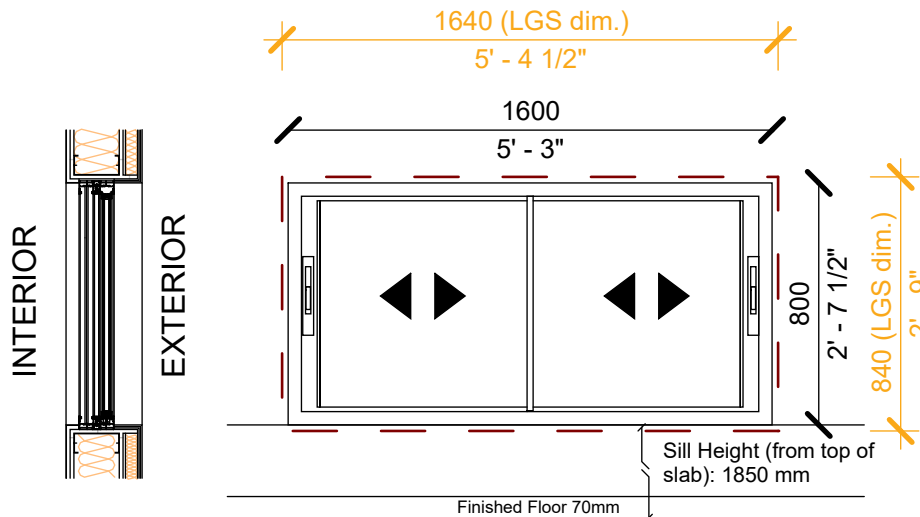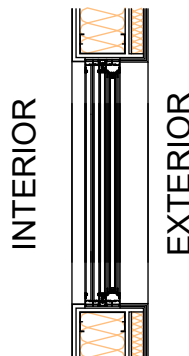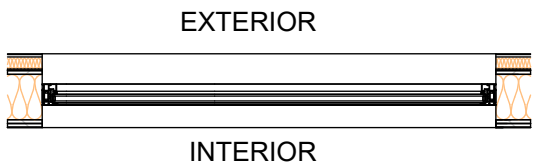


W03

Type: Cor Vision  
Size: 1600/800 mm  
R.O.Size: 1640/840 mm  
Colour: Anthracite  
Nr. of leaves: 2  
Total Piece: 2  
Hinge Side: Sliding  
Sill Height (from top of slab): 1850 mm

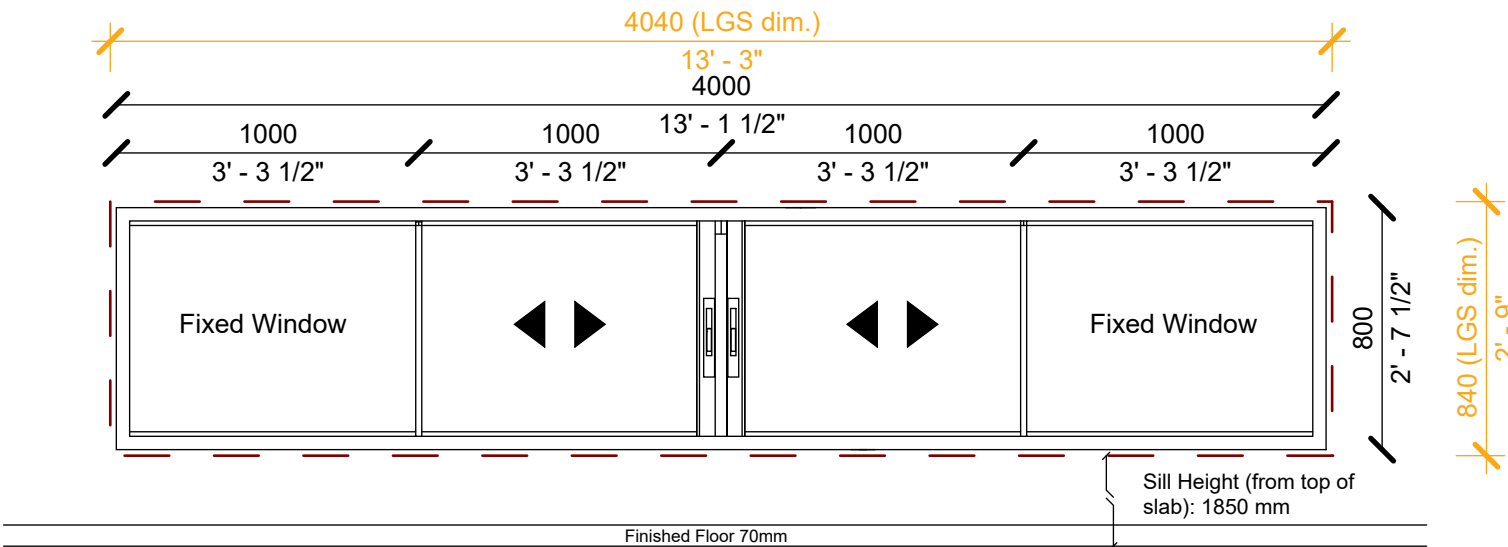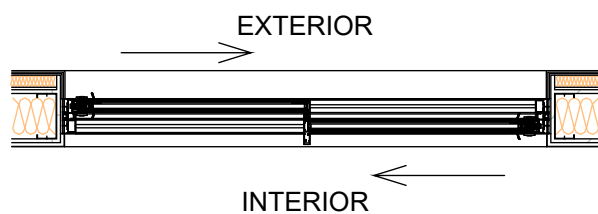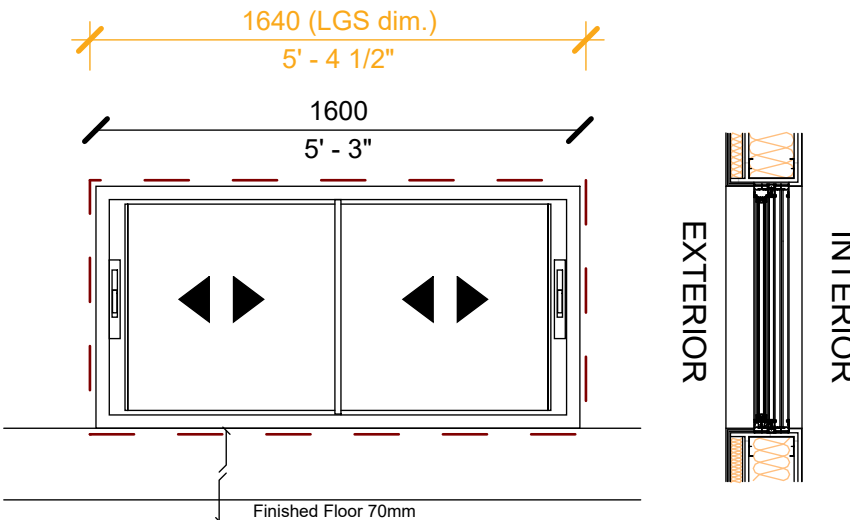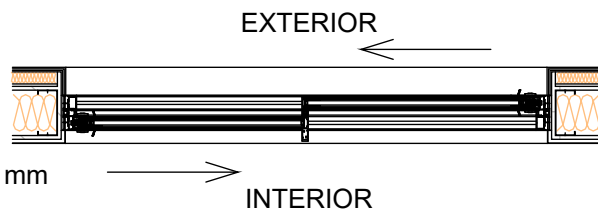

W04

Type: Cor Vision  
Size: 4000/800 mm  
R.O.Size: 4040/840 mm  
Colour: Anthracite  
Nr. of leaves: 4  
Total Piece: 1  
Hinge Side: Fixed/sliding  
Sill Height (from top of slab): 1850 mm

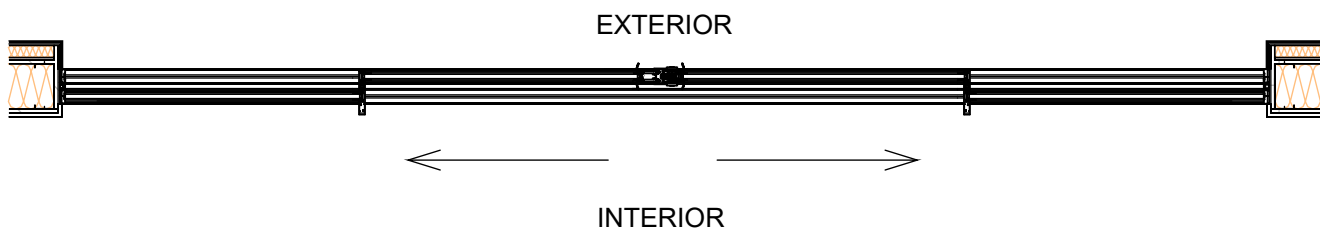

1. THESE DRAWINGS MUST BE CHECKED BY THE CUSTOMER OR CONTRACTOR PRIOR TO APPROVAL. ANY ERRORS OR OMISSIONS MUST BE REPORTED IN WRITING TO BAUHU PRIOR TO COMMENCEMENT OF CONSTRUCTION.
2. ARCHITECTURAL DRAWINGS SHOULD BE READ IN CONJUNCTION WITH STRUCTURAL DETAILING AND FABRICATION GENERAL ASSEMBLY DRAWINGS.
3. FOR CONSTRUCTION PURPOSES, USE ONLY THE LATEST APPROVED DRAWINGS LABELED 'ISSUED FOR CONSTRUCTION'.
4. DO NOT SCALE FROM THIS DRAWING.
5. THE COMPANY OPERATES USING METRIC DIMENSIONS AS THE PRINCIPAL DENOMINATION.
6. ALL CONCRETE WORKS ARE OUTSIDE OF THE SCOPE OF THE COMPANY. INFORMATION REGARDING SLAB DESIGN AND CONNECTIONS IN THESE DRAWINGS ARE INTENDED FOR GUIDENCE ONLY. FOUNDATION AND SLAB WORKS SHOULD BE DESIGNED AND APPROVED BY A LOCAL STRUCTURAL ENGINEER.
7. THE COMPANY RETAINS FULL TITLE AND OWNERSHIP OF THESE PLANS AND DESIGNS. ANY UNAUTHORISED USE, REPRODUCTION, OR DISTRIBUTION OF THESE PLANS, WHETHER IN WHOLE OR PART, IS EXPRESSLY PROHIBITED WITHOUT PRIOR WRITTEN CONSENT.

| No. | Revision | Date |
|-----|----------|------|
|     |          |      |
|     |          |      |
ISSUED FOR:

Issued for information

Issued for client approval

Issued for fabrication

Issued for construction

Firefly

DRAWING TITLE:

Opening Schedule 2

DRAWN BY:

Mladin Monica-Mihaela

SCALE:

As indicated

DRAWING NO:


A12

DATE:

04.03.2024



W05

Type: Cor Vision  
Size: 6400/2600 mm  
R.O.Size: 6440/2690 mm  
Colour: Anthracite  
Nr. of leaves: 4  
Total Piece: 2  
Hinge Side: Sliding  
Sill Height (from top of slab): 70 mm

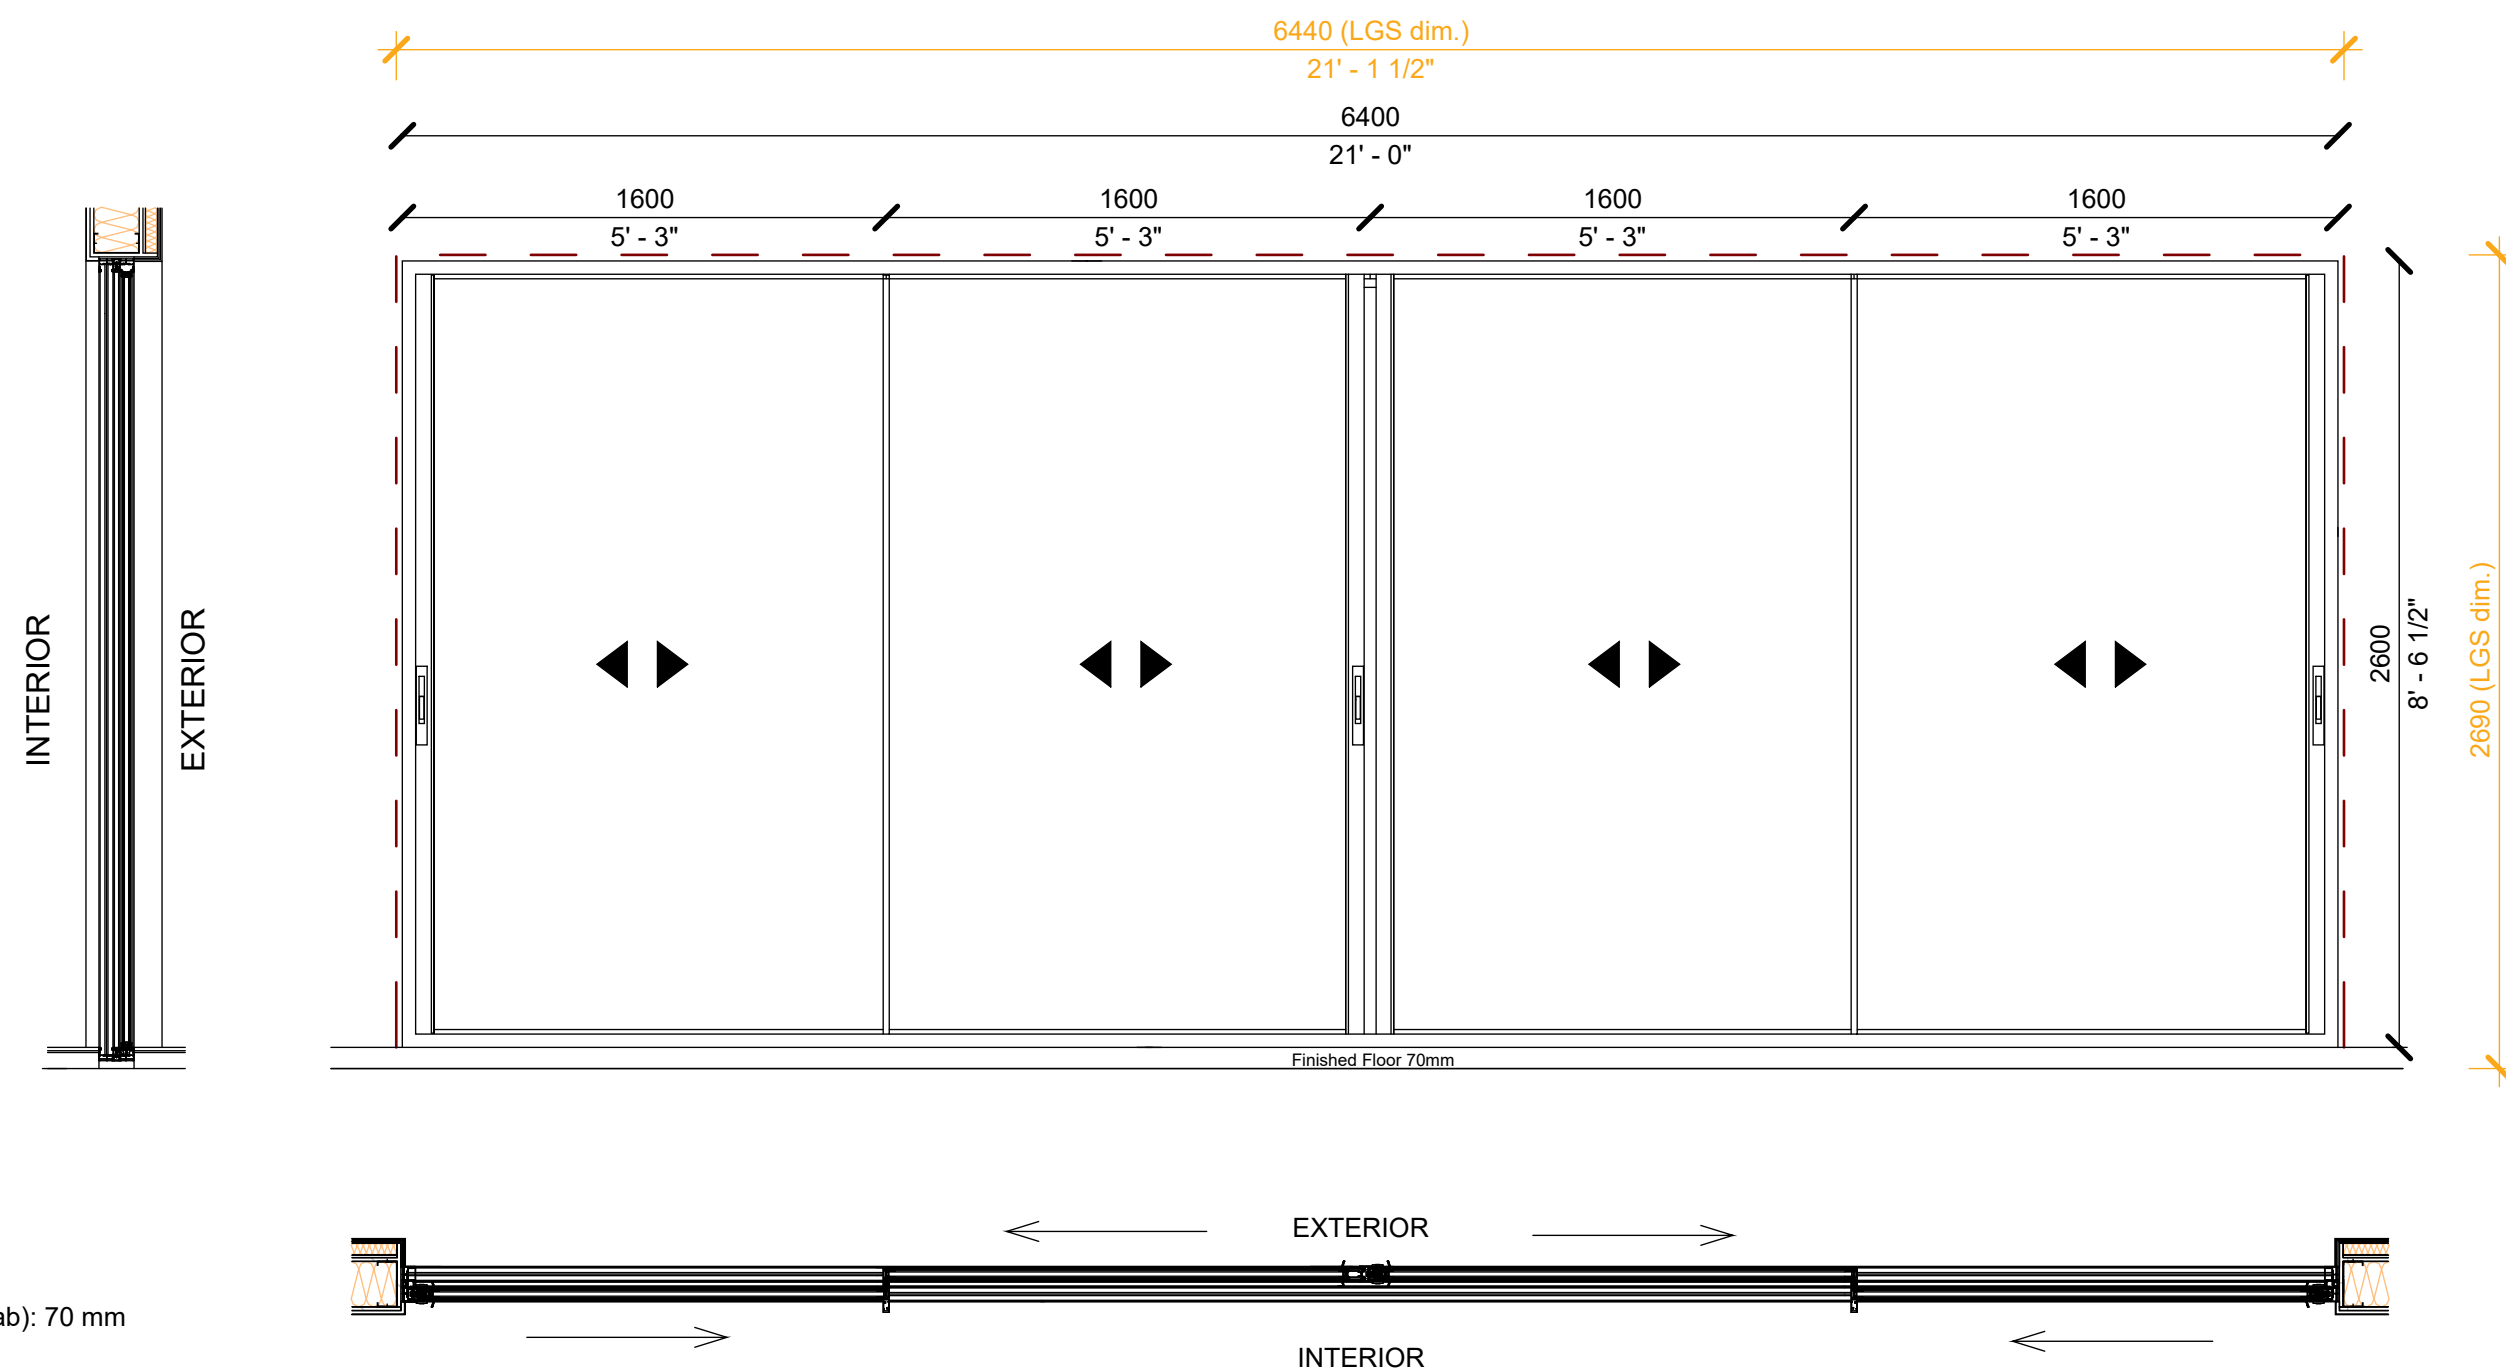



D01

Type: Exterior casement door  
Size: 800/2600 mm  
R.O. Size: 843/2690  
Colour: -  
Number of Leaves: 1  
Total Piece: 1 pcs  
Hinge Side: right  
Lock: yes  
Sill Height (from top of slab): 70 mm

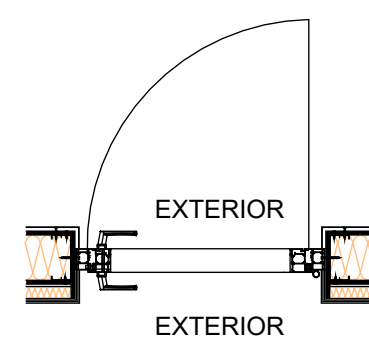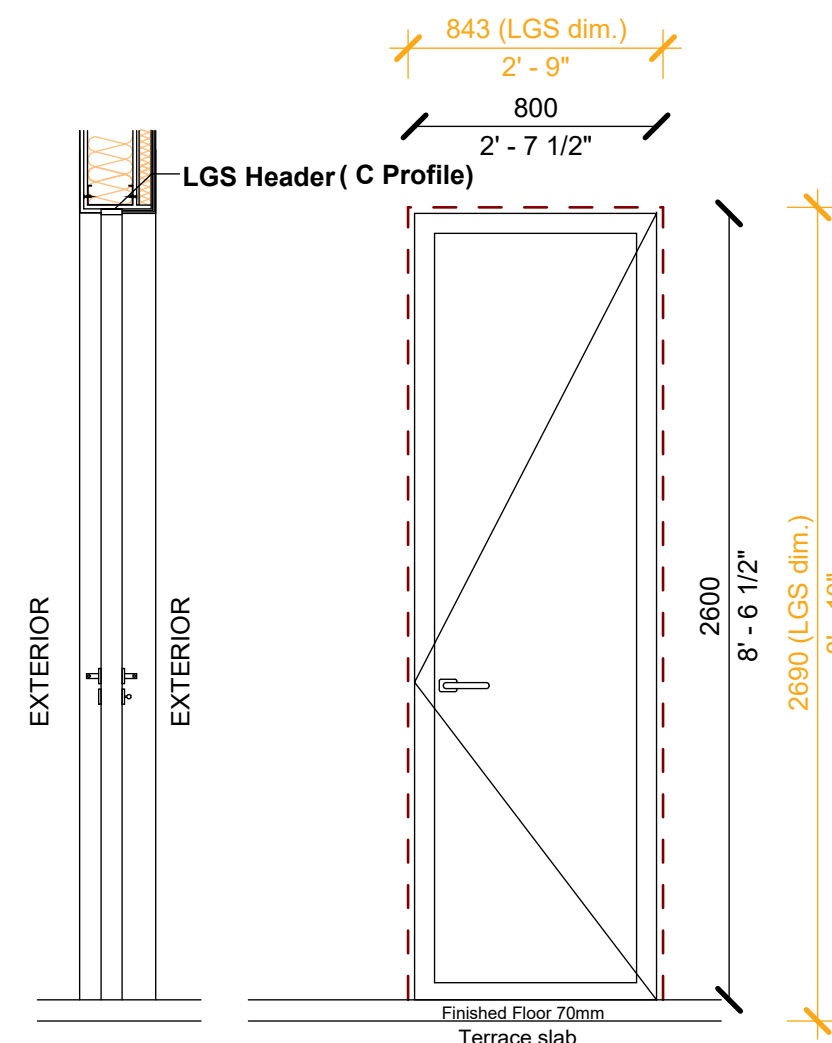

D02

Type: Interior casement door  
Size: 800/2500 mm  
R.O. Size: 843/2590  
Colour: -  
Number of Leaves: 1  
Total Piece: 3 pcs  
Hinge Side: 1pcs right / 2pcs left  
Lock: yes  
Sill Height (from top of slab): 70 mm

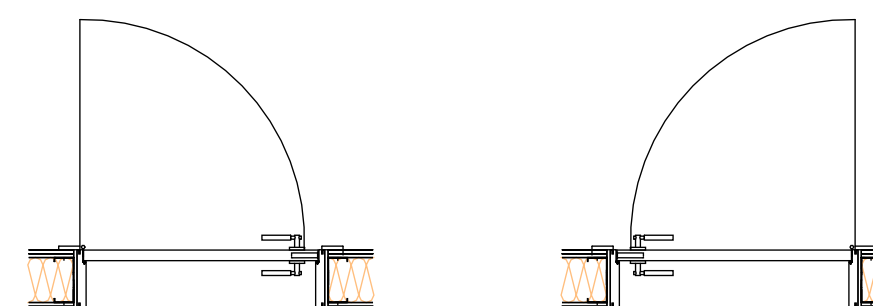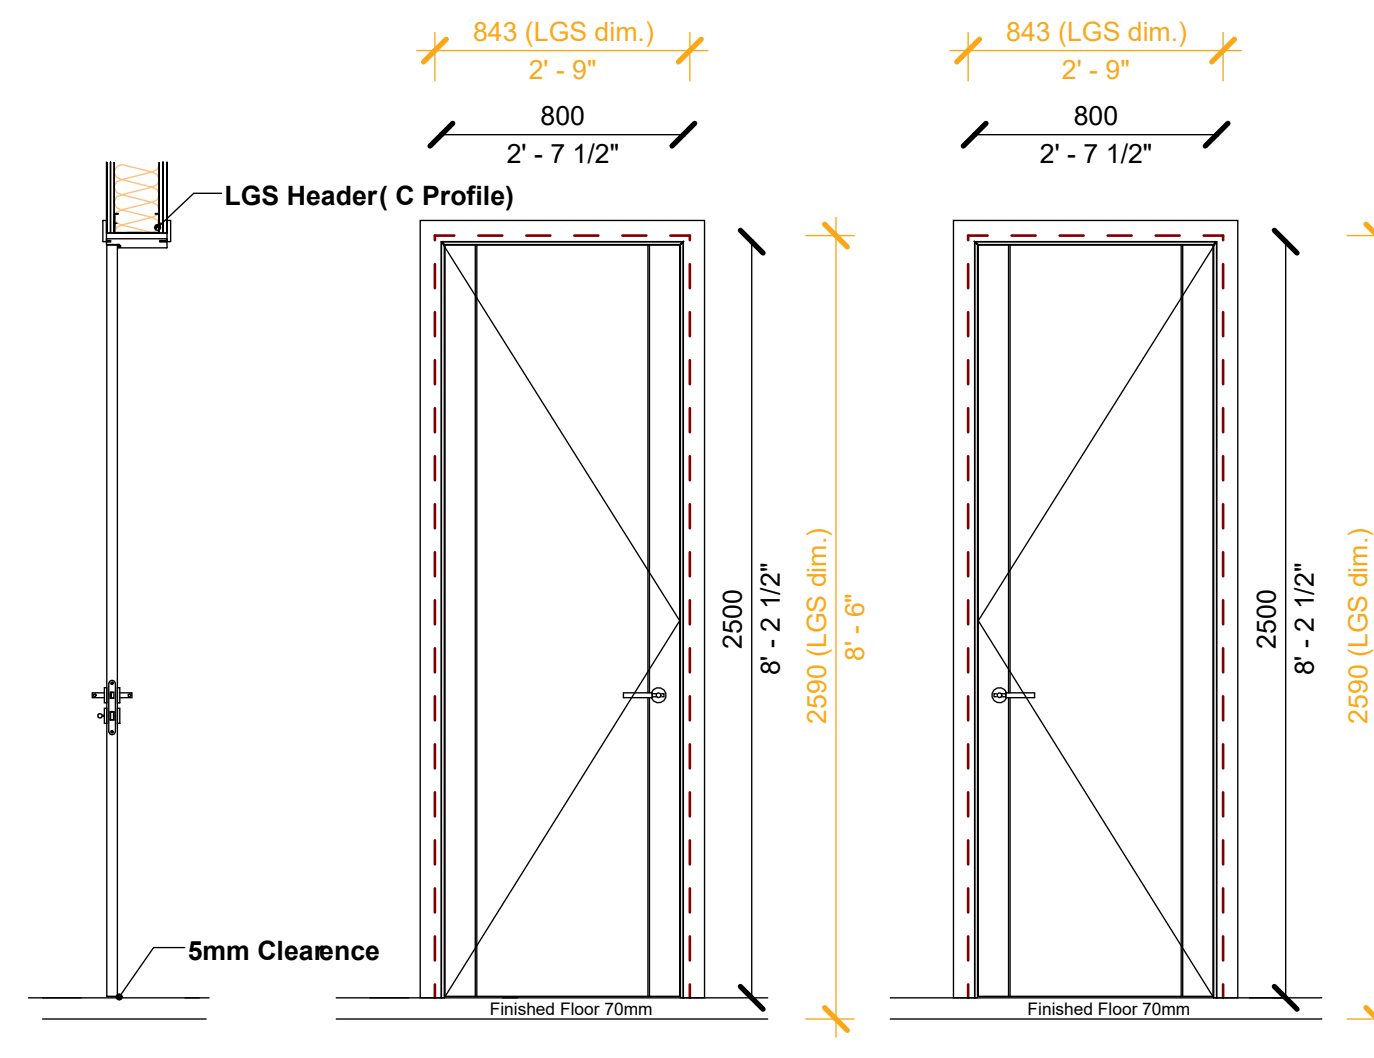

1. THESE DRAWINGS MUST BE CHECKED BY THE CUSTOMER OR CONTRACTOR PRIOR TO APPROVAL. ANY ERRORS OR OMISSIONS MUST BE REPORTED IN WRITING TO BAUHU PRIOR TO COMMENCEMENT OF CONSTRUCTION.
2. ARCHITECTURAL DRAWINGS SHOULD BE READ IN CONJUNCTION WITH STRUCTURAL DETAILING AND FABRICATION GENERAL ASSEMBLY DRAWINGS.
3. FOR CONSTRUCTION PURPOSES, USE ONLY THE LATEST APPROVED DRAWINGS LABELED 'ISSUED FOR CONSTRUCTION'.
4. DO NOT SCALE FROM THIS DRAWING.
5. THE COMPANY OPERATES USING METRIC DIMENSIONS AS THE PRINCIPAL DENOMINATION.
6. ALL CONCRETE WORKS ARE OUTSIDE OF THE SCOPE OF THE COMPANY. INFORMATION REGARDING SLAB DESIGN AND CONNECTIONS IN THESE DRAWINGS ARE INTENDED FOR GUIDENCE ONLY. FOUNDATION AND SLAB WORKS SHOULD BE DESIGNED AND APPROVED BY A LOCAL STRUCTURAL ENGINEER.
7. THE COMPANY RETAINS FULL TITLE AND OWNERSHIP OF THESE PLANS AND DESIGNS. ANY UNAUTHORISED USE, REPRODUCTION, OR DISTRIBUTION OF THESE PLANS, WHETHER IN WHOLE OR PART, IS EXPRESSLY PROHIBITED WITHOUT PRIOR WRITTEN CONSENT.

| No. | Revision | Date |
|-----|----------|------|
|     |          |      |
|     |          |      |
ISSUED FOR:

Issued for information

Issued for client approval

Issued for fabrication

Issued for construction

Firefly

DRAWING TITLE:

Room Legend

DRAWN BY:

Mladin Monica-Mihaela

SCALE:

1 : 70

DRAWING NO:


A13

DATE:

04.03.2024

## Room Legend


- Bedroom 1
- Bedroom 2
- Carport
- En-Suite Bathroom 1
- En-Suite Bathroom 2
- Living Room and Kitchen
- Master Bedroom
- Master En-Suite Bathroom
- Outdoor covered Terrace
- Pool Terrace Area

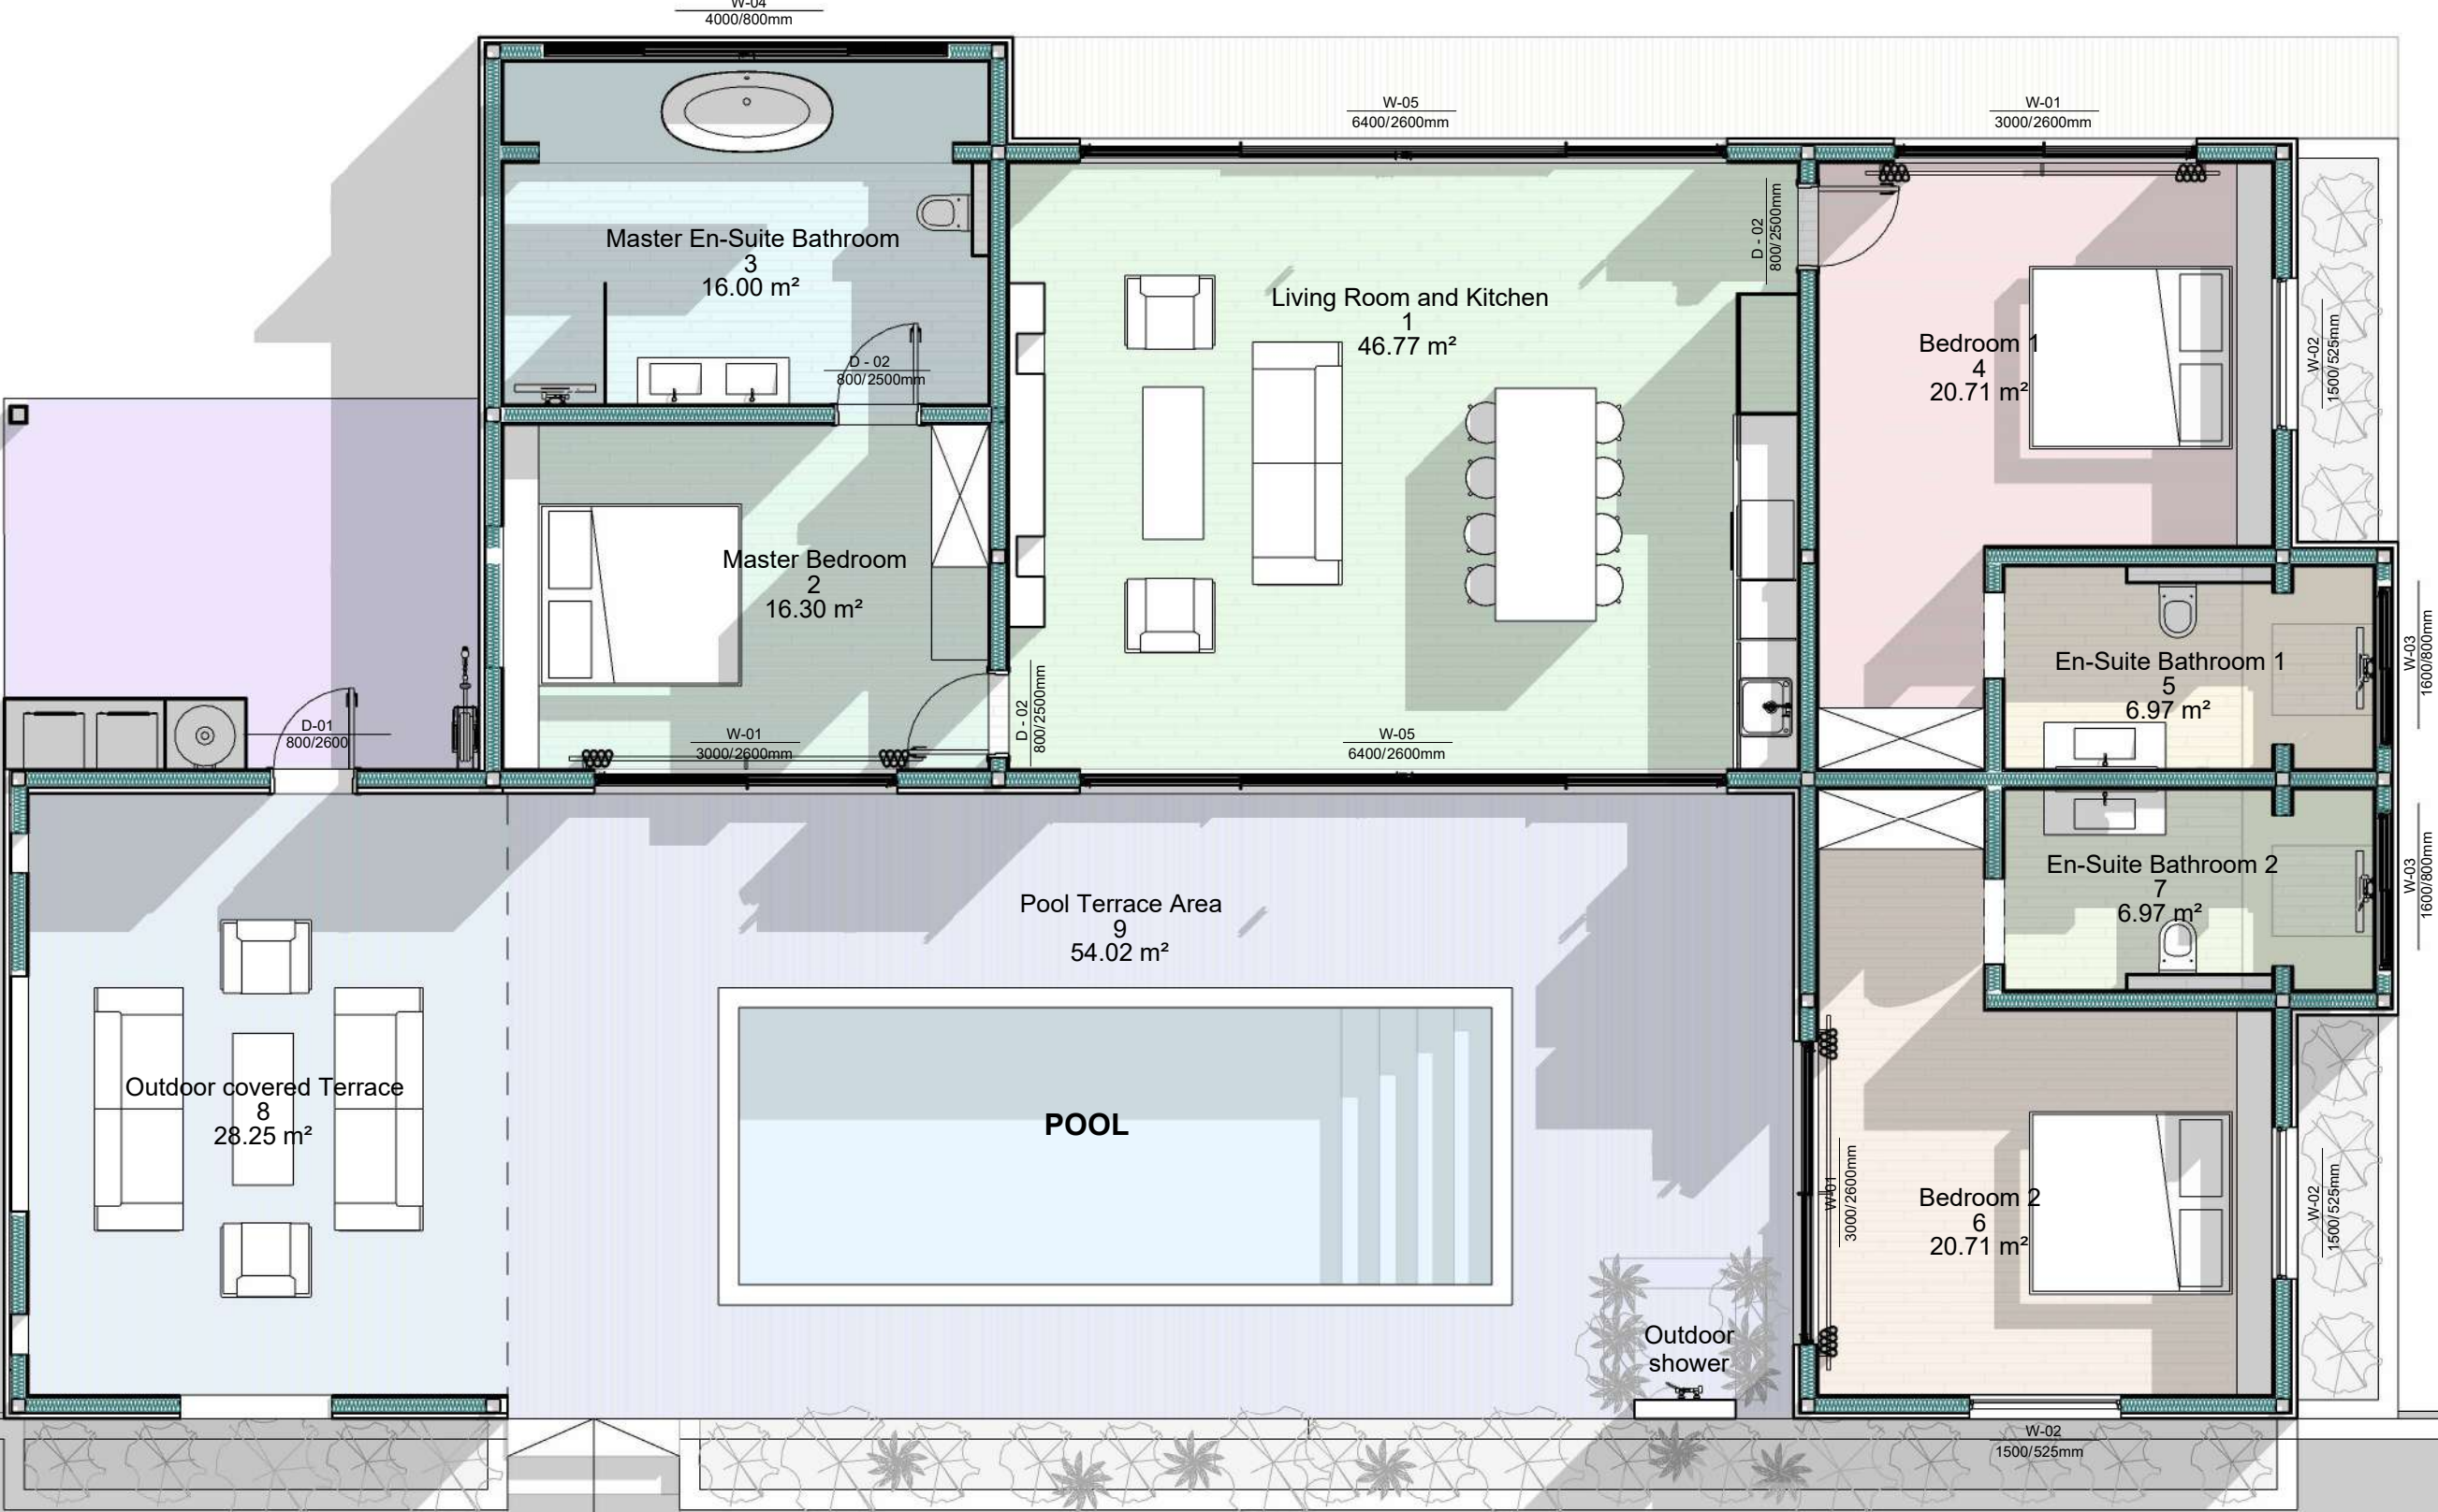

## Finishes Schedule

| No.          | Room Name                | Floor Area | Room Perimeter | Floor Finish (tiles and grout colour) | Ceiling Colour | Wall Colour |
|--------------|--------------------------|------------|----------------|---------------------------------------|----------------|-------------|
| Ground Floor |                          |            |                |                                       |                |             |
| 1            | Living Room and Kitchen  | 46.77 m²   | 27592          |                                       |                |             |
| 2            | Master Bedroom           | 16.30 m²   | 16392          |                                       |                |             |
| 3            | Master En-Suite Bathroom | 16.00 m²   | 20190          |                                       |                |             |
| 4            | Bedroom 1                | 20.71 m²   | 20992          |                                       |                |             |
| 5            | En-Suite Bathroom 1      | 6.97 m²    | 12095          |                                       |                |             |
| 6            | Bedroom 2                | 20.71 m²   | 20992          |                                       |                |             |
| 7            | En-Suite Bathroom 2      | 6.97 m²    | 12137          |                                       |                |             |
| 8            | Outdoor covered Terrace  | 28.25 m²   | 21398          |                                       |                |             |
| 9            | Pool Terrace Area        | 54.02 m²   | 38226          |                                       |                |             |
| 10           | Carport                  | 15.46 m²   | 15955          |                                       |                |             |
| Grand total  |                          | 232.16 m²  | 205969         |                                       |                |             |

Building Footprint: 157.542 Sqm , 1695.766 Sq feet  
Outdoor Covered Terrace: 28.25 Sqm, 304.080 Sq feet  
Pool Terrace Area: 54.02 Sqm, 581.466 Sq feet  
Carport: 15.46 Sqm, 166.410 Sq feet  
Pool Area: 24.60 Sqm, 264.792 Sq feet  
Total construction footprint: 279.872 Sqm, 3012.514 Sq feet

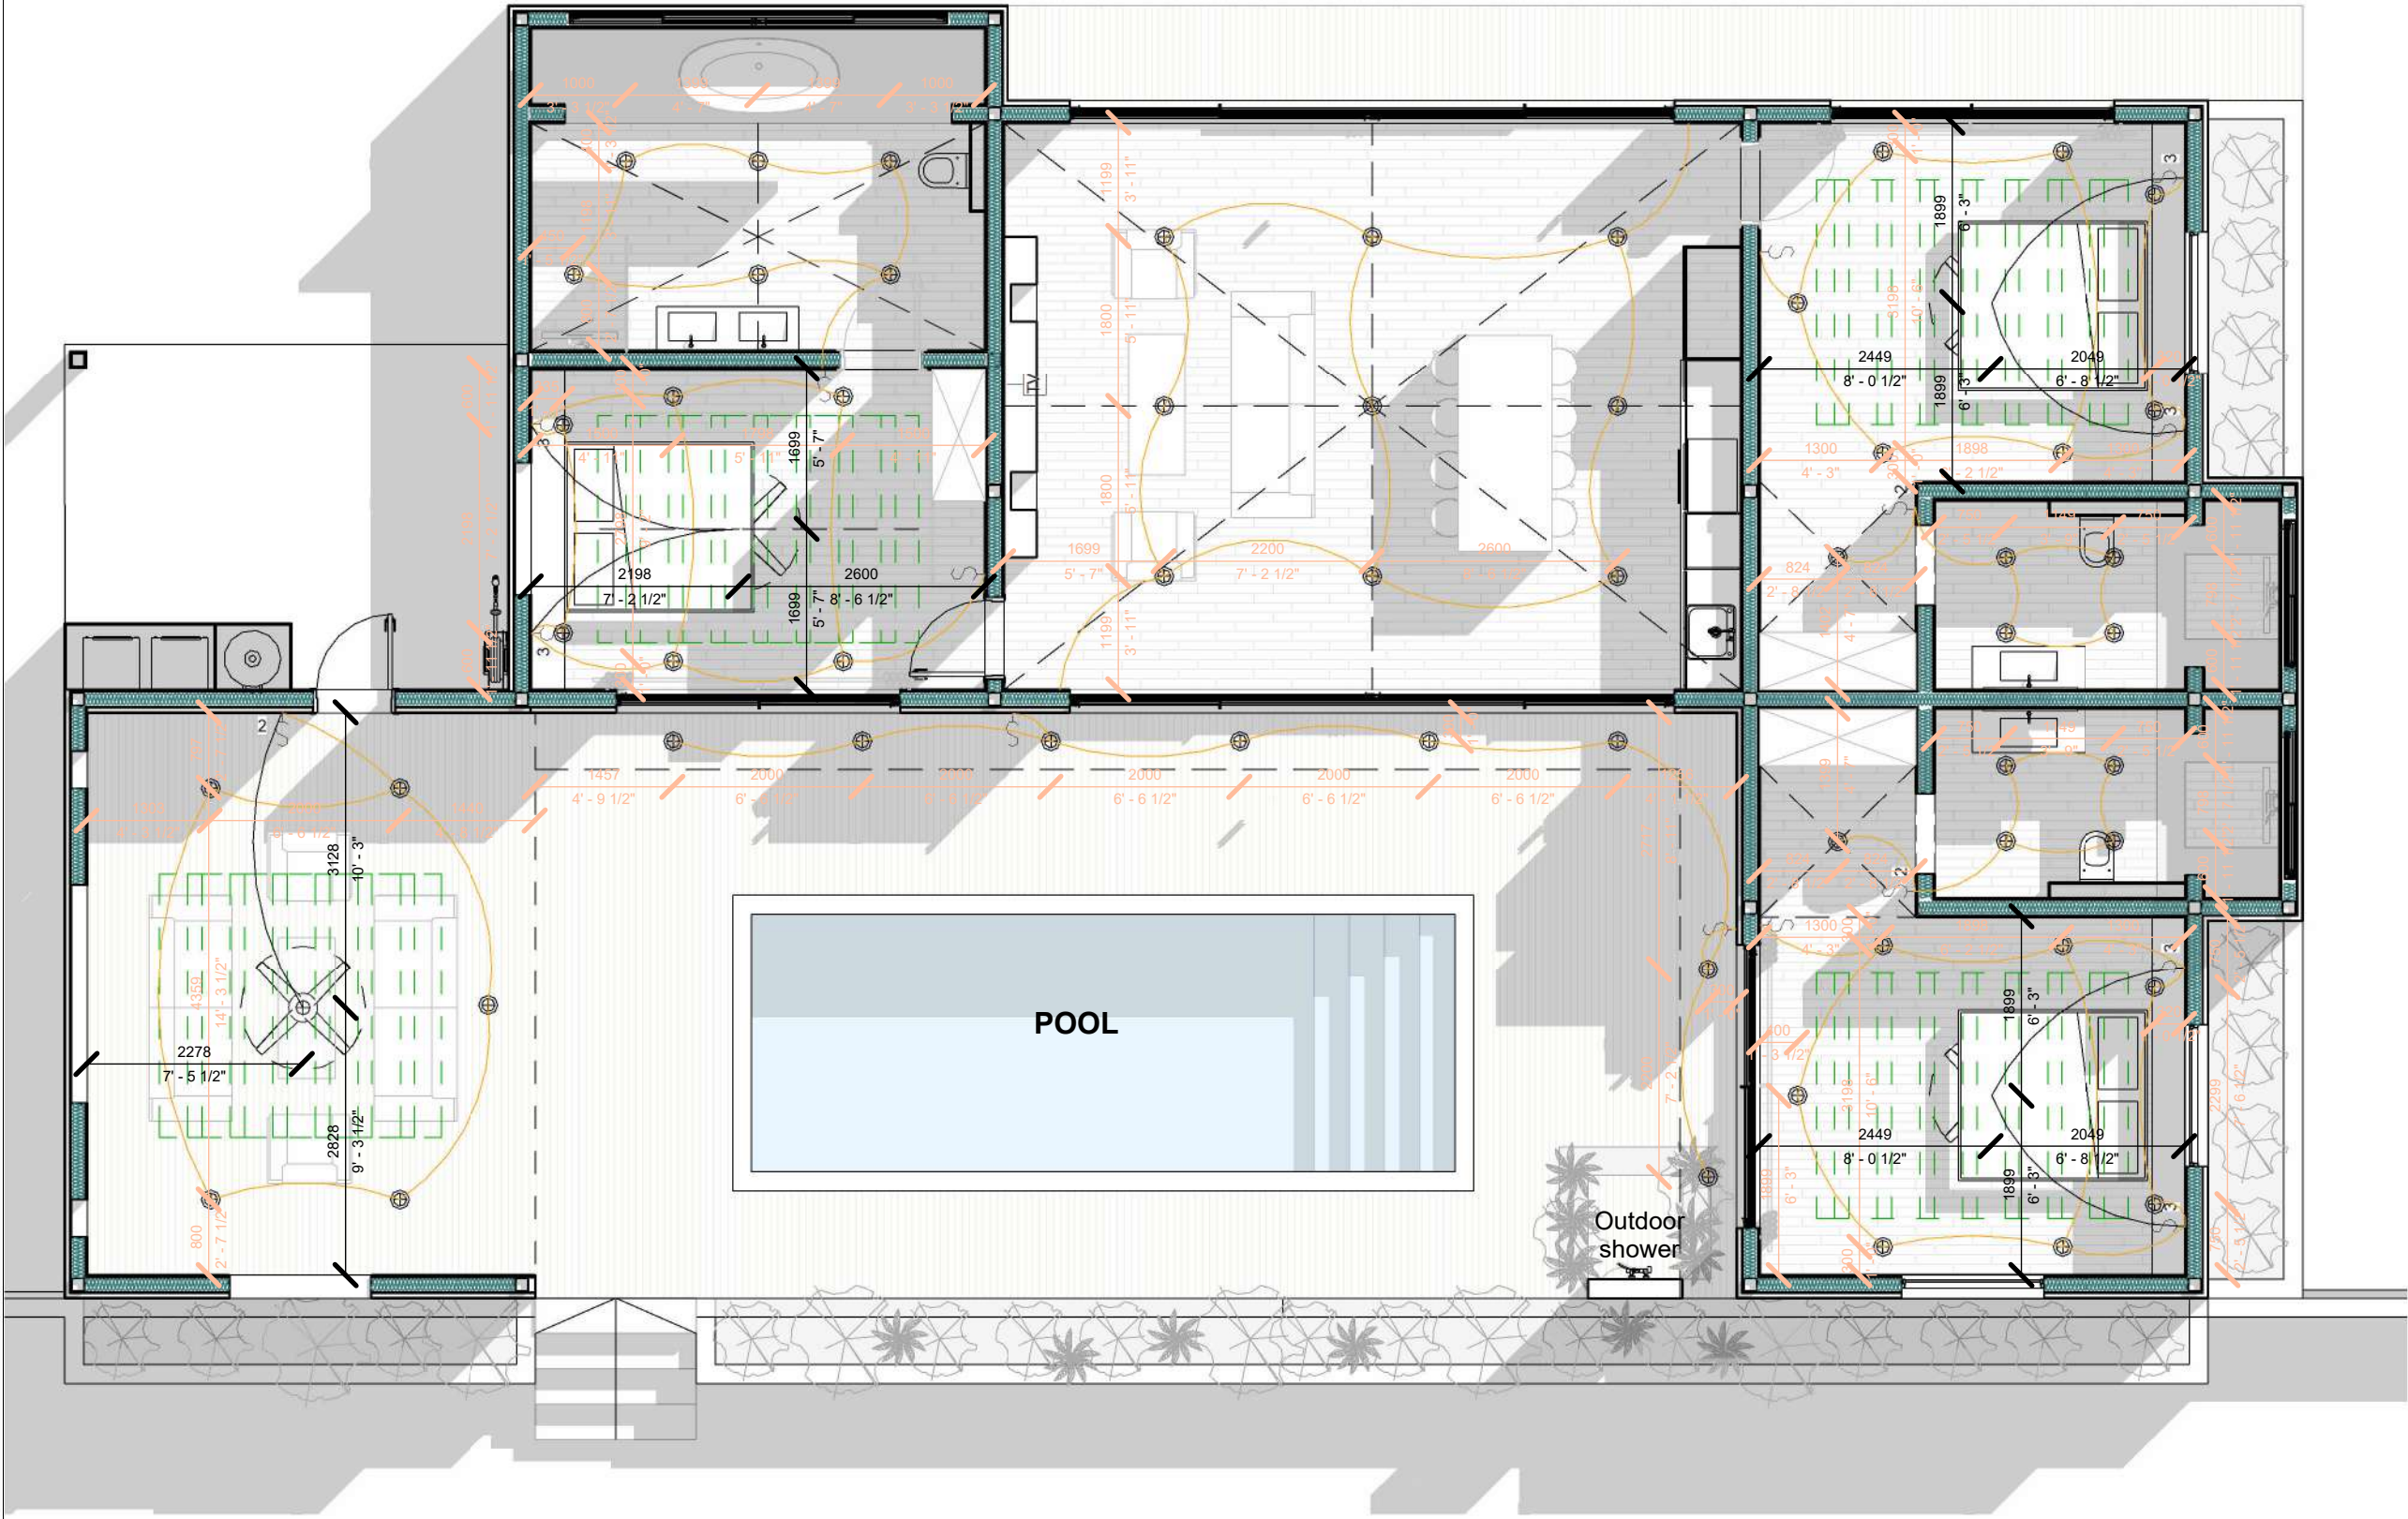

Panel "A"

120/240 1 60h 3W

| CKT. NO. | IDENTIFICATION                      | CIRCUIT BREAKER |      |     |
|----------|-------------------------------------|-----------------|------|-----|
|          |                                     | BKR.            | WIRE | KW. |
| 1        | General Lightning and Receptacles   | 15 A.           | # 14 |     |
| 2        | General Lightning and Receptacles   | 15 A.           | # 14 |     |
| 3        | General Lightning and Receptacles   | 15 A.           | # 14 |     |
| 4        | General Lightning and Receptacles   | 15 A.           | # 14 |     |
| 5        | General Lightning and Receptacles   | 15 A.           | # 14 |     |
| 6        | GFI Receptacles                     | 20 A.           | # 12 |     |
| 7        | General Lightning and Receptacles   | 15 A.           | # 14 |     |
| 8        | Kitchen Small Appliance Receptacles | 20 A.           | # 12 |     |
| 9        | Kitchen Small Appliance Receptacles | 20 A.           | # 12 | 1.5 |
| 10       | Garbage Disposer                    | 20 A.           | # 12 | 1.2 |
| 11       | Outdoor Lightning and Receptacles   | 20 A.           | # 12 | 1.5 |
| 12       | Dishwasher                          | 20 A.           | # 12 | 1.2 |
| 13       | Refrigerator                        | 20 A.           | # 12 | 1.2 |
| 14       | Microwave                           | 20 A.           | # 12 |     |
| 15       | Range/Oven                          | 50 A.           | # 6  | 12  |
| 16       | AC/MSCU #1 (Living Room)            | 30 A.           | # 10 | 3.6 |
| 18       | Water Heater #1                     | 30 A.           | # 10 | 4.5 |
| 19       | AC/MSCU #2 (Dining/Kitchen)         | 30 A.           | # 10 | 3.6 |
| 20       | AC/MSU #3 (Master Bedroom)          | 30 A.           | # 10 | 3.6 |
| 21       | AC/MSU #4 (Bedroom 2)               | 30 A.           | # 10 | 3.6 |
| 22       | Spare                               |                 |      |     |
| 23       | AC/MSU #5 (Bedroom 3)               | 30 A.           | # 10 | 3.6 |
| 24       | Spare                               |                 |      |     |
| 25       |                                     |                 |      |     |
| 26       |                                     |                 |      |     |
| 27       |                                     |                 |      |     |
| 28       |                                     |                 |      |     |
| 29       |                                     |                 |      |     |

- THESE DRAWINGS MUST BE CHECKED BY THE CUSTOMER OR CONTRACTOR PRIOR TO APPROVAL. ANY ERRORS OR OMISSIONS MUST BE REPORTED IN WRITING TO BAUHU PRIOR TO COMMENCEMENT OF CONSTRUCTION.
- ARCHITECTURAL DRAWINGS SHOULD BE READ IN CONJUNCTION WITH STRUCTURAL DETAILING AND FABRICATION GENERAL ASSEMBLY DRAWINGS.
- FOR CONSTRUCTION PURPOSES, USE ONLY THE LATEST APPROVED DRAWINGS LABELED 'ISSUED FOR CONSTRUCTION'.
- DO NOT SCALE FROM THIS DRAWING.
- THE COMPANY OPERATES USING METRIC DIMENSIONS AS THE PRINCIPAL DENOMINATION.
- ALL CONCRETE WORKS ARE OUTSIDE OF THE SCOPE OF THE COMPANY. INFORMATION REGARDING SLAB DESIGN AND CONNECTIONS IN THESE DRAWINGS ARE INTENDED FOR GUIDANCE ONLY. FOUNDATION AND SLAB WORKS SHOULD BE DESIGNED AND APPROVED BY A LOCAL STRUCTURAL ENGINEER.
- THE COMPANY RETAINS FULL TITLE AND OWNERSHIP OF THESE PLANS AND DESIGNS. ANY UNAUTHORISED USE, REPRODUCTION, OR DISTRIBUTION OF THESE PLANS, WHETHER IN WHOLE OR PART, IS EXPRESSLY PROHIBITED WITHOUT PRIOR WRITTEN CONSENT.

| No. | Revision | Date |
|-----|----------|------|
|     |          |      |
|     |          |      |
ISSUED FOR:

Issued for information

Issued for client approval

Issued for fabrication

Issued for construction


Firefly

Double Switch

- Bell
- Television Outlet
- Duplex Outlet
- Single Switch
- Double Switch
- Three Way Switch
- Outlet Fixed Kitchen Equipment

Note:  
• Electrical engineer to provide adequate grounding to all steel members.

Panel "B" Feeder  
(3) #3 CU W/  
(1) #8 CU GND. In 2" C.

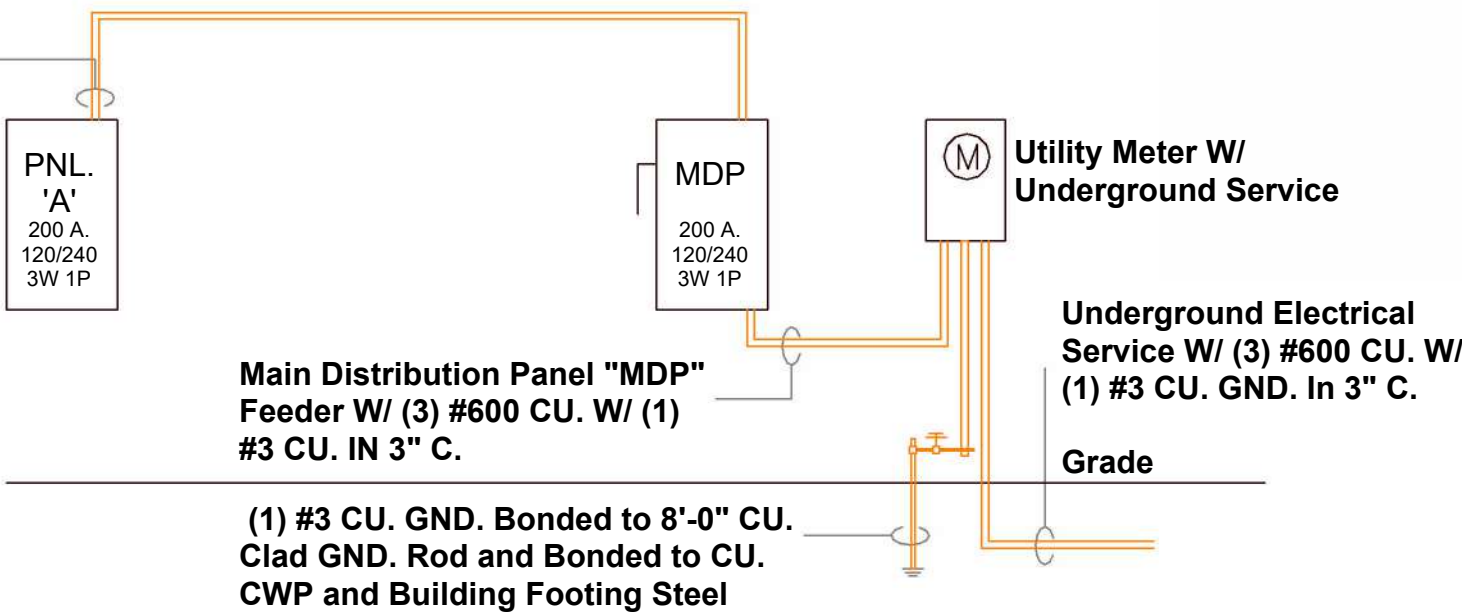

Typical Service Riser

DRAWING TITLE:

Electrical Plan 1

DRAWN BY:

Mladin Monica-Mihaela

SCALE:


As indicated

DRAWING NO:

A14

DATE:

04.03.2024

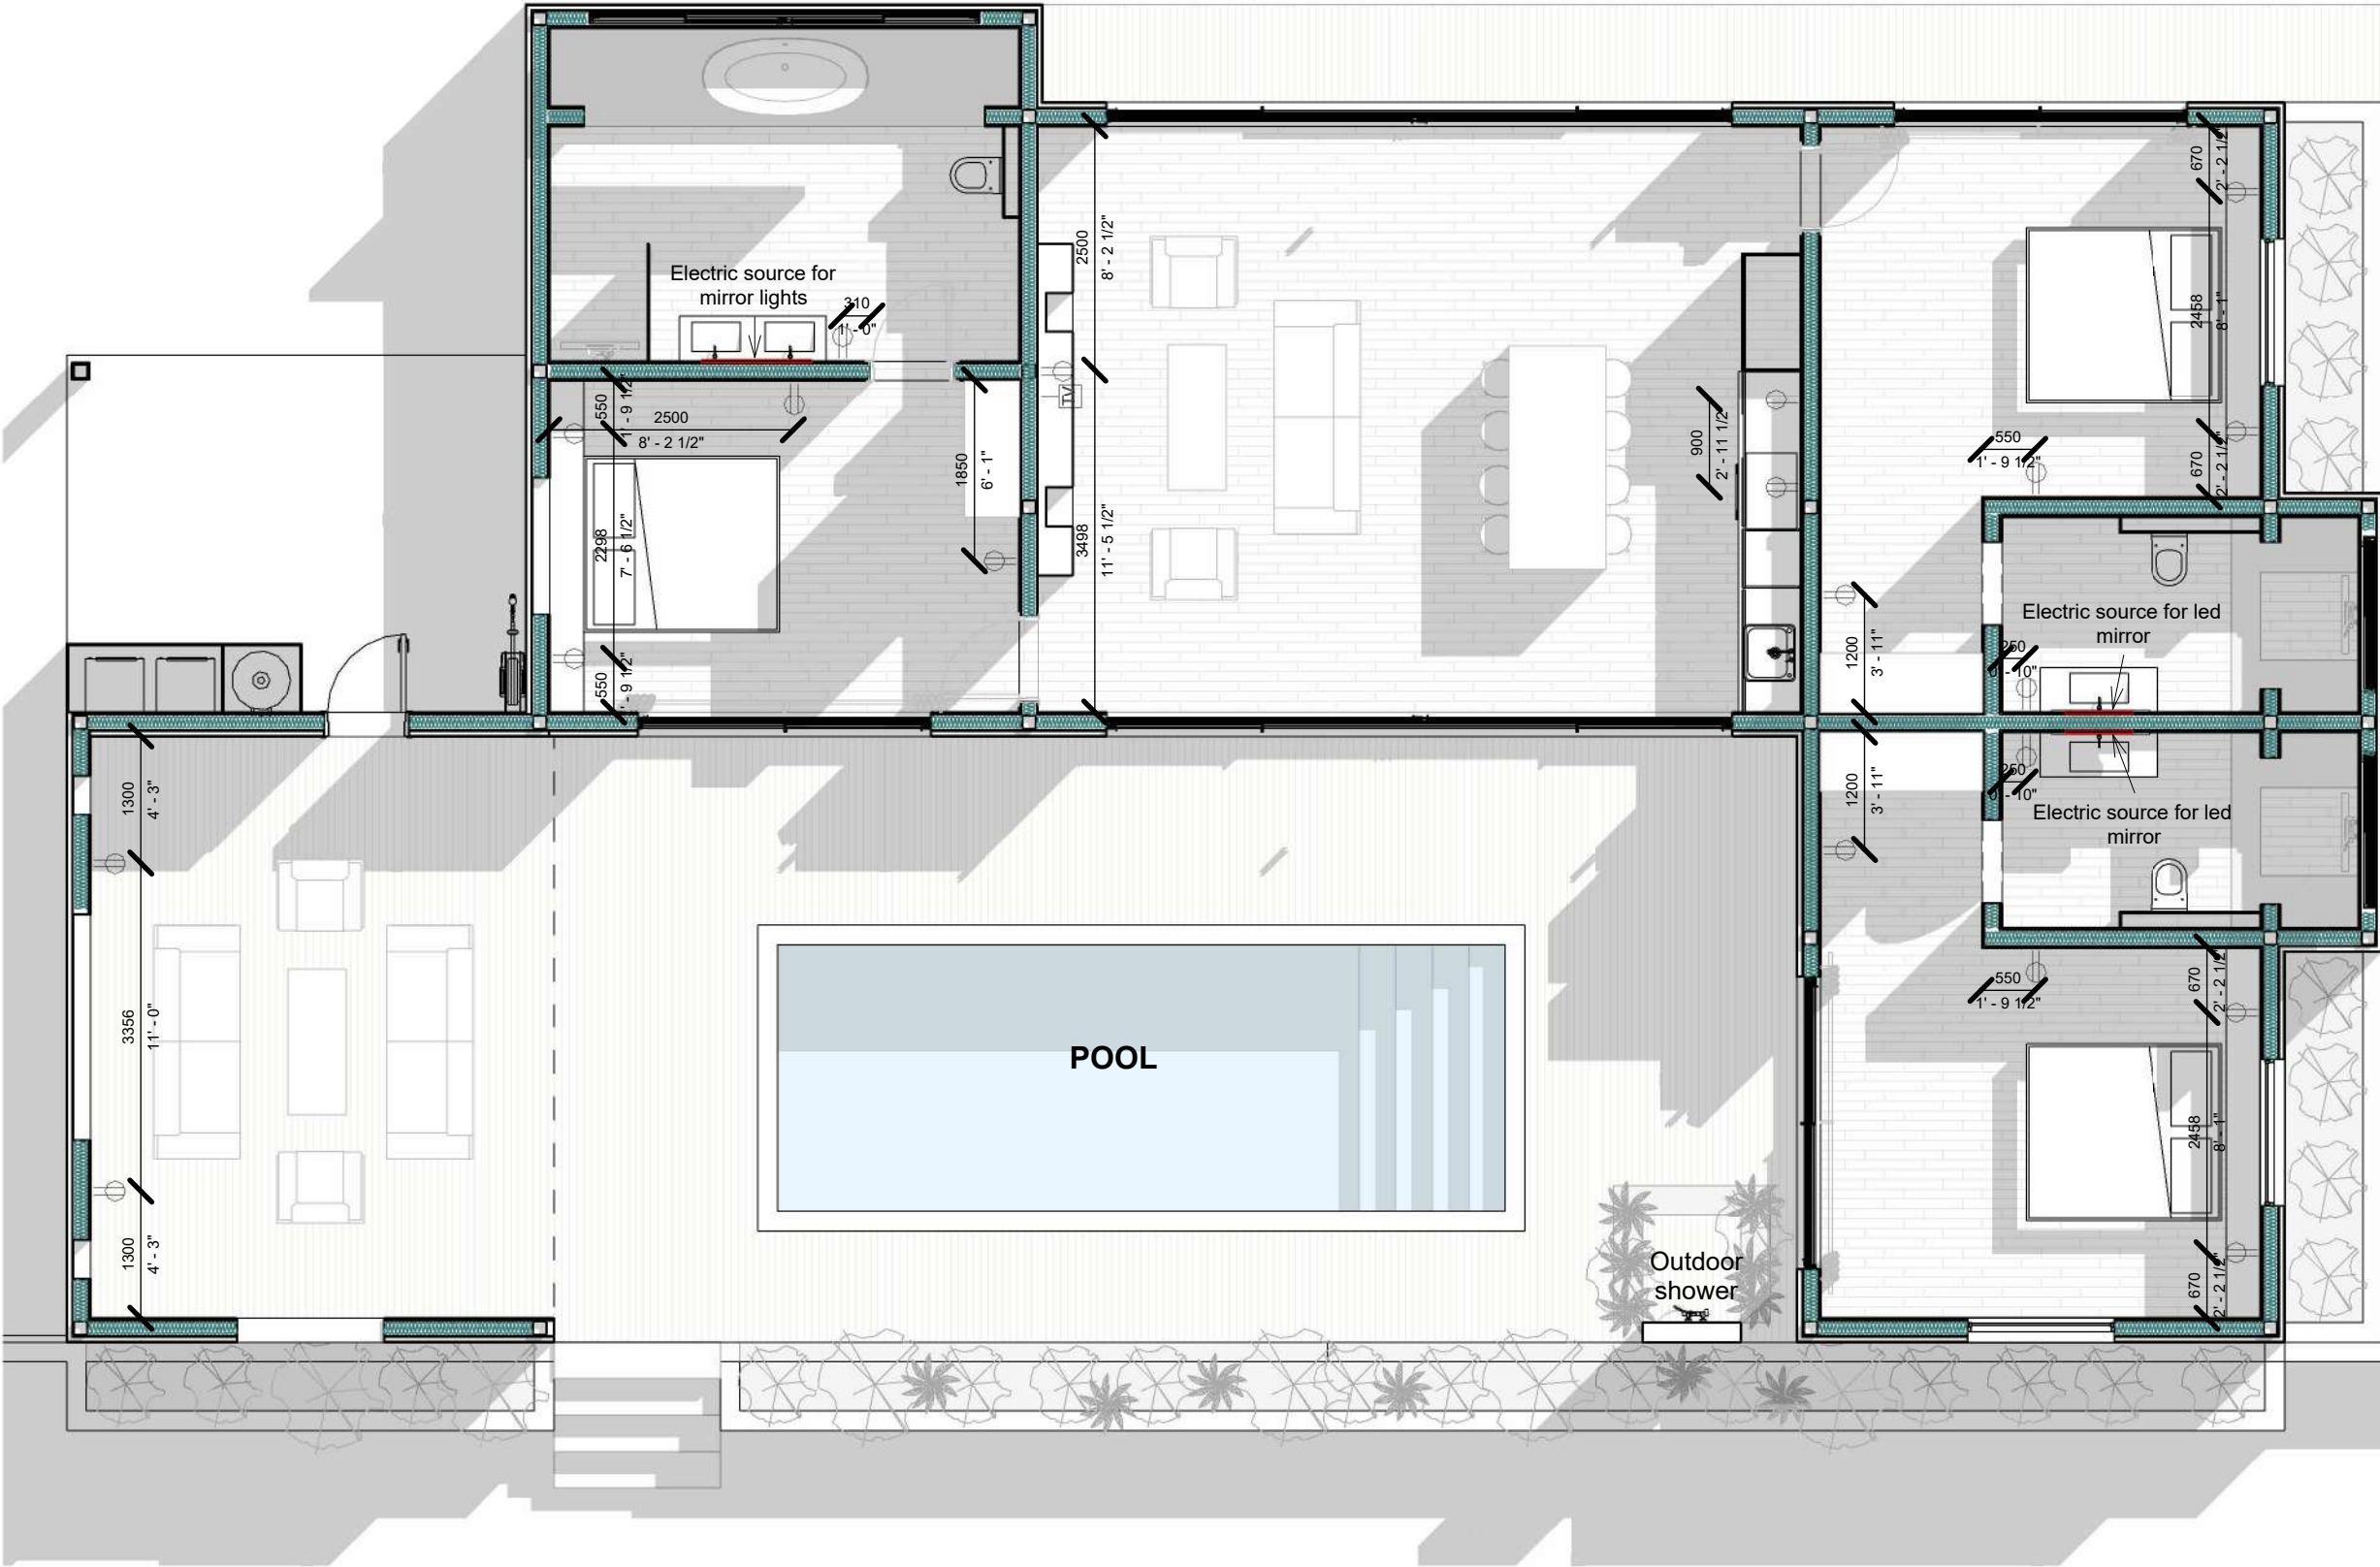

Panel "A"

120/240 1 60h 3W

| CKT. NO. | IDENTIFICATION                      | CIRCUIT BREAKER |      |     |
|----------|-------------------------------------|-----------------|------|-----|
|          |                                     | BKR.            | WIRE | KW. |
| 1        | General Lightning and Receptacles   | 15 A.           | # 14 |     |
| 2        | General Lightning and Receptacles   | 15 A.           | # 14 |     |
| 3        | General Lightning and Receptacles   | 15 A.           | # 14 |     |
| 4        | General Lightning and Receptacles   | 15 A.           | # 14 |     |
| 5        | General Lightning and Receptacles   | 15 A.           | # 14 |     |
| 6        | GFI Receptacles                     | 20 A.           | # 12 |     |
| 7        | General Lightning and Receptacles   | 15 A.           | # 14 |     |
| 8        | Kitchen Small Appliance Receptacles | 20 A.           | # 12 |     |
| 9        | Kitchen Small Appliance Receptacles | 20 A.           | # 12 | 1.5 |
| 10       | Garbage Disposer                    | 20 A.           | # 12 | 1.2 |
| 11       | Outdoor Lightning and Receptacles   | 20 A.           | # 12 | 1.5 |
| 12       | Dishwasher                          | 20 A.           | # 12 | 1.2 |
| 13       | Refrigerator                        | 20 A.           | # 12 | 1.2 |
| 14       | Microwave                           | 20 A.           | # 12 |     |
| 15       | Range/Oven                          | 50 A.           | # 6  | 12  |
| 16       | AC/MSCU #1 (Living Room)            | 30 A.           | # 10 | 3.6 |
| 18       |                                     |                 |      |     |
| 19       |                                     |                 |      |     |
| 21       | Water Heater #1                     | 30 A.           | # 10 | 4.5 |
| 20       | AC/MSCU #2 (Dining/Kitchen)         | 30 A.           | # 10 | 3.6 |
| 22       |                                     |                 |      |     |
| 23       | AC/MSU #3 (Master Bedroom)          | 30 A.           | # 10 | 3.6 |
| 25       |                                     |                 |      |     |
| 24       | AC/MSU #4 (Bedroom 2)               | 30 A.           | # 10 | 3.6 |
| 26       |                                     |                 |      |     |
| 27       | Spare                               |                 |      |     |
| 28       | AC/MSU #5 (Bedroom 3)               | 30 A.           | # 10 | 3.6 |
| 30       |                                     |                 |      |     |
| 29       |                                     |                 |      |     |

- THESE DRAWINGS MUST BE CHECKED BY THE CUSTOMER OR CONTRACTOR PRIOR TO APPROVAL. ANY ERRORS OR OMISSIONS MUST BE REPORTED IN WRITING TO BAUHU PRIOR TO COMMENCEMENT OF CONSTRUCTION.
- ARCHITECTURAL DRAWINGS SHOULD BE READ IN CONJUNCTION WITH STRUCTURAL DETAILING AND FABRICATION GENERAL ASSEMBLY DRAWINGS.
- FOR CONSTRUCTION PURPOSES, USE ONLY THE LATEST APPROVED DRAWINGS LABELED 'ISSUED FOR CONSTRUCTION'.
- DO NOT SCALE FROM THIS DRAWING.
- THE COMPANY OPERATES USING METRIC DIMENSIONS AS THE PRINCIPAL DENOMINATION.
- ALL CONCRETE WORKS ARE OUTSIDE OF THE SCOPE OF THE COMPANY. INFORMATION REGARDING SLAB DESIGN AND CONNECTIONS IN THESE DRAWINGS ARE INTENDED FOR GUIDENCE ONLY. FOUNDATION AND SLAB WORKS SHOULD BE DESIGNED AND APPROVED BY A LOCAL STRUCTURAL ENGINEER.
- THE COMPANY RETAINS FULL TITLE AND OWNERSHIP OF THESE PLANS AND DESIGNS. ANY UNAUTHORISED USE, REPRODUCTION, OR DISTRIBUTION OF THESE PLANS, WHETHER IN WHOLE OR PART, IS EXPRESSLY PROHIBITED WITHOUT PRIOR WRITTEN CONSENT.

| No. | Revision | Date |
|-----|----------|------|
|     |          |      |
|     |          |      |
ISSUED FOR:

- Issued for information
- Issued for client approval
- Issued for fabrication
- Issued for construction


Firefly

Double Switch

- Bell
- Television Outlet
- Duplex Outlet
- Single Switch
- Double Switch
- Three Way Switch
- Outlet Fixed Kitchen Equipment

- Note:
- Electrical engineer to provide adequate grounding to all steel members.

Panel "B" Feeder  
(3) #3 CU W/  
(1) #8 CU GND. In 2" C.

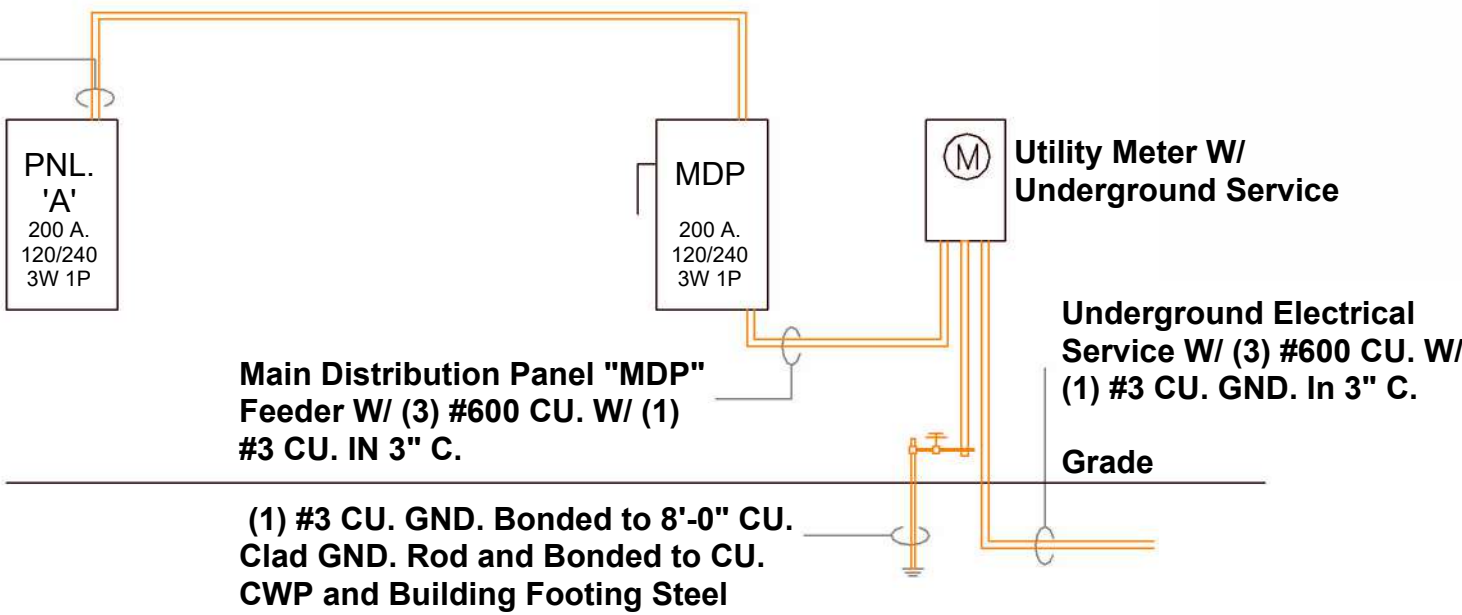

Typical Service Riser

DRAWING TITLE:

Electrical Plan 2

DRAWN BY:

Mladin Monica-Mihaela

SCALE:

As indicated


DRAWING NO:

A15


DATE:

04.03.2024


Typical Plumbing Riser Plan

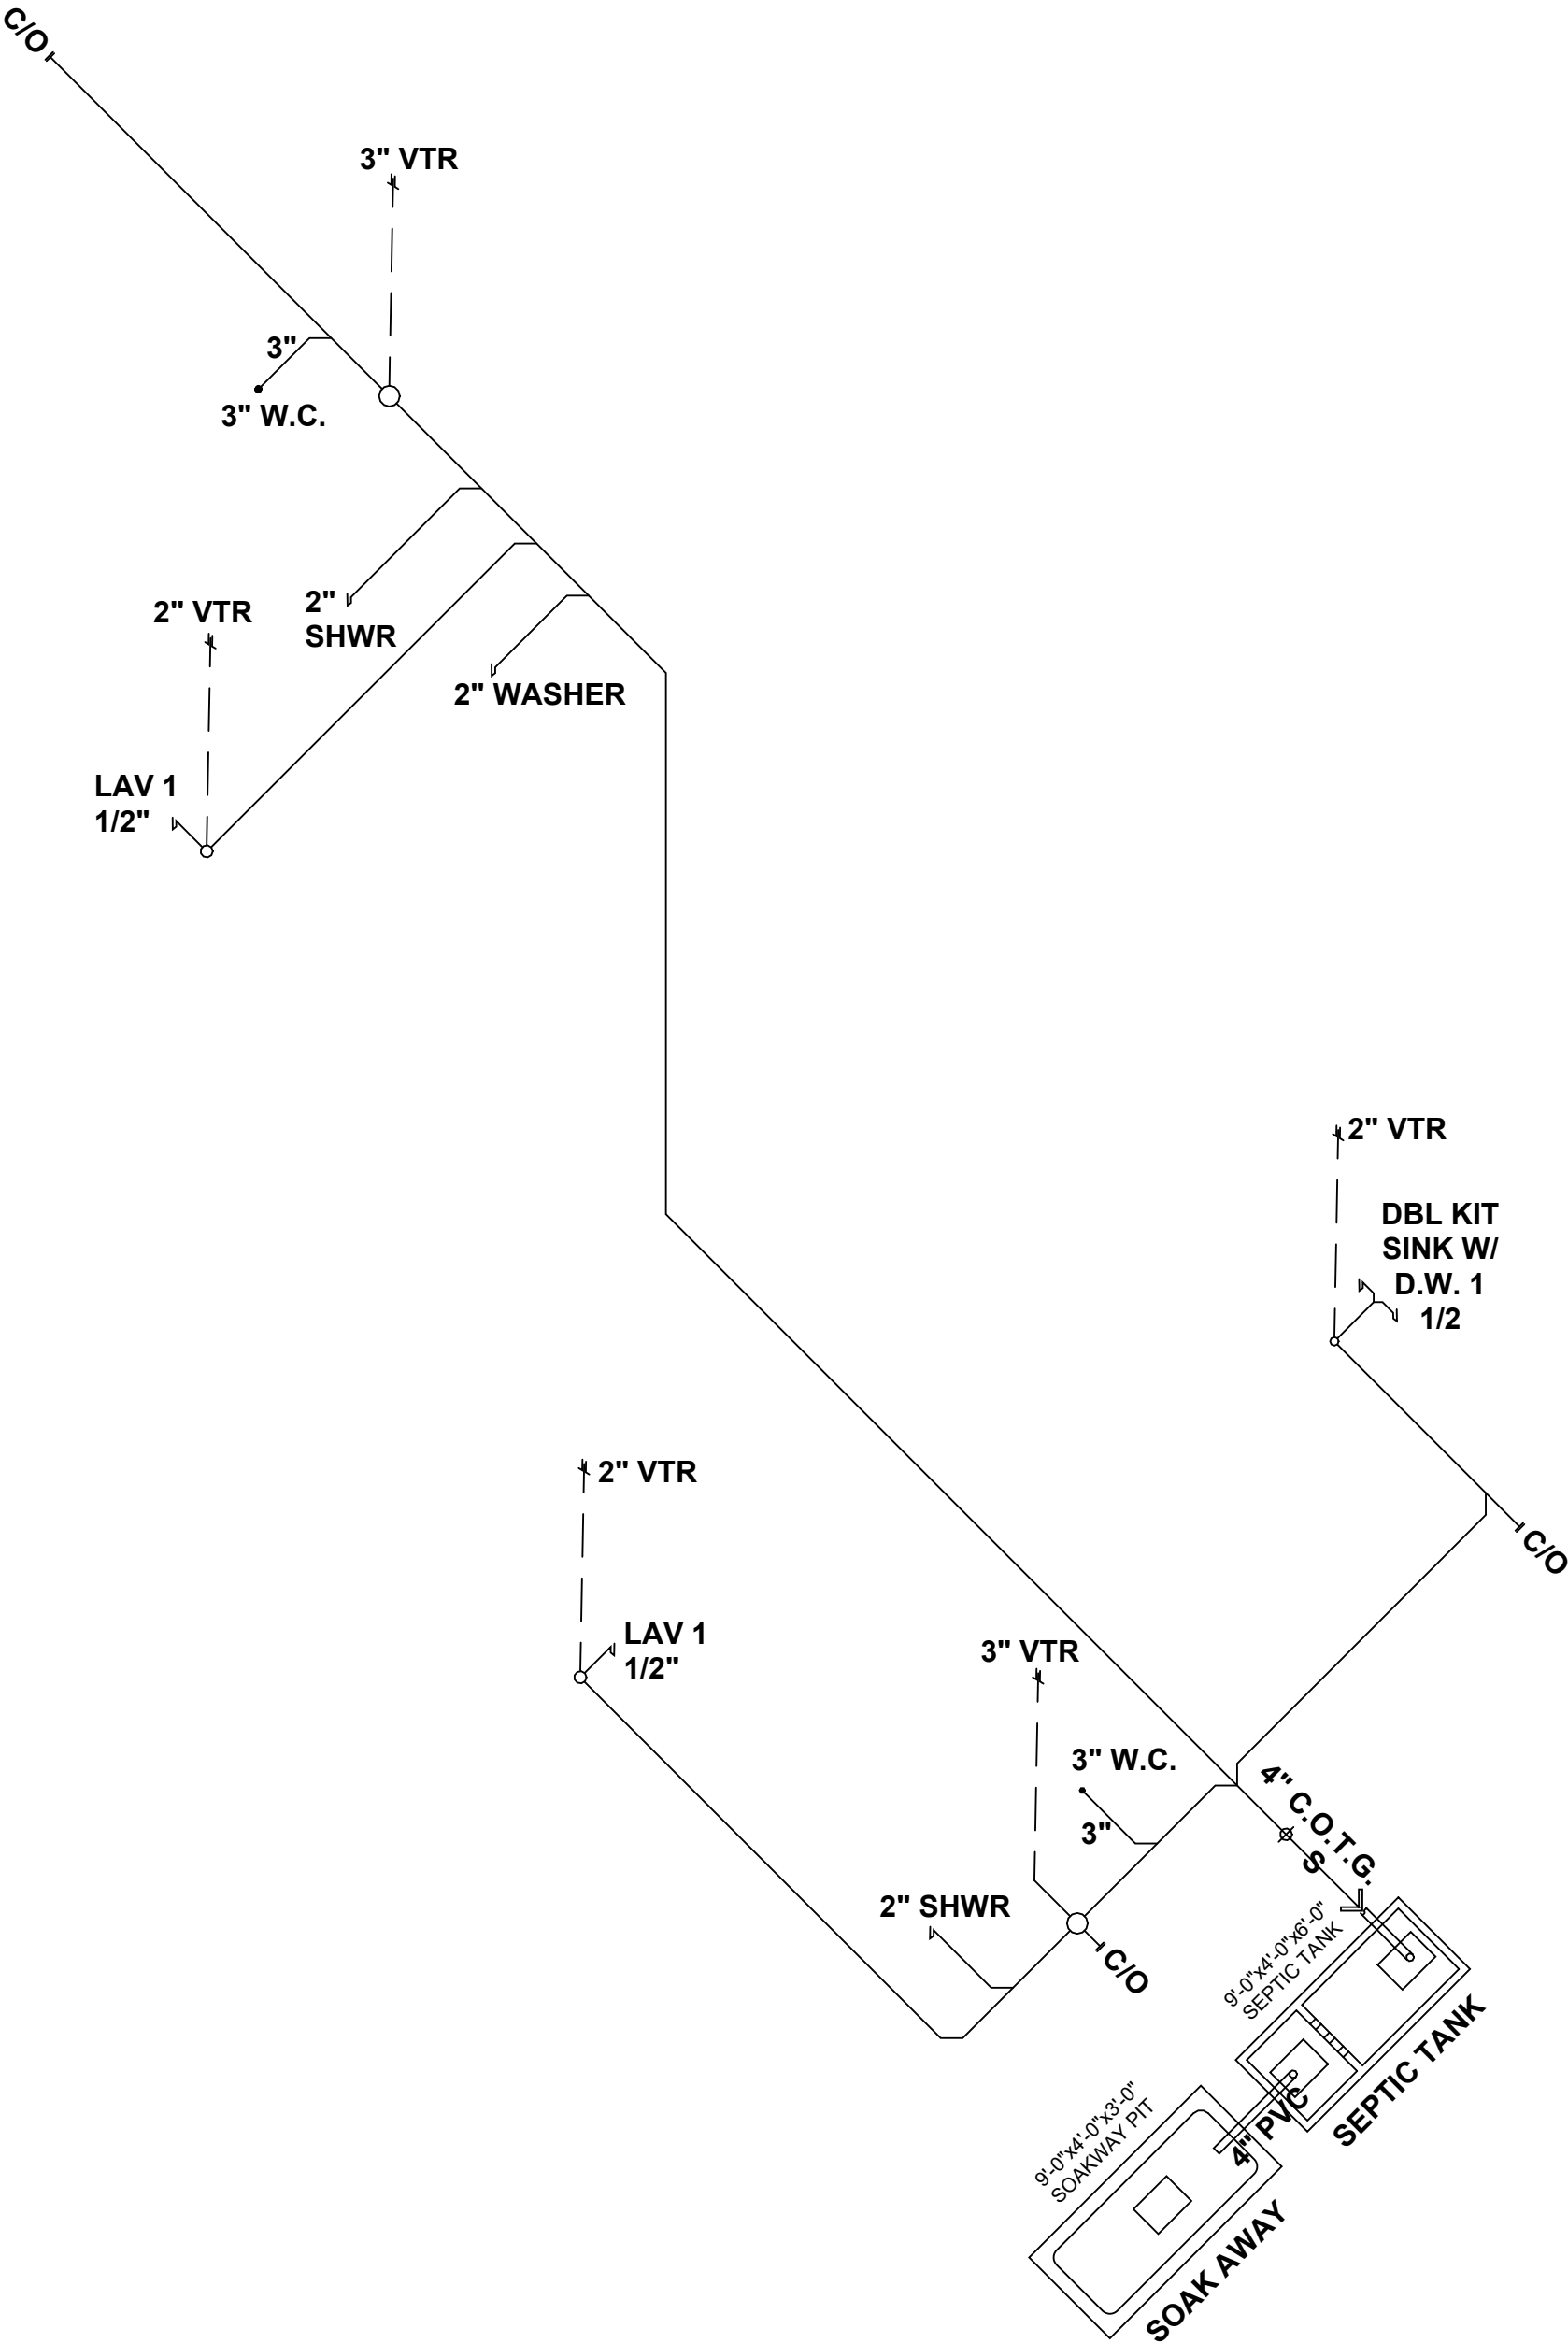

Typical Piping at Water Heater

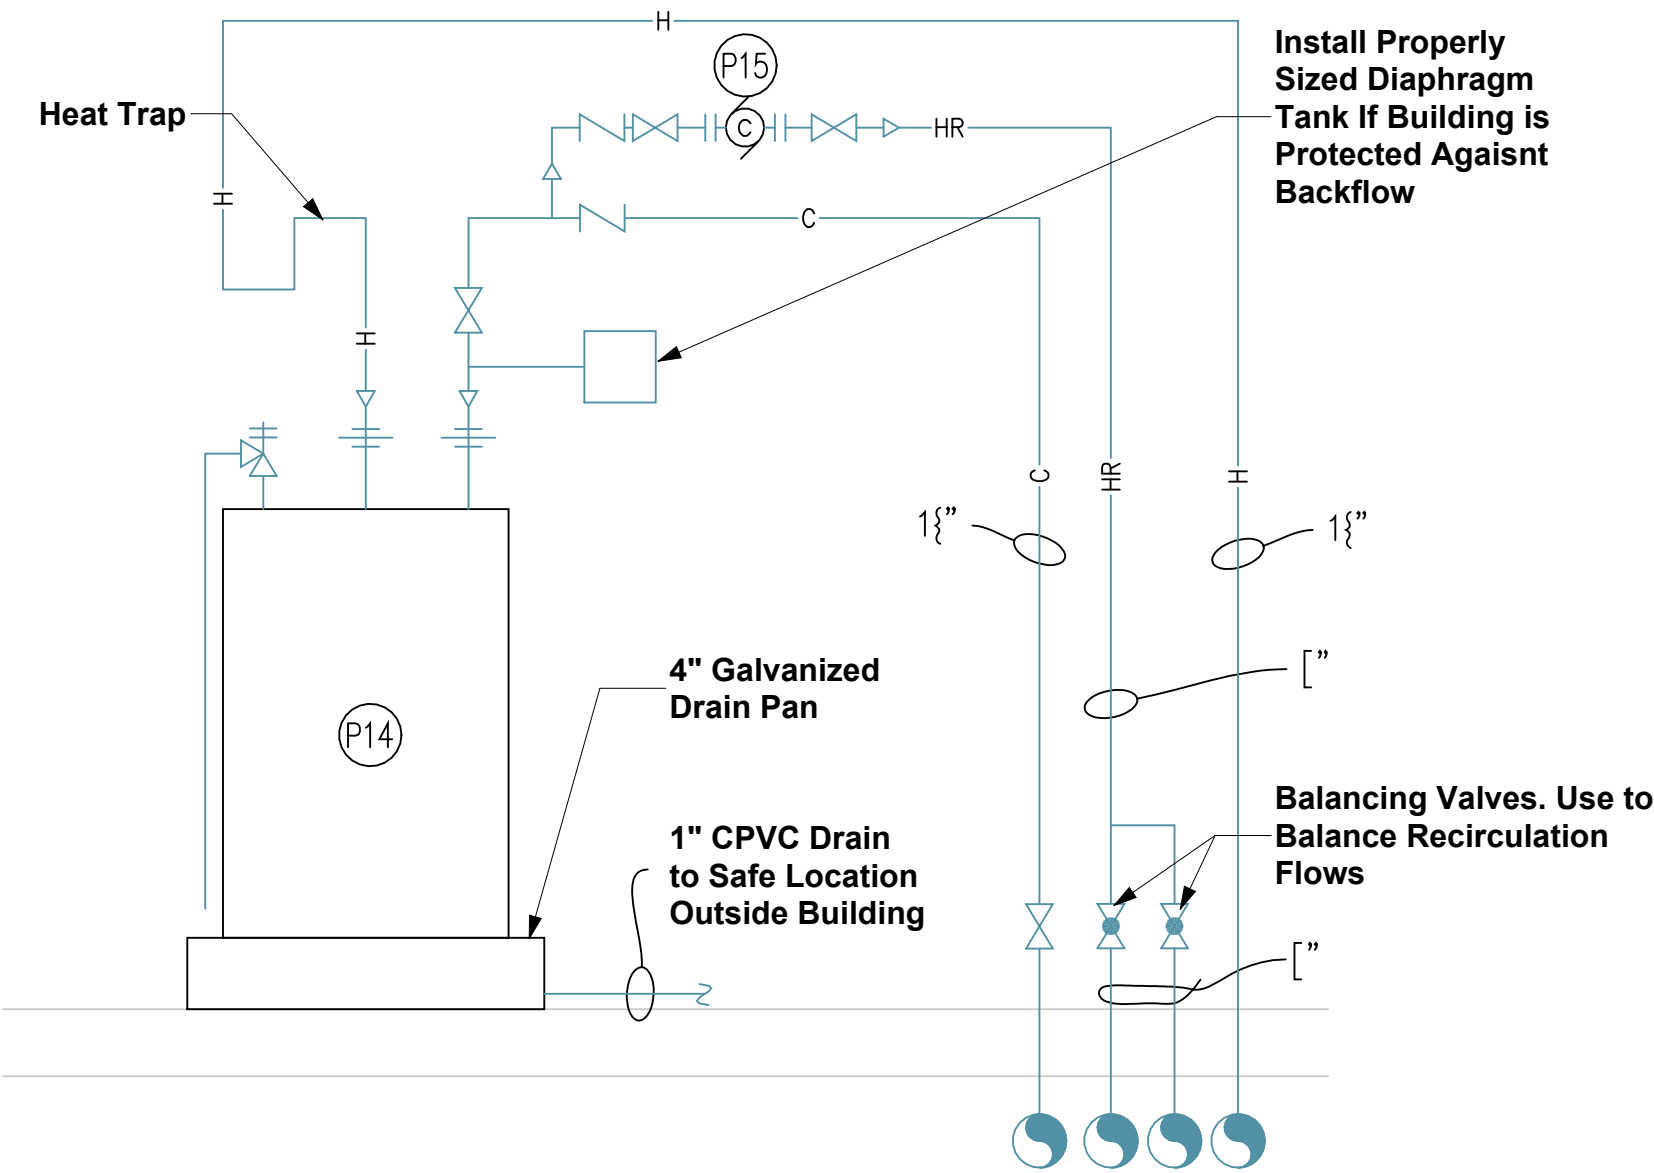

Typical Sceptic Tank & Soak Away Section

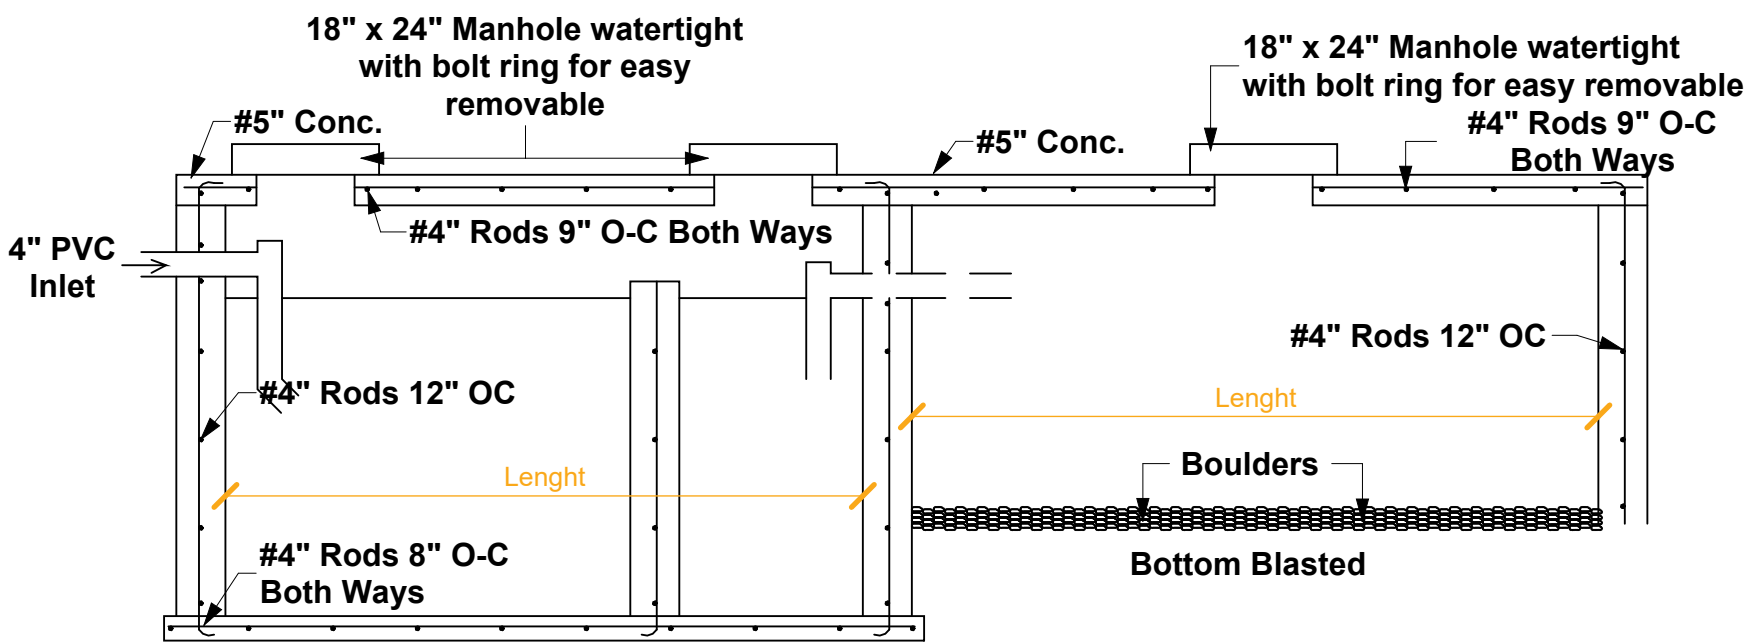

1. THESE DRAWINGS MUST BE CHECKED BY THE CUSTOMER OR CONTRACTOR PRIOR TO APPROVAL. ANY ERRORS OR OMISSIONS MUST BE REPORTED IN WRITING TO BAUHU PRIOR TO COMMENCEMENT OF CONSTRUCTION.
2. ARCHITECTURAL DRAWINGS SHOULD BE READ IN CONJUNCTION WITH STRUCTURAL DETAILING AND FABRICATION GENERAL ASSEMBLY DRAWINGS.
3. FOR CONSTRUCTION PURPOSES, USE ONLY THE LATEST APPROVED DRAWINGS LABELED 'ISSUED FOR CONSTRUCTION'.
4. DO NOT SCALE FROM THIS DRAWING.
5. THE COMPANY OPERATES USING METRIC DIMENSIONS AS THE PRINCIPAL DENOMINATION.
6. ALL CONCRETE WORKS ARE OUTSIDE OF THE SCOPE OF THE COMPANY. INFORMATION REGARDING SLAB DESIGN AND CONNECTIONS IN THESE DRAWINGS ARE INTENDED FOR GUIDENCE ONLY. FOUNDATION AND SLAB WORKS SHOULD BE DESIGNED AND APPROVED BY A LOCAL STRUCTURAL ENGINEER.
7. THE COMPANY RETAINS FULL TITLE AND OWNERSHIP OF THESE PLANS AND DESIGNS. ANY UNAUTHORISED USE, REPRODUCTION, OR DISTRIBUTION OF THESE PLANS, WHETHER IN WHOLE OR PART, IS EXPRESSLY PROHIBITED WITHOUT PRIOR WRITTEN CONSENT.

| No. | Revision | Date |
|-----|----------|------|
|     |          |      |
|     |          |      |
ISSUED FOR:

Issued for information

Issued for client approval

Issued for fabrication

Issued for construction

Firefly

DRAWING TITLE:

Plumbing Plan

DRAWN BY:

Mladin Monica-Mihaela

SCALE:

DRAWING NO:

A16

DATE:

04.03.2024

- Hot Water
- Cold Water
- Waste Water
- Rain Water Collection Pipes (underground)

1. THESE DRAWINGS MUST BE CHECKED BY THE CUSTOMER OR CONTRACTOR PRIOR TO APPROVAL. ANY ERRORS OR OMISSIONS MUST BE REPORTED IN WRITING TO BAUHU PRIOR TO COMMENCEMENT OF CONSTRUCTION.
2. ARCHITECTURAL DRAWINGS SHOULD BE READ IN CONJUNCTION WITH STRUCTURAL DETAILING AND FABRICATION GENERAL ASSEMBLY DRAWINGS.
3. FOR CONSTRUCTION PURPOSES, USE ONLY THE LATEST APPROVED DRAWINGS LABELED 'ISSUED FOR CONSTRUCTION'.
4. DO NOT SCALE FROM THIS DRAWING.
5. THE COMPANY OPERATES USING METRIC DIMENSIONS AS THE PRINCIPAL DENOMINATION.
6. ALL CONCRETE WORKS ARE OUTSIDE OF THE SCOPE OF THE COMPANY. INFORMATION REGARDING SLAB DESIGN AND CONNECTIONS IN THESE DRAWINGS ARE INTENDED FOR GUIDENCE ONLY. FOUNDATION AND SLAB WORKS SHOULD BE DESIGNED AND APPROVED BY A LOCAL STRUCTURAL ENGINEER.
7. THE COMPANY RETAINS FULL TITLE AND OWNERSHIP OF THESE PLANS AND DESIGNS. ANY UNAUTHORISED USE, REPRODUCTION, OR DISTRIBUTION OF THESE PLANS, WHETHER IN WHOLE OR PART, IS EXPRESSLY PROHIBITED WITHOUT PRIOR WRITTEN CONSENT.

| No. | Revision | Date |
|-----|----------|------|
|     |          |      |
|     |          |      |
ISSUED FOR:

Issued for information

Issued for client approval

Issued for fabrication

Issued for construction

Firefly

DRAWING TITLE:

GF Plumbing Plan

DRAWN BY:

Mladin Monica-Mihaela

SCALE:


1 : 70

DRAWING NO:

A17


DATE:

04.03.2024

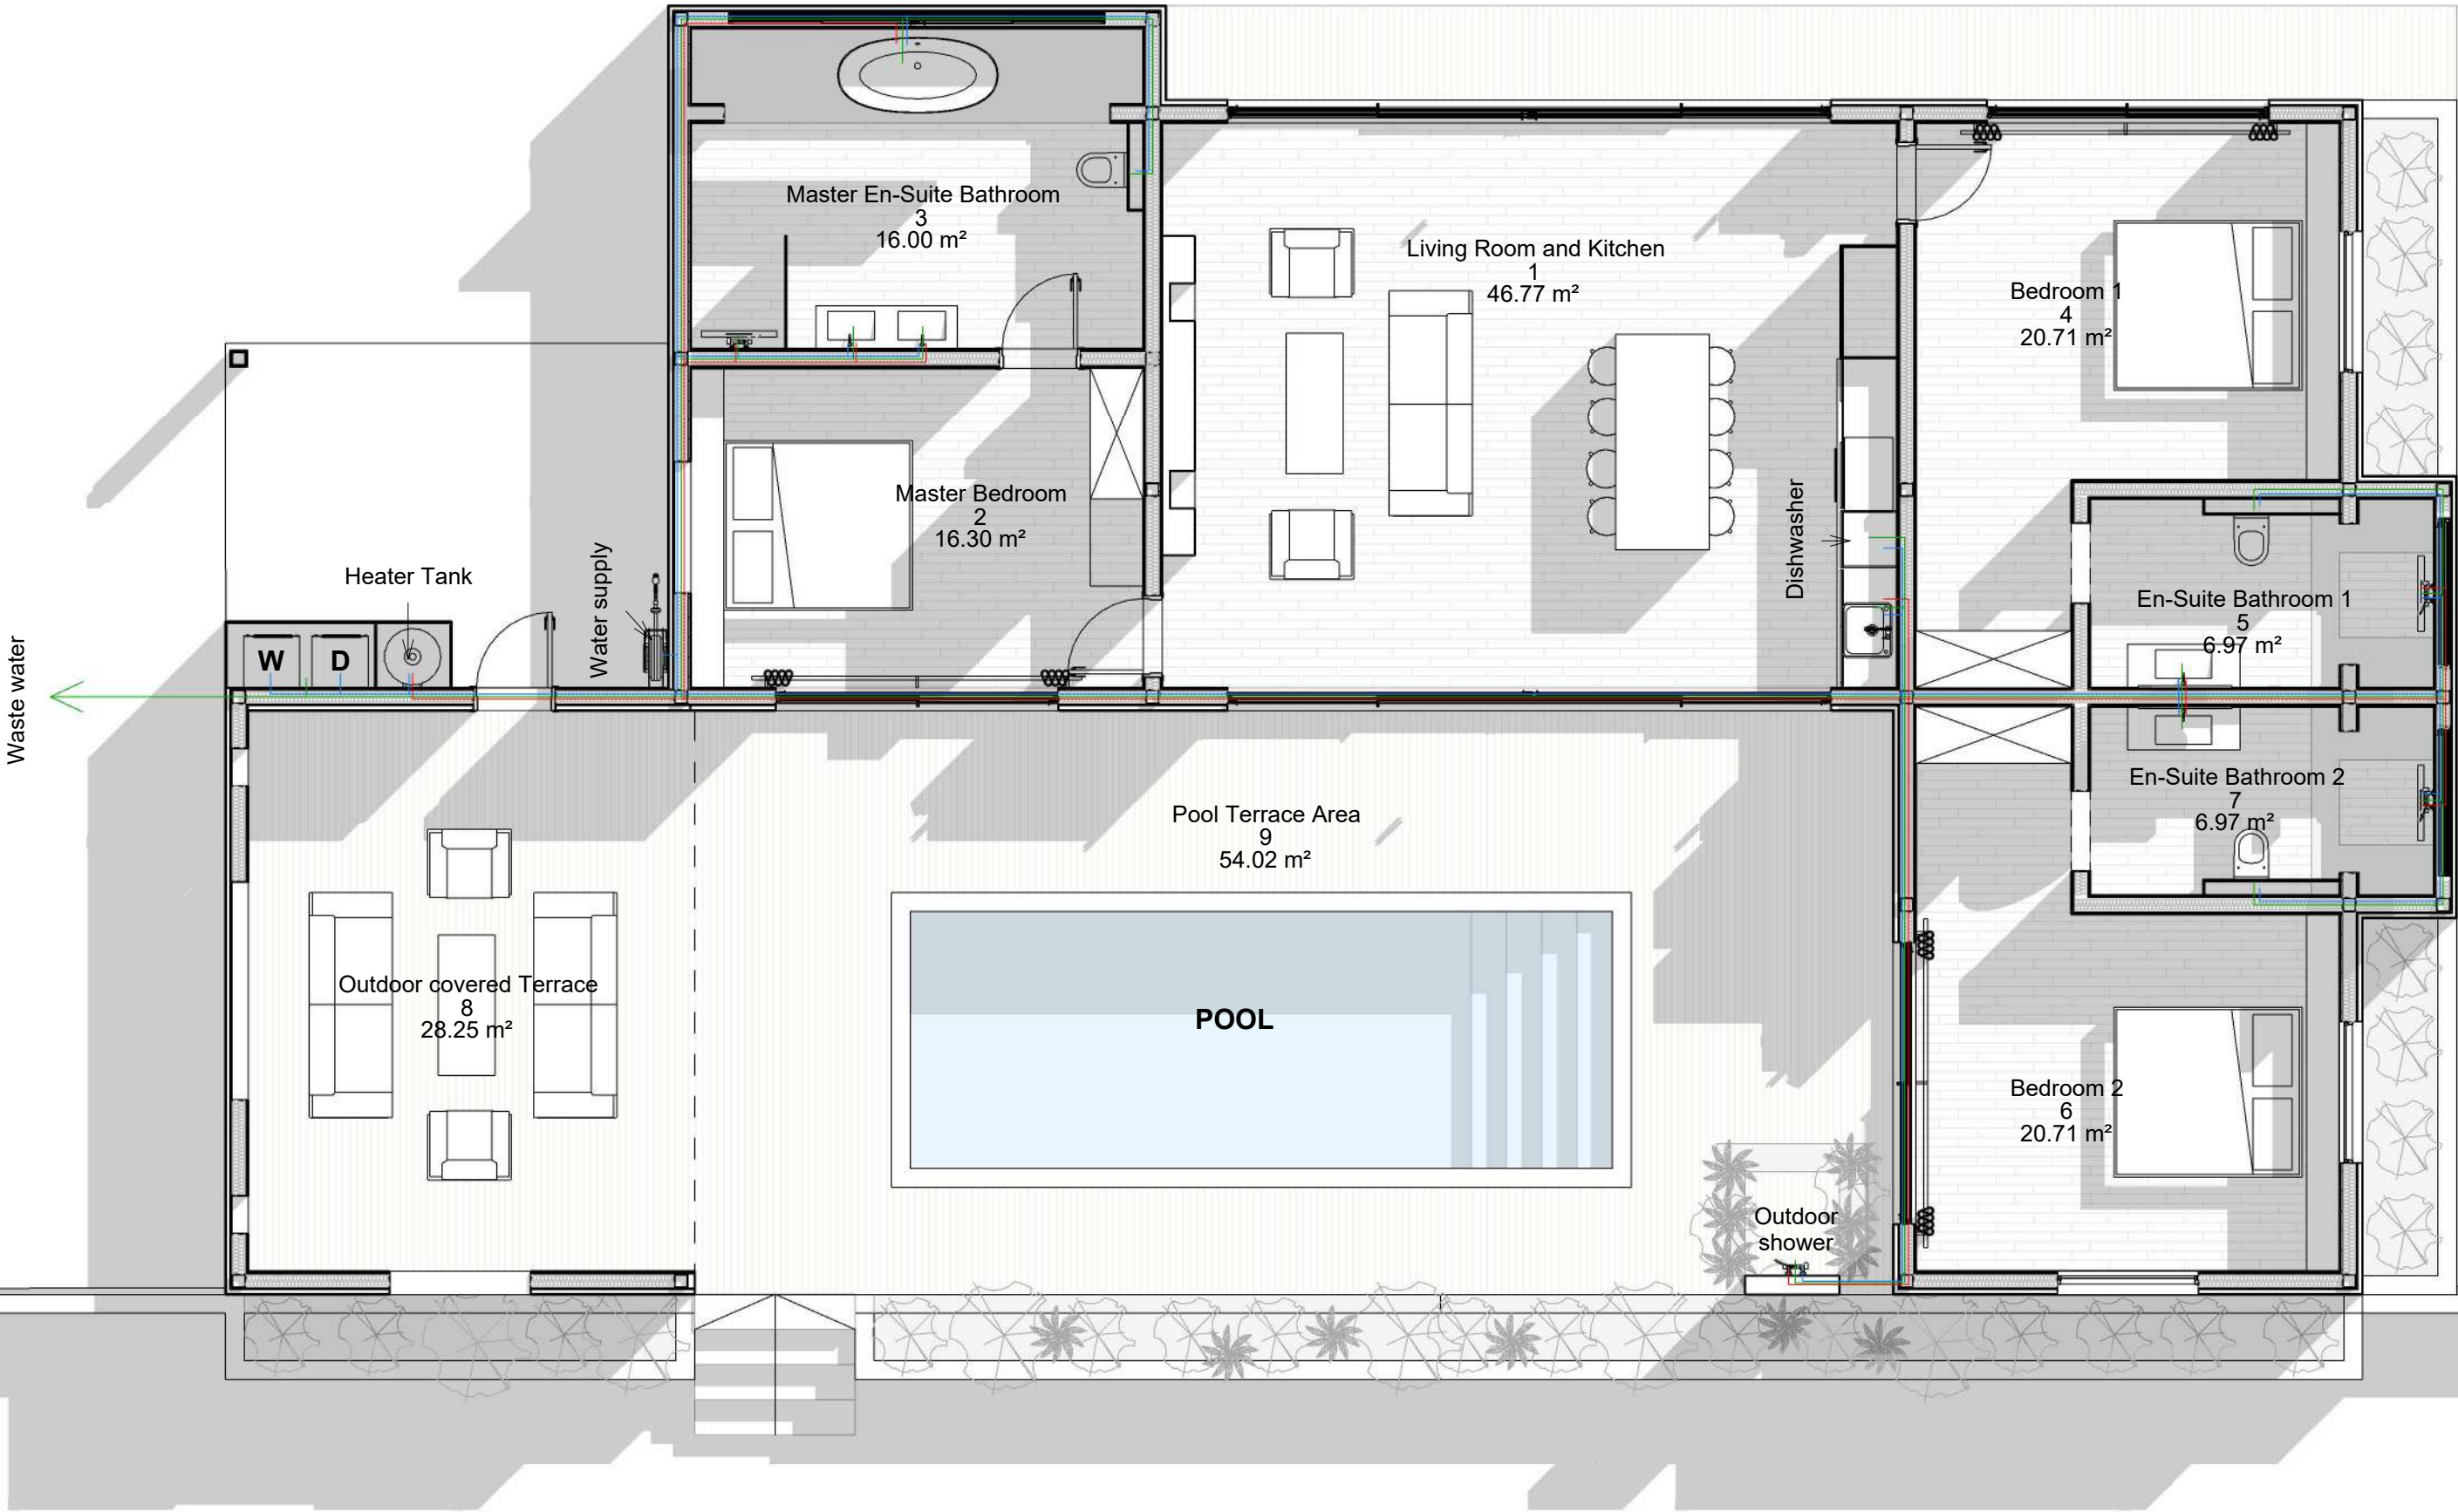

Toilet


Sanindusa  
Model: F/D low level toilet  
Reference: 136011  
concealed cistern boxed in to ceiling  
Count: 3 pcs

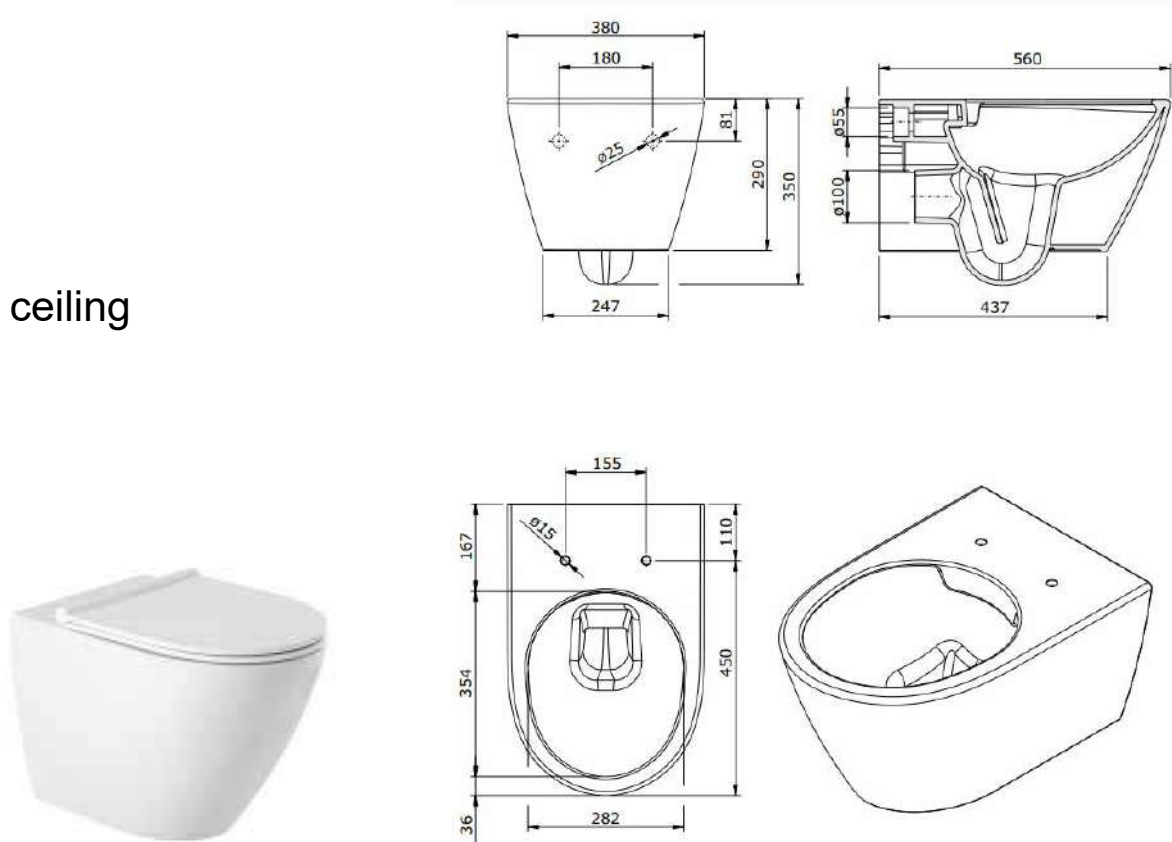

https://www.tec.sanindusa.pt/winner-wd-rimflush-close-coupled-toilet

Shower Taps


Bruma  
Model: Shower system for wall mounting with adjustable ABS head shower Ø230mm and shower rail  
Reference: 181 271 1CR  
Finishes: Chrome  
Count: 4 pcs

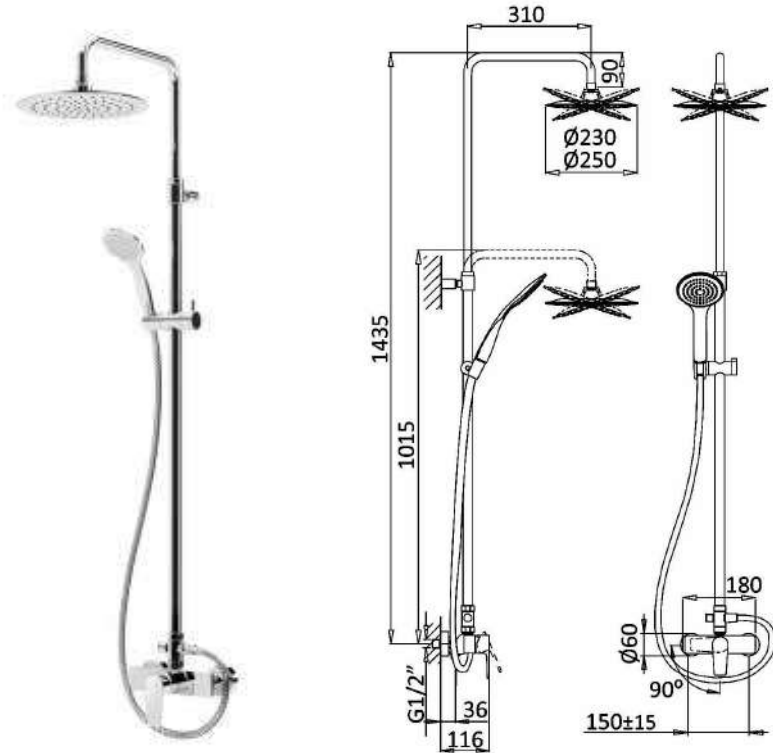

https://www.bruma.pt/index.php?page=products&prod=5482#open\_product

Shower Drain

Sanindusa  
Model: Shower channel drain with grid 700/800/900  
Reference: 49070  
Finishes: Brushed Stainless Steel  
Count: 4 pcs

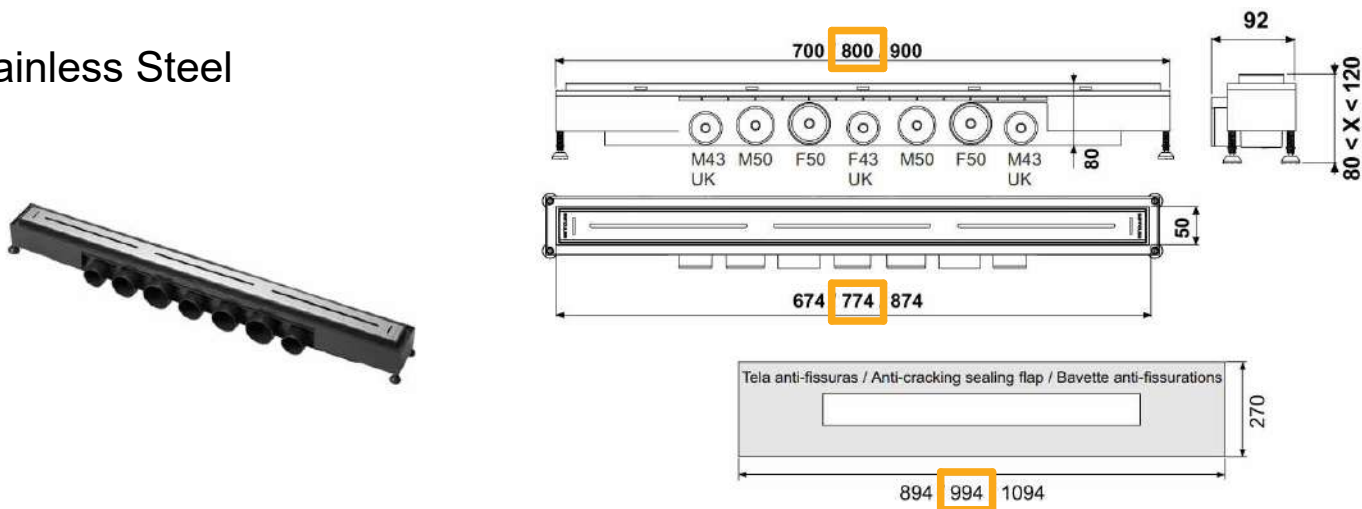


https://www.tec.sanindusa.pt/metric-70-shower-channel-with-grid

Mirror

Kitbanho  
Model: ESPELHO GRANADA 67  
Count: 2 pcs x 600Ø mm - Master Bathroom

Model: ESPELHO POMPEIA  
Count: 2 pcs x 1000Ø mm - Bathroom 1&2

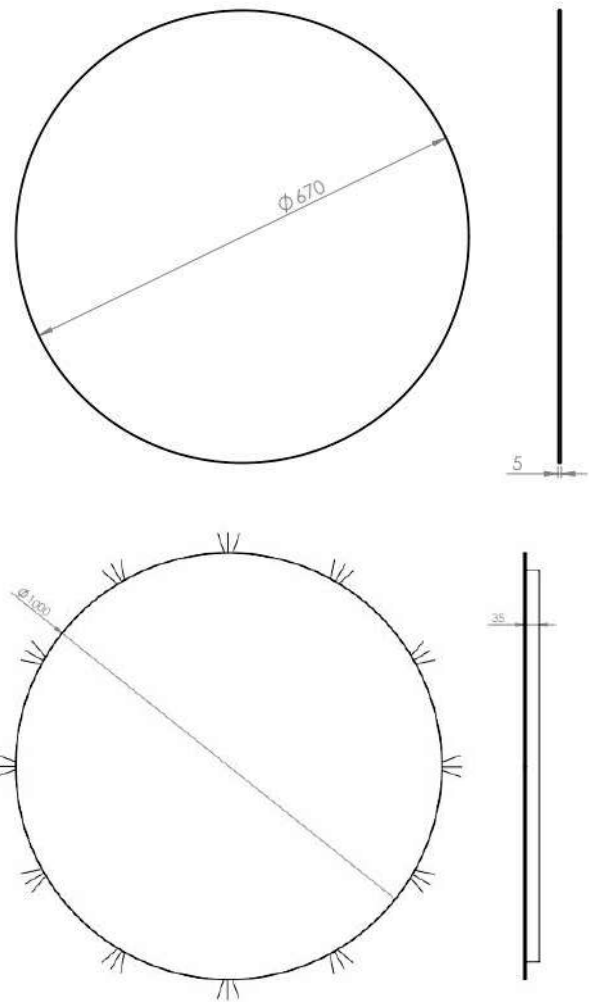


Vanity Unit/Sink

Consentino  
Model: Armony  
Finishes: White  
Count: 2 pcs x 1200 mm - one sink  
Count: 1 pcs x 1500mm - two sinks



Vanity Faucet

Bruma  
Model: Nautic  
Reference: 181 010 1CR  
Finishes: Chrome  
Count: 4 pcs

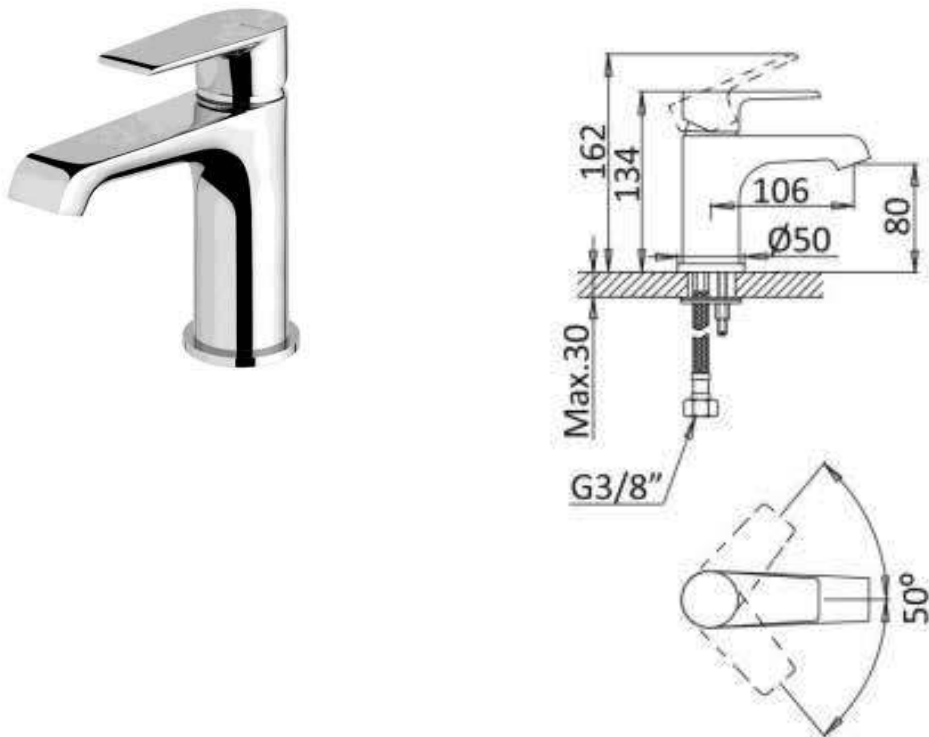

https://www.bruma.pt/index.php?page=products&prod=5426#open\_product



1. THESE DRAWINGS MUST BE CHECKED BY THE CUSTOMER OR CONTRACTOR PRIOR TO APPROVAL. ANY ERRORS OR OMISSIONS MUST BE REPORTED IN WRITING TO BAUHU PRIOR TO COMMENCEMENT OF CONSTRUCTION.
2. ARCHITECTURAL DRAWINGS SHOULD BE READ IN CONJUNCTION WITH STRUCTURAL DETAILING AND FABRICATION GENERAL ASSEMBLY DRAWINGS.
3. FOR CONSTRUCTION PURPOSES, USE ONLY THE LATEST APPROVED DRAWINGS LABELED 'ISSUED FOR CONSTRUCTION'.
4. DO NOT SCALE FROM THIS DRAWING.
5. THE COMPANY OPERATES USING METRIC DIMENSIONS AS THE PRINCIPAL DENOMINATION.
6. ALL CONCRETE WORKS ARE OUTSIDE OF THE SCOPE OF THE COMPANY. INFORMATION REGARDING SLAB DESIGN AND CONNECTIONS IN THESE DRAWINGS ARE INTENDED FOR GUIDENCE ONLY. FOUNDATION AND SLAB WORKS SHOULD BE DESIGNED AND APPROVED BY A LOCAL STRUCTURAL ENGINEER.
7. THE COMPANY RETAINS FULL TITLE AND OWNERSHIP OF THESE PLANS AND DESIGNS. ANY UNAUTHORISED USE, REPRODUCTION, OR DISTRIBUTION OF THESE PLANS, WHETHER IN WHOLE OR PART, IS EXPRESSLY PROHIBITED WITHOUT PRIOR WRITTEN CONSENT.

| No. | Revision | Date |
|-----|----------|------|
|     |          |      |
|     |          |      |
ISSUED FOR:

☐ Issued for information

☒ Issued for client approval

☐ Issued for fabrication

☐ Issued for construction

Firefly

DRAWING TITLE:

Bathroom Schedule

DRAWN BY:

Mladin Monica-Mihaela


SCALE:

DRAWING NO:



A18

DATE:


04.03.2024

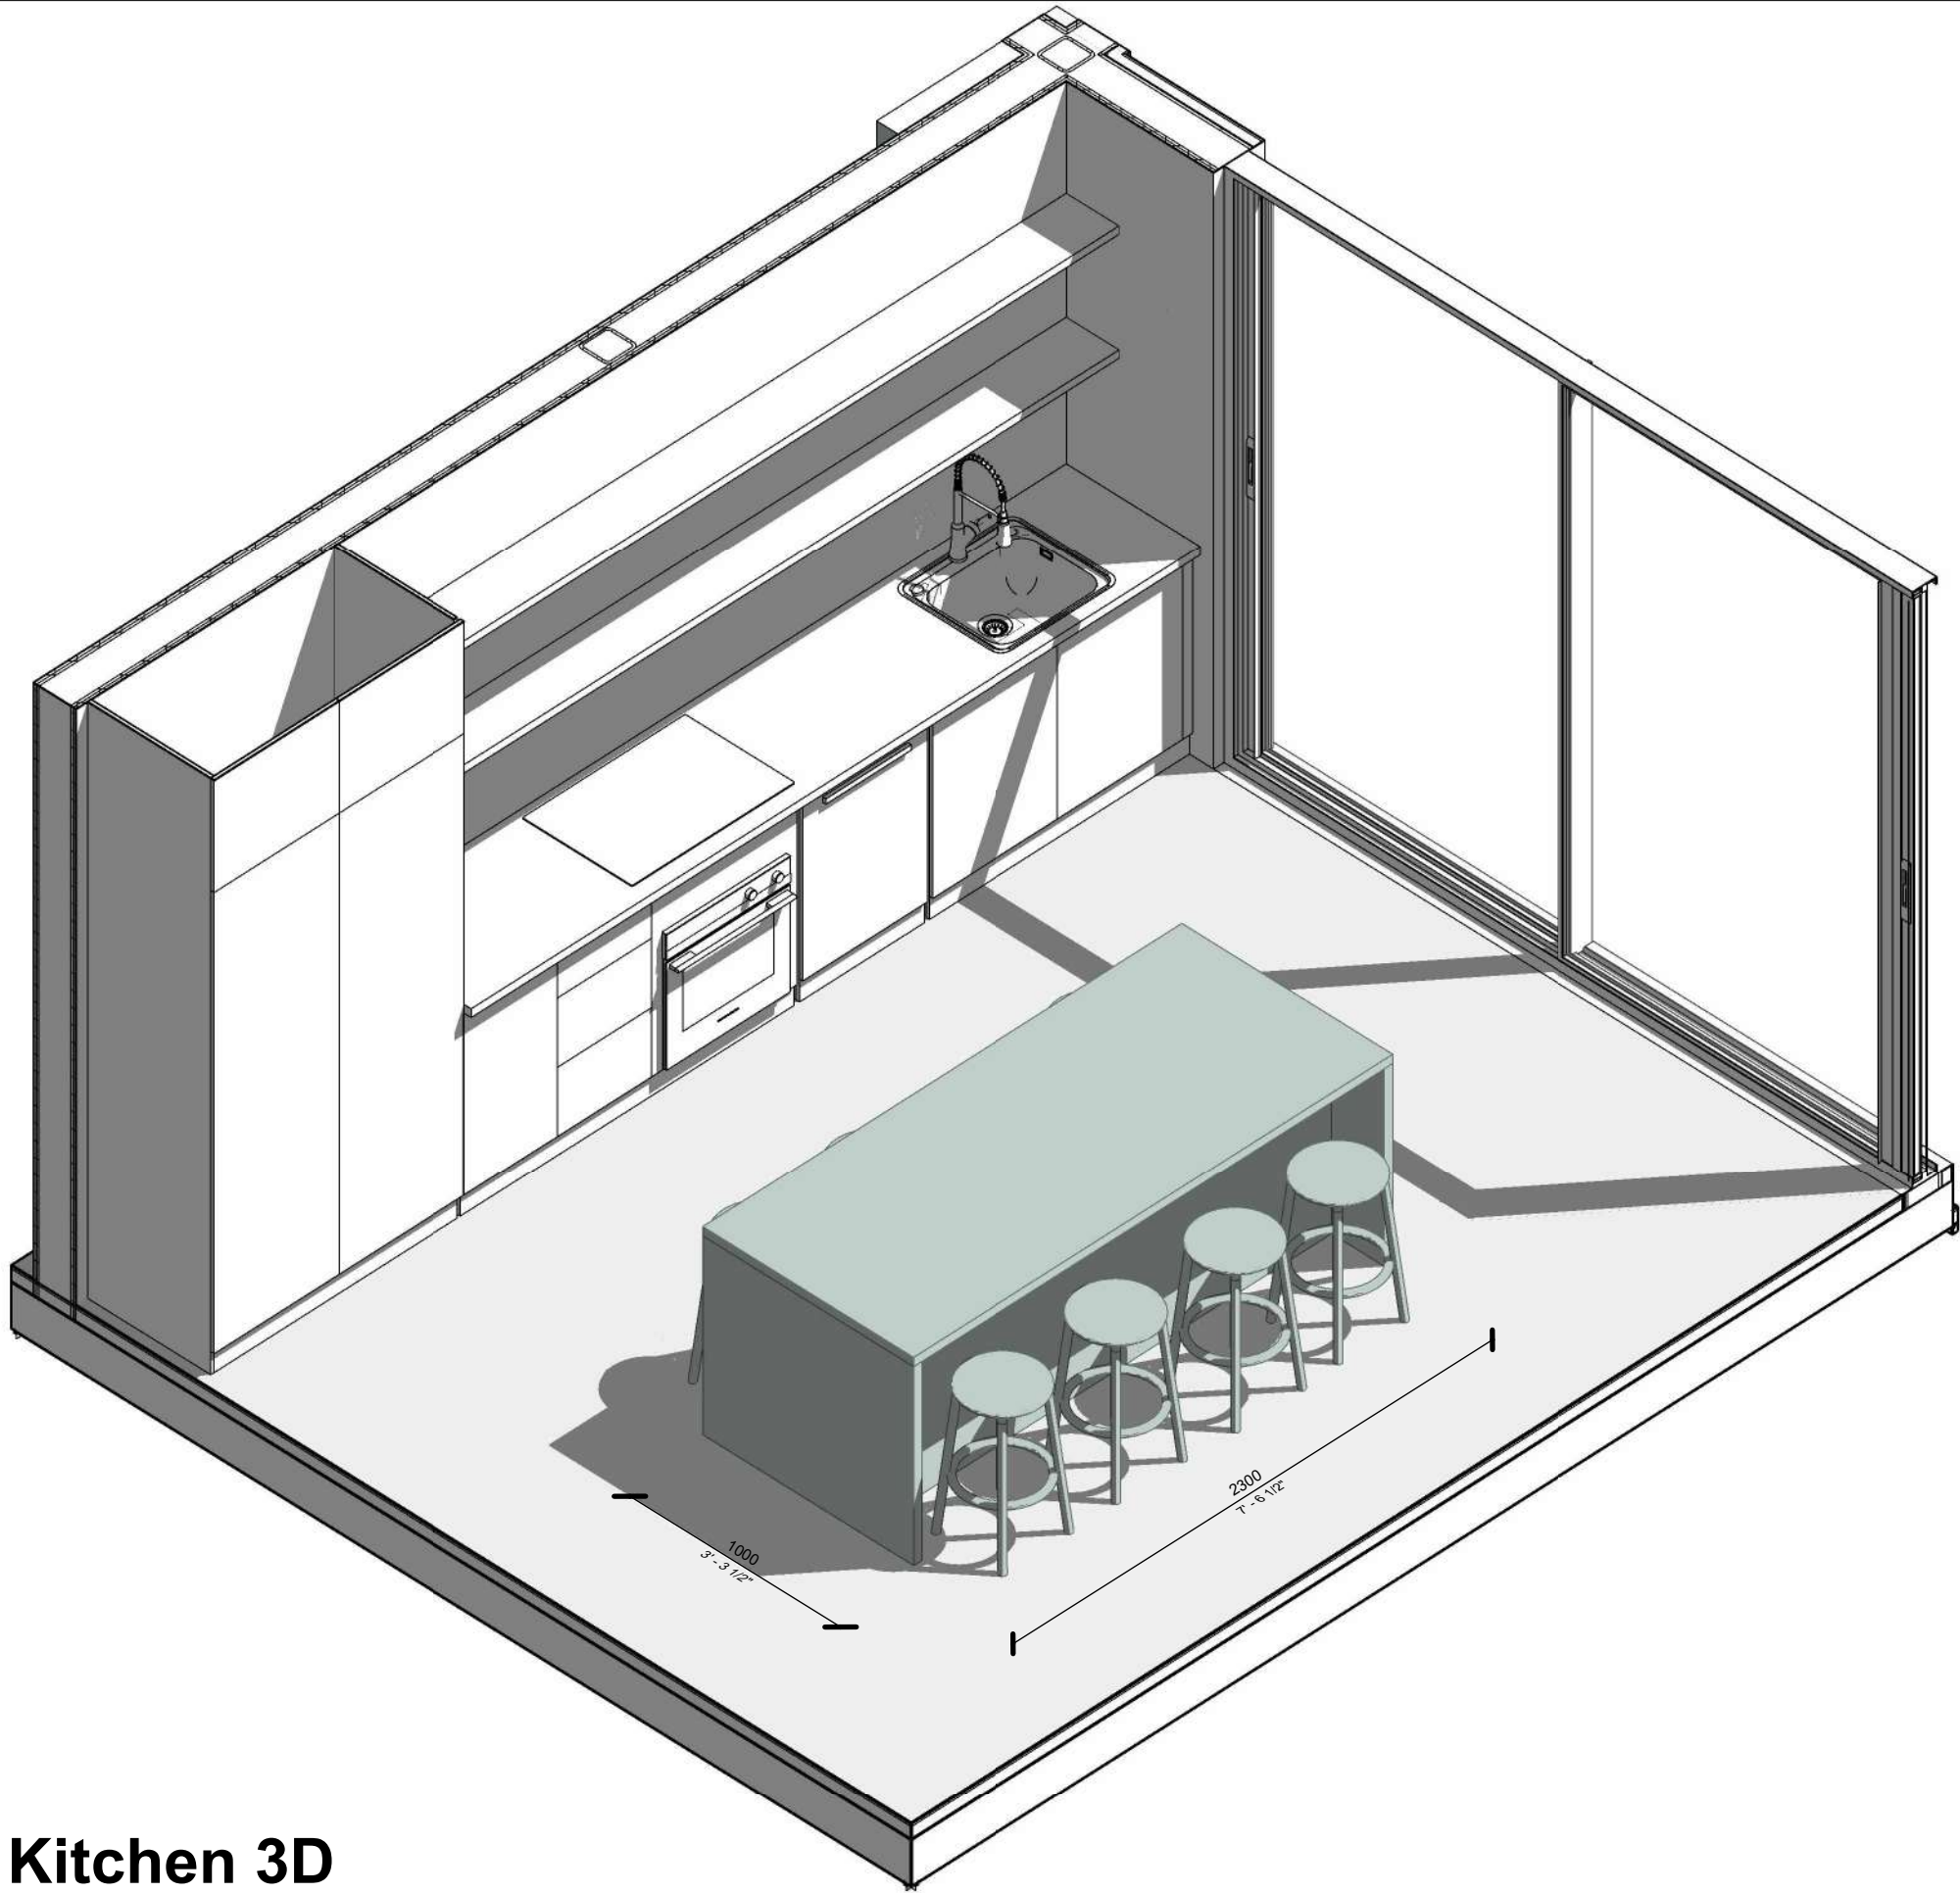


Kitchen 3D

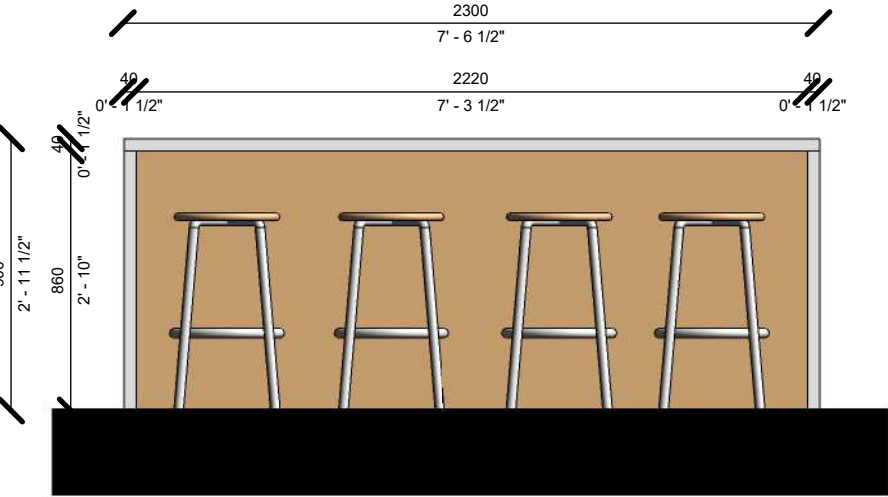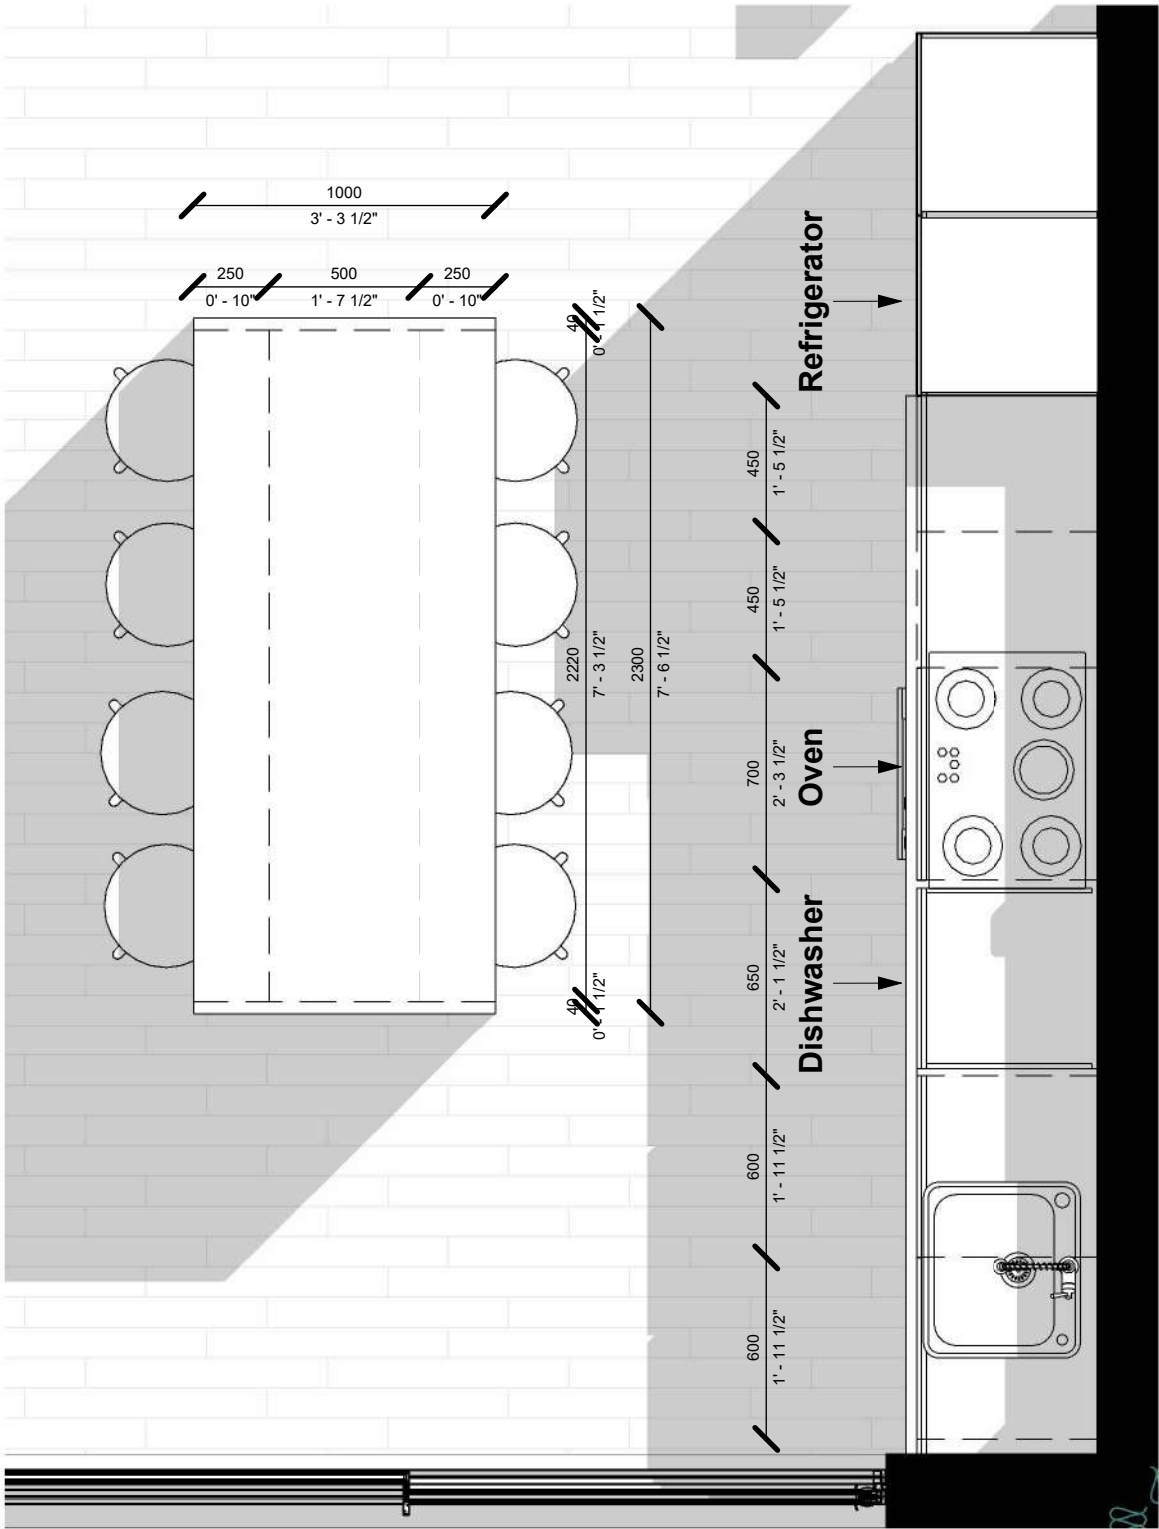

Island Front/Back view

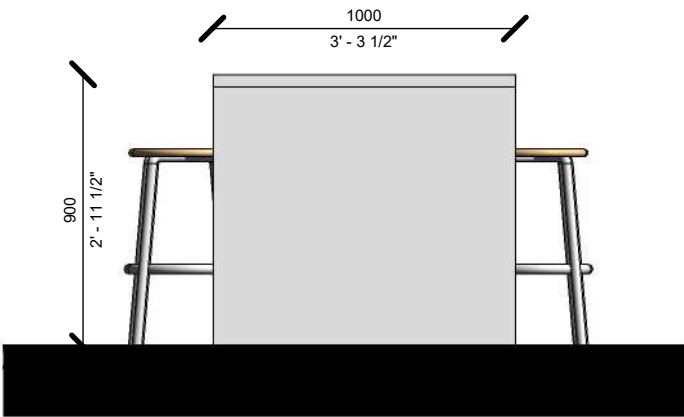

Island Side view

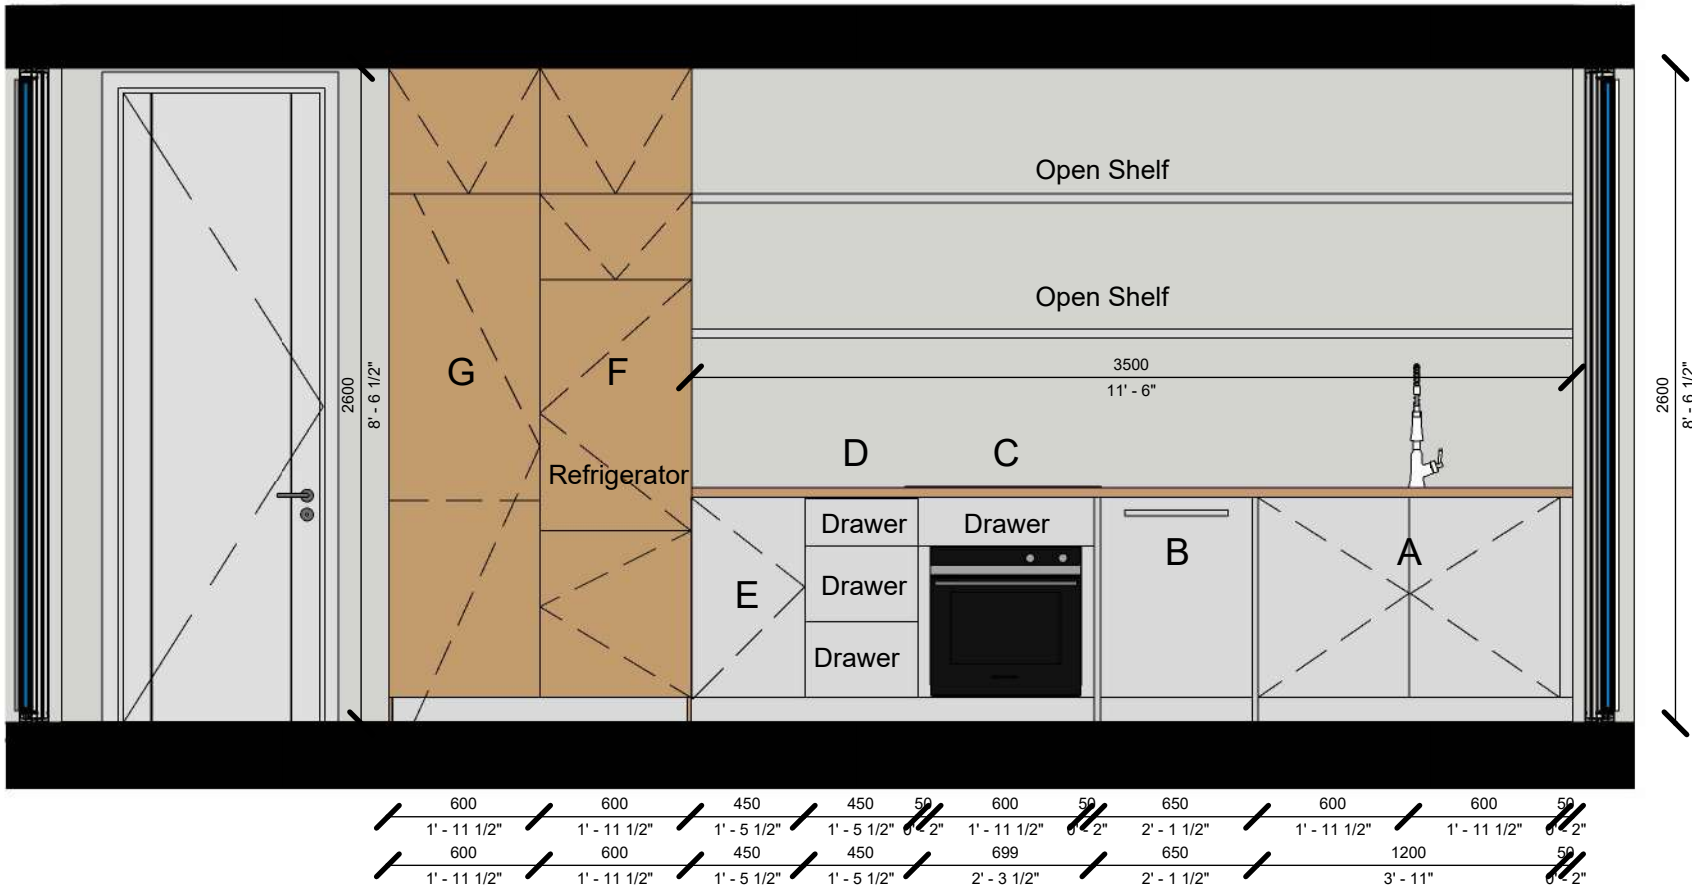

Kitchen view

1. THESE DRAWINGS MUST BE CHECKED BY THE CUSTOMER OR CONTRACTOR PRIOR TO APPROVAL. ANY ERRORS OR OMISSIONS MUST BE REPORTED IN WRITING TO BAUHU PRIOR TO COMMENCEMENT OF CONSTRUCTION.
2. ARCHITECTURAL DRAWINGS SHOULD BE READ IN CONJUNCTION WITH STRUCTURAL DETAILING AND FABRICATION GENERAL ASSEMBLY DRAWINGS.
3. FOR CONSTRUCTION PURPOSES, USE ONLY THE LATEST APPROVED DRAWINGS LABELED 'ISSUED FOR CONSTRUCTION'.
4. DO NOT SCALE FROM THIS DRAWING.
5. THE COMPANY OPERATES USING METRIC DIMENSIONS AS THE PRINCIPAL DENOMINATION.
6. ALL CONCRETE WORKS ARE OUTSIDE OF THE SCOPE OF THE COMPANY. INFORMATION REGARDING SLAB DESIGN AND CONNECTIONS IN THESE DRAWINGS ARE INTENDED FOR GUIDENCE ONLY. FOUNDATION AND SLAB WORKS SHOULD BE DESIGNED AND APPROVED BY A LOCAL STRUCTURAL ENGINEER.
7. THE COMPANY RETAINS FULL TITLE AND OWNERSHIP OF THESE PLANS AND DESIGNS. ANY UNAUTHORISED USE, REPRODUCTION, OR DISTRIBUTION OF THESE PLANS, WHETHER IN WHOLE OR PART, IS EXPRESSLY PROHIBITED WITHOUT PRIOR WRITTEN CONSENT.

| No. | Revision | Date |
|-----|----------|------|
|     |          |      |
|     |          |      |
ISSUED FOR:

Issued for information

Issued for client approval

Issued for fabrication

Issued for construction

Firefly

DRAWING TITLE:

Kitchen Schedule

DRAWN BY:

Mladin Monica-Mihaela

SCALE:

As indicated

DRAWING NO:

A19

DATE:

04.03.2024

Dishwasher

-Geappliances  
-Dimensions: 34 H x 23 3/4 W x 24 D  
-Color: Fingerprint Resistant Stainless  
-  
<https://www.geappliances.com/appliance/GE-Profile-ENERGY-STAR-Fingerprint-Resistant-Top-Control-Stainless-Interior-Dishwasher-with-Microban-Antimicrobial-Protection-with-Sanitiz-Cycle-PDT715SYVFS>



Kitchen Furniture

| Name           | Width | Carcase Height | Depth | Plinth Height | Count | Notes                                  |
|----------------|-------|----------------|-------|---------------|-------|----------------------------------------|
| Kitchen Island | 2300  | 900            | 1000  | -             | x1    |                                        |
| Unit A         | 1200  | 792            | 600   | 100           | x1    |                                        |
| Unit B         | 650   | 892            | 600   | -             | x1    | Dishwasher space                       |
| Unit C         | 650   | 792            | 600   | 100           | x1    | Oven space and drawer                  |
| Unit D         | 450   | 792            | 600   | 100           | x1    | Drawers                                |
| Unit E         | 450   | 792            | 600   | 100           | x1    |                                        |
| Unit F         | 600   | 2600           | 600   | 100           | x1    | In-built Refrigerator + deposit spaces |
| Unit F         | 600   | 2600           | 600   | 100           | x1    | Tall Cabinet                           |
| Open Shelf     | 3500  | -              | 250   | -             | x2    |                                        |



- THESE DRAWINGS MUST BE CHECKED BY THE CUSTOMER OR CONTRACTOR PRIOR TO APPROVAL. ANY ERRORS OR OMISSIONS MUST BE REPORTED IN WRITING TO BAUHU PRIOR TO COMMENCEMENT OF CONSTRUCTION.
- ARCHITECTURAL DRAWINGS SHOULD BE READ IN CONJUNCTION WITH STRUCTURAL DETAILING AND FABRICATION GENERAL ASSEMBLY DRAWINGS.
- FOR CONSTRUCTION PURPOSES, USE ONLY THE LATEST APPROVED DRAWINGS LABELED 'ISSUED FOR CONSTRUCTION'.
- DO NOT SCALE FROM THIS DRAWING.
- THE COMPANY OPERATES USING METRIC DIMENSIONS AS THE PRINCIPAL DENOMINATION.
- ALL CONCRETE WORKS ARE OUTSIDE OF THE SCOPE OF THE COMPANY. INFORMATION REGARDING SLAB DESIGN AND CONNECTIONS IN THESE DRAWINGS ARE INTENDED FOR GUIDENCE ONLY. FOUNDATION AND SLAB WORKS SHOULD BE DESIGNED AND APPROVED BY A LOCAL STRUCTURAL ENGINEER.
- THE COMPANY RETAINS FULL TITLE AND OWNERSHIP OF THESE PLANS AND DESIGNS. ANY UNAUTHORISED USE, REPRODUCTION, OR DISTRIBUTION OF THESE PLANS, WHETHER IN WHOLE OR PART, IS EXPRESSLY PROHIBITED WITHOUT PRIOR WRITTEN CONSENT.

Oven

-Geappliances  
-24" Electric Single Self-Cleaning Wall Oven  
-Dimensions: 28 3/16 H x 23 3/4 W x 23 1/8 D  
-Color: Black on Black  
-  
<https://www.geappliances.com/appliance/GE-24-Electric-Single-Self-Cleaning-Wall-Oven-JRP20BJBB>



Kitchen  
Nobilia  
Front: 427 Alpine white  
Worktop: 193 Alpine white  
Carcase colour: 060 Alpine white gloss  
Front-inside island/tall cabinets: 843 Bergamo oak reproduction



Cooktop

-Geappliances  
-30" Built-In Touch Control Electric Cooktop  
-Dimensions: 3 1/4 H x 29 7/8 W x 21 1/2 D  
-Color: Black  
-  
<https://www.geappliances.com/appliance/GE-Profile-30-Built-In-Touch-Control-Electric-Cooktop-PEP9030STSS>



Kitchen blacksplash  
Brilho / Glossy vogue VO01R / R16  
34x66,5, 13,4"x26,2"



| No. | Revision | Date |
|-----|----------|------|
|     |          |      |
|     |          |      |
- ISSUED FOR:
- Issued for information
  - Issued for client approval
  - Issued for fabrication
  - Issued for construction

Firefly

DRAWING TITLE:  
Kitchen Schedule 2

DRAWN BY:  
Mladin Monica-Mihaela


SCALE:  
1 : 25

DRAWING NO:  
A20

DATE:  
04.03.2024

Refrigerator

-Forte Appliances 650 series  
24" Buil-In Bottom Mount Refrigerator  
Code: F9BFRESIC450PR  
Width: 21 1/4 in, 54 cm  
Height:69 5/8 in, 176.9 cm  
Depth: 21 5/8 in, 55 cm  
Height excluding hinge: 69 5/8 in, 176.8 cm  
Depth excluding door: 20 1/4 in, 51.3 cm  
Weight: 148 lbs, 67.1 kg

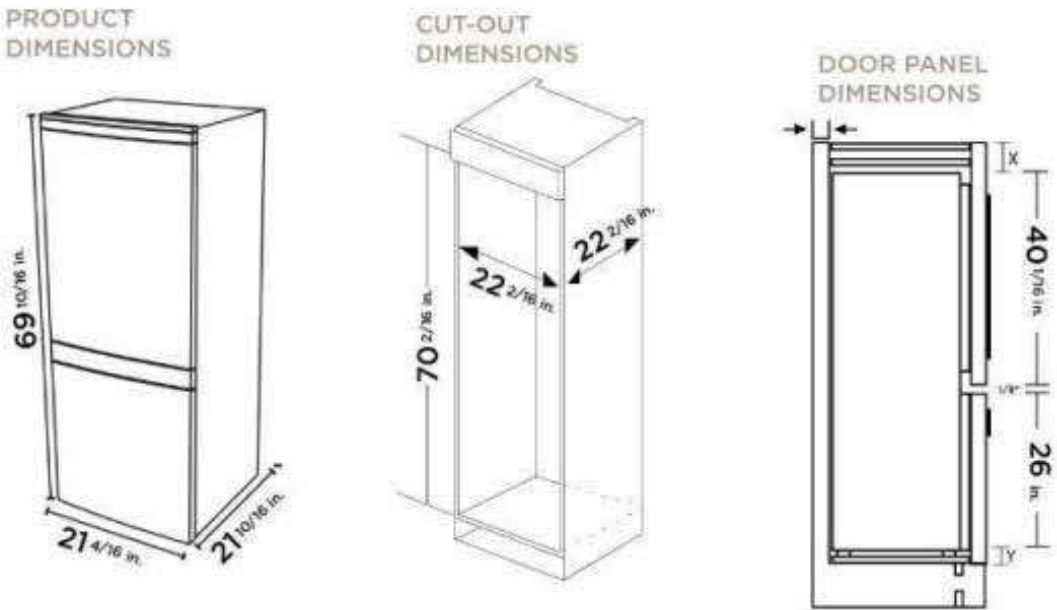

1. THESE DRAWINGS MUST BE CHECKED BY THE CUSTOMER OR CONTRACTOR PRIOR TO APPROVAL. ANY ERRORS OR OMISSIONS MUST BE REPORTED IN WRITING TO BAUHU PRIOR TO COMMENCEMENT OF CONSTRUCTION.
2. ARCHITECTURAL DRAWINGS SHOULD BE READ IN CONJUNCTION WITH STRUCTURAL DETAILING AND FABRICATION GENERAL ASSEMBLY DRAWINGS.
3. FOR CONSTRUCTION PURPOSES, USE ONLY THE LATEST APPROVED DRAWINGS LABELED 'ISSUED FOR CONSTRUCTION'.
4. DO NOT SCALE FROM THIS DRAWING.
5. THE COMPANY OPERATES USING METRIC DIMENSIONS AS THE PRINCIPAL DENOMINATION.
6. ALL CONCRETE WORKS ARE OUTSIDE OF THE SCOPE OF THE COMPANY. INFORMATION REGARDING SLAB DESIGN AND CONNECTIONS IN THESE DRAWINGS ARE INTENDED FOR GUIDENCE ONLY. FOUNDATION AND SLAB WORKS SHOULD BE DESIGNED AND APPROVED BY A LOCAL STRUCTURAL ENGINEER.
7. THE COMPANY RETAINS FULL TITLE AND OWNERSHIP OF THESE PLANS AND DESIGNS. ANY UNAUTHORISED USE, REPRODUCTION, OR DISTRIBUTION OF THESE PLANS, WHETHER IN WHOLE OR PART, IS EXPRESSLY PROHIBITED WITHOUT PRIOR WRITTEN CONSENT.

| No. | Revision | Date |
|-----|----------|------|
|     |          |      |
|     |          |      |
ISSUED FOR:

Issued for information

Issued for client approval

Issued for fabrication

Issued for construction

Firefly

DRAWING TITLE:

Details 1

DRAWN BY:

Mladin Monica-Mihaela

SCALE:


1 : 6

DRAWING NO:


A21

DATE:


04.03.2024

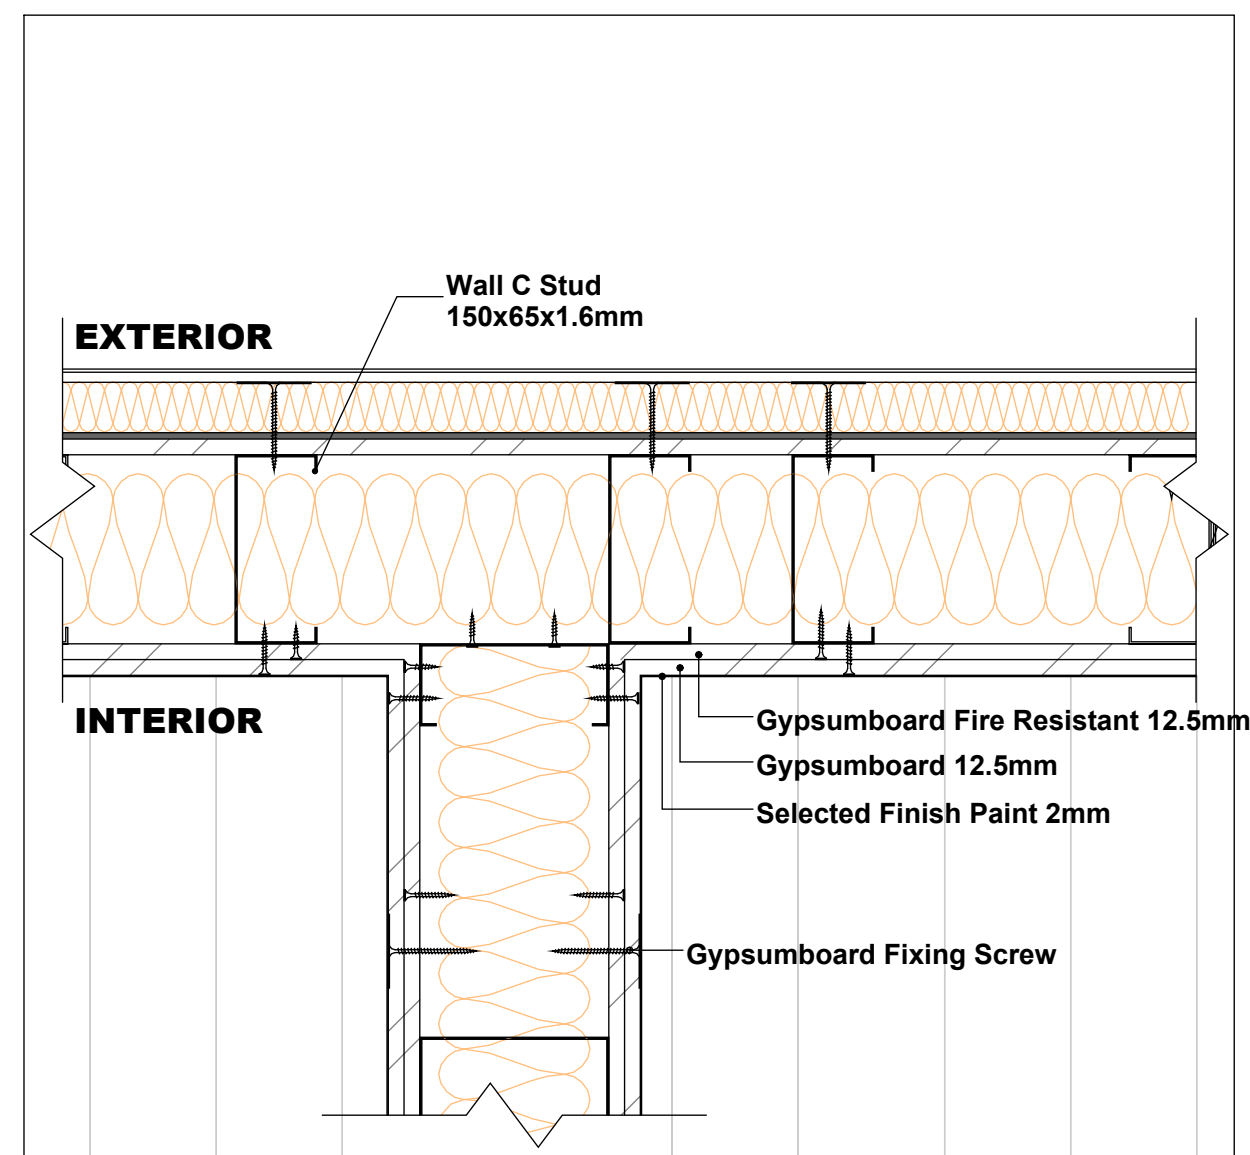

D1:Exterior interior wall conection / Sc. 1:6

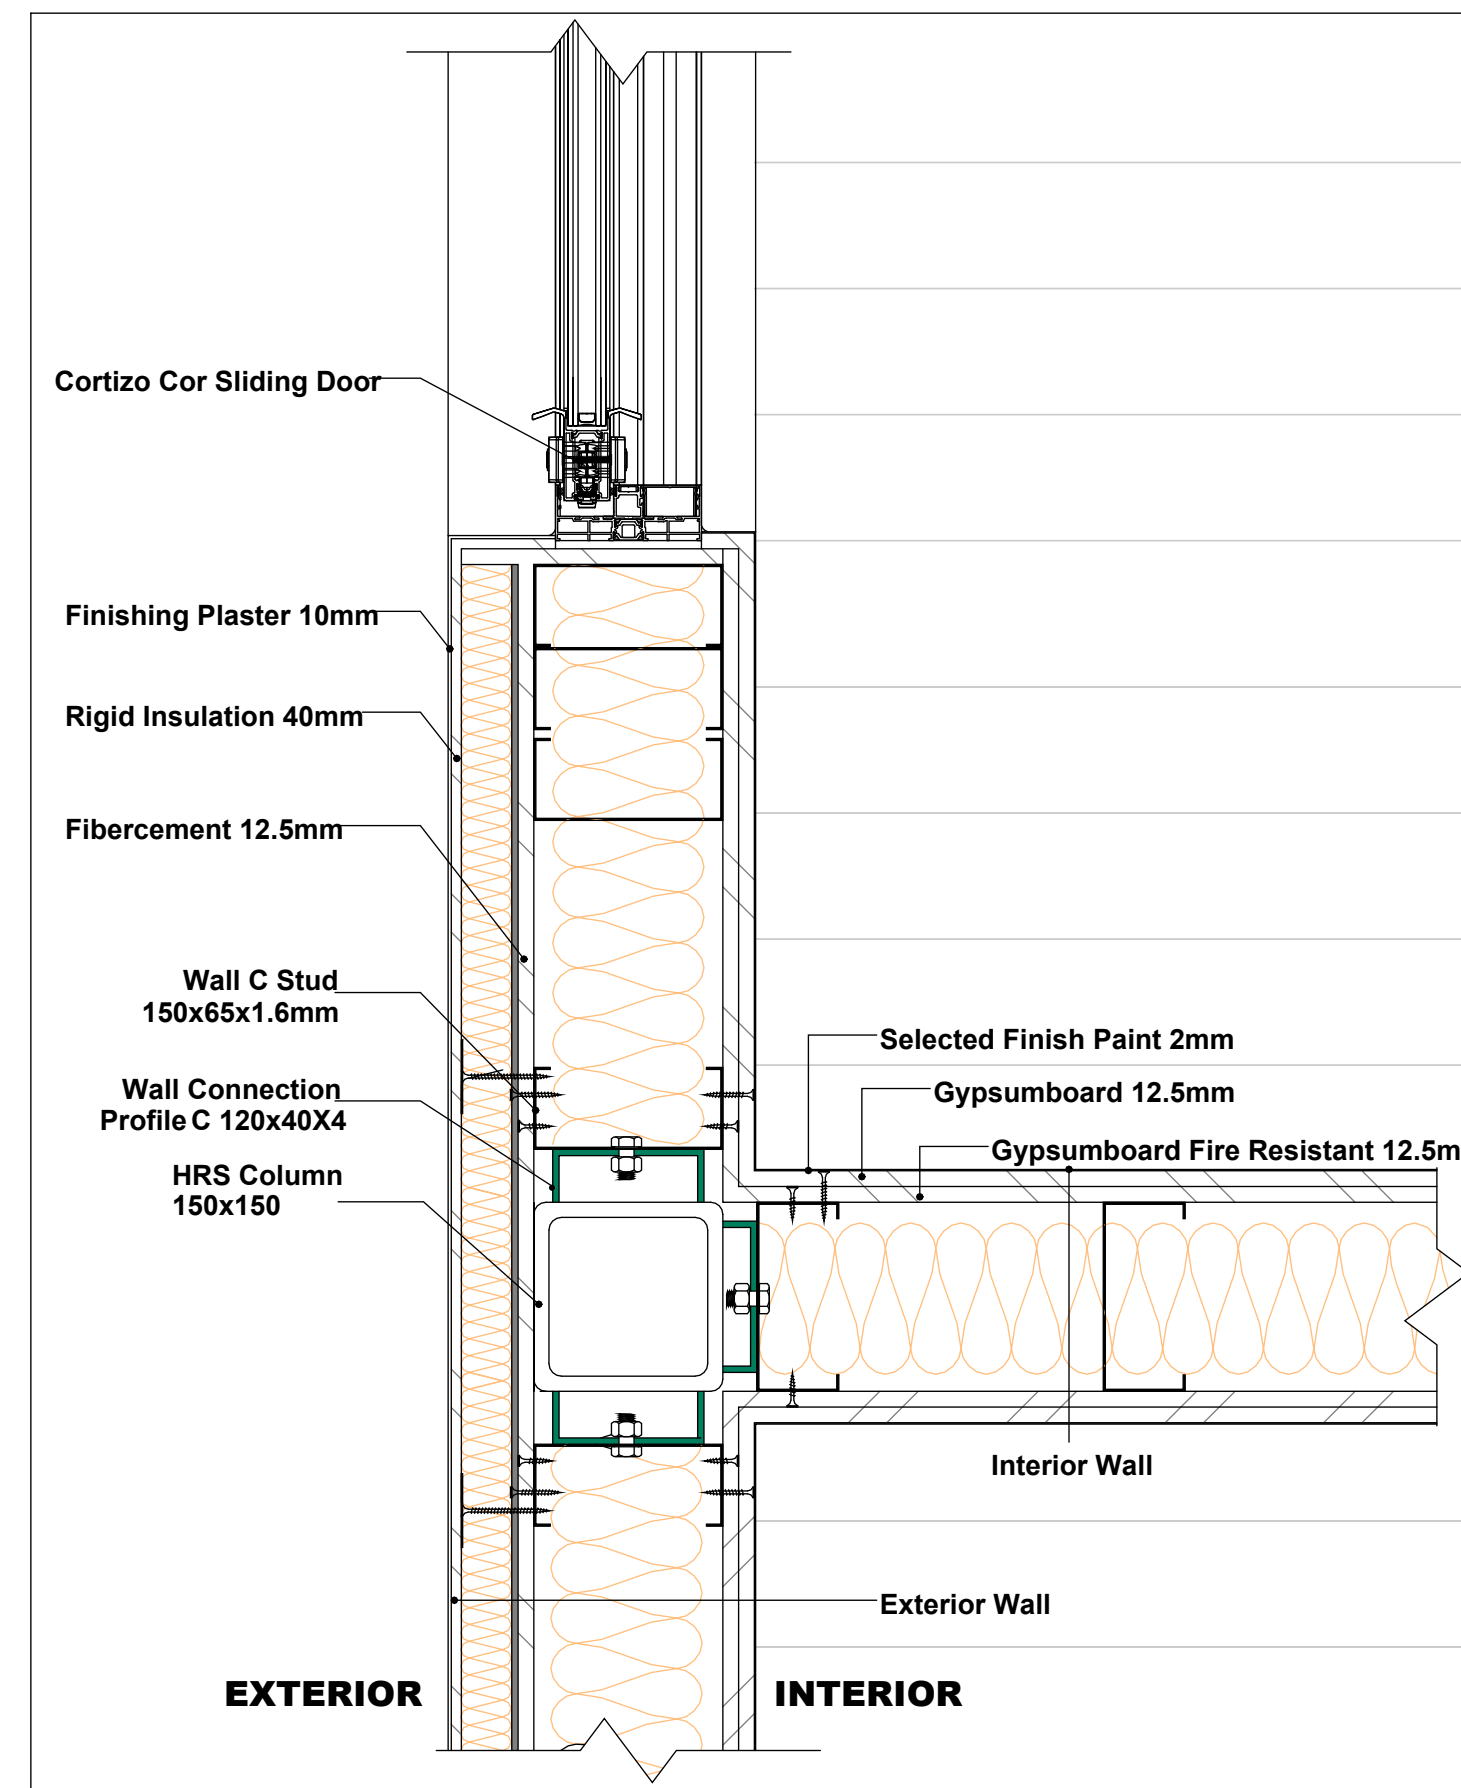

D2:Wall conection detail / Sc. 1:6

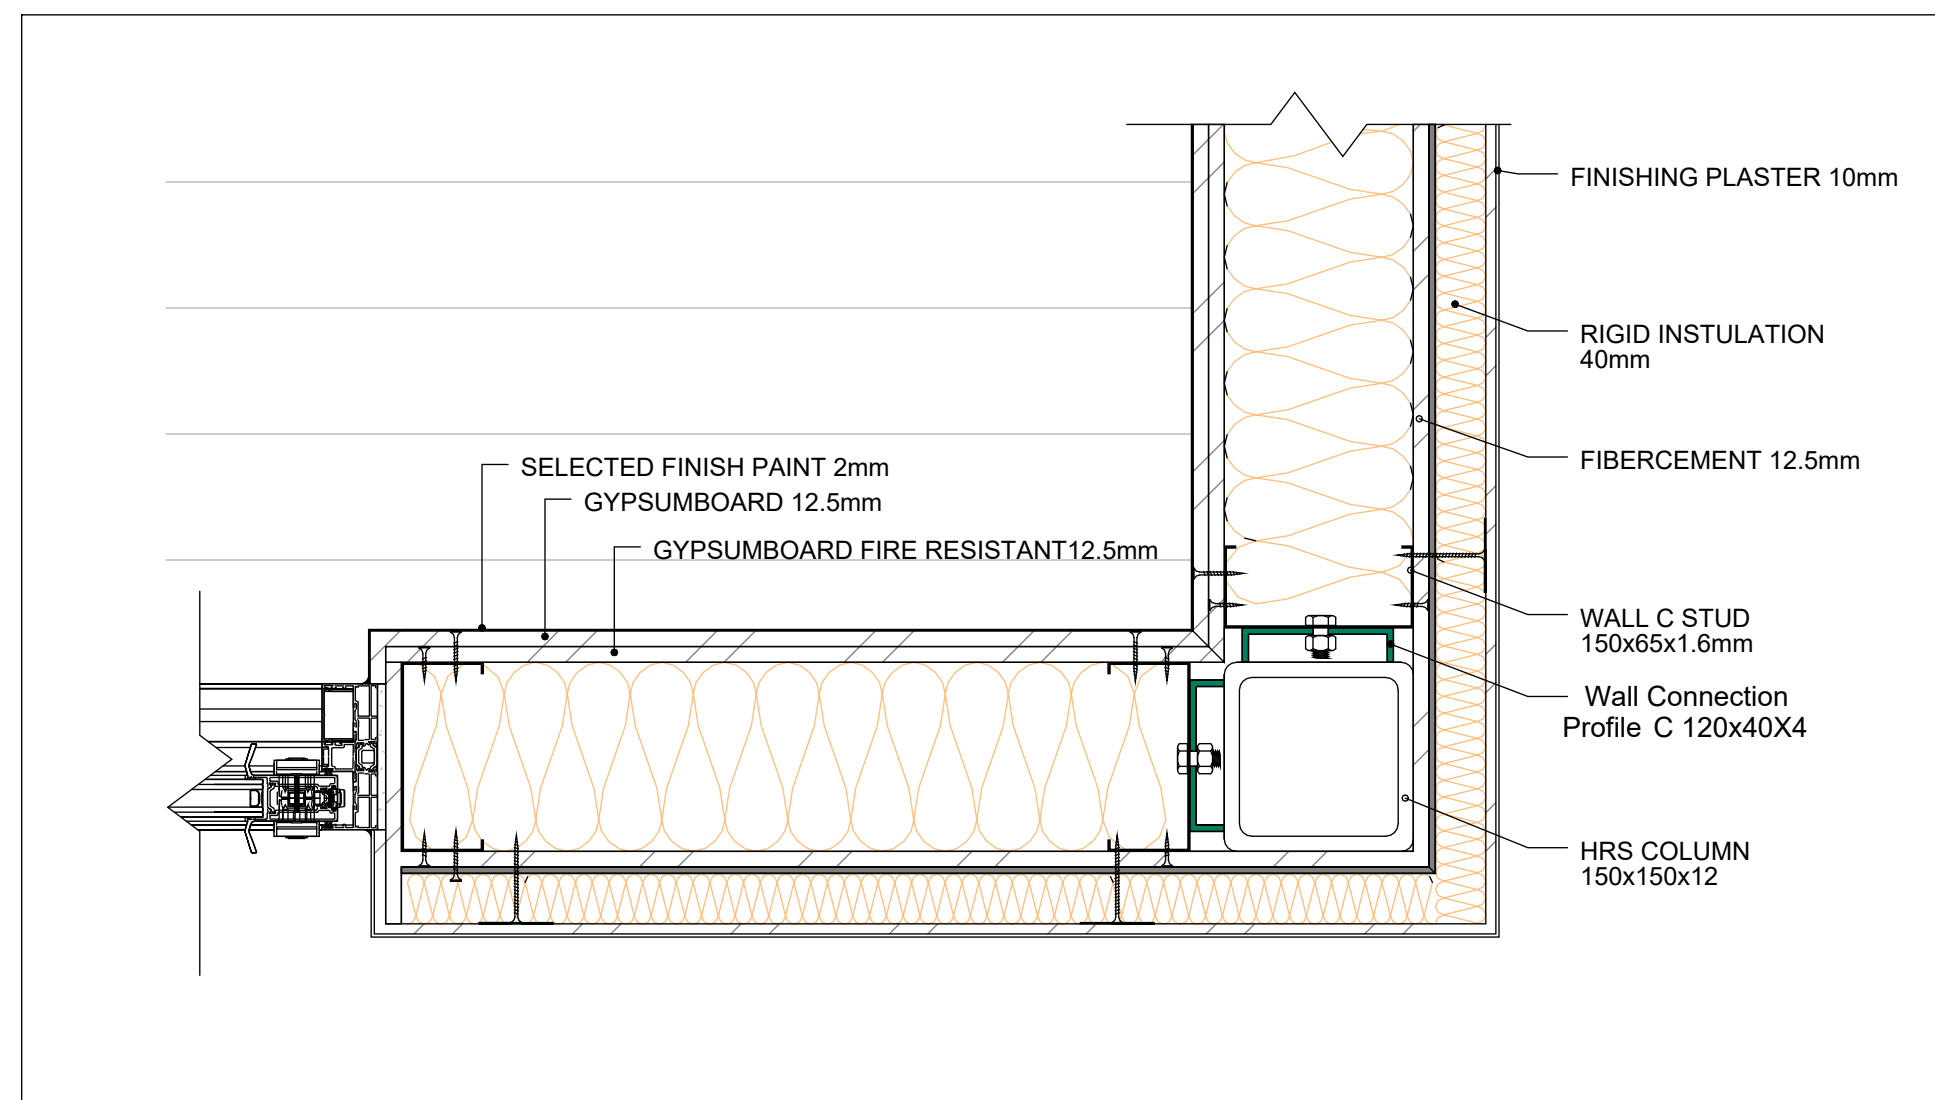

D3:Corner exterior wall conection / Sc. 1:6

## Wall Details

### Exterior Wall

- Interior side
  - Selected Paint Finish
  - Gypsum Wall Board - Moisture resistant (12.5mm)
  - Gypsum Wall Board - Fire resistant (12.5mm)
  - Light Gauge Steel Frame (150mm)
  - Mineral Rockwool (150mm)
  - Cementboard (12.5mm)
  - Rockwool Insulation Panel 40mm (ETICS)
  - STO Cement-free Reinforcing Coat with Mesh
  - STO Decorative Render Finish Plaster
- Exterior side

### Interior Wall

- Interior side
  - Selected Paint Finish
  - Gypsum Wall Board - Moisture resistant (12.5mm)
  - Gypsum Wall Board - Fire resistant (12.5mm)
  - Light Gauge Steel Frame (150mm)
  - Mineral Rockwool (150mm)
  - Gypsum Wall Board - Fire resistant (12.5mm)
  - Gypsum Wall Board - Moisture resistant (12.5mm)
  - Selected Paint Finish
- Interior side

1. THESE DRAWINGS MUST BE CHECKED BY THE CUSTOMER OR CONTRACTOR PRIOR TO APPROVAL. ANY ERRORS OR OMISSIONS MUST BE REPORTED IN WRITING TO BAUHU PRIOR TO COMMENCEMENT OF CONSTRUCTION.
2. ARCHITECTURAL DRAWINGS SHOULD BE READ IN CONJUNCTION WITH STRUCTURAL DETAILING AND FABRICATION GENERAL ASSEMBLY DRAWINGS.
3. FOR CONSTRUCTION PURPOSES, USE ONLY THE LATEST APPROVED DRAWINGS LABELED 'ISSUED FOR CONSTRUCTION'.
4. DO NOT SCALE FROM THIS DRAWING.
5. THE COMPANY OPERATES USING METRIC DIMENSIONS AS THE PRINCIPAL DENOMINATION.
6. ALL CONCRETE WORKS ARE OUTSIDE OF THE SCOPE OF THE COMPANY. INFORMATION REGARDING SLAB DESIGN AND CONNECTIONS IN THESE DRAWINGS ARE INTENDED FOR GUIDENCE ONLY. FOUNDATION AND SLAB WORKS SHOULD BE DESIGNED AND APPROVED BY A LOCAL STRUCTURAL ENGINEER.
7. THE COMPANY RETAINS FULL TITLE AND OWNERSHIP OF THESE PLANS AND DESIGNS. ANY UNAUTHORISED USE, REPRODUCTION, OR DISTRIBUTION OF THESE PLANS, WHETHER IN WHOLE OR PART, IS EXPRESSLY PROHIBITED WITHOUT PRIOR WRITTEN CONSENT.

| No. | Revision | Date |
|-----|----------|------|
|     |          |      |
|     |          |      |
ISSUED FOR:

Issued for information

Issued for client approval

Issued for fabrication

Issued for construction

Firefly

DRAWING TITLE:

Details 2

DRAWN BY:

Mladin Monica-Mihaela

SCALE:

1 : 8


DRAWING NO:

A22


DATE:

04.03.2024

D4: Roof/parapet detail Sc: 1:8

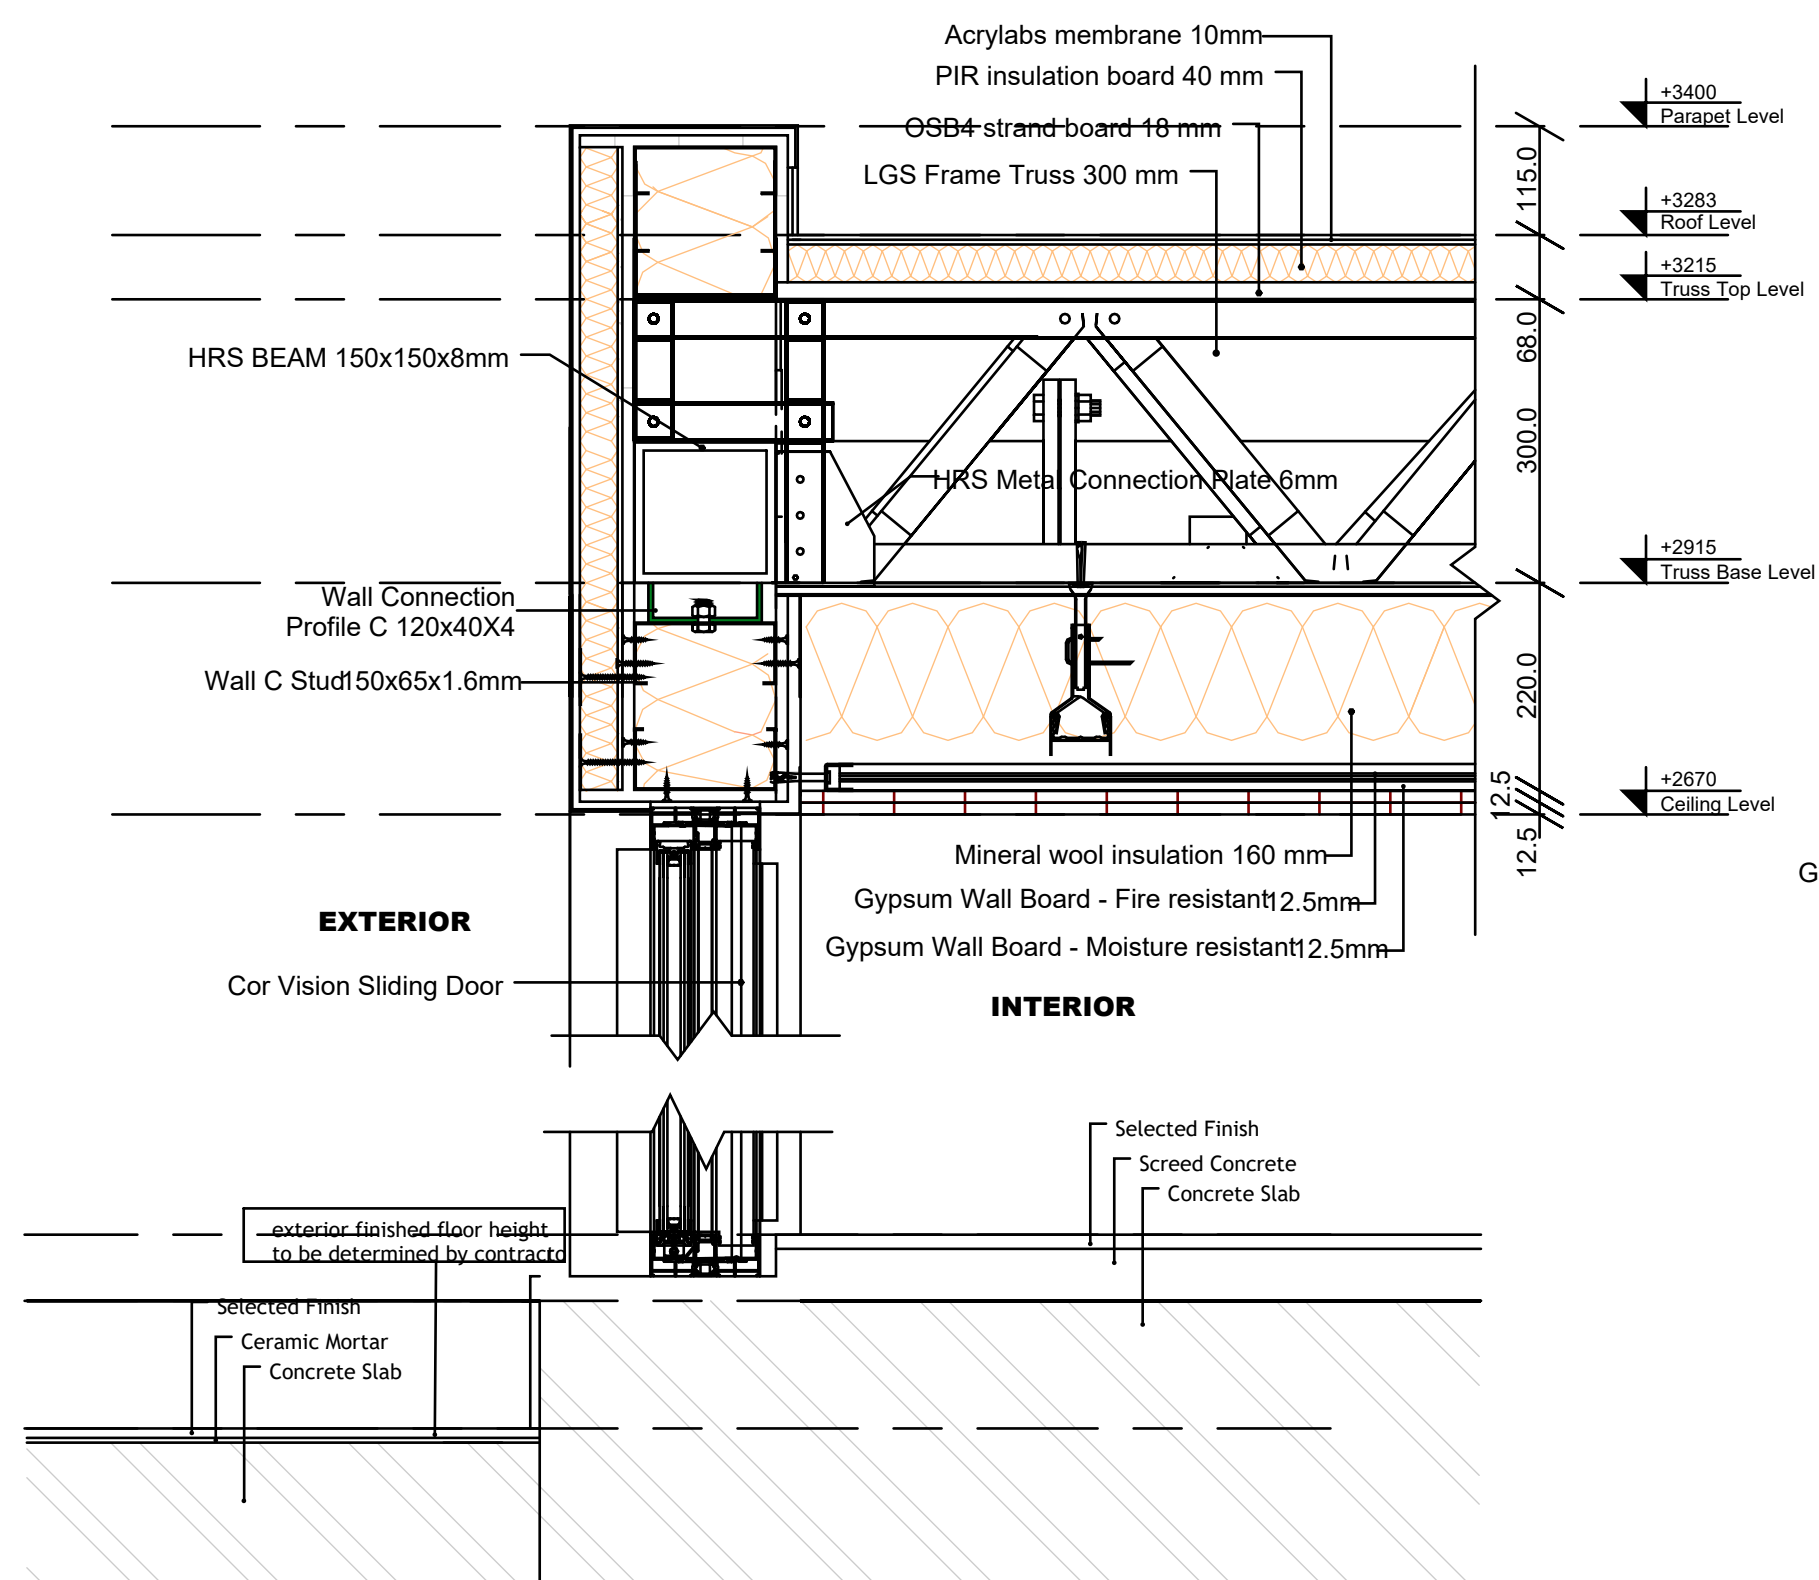

D5: Roof/parapet detail Sc: 1:8

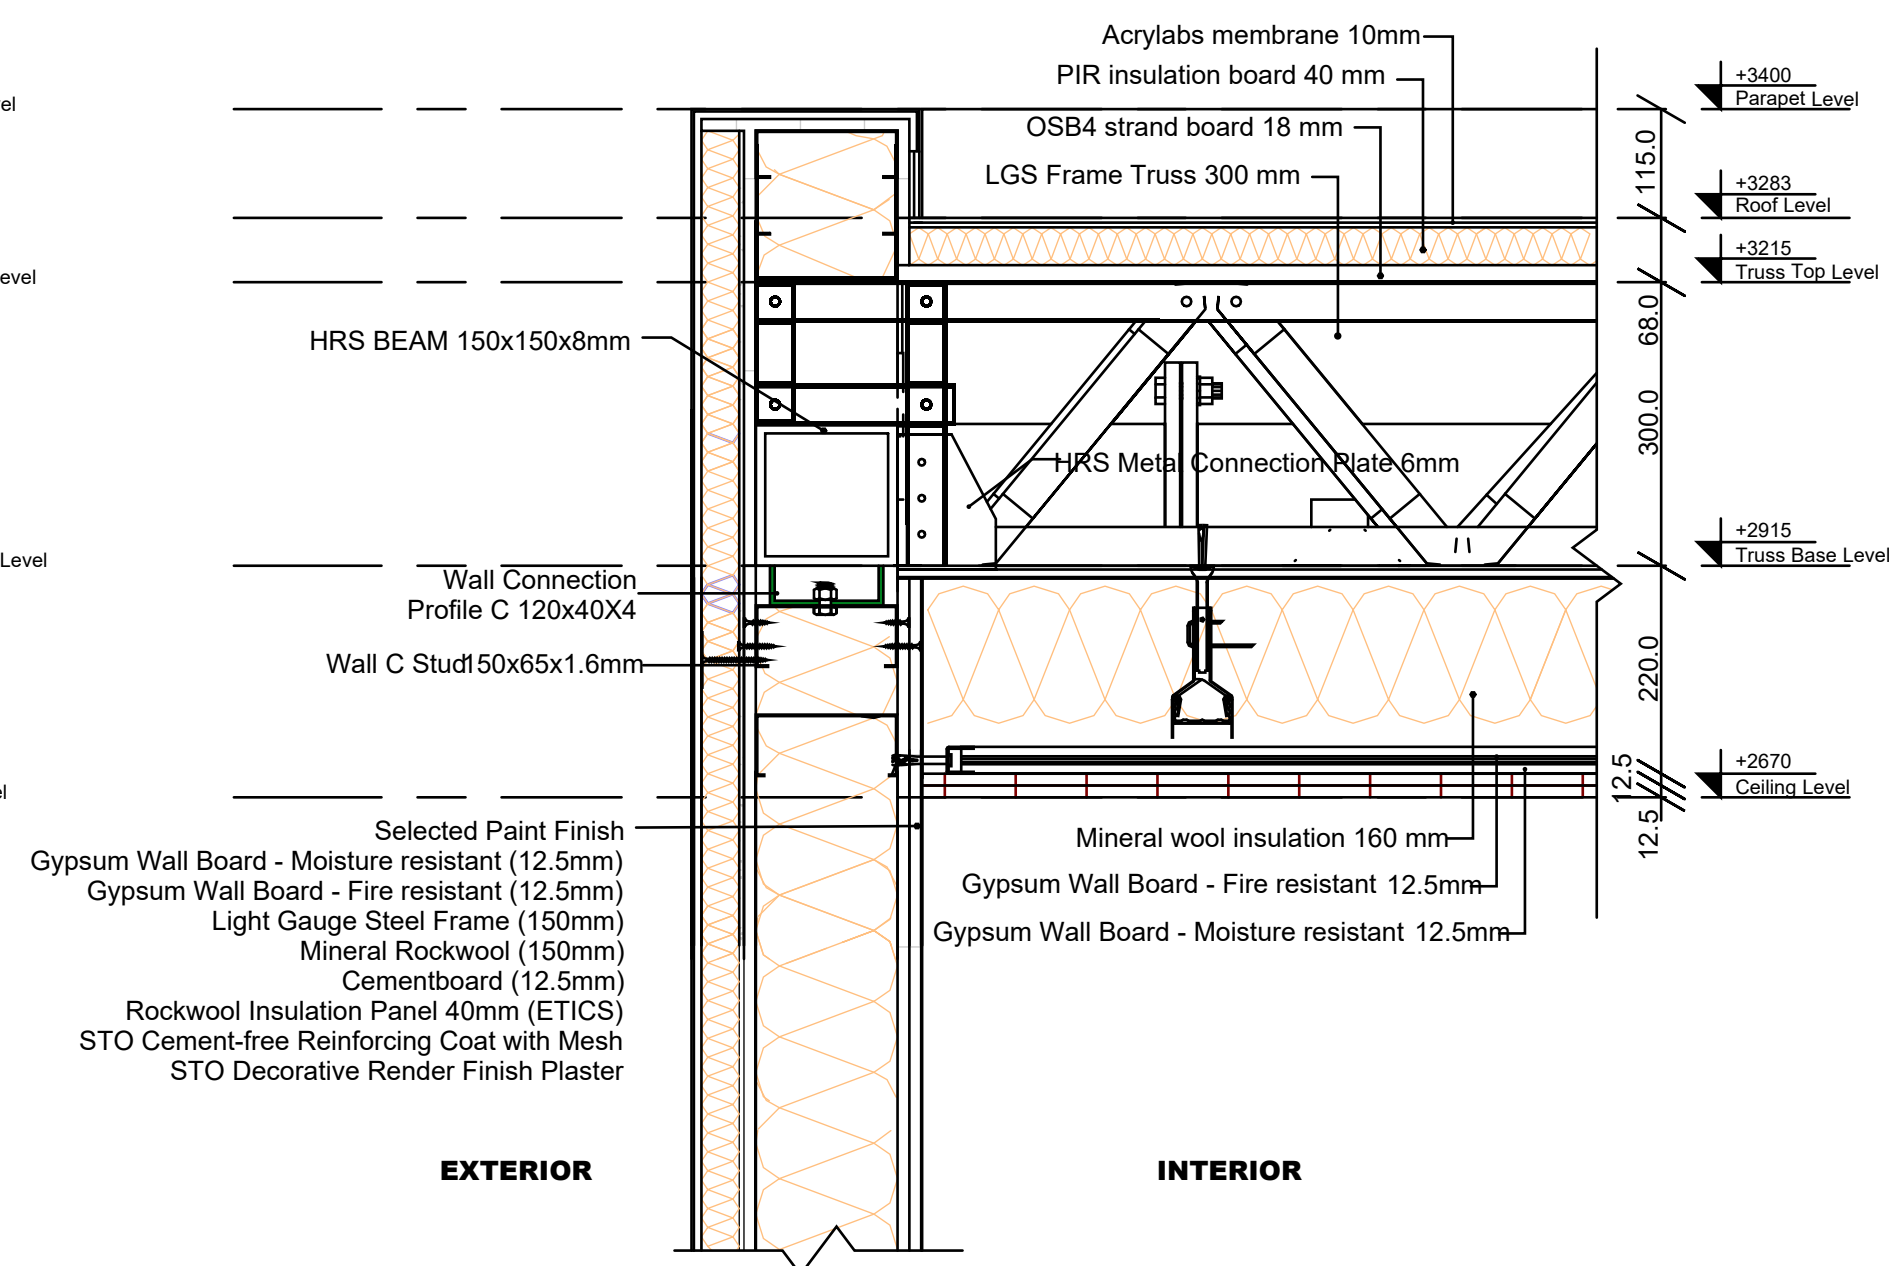

D6: Ground Floor detail Sc: 1:8

1. THESE DRAWINGS MUST BE CHECKED BY THE CUSTOMER OR CONTRACTOR PRIOR TO APPROVAL. ANY ERRORS OR OMISSIONS MUST BE REPORTED IN WRITING TO BAUHU PRIOR TO COMMENCEMENT OF CONSTRUCTION.
2. ARCHITECTURAL DRAWINGS SHOULD BE READ IN CONJUNCTION WITH STRUCTURAL DETAILING AND FABRICATION GENERAL ASSEMBLY DRAWINGS.
3. FOR CONSTRUCTION PURPOSES, USE ONLY THE LATEST APPROVED DRAWINGS LABELED 'ISSUED FOR CONSTRUCTION'.
4. DO NOT SCALE FROM THIS DRAWING.
5. THE COMPANY OPERATES USING METRIC DIMENSIONS AS THE PRINCIPAL DENOMINATION.
6. ALL CONCRETE WORKS ARE OUTSIDE OF THE SCOPE OF THE COMPANY. INFORMATION REGARDING SLAB DESIGN AND CONNECTIONS IN THESE DRAWINGS ARE INTENDED FOR GUIDENCE ONLY. FOUNDATION AND SLAB WORKS SHOULD BE DESIGNED AND APPROVED BY A LOCAL STRUCTURAL ENGINEER.
7. THE COMPANY RETAINS FULL TITLE AND OWNERSHIP OF THESE PLANS AND DESIGNS. ANY UNAUTHORISED USE, REPRODUCTION, OR DISTRIBUTION OF THESE PLANS, WHETHER IN WHOLE OR PART, IS EXPRESSLY PROHIBITED WITHOUT PRIOR WRITTEN CONSENT.

| No. | Revision | Date |
|-----|----------|------|
|     |          |      |
|     |          |      |
ISSUED FOR:

Issued for information

Issued for client approval

Issued for fabrication

Issued for construction

Firefly

|                |                       |
|----------------|-----------------------|
| DRAWING TITLE: | Schedules             |
| DRAWN BY:      | Mladin Monica-Mihaela |
| SCALE:         | 1 : 5                 |
| DRAWING NO:    | A23                   |
| DATE:          | 04.03.2024            |

Interior Schedule

| Room                     | Perimeter | Floor    |           |                      | Ceiling  |                 | Walls            |                                |
|--------------------------|-----------|----------|-----------|----------------------|----------|-----------------|------------------|--------------------------------|
|                          |           | Area sqm | Perimeter | Finish               | Area sqm | Finish          | Area sqm         | Finish                         |
| Living room+Kitchen      | 1         | 46.77    | 27592     | Ecoliving Pearl OG02 | 46.77    | Client supplied | 49.770<br>4.0950 |                                |
| Master Bedroom           | 2         | 16.30    | 16392     |                      | 16.30    |                 | 35.972           |                                |
| Master En-Suite Bathroom | 3         | 16.15    | 20190     |                      | 16.15    |                 | 32.106<br>2.119  |                                |
| Bedroom 1                | 4         | 20.71    | 20992     |                      | 20.71    |                 | 47.33            |                                |
| Bathroom 1               | 5         | 7.19     | 12288     |                      | 7.19     |                 | 14.863<br>2.272  |                                |
| Bedroom 2                | 6         | 20.71    | 20992     |                      | 20.71    |                 | 40.639           |                                |
| Bathroom 2               | 7         | 7.19     | 12288     |                      | 7.19     |                 | 14.863<br>2.272  |                                |
| Total                    |           | 135.02   | 130 734   |                      | 176.06   | Client supplied | 4.391            | Halma Bege HM25R               |
|                          |           |          |           |                      |          |                 | 6.015            | 353white concrete reproduction |
|                          |           |          |           |                      |          |                 | 349.318          | Client supplied                |

| <div>Interior paint wall finish and ceiling<br/>Colour:white</div> <div>Exterior wall finish<br/>Stolit K fine grain exterior plaster<br/>Colour: pure white</div>   | <div>Interior doors and furniture</div> <div>Furniture type: Compincar, model 1003</div> <div>Interior doors:Compincar:Model 314</div>   | <div><div>BAUHU</div><div>MODULAR • BUILDING • SOLUTIONS</div></div> <div><div>1. THESE DRAWINGS MUST BE CHECKED BY THE CUSTOMER OR CONTRACTOR PRIOR TO APPROVAL. ANY ERRORS OR OMISSIONS MUST BE REPORTED IN WRITING TO BAUHU PRIOR TO COMMENCEMENT OF CONSTRUCTION.</div><div>2. ARCHITECTURAL DRAWINGS SHOULD BE READ IN CONJUNCTION WITH STRUCTURAL DETAILING AND FABRICATION GENERAL ASSEMBLY DRAWINGS.</div><div>3. FOR CONSTRUCTION PURPOSES, USE ONLY THE LATEST APPROVED DRAWINGS LABELED 'ISSUED FOR CONSTRUCTION'.</div><div>4. DO NOT SCALE FROM THIS DRAWING.</div><div>5. THE COMPANY OPERATES USING METRIC DIMENSIONS AS THE PRINCIPAL DENOMINATION.</div><div>6. ALL CONCRETE WORKS ARE OUTSIDE OF THE SCOPE OF THE COMPANY. INFORMATION REGARDING SLAB DESIGN AND CONNECTIONS IN THESE DRAWINGS ARE INTENDED FOR GUIDENCE ONLY. FOUNDATION AND SLAB WORKS SHOULD BE DESIGNED AND APPROVED BY A LOCAL STRUCTURAL ENGINEER.</div><div>7. THE COMPANY RETAINS FULL TITLE AND OWNERSHIP OF THESE PLANS AND DESIGNS. ANY UNAUTHORISED USE, REPRODUCTION, OR DISTRIBUTION OF THESE PLANS, WHETHER IN WHOLE OR PART, IS EXPRESSLY PROHIBITED WITHOUT PRIOR WRITTEN CONSENT.</div></div> |     |          |      |  |  |  |  |  |  |  |  |  |  |  |  |  |  |  |  |  |  |  |  |  |  |  |  |  |  |  |  |  |  |
|---|---|---|-----|----------|------|--|--|--|--|--|--|--|--|--|--|--|--|--|--|--|--|--|--|--|--|--|--|--|--|--|--|--|--|--|--|
| <div><div>Windows</div><div>Refer to plans for individual opening detail and dimensions<br/>CORTIZO COR VISION aluminium window systems.<br/>Finish – Pure White<br/>Locking – integrated<br/>Handles – integrated<br/>Fixing kit<br/>Anthracite RAL7016<br/><a href="https://www.cortizo.com/en/sistemas/ver/55/cor-vision-sliding.html">https://www.cortizo.com/en/sistemas/ver/55/cor-vision-sliding.html</a></div><div><div>Glazing</div><div>Double glazed sealed glass unit - Laminated security glass<br/>4mm +<br/>2mmPVB+ 4mm + 16mm argon filled void + 6mm SNX low E<br/>SunGuard SNX60 extra selective solar control glass<br/><a href="https://www.guardianglass.com/gb/en/our-glass/solar-controlglass/sunguard-extraselective/product.690.snx-60?page=1&amp;region=GB&amp;networkOfSuppliers=&amp;sortBy=a-z">https://www.guardianglass.com/gb/en/our-glass/solar-controlglass/sunguard-extraselective/product.690.snx-60?page=1&amp;region=GB&amp;networkOfSuppliers=&amp;sortBy=a-z</a></div></div></div> | <div>Interior/exterior<br/>Innova Brick Beige IV23R<br/>34x66,5, 13,4"x26,2" / R17</div> <div>Interior shower<br/>Travertino Bege RT27R / R21<br/>32,5x90, 12,8"x35,4"</div> <div>Kitchen blacksplash<br/>Brilho / Glossy vogue VO01R / R16<br/>34x66,5, 13,4"x26,2"</div> <div>Floor<br/>Halma - Cinza<br/>45x45, 18"x18"</div> <div>Ceiling interior and exterior<br/>cladding</div> | <table><tr><th>No.</th><th>Revision</th><th>Date</th></tr><tr><td></td><td></td><td></td></tr><tr><td></td><td></td><td></td></tr><tr><td></td><td></td><td></td></tr><tr><td></td><td></td><td></td></tr><tr><td></td><td></td><td></td></tr><tr><td></td><td></td><td></td></tr><tr><td></td><td></td><td></td></tr><tr><td></td><td></td><td></td></tr><tr><td></td><td></td><td></td></tr><tr><td></td><td></td><td></td></tr></table> <div><div>ISSUED FOR:</div><div><div>Issued for information</div><div>Issued for client approval</div><div>Issued for fabrication</div><div>Issued for construction</div></div><div>Firefly</div></div>   | No. | Revision | Date |  |  |  |  |  |  |  |  |  |  |  |  |  |  |  |  |  |  |  |  |  |  |  |  |  |  |  |  |  |  |
| No.   | Revision   | Date   |     |          |      |  |  |  |  |  |  |  |  |  |  |  |  |  |  |  |  |  |  |  |  |  |  |  |  |  |  |  |  |  |  |
|   |   
|   |   
| <div>Kitchen<br/>Nobilis<br/>Front: 427 Alpine white<br/>Worktop: 193 Alpine white<br/>Carcase colour: 060 Alpine white gloss<br/>Front-inside island/tall cabinets: 843 Bergamo oak reproduction</div>   | <div></div>   | <div><div>DRAWING TITLE:</div><div>Finish Schedules</div><div>DRAWN BY:</div><div>Mladin Monica-Mihaela</div><div>SCALE:</div><div>DRAWING NO:</div><div>A24</div><div>DATE:</div><div>04.03.2024</div></div>   |     |          |      |  |  |  |  |  |  |  |  |  |  |  |  |  |  |  |  |  |  |  |  |  |  |  |  |  |  |  |  |  |  |

FRONT ELEVATION

1. THESE DRAWINGS MUST BE CHECKED BY THE CUSTOMER OR CONTRACTOR PRIOR TO APPROVAL. ANY ERRORS OR OMISSIONS MUST BE REPORTED IN WRITING TO BAUHU PRIOR TO COMMENCEMENT OF CONSTRUCTION.
2. ARCHITECTURAL DRAWINGS SHOULD BE READ IN CONJUNCTION WITH STRUCTURAL DETAILING AND FABRICATION GENERAL ASSEMBLY DRAWINGS.
3. FOR CONSTRUCTION PURPOSES, USE ONLY THE LATEST APPROVED DRAWINGS LABELED 'ISSUED FOR CONSTRUCTION'.
4. DO NOT SCALE FROM THIS DRAWING.
5. THE COMPANY OPERATES USING METRIC DIMENSIONS AS THE PRINCIPAL DENOMINATION.
6. ALL CONCRETE WORKS ARE OUTSIDE OF THE SCOPE OF THE COMPANY. INFORMATION REGARDING SLAB DESIGN AND CONNECTIONS IN THESE DRAWINGS ARE INTENDED FOR GUIDENCE ONLY. FOUNDATION AND SLAB WORKS SHOULD BE DESIGNED AND APPROVED BY A LOCAL STRUCTURAL ENGINEER.
7. THE COMPANY RETAINS FULL TITLE AND OWNERSHIP OF THESE PLANS AND DESIGNS. ANY UNAUTHORISED USE, REPRODUCTION, OR DISTRIBUTION OF THESE PLANS, WHETHER IN WHOLE OR PART, IS EXPRESSLY PROHIBITED WITHOUT PRIOR WRITTEN CONSENT.

| No. | Revision | Date |
|-----|----------|------|
|     |          |      |
|     |          |      |
ISSUED FOR:

Issued for information

Issued for client approval

Issued for fabrication

Issued for construction

Firefly

DRAWING TITLE:

Ground Floor Dimensions

DRAWN BY:

Mladin Monica-Mihaela

SCALE:

1 : 70

DRAWING NO:

A25

DATE:

04.03.2024

RIGHT ELEVATION

LEFT ELEVATION

BACK ELEVATION

- THESE DRAWINGS MUST BE CHECKED BY THE CUSTOMER OR CONTRACTOR PRIOR TO APPROVAL. ANY ERRORS OR OMISSIONS MUST BE REPORTED IN WRITING TO BAUHU PRIOR TO COMMENCEMENT OF CONSTRUCTION.
- ARCHITECTURAL DRAWINGS SHOULD BE READ IN CONJUNCTION WITH STRUCTURAL DETAILING AND FABRICATION GENERAL ASSEMBLY DRAWINGS.
- FOR CONSTRUCTION PURPOSES, USE ONLY THE LATEST APPROVED DRAWINGS LABELED 'ISSUED FOR CONSTRUCTION'.
- DO NOT SCALE FROM THIS DRAWING.
- THE COMPANY OPERATES USING METRIC DIMENSIONS AS THE PRINCIPAL DENOMINATION.
- ALL CONCRETE WORKS ARE OUTSIDE OF THE SCOPE OF THE COMPANY. INFORMATION REGARDING SLAB DESIGN AND CONNECTIONS IN THESE DRAWINGS ARE INTENDED FOR GUIDENCE ONLY. FOUNDATION AND SLAB WORKS SHOULD BE DESIGNED AND APPROVED BY A LOCAL STRUCTURAL ENGINEER.
- THE COMPANY RETAINS FULL TITLE AND OWNERSHIP OF THESE PLANS AND DESIGNS. ANY UNAUTHORISED USE, REPRODUCTION, OR DISTRIBUTION OF THESE PLANS, WHETHER IN WHOLE OR PART, IS EXPRESSLY PROHIBITED WITHOUT PRIOR WRITTEN CONSENT.

| No. | Revision | Date |
|-----|----------|------|
|     |          |      |
|     |          |      |
ISSUED FOR:

Issued for information

Issued for client approval

Issued for fabrication

Issued for construction

Firefly

DRAWING TITLE:

Rain water drainage plan

DRAWN BY:

Mladin Monica-Mihaela

SCALE:



As indicated

DRAWING NO:


A26

DATE:


04.03.2024

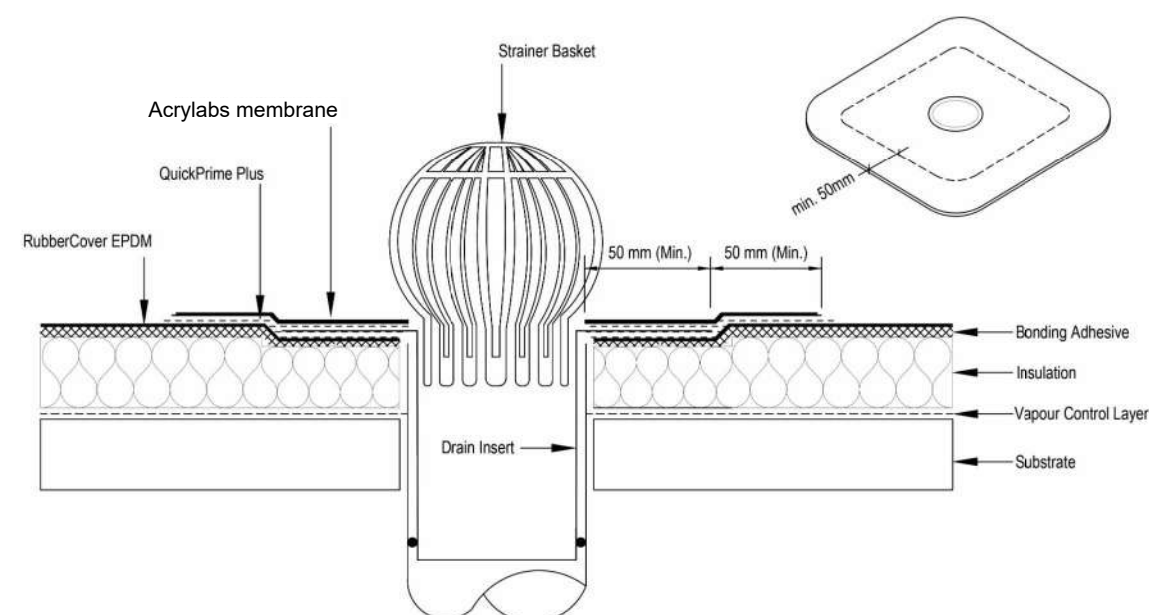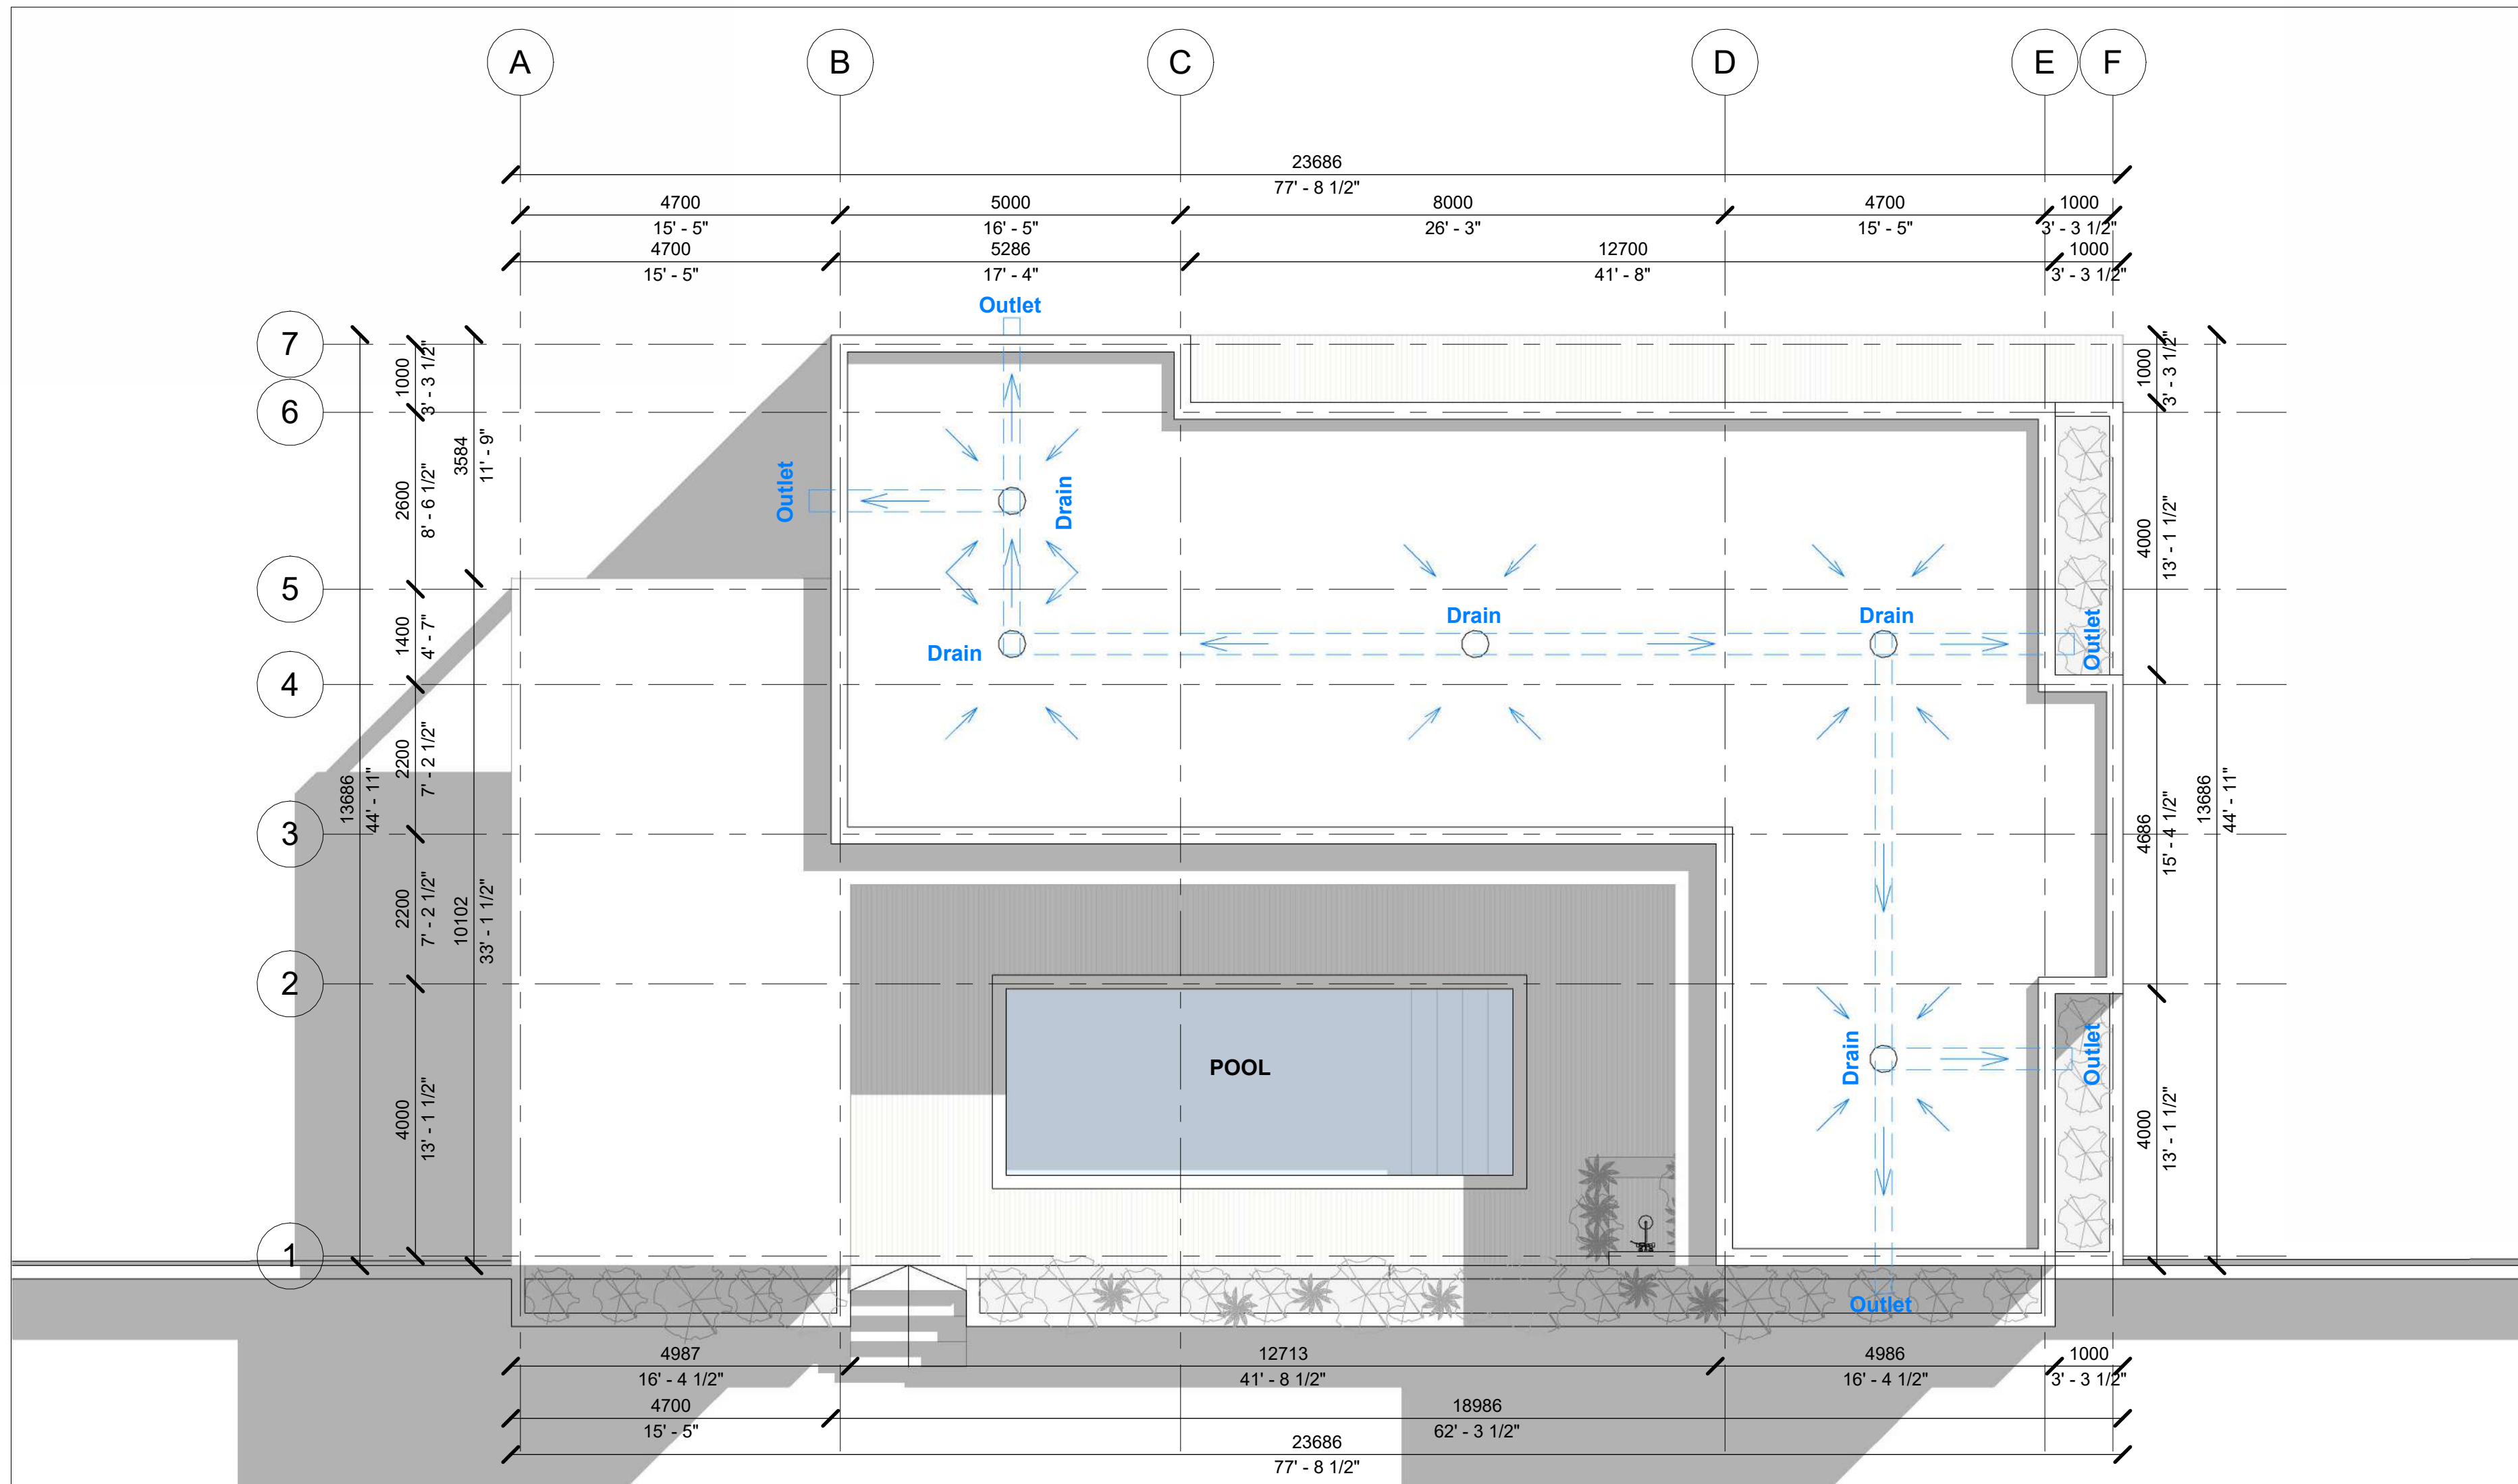

Roof Drain Detail

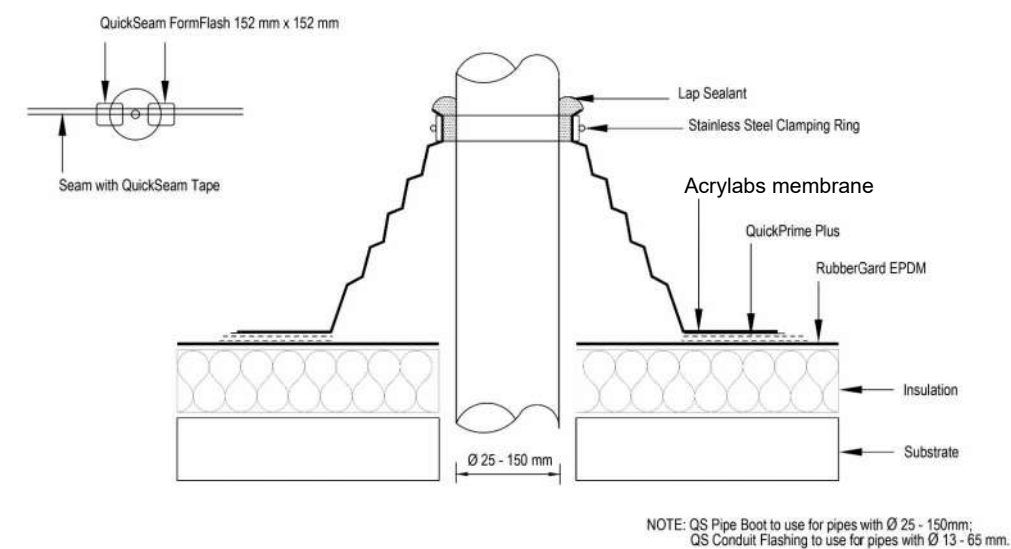

Roof Breather Pipe Detail

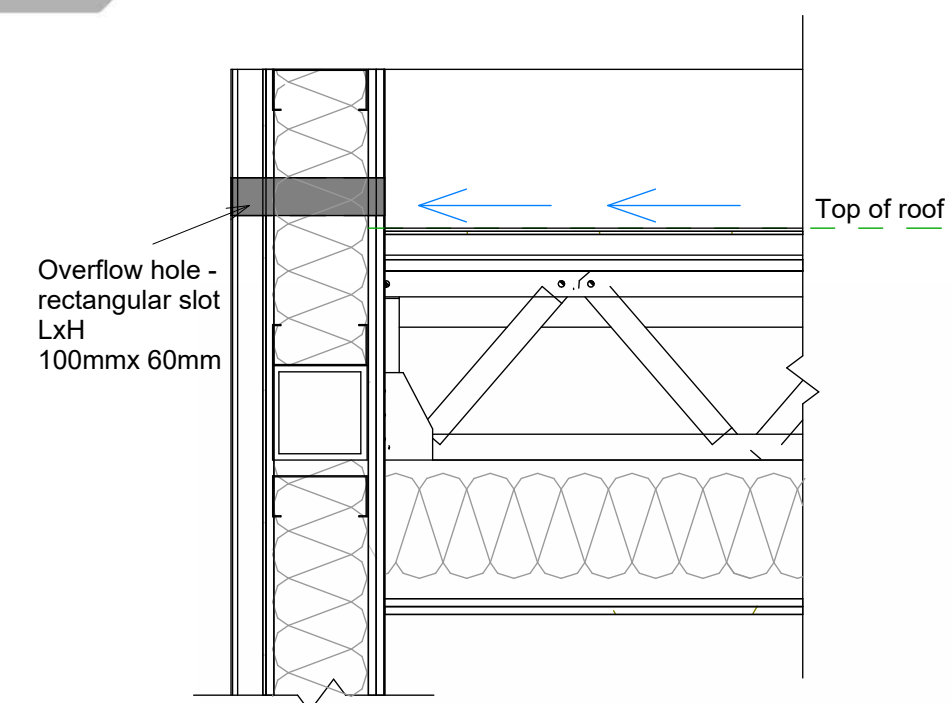

Roof parapet overflow hole

Note!  
\*Contractor to form overflow slots in appropriate locations

HRS CONNECTIONS

1. THESE DRAWINGS MUST BE CHECKED BY THE CUSTOMER OR CONTRACTOR PRIOR TO APPROVAL. ANY ERRORS OR OMISSIONS MUST BE REPORTED IN WRITING TO BAUHU PRIOR TO COMMENCEMENT OF CONSTRUCTION.
2. ARCHITECTURAL DRAWINGS SHOULD BE READ IN CONJUNCTION WITH STRUCTURAL DETAILING AND FABRICATION GENERAL ASSEMBLY DRAWINGS.
3. FOR CONSTRUCTION PURPOSES, USE ONLY THE LATEST APPROVED DRAWINGS LABELED 'ISSUED FOR CONSTRUCTION'.
4. DO NOT SCALE FROM THIS DRAWING.
5. THE COMPANY OPERATES USING METRIC DIMENSIONS AS THE PRINCIPAL DENOMINATION.
6. ALL CONCRETE WORKS ARE OUTSIDE OF THE SCOPE OF THE COMPANY. INFORMATION REGARDING SLAB DESIGN AND CONNECTIONS IN THESE DRAWINGS ARE INTENDED FOR GUIDENCE ONLY. FOUNDATION AND SLAB WORKS SHOULD BE DESIGNED AND APPROVED BY A LOCAL STRUCTURAL ENGINEER.
7. THE COMPANY RETAINS FULL TITLE AND OWNERSHIP OF THESE PLANS AND DESIGNS. ANY UNAUTHORISED USE, REPRODUCTION, OR DISTRIBUTION OF THESE PLANS, WHETHER IN WHOLE OR PART, IS EXPRESSLY PROHIBITED WITHOUT PRIOR WRITTEN CONSENT.

| No. | Revision | Date |
|-----|----------|------|
|     |          |      |
|     |          |      |
ISSUED FOR:

Issued for information

Issued for client approval

Issued for fabrication

Issued for construction

Firefly

DRAWING TITLE:

HRS Connections 3D

DRAWN BY:

Mladin Monica-Mihaela


SCALE:

DRAWING NO:


A27

DATE:


04.03.2024

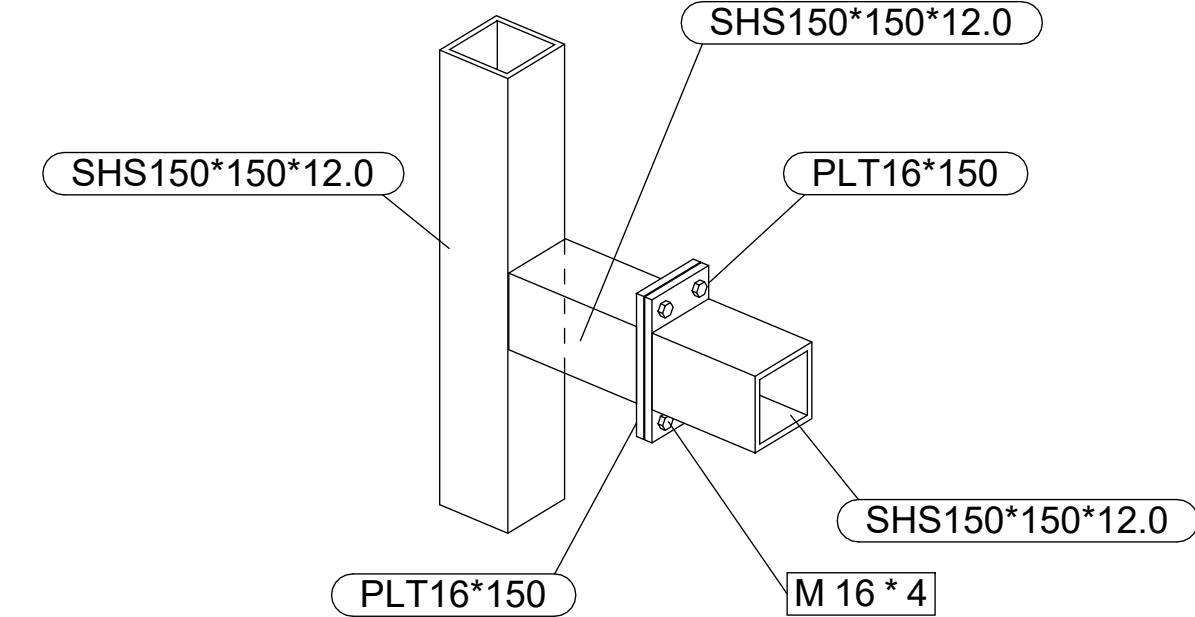


Typical Column Beam Stub Connection

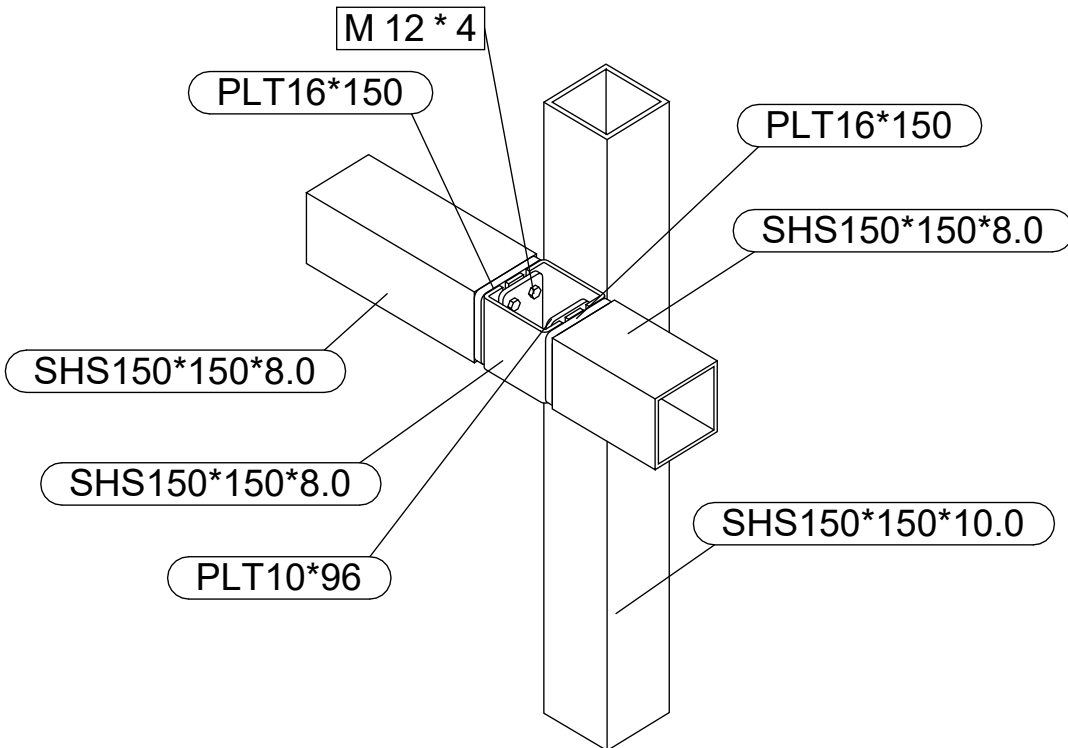


Typical Beam Offset Connection

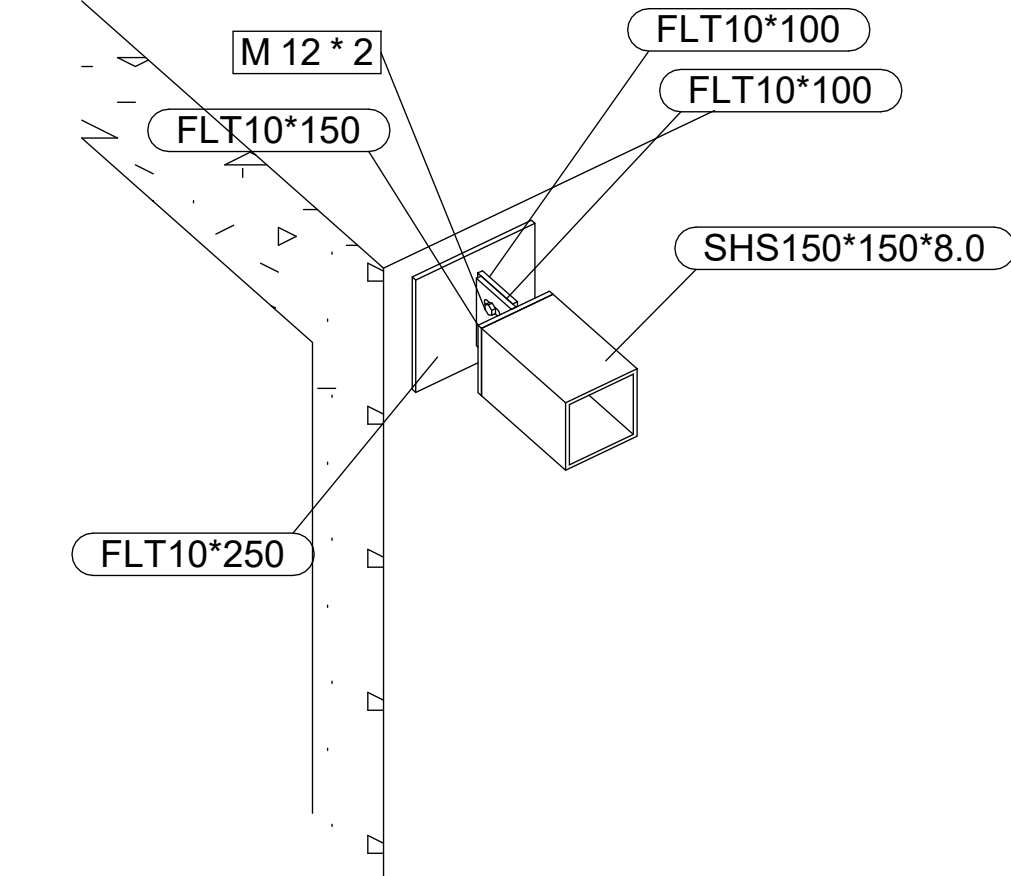


Typical Beam to Concrete Connection

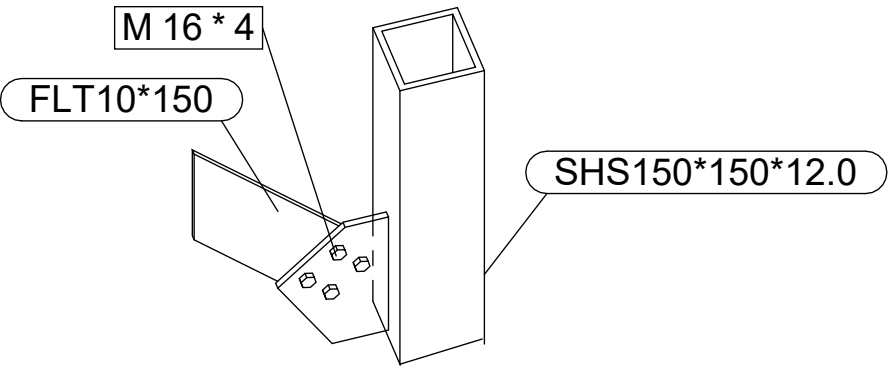


Typical Bracing Connection

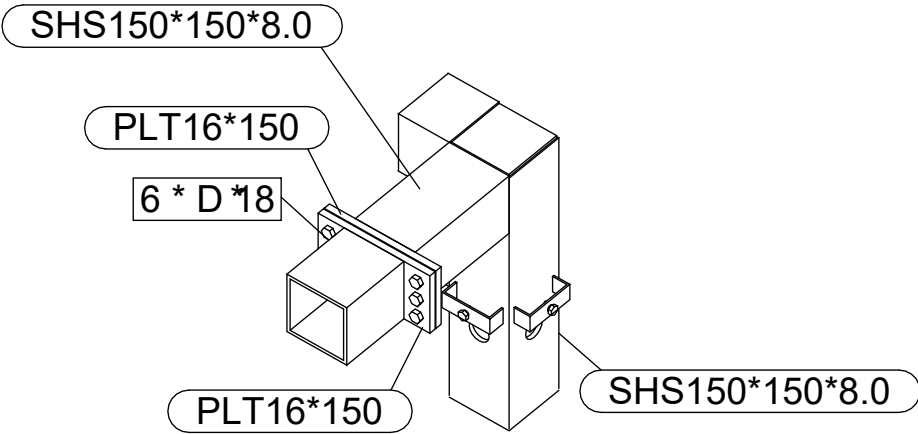


Typical Column to Beam Splice Connection

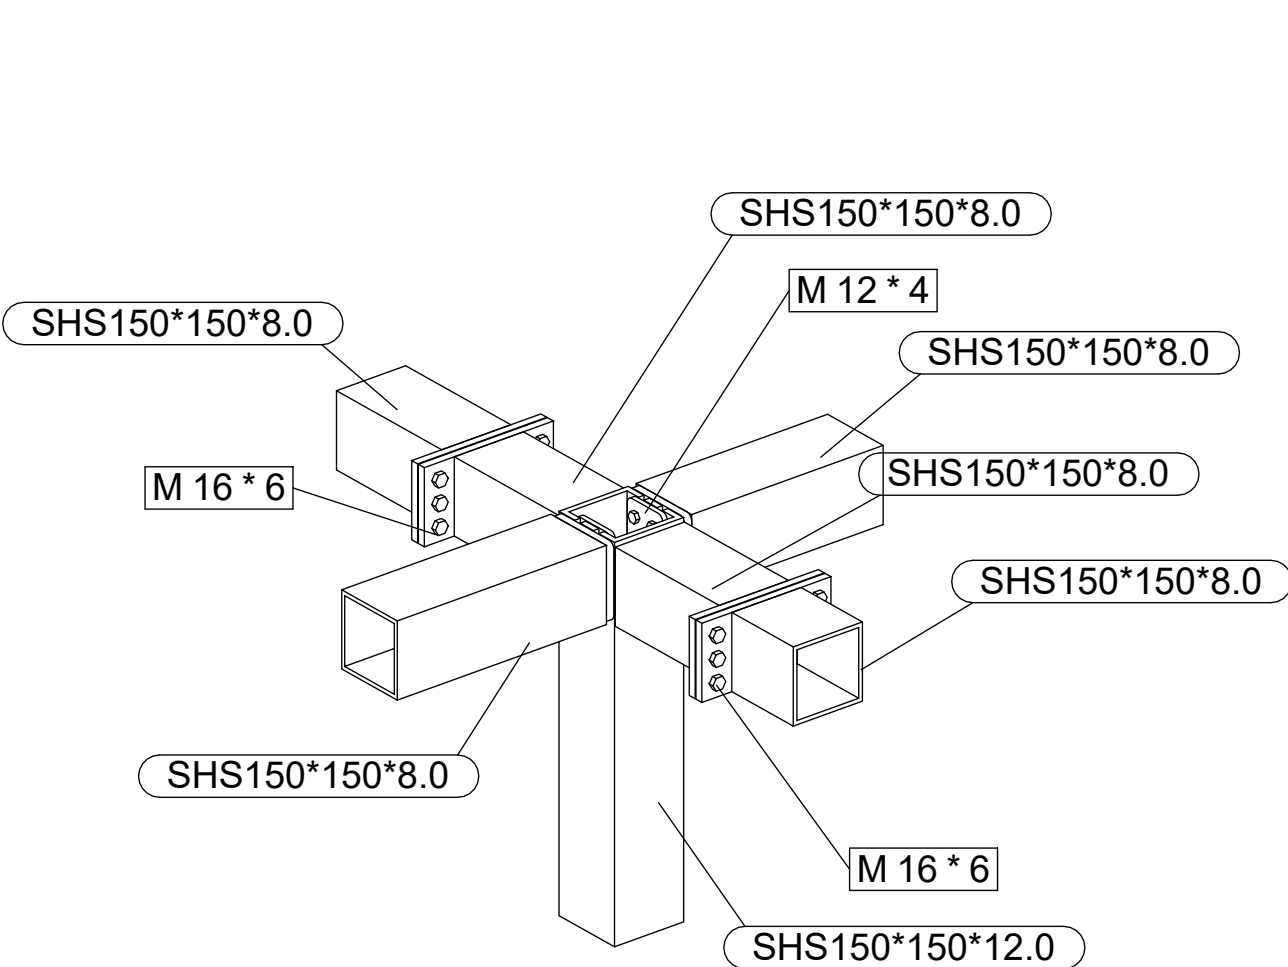

Typical Roof Column Beam Connection

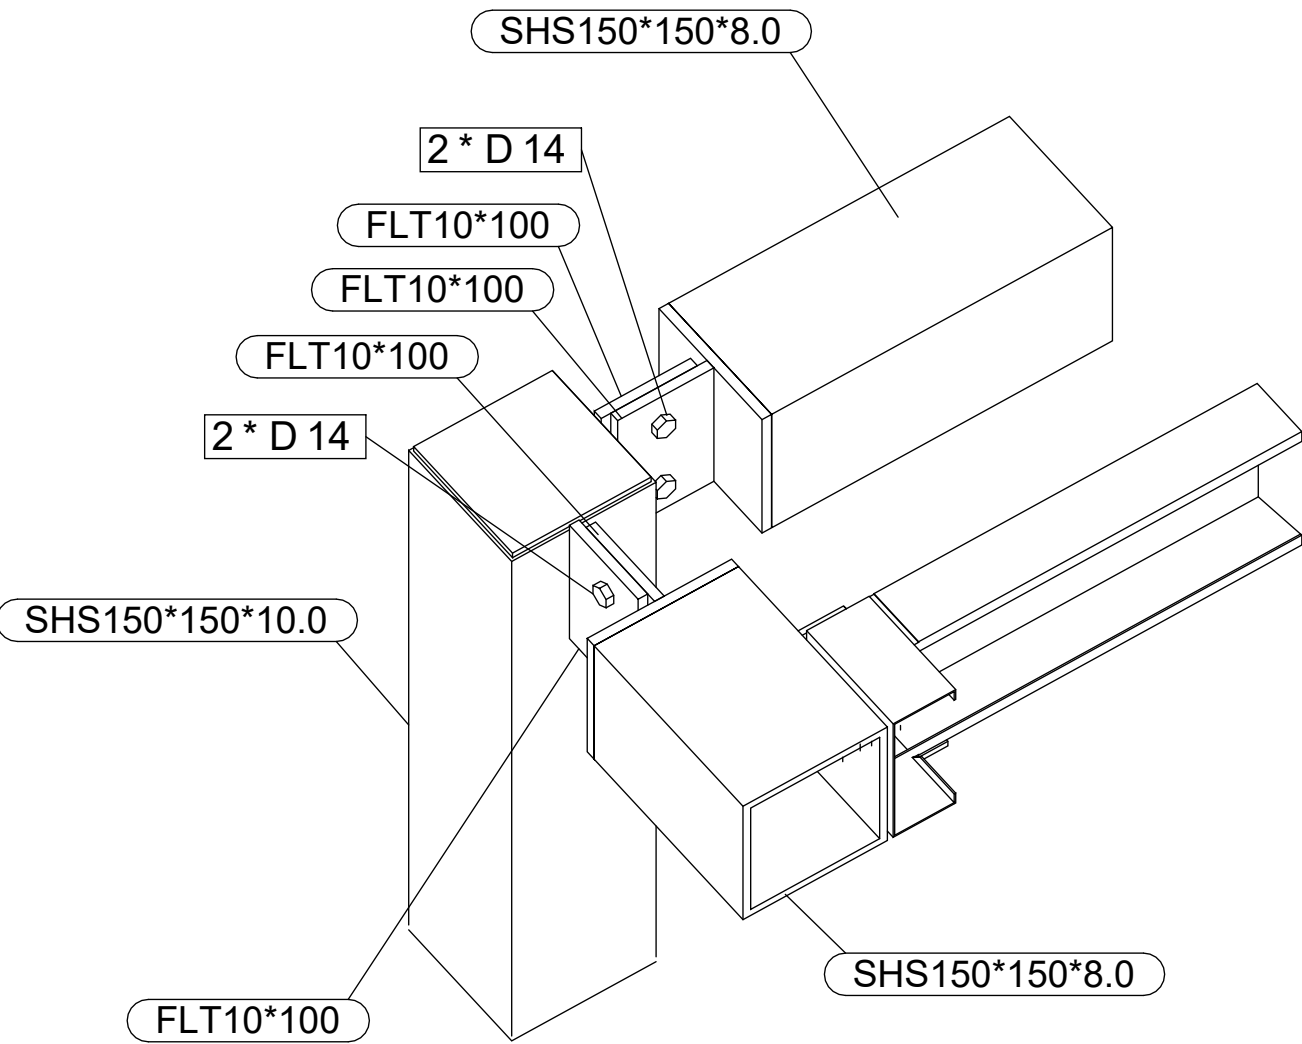


Typical Column to Beam Fine Plate Connection

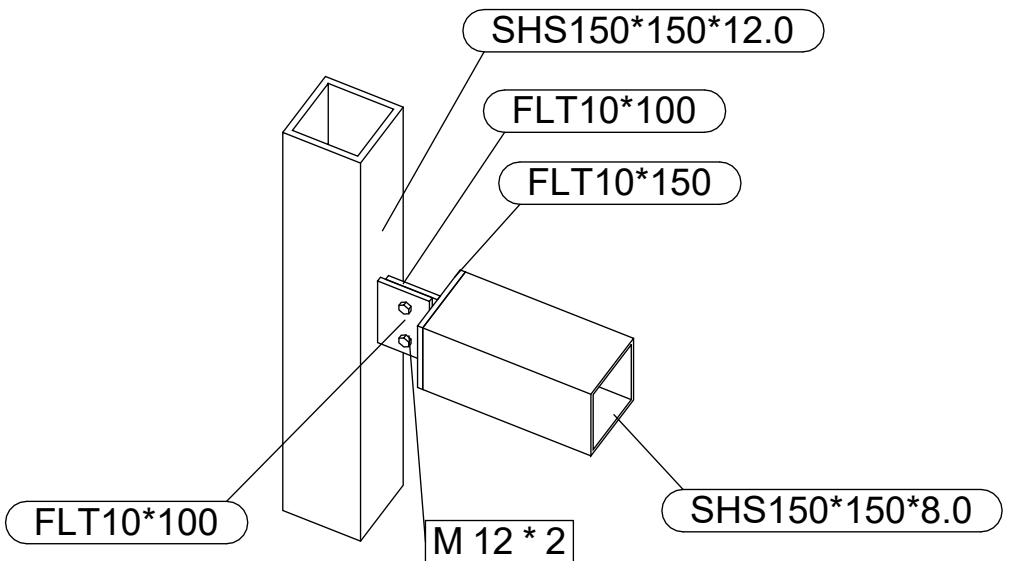


Typical Column Beam Fine Plate Connection


LGS CONNECTIONS

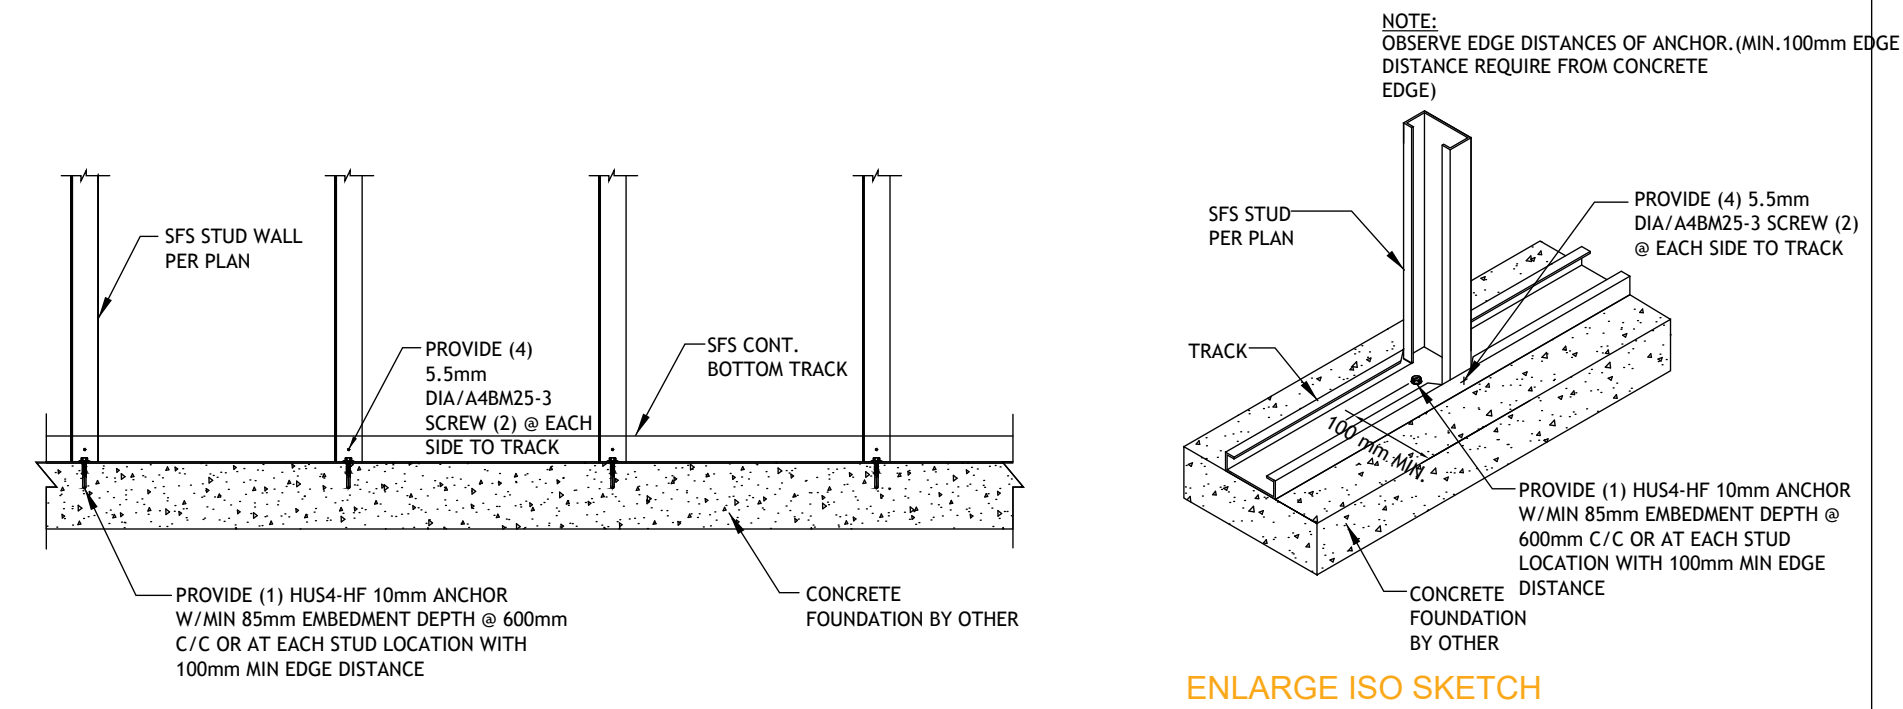


Typical Detail : SFS Bottom Track to Concerete Connection (External Wall)

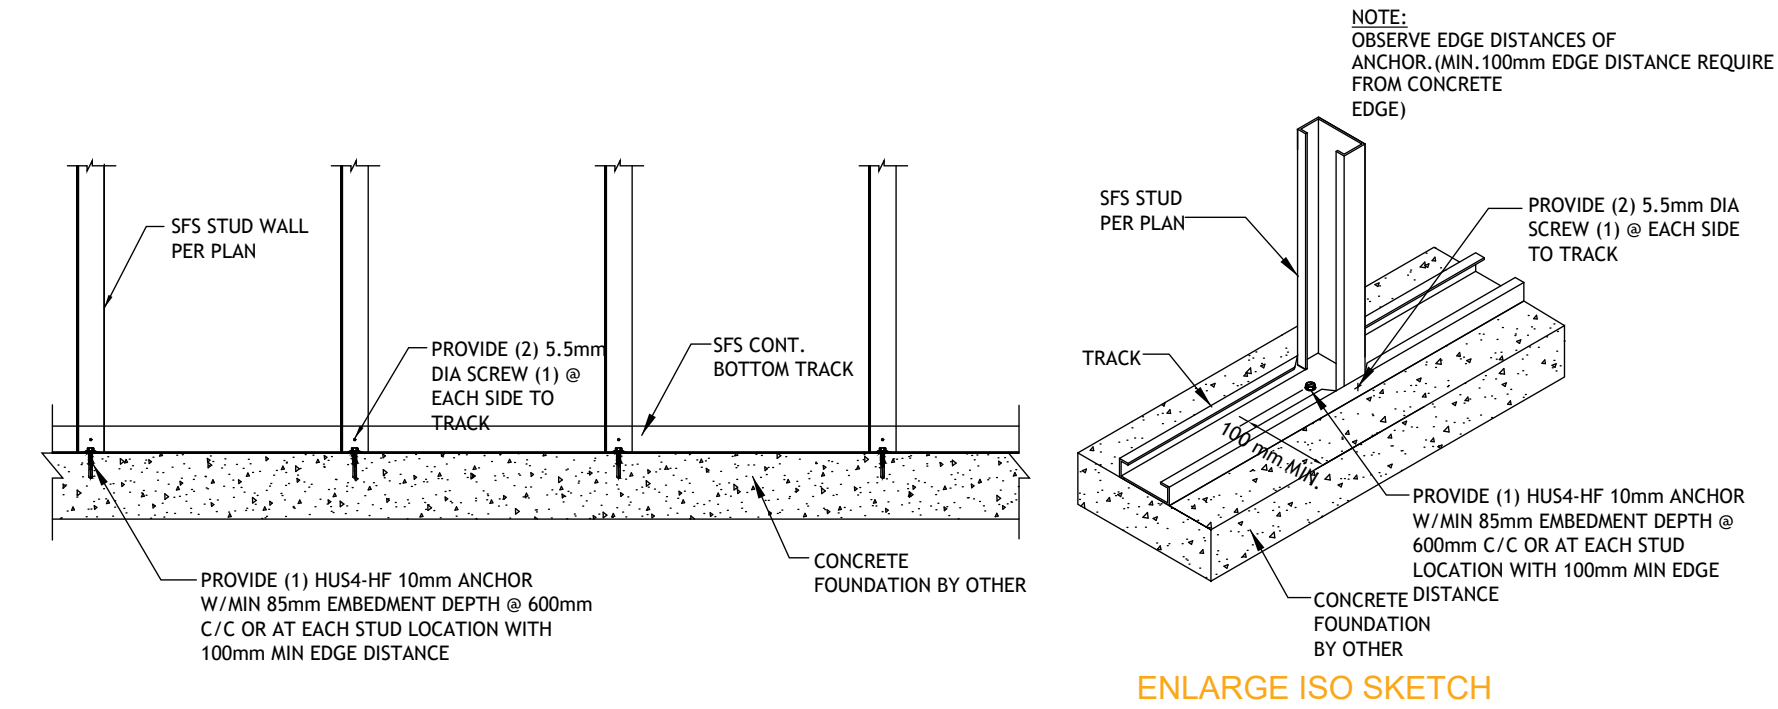


Typical Detail : Bottom Track to Concerete Connection (Internal Wall)

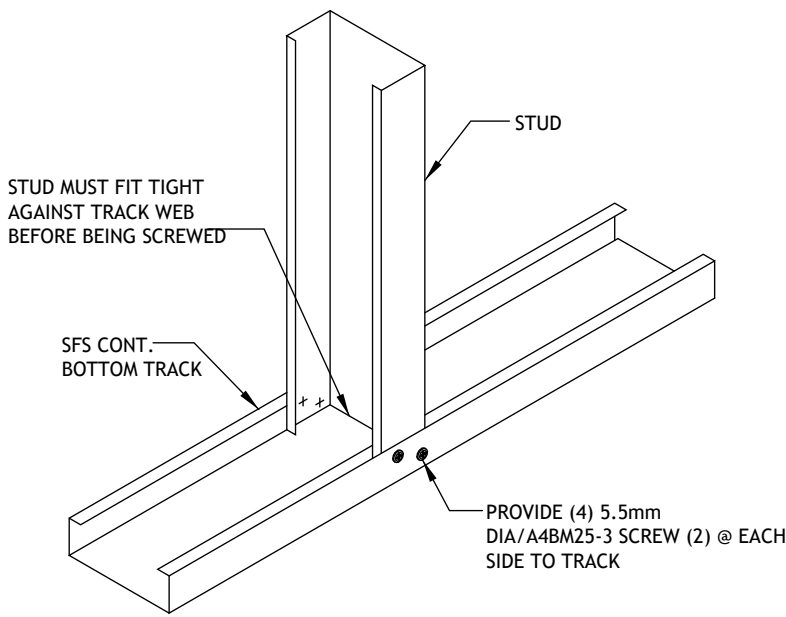


Stud to Bottom Track Connection (External Wall)

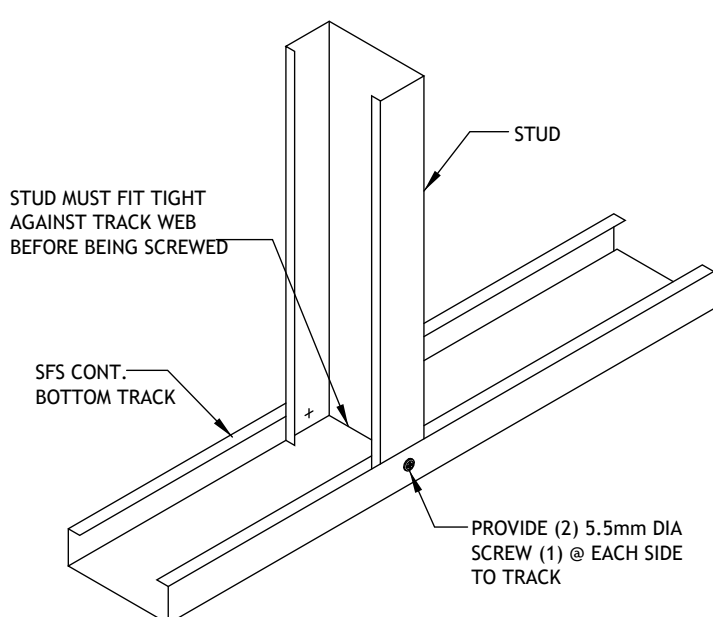


Stud to Bottom Track Connection (Internal Wall)

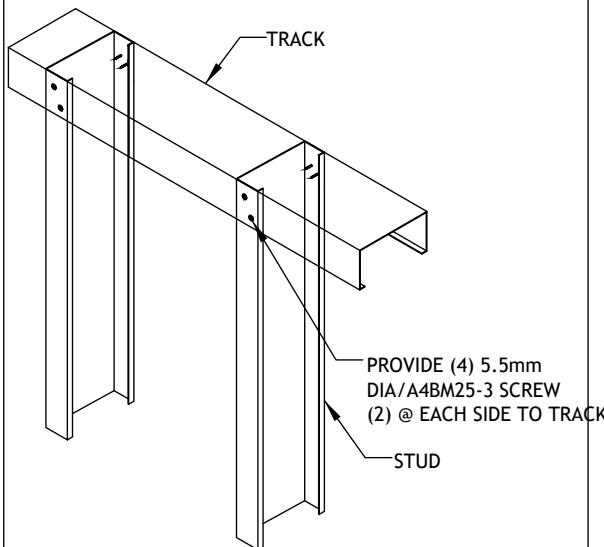


Stud to Top Track Connection (External Wall)

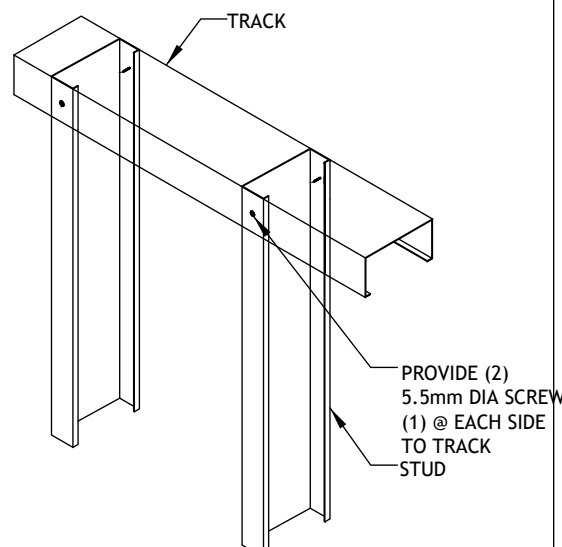


Stud to Top Track Connection (Internal Wall)

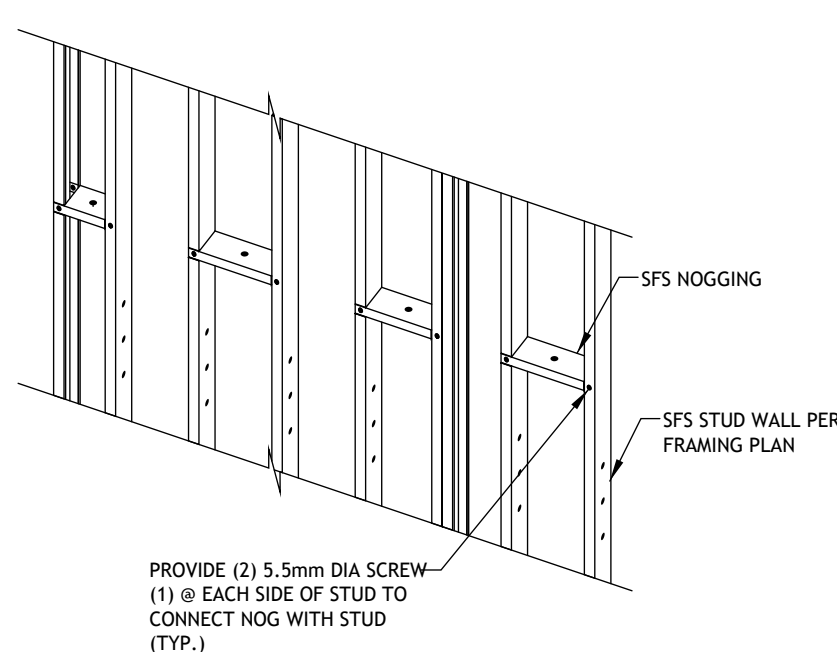


Hit and Miss Nogging to Stud Connection Detail

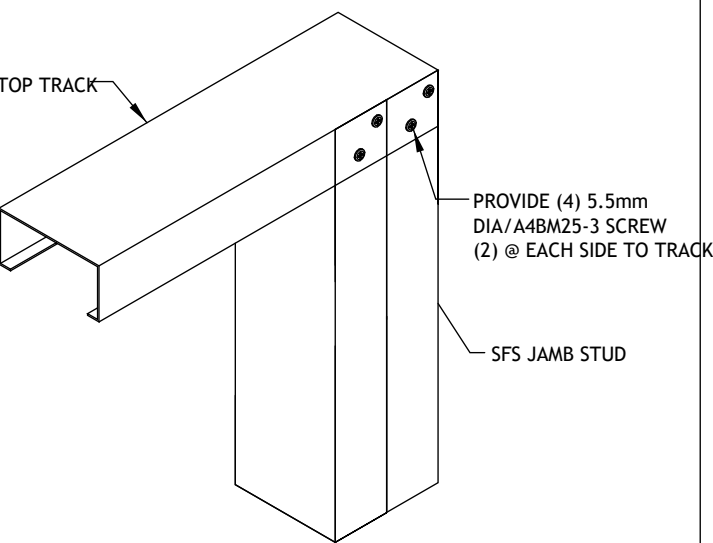


Box Jamb to Top Track Connection

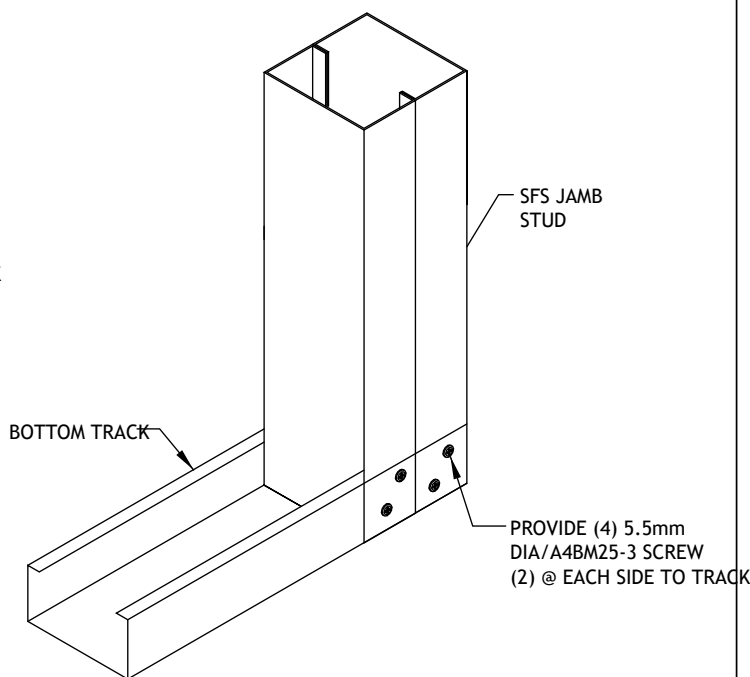


Box Jamb to Bottom Track Connection

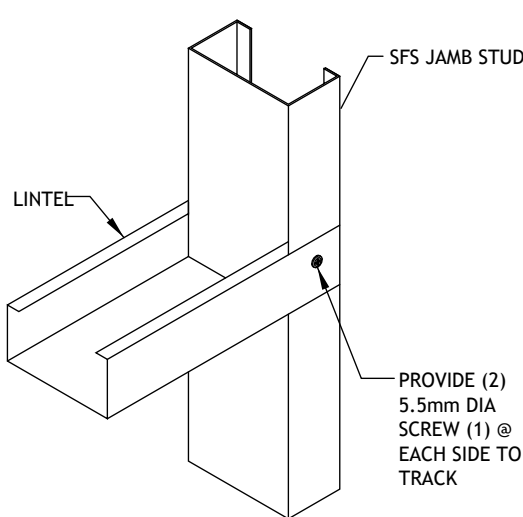


Lintel to Jamb Stud Connection

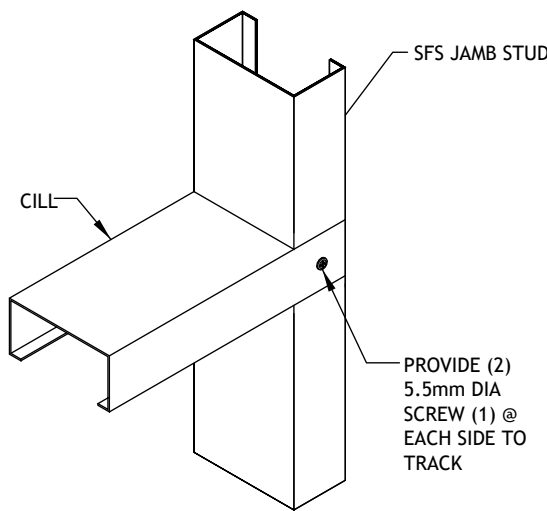

Typ. Cill to Jamb Stud Connection

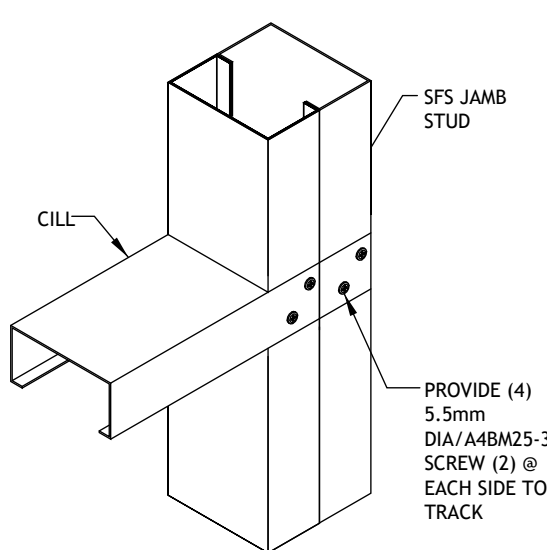

Typ. Cill to Jamb Stud Connection

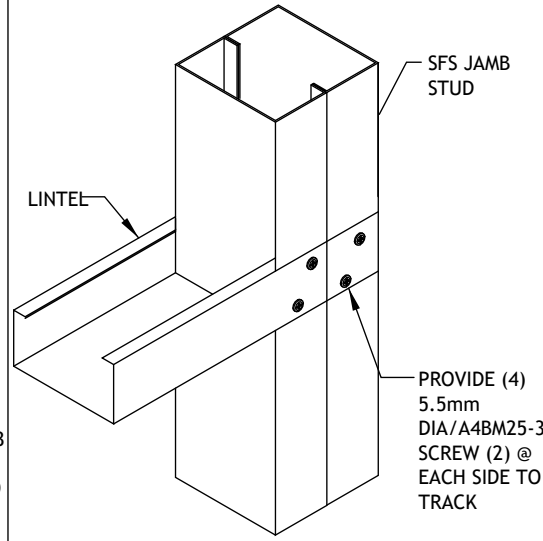

Lintel to Jamb Stud Connection

1. THESE DRAWINGS MUST BE CHECKED BY THE CUSTOMER OR CONTRACTOR PRIOR TO APPROVAL. ANY ERRORS OR OMISSIONS MUST BE REPORTED IN WRITING TO BAUHU PRIOR TO COMMENCEMENT OF CONSTRUCTION.
2. ARCHITECTURAL DRAWINGS SHOULD BE READ IN CONJUNCTION WITH STRUCTURAL DETAILING AND FABRICATION GENERAL ASSEMBLY DRAWINGS.
3. FOR CONSTRUCTION PURPOSES, USE ONLY THE LATEST APPROVED DRAWINGS LABELED 'ISSUED FOR CONSTRUCTION'.
4. DO NOT SCALE FROM THIS DRAWING.
5. THE COMPANY OPERATES USING METRIC DIMENSIONS AS THE PRINCIPAL DENOMINATION.
6. ALL CONCRETE WORKS ARE OUTSIDE OF THE SCOPE OF THE COMPANY. INFORMATION REGARDING SLAB DESIGN AND CONNECTIONS IN THESE DRAWINGS ARE INTENDED FOR GUIDENCE ONLY. FOUNDATION AND SLAB WORKS SHOULD BE DESIGNED AND APPROVED BY A LOCAL STRUCTURAL ENGINEER.
7. THE COMPANY RETAINS FULL TITLE AND OWNERSHIP OF THESE PLANS AND DESIGNS. ANY UNAUTHORISED USE, REPRODUCTION, OR DISTRIBUTION OF THESE PLANS, WHETHER IN WHOLE OR PART, IS EXPRESSLY PROHIBITED WITHOUT PRIOR WRITTEN CONSENT.

| No. | Revision | Date |
|-----|----------|------|
|     |          |      |
|     |          |      |
ISSUED FOR:

Issued for information

Issued for client approval

Issued for fabrication


Issued for construction

Firefly


|                |                       |
|----------------|-----------------------|
| DRAWING TITLE: | LGS Connections 3D    |
| DRAWN BY:      | Mladin Monica-Mihaela |
| SCALE:         |                       |
| DRAWING NO:    | A28                   |
| DATE:          | 04.03.2024            |

Typical Frame Connections 1


1. THESE DRAWINGS MUST BE CHECKED BY THE CUSTOMER OR CONTRACTOR PRIOR TO APPROVAL. ANY ERRORS OR OMISSIONS MUST BE REPORTED IN WRITING TO BAUHU PRIOR TO COMMENCEMENT OF CONSTRUCTION.
2. ARCHITECTURAL DRAWINGS SHOULD BE READ IN CONJUNCTION WITH STRUCTURAL DETAILING AND FABRICATION GENERAL ASSEMBLY DRAWINGS.
3. FOR CONSTRUCTION PURPOSES, USE ONLY THE LATEST APPROVED DRAWINGS LABELED 'ISSUED FOR CONSTRUCTION'.
4. DO NOT SCALE FROM THIS DRAWING.
5. THE COMPANY OPERATES USING METRIC DIMENSIONS AS THE PRINCIPAL DENOMINATION.
6. ALL CONCRETE WORKS ARE OUTSIDE OF THE SCOPE OF THE COMPANY. INFORMATION REGARDING SLAB DESIGN AND CONNECTIONS IN THESE DRAWINGS ARE INTENDED FOR GUIDENCE ONLY. FOUNDATION AND SLAB WORKS SHOULD BE DESIGNED AND APPROVED BY A LOCAL STRUCTURAL ENGINEER.
7. THE COMPANY RETAINS FULL TITLE AND OWNERSHIP OF THESE PLANS AND DESIGNS. ANY UNAUTHORISED USE, REPRODUCTION, OR DISTRIBUTION OF THESE PLANS, WHETHER IN WHOLE OR PART, IS EXPRESSLY PROHIBITED WITHOUT PRIOR WRITTEN CONSENT.

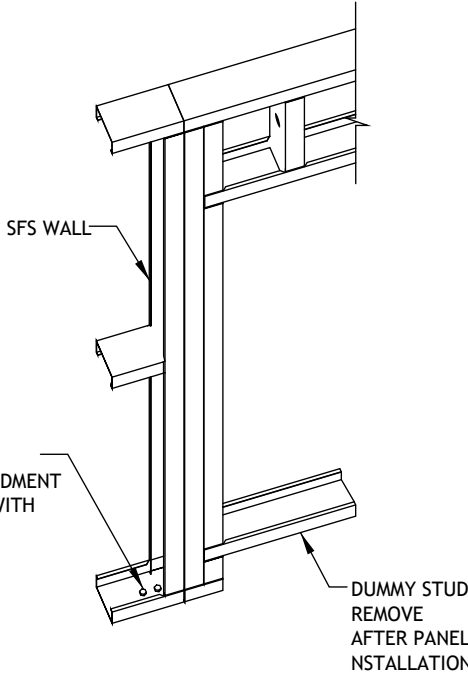


Typical Detail for Two Anchor at Jamb Location

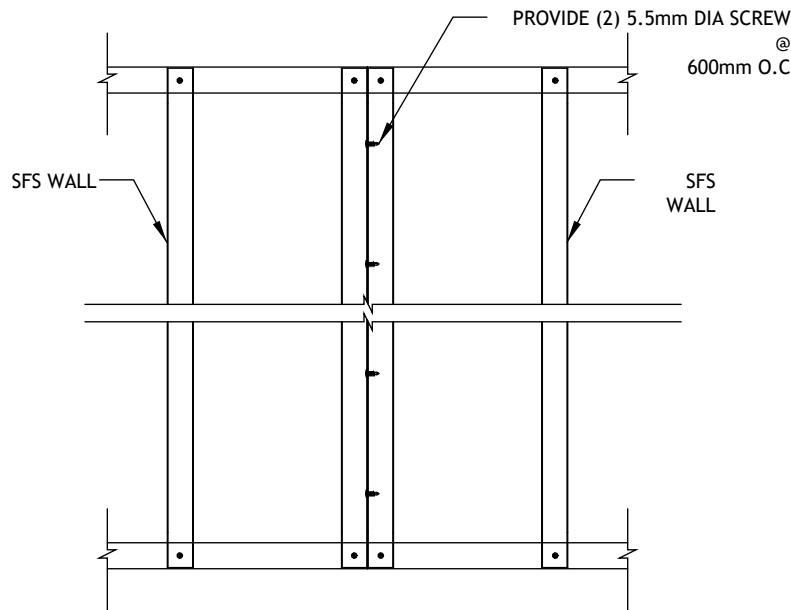


Typical Wall to SFS Wall Connection

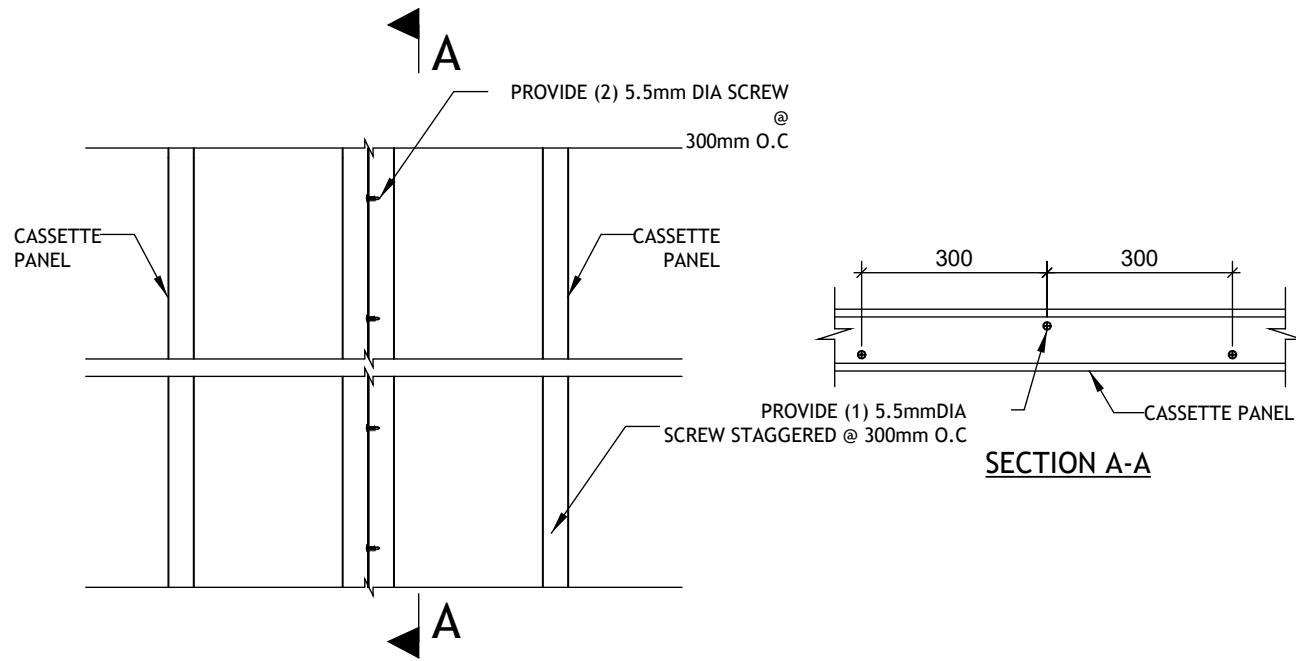


Cassette to Cassette Connection

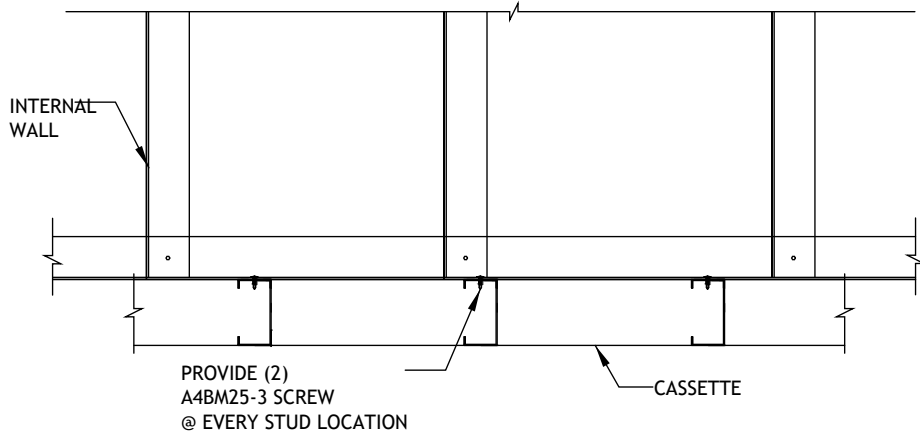


Internal Wall to Cassette Connection at Base

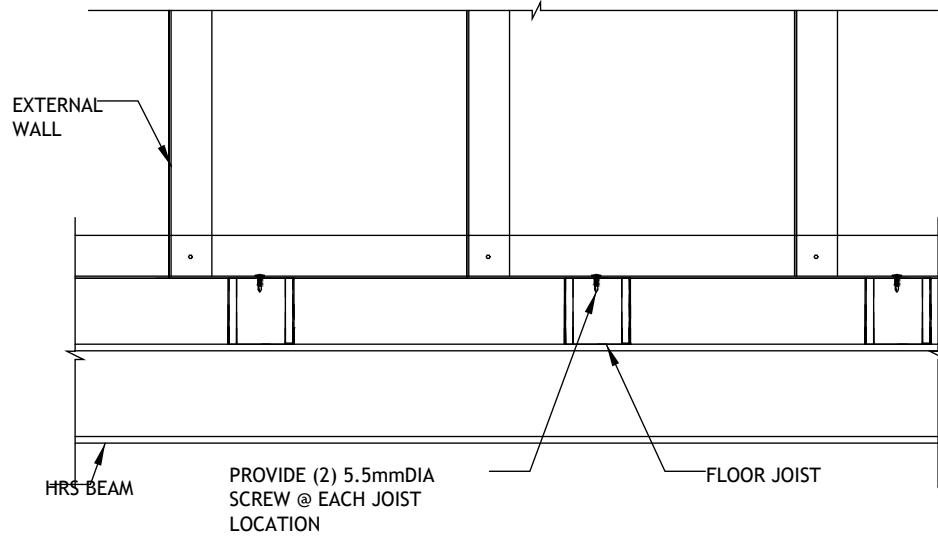


External Wall toJoist Connection at Base

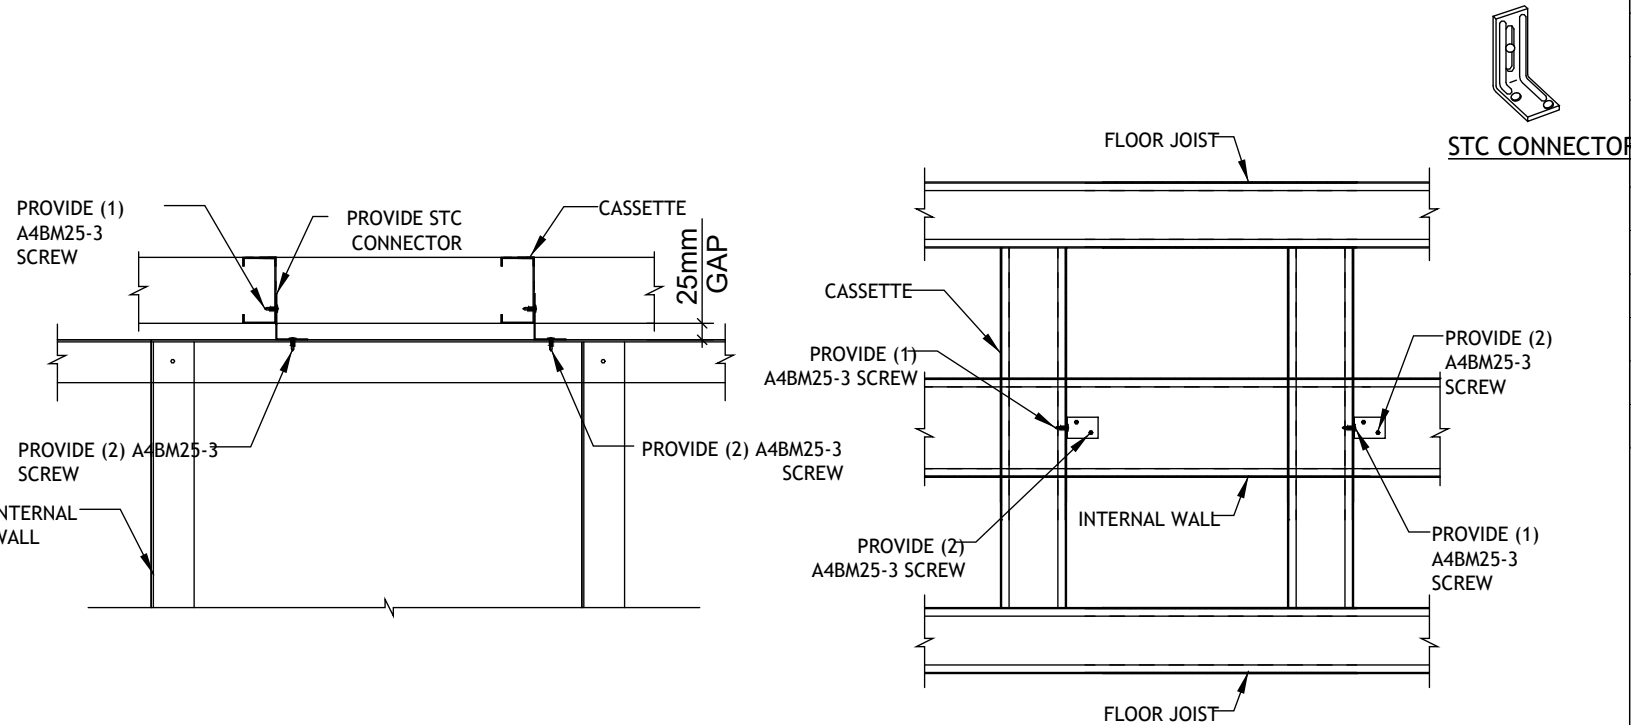


Typ. Internal Wall Connection at Roof Truss at Cassette Location

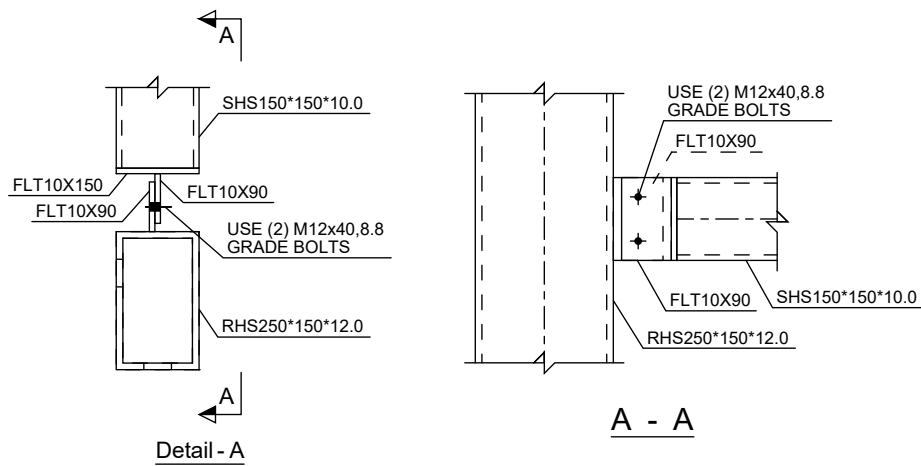

Typ. Fin Plate Connection Detail

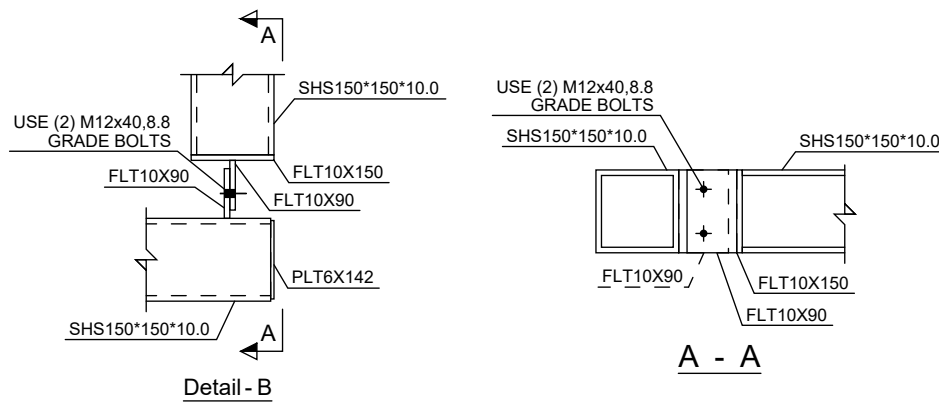

Typ. Fin Plate Connection Detail

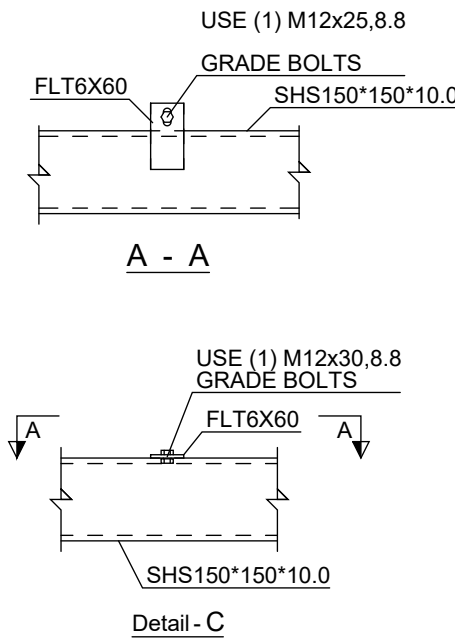

SFS Wall to HRS Beam Connection

| No. | Revision | Date |
|-----|----------|------|
|     |          |      |
|     |          |      |
ISSUED FOR:

Issued for information

Issued for client approval

Issued for fabrication

Issued for construction

Firefly

DRAWING TITLE:

Typical Frame Connections

DRAWN BY:

Mladin Monica-Mihaela

SCALE:


DRAWING NO:

A29


DATE:

04.03.2024

## Typical Frame Connections 2

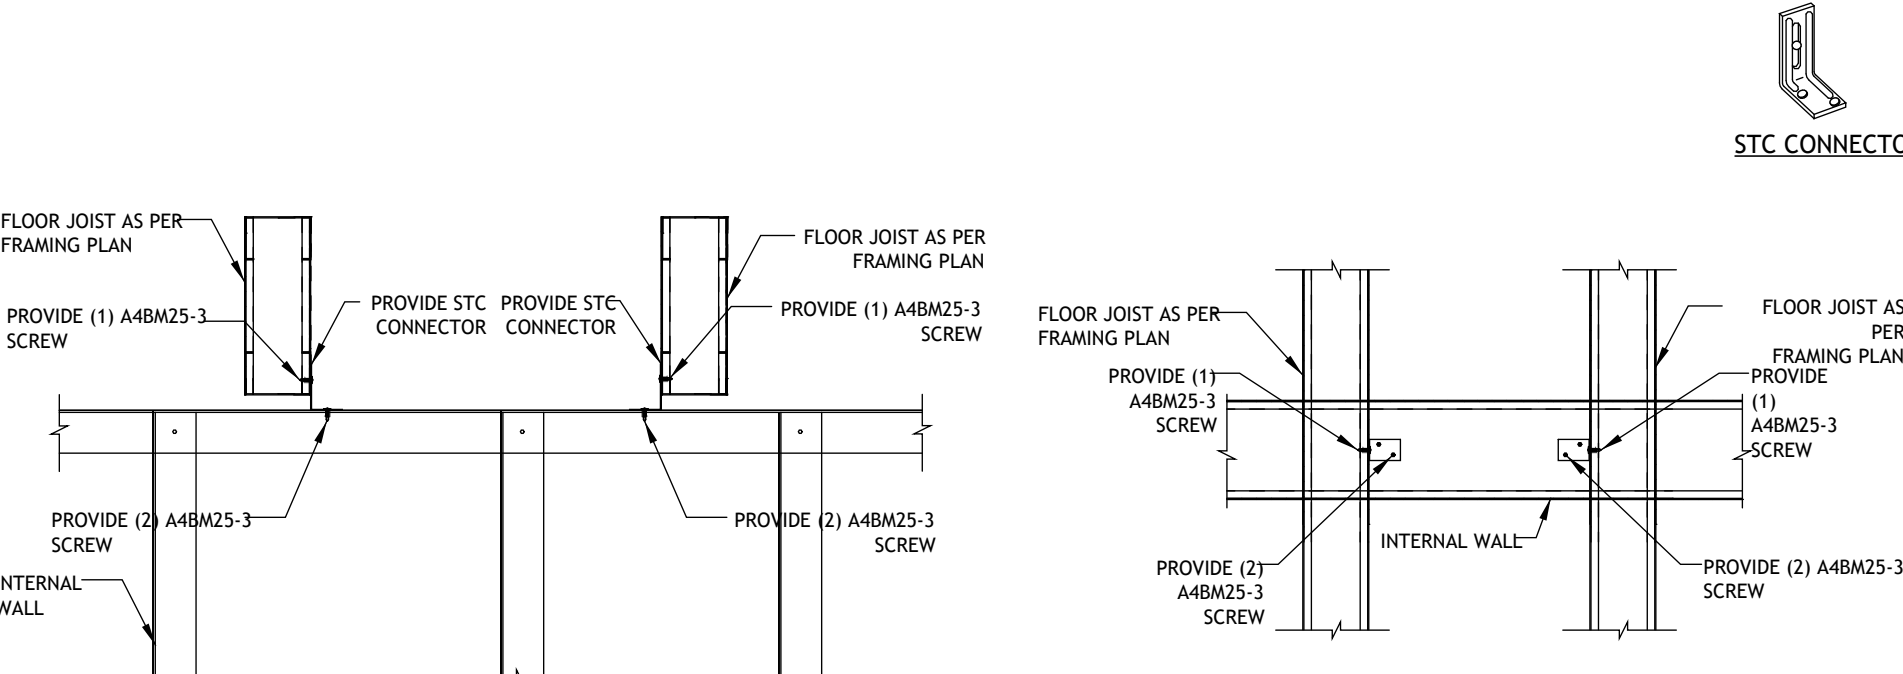

## Typical Internal Wall Connection Floor Joist

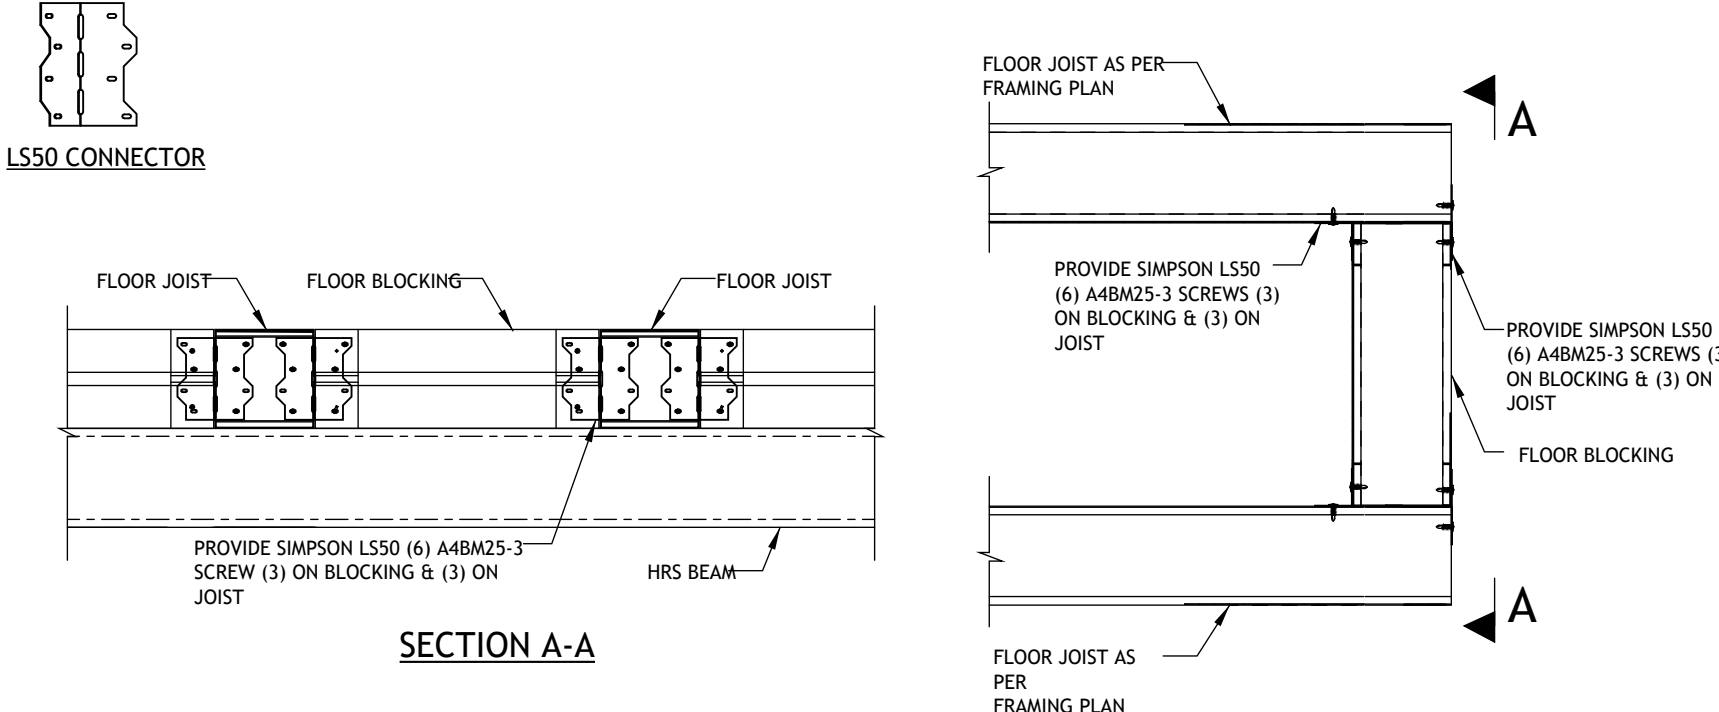

## Floor Blocking to Floor Joist Connection

1. THESE DRAWINGS MUST BE CHECKED BY THE CUSTOMER OR CONTRACTOR PRIOR TO APPROVAL. ANY ERRORS OR OMISSIONS MUST BE REPORTED IN WRITING TO BAUHU PRIOR TO COMMENCEMENT OF CONSTRUCTION.
2. ARCHITECTURAL DRAWINGS SHOULD BE READ IN CONJUNCTION WITH STRUCTURAL DETAILING AND FABRICATION GENERAL ASSEMBLY DRAWINGS.
3. FOR CONSTRUCTION PURPOSES, USE ONLY THE LATEST APPROVED DRAWINGS LABELED 'ISSUED FOR CONSTRUCTION'.
4. DO NOT SCALE FROM THIS DRAWING.
5. THE COMPANY OPERATES USING METRIC DIMENSIONS AS THE PRINCIPAL DENOMINATION.
6. ALL CONCRETE WORKS ARE OUTSIDE OF THE SCOPE OF THE COMPANY. INFORMATION REGARDING SLAB DESIGN AND CONNECTIONS IN THESE DRAWINGS ARE INTENDED FOR GUIDANCE ONLY. FOUNDATION AND SLAB WORKS SHOULD BE DESIGNED AND APPROVED BY A LOCAL STRUCTURAL ENGINEER.
7. THE COMPANY RETAINS FULL TITLE AND OWNERSHIP OF THESE PLANS AND DESIGNS. ANY UNAUTHORISED USE, REPRODUCTION, OR DISTRIBUTION OF THESE PLANS, WHETHER IN WHOLE OR PART, IS EXPRESSLY PROHIBITED WITHOUT PRIOR WRITTEN CONSENT.

[illegible]**ISSUED FOR:**

**Issued for information**

**Issued for client approval**

**Issued for fabrication**

**Issued for construction**

# Firefly

**DRAWING TITLE:**

## Typical Frame Connections 2

DRAWN BY:

Mladin Monica-Mihaela


**SCALE:**

**DRAWING NO.**


A30

DATE:


04.03.2024

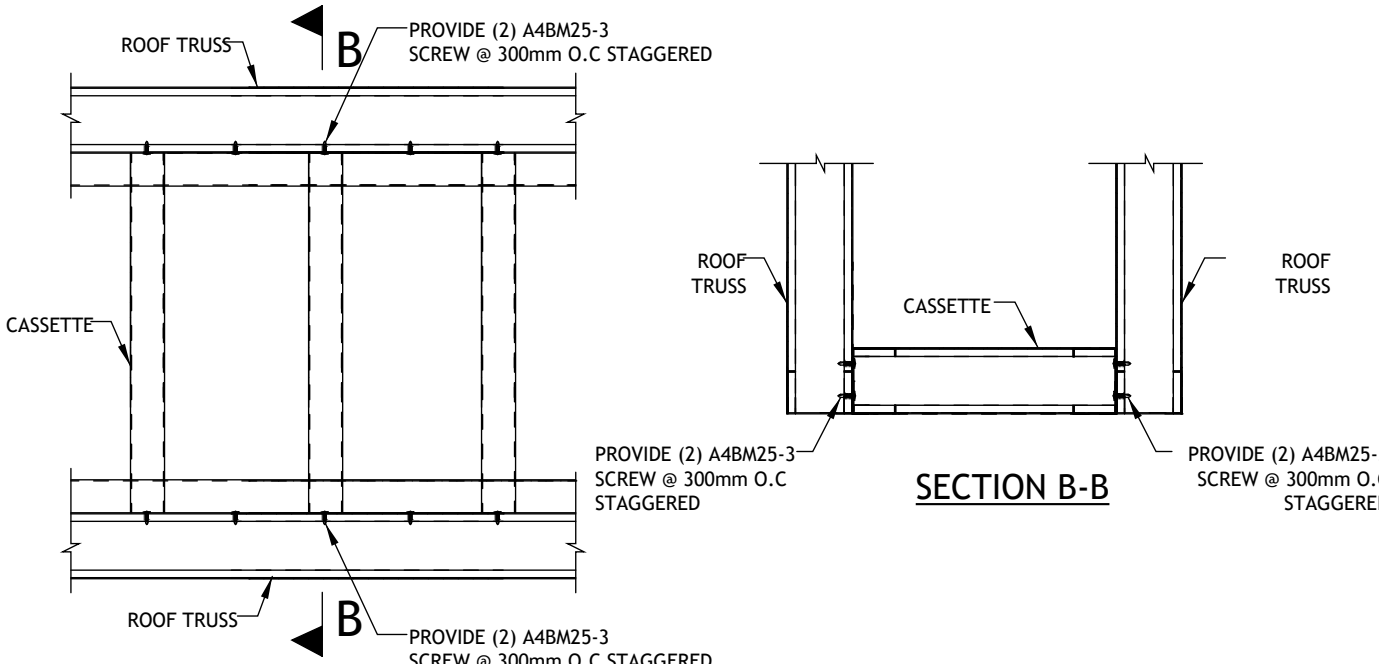


## Cassette to Roof Trusses Connection

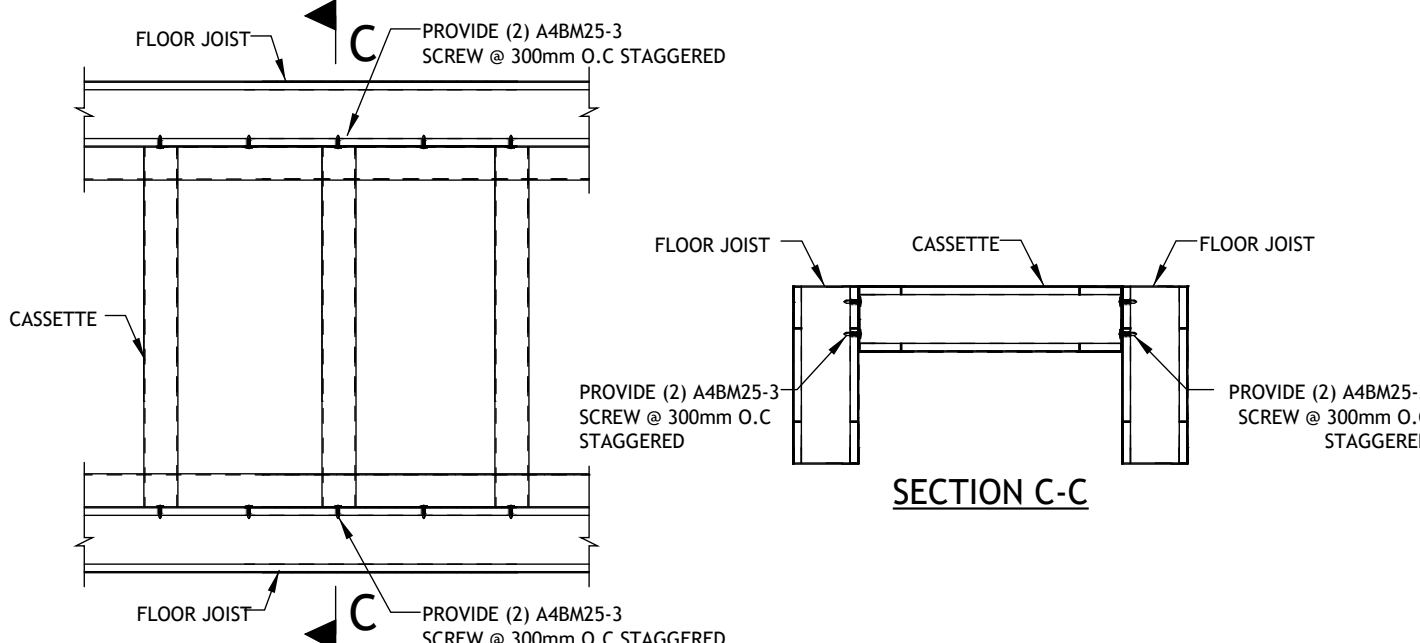

## Cassette to Floor Joist Connection

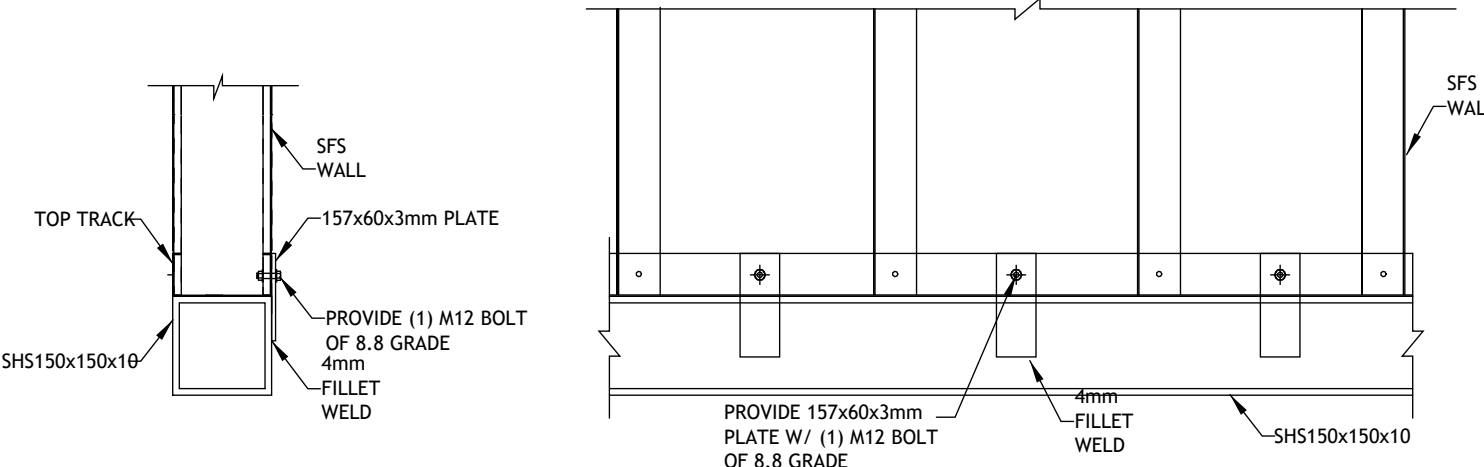



## Typical Detail at SFS Bottom Track to HRS Beam Connection (External & Internal Wall)

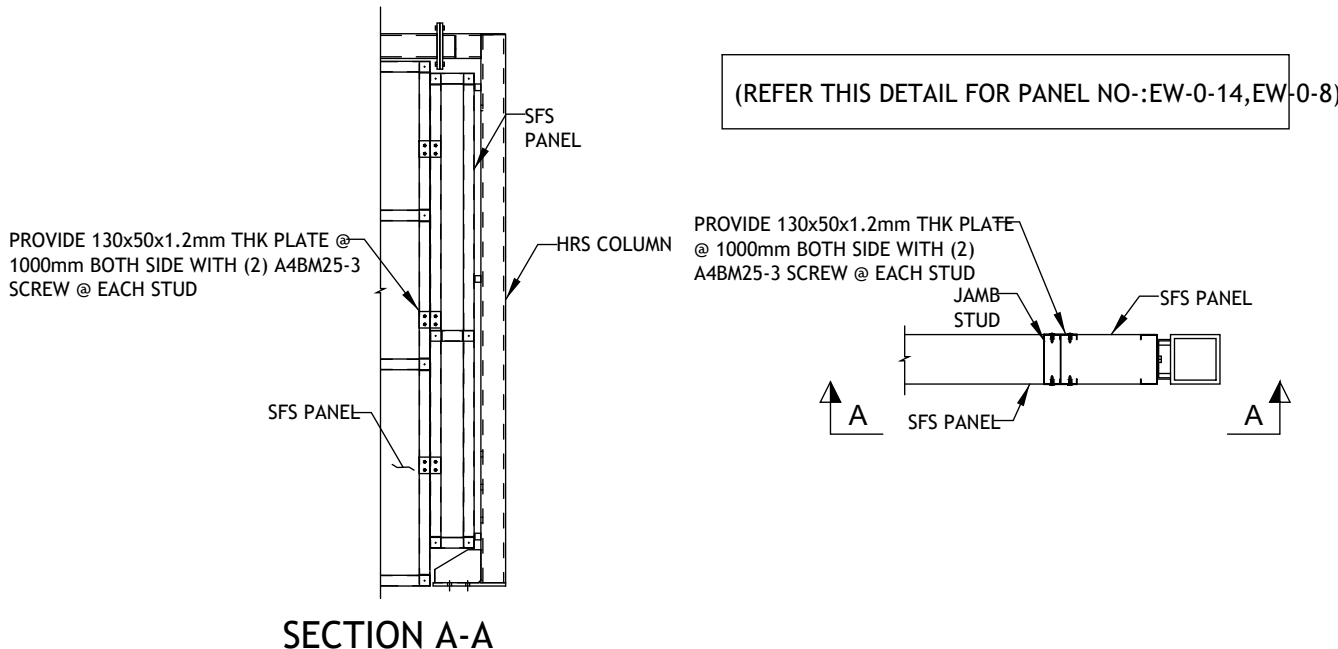


## SFS Panel Connection Detail

Typical Frame Connections 3


NOTES:  
ALL WELDS FOR CONNECTION OF ASSEMBLY TO BE NOTE FROM FABRICATION DRAWING

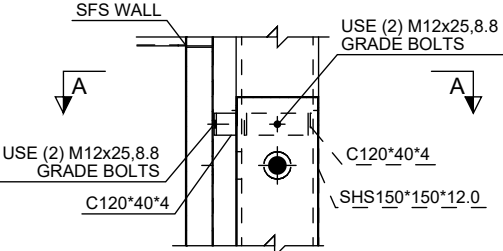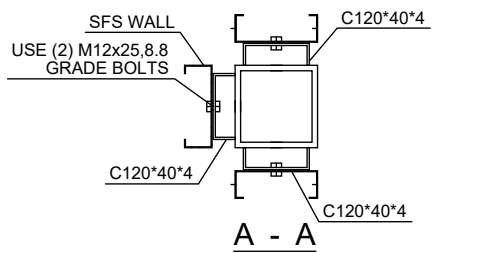

Typ. Truss Outside Plate Connection

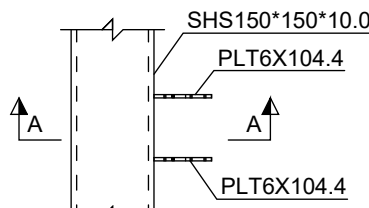


Detail - A

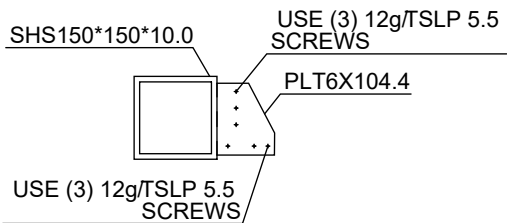


A - A

Typ. Vertical Splice Connection

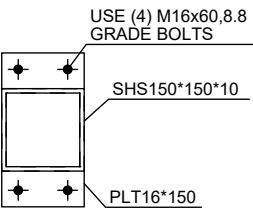


B - B

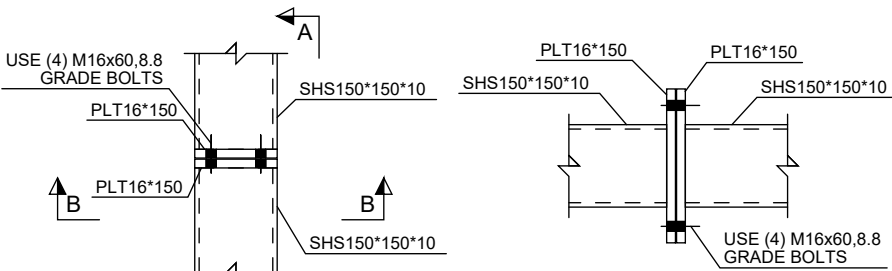


Detail - B

A - A

Typ. Horizontal Splice Connection

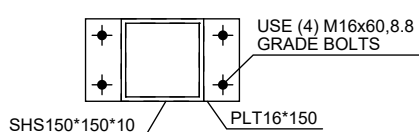


B - B

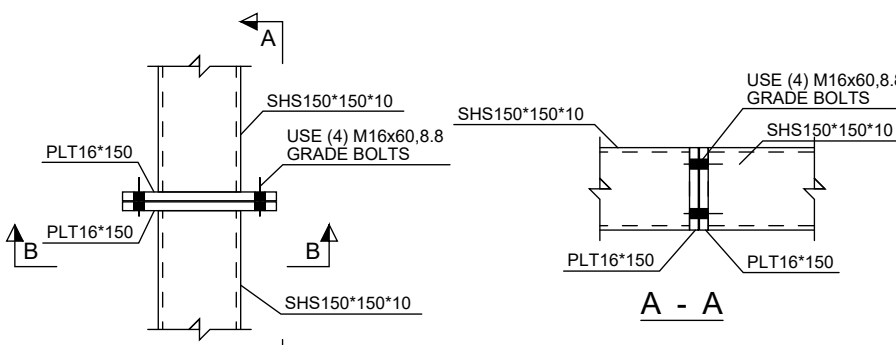


Detail - C

A - A

Typ. Truss Bracket Connection

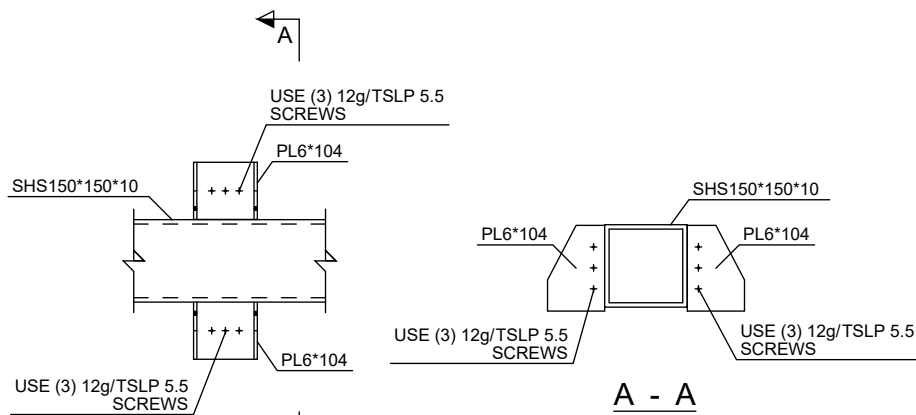


Detail - D

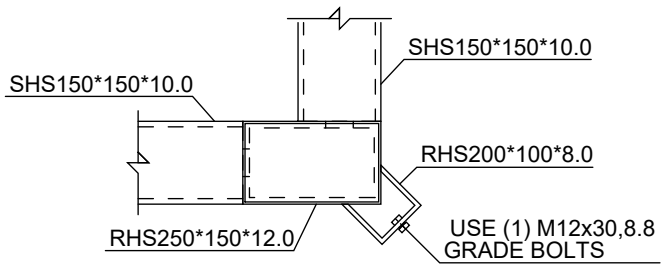


A - A

Typ. Corner Truss Connection

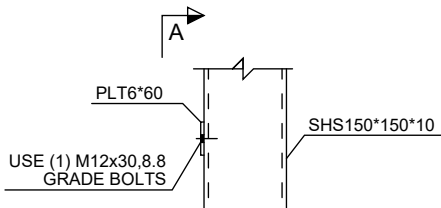


Detail - E

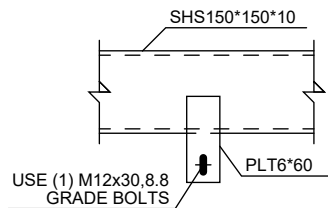


A - A

Typ. Lintel to Wind Post Connection

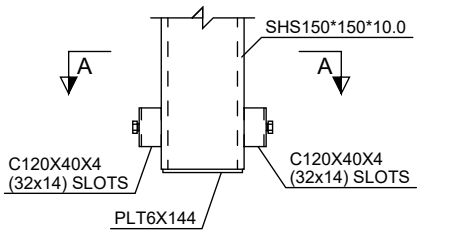


Detail - F

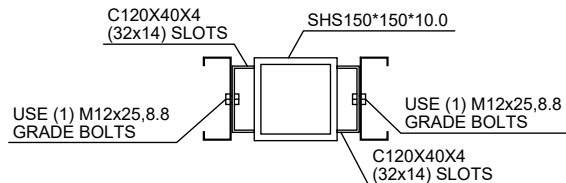


A - A

Cassette to Beam Connection

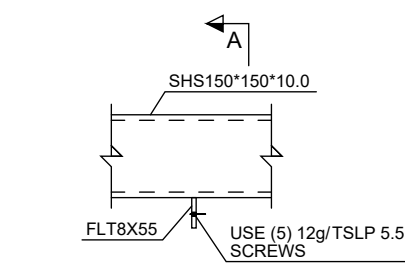

Detail - G

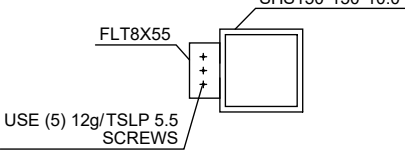

A - A

| No. | Revision | Date |
|-----|----------|------|
|     |          |      |
|     |          |      |
ISSUED FOR:

Issued for information

Issued for client approval

Issued for fabrication

Issued for construction

Firefly

DRAWING TITLE:

Typical Frame Connections 3

DRAWN BY:

Mladin Monica-Mihaela

SCALE:

DRAWING NO:

A31


DATE:

04.03.2024

Typ. Beam to Column Connection Using C Bracket


Typ. Beam to Column Connection Using C Bracket

Typ. Beam to Column Connection Using C Bracket

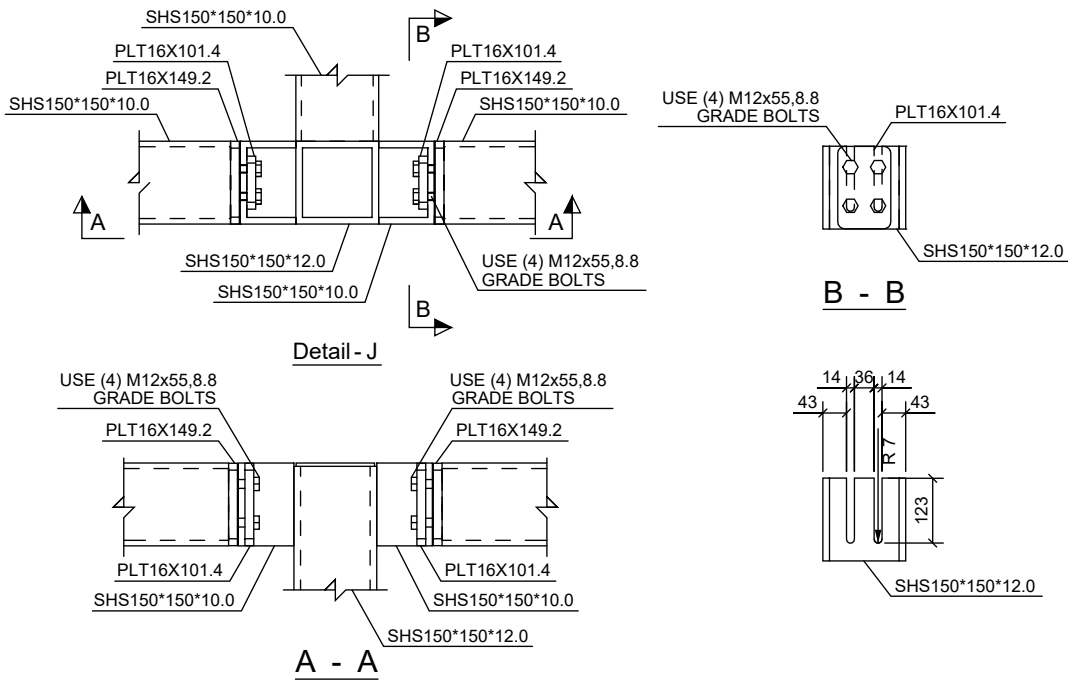


Detail - J


B - B

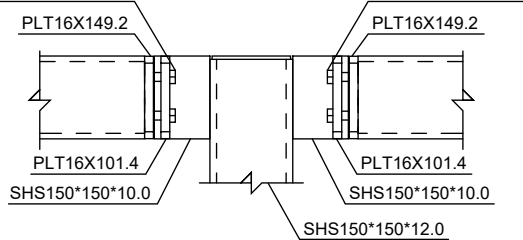

A - A

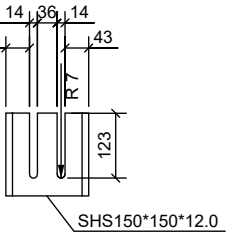


B - B

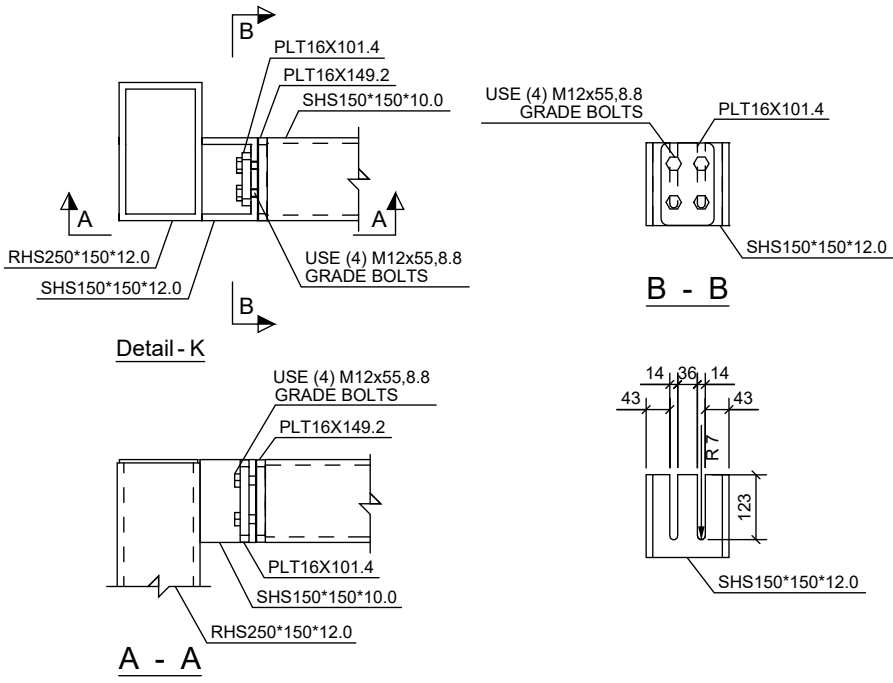


Detail - K

A - A

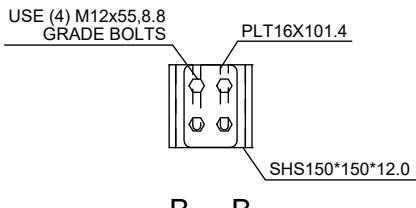


B - B

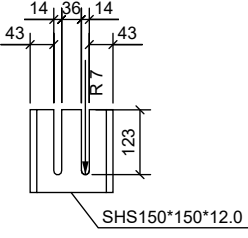

B - B


Typical Frame Connections 4

Hold Down Detail

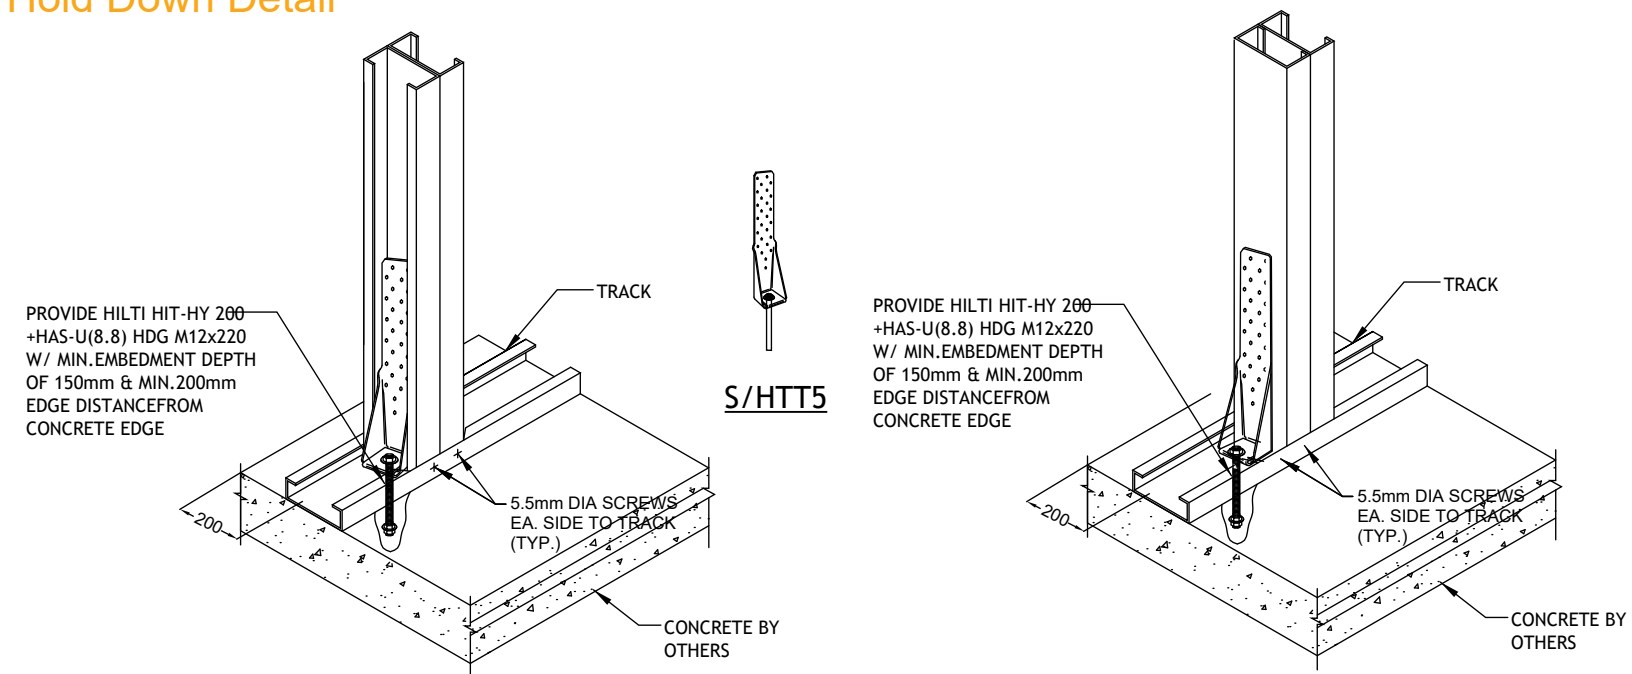

- NOTE -
- 1. ANCHOR & SCREWS SPECIFICATION AS PER SPECIFIED ON STRUCTURAL PLAN
  - 2. FIXING SPECIFICATION SUBJECT TO CHANGE AS PER DESIGN.


Casette to Floor/Roof Joist Connection

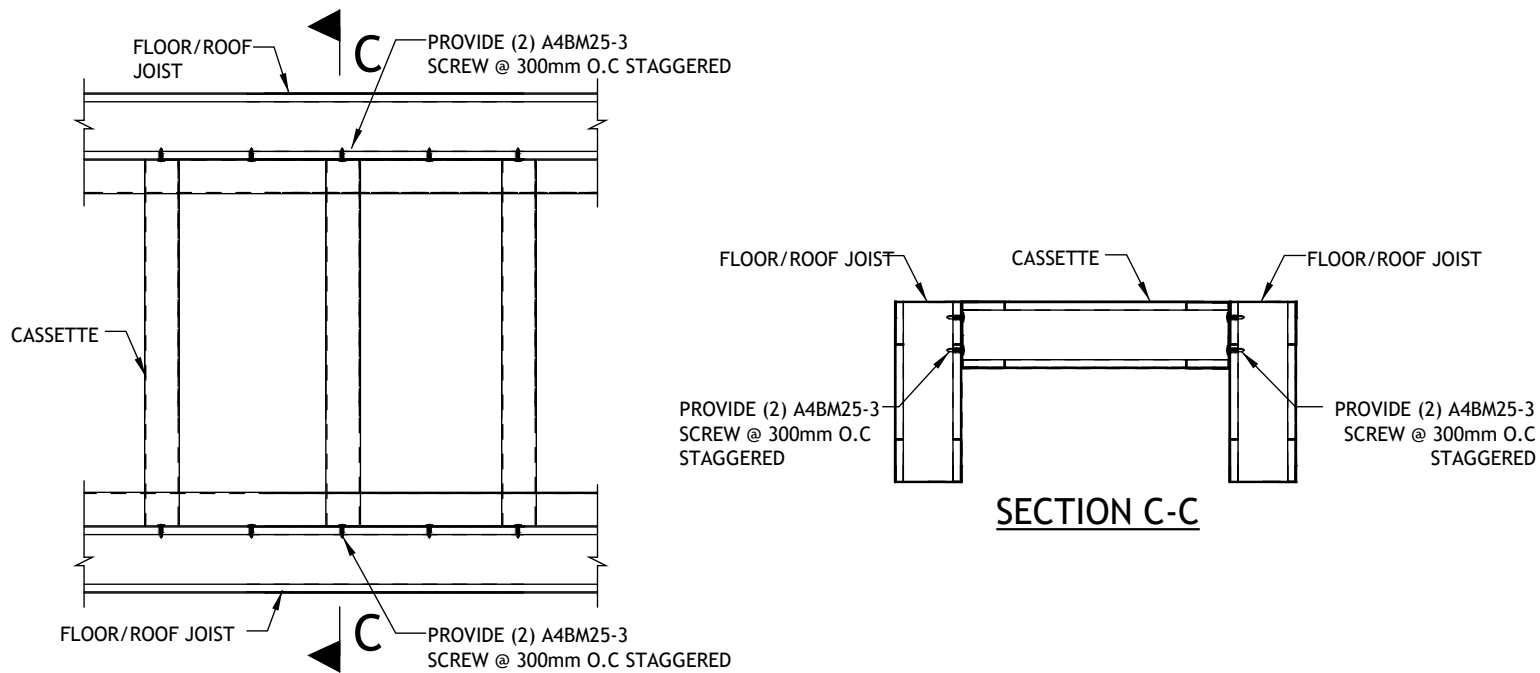

NOTE -FIXING SPECIFICATION SUBJECT TO CHANGE AS PER DESIGN.





Typ. Internal Wall Connection Floor/Roof Joist

(Perpendicular Condition)

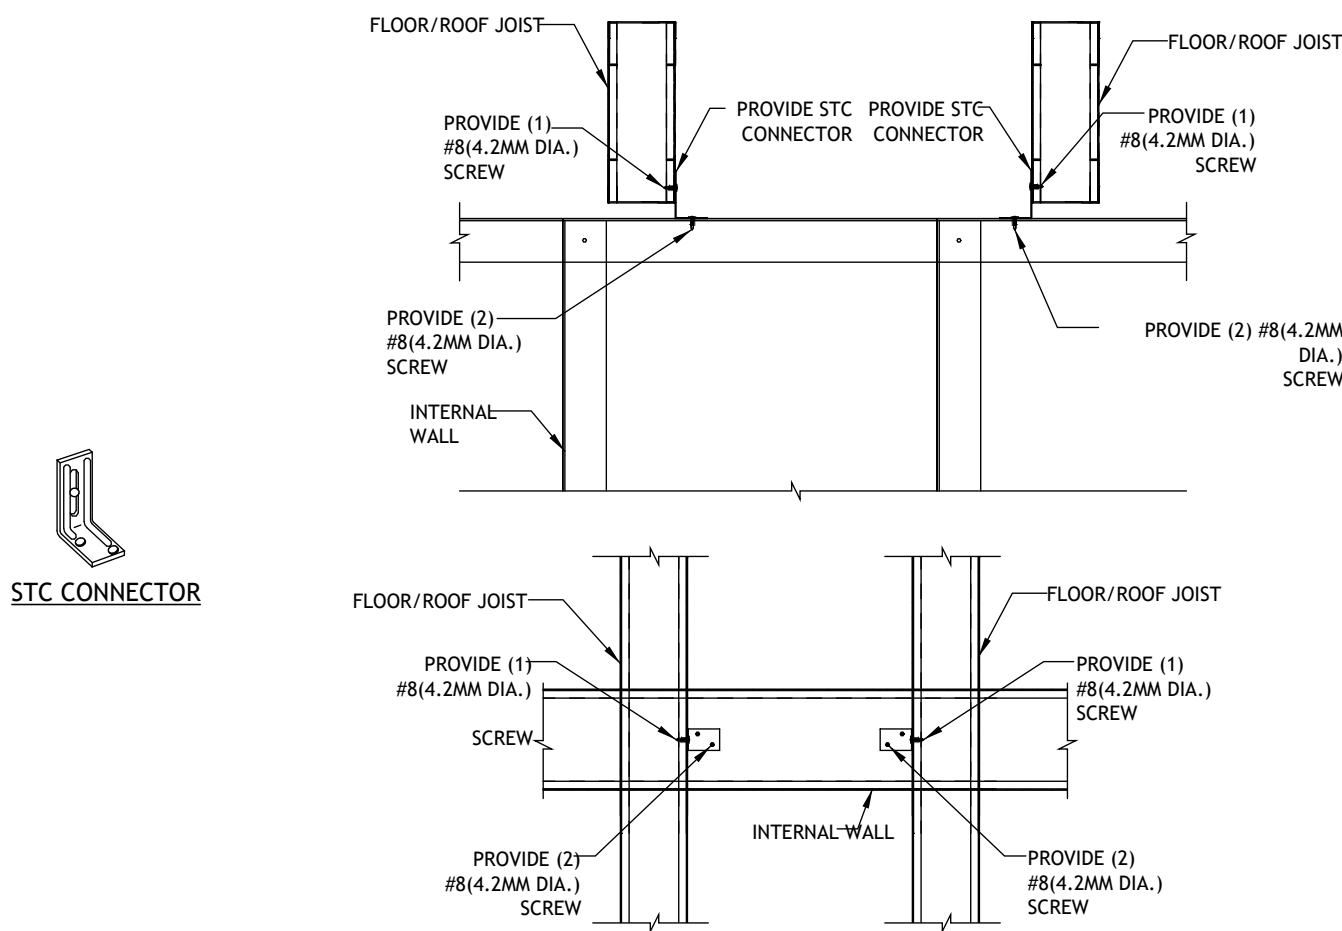


NOTE -FIXING SPECIFICATION SUBJECT TO CHANGE AS PER DESIGN.



Typ. Brace Wall Panel Connection with Treaded Rod

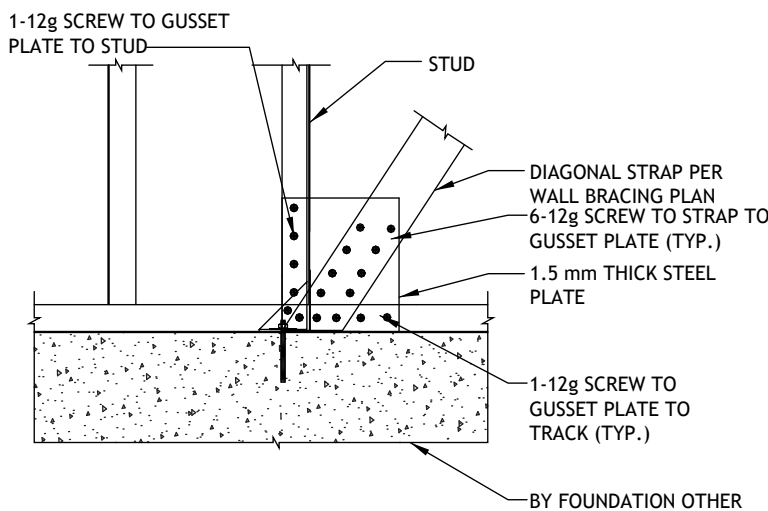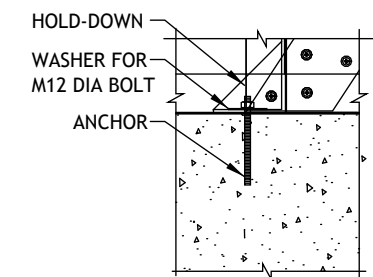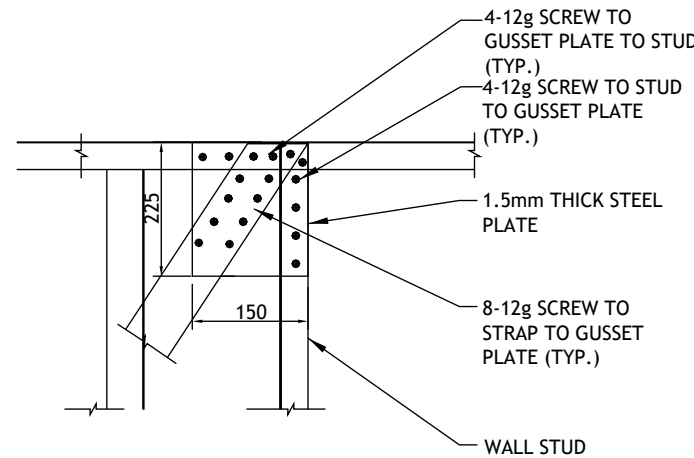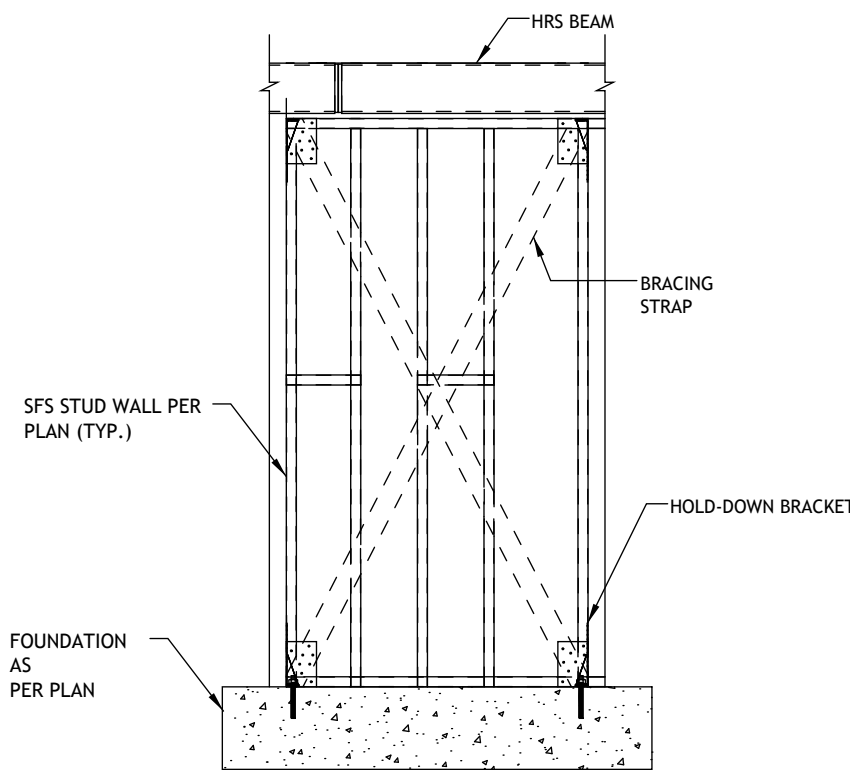

- NOTE -
- 1. ANCHOR & SCREWS SPECIFICATION AS PER SPECIFIED ON STRUCTURAL PLAN
  - 2. FIXING SPECIFICATION SUBJECT TO CHANGE AS PER DESIGN.

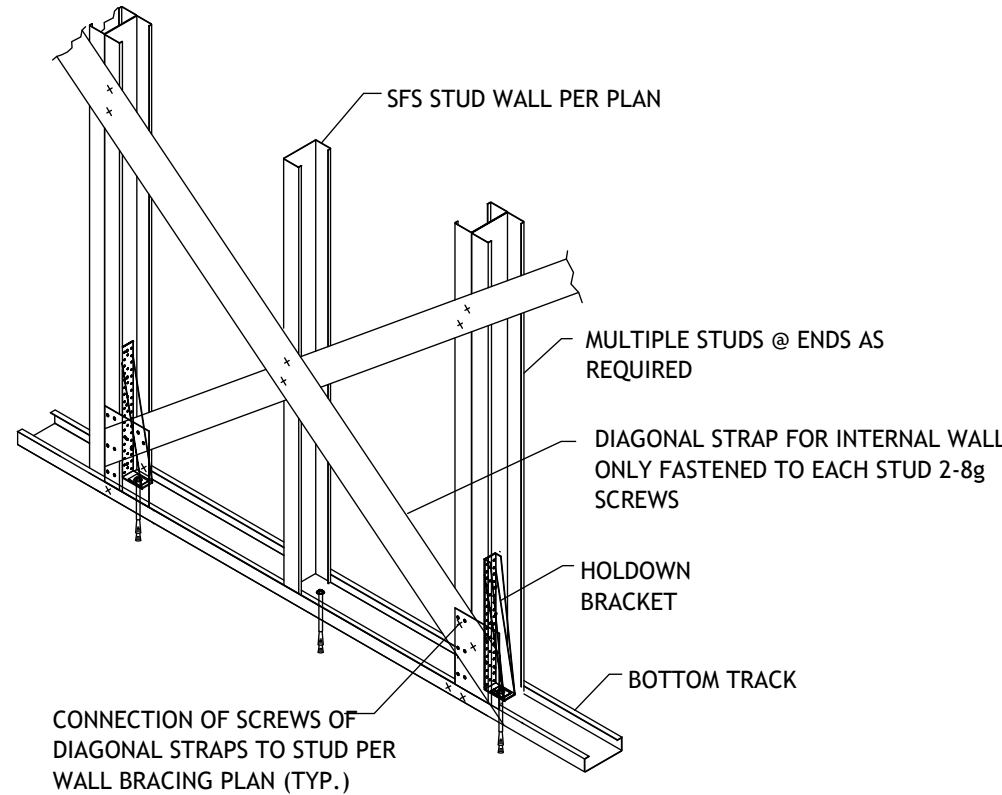

STRAP TO TRACK CONNECTION

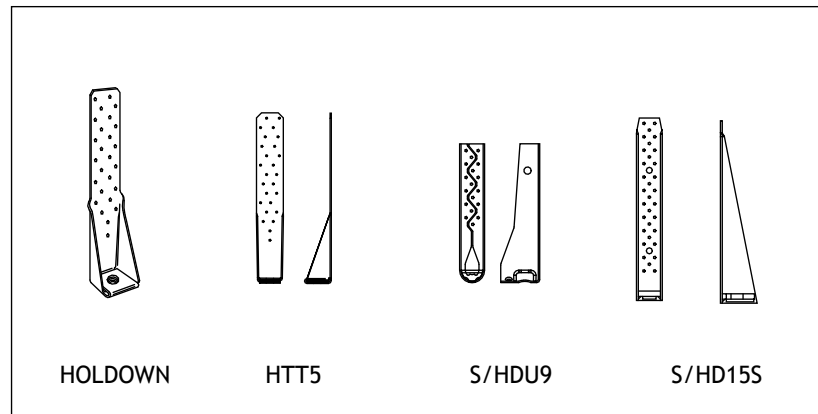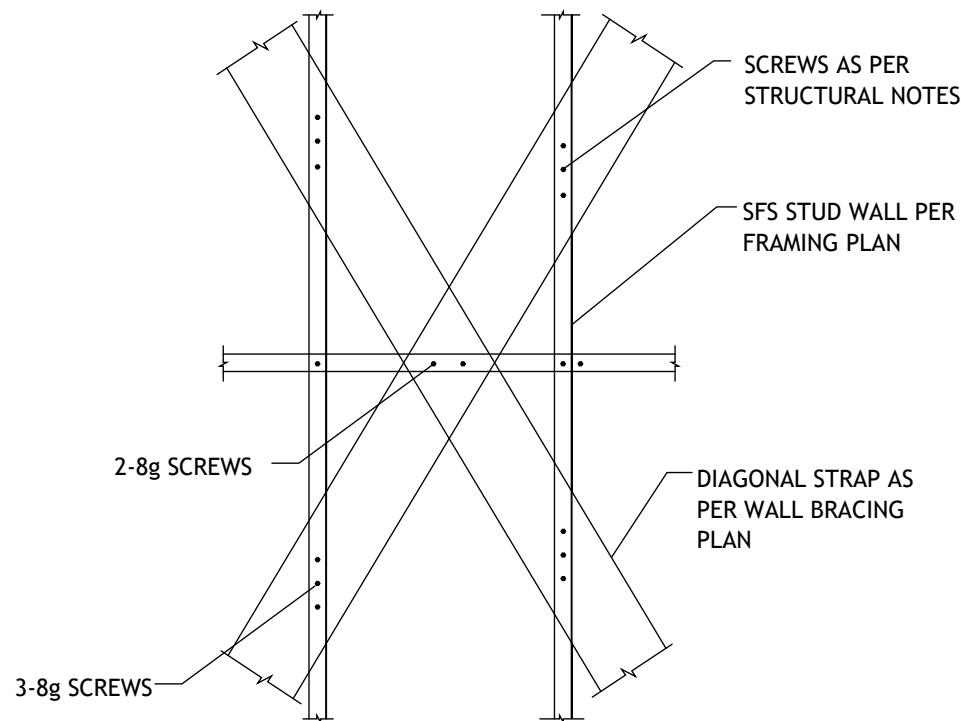

- 1. THESE DRAWINGS MUST BE CHECKED BY THE CUSTOMER OR CONTRACTOR PRIOR TO APPROVAL. ANY ERRORS OR OMISSIONS MUST BE REPORTED IN WRITING TO BAUHU PRIOR TO COMMENCEMENT OF CONSTRUCTION.
- 2. ARCHITECTURAL DRAWINGS SHOULD BE READ IN CONJUNCTION WITH STRUCTURAL DETAILING AND FABRICATION GENERAL ASSEMBLY DRAWINGS.
- 3. FOR CONSTRUCTION PURPOSES, USE ONLY THE LATEST APPROVED DRAWINGS LABELED 'ISSUED FOR CONSTRUCTION'.
- 4. DO NOT SCALE FROM THIS DRAWING.
- 5. THE COMPANY OPERATES USING METRIC DIMENSIONS AS THE PRINCIPAL DENOMINATION.
- 6. ALL CONCRETE WORKS ARE OUTSIDE OF THE SCOPE OF THE COMPANY. INFORMATION REGARDING SLAB DESIGN AND CONNECTIONS IN THESE DRAWINGS ARE INTENDED FOR GUIDENCE ONLY. FOUNDATION AND SLAB WORKS SHOULD BE DESIGNED AND APPROVED BY A LOCAL STRUCTURAL ENGINEER.
- 7. THE COMPANY RETAINS FULL TITLE AND OWNERSHIP OF THESE PLANS AND DESIGNS. ANY UNAUTHORISED USE, REPRODUCTION, OR DISTRIBUTION OF THESE PLANS, WHETHER IN WHOLE OR PART, IS EXPRESSLY PROHIBITED WITHOUT PRIOR WRITTEN CONSENT.

| No. | Revision | Date |
|-----|----------|------|
|     |          |      |
|     |          |      |
- ISSUED FOR:
- Issued for information
  - Issued for client approval
  - Issued for fabrication
  - Issued for construction

Firefly

|                |                             |
|----------------|-----------------------------|
| DRAWING TITLE: | Typical Frame Connections 4 |
| DRAWN BY:      | Mladin Monica-Mihaela       |
| SCALE:         |                             |
| DRAWING NO:    | A32                         |
| DATE:          | 04.03.2024                  |