

Sheet List	
Sheet Number	Sheet Name
A01	Title Sheet
A02	Front View
A03	Rear View
A04	Building Axonometry
A05	Ground Floor Axonometry
A06	Sun Analysis
A08	Site Plan
A09	Ground Floor Plan
A10	Front Elevation
A11	Rear Elevation
A12	Left Elevation
A13	Right Elevation
A14	Section 1
A15	Section 2
A24	Openings Schedule
A25	Doors / Window Openings
A28	Wall Details
A29	Details 1
A30	Details 2
A31	Details 3
A32	Details 4
A33	Details 5
A34	Details 6
A35	Details 7

Sheet List	
Sheet Number	Sheet Name
A36	Details 8
A37	3D detail
A38	Room Legend
A39	Schedules
A42	Bathroom Schedule
A43	Bathroom
A44	Kitchen Plan and 3D view
A45	Kitchen Finishes
A46	Kitchen Appliances
A47	Finishes
A51	HRS Connections 3D
A52	LGS Connections 3D
A53	Typical Frame Connections
A54	Typical Frame Connections 2
A55	Typical Frame Connections 3
A56	Typical Frame Connections 4
A57	General Construction Notes
B07	Site Location
B40	Electrical Plan
B41	Plumbing Plan
B48	Floor Plan Dimensions
B49	Roof Dimensions
B50	Rain water drainage plan

1. THESE DRAWINGS MUST BE CHECKED BY THE CUSTOMER OR CONTRACTOR PRIOR TO APPROVAL. ANY ERRORS OR OMISSIONS MUST BE REPORTED IN WRITING TO BAUHU PRIOR TO COMMENCEMENT OF CONSTRUCTION.
2. ARCHITECTURAL DRAWINGS SHOULD BE READ IN CONJUNCTION WITH STRUCTURAL DETAILING AND FABRICATION GENERAL ASSEMBLY DRAWINGS.
3. FOR CONSTRUCTION PURPOSES, USE ONLY THE LATEST APPROVED DRAWINGS LABELED 'ISSUED FOR CONSTRUCTION'.
4. DO NOT SCALE FROM THIS DRAWING.
5. THE COMPANY OPERATES USING METRIC DIMENSIONS AS THE PRINCIPAL DENOMINATION.
6. ALL CONCRETE WORKS ARE OUTSIDE OF THE SCOPE OF THE COMPANY. INFORMATION REGARDING SLAB DESIGN AND CONNECTIONS IN THESE DRAWINGS ARE INTENDED FOR GUIDENCE ONLY. FOUNDATION AND SLAB WORKS SHOULD BE DESIGNED AND APPROVED BY A LOCAL STRUCTURAL ENGINEER.
7. THE COMPANY RETAINS FULL TITLE AND OWNERSHIP OF THESE PLANS AND DESIGNS. ANY UNAUTHORISED USE, REPRODUCTION, OR DISTRIBUTION OF THESE PLANS, WHETHER IN WHOLE OR PART, IS EXPRESSLY PROHIBITED WITHOUT PRIOR WRITTEN CONSENT.
8. THE HYBRID STEEL FRAME CONSTRUCTION SYSTEM AND METHODOLOGY DESCRIBED IN THESE PLANS HAS BEEN DEVELOPED BY THE COMPANY AND IS SUBJECT TO A PATENT APPLICATION & ASSIGNMENT - US APPLICATION No. 63/722,841.

No.	Revision	Date

- ISSUED FOR:
- Issued for information

Issued for client approval

Issued for fabrication

Issued for construction

Caribbean cottage

DRAWING TITLE:	Title Sheet
DRAWN BY:	Bernat Stefana
SCALE:	
DRAWING NO:	A01
DATE:	18.11.2025

Entrance View





1 Front view

1. THESE DRAWINGS MUST BE CHECKED BY THE CUSTOMER OR CONTRACTOR PRIOR TO APPROVAL. ANY ERRORS OR OMISSIONS MUST BE REPORTED IN WRITING TO BAUHU PRIOR TO COMMENCEMENT OF CONSTRUCTION.
2. ARCHITECTURAL DRAWINGS SHOULD BE READ IN CONJUNCTION WITH STRUCTURAL DETAILING AND FABRICATION GENERAL ASSEMBLY DRAWINGS.
3. FOR CONSTRUCTION PURPOSES, USE ONLY THE LATEST APPROVED DRAWINGS LABELED 'ISSUED FOR CONSTRUCTION'.
4. DO NOT SCALE FROM THIS DRAWING.
5. THE COMPANY OPERATES USING METRIC DIMENSIONS AS THE PRINCIPAL DENOMINATION.
6. ALL CONCRETE WORKS ARE OUTSIDE OF THE SCOPE OF THE COMPANY. INFORMATION REGARDING SLAB DESIGN AND CONNECTIONS IN THESE DRAWINGS ARE INTENDED FOR GUIDENCE ONLY. FOUNDATION AND SLAB WORKS SHOULD BE DESIGNED AND APPROVED BY A LOCAL STRUCTURAL ENGINEER.
7. THE COMPANY RETAINS FULL TITLE AND OWNERSHIP OF THESE PLANS AND DESIGNS. ANY UNAUTHORISED USE, REPRODUCTION, OR DISTRIBUTION OF THESE PLANS, WHETHER IN WHOLE OR PART, IS EXPRESSLY PROHIBITED WITHOUT PRIOR WRITTEN CONSENT.
8. THE HYBRID STEEL FRAME CONSTRUCTION SYSTEM AND METHODOLOGY DESCRIBED IN THESE PLANS HAS BEEN DEVELOPED BY THE COMPANY AND IS SUBJECT TO A PATENT APPLICATION & ASSIGNMENT - US APPLICATION No. 63/722,841.

No.	Revision	Date

ISSUED FOR:

Issued for information

Issued for client approval

Issued for fabrication

Issued for construction

Caribbean cottage

DRAWING TITLE:
Front View

DRAWN BY:
Bernat Stefana

SCALE:

DRAWING NO:
A02

DATE:
18.11.2025



2

Rear view

1. THESE DRAWINGS MUST BE CHECKED BY THE CUSTOMER OR CONTRACTOR PRIOR TO APPROVAL. ANY ERRORS OR OMISSIONS MUST BE REPORTED IN WRITING TO BAUHU PRIOR TO COMMENCEMENT OF CONSTRUCTION.
2. ARCHITECTURAL DRAWINGS SHOULD BE READ IN CONJUNCTION WITH STRUCTURAL DETAILING AND FABRICATION GENERAL ASSEMBLY DRAWINGS.
3. FOR CONSTRUCTION PURPOSES, USE ONLY THE LATEST APPROVED DRAWINGS LABELED 'ISSUED FOR CONSTRUCTION'.
4. DO NOT SCALE FROM THIS DRAWING.
5. THE COMPANY OPERATES USING METRIC DIMENSIONS AS THE PRINCIPAL DENOMINATION.
6. ALL CONCRETE WORKS ARE OUTSIDE OF THE SCOPE OF THE COMPANY. INFORMATION REGARDING SLAB DESIGN AND CONNECTIONS IN THESE DRAWINGS ARE INTENDED FOR GUIDENCE ONLY. FOUNDATION AND SLAB WORKS SHOULD BE DESIGNED AND APPROVED BY A LOCAL STRUCTURAL ENGINEER.
7. THE COMPANY RETAINS FULL TITLE AND OWNERSHIP OF THESE PLANS AND DESIGNS. ANY UNAUTHORISED USE, REPRODUCTION, OR DISTRIBUTION OF THESE PLANS, WHETHER IN WHOLE OR PART, IS EXPRESSLY PROHIBITED WITHOUT PRIOR WRITTEN CONSENT.
8. THE HYBRID STEEL FRAME CONSTRUCTION SYSTEM AND METHODOLOGY DESCRIBED IN THESE PLANS HAS BEEN DEVELOPED BY THE COMPANY AND IS SUBJECT TO A PATENT APPLICATION & ASSIGNMENT - US APPLICATION No. 63/722,841.


No.	Revision	Date

ISSUED FOR:

- Issued for information
- Issued for client approval
- Issued for fabrication
- Issued for construction

Caribbean cottage

DRAWING TITLE:	Rear View
DRAWN BY:	Bernat Stefana
SCALE:	
DRAWING NO:	A03
DATE:	18.11.2025

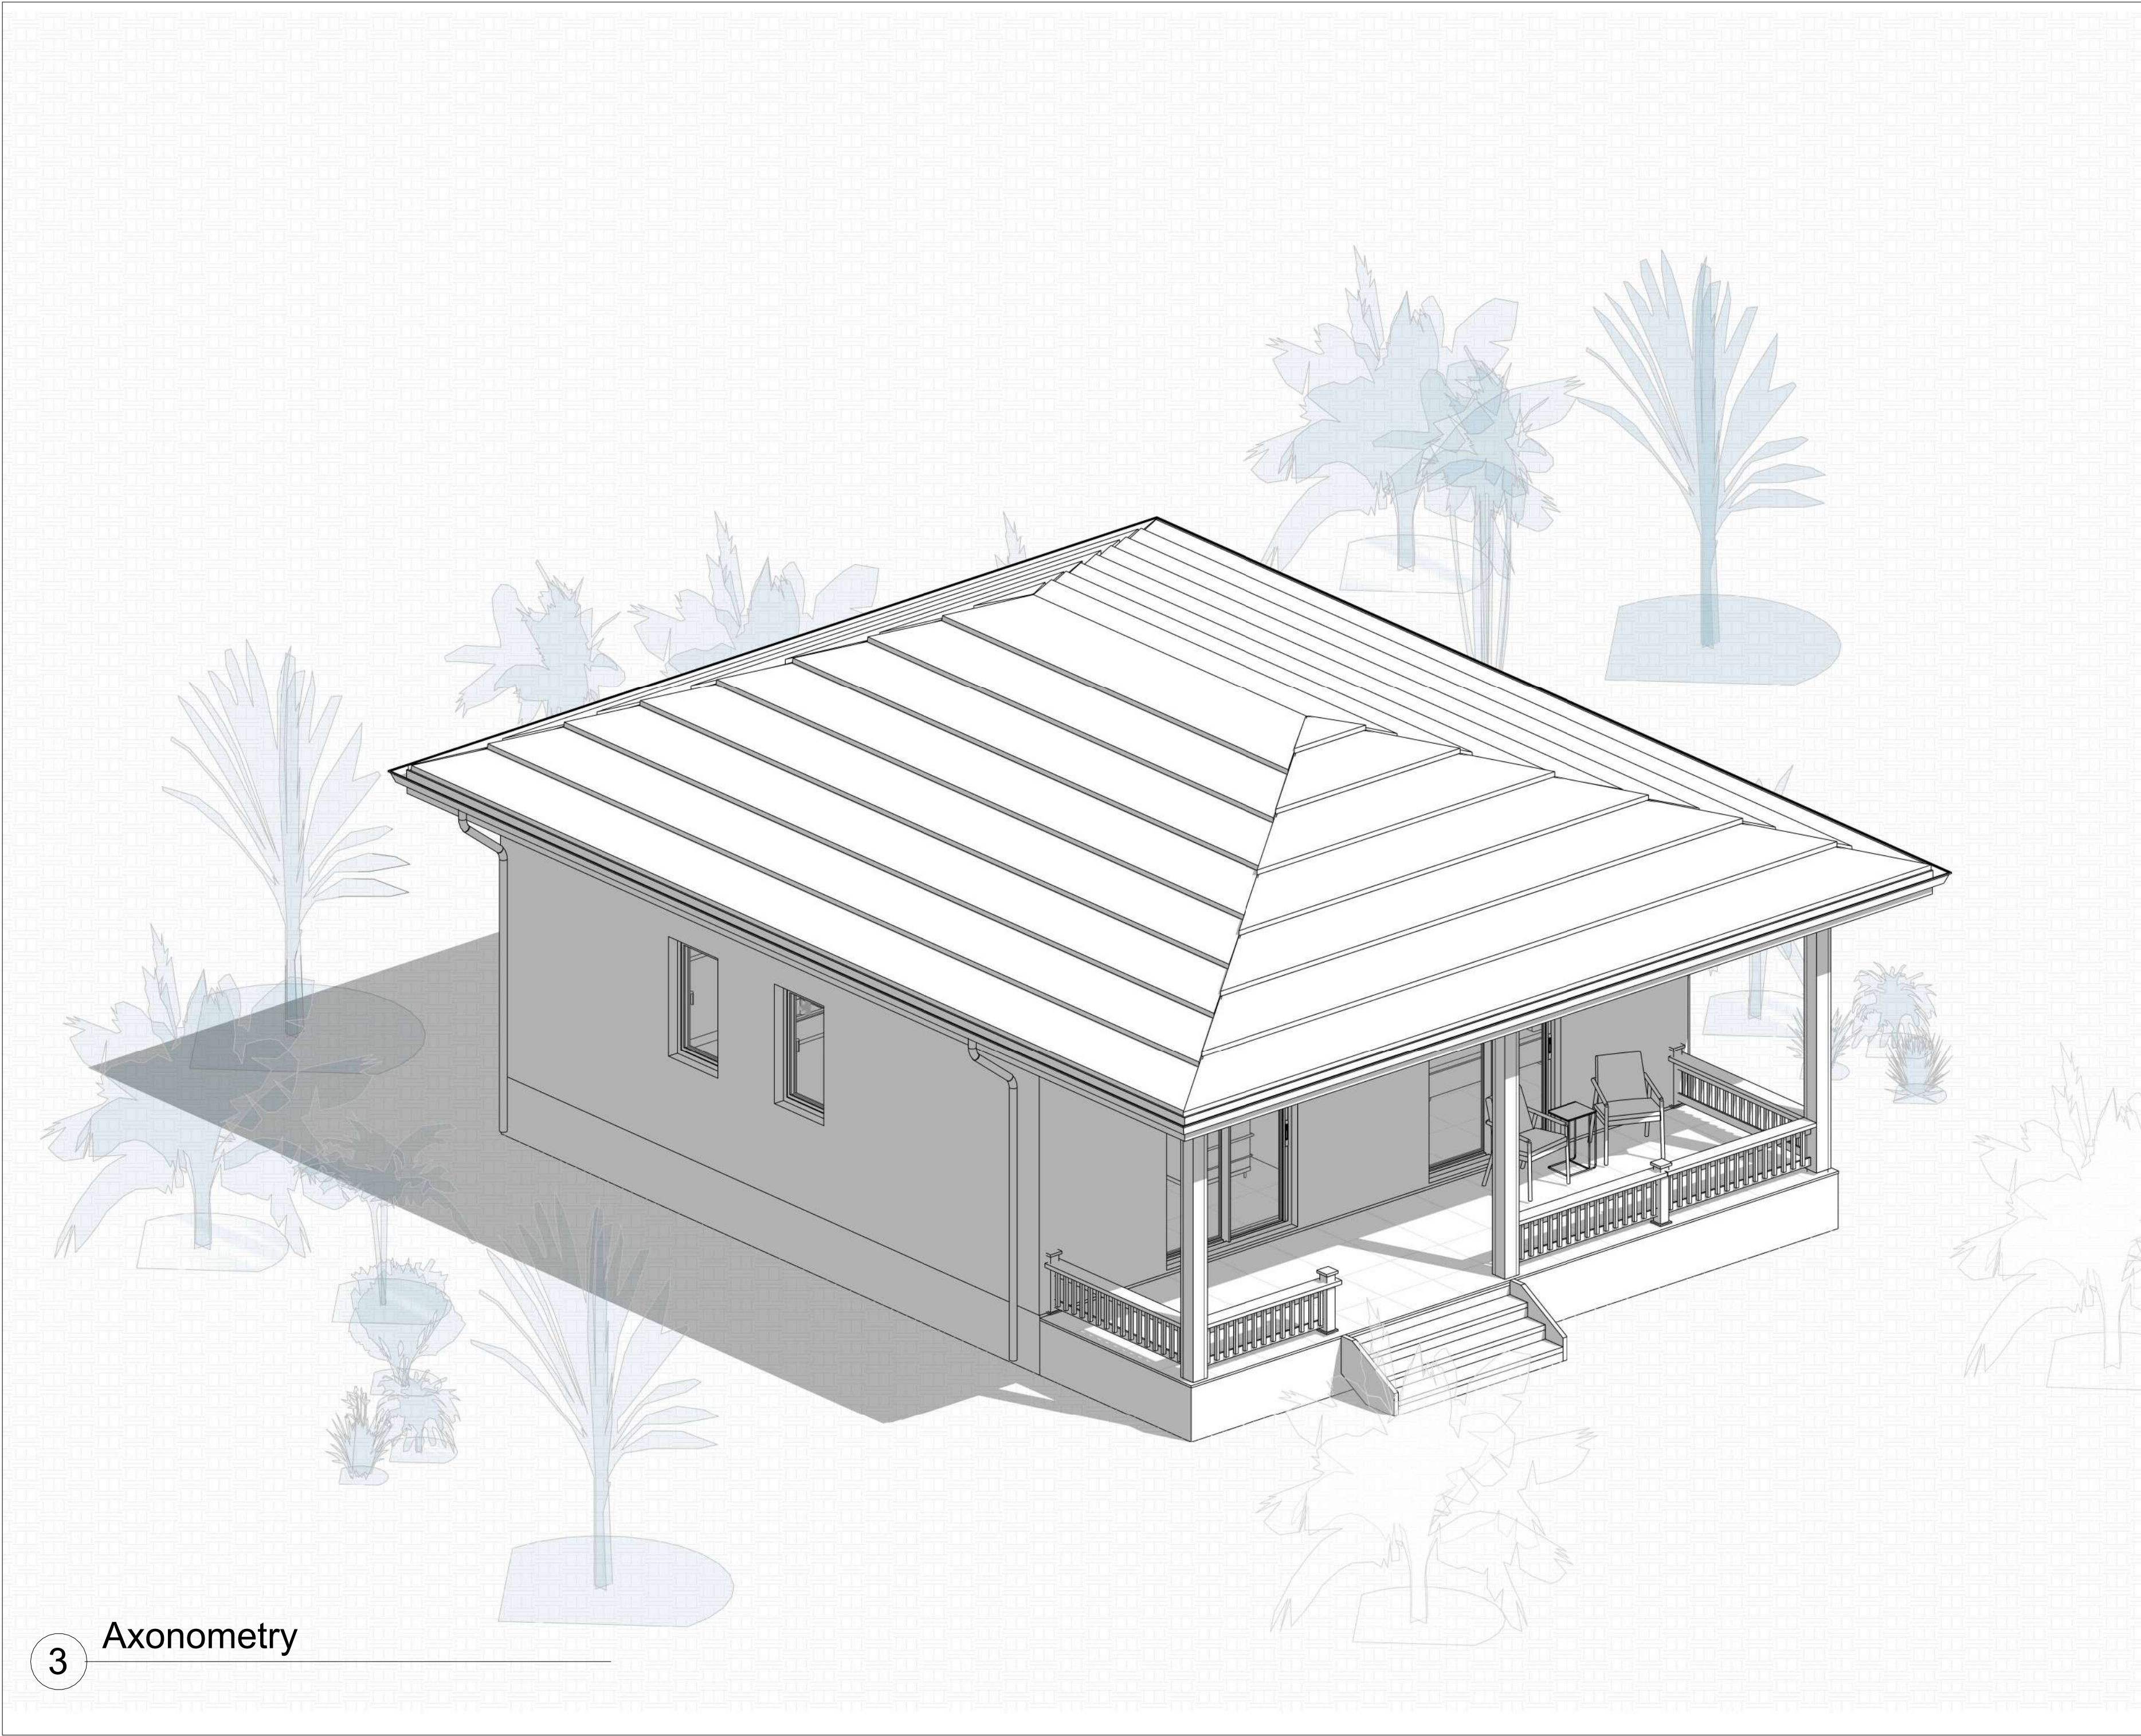

1. THESE DRAWINGS MUST BE CHECKED BY THE CUSTOMER OR CONTRACTOR PRIOR TO APPROVAL. ANY ERRORS OR OMISSIONS MUST BE REPORTED IN WRITING TO BAUHU PRIOR TO COMMENCEMENT OF CONSTRUCTION.
2. ARCHITECTURAL DRAWINGS SHOULD BE READ IN CONJUNCTION WITH STRUCTURAL DETAILING AND FABRICATION GENERAL ASSEMBLY DRAWINGS.
3. FOR CONSTRUCTION PURPOSES, USE ONLY THE LATEST APPROVED DRAWINGS LABELED 'ISSUED FOR CONSTRUCTION'.
4. DO NOT SCALE FROM THIS DRAWING.
5. THE COMPANY OPERATES USING METRIC DIMENSIONS AS THE PRINCIPAL DENOMINATION.
6. ALL CONCRETE WORKS ARE OUTSIDE OF THE SCOPE OF THE COMPANY. INFORMATION REGARDING SLAB DESIGN AND CONNECTIONS IN THESE DRAWINGS ARE INTENDED FOR GUIDENCE ONLY. FOUNDATION AND SLAB WORKS SHOULD BE DESIGNED AND APPROVED BY A LOCAL STRUCTURAL ENGINEER.
7. THE COMPANY RETAINS FULL TITLE AND OWNERSHIP OF THESE PLANS AND DESIGNS. ANY UNAUTHORISED USE, REPRODUCTION, OR DISTRIBUTION OF THESE PLANS, WHETHER IN WHOLE OR PART, IS EXPRESSLY PROHIBITED WITHOUT PRIOR WRITTEN CONSENT.
8. THE HYBRID STEEL FRAME CONSTRUCTION SYSTEM AND METHODOLOGY DESCRIBED IN THESE PLANS HAS BEEN DEVELOPED BY THE COMPANY AND IS SUBJECT TO A PATENT APPLICATION & ASSIGNMENT - US APPLICATION No. 63/722,841.

No.	Revision	Date

ISSUED FOR:

Issued for information

Issued for client approval

Issued for fabrication

Issued for construction

Caribbean cottage


DRAWING TITLE:
Building Axonometry

DRAWN BY:
Bernat Stefana

SCALE:

DRAWING NO:
A04

DATE:
18.11.2025

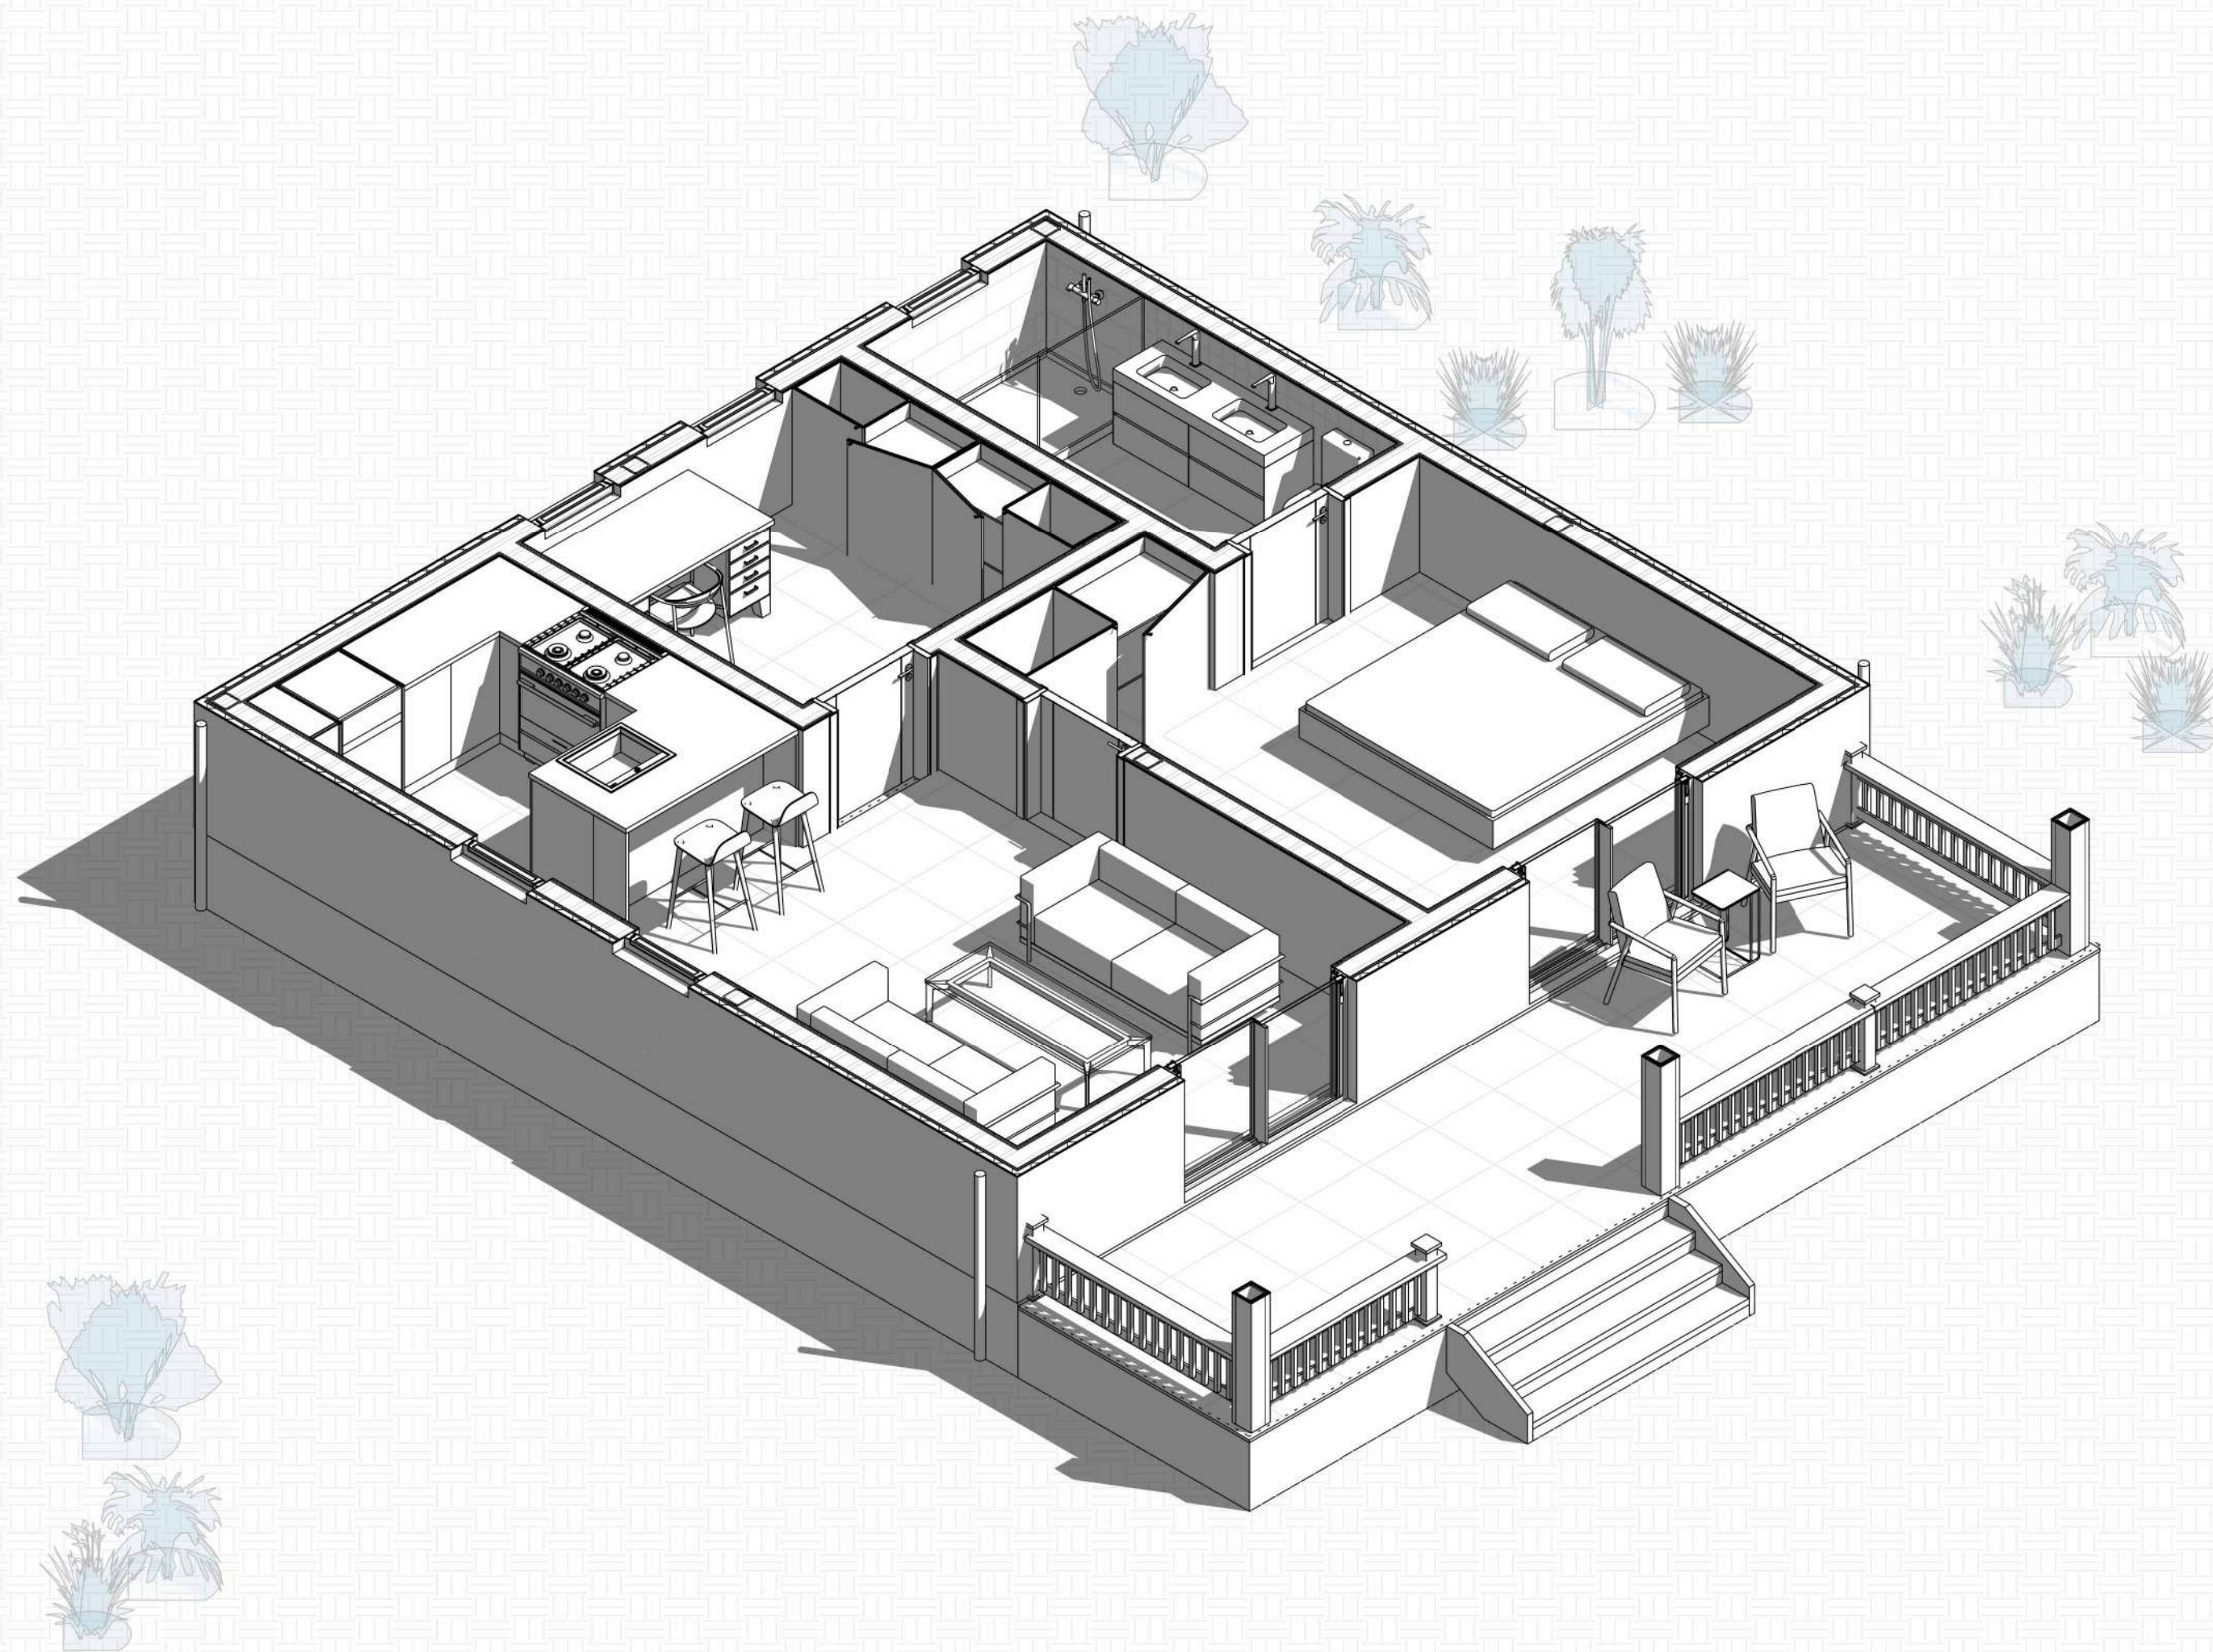

1. THESE DRAWINGS MUST BE CHECKED BY THE CUSTOMER OR CONTRACTOR PRIOR TO APPROVAL. ANY ERRORS OR OMISSIONS MUST BE REPORTED IN WRITING TO BAUHU PRIOR TO COMMENCEMENT OF CONSTRUCTION.
2. ARCHITECTURAL DRAWINGS SHOULD BE READ IN CONJUNCTION WITH STRUCTURAL DETAILING AND FABRICATION GENERAL ASSEMBLY DRAWINGS.
3. FOR CONSTRUCTION PURPOSES, USE ONLY THE LATEST APPROVED DRAWINGS LABELED 'ISSUED FOR CONSTRUCTION'.
4. DO NOT SCALE FROM THIS DRAWING.
5. THE COMPANY OPERATES USING METRIC DIMENSIONS AS THE PRINCIPAL DENOMINATION.
6. ALL CONCRETE WORKS ARE OUTSIDE OF THE SCOPE OF THE COMPANY. INFORMATION REGARDING SLAB DESIGN AND CONNECTIONS IN THESE DRAWINGS ARE INTENDED FOR GUIDENCE ONLY. FOUNDATION AND SLAB WORKS SHOULD BE DESIGNED AND APPROVED BY A LOCAL STRUCTURAL ENGINEER.
7. THE COMPANY RETAINS FULL TITLE AND OWNERSHIP OF THESE PLANS AND DESIGNS. ANY UNAUTHORISED USE, REPRODUCTION, OR DISTRIBUTION OF THESE PLANS, WHETHER IN WHOLE OR PART, IS EXPRESSLY PROHIBITED WITHOUT PRIOR WRITTEN CONSENT.
8. THE HYBRID STEEL FRAME CONSTRUCTION SYSTEM AND METHODOLOGY DESCRIBED IN THESE PLANS HAS BEEN DEVELOPED BY THE COMPANY AND IS SUBJECT TO A PATENT APPLICATION & ASSIGNMENT - US APPLICATION No. 63/722,841.

No.	Revision	Date

ISSUED FOR:

Issued for information

Issued for client approval

Issued for fabrication

Issued for construction

Caribbean cottage


DRAWING TITLE:
Ground Floor Axonometry

DRAWN BY:
Bernat Stefana

SCALE:

DRAWING NO:
A05

DATE:
18.11.2025

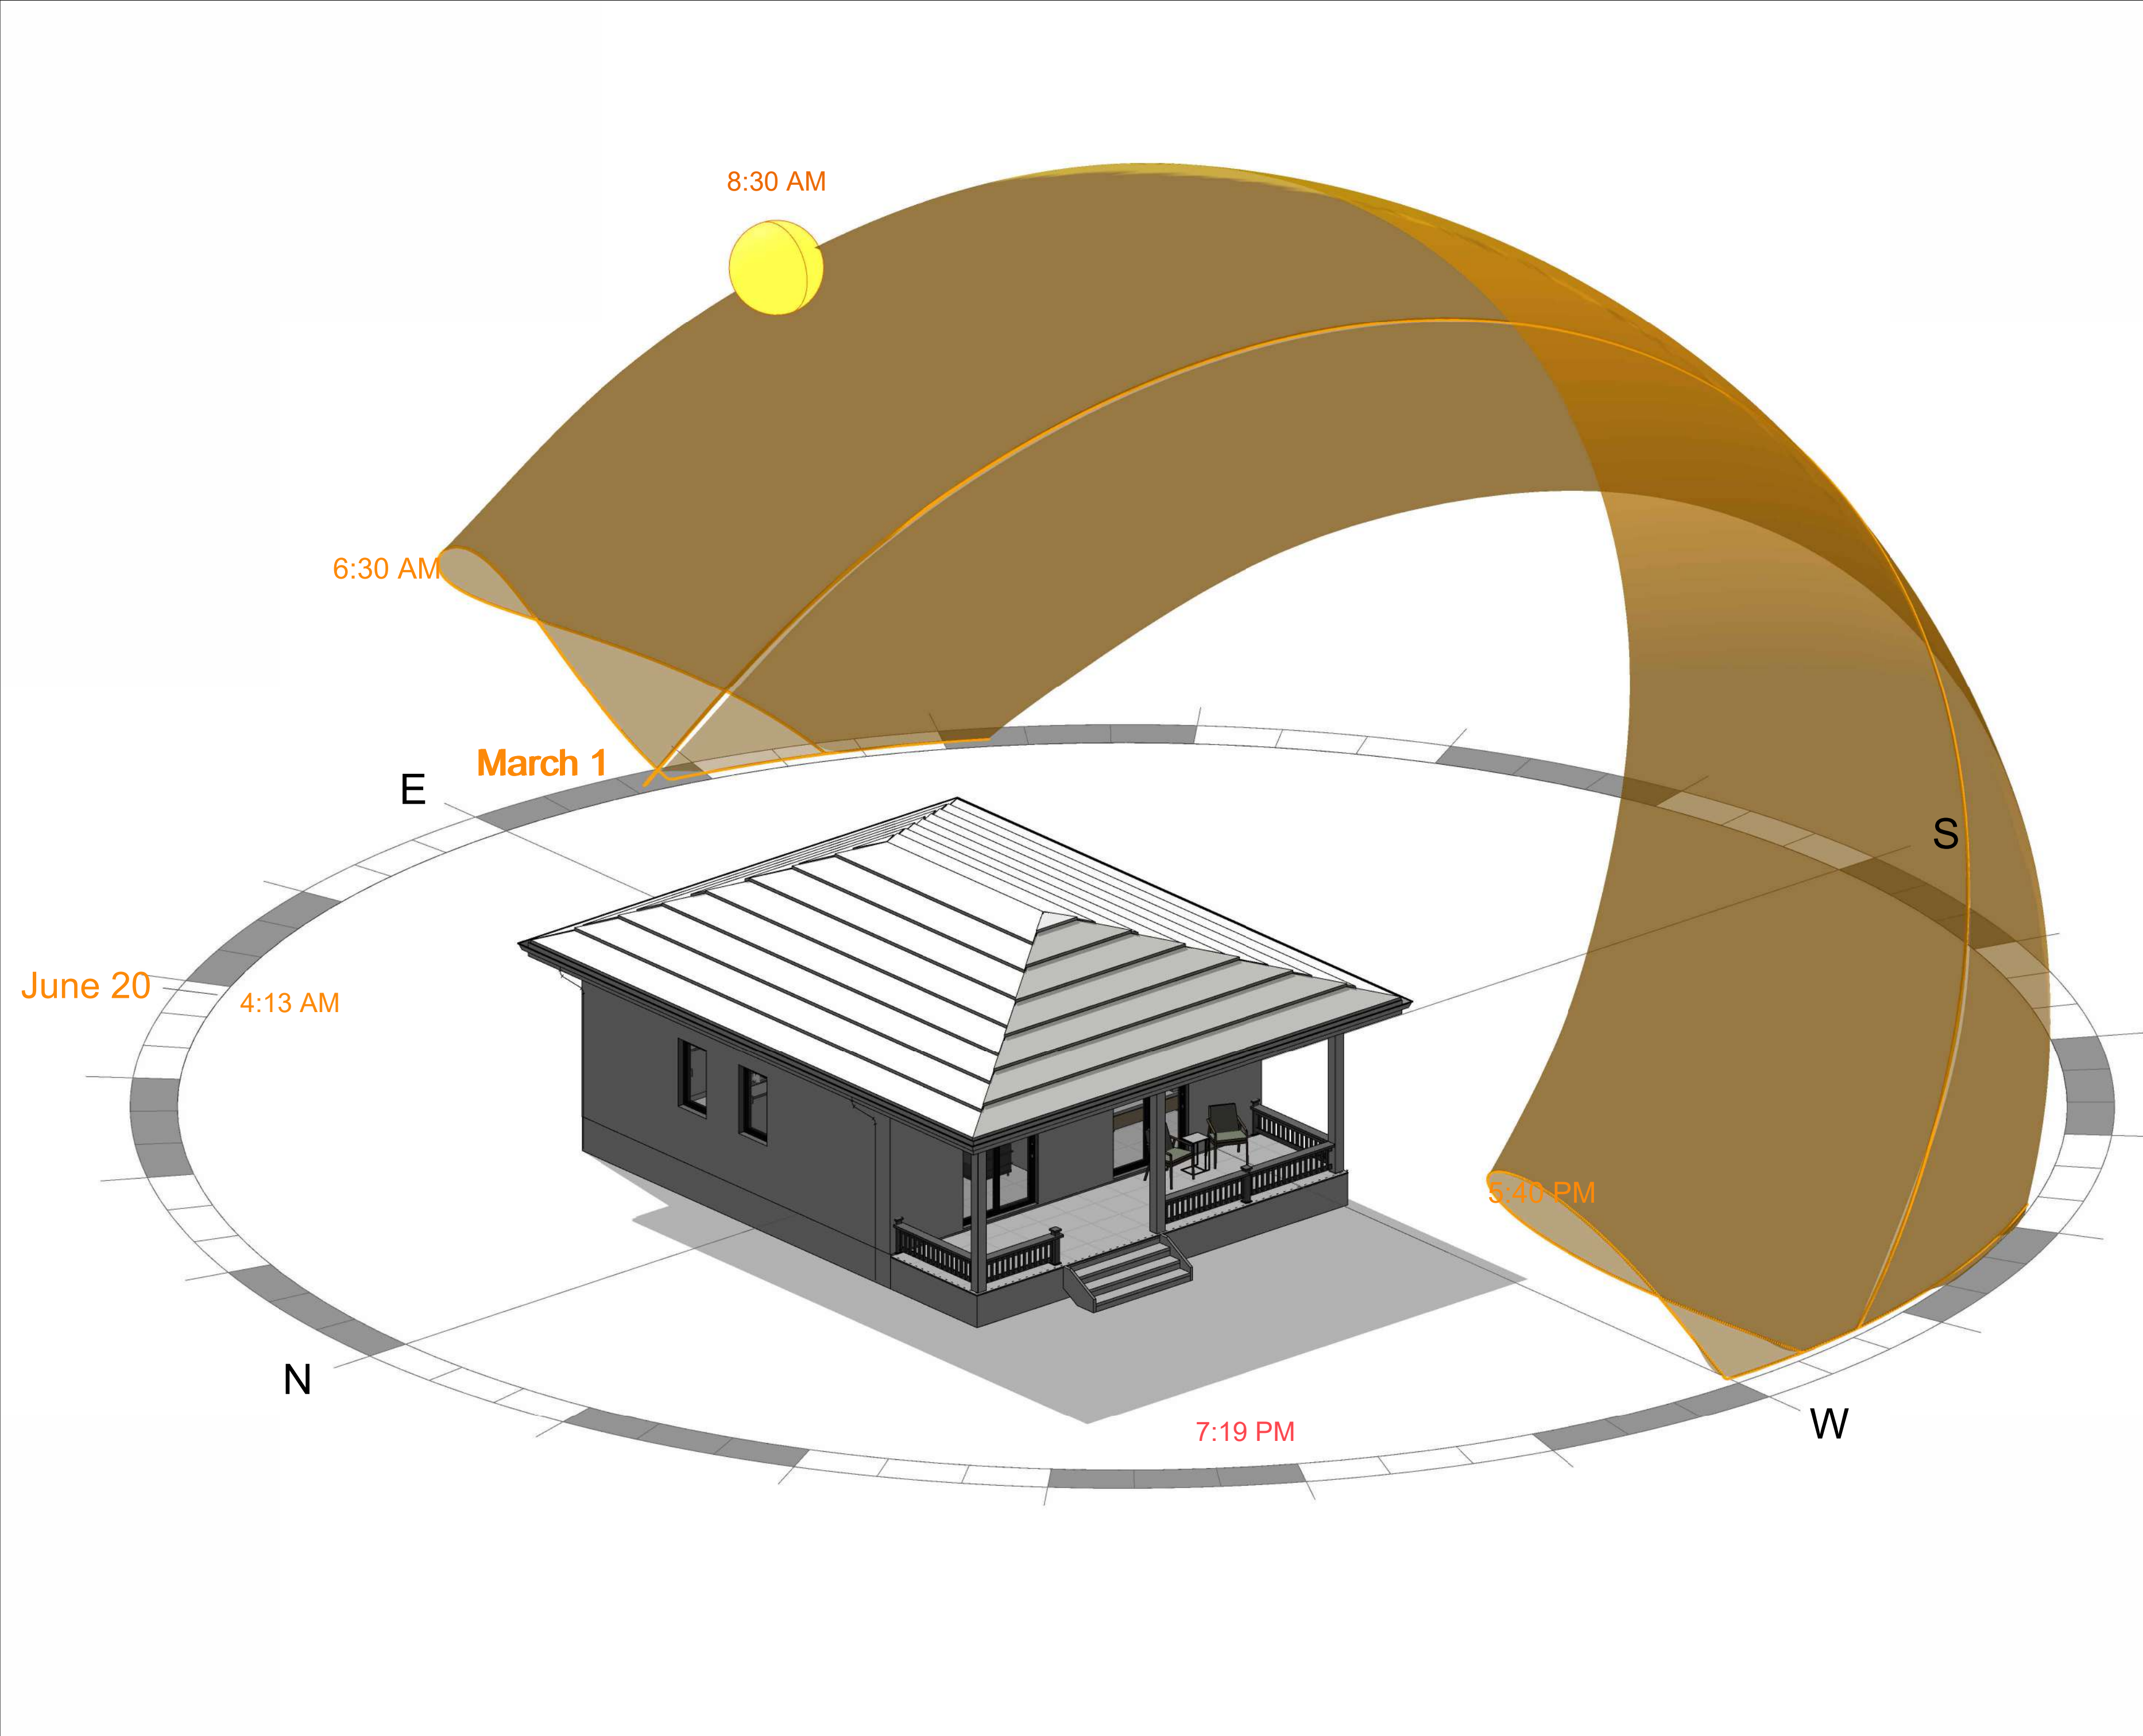

BAUHU

MODULAR • BUILDING • SOLUTIONS

1. THESE DRAWINGS MUST BE CHECKED BY THE CUSTOMER OR CONTRACTOR PRIOR TO APPROVAL. ANY ERRORS OR OMISSIONS MUST BE REPORTED IN WRITING TO BAUHU PRIOR TO COMMENCEMENT OF CONSTRUCTION.

2. ARCHITECTURAL DRAWINGS SHOULD BE READ IN CONJUNCTION WITH STRUCTURAL DETAILING AND FABRICATION GENERAL ASSEMBLY DRAWINGS.

3. FOR CONSTRUCTION PURPOSES, USE ONLY THE LATEST APPROVED DRAWINGS LABELED 'ISSUED FOR CONSTRUCTION'.

4. DO NOT SCALE FROM THIS DRAWING.

5. THE COMPANY OPERATES USING METRIC DIMENSIONS AS THE PRINCIPAL DENOMINATION.

6. ALL CONCRETE WORKS ARE OUTSIDE OF THE SCOPE OF THE COMPANY. INFORMATION REGARDING SLAB DESIGN AND CONNECTIONS IN THESE DRAWINGS ARE INTENDED FOR GUIDENCE ONLY. FOUNDATION AND SLAB WORKS SHOULD BE DESIGNED AND APPROVED BY A LOCAL STRUCTURAL ENGINEER.

7. THE COMPANY RETAINS FULL TITLE AND OWNERSHIP OF THESE PLANS AND DESIGNS. ANY UNAUTHORISED USE, REPRODUCTION, OR DISTRIBUTION OF THESE PLANS, WHETHER IN WHOLE OR PART, IS EXPRESSLY PROHIBITED WITHOUT PRIOR WRITTEN CONSENT.

8. THE HYBRID STEEL FRAME CONSTRUCTION SYSTEM AND METHODOLOGY DESCRIBED IN THESE PLANS HAS BEEN DEVELOPED BY THE COMPANY AND IS SUBJECT TO A PATENT APPLICATION & ASSIGNMENT - US APPLICATION No. 63/722,841.

No.	Revision	Date

ISSUED FOR:

Issued for information

Issued for client approval

Issued for fabrication

Issued for construction

Caribbean cottage

DRAWING TITLE:

Sun Analysis

DRAWN BY:

Bernat Stefana

SCALE:


DRAWING NO:

A06

DATE:

18.11.2025

LEFT ELEVATION

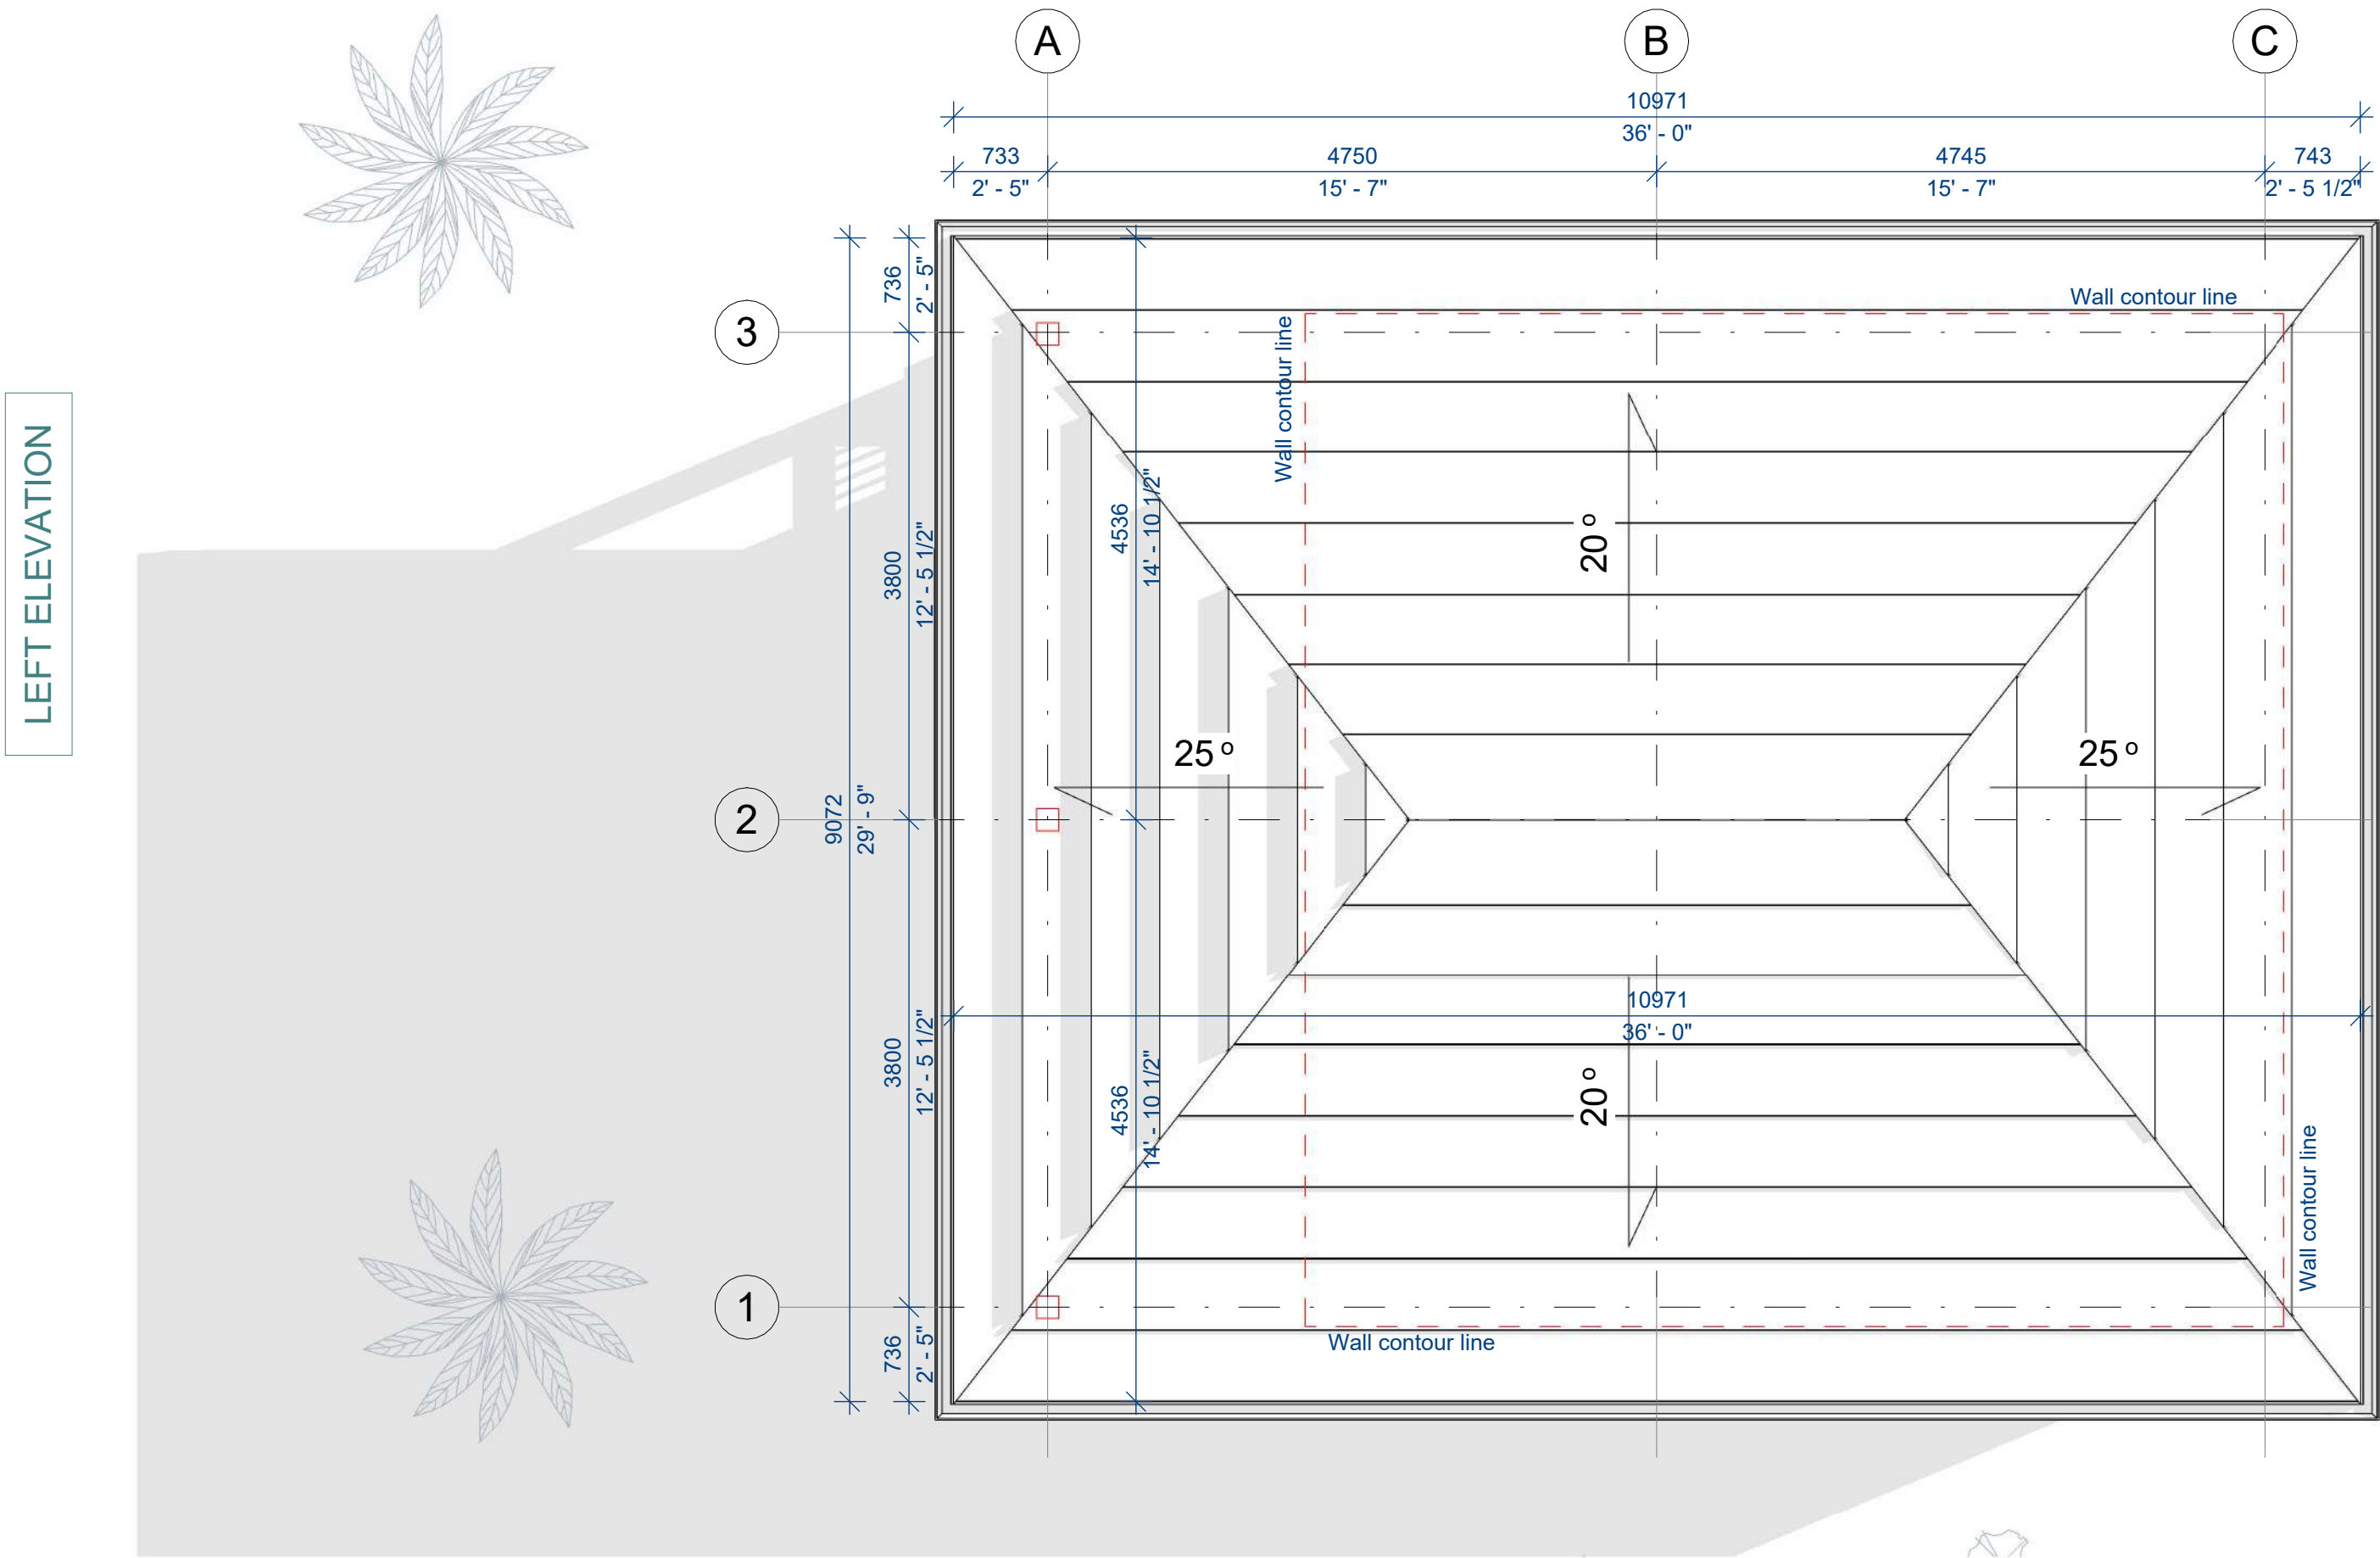

Note:

- Foundation details, slab plans and layout are provided for information only. Refer to structural engineering plans for layout, connection details, stud embedment and edge distances. RC pier and footing to be designed by a local structural engineer according to site conditions.
- All groundworks, landscape and hardscape, fencing, footings, foundation and floor slab works, cisterns and septic tanks are the responsibility of the owner. Building components are provided on the assumption that the site is prepared and an adequate foundation approved by a competent local structural engineer, has been provided. All services and sub-slab conduits should be completed finishing in a perfectly square and level concrete platform to enable the building erection
- Gutters and downspouts - by others

1. THESE DRAWINGS MUST BE CHECKED BY THE CUSTOMER OR CONTRACTOR PRIOR TO APPROVAL. ANY ERRORS OR OMISSIONS MUST BE REPORTED IN WRITING TO BAUHU PRIOR TO COMMENCEMENT OF CONSTRUCTION.
2. ARCHITECTURAL DRAWINGS SHOULD BE READ IN CONJUNCTION WITH STRUCTURAL DETAILING AND FABRICATION GENERAL ASSEMBLY DRAWINGS.
3. FOR CONSTRUCTION PURPOSES, USE ONLY THE LATEST APPROVED DRAWINGS LABELED 'ISSUED FOR CONSTRUCTION'.
4. DO NOT SCALE FROM THIS DRAWING.
5. THE COMPANY OPERATES USING METRIC DIMENSIONS AS THE PRINCIPAL DENOMINATION.
6. ALL CONCRETE WORKS ARE OUTSIDE OF THE SCOPE OF THE COMPANY. INFORMATION REGARDING SLAB DESIGN AND CONNECTIONS IN THESE DRAWINGS ARE INTENDED FOR GUIDENCE ONLY. FOUNDATION AND SLAB WORKS SHOULD BE DESIGNED AND APPROVED BY A LOCAL STRUCTURAL ENGINEER.
7. THE COMPANY RETAINS FULL TITLE AND OWNERSHIP OF THESE PLANS AND DESIGNS. ANY UNAUTHORISED USE, REPRODUCTION, OR DISTRIBUTION OF THESE PLANS, WHETHER IN WHOLE OR PART, IS EXPRESSLY PROHIBITED WITHOUT PRIOR WRITTEN CONSENT.
8. THE HYBRID STEEL FRAME CONSTRUCTION SYSTEM AND METHODOLOGY DESCRIBED IN THESE PLANS HAS BEEN DEVELOPED BY THE COMPANY AND IS SUBJECT TO A PATENT APPLICATION & ASSIGNMENT - US APPLICATION No. 63/722,841.

No.	Revision	Date

ISSUED FOR:

Issued for information

Issued for client approval

Issued for fabrication

Issued for construction

Caribbean cottage

DRAWING TITLE: Site Plan

DRAWN BY: Bernat Stefana

SCALE: 1 : 50

DRAWING NO: A08

DATE: 18.11.2025

- THESE DRAWINGS MUST BE CHECKED BY THE CUSTOMER OR CONTRACTOR PRIOR TO APPROVAL. ANY ERRORS OR OMISSIONS MUST BE REPORTED IN WRITING TO BAUHU PRIOR TO COMMENCEMENT OF CONSTRUCTION.
- ARCHITECTURAL DRAWINGS SHOULD BE READ IN CONJUNCTION WITH STRUCTURAL DETAILING AND FABRICATION GENERAL ASSEMBLY DRAWINGS.
- FOR CONSTRUCTION PURPOSES, USE ONLY THE LATEST APPROVED DRAWINGS LABELED 'ISSUED FOR CONSTRUCTION'.
- DO NOT SCALE FROM THIS DRAWING.
- THE COMPANY OPERATES USING METRIC DIMENSIONS AS THE PRINCIPAL DENOMINATION.
- ALL CONCRETE WORKS ARE OUTSIDE OF THE SCOPE OF THE COMPANY. INFORMATION REGARDING SLAB DESIGN AND CONNECTIONS IN THESE DRAWINGS ARE INTENDED FOR GUIDANCE ONLY. FOUNDATION AND SLAB WORKS SHOULD BE DESIGNED AND APPROVED BY A LOCAL STRUCTURAL ENGINEER.
- THE COMPANY RETAINS FULL TITLE AND OWNERSHIP OF THESE PLANS AND DESIGNS. ANY UNAUTHORISED USE, REPRODUCTION, OR DISTRIBUTION OF THESE PLANS, WHETHER IN WHOLE OR PART, IS EXPRESSLY PROHIBITED WITHOUT PRIOR WRITTEN CONSENT.
- THE HYBRID STEEL FRAME CONSTRUCTION SYSTEM AND METHODOLOGY DESCRIBED IN THESE PLANS HAS BEEN DEVELOPED BY THE COMPANY AND IS SUBJECT TO A PATENT APPLICATION & ASSIGNMENT - US APPLICATION No. 63/722,841.

No.	Revision	Date

ISSUED FOR:

Issued for information

Issued for client approval

Issued for fabrication

Issued for construction

Caribbean cottage

DRAWING TITLE:

Ground Floor Plan

DRAWN BY:

Bernat Stefana

SCALE:

As indicated


DRAWING NO:

A09

DATE:

18.11.2025

FRONT ELEVATION

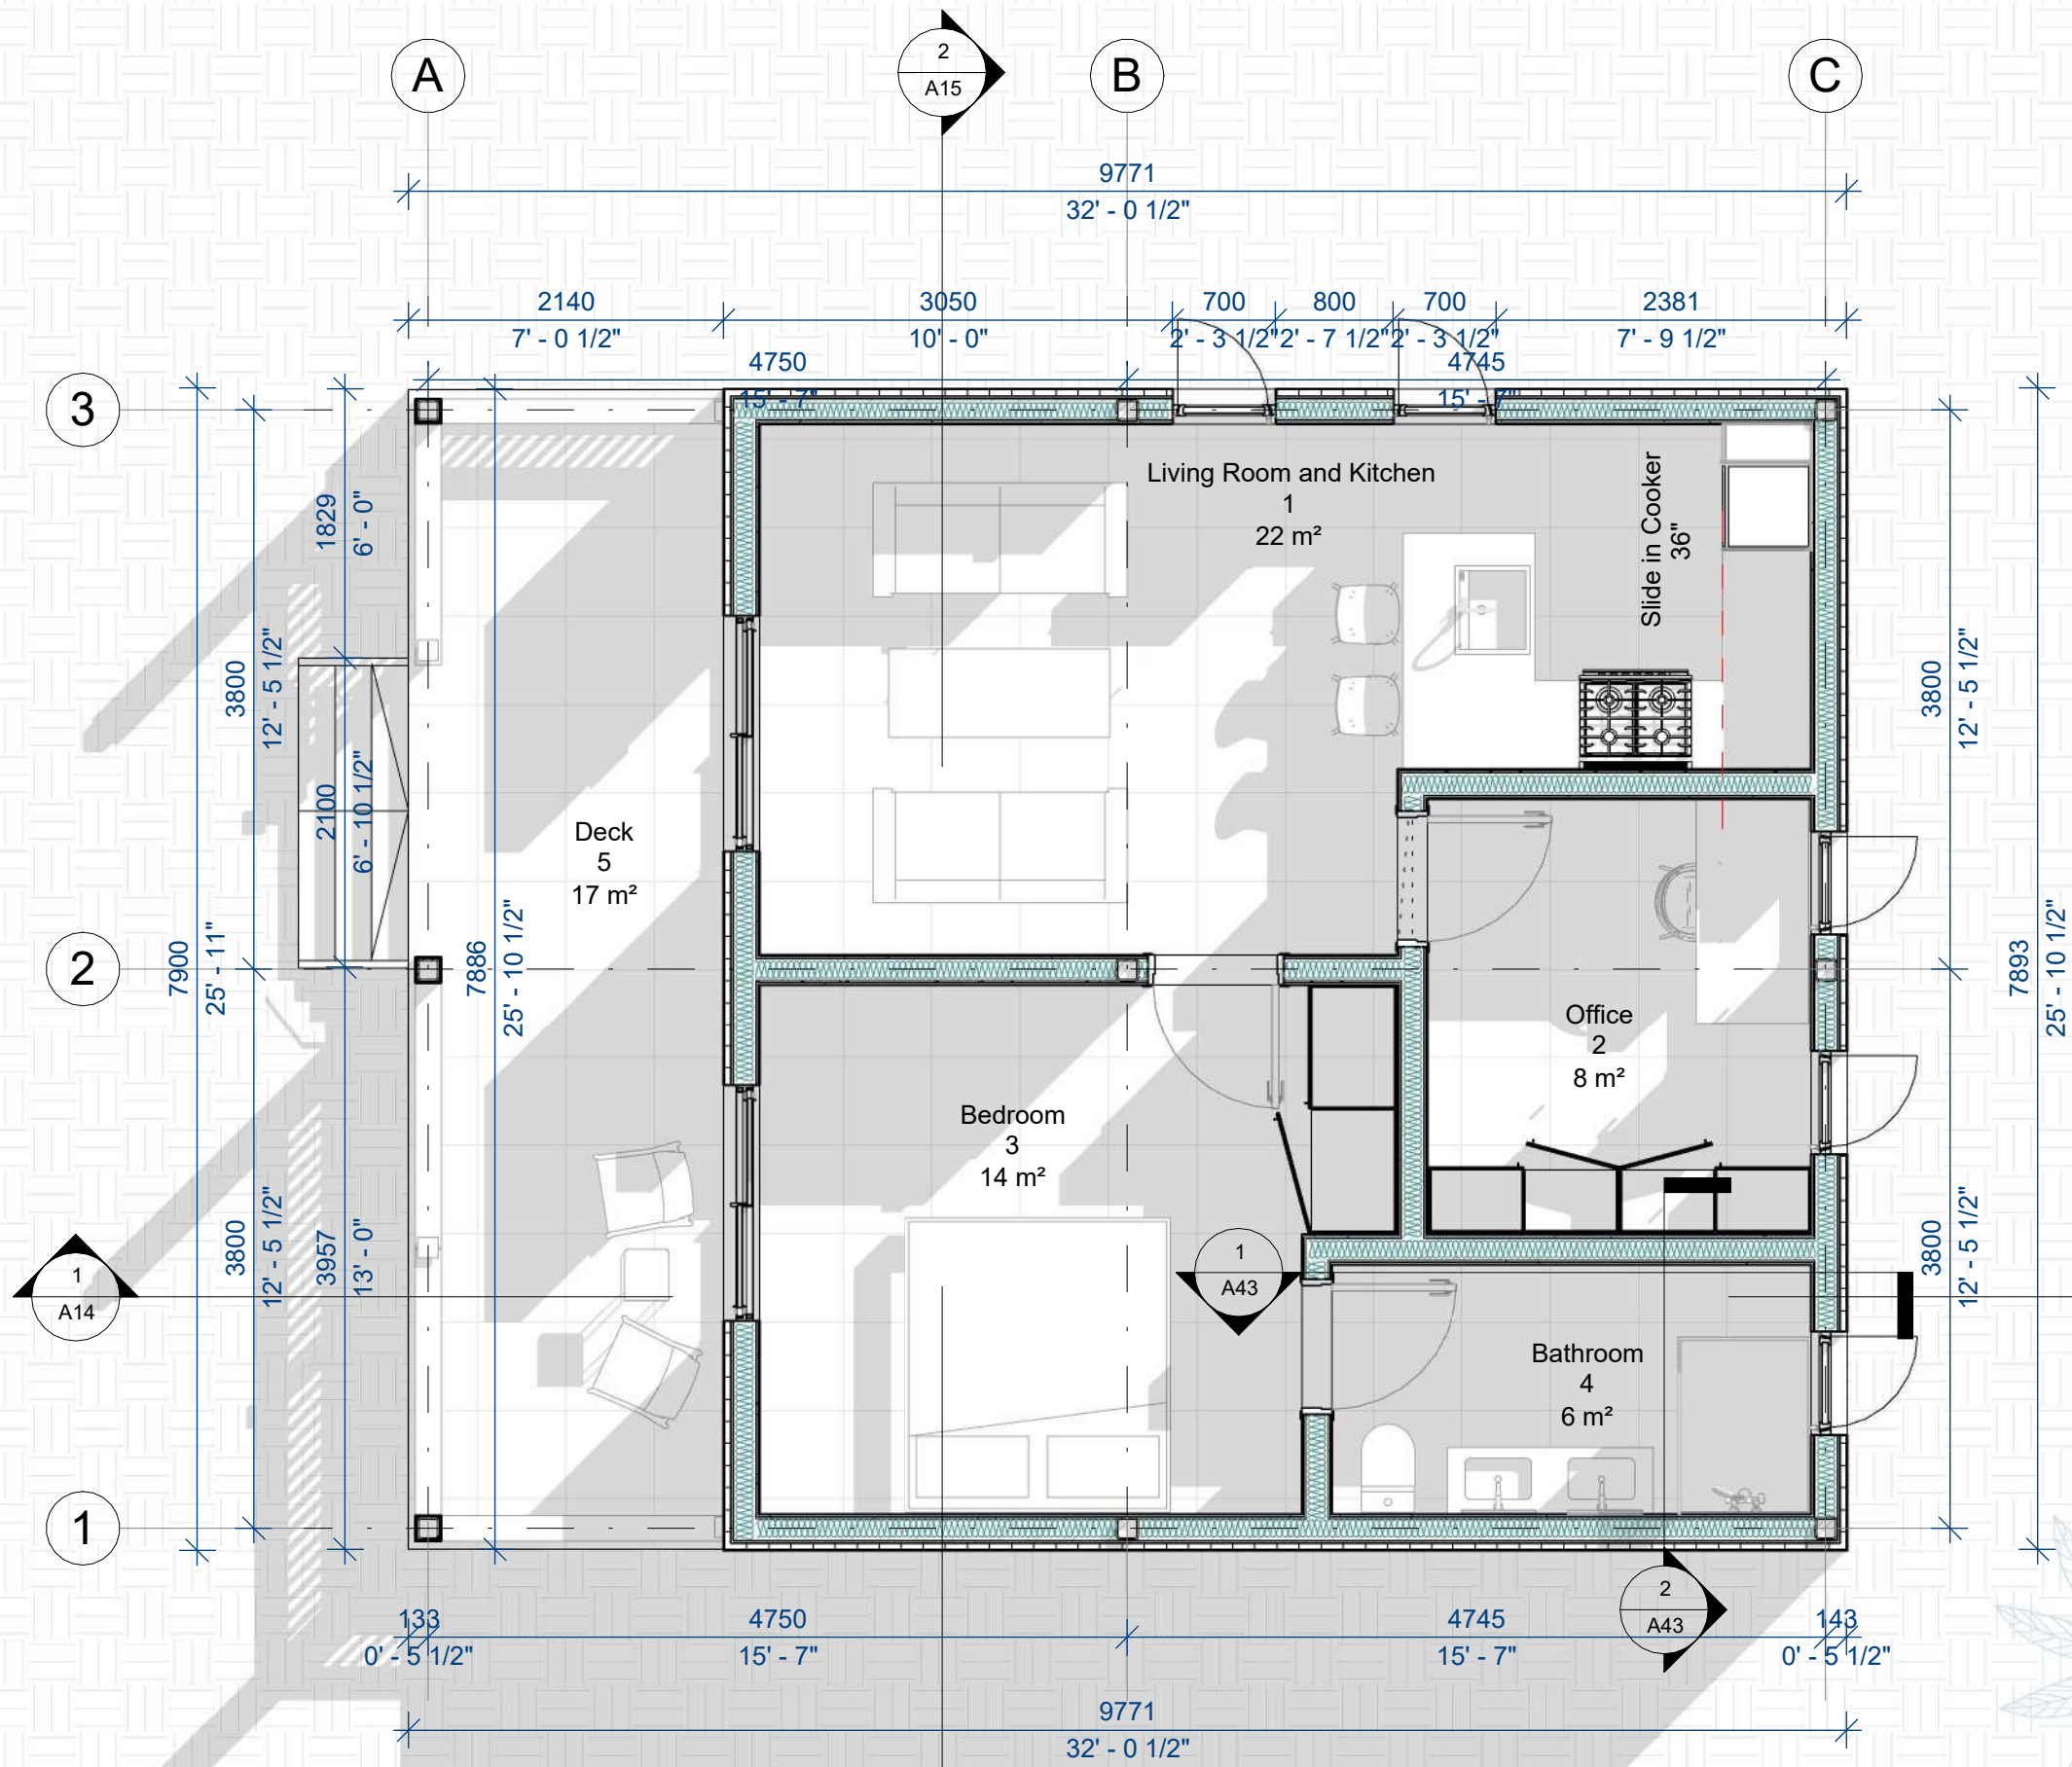

REAR ELEVATION

Room Schedule				
No.	Room Name	Sq. Meter	Sq. Feet	Perimeter
1	Living Room and Kitchen	22 m²	239.4 ft²	21568
2	Office	8 m²	83.2 ft²	11141
3	Bedroom	14 m²	154.8 ft²	15869
4	Bathroom	6 m²	59.4 ft²	9902
5	Deck	17 m²	180.2 ft²	20495
Grand total		67 m²	716.8 ft²	

Note:

- Freestanding furniture and equipment are shown for illustrative purposes only. Renderings and reference images are for guidance only.
- Artisanal timber and carpentry requirements such as fretwork, architectural timber finishes, decorative railings, deck and pergola structures, shade louvres, interior stairs and hand railing are to be provided by others.
- Railings and balustrades will be provided by others. Drawings are made for design purposes only. Refer to structural design drawings for post fixing dimensions.
- External HRS columns will be provided assuming a 50mm (2") height drop between interior concrete slab and exterior terrace concrete slab unless site conditions dictate otherwise. Final exterior slab height to be determined by the contractor. Internal floor screed and waterproofing membrane is to be supplied by the contractor.
- Contractors should ensure a correct fall is applied to external tiled terrace areas to facilitate rainwater drainage.
- Contractors should read these drawings in conjunction with structural engineering design drawings.
- Foundation details, slab plans and layout are provided for information only. Refer to structural engineering plans for layout, connection details, stud embedment and edge distances. RC pier and footing to be designed by a local structural engineer according to site conditions.
- All groundworks, landscape and hardscape, fencing, footings, foundation and floor slab works, cisterns and septic tanks are the responsibility of the owner. Building components are provided on the assumption that the site is prepared and an adequate foundation approved by a competent local structural engineer, has been provided. All services and sub-slab conduits should be completed finishing in a perfectly square and level concrete platform to enable the building erection.
- Gutters and downspouts - by others

LEFT ELEVATION

RIGHT ELEVATION

Acces

Deck
17m² / 183 ft²

Building
60.3 m² / 649 ft²

1. THESE DRAWINGS MUST BE CHECKED BY THE CUSTOMER OR CONTRACTOR PRIOR TO APPROVAL. ANY ERRORS OR OMISSIONS MUST BE REPORTED IN WRITING TO BAUHU PRIOR TO COMMENCEMENT OF CONSTRUCTION.
2. ARCHITECTURAL DRAWINGS SHOULD BE READ IN CONJUNCTION WITH STRUCTURAL DETAILING AND FABRICATION GENERAL ASSEMBLY DRAWINGS.
3. FOR CONSTRUCTION PURPOSES, USE ONLY THE LATEST APPROVED DRAWINGS LABELED 'ISSUED FOR CONSTRUCTION'.
4. DO NOT SCALE FROM THIS DRAWING.
5. THE COMPANY OPERATES USING METRIC DIMENSIONS AS THE PRINCIPAL DENOMINATION.
6. ALL CONCRETE WORKS ARE OUTSIDE OF THE SCOPE OF THE COMPANY. INFORMATION REGARDING SLAB DESIGN AND CONNECTIONS IN THESE DRAWINGS ARE INTENDED FOR GUIDENCE ONLY. FOUNDATION AND SLAB WORKS SHOULD BE DESIGNED AND APPROVED BY A LOCAL STRUCTURAL ENGINEER.
7. THE COMPANY RETAINS FULL TITLE AND OWNERSHIP OF THESE PLANS AND DESIGNS. ANY UNAUTHORISED USE, REPRODUCTION, OR DISTRIBUTION OF THESE PLANS, WHETHER IN WHOLE OR PART, IS EXPRESSLY PROHIBITED WITHOUT PRIOR WRITTEN CONSENT.
8. THE HYBRID STEEL FRAME CONSTRUCTION SYSTEM AND METHODOLOGY DESCRIBED IN THESE PLANS HAS BEEN DEVELOPED BY THE COMPANY AND IS SUBJECT TO A PATENT APPLICATION & ASSIGNMENT - US APPLICATION No. 63/722,841.

No.	Revision	Date

ISSUED FOR:

- Issued for information
- Issued for client approval
- Issued for fabrication
- Issued for construction

Caribbean cottage

DRAWING TITLE:
Front Elevation

DRAWN BY:
Bernat Stefana

SCALE:
1 : 40


DRAWING NO:
A10

DATE:
18.11.2025



143 4745 4750 133
0' - 5 1/2" 15' - 7" 15' - 7" 0' - 5 1/2"

1 Front Elevation
1 : 40

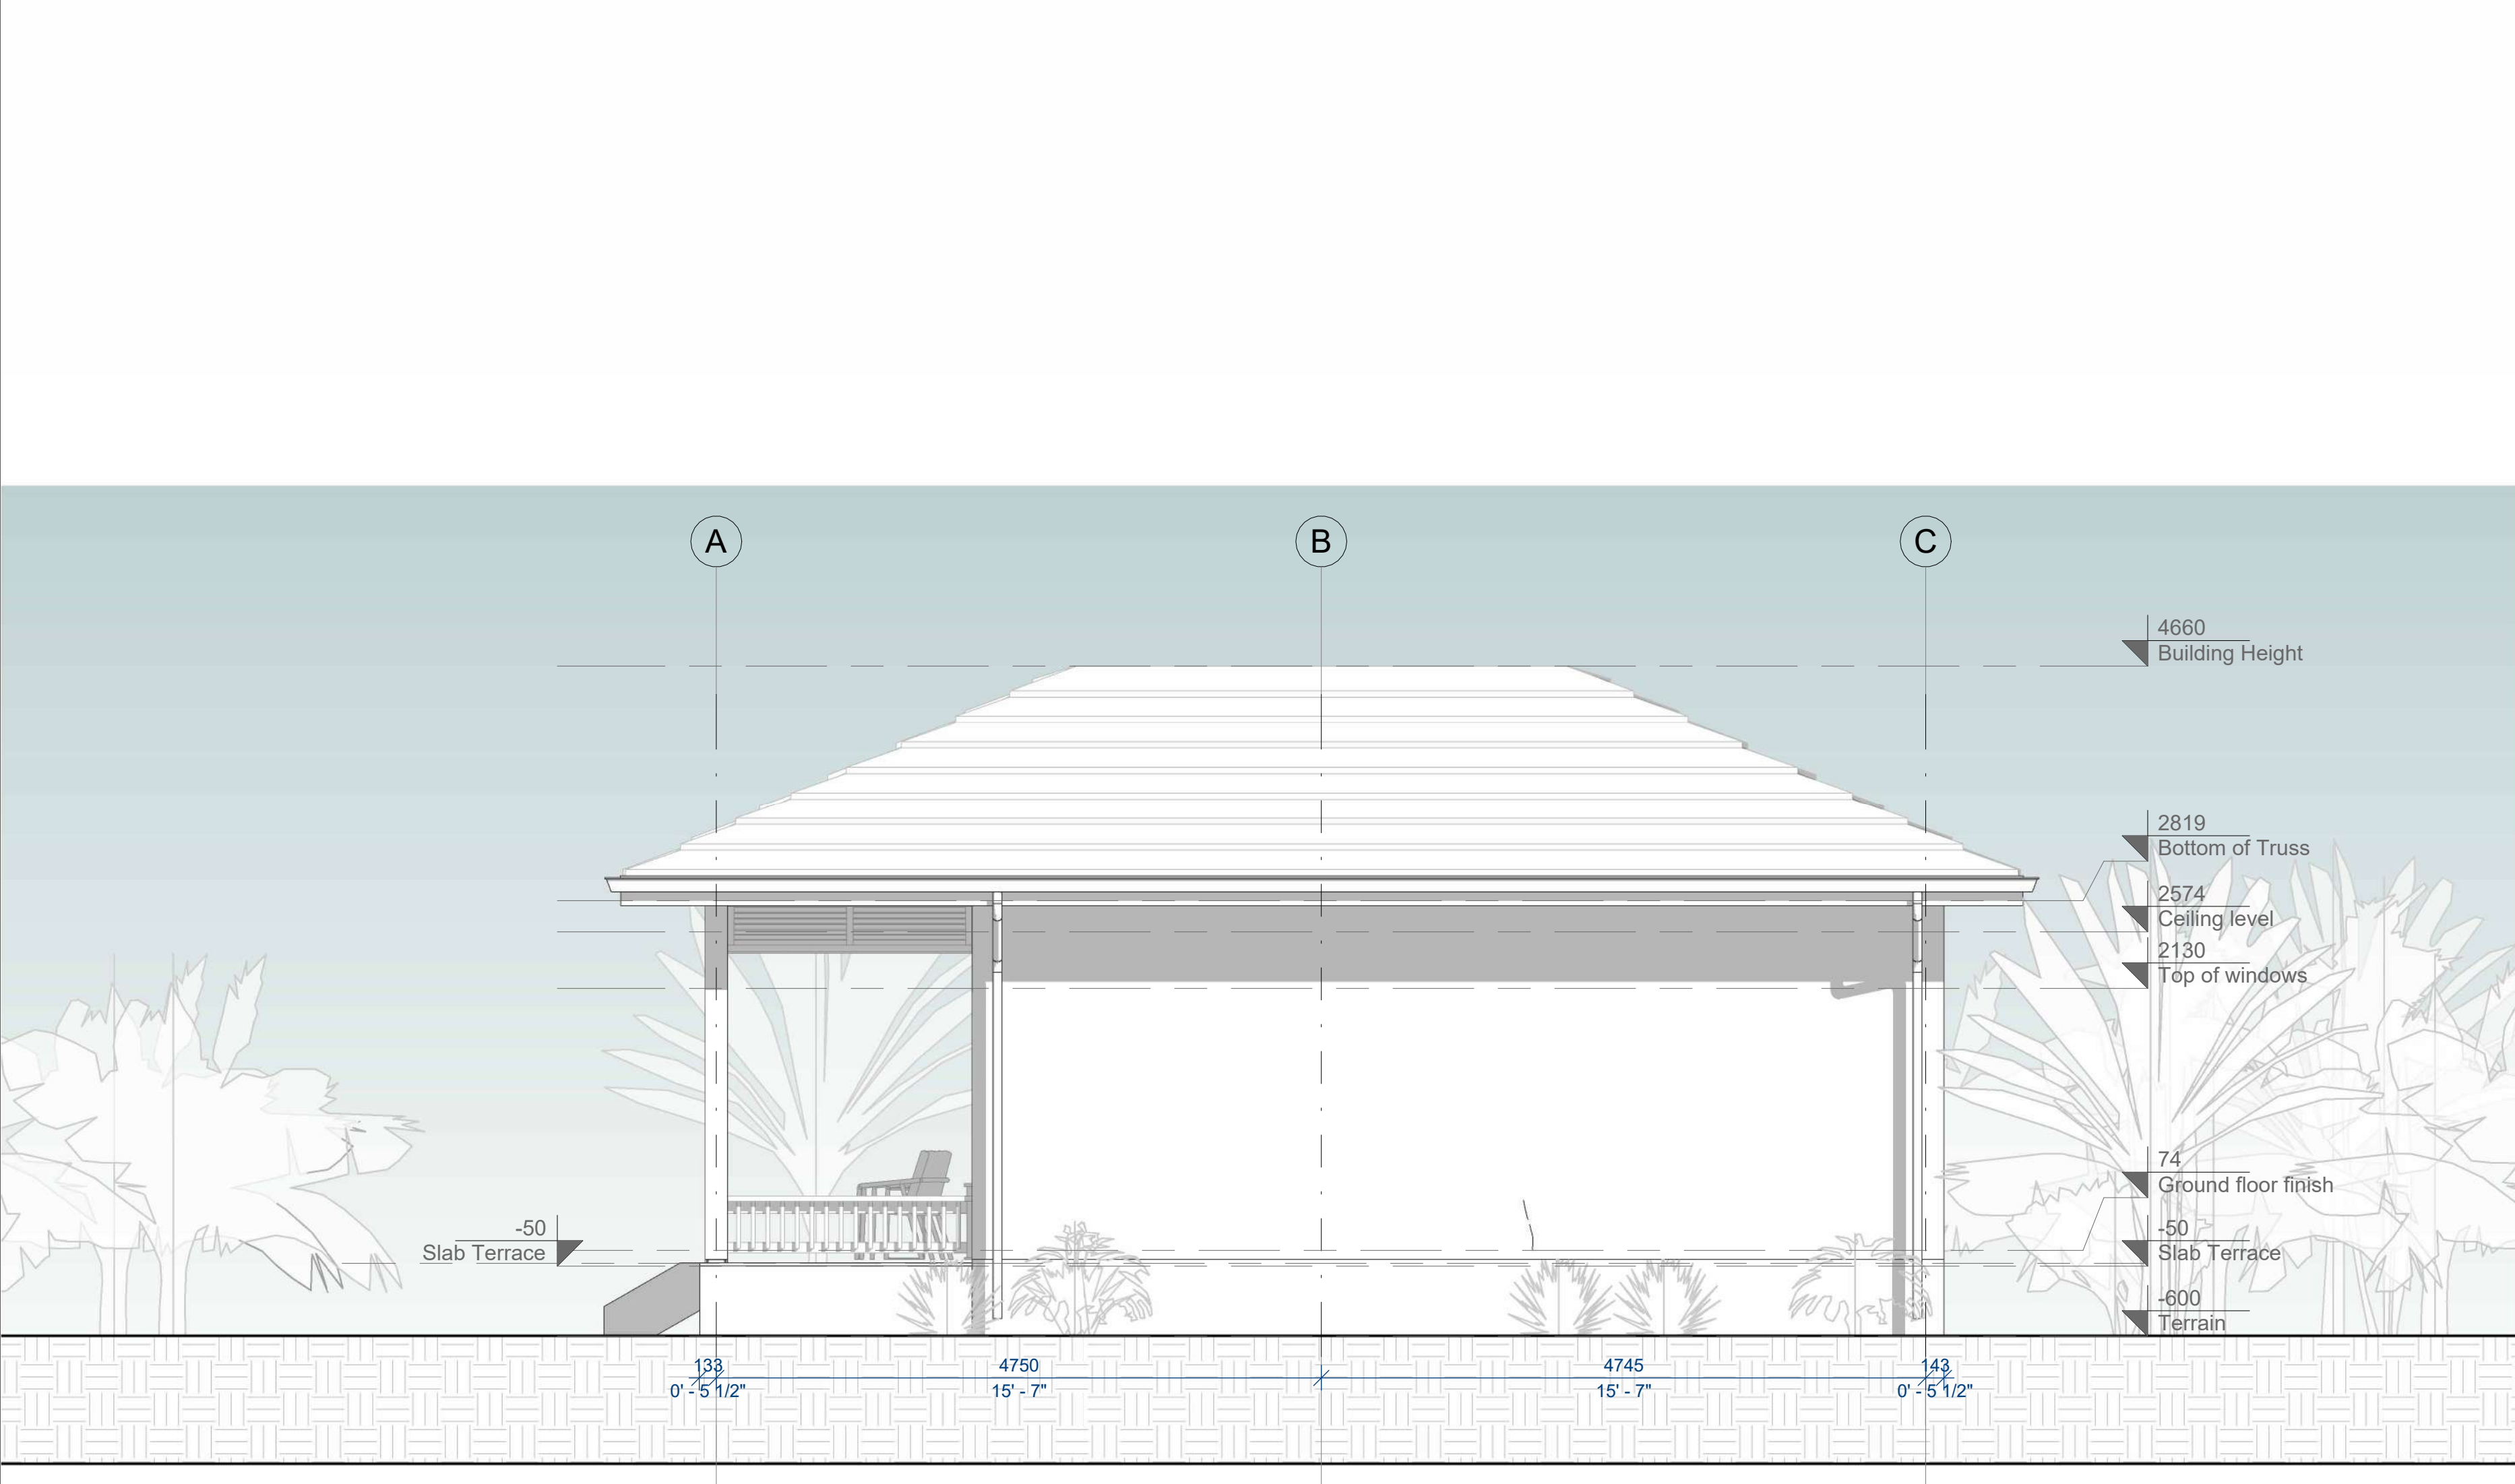

2 Rear Elevation
1 : 40

1. THESE DRAWINGS MUST BE CHECKED BY THE CUSTOMER OR CONTRACTOR PRIOR TO APPROVAL. ANY ERRORS OR OMISSIONS MUST BE REPORTED IN WRITING TO BAUHU PRIOR TO COMMENCEMENT OF CONSTRUCTION.
2. ARCHITECTURAL DRAWINGS SHOULD BE READ IN CONJUNCTION WITH STRUCTURAL DETAILING AND FABRICATION GENERAL ASSEMBLY DRAWINGS.
3. FOR CONSTRUCTION PURPOSES, USE ONLY THE LATEST APPROVED DRAWINGS LABELED 'ISSUED FOR CONSTRUCTION'.
4. DO NOT SCALE FROM THIS DRAWING.
5. THE COMPANY OPERATES USING METRIC DIMENSIONS AS THE PRINCIPAL DENOMINATION.
6. ALL CONCRETE WORKS ARE OUTSIDE OF THE SCOPE OF THE COMPANY. INFORMATION REGARDING SLAB DESIGN AND CONNECTIONS IN THESE DRAWINGS ARE INTENDED FOR GUIDENCE ONLY. FOUNDATION AND SLAB WORKS SHOULD BE DESIGNED AND APPROVED BY A LOCAL STRUCTURAL ENGINEER.
7. THE COMPANY RETAINS FULL TITLE AND OWNERSHIP OF THESE PLANS AND DESIGNS. ANY UNAUTHORISED USE, REPRODUCTION, OR DISTRIBUTION OF THESE PLANS, WHETHER IN WHOLE OR PART, IS EXPRESSLY PROHIBITED WITHOUT PRIOR WRITTEN CONSENT.
8. THE HYBRID STEEL FRAME CONSTRUCTION SYSTEM AND METHODOLOGY DESCRIBED IN THESE PLANS HAS BEEN DEVELOPED BY THE COMPANY AND IS SUBJECT TO A PATENT APPLICATION & ASSIGNMENT - US APPLICATION No. 63/722,841.

No.	Revision	Date

ISSUED FOR:

Issued for information

Issued for client approval

Issued for fabrication

Issued for construction

Caribbean cottage

DRAWING TITLE:	Rear Elevation
DRAWN BY:	Bernat Stefana
SCALE:	1 : 40
DRAWING NO:	A11
DATE:	18.11.2025

1. THESE DRAWINGS MUST BE CHECKED BY THE CUSTOMER OR CONTRACTOR PRIOR TO APPROVAL. ANY ERRORS OR OMISSIONS MUST BE REPORTED IN WRITING TO BAUHU PRIOR TO COMMENCEMENT OF CONSTRUCTION.
2. ARCHITECTURAL DRAWINGS SHOULD BE READ IN CONJUNCTION WITH STRUCTURAL DETAILING AND FABRICATION GENERAL ASSEMBLY DRAWINGS.
3. FOR CONSTRUCTION PURPOSES, USE ONLY THE LATEST APPROVED DRAWINGS LABELED 'ISSUED FOR CONSTRUCTION'.
4. DO NOT SCALE FROM THIS DRAWING.
5. THE COMPANY OPERATES USING METRIC DIMENSIONS AS THE PRINCIPAL DENOMINATION.
6. ALL CONCRETE WORKS ARE OUTSIDE OF THE SCOPE OF THE COMPANY. INFORMATION REGARDING SLAB DESIGN AND CONNECTIONS IN THESE DRAWINGS ARE INTENDED FOR GUIDENCE ONLY. FOUNDATION AND SLAB WORKS SHOULD BE DESIGNED AND APPROVED BY A LOCAL STRUCTURAL ENGINEER.
7. THE COMPANY RETAINS FULL TITLE AND OWNERSHIP OF THESE PLANS AND DESIGNS. ANY UNAUTHORISED USE, REPRODUCTION, OR DISTRIBUTION OF THESE PLANS, WHETHER IN WHOLE OR PART, IS EXPRESSLY PROHIBITED WITHOUT PRIOR WRITTEN CONSENT.
8. THE HYBRID STEEL FRAME CONSTRUCTION SYSTEM AND METHODOLOGY DESCRIBED IN THESE PLANS HAS BEEN DEVELOPED BY THE COMPANY AND IS SUBJECT TO A PATENT APPLICATION & ASSIGNMENT - US APPLICATION No. 63/722,841.

No.	Revision	Date

ISSUED FOR:

- Issued for information
- Issued for client approval
- Issued for fabrication
- Issued for construction

Caribbean cottage


DRAWING TITLE:
Left Elevation

DRAWN BY:
Bernat Stefana

SCALE:
1 : 40

DRAWING NO:
A12

DATE:
18.11.2025

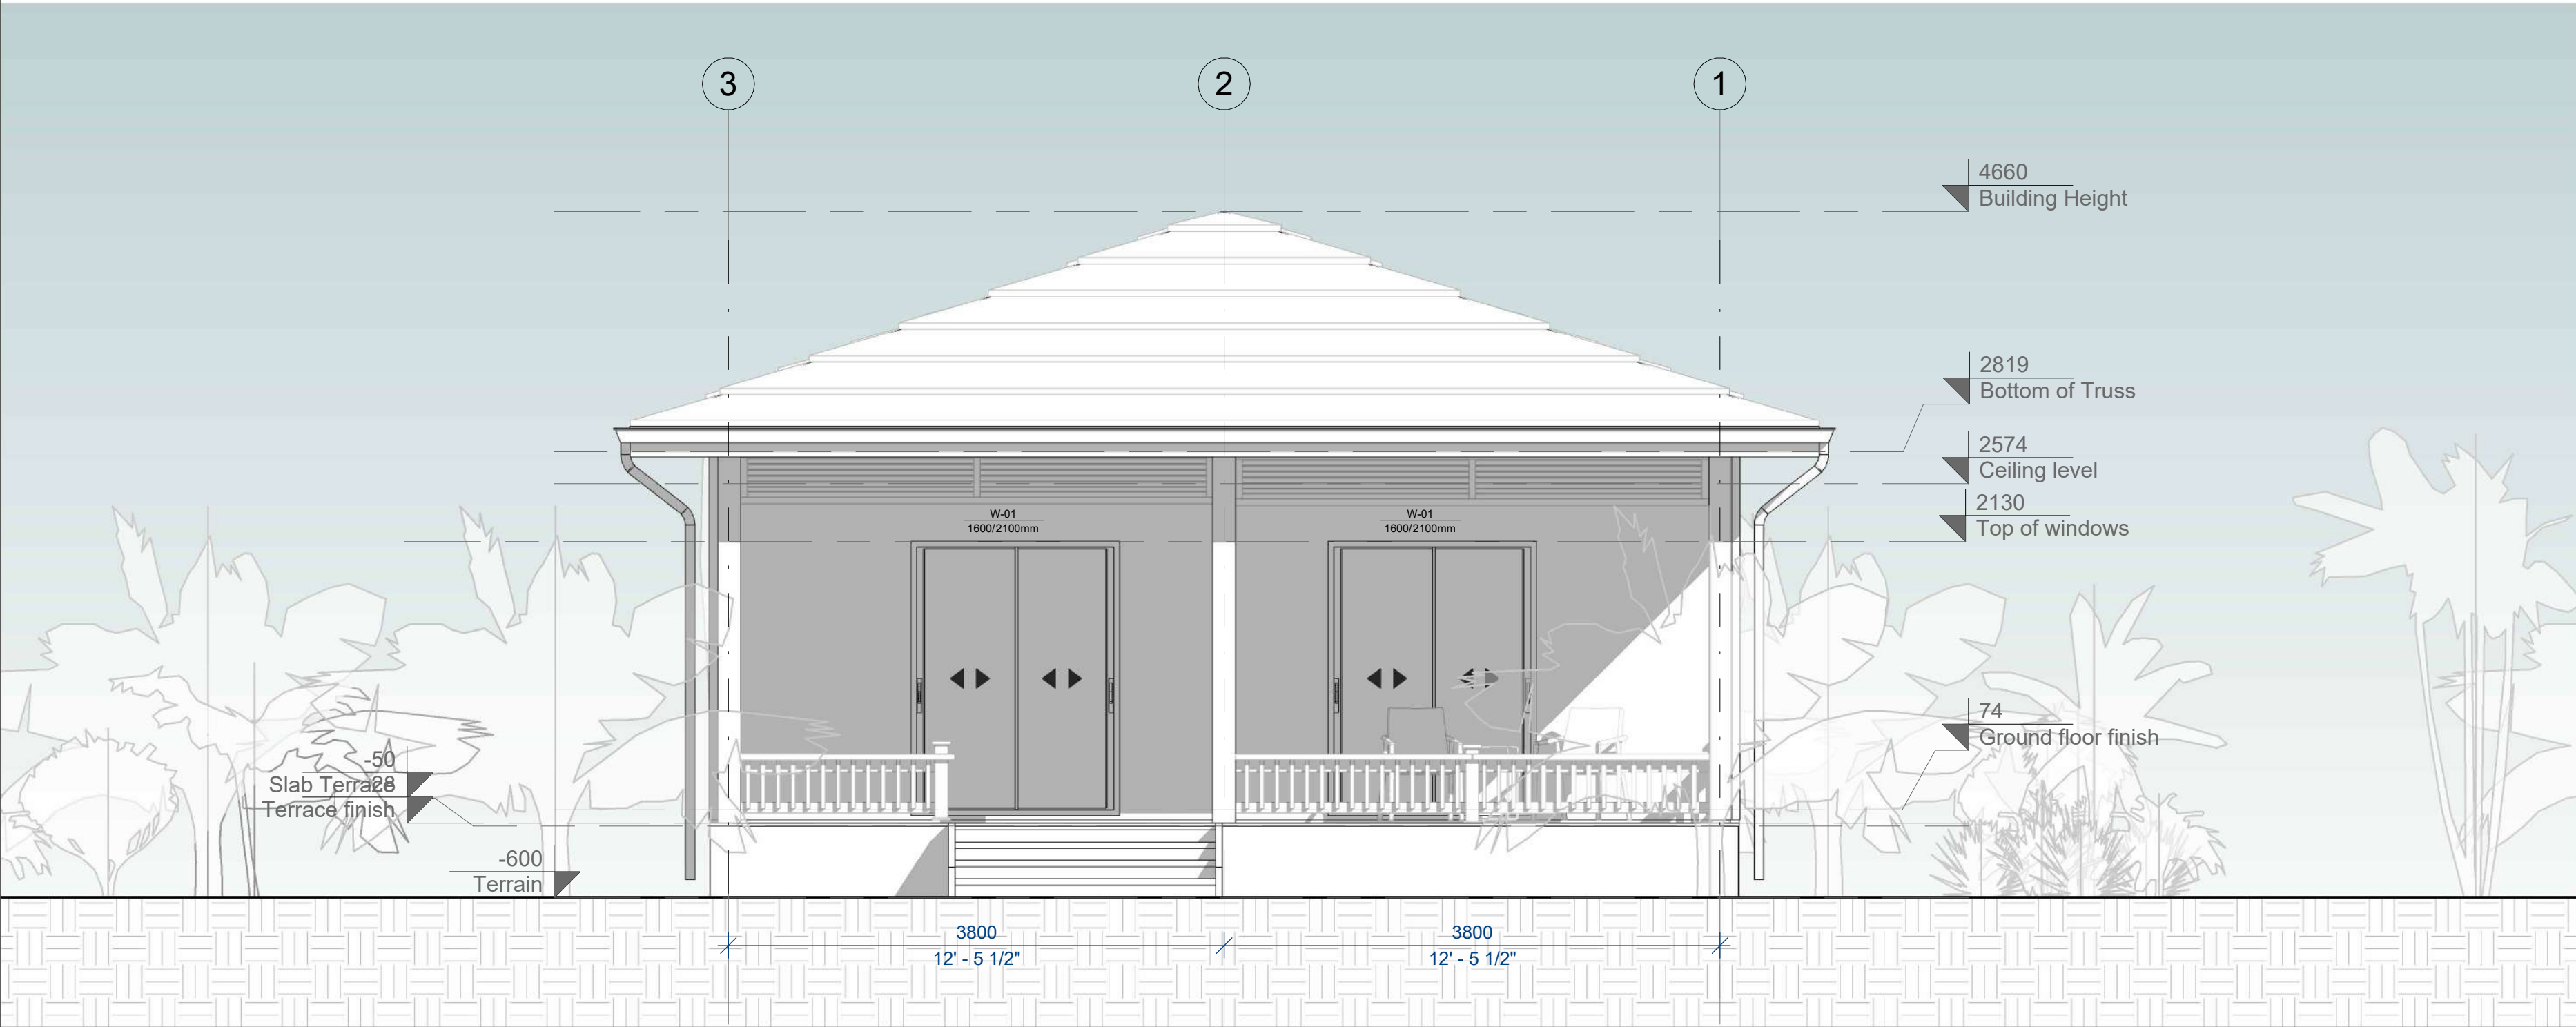

3 Left Elevation
1 : 40

1. THESE DRAWINGS MUST BE CHECKED BY THE CUSTOMER OR CONTRACTOR PRIOR TO APPROVAL. ANY ERRORS OR OMISSIONS MUST BE REPORTED IN WRITING TO BAUHU PRIOR TO COMMENCEMENT OF CONSTRUCTION.
2. ARCHITECTURAL DRAWINGS SHOULD BE READ IN CONJUNCTION WITH STRUCTURAL DETAILING AND FABRICATION GENERAL ASSEMBLY DRAWINGS.
3. FOR CONSTRUCTION PURPOSES, USE ONLY THE LATEST APPROVED DRAWINGS LABELED 'ISSUED FOR CONSTRUCTION'.
4. DO NOT SCALE FROM THIS DRAWING.
5. THE COMPANY OPERATES USING METRIC DIMENSIONS AS THE PRINCIPAL DENOMINATION.
6. ALL CONCRETE WORKS ARE OUTSIDE OF THE SCOPE OF THE COMPANY. INFORMATION REGARDING SLAB DESIGN AND CONNECTIONS IN THESE DRAWINGS ARE INTENDED FOR GUIDENCE ONLY. FOUNDATION AND SLAB WORKS SHOULD BE DESIGNED AND APPROVED BY A LOCAL STRUCTURAL ENGINEER.
7. THE COMPANY RETAINS FULL TITLE AND OWNERSHIP OF THESE PLANS AND DESIGNS. ANY UNAUTHORISED USE, REPRODUCTION, OR DISTRIBUTION OF THESE PLANS, WHETHER IN WHOLE OR PART, IS EXPRESSLY PROHIBITED WITHOUT PRIOR WRITTEN CONSENT.
8. THE HYBRID STEEL FRAME CONSTRUCTION SYSTEM AND METHODOLOGY DESCRIBED IN THESE PLANS HAS BEEN DEVELOPED BY THE COMPANY AND IS SUBJECT TO A PATENT APPLICATION & ASSIGNMENT - US APPLICATION No. 63/722,841.

No.	Revision	Date

ISSUED FOR:

Issued for information

Issued for client approval

Issued for fabrication

Issued for construction

Caribbean cottage


DRAWING TITLE:
Right Elevation

DRAWN BY:
Bernat Stefana

SCALE:
1 : 40

DRAWING NO:
A13

DATE:
18.11.2025

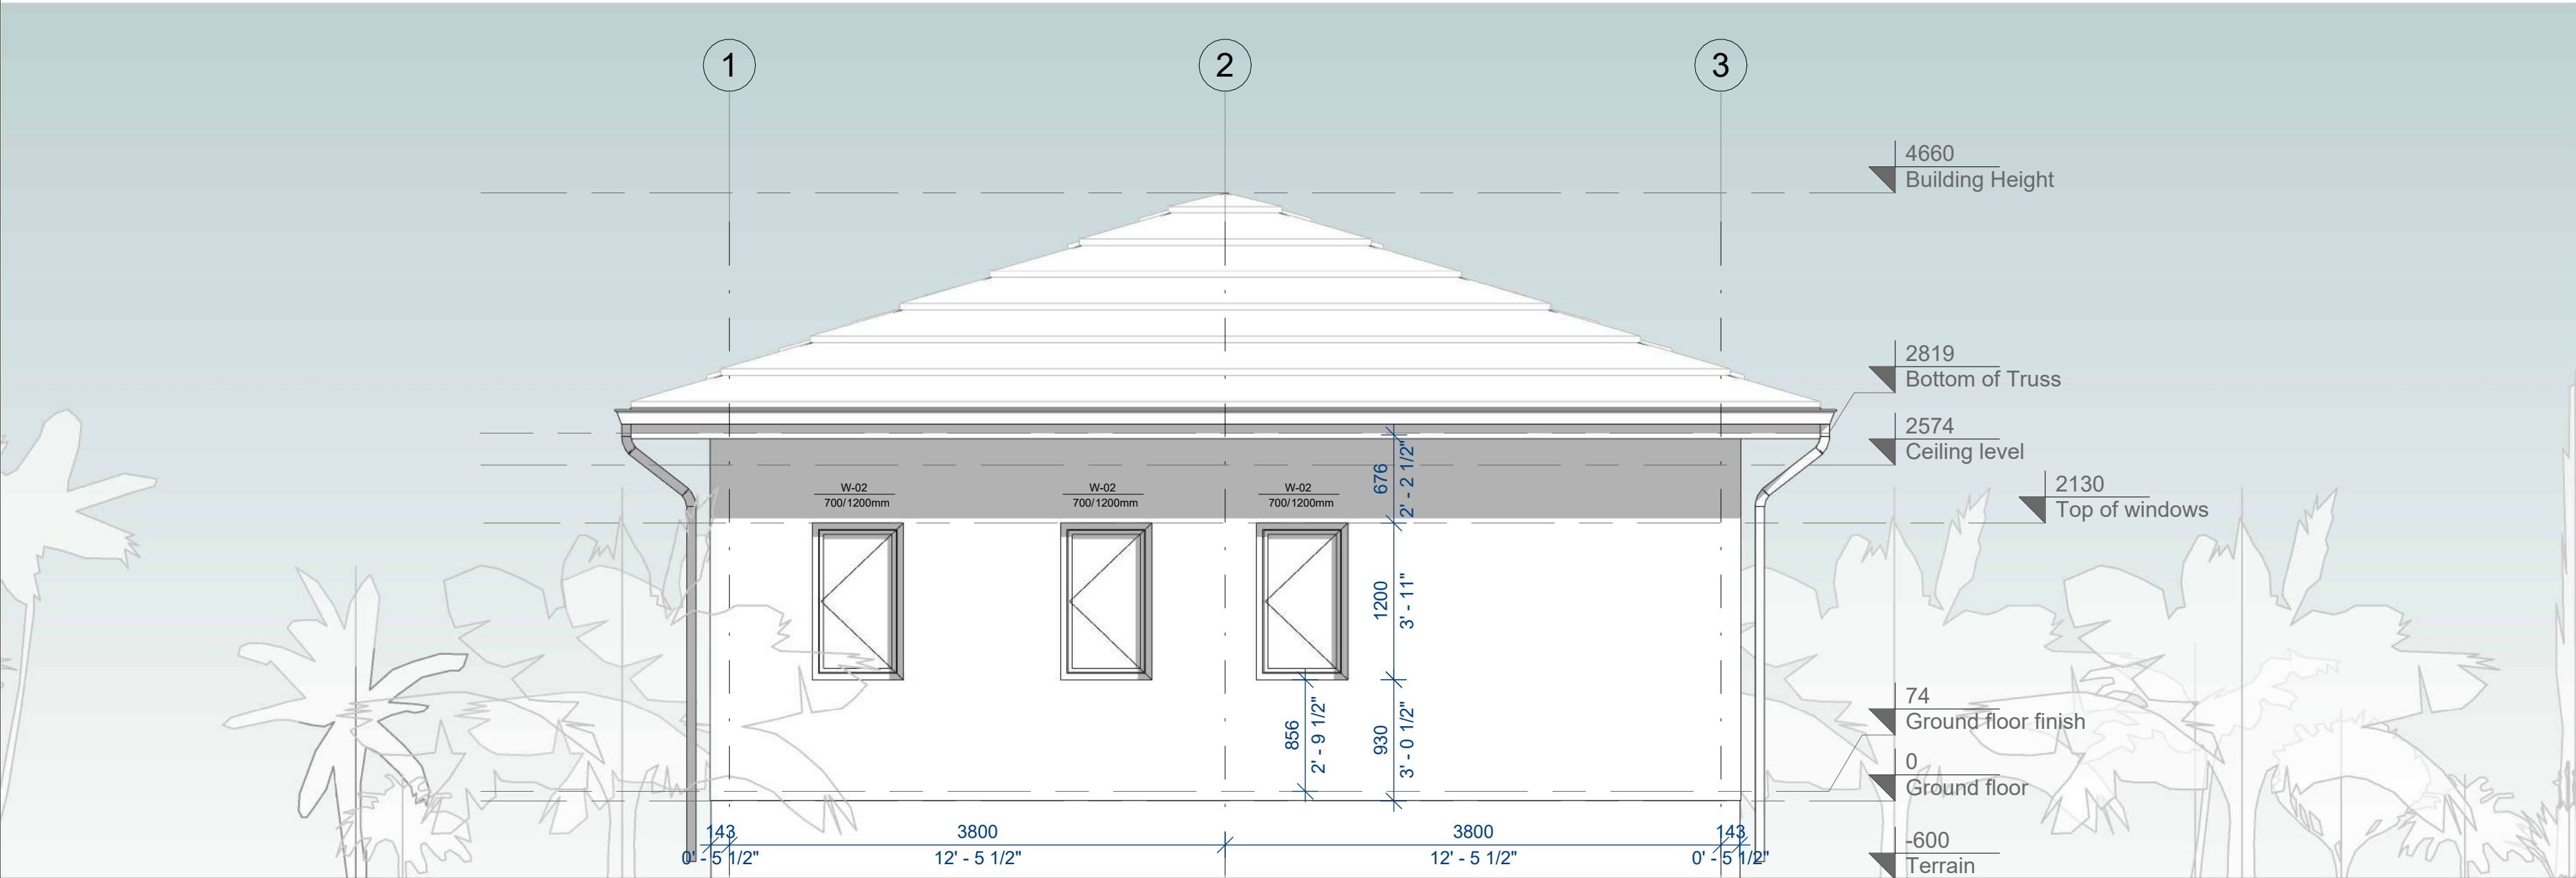

4 Right Elevation
1 : 40

1. THESE DRAWINGS MUST BE CHECKED BY THE CUSTOMER OR CONTRACTOR PRIOR TO APPROVAL. ANY ERRORS OR OMISSIONS MUST BE REPORTED IN WRITING TO BAUHU PRIOR TO COMMENCEMENT OF CONSTRUCTION.
2. ARCHITECTURAL DRAWINGS SHOULD BE READ IN CONJUNCTION WITH STRUCTURAL DETAILING AND FABRICATION GENERAL ASSEMBLY DRAWINGS.
3. FOR CONSTRUCTION PURPOSES, USE ONLY THE LATEST APPROVED DRAWINGS LABELED 'ISSUED FOR CONSTRUCTION'.
4. DO NOT SCALE FROM THIS DRAWING.
5. THE COMPANY OPERATES USING METRIC DIMENSIONS AS THE PRINCIPAL DENOMINATION.
6. ALL CONCRETE WORKS ARE OUTSIDE OF THE SCOPE OF THE COMPANY. INFORMATION REGARDING SLAB DESIGN AND CONNECTIONS IN THESE DRAWINGS ARE INTENDED FOR GUIDENCE ONLY. FOUNDATION AND SLAB WORKS SHOULD BE DESIGNED AND APPROVED BY A LOCAL STRUCTURAL ENGINEER.
7. THE COMPANY RETAINS FULL TITLE AND OWNERSHIP OF THESE PLANS AND DESIGNS. ANY UNAUTHORISED USE, REPRODUCTION, OR DISTRIBUTION OF THESE PLANS, WHETHER IN WHOLE OR PART, IS EXPRESSLY PROHIBITED WITHOUT PRIOR WRITTEN CONSENT.
8. THE HYBRID STEEL FRAME CONSTRUCTION SYSTEM AND METHODOLOGY DESCRIBED IN THESE PLANS HAS BEEN DEVELOPED BY THE COMPANY AND IS SUBJECT TO A PATENT APPLICATION & ASSIGNMENT - US APPLICATION No. 63/722,841.

No.	Revision	Date

ISSUED FOR:

Issued for information

Issued for client approval

Issued for fabrication

Issued for construction

Caribbean cottage

DRAWING TITLE:

Section 1

DRAWN BY:

Bernat Stefana

SCALE:


1 : 40

DRAWING NO:

A14

DATE:

18.11.2025

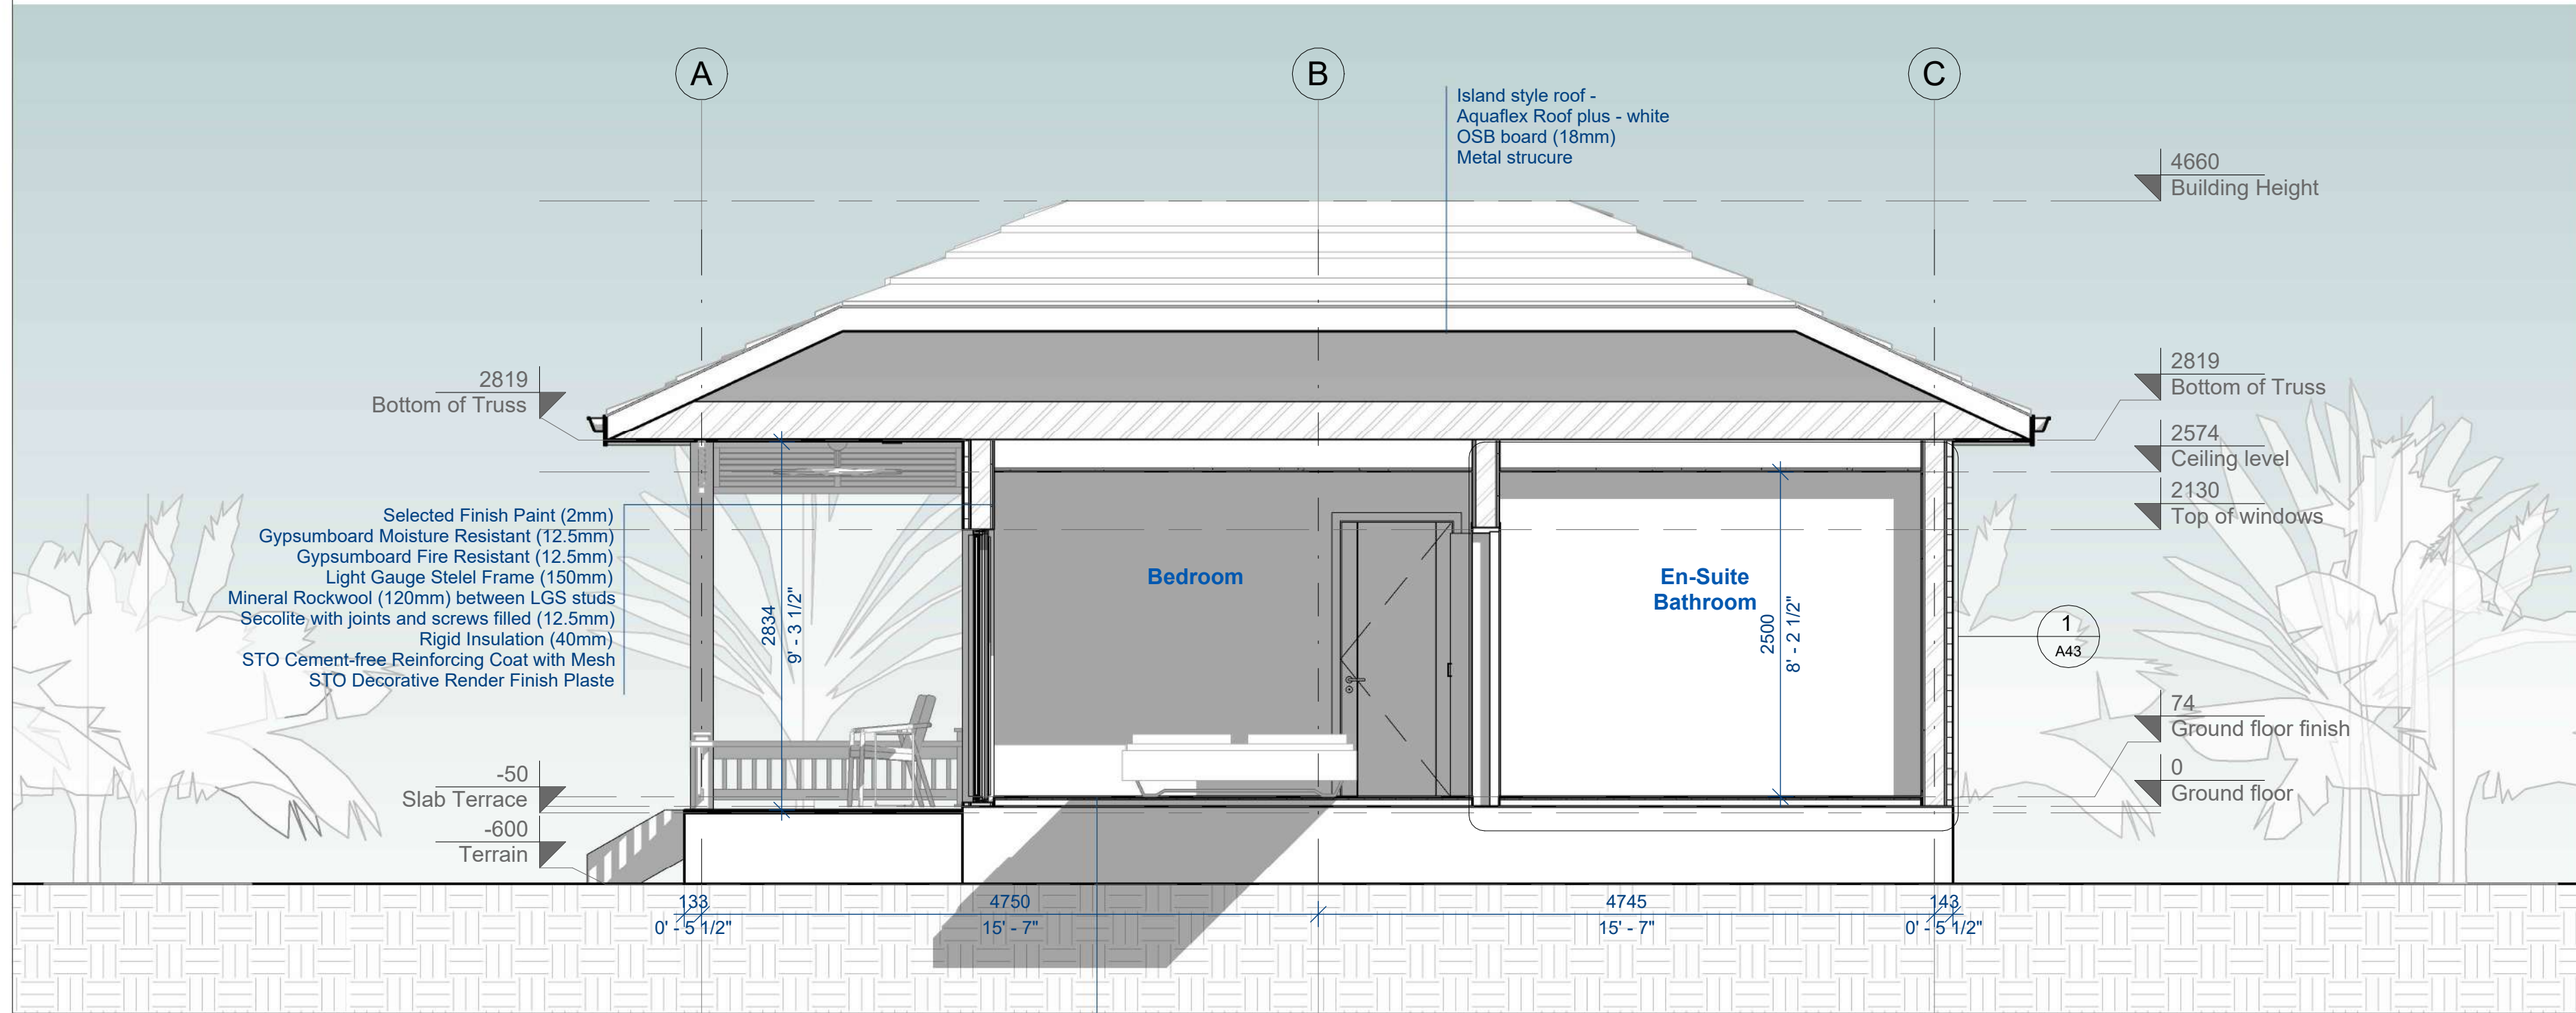

1

Section 1

1 : 40

Floor finish (tiles) 12mm
Adhesive 10mm
Tile bracker board 12.5mm (optional) by others
Insulation panels 40mm (optional) by others
Waterproofing membrane - by others
Floor leveling screed +/-24 mm according to site conditions
by others (mixed with waterproofing additive)
Concrete slab - by others

1. THESE DRAWINGS MUST BE CHECKED BY THE CUSTOMER OR CONTRACTOR PRIOR TO APPROVAL. ANY ERRORS OR OMISSIONS MUST BE REPORTED IN WRITING TO BAUHU PRIOR TO COMMENCEMENT OF CONSTRUCTION.
2. ARCHITECTURAL DRAWINGS SHOULD BE READ IN CONJUNCTION WITH STRUCTURAL DETAILING AND FABRICATION GENERAL ASSEMBLY DRAWINGS.
3. FOR CONSTRUCTION PURPOSES, USE ONLY THE LATEST APPROVED DRAWINGS LABELED 'ISSUED FOR CONSTRUCTION'.
4. DO NOT SCALE FROM THIS DRAWING.
5. THE COMPANY OPERATES USING METRIC DIMENSIONS AS THE PRINCIPAL DENOMINATION.
6. ALL CONCRETE WORKS ARE OUTSIDE OF THE SCOPE OF THE COMPANY. INFORMATION REGARDING SLAB DESIGN AND CONNECTIONS IN THESE DRAWINGS ARE INTENDED FOR GUIDENCE ONLY. FOUNDATION AND SLAB WORKS SHOULD BE DESIGNED AND APPROVED BY A LOCAL STRUCTURAL ENGINEER.
7. THE COMPANY RETAINS FULL TITLE AND OWNERSHIP OF THESE PLANS AND DESIGNS. ANY UNAUTHORISED USE, REPRODUCTION, OR DISTRIBUTION OF THESE PLANS, WHETHER IN WHOLE OR PART, IS EXPRESSLY PROHIBITED WITHOUT PRIOR WRITTEN CONSENT.
8. THE HYBRID STEEL FRAME CONSTRUCTION SYSTEM AND METHODOLOGY DESCRIBED IN THESE PLANS HAS BEEN DEVELOPED BY THE COMPANY AND IS SUBJECT TO A PATENT APPLICATION & ASSIGNMENT - US APPLICATION No. 63/722,841.

No.	Revision	Date

ISSUED FOR:

Issued for information


Issued for client approval

Issued for fabrication

Issued for construction

Caribbean cottage

DRAWING TITLE:	Section 2
DRAWN BY:	Bernat Stefana
SCALE:	1 : 40
DRAWING NO:	A15
DATE:	18.11.2025

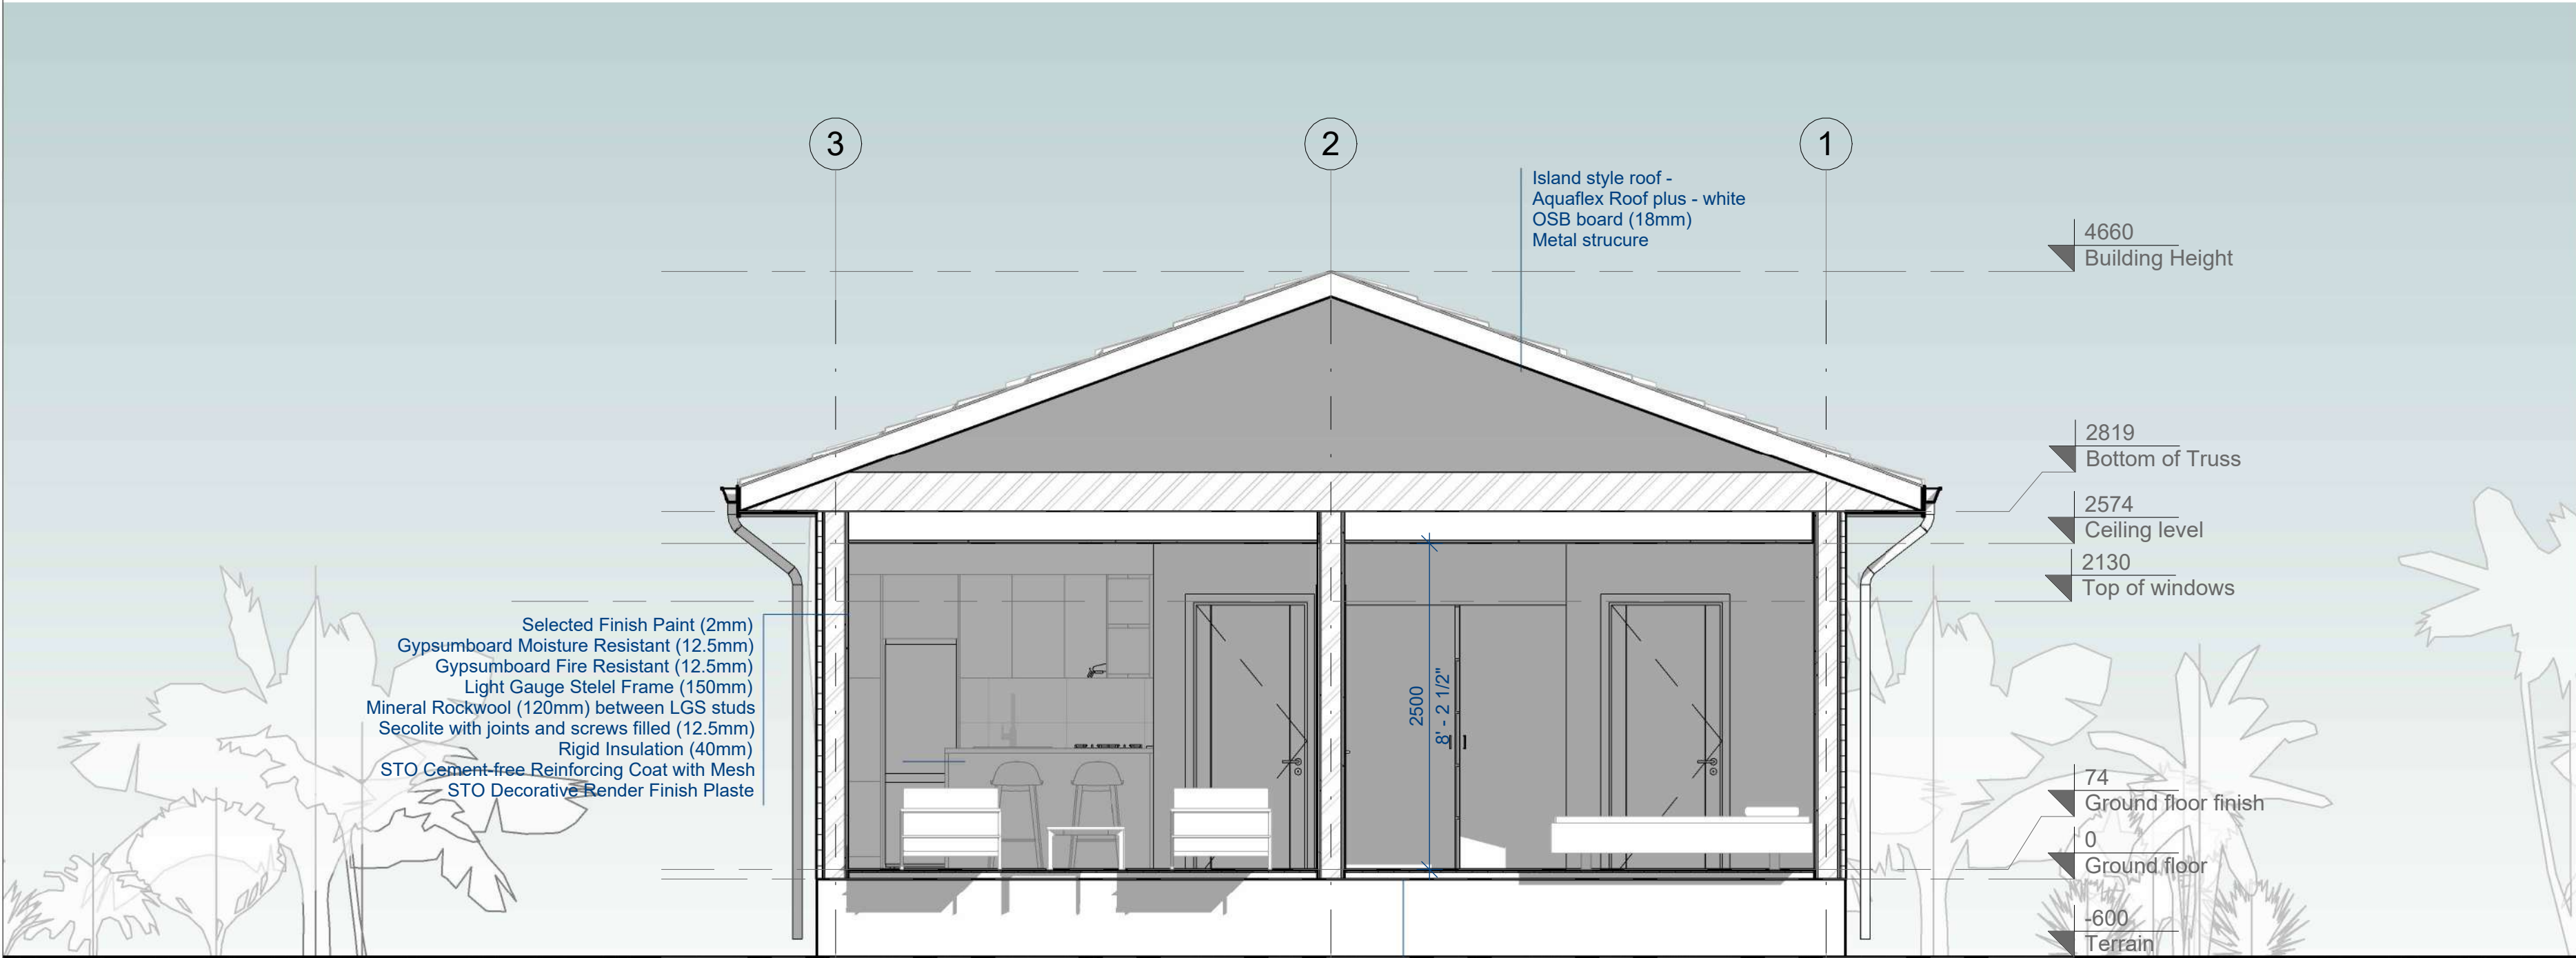


Floor finish (tiles) 12mm
Adhesive 10mm
Tile bracker board 12.5mm (optional) by others
Insulation panels 40mm (optional) by others
Waterproofing membrane - by others
Floor leveling screed +/-24 mm according to site conditions
by others (mixed with waterproofing additive)
Concrete slab - by others


Door Schedule											
No	Type	Size		RO Size		Count	Opening Direction	Finishing	No of Leaves	Hinge Side	Lock
		Width	Height	RO Width	RO. Height						
D - 01	Interior Door 850 X 2100mm	850 mm	2100 mm	950	2145	3	3L	matt white	1	3L	Yes
Grand total						3					

Window Schedule													
No	Type	Size		RO Size		Count	Opening Direction	Interior pane	Frame Finish	No of Leaves	Hinge Side	Lock	Insect screen
		Width	Height	RO. Width	RO. Height								
W-01	CORVISION Slider	1600 mm	2100	1634	2147	2	X	2R	Anthracite grey RAL 7016 matt	2	X	Yes	No
W-02	COR 70 - Casement - one sash	700 mm	1200	734	1234	5	5L	X	Anthracite grey RAL 7016 matt	1	5L	Yes	No
Grand total						7							

Interior Doors

Compincar
Colour: Matt White Lac.
Model: Lisa

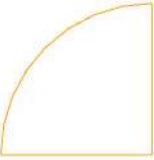- 

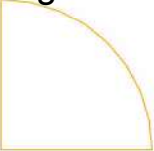R: Right hinge
- 

L: Left hinge
- 
- LISA



Model: 1003

Window/Door Frames



Colour: Anthracite grey matt
RAL 7016

Glass

<https://www.guardianglass.com/gb/en/our-glass/glass-types/solar-control-glass>

- 44.2+16argon we+6 SNX

- Note:**
- *Openings are provided without insect screens as standard. Insect screens can be provided at additional cost.
 - *Shutters are excluded. If required these will be provided by others-acquired locally according to dimensions of finished openings after finish application. Drawings are made for design purposesonly.
 - Garage type doors are excluded and should be sourced by the owner.
 - All opening windows open outwards.
 - All opening drawings are viewed from the outside



- THESE DRAWINGS MUST BE CHECKED BY THE CUSTOMER OR CONTRACTOR PRIOR TO APPROVAL. ANY ERRORS OR OMISSIONS MUST BE REPORTED IN WRITING TO BAUHU PRIOR TO COMMENCEMENT OF CONSTRUCTION.
- ARCHITECTURAL DRAWINGS SHOULD BE READ IN CONJUNCTION WITH STRUCTURAL DETAILING AND FABRICATION GENERAL ASSEMBLY DRAWINGS.
- FOR CONSTRUCTION PURPOSES, USE ONLY THE LATEST APPROVED DRAWINGS LABELED 'ISSUED FOR CONSTRUCTION'.
- DO NOT SCALE FROM THIS DRAWING.
- THE COMPANY OPERATES USING METRIC DIMENSIONS AS THE PRINCIPAL DENOMINATION.
- ALL CONCRETE WORKS ARE OUTSIDE OF THE SCOPE OF THE COMPANY. INFORMATION REGARDING SLAB DESIGN AND CONNECTIONS IN THESE DRAWINGS ARE INTENDED FOR GUIDENCE ONLY. FOUNDATION AND SLAB WORKS SHOULD BE DESIGNED AND APPROVED BY A LOCAL STRUCTURAL ENGINEER.
- THE COMPANY RETAINS FULL TITLE AND OWNERSHIP OF THESE PLANS AND DESIGNS. ANY UNAUTHORISED USE, REPRODUCTION, OR DISTRIBUTION OF THESE PLANS, WHETHER IN WHOLE OR PART, IS EXPRESSLY PROHIBITED WITHOUT PRIOR WRITTEN CONSENT.
- THE HYBRID STEEL FRAME CONSTRUCTION SYSTEM AND METHODOLOGY DESCRIBED IN THESE PLANS HAS BEEN DEVELOPED BY THE COMPANY AND IS SUBJECT TO A PATENT APPLICATION & ASSIGNMENT
US APPLICATION NO. 63/722,841

No.	Revision	Date

ISSUED FOR:

Issued for information

Issued for client approval

Issued for fabrication

Issued for construction

Caribbean cottage

DRAWING TITLE:

Openings Schedule

DRAWN BY:

Bernat Stefana

SCALE:

DRAWING NO:

A24

DATE:

18.11.2025

- THESE DRAWINGS MUST BE CHECKED BY THE CUSTOMER OR CONTRACTOR PRIOR TO APPROVAL. ANY ERRORS OR OMISSIONS MUST BE REPORTED IN WRITING TO BAUHU PRIOR TO COMMENCEMENT OF CONSTRUCTION.
- ARCHITECTURAL DRAWINGS SHOULD BE READ IN CONJUNCTION WITH STRUCTURAL DETAILING AND FABRICATION GENERAL ASSEMBLY DRAWINGS.
- FOR CONSTRUCTION PURPOSES, USE ONLY THE LATEST APPROVED DRAWINGS LABELED 'ISSUED FOR CONSTRUCTION'.
- DO NOT SCALE FROM THIS DRAWING.
- THE COMPANY OPERATES USING METRIC DIMENSIONS AS THE PRINCIPAL DENOMINATION.
- ALL CONCRETE WORKS ARE OUTSIDE OF THE SCOPE OF THE COMPANY. INFORMATION REGARDING SLAB DESIGN AND CONNECTIONS IN THESE DRAWINGS ARE INTENDED FOR GUIDENCE ONLY. FOUNDATION AND SLAB WORKS SHOULD BE DESIGNED AND APPROVED BY A LOCAL STRUCTURAL ENGINEER.
- THE COMPANY RETAINS FULL TITLE AND OWNERSHIP OF THESE PLANS AND DESIGNS. ANY UNAUTHORISED USE, REPRODUCTION, OR DISTRIBUTION OF THESE PLANS, WHETHER IN WHOLE OR PART, IS EXPRESSLY PROHIBITED WITHOUT PRIOR WRITTEN CONSENT.
- THE HYBRID STEEL FRAME CONSTRUCTION SYSTEM AND METHODOLOGY DESCRIBED IN THESE PLANS HAS BEEN DEVELOPED BY THE COMPANY AND IS SUBJECT TO A PATENT APPLICATION & ASSIGNMENT - US APPLICATION No. 63/722,841.

No.	Revision	Date

ISSUED FOR:

Issued for information

Issued for client approval

Issued for fabrication

Issued for construction

Caribbean cottage


DRAWING TITLE:
Doors / Window Openings

DRAWN BY:
Bernat Stefana

SCALE:
1 : 20

DRAWING NO:
A25

DATE:
18.11.2025

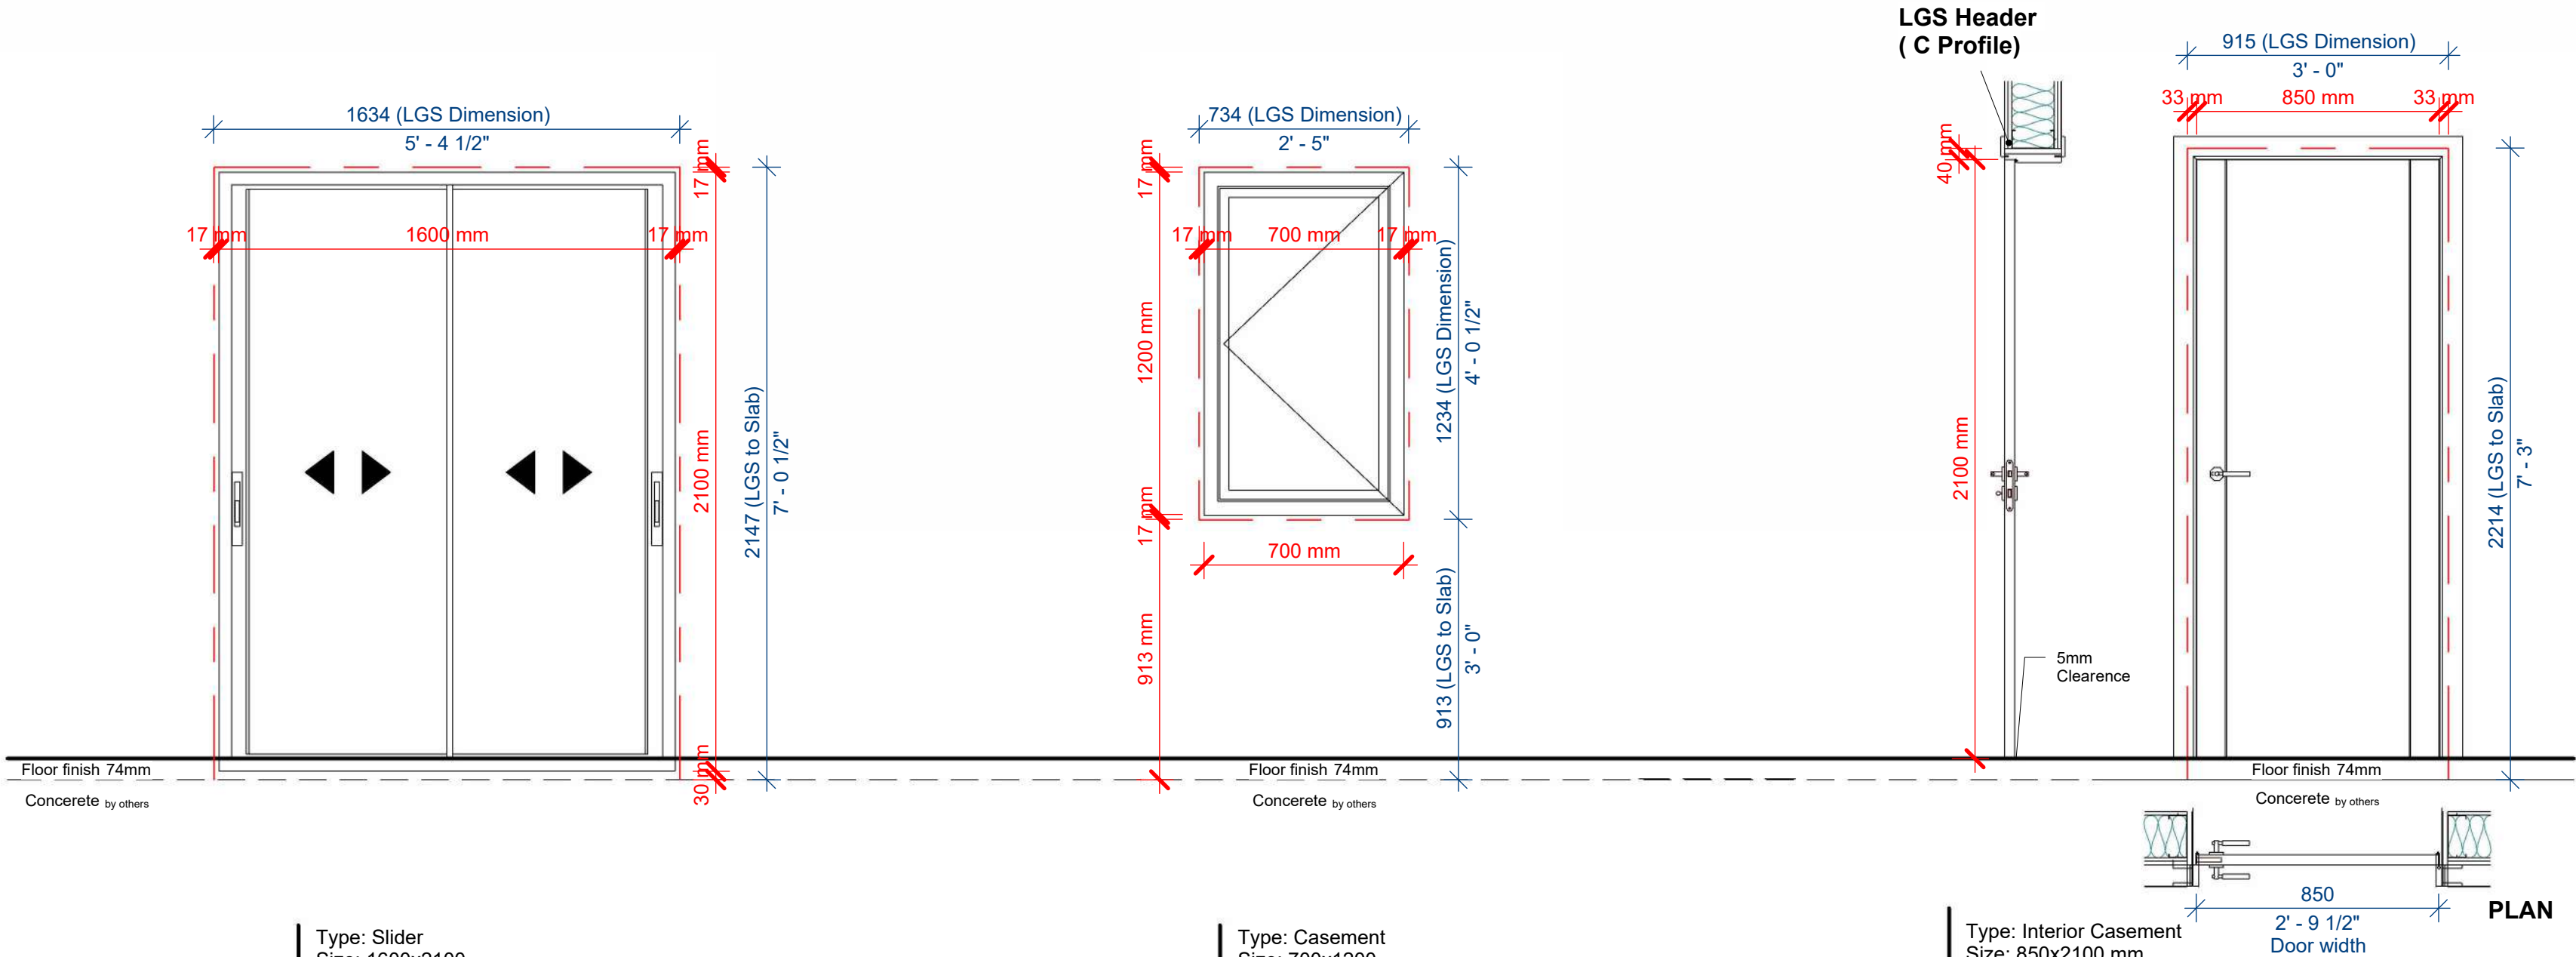

Note:

- *Openings are provided without insect screens as standard. Insect screens can be provided at additional cost.
- *Shutters are excluded. If required these will be provided by others-acquired locally according to dimensions of finished openings after finish application. Drawings are made for design purposesonly.
- Garage type doors are excluded and should be sourced by the owner.
- All opening windows open outwards.
- All opening drawings are viewed from the outside

Wall Details

Exterior Wall

Interior side

- Selected Finish Paint (2mm)
- Gypsumboard Moisture Resistant (12.5mm)
- Gypsumboard Fire Resistant (12.5mm)
- Light Gauge Stelel Frame (150mm)
- Mineral Rockwool (120mm) between LGS studs
- Secolite with joints and screws filled (12.5mm)
- Rigid Insulation 40mm
- STO Cement-free Reinforcing Coat with Mesh
- STO Decorative Render Finish Plaster


Exterior side

Interior Wall


Interior side

- Selected Paint Finish
 - Gypsum Wall Board - Moisture resistant (12.5mm)
 - Gypsum Wall Board - Fire resistant (12.5mm)
 - Light Gauge Steel Frame (150mm)
 - Mineral Rockwool (120mm) between LGS studs
 - Gypsum Wall Board - Fire resistant (12.5mm)
 - Gypsum Wall Board - Moisture resistant (12.5mm)
 - Selected Paint Finish
- Interior side


D8.Exterior - Interior Wall Connection Sc: 1/6

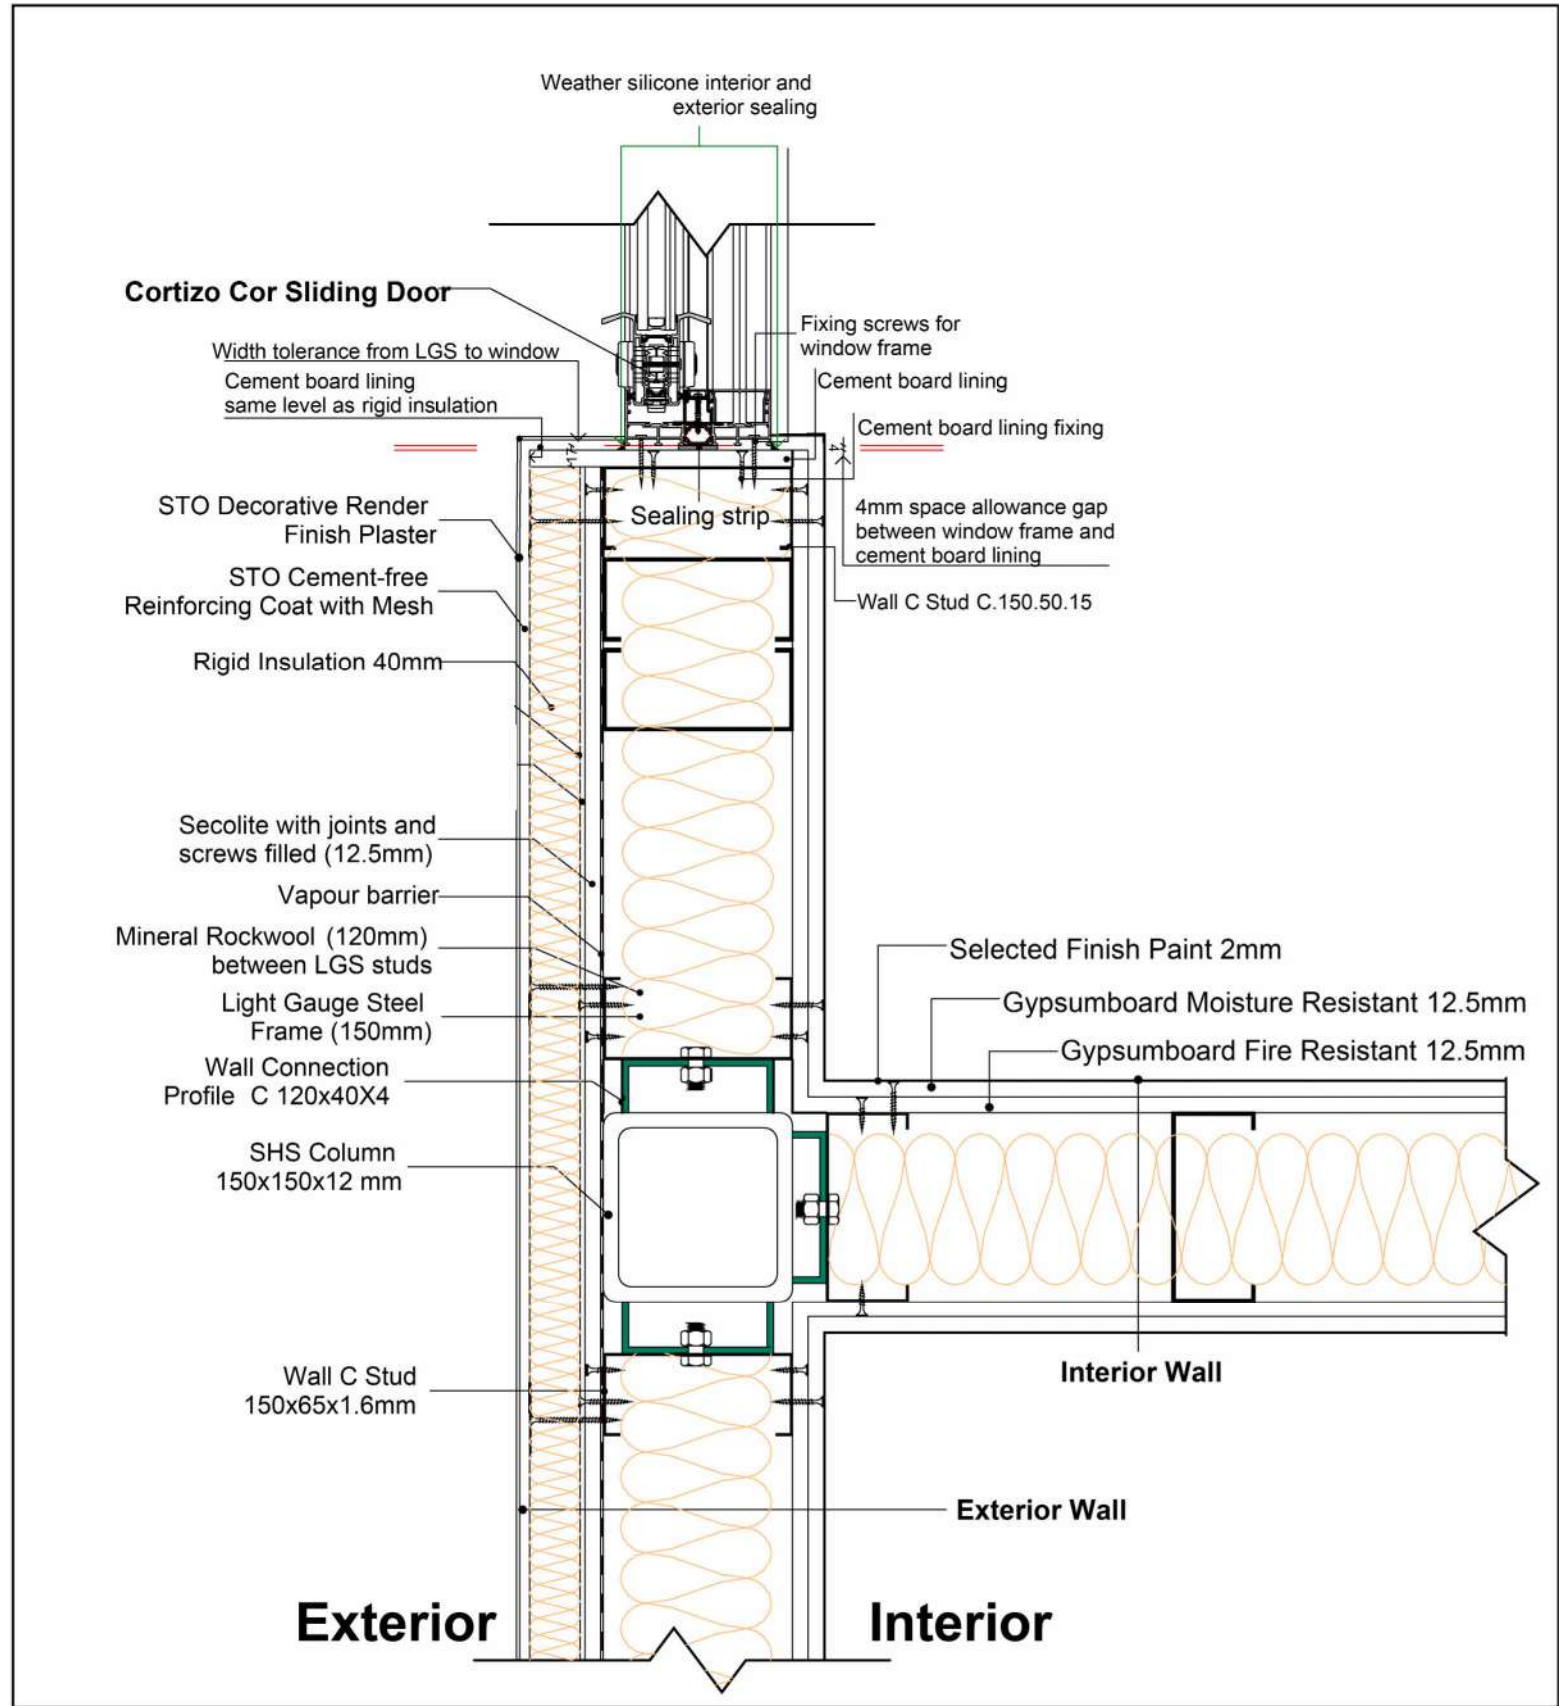

D7.Exterior - Interior Wall Connection Sc: 1/6

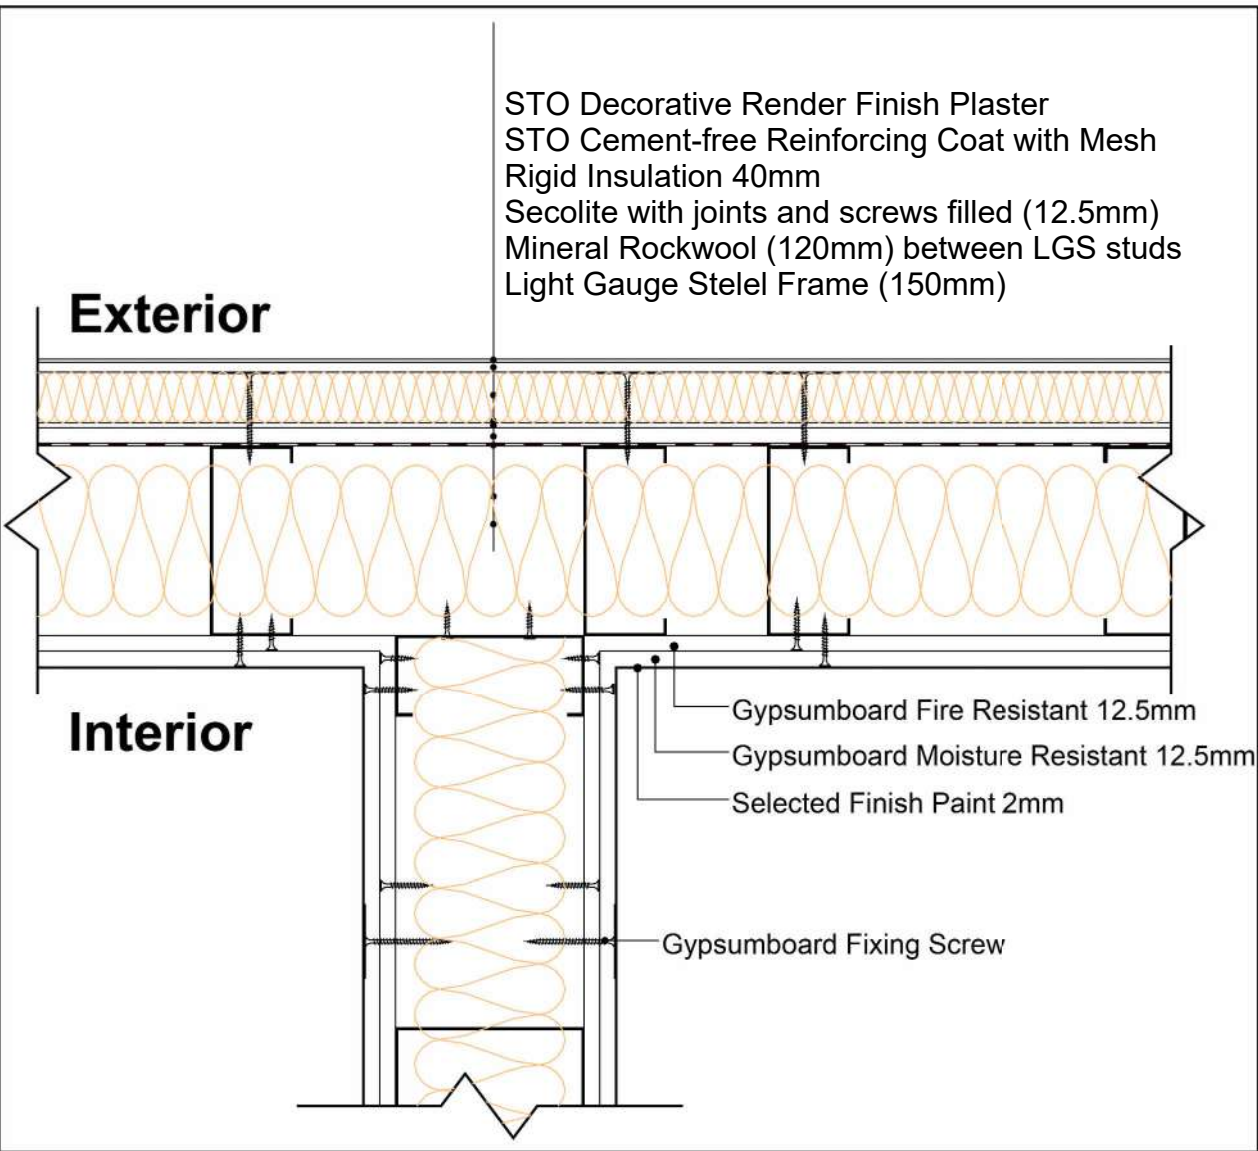

D9.Exterior Corner Wall Sc: 1/6

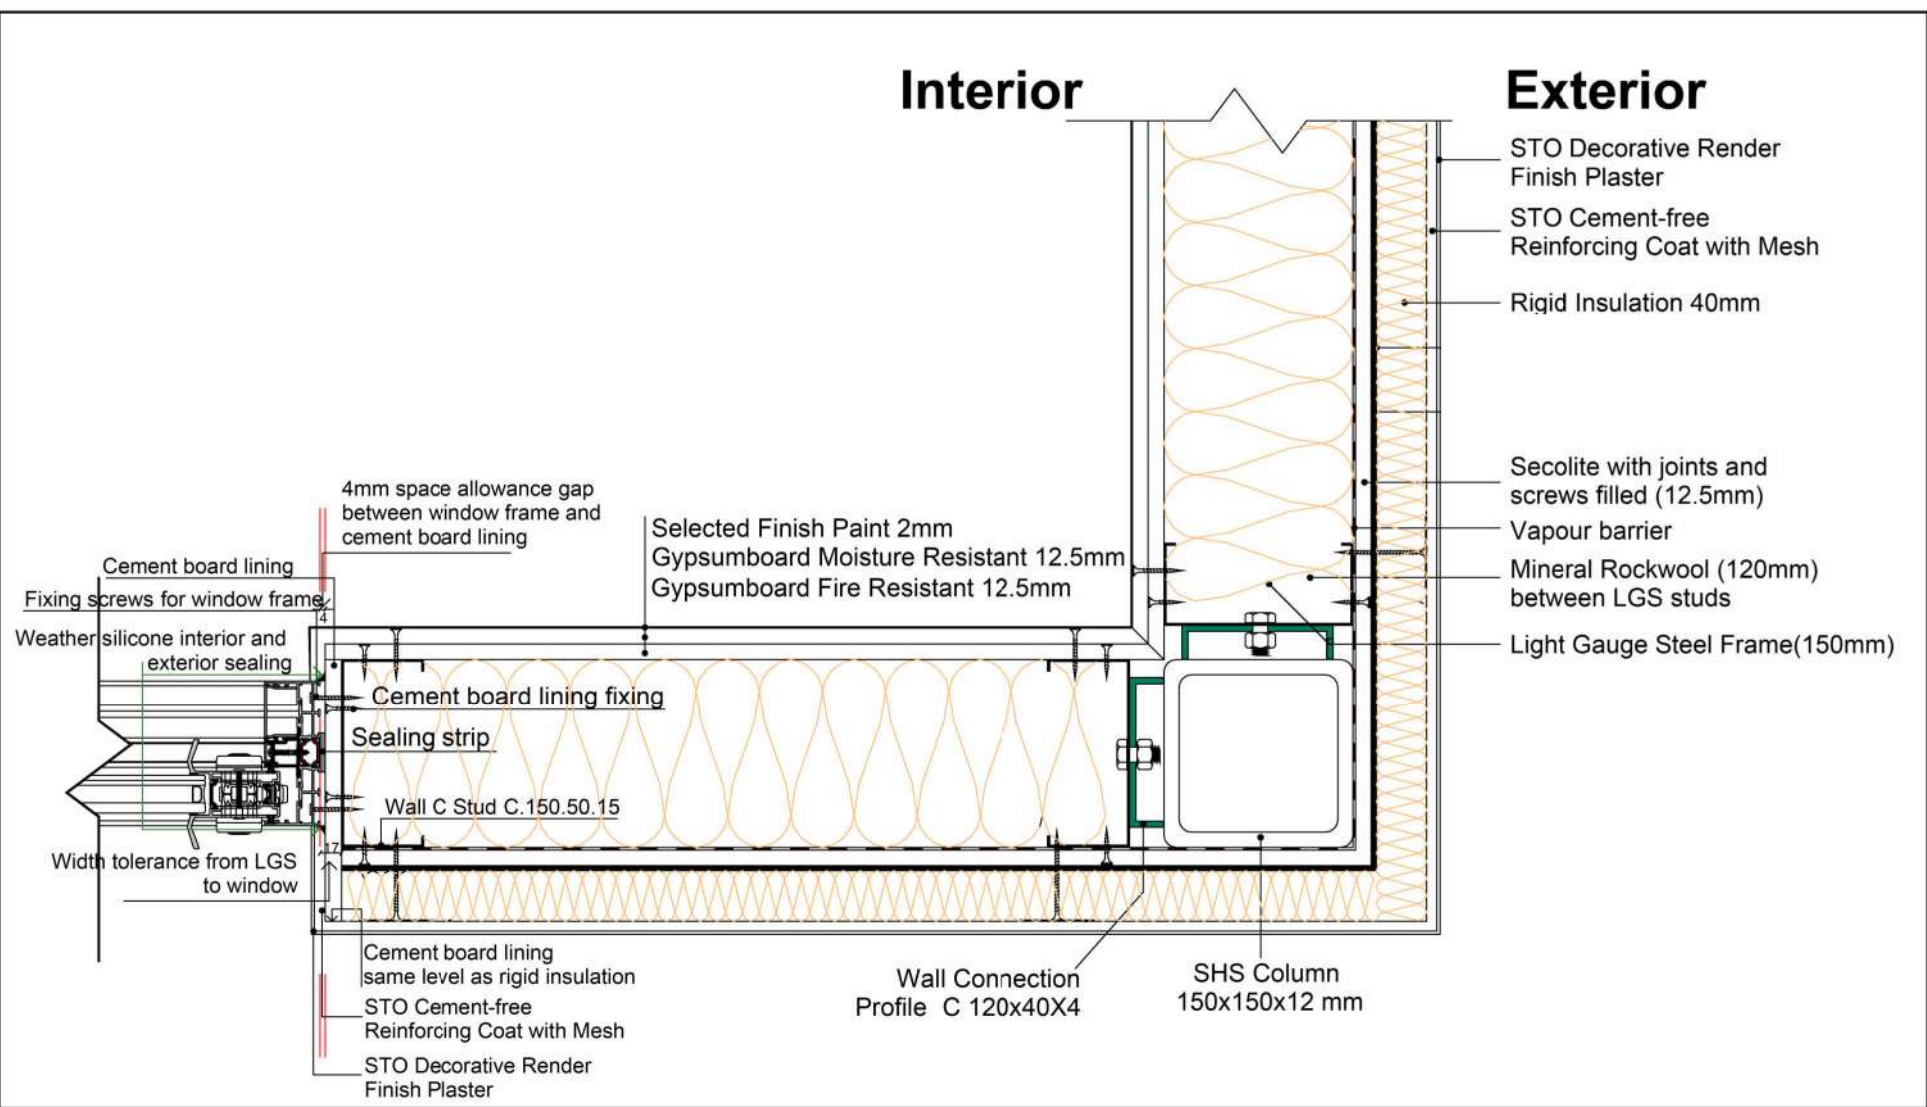

1. THESE DRAWINGS MUST BE CHECKED BY THE CUSTOMER OR CONTRACTOR PRIOR TO APPROVAL. ANY ERRORS OR OMISSIONS MUST BE REPORTED IN WRITING TO BAUHU PRIOR TO COMMENCEMENT OF CONSTRUCTION.
2. ARCHITECTURAL DRAWINGS SHOULD BE READ IN CONJUNCTION WITH STRUCTURAL DETAILING AND FABRICATION GENERAL ASSEMBLY DRAWINGS.
3. FOR CONSTRUCTION PURPOSES, USE ONLY THE LATEST APPROVED DRAWINGS LABELED 'ISSUED FOR CONSTRUCTION'.
4. DO NOT SCALE FROM THIS DRAWING.
5. THE COMPANY OPERATES USING METRIC DIMENSIONS AS THE PRINCIPAL DENOMINATION.
6. ALL CONCRETE WORKS ARE OUTSIDE OF THE SCOPE OF THE COMPANY. INFORMATION REGARDING SLAB DESIGN AND CONNECTIONS IN THESE DRAWINGS ARE INTENDED FOR GUIDENCE ONLY. FOUNDATION AND SLAB WORKS SHOULD BE DESIGNED AND APPROVED BY A LOCAL STRUCTURAL ENGINEER.
7. THE COMPANY RETAINS FULL TITLE AND OWNERSHIP OF THESE PLANS AND DESIGNS. ANY UNAUTHORISED USE, REPRODUCTION, OR DISTRIBUTION OF THESE PLANS, WHETHER IN WHOLE OR PART, IS EXPRESSLY PROHIBITED WITHOUT PRIOR WRITTEN CONSENT.
8. THE INFORMATION CONTAINED WITHIN IS INTENDED TO BE AN AID FOR CONTRACTORS AND INSTALLERS AND IS NOT A SUBSTITUTE FOR PROFESSIONAL JUDGEMENT.

No.	Revision	Date

ISSUED FOR:

- Issued for information
- Issued for client approval
- Issued for fabrication
- Issued for construction

Caribbean
cottage



DRAWING TITLE: Wall Details

DRAWN BY: Bernat Stefana

SCALE:

DRAWING NO: A28

DATE: 18.11.2025

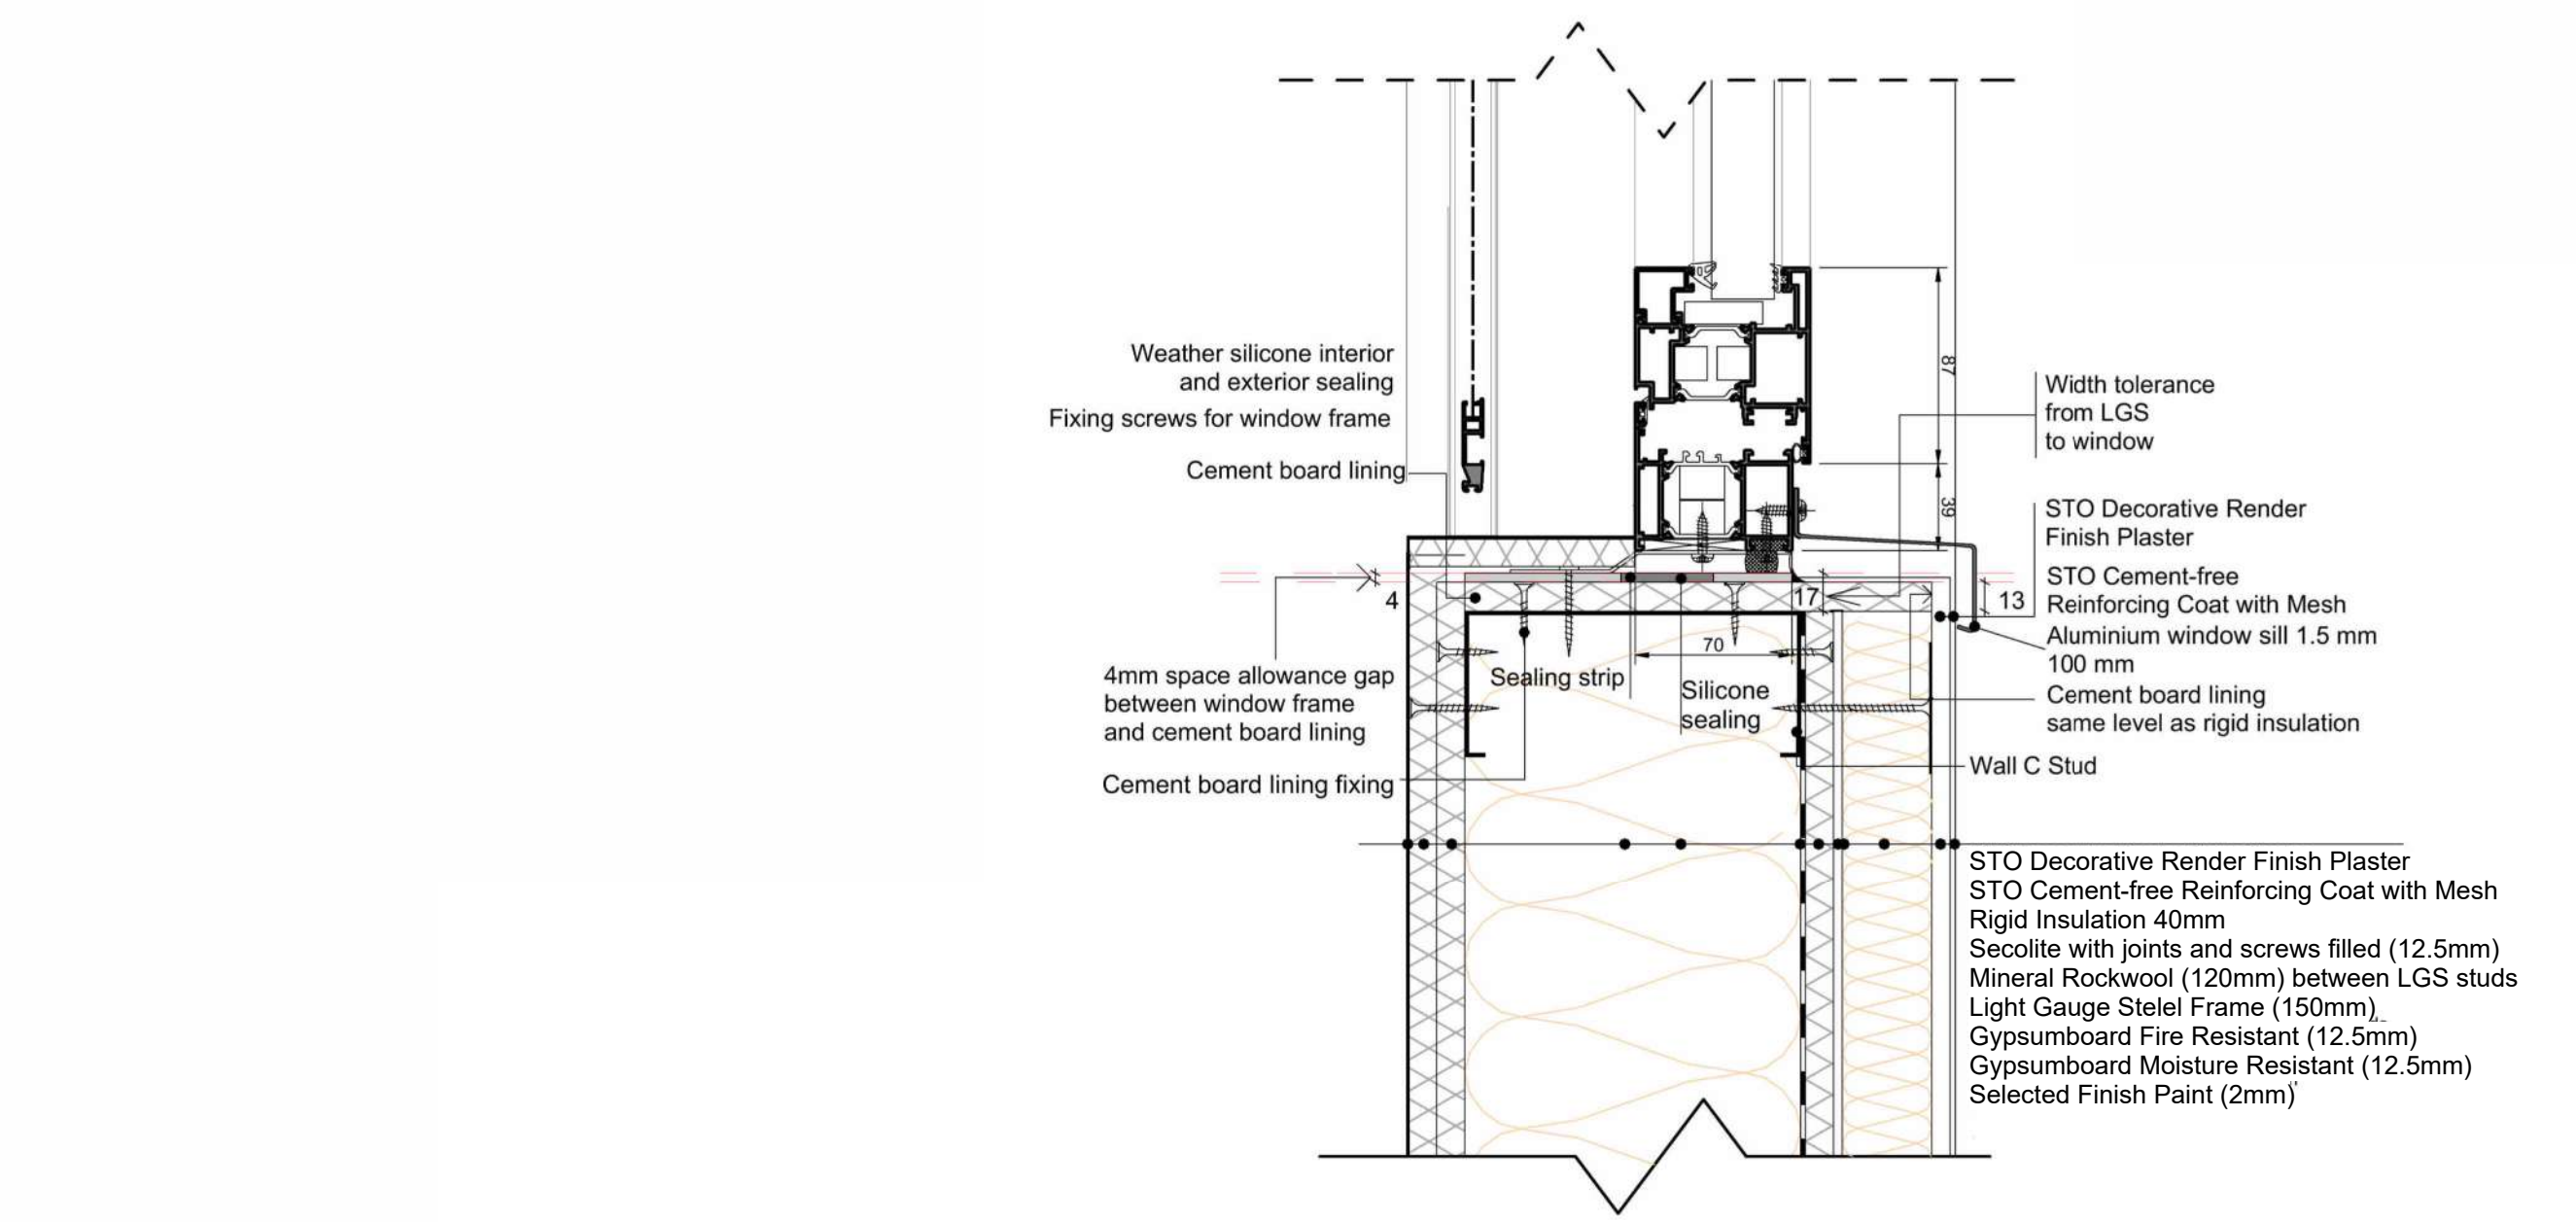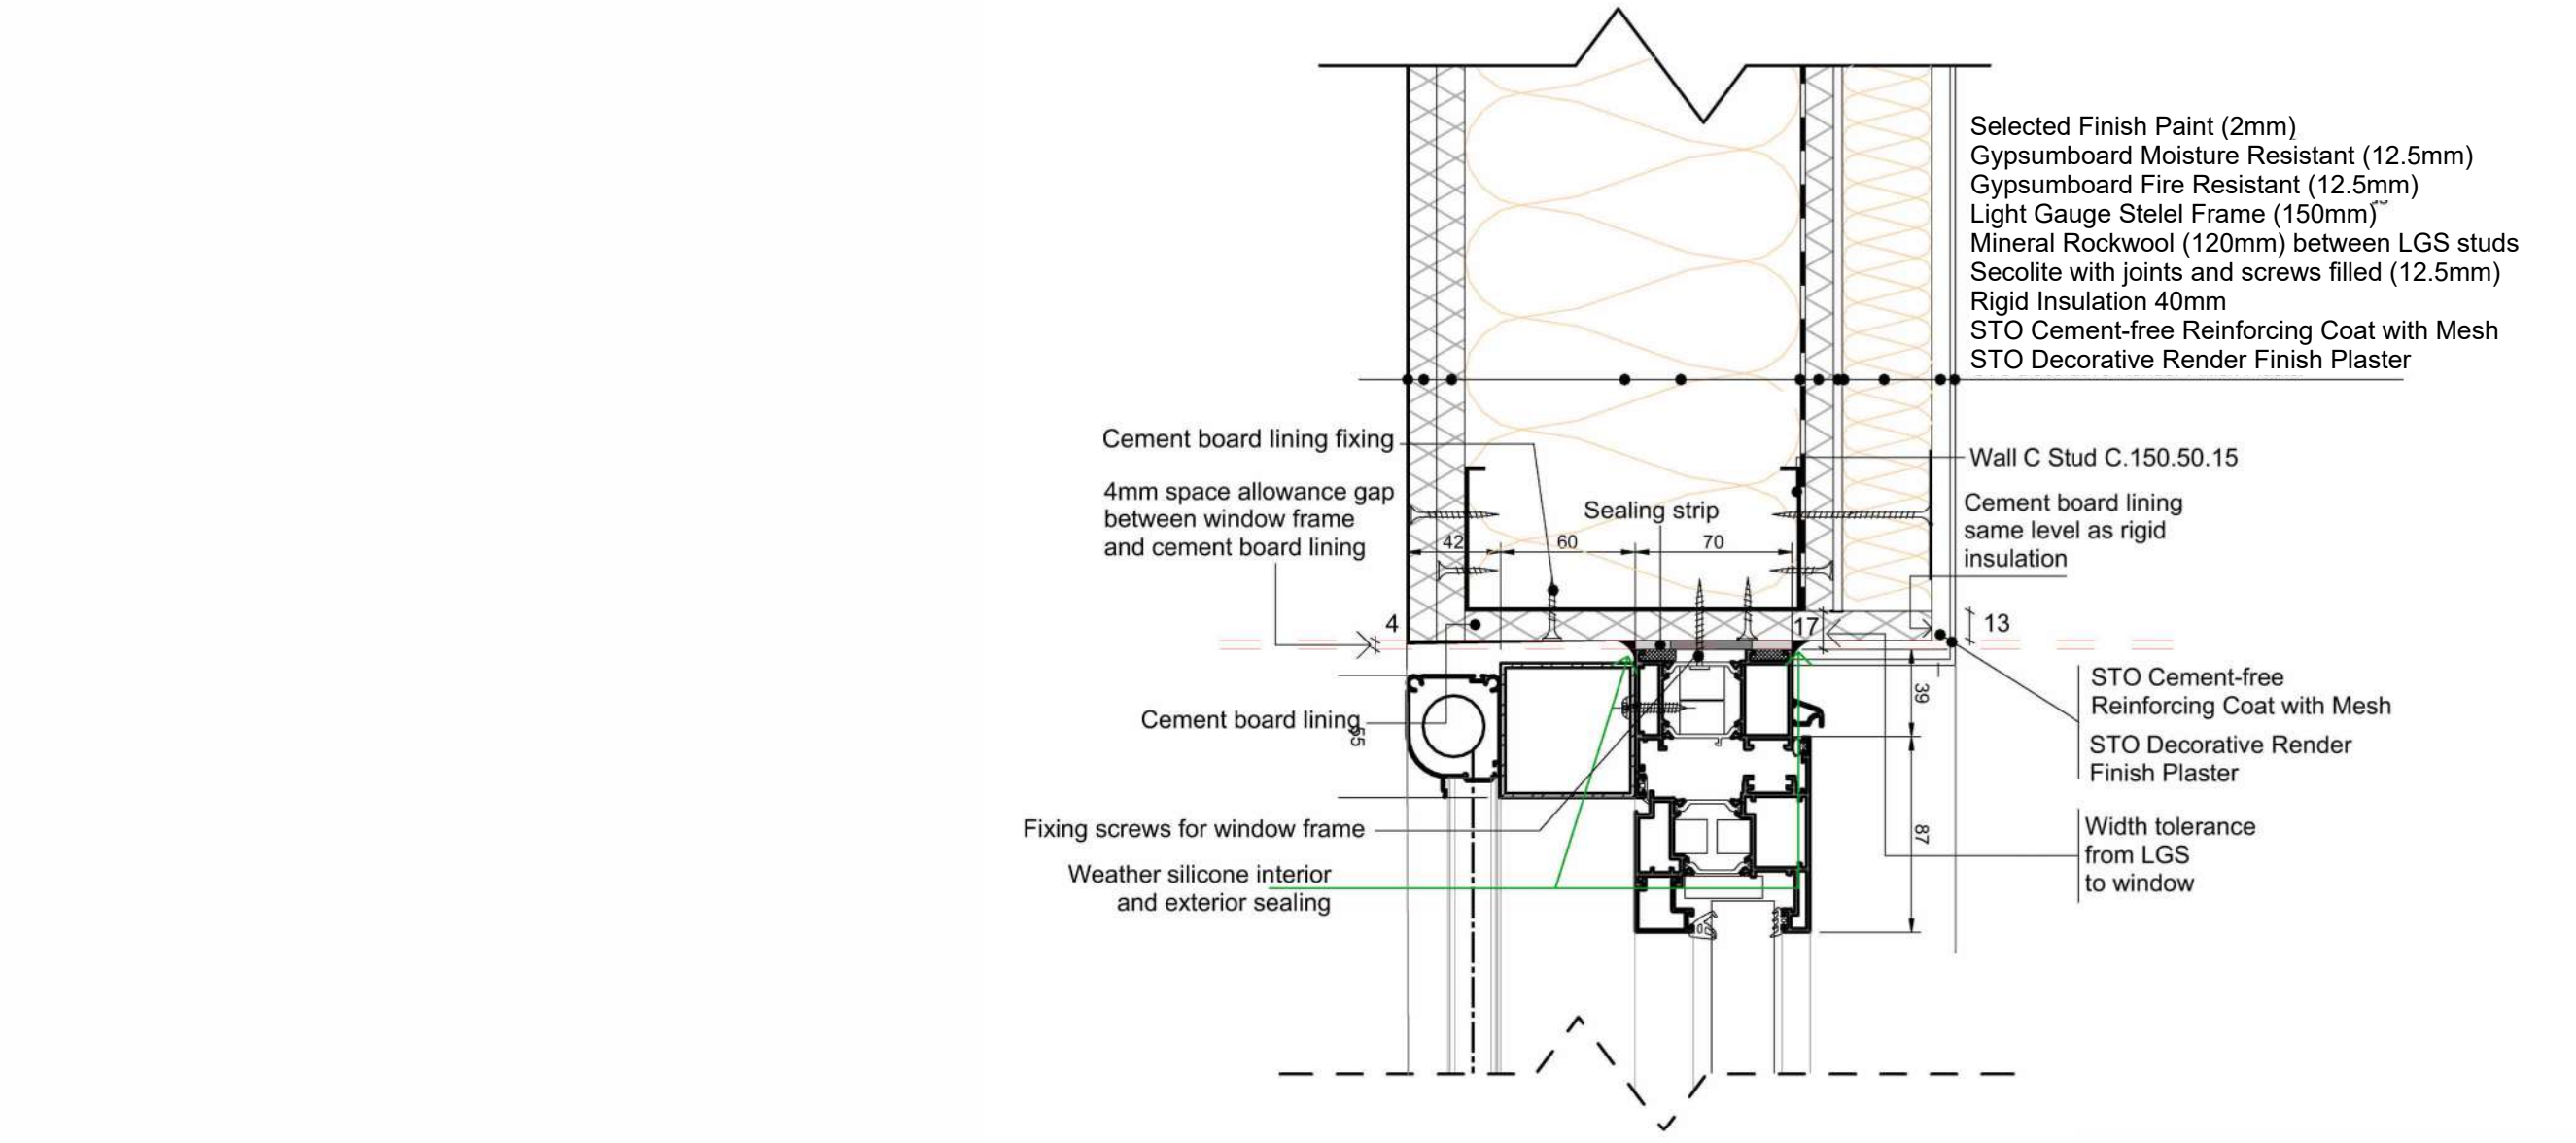

D1.Casement Door/Window Section with insect screens

1. THESE DRAWINGS MUST BE CHECKED BY THE CUSTOMER OR CONTRACTOR PRIOR TO APPROVAL. ANY ERRORS OR OMISSIONS MUST BE REPORTED IN WRITING TO BAUHU PRIOR TO COMMENCEMENT OF CONSTRUCTION.
2. ARCHITECTURAL DRAWINGS SHOULD BE READ IN CONJUNCTION WITH STRUCTURAL DETAILING AND FABRICATION GENERAL ASSEMBLY DRAWINGS.
3. FOR CONSTRUCTION PURPOSES, USE ONLY THE LATEST APPROVED DRAWINGS LABELED 'ISSUED FOR CONSTRUCTION'.
4. DO NOT SCALE FROM THIS DRAWING.
5. THE COMPANY OPERATES USING METRIC DIMENSIONS AS THE PRINCIPAL DENOMINATION.
6. ALL CONCRETE WORKS ARE OUTSIDE OF THE SCOPE OF THE COMPANY. INFORMATION REGARDING SLAB DESIGN AND CONNECTIONS IN THESE DRAWINGS ARE INTENDED FOR GUIDENCE ONLY. FOUNDATION AND SLAB WORKS SHOULD BE DESIGNED AND APPROVED BY A LOCAL STRUCTURAL ENGINEER.
7. THE COMPANY RETAINS FULL TITLE AND OWNERSHIP OF THESE PLANS AND DESIGNS. ANY UNAUTHORISED USE, REPRODUCTION, OR DISTRIBUTION OF THESE PLANS, WHETHER IN WHOLE OR PART, IS EXPRESSLY PROHIBITED WITHOUT PRIOR WRITTEN CONSENT.
8. THE INFORMATION CONTAINED WITHIN IS INTENDED TO BE AN AID FOR CONTRACTORS AND INSTALLERS AND IS NOT A SUBSTITUTE FOR PROFESSIONAL JUDGEMENT.

No.	Revision	Date

ISSUED FOR:

Issued for information

Issued for client approval

Issued for fabrication

Issued for construction

Caribbean
cottage

DRAWING TITLE: Details 1

DRAWN BY: Bernat Stefana

SCALE:

DRAWING NO: A29

DATE: 18.11.2025

1. THESE DRAWINGS MUST BE CHECKED BY THE CUSTOMER OR CONTRACTOR PRIOR TO APPROVAL. ANY ERRORS OR OMISSIONS MUST BE REPORTED IN WRITING TO BAUHU PRIOR TO COMMENCEMENT OF CONSTRUCTION.
2. ARCHITECTURAL DRAWINGS SHOULD BE READ IN CONJUNCTION WITH STRUCTURAL DETAILING AND FABRICATION GENERAL ASSEMBLY DRAWINGS.
3. FOR CONSTRUCTION PURPOSES, USE ONLY THE LATEST APPROVED DRAWINGS LABELED 'ISSUED FOR CONSTRUCTION'.
4. DO NOT SCALE FROM THIS DRAWING.
5. THE COMPANY OPERATES USING METRIC DIMENSIONS AS THE PRINCIPAL DENOMINATION.
6. ALL CONCRETE WORKS ARE OUTSIDE OF THE SCOPE OF THE COMPANY. INFORMATION REGARDING SLAB DESIGN AND CONNECTIONS IN THESE DRAWINGS ARE INTENDED FOR GUIDENCE ONLY. FOUNDATION AND SLAB WORKS SHOULD BE DESIGNED AND APPROVED BY A LOCAL STRUCTURAL ENGINEER.
7. THE COMPANY RETAINS FULL TITLE AND OWNERSHIP OF THESE PLANS AND DESIGNS. ANY UNAUTHORISED USE, REPRODUCTION, OR DISTRIBUTION OF THESE PLANS, WHETHER IN WHOLE OR PART, IS EXPRESSLY PROHIBITED WITHOUT PRIOR WRITTEN CONSENT.
8. THE INFORMATION CONTAINED WITHIN IS INTENDED TO BE AN AID FOR CONTRACTORS AND INSTALLERS AND IS NOT A SUBSTITUTE FOR PROFESSIONAL JUDGEMENT.

No.	Revision	Date

ISSUED FOR:

Issued for information

Issued for client approval

Issued for fabrication

Issued for construction

Caribbean
cottage


DRAWING TITLE: Details 2

DRAWN BY: Bernat Stefana


SCALE:

DRAWING NO: A30

DATE: 18.11.2025

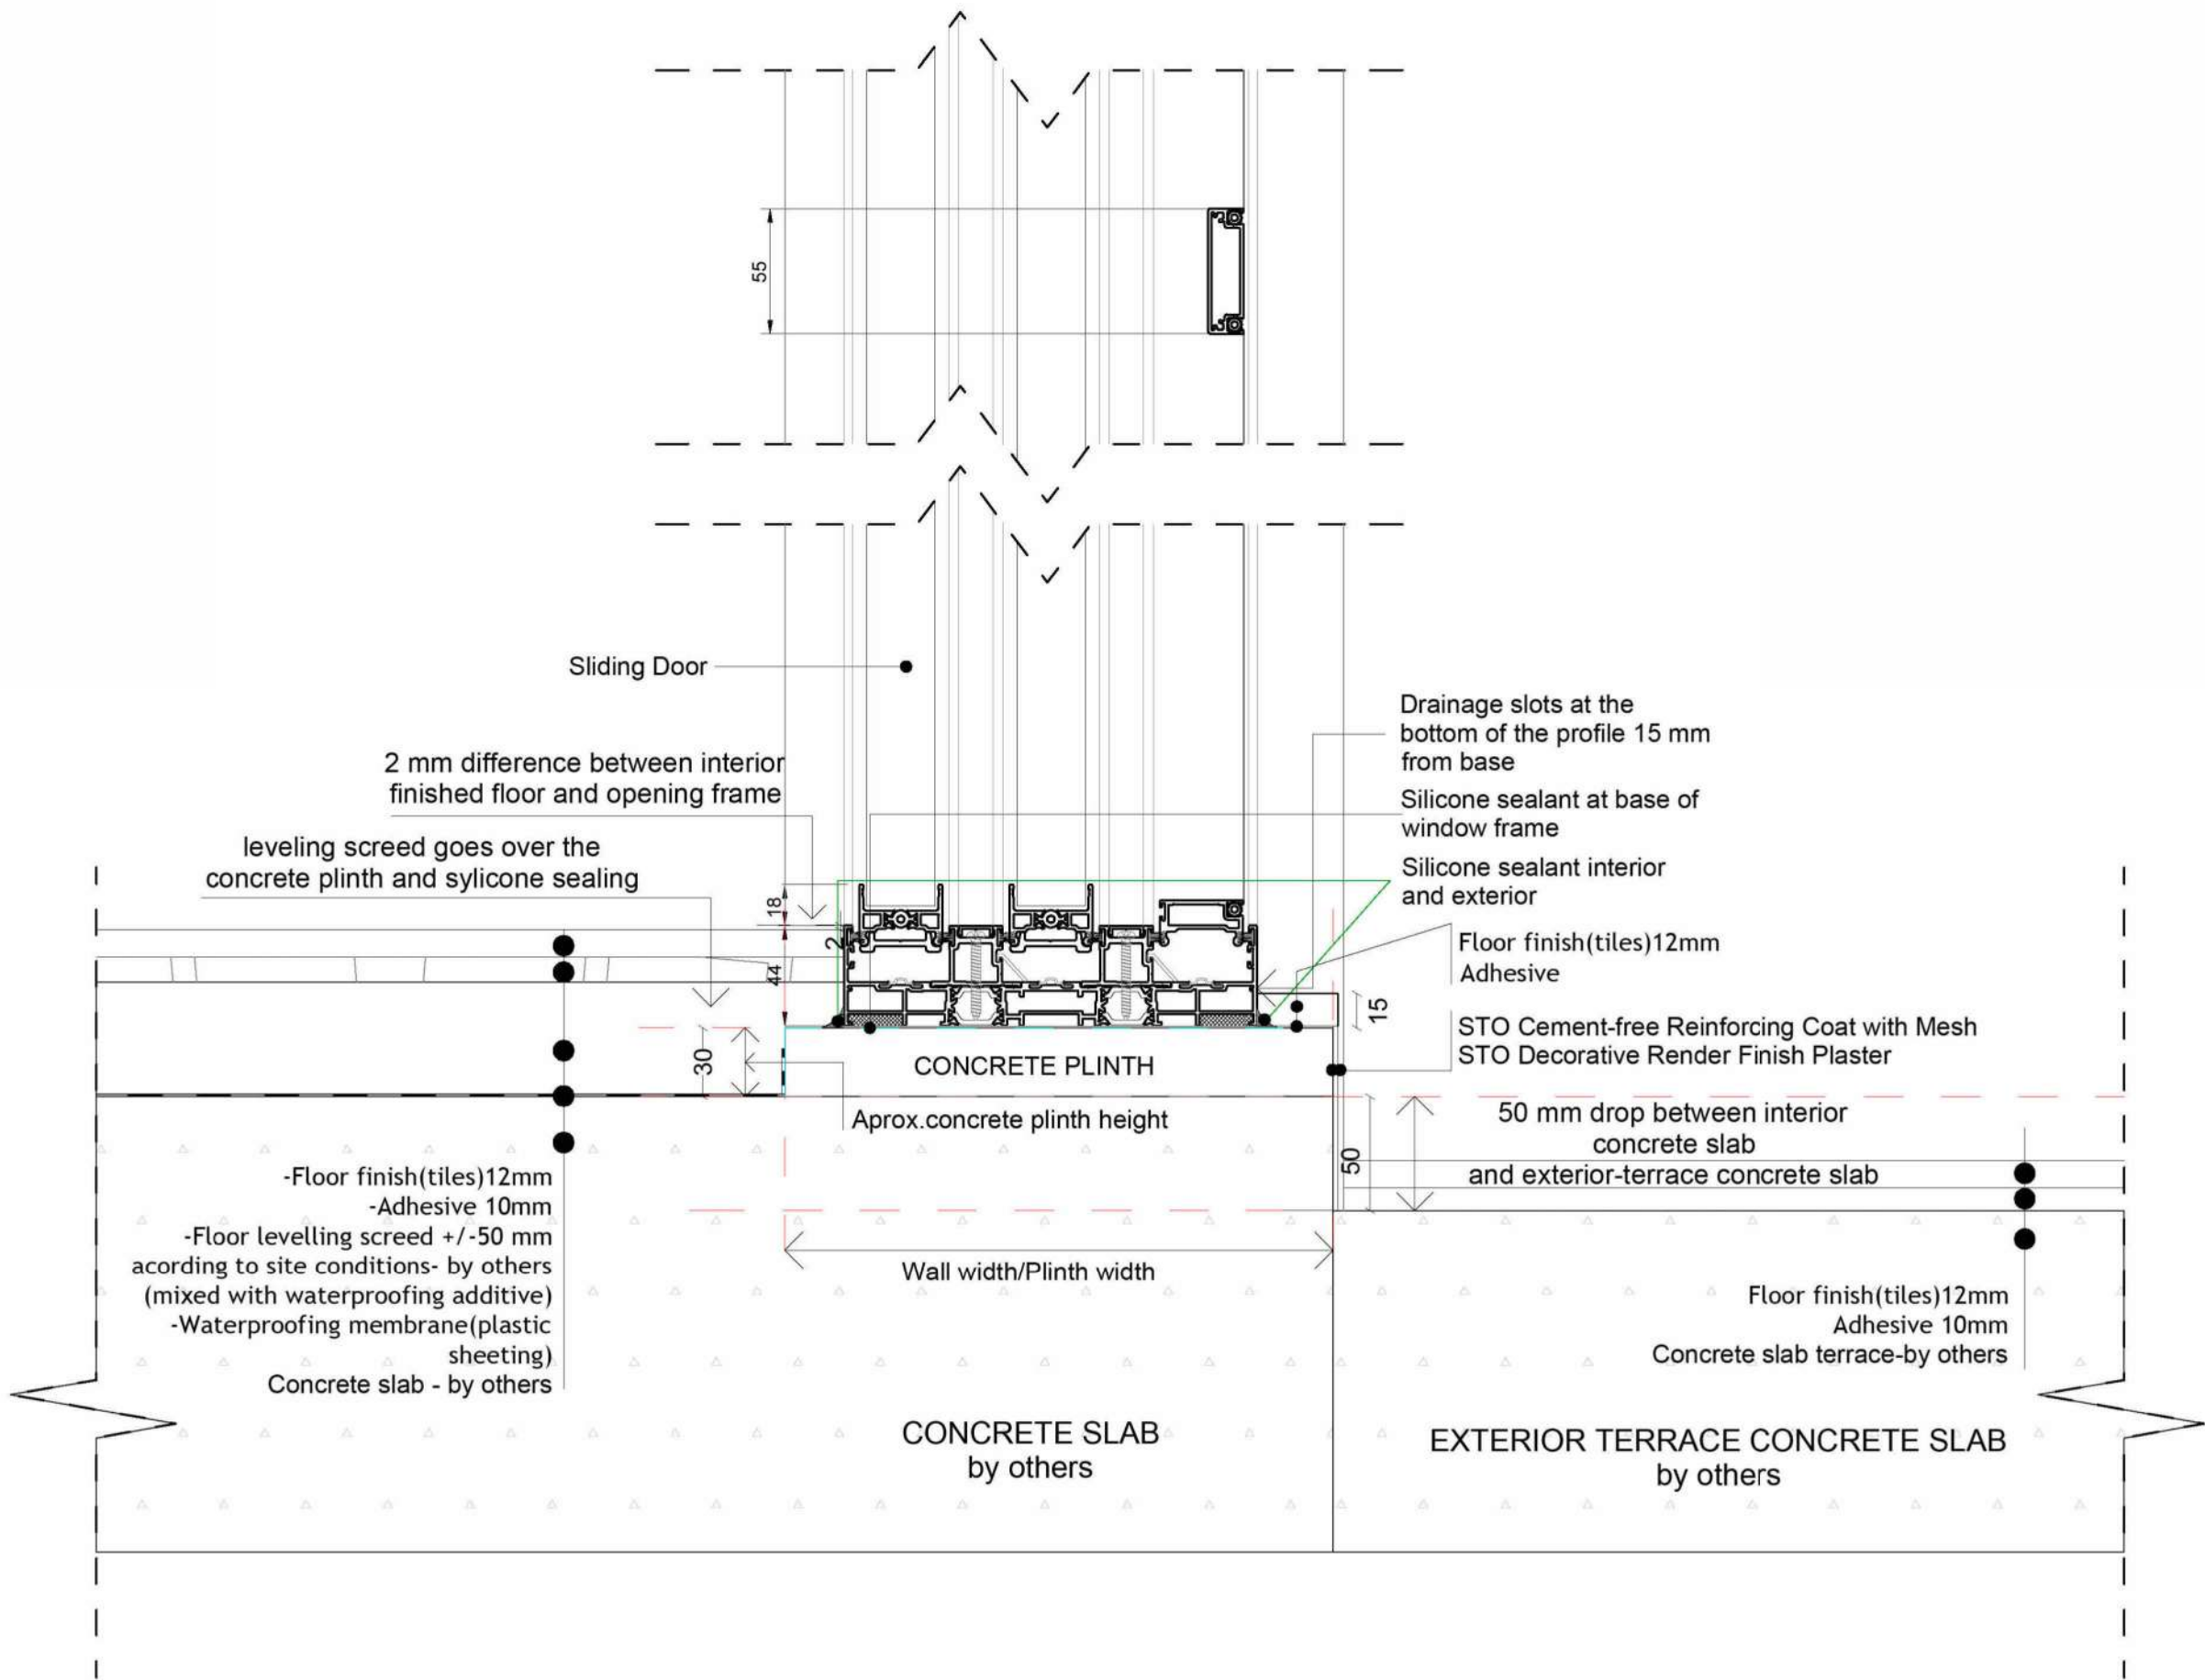

D2.Sliding Door/Window Section
Ground Floor with insect screens

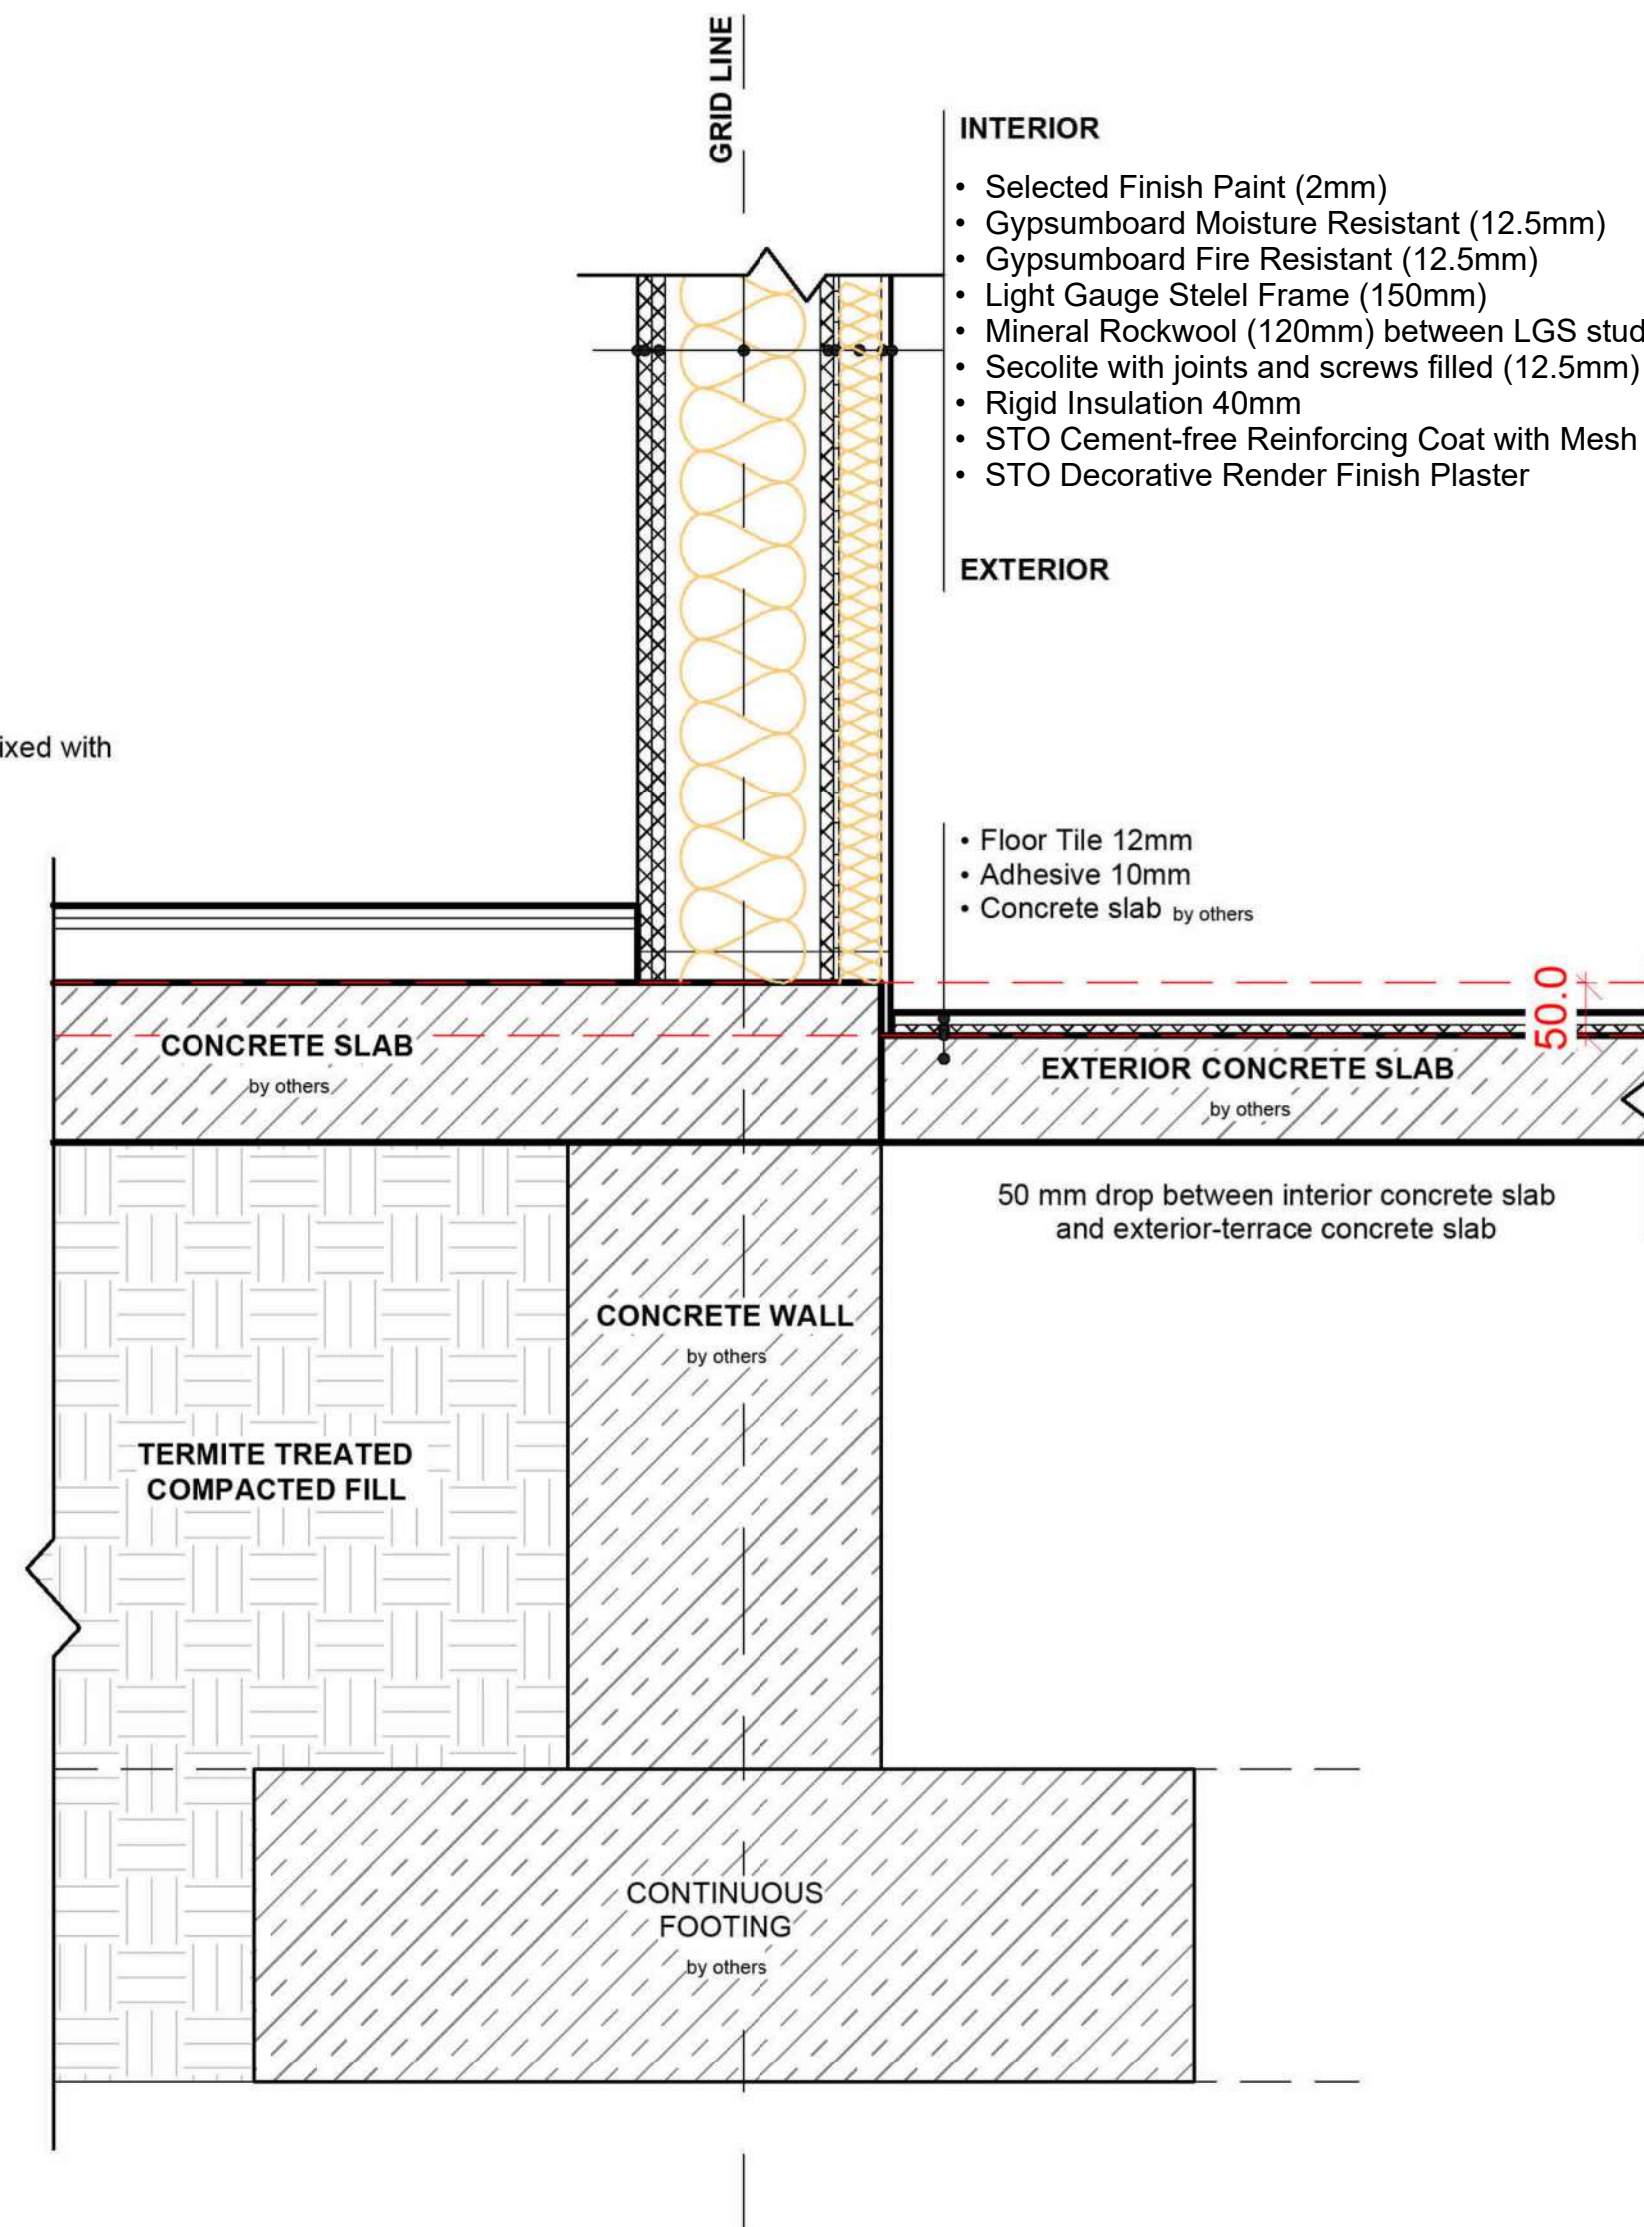[illegible]

ISSUED FOR:

Issued for information

Issued for client approval

Issued for fabrication

Issued for construction

Caribbean cottage

DRAWING TITLE:	Details 4
-----------------------	-----------

DRAWN BY:

Bernat Stefana

SCALE:

DRAWING NO:

A32

DATE: 18.11.2025

1. THESE DRAWINGS MUST BE CHECKED BY THE CUSTOMER OR CONTRACTOR PRIOR TO APPROVAL. ANY ERRORS OR OMISSIONS MUST BE REPORTED IN WRITING TO BAUHU PRIOR TO COMMENCEMENT OF CONSTRUCTION.
2. ARCHITECTURAL DRAWINGS SHOULD BE READ IN CONJUNCTION WITH STRUCTURAL DETAILING AND FABRICATION GENERAL ASSEMBLY DRAWINGS.
3. FOR CONSTRUCTION PURPOSES, USE ONLY THE LATEST APPROVED DRAWINGS LABELED 'ISSUED FOR CONSTRUCTION'.
4. DO NOT SCALE FROM THIS DRAWING.
5. THE COMPANY OPERATES USING METRIC DIMENSIONS AS THE PRINCIPAL DENOMINATION.
6. ALL CONCRETE WORKS ARE OUTSIDE OF THE SCOPE OF THE COMPANY. INFORMATION REGARDING SLAB DESIGN AND CONNECTIONS IN THESE DRAWINGS ARE INTENDED FOR GUIDENCE ONLY. FOUNDATION AND SLAB WORKS SHOULD BE DESIGNED AND APPROVED BY A LOCAL STRUCTURAL ENGINEER.
7. THE COMPANY RETAINS FULL TITLE AND OWNERSHIP OF THESE PLANS AND DESIGNS. ANY UNAUTHORISED USE, REPRODUCTION, OR DISTRIBUTION OF THESE PLANS, WHETHER IN WHOLE OR PART, IS EXPRESSLY PROHIBITED WITHOUT PRIOR WRITTEN CONSENT.
8. THE INFORMATION CONTAINED WITHIN IS INTENDED TO BE AN AID FOR CONTRACTORS AND INSTALLERS AND IS NOT A SUBSTITUTE FOR PROFESSIONAL JUDGEMENT.

No.	Revision	Date

ISSUED FOR:

- Issued for information
Issued for client approval
Issued for fabrication
Issued for construction

Caribbean
cottage


DRAWING TITLE: Details 5

DRAWN BY: Bernat Stefana

SCALE:

DRAWING NO: A33

DATE: 18.11.2025

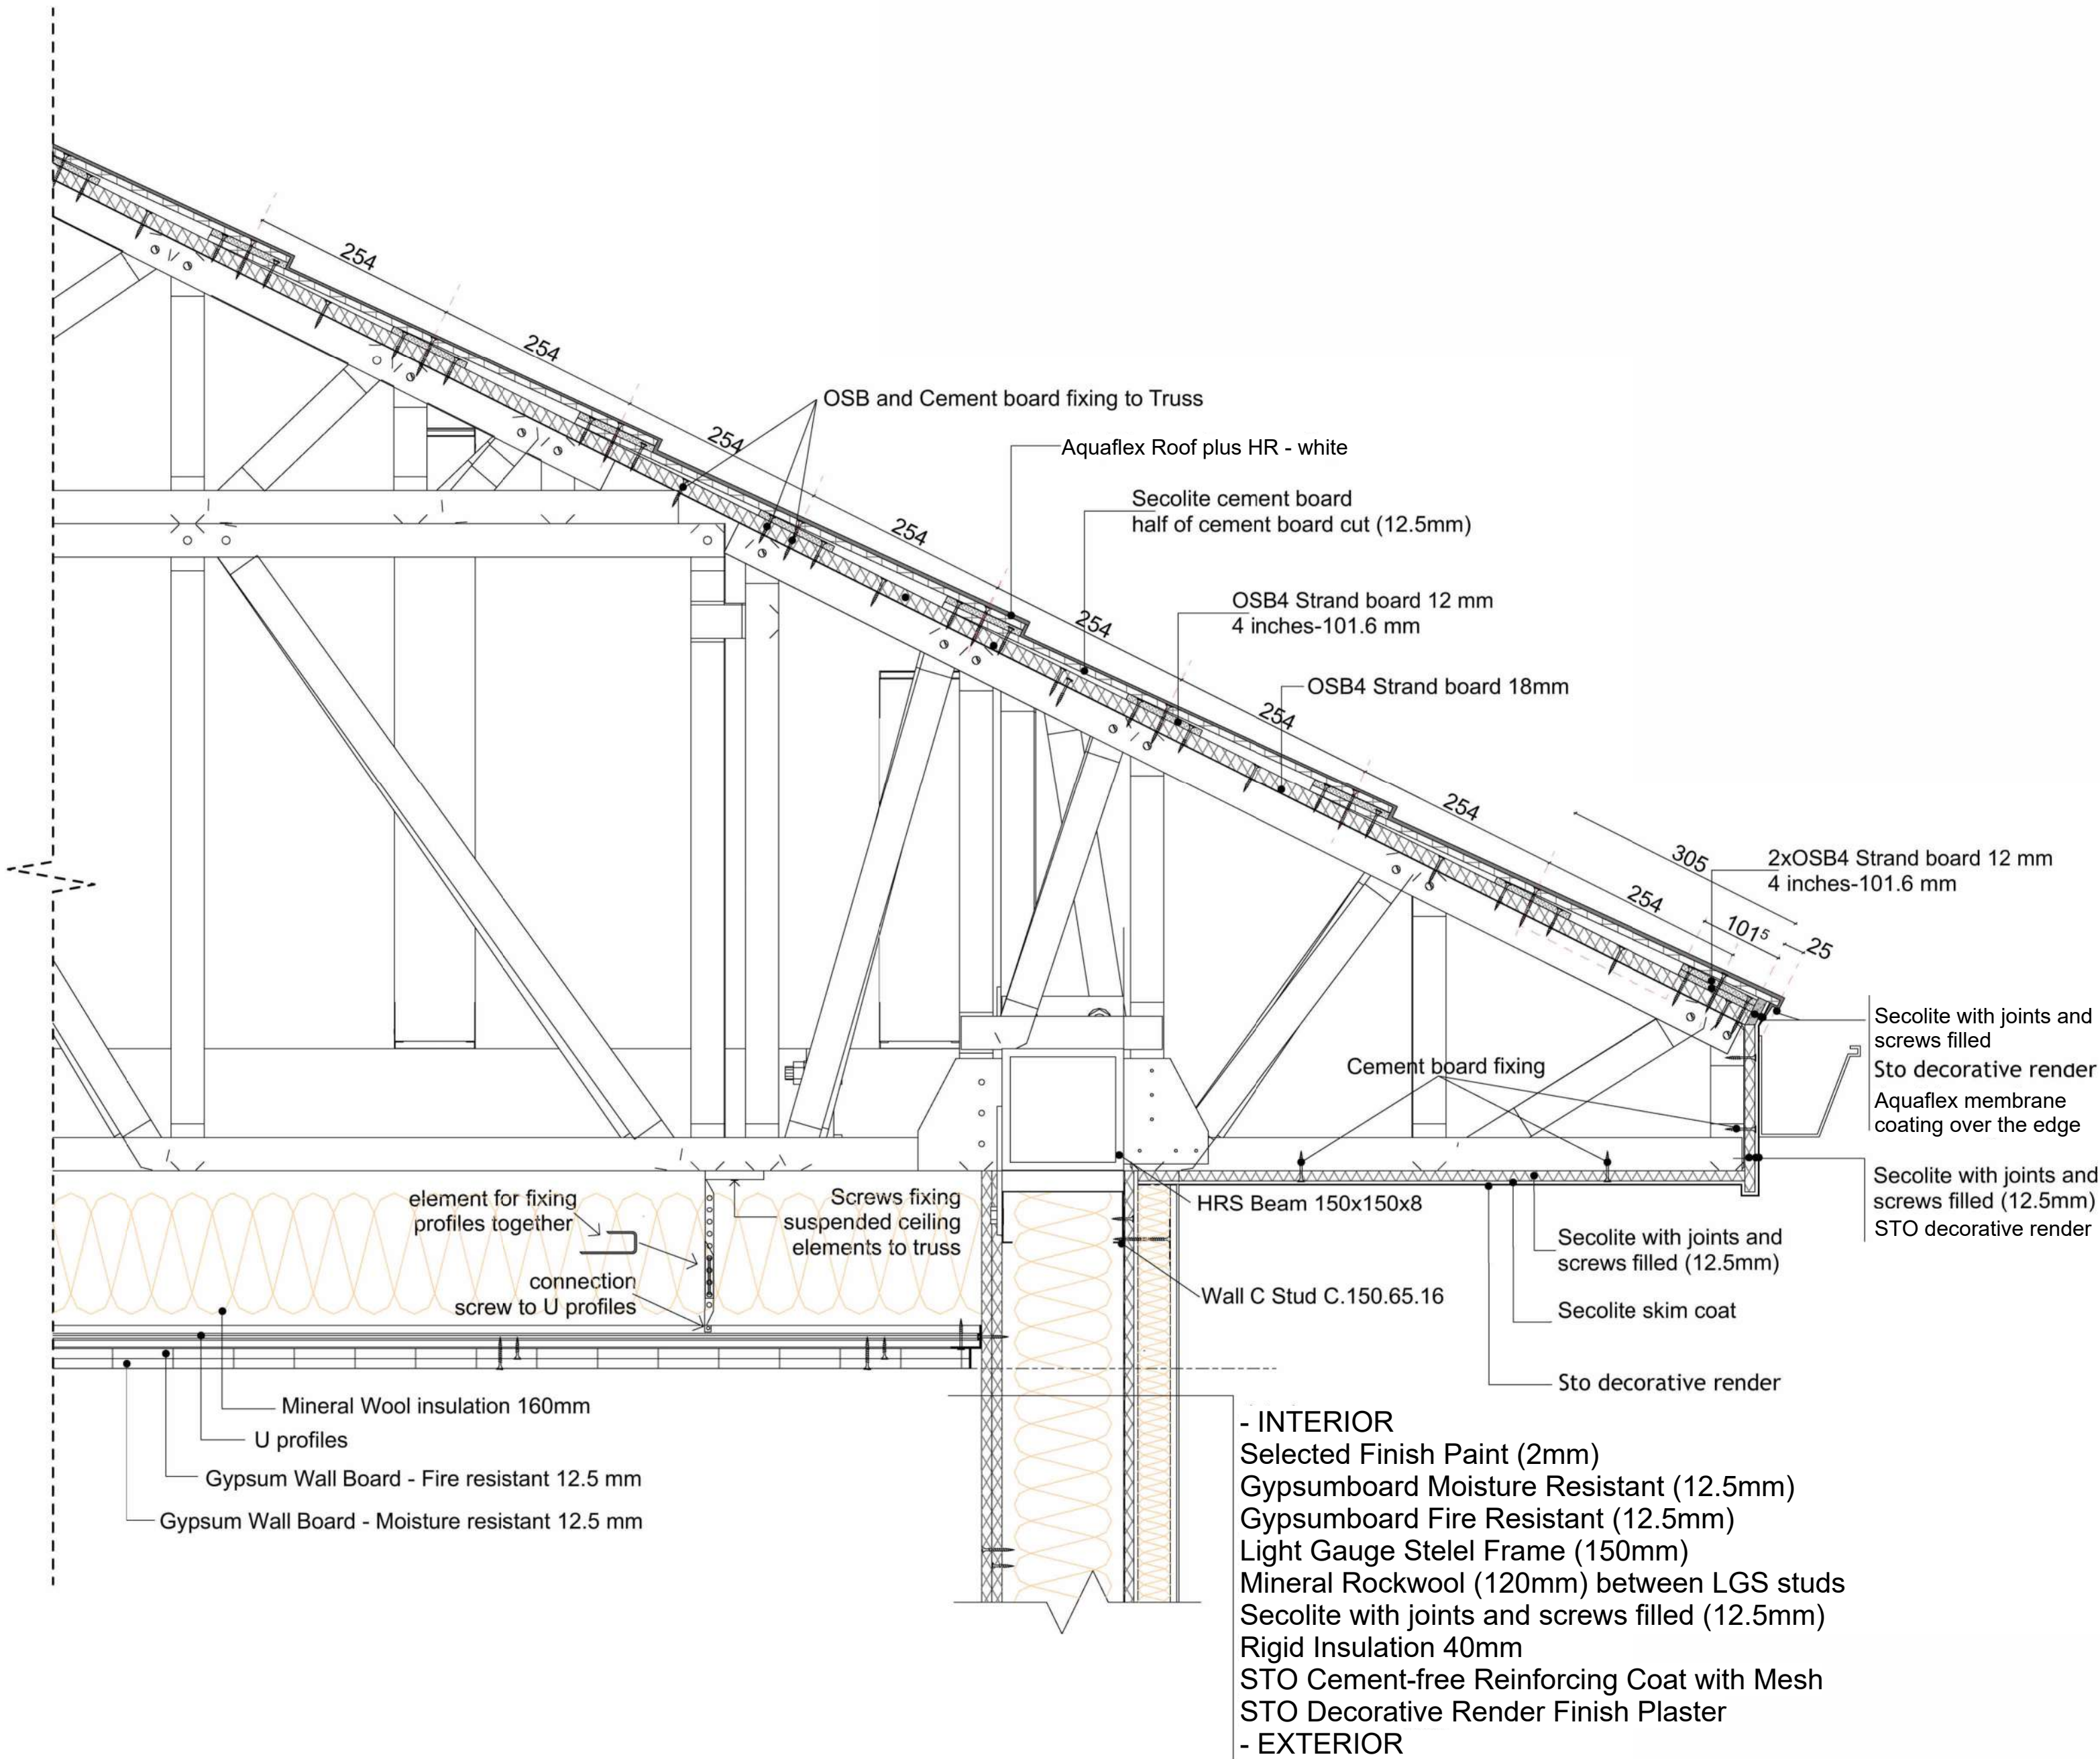

D11.Island Style Roof Detail

1. THESE DRAWINGS MUST BE CHECKED BY THE CUSTOMER OR CONTRACTOR PRIOR TO APPROVAL. ANY ERRORS OR OMISSIONS MUST BE REPORTED IN WRITING TO BAUHU PRIOR TO COMMENCEMENT OF CONSTRUCTION.
2. ARCHITECTURAL DRAWINGS SHOULD BE READ IN CONJUNCTION WITH STRUCTURAL DETAILING AND FABRICATION GENERAL ASSEMBLY DRAWINGS.
3. FOR CONSTRUCTION PURPOSES, USE ONLY THE LATEST APPROVED DRAWINGS LABELED 'ISSUED FOR CONSTRUCTION'.
4. DO NOT SCALE FROM THIS DRAWING.
5. THE COMPANY OPERATES USING METRIC DIMENSIONS AS THE PRINCIPAL DENOMINATION.
6. ALL CONCRETE WORKS ARE OUTSIDE OF THE SCOPE OF THE COMPANY. INFORMATION REGARDING SLAB DESIGN AND CONNECTIONS IN THESE DRAWINGS ARE INTENDED FOR GUIDENCE ONLY. FOUNDATION AND SLAB WORKS SHOULD BE DESIGNED AND APPROVED BY A LOCAL STRUCTURAL ENGINEER.
7. THE COMPANY RETAINS FULL TITLE AND OWNERSHIP OF THESE PLANS AND DESIGNS. ANY UNAUTHORISED USE, REPRODUCTION, OR DISTRIBUTION OF THESE PLANS, WHETHER IN WHOLE OR PART, IS EXPRESSLY PROHIBITED WITHOUT PRIOR WRITTEN CONSENT.
8. THE INFORMATION CONTAINED WITHIN IS INTENDED TO BE AN AID FOR CONTRACTORS AND INSTALLERS AND IS NOT A SUBSTITUTE FOR PROFESSIONAL JUDGEMENT.

No.	Revision	Date

ISSUED FOR:

- Issued for information
Issued for client approval
Issued for fabrication
Issued for construction

Caribbean
cottage


DRAWING TITLE: Details 6

DRAWN BY: Bernat Stefana

SCALE:

DRAWING NO: A34

DATE: 18.11.2025

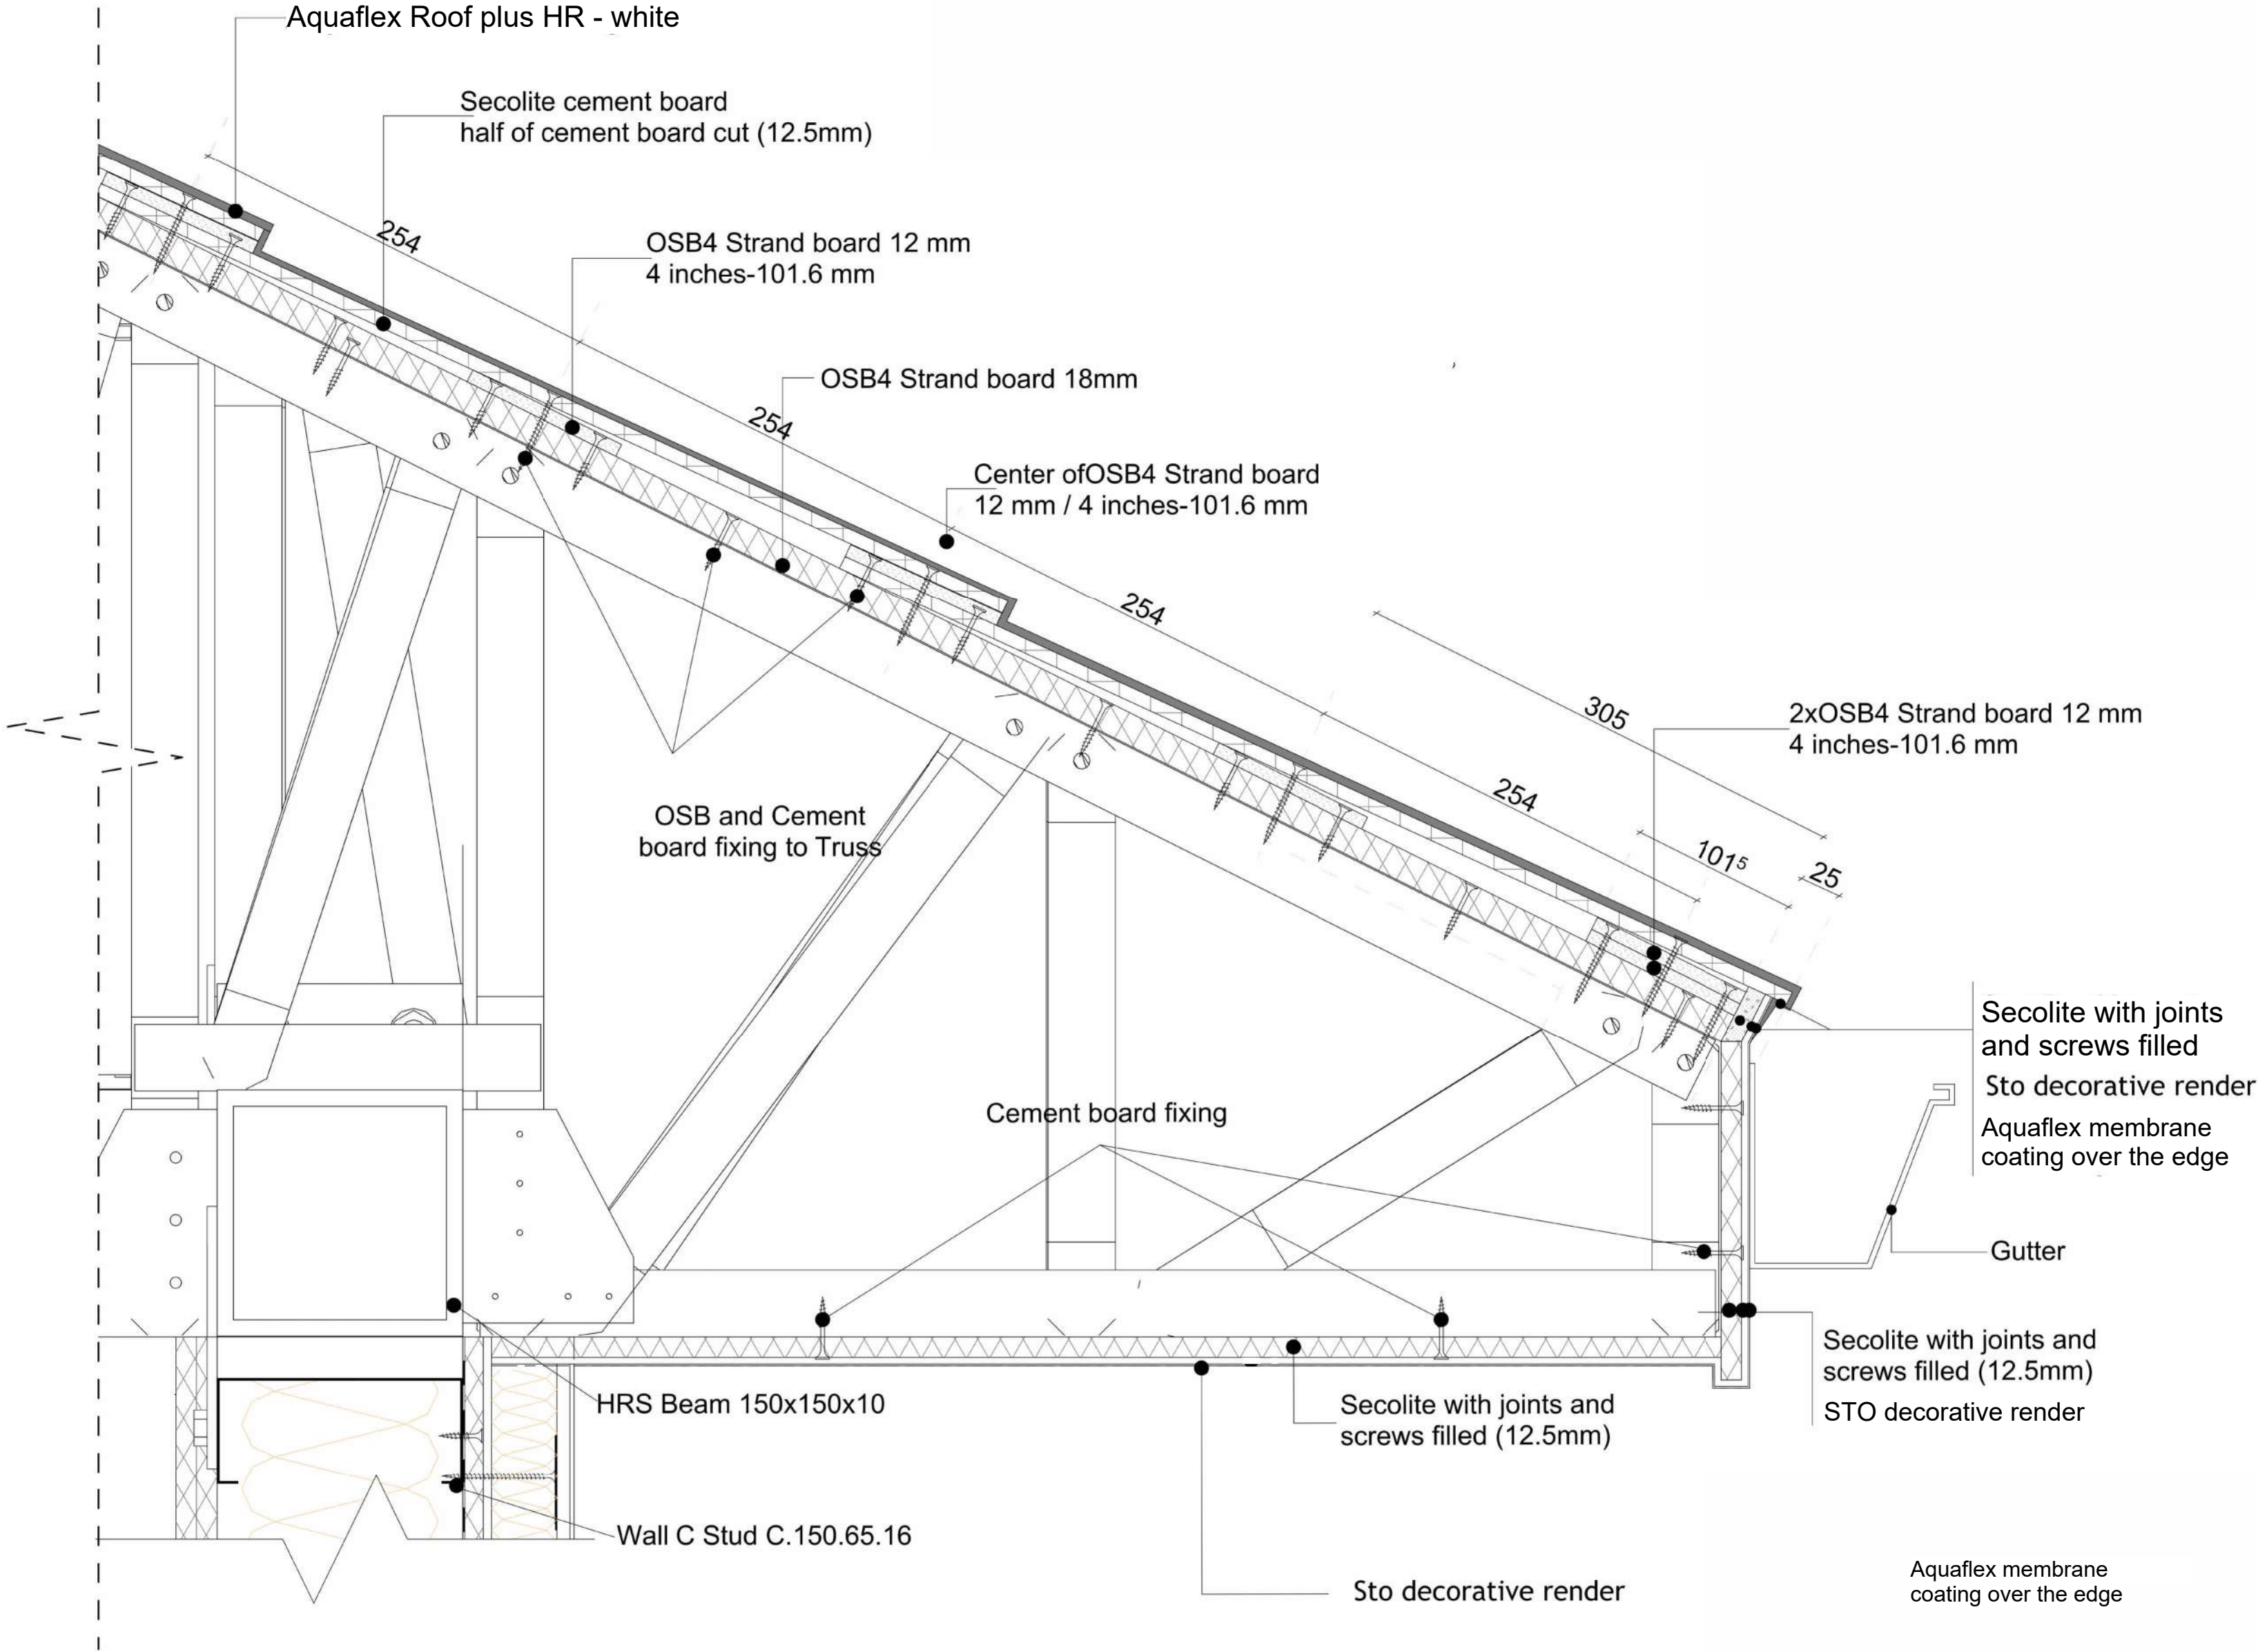

D12.Island Style Roof Detail

1. THESE DRAWINGS MUST BE CHECKED BY THE CUSTOMER OR CONTRACTOR PRIOR TO APPROVAL. ANY ERRORS OR OMISSIONS MUST BE REPORTED IN WRITING TO BAUHU PRIOR TO COMMENCEMENT OF CONSTRUCTION.
2. ARCHITECTURAL DRAWINGS SHOULD BE READ IN CONJUNCTION WITH STRUCTURAL DETAILING AND FABRICATION GENERAL ASSEMBLY DRAWINGS.
3. FOR CONSTRUCTION PURPOSES, USE ONLY THE LATEST APPROVED DRAWINGS LABELED 'ISSUED FOR CONSTRUCTION'.
4. DO NOT SCALE FROM THIS DRAWING.
5. THE COMPANY OPERATES USING METRIC DIMENSIONS AS THE PRINCIPAL DENOMINATION.
6. ALL CONCRETE WORKS ARE OUTSIDE OF THE SCOPE OF THE COMPANY. INFORMATION REGARDING SLAB DESIGN AND CONNECTIONS IN THESE DRAWINGS ARE INTENDED FOR GUIDENCE ONLY. FOUNDATION AND SLAB WORKS SHOULD BE DESIGNED AND APPROVED BY A LOCAL STRUCTURAL ENGINEER.
7. THE COMPANY RETAINS FULL TITLE AND OWNERSHIP OF THESE PLANS AND DESIGNS. ANY UNAUTHORISED USE, REPRODUCTION, OR DISTRIBUTION OF THESE PLANS, WHETHER IN WHOLE OR PART, IS EXPRESSLY PROHIBITED WITHOUT PRIOR WRITTEN CONSENT.
8. THE INFORMATION CONTAINED WITHIN IS INTENDED TO BE AN AID FOR CONTRACTORS AND INSTALLERS AND IS NOT A SUBSTITUTE FOR PROFESSIONAL JUDGEMENT.

No.	Revision	Date

ISSUED FOR:

- Issued for information
Issued for client approval
Issued for fabrication
Issued for construction

Caribbean cottage

DRAWING TITLE:

Details 7

DRAWN BY:

Bernat Stefana


SCALE:

DRAWING NO:


A35

DATE:

18.11.2025

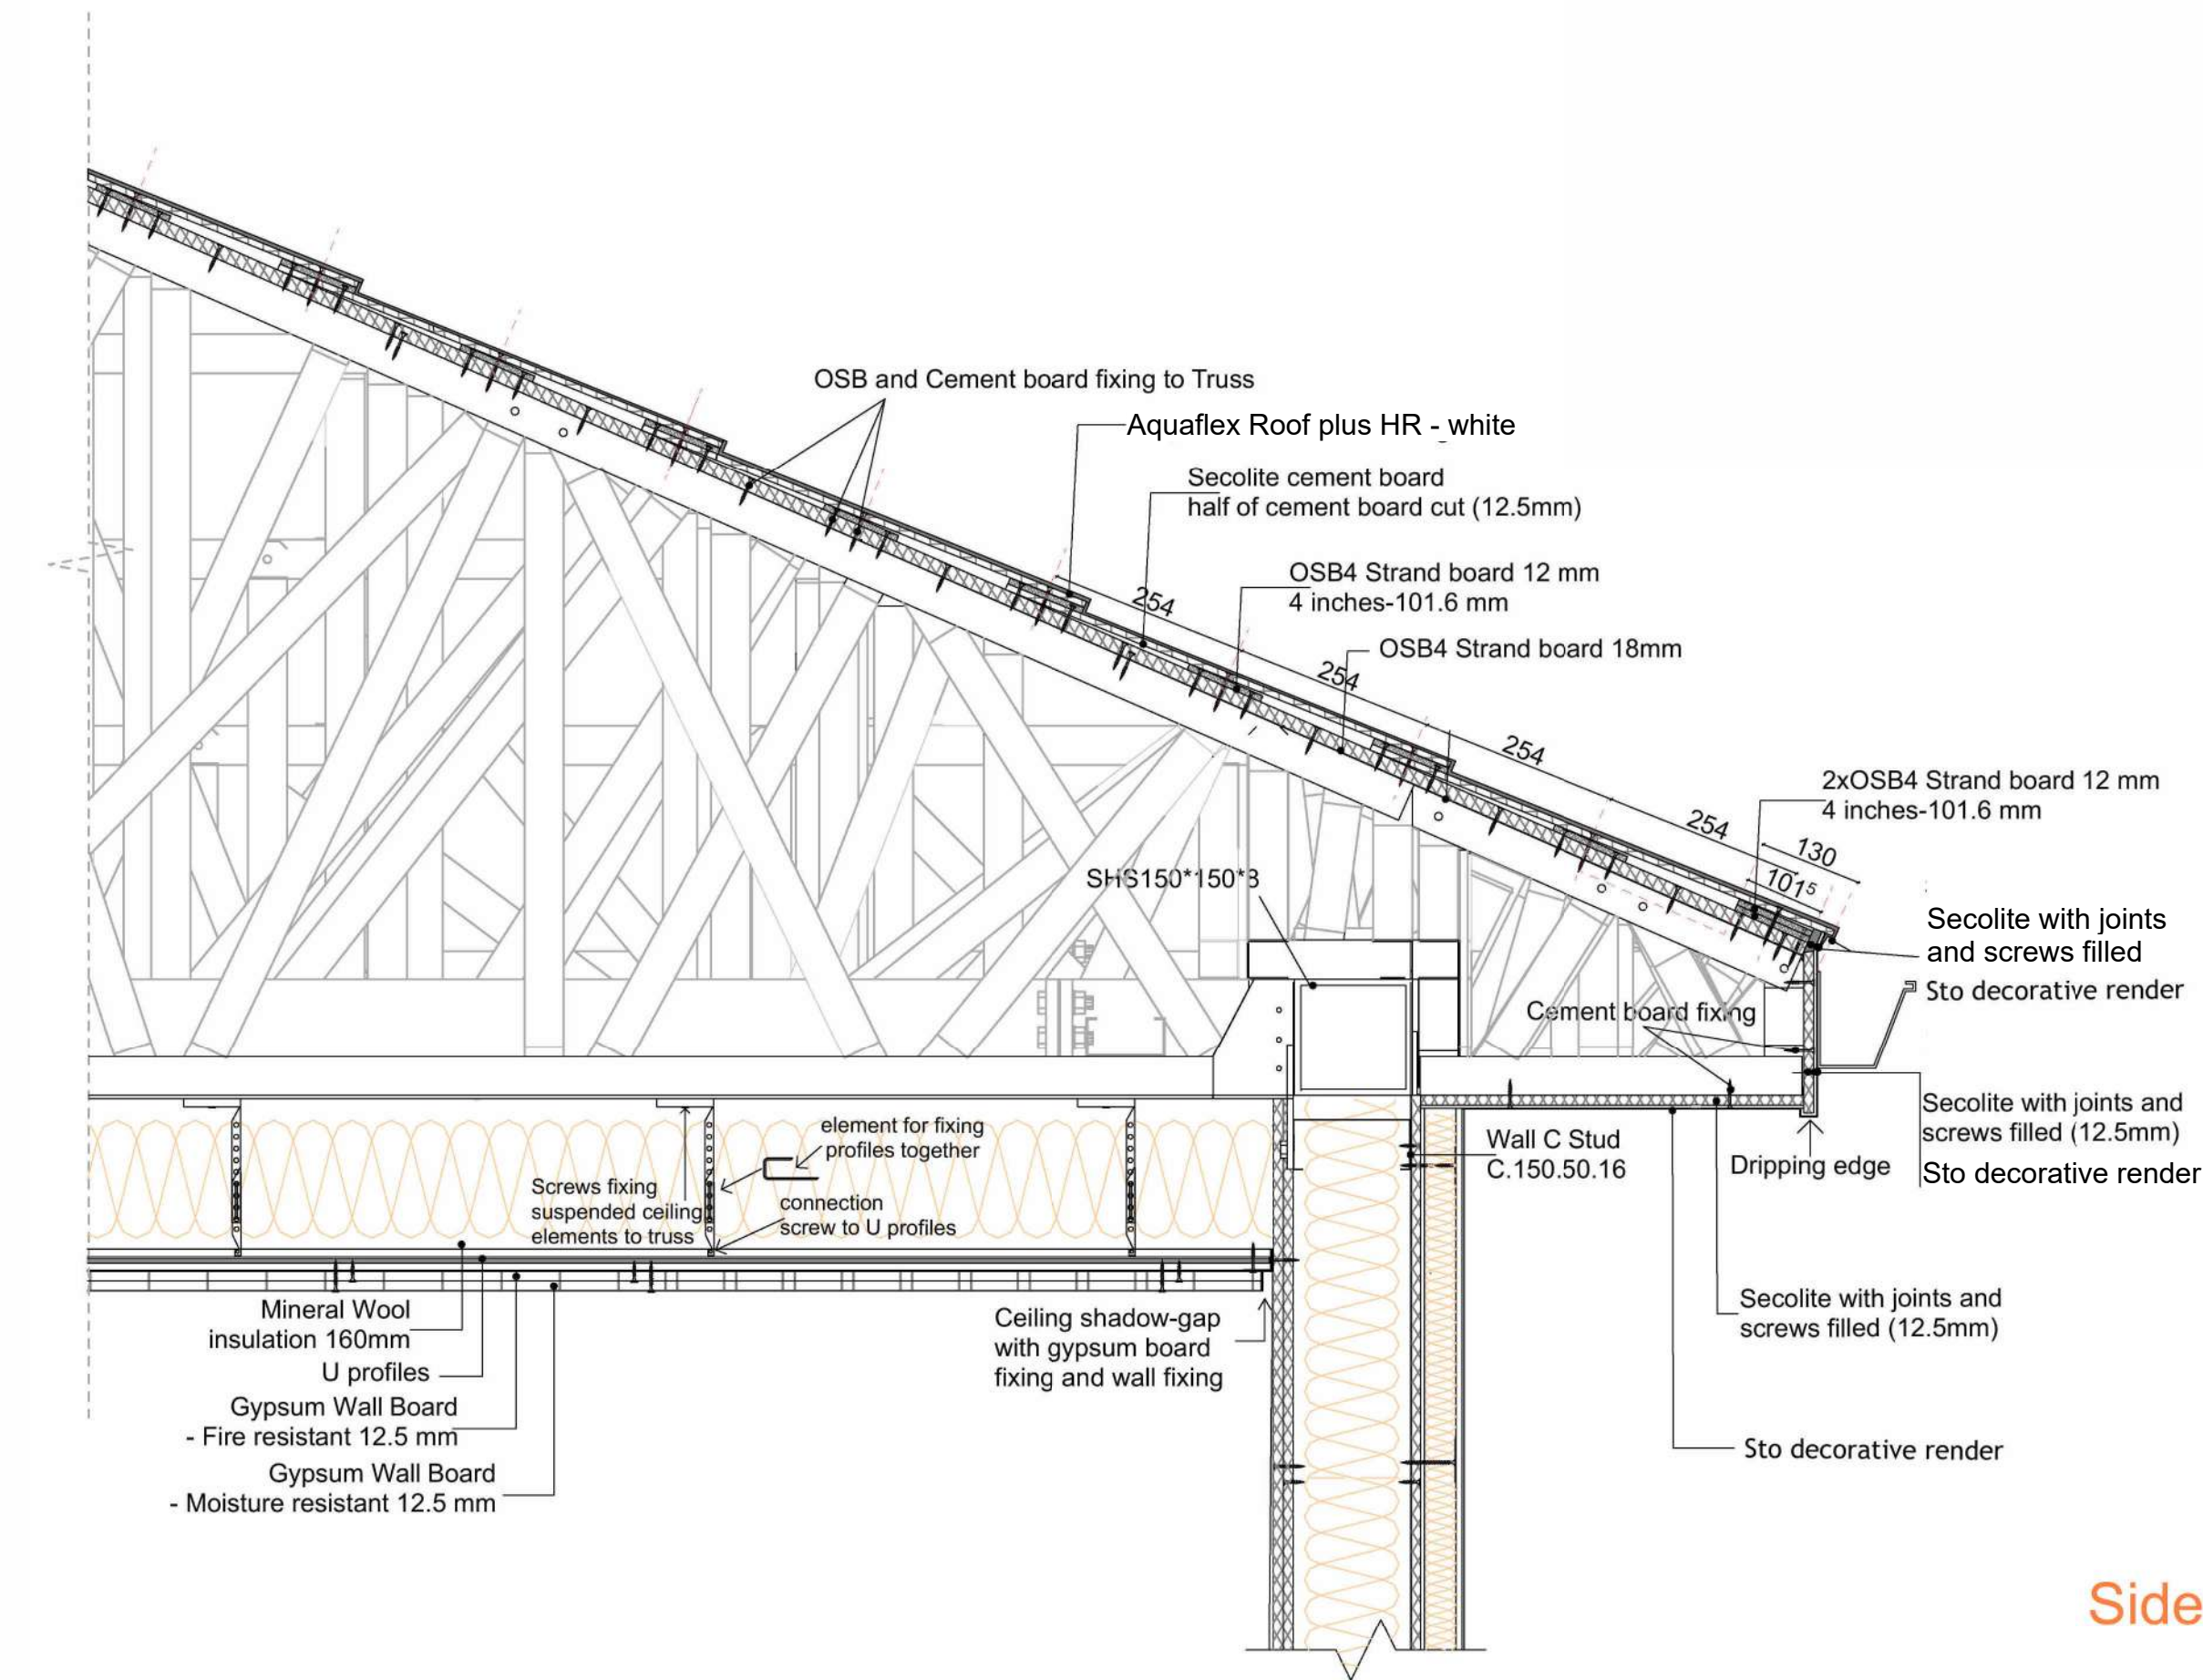

Side of proposed house

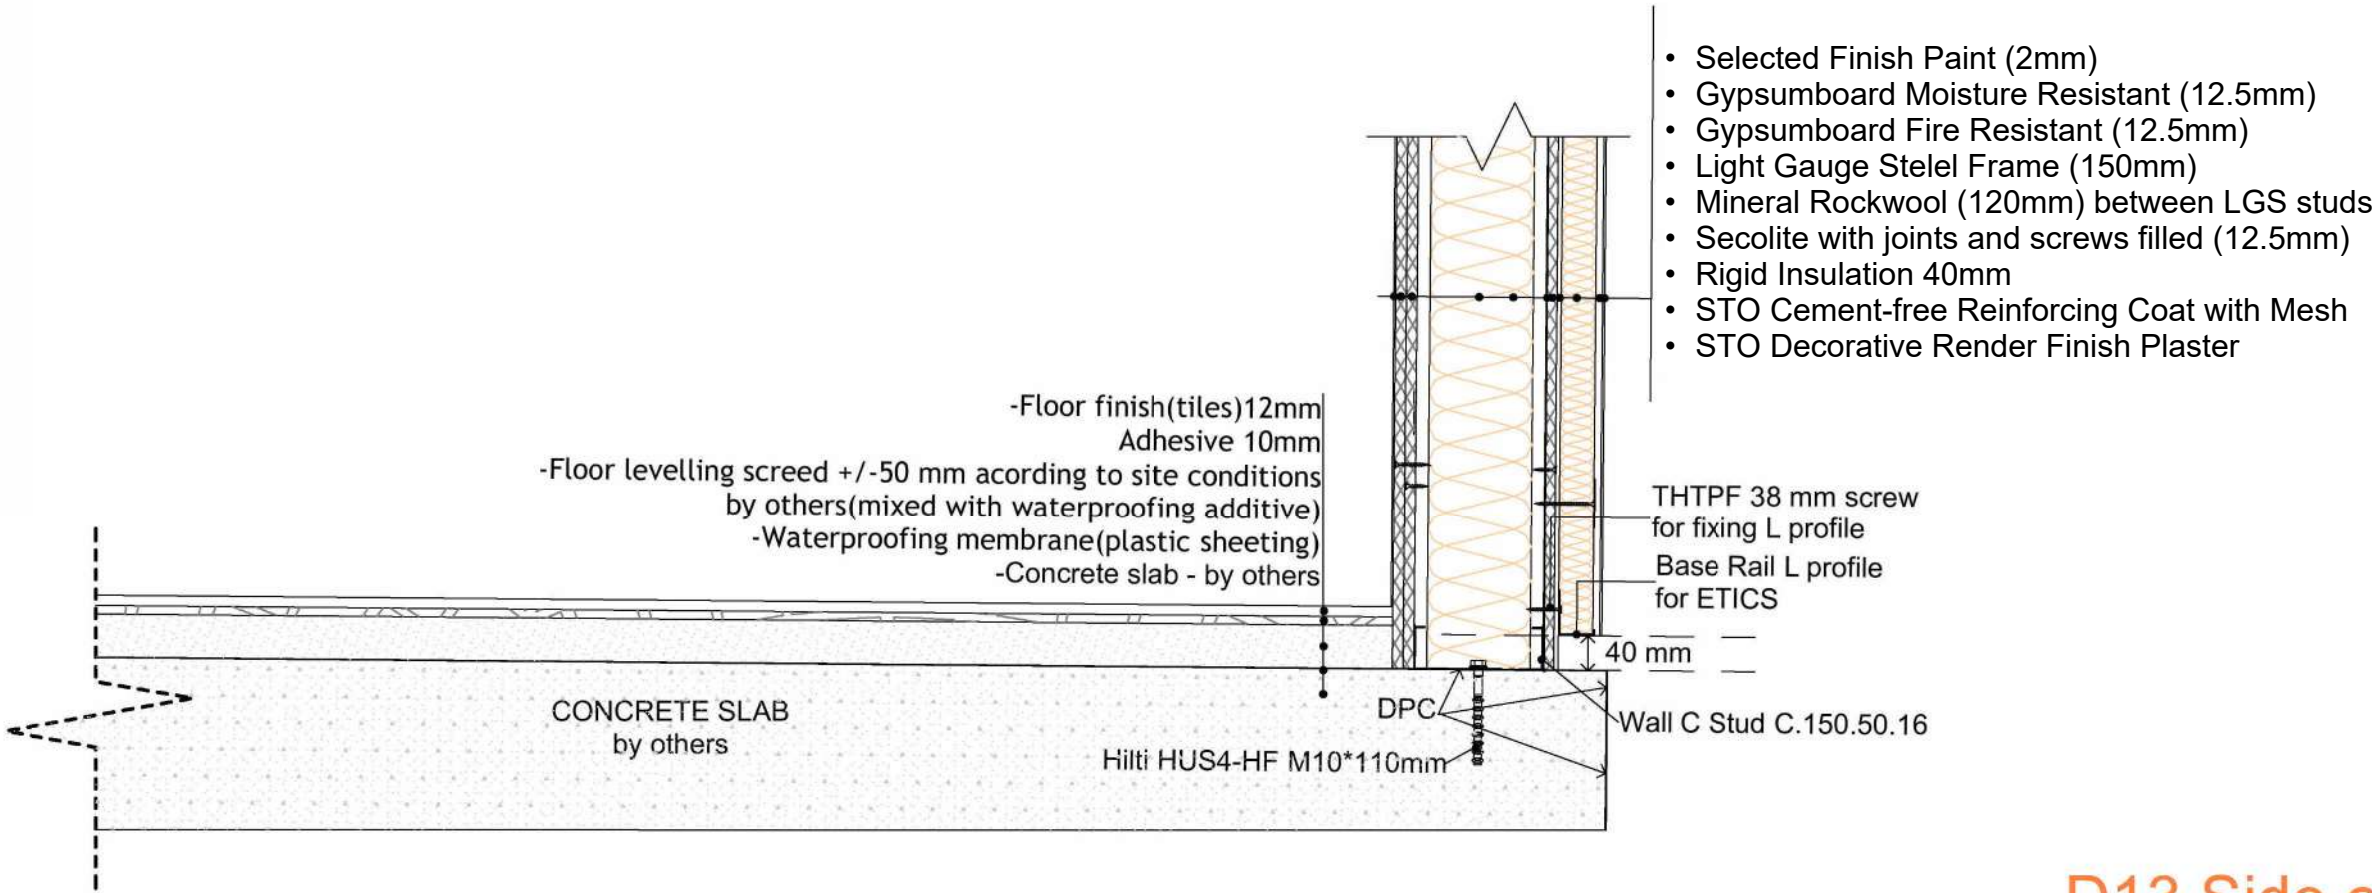

D13.Side of proposed house detail

1. THESE DRAWINGS MUST BE CHECKED BY THE CUSTOMER OR CONTRACTOR PRIOR TO APPROVAL. ANY ERRORS OR OMISSIONS MUST BE REPORTED IN WRITING TO BAUHU PRIOR TO COMMENCEMENT OF CONSTRUCTION.
2. ARCHITECTURAL DRAWINGS SHOULD BE READ IN CONJUNCTION WITH STRUCTURAL DETAILING AND FABRICATION GENERAL ASSEMBLY DRAWINGS.
3. FOR CONSTRUCTION PURPOSES, USE ONLY THE LATEST APPROVED DRAWINGS LABELED 'ISSUED FOR CONSTRUCTION'.
4. DO NOT SCALE FROM THIS DRAWING.
5. THE COMPANY OPERATES USING METRIC DIMENSIONS AS THE PRINCIPAL DENOMINATION.
6. ALL CONCRETE WORKS ARE OUTSIDE OF THE SCOPE OF THE COMPANY. INFORMATION REGARDING SLAB DESIGN AND CONNECTIONS IN THESE DRAWINGS ARE INTENDED FOR GUIDENCE ONLY. FOUNDATION AND SLAB WORKS SHOULD BE DESIGNED AND APPROVED BY A LOCAL STRUCTURAL ENGINEER.
7. THE COMPANY RETAINS FULL TITLE AND OWNERSHIP OF THESE PLANS AND DESIGNS. ANY UNAUTHORISED USE, REPRODUCTION, OR DISTRIBUTION OF THESE PLANS, WHETHER IN WHOLE OR PART, IS EXPRESSLY PROHIBITED WITHOUT PRIOR WRITTEN CONSENT.
8. THE INFORMATION CONTAINED WITHIN IS INTENDED TO BE AN AID FOR CONTRACTORS AND INSTALLERS AND IS NOT A SUBSTITUTE FOR PROFESSIONAL JUDGEMENT.

No.	Revision	Date

ISSUED FOR:

Issued for information

Issued for client approval

Issued for fabrication

Issued for construction

Caribbean
cottage


DRAWING TITLE: Details 8

DRAWN BY: Bernat Stefana


SCALE:

DRAWING NO: A36

DATE: 18.11.2025

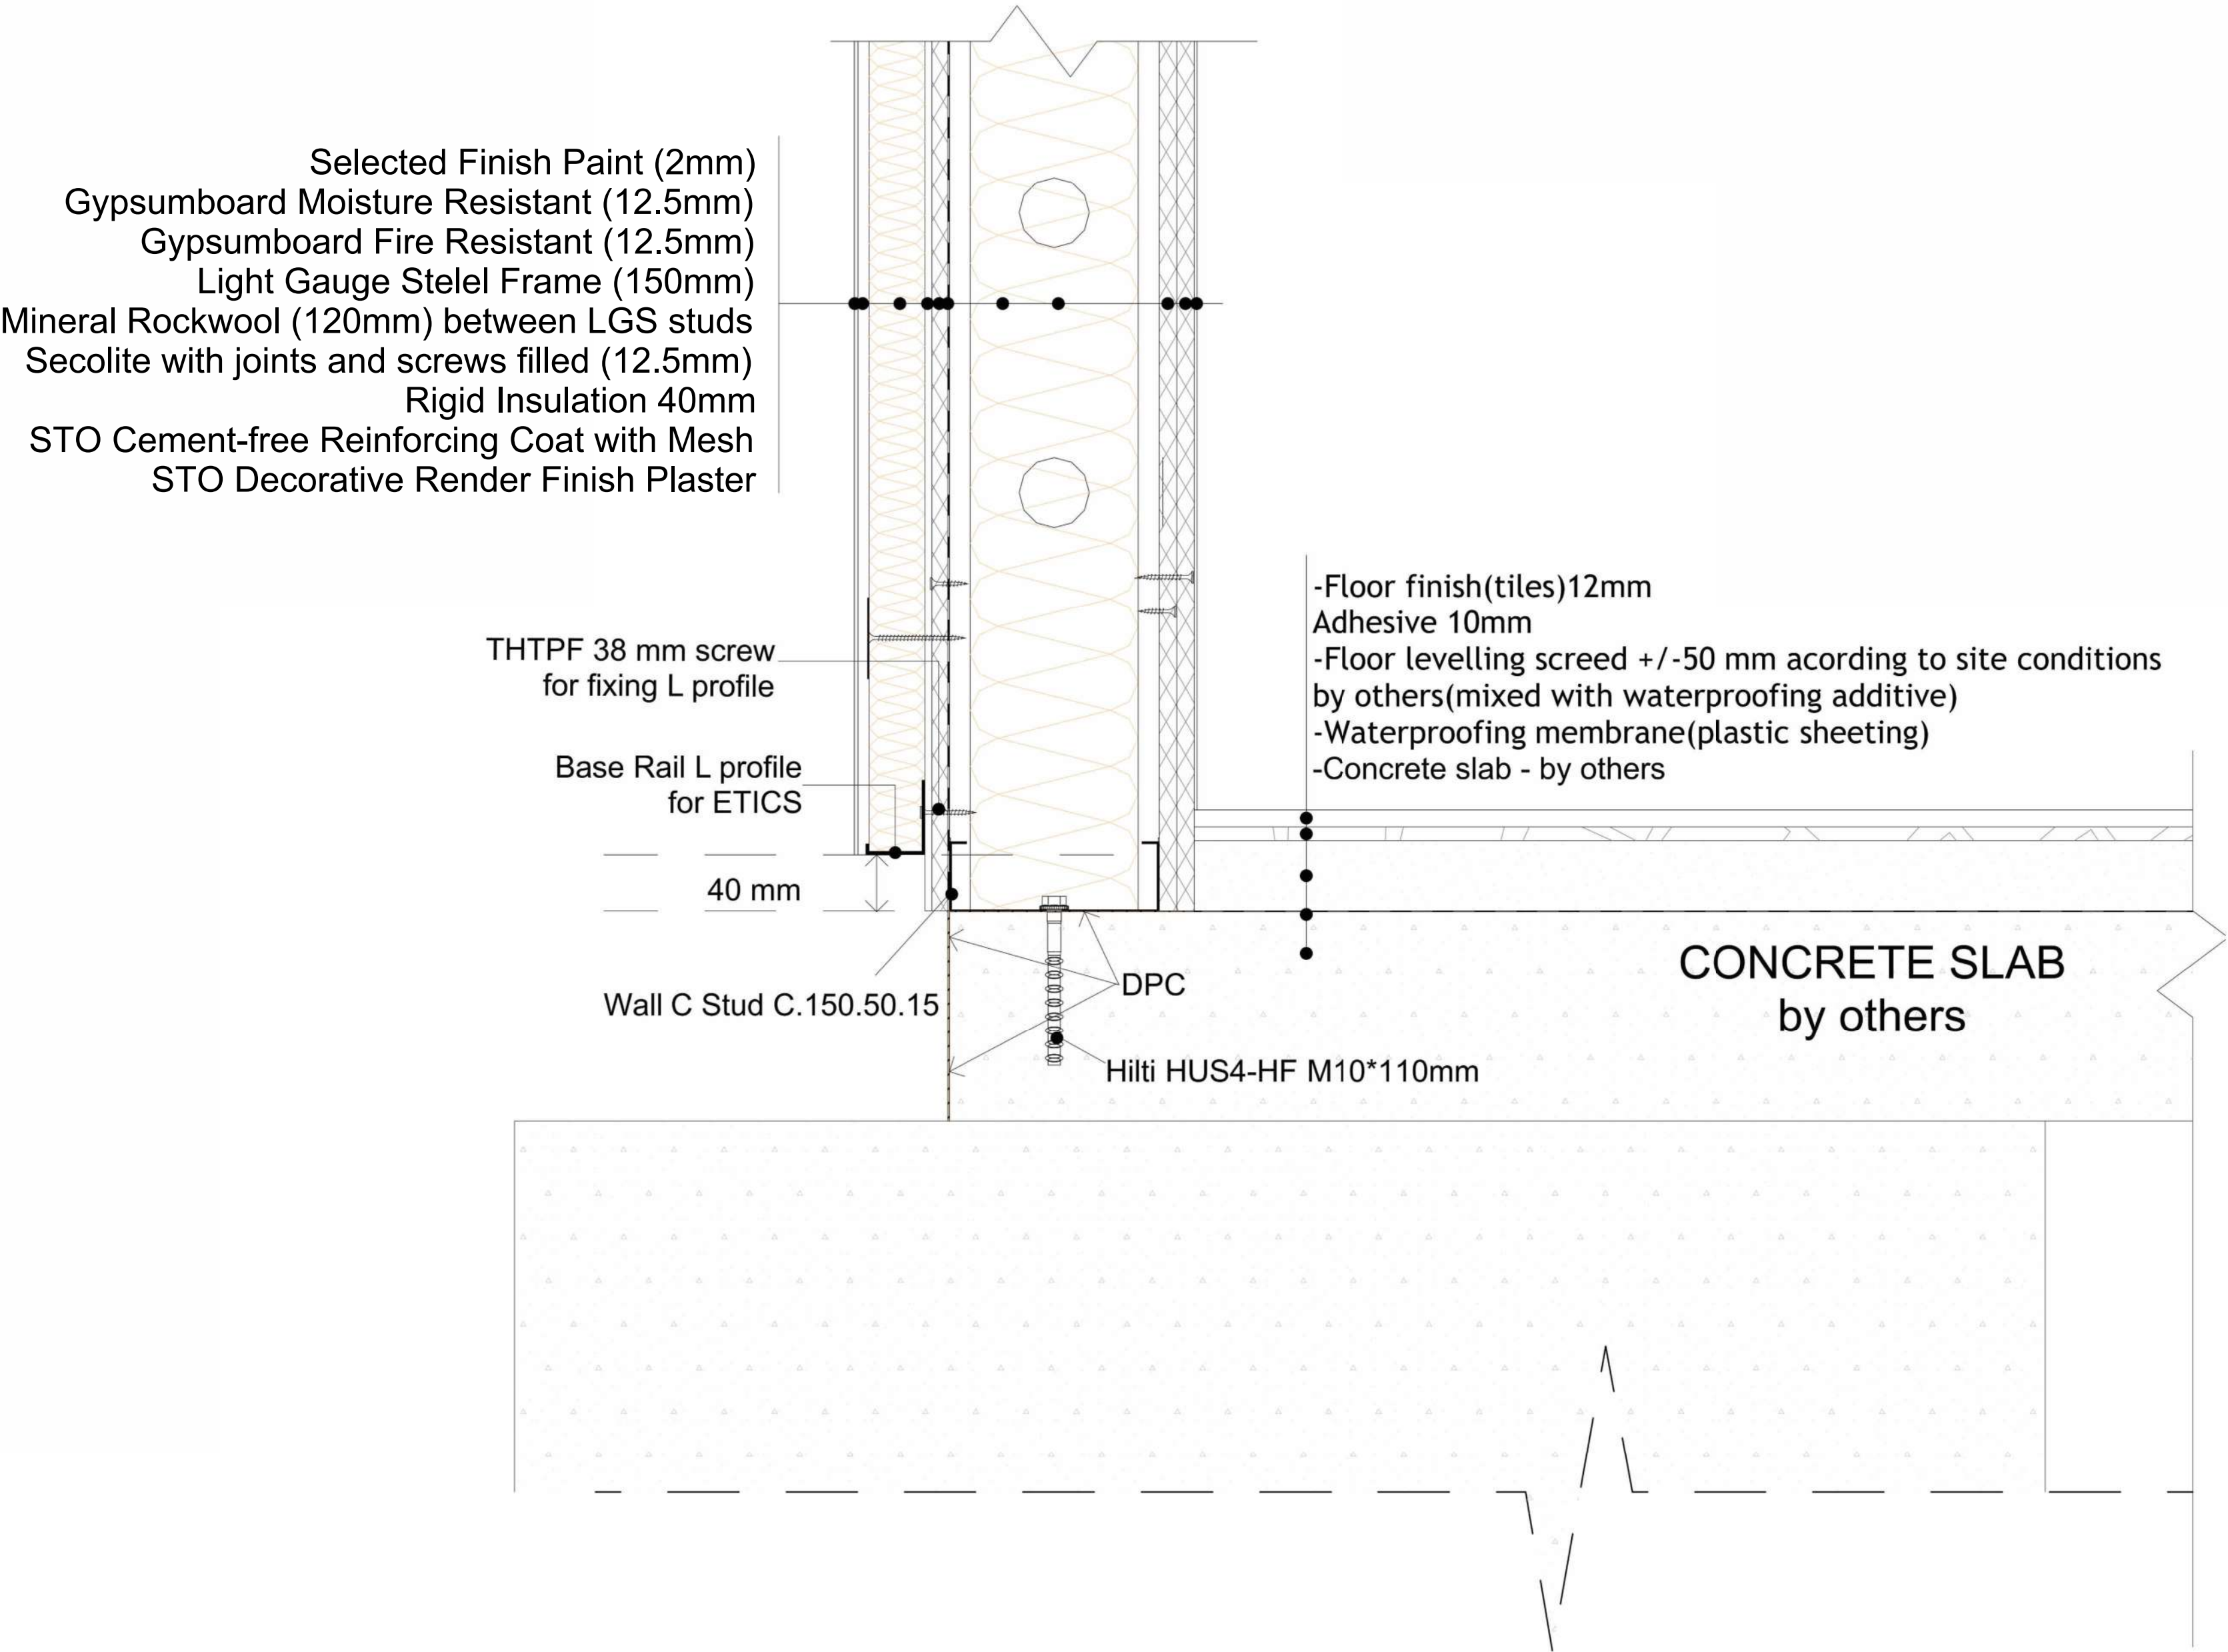

D14.Exterior wall base Detail

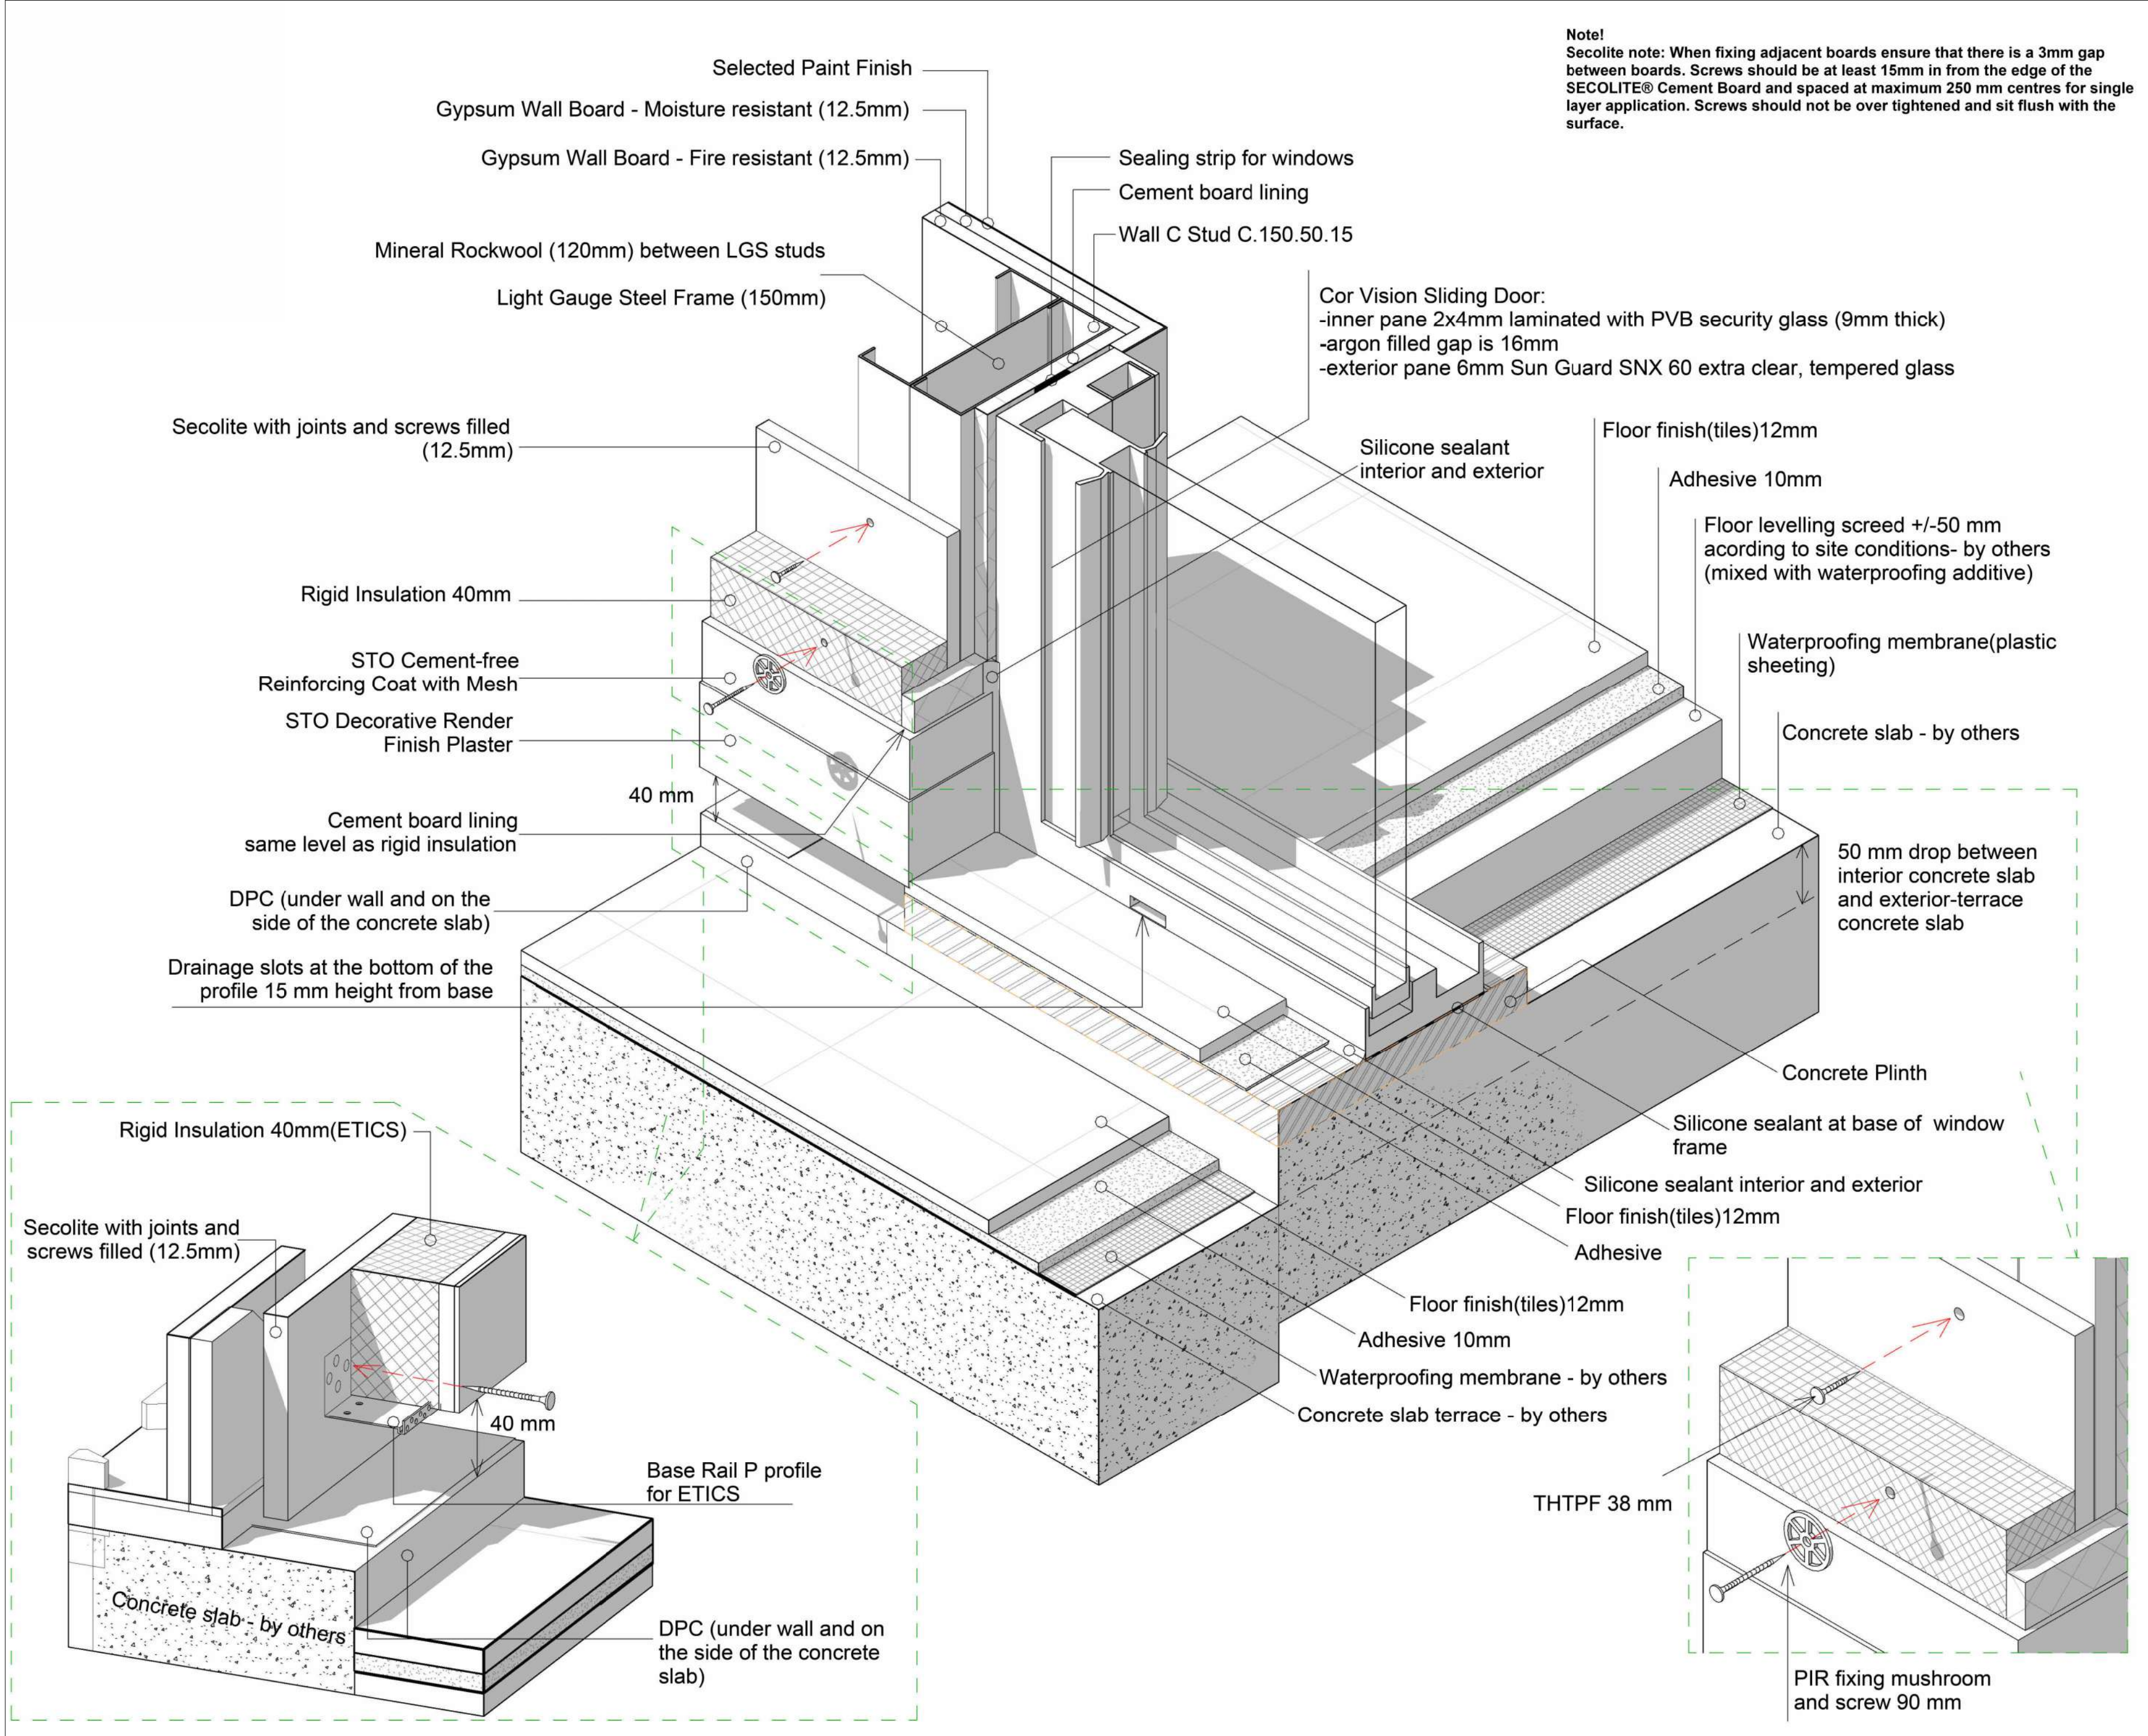

BAUHU

MODULAR • BUILDING • SOLUTIONS

1. THESE DRAWINGS MUST BE CHECKED BY THE CUSTOMER OR CONTRACTOR PRIOR TO APPROVAL. ANY ERRORS OR OMISSIONS MUST BE REPORTED IN WRITING TO BAUHU PRIOR TO COMMENCEMENT OF CONSTRUCTION.

2. ARCHITECTURAL DRAWINGS SHOULD BE READ IN CONJUNCTION WITH STRUCTURAL DETAILING AND FABRICATION GENERAL ASSEMBLY DRAWINGS.

3. FOR CONSTRUCTION PURPOSES, USE ONLY THE LATEST APPROVED DRAWINGS LABELED 'ISSUED FOR CONSTRUCTION'.

4. DO NOT SCALE FROM THIS DRAWING.

5. THE COMPANY OPERATES USING METRIC DIMENSIONS AS THE PRINCIPAL DENOMINATION.

6. ALL CONCRETE WORKS ARE OUTSIDE OF THE SCOPE OF THE COMPANY. INFORMATION REGARDING SLAB DESIGN AND CONNECTIONS IN THESE DRAWINGS ARE INTENDED FOR GUIDANCE ONLY. FOUNDATION AND SLAB WORKS SHOULD BE DESIGNED AND APPROVED BY A LOCAL STRUCTURAL ENGINEER.

7. THE COMPANY RETAINS FULL TITLE AND OWNERSHIP OF THESE PLANS AND DESIGNS. ANY UNAUTHORIZED USE, REPRODUCTION, OR DISTRIBUTION OF THESE PLANS, WHETHER IN WHOLE OR PART, IS EXPRESSLY PROHIBITED WITHOUT PRIOR WRITTEN CONSENT.

8. THE INFORMATION CONTAINED WITHIN IS INTENDED TO BE AN AID FOR CONTRACTORS AND INSTALLERS AND IS NOT A SUBSTITUTE FOR PROFESSIONAL JUDGEMENT.

No.	Revision	Date

ISSUED FOR:

Issued for information

Issued for client approval

Issued for fabrication

Issued for construction

Caribbean cottage

DRAWING TITLE:

3D detail

DRAWN BY:

Bernat Stefana

SCALE:

DRAWING NO:

A37

DATE:

18.11.2025

1. THESE DRAWINGS MUST BE CHECKED BY THE CUSTOMER OR CONTRACTOR PRIOR TO APPROVAL. ANY ERRORS OR OMISSIONS MUST BE REPORTED IN WRITING TO BAUHU PRIOR TO COMMENCEMENT OF CONSTRUCTION.
2. ARCHITECTURAL DRAWINGS SHOULD BE READ IN CONJUNCTION WITH STRUCTURAL DETAILING AND FABRICATION GENERAL ASSEMBLY DRAWINGS.
3. FOR CONSTRUCTION PURPOSES, USE ONLY THE LATEST APPROVED DRAWINGS LABELED 'ISSUED FOR CONSTRUCTION'.
4. DO NOT SCALE FROM THIS DRAWING.
5. THE COMPANY OPERATES USING METRIC DIMENSIONS AS THE PRINCIPAL DENOMINATION.
6. ALL CONCRETE WORKS ARE OUTSIDE OF THE SCOPE OF THE COMPANY. INFORMATION REGARDING SLAB DESIGN AND CONNECTIONS IN THESE DRAWINGS ARE INTENDED FOR GUIDENCE ONLY. FOUNDATION AND SLAB WORKS SHOULD BE DESIGNED AND APPROVED BY A LOCAL STRUCTURAL ENGINEER.
7. THE COMPANY RETAINS FULL TITLE AND OWNERSHIP OF THESE PLANS AND DESIGNS. ANY UNAUTHORISED USE, REPRODUCTION, OR DISTRIBUTION OF THESE PLANS, WHETHER IN WHOLE OR PART, IS EXPRESSLY PROHIBITED WITHOUT PRIOR WRITTEN CONSENT.
8. THE HYBRID STEEL FRAME CONSTRUCTION SYSTEM AND METHODOLOGY DESCRIBED IN THESE PLANS HAS BEEN DEVELOPED BY THE COMPANY AND IS SUBJECT TO A PATENT APPLICATION & ASSIGNMENT
US APPLICATION NO. 63/722,841

No.	Revision	Date

ISSUED FOR:

Issued for information

Issued for client approval

Issued for fabrication

Issued for construction

Caribbean cottage

DRAWING TITLE:

Room Legend

DRAWN BY:

Bernat Stefana

SCALE:


1 : 50

DRAWING NO:

A38

DATE:

18.11.2025

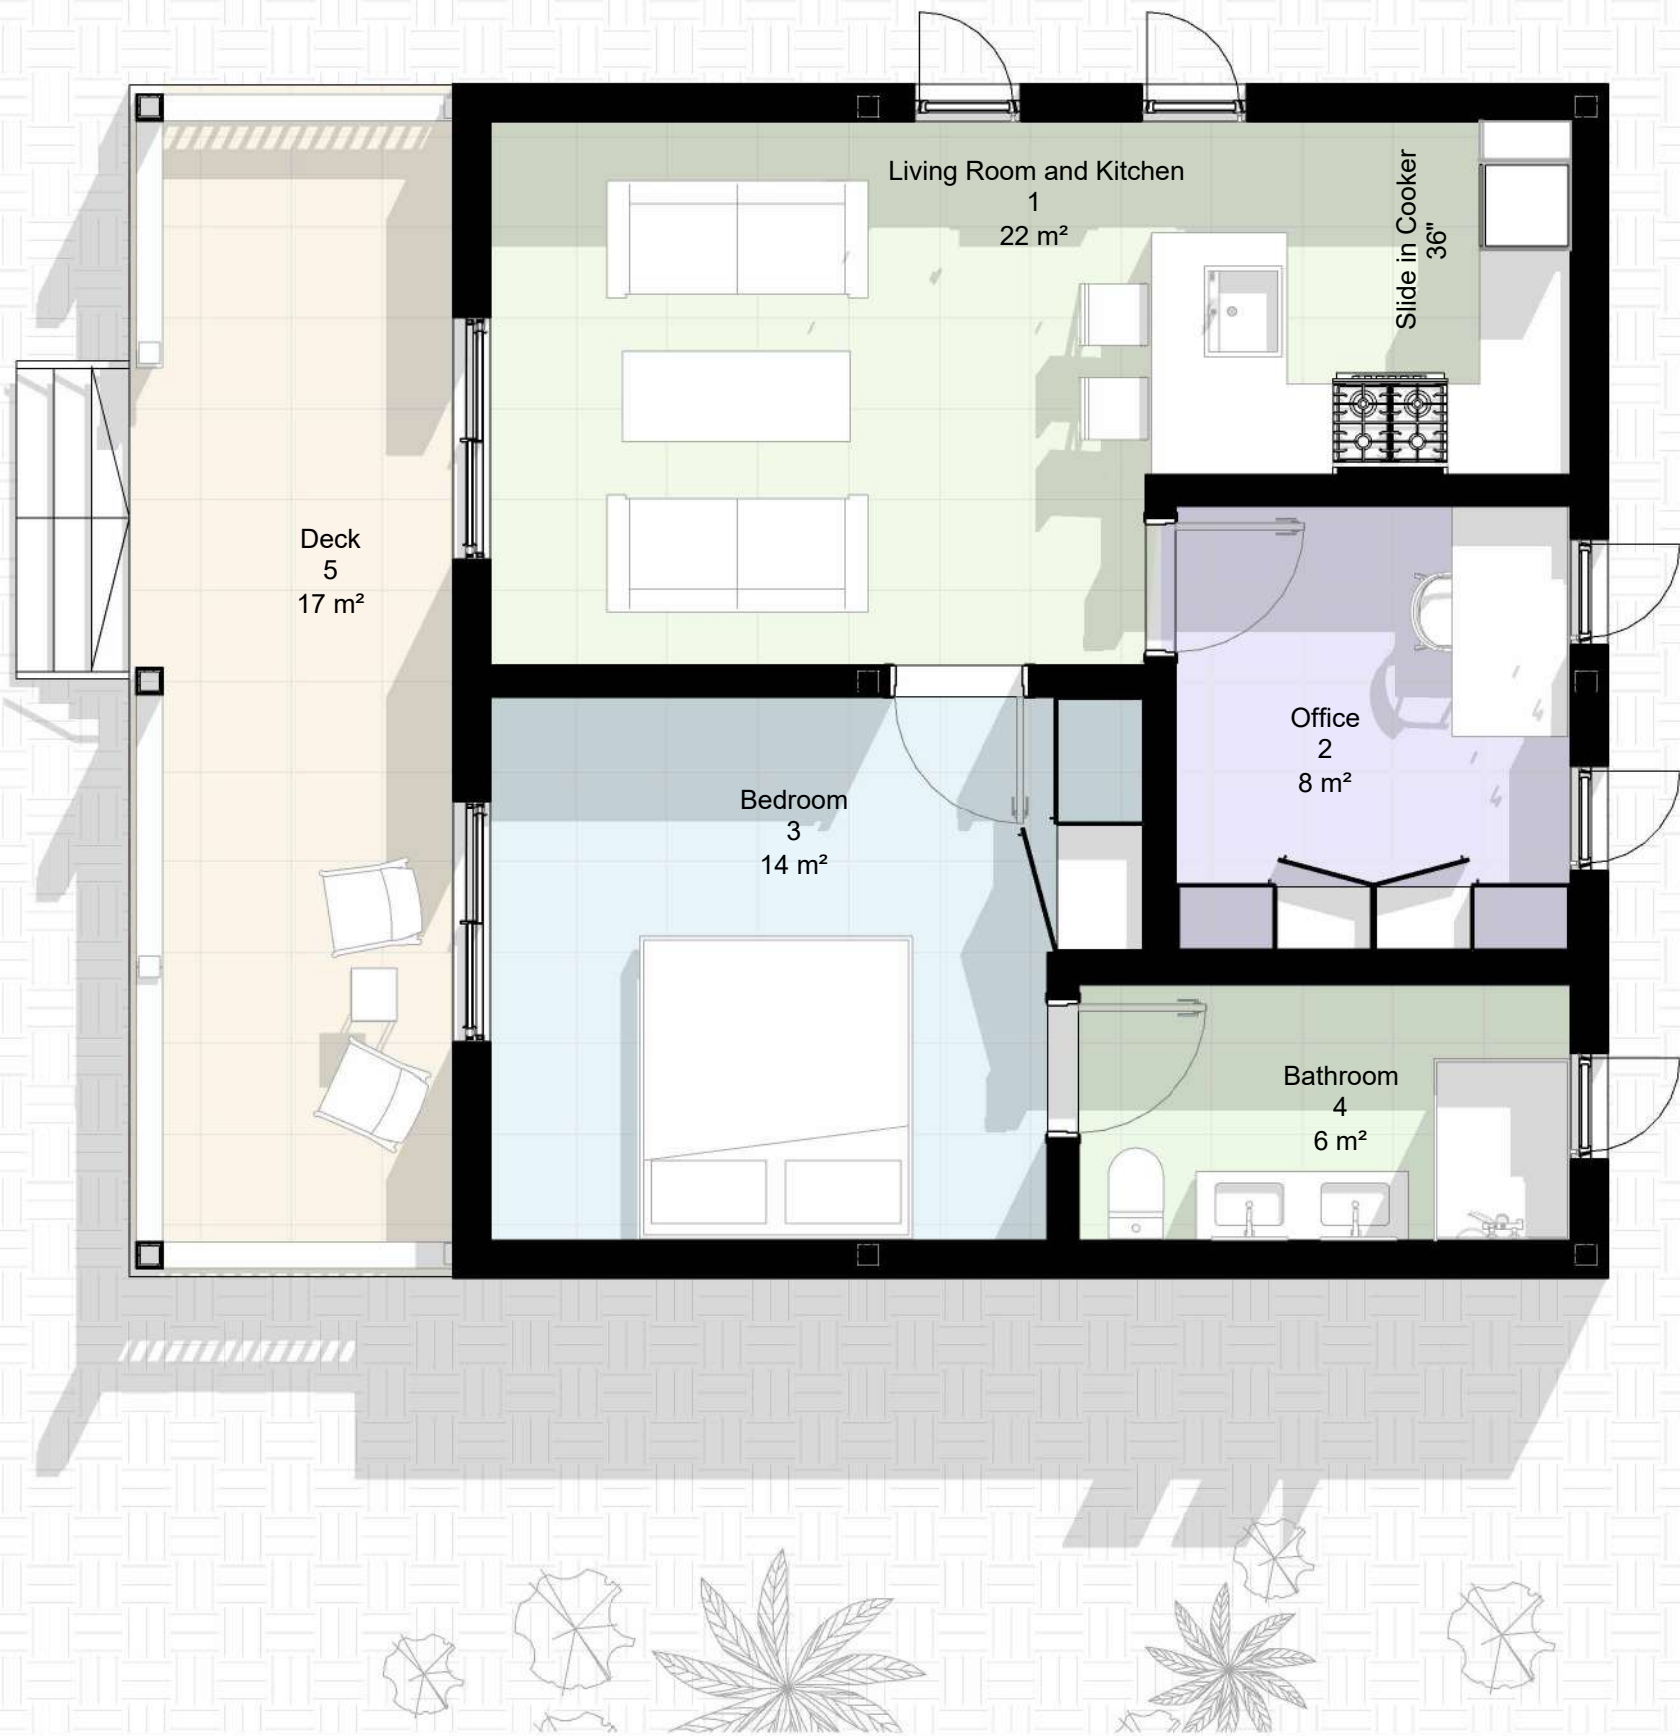

Room legend

1 : 50

Room Schedule I

No.	Room Name	Sq. Meter	Sq. Feet	Perimeter
1	Living Room and Kitchen	22 m²	239.4 ft²	21568
2	Office	8 m²	83.2 ft²	11141
3	Bedroom	14 m²	154.8 ft²	15869
4	Bathroom	6 m²	59.4 ft²	9902
5	Deck	17 m²	180.2 ft²	20495
Grand total		67 m²	716.8 ft²	

Room Legend

Bathroom

Bedroom

Deck

Living Room and Kitchen

Office



1. THESE DRAWINGS MUST BE CHECKED BY THE CUSTOMER OR CONTRACTOR PRIOR TO APPROVAL. ANY ERRORS OR OMISSIONS MUST BE REPORTED IN WRITING TO BAUHU PRIOR TO COMMENCEMENT OF CONSTRUCTION.
2. ARCHITECTURAL DRAWINGS SHOULD BE READ IN CONJUNCTION WITH STRUCTURAL DETAILING AND FABRICATION GENERAL ASSEMBLY DRAWINGS.
3. FOR CONSTRUCTION PURPOSES, USE ONLY THE LATEST APPROVED DRAWINGS LABELED 'ISSUED FOR CONSTRUCTION'.
4. DO NOT SCALE FROM THIS DRAWING.
5. THE COMPANY OPERATES USING METRIC DIMENSIONS AS THE PRINCIPAL DENOMINATION.
6. ALL CONCRETE WORKS ARE OUTSIDE OF THE SCOPE OF THE COMPANY. INFORMATION REGARDING SLAB DESIGN AND CONNECTIONS IN THESE DRAWINGS ARE INTENDED FOR GUIDANCE ONLY. FOUNDATION AND SLAB WORKS SHOULD BE DESIGNED AND APPROVED BY A LOCAL STRUCTURAL ENGINEER.
7. THE COMPANY RETAINS FULL TITLE AND OWNERSHIP OF THESE PLANS AND DESIGNS. ANY UNAUTHORISED USE, REPRODUCTION, OR DISTRIBUTION OF THESE PLANS, WHETHER IN WHOLE OR PART, IS EXPRESSLY PROHIBITED WITHOUT PRIOR WRITTEN CONSENT.
8. THE HYBRID STEEL FRAME CONSTRUCTION SYSTEM AND METHODOLOGY DESCRIBED IN THESE PLANS HAS BEEN DEVELOPED BY THE COMPANY AND IS SUBJECT TO A PATENT APPLICATION & ASSIGNMENT
US APPLICATION NO. 63/722,841

[illegible]

ISSUED FOR:

Issued for information

Issued for client approval

Issued for fabrication

Issued for construction

Caribbean cottage

DRAWING TITLE:

Schedules

DRAWN BY:

Bernat Stefana

SCALE:

DRAWING NO:

A39

DATE:

18.11.2025

Finishes Schedule										
No.	Room Name	Floor Area		Room Perimeter	Floor Finish		Ceiling Finish		Wall Finish	
		Sq.Meter	Sq. Feet		Grout Colour	Tiles	Ceiling Colour	Ceiling Height	Wall Colour	Wall Tile
Ground floor										
1	Living Room and Kitchen	22 m²	239.4 ft²	21568	Jasmine 130	Garland Pearl RL05	White #0501	2500	Marble Beige #1390	Garland Pearl RL05
2	Office	8 m²	83.2 ft²	11141	Jasmine 130	Garland Pearl RL05	White #0501	2500	Marble Beige #1390	x
3	Bedroom	14 m²	154.8 ft²	15869	Jasmine 130	Garland Pearl RL05	White #0501	2500	Marble Beige #1390	x
4	Bathroom	6 m²	59.4 ft²	9902	Jasmine 130	Garland Pearl RL05	White #0501	2500	Marble Beige #1390	Stella White & Stella Brick Blue
5	Deck	17 m²	180.2 ft²	20495	Jasmine 130	Garland Pearl RL05	Stolit K - white	2834	Stolit K - White	x
Grand total		67 m²	716.8 ft²	78973						

Ceiling Schedule			
Type	Area	Perimeter	Finish colour
Ceiling level			
Suspended	50 m ²	58356	White #0501
Ceiling Living Area			
Grand total	50 m ²	58356	

Wall Material Takeoff	
Room	Wall Area
EIFS, Exterior Insulation	74 m ²
Garland Pearl RL05	2 m ²
Gypsum Wall Board - Fire resistant	148 m ²
Gypsum Wall Board - Moisture resistant	148 m ²
Light Gauge Steel frame	111 m ²
Marble Beige #1390	148 m ²
Rigid insulation	111 m ²
Secolite skim coat with embedded mesh	74 m ²
Secolite with joints and screws filled	74 m ²
Stella Brick Blue	5 m ²
Stella White SA05R	3 m ²
STO Cement-free reinforcing coat	74 m ²
STO Decorative Render Finish Plaster	79 m ²
Vapour Barrier	111 m ²
Grand total	1162 m ²

Level Schedule		
Name	Elevation	Elevation (feet)
Building Height	4660	15.29'
Bottom of Truss	2819	9.25'
Ceiling level	2574	8.44'
Top of windows	2130	6.99'
Ground floor finish	74	0.24'
Ground floor	0	0.00'
Terrace finish	-28	-0.09'
Slab Terrace	-50	-0.16'
Terrain	-600	-1.97'

Roof Schedule			
Type	Material	Slope	Area
Roof	Aquaflex Plus - white		107 m²
Grand total			107 m²

Roof Soffit Schedule			
Type	Area	Perimeter	Level
Roof Soffit	39 m ²	71110	Bottom of Truss

Type	Width	Length	Area
BAU Exterior Wall	245	30082	74 m²
BAU Interior Wall	204	15953	37 m²
Column Wrap	13	1950	6 m²
Grand total		47985	116 m²

Room Schedule II				
No.	Room Name	Sq. Meter	Sq. Feet	Perimeter
1	Living Room and Kitchen	22 m ²	239.4 ft ²	21568
2	Office	8 m ²	83.2 ft ²	11141
3	Bedroom	14 m ²	154.8 ft ²	15869
4	Bathroom	6 m ²	59.4 ft ²	9902
5	Deck	17 m ²	180.2 ft ²	20495
Grand total		67 m ²	716.8 ft ²	

Door Schedule 2											
No	Type	Size		RO Size		Count	Opening Direction	Finishing	No of Leaves	Hinge Side	Lock
		Width	Height	RO Width	RO. Height						
D - 01	Interior Door 850 X 2100mm	850 mm	2100 mm	950	2145	3	3L	matt white	1	3L	Yes
Grand total						3					


Window Schedule II													
No	Type	Size		RO Size		Count	Opening Direction	Interior pane	Frame Finish	No of Leaves	Hinge Side	Lock	Insect screen
		Width	Height	RO. Width	RO. Height								
W-01	CORVISION Slider	1600 mm	2100	1634	2147	2	X	2R	Anthracite grey RAL 7016 matt	2	X	Yes	No
W-02	COR 70 - Casement - one sash	700 mm	1200	734	1234	5	5L	X	Anthracite grey RAL 7016 matt	1	5L	Yes	No
Grand total						7							

Shower Screen

Sanindusa
Model: Safira
Name: Safira shower panel
Reference: 8966002211
Finishes: 11-Chrome
Dimensions: 965Lx2000H mm
Count: 1

Support arm

Support arm for Cristal shower enclosure
Ref. 8A120011
Finishes: Chrome
Count: 1

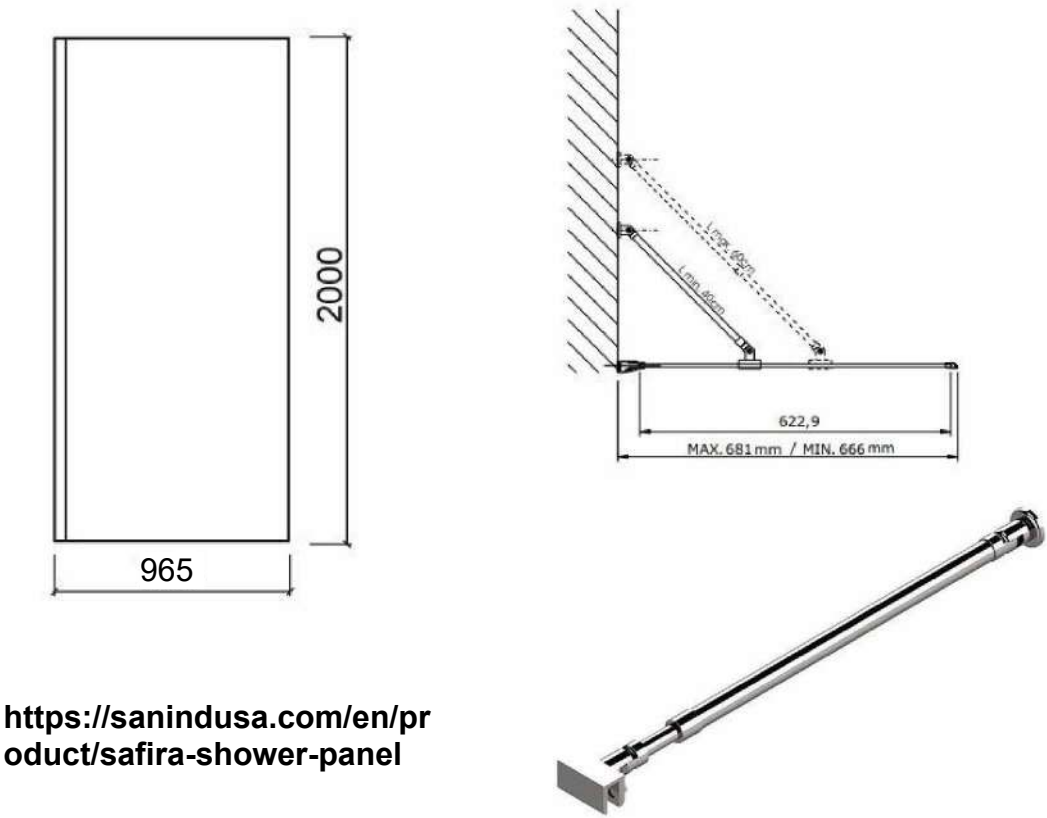

https://sanindusa.com/en/product/safira-shower-panel


Vanity Mixer

Bruma
Model: Nautic
Reference: 181 010 1CR
Finishes: Chrome
Count: 2

Mirror

Kitbanho
Model: Espelho Simples
Dimension: 50x80
Count: 2

https://www.bruma.pt/?page=products&prod=5426#open_product

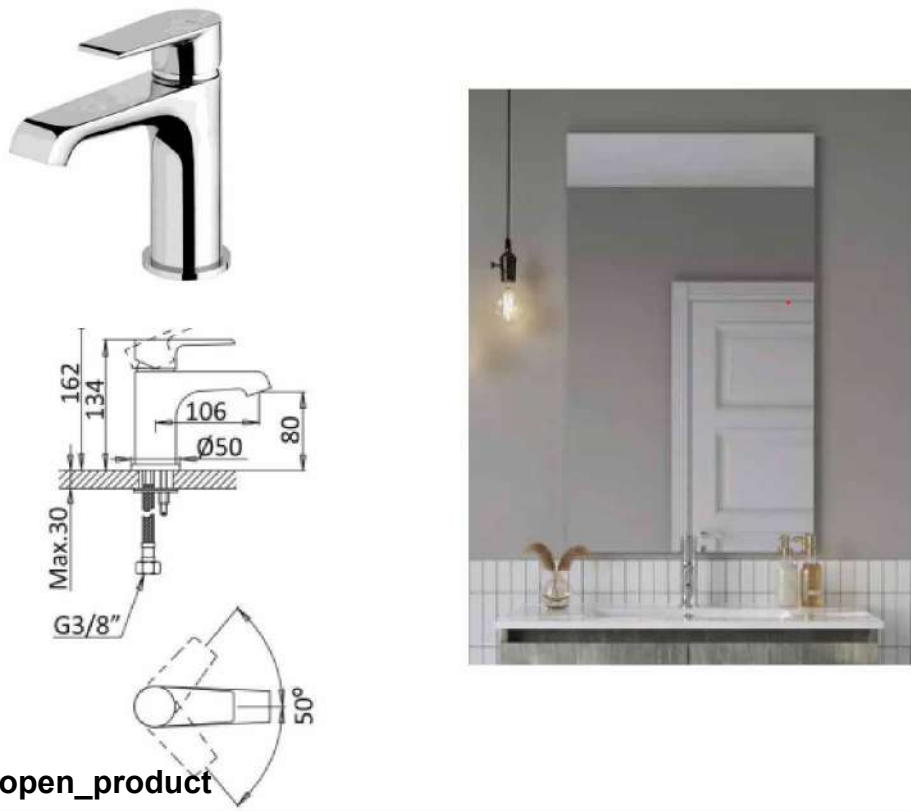

- THESE DRAWINGS MUST BE CHECKED BY THE CUSTOMER OR CONTRACTOR PRIOR TO APPROVAL. ANY ERRORS OR OMISSIONS MUST BE REPORTED IN WRITING TO BAUHU PRIOR TO COMMENCEMENT OF CONSTRUCTION.
- ARCHITECTURAL DRAWINGS SHOULD BE READ IN CONJUNCTION WITH STRUCTURAL DETAILING AND FABRICATION GENERAL ASSEMBLY DRAWINGS.
- FOR CONSTRUCTION PURPOSES, USE ONLY THE LATEST APPROVED DRAWINGS LABELED 'ISSUED FOR CONSTRUCTION'.
- DO NOT SCALE FROM THIS DRAWING.
- THE COMPANY OPERATES USING METRIC DIMENSIONS AS THE PRINCIPAL DENOMINATION.
- ALL CONCRETE WORKS ARE OUTSIDE OF THE SCOPE OF THE COMPANY. INFORMATION REGARDING SLAB DESIGN AND CONNECTIONS IN THESE DRAWINGS ARE INTENDED FOR GUIDENCE ONLY. FOUNDATION AND SLAB WORKS SHOULD BE DESIGNED AND APPROVED BY A LOCAL STRUCTURAL ENGINEER.
- THE COMPANY RETAINS FULL TITLE AND OWNERSHIP OF THESE PLANS AND DESIGNS. ANY UNAUTHORISED USE, REPRODUCTION, OR DISTRIBUTION OF THESE PLANS, WHETHER IN WHOLE OR PART, IS EXPRESSLY PROHIBITED WITHOUT PRIOR WRITTEN CONSENT.
- THE HYBRID STEEL FRAME CONSTRUCTION SYSTEM AND METHODOLOGY DESCRIBED IN THESE PLANS HAS BEEN DEVELOPED BY THE COMPANY AND IS SUBJECT TO A PATENT APPLICATION & ASSIGNMENT US APPLICATION NO. 63/722,841

Shower Tray

Sanindusa
Model: Piano
Name: Piano anti-slip rectangular shower tray
Reference: 8031500000
Finishes: white
Dimensions: 1203x903x75 mm
Count: 1
Features: Ø90mm waste with built-in trap not included




https://sanindusa.com/en/product/piano-antislip-rectangular-showertray

Washbasin

Kitbanho
Model: LAV. BANCA KLOSS STD ALT.10 - 140 D
Finishes: White Bright (glossy)
Dimensions: 1400mm
Count: 1


Bathroom Vanity Unit

Kitbanho
Model: OLIMPO ALT. 50 140 DD
Finishes: light grey
Dimensions: 1400mm
Count: 1

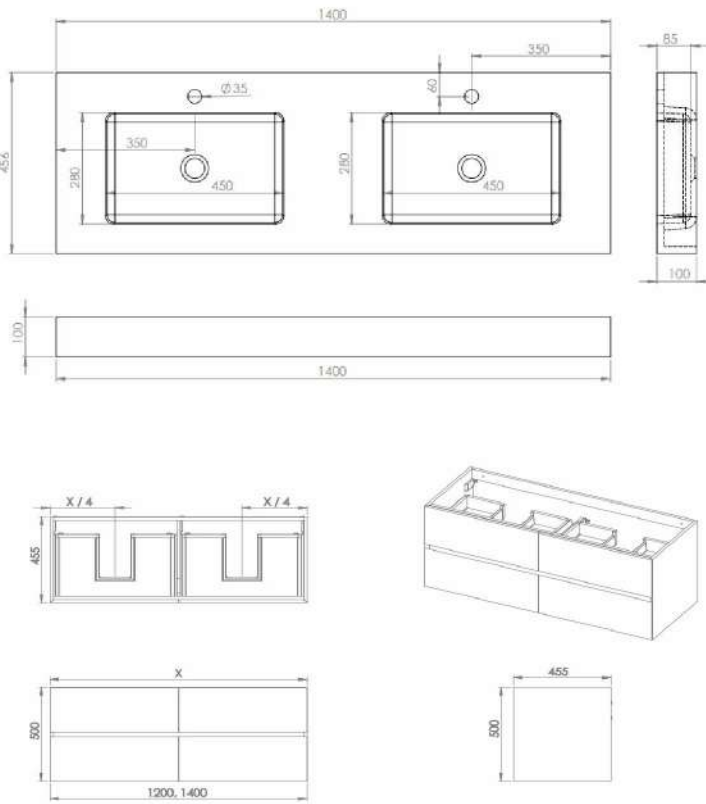

Shower System

Bruma
Model: Nautic
Name: Shower system with adjustable arm, Ø230mm ABS shower head and shower rail
Reference: 181 271 1CR
Finishes: Chrome
Count: 1

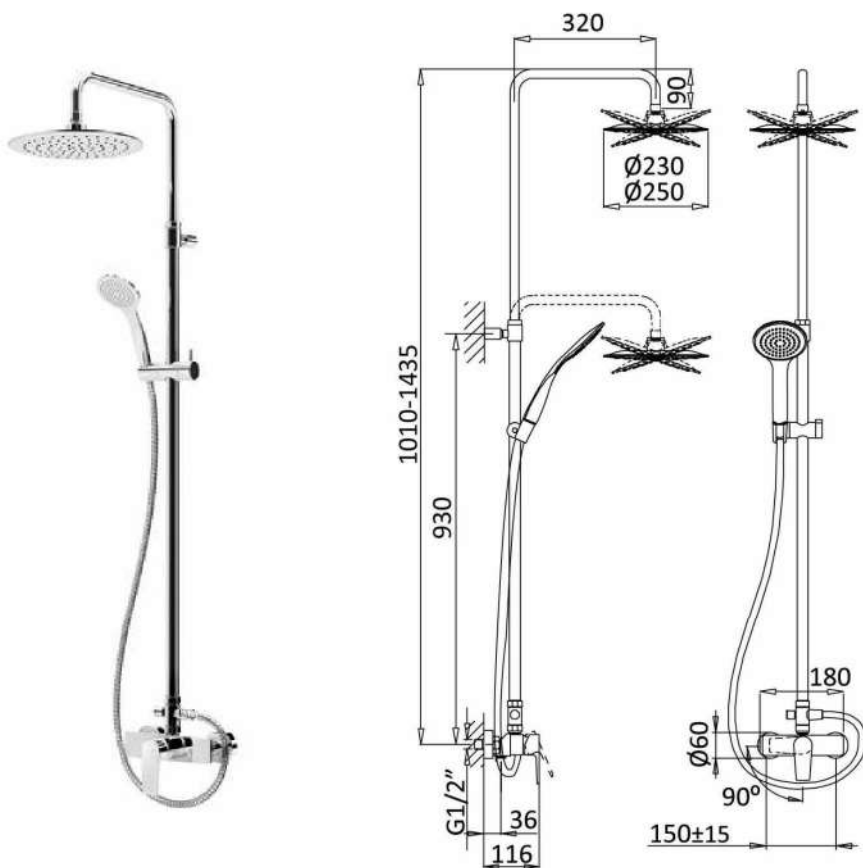

https://www.bruma.pt/?page=products&prod=4736#open_product


Toilet

Sanindusa
Model: Winner Confort FJD close coupled toilet
Reference: 144021
Dimensions: L65xW37xH47
Finishes: Vitreous China 00-White
Count: 1

Toilet Seat

Sanindusa
Model: Winner toilet seat with easyclip system
Reference: 24231
Finishes: Duroplast - 00-Chrome|White
Count: 1

https://www.tec.sanindusa.pt/winner-confort-fd-close-coupled-toilet

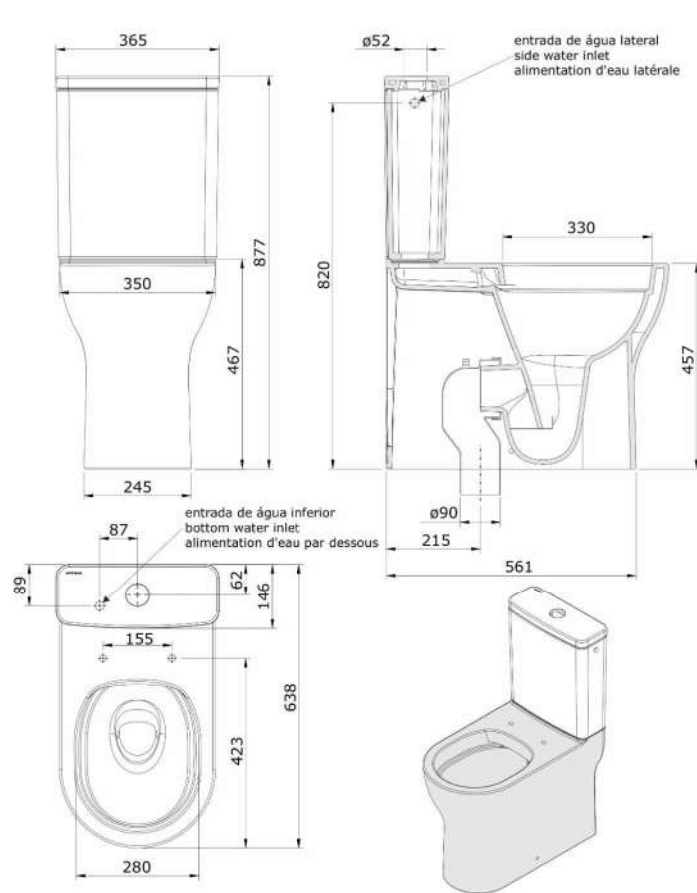

ISSUED FOR:

Issued for information

Issued for client approval

Issued for fabrication

Issued for construction

Caribbean cottage

DRAWING TITLE:

Bathroom Schedule

DRAWN BY:

Bernat Stefana

SCALE:


DRAWING NO:

A42


DATE:

18.11.2025


Note:
• Sanitary ware, faucets, kitchen and bathroom equipment are provided. Plumbing supply pipework, waste and sub-slab roughings are excluded. Plumbing plan is provided as a guide for contractor information only.
• Shower glass screens are fixed.

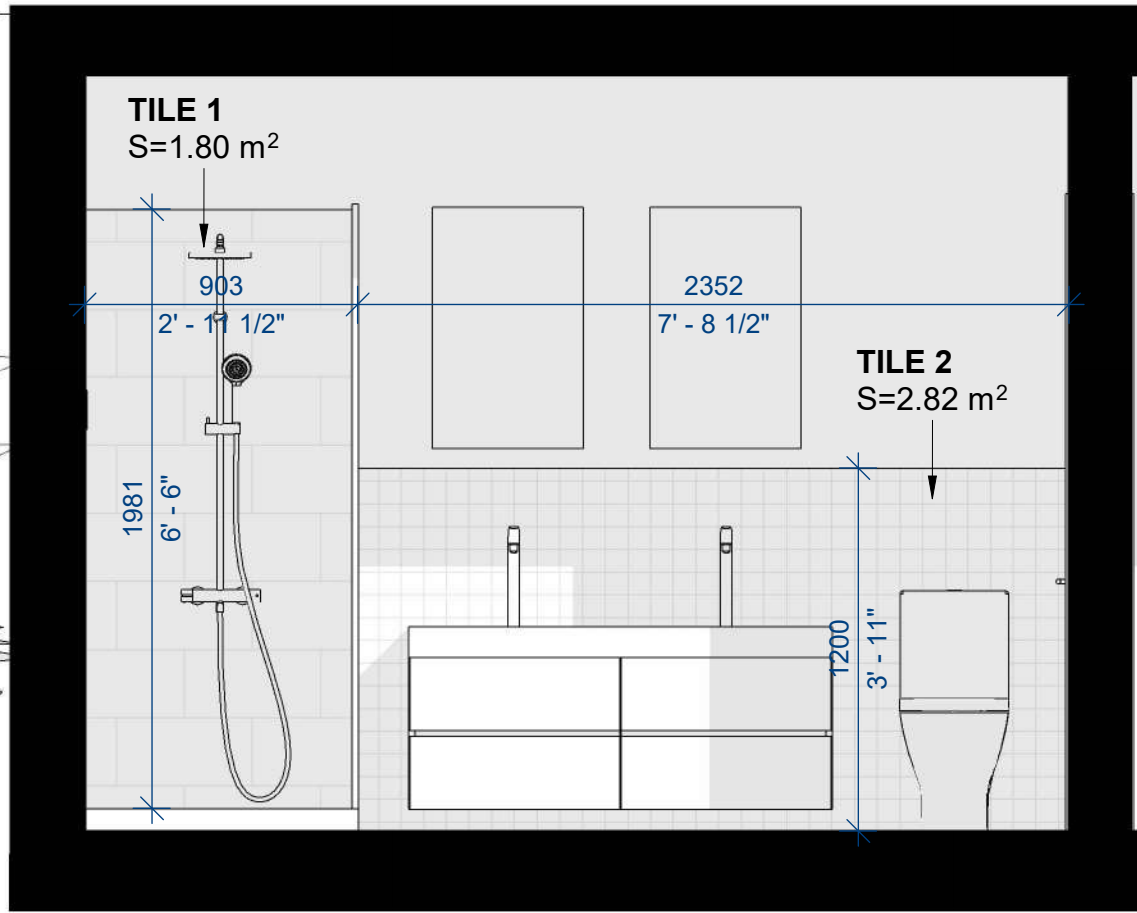

1 Bathroom - S1
1 : 25

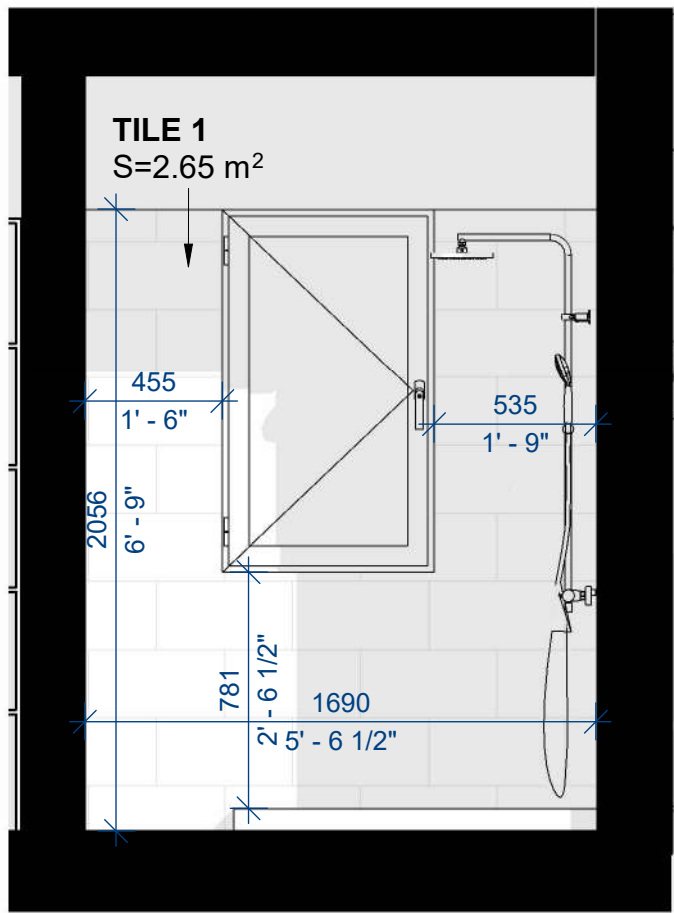

2 Bathroom - S2
1 : 25

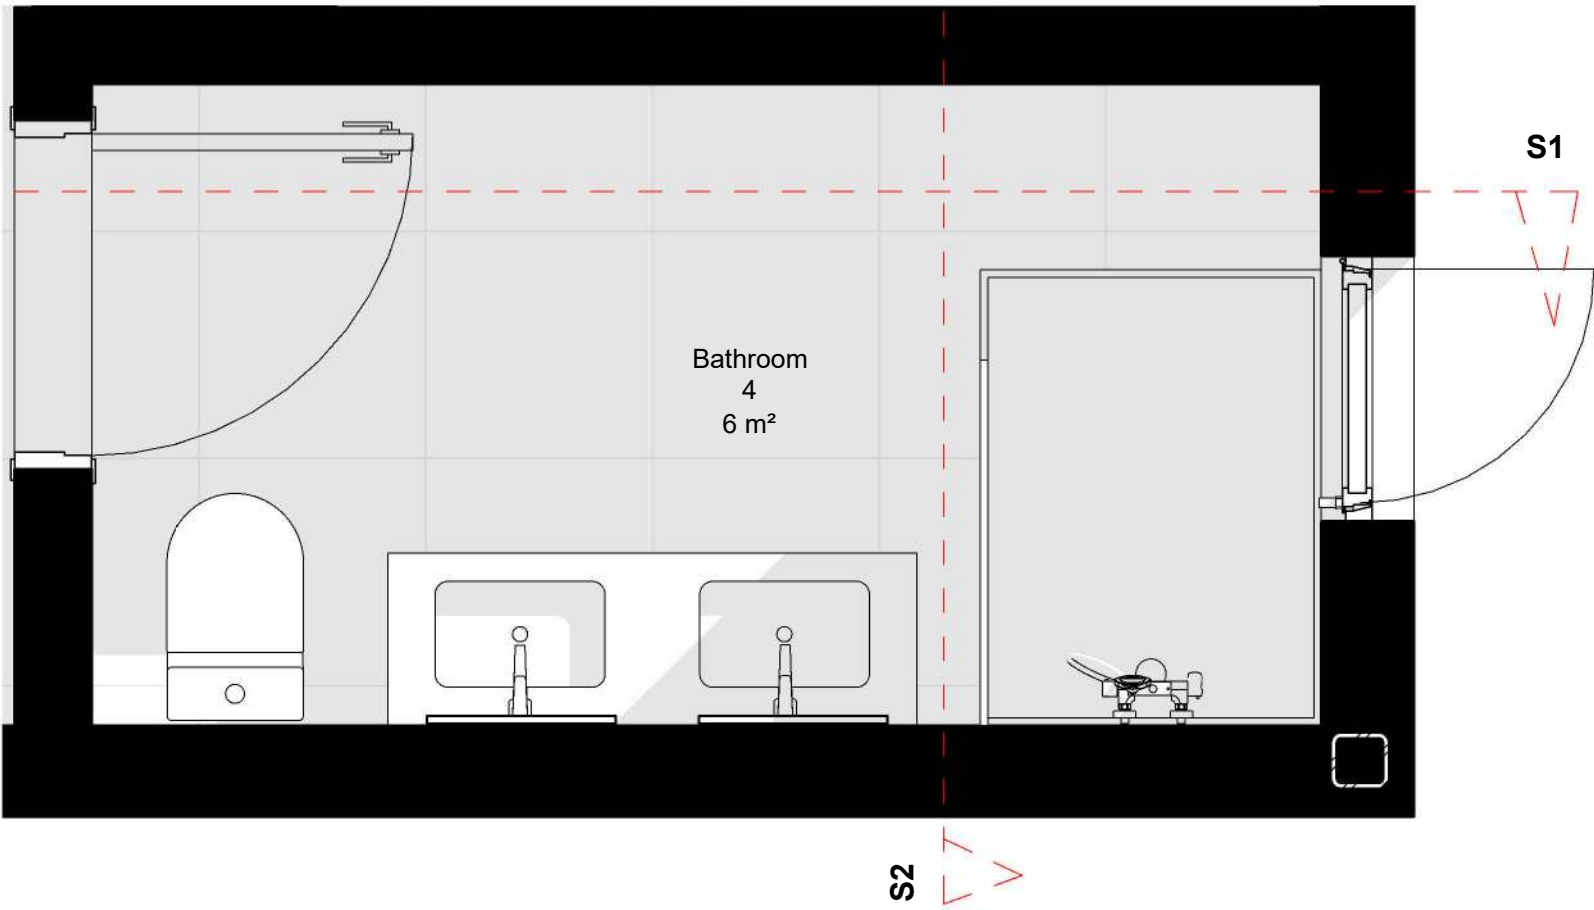

3 Bathroom plan
1 : 20

FINISHES

Floor Tiles

Garland Pearl RL05 - 45 x 45 cm . 18" x 18" / M15
45x45cm, Stone, Not Rectified
Glazed Porcelain Tiles, Mate



Grout Jasmine 130

Wall tiles

TILE 1

Stella White SA05R - 34 x 66,5 cm . 13,4" x 26,2" / R16
34x66,5cm, Cor, Não Rectificado
Revestimento Pasta Branca, Brilho



TILE 2

Stella Brick Blue SA53R - 34 x 66,5 cm . 13,4" x 26,2" / R17
Decorações 34x66,5cm, Cor, Não Rectificado
Revestimento Pasta Branca, Brilho



Grout White 100

Ceiling Colour

CIN
White #0501



Wall Colour

CIN
Marble Beige #1390



BAUHU
MODULAR • BUILDING • SOLUTIONS

- THESE DRAWINGS MUST BE CHECKED BY THE CUSTOMER OR CONTRACTOR PRIOR TO APPROVAL. ANY ERRORS OR OMISSIONS MUST BE REPORTED IN WRITING TO BAUHU PRIOR TO COMMENCEMENT OF CONSTRUCTION.
- ARCHITECTURAL DRAWINGS SHOULD BE READ IN CONJUNCTION WITH STRUCTURAL DETAILING AND FABRICATION GENERAL ASSEMBLY DRAWINGS.
- FOR CONSTRUCTION PURPOSES, USE ONLY THE LATEST APPROVED DRAWINGS LABELED 'ISSUED FOR CONSTRUCTION'.
- DO NOT SCALE FROM THIS DRAWING.
- THE COMPANY OPERATES USING METRIC DIMENSIONS AS THE PRINCIPAL DENOMINATION.
- ALL CONCRETE WORKS ARE OUTSIDE OF THE SCOPE OF THE COMPANY. INFORMATION REGARDING SLAB DESIGN AND CONNECTIONS IN THESE DRAWINGS ARE INTENDED FOR GUIDANCE ONLY. FOUNDATION AND SLAB WORKS SHOULD BE DESIGNED AND APPROVED BY A LOCAL STRUCTURAL ENGINEER.
- THE COMPANY RETAINS FULL TITLE AND OWNERSHIP OF THESE PLANS AND DESIGNS. ANY UNAUTHORISED USE, REPRODUCTION, OR DISTRIBUTION OF THESE PLANS, WHETHER IN WHOLE OR PART, IS EXPRESSLY PROHIBITED WITHOUT PRIOR WRITTEN CONSENT.
- THE HYBRID STEEL FRAME CONSTRUCTION SYSTEM AND METHODOLOGY DESCRIBED IN THESE PLANS HAS BEEN DEVELOPED BY THE COMPANY AND IS SUBJECT TO A PATENT APPLICATION & ASSIGNMENT US APPLICATION NO. 63/722,841

No.	Revision	Date

ISSUED FOR:

Issued for information

Issued for client approval

Issued for fabrication

Issued for construction

Caribbean cottage

DRAWING TITLE:

Bathroom

DRAWN BY:

Bernat Stefana

SCALE:

As indicated

DRAWING NO:





A43

DATE:

18.11.2025



4 Bathroom 3D view

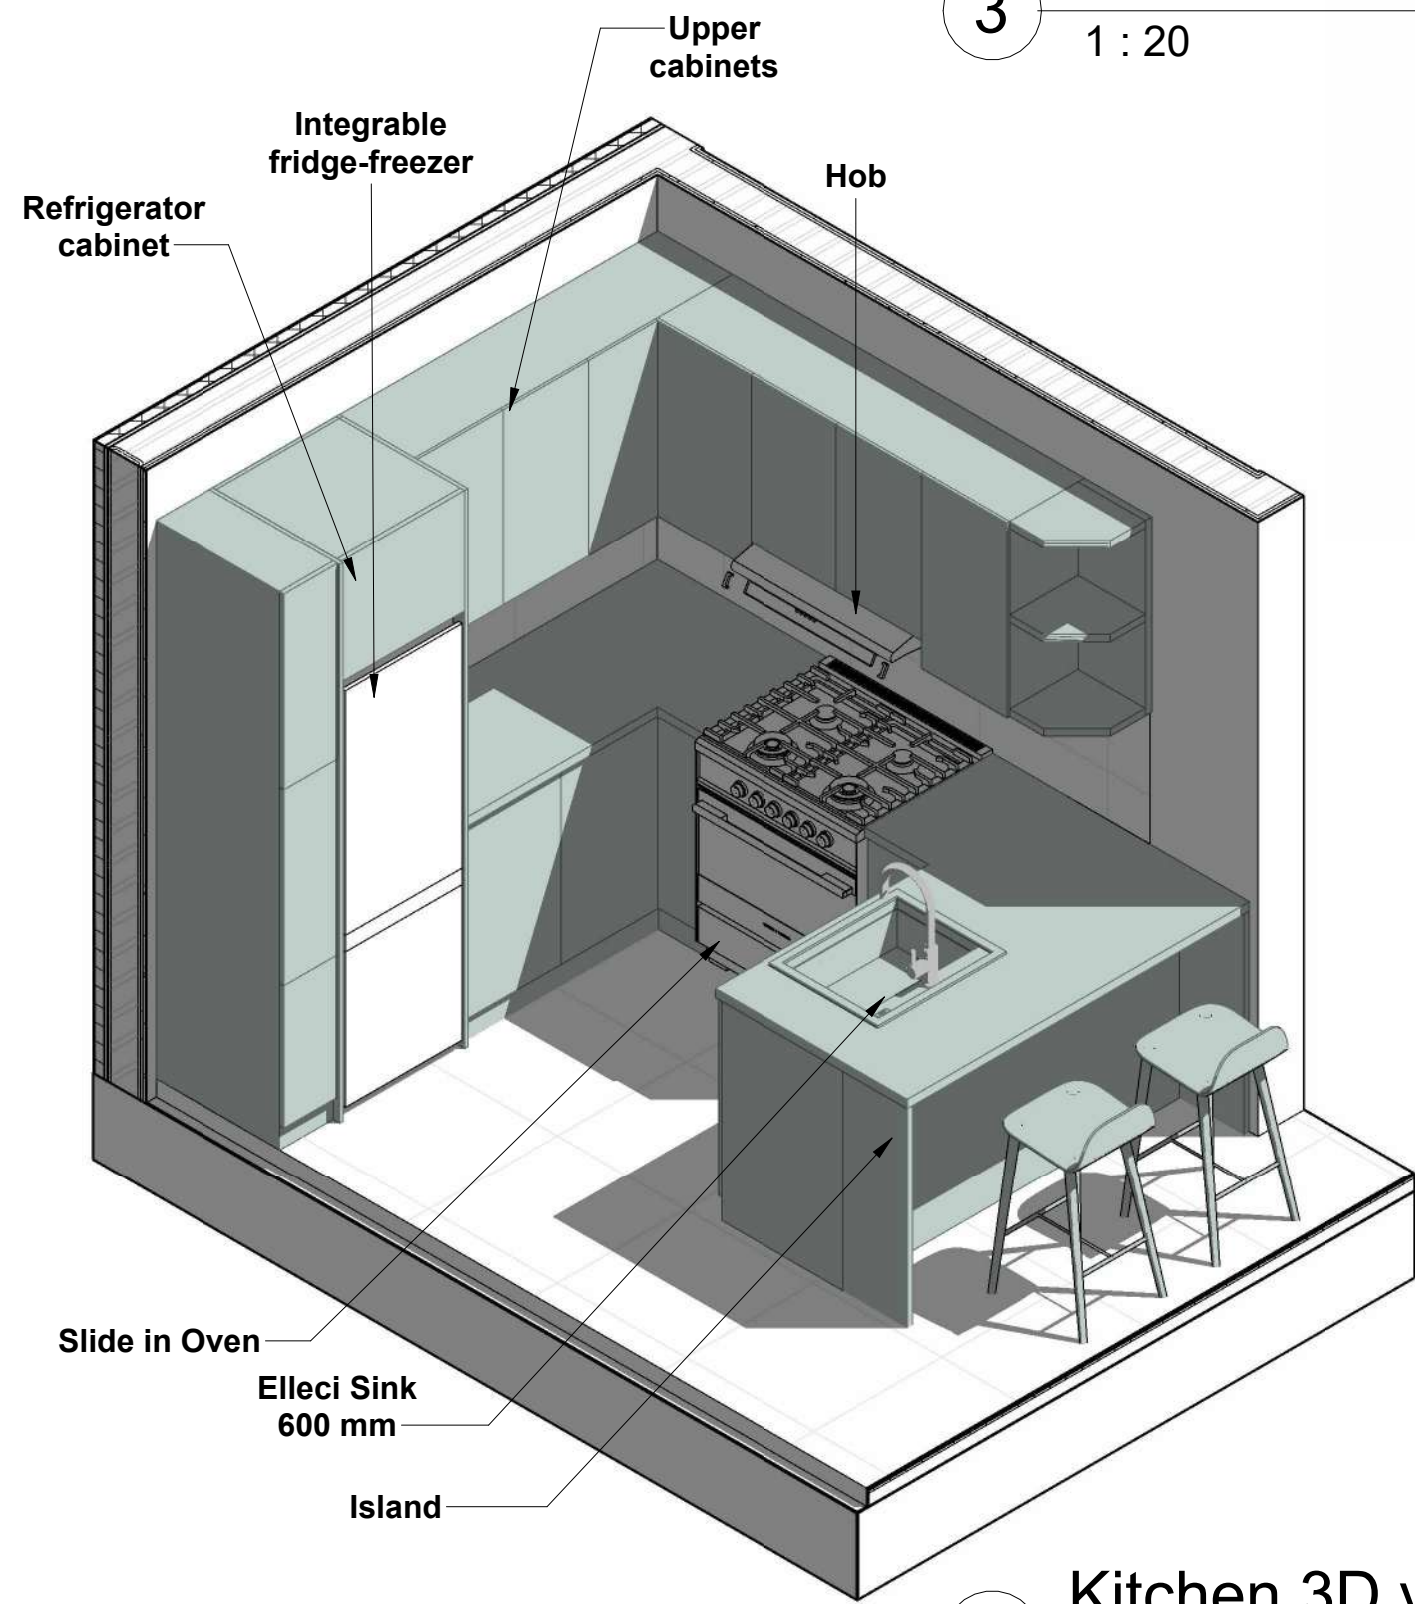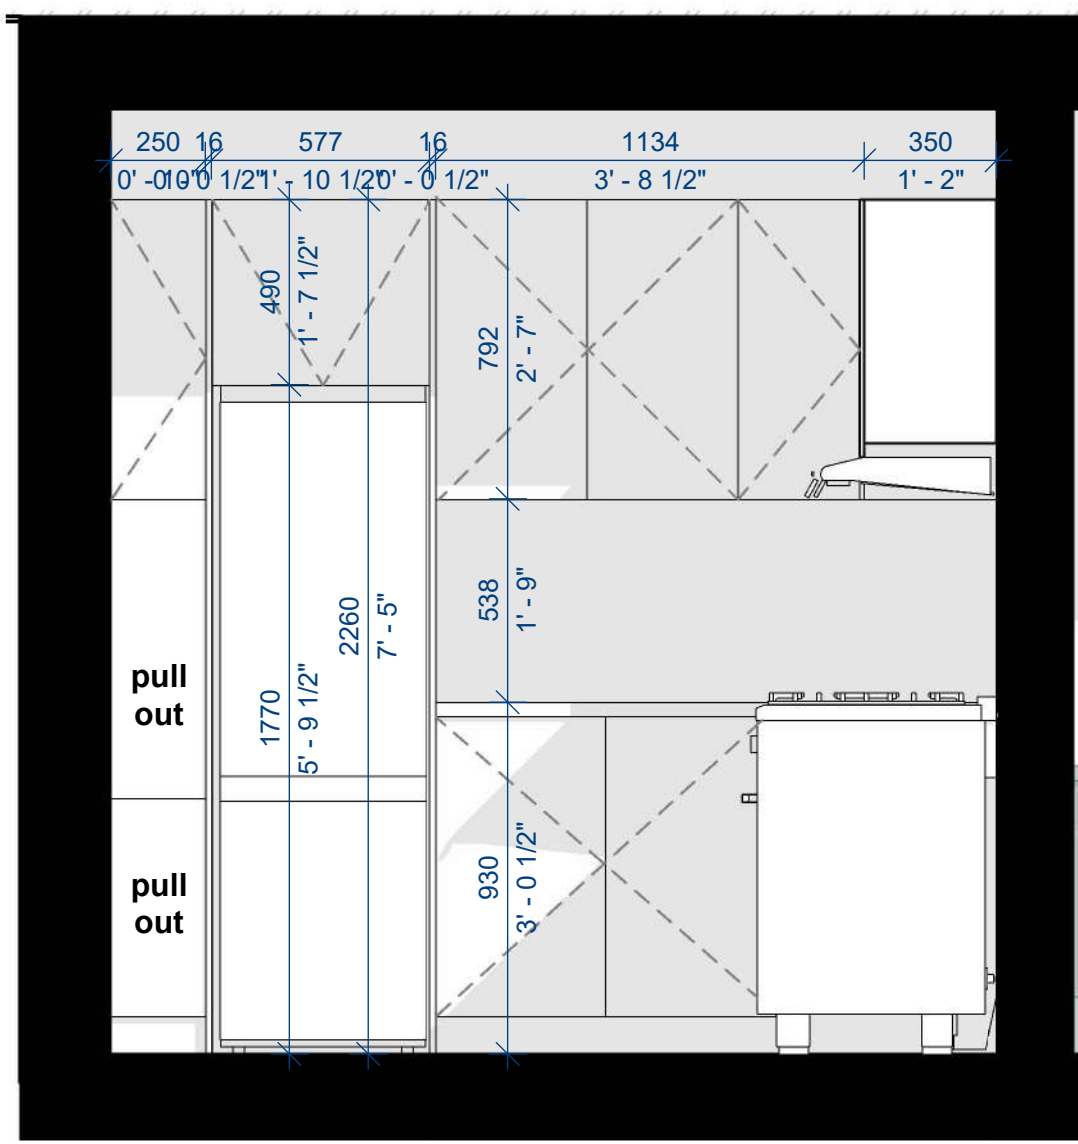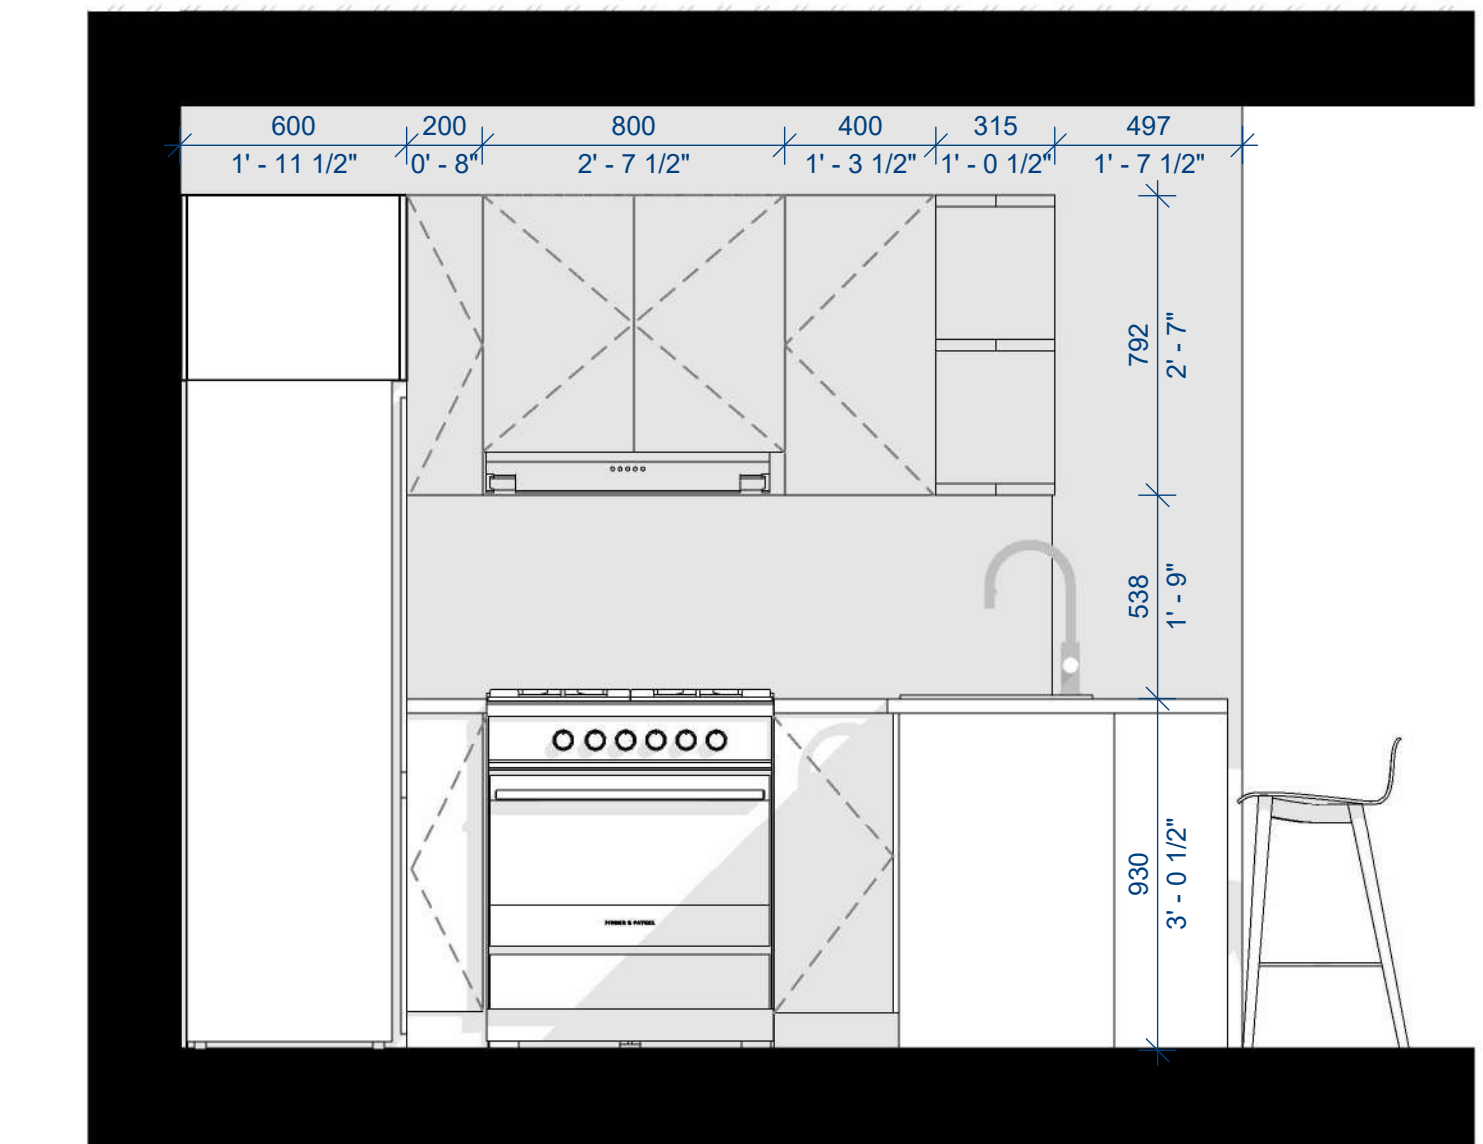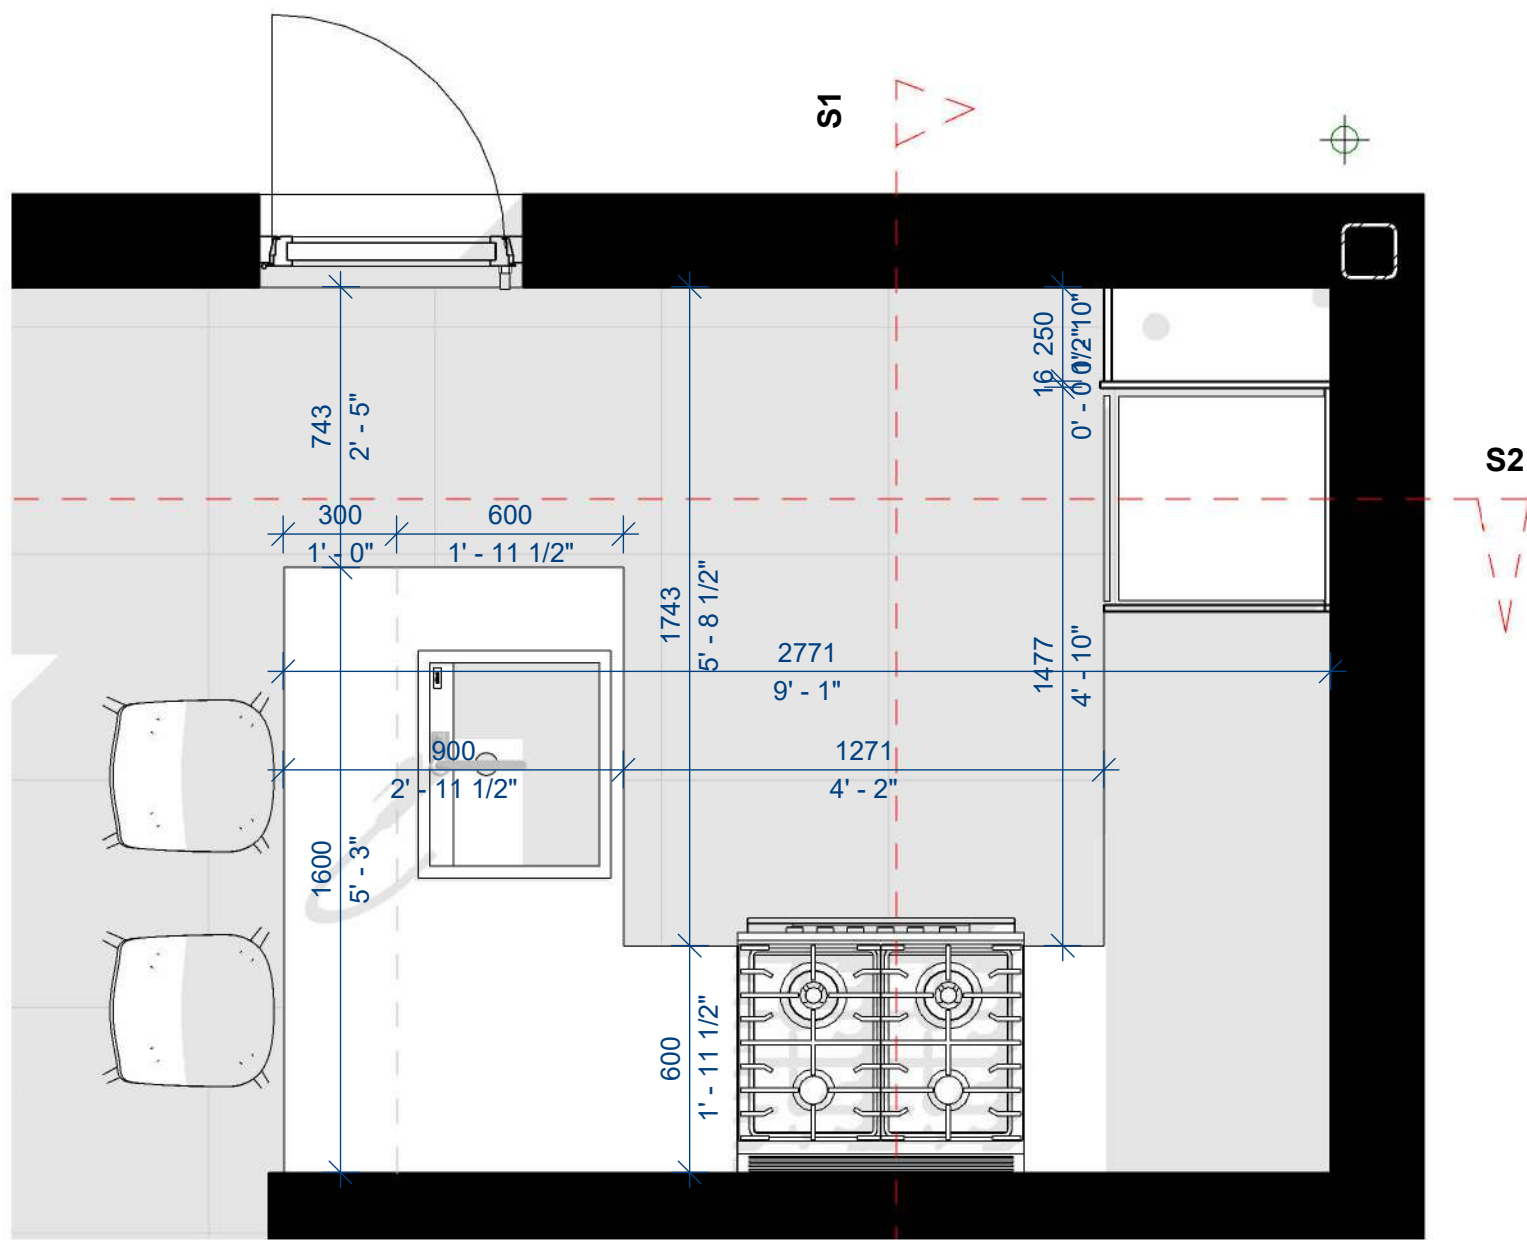

- THESE DRAWINGS MUST BE CHECKED BY THE CUSTOMER OR CONTRACTOR PRIOR TO APPROVAL. ANY ERRORS OR OMISSIONS MUST BE REPORTED IN WRITING TO BAUHU PRIOR TO COMMENCEMENT OF CONSTRUCTION.
- ARCHITECTURAL DRAWINGS SHOULD BE READ IN CONJUNCTION WITH STRUCTURAL DETAILING AND FABRICATION GENERAL ASSEMBLY DRAWINGS.
- FOR CONSTRUCTION PURPOSES, USE ONLY THE LATEST APPROVED DRAWINGS LABELED 'ISSUED FOR CONSTRUCTION'.
- DO NOT SCALE FROM THIS DRAWING.
- THE COMPANY OPERATES USING METRIC DIMENSIONS AS THE PRINCIPAL DENOMINATION.
- ALL CONCRETE WORKS ARE OUTSIDE OF THE SCOPE OF THE COMPANY. INFORMATION REGARDING SLAB DESIGN AND CONNECTIONS IN THESE DRAWINGS ARE INTENDED FOR GUIDANCE ONLY. FOUNDATION AND SLAB WORKS SHOULD BE DESIGNED AND APPROVED BY A LOCAL STRUCTURAL ENGINEER.
- THE COMPANY RETAINS FULL TITLE AND OWNERSHIP OF THESE PLANS AND DESIGNS. ANY UNAUTHORIZED USE, REPRODUCTION, OR DISTRIBUTION OF THESE PLANS, WHETHER IN WHOLE OR PART, IS EXPRESSLY PROHIBITED WITHOUT PRIOR WRITTEN CONSENT.
- THE HYBRID STEEL FRAME CONSTRUCTION SYSTEM AND METHODOLOGY DESCRIBED IN THESE PLANS HAS BEEN DEVELOPED BY THE COMPANY AND IS SUBJECT TO A PATENT APPLICATION & ASSIGNMENT US APPLICATION NO. 63/722,841

No.	Revision	Date

ISSUED FOR:

- ☐ Issued for information
- ☐ Issued for client approval
- ☐ Issued for fabrication
- ☐ Issued for construction

Caribbean cottage

DRAWING TITLE:

Kitchen Plan and 3D view

DRAWN BY:

Bernat Stefana

SCALE:

1 : 20

DRAWING NO:


A44

DATE:

18.11.2025

Mixer

Bruma
Model: Kitchen Faucets
Name: Sink mixer with swivel spout
and pull out handshower - Ginger
Reference: 122 700 3CR
Colour: Chrome
Count: 1

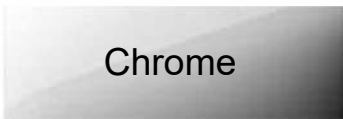

Nobilia Finishes

Worktop
Laminated 38 mm
376
Limestone reproduction




Kitchen - tiles

Garland Pearl RL05 - 45 x
45 cm . 18" x 18" / M15
45x45cm, Stone, Not
Rectified
Glazed Porcelain Tiles,
Mate

Kitchen Sink/Laundry sink

Sink Model: Elleci 1 bowl sink
Dimensions: 610x500
Reference: QUADRA 110
Colour: Dark Grey K99
Count: 1
<https://www.elleci.com/sinks/quadra-110/>

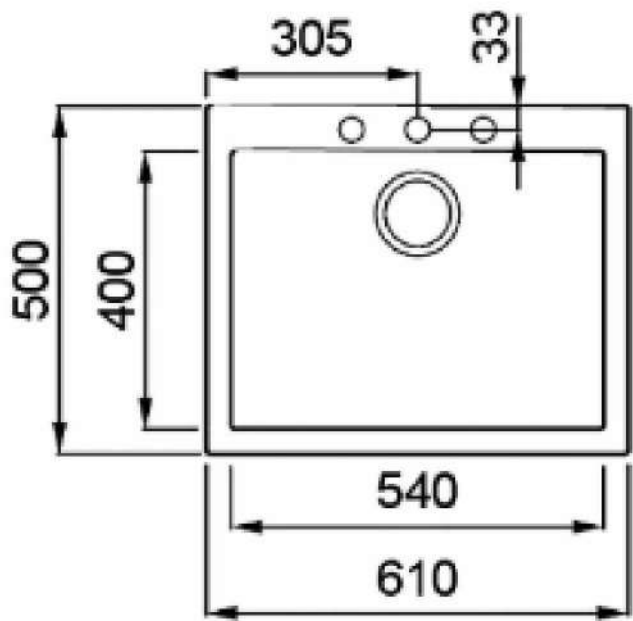

Nobilia Finishes

Handles - lower cabinets
012
Recessed Handle (LINE N),
Bronze metallic colour



Nobilia Finishes

Fronts suspended cabinets
415 - Sand

Carcase
122 - Sand



Carcase




Fronts

Nobilia Finishes

Fronts lower cabinets+
fridge cabinet + island
414 - Volcanic grey

Carcase
194 - Slate grey

 

Carcase



Fronts



1. THESE DRAWINGS MUST BE CHECKED BY THE CUSTOMER OR CONTRACTOR PRIOR TO APPROVAL. ANY ERRORS OR OMISSIONS MUST BE REPORTED IN WRITING TO BAUHU PRIOR TO COMMENCEMENT OF CONSTRUCTION.
2. ARCHITECTURAL DRAWINGS SHOULD BE READ IN CONJUNCTION WITH STRUCTURAL DETAILING AND FABRICATION GENERAL ASSEMBLY DRAWINGS.
3. FOR CONSTRUCTION PURPOSES, USE ONLY THE LATEST APPROVED DRAWINGS LABELED 'ISSUED FOR CONSTRUCTION'.
4. DO NOT SCALE FROM THIS DRAWING.
5. THE COMPANY OPERATES USING METRIC DIMENSIONS AS THE PRINCIPAL DENOMINATION.
6. ALL CONCRETE WORKS ARE OUTSIDE OF THE SCOPE OF THE COMPANY. INFORMATION REGARDING SLAB DESIGN AND CONNECTIONS IN THESE DRAWINGS ARE INTENDED FOR GUIDENCE ONLY. FOUNDATION AND SLAB WORKS SHOULD BE DESIGNED AND APPROVED BY A LOCAL STRUCTURAL ENGINEER.
7. THE COMPANY RETAINS FULL TITLE AND OWNERSHIP OF THESE PLANS AND DESIGNS. ANY UNAUTHORISED USE, REPRODUCTION, OR DISTRIBUTION OF THESE PLANS, WHETHER IN WHOLE OR PART, IS EXPRESSLY PROHIBITED WITHOUT PRIOR WRITTEN CONSENT.
8. THE HYBRID STEEL FRAME CONSTRUCTION SYSTEM AND METHODOLOGY DESCRIBED IN THESE PLANS HAS BEEN DEVELOPED BY THE COMPANY AND IS SUBJECT TO A PATENT APPLICATION & ASSIGNMENT US APPLICATION NO. 63/722,841

No.	Revision	Date

ISSUED FOR:

Issued for information

Issued for client approval


Issued for fabrication



Issued for construction

Caribbean cottage

DRAWING TITLE:	Kitchen Finishes
DRAWN BY:	Bernat Stefana
SCALE:	
DRAWING NO:	A45
DATE:	18.11.2025

Note:
• Kitchen appliances are shown for cabinet design purposes only and are not supplied.

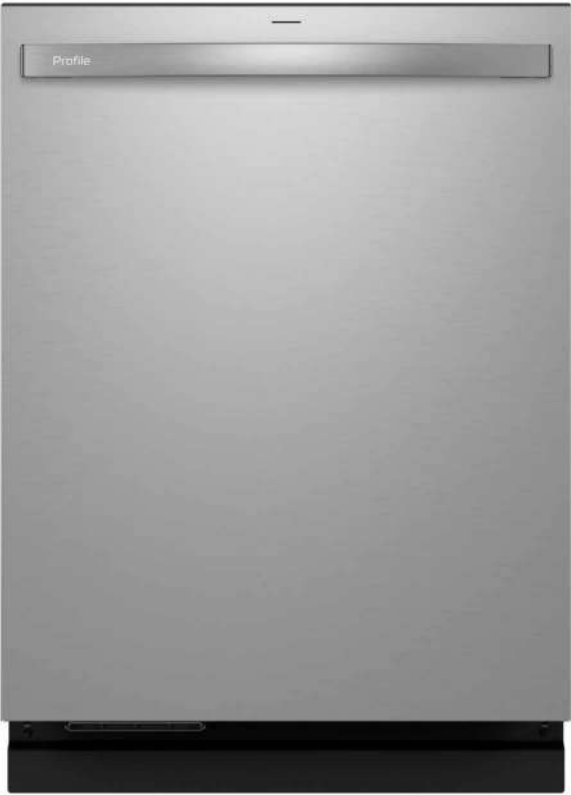Refrigerator GTE18MSRRSS GE® ENERGY STAR® 18.3 Cu. Ft. Top-Freezer Refrigerator Dimensions: 66 3/4 H x 29 3/4 W x 32 7/8 D 1695.45 H x 755.65 W x 835.025 D (mm) 	Refrigerator GTE18MSRRSS DeLonghi Modern 70 DDC 707-DF Dimensions: width 70 cm 	BAUHU MODULAR • BUILDING • SOLUTIONS 1. THESE DRAWINGS MUST BE CHECKED BY THE CUSTOMER OR CONTRACTOR PRIOR TO APPROVAL. ANY ERRORS OR OMISSIONS MUST BE REPORTED IN WRITING TO BAUHU PRIOR TO COMMENCEMENT OF CONSTRUCTION. 2. ARCHITECTURAL DRAWINGS SHOULD BE READ IN CONJUNCTION WITH STRUCTURAL DETAILING AND FABRICATION GENERAL ASSEMBLY DRAWINGS. 3. FOR CONSTRUCTION PURPOSES, USE ONLY THE LATEST APPROVED DRAWINGS LABELED 'ISSUED FOR CONSTRUCTION'. 4. DO NOT SCALE FROM THIS DRAWING. 5. THE COMPANY OPERATES USING METRIC DIMENSIONS AS THE PRINCIPAL DENOMINATION. 6. ALL CONCRETE WORKS ARE OUTSIDE OF THE SCOPE OF THE COMPANY. INFORMATION REGARDING SLAB DESIGN AND CONNECTIONS IN THESE DRAWINGS ARE INTENDED FOR GUIDENCE ONLY. FOUNDATION AND SLAB WORKS SHOULD BE DESIGNED AND APPROVED BY A LOCAL STRUCTURAL ENGINEER. 7. THE COMPANY RETAINS FULL TITLE AND OWNERSHIP OF THESE PLANS AND DESIGNS. ANY UNAUTHORISED USE, REPRODUCTION, OR DISTRIBUTION OF THESE PLANS, WHETHER IN WHOLE OR PART, IS EXPRESSLY PROHIBITED WITHOUT PRIOR WRITTEN CONSENT. 8. THE HYBRID STEEL FRAME CONSTRUCTION SYSTEM AND METHODOLOGY DESCRIBED IN THESE PLANS HAS BEEN DEVELOPED BY THE COMPANY AND IS SUBJECT TO A PATENT APPLICATION & ASSIGNMENT US APPLICATION NO. 63/722,841																																	
Built-in Dishwasher PDT795SYVFS GE Profile™ ENERGY STAR Smart UltraFresh System Dishwasher with Microban™ Antimicrobial Technology with Deep Clean Washing 3rd Rack, 39 dBA Dimensions: 34 H x 23 3/4 W x 24 D 863.6 H x 603.25 W x 609.6 D (mm) Color: Fingerprint Resistant Stainless 	Hood PVX7300SJSS GE Profile™ 30" Under The Cabinet Hood Dimensions: 5 1/2 H x 29 7/8 W x 20 D 139.7 H x 758.825 W x 508 D (mm) 	<table><tr><th>No.</th><th>Revision</th><th>Date</th></tr><tr><td> </td><td> </td><td> </td></tr><tr><td> </td><td> </td><td> </td></tr><tr><td> </td><td> </td><td> </td></tr><tr><td> </td><td> </td><td> </td></tr><tr><td> </td><td> </td><td> </td></tr><tr><td> </td><td> </td><td> </td></tr><tr><td> </td><td> </td><td> </td></tr><tr><td> </td><td> </td><td> </td></tr><tr><td> </td><td> </td><td> </td></tr><tr><td> </td><td> </td><td> </td></tr></table> ISSUED FOR: Issued for information Issued for client approval Issued for fabrication Issued for construction Caribbean cottage	No.	Revision	Date																														
No.	Revision	Date																																	
Washer GFW655SSVWW 5.0 cu. ft. Capacity Smart Front Load ENERGY STAR® Steam Washer with SmartDispense™ UltraFresh Vent System with OdorBlock™ and Sanitize + Allergen 	Dryer GFD65GSSVWW 7.8 cu. ft. Capacity Smart Front Load Gas Dryer with Steam and Sanitize Cycle 	DRAWING TITLE: Kitchen Appliances DRAWN BY: Bernat Stefana SCALE: DRAWING NO: A46																																	
Note: • Kitchen appliances are shown for cabinet design purposes only and are not supplied.		DATE: 18.11.2025																																	

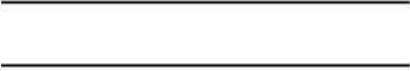 Interior Finishes Floor Tiles Garland Pearl RL05 - 45 x 45 cm . 18" x 18" / M15 45x45cm, Stone, Not Rectified Glazed Porcelain Tiles, Mate Kitchen backsplash Garland Pearl RL05 - 45 x 45 cm . 18" x 18" / M15 45x45cm, Stone, Not Rectified Glazed Porcelain Tiles, Mate  Grout Jasmine 130	Exterior Finishes Exterior Wall Finish Exterior Wall Finish Stolit K fine grain exterior plaster Colour: RAL9003 Signal White RGB: 236, 236, 232 HEX code: #ECECE8. 	BAUHU MODULAR • BUILDING • SOLUTIONS 1. THESE DRAWINGS MUST BE CHECKED BY THE CUSTOMER OR CONTRACTOR PRIOR TO APPROVAL. ANY ERRORS OR OMISSIONS MUST BE REPORTED IN WRITING TO BAUHU PRIOR TO COMMENCEMENT OF CONSTRUCTION. 2. ARCHITECTURAL DRAWINGS SHOULD BE READ IN CONJUNCTION WITH STRUCTURAL DETAILING AND FABRICATION GENERAL ASSEMBLY DRAWINGS. 3. FOR CONSTRUCTION PURPOSES, USE ONLY THE LATEST APPROVED DRAWINGS LABELED 'ISSUED FOR CONSTRUCTION'. 4. DO NOT SCALE FROM THIS DRAWING. 5. THE COMPANY OPERATES USING METRIC DIMENSIONS AS THE PRINCIPAL DENOMINATION. 6. ALL CONCRETE WORKS ARE OUTSIDE OF THE SCOPE OF THE COMPANY. INFORMATION REGARDING SLAB DESIGN AND CONNECTIONS IN THESE DRAWINGS ARE INTENDED FOR GUIDENCE ONLY. FOUNDATION AND SLAB WORKS SHOULD BE DESIGNED AND APPROVED BY A LOCAL STRUCTURAL ENGINEER. 7. THE COMPANY RETAINS FULL TITLE AND OWNERSHIP OF THESE PLANS AND DESIGNS. ANY UNAUTHORISED USE, REPRODUCTION, OR DISTRIBUTION OF THESE PLANS, WHETHER IN WHOLE OR PART, IS EXPRESSLY PROHIBITED WITHOUT PRIOR WRITTEN CONSENT. 8. THE HYBRID STEEL FRAME CONSTRUCTION SYSTEM AND METHODOLOGY DESCRIBED IN THESE PLANS HAS BEEN DEVELOPED BY THE COMPANY AND IS SUBJECT TO A PATENT APPLICATION & ASSIGNMENT US APPLICATION NO. 63/722,841																														
Bathroom tiles 1.Stella White SA05R - 34 x 66,5 cm . 13,4" x 26,2" / R16 34x66,5cm, Cor, Não Rectificado Revestimento Pasta Branca, Brilho 2.Stella Brick Blue SA53R - 34 x 66,5 cm . 13,4" x 26,2" / R17 Decorações 34x66,5cm, Cor, Não Rectificado Revestimento Pasta Branca, Brilho  Grout White 100 Stella White SA05R Stella Brick Blue SA53R	Cortizo Window/Door Frames https://www.cortizo.com/paginas/carta_standard Glass https://www.guardianglass.com/gb/en/our-glass/glass-types/solar-control-glass 44.2+16argon we+6 SNX	<table><tr><th>No.</th><th>Revision</th><th>Date</th></tr><tr><td></td><td></td><td></td></tr><tr><td></td><td></td><td></td></tr><tr><td></td><td></td><td></td></tr><tr><td></td><td></td><td></td></tr><tr><td></td><td></td><td></td></tr><tr><td></td><td></td><td></td></tr><tr><td></td><td></td><td></td></tr><tr><td></td><td></td><td></td></tr><tr><td></td><td></td><td></td></tr></table>	No.	Revision	Date																											
No.	Revision	Date																														
Ceiling Colour CIN White #0501 Wall Colour CIN Marble Beige #1390 		ISSUED FOR: Issued for information Issued for client approval Issued for fabrication Issued for construction Caribbean cottage																														
 Furniture type: Compincar - model 1003 Interior Doors: Compincar - Lisa  LISA		DRAWING TITLE: Finishes DRAWN BY: Bernat Stefana SCALE: DRAWING NO: A47 DATE: 18.11.2025																														

HRS CONNECTIONS			BAUHU MODULAR • BUILDING • SOLUTIONS 1. THESE DRAWINGS MUST BE CHECKED BY THE CUSTOMER OR CONTRACTOR PRIOR TO APPROVAL. ANY ERRORS OR OMISSIONS MUST BE REPORTED IN WRITING TO BAUHU PRIOR TO COMMENCEMENT OF CONSTRUCTION. 2. ARCHITECTURAL DRAWINGS SHOULD BE READ IN CONJUNCTION WITH STRUCTURAL DETAILING AND FABRICATION GENERAL ASSEMBLY DRAWINGS. 3. FOR CONSTRUCTION PURPOSES, USE ONLY THE LATEST APPROVED DRAWINGS LABELED 'ISSUED FOR CONSTRUCTION'. 4. DO NOT SCALE FROM THIS DRAWING. 5. THE COMPANY OPERATES USING METRIC DIMENSIONS AS THE PRINCIPAL DENOMINATION. 6. ALL CONCRETE WORKS ARE OUTSIDE OF THE SCOPE OF THE COMPANY. INFORMATION REGARDING SLAB DESIGN AND CONNECTIONS IN THESE DRAWINGS ARE INTENDED FOR GUIDENCE ONLY. FOUNDATION AND SLAB WORKS SHOULD BE DESIGNED AND APPROVED BY A LOCAL STRUCTURAL ENGINEER. 7. THE COMPANY RETAINS FULL TITLE AND OWNERSHIP OF THESE PLANS AND DESIGNS. ANY UNAUTHORISED USE, REPRODUCTION, OR DISTRIBUTION OF THESE PLANS, WHETHER IN WHOLE OR PART, IS EXPRESSLY PROHIBITED WITHOUT PRIOR WRITTEN CONSENT. 8. THE HYBRID STEEL FRAME CONSTRUCTION SYSTEM AND METHODOLOGY DESCRIBED IN THESE PLANS HAS BEEN DEVELOPED BY THE COMPANY AND IS SUBJECT TO A PATENT APPLICATION & ASSIGNMENT US APPLICATION NO. 63/722,841																														
			<table><tr><th>No.</th><th>Revision</th><th>Date</th></tr><tr><td></td><td></td><td></td></tr><tr><td></td><td></td><td></td></tr><tr><td></td><td></td><td></td></tr><tr><td></td><td></td><td></td></tr><tr><td></td><td></td><td></td></tr><tr><td></td><td></td><td></td></tr><tr><td></td><td></td><td></td></tr><tr><td></td><td></td><td></td></tr><tr><td></td><td></td><td></td></tr></table>	No.	Revision	Date																											
No.	Revision	Date																															
Typical Column Beam Stub Connection	Typical Beam Offset Connection																																
Typical Bracing Connection	Typical Column to Beam Splice Connection	Typical Beam to Concrete Connection																															
Typical Roof Column Beam Connection	Typical Column to Beam Fine Plate Connection	Typical Column Beam Fine Plate Connection	ISSUED FOR: Issued for information Issued for client approval Issued for fabrication Issued for construction Caribbean cottage DRAWING TITLE: HRS Connections 3D DRAWN BY: Bernat Stefana SCALE: DRAWING NO: A51 DATE: 18.11.2025																														

LGS CONNECTIONS



- 1. THESE DRAWINGS MUST BE CHECKED BY THE CUSTOMER OR CONTRACTOR PRIOR TO APPROVAL. ANY ERRORS OR OMISSIONS MUST BE REPORTED IN WRITING TO BAUHU PRIOR TO COMMENCEMENT OF CONSTRUCTION.
- 2. ARCHITECTURAL DRAWINGS SHOULD BE READ IN CONJUNCTION WITH STRUCTURAL DETAILING AND FABRICATION GENERAL ASSEMBLY DRAWINGS.
- 3. FOR CONSTRUCTION PURPOSES, USE ONLY THE LATEST APPROVED DRAWINGS LABELED 'ISSUED FOR CONSTRUCTION'.
- 4. DO NOT SCALE FROM THIS DRAWING.
- 5. THE COMPANY OPERATES USING METRIC DIMENSIONS AS THE PRINCIPAL DENOMINATION.
- 6. ALL CONCRETE WORKS ARE OUTSIDE OF THE SCOPE OF THE COMPANY. INFORMATION REGARDING SLAB DESIGN AND CONNECTIONS IN THESE DRAWINGS ARE INTENDED FOR GUIDENCE ONLY. FOUNDATION AND SLAB WORKS SHOULD BE DESIGNED AND APPROVED BY A LOCAL STRUCTURAL ENGINEER.
- 7. THE COMPANY RETAINS FULL TITLE AND OWNERSHIP OF THESE PLANS AND DESIGNS. ANY UNAUTHORISED USE, REPRODUCTION, OR DISTRIBUTION OF THESE PLANS, WHETHER IN WHOLE OR PART, IS EXPRESSLY PROHIBITED WITHOUT PRIOR WRITTEN CONSENT.
- 8. THE HYBRID STEEL FRAME CONSTRUCTION SYSTEM AND METHODOLOGY DESCRIBED IN THESE PLANS HAS BEEN DEVELOPED BY THE COMPANY AND IS SUBJECT TO A PATENT APPLICATION & ASSIGNMENT US APPLICATION NO. 63/722,841

No.	Revision	Date

ISSUED FOR:

Issued for information

Issued for client approval

Issued for fabrication

Issued for construction

Caribbean cottage

DRAWING TITLE:

LGS Connections 3D

DRAWN BY:

Bernat Stefana

SCALE:

DRAWING NO:

A52

DATE:

18.11.2025

ENLARGE ISO SKETCH

Typical Detail : SFS Bottom Track to Concerete Connection (External Wall)

ENLARGE ISO SKETCH

Typical Detail : Bottom Track to Concerete Connection (Internal Wall)

Stud to Bottom Track Connection
(External Wall)

Stud to Bottom Track Connection
(Internal Wall)

Stud to Top Track
Connection (External Wall)

Stud to Top Track
Connection (Internal Wall)

Hit and Miss Nogging to Stud Connection
Detail

Box Jamb to Top Track Connection

Box Jamb to Bottom Track
Connection

Lintel to Jamb Stud
Connection

Typ. Cill to Jamb Stud
Connection

Typ. Cill to Jamb Stud
Connection

Lintel to Jamb Stud
Connection

Typical Frame Connections 1



- 1. THESE DRAWINGS MUST BE CHECKED BY THE CUSTOMER OR CONTRACTOR PRIOR TO APPROVAL. ANY ERRORS OR OMISSIONS MUST BE REPORTED IN WRITING TO BAUHU PRIOR TO COMMENCEMENT OF CONSTRUCTION.
- 2. ARCHITECTURAL DRAWINGS SHOULD BE READ IN CONJUNCTION WITH STRUCTURAL DETAILING AND FABRICATION GENERAL ASSEMBLY DRAWINGS.
- 3. FOR CONSTRUCTION PURPOSES, USE ONLY THE LATEST APPROVED DRAWINGS LABELED 'ISSUED FOR CONSTRUCTION'.
- 4. DO NOT SCALE FROM THIS DRAWING.
- 5. THE COMPANY OPERATES USING METRIC DIMENSIONS AS THE PRINCIPAL DENOMINATION.
- 6. ALL CONCRETE WORKS ARE OUTSIDE OF THE SCOPE OF THE COMPANY. INFORMATION REGARDING SLAB DESIGN AND CONNECTIONS IN THESE DRAWINGS ARE INTENDED FOR GUIDENCE ONLY. FOUNDATION AND SLAB WORKS SHOULD BE DESIGNED AND APPROVED BY A LOCAL STRUCTURAL ENGINEER.
- 7. THE COMPANY RETAINS FULL TITLE AND OWNERSHIP OF THESE PLANS AND DESIGNS. ANY UNAUTHORISED USE, REPRODUCTION, OR DISTRIBUTION OF THESE PLANS, WHETHER IN WHOLE OR PART, IS EXPRESSLY PROHIBITED WITHOUT PRIOR WRITTEN CONSENT.
- 8. THE HYBRID STEEL FRAME CONSTRUCTION SYSTEM AND METHODOLOGY DESCRIBED IN THESE PLANS HAS BEEN DEVELOPED BY THE COMPANY AND IS SUBJECT TO A PATENT APPLICATION & ASSIGNMENT
US APPLICATION NO. 63/722,841

No.	Revision	Date

ISSUED FOR:

Issued for information

Issued for client approval

Issued for fabrication

Issued for construction

Caribbean cottage

DRAWING TITLE:
Typical Frame Connections
DRAWN BY:
Bernat Stefana
SCALE:
DRAWING NO:
A53
DATE:
18.11.2025

Typical Detail for Two Anchor at Jamb Location

Typical Wall to SFS Wall Connection

Cassette to Cassette Connection

Internal Wall to Cassette Connection at Base

External Wall toJoist Connection at Base

Typ. Internal Wall Connection at Roof Truss at Cassette Location

Typ. Fin Plate Connection Detail

Typ. Fin Plate Connection Detail

SFS Wall to HRS Beam Connection

Typical Frame Connections 2



- 1. THESE DRAWINGS MUST BE CHECKED BY THE CUSTOMER OR CONTRACTOR PRIOR TO APPROVAL. ANY ERRORS OR OMISSIONS MUST BE REPORTED IN WRITING TO BAUHU PRIOR TO COMMENCEMENT OF CONSTRUCTION.
- 2. ARCHITECTURAL DRAWINGS SHOULD BE READ IN CONJUNCTION WITH STRUCTURAL DETAILING AND FABRICATION GENERAL ASSEMBLY DRAWINGS.
- 3. FOR CONSTRUCTION PURPOSES, USE ONLY THE LATEST APPROVED DRAWINGS LABELED 'ISSUED FOR CONSTRUCTION'.
- 4. DO NOT SCALE FROM THIS DRAWING.
- 5. THE COMPANY OPERATES USING METRIC DIMENSIONS AS THE PRINCIPAL DENOMINATION.
- 6. ALL CONCRETE WORKS ARE OUTSIDE OF THE SCOPE OF THE COMPANY. INFORMATION REGARDING SLAB DESIGN AND CONNECTIONS IN THESE DRAWINGS ARE INTENDED FOR GUIDENCE ONLY. FOUNDATION AND SLAB WORKS SHOULD BE DESIGNED AND APPROVED BY A LOCAL STRUCTURAL ENGINEER.
- 7. THE COMPANY RETAINS FULL TITLE AND OWNERSHIP OF THESE PLANS AND DESIGNS. ANY UNAUTHORISED USE, REPRODUCTION, OR DISTRIBUTION OF THESE PLANS, WHETHER IN WHOLE OR PART, IS EXPRESSLY PROHIBITED WITHOUT PRIOR WRITTEN CONSENT.
- 8. THE HYBRID STEEL FRAME CONSTRUCTION SYSTEM AND METHODOLOGY DESCRIBED IN THESE PLANS HAS BEEN DEVELOPED BY THE COMPANY AND IS SUBJECT TO A PATENT APPLICATION & ASSIGNMENT US APPLICATION NO. 63/722,841

No.	Revision	Date

ISSUED FOR:

Issued for information

Issued for client approval

Issued for fabrication

Issued for construction

Caribbean cottage

DRAWING TITLE:
Typical Frame Connections 2
DRAWN BY:
Bernat Stefana
SCALE:
DRAWING NO:
A54
DATE:
18.11.2025

Typical Internal Wall Connection Floor Joist

Floor Blocking to Floor Joist Connection

Cassette to Roof Trusss Connection

Cassette to Floor Joist Connection

Typical Detail at SFS Bottom Track to HRS Beam Connection (External & Internal Wall)

SFS Panel Connection Detail

Typical Frame Connections 3



1. THESE DRAWINGS MUST BE CHECKED BY THE CUSTOMER OR CONTRACTOR PRIOR TO APPROVAL. ANY ERRORS OR OMISSIONS MUST BE REPORTED IN WRITING TO BAUHU PRIOR TO COMMENCEMENT OF CONSTRUCTION.
2. ARCHITECTURAL DRAWINGS SHOULD BE READ IN CONJUNCTION WITH STRUCTURAL DETAILING AND FABRICATION GENERAL ASSEMBLY DRAWINGS.
3. FOR CONSTRUCTION PURPOSES, USE ONLY THE LATEST APPROVED DRAWINGS LABELED 'ISSUED FOR CONSTRUCTION'.
4. DO NOT SCALE FROM THIS DRAWING.
5. THE COMPANY OPERATES USING METRIC DIMENSIONS AS THE PRINCIPAL DENOMINATION.
6. ALL CONCRETE WORKS ARE OUTSIDE OF THE SCOPE OF THE COMPANY. INFORMATION REGARDING SLAB DESIGN AND CONNECTIONS IN THESE DRAWINGS ARE INTENDED FOR GUIDENCE ONLY. FOUNDATION AND SLAB WORKS SHOULD BE DESIGNED AND APPROVED BY A LOCAL STRUCTURAL ENGINEER.
7. THE COMPANY RETAINS FULL TITLE AND OWNERSHIP OF THESE PLANS AND DESIGNS. ANY UNAUTHORISED USE, REPRODUCTION, OR DISTRIBUTION OF THESE PLANS, WHETHER IN WHOLE OR PART, IS EXPRESSLY PROHIBITED WITHOUT PRIOR WRITTEN CONSENT.
8. THE HYBRID STEEL FRAME CONSTRUCTION SYSTEM AND METHODOLOGY DESCRIBED IN THESE PLANS HAS BEEN DEVELOPED BY THE COMPANY AND IS SUBJECT TO A PATENT APPLICATION & ASSIGNMENT
US APPLICATION NO. 63/722,841

No.	Revision	Date

ISSUED FOR:

Issued for information

Issued for client approval

Issued for fabrication

Issued for construction

Caribbean cottage

DRAWING TITLE:

Typical Frame Connections 3

DRAWN BY:

Bernat Stefana

SCALE:

DRAWING NO:

A55

DATE:

18.11.2025

HRS Bracket Detail for Wall Connection

Typ. Truss Outside Plate Connection

Typ. Vertical Splice Connection

Typ. Horizontal Splice Connection

Typ. Truss Bracket Connection

Typ. Corner Truss Connection

Typ. Wall to Beam Top Plate Connection

Typ. Lintel to Wind Post Connection

Cassette to Beam Connection

Typ. Beam to Column Connection Using C Bracket

Typ. Beam to Column Connection Using C Bracket

Typ. Beam to Column Connection Using C Bracket

Typical Frame Connections 4

Hold Down Detail

Typ. Brace Wall Panel Connection with Treaded Rod

Casette to Floor/Roof Joist Connection

Typ. Internal Wall Connection Floor/Roof Joist

(Perpendicular Condition)



- 1. THESE DRAWINGS MUST BE CHECKED BY THE CUSTOMER OR CONTRACTOR PRIOR TO APPROVAL. ANY ERRORS OR OMISSIONS MUST BE REPORTED IN WRITING TO BAUHU PRIOR TO COMMENCEMENT OF CONSTRUCTION.
- 2. ARCHITECTURAL DRAWINGS SHOULD BE READ IN CONJUNCTION WITH STRUCTURAL DETAILING AND FABRICATION GENERAL ASSEMBLY DRAWINGS.
- 3. FOR CONSTRUCTION PURPOSES, USE ONLY THE LATEST APPROVED DRAWINGS LABELED 'ISSUED FOR CONSTRUCTION'.
- 4. DO NOT SCALE FROM THIS DRAWING.
- 5. THE COMPANY OPERATES USING METRIC DIMENSIONS AS THE PRINCIPAL DENOMINATION.
- 6. ALL CONCRETE WORKS ARE OUTSIDE OF THE SCOPE OF THE COMPANY. INFORMATION REGARDING SLAB DESIGN AND CONNECTIONS IN THESE DRAWINGS ARE INTENDED FOR GUIDENCE ONLY. FOUNDATION AND SLAB WORKS SHOULD BE DESIGNED AND APPROVED BY A LOCAL STRUCTURAL ENGINEER.
- 7. THE COMPANY RETAINS FULL TITLE AND OWNERSHIP OF THESE PLANS AND DESIGNS. ANY UNAUTHORISED USE, REPRODUCTION, OR DISTRIBUTION OF THESE PLANS, WHETHER IN WHOLE OR PART, IS EXPRESSLY PROHIBITED WITHOUT PRIOR WRITTEN CONSENT.
- 8. THE HYBRID STEEL FRAME CONSTRUCTION SYSTEM AND METHODOLOGY DESCRIBED IN THESE PLANS HAS BEEN DEVELOPED BY THE COMPANY AND IS SUBJECT TO A PATENT APPLICATION & ASSIGNMENT
US APPLICATION NO. 63/722,841

No.	Revision	Date

ISSUED FOR:

Issued for information

Issued for client approval

Issued for fabrication

Issued for construction

Caribbean cottage

DRAWING TITLE:
Typical Frame Connections 4
DRAWN BY:
Bernat Stefana
SCALE:
DRAWING NO:
A56
DATE:
18.11.2025

General Construction notes

STANDARDS AND CODES OF PRACTICE

- International Building Code (IBC) 2015
- ASCE 7-16- American Society of civil Engineers (Minimum Design loads for buildings & other structures)
- AISC 360-10 - American Institute of steel construction (Specification for structural steel buildings)
- AISI -100-16 - American Iron and Steel Institute (Design of Cold Formed steel & structural members)
- ASTM - American Society for Testing and materials.
- All CFS frame will be designed to AISI LRFD CFS design standard

COLD FORMED STEEL (LGS)

Walls panels and trusses are made up by roll-formed cold rolled, galvanised steel sections fabricated and assembled into frames. Section properties in accordance with BS EN 1993-1-3:2006.
Steel grade S450GD + Z275.
C 70 -50/70- 1.2/1.5/2
C 100 -50/70- 1.2/1.5/2
C 150 -50/70- 1.2/1.5/2
LGS frames are fixed to each other and to the HRS members with specified mechanical fixings.

HOT ROLLED STEEL (HRS)

Material Availability of Hot Rolled Steel Sections is as per European/British sections with grade of S275.
Plate thickness 6, 8, 10, 12mm grade S275, S355.
HRS members are hot dip galvanised and fixed to each other with specified mechanical fixings to form a portal frame.

SLAB FIXINGS

Concrete slab and foundation design is carried out by relevant local engineers and falls outside of the scope of Bauhu construction. HRS columns are supplied with pre-drilled column base plates for ground fixing with specified chemical anchor bolts.
LGS frame base rails are pre-punched for mechanical fixing to a concrete slab using the specified expanding bolts. A damp proof membrane is required.

CONSTRUCTIVE CLADDING

12.5mm lightweight, fire resistant, high density cement board is fixed to the entire exterior wall surface of the assembled building. Cement board is fixed at 300mm CTS to LGS studs and track profiles with AISI C1022 grade coated steel wing tip TEK-3 self-drilling and countersinking fixings 4.8mmx48mm.
Cement board spanning HRS members is adhered to the HRS outer surface.
Constructive cladding joints are sealed with mastic.

OPENING REVEALS CLADDING

12.5mm lightweight, fire resistant, high density cement board is fixed to opening reveals in the same manner. See assembly information and section drawings for dimension details.

CEILINGS

Ceilings are suspended from LGS roof or intermediate floor joists using Knauf C-Form suspended ceiling system mechanically fixed to joists. An insulation layer of 160mm mineral wool insulation is laid inside the ceiling void. Ceilings are finished in two layers of 12.5mm gypsumboard. Knauf moisture panel + Knauf fire panel fixed at 300mm CTS to suspended ceiling profiles with AISI C1022 grade coated steel wing tip TEK-3 self drilling and countersinking fixings 4.8mmx48mm with joints taped and filled.
Internal low VOC acrylic paint finishes are applied per customer selection.

INTERMEDIATE FLOORS

Intermediate floor structures are supported by LGS lattice frame joists mechanically fixed to HRS beams typically at 500mm CTS according to project engineering.
18mm OSB4, termite treated, oriented strand board is fixed to the entire floor surface of the assembled building. OSB4 board is fixed at 300mm CTS to LGS joists with AISI C1022 grade coated steel wing tip TEK-3 self drilling and countersinking fixings 4.8mmx48mm.
6mm cement board floor backer sheets are mechanically fixed to the floor surface to accept client specified floor finishes.

EXTERIOR WALLS

Exterior walls are formed by pre-assembled 150mm x1.5mm profile LGS frames mechanically fixed to adjacent frames, floors and roof/floor joists. Section properties in accordance with BS EN 1993-1-3:2006. Steel grade S450GD + Z275. Frame profiles have pre-punched service holes for cable and pipe passage.
120mm mineral wool insulation is applied in the frame web.
The exterior wall surfaces are clad in a cement board constructive coating (see CONSTRUCTIVE COATING)
The interior wall surfaces are finished in two layers of 12.5mm gypsumboard Knauf moisture panel applied in horizontal format + Knauf fire panel applied in vertical format fixed at 300mm CTS to LGS profiles with AISI C1022 grade coated steel wing tip TEK-3 self drilling and countersinking fixings 4.8mmx48mm with joints taped and filled.
Internal low VOC acrylic paint finishes are applied per customer selection.

INTERIOR WALLS

Interior walls are formed by pre-assembled 150mm x1.5mm profile LGS frames mechanically fixed to adjacent walls, floors and roof/floor joists. Section properties in accordance with BS EN 1993-1-3:2006. Steel grade S450GD + Z275. Frame profiles have pre-punched service holes for cable and pipe passage.
120mm mineral wool insulation is applied in the frame web.
Internal walls are finished in two opposing layers of 12.5mm gypsumboard fixed at 300mm CTS to LGS profiles with AISI C1022 grade coated steel wing tip TEK-3 self drilling and countersinking fixings 4.8mmx48mm.
Knauf moisture panel applied in horizontal format + Knauf fire panel applied in vertical format with joints taped and filled.
Internal low VOC acrylic paint finishes are applied per customer selection.
EXTERIOR FACADE (ETICs)
The external facade is finished in an impact resistant, self colour, thermal and acoustic ETICs (External thermal insulation composite system) coating. An insulation layer of 40mm rigid Rockwool is applied to the cement board constructive coating with mechanical fixings. STO impact resistant plaster base coat is applied with fiberglass mesh and finished in STOLIT finish plaster coat.

FLAT ROOF STRUCTURE (EPDM)

Flat roof structures are supported by LGS lattice frame joists mechanically fixed to HRS beams typically at 500mm CTS according to project engineering.
18mm OSB4, termite treated, oriented strand board is fixed to the entire exterior roof surface of the assembled building. OSB4 is fixed at 300mm CTS to LGS joists with AISI C1022 grade coated steel wing tip TEK-3 self drilling and countersinking fixings 4.8mmx38mm.
A rigid 40mm PIR insulation board is mechanically fixed to the cement board constructive cladding.
Firestone 1.5mm heavy duty EPDM waterproofing membrane is fully bonded to the roof surface and parapet sides with rain water outlets and breather pipe boots at appropriate locations.
Leaf guards are installed in rain water outlets.

PARAPET DETAIL

LGS panels are mechanically fixed to HRS beams to form a parapet extension of exterior walls.
LGS parapet frames are clad in SECOLITE 12.5mm cement board on inner and top faces. A metal capping or acrylic render finishes parapet tops.

ACCESSIBLE ROOFS

Accessible roofs have the same properties as flat (EPDM) roofs. Final floor finishes of ceramic tile or composite decking should be laid over a supplementary geotextile membrane to protect the EPDM membrane. Refer to project files for specific details.

GREEN ROOFS

Green roofs have the same properties as flat (EPDM) roofs. Vegetation in specified containers is added over a textile membrane. Vegetation is NOT supplied.

SOLAR ROOFS

Projects requiring solar (PV) arrays to be roof mounted are subject to specialist analysis.



1. THESE DRAWINGS MUST BE CHECKED BY THE CUSTOMER OR CONTRACTOR PRIOR TO APPROVAL. ANY ERRORS OR OMISSIONS MUST BE REPORTED IN WRITING TO BAUHU PRIOR TO COMMENCEMENT OF CONSTRUCTION.
2. ARCHITECTURAL DRAWINGS SHOULD BE READ IN CONJUNCTION WITH STRUCTURAL DETAILING AND FABRICATION GENERAL ASSEMBLY DRAWINGS.
3. FOR CONSTRUCTION PURPOSES, USE ONLY THE LATEST APPROVED DRAWINGS LABELED 'ISSUED FOR CONSTRUCTION'.
4. DO NOT SCALE FROM THIS DRAWING.
5. THE COMPANY OPERATES USING METRIC DIMENSIONS AS THE PRINCIPAL DENOMINATION.
6. ALL CONCRETE WORKS ARE OUTSIDE OF THE SCOPE OF THE COMPANY. INFORMATION REGARDING SLAB DESIGN AND CONNECTIONS IN THESE DRAWINGS ARE INTENDED FOR GUIDENCE ONLY. FOUNDATION AND SLAB WORKS SHOULD BE DESIGNED AND APPROVED BY A LOCAL STRUCTURAL ENGINEER.
7. THE COMPANY RETAINS FULL TITLE AND OWNERSHIP OF THESE PLANS AND DESIGNS. ANY UNAUTHORISED USE, REPRODUCTION, OR DISTRIBUTION OF THESE PLANS, WHETHER IN WHOLE OR PART, IS EXPRESSLY PROHIBITED WITHOUT PRIOR WRITTEN CONSENT.
8. THE HYBRID STEEL FRAME CONSTRUCTION SYSTEM AND METHODOLOGY DESCRIBED IN THESE PLANS HAS BEEN DEVELOPED BY THE COMPANY AND IS SUBJECT TO A PATENT APPLICATION & ASSIGNMENT
US APPLICATION NO. 63/722,841

No.	Revision	Date

ISSUED FOR:

Issued for information

Issued for client approval

Issued for fabrication

Issued for construction

Caribbean cottage

DRAWING TITLE:
General Construction Notes
DRAWN BY:
Bernat Stefana
SCALE:
DRAWING NO:
A57
DATE:
18.11.2025